


■ 안 내 도



■ 지 적 도

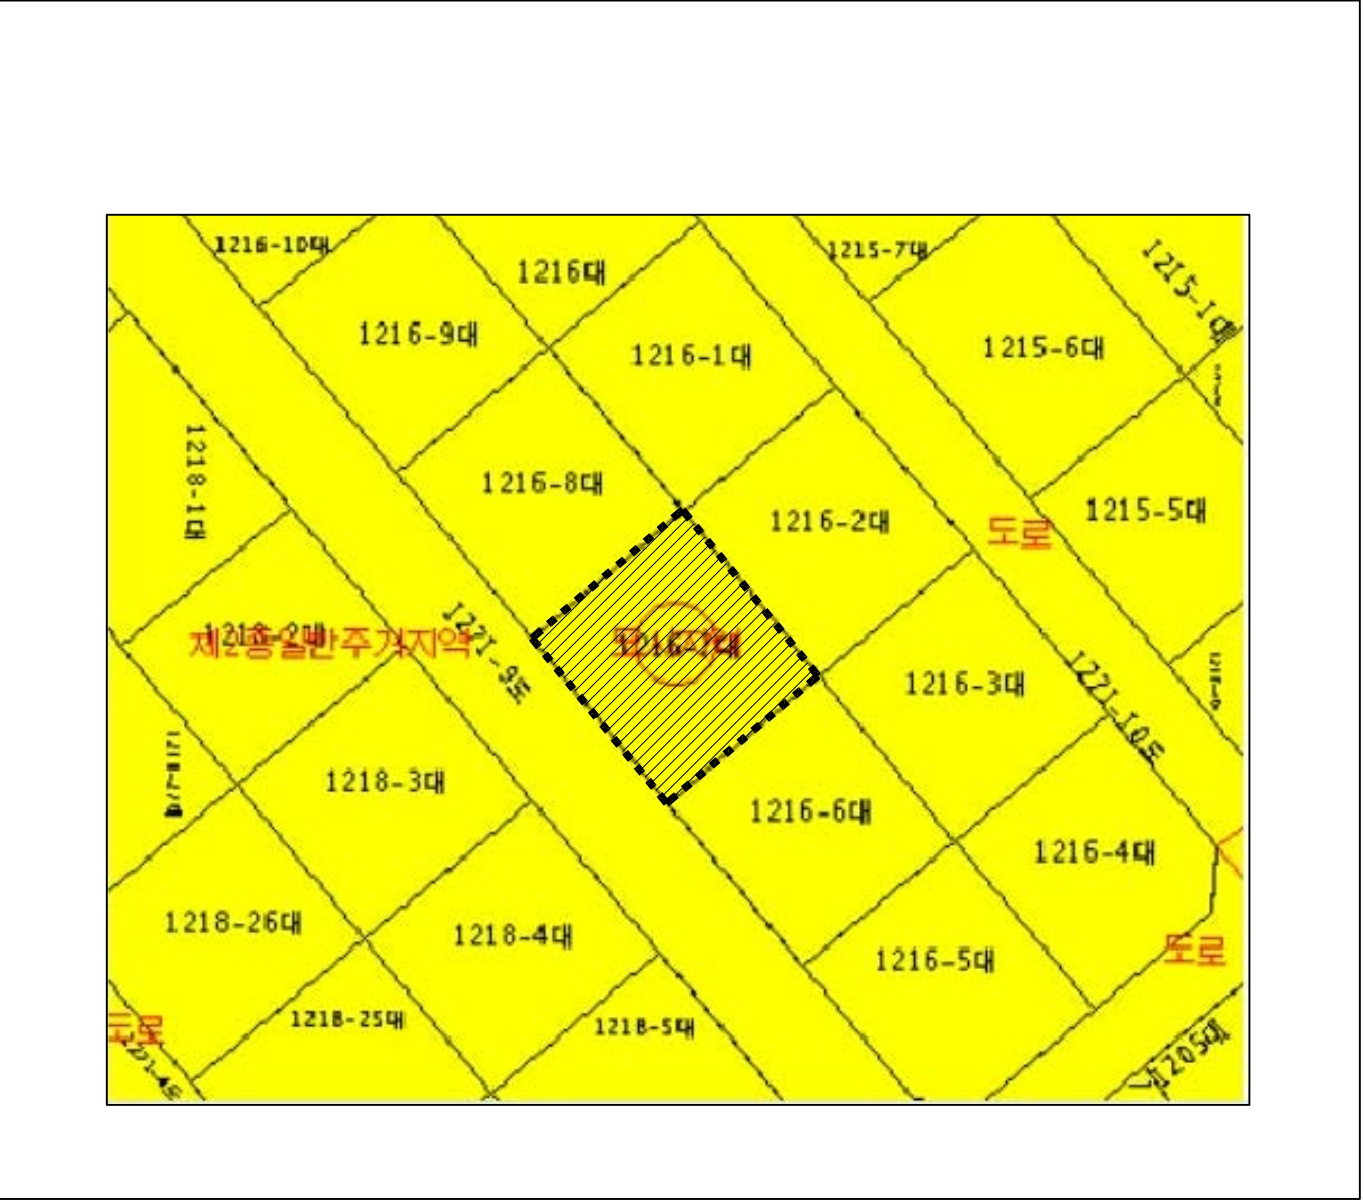



8,000도루


도로경계선 →

경계식단차제거 →

[보행로]
보행안전통로 1500이상
보행자안전통로는 주차장 및 차도의 비탈제와
재질과 색상상 멀리하여 설치
(페인트, 우레탄, 칼리크온크리트 시공금지
/ 석재 또는 블록시공)
보행자안전통로는 미끄러지지 아니하는 재질로
평탄하게 마감하여야함

자동문 설치:유효폭 1000이상
비가연성 1시간
(출입문단차제거)

전자블럭 황색표준매립형 (300x300)
인터폰앞에설치
호출버튼 (*버튼중간에 점자표기 할것)
(높이 800~1200)

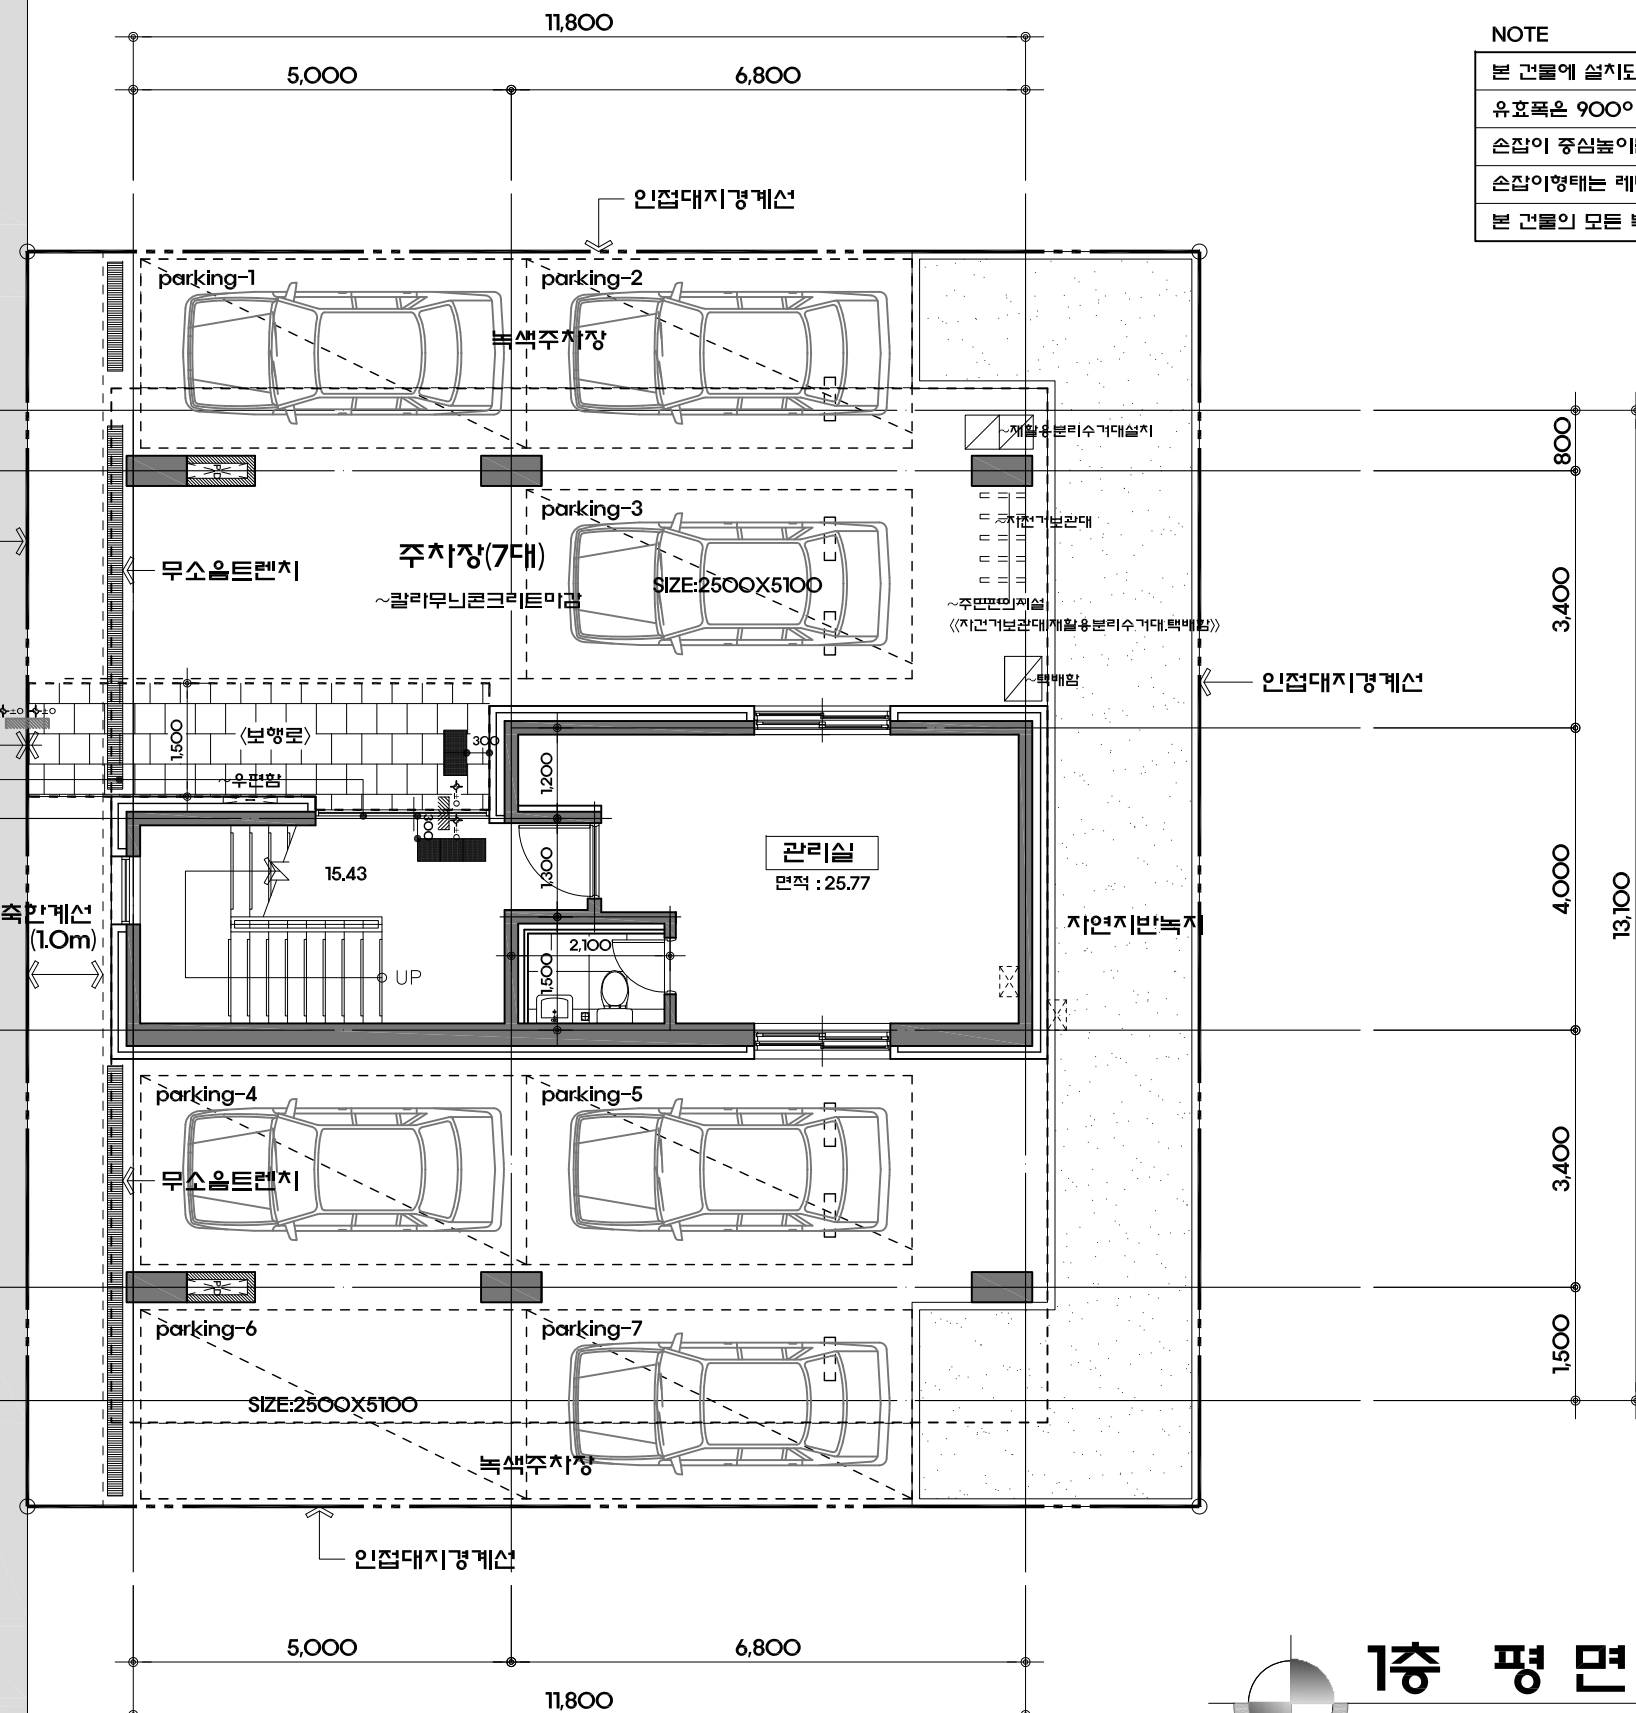

NOTE


본 건물에 설치되는 모든 출입문(내,외부포함)

유효폭은 900이상(단차제거)

손잡이 중심높이는 800~900



손잡이형태는 레버식 또는 수평수직 바형식

본 건물의 모든 복도 유효폭은 1200이상(단차제거)

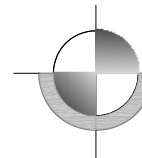

1층 평면도

scale:1/100

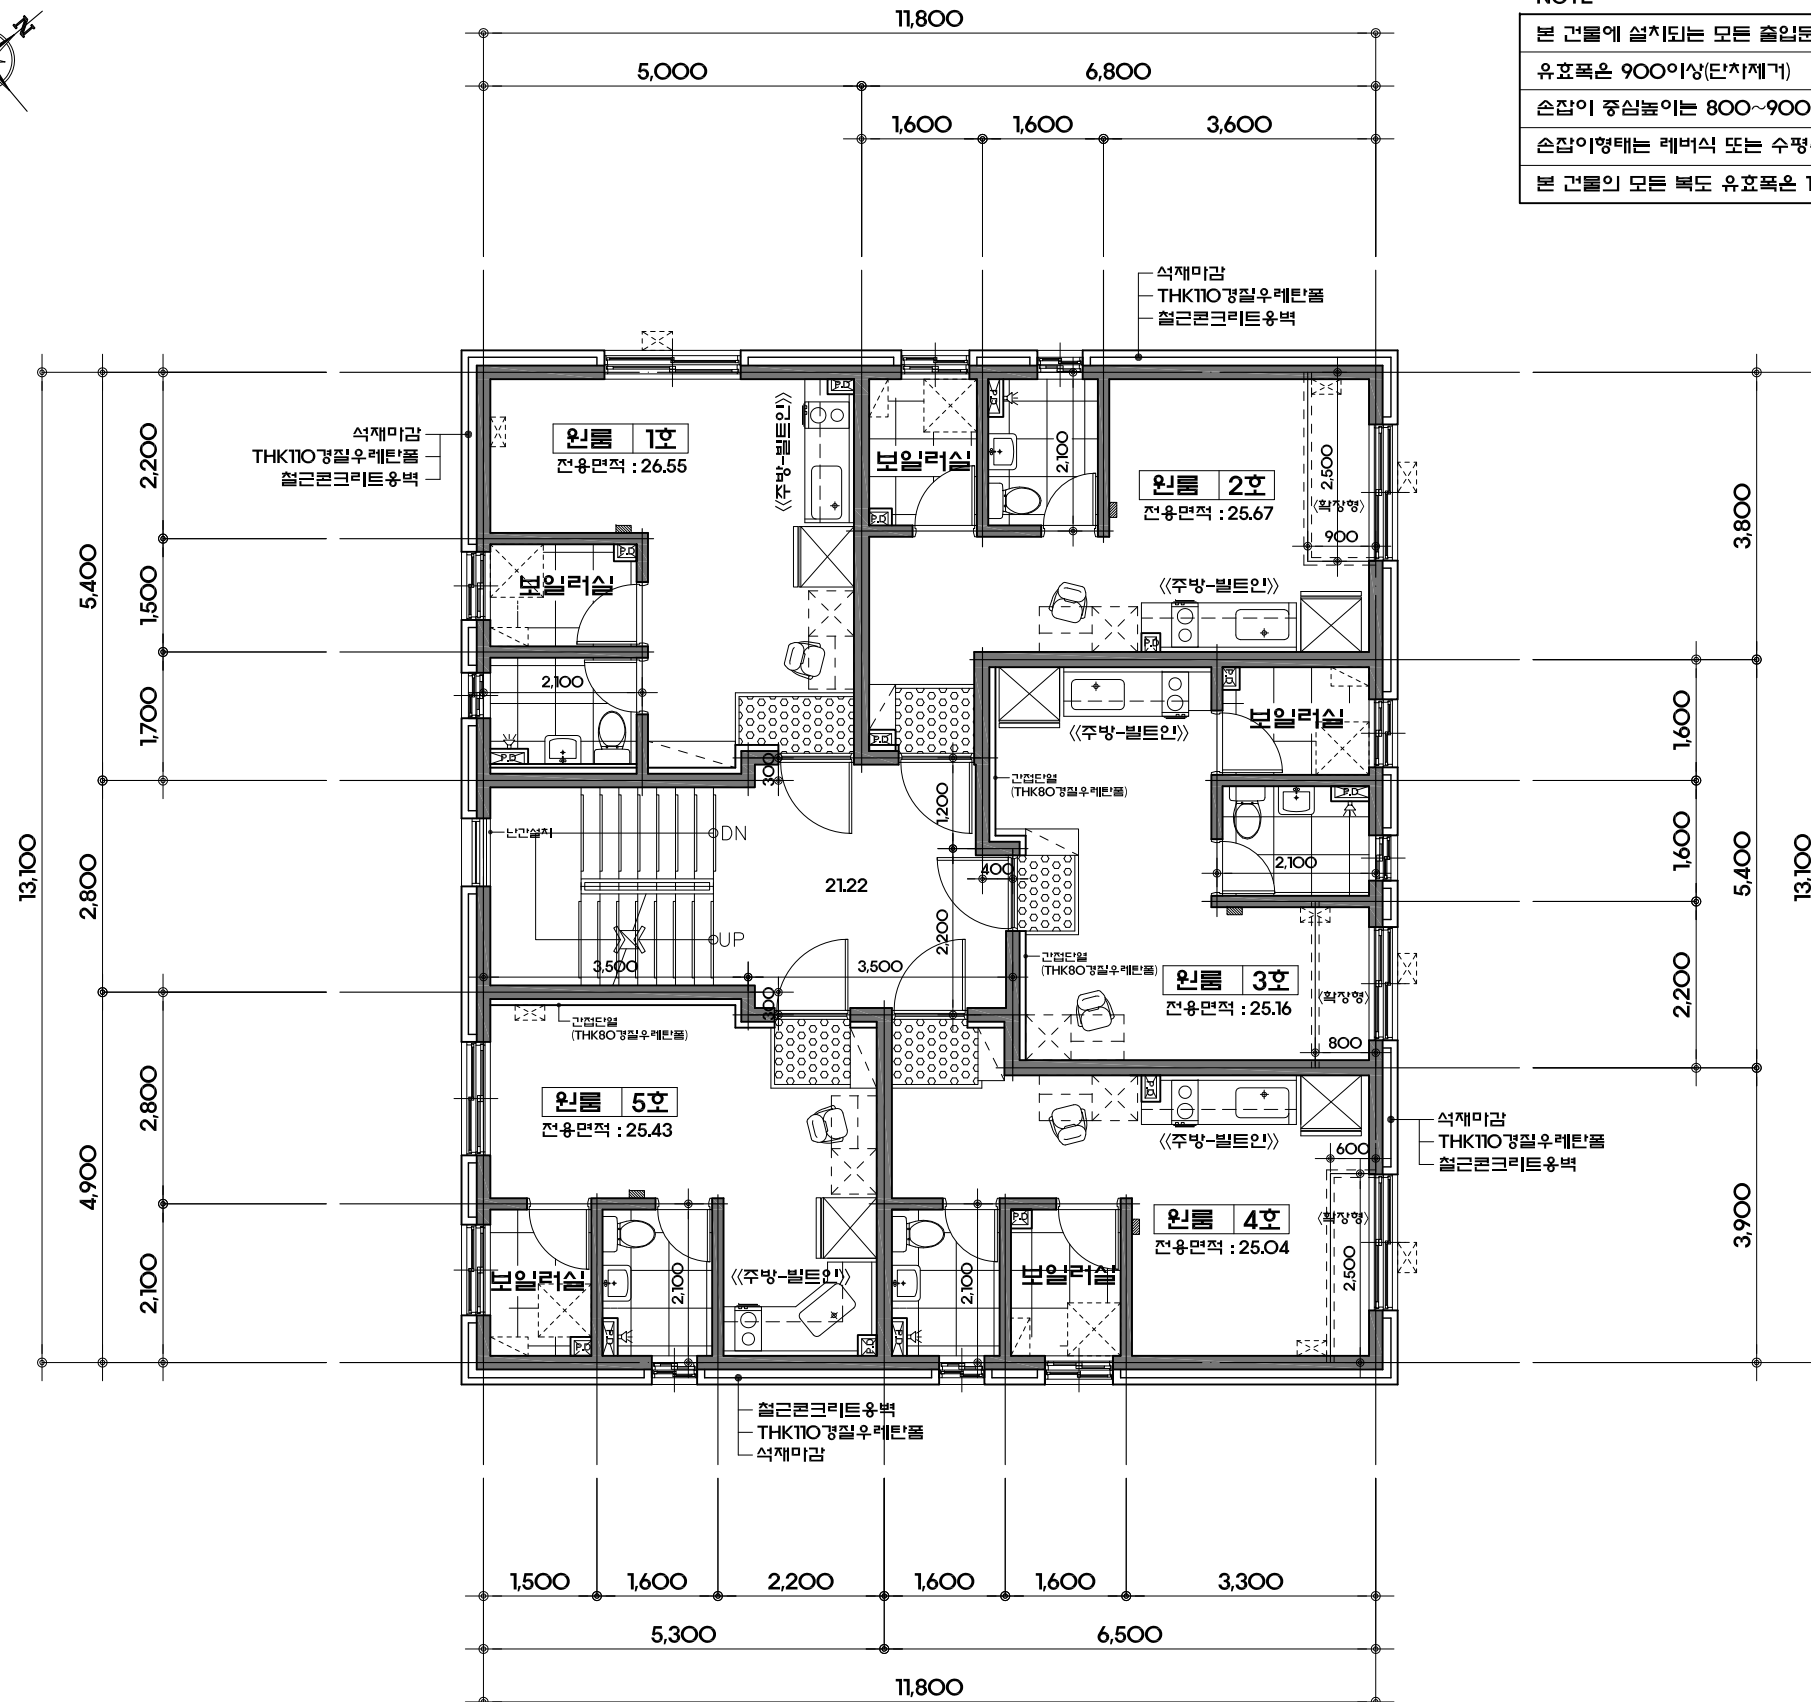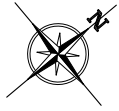


NOTE

본 건물에 설치되는 모든 출입문(내,외부포함)
유효폭은 900이상(단차제거)
손잡이 중심높이는 800~900
손잡이형태는 레버식 또는 수평수직 비행식
본 건물의 모든 복도 유효폭은 1200이상(단차제거)



주 기

구 조	1 (외부)	주차장내 CCTV,쓰레기분리수거,자전거보관대 설치
		우편함 설치 (세대전용, 공용, 반송용, 폐건전지함 구분 설치)
		테라스 창호 PL이중창 설치
		세대 테라스 설치시 세대간 분리벽 계획
		세대 발코니 설치시 차양시설 설치
	2 (계단실)	세대 현관문 도어체크 설치
	3 (내부)	계단참의 현관과 계단 이격거리 (최소600mm이상)
		세대내 욕실, 휴지걸이 매립형 설치
	4 (시공)	콘크리트 폴타이 제거 후 마감공사 시공 (방수, 단열재 시공 등)
		욕실 & 다용도실 스위치 : 문 열리는 방향으로 시공 주차장 차량 진출입구간 무소음트랜치 시공
전 기	5 (미감)	-직접외기(외벽)에 면한 실내벽면 단열재 [아이소핑크(10mm) + 석고보드 마감도면 표기]
		-간접외기(계단실,복도)에 면한 실내벽면 단열재 일반내부 : [경질우레탄폼(80mm) + 석고보드 마감도면 표기] 욕실,다용도실 : [단열재판넬(80mm) 시공]
		*기타 실내 벽면 시멘트 미장 마감
	1	철근 : $f_y=400\text{MPa}$ (HD16이하), 500MPa (SHD19이상)
		콘크리트 : $f_{ck}=24\text{Mpa}$
	2	스리브두께 : 210mm (복배근)
		인벽두께 : 180mm (복배근)
		균이벽두께 : 180mm (복배근)
		세대간벽두께 : 200mm (복배근)
비 고	1	내벽두께 : 150mm (복배근)
		-콘센트 설치 (바닥 마감선 기준)
		[거실] 스탠드형 에어컨 : 350
		[안방] 벽걸이형 에어컨 : 1900
		[화장실] 양변기 원 : 900
	2	[주방] 조리대 : 중양 / 냉장고 : 350 / 후드 : 2100
		-비디오폰(VP),보일러온도조절기(B), 스위치(S), 전열교환기스위치(E) (거실이트홀 위치)
		에어컨 실외기
		냉매, 배수관 (배수관수직매립)
		* 세대현관문 ## 규격"를"포함 : 1000X2200 * 반드시 가열대위에도 선반 설치할 것. * 청년주택(빌트인) : 냉장고,벽걸이에어컨,세탁기,불박이장,책상

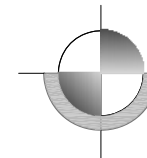

2,3층 평 면 도

scale:1/100

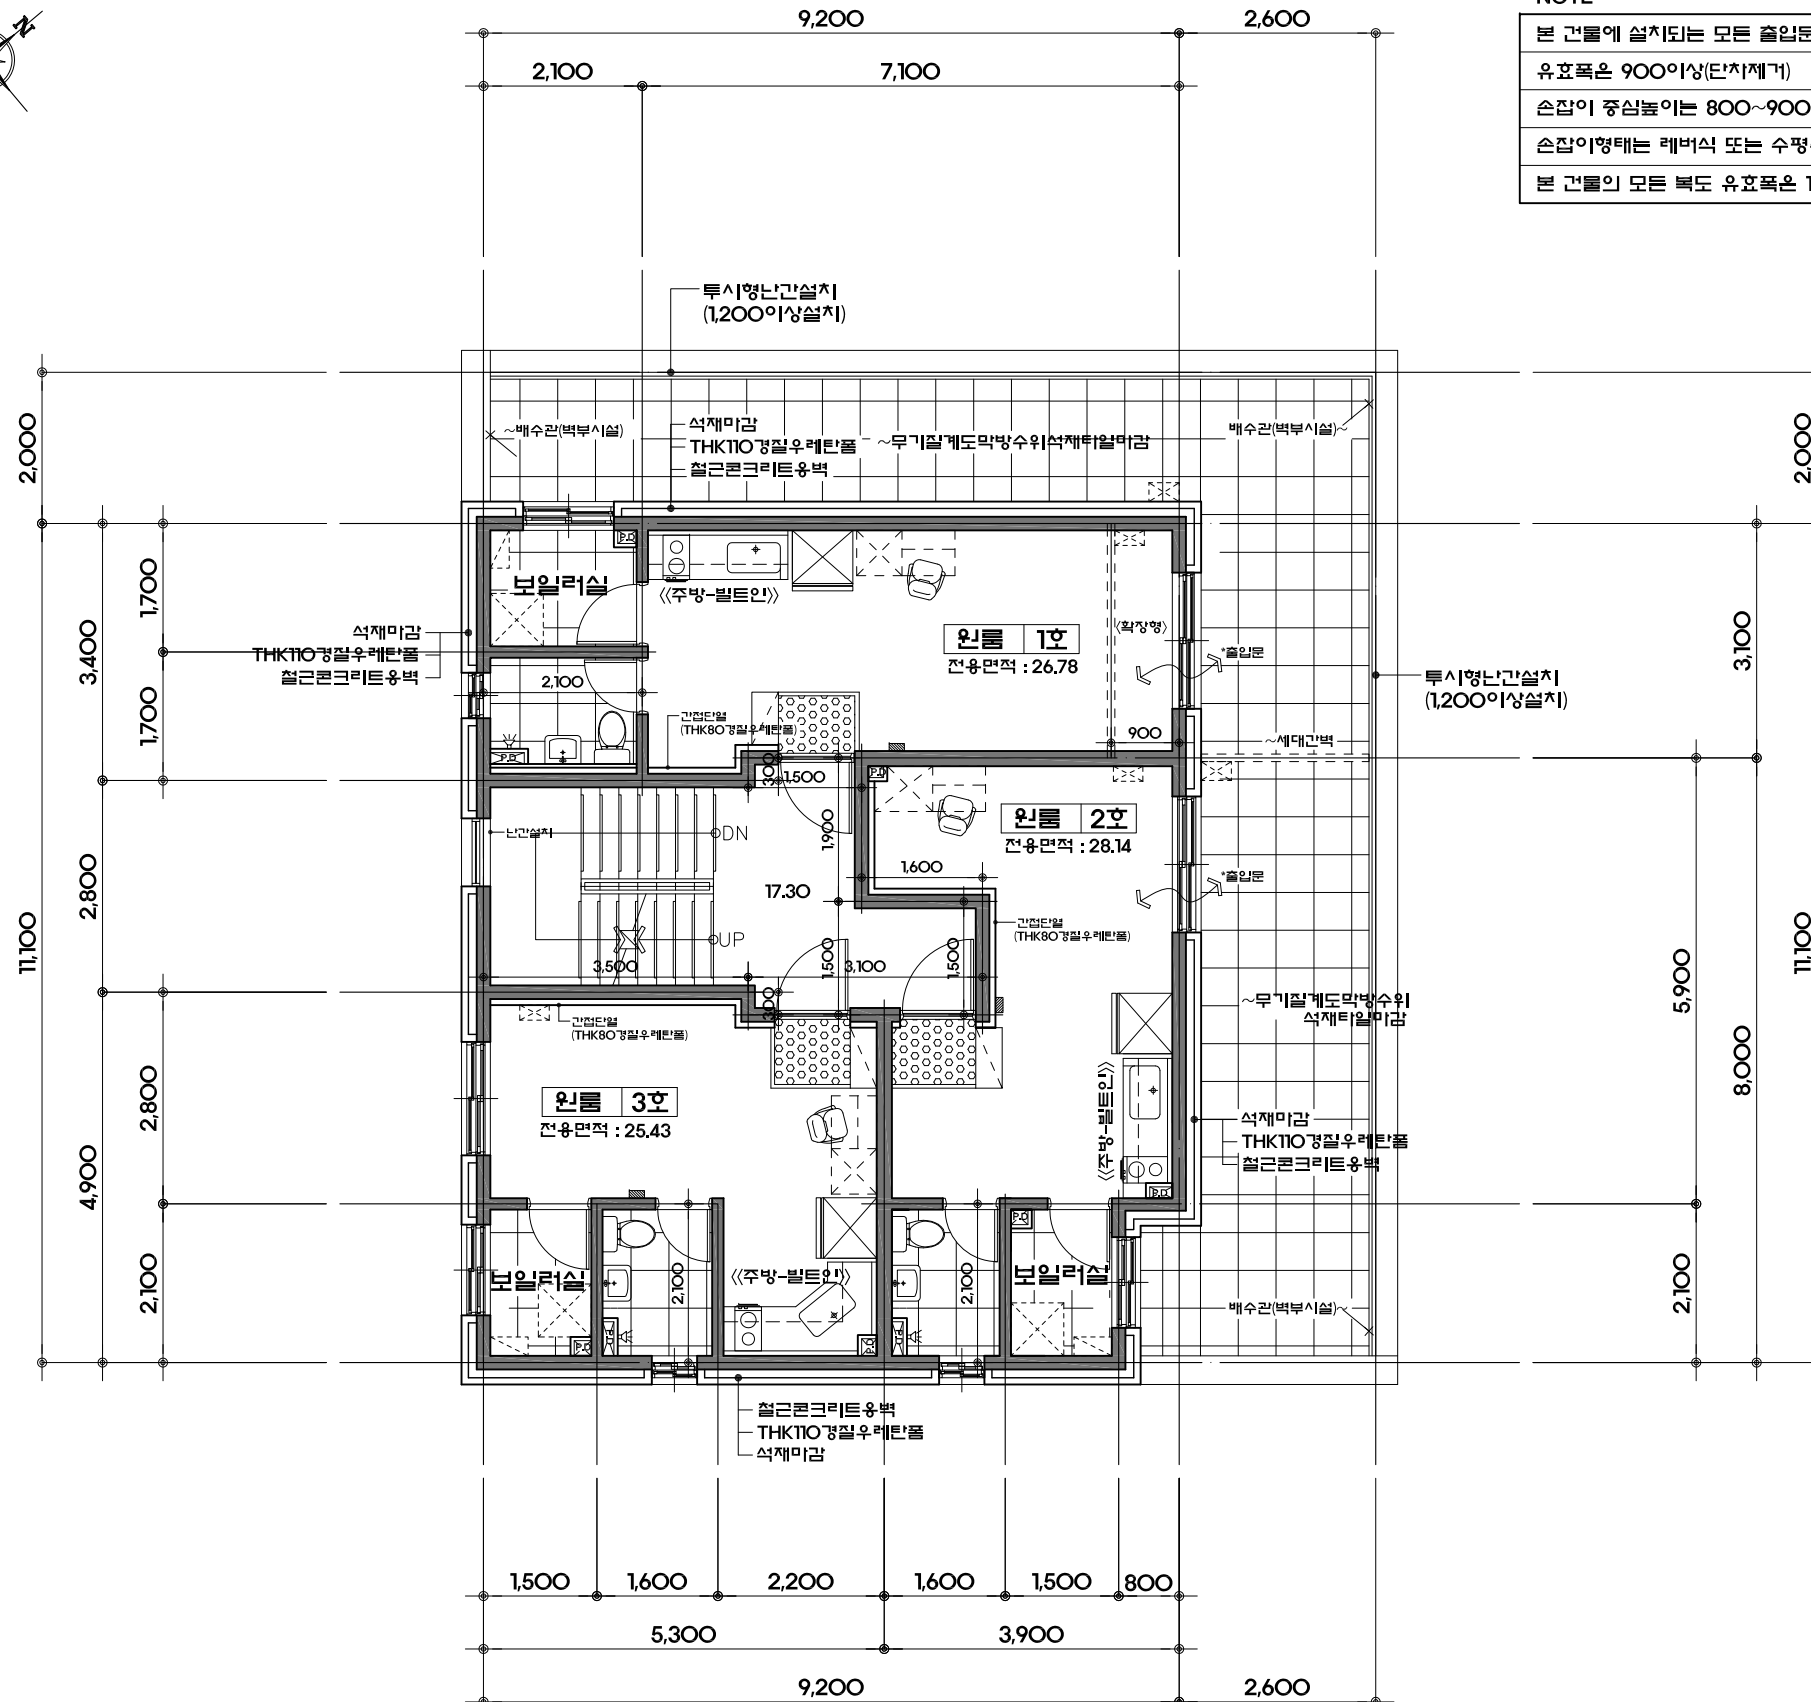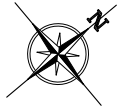


NOTE

본 건물에 설치되는 모든 출입문(내,외부포함)
유효폭은 900이상(단차제거)
손잡이 중심높이는 800~900
손잡이형태는 레버식 또는 수평수직 비행식
본 건물의 모든 복도 유효폭은 1200이상(단차제거)

주 기


건 조	1 (외부)	주차장내 CCTV,쓰레기분리수거,자전거보관대 설치					
		우편함 설치 (세대전용, 공용, 반송용, 폐건전지함 구분 설치)					
		테라스 창호 PL이중창 설치					
		세대 테라스 설치시 세대간 분리벽 계획					
		세대 발코니 설치시 차양시설 설치					
	2 (계단실)	세대 현관문 도어체크 설치					
		계단참의 현관과 계단 이격거리 (최소600mm이상)					
	3 (내부)	세대내 욕실, 휴지걸이 매립형 설치					
	4 (시공)	콘크리트 폴타이 제거 후 마감공사 시공 (방수, 단열재 시공 등)					
욕실 & 다용도실 스위치 : 문 열리는 방향으로 시공 주차장 차량 진출입구간 무소음트랜치 시공							
5 (미감)	-직접외기(외벽)에 면한 실내벽면 단열재 [아이소핑크(10mm) + 석고보드 마감도면 표기]						
	-간접외기(계단실,복도)에 면한 실내벽면 단열재 일반내부 : [경질우레탄폼(80mm) + 석고보드 마감도면 표기] 욕실,다용도실 : [단열재판넬(80mm) 시공]						
	*기타 실내 벽면 시멘트 미장 마감						
구 조	1	철근 : $f_y=400\text{MPa}$ (HD16이하), 500MPa (SHD19이상)					
		콘크리트 : $f_{ck}=24\text{Mpa}$					
	2	스라브두께 : 210mm (복배근)					
		외벽두께 : 180mm (복배근)					
		코어벽두께 : 180mm (복배근)					
		세대간벽두께 : 200mm (복배근) 내벽두께 : 150mm (복배근)					
전 기	1	-콘센트 설치 (바닥 마감선 기준)					
		[거실] 스탠드형 에어컨 : 350					
		[안방] 벽걸이형 에어컨 : 1900					
		[화장실] 양변기 원 : 900					
		[주방] 조리대 : 중앙 / 냉장고 : 350 / 후드 : 2100					
	2	-비디오폰(VP),보일러온도조절기(B), 스위치(S), 전열교환기스위치(E) (거실이트홀 위치)					
		<table><tr><td colspan="3">VP</td></tr><tr><td>S</td><td>E</td><td>B</td></tr></table>	VP			S	E
	VP						
S	E	B					
3	에어컨 실외기	<table><tr><td colspan="3">-----</td></tr></table>	-----				

냉매, 배수관 (배수관수직매립)	<table><tr><td colspan="3">X</td></tr></table>	X					
X							
비 고		* 세대현관문 ## 규격"를"포함 : 1000X2200 * 반드시 가열대위에도 선반 설치할 것. * 청년주택(빌트인) : 냉장고,벽걸이에어컨,세탁기,블랙이장,책상					

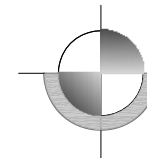


4층 평면도

scale:1/100



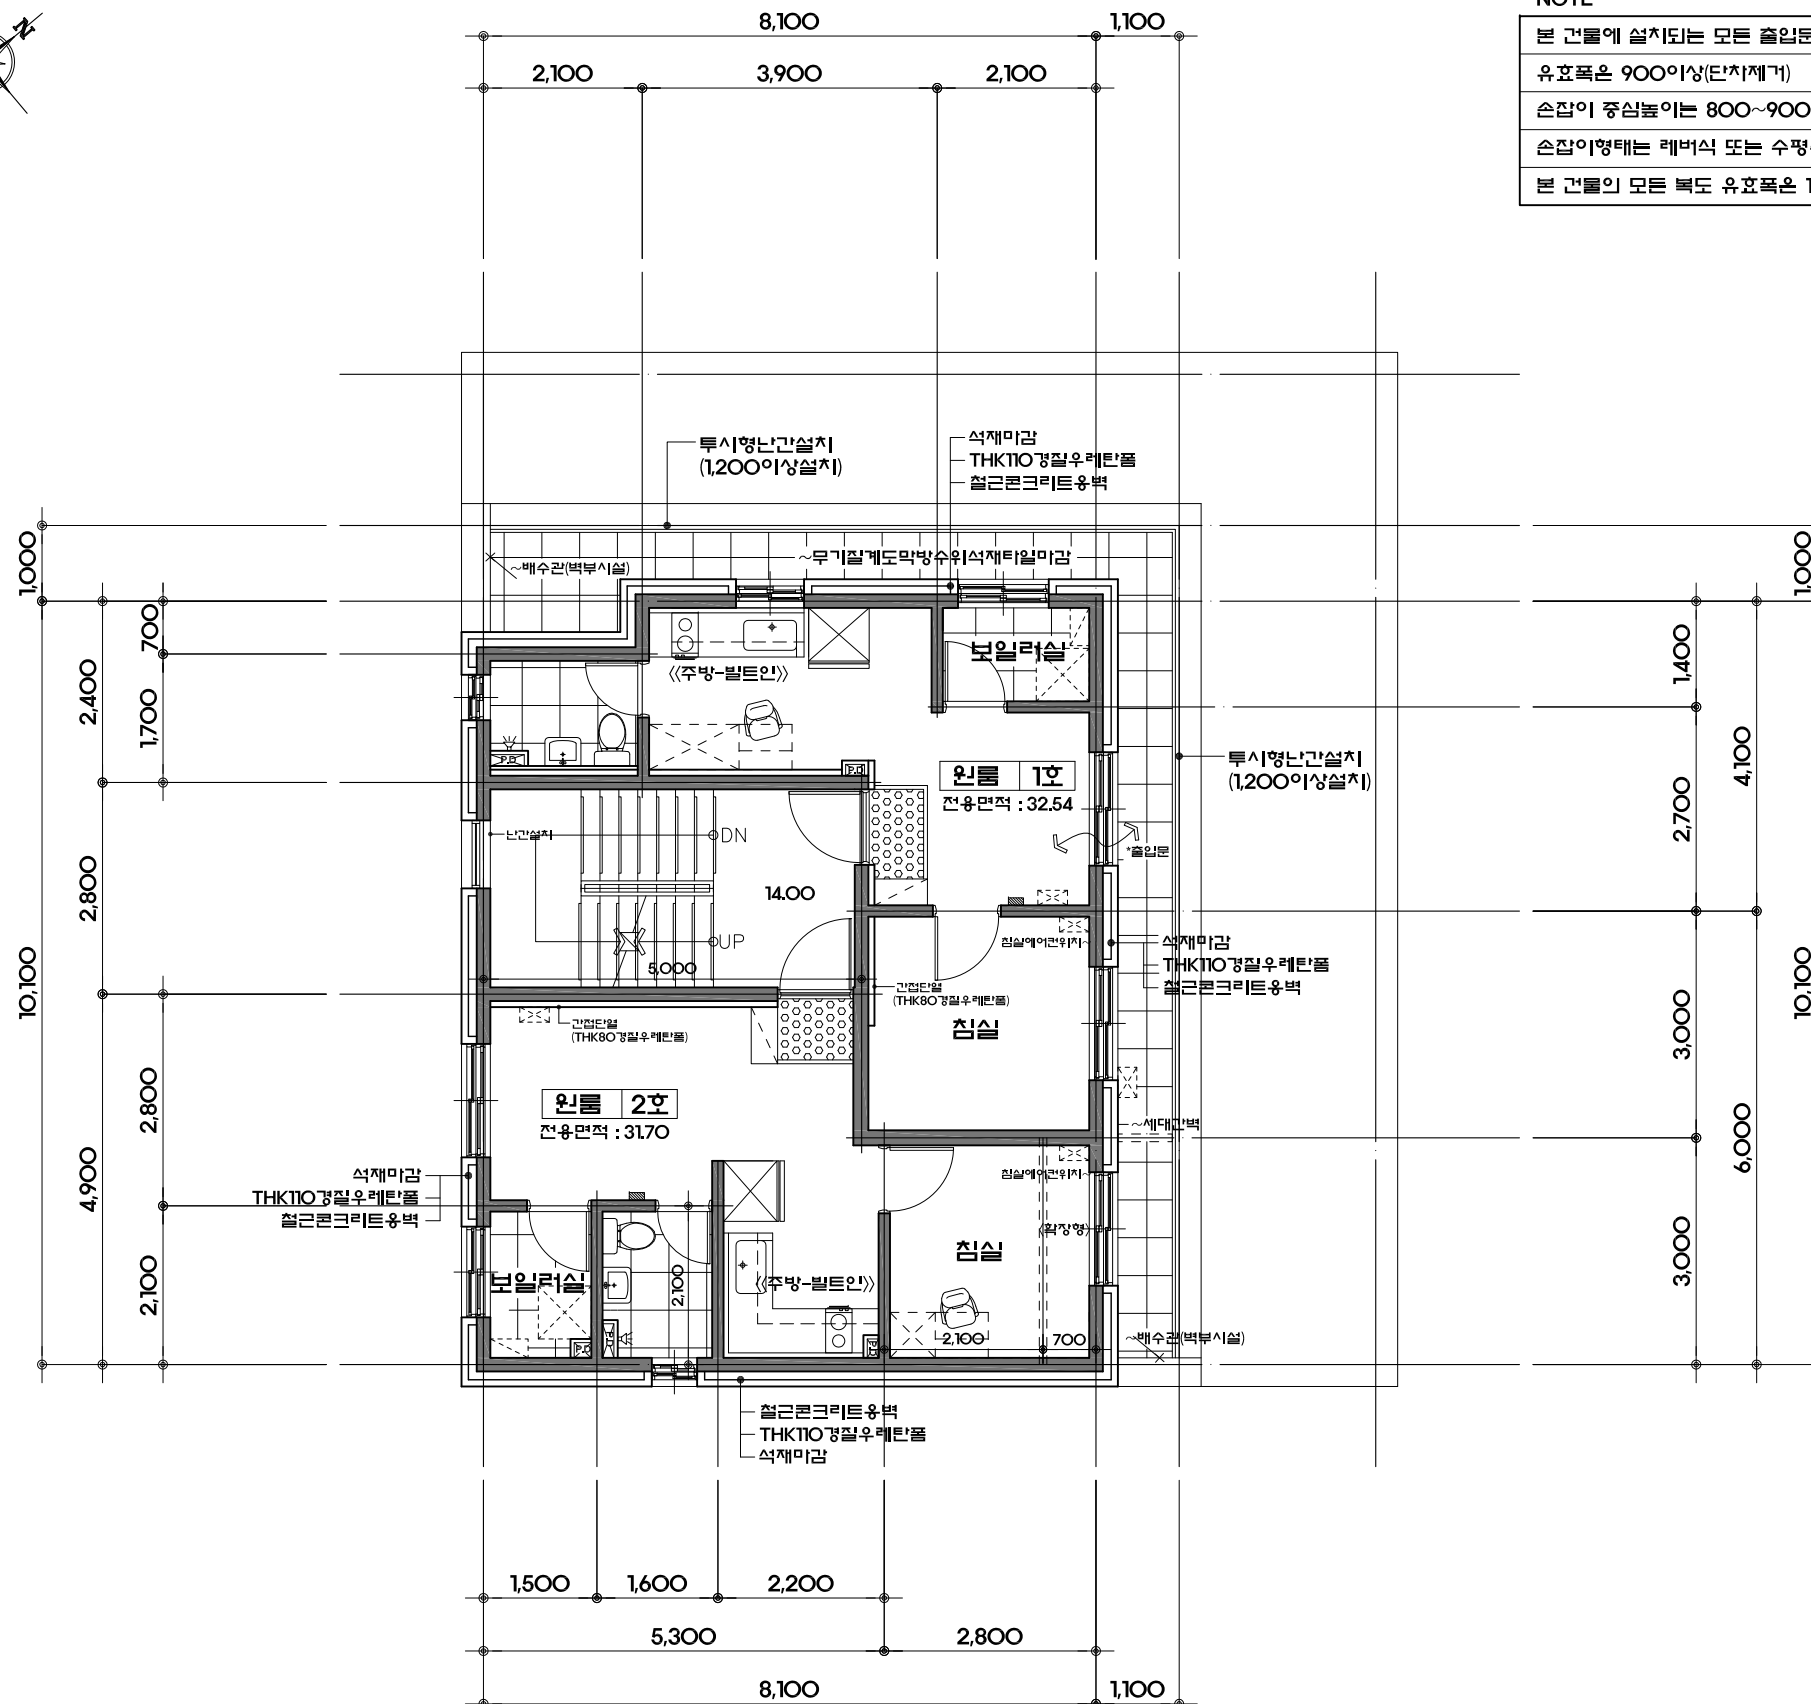


본 건물에 설치되는 모든 출입문(내,외부포함)
유효폭은 900이상(단차제거)
손잡이 중심높이는 800~900
손잡이형태는 레버식 또는 수평수직 바형식
본 건물의 모든 복도 유효폭은 1200이상(단차제거)



주 기		
건 축	1 (외부)	주차장내 CCTV,쓰레기분리수거,자전거보관대 설치
		우편함 설치 (세대전용, 공용, 반송용, 폐건전지함 구분 설치)
		테라스 창호 PL이중창 설치
		세대 테라스 설치시 세대간 분리벽 계획
		세대 발코니 설치시 차양시설 설치
	2 (계단실)	세대 현관문 도어체크 설치
	3 (내부)	계단참의 현관과 계단 이격거리 (최소600mm이상)
		세대내 욕실, 휴지걸이 매립형 설치
	4 (시공)	콘크리트 폴타이 제거 후 마감공사 시공 (방수, 단열재 시공 등)
		욕실 & 다용도실 스위치 : 문 열리는 방향으로 시공
		주차장 차량 진출입구간 무소울트랜치 시공
	5 (미감)	-직접외기(외벽)에 면한 실내벽면 단열재
		[아이소핑크(10mm) + 석고보드 마감도면 표기]
		-간접외기(계단실,복도)에 면한 실내벽면 단열재
		일반내부 : [경질우레탄폼(80mm) + 석고보드 마감도면 표기]
		욕실,다용도실 : [단열재판넬(80mm) 시공]
구 조	1	철근 : fy=400MPa(HD16이하), 500MPa(SHD19이상)
		콘크리트 : fck=24Mpa
	2	스라브두께 : 210mm (복배근)
		외벽두께 : 180mm (복배근)
		코어벽두께 : 180mm (복배근)
		세대간벽두께 : 200mm (복배근)
		내벽두께 : 150mm (복배근)
전 기	1	-콘센트 설치 (바닥 마감선 기준)
		[거실] 스탠드형 에어컨 : 350
		[안방] 벽걸이형 에어컨 : 1900
		[화장실] 양변기 옆 : 900
		[주방] 조리대 : 중앙 / 냉장고 : 350 / 후드 : 2100
	2	-비디오폰(VP),보일러온도조절기(B), 스위치(S), 전열교환기스위치(E) (거실 아트홀 위치)
	3	에어컨 실외기
		냉매, 배수관 (배수관수직매립)
비 고		
	* 세대현관문 ## 규격"를"포함 : 1000X2200	
	* 반드시 기월대뒤에도 선반 설치할 것.	
	* 청년주택(빌트인) : 냉장고,벽걸이에전,세탁기,물박이장,책상	

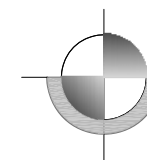

scale:1/100

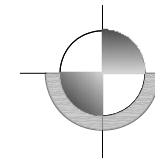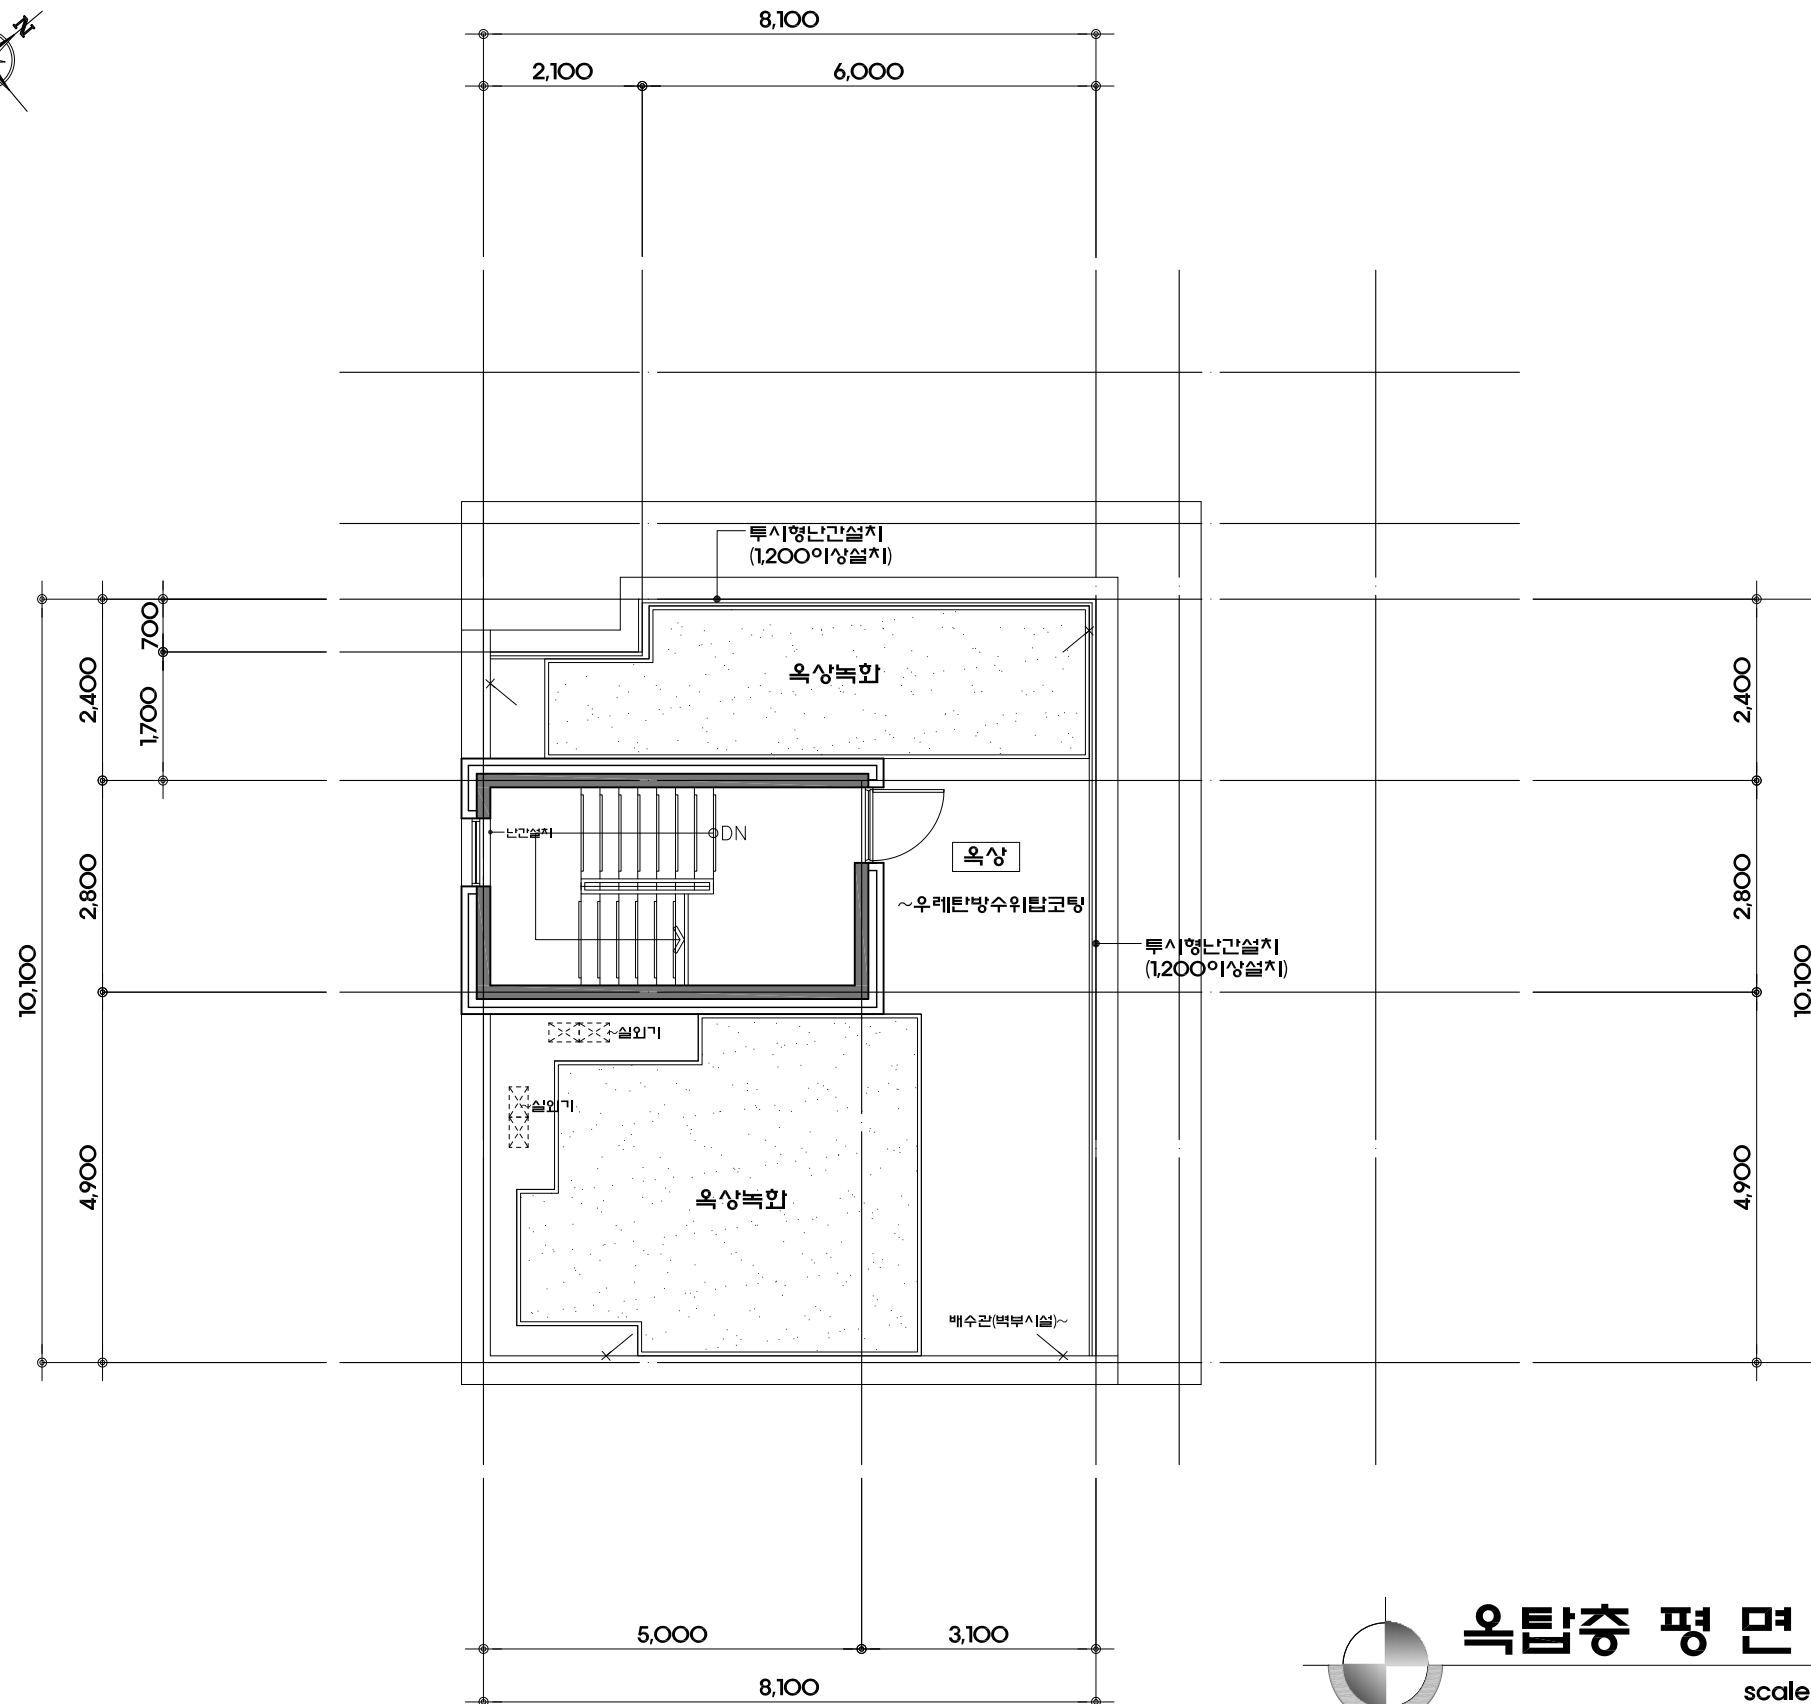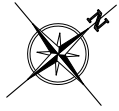


옥탑층 평면도
scale:1/100

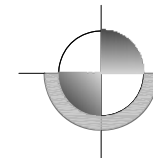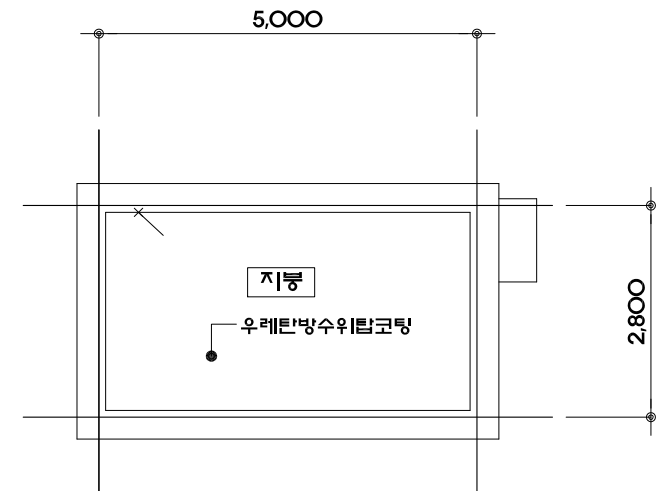

옥탑지붕 평면도
scale:1/100

창호색상	PVC(검정색)
우수배관	정면설치지양
지정석재1	미천석
지정석재2	환강석

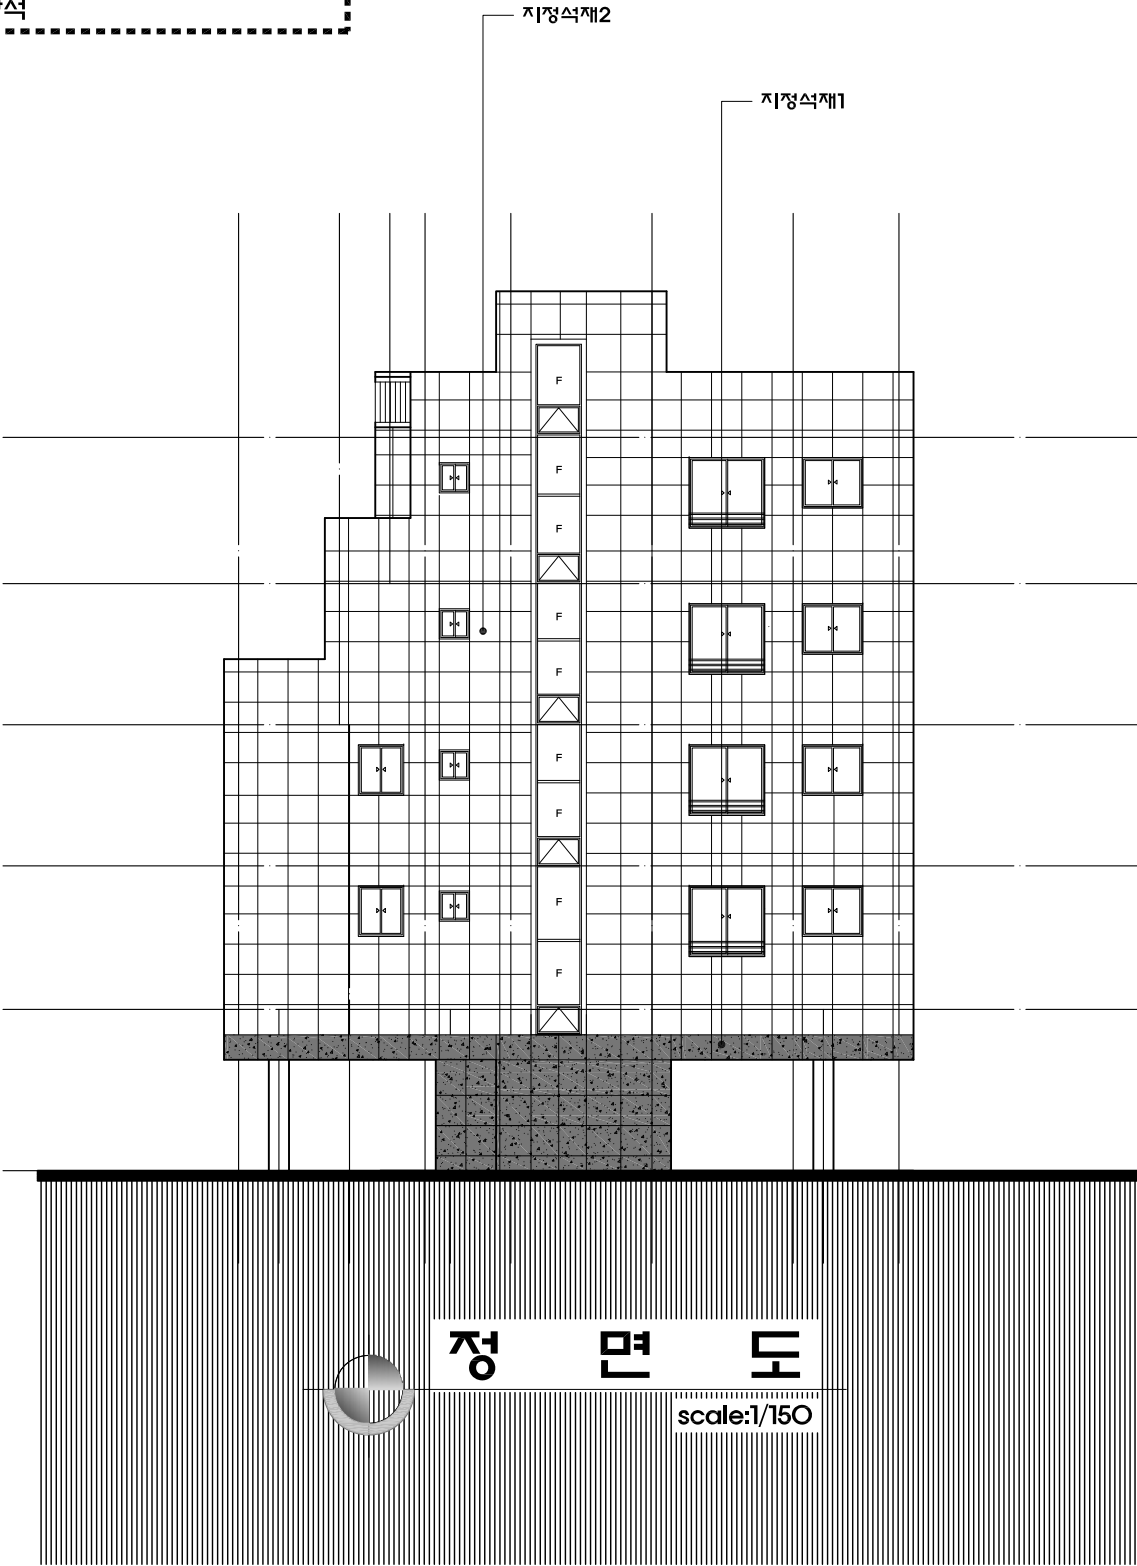

옥탑1층스리브선


5층스리브선

4층스리브선



3층스리브선


2층스리브선

1층스리브선

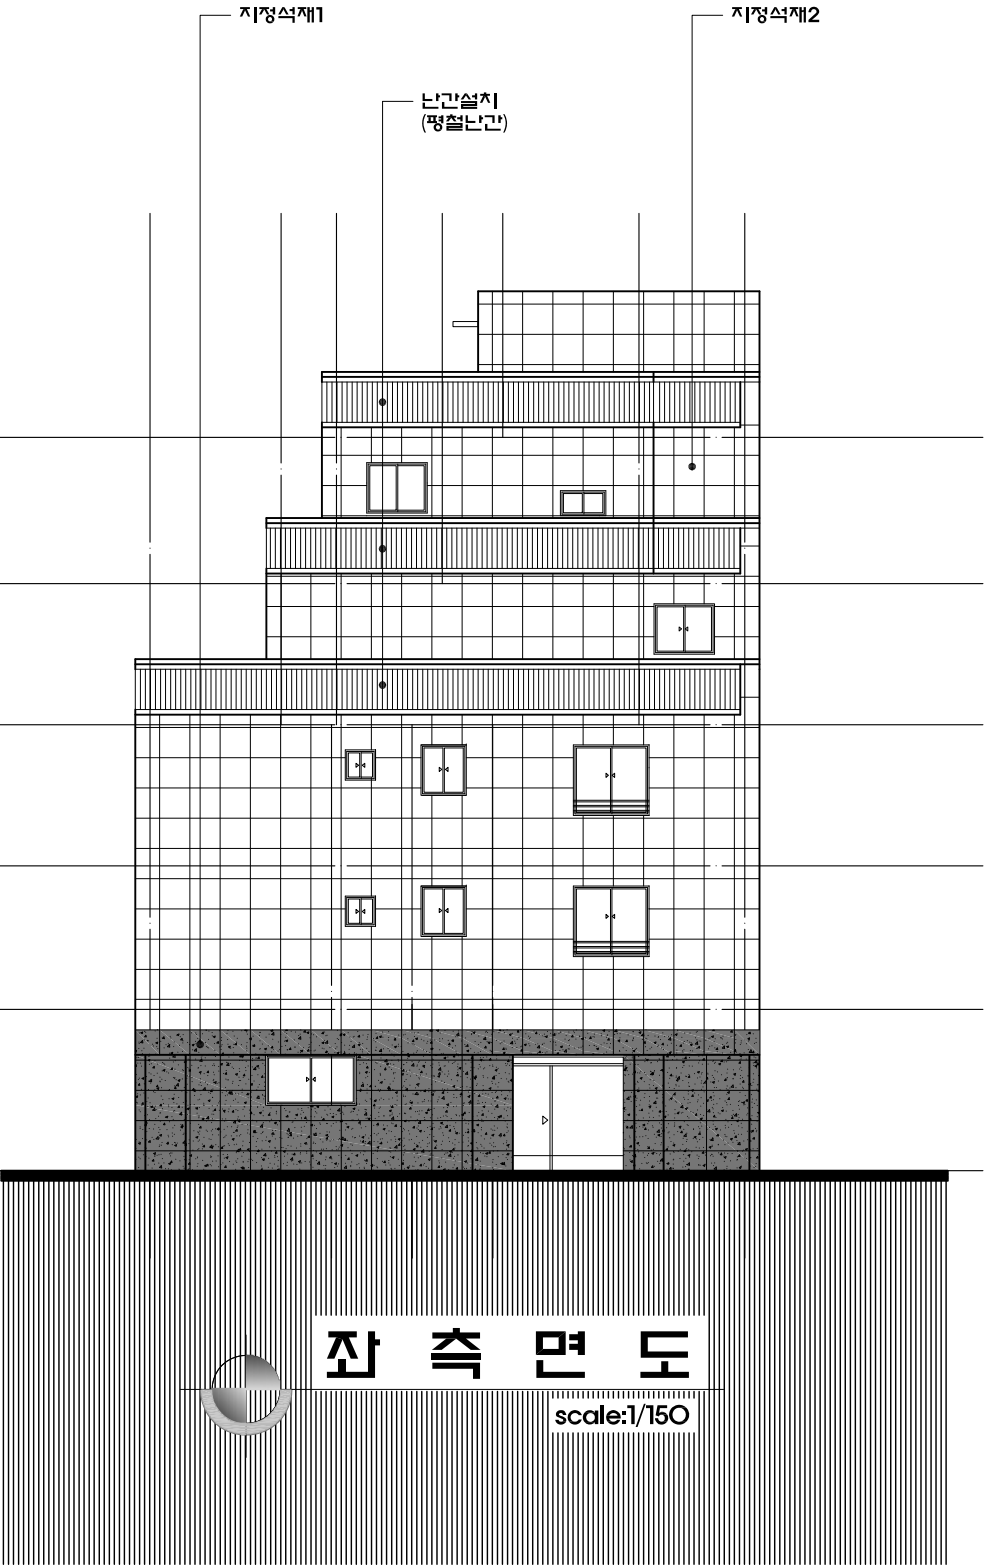

창호색상	PVC(검정색)
우수배관	정면설치지양
지정석재1	미천석
지정석재2	환강석

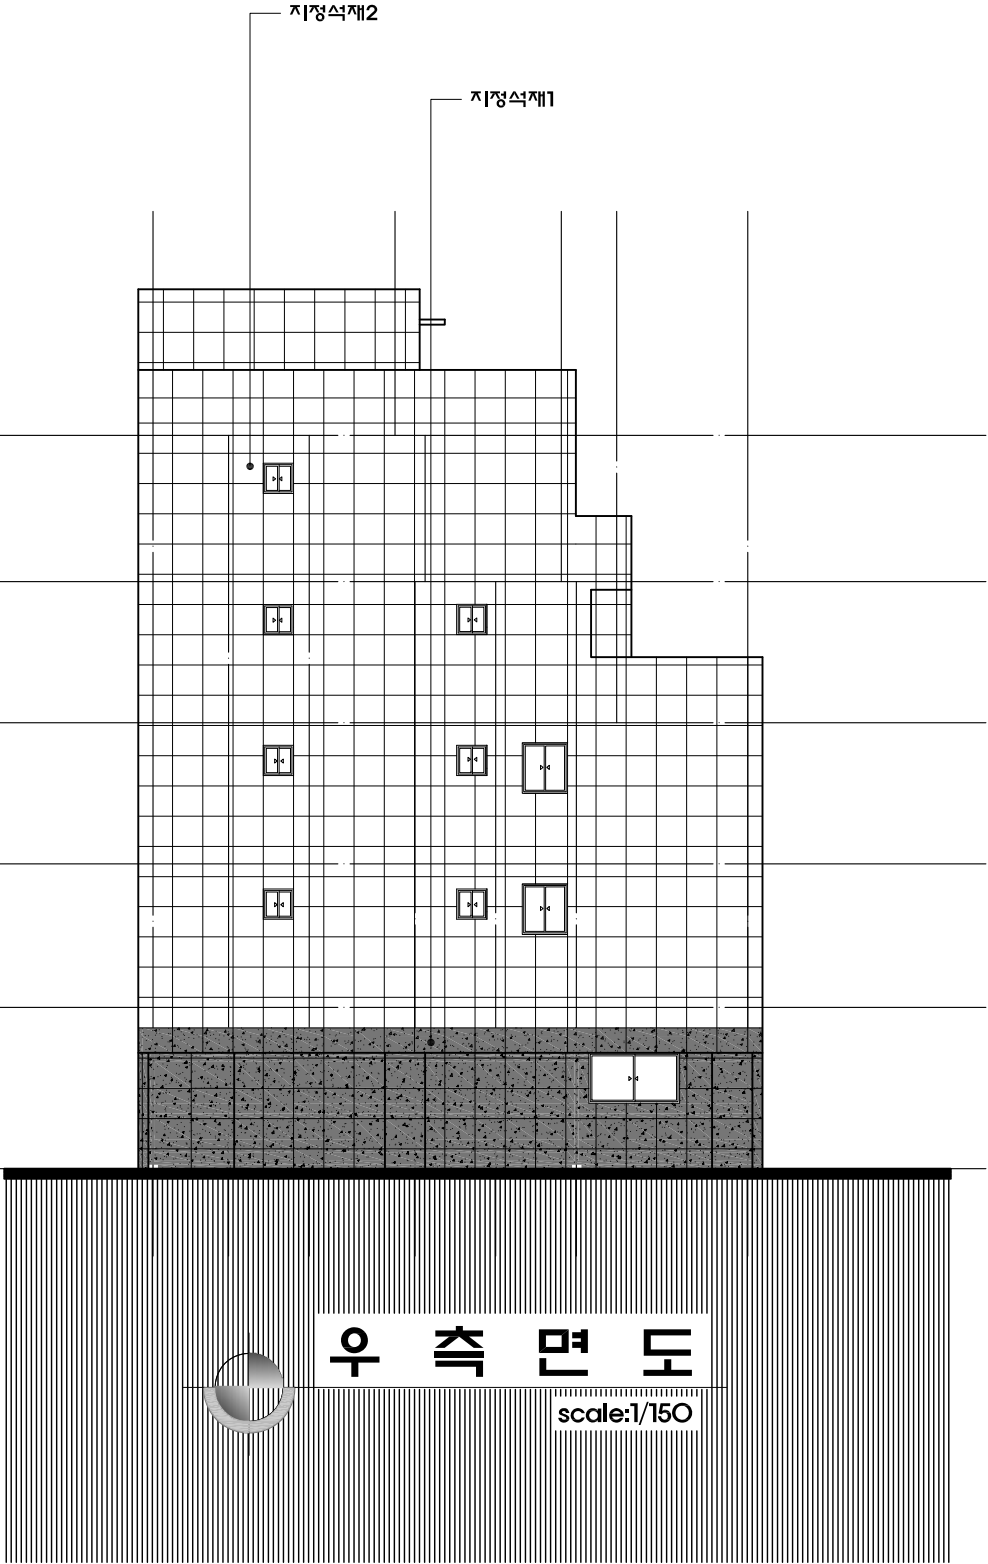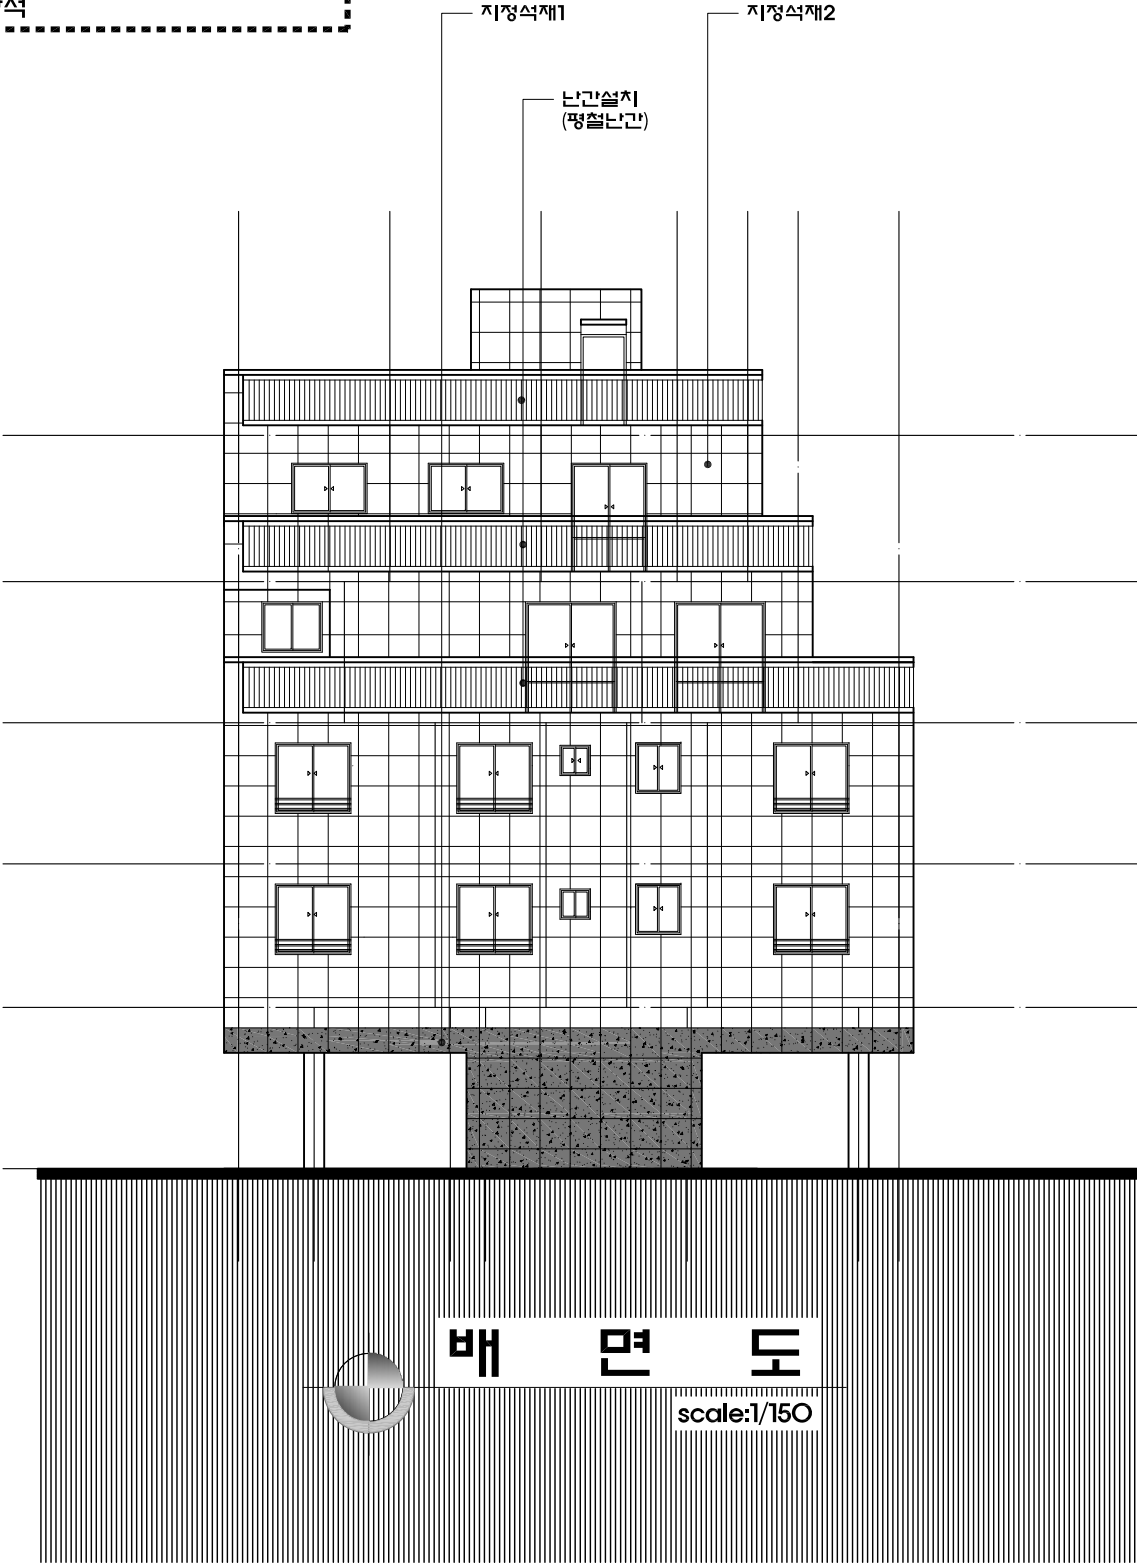

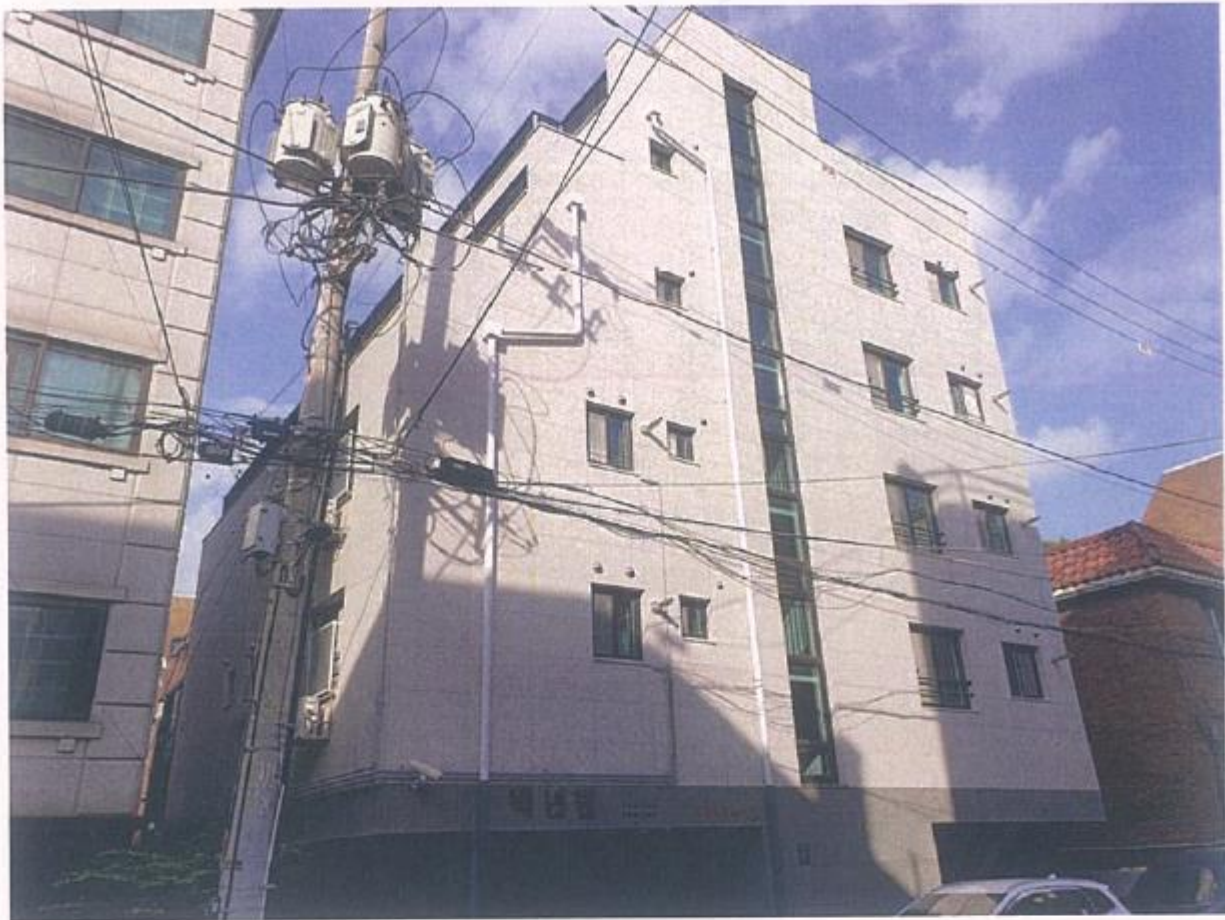

【본건전경】



【주위환경】