


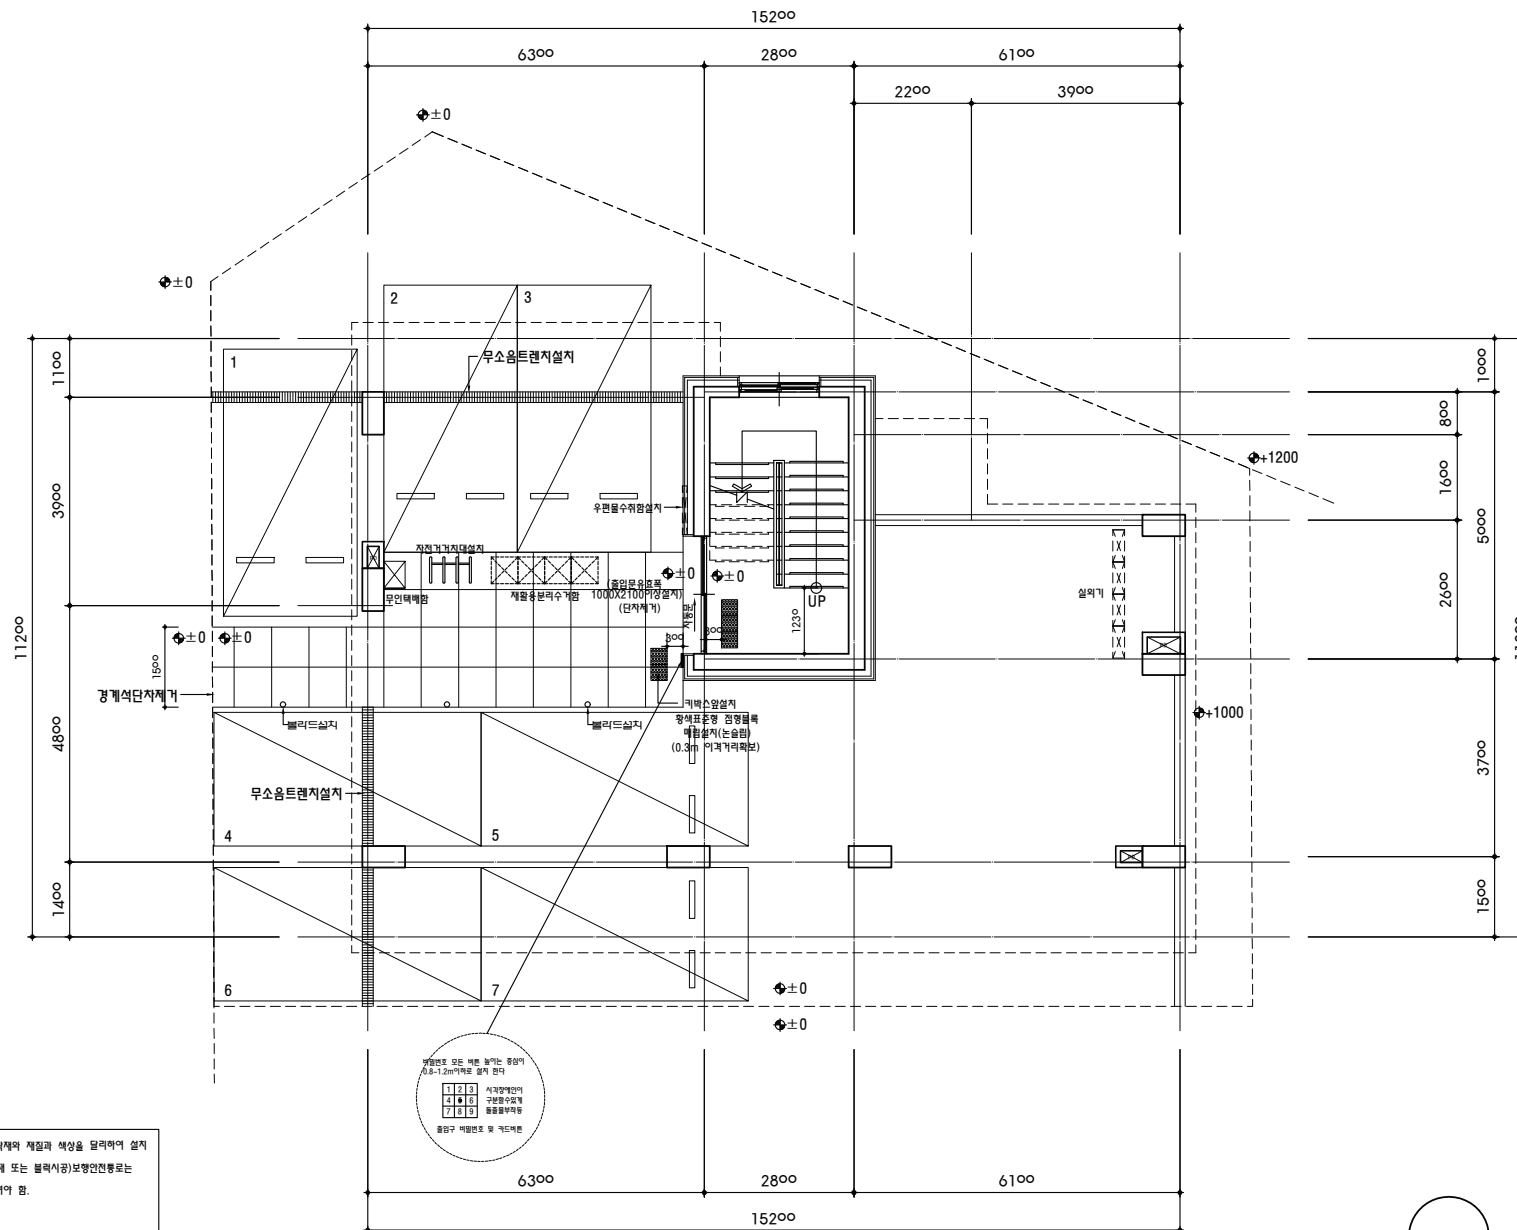


1. 접근도(보행환경정보)는 주상경 및 지도의 바닥재와 재질과 색상을 일목여어 설치 (책판, 우레탄, 플라스틱, 콘크리트 시공성) / 색채 또는 불리시공)보행환경정보는 마끄라지지 어서는 재질로 정한한계 마끄라지지 어 함.
2. 모든 잠자블록은 황색표준형색표현으로 설치
3. 건물에 설치되는 출입문(내·외부유동)유도선은 900이성(단자제거),손잡이 중심높이는 1000이성(단자제거)로 설치
4. 벽, 건물 외면 벽도 표본은 1200이성(단자제거)

건축	1 (외부)	주거주택단축CTV, 제품용분류수계, 직접기보관소설계
		수질환경평가(하천단상, 용출, 관측용, 저감장치연구보존설계)
	2 (개단)	세대 하역소 설치시 석자강 설계 계획
		세대 하역소 설치시 저장시설 설계
	3 (내부)	세대 단면은 도약크지 않도록 설계
		일단단면 단면과 점진 여가구역 (폭≤600mm이상)
4 (사공)	세대 내 속설 표지판설치 설계	
	콘크리트 바닥에 직각수 파손방지 시설(방수, 단열재 시공등)	
구조	1	육설 & 다용도설 수위계 : 완충벽는 방방향으로 시공
		주요장 건물틀구간 주소를 트랜스미션
	5 (마감)	국립 석자강 일대내의 단면
		국립 석자강(하천단상, 복도) 전한 실내배관은 단면
	2	(경로수리점30mm+속고비드 마경도표 포함)
		국립 석자강(하천단상, 복도) 전한 실내배관은 단면
		(경로수리점30mm+속고비드 마경도표 포함)
전 기	1	국립 석자강 일대내의 단면
		(경로수리점30mm+속고비드 마경도표 포함)
		국립 석자강 일대내의 단면
2	2	국립 석자강 일대내의 단면
		(경로수리점30mm+속고비드 마경도표 포함)
		(경로수리점30mm+속고비드 마경도표 포함)

SCALE 1/100

[illegible]

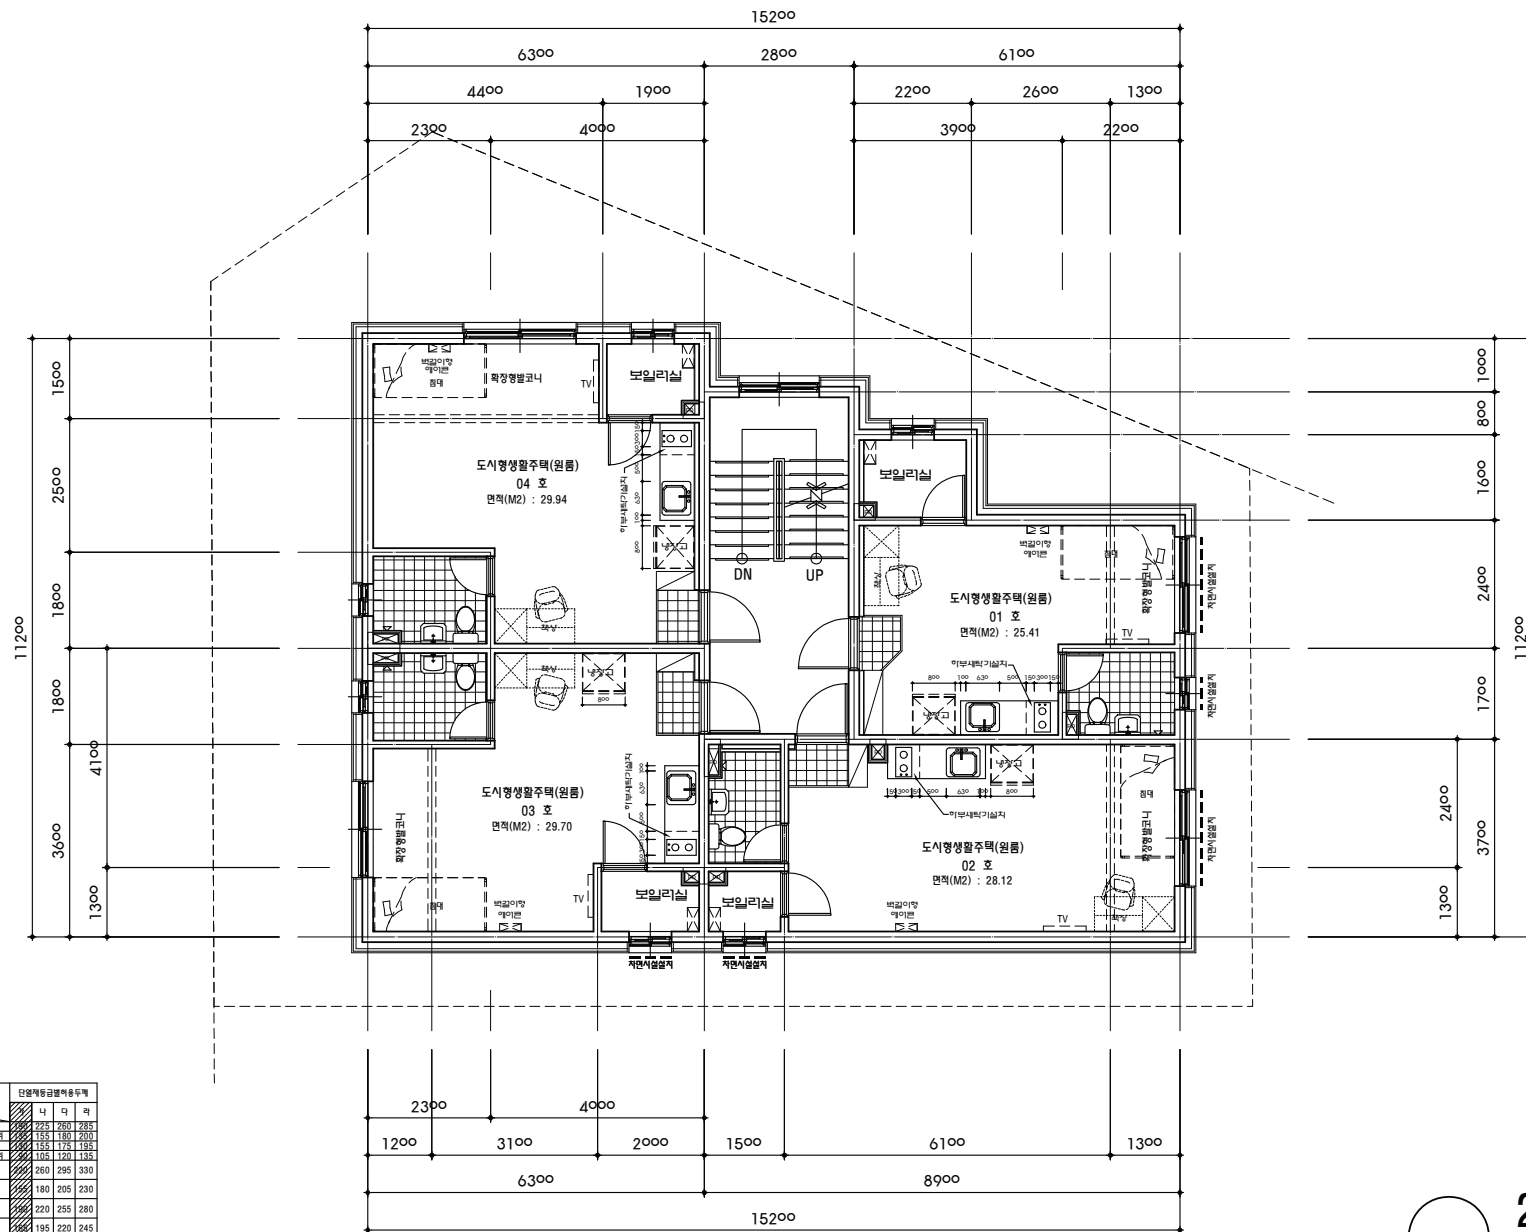

■ 단일주택의 두배·(중부2지역)		단일주택의 층급		단일주택층급당면적당용량			
건축물의 부위				니 다 라 리			
기실비 바닥	각각의 층급 면적에 한층의 경우	공공주택	225	250	275	300	
	각각의 층급 면적에 한층의 경우	일반주택	150	175	190	210	
최상층을 있는 기실비 연한 또는 지붕	각각의 층급 면적에 한층의 경우	공공주택	250	285	300	330	
	각각의 층급 면적에 한층의 경우	일반주택	180	205	220	240	
최상층을 없는 기실비 바닥	백리산면적의 경우	220	255	280	300		
	백리산면적의 아닌 경우	일반주택	195	225	240	260	
백리산면적의 연한 또는 지붕	백리산면적의 경우	250	275	300	330		
	백리산면적의 아닌 경우	일반주택	125	145	160	180	
백리산면적의 용기주택			30	35	40	50	

주 기			
건축	주구조체(BCCTV, 재충분류수거기, 자전·보존소설기) 우면관통벽(벽간연속층, 공동, 연송층, 벽간연접구분설기) 서대 벽두께 설계치 평단면 분석에 결과 서대 벽두께 설계치 차장시설 설계		
	서대 천간의 도약크기 및 스톱트 설계 천단폭과 천단개 절단 각지각 (최소600mm이상)		
	서대 내 옥실 유지관리 설계		
	콘크리트 골짜기 제방 부공적 사강(양사,요제방 사강등)		
	옥실 & 다출동 수취기 : 분할되는 방향으로 사강 주차장 단합물상 구조물 트랜스미서용		
	절단 각지각 단합물 상면면역은 단합물 (각지소망크기10mm+식고보드 적용도면 표기)		
	경첩기(경첩설,비드) 단합물 상면면역은 단합물 (경첩소망크기80mm+식고보드 적용도면 표기)		
	각지 상면면역은 시멘트 타일 마감		
	1층 계단부분 코너보호모형설계		
	1층 계단부분 코너보호모형설계		
구조	1 콘크리트 : fck=24MPa 원근 : fy=400Mpa		
	2 서대 벽두께 : 180mm(벽두께) 벽두께 : 200mm(벽두께) 코어 벽두께 : 200mm(벽두께) 스택의 두께 : 210mm(벽두께)		
	전기	- 콘센트 설치 (벽과 직결된 지점) 벽걸이형 에어컨 - H1900/가열시스템 - H350 (옥실) 방화기 설 - H300 (주방) 조리기구형/ 방화기-H3500/ 후드-H2100	
	2 - 비디오폰 (VP) - 보일러실도조명기 (B) - 스위치 (S) - 전선교환수취기 (E)	기술 이름 위치	VP S E I
공동주택 바닥정착을 위한구조기준			
T=10 여야소크			
 배반계회트막 T=40 지멘트몰입(1.3) T=40 경첩기보콘크리트 T=0.06 PE플러그1건 T=30 완충재 T=210 콘크리트를레브			
옥실 건립면 부분상세도			
 콘크리트층 T=80 단합물(중공열완함) (원단도움 : 0.020) -0.5시멘트몰입각 타일알림			
석기 건립면 면			
기술 내부		옥실 내부	보일러실 내부
식고보드		0.58타일배설막	C/C보드/배설



2-4층 평면도

SCALE


1/100



다원 건축사사무소

서울시 송파구 가락동 99-3 제일오피스텔 513호
Tel:02-449-9106 Fax:02-449-9107 E-mail:kyun81@daum.net

[illegible]

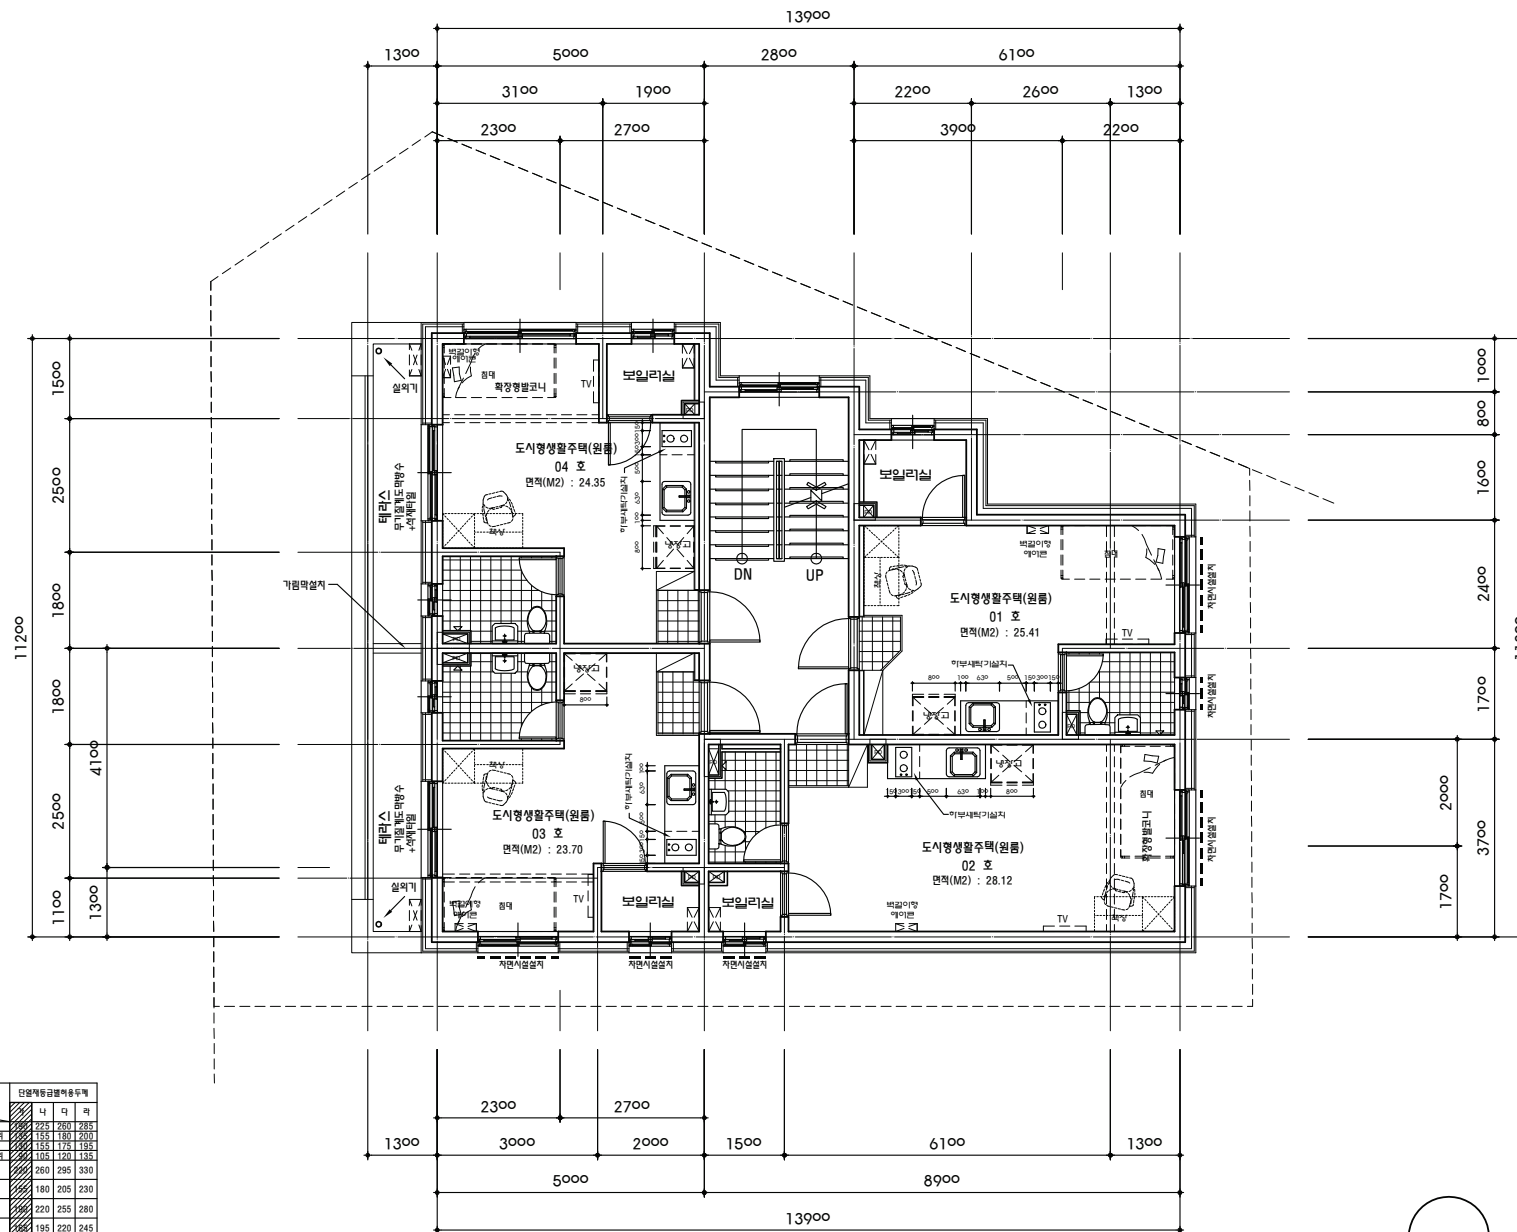

건축물의 부위	단일주택의 층급	단일주택층급당면적당용량			
		니	다	라	리
기밀비 바닥	각각의 층급 면적에 한층의 경우	공공용량	225	250	275
	각각의 층급 면적에 한층의 경우	민간용량	150	175	195
최상층을 있는 기밀비 천한 또는 지붕	각각의 층급 면적에 한층의 경우	공공용량	250	285	300
	각각의 층급 면적에 한층의 경우	민간용량	180	205	220
최상층을 없는 기밀비 바닥	각각의 층급 면적에 한층의 경우	민간용량	220	255	280
	각각의 층급 면적에 한층의 경우	민간용량	195	225	245
최상층을 있는 기밀비 천한 또는 지붕	각각의 층급 면적에 한층의 경우	민간용량	150	175	185
	각각의 층급 면적에 한층의 경우	민간용량	125	145	160
최상층을 있는 기밀비 천한 또는 지붕	각각의 층급 면적에 한층의 경우	민간용량	150	175	185
최상층을 있는 기밀비 천한 또는 지붕	각각의 층급 면적에 한층의 경우	민간용량	125	145	160




5층 평면도

SCALE 1/100

주 기	
건축	주거주택NCTV, 생활문화수거차, 직접거점보조시설기 주원설비(가/배관용,공용,냉난방,배관기/배관설비기) 1 (외부) 상단 벽측소 설치기 상단벽 본체벽 절개 상단 벽측소 설치기 저장실벽 설치 2 (기단) 상단 원통문 도어까지 및 토트 벽측소 설치 3 (내부) 상단 내 측벽 후방구조물 설치 4 (시공) 콘크리트 블록기 벽단기 저장기 시공(경우요청시 시공함) 5 (마감) 측벽 & 다용도소 시공기: 콘크리트는 방형으로 시공 주거용 건물공간과 무소소 트랜스시공 측벽 벽기 벽단기 내부벽면은 단열벽 (기/배관용10mm+외/배관용 20mm) 경량벽(기/배관,벽단) 벽단 내부벽면은 단열벽 (경량벽10mm+외/배관용 20mm) 각각 내부벽면은 시멘트 마감벽 1층 거점용 콘크리트보조시설기
	구조
	1
	2
	3
	4
	5
	6
	7
	8
전기	1
	2
	3
	4
	5
	6
	7
	8
	9
	10
공통주택 벽단기용 직접거점보조시설	
T=10 여야소공크 벽단기벽기/벽단기 T=40 시멘트블록(1:3) T=40 경량기/벽단기 T=0.06 P.블록1기 T=30 단열벽 T=210 콘크리트슬래브	
측벽 건물단기 부분상세도	
콘크리트블록벽 T=40 단열벽(경량유기단열) (열전도율: 0.020) 0.05시멘트블록벽 리얼벽	
벽기 건물단기 마감	
기/배관 측벽 보일러실 내부	
외/배관 0.05시멘트블록벽 0.05시멘트블록벽	

 다원 건축사사무소 서울시 송파구 가락동 99-3 제일오피스텔 513호 Tel:02-449-9106 Fax:02-449-9107 E-mail:kyun81@daum.net		REV	DATE	DESCRIPTION	BY	BY	APP	PROJECT TITLE	APPROVED		DRAWING TITLE	5층 평면도	DRAWING NO.
		△						서울특별시 강남구 도곡동 547-11	CHECKED 1		SCALE	1/100	A - 26
		△					ENGINEER						
		△											

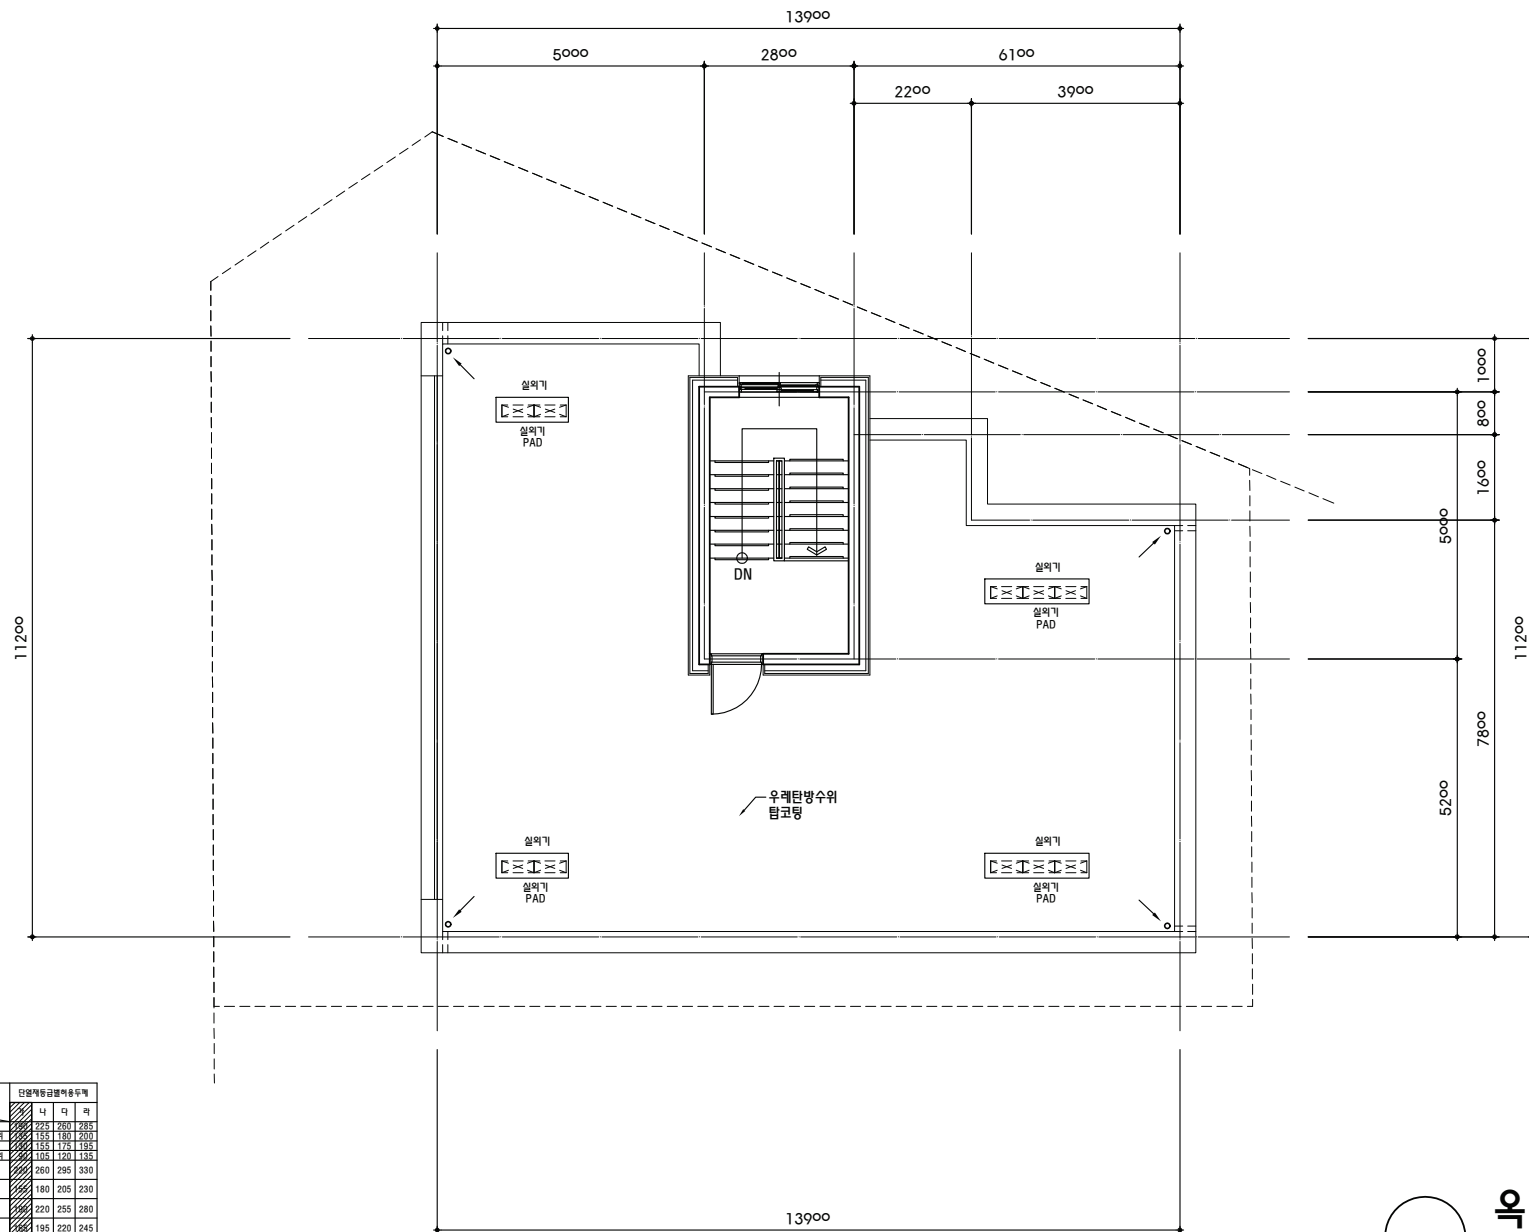


건축물의 부위	단열재의 등급	단열계수(열전달계수)두께		
		단	열	두께
기실의 바닥	외벽과 직접 접촉하는 경우	외벽단열	225	280
	외벽과 간접 접촉하는 경우	외벽단열	150	180
화장실용 또는 '기실의 안방' 또는 '침방'	외벽과 직접 접촉하는 경우	외벽단열	135	175
	외벽과 간접 접촉하는 경우	외벽단열	280	280
화장실용 또는 '기실의 바닥'	외벽과 직접 접촉하는 경우	외벽단열	180	205
	외벽과 간접 접촉하는 경우	외벽단열	220	255
화장실용 또는 '기실의 벽'	외벽과 직접 접촉하는 경우	외벽단열	195	225
	외벽과 간접 접촉하는 경우	외벽단열	150	175
벽단열방열 온도차	외벽과 직접 접촉하는 경우	외벽단열	125	145
	외벽과 간접 접촉하는 경우	외벽단열	35	45

[illegible]

옥탑1층 평면도

SCALE 1/100

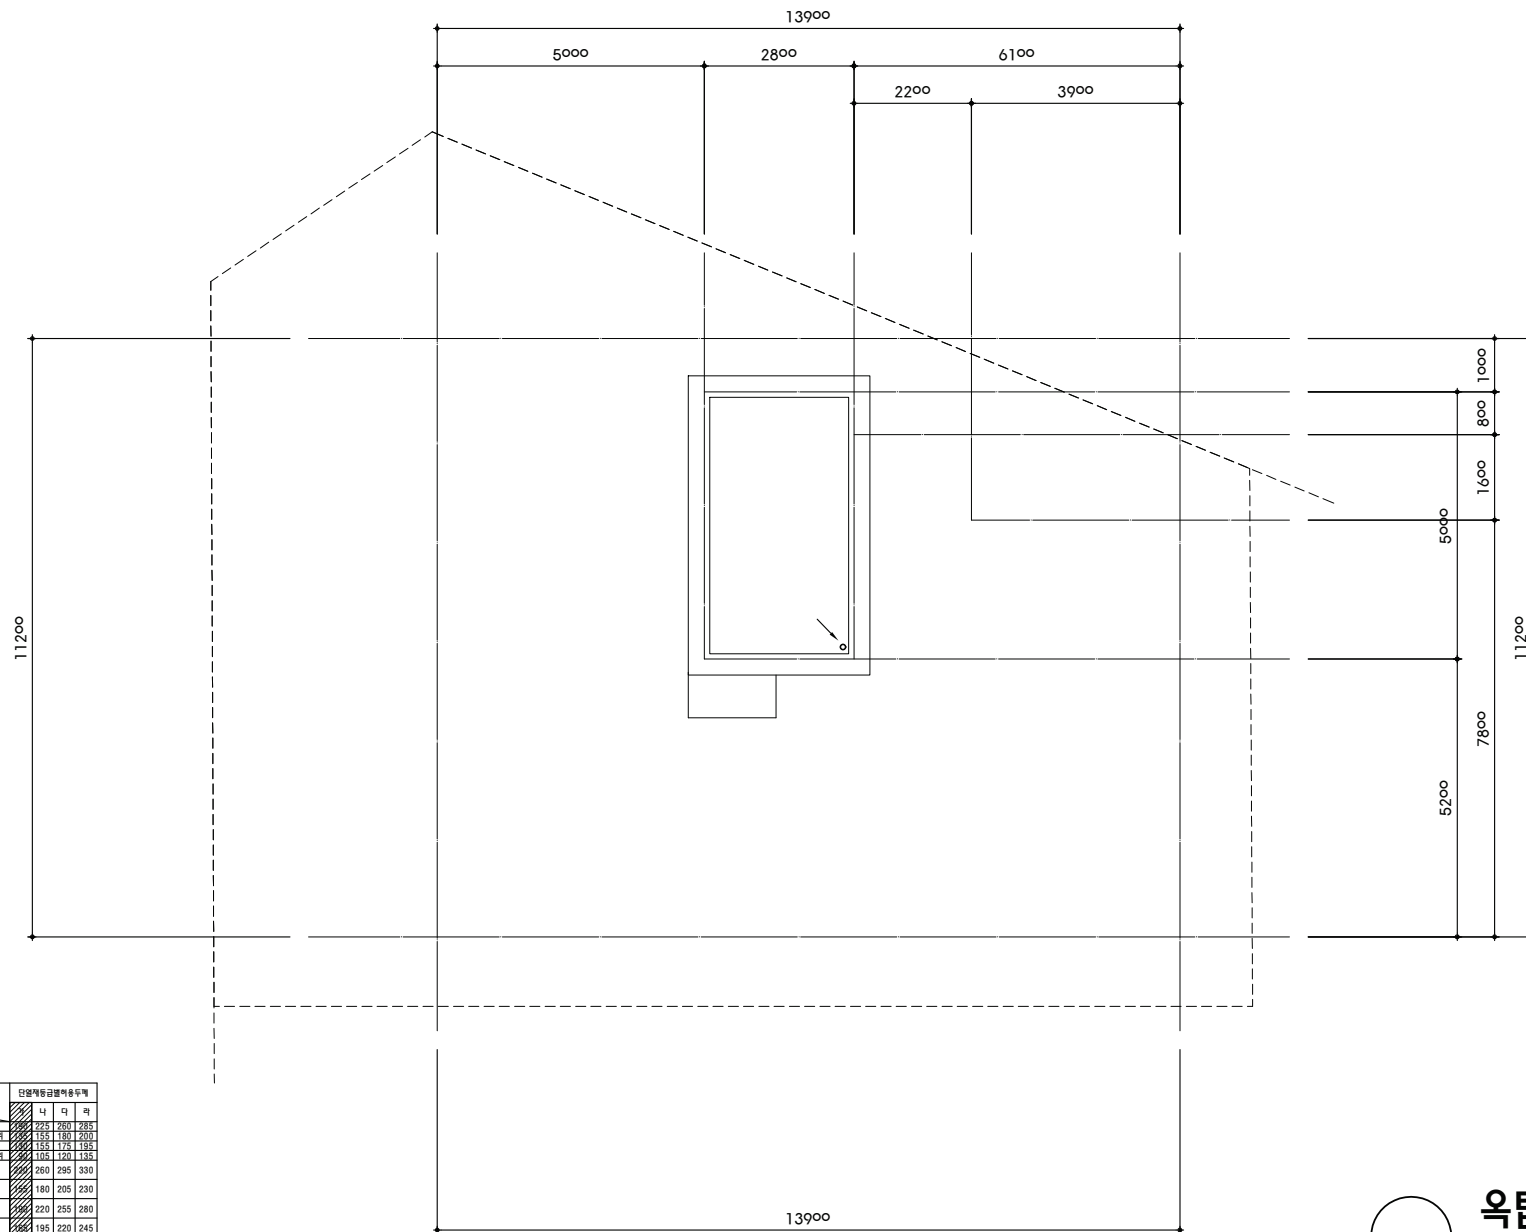

건축물의 부위	단일지역의 등급	단일지역등급비율의두배			
		비	리	다	라
기둥벽 바닥	기둥벽, 기둥, 천정면의 경우	225	285	285	285
	기둥벽, 기둥, 천정면의 경우	150	150	150	150
화장실은 있는 기둥벽 천하 또는 계층	기둥벽, 기둥, 천정면의 경우	285	285	285	285
	기둥벽, 기둥, 천정면의 경우	180	205	230	230
화장실은 없는 기둥벽 바닥	기둥벽, 기둥, 천정면의 경우	220	255	280	280
	기둥벽, 기둥, 천정면의 경우	195	225	245	245
바닥판은 종관방향	기둥벽, 기둥, 천정면의 경우	125	145	165	165
	기둥벽, 기둥, 천정면의 경우	35	45	50	50

주 기	
건축	주거형RCCTV, 자율운동복수기, 자연·자연소설기 유전합성기(자연운동, 공중, 연속층, 자연·자연구분설기) 서대 특산 설계사 설계도 분석 및 계획 서대 특산 설계사 자정시설 설계 서대 한천의 도야제 및 토트 시설 설계 경관계획 한천과 현대 건축가 (최소600mm²)
	서대 내 옥실 유지관리 설계
	콘크리트 블록에 제방 부속공사 시공(영양, 보양) 시공용 옥실 & 다목적 수위기 : 분할되는 방향으로 사용 주요장 건물 내부 구조물 특성조사용
	계단 석벽기 단면 설계비율을 단면적 (약기소량310mm×시고보드 크기인 표기) 강점기(계단식, 계단) 단면 설계비율을 단면적 (강점기소량80mm×시고보드 크기인 표기) 계단 설계비율에 시멘트 타일사용 1층 계단부분 코너보호장치
	구조
구조	1 콘크리트 : fck=24MPa 철근 : fy=400Mpa 2 서대 벽두께 : 180mm(벽두께) 계단 벽두께 : 200mm(벽두께) 코어 벽두께 : 200mm(벽두께) 스택의 두께 : 210mm(벽두께) 전기
	- 콘센트 설치 (벽과 계단간 거연) 벽걸이형 에어컨 - H1900/와일드스텝 - H350 (옥실) 방한기 열 - H300 (주방) 조리대방열 / 방풍고-H350 / 후드-H2100
	2 - 바닥온 (VP) - 보일러온도조절기 (B) - 스위치 (S) - 전선교환기(수위기) (E)
	건설 업종 취지
	VP S E I
공동주택 바닥단계를 위한구조기준	
T=10 여객소크	
옥실 건립단면 부분상세도	
석기 건립단면 대강	
기술 내부	옥실 내부
시고보드	0.58타일·블록·대강
시고보드	C/C노드/내외



옥탑지|분 평면도

SCALE


1/100



다원 건축사사무소


서울시 송파구 가락동 99-3 제일오피스텔 513호
Tel:02-449-9106 Fax:02-449-9107 E-mail:kyun81@daum.net

[illegible]

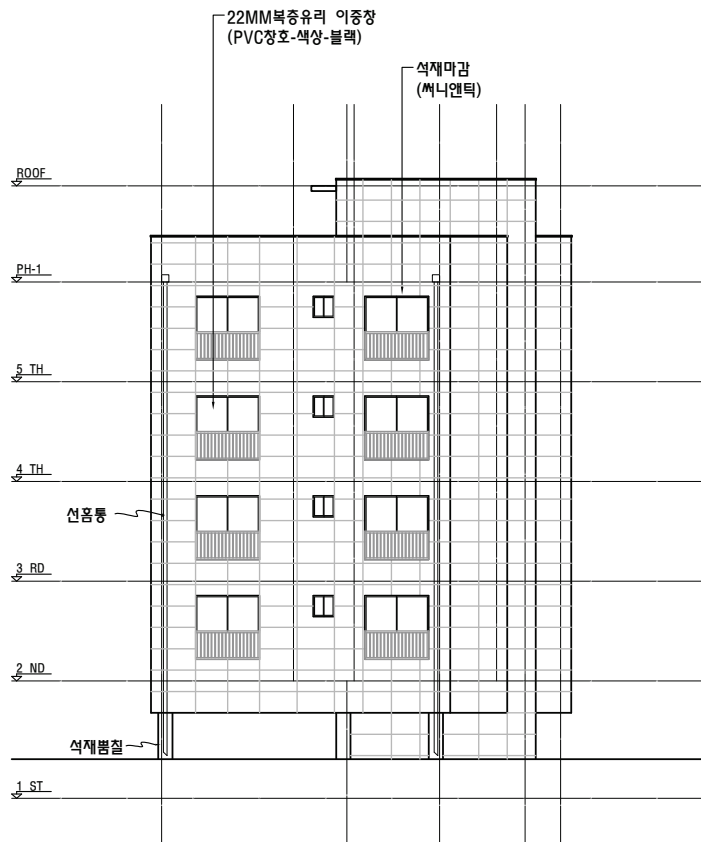

남측 면도

SCALE 1/150

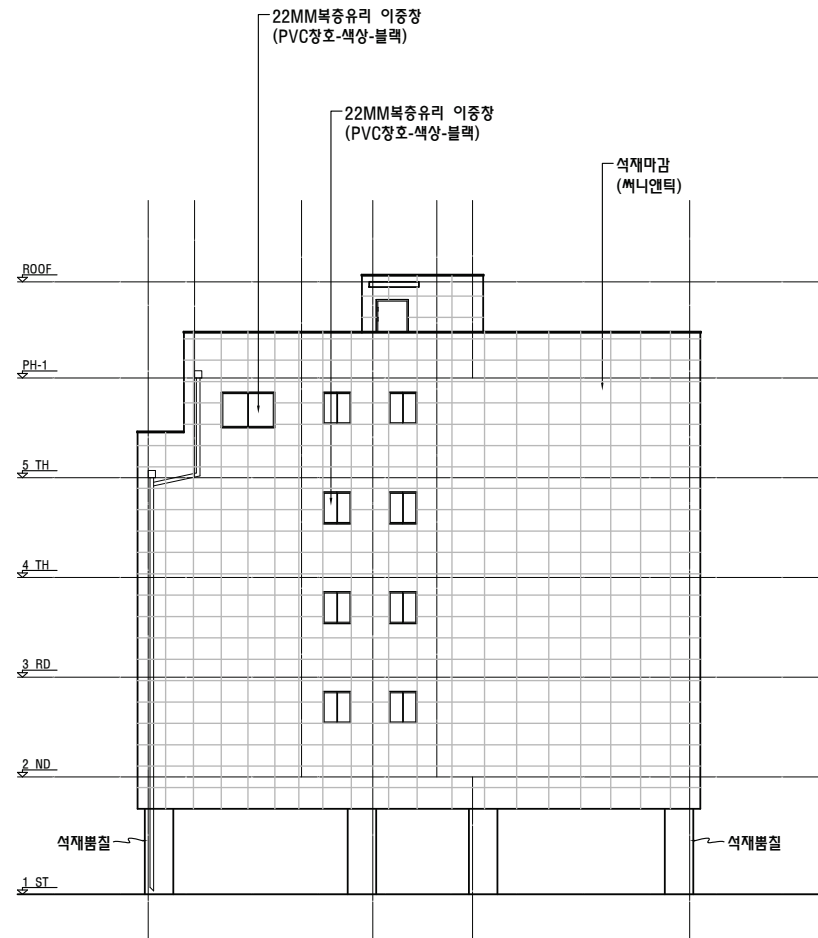

서측 면도

SCALE 1/150



다원 건축사사무소


서울시 송파구 가락동 99-3 제일오피스텔 513호
Tel:02-449-9106 Fax:02-449-9107 E-mail:kyun81@daum.net

REV.	DATE	DESCRIPTION	BY	BY	APP
△					
△					
△					

PROJECT TITLE
서울특별시 강남구 도곡동 547-11


APPROVED	
CHECKED 1	
ENGINEER	

DRAWING TITLE	남측 면도 서측 면도	DRAWING NO.
SCALE	1/150	A - 29

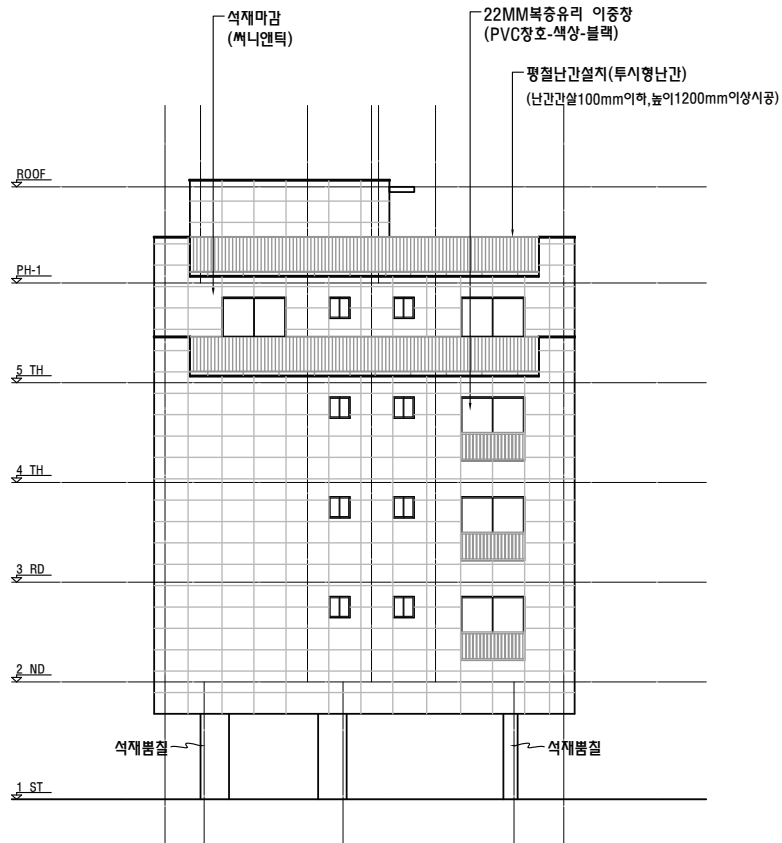

북측 면도

SCALE 1/150

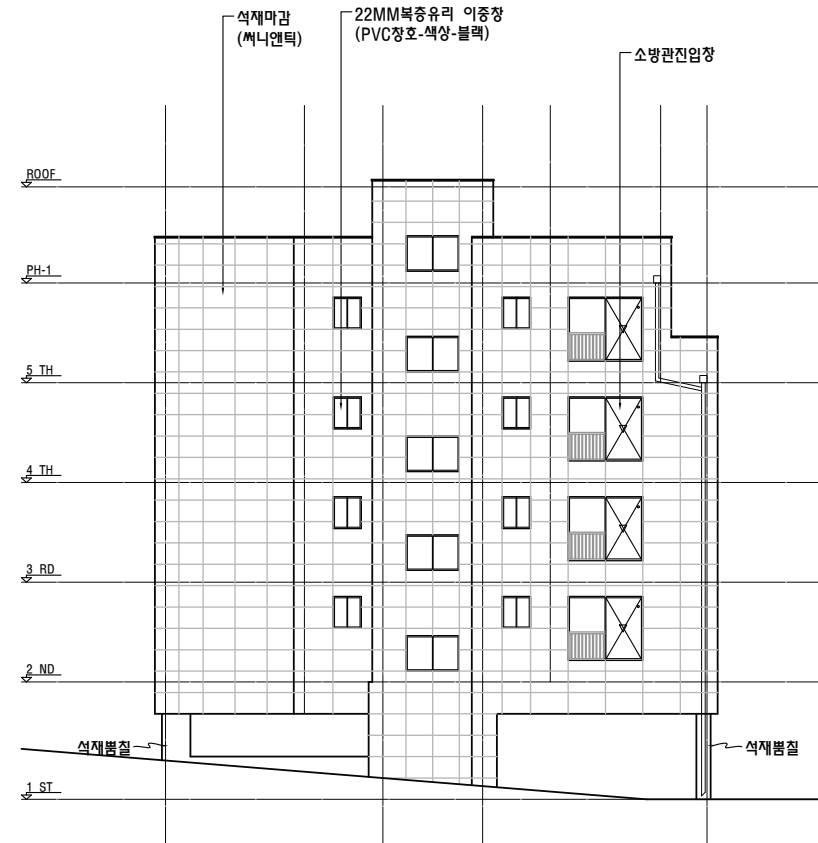

동측 면도

SCALE 1/150



다원 건축사사무소

서울시 송파구 가락동 99-3 제일오피스텔 513호
Tel:02-449-9106 Fax:02-449-9107 E-mail:kyun81@daum.net

REV.	DATE	DESCRIPTION	BY	BY	APP
△					
△					
△					

PROJECT TITLE
서울특별시 강남구 도곡동 547-11

APPROVED
CHECKED 1
ENGINEER

DRAWING TITLE
SCALE

북측 면도 동측 면도
SCALE 1/150

DRAWING NO.
A - 30