
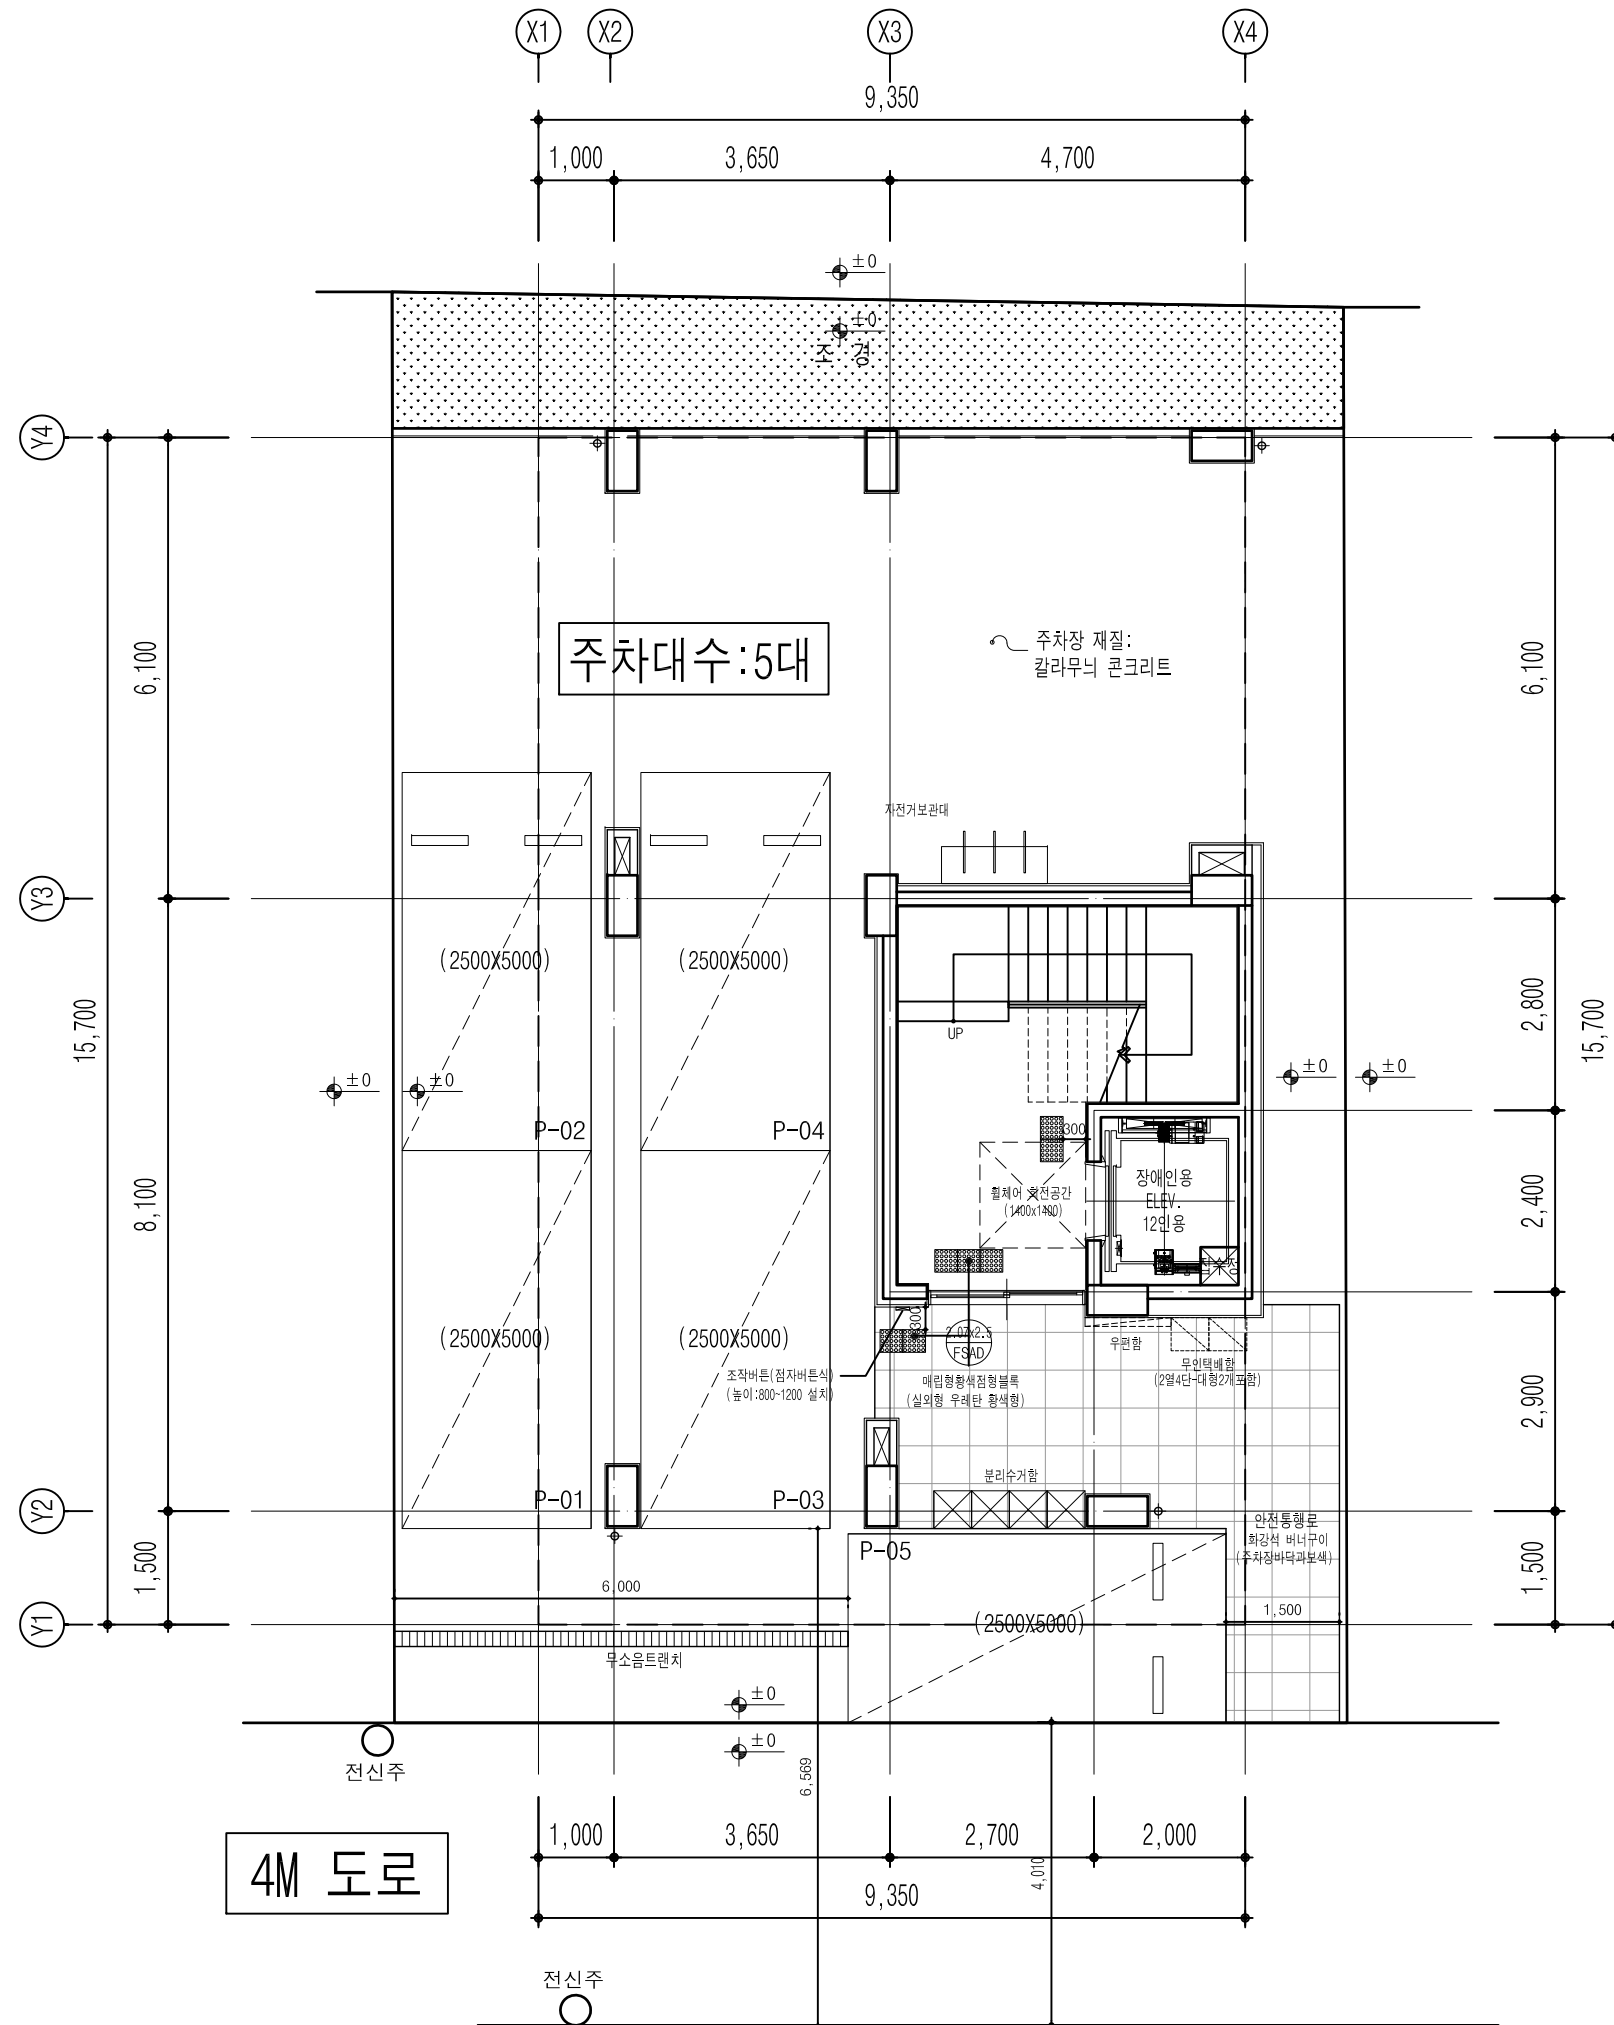


1 층 평 면 도

SCALE : A3 : 1/100

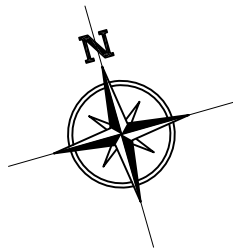

다 해 건축사무소
ARCHITECT & ENGINEERS
TEL : 02 - 879 - 2528
FAX : 02 - 877 - 3388

설 계 명 PROJECT TITLE

강동구 성내동 404-10호
도시형생활주택(소형주택)
신축공사

작성승인

내 용

3

내 용

2

내 용

1

내 용

0

작성

검 토

승 인

특 기 사 항 NOTE

차면시설

보일러

에어컨 실외기

* 구 조 *

1. 콘크리트: fck = 27 MPa
2. 철근: fy = 400 MPa
3. 세대간벽두께: 180mm(복배근)
(미장마감포함 210mm이상)
4. 외벽두께: 180mm(복배근)
5. 코아벽두께: 180mm(복배근)
6. 스라브두께: 210mm(복배근)

제 도 DRAWN

0 0 0

설 계 DESIGNED

0 0 0

검 토 CHECK

심 사 SUBMIT

승 인 APPROVE

설계일자 DATE

2025 . 01 . .

도 면 명 DRAWING TITLE

1 층 평 면 도

축척 SCALE


1 / 100

도면번호 DRAWING NO.

00-0A-031

일련번호 SHEET NO

00-00-000

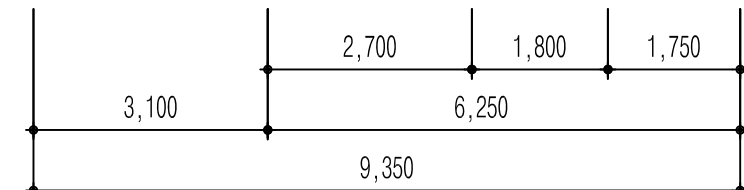다 해 건축사사무.
ARCHITECT & ENGINEER

TEX : 02 - 879 - 25
FAX : 02 - 877 - 32

설 계 명 PROJECT TITLE

강동구 성내동 404-10호
도시형생활주택(소형주택)
신축공사

작성승인

50



5/0

2

50



5

--	--

 Δ

특기사항 NOTE

제 도 DRAWN	설 계 DESIGNED
-----------	--------------

000

설 계 DESIGNED

000

검 토 CHECK

심 사 SUBMIT

인 APPROVE

설계일자 DATE

2024 . 05 .

도면명 DRAWING TITLE

4 초평면도

축척 SCALE

1 / 100

도면번호 DRAWING NO.


			A	0	3	3
--	--	--	---	---	---	---




일련번호 SHEET NO

11-11-11

4 층 평 면 도

SCALE : A3 : 1/100

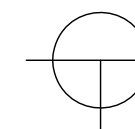

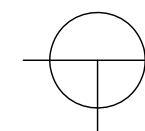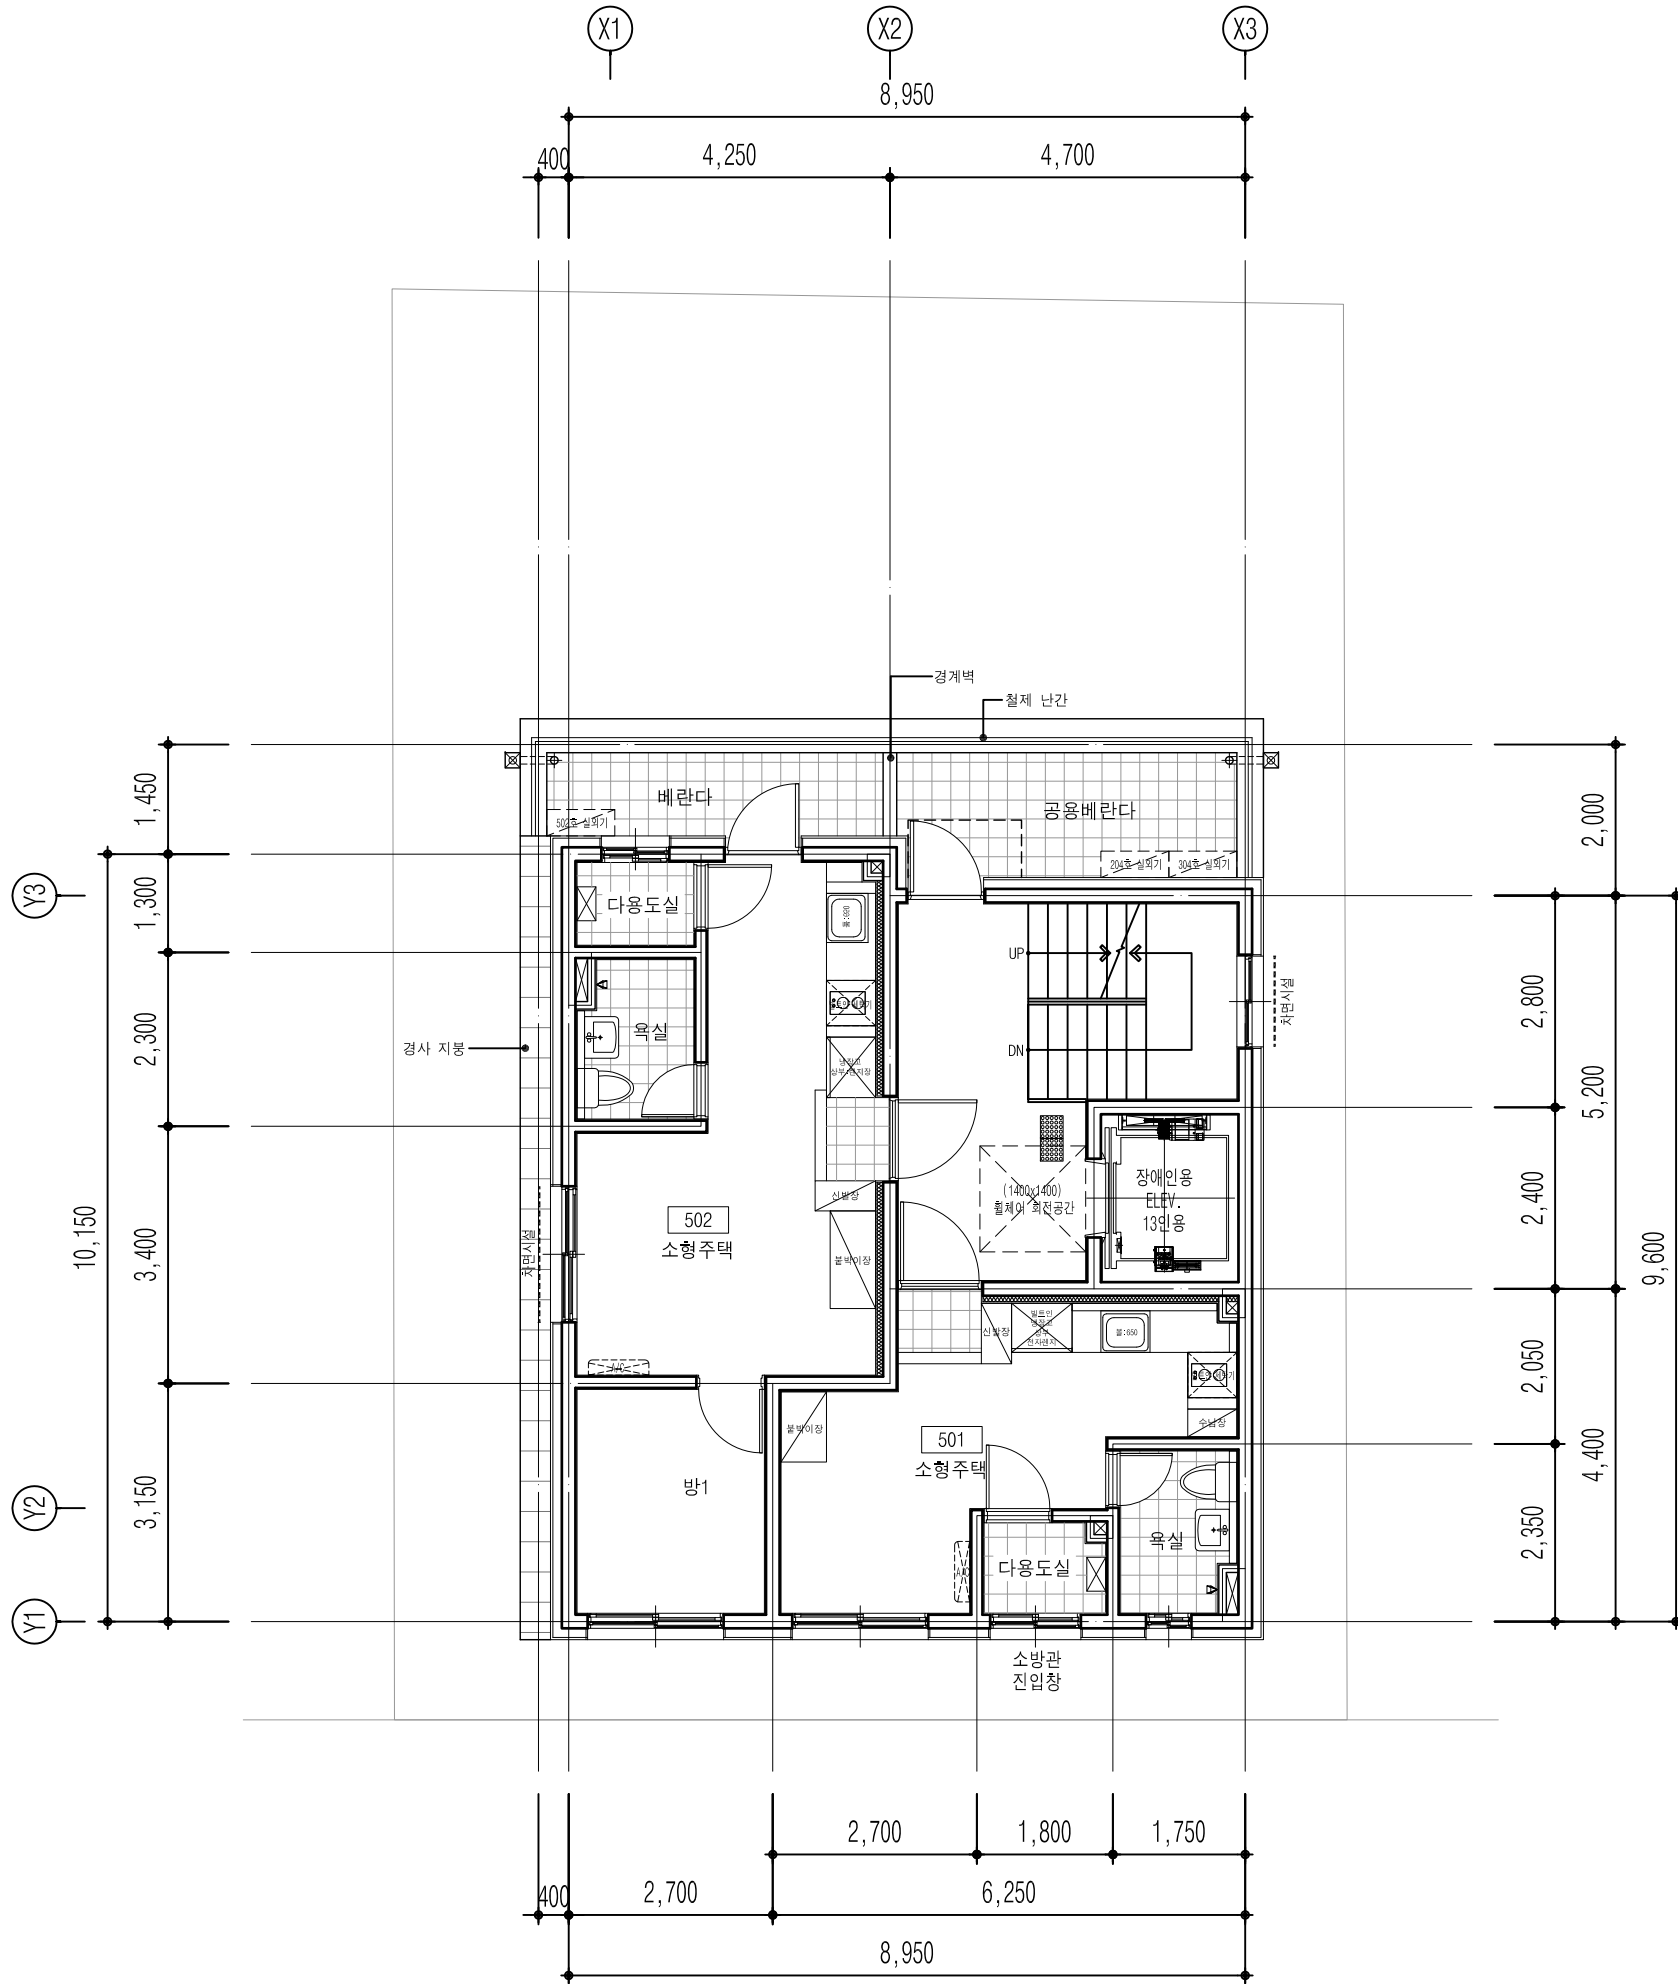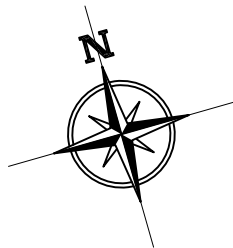

5층 평면도

SCALE : A3 : 1/100



다해 건축사사무소
ARCHITECT & ENGINEERS
TEL : 02 - 879 - 2528
FAX : 02 - 877 - 3388

설계명 PROJECT TITLE

강동구 성내동 404-10호
도시형생활주택(소형주택)
신축공사

작성승인

내 용

3

내 용

2

내 용

1

내 용

0

작성 검토 승인

특기사항 NOTE

제 도 DRAWN 설 계 DESIGNED

000 000

검 토 CHECK 심 사 SUBMIT

승 인 APPROVE

설계일자 DATE

2024 . 05 . .

도면명 DRAWING TITLE

5층 평면도

축척 SCALE





1 / 100

도면번호 DRAWING NO.

00-0A-034

일련번호 SHEET NO

00-00-000

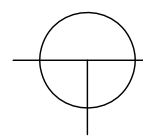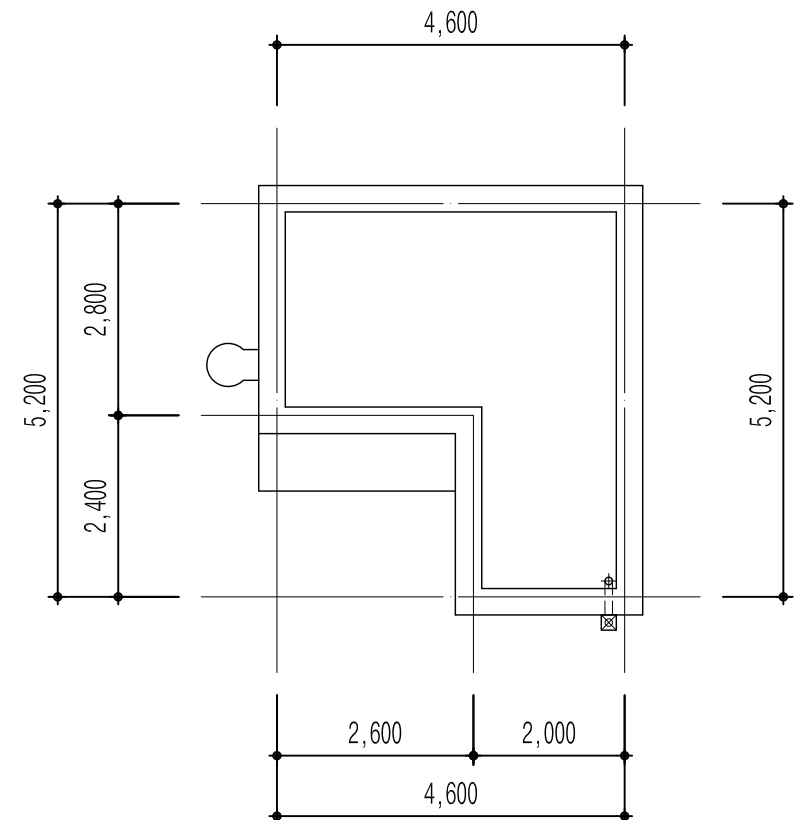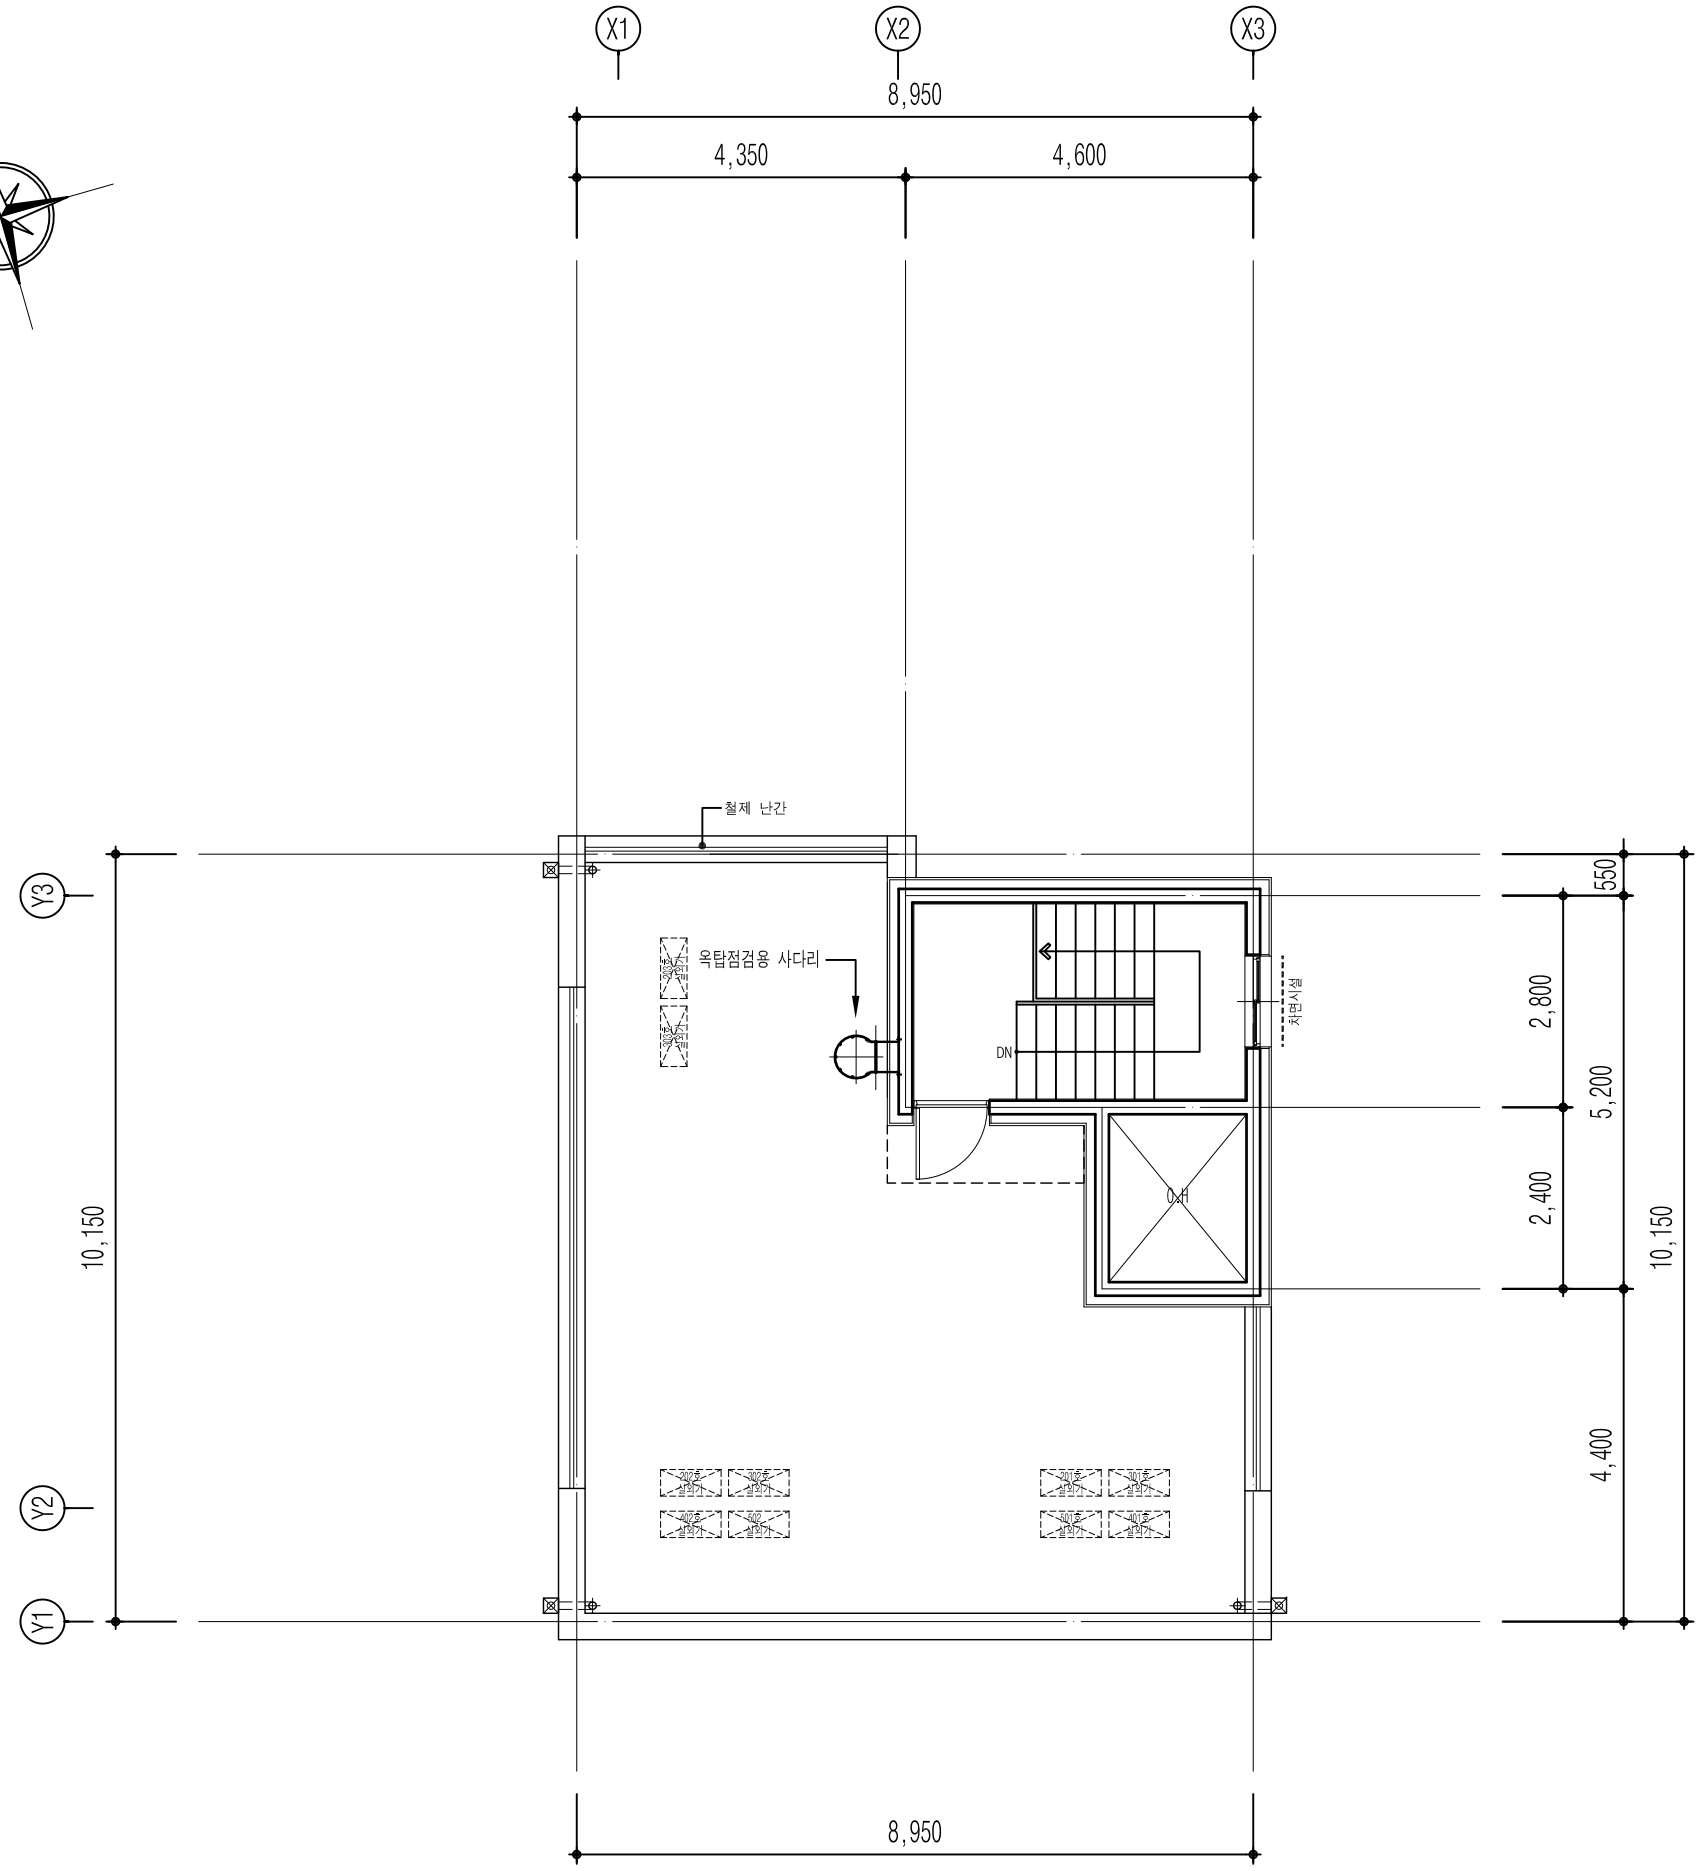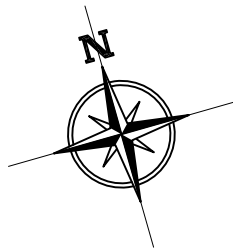

지붕및옥탑지붕평면도

SCALE : A3 : 1/100



설 계 명 PROJECT TITLE
강동구 성내동 404-10호
도시형생활주택(소형주택)
신축공사

작성승인

내 품

3

내 용

2

내 용

1

내 용

0

작성 검토 승인

특 기 사 항 NOTE

* 구 조 *

제 도 DRAWN 설 계 DESIGNED

0 0 0 0 0 0

검 토 CHECK 실 사 SUBMIT

승 인 APPROVE

설계일자 DATE

2024 . 05 . .

도 면 명 DRAWING TITLE

지붕및옥탑평면도

축 척 SCALE

1 / 100

도면번호 DRAWING NO.

00-0A-035

일련번호 SHEET NO

00-00-000



다 해 건축사무소
ARCHITECT & ENGINEERS

TEL : 02 - 879 - 2528
FAX : 02 - 877 - 3388

설 계 명 PROJECT TITLE

강동구 성내동 404-10호
도시형생활주택(소형주택)
신축공사

작성승인

내 용

3

내 용

2

내 용

1

내 용

0

작성

검 토

승 인

특 기 사 항 NOTE

제 도 DRAWN 설 계 DESIGNED

000

000

검 토 CHECK

심 사 SUBMIT

승 인 APPROVE

설계일자 DATE

2025 . 01 . .

도 면 명 DRAWING TITLE

입면도-1

축척 SCALE


1 / 100

도면번호 DRAWING NO.

00-0A-041

일련번호 SHEET NO

00-00-000

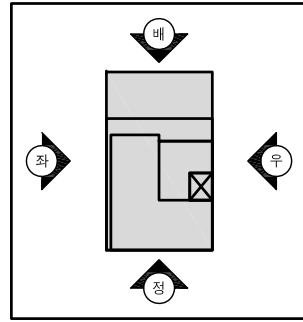

화강석 마감
(고층석 계열)

화강석 마감
(거창석 계열)

화강석 마감
(고층석 계열)

화강석 마감
(거창석 계열)

철제난간

▽지붕층 바닥

우수드레인
(외부벽체 색상과
유사한 색상설치)

▽5층 바닥

▽4층 바닥

▽3층 바닥

▽2층 바닥

▽1층 바닥

석재뿔칠
(화이트색상)

석재뿔칠
(화이트색상)

정 면 도

SCALE : A3 : 1/100

우 측 면 도

SCALE : A3 : 1/100

설 계 명 PROJECT TITLE

강동구 성내동 404-10호
도시형생활주택(소형주택)
신축공사

작성승인			
내 용			
3			
내 용			
2			
내 용			
1			
내 용			
0	작성	검 토	승 인

특 기 사 항 NOTE

제 도 DRAWN	설 계 DESIGNED
0 0 0	0 0 0
검 토 CHECK	심 사 SUBMIT

승 인 APPROVE



설계일자 DATE
2025 . 01 . .

도 면 명 DRAWING TITLE
입면도-2

축척 SCALE
1 / 100

도면번호 DRAWING NO.
□□-□A-□□□□

일련번호 SHEET NO
□□-□□-□□□□

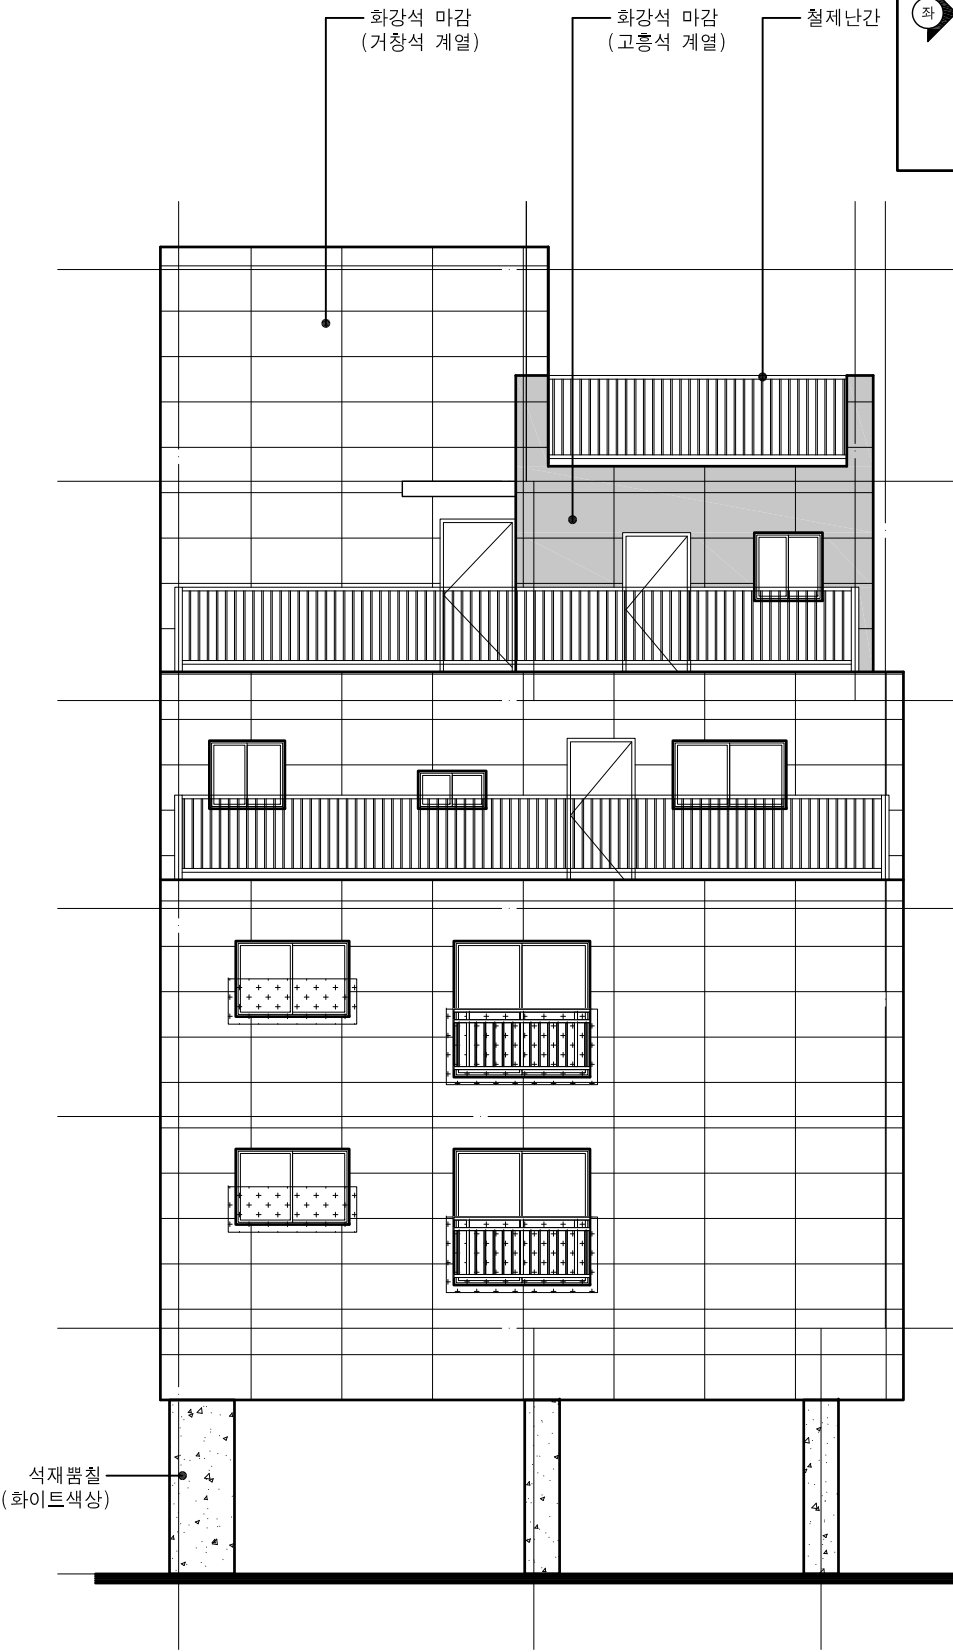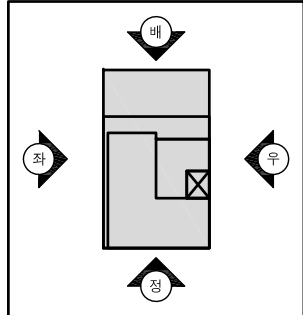

▽지붕층 바닥
▽5층 바닥
▽4층 바닥
▽3층 바닥
▽2층 바닥
▽1층 바닥

배 면 도
SCALE : A3 : 1/100



우수드레인
(외부벽채 색상과
유사한 색상설치)

좌 측 면 도
SCALE : A3 : 1/100