



FORUM
Hanwon
한원포럼건축사사무소
서울시 송파구 법원로8길 7
901호 (문정동 화엄타워)
TEL : 3445-8361
FAX : 3445-8363

작품번호
PROJ. NO

작품명
PROJ. TITLE
천호동 399-25,26
다세대주택신축공사
(자율주택정비사업)

기

사

투시도



SCALE 1 / 100

DATE 2022. 02.

DRAWING NO

A 021

SHEET NO

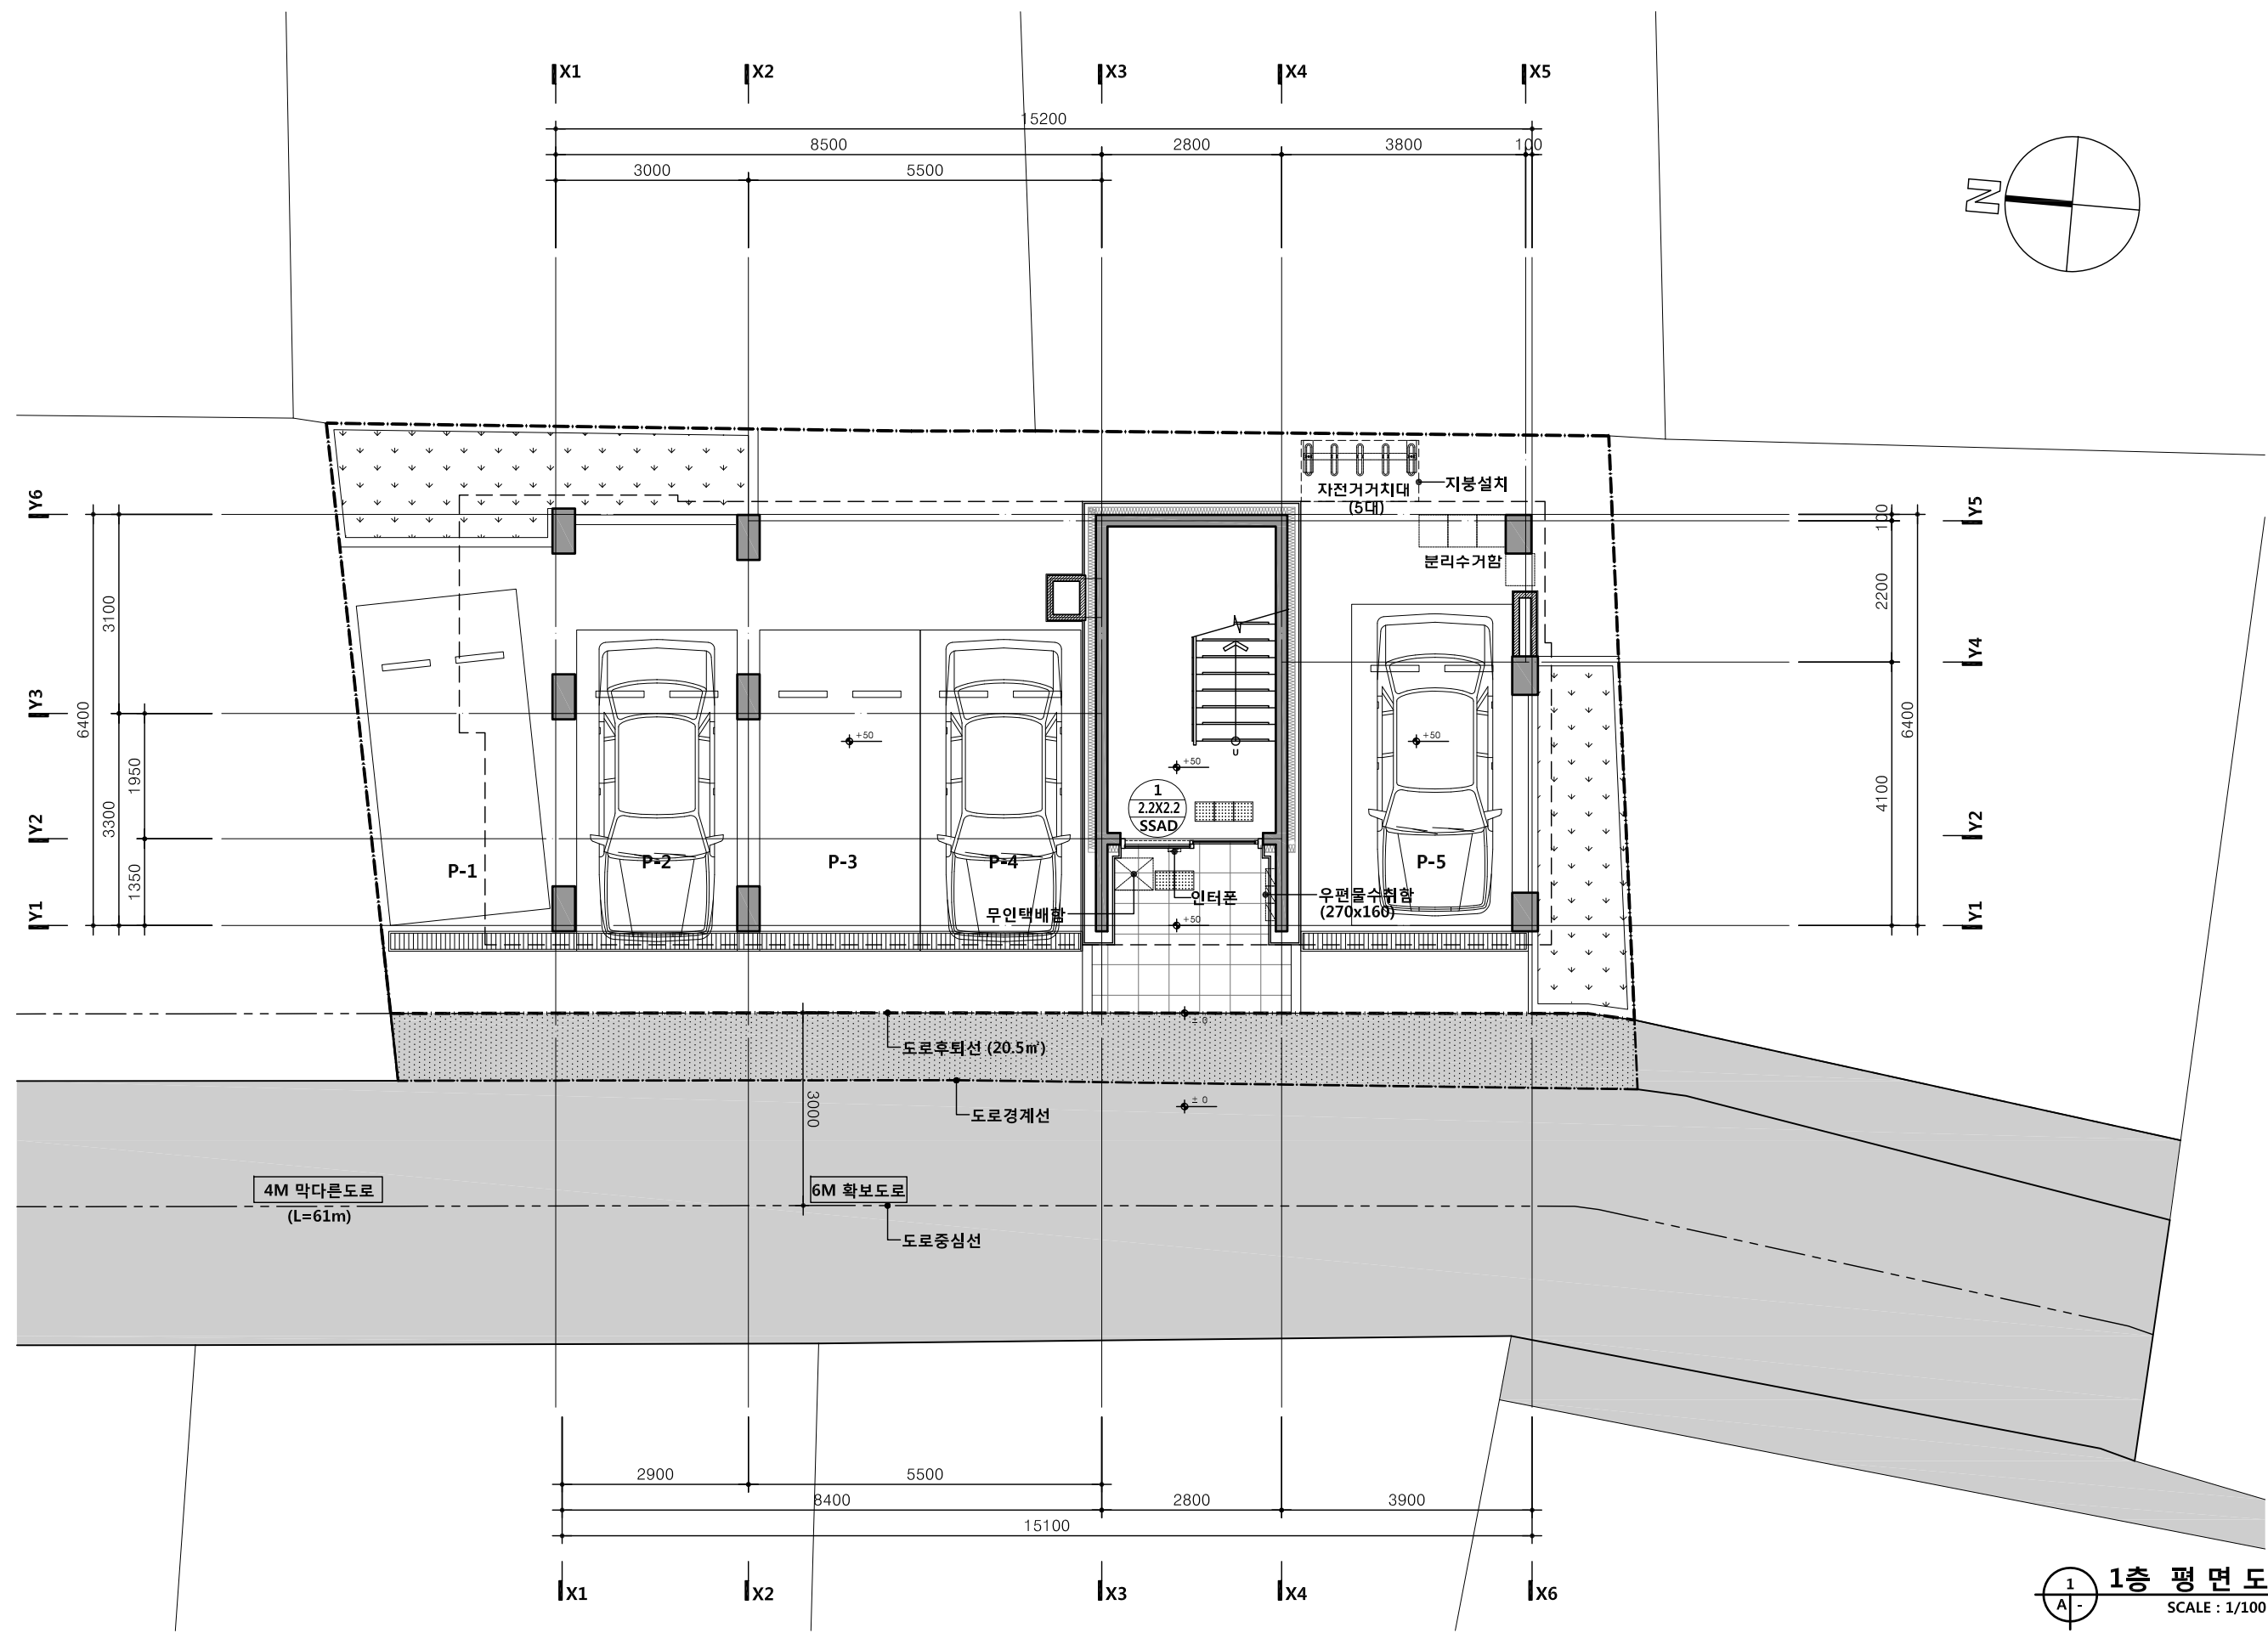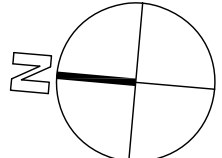

1층 평면도
SCALE : 1/100



2.3층 평면도
SCALE : 1/100

FORUM

Hanwon

한원포럼건축사사무소

서울시 송파구 법원로8길 7
901호 (문정동 화엄타워)
TEL : 3445-8361
FAX : 3445-8363

작품번호

PROJ. NO

작품명

PROJ. TITLE

천호동 399-25,26
다세대주택신축공사
(자율주택정비사업)

기

사

수정

REVISED

건축설계

ARC. DESIGNED BY

구조설계

STR. DESIGNER BY

설비설계

MEC. DESIGNED BY

전기설계

ELE. DESIGNED BY

계도

DRAWN BY

심사

CHECKED BY

승인

APPROVED BY

도면명

DRAWING TITLE

2,3층 평면도

축척

SCALE

1 / 100

일자

DATE

2022. 02.


도면번호

DRAWING NO

A - 202

시트번호

SHEET NO

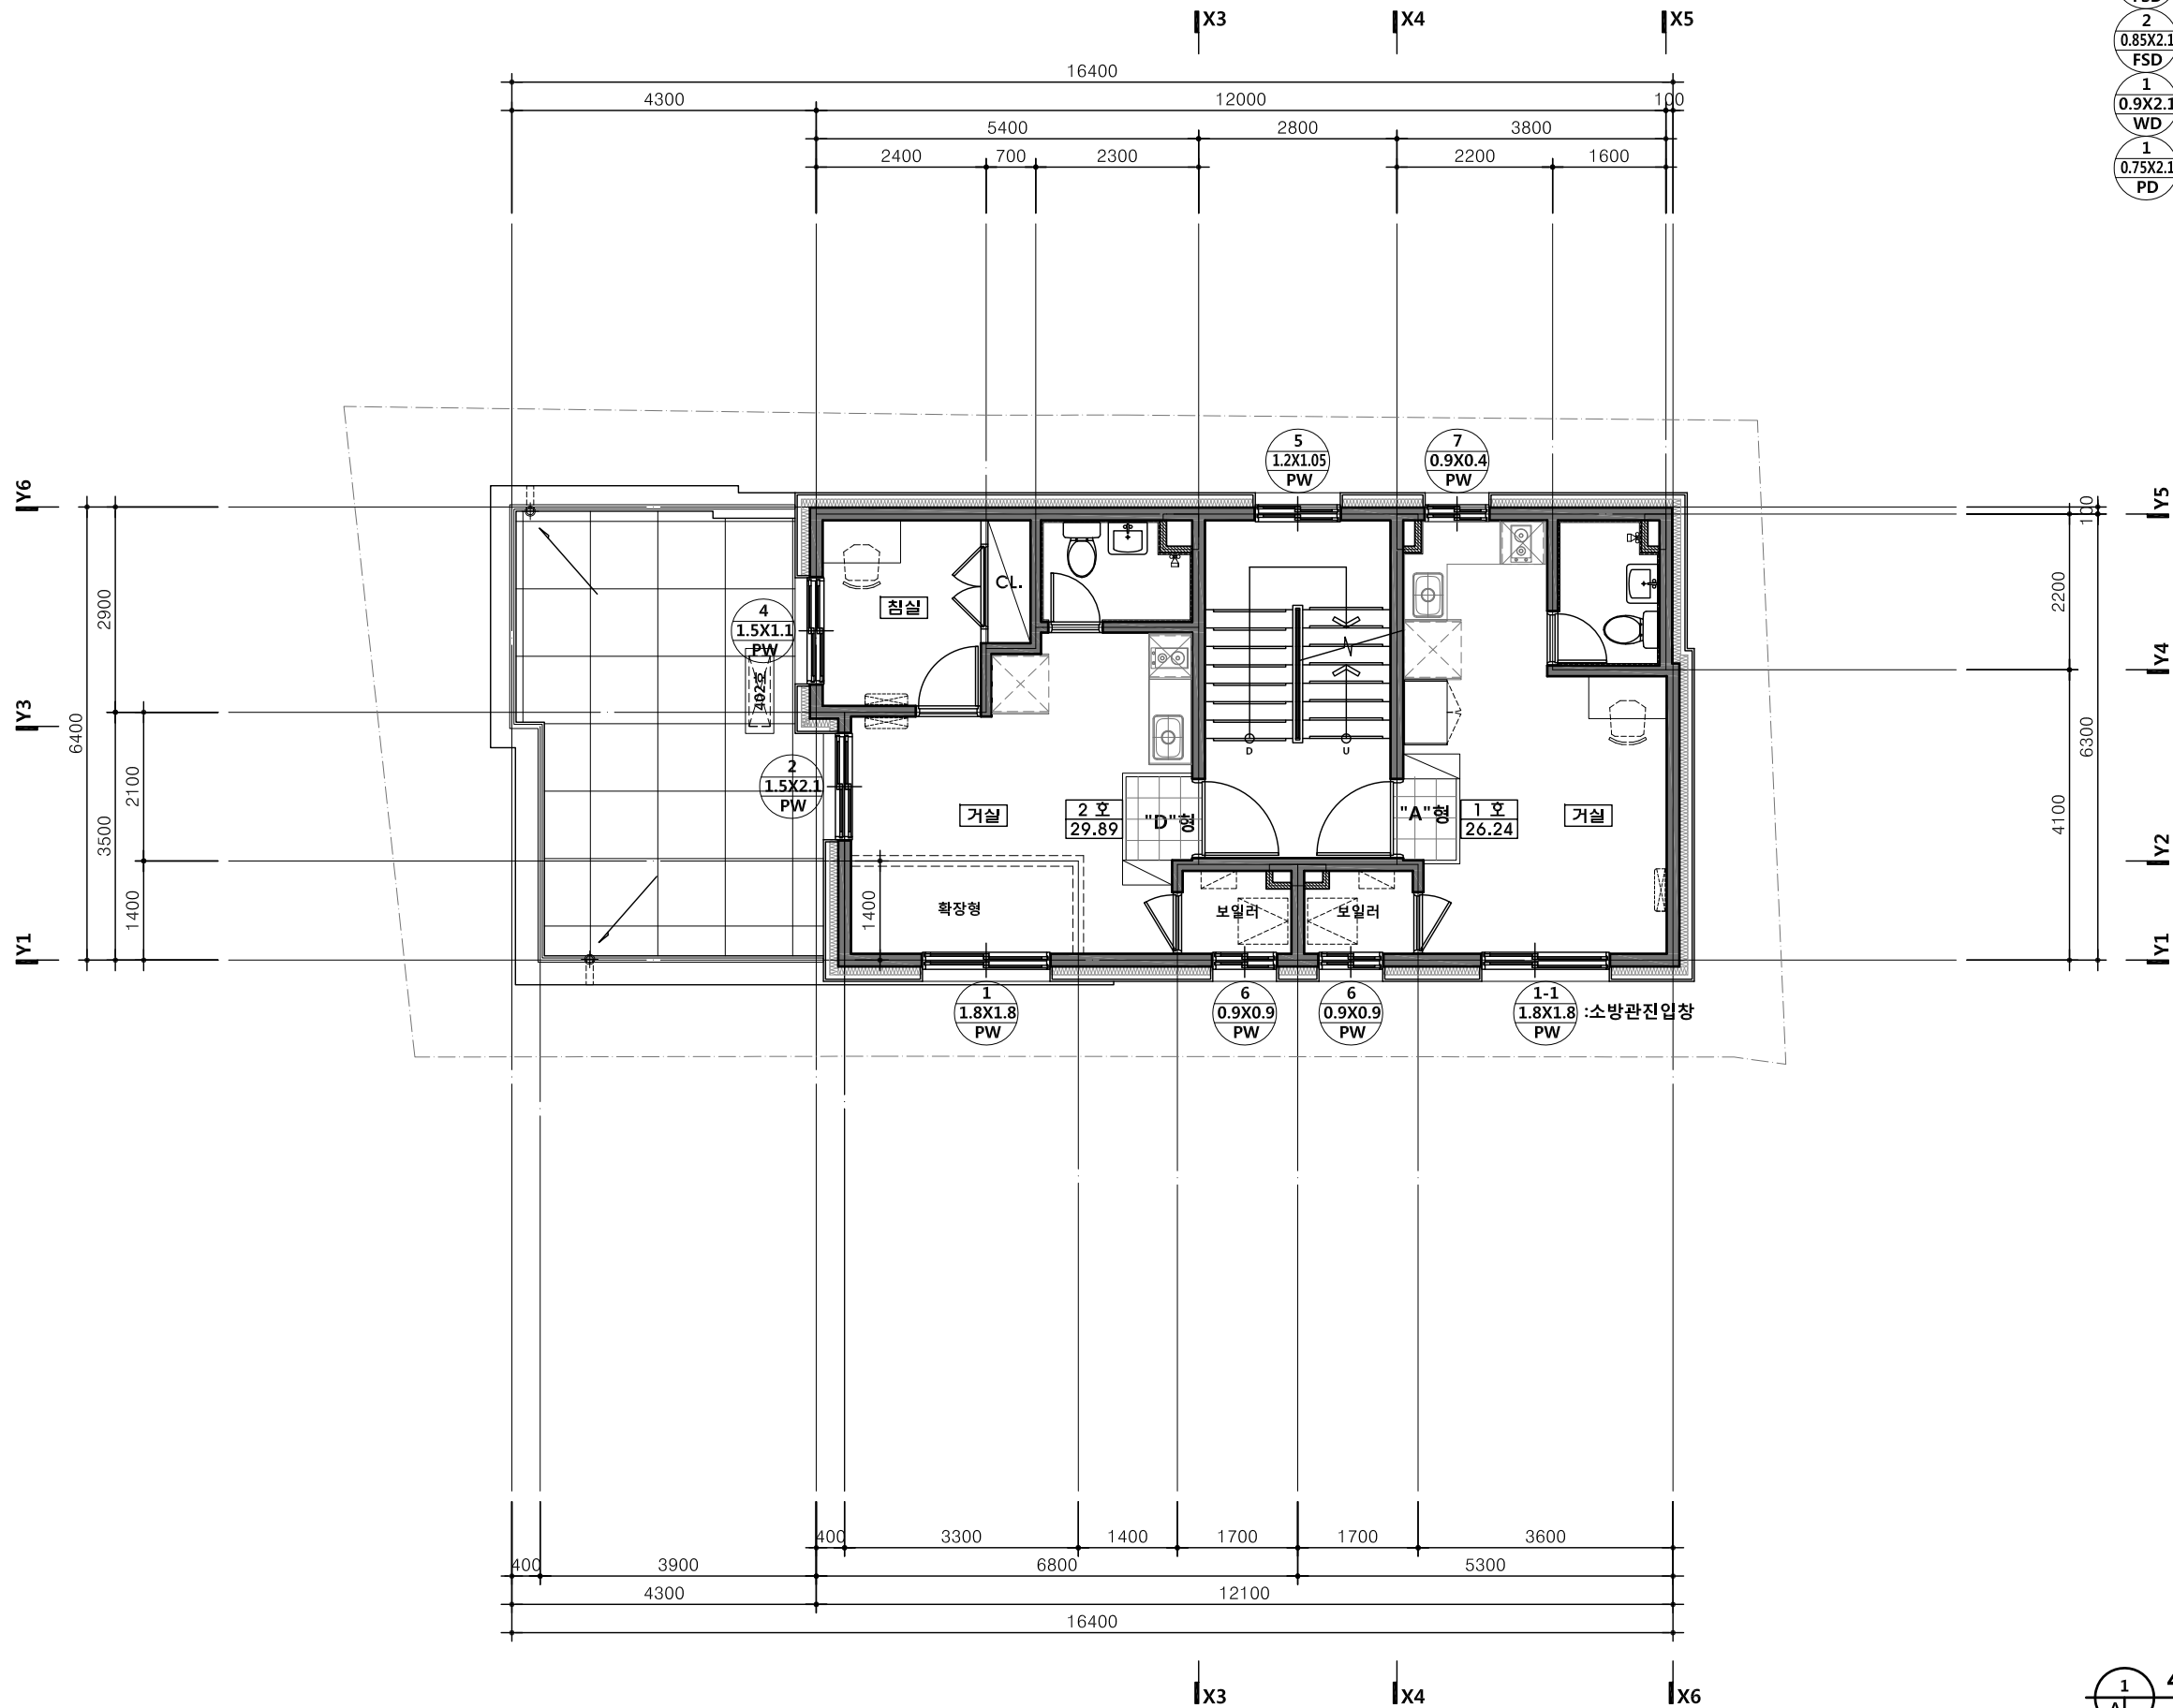

- * 내부창호
- 1. 1.1X2.2 FSD : 세대출입문
 - 2. 0.85X2.1 FSD : 보일러실
 - 1. 0.9X2.1 WD : 침실
 - 1. 0.75X2.1 PD : 화장실

1 4층 평면도
A - SCALE : 1/100

FORUM
Hanwon
한원포럼건축사사무소
서울시 송파구 법원로8길 7
901호 (문정동 화엄타워)
TEL : 3445-8361
FAX : 3445-8363

작품번호
PROJ. NO
작품명
PROJ. TITLE
천호동 399-25,26
다세대주택신축공사
(자율주택정비사업)

기 사

수정
REVISED

건축설계
ARC. DESIGNED BY

구조설계
STR. DESIGNER BY

설비설계
MEC. DESIGNED BY

전기설계
ELE. DESIGNED BY

제도
DRAWN BY

심사
CHECKED BY

승인
APPROVED BY

도면명
DRAWING TITLE

4층 평면도


축척
SCALE 1 / 100

일자
DATE 2022. 02.

도면번호
DRAWING NO

A - 203

시트번호
SHEET NO

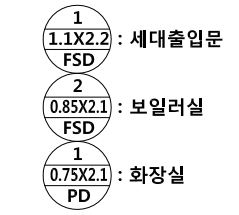

$\frac{1}{1.1 \times 2.2}$: 세대출입문
 FSD
 $\frac{2}{0.85 \times 2.1}$: 보일러실
 FSD
 $\frac{1}{0.75 \times 2.1}$: 화장실
 PD

$\frac{2}{0.85 \times 2.1}$: 보일러실
 $\frac{1}{0.75 \times 2.1}$: 화장실


$\frac{1}{0.75 \times 2.1} : \text{화장실}$

SHEET NO

1
A -

5층 평면도

SCALE : 1/100

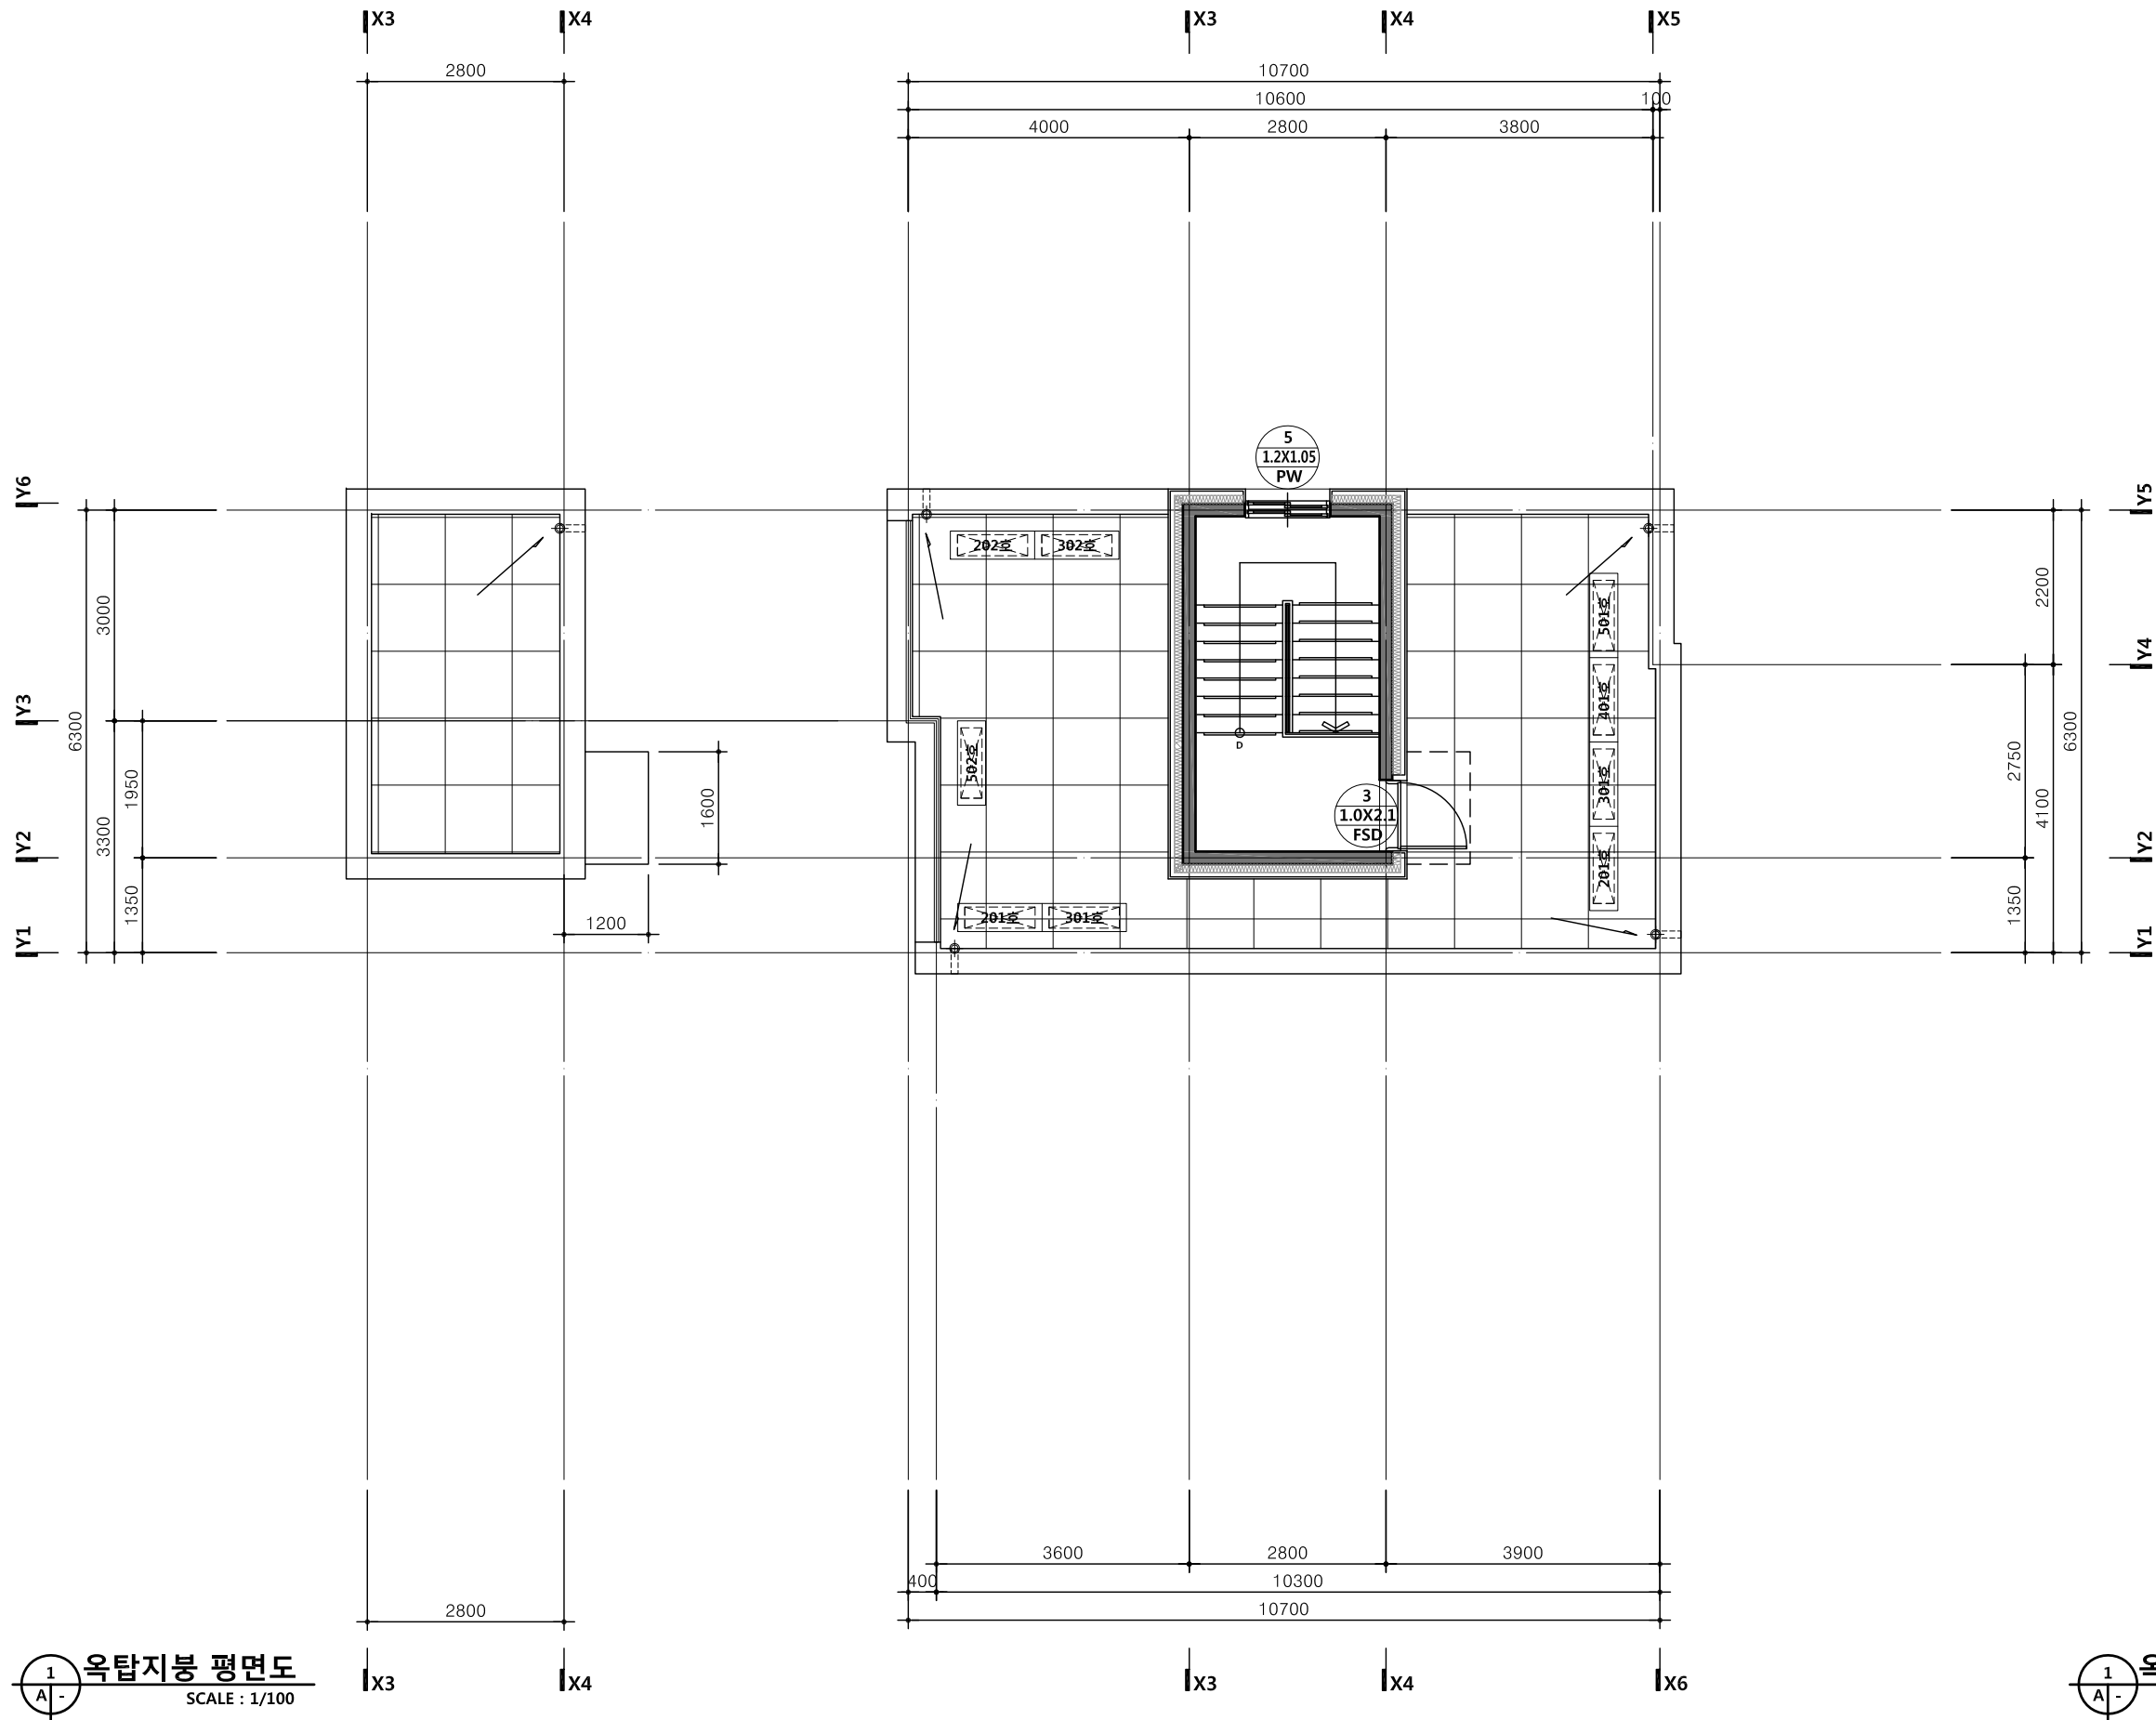

1 옥탑지붕 평면도
SCALE : 1/100

1 옥탑 평면도
SCALE : 1/100

FORUM
Hanwon
한원포럼건축사사무소
서울시 송파구 법원로8길 7
901호 (문정동 화엄타워)
TEL : 3445-8361
FAX : 3445-8363

작품번호
PROJ. NO

작품명
PROJ. TITLE
천호동 399-25,26
다세대주택신축공사
(자율주택정비사업)

기 사

수정
REVISED

건축설계
ARC. DESIGNED BY

구조설계
STR. DESIGNER BY

설비설계
MEC. DESIGNED BY

전기설계
ELE. DESIGNED BY

제 도
DRAWN BY

심 사
CHECKED BY

승 인
APPROVED BY

도면명
DRAWING TITLE

옥탑 평면도


SCALE 1 / 100

DATE 2022. 02.

도면번호
DRAWING NO

A 205

시트번호
SHEET NO

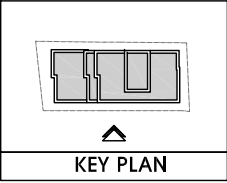

FORUM
Hanwon
한원포럼건축사사무소
서울시 송파구 법원로8길 7
901호 (문정동 화엄타워)
TEL : 3445-8361
FAX : 3445-8363

작품 번호
PROJ. NO

작품명
PROJ. TITLE
천호동 399-25,26
다세대주택신축공사
(자율주택정비사업)

기 사

*선출품 : Ø100 S'ST PIPE

수 정
REVISED

건축 설계
ARC. DESIGNED BY

구조 설계
STR. DESIGNEN BY

설비 설계
MEC. DESIGNED BY

전기 설계
ELE. DESIGNED BY

제 도
DRAWIN BY

심 사
CHECKED BY

승 인
APPROVED BY

도면명
DRAWING TITLE

정 면 도

축 척
SCALE 1 / 100


일 자
DATE 2022. 02.

도면번호
DRAWING NO


A — 211



일련번호
SHEET NO

—

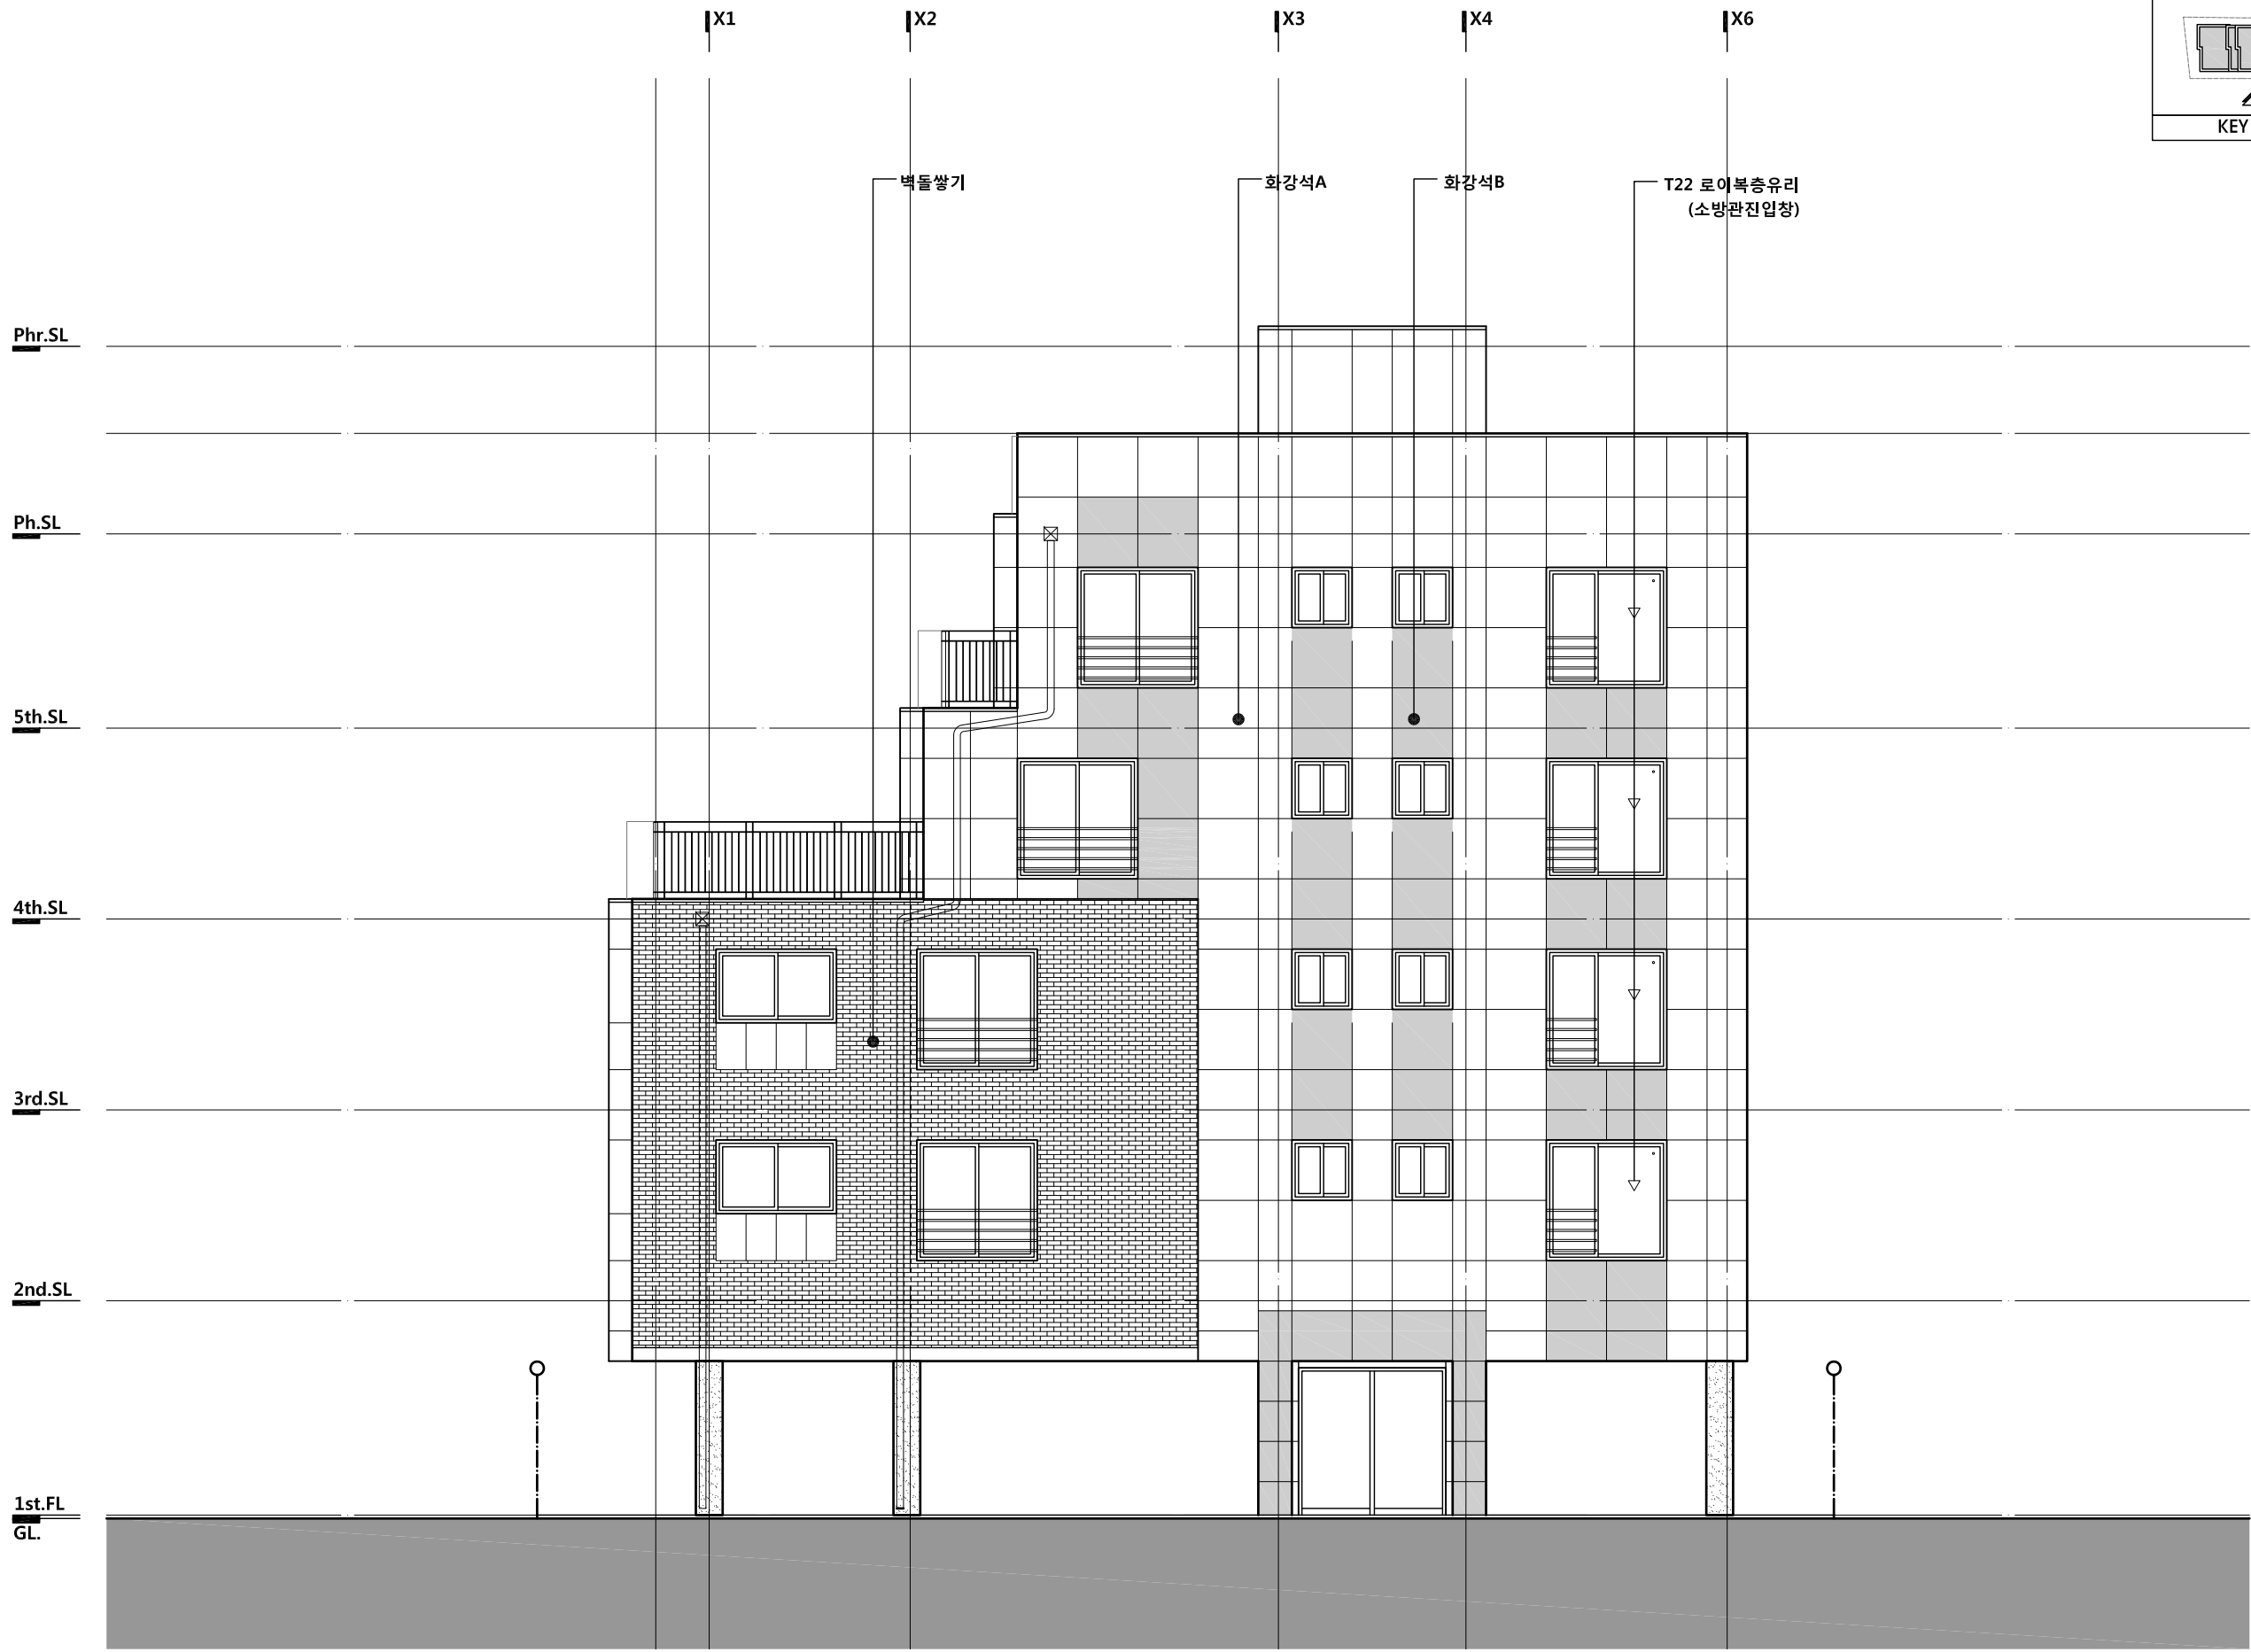

1
A - 정 면 도
SCALE : 1/100

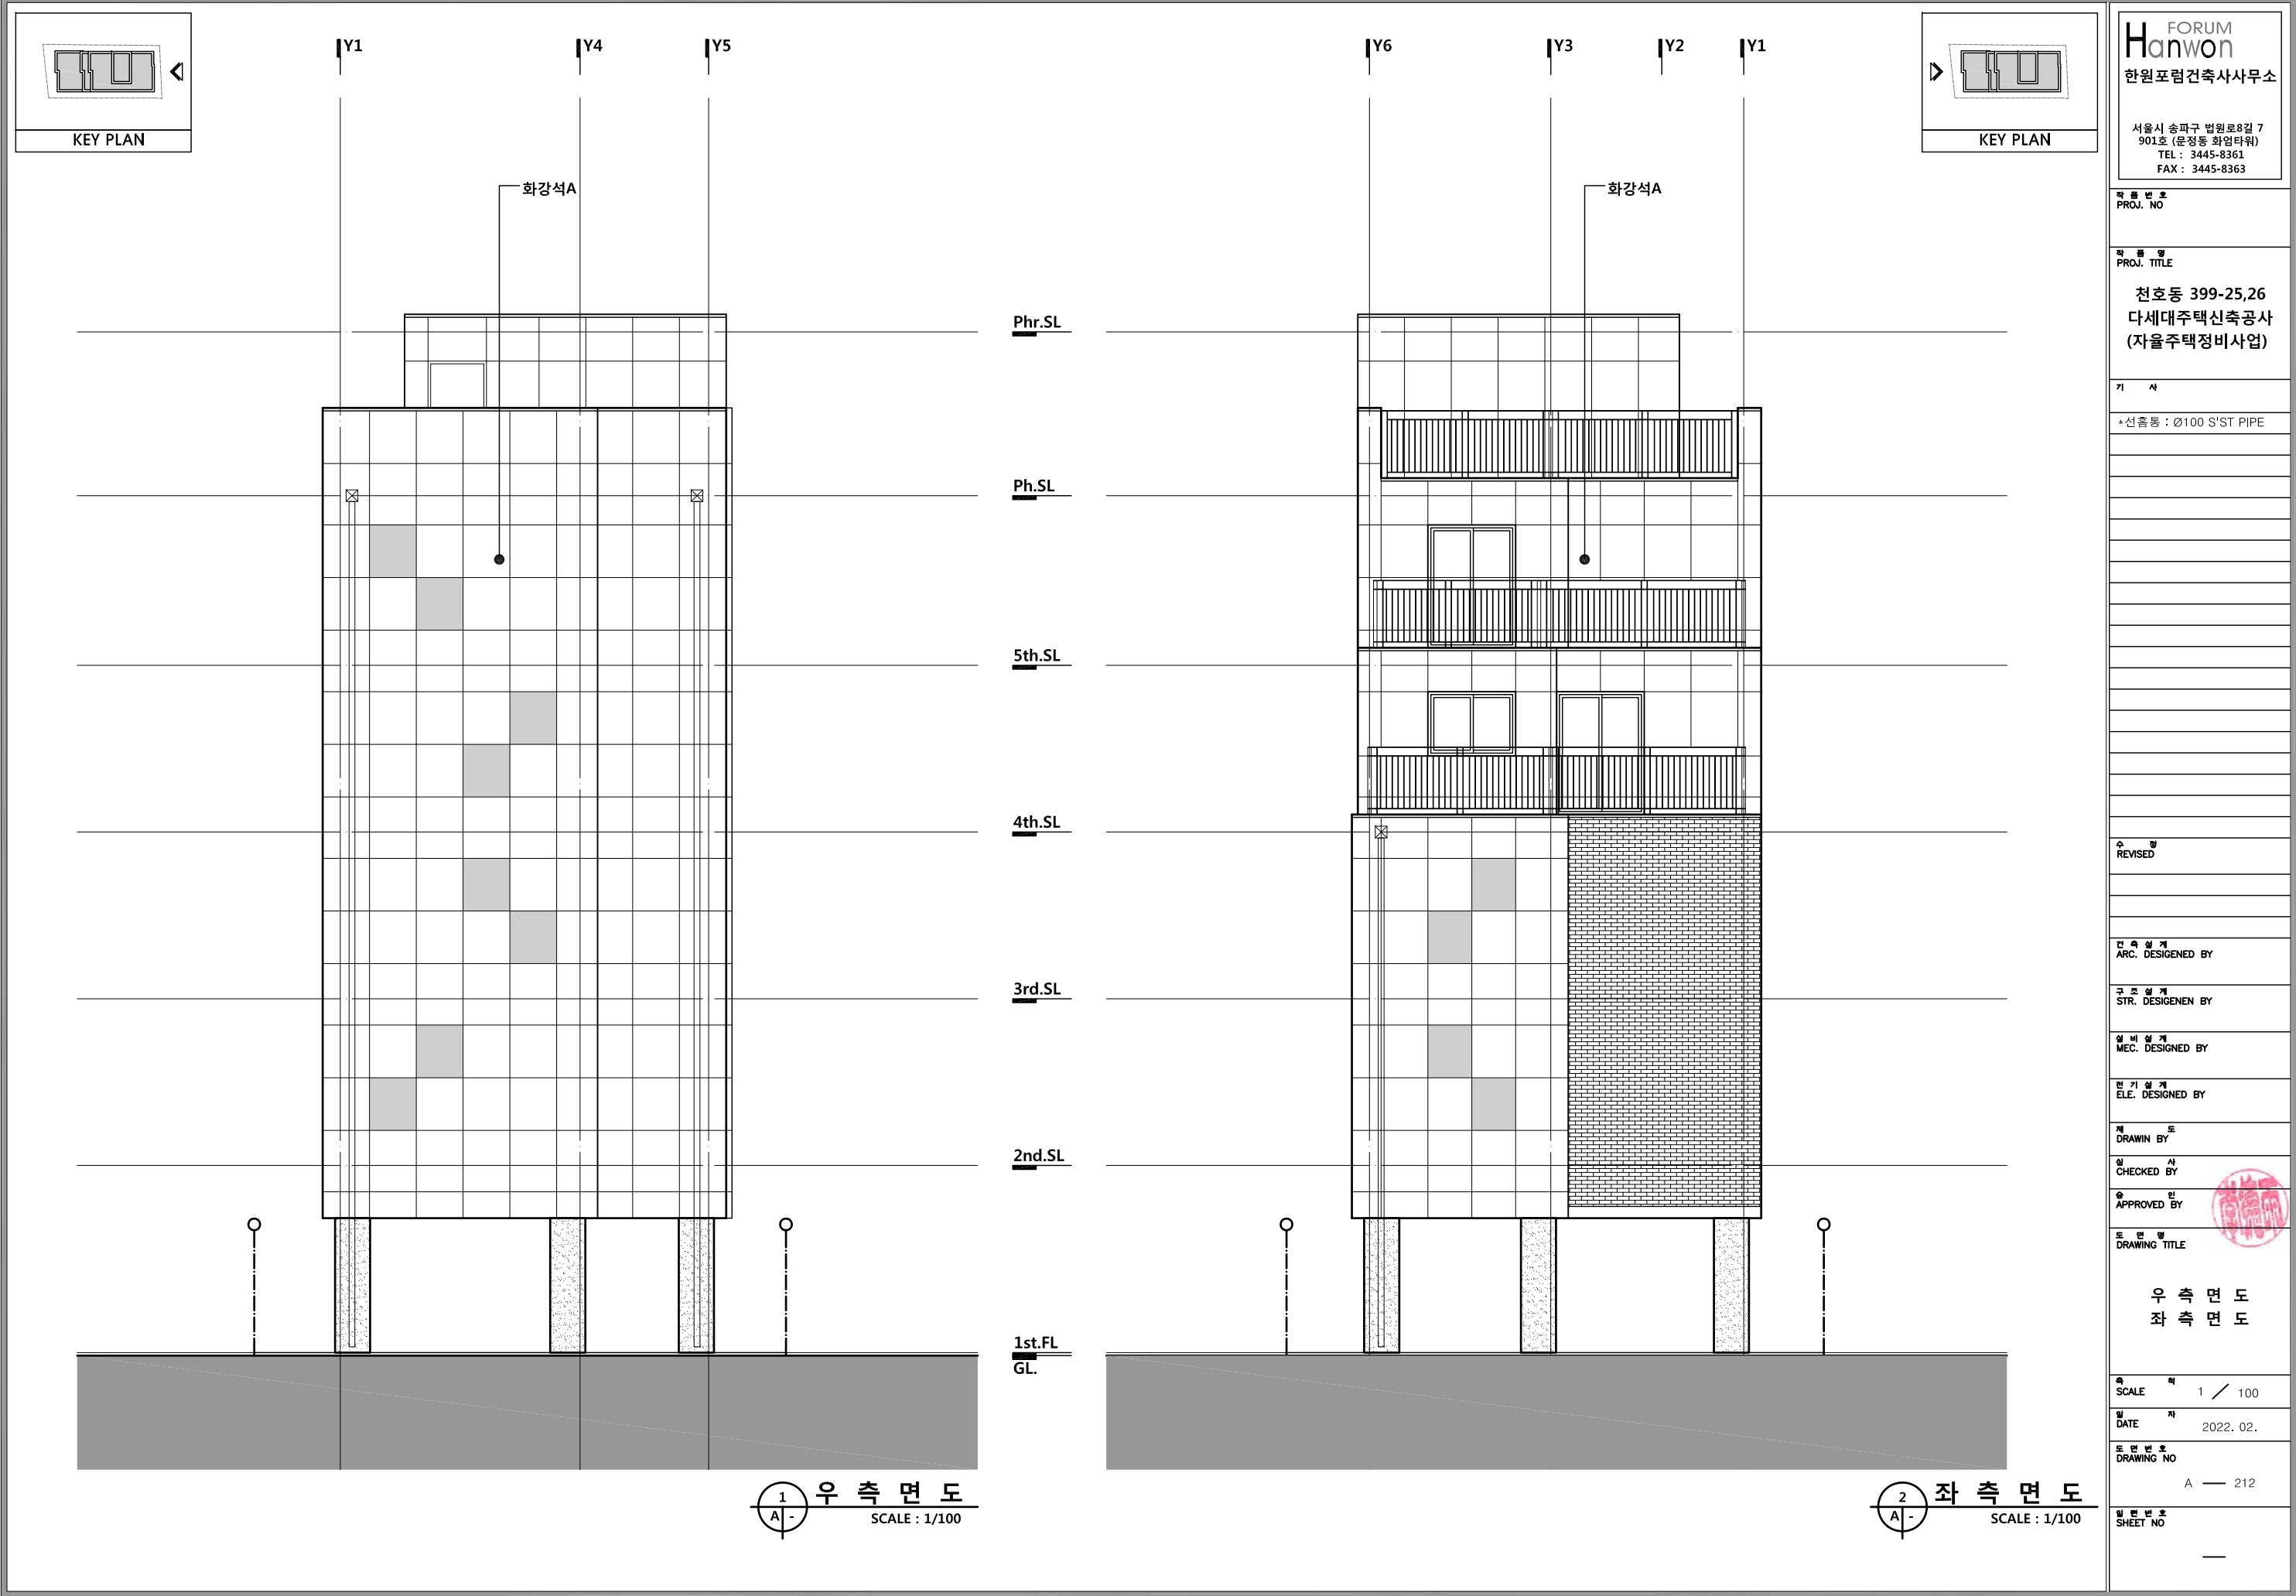

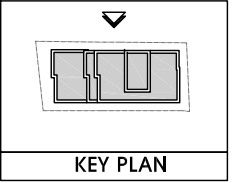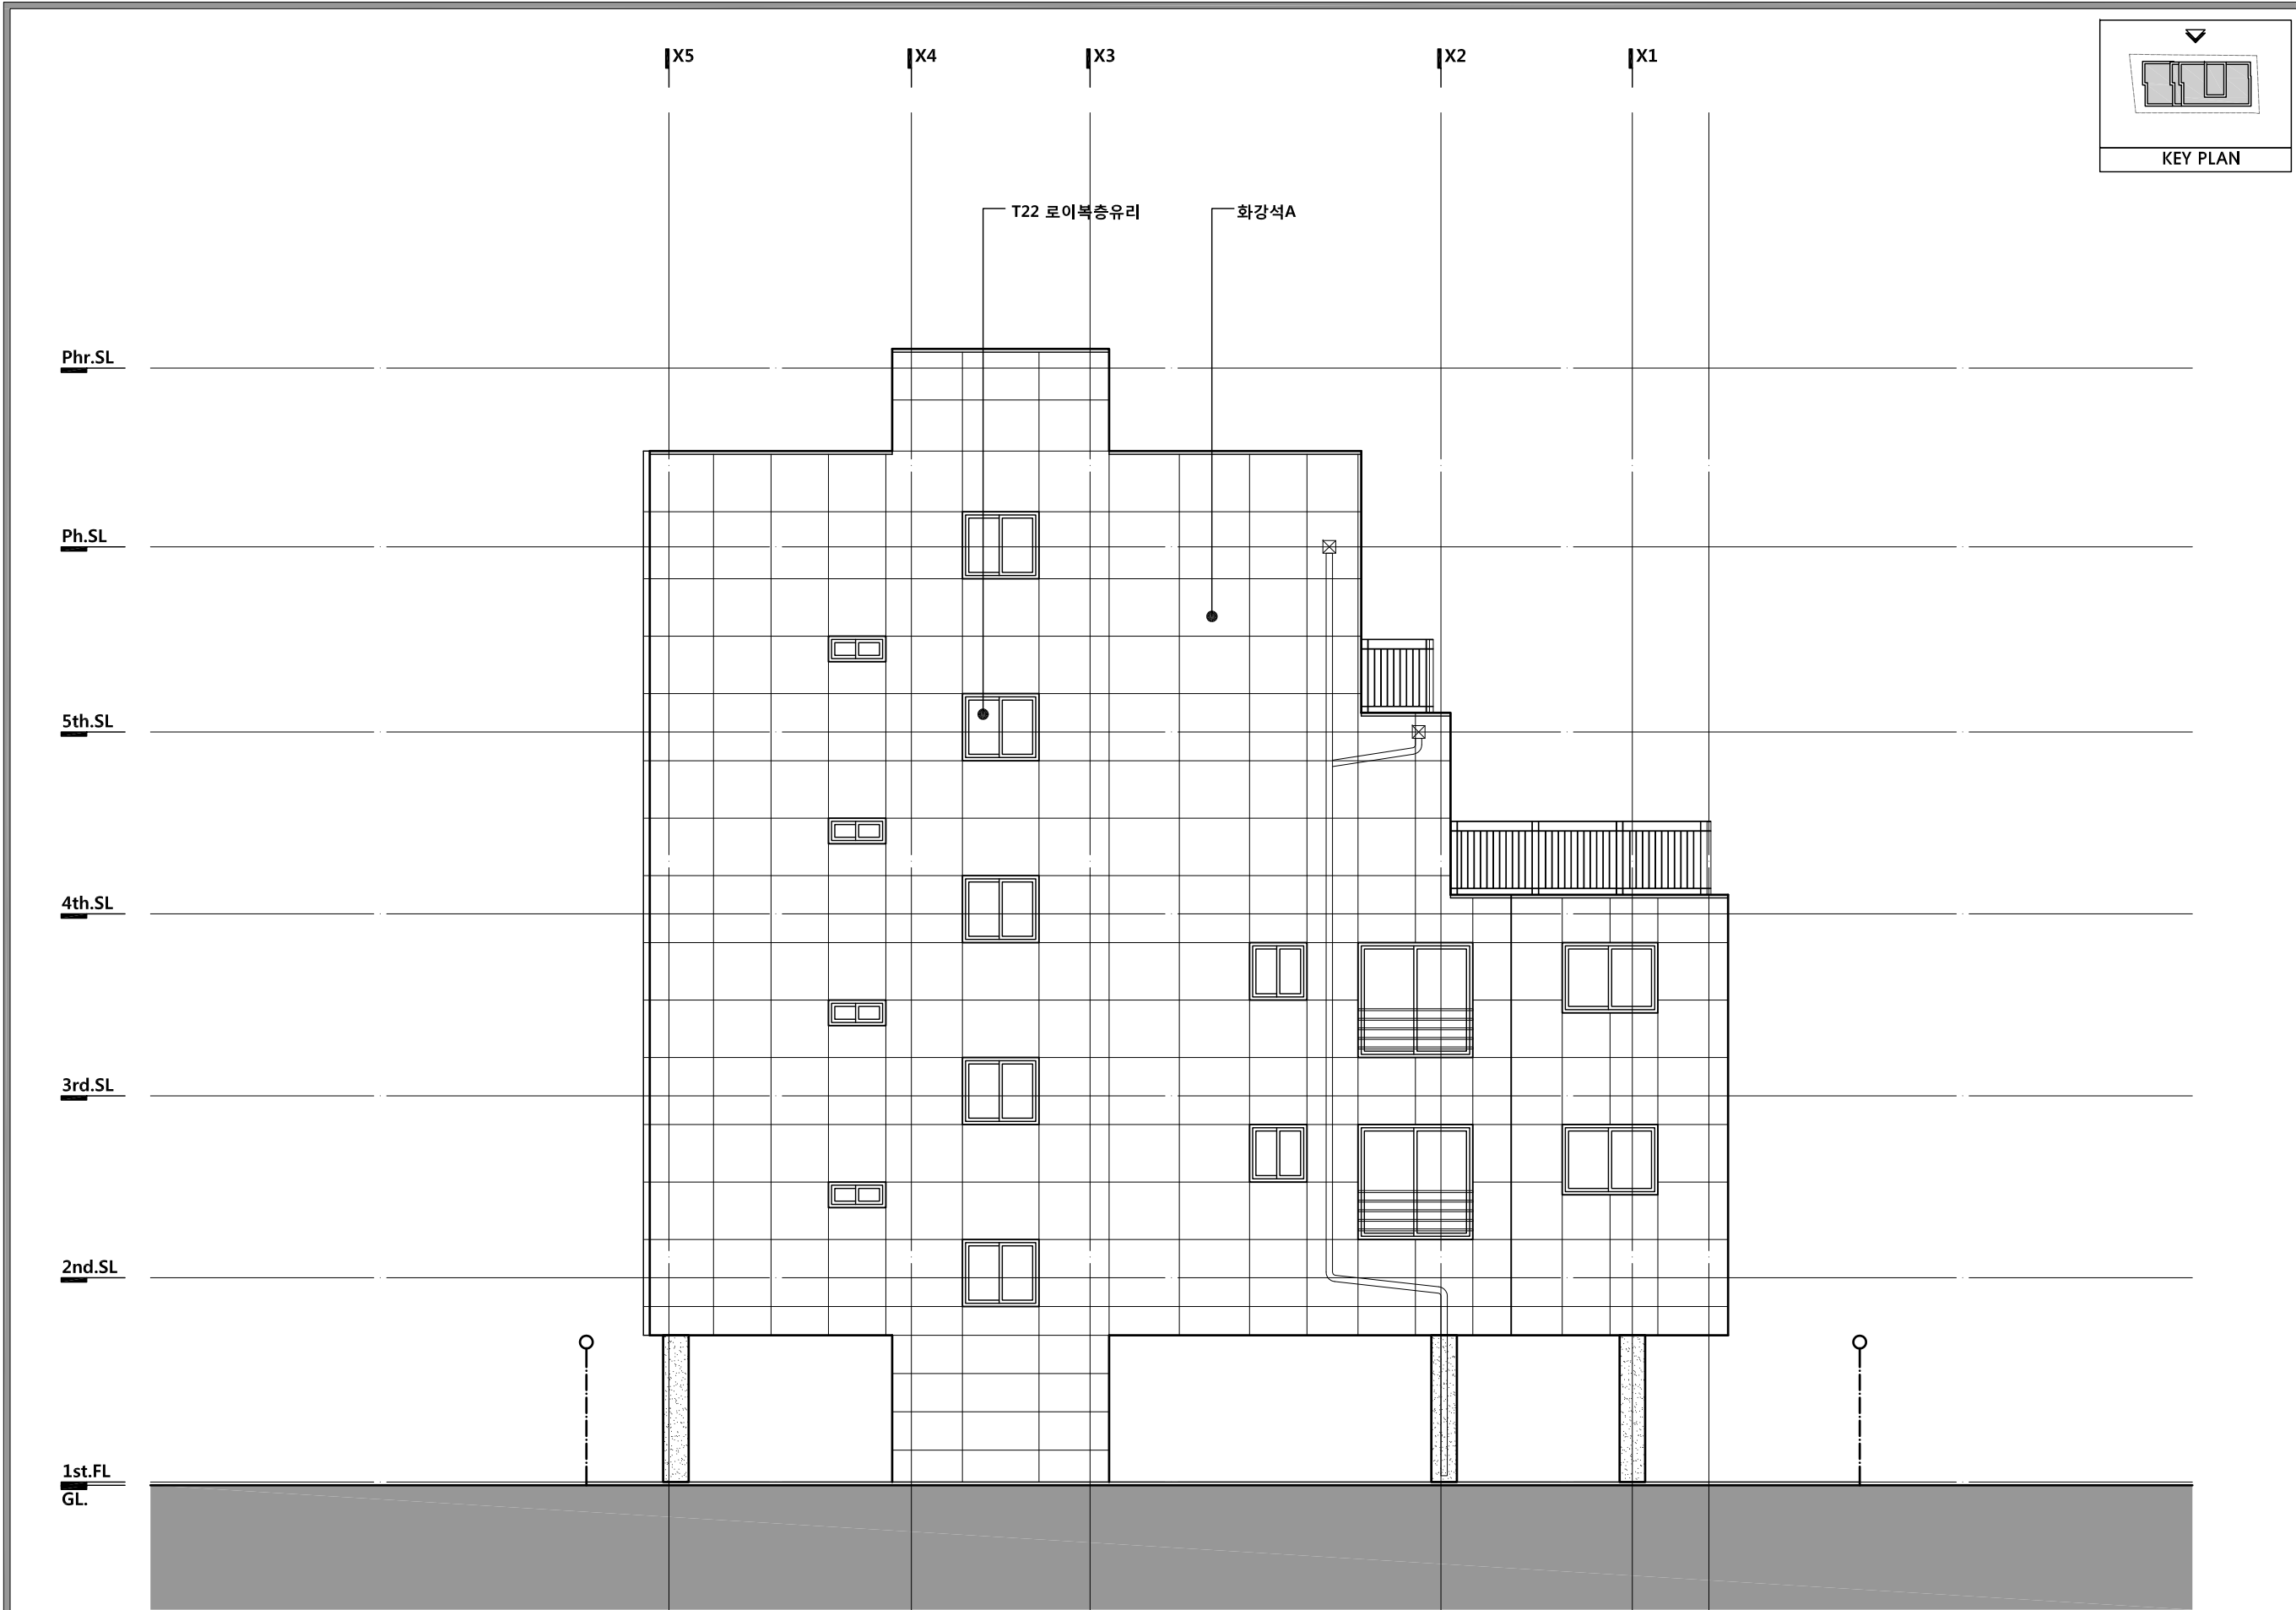

FORUM
Hanwon
한원포럼건축사사무소
서울시 송파구 법원로8길 7
901호 (문정동 화엄타워)
TEL : 3445-8361
FAX : 3445-8363

작품번호
PROJ. NO

작품명
PROJ. TITLE
천호동 399-25,26
다세대주택신축공사
(자율주택정비사업)

기 사

*선출품 : Ø100 S'ST PIPE

수 정
REVISED

건축 설계
ARC. DESIGNED BY

구조 설계
STR. DESIGNER BY

설비 설계
MEC. DESIGNED BY

전기 설계
ELE. DESIGNED BY

계 도
DRAWN BY

심 사
CHECKED BY

승 인
APPROVED BY

도 면 명
DRAWING TITLE

배 면 도

축 척
SCALE 1 / 100

일 자
DATE 2022. 02.

도 면 번호
DRAWING NO

A — 213

일 편 번호
SHEET NO

—

1 배 면 도
A - SCALE : 1/100