


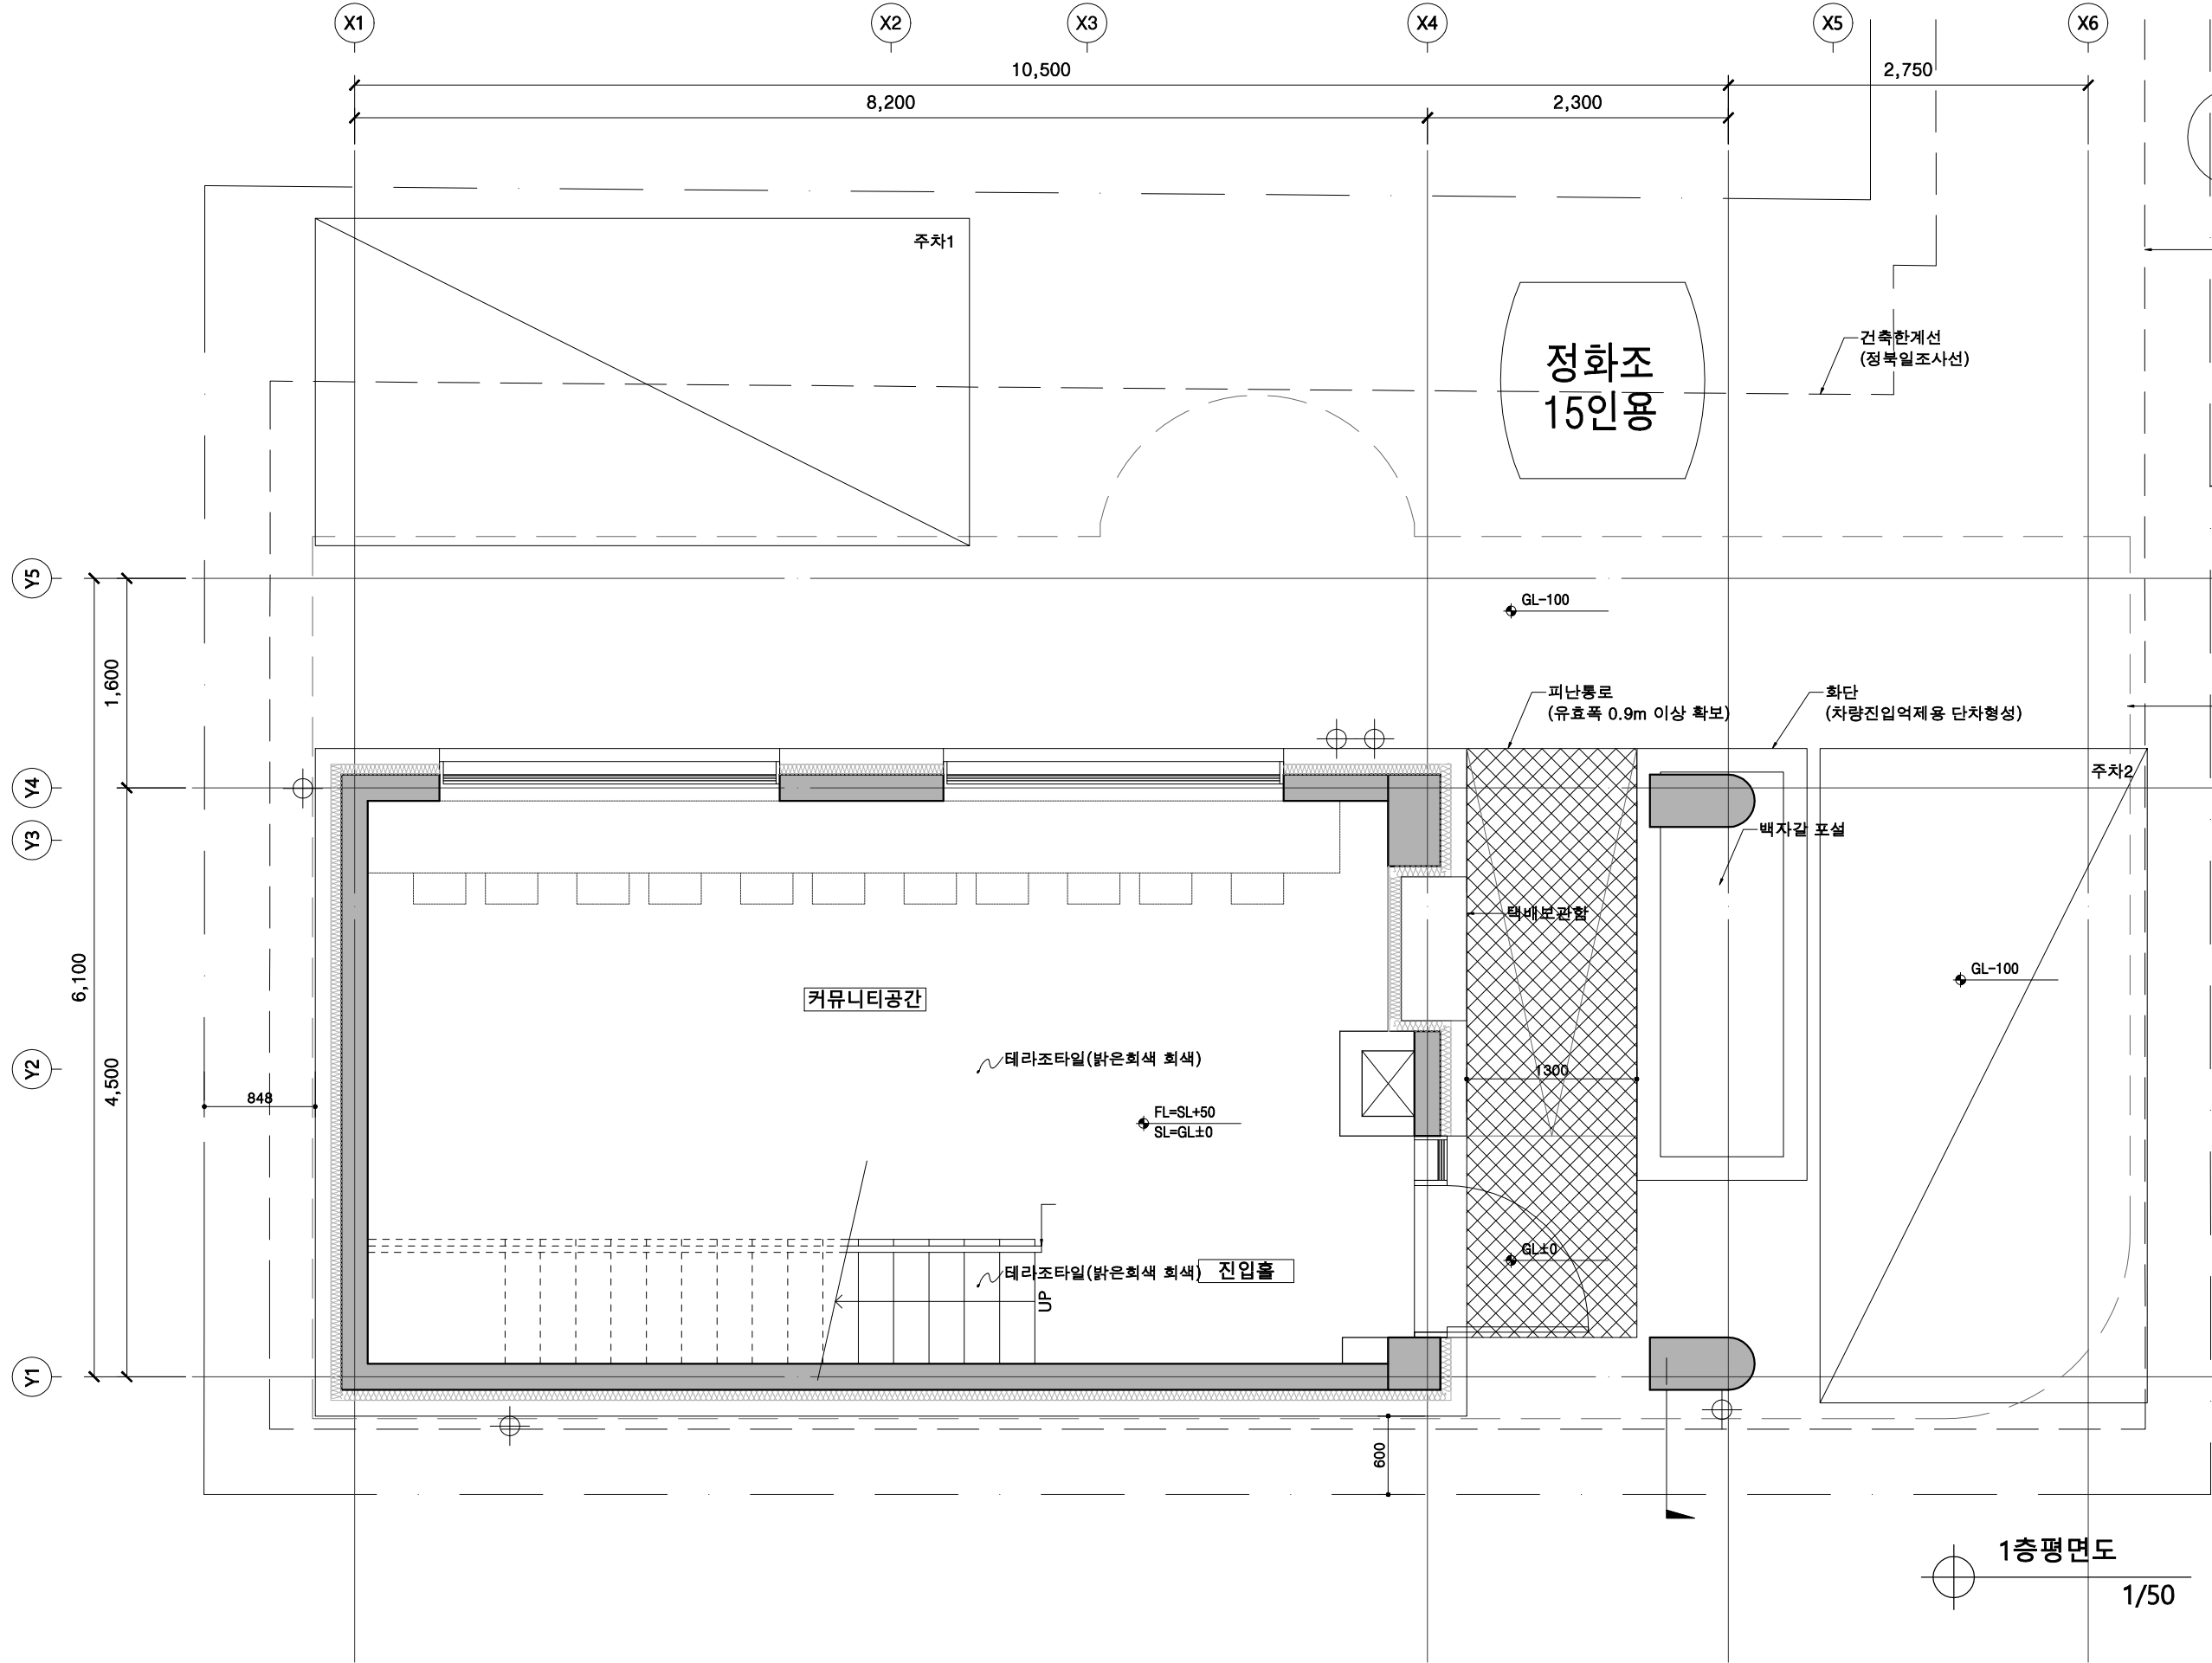

SH
서울주택도시공사

설계명 PROJECT TITLE

SH빈집 Bank
천호동 27-18
다가구주택 신축공사

주 기 NOTE

GL ±0 = EL +28.1
GL ±0 = SL ±0

설 계 변 경
DESCRIPTION OF REVISION

일 자 설계 검토 심사 승인

설 계 DRAWN 검토 CHECK

심 사 SUBMIT 승 인 APPROVE

축 척 SCALE
1/50


일 자 DATE

도면번호 SHEET NO
A-301

도면명 SUBJECT TITLE
1층 평면도

설계용역 PROJECT OFFICE

이 상 도 시 종 합
건축사사무소
昭普 SOBO
Architects
(주)소보건축사사무소

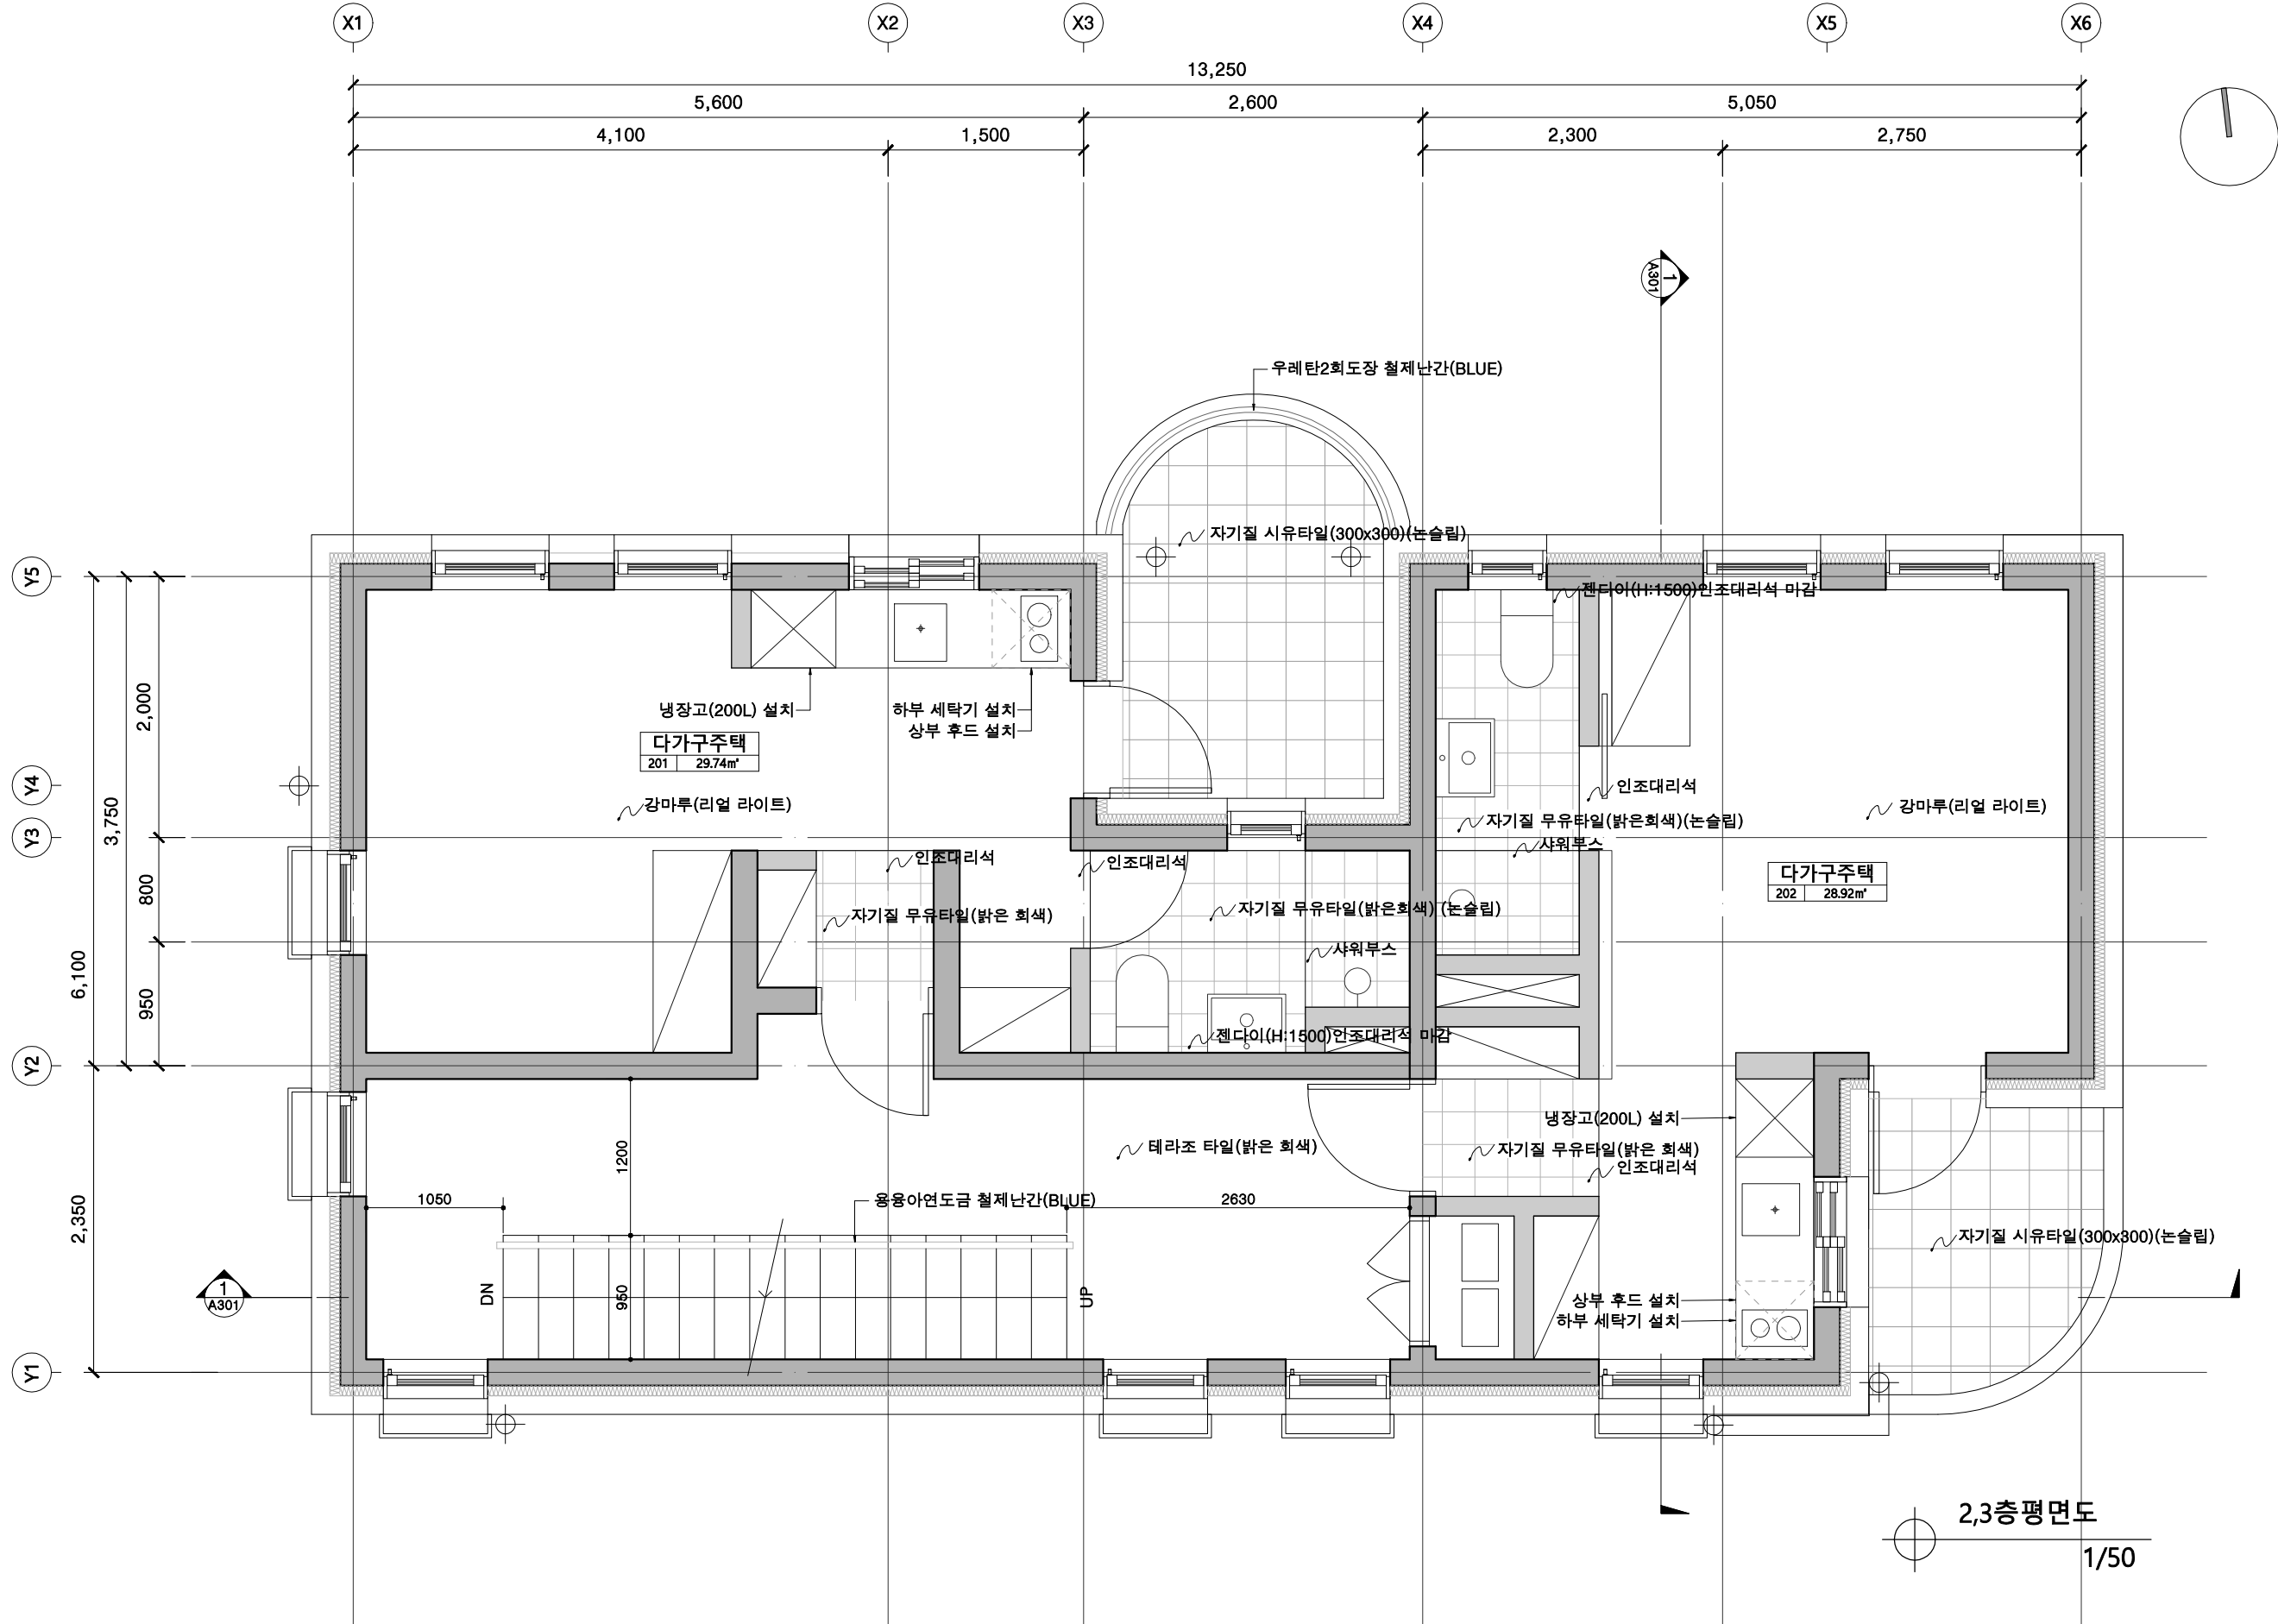

2,3층평면도
1/50

설 계 변 경				
DESCRIPTION OF REVISION				
일	자	설	계	검
토	심	사	승	인


설	계	DRAWN	검	토	CHECK
심	사	SUBMIT	승	인	APPROVE

축척 SCALE
1/50

일 자 DATE

도면번호 SHEET NO
A-302

도면명 SUBJECT TITLE
2,3층 평면도

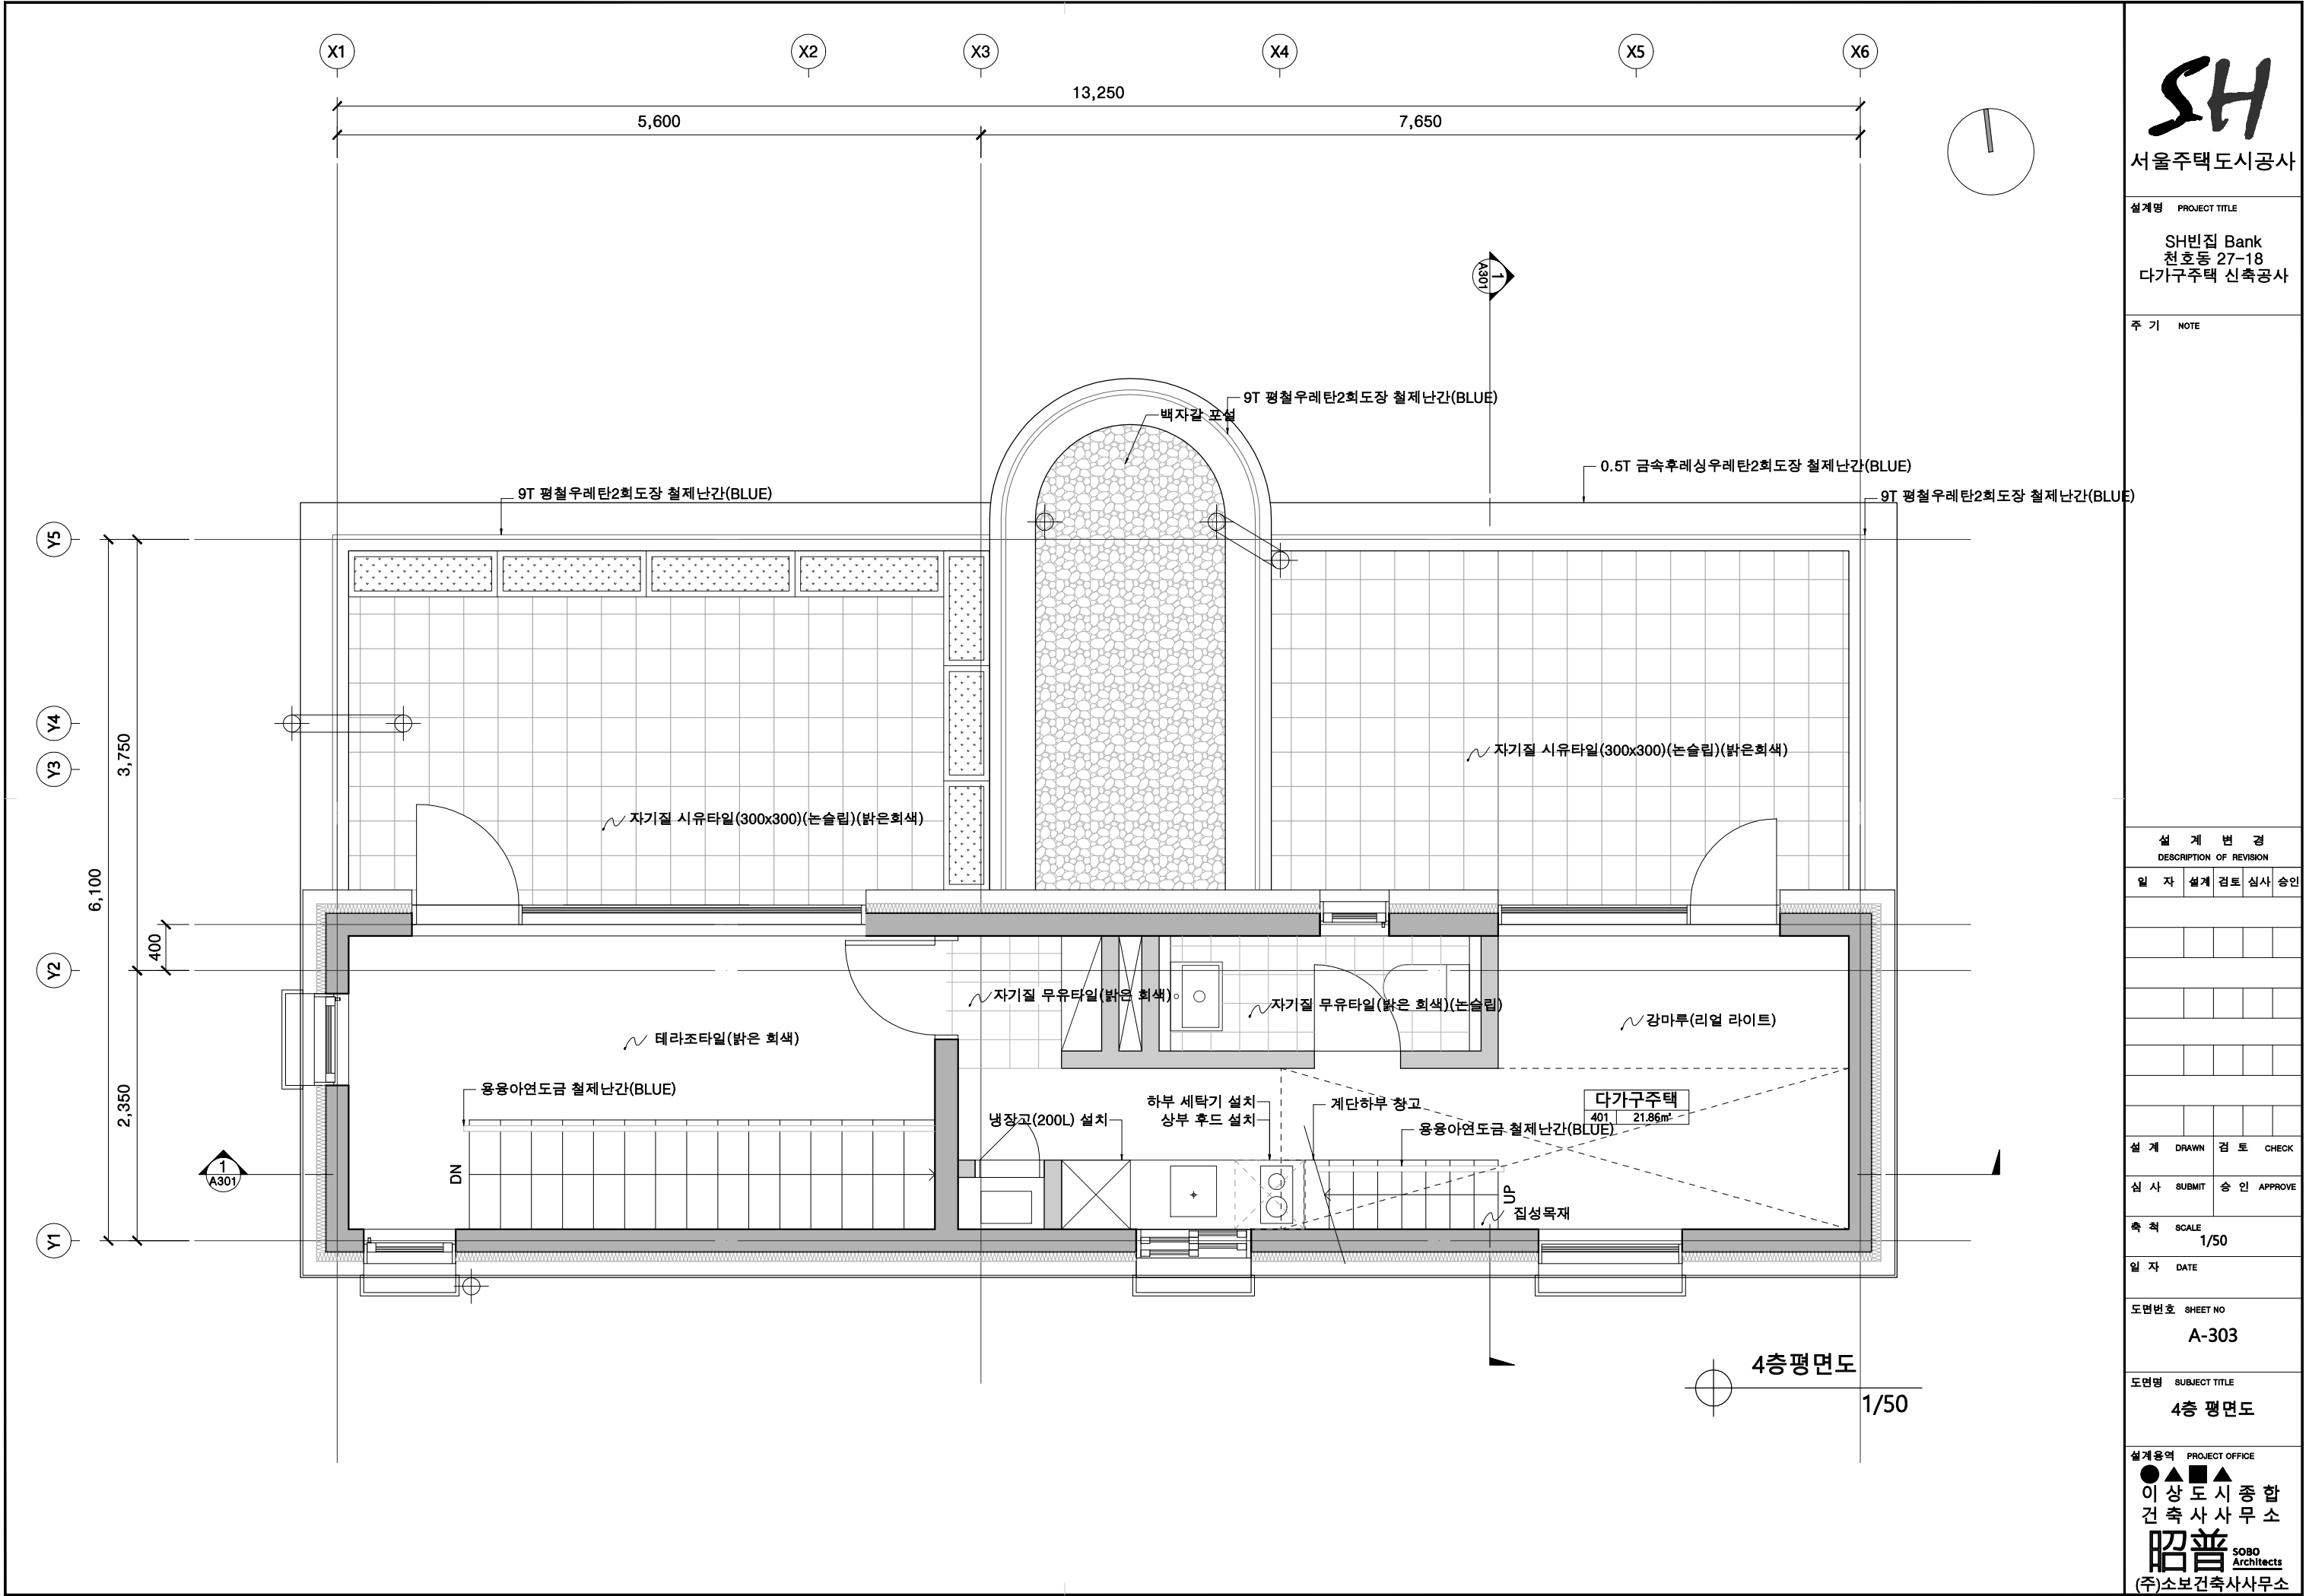

SH
서울주택도시공사

설계명 PROJECT TITLE
SH빈집 Bank
천호동 27-18
다가구주택 신축공사

주 기 NOTE

설 계 변 경
DESCRIPTION OF REVISION

일 자 설계 검토 심사 승인

설 계 DRAWN 검 토 CHECK

심 사 SUBMIT 승 인 APPROVE


축척 SCALE
1/50

일 자 DATE

도면번호 SHEET NO
A-303

도면명 SUBJECT TITLE
4층 평면도

설계용역 PROJECT OFFICE
이 상 도 시 종 합
건축사사무소
昭普 SOBO
Architects
(주)소보건축사사무소

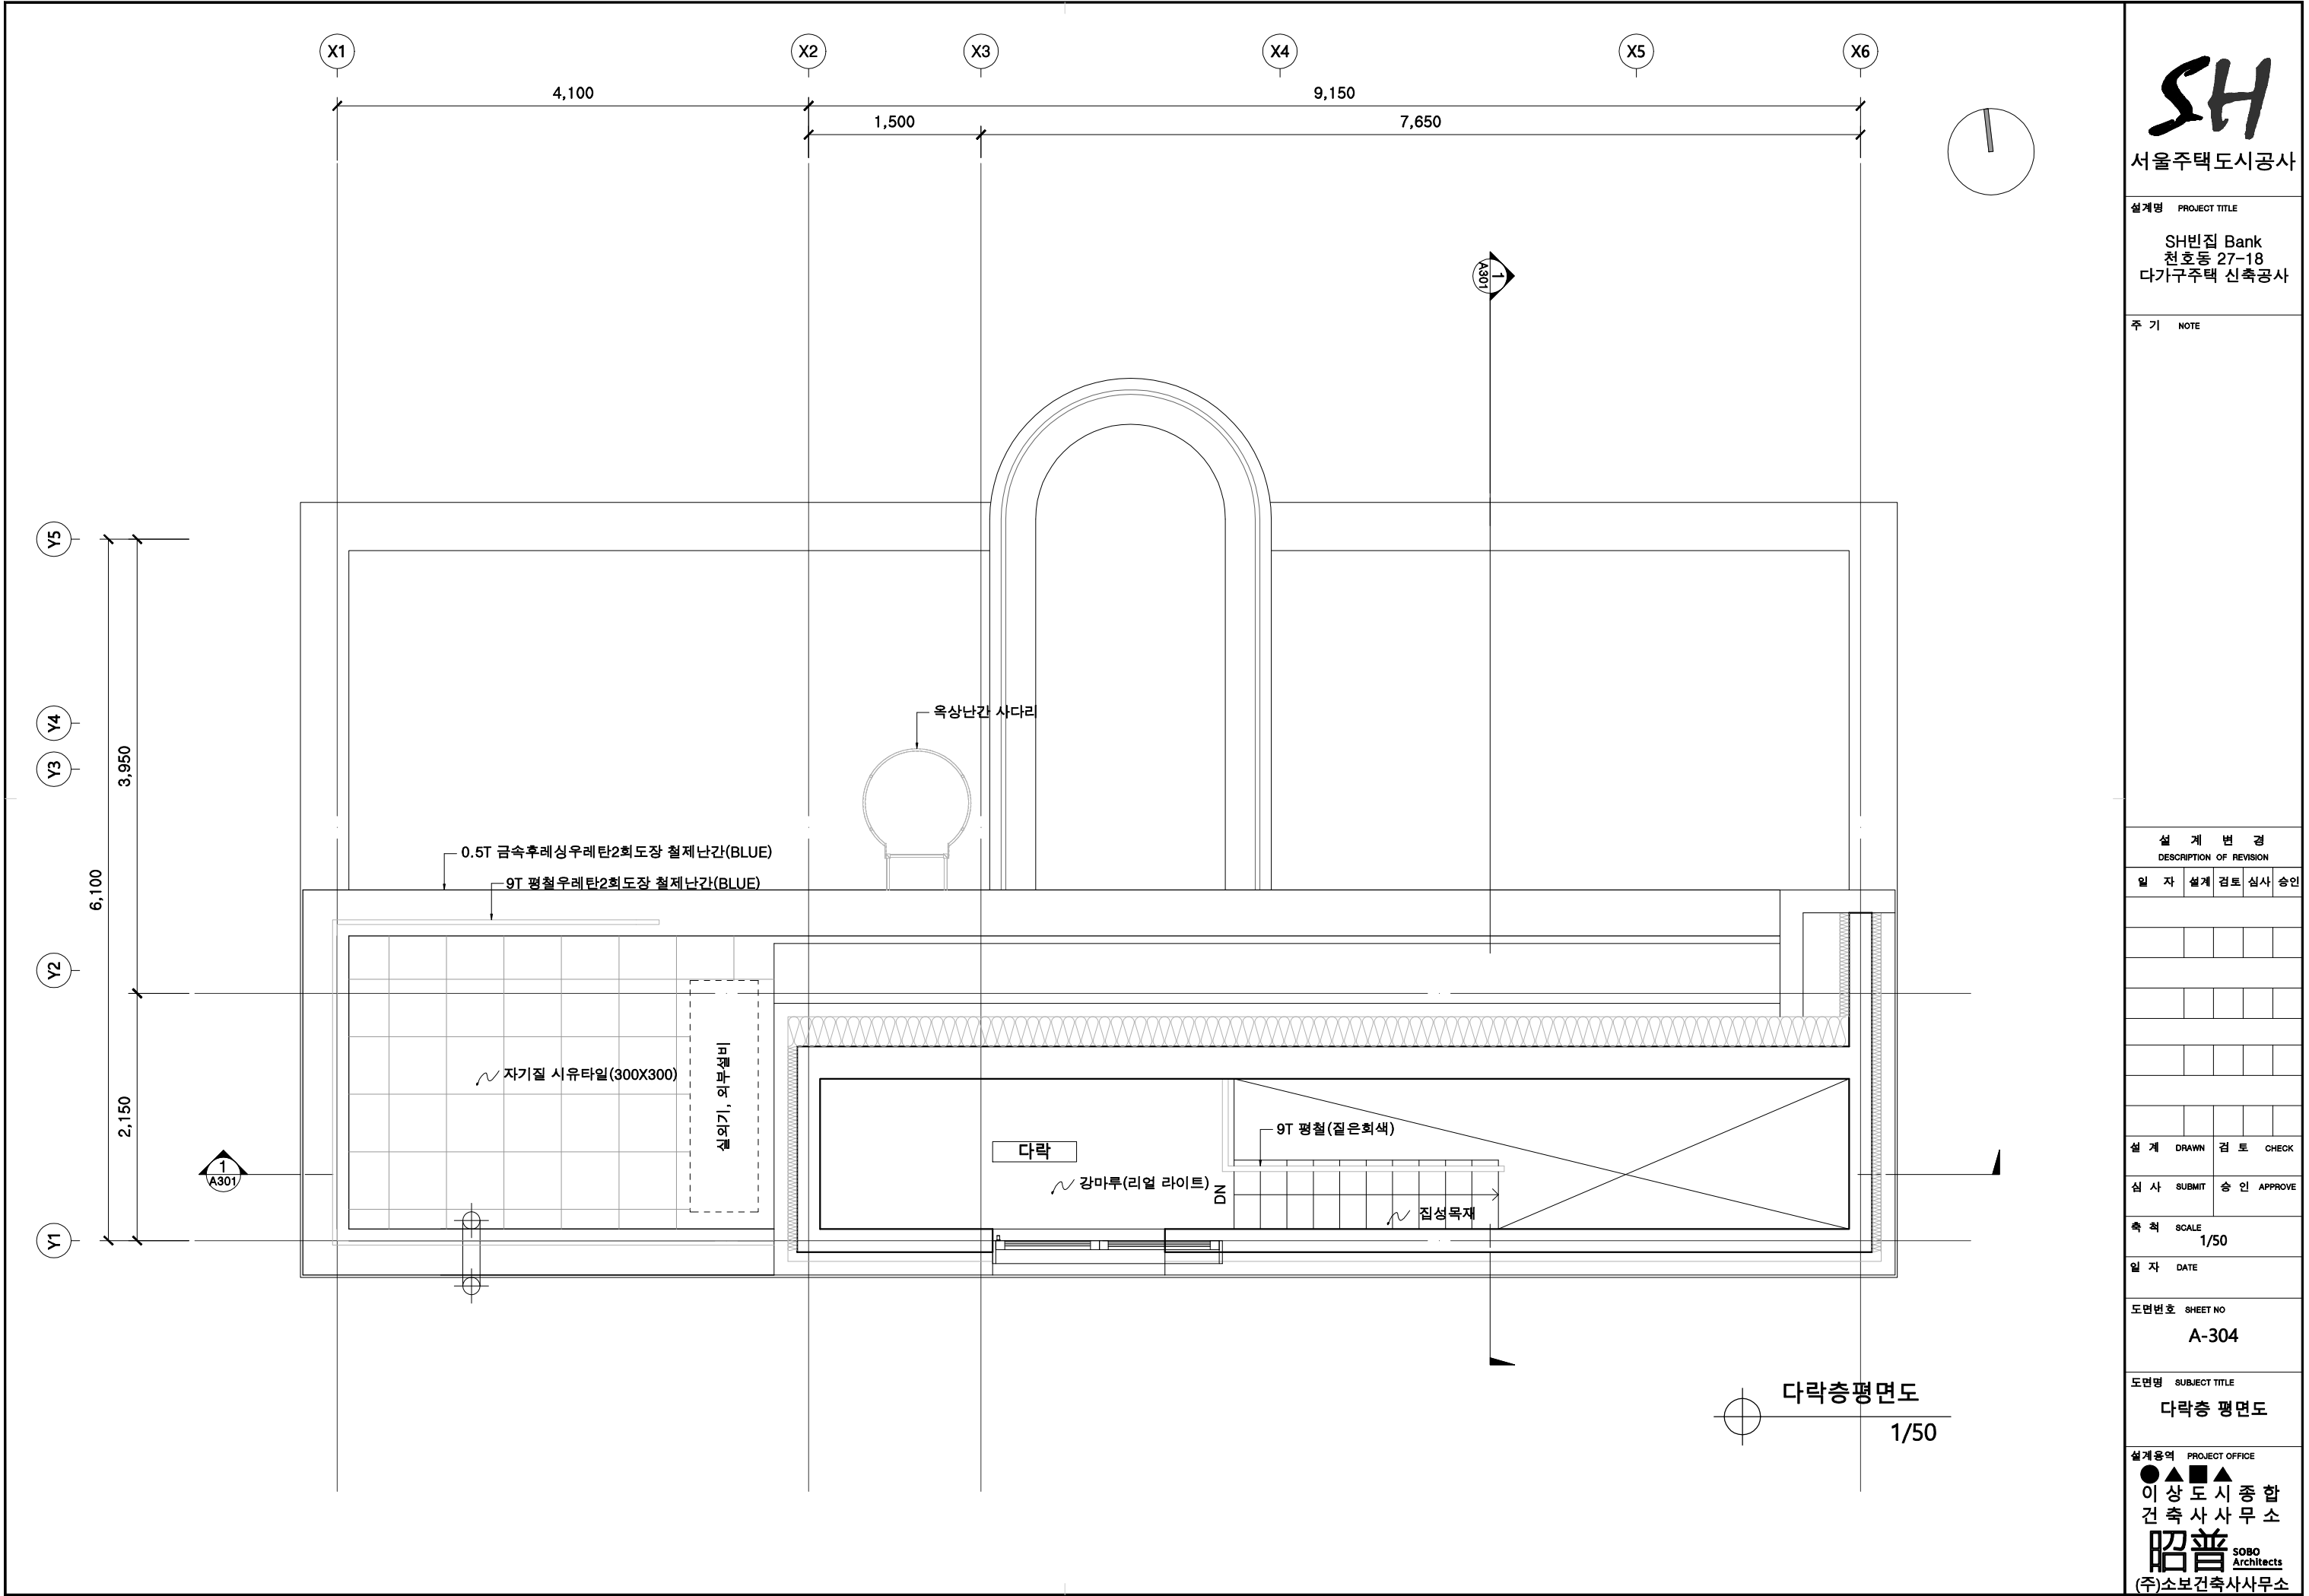

설 계 변 경 DESCRIPTION OF REVISION				
일	자	설 계	검 토	심 사


설 계	DRAWN	검 토	CHECK
심 사	SUBMIT	승 인	APPROVE

축 척 SCALE
1/50

일 자 DATE

도면번호 SHEET NO
A-304

도면명 SUBJECT TITLE
다락층 평면도

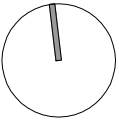

SH

서울주택도시공사

PROJECT TITLE

SH빈집 Bank
천호동 27-18
다가구주택 신축공사

주 기 NOTE

설 계 변 경
DESCRIPTION OF REVISION

일	자	설계	검토	심사	승인
---	---	----	----	----	----

설 계	DRAWN	검 토	CHECK
-----	-------	-----	-------

심 사 SUBMIT 승 인 APPROVE

측척 SCALE 1/50

일 자 DATE

도면번호 SHEET NO

A-305

도면명 SUBJECT TITLE

지붕층 평면도

설계용역 PROJECT OFFICE

이 상 도 시 종 합
건 축 사 사 무 소

昭普 **SOBO**
Architects

(주)소보건축사사무소



서울주택도시공사

설계명 PROJECT TITLE

SH빈집 Bank
천호동 27-18
다가구주택 신축공사

주 기 NOTE

설 계 변 경

DESCRIPTION OF REVISION

일 자 설계 검토 심사 승인

1. 현장 협의내용 반영

24.03.13

설 계 DRAWN 검토 CHECK

심 사 SUBMIT 승 인 APPROVE

축 척 SCALE
1/100

일 자 DATE

도면번호 SHEET NO

A-401

도면명 SUBJECT TITLE

종단면도

설계용역 PROJECT OFFICE

이 상 도 시 중 합
건축사사무소
昭普 SOBO
Architects
(주)소보건축사사무소

▼최고높이

▼지붕 SL
=GL +13,400

▼다락 SL
=GL +11,600

▼지상 4층 SL
=GL +8,700

▼지상 3층 SL
=GL +5,750

▼지상 2층 SL
=GL +2,800

▼지상 1층 SL
=GL ±0

X1 X2 X3 X4 X5 X6

13,250

8,200

5,050

4,100

1,200


300

2,600

2,300

2,750

인접대지경계선

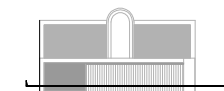

지정세 리얼링크 (돌출아름)
T8 환기이격재
T12 내수합판 위 T2 부직포 방수시트
□-40×40 아연도강판 프레임 2겹
THK130 PF보드 (준불연)
(열관류율 0.240 W/m² 이하)
구체 도막방수

THK0.5 급속후레싱
-에폭시본드
-우레탄도막방수
THK100 무근콘크리트 (와이어메쉬)
THK130 PF보드 (준불연)
(열관류율 0.240 W/m² 이하)
점투성 액체방수

자기질 시유타일(300X300)
-도막방수
-점투성 액체방수

0.5T 급속후레싱우레탄2회도장 철제난간(BLUE)

노출형 우레탄 도막방수
THK150 무근콘크리트
점투성 액체방수

다락
THK10 강마루
THK40경향기포콘크리트900
THK40불연물발
THK30 층간단열재

실크 천장지(천환경)

목재천정물(라왕 30x30)
T8, 6색고보드2겹
실크천장지

401호

THK10 강마루
THK120경향기포콘크리트(온수파이프)
THK40불연물발
THK30 층간단열재

THK80 PF보드 (준불연)
(열관류율 0.240 W/m² 이하)
아연도강판틀
THK9 포세린타일

THK80 PF보드 (준불연)
(열관류율 0.240 W/m² 이하)
아연도강판틀
THK18 포세린타일

THK10 강마루
THK40경향기포콘크리트
THK40불연물발
THK30 층간단열재

302호

목재천정물(라왕 90X30)
T9, 5색고보드2겹
실크천장지

THK80 PF보드 (준불연)
(열관류율 0.240 W/m² 이하)
THK60 공간
THK90 점토벽돌 치장쌓기

자기질 시유타일(300X300)
THK41 무근콘크리트
-도막방수
-점투성 액체방수

THK130 PF보드
급속고장중 뜯짜기
급속후레싱

THK80 PF보드(준불연)
(열관류율 0.240 W/m² 이하)
THK50 공간
THK90 점토벽돌
(치장쌓기)

THK9 테라조타일
THK11 불연물발

THK10 강마루
THK40경향기포콘크리트
THK40불연물발(온수파이프)
THK30 층간단열재

202호

THK10 강마루
THK40경향기포콘크리트
THK40불연물발(온수파이프)
THK30 층간단열재

THK80 PF보드 (준불연)
(열관류율 0.240 W/m² 이하)
THK60 공간
THK90 점토벽돌 치장쌓기

자기질 시유타일(300X300)
THK41 무근콘크리트
-도막방수
-점투성 액체방수

THK90 PF보드 (준불연)
(열관류율 0.240 W/m² 이하)
급속고장중 뜯짜기
급속후레싱

THK80 PF보드 (준불연)
(열관류율 0.240 W/m² 이하)
아연도강판틀
THK18 포세린타일

THK9 테라조타일
THK11 불연물발

목재천정물(라왕 30X30)
T9, 5색고보드2겹
내부용수성페인트

진입홀

T25 테라조타일
T25 불연물발
점투성 구체방수

주차장

THK400 온돌기초
THK220 방출법 보온판
(열관류율 0.200 W/m² 이하)
THK60 비빔콘크리트
THK0.02 필름 2겹
THK200 잠식다짐

종단면도

1/100



서울주택도시공사

설계명 PROJECT TITLE

SH빈집 Bank
천호동 27-18
다가구주택 신축공사

주 기 NOTE

설 계 변 경
DESCRIPTION OF REVISION

일 자	설 계	검 토	심 사	승 인
-----	-----	-----	-----	-----

1. 현장 협의내용 반영

24.03.13

2. 다락 지붕 형태 변경

24.05.02

설 계	DRAWN	검 토	CHECK
-----	-------	-----	-------

심 사	SUBMIT	승 인	APPROVE
-----	--------	-----	---------

축 척 SCALE
1/100

일 자 DATE

도면번호 SHEET NO


A-402

도면명 SUBJECT TITLE

횡단면도 1

설계용역 PROJECT OFFICE

이 상 도 시 종 합
건 축 사 사 무 소
昭普 SOBO
Architects
(주)소보건축사사무소

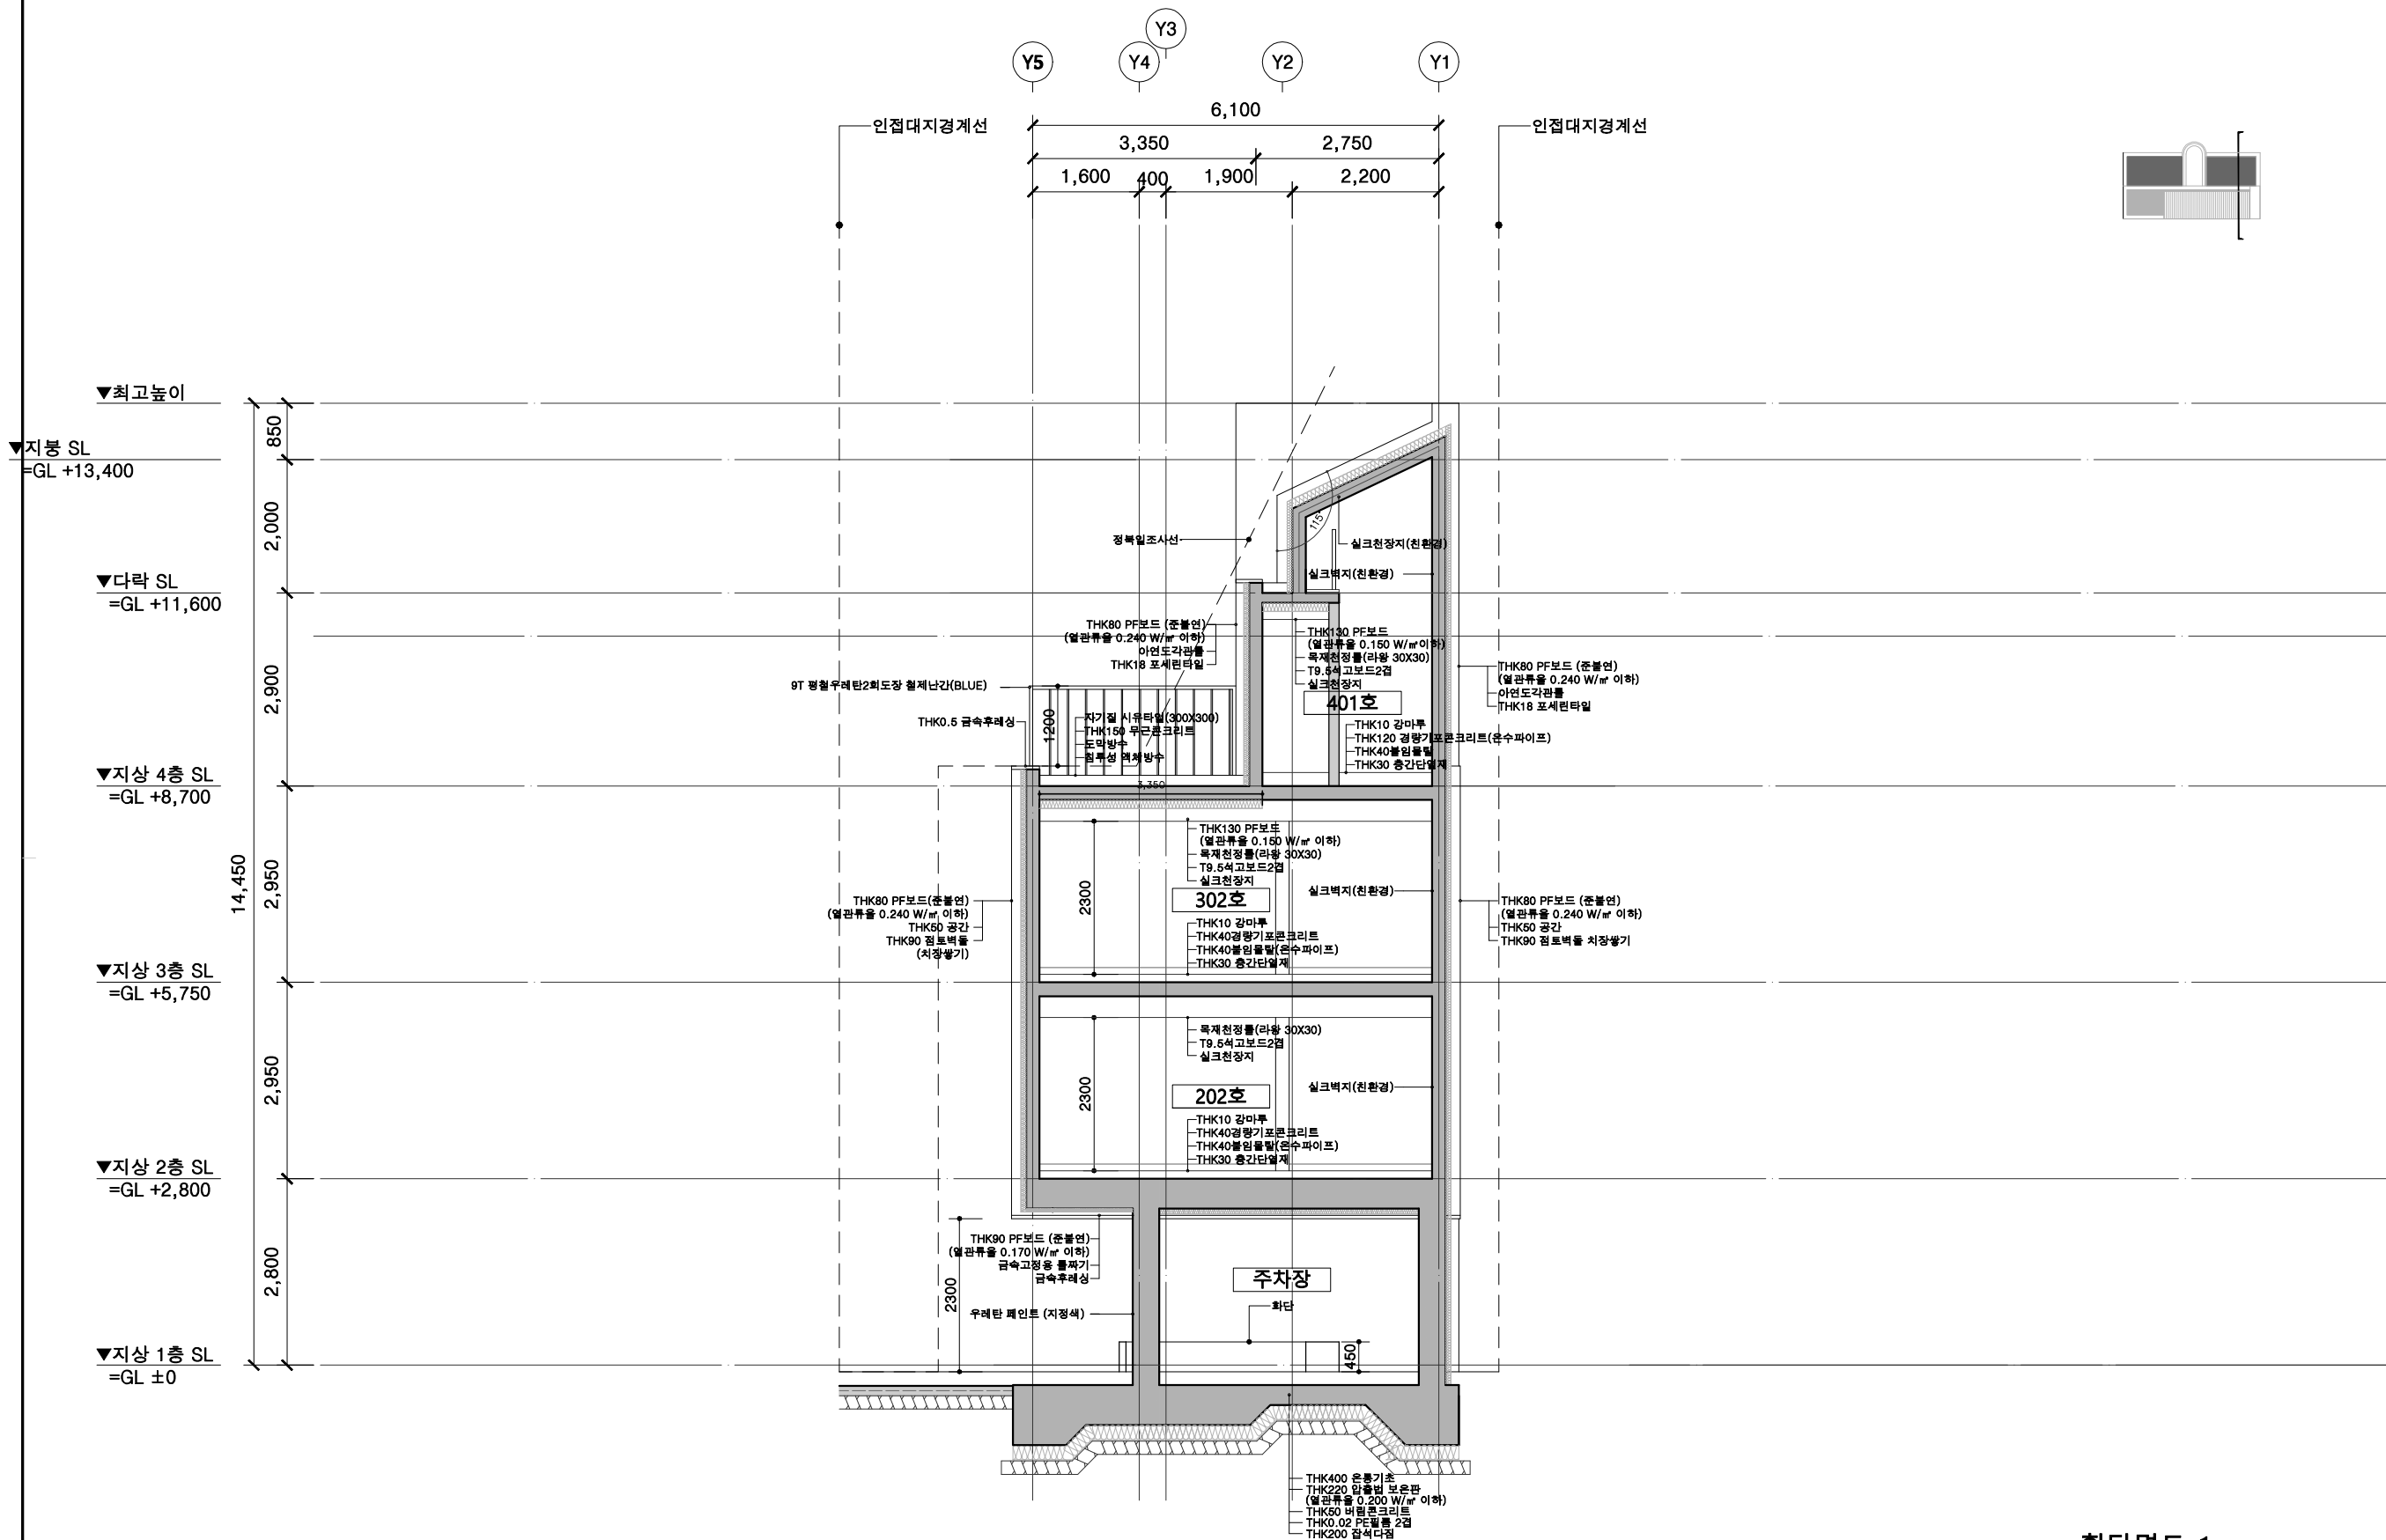

횡단면도-1
1/100



서울주택도시공사

설계명 PROJECT TITLE

SH빈집 Bank
천호동 27-18
다가구주택 신축공사

주 기 NOTE

설 계 변 경
DESCRIPTION OF REVISION

일 자 설계 검토 심사 승인

1. 현장 협의내용 반영

24.03.13

2. 다락 지붕 형태 변경

24.05.02

설 계 DRAWN 검토 CHECK

심 사 SUBMIT 승 인 APPROVE

축척 SCALE
1/100

일 자 DATE

도면번호 SHEET NO


A-403

도면명 SUBJECT TITLE

횡단면도 2

설계용역 PROJECT OFFICE

이 상 도 시 종 합
건축사사무소
昭普 SOBO
Architects
(주)소보건축사사무소

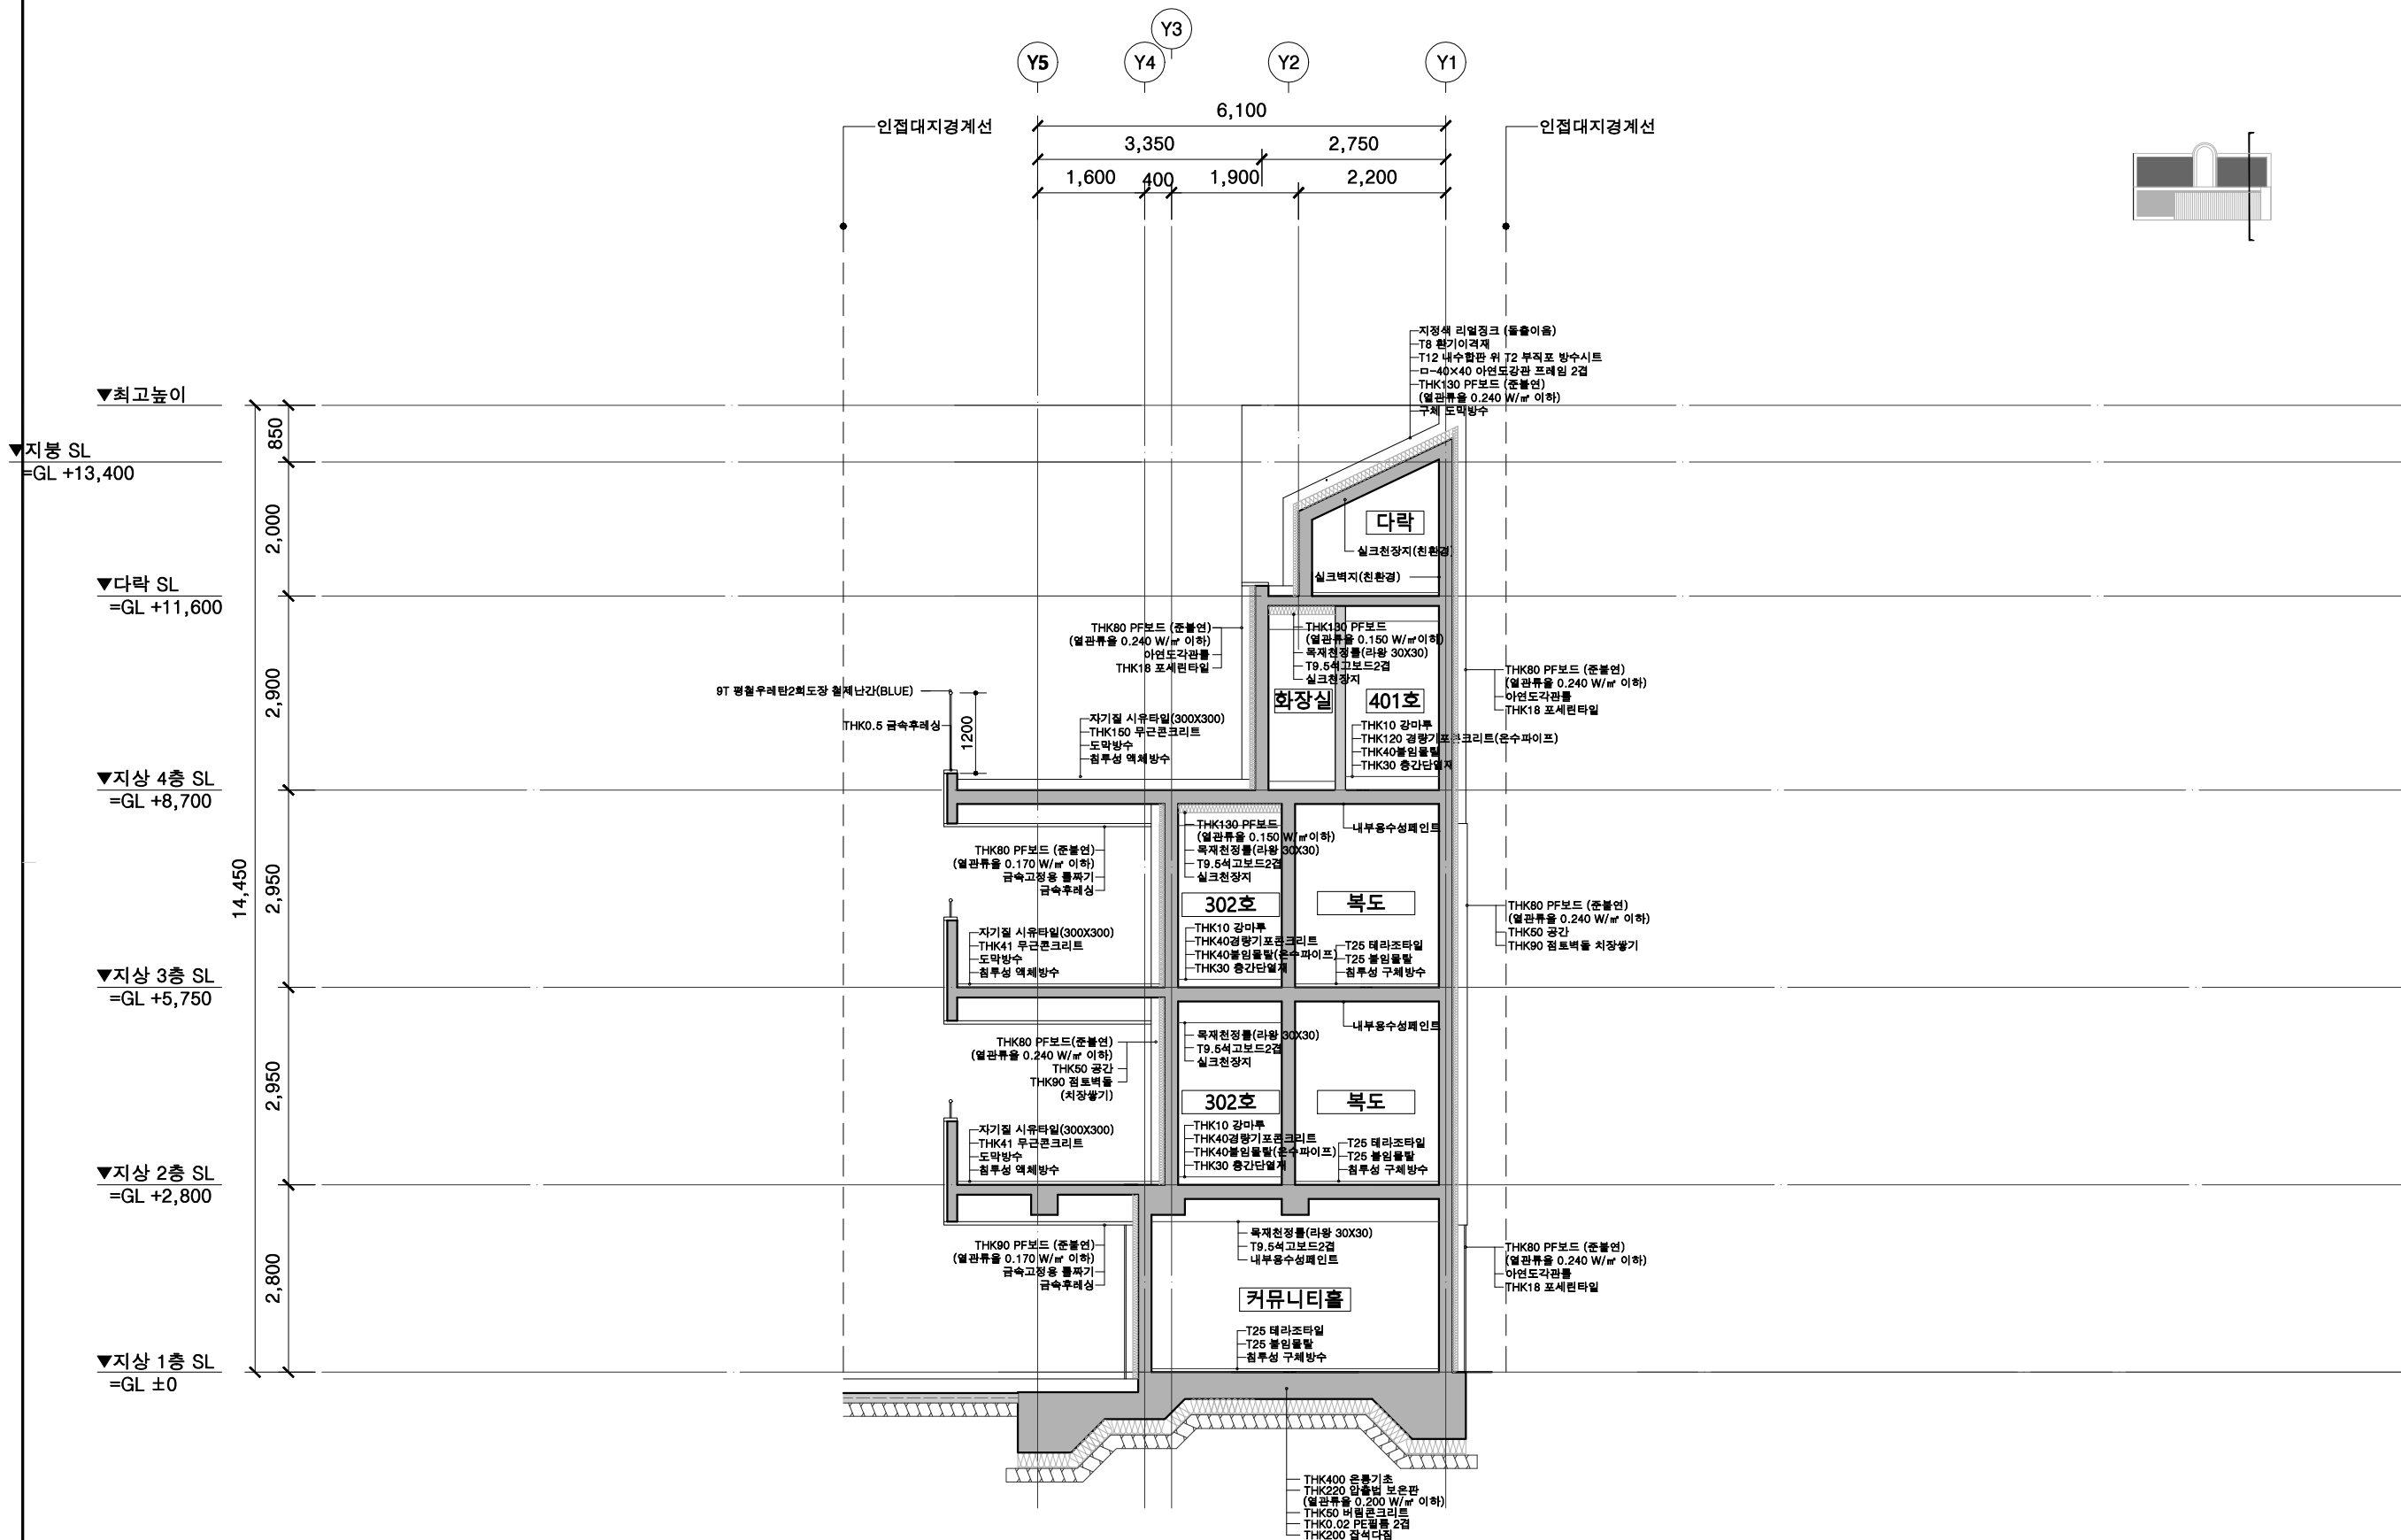

횡단면도-2

1/100