



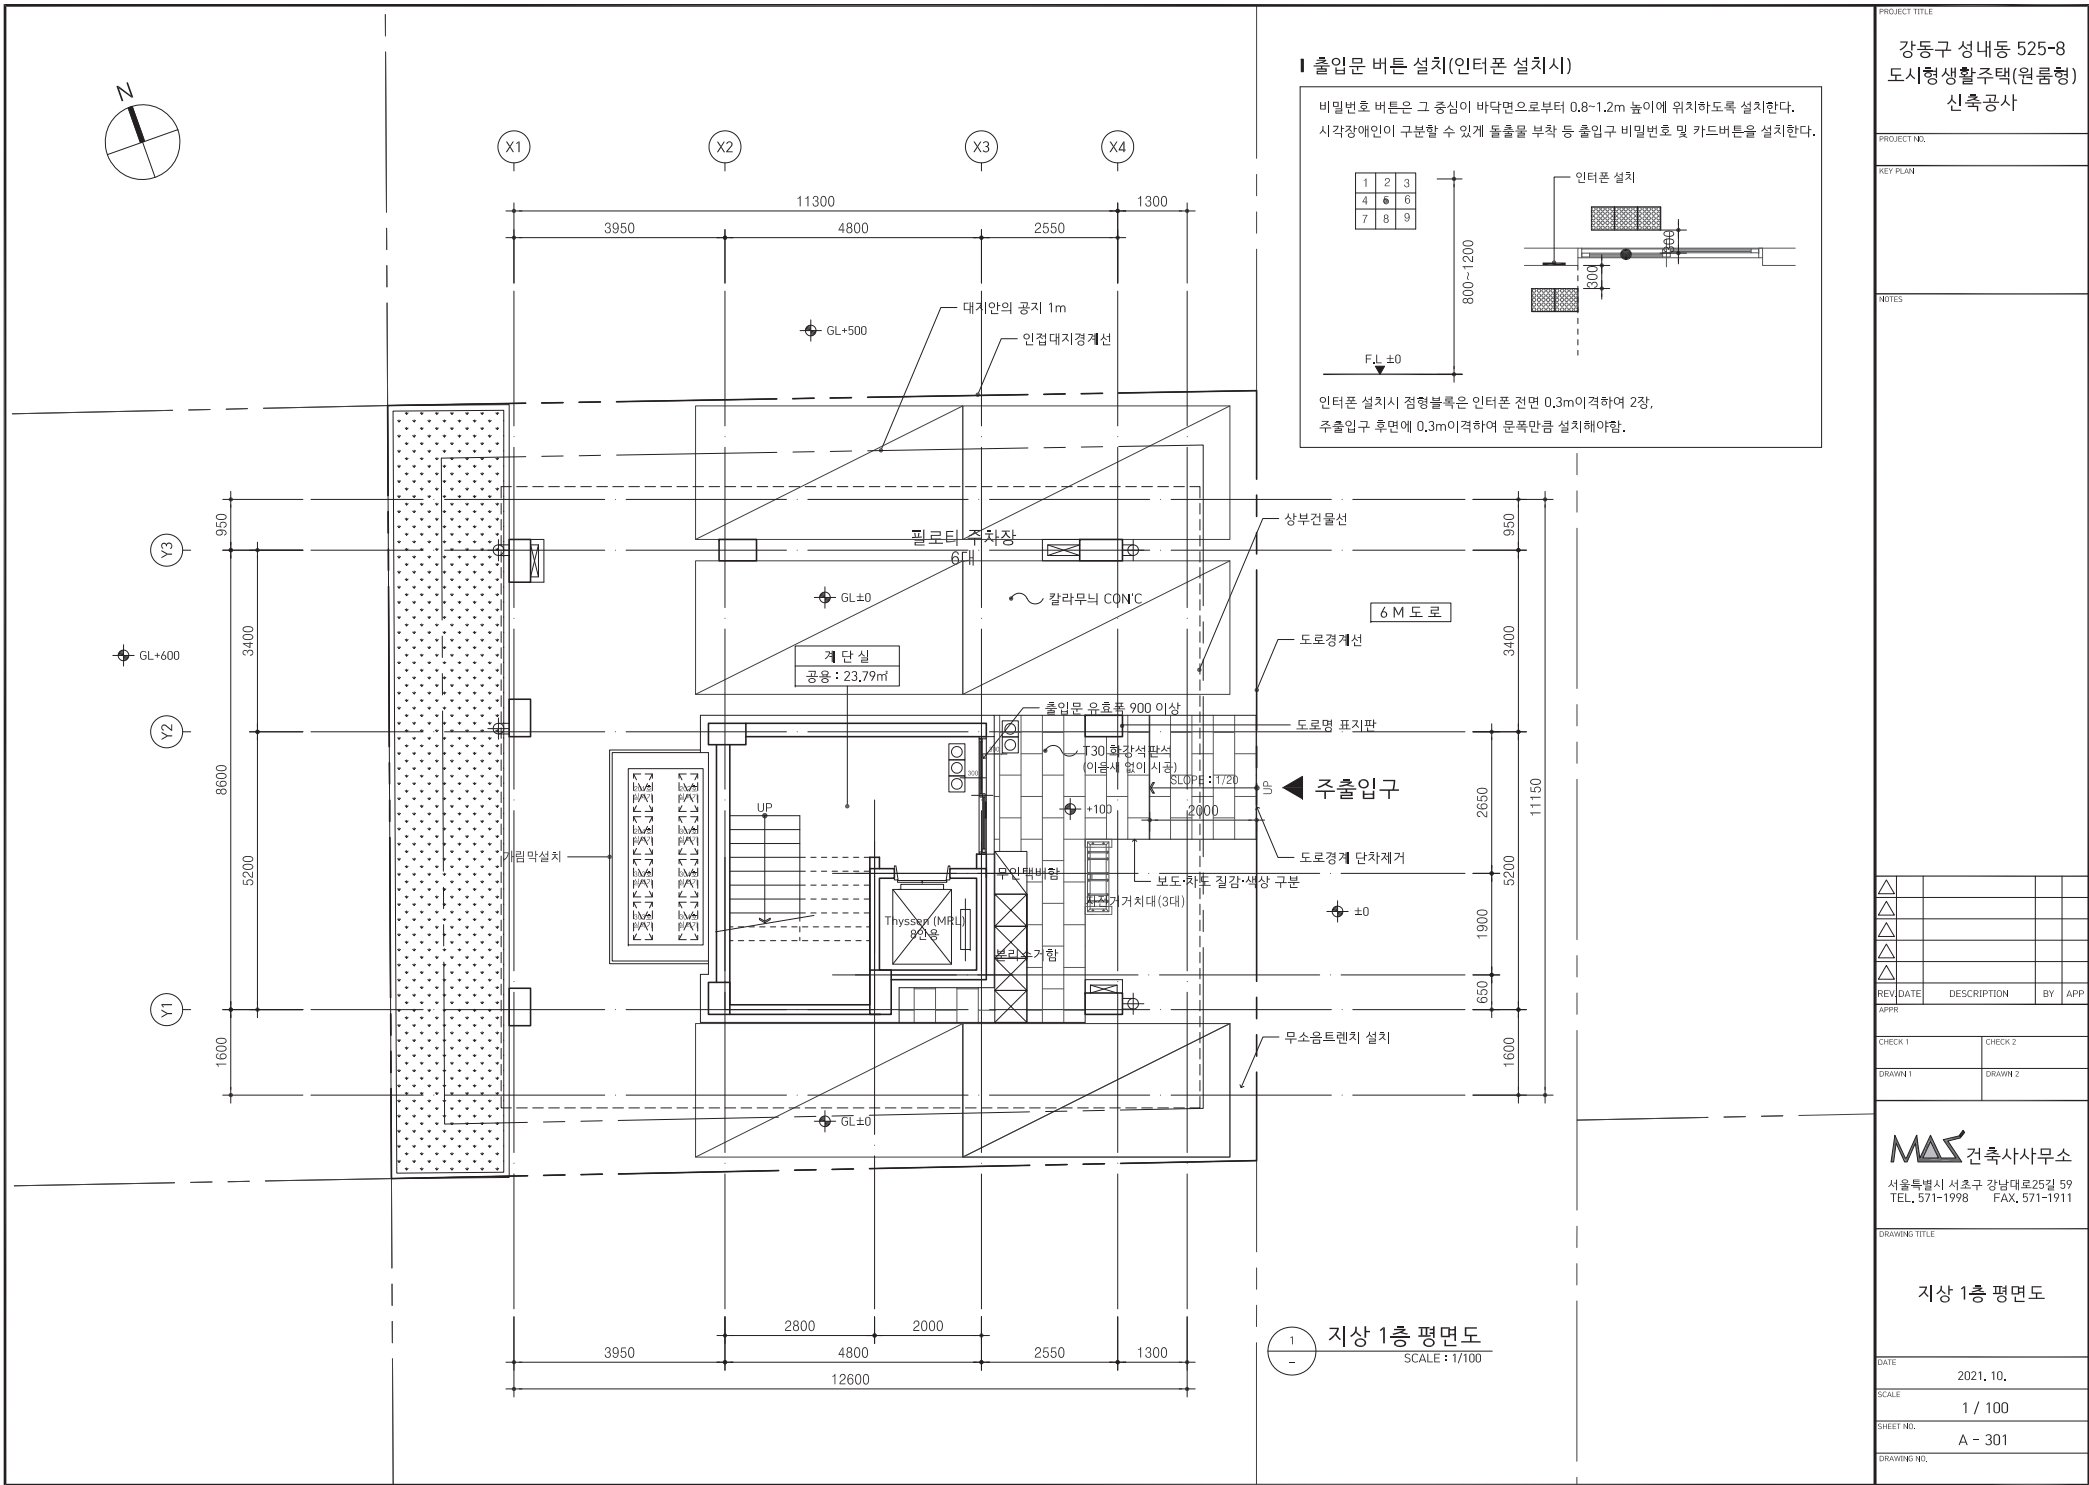

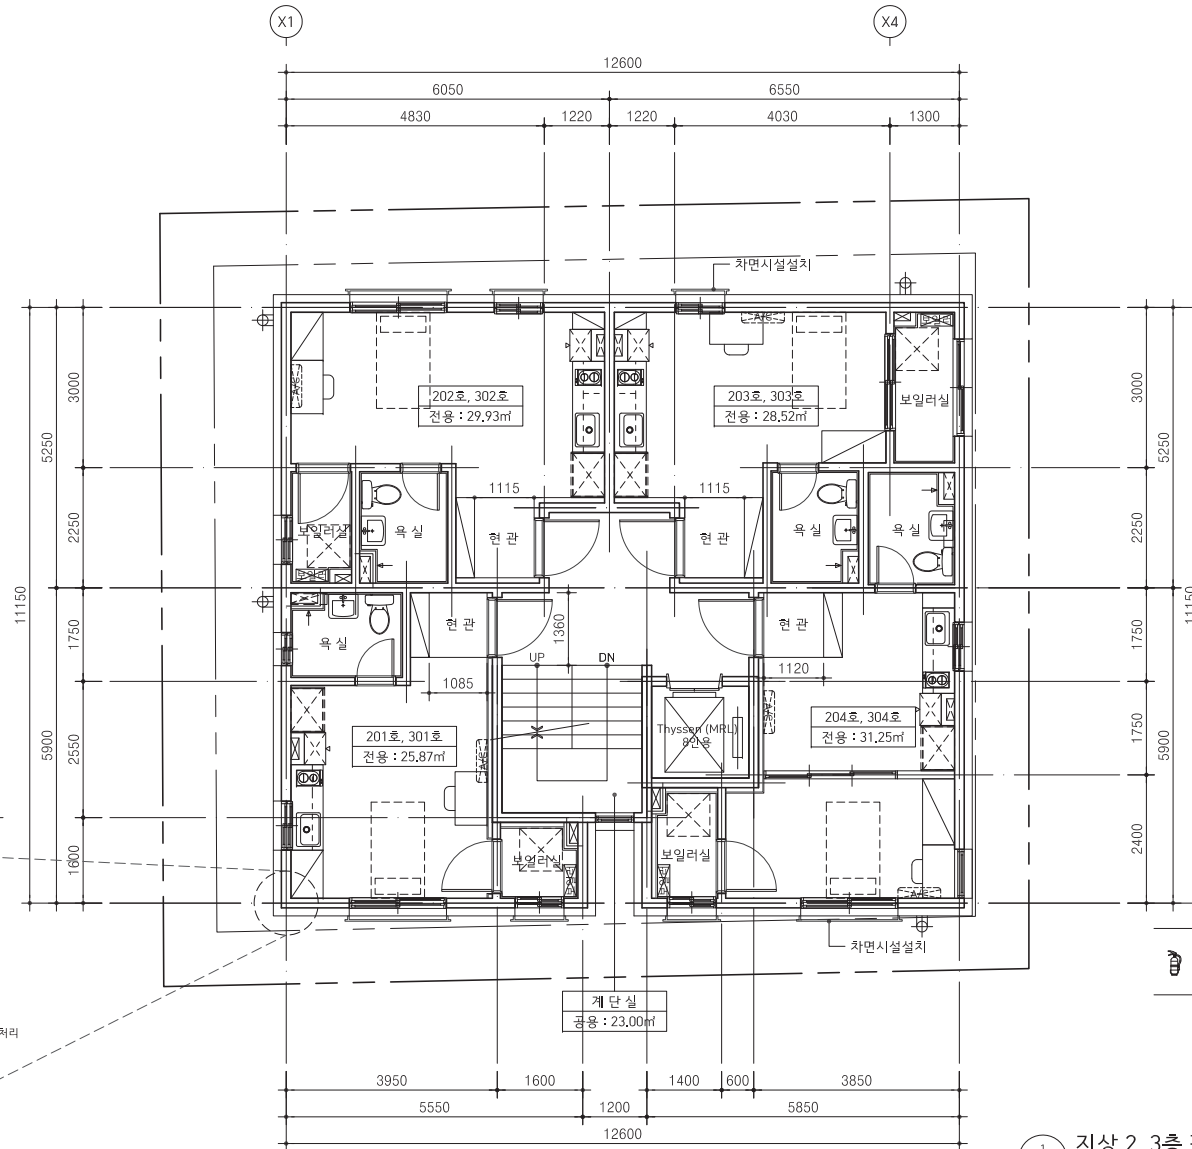

	A,B,C 분말소화기
	A,B,C DRY CHEMICAL
	EXTINGUISHER
	(3.3KG) x 4 EA

1 지상 2, 3층 평면도
SCALE : 1/100

강동구 성내동 525-8
도시형생활주택(원룸형)
신축공사

PROJECT NO.

KEY PLAN

NOTES

△			
△			
△			
△			

REV.	DATE	DESCRIPTION	BY	APP.
------	------	-------------	----	------

CHECK 1	CHECK 2
DRAWN 1	DRAWN 2

MAX 건축사사무소
서울특별시 서초구 강남대로25길 59
TEL. 571-1998 FAX. 571-1911

DRAWING TITLE


지상 2, 3층 평면도

DATE 2021. 10.

SCALE 1 / 100

SHEET NO. A - 302

DRAWING NO.

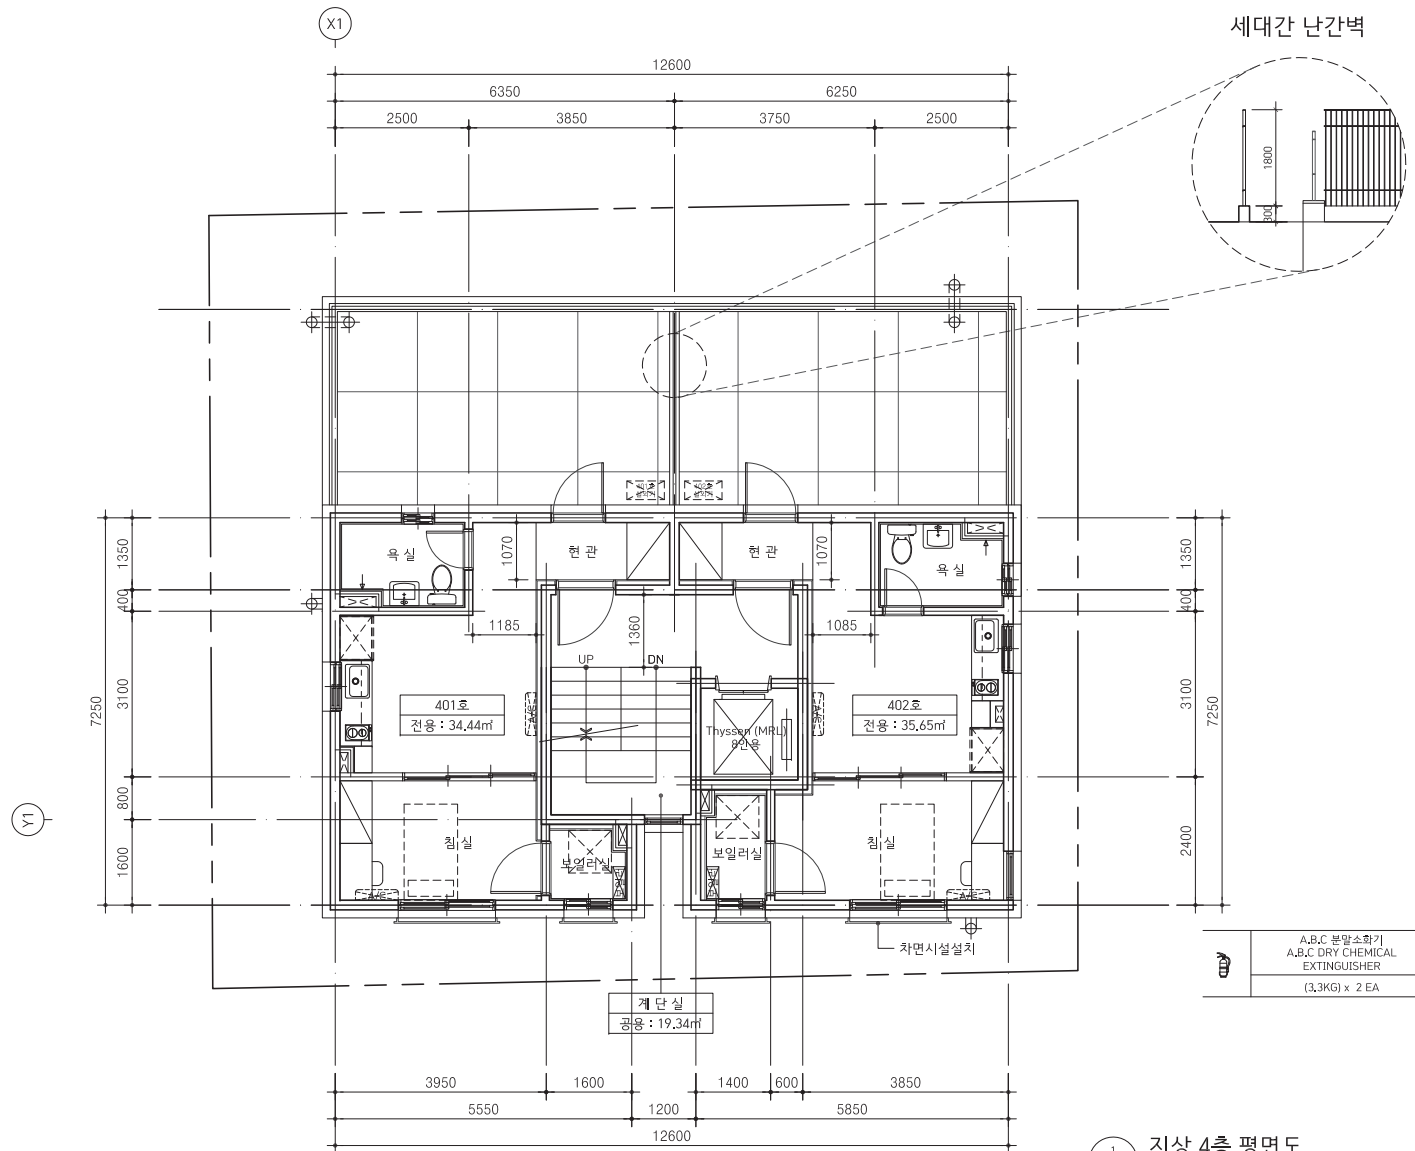

지상 4층 평면도
SCALE : 1/100

강동구 성내동 525-8
도시형생활주택(원룸형)
신축공사

PROJECT NO.

KEY PLAN

NOTES

△				
△				
△				
△				

REV.	DATE	DESCRIPTION	BY	APP.


CHECK 1	CHECK 2
DRAWN 1	DRAWN 2

MAX 건축사사무소
서울특별시 서초구 강남대로25길 59
TEL. 571-1998 FAX. 571-1911

DRAWING TITLE

지상 4층 평면도

DATE 2021. 10.
SCALE 1 / 100
SHEET NO. A - 303
DRAWING NO.

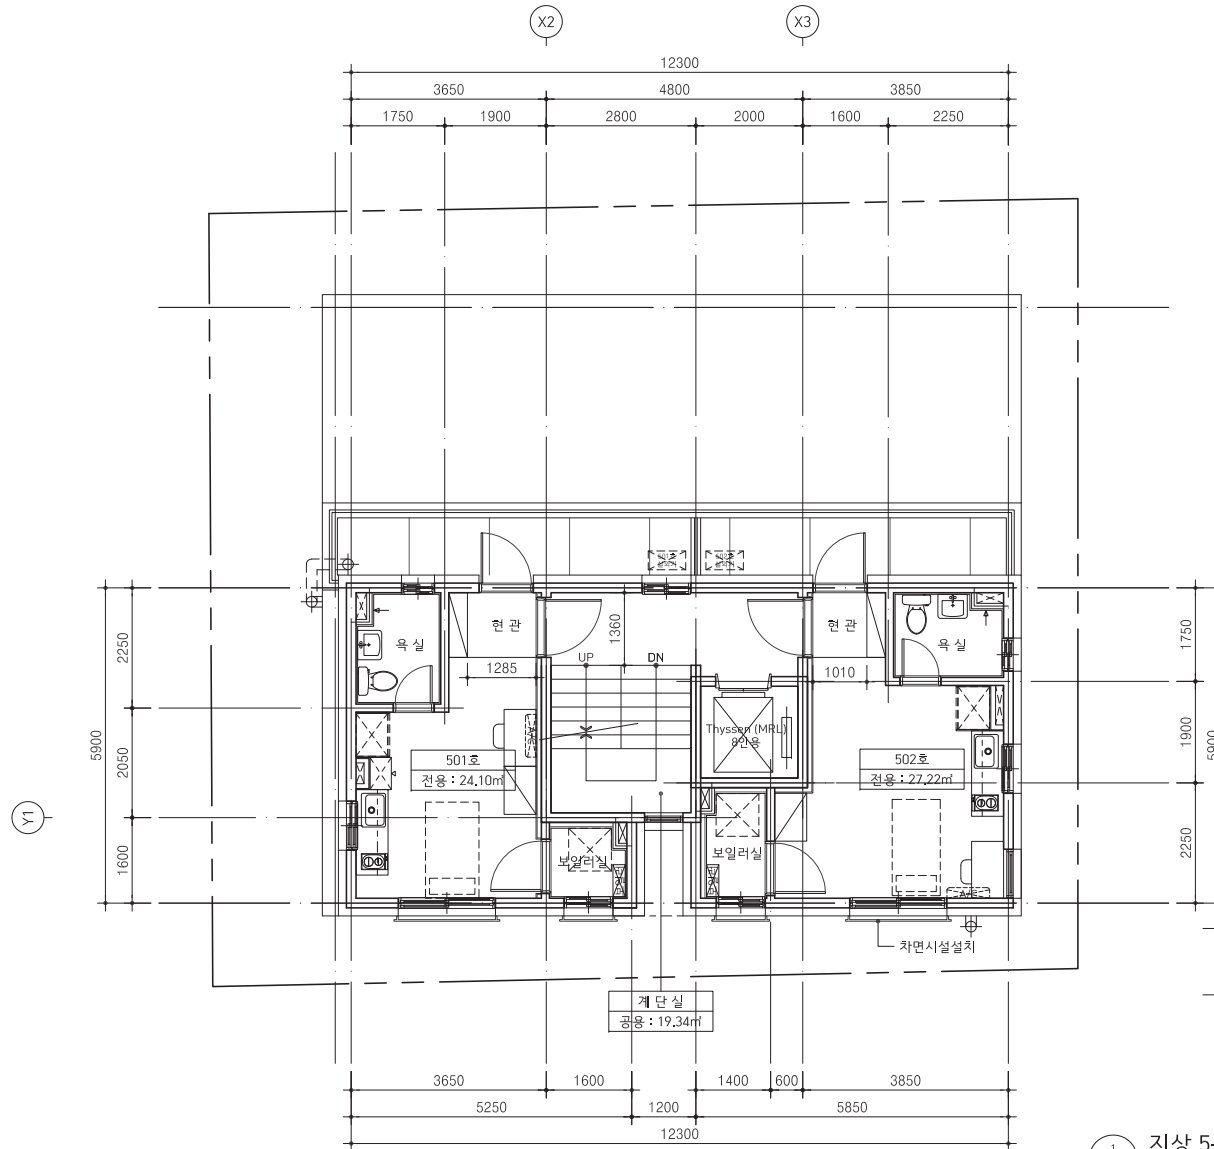

	A,B,C 분말소화기
	A,B,C DRY CHEMICAL
	EXTINGUISHER
	(3.3KG) x 2 EA

지상 5층 평면도
SCALE : 1/100

PROJECT TITLE
강동구 성내동 525-8
도시형생활주택(원룸형)
신축공사

PROJECT NO.

KEY PLAN

NOTES

△				
△				
△				
△				

REV.	DATE	DESCRIPTION	BY	APP.
APPR.				


CHECK 1	CHECK 2
DRAWN 1	DRAWN 2

MAS 건축사사무소
서울특별시 서초구 강남대로25길 59
TEL. 571-1998 FAX. 571-1911


DRAWING TITLE

지상 5층 평면도

DATE	2021. 10.
SCALE	1 / 100
SHEET NO.	A - 304
DRAWING NO.	

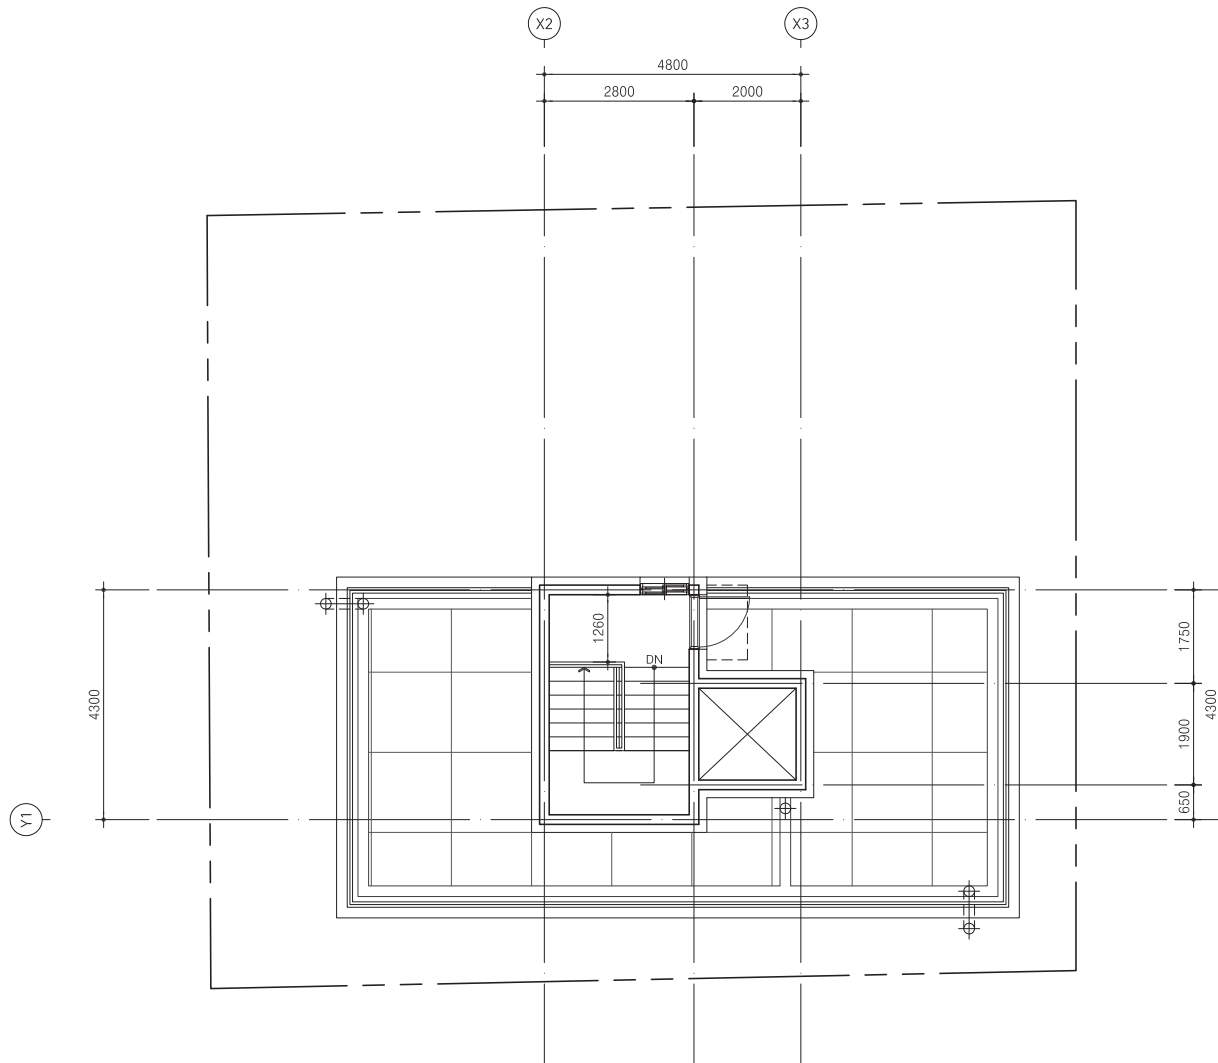

1 옥탑층 평면도
SCALE : 1/100

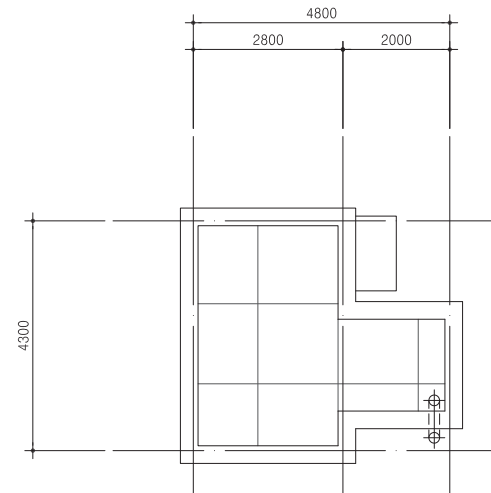

2 옥탑지붕 평면도
SCALE : 1/100

강동구 성내동 525-8
도시형생활주택(원룸형)
신축공사

PROJECT NO.

KEY PLAN

NOTES

△				
△				
△				
△				
REV.	DATE	DESCRIPTION	BY	APP.

CHECK 1	CHECK 2
DRAWN 1	DRAWN 2

MAS 건축사사무소
서울특별시 서초구 강남대로25길 59
TEL. 571-1998 FAX. 571-1911

DRAWING TITLE

옥탑층 평면도

DATE 2021. 10.

SCALE 1 / 100

SHEET NO. A - 305

DRAWING NO.



DRAWING NO.



1 배면도
SCALE : 1/100

2 좌측면도
SCALE : 1/100

PROJECT TITLE				
강동구 성내동 525-8 도시형생활주택(원룸형) 신축공사				
PROJECT NO.				
KEY PLAN				
NOTES				
REV. DATE DESCRIPTION BY APPR.				
CHECK 1 CHECK 2				
DRAWN 1 DRAWN 2				
DRAWING TITLE				
배면도 및 좌측면도				
DATE 2021. 10.				
SCALE 1 / 100				
SHEET NO. A - 402				
DRAWING NO.				