


1. 조감도



2. 건축개요 및 현황도

■ 건축개요

- 설 계 명 : 성내동 420-4호 (2필지) 도시형생활주택(원룸형)
신축공사 - 청년-
- 대 지 위 치 : 서울특별시 강동구 성내동 420-4호 (2필지)
- 지 역 지 구 : 제2종일반주거지역
- 건 물 용 도 : 도시형생활주택(원룸형)
- 건 물 규 모 : 지상5층
- 대 지 면 적 : 267.50 m²
- 건 축 면 적 : 159.99 m²
- 연 면 적 : 534.56 m²
- 건 폐 율 : 60%(법정) / 59.81%
- 용 적 율 : 200.00%(법정) / 199.84%
- 최 고 높 이 : 14.50m
- 건 물 구 조 : 철근콘크리트구조
- 주 차 대 수 : 7대(법정) / 8대
- 조 경 면 적 : 13.38m² 이상(5%)(법정) / 32.43 m²(12.12%)

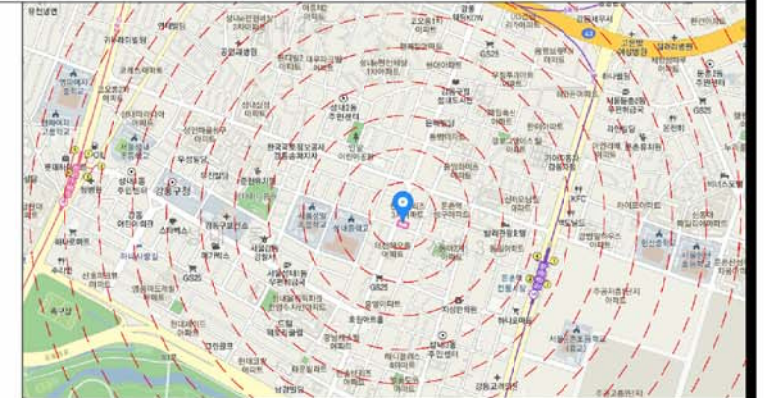

■ 위치도




■ 주변현황도

3. 입면도



본 상기도면은 디자인심의시 제출된 심의도면이며 설계도면과 일부 상이한 참조용이며 설계도면이 우선함

4. 설계자 의도

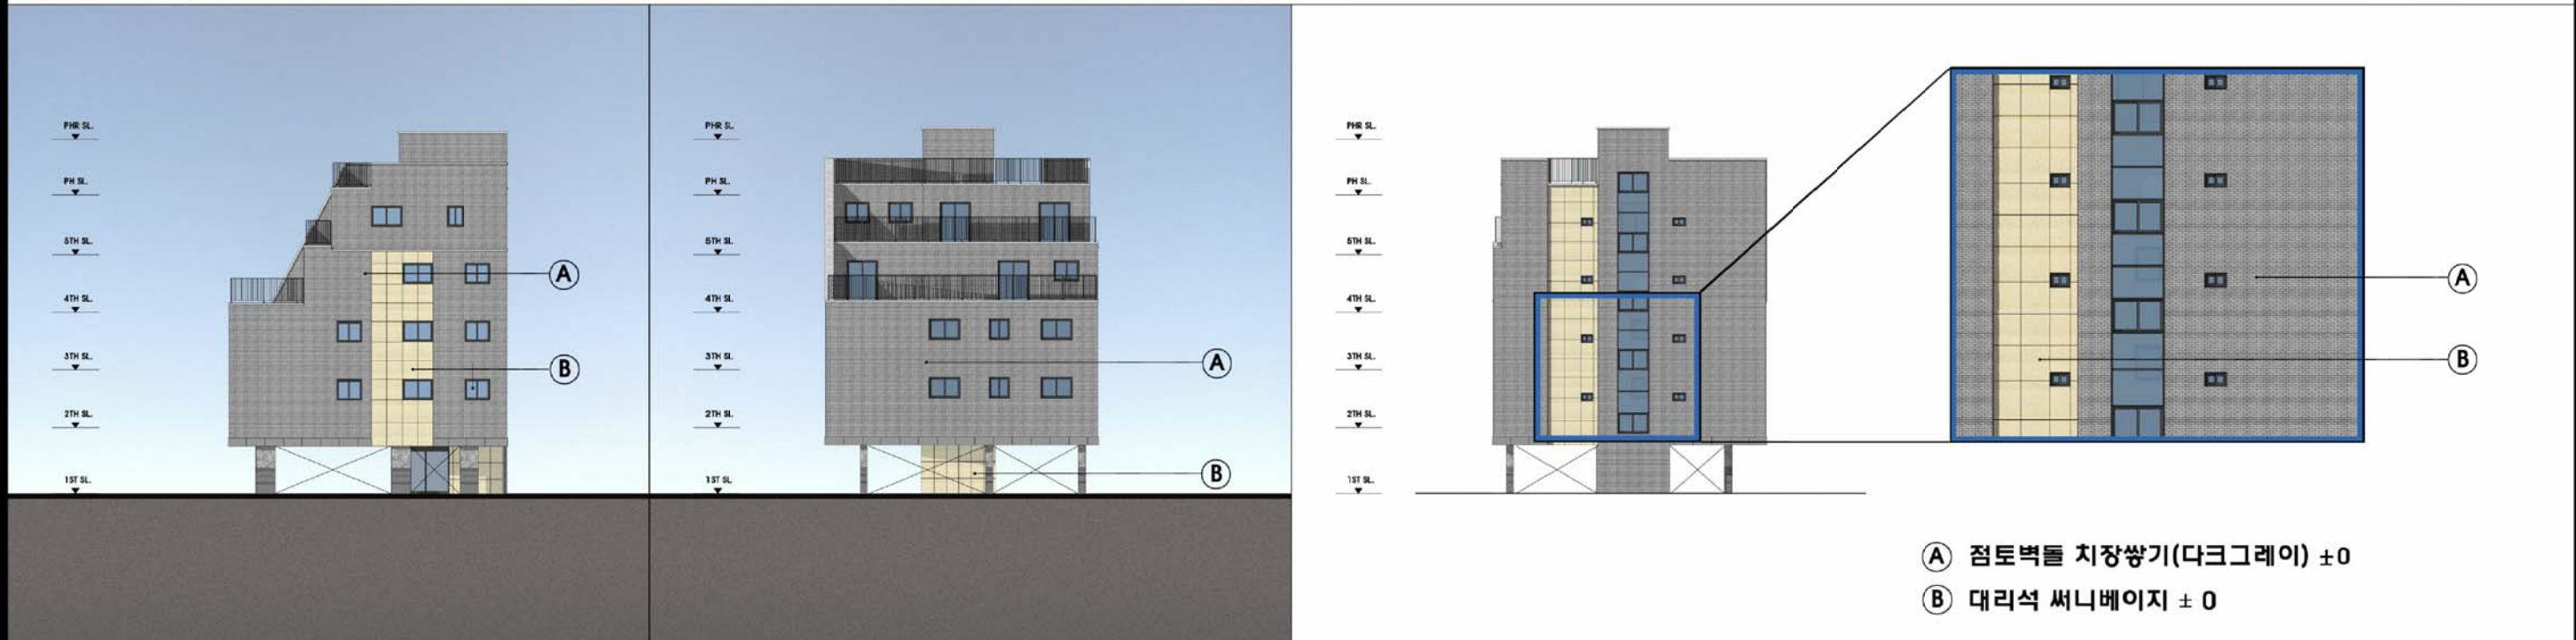


- ① 외장재 점토벽돌 치장쌓기(다크그레이)와 모던하고 고급스러운 외관이 장점인 대리석 써니베이지 물갈기를 조화롭게 배치하고 MASS감을 부각시킨 디자인
② 대리석 써니베이지 물갈기 강조색과 외장재 점토벽돌 치장쌓기(다크그레이)를 사용하여 건물의 인지성을 부여

- 기본 점토벽돌 치장쌓기(다크그레이) 위주 / 외장재 대리석 써니베이지 시공

5. 재료계획

1.점토벽돌 : 주변도시 경관과 이질감이 적고 세련된 재료

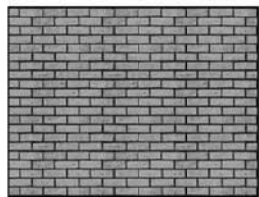

- 외장재 : 점토벽돌 치장쌓기(다크그레이)

2.석재 : 시선의 흐름과 인지성을 고려한 재료



- 외장재 : 대리석 써니베이지 물갈기

3.기둥 : 안정감이 느껴지는 색상의 재료



- 외장재 : 석재뿔칠마감

■ 외장재

구분	실명	재료명
1층	피로티 주차장	바닥 : THK100칼라무늬 CON' C 천정 : AL천정재
2~5층	현관	플리싱타일
	방	바닥 : 데코타일 무늬목 마감 벽 : 친환경실크벽지 천정 : 친환경천정기
	거실	바닥 : 데코타일 무늬목 마감 벽 : 친환경실크벽지 천정 : 친환경천정기
	계단실	바닥 : THK30 화강석 물갈기 벽 : 다채무늬도료

■ 내장재

6. 색채계획


- 주조색 / 보조색 / 강조색



BEIGE



GREY


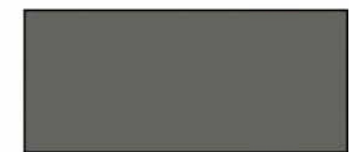


DARK GREY



- 베이지 색상과 다크그레이의 색상을 적용한 조화로운 이미지를 부각시킨 무난하고 편안한 디자인 연출

본 상기도면은 디자인심의회 제출된 심의도면이며 설계도면과 일부 상이한 참조용이며 설계도면이 우선함

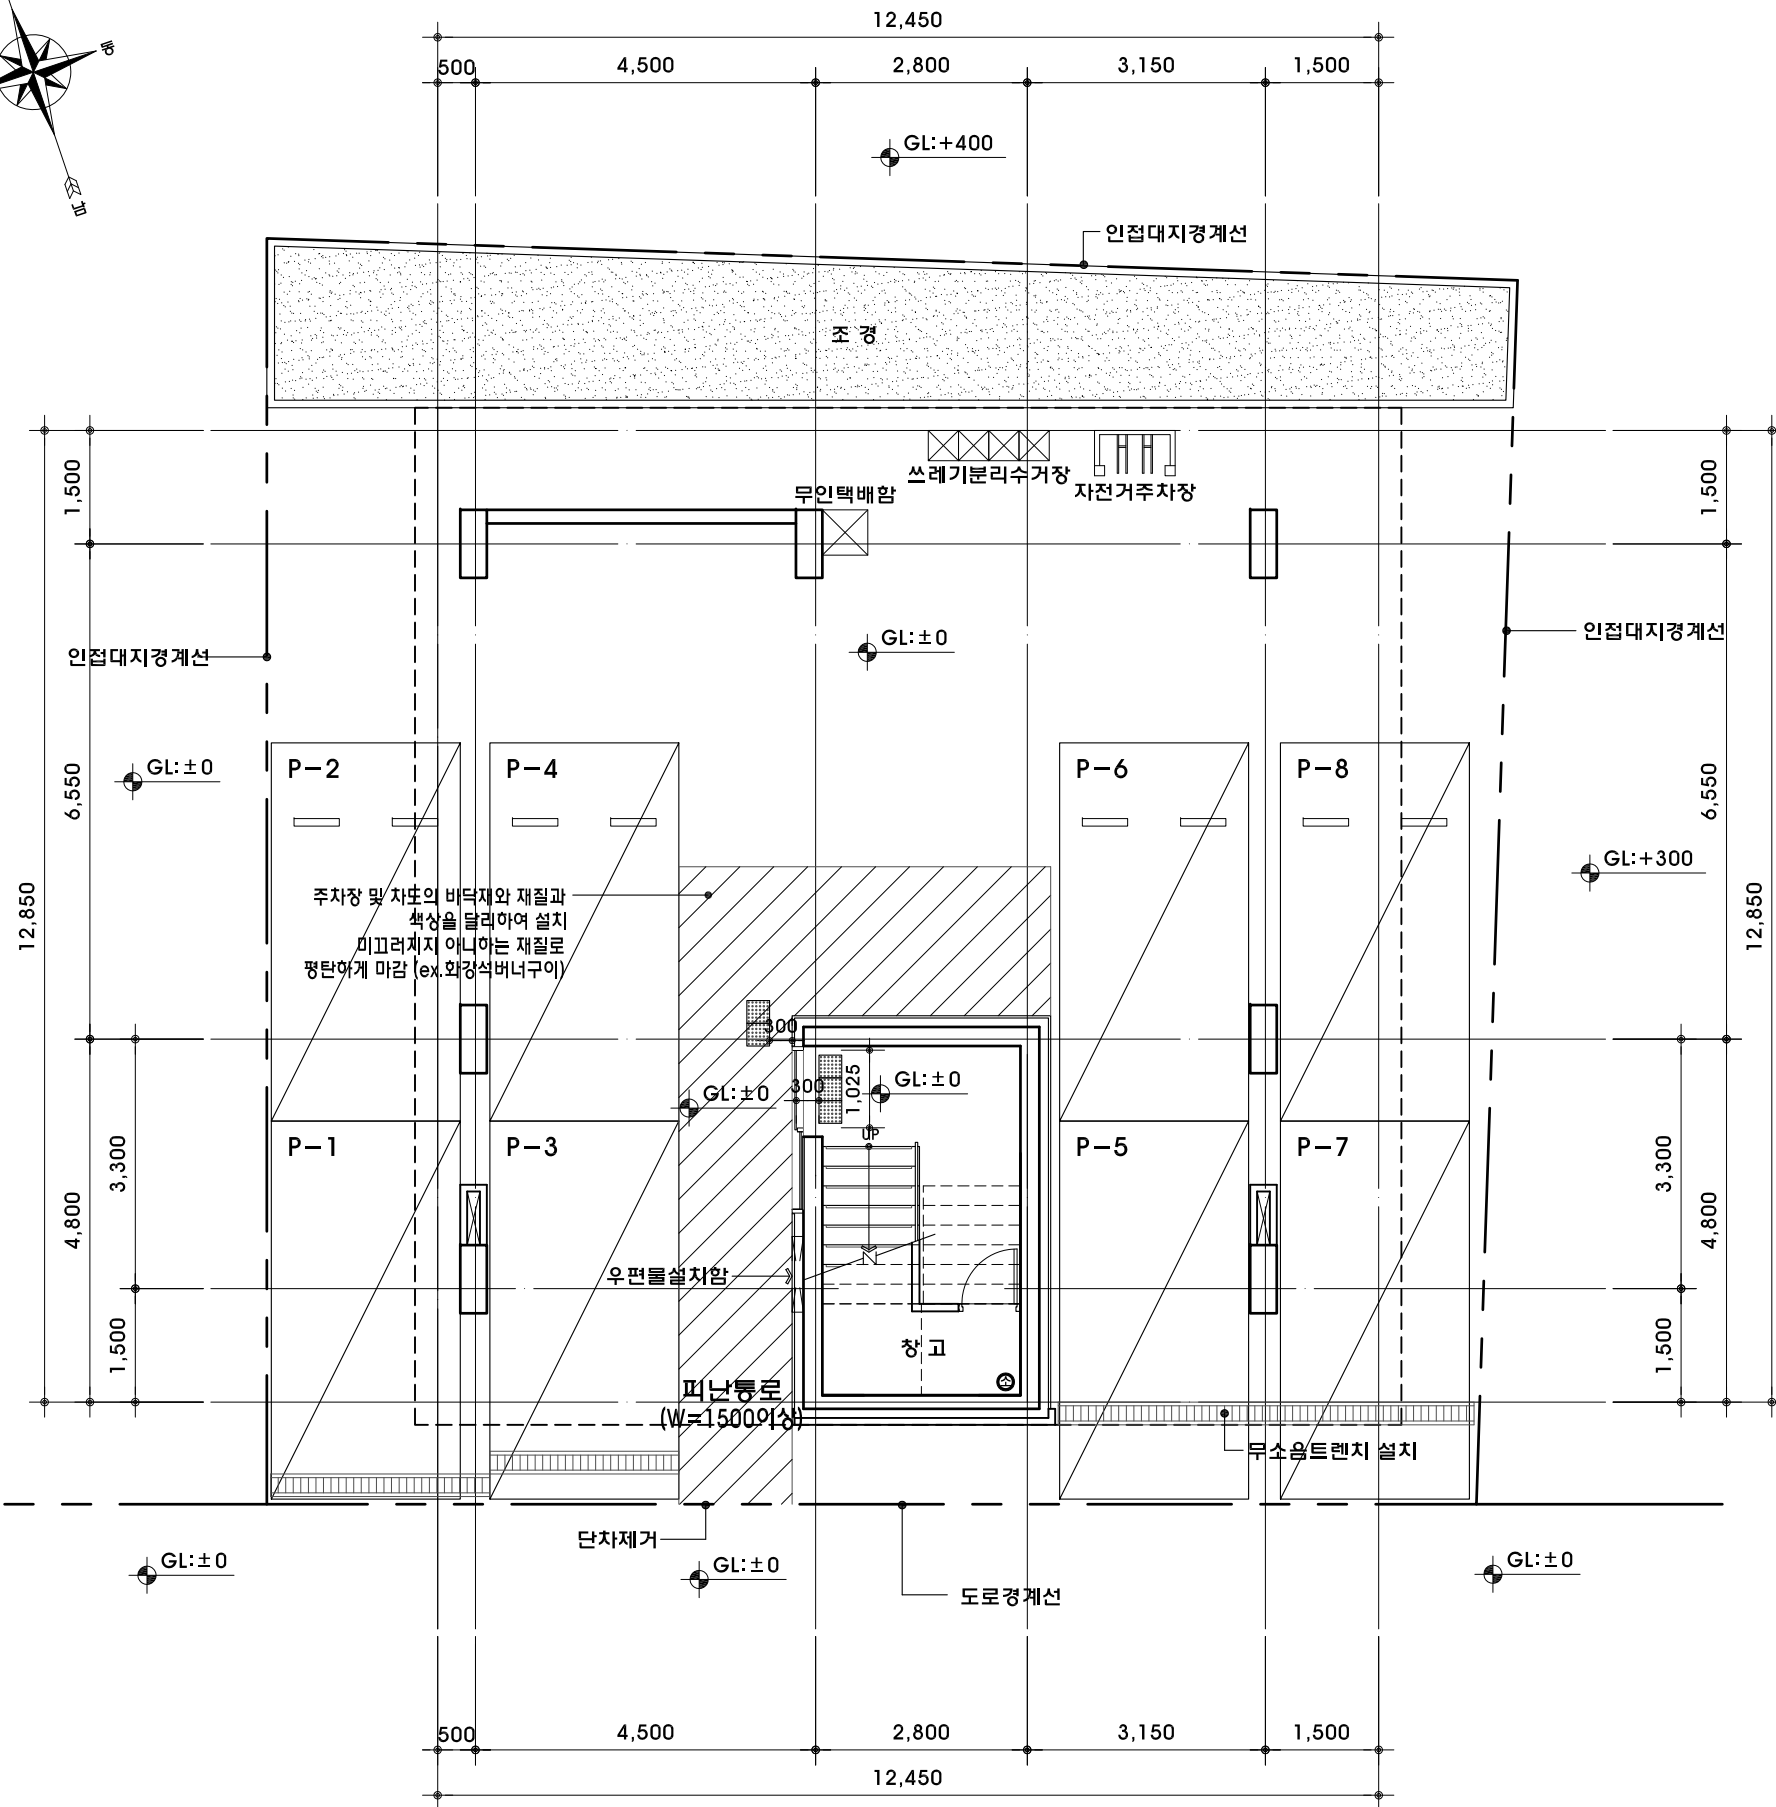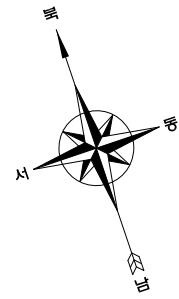

10M 도로

주 기

건 축 구 조 전 기 비 고	1 (외부)	주차장내 CCTV,쓰레기분리수거,자전거보관대 설치	강동구 성내동 420-49 도시형생활주택(원룸형) 신축공사 (청년주택)
		우편함 설치 (세대전용, 공용, 반송용, 폐전지함 구분 설치)	
		세대 테라스 설치시 세대간 분리벽 계획	
		세대 발코니 설치시 차양시설 설치	
		세대내 비디오존 설치	
	2 (계단실)	세대 현관문 도어체크 및 스토퍼 설치	사원번호 PROJECT NO.
		계단참의 현관과 계단 이격거리 (최소600mm이상)	
	3 (내부)	세대내 욕실, 휴지걸이 매립형 설치	변경사항 ISSUER & REVISIONS
		불박이 가구 내부 다용도 수납가능토록 수평 이동 칸막이 설치	
		에어컨 실외기 설치위치 및 에어컨 콘센트, 냉매 및 배수관 위치 도면표기(배수관 수직으로 매립) ☹ - 에어컨 콘센트 표기	
	4 (시공)	콘크리트 폴타이 제거 후 마감공사 시공 (방수, 단열재 시공 등)	△
		욕실 & 다용도실 스위치 : 문 열리는 방향으로 시공 주차장 차량 진출입구간,화장실 무소음트렌치 시공	
	5 (마감)	- 직접외기(외벽)에 면한 실내벽면 단열재	△
		[아이소핑크(10mm) + 석고보드 마감도면 표기]	
		- 간접외기(계단실,복도)에 면한 실내벽면 단열재	
		[경찰우레탄폼(80mm) + 석고보드 마감도면 표기]	△
		*기타 실내 벽면 시멘트 미장 마감	
	1	철근 : fy=400Mpa	설 계 DESIGNED BY
		콘크리트 : fck=24Mpa	
		스라브두께 : 210mm (복배근)	
		외벽벽두께 : 180mm (복배근)	
		코아벽두께 : 180mm (복배근)	
	2	세대벽두께 : 180mm (복배근)	승 인 APPROVED BY
		-콘센트 설치 (바닥 마감선 기준)	
		스탠드형 에어컨 : 350	
		벽걸이형 에어컨 : 1900	
		[화장실] 양변기 옆 : 900	
	1	[주방] 조리대 : 중양 / 냉장고 : 350 / 후드 : 2100	주기사항 NOTE
		-비디오존(VP),보일러온도조절기(B), 스위치(S) 설치 (거실 아트홀 위치)	
		-위치 표기	
		에어컨 실외기	
		에어컨 콘센트	
	2	냉매, 배수관 (배수관수직매립)	건축사 이선영
		우편함 규격은 관련법규에 맞추어 적절한 위치에 설치하고	
		세대전용,공용,반송용,폐전지함으로 구분 설치한다.	
		난간대에 국기봉을 설치한다	



안전광역시 연구구 남달로55번길 6-12, 2층
T.032,464,6775 F.032,881,9102

제 도
DRAWN BY

설 계
DESIGNED BY

심 사
CHECKED BY

승 인
APPROVED BY

주기사항
NOTE

■ 출입문 버튼 설치(인터폰 설치시)

비밀번호 버튼은 그 중심이 바닥면으로부터 0.8~1.2m 높이에 위치하도록 설치한다.
시각장애인연구개발수있게 돌출물 부착형 출입구 비밀번호 및 카드버튼 설치

1	2	3
4	6	6
7	8	9

800~1200

FL+0

인터폰 설치

인터폰 설치시 정형블록은 인터폰 전면 0.3m이격하여 2장, 주출입구 후면에 0.3m이격하여 문쪽만큼 설치해야함.

협동설계
CONSULTANTS

일 자
DATE

도면번호
DRAWING NO.

A - 101

축 적
SCALE



A3 : 1 / 100

도면명
NAME OF DRAWING

지상1층 평면도

지상1층 평면도

SCALE = 1/100

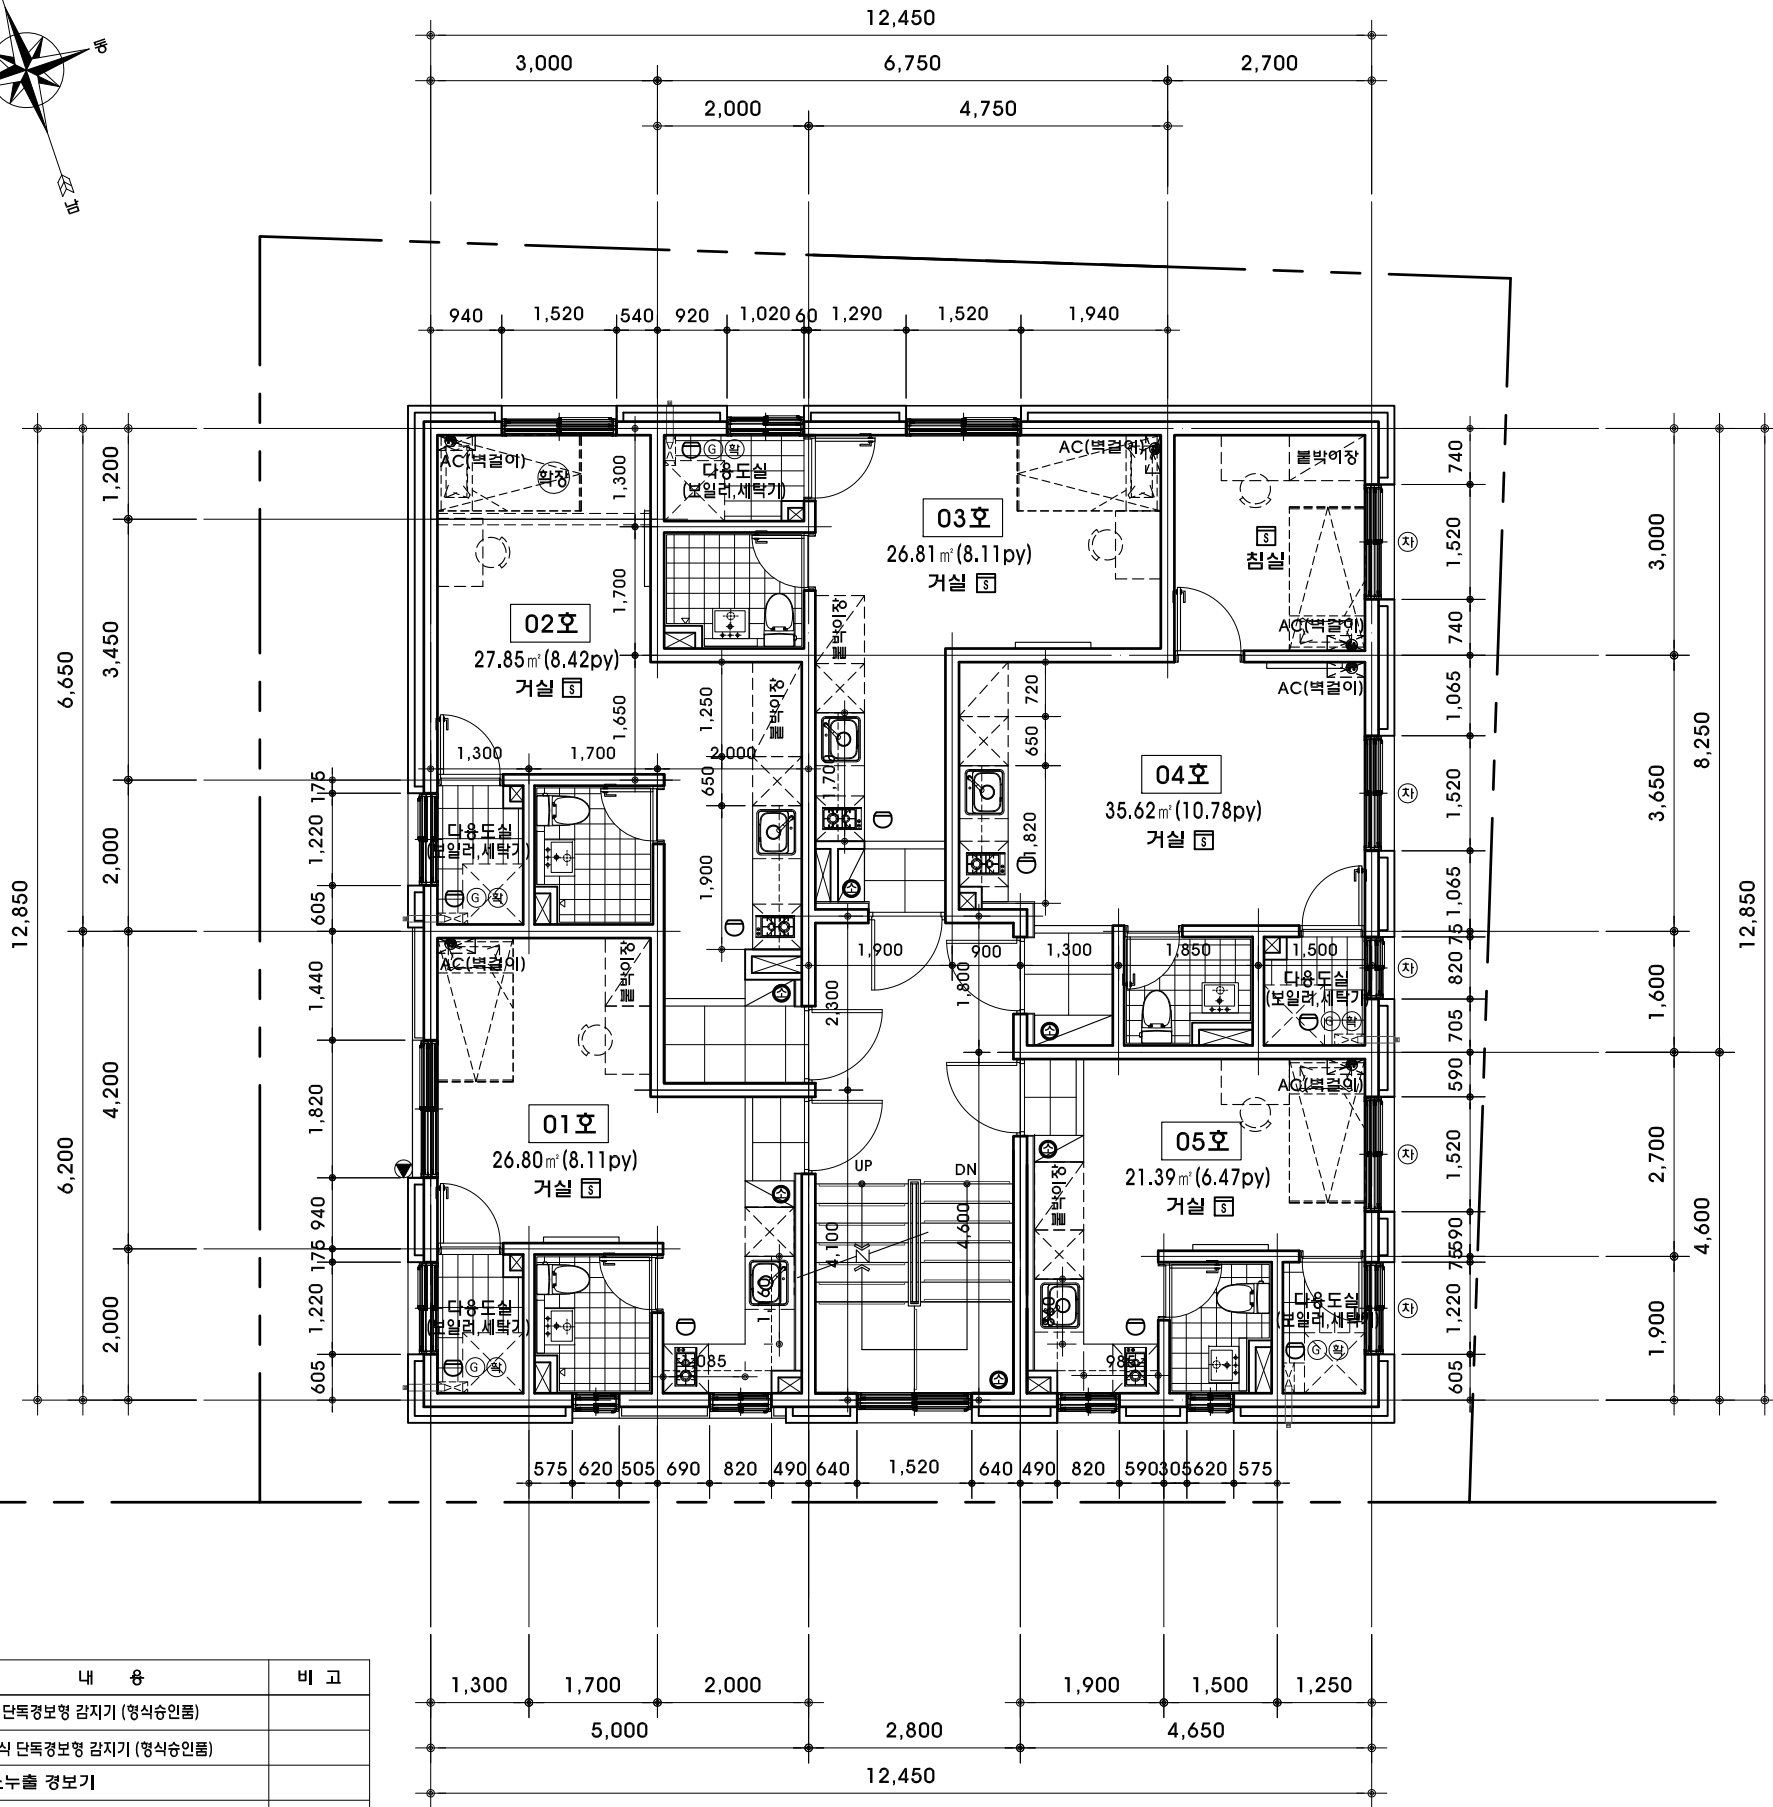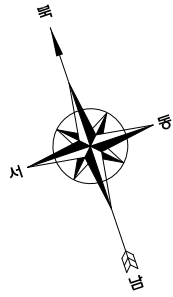

* 주 기 *


상	내	비
상	내	비
○	열식 단독경보형 감지기 (형식승인품)	
㉑	연기식 단독경보형 감지기 (형식승인품)	
㉒	가스누출 경보기	
㉓	ABC 분말 소화기	
㉔	차면시설	
㉕	소방관 진입창	
㉖	확장형 발코니	
㉗	확산 소화기	

■ 주 기

1 (외부)	주차장내 CCTV,쓰레기분리수거,자전거보관대 설치	강동구 성내동 420-49 도시형생활주택(원룸형) 신축공사 (청년주택)
	우편함 설치 (세대전용, 공용, 반송용, 폐건전지함 구분 설치)	
	세대 테라스 설치시 세대간 분리벽 계획	
	세대 발코니 설치시 차양시설 설치	
	세대내 비디오존 설치	
2 (계단실)	세대 현관문 도어체크 및 스토퍼 설치	사
	계단참의 현관과 계단 이격거리 (최소600mm이상)	
	세대내 욕실, 휴지걸이 매립형 설치	
	불박이 가구 내부 다용도 수납가능토록 수평 이동 칸막이 설치	
	에어컨 실외기 설치위치 및 에어컨 콘센트, 냉매 및 배수관 위치 도면표기(배수관 수직으로 매립)	
3 (내부)	에어컨 콘센트 표기	A
4 (시공)	콘크리트 폴타이 제거 후 마감공사 시공 (방수, 단열재 시공 등)	A
	욕실 & 다용도실 스위치 : 문 열리는 방향으로 시공	
	주차장 차량 진출입구간,화장실 무소음트렌치 시공	
5 (마감)	- 직접외기(외벽)에 면한 실내벽면 단열재	A
	[아이소핑크(10mm) + 석고보드 마감도면 표기]	
	- 간접외기(계단실,복도)에 면한 실내벽면 단열재	
	[경찰우레탄폼(80mm) + 석고보드 마감도면 표기]	
	*기타 실내 벽면 시멘트 미장 마감	
구	철근 : fy=400Mpa	설
	콘크리트 : fck=24Mpa	
	스라브두께 : 210mm (복배근)	
	외벽벽두께 : 180mm (복배근)	
	코아벽두께 : 180mm (복배근)	
조	세대벽두께 : 180mm (복배근)	심
	-콘센트 설치 (바닥 마감선 기준)	
	스탠드형 에어컨 : 350	
	벽걸이형 에어컨 : 1900	
	[화장실] 양변기 옆 : 900	
전	[주방] 조리대 : 중양 / 냉장고 : 350 / 후드 : 2100	승
	-비디오존(VP),보일러온도조절기(B), 스위치(S) 설치 (거실 아트홀 위치)	
기	-위치 표기	인
	에어컨 실외기	
	에어컨 콘센트	
	냉매, 배수관 (배수관수직매립)	
비	우편함 규격은 관련법규에 맞추어 적절한 위치에 설치하고	주
	세대전용,공용,반송용,폐건전지함으로 구분 설치한다.	
	난간대에 국기봉을 설치한다	





제	도
DRAWN BY	
설	계
DESIGNED BY	
심	사
CHECKED BY	
승	인
APPROVED BY	건축사 이선영
주	기
NOTE	* (㉔) : 2m 이내일 경우 설치

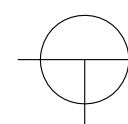

지상 2~3층 평면도
SCALE = 1/100

협	동
CONSULTANTS	
일	자
DATE	
도	면
DRAWING NO.	A - 102
축	척
SCALE	A3 : 1 / 100
도	면
NAME OF DRAWING	지상 2~3층 평면도

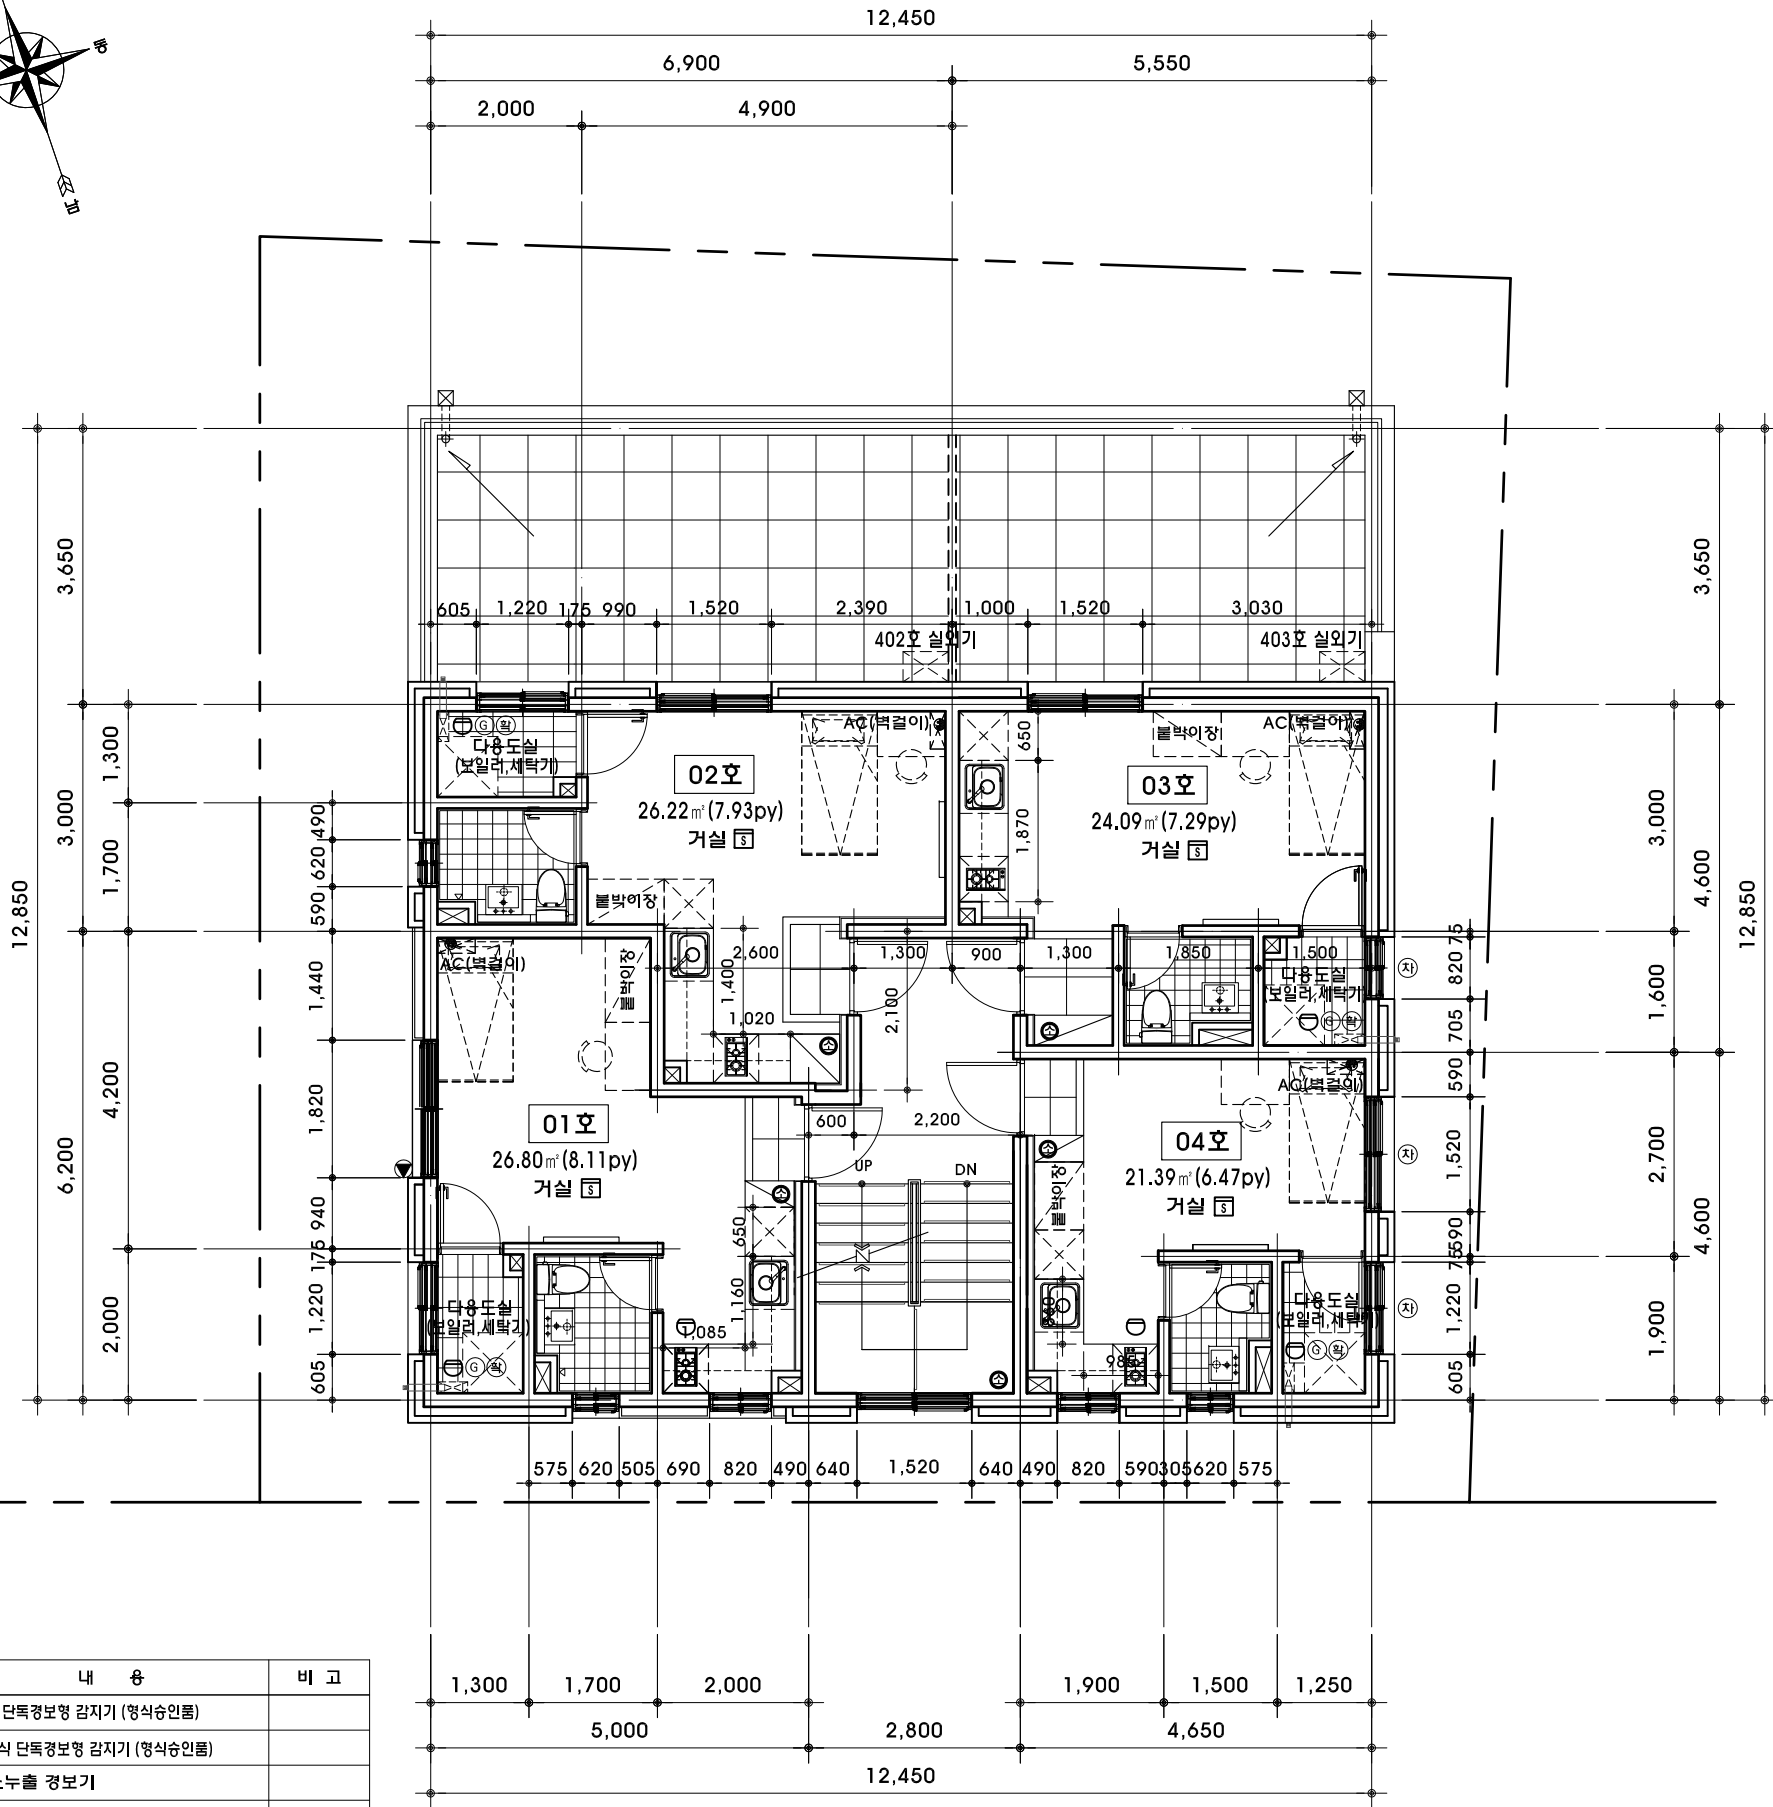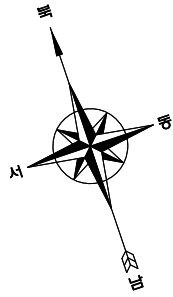

* 주 기 *



심볼	내용	비고
○	열식 단독경보형 감지기 (형식승인품)	
㉑	연기식 단독경보형 감지기 (형식승인품)	
㉒	가스누출 경보기	
㉓	ABC 분말 소화기	
㉔	차면시설	
㉕	소방관 진입창	
㉖	확장형 발코니	
㉗	확산 소화기	

■ 주 기

건	1 (외부)	주차장내 CCTV,쓰레기분리수거,자전거보관대 설치
		우편함 설치 (세대전용, 공용, 반송용, 폐전지함 구분 설치)
		세대 테라스 설치시 세대간 분리벽 계획
		세대 발코니 설치시 차양시설 설치
		세대내 비디오존 설치
층	2 (계단실)	세대 현관문 도어체크 및 스토퍼 설치
		계단참의 현관과 계단 이격거리 (최소600mm이상)
	3 (내부)	세대내 욕실, 휴지걸이 매립형 설치
		불박이 가구 내부 다용도 수납가능토록 수평 이동 칸막이 설치
		에어컨 실외기 설치위치 및 에어컨 콘센트, 냉매 및 배수관 위치 도면표기(배수관 수직으로 매립) ☹ - 에어컨 콘센트 표기
구	4 (시공)	콘크리트 폴타이 제거 후 마감공사 시공 (방수, 단열재 시공 등)
		욕실 & 다용도실 스위치 : 문 열리는 방향으로 시공
	5 (마감)	주차장 차량 진출입구간,화장실 무소음트렌치 시공
		- 직접외기(외벽)에 면한 실내벽면 단열재
		[아이소핑크(10mm) + 석고보드 마감도면 표기]
전	1	- 간접외기(계단실,복도)에 면한 실내벽면 단열재
		[경찰우레탄폼(80mm) + 석고보드 마감도면 표기]
		*기타 실내 벽면 시멘트 미장 마감
		철근 : fy=400Mpa
		콘크리트 : fck=24Mpa
기	2	스라브두께 : 210mm (복배근)
		외벽벽두께 : 180mm (복배근)
		코아벽두께 : 180mm (복배근)
		세대벽두께 : 180mm (복배근)
		세대벽두께 : 180mm (복배근)
비	1	-콘센트 설치 (바닥 마감선 기준)
		스탠드형 에어컨 : 350
		벽걸이형 에어컨 : 1900
		[화장실] 양변기 옆 : 900
		[주방] 조리대 : 중양 / 냉장고 : 350 / 후드 : 2100
고	2	-비디오존(VP),보일러온도조절기(B), 스위치(S) 설치 (거실 아트홀 위치)
		VP S B
	3	-위치 표기
		에어컨 실외기
		에어컨 콘센트
비	고	냉매, 배수관 (배수관수직매립)
		우편함 규격은 관련법규에 맞추어 적절한 위치에 설치하고
		세대전용,공용,반송용,폐전지함으로 구분 설치한다.
		난간대에 국기봉을 설치한다

사업명칭 PROJECT TITLE	강동구 성내동 420-49 도시형생활주택(원룸형) 신축공사 (청년주택)
사업번호 PROJECT NO.	
변경사항 ISSUER & REVISIONS	
제 도 DRAWN BY	
설 계 DESIGNED BY	
심 사 CHECKED BY	
승 인 APPROVED BY	건축사 이선영
주기사향 NOTE	* (㉔): 2m 이내일 경우 설치
협동업체 CONSULTANTS	
일 자 DATE	
도면번호 DRAWING NO.	A - 103
축 척 SCALE	A3 : 1 / 100
도면명 NAME OF DRAWING	지상4층 평면도

지상 4층 평면도
SCALE = 1/100

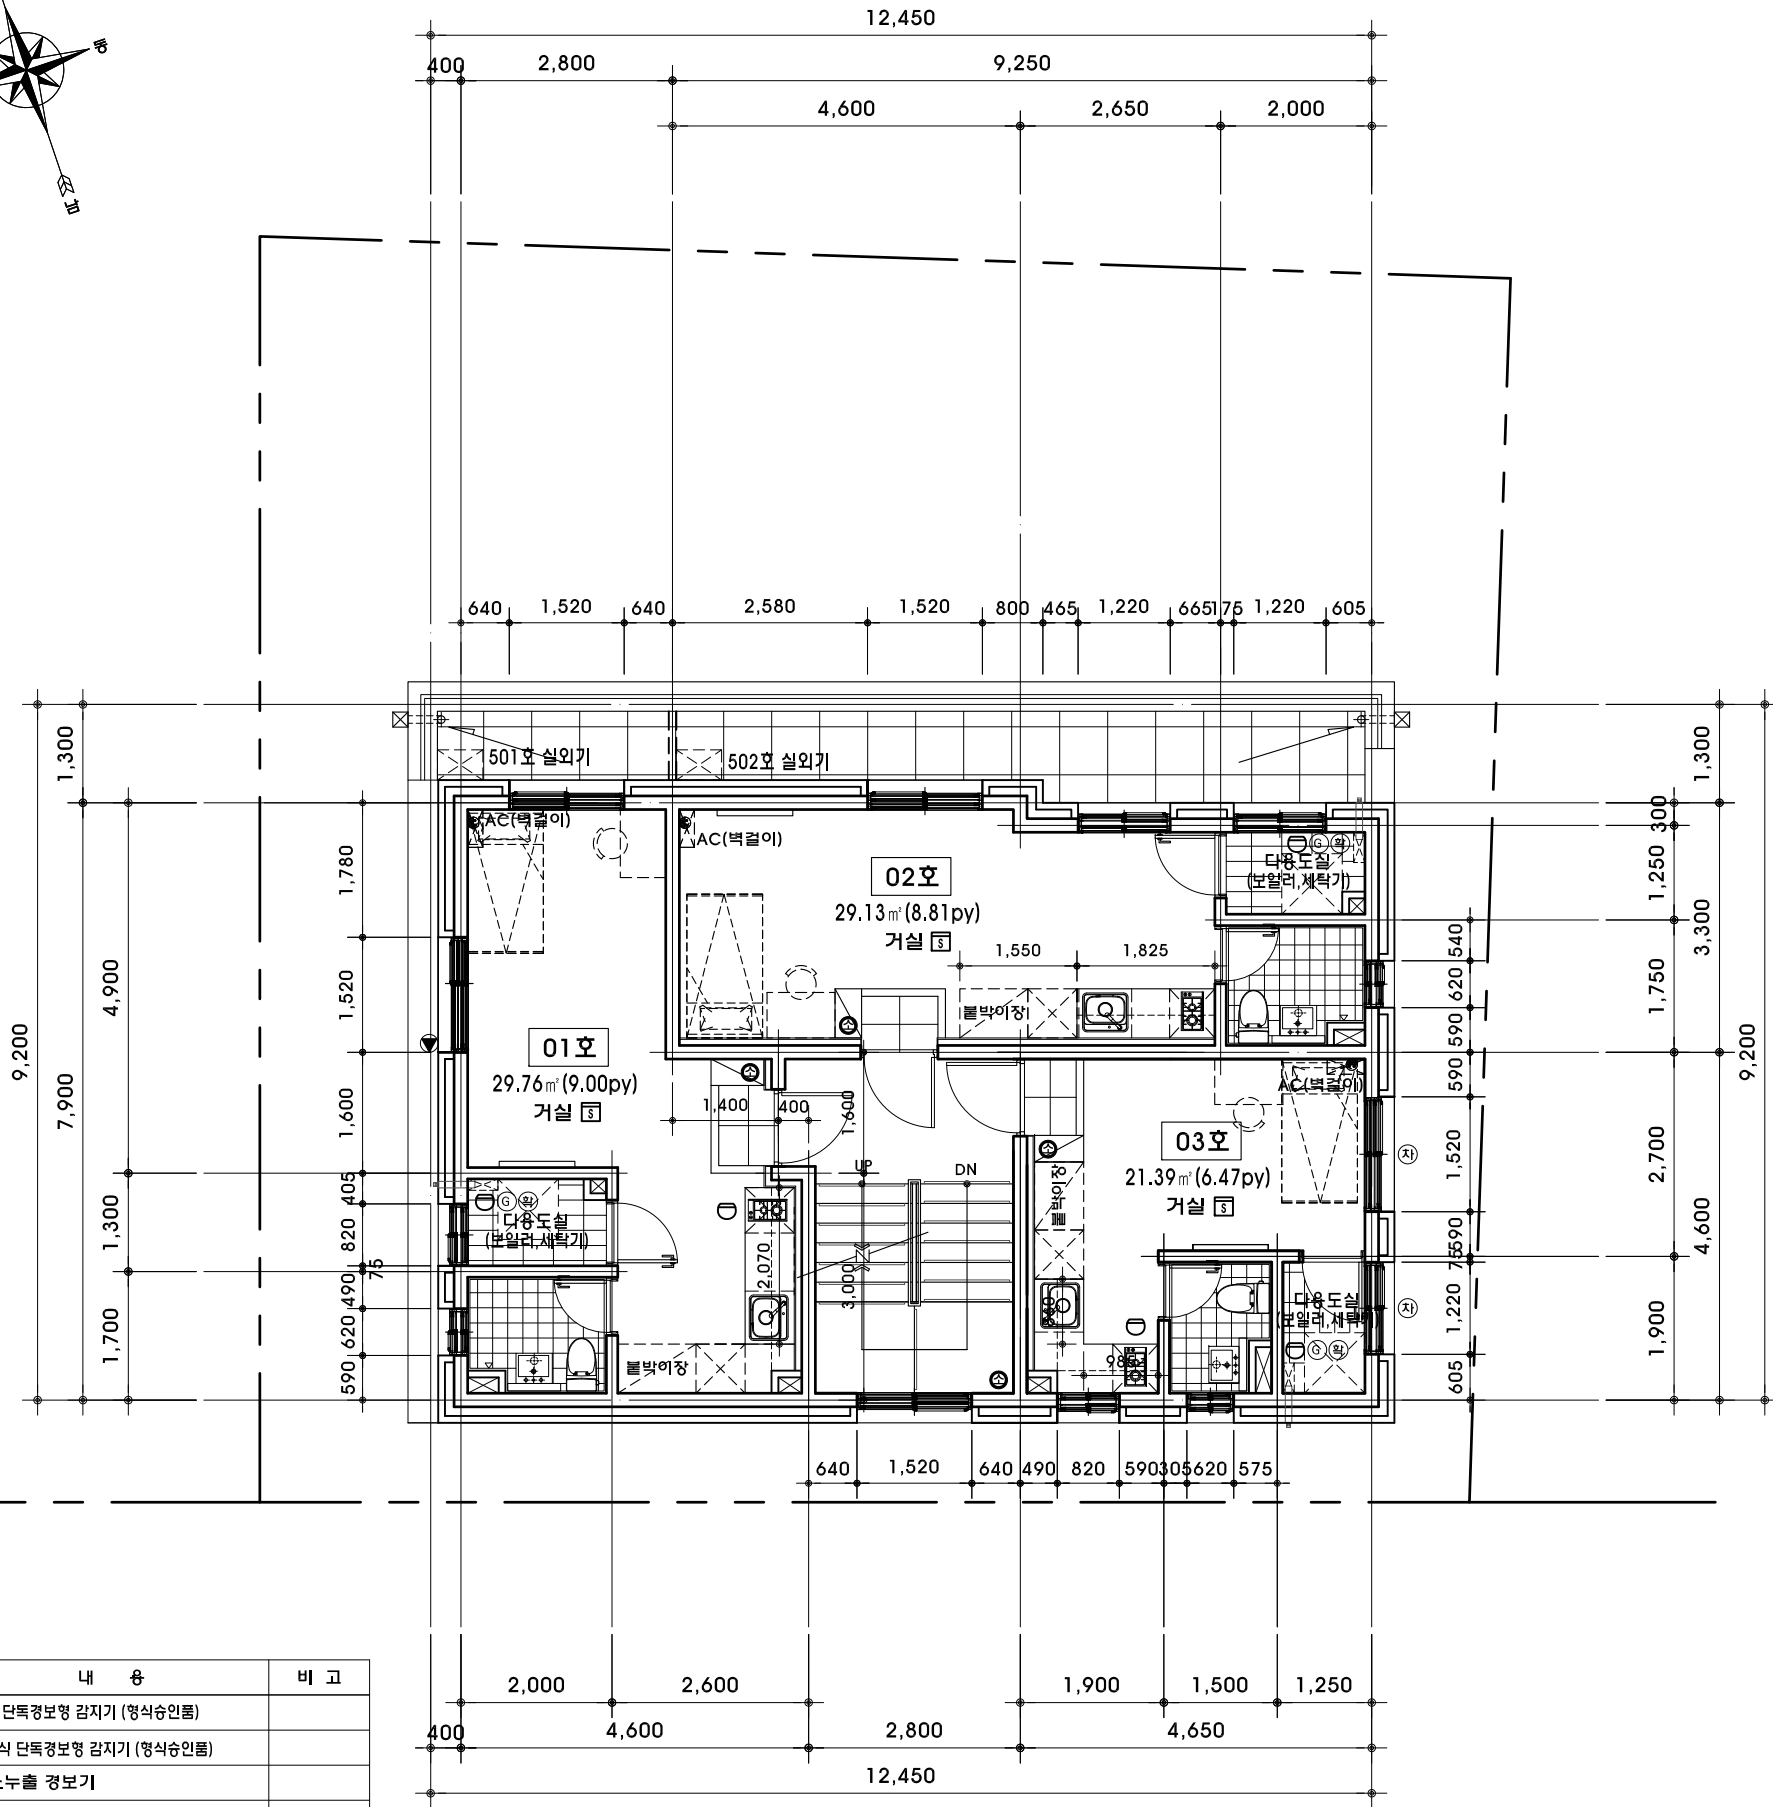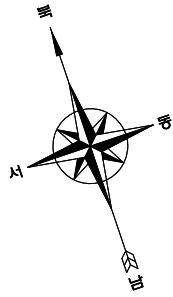


* 주 기 *

상 표	내 용	비 고
㉠	열식 단독경보형 감지기 (형식승인품)	
㉡	연기식 단독경보형 감지기 (형식승인품)	
㉢	가스누출 경보기	
㉣	ABC 분말 소화기	
㉤	차면시설	
㉥	소방관 진입창	
㉦	확장형 발코니	
㉧	확산 소화기	




■ 주 기

건축	1 (외부)	주차장내 CCTV,쓰레기분리수거,자전거보관대 설치		강동구 성내동 420-49 도시형생활주택(원룸형) 신축공사 (청년주택)	
		우편함 설치 (세대전용, 공용, 반송용, 폐건전지함 구분 설치)			
		세대 테라스 설치시 세대간 분리벽 계획			
		세대 발코니 설치시 차양시설 설치			
		세대내 비디오존 설치			
	2 (계단실)	세대 현관문 도어체크 및 스토퍼 설치		사업번호 PROJECT NO.	
		계단참의 현관과 계단 이격거리 (최소600mm이상)		변경사항 ISSUER & REVISIONS	
	3 (내부)	세대내 욕실, 휴지걸이 매립형 설치		△	
		불박이 가구 내부 다용도 수납가능토록 수평 이동 칸막이 설치			
		에어컨 실외기 설치위치 및 에어컨 콘센트, 냉매 및 배수관 위치 도면표기(배수관 수직으로 매립) 👤 - 에어컨 콘센트 표기			△
	4 (시공)	콘크리트 폼타이 제거 후 마감공사 시공 (방수, 단열재 시공 등)		△	
		욕실 & 다용도실 스위치 : 문 열리는 방향으로 시공		△	
		주차장 차량 진출입구간,화장실 무소음트렌치 시공		△	
	5 (마감)	-직접외기(외벽)에 면한 실내벽면 단열재		 hanndas Architects & Interiors 안전광역시 연수구 남달로55번길 6-12, 2층 T_032,464,6775 F_032,681,9102	
		[아이소핑크(10mm) + 석고보드 마감도면 표기]			
		-간접외기(계단실,복도)에 면한 실내벽면 단열재			
		[경질우레탄폼(80mm) + 석고보드 마감도면 표기]			
		*기타 실내 벽면 시멘트 미장 마감			
	구조	1	철근 : fy=400Mpa		설 계 DESIGNED BY
			콘크리트 : fck=24Mpa		
2		스라브두께 : 210mm (복배근)		심 사 CHECKED BY	
		외벽벽두께 : 180mm (복배근)			
		코아벽두께 : 180mm (복배근)			
세대벽두께 : 180mm (복배근)		승 인 APPROVED BY	건축사 이선영		
세탁벽두께 : 180mm (복배근)		주기사향 NOTE	*㉠: 2m 이내일 경우 설치		
전기	1	-콘센트 설치 (바닥 마감선 기준)		*㉠: 2m 이내일 경우 설치	
		스탠드형 에어컨 : 350			
		벽걸이형 에어컨 : 1900			
		[화장실] 양변기 옆 : 900			
		[주방] 조리대 : 중앙 / 냉장고 : 350 / 후드 : 2100			
	2	-비디오존(VP),보일러온도조절기(B), 스위치(S) 설치 (거실 아트홀 위치)			VP S B
	3	-위치 표기			
		에어컨 실외기			⊠
		에어컨 콘센트			👤
냉매, 배수관 (배수관수직매립)		⊠			
비고	우편함 규격은 관련법규에 맞추어 적절한 위치에 설치하고				
	세대전용,공용,반송용,폐건전지함으로 구분 설치한다.				
	난간대에 국기봉을 설치한다				

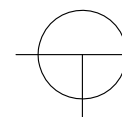


지상 5층 평면도

SCALE = 1/100

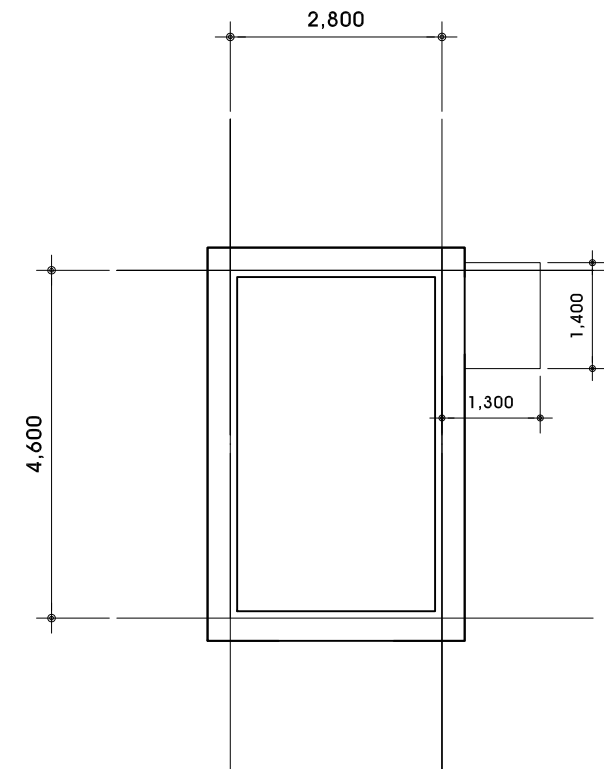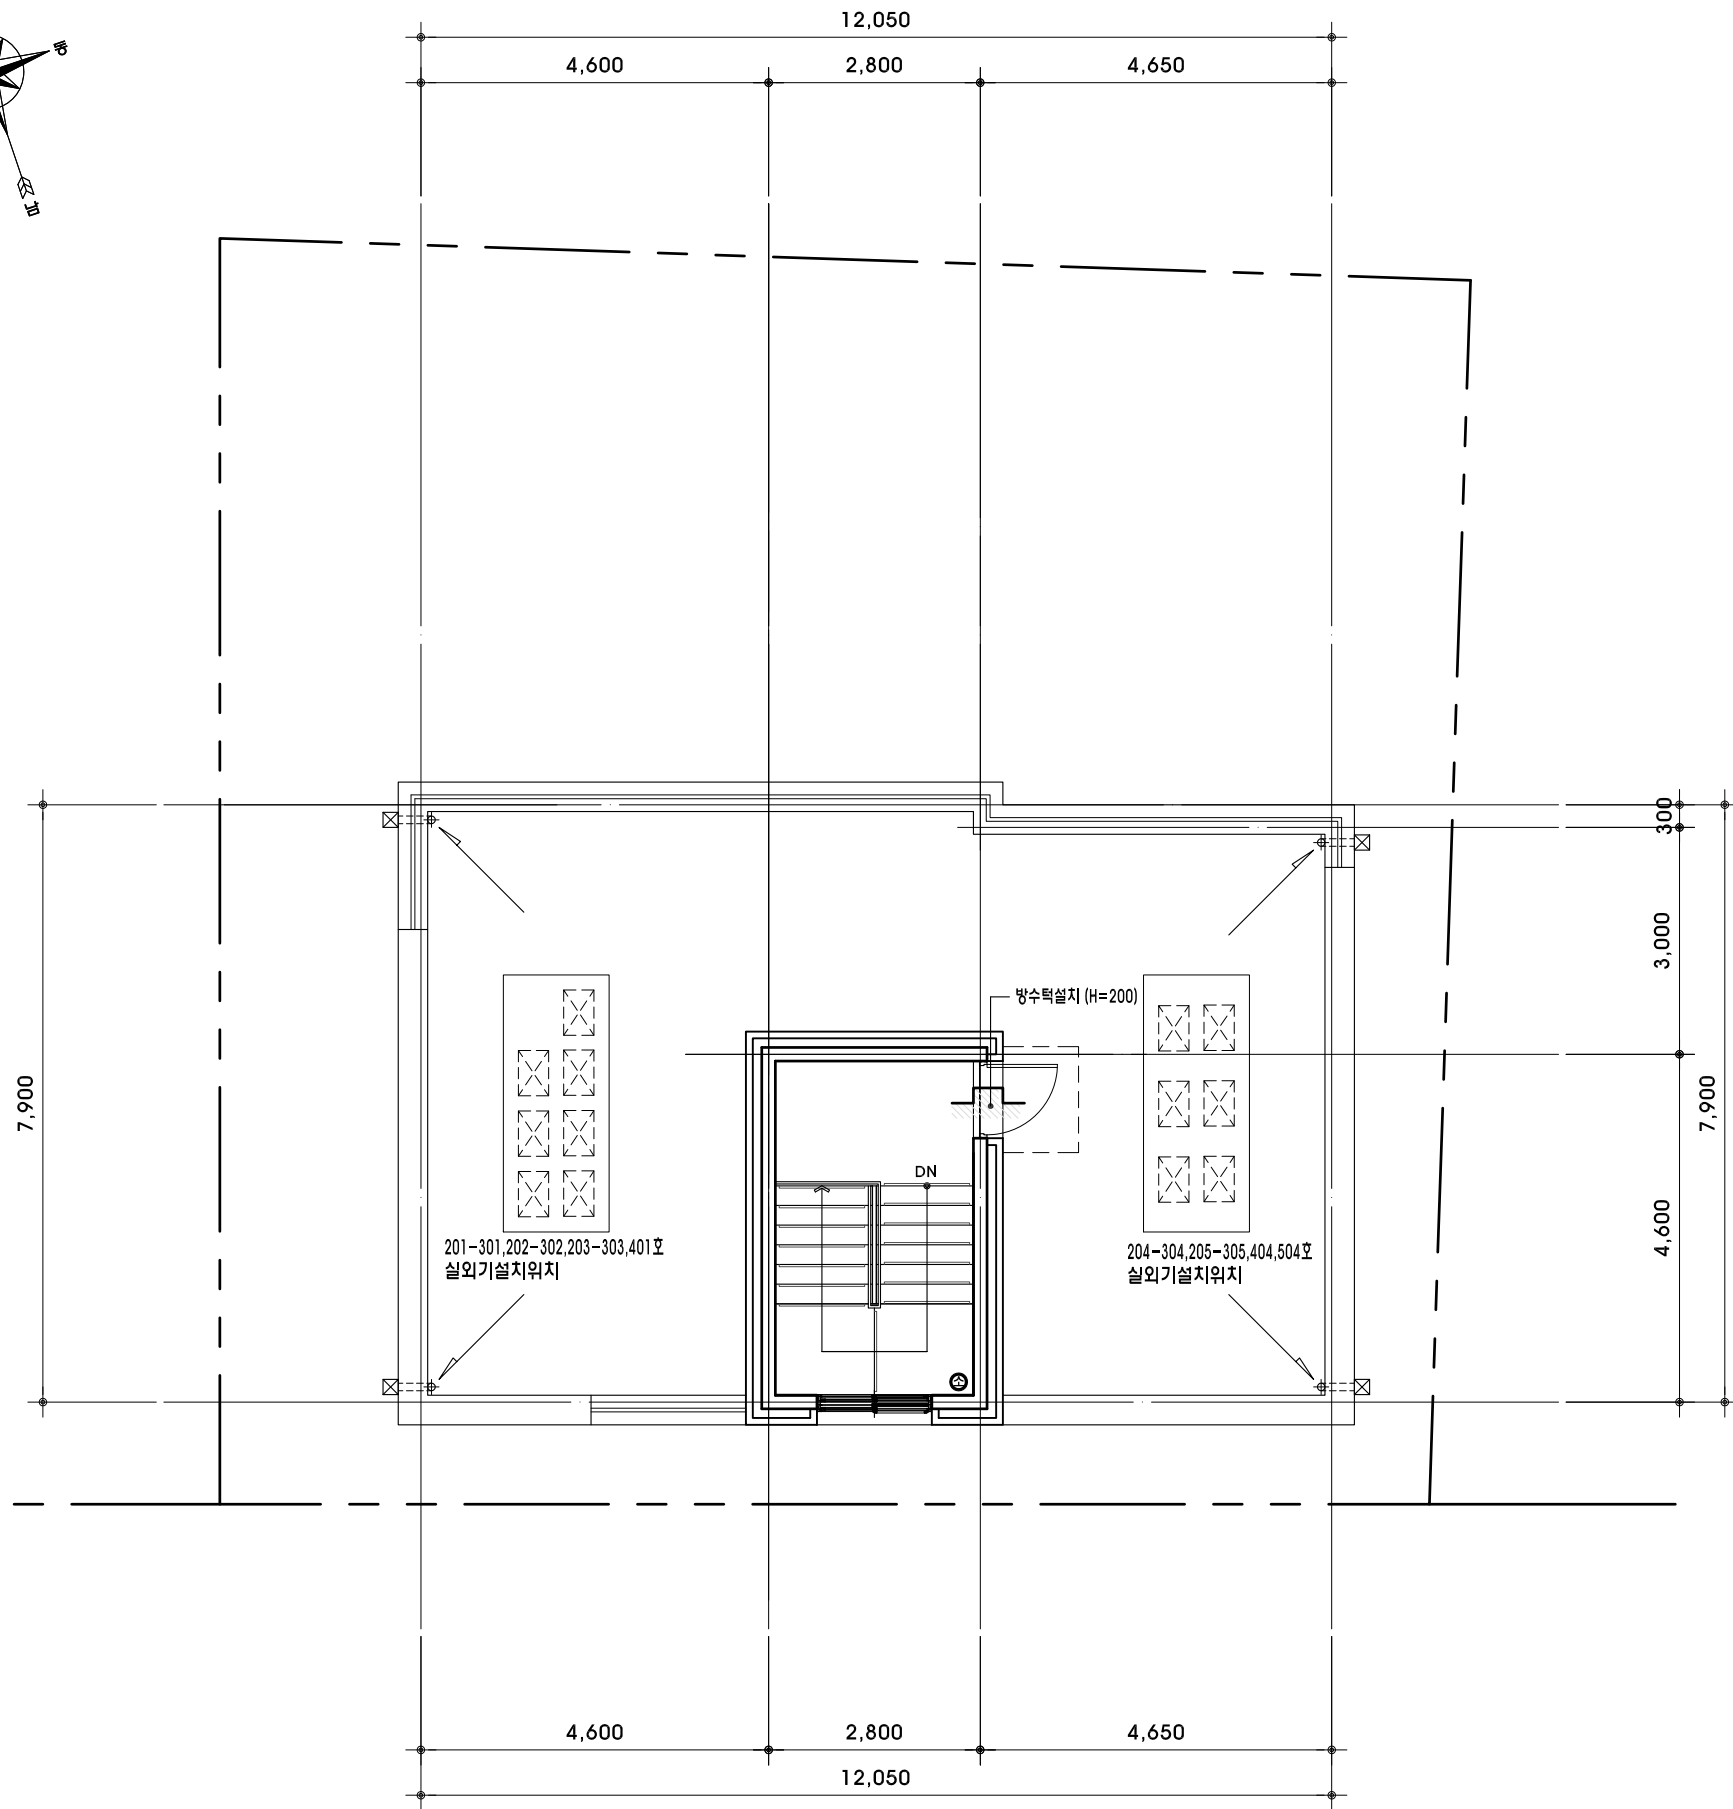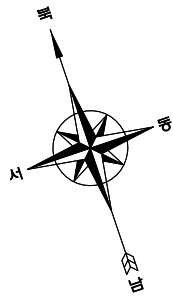

옥탑지붕층

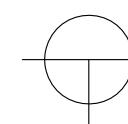

지붕층 및 옥탑지붕층 평면도

SCALE = 1/100

사업명칭
PROJECT TITLE
강동구 성내동 420-49
도시형생활주택(원룸형)
신축공사 (청년주택)

사업번호
PROJECT NO.

변경사항
ISSUER & REVISIONS

△	
△	
△	
△	
△	

hanndas
Architects & Interiors
안전광역시 연수구 남암로55번길 6-12, 2층
T.032,464,6775 F.032,881,9102

제 도
DRAWN BY

설 계
DESIGNED BY

심 사
CHECKED BY

승 인
APPROVED BY
건축사 이선영

주기사항
NOTE

협동업체
CONSULTANTS

일 자
DATE

도면번호
DRAWING NO.


A - 105

축 적
SCALE

A3 : 1 / 100

도면명
NAME OF DRAWING

지붕층 및 옥탑지붕층
평면도

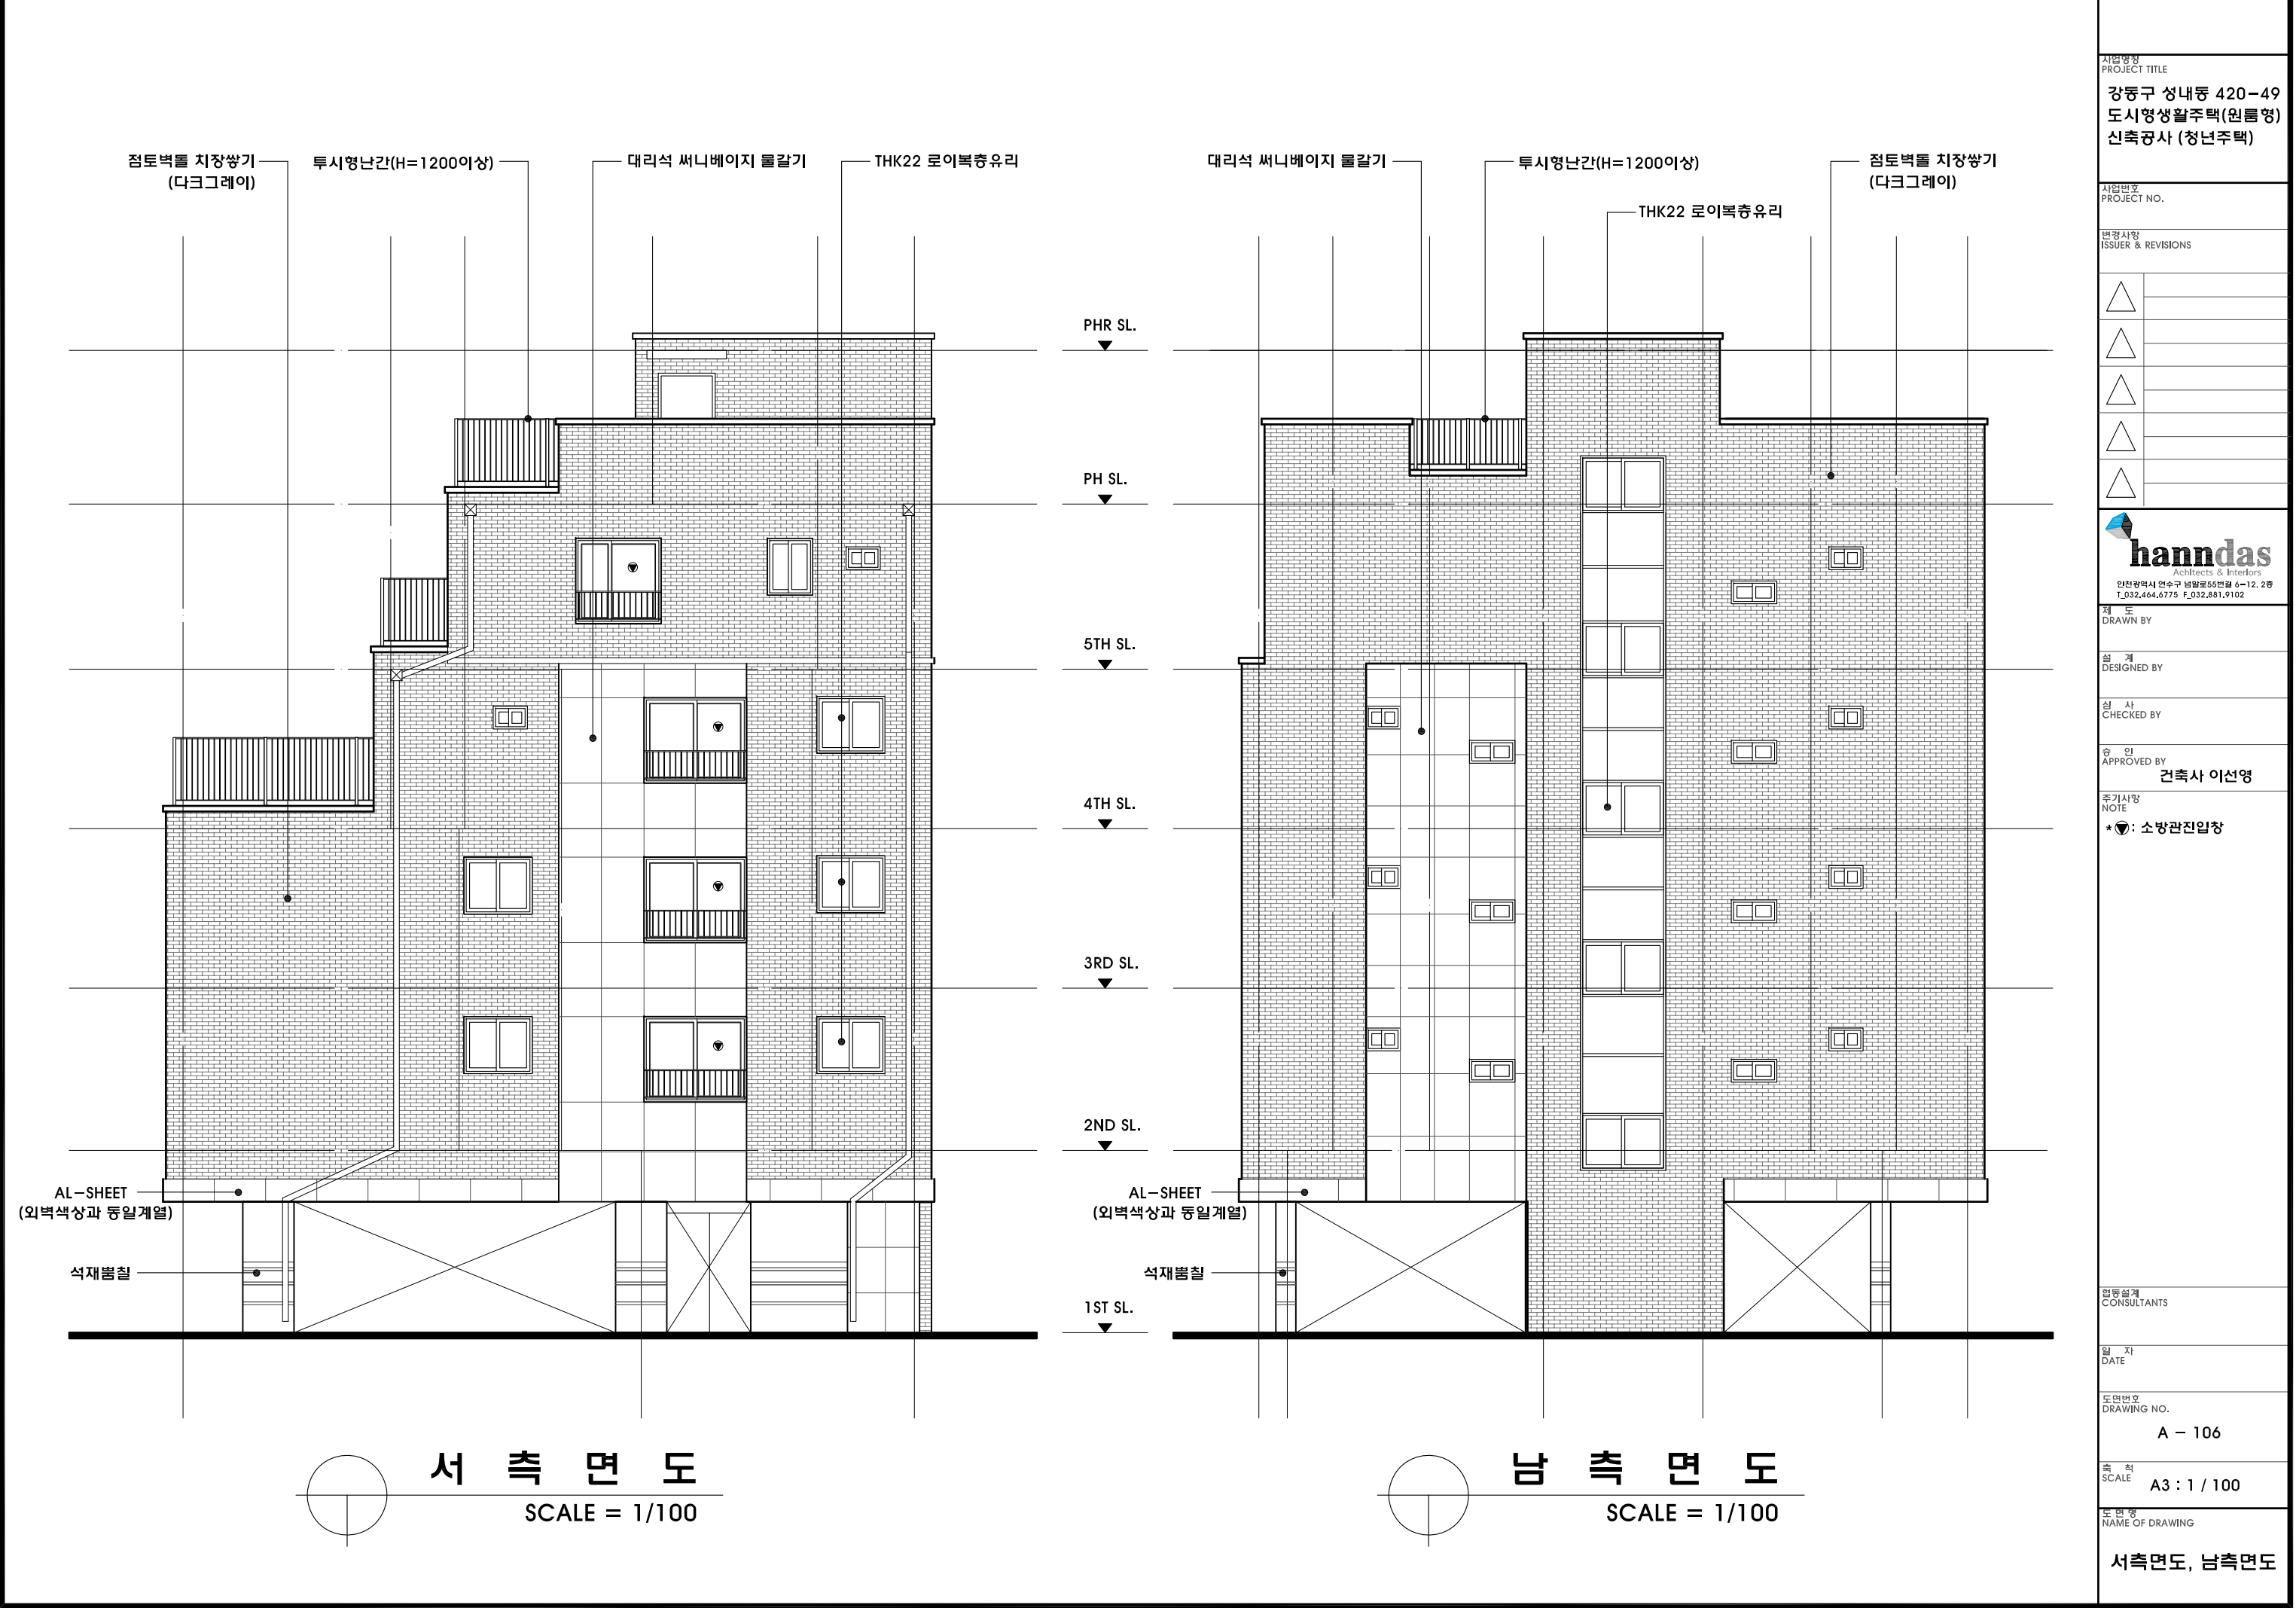

사업명 PROJECT TITLE		강동구 성내동 420-49 도시형생활주택(원룸형) 신축공사 (청년주택)
사업번호 PROJECT NO.		
변경사항 ISSUER & REVISIONS		
△		
△		
△		
△		
△		
hanndas Architects & Interiors 안전광역시 연수구 남달로55번길 6-12, 2층 T.032.464.6775 F.032.881.9102		
제 도 DRAWN BY		
설 계 DESIGNED BY		
심 사 CHECKED BY		
승 인 APPROVED BY		건축사 이선영
주기사장 NOTE		* ㉠: 소방관진입창
협동업체 CONSULTANTS		
일 자 DATE		
도면번호 DRAWING NO.		A - 106
축 척 SCALE		A3 : 1 / 100
도면명 NAME OF DRAWING		서측면도, 남측면도



동 측 면 도
SCALE = 1/100

북 측 면 도
SCALE = 1/100

사업명 PROJECT TITLE	
강동구 성내동 420-49 도시형생활주택(원룸형) 신축공사 (청년주택)	
사업번호 PROJECT NO.	
변경사항 ISSUER & REVISIONS	
△	
△	
△	
△	
△	
 hanndas Architects & Interiors 안전광역시 연구구 본점55번길 6-12, 2층 T.032.464.6775 F.032.881.9102	
제 도 DRAWN BY	
설 계 DESIGNED BY	
심 사 CHECKED BY	
승 인 APPROVED BY 건축사 이선영	
주기사항 NOTE	
영동 설계 CONSULTANTS	
일 자 DATE	
도면번호 DRAWING NO. A - 107	
축 척 SCALE A3 : 1 / 100	
도면명 NAME OF DRAWING 동측면도, 북측면도	