

An architectural rendering of a modern, multi-story residential building. The building features a prominent grid-like facade made of light-colored, textured panels. It has several rectangular windows of varying sizes, some with dark frames. A central vertical section is slightly taller than the rest of the building. Balconies with black metal railings are visible on the upper floors. The ground floor has large glass doors and windows, suggesting a modern entrance. In the foreground, there is a paved area with a few people: a person on a bicycle on the left, a person walking near a car on the left, and a group of three people standing near a car on the right. The background is a clear blue sky with some light clouds.

■ 건축개요

- 설 계 명 : 강동구 성내동 404-14호 도시형생활주택(소형주택) 신축공사
- 대 지 위 치 : 서울특별시 강동구 성내동 404-14호
- 지 역·지 구 : 제2종 일반주거지역
- 건 물 용 도 : 다세대주택-도시형생활주택(소형주택)-13세대
- 건 물 규 모 : 지상 5층
- 대 지 면 적 : 231.00 m²
- 건 축 면 적 : 137.04 m²
- 연 면 적 : 451.26 m²
- 건 폐 율 : 59.33 %
- 용 적 륜 : 196.35 %
- 최 고 높 이 : 15.80 m
- 건 물 구 조 : 철근콘크리트조
- 주 차 대 수 : 6대(법정), 8대(계획)
- 조 경 면 적 : 11.55(법정), 13.34m²(계획)

The image displays four distinct architectural elevation drawings of modern buildings, each characterized by a light gray grid pattern. The buildings are set against a solid blue sky and a dark gray ground plane. The first building on the left features a central vertical section with five windows, each marked with a red downward-pointing triangle, and a dark gray base. The second building has a dark gray base and two balconies with blue railings. The third building is more complex, with multiple balconies and a dark gray base. The fourth building on the right has a dark gray base and a dark gray vertical section on its right side. All buildings have various window sizes and placements, some with blue panes.


좌측면도

[illegible]

4. 설계자 의도

■ 디자인 의도

- 보행자, 차량 출입의 원활한 계획
- 도로측에 순응한 주동 배치
- 정면성을 강조하는 디자인 계획

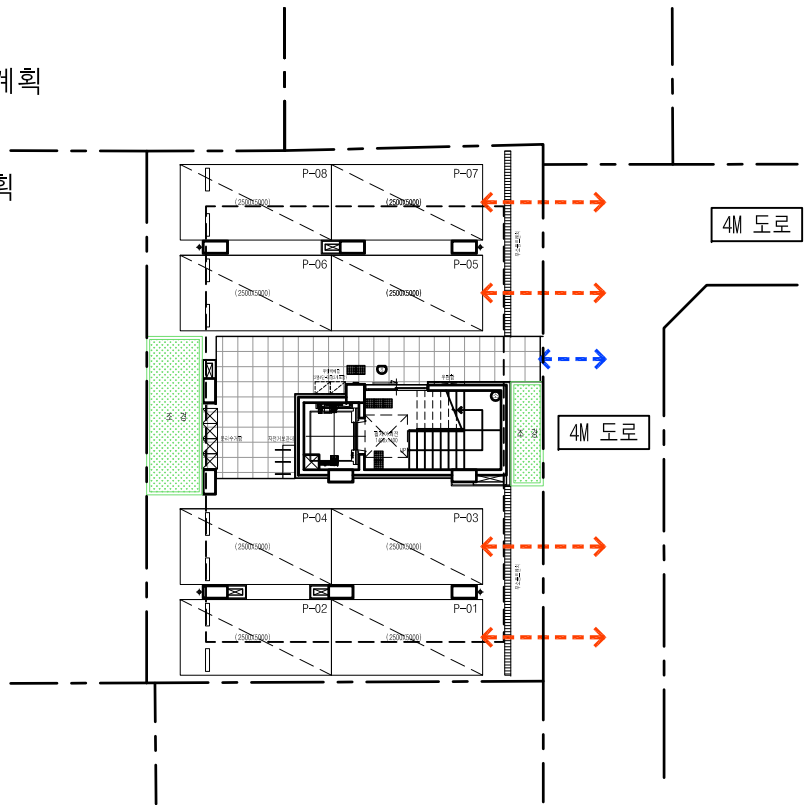

■ 입면 디자인 계획

- 창호크기 및 열을 맞추어 입면에 정돈된 이미지를 부여함.


단조롭고 심심한 입면에 면분할을 활용하여 단조로운 입면계획 탈피.

동일한 창호 배치로 단정함과 균일성을 부여하여 통일감 표현.



5. 재료계획

1. 외벽 마감재

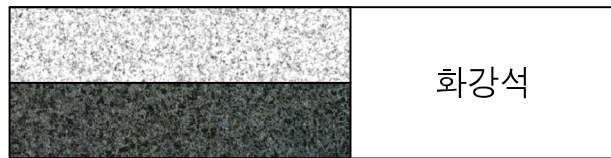

2. 주차장 바닥재



3. 옥외 난간대



■ 외장재

구분	실명	재료명
1층	필로티 주차장	바닥 : 칼라무늬콘크리트 천정 : 내풍압형 AL 천정재
	현관	바닥 : 폴리싱타일
2~5층	방	바닥 : 데코타일 마감 천정 : 실크 또는 발포벽지
	거실	바닥 : 데코타일 마감 천정 : 실크 또는 발포벽지
	베란다	바닥 : 칼라 콘크리트 천정 : AL 천정판

■ 내장재

6. 색채계획

- 자연스러운 색상과 주변과의 조화
- 주변과 어울리는 색상을 활용한 입면 계획
- 가로경관 미관성 및 친근성



고층석 계열 : 화강석

거창석 계열 : 화강석

마천석 계열 : 화강석

PROJECT TITLE
사업명
강동구 성내동 404-14호
도시형생활주택(소형주택) 신축공사
다세대주택 신축공사

NAME OF DRAWING
도면명

디자인 의도

NOTE
주 기

NO. ▲ REVISIONS ▲ DATE
번호 수정 일자

DESIGNED BY
설 계

CHECKED BY
심 사

APPROVED BY
승 인

CONSULTANTS
협 동 설 계




SCALE
축척 1/

DATE
일 자 2024. 02.

DWG NO.
도면 번호 A-03

SHEET NO.
일련 번호 □-□□□

다움
다움
건축사사무소 다움건축
THE ARCHITECTS DESIGN GROUP
TEL. 02.414.6061 (☎)
FAX. 02.414.6062

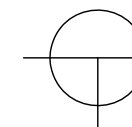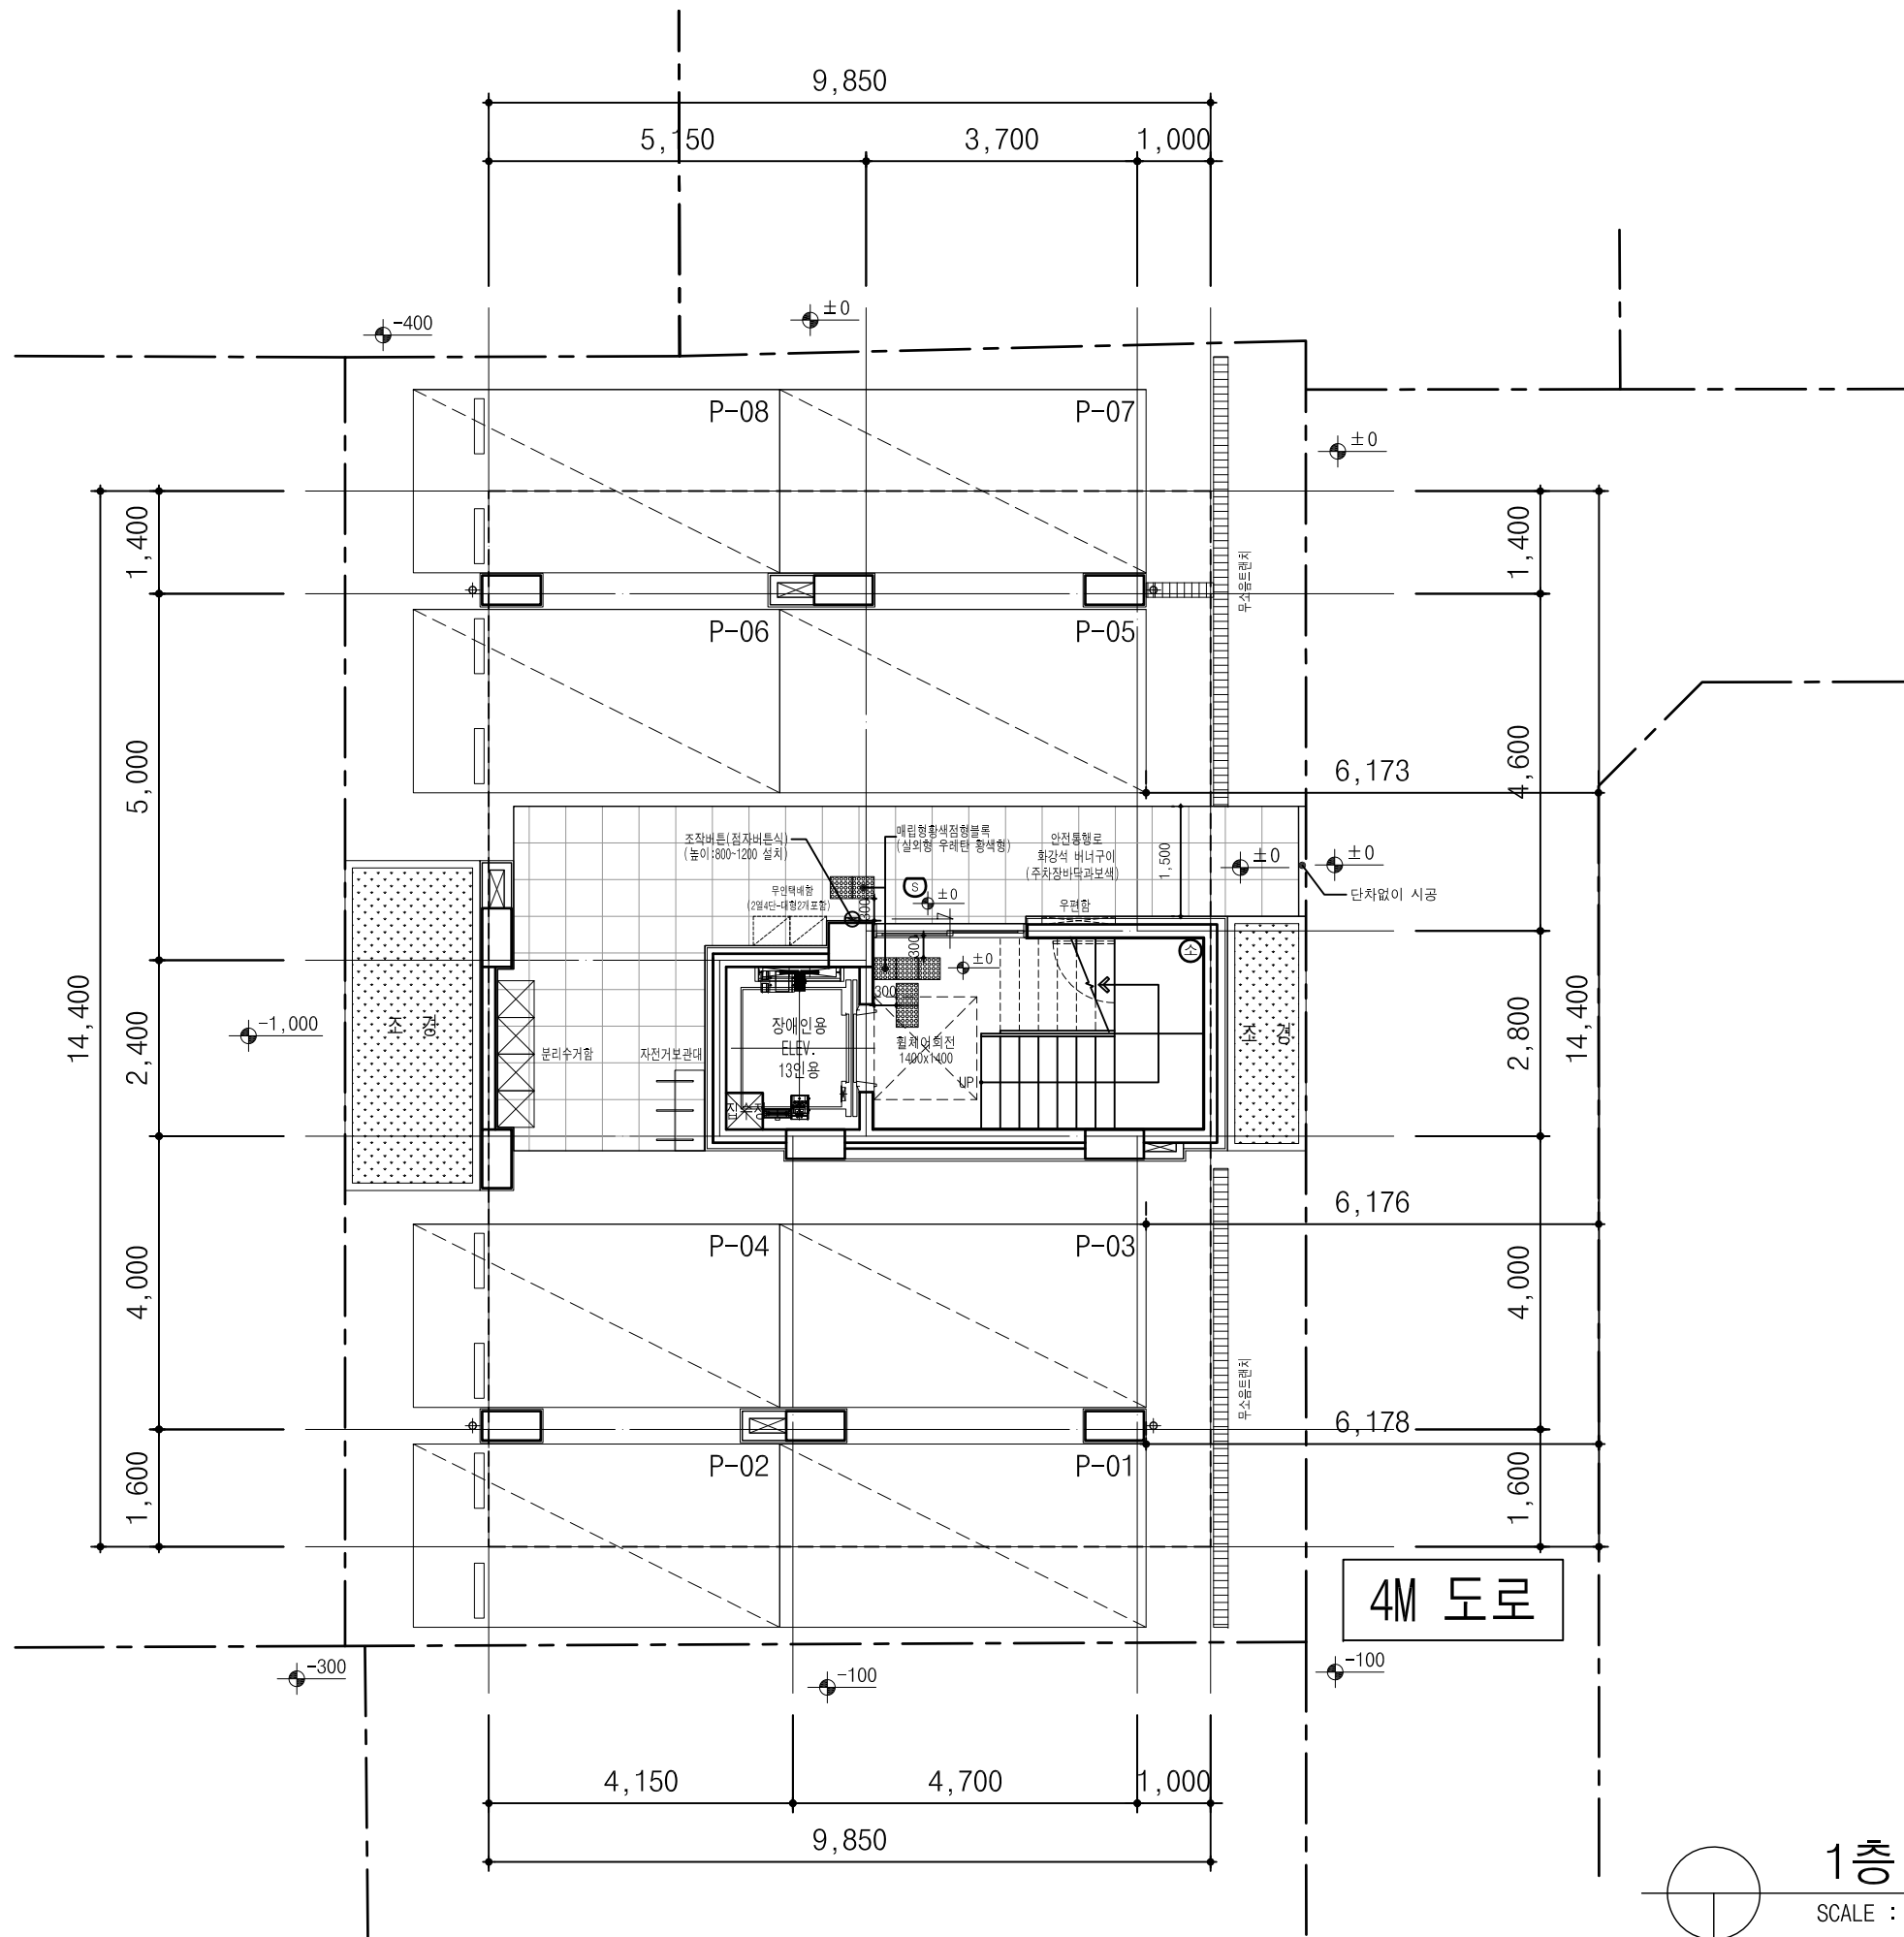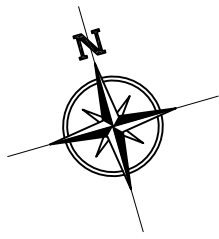

1층 평면도

SCALE : A3 : 1/100

PROJECT TITLE
사업명
강동구 성내동 404-14호
도시형생활주택(소형주택) 신축공사
다세대주택 신축공사

NAME OF DRAWING
도면명
1층 평면도

- NOTE
주 기
- 단독경보감지기(연기식)
 - 단독경보감지기(열감지)
 - ABC분말소화기(2.5KG)
 - 가스누설경보기
 - 일산화탄소경보기
 - 차면시설
 - 보일러
 - 에어컨 실외기

NO. ▲ REVISIONS ▲ DATE
번호 수정 일자

DESIGNED BY
설 계

CHECKED BY
검 사

APPROVED BY
승 인

CONSULTANTS
협 동 설 계




SCALE
축척 1/100

DATE
일 자 2024. 09.

DWG NO.
도면 번호 A-31

SHEET NO.
일련 번호 □-□□□

다움건축
dawoom
건축사사무소 다움건축
THE ARCHITECTS DESIGN GROUP
TEL. 02.414.6061 (☎)
FAX. 02.414.6062

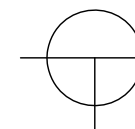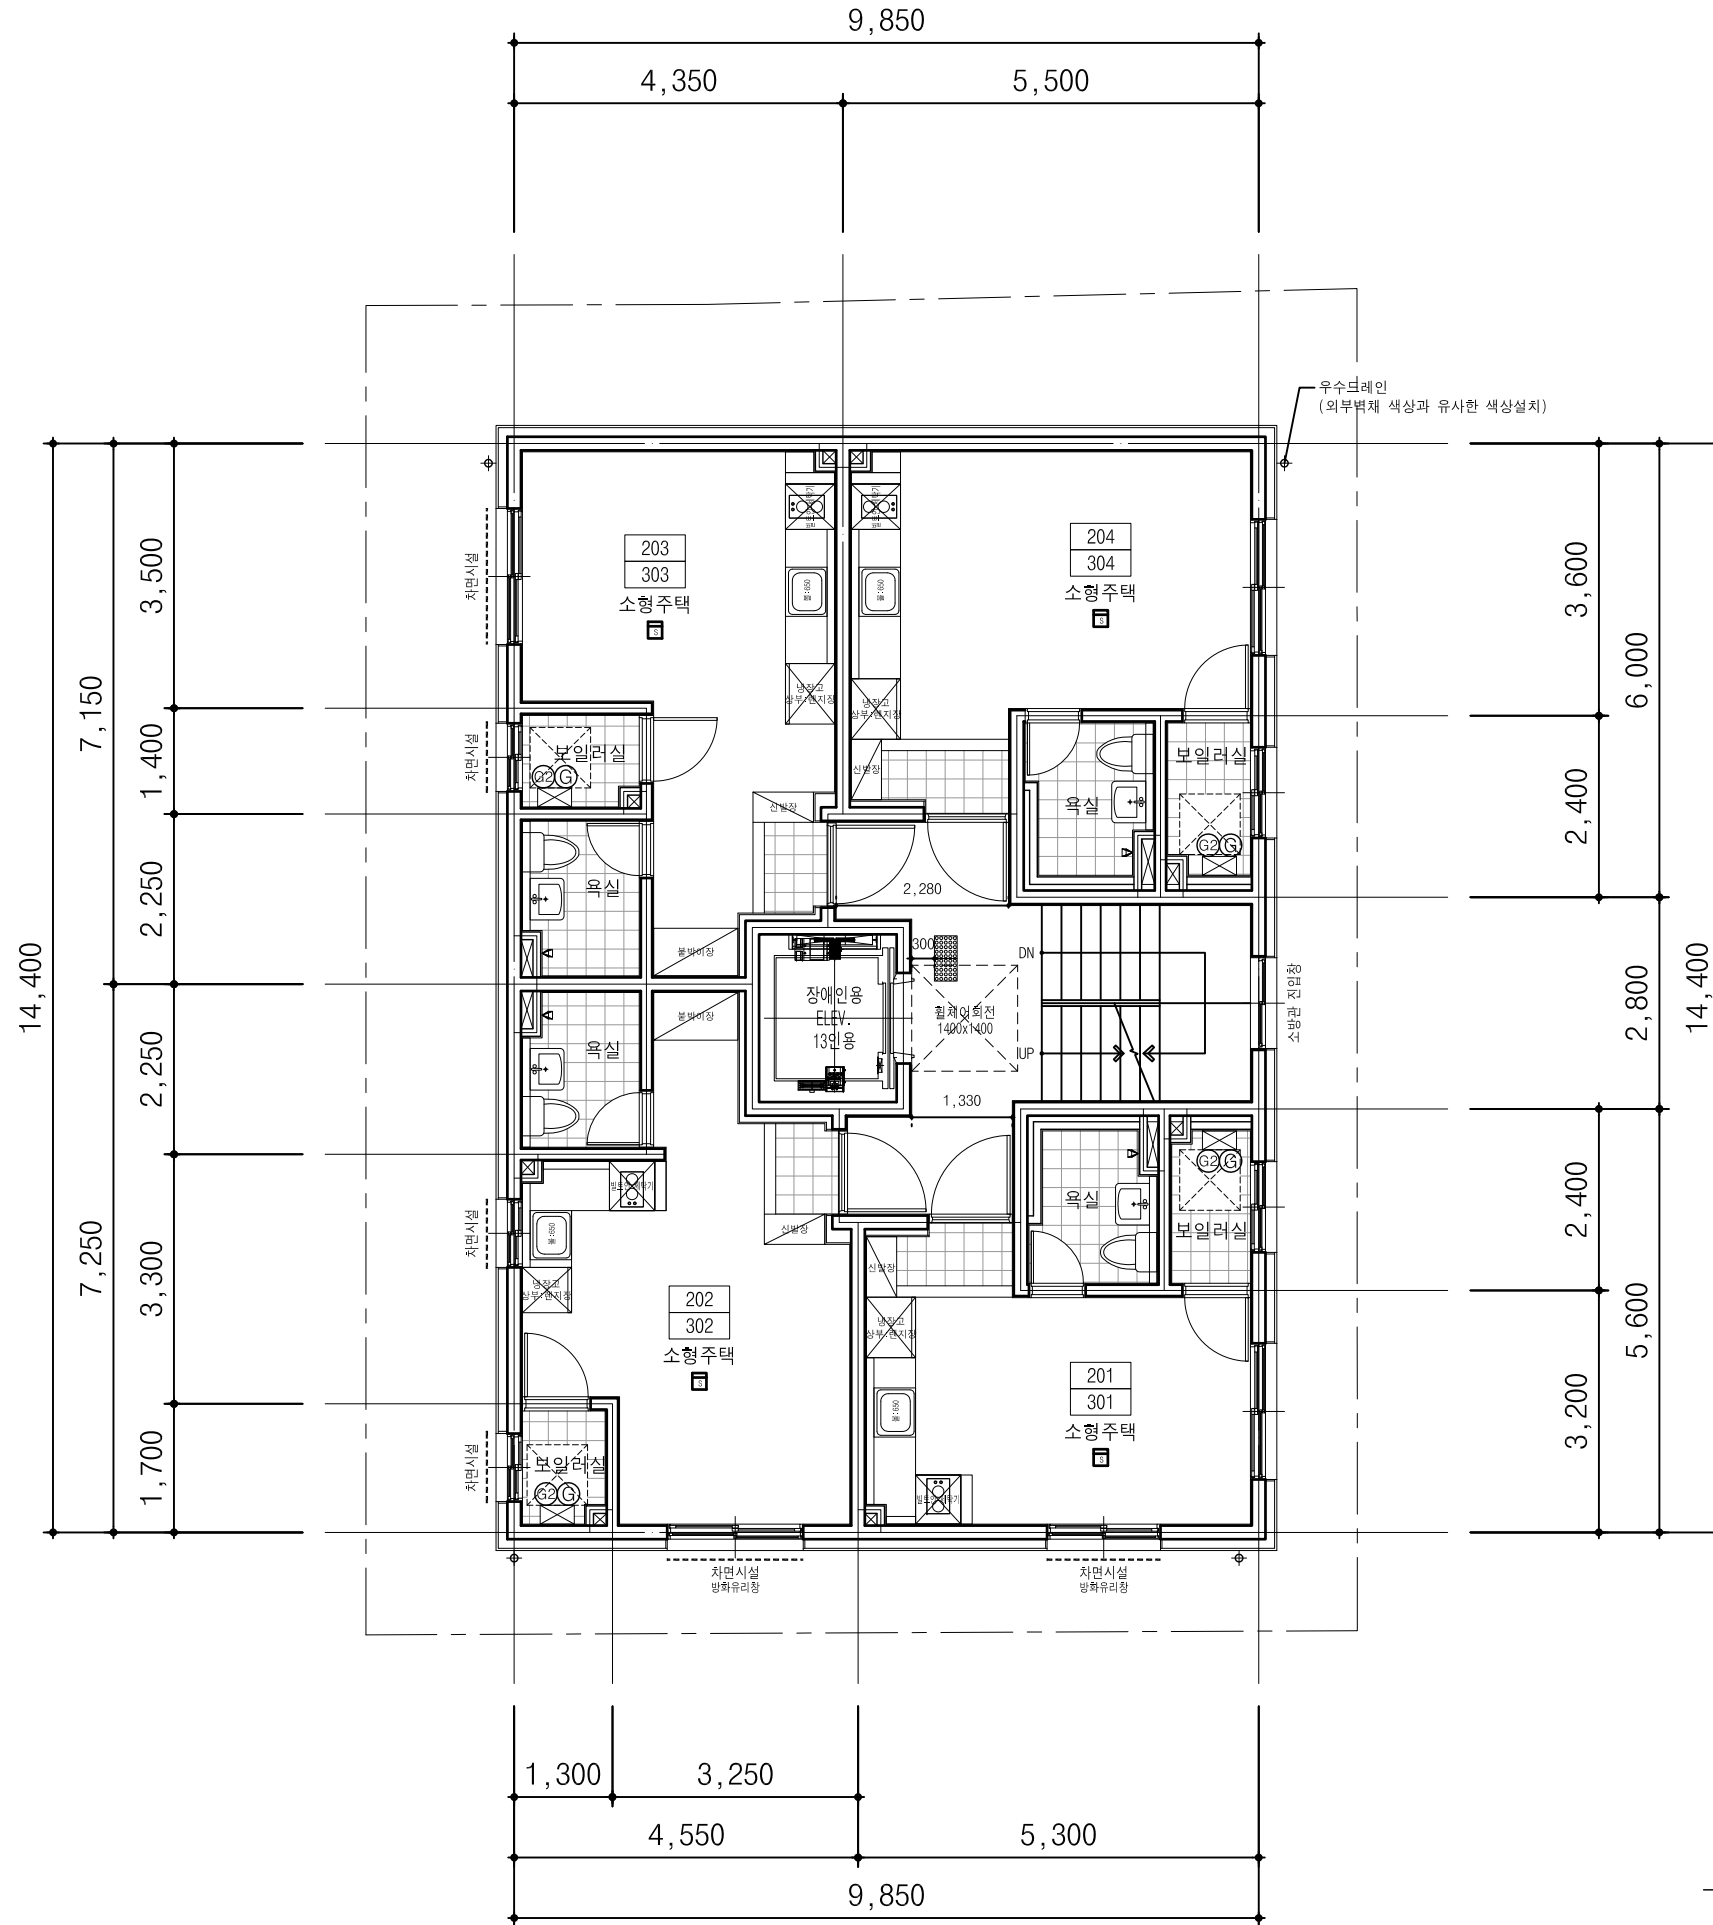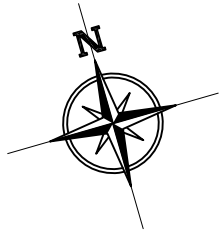

2~3층 평면도
SCALE : A3 : 1/100

PROJECT TITLE
사업명
강동구 성내동 404-14호
도시형생활주택(소형주택) 신축공사
다세대주택 신축공사

NAME OF DRAWING
도면명

2~3층 평면도

NOTE
주 기

- 단독경보감지기(연기식)
- 단독경보감지기(열감지)
- ABC분말소화기(2.5KG)
- 가스누설경보기
- 일산화탄소경보기
- 차면시설
- 보일러
- 에어컨 실외기

NO. ▲ REVISIONS ▲ DATE
번호 수정 일자

DESIGNED BY
설 계

CHECKED BY
심 사

APPROVED BY
승 인

CONSULTANTS
협 동 설 계




SCALE
축척 1/100

DATE
일 자 2024. 09.

DWG NO.
도면 번호 A-32

SHEET NO.
일련 번호 □-□□□


dawoom
건축사사무소 다음건축
THE ARCHITECTS DESIGN GROUP
TEL. 02.414.6061 (☎)
FAX. 02.414.6062

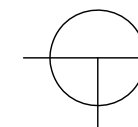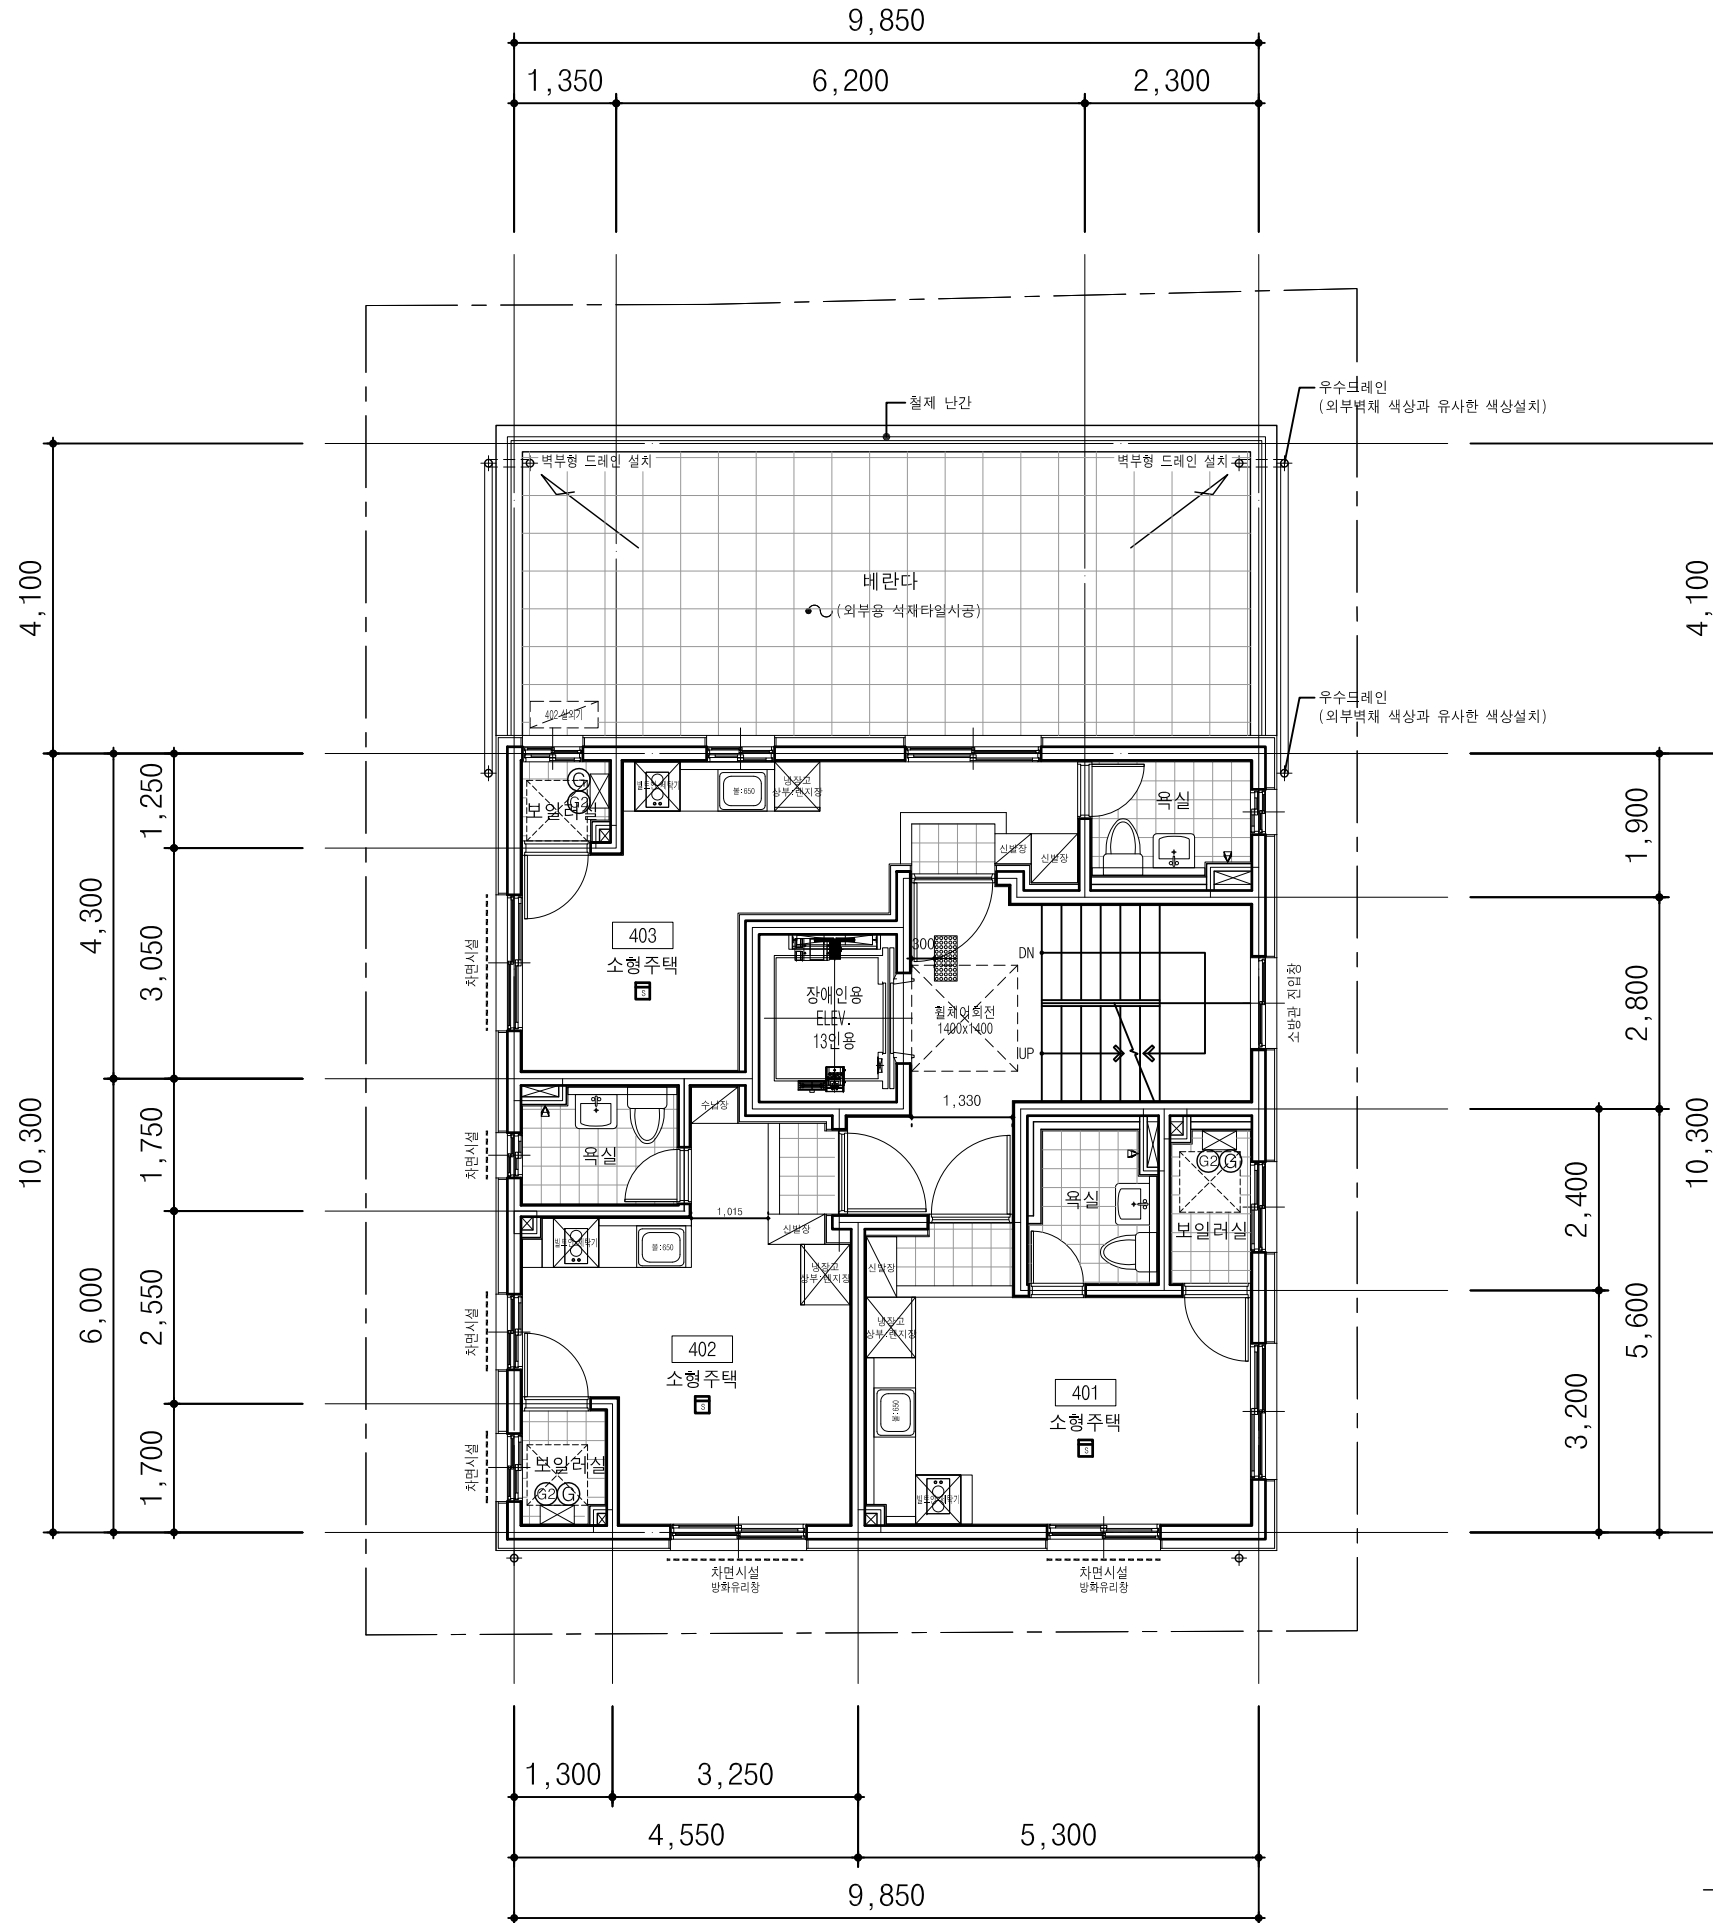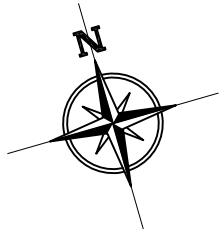

4층 평면도
SCALE : A3 : 1/100

PROJECT TITLE
사업명

강동구 성내동 404-14호
도시형생활주택(소형주택) 신축공사
다세대주택 신축공사

NAME OF DRAWING
도면명

2~3층 평면도

NOTE
주 기

- 단독경보감지기(연기식)
- 단독경보감지기(열감지)
- ABC분말소화기(2.5KG)
- 가스누설경보기
- 일산화탄소경보기
- 차면시설
- 보일러
- 에어컨 실외기

NO. ▲ REVISIONS ▲ DATE
번호 수정 일자

DESIGNED BY
설 계

CHECKED BY
검 사

APPROVED BY
승 인

CONSULTANTS
협 동 설 계



SCALE
축 척 1/100

DATE
일 자 2024. 09.




DWG NO.
도면 번호 A-33

SHEET NO.
일련 번호 □-□□□

 DAWOM
건축사사무소 다음건축
THE ARCHITECTS DESIGN GROUP
TEL. 02.414.6061 (☎)
FAX. 02.414.6062

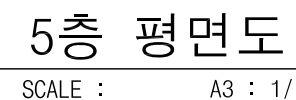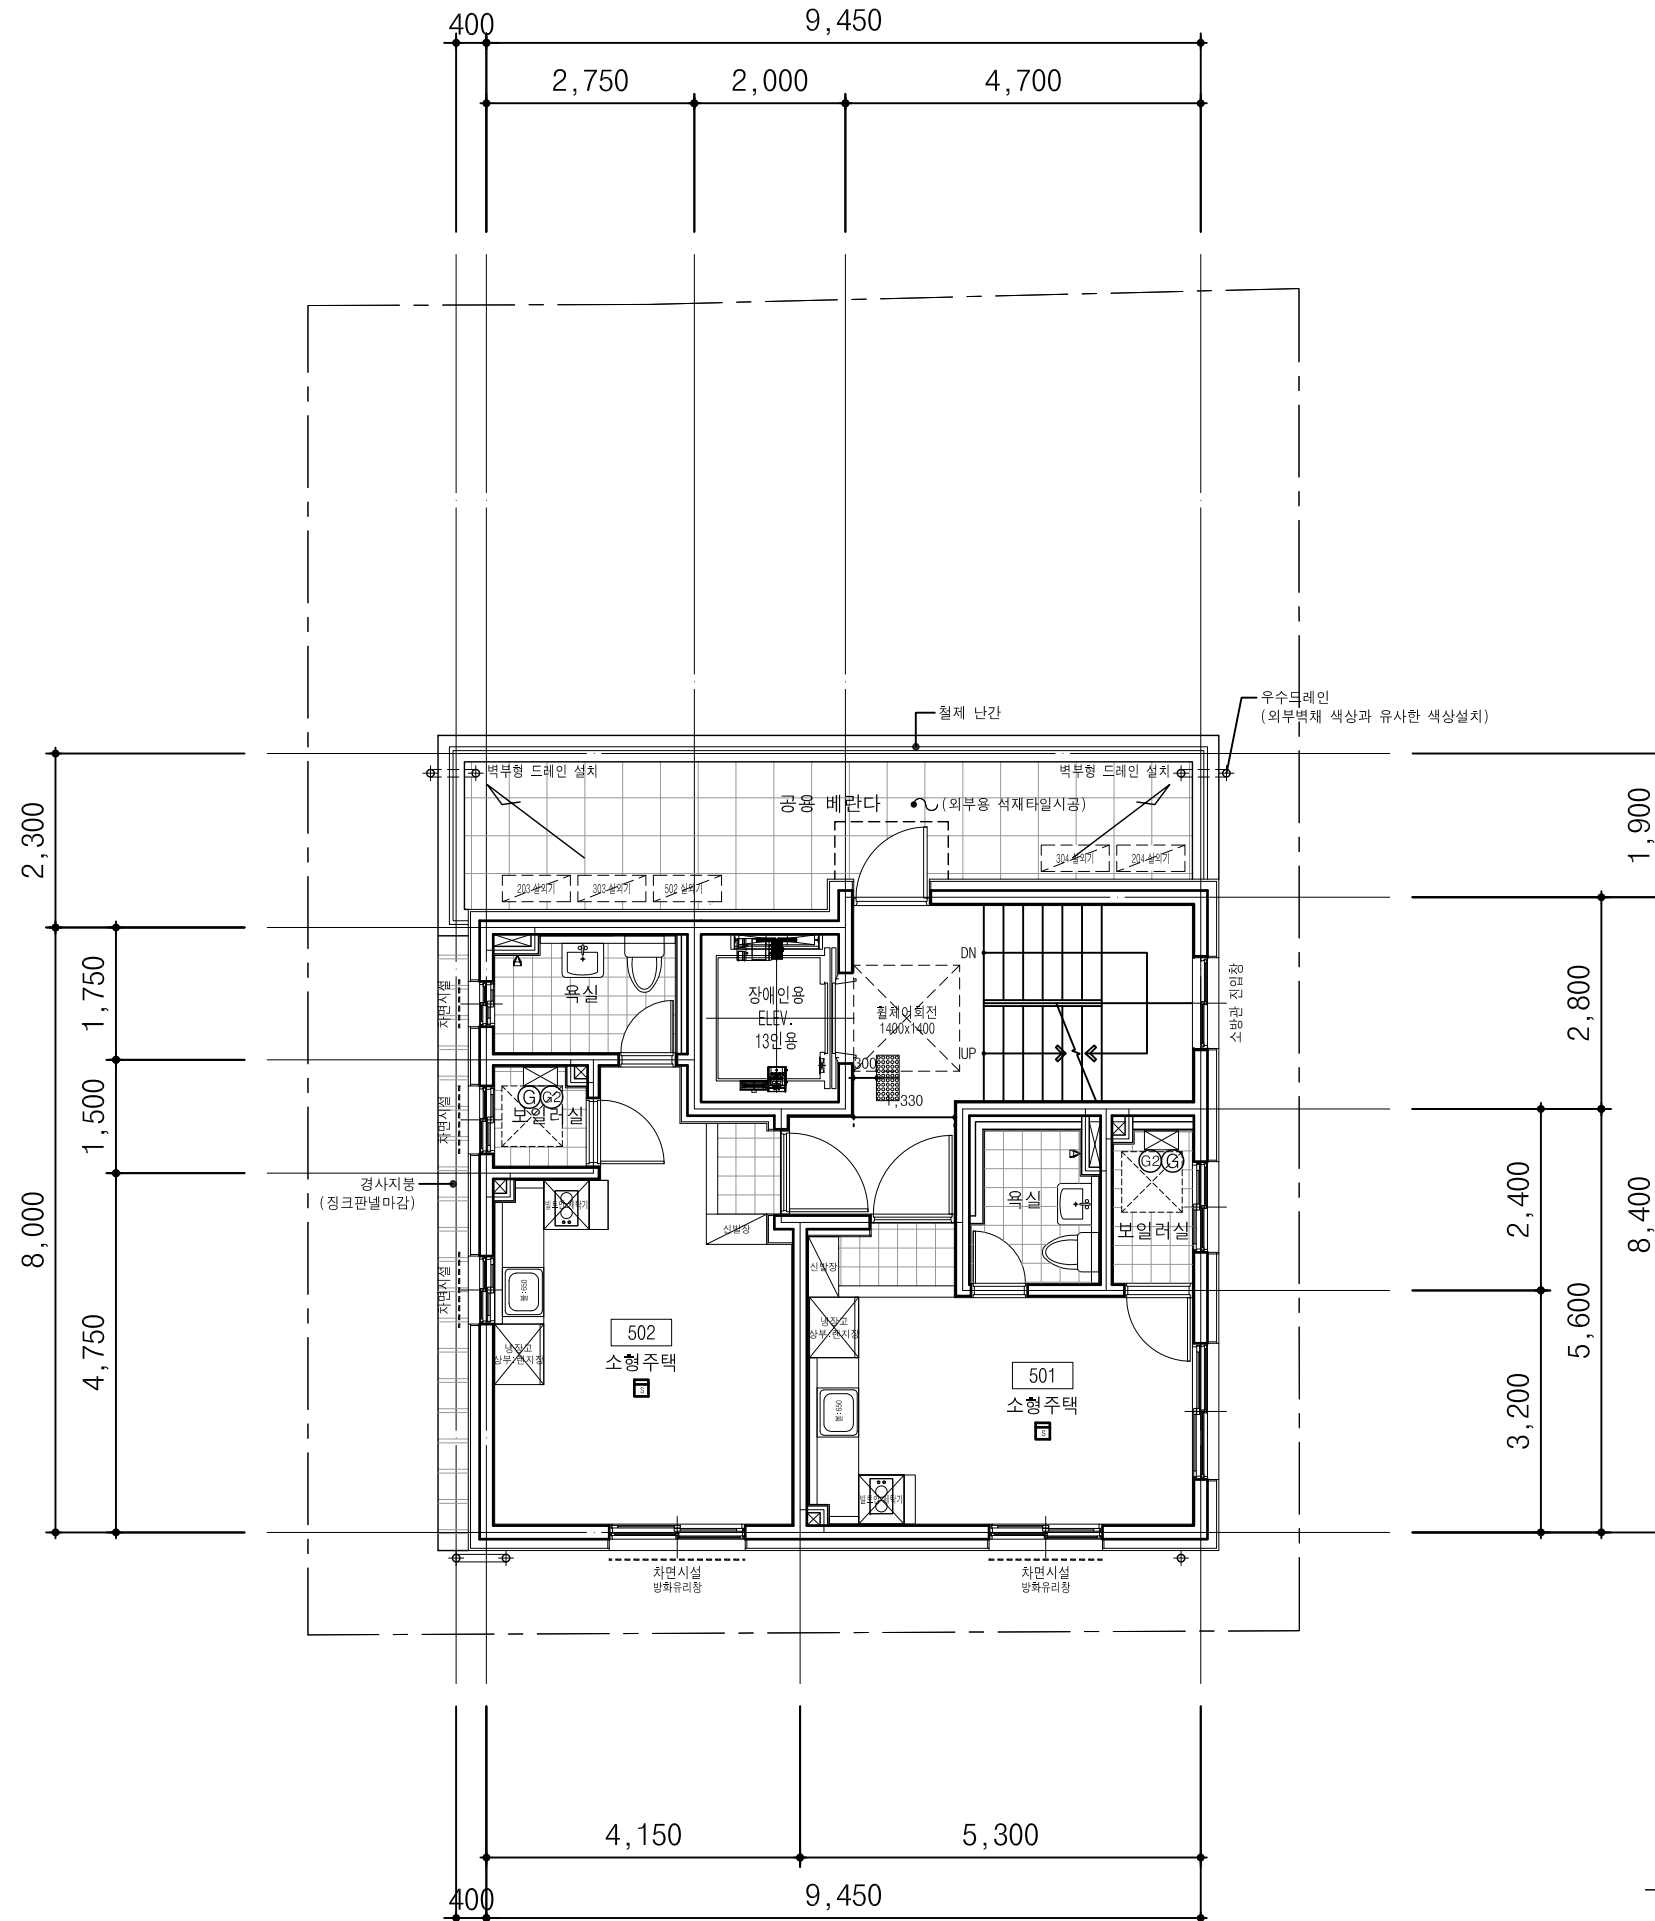

다움건축
THE ARCHITECTS DESIGN GROUP
TEL. 02.414.6061 (代)
FAX. 02.414.6062

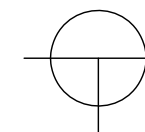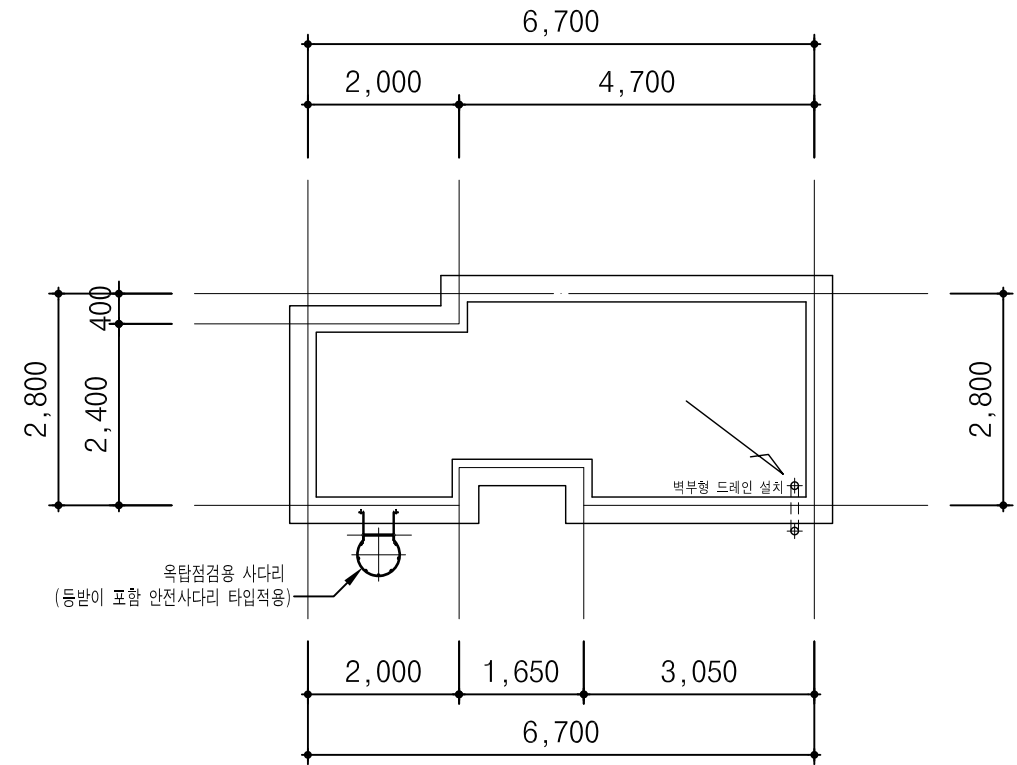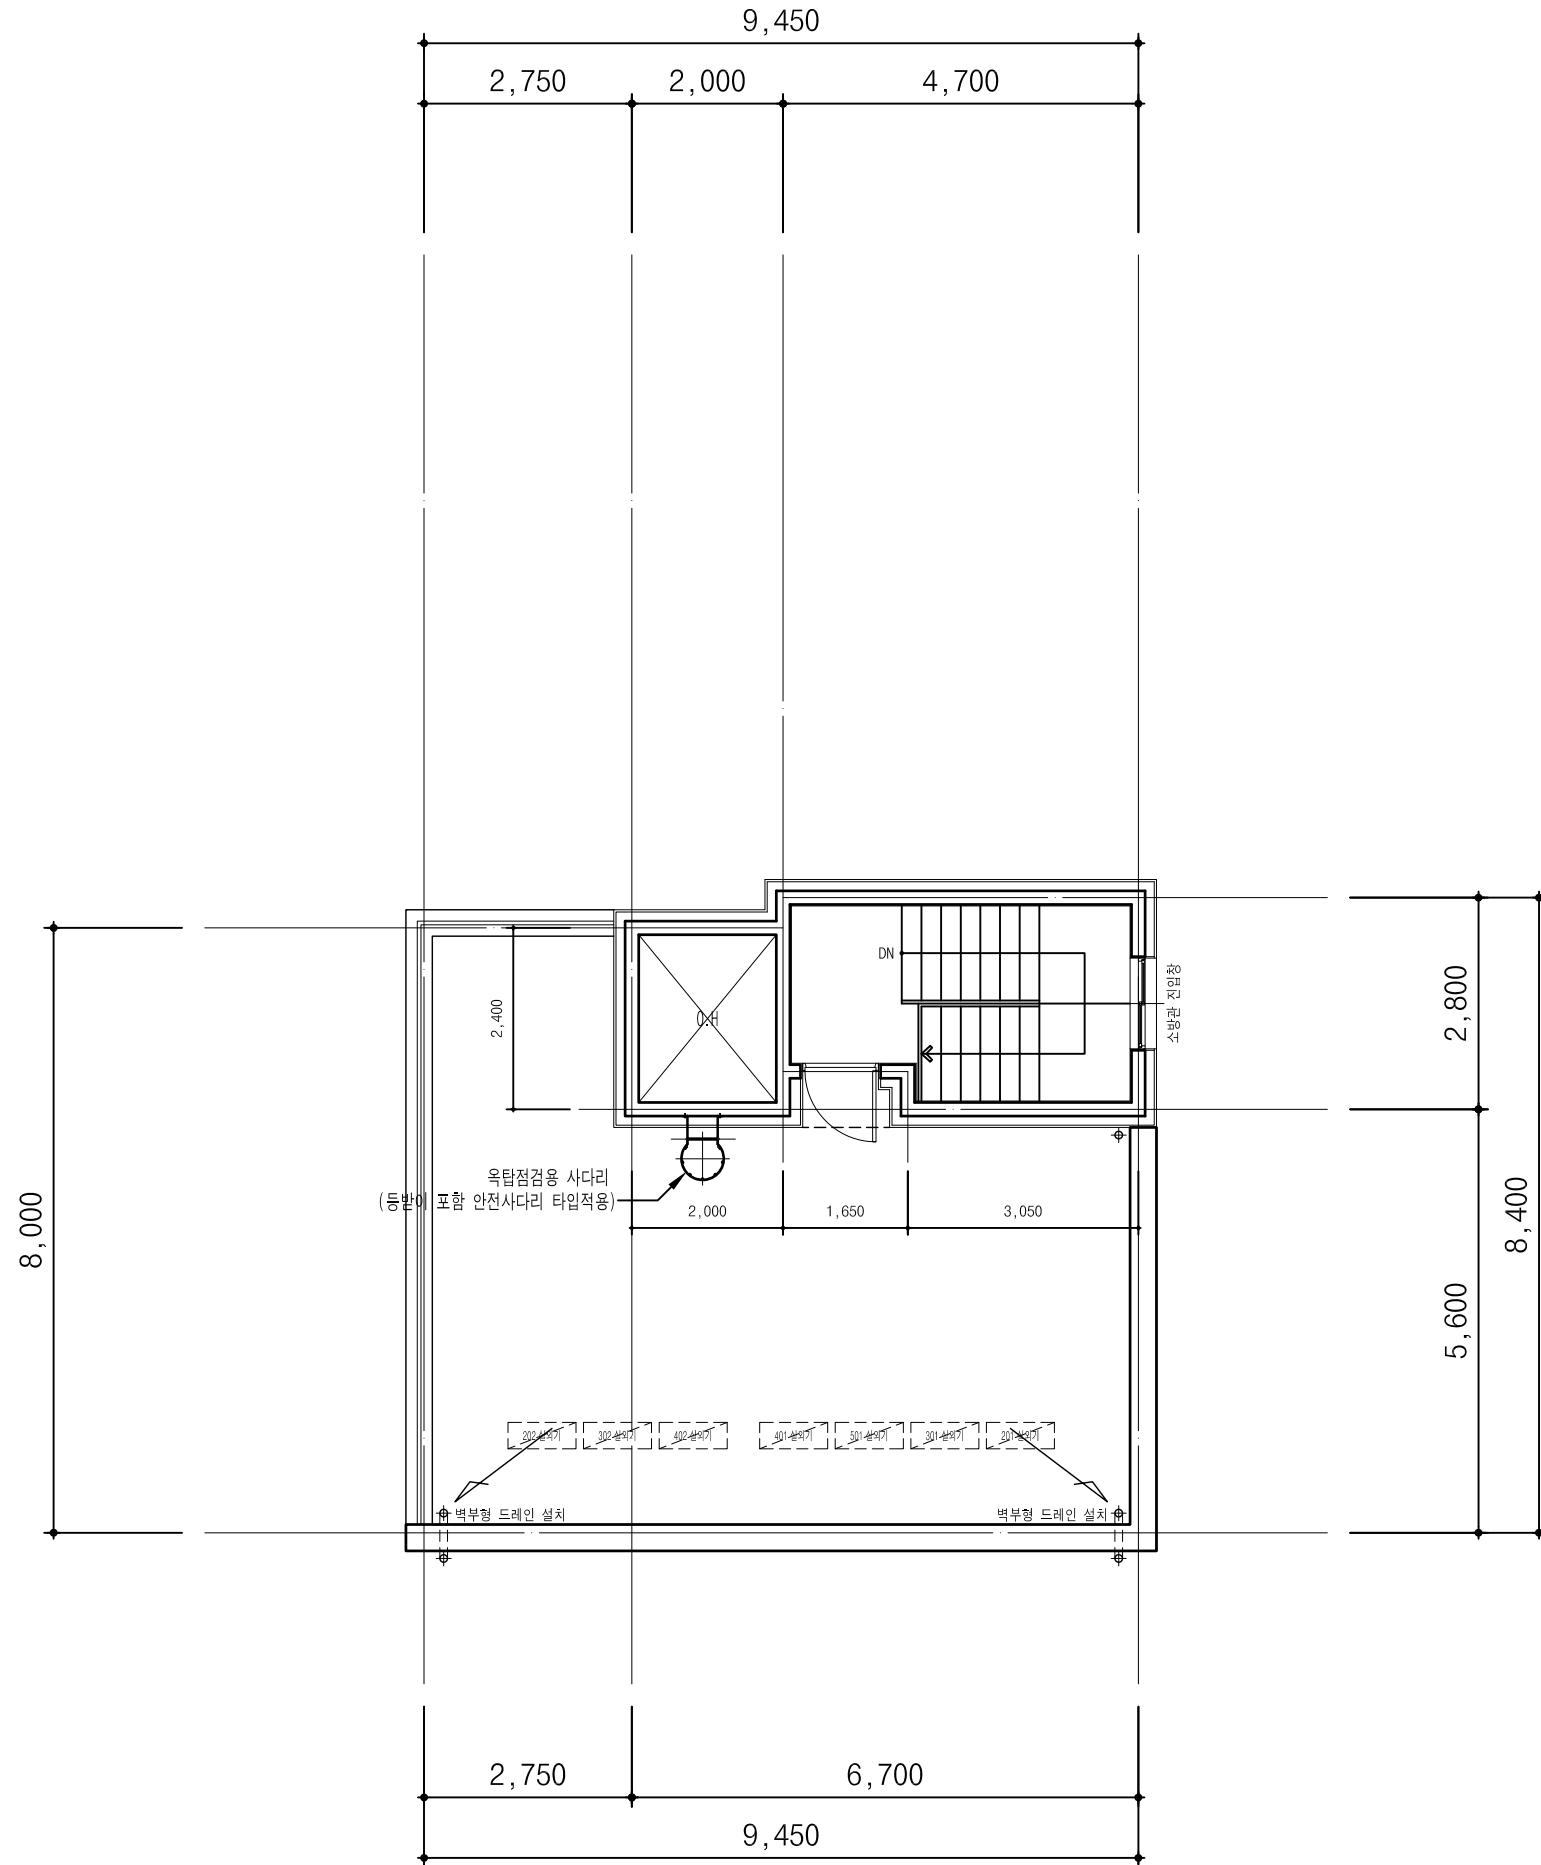

지붕밋옥탑 평면도

SCALE : A3 : 1/100

PROJECT TITLE
사업명
강동구 성내동 404-14호
도시형생활주택(소형주택) 신축공사
다세대주택 신축공사

NAME OF DRAWING
도면명
지붕밋옥탑 평면도

NOTE
주
기

NO. ▲ REVISIONS ▲ DATE
번호 수정 일자

DESIGNED BY
설계

CHECKED BY
심사

APPROVED BY
승인


CONSULTANTS
협동설계


SCALE
축척 1/100

DATE
일자 2024. 09.

DWG NO.
도면번호 A-35


SHEET NO.
일련번호 □-□□□

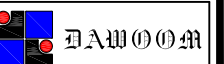
다움건축
건축사사무소 다움건축
THE ARCHITECTS DESIGN GROUP
TEL. 02.414.6061 (代)
FAX. 02.414.6062

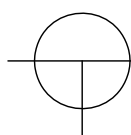


정 면 도

SCALE : A3 : 1/100

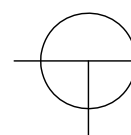

우 측 면 도

SCALE : A3 : 1/100

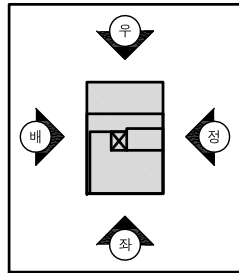

PROJECT TITLE
사업명
강동구 성내동 404-14호
도시형생활주택(소형주택) 신축공사
다세대주택 신축공사

NAME OF DRAWING
도면명
입면도-1

NOTE
주 기

창호 PVC 블랙
소방관진입창 - 스티커 부착

NO. ▲ REVISIONS ▲ DATE
번호 수정 일자

DESIGNED BY
설 계

CHECKED BY
심 사

APPROVED BY
승 인

CONSULTANTS
협 동 설 계


SCALE
축척 1/100

DATE
일 자 2024. 09.

DWG NO.
도면 번호 A-41

SHEET NO.
일련 번호 □-□□□

 **다원건축**
다원건축
건축사무소 다원건축
THE ARCHITECTS DESIGN GROUP
TEL. 02.414.6061 (☎)
FAX. 02.414.6062

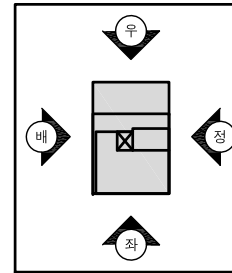

PROJECT TITLE
사업명
강동구 성내동 404-14호
도시형생활주택(소형주택) 신축공사
다세대주택 신축공사

NAME OF DRAWING
도면명
입면도-2

NOTE
주 기
창호 PVC 블랙

NO. ▲ REVISIONS ▲ DATE
번호 수정 일자

DESIGNED BY
설 계

CHECKED BY
심 사

APPROVED BY
승 인

CONSULTANTS
협 동 설 계

SCALE
축척 1/100

DATE
일 자 2024. 09.

DWG NO.
도면 번호 A-42

SHEET NO.
일련 번호 □-□□□


THE ARCHITECTS DESIGN GROUP
TEL. 02.414.6061 (代)
FAX. 02.414.6062

배 면 도
SCALE : A3 : 1/100

좌 측 면 도
SCALE : A3 : 1/100