

NOTE

- ⑦ 단독경보감지기(연기)
- ⑧ 단독경보감지기(열)
- ⑨ ABC분말소화기(3.3KG)

- 차면시설
- | | |
|---|-----|
|  | 보일러 |
|  | 에어컨 |
- ※구조일반사항*
1. 콘크리트: $f_c k = 24 \text{ Mpa}$
 2. 철근: $f_y = 400 \text{ Mpa}$
 3. 새디배벽두께: 150mm(복배근)
 4. 외벽두께: 180mm(복배근)
 5. 코어벽두께: 180mm(복배근)
 6. 새디간벽두께: 180mm(복배근)


Fire Protection



Drawing Title:

1층 평면도


A- 20

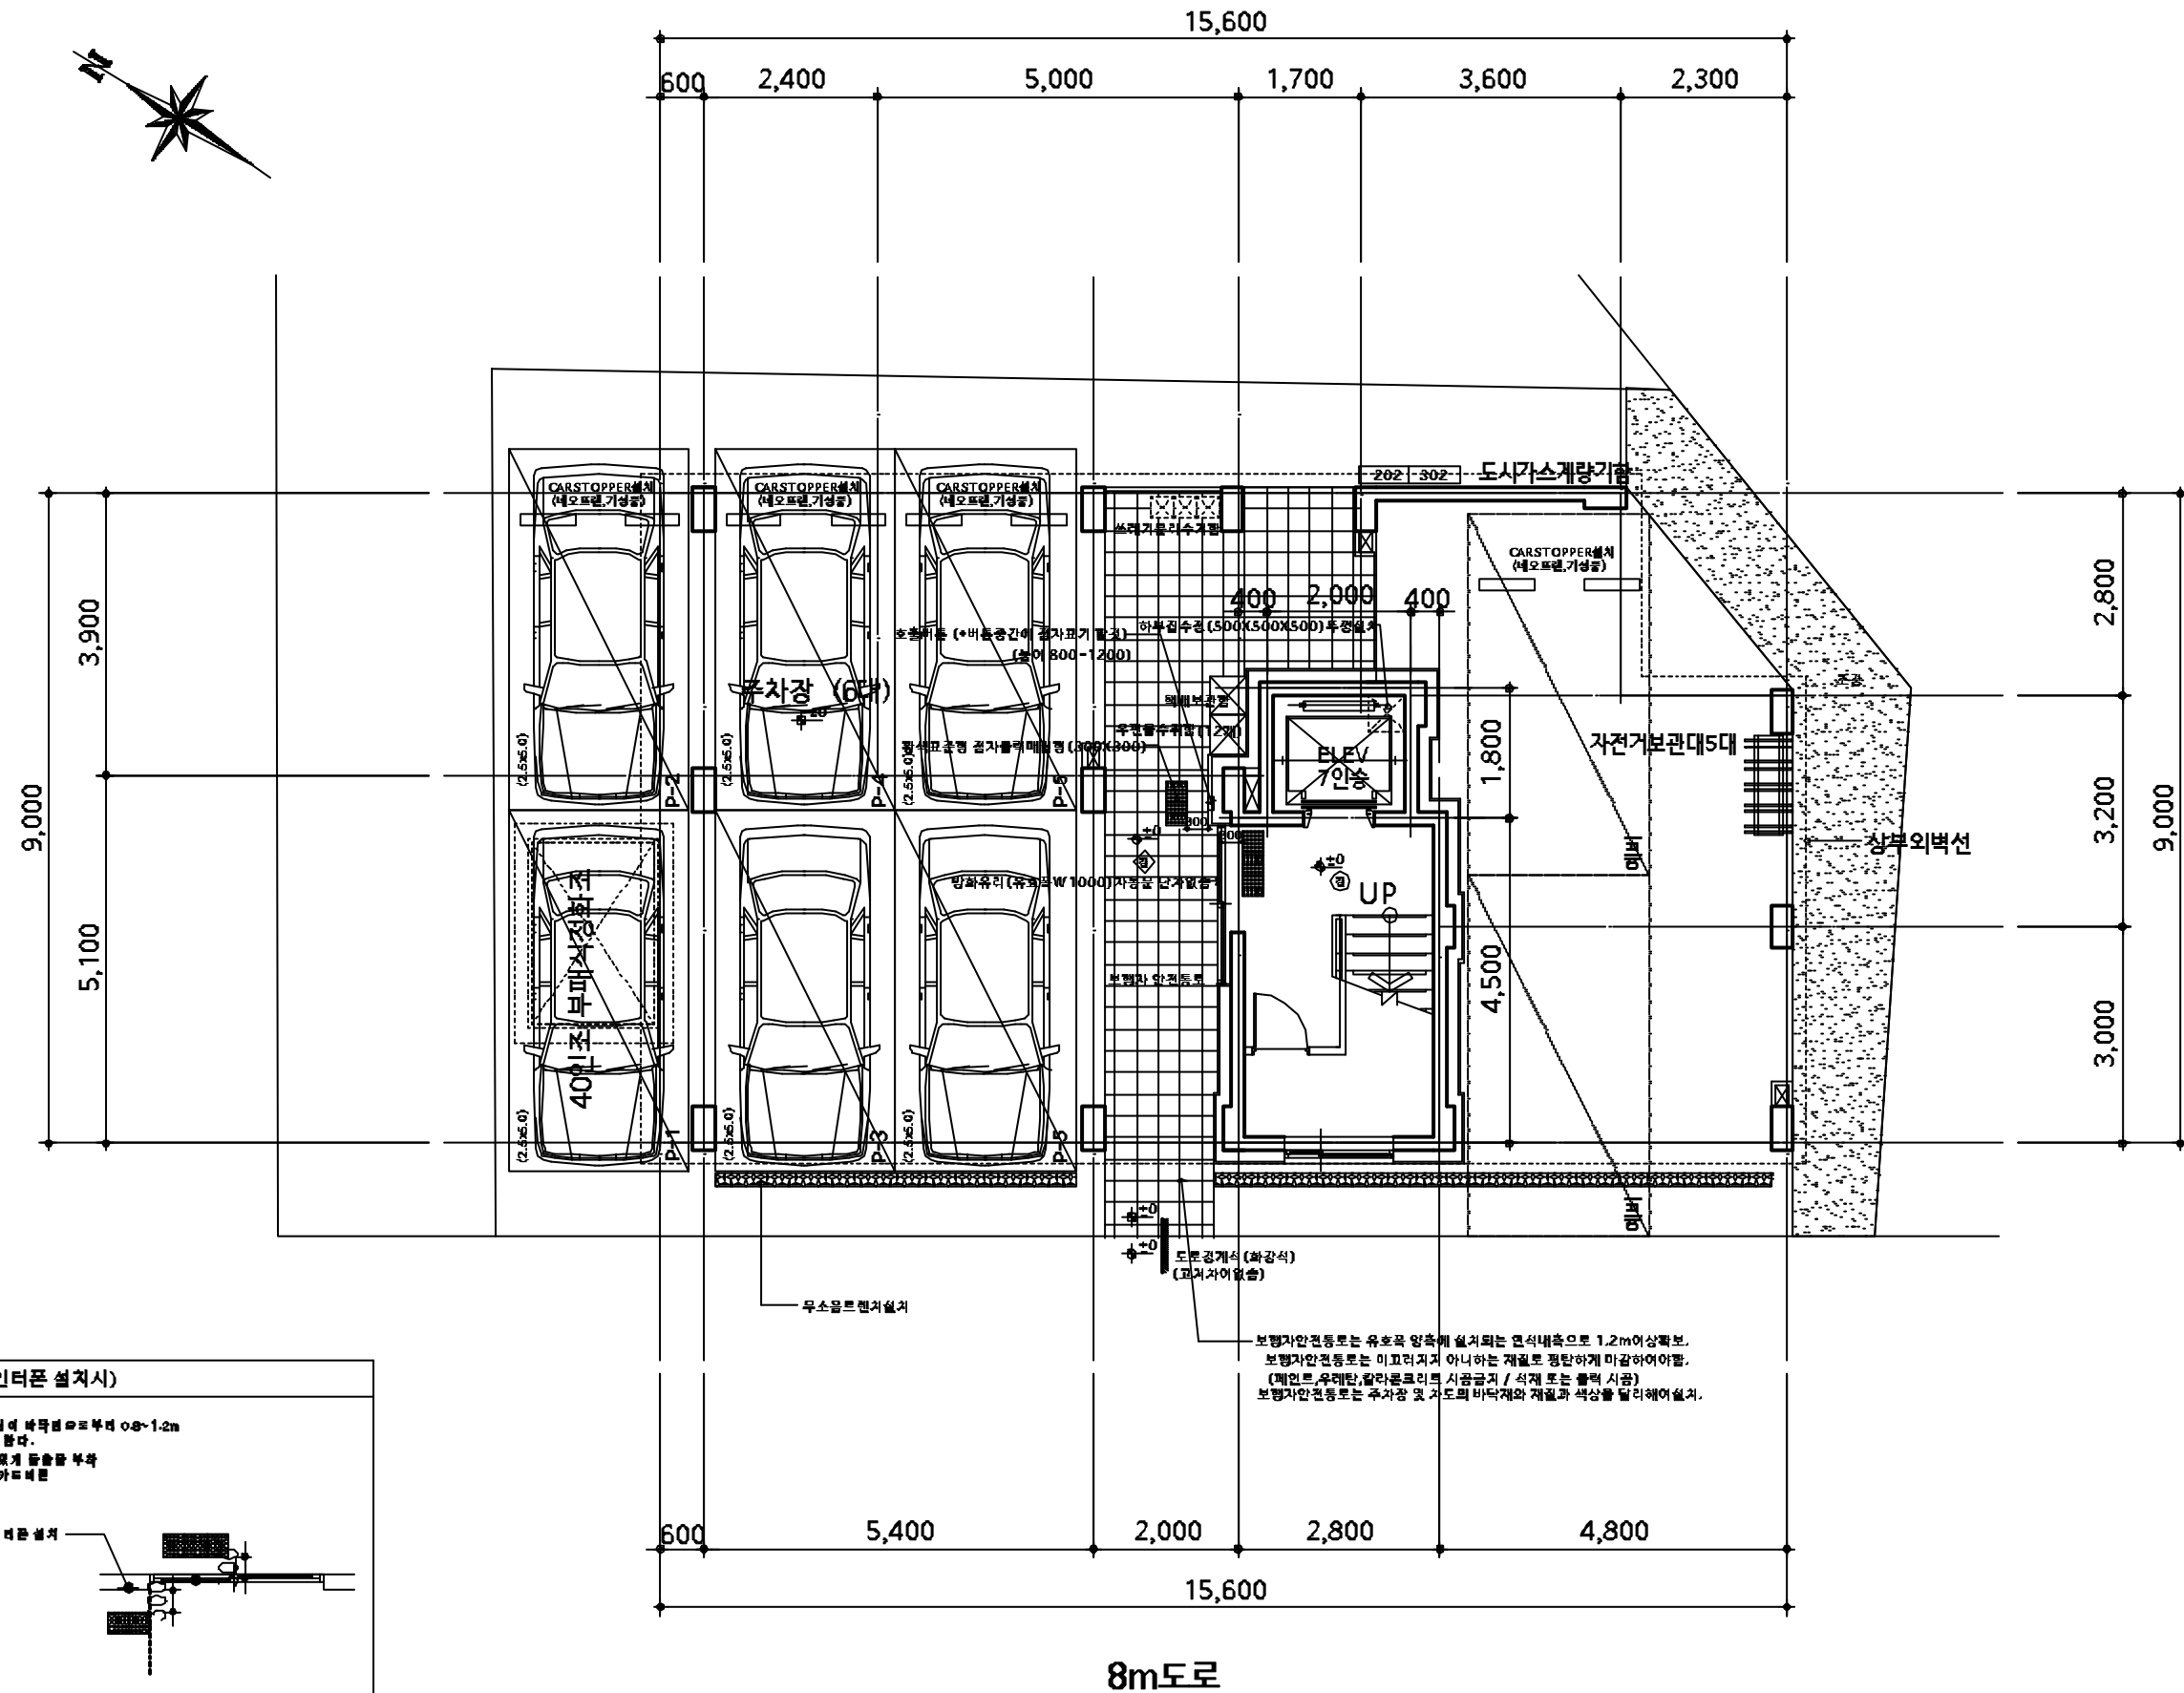

■ 출입문 버튼 설치 (인터폰 설치시)

비밀함으로 비문은 그 중심에 박막질로부터 0.8~1.2m
높이에 위치하도록 설치한다.


서각공에 연이구로 물을 수 있게 물을 받기
를 위한 비밀함으로 못 카트 비문

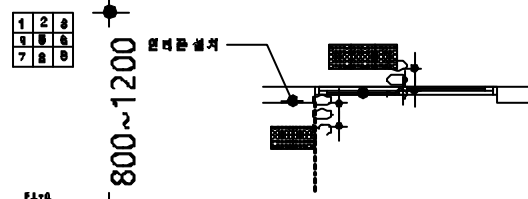

원터콘 설치시 점층물류는 원터콘 점면
0.3m여격 파여 2층, 주출입구 수변에
0.3m여격 파여 문턱바닥 설치해 아발.

1층 평면도

축척: 1/ 100

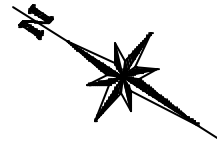

암사동 493-15
도시형생활주택
신축공사 (청년)

[illegible]

NOTE

- ① 단독경보감지기(연기)
- ② 단독경보감지기(열)
- ③ ABC분말소화기(3.3KG)

-----차면시설

☒	보일러(설비도면우선)
☒	에어컨(설비도면우선)

※구조일반사항※

1. 콘크리트: $f_c k = 24 \text{Mpa}$
2. 철근: $f_y = 400 \text{Mpa}$
3. 샤프트내벽두께: 150mm(복벽진)
4. 외벽두께: 180mm(복벽진)
5. 코아벽두께: 180mm(복벽진)
6. 샤프트간벽두께: 180mm(복벽진)
7. 스크류부두께: 210mm(복벽진)
(중간소홀)

Structure

Methoden

Electrical

Fire Protection



서울시 송파구 방이동 131-1 부경빌딩 2층
(주)부경건설(주)부경건설
TEL 02) 417-0606 FAX 02) 514-1852

Drawing Title

2.3층 평면도

Scale 1/100



2021.

Approved By:


Checked By:

Dr. Chongyi

Continued A- 21

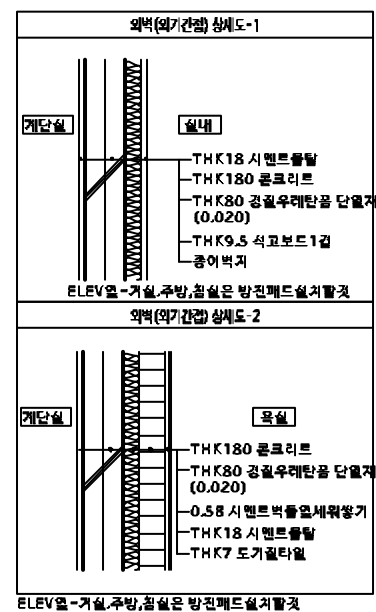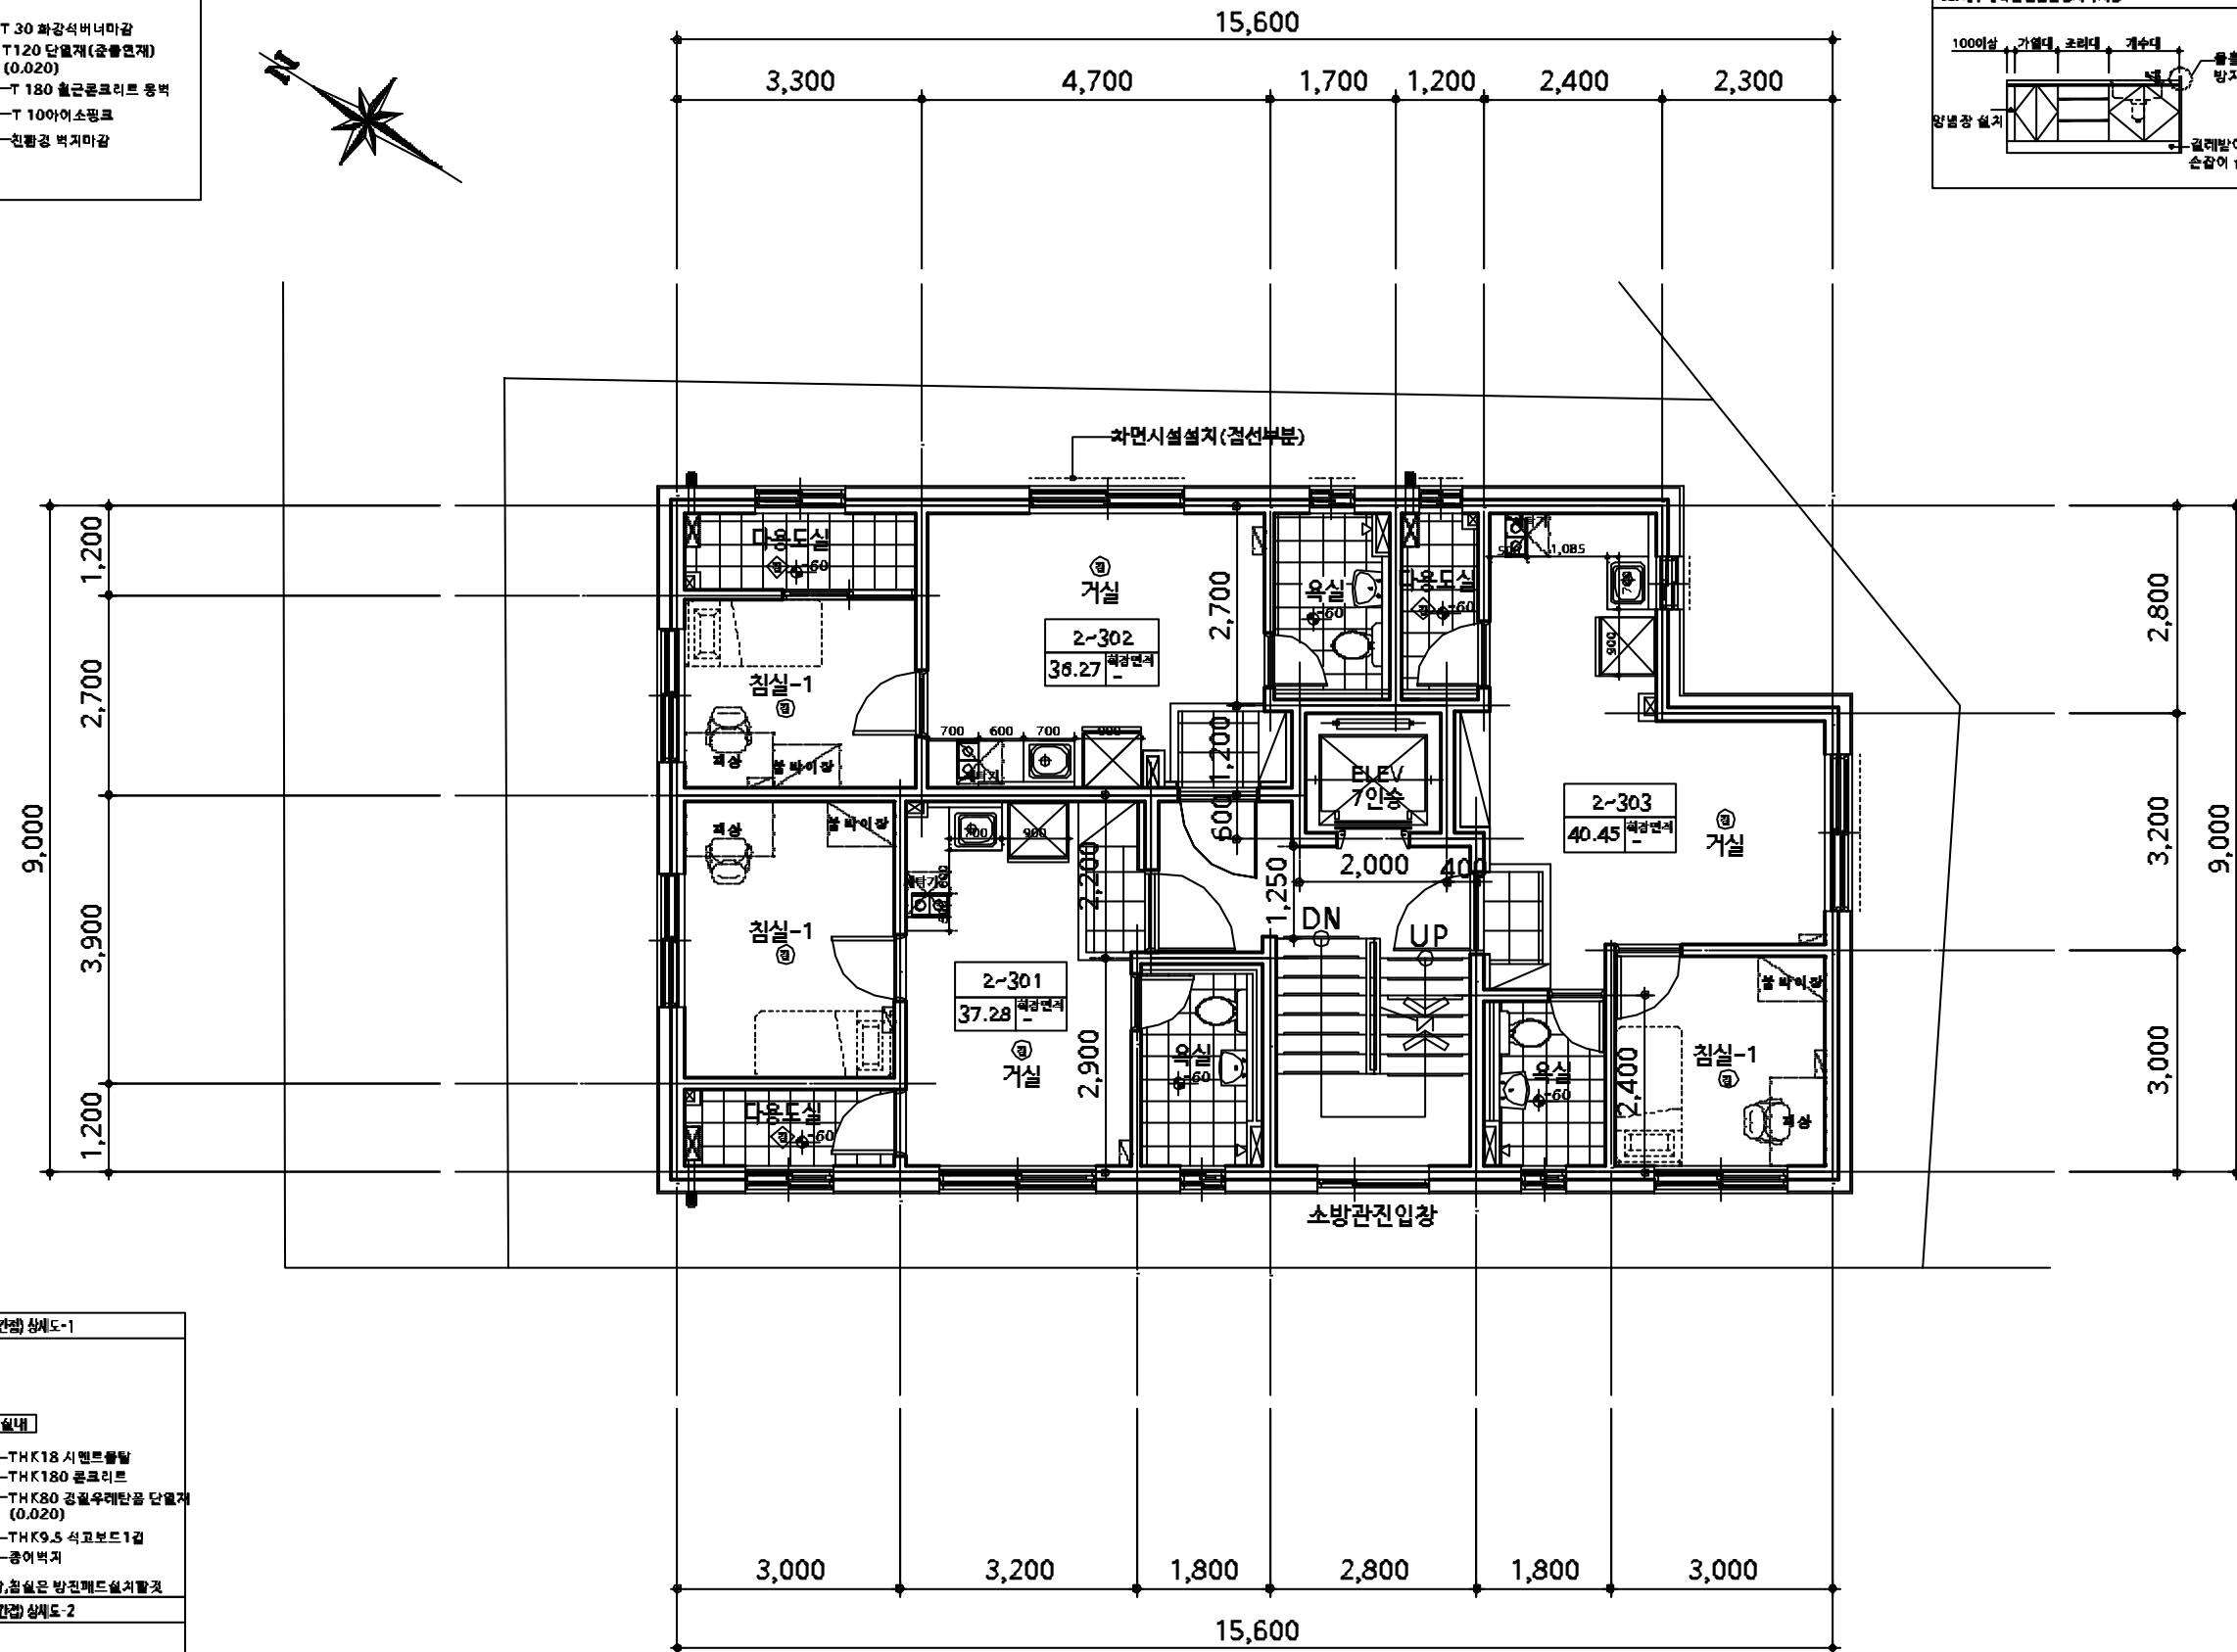

2,3층 평면도

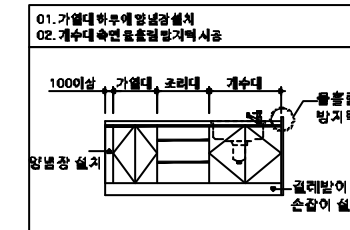

암사동 493-15
도시형생활주택
신축공사 (청년)

[illegible]

NOTE

- ㉠ 단독경보감지기(연기)
- ㉡ 단독경보감지기(열)
- ㉢ ABC분말소화기(3.3KG)

- 차면시설
- | | |
|---|-------------|
|  | 보일러(설비도면우선) |
|  | 에어컨(설비도면우선) |

구조일반시험


1. 콘크리트: $f_c = 24 \text{ Mpa}$
2. 철근: $f_y = 400 \text{ Mpa}$
3. 사다리배두께: 150 mm (복배근)
4. 외배두께: 180 mm (복배근)
5. 코아배두께: 180 mm (복배근)
6. 사디간배두께: 180 mm (복배근)
7. 스크립트두께: 210 mm (복배근)
(강간소음)

Structure

Methodology

Electrical

Fire Protection


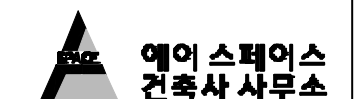


서울시 송파구 올림픽로 151-1 부암동 2층
 (주)한국문화재단 4층 404호
 TEL 02) 417-0606 FAX 02) 516-1662


Drawing Title:

4 층 평면도

Scale: 1/100
Date: 2021
Approved by:
Checked by:
In-Charge:
Drawn by: A- 22

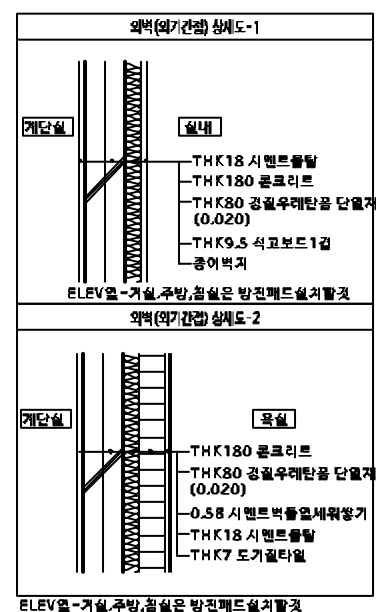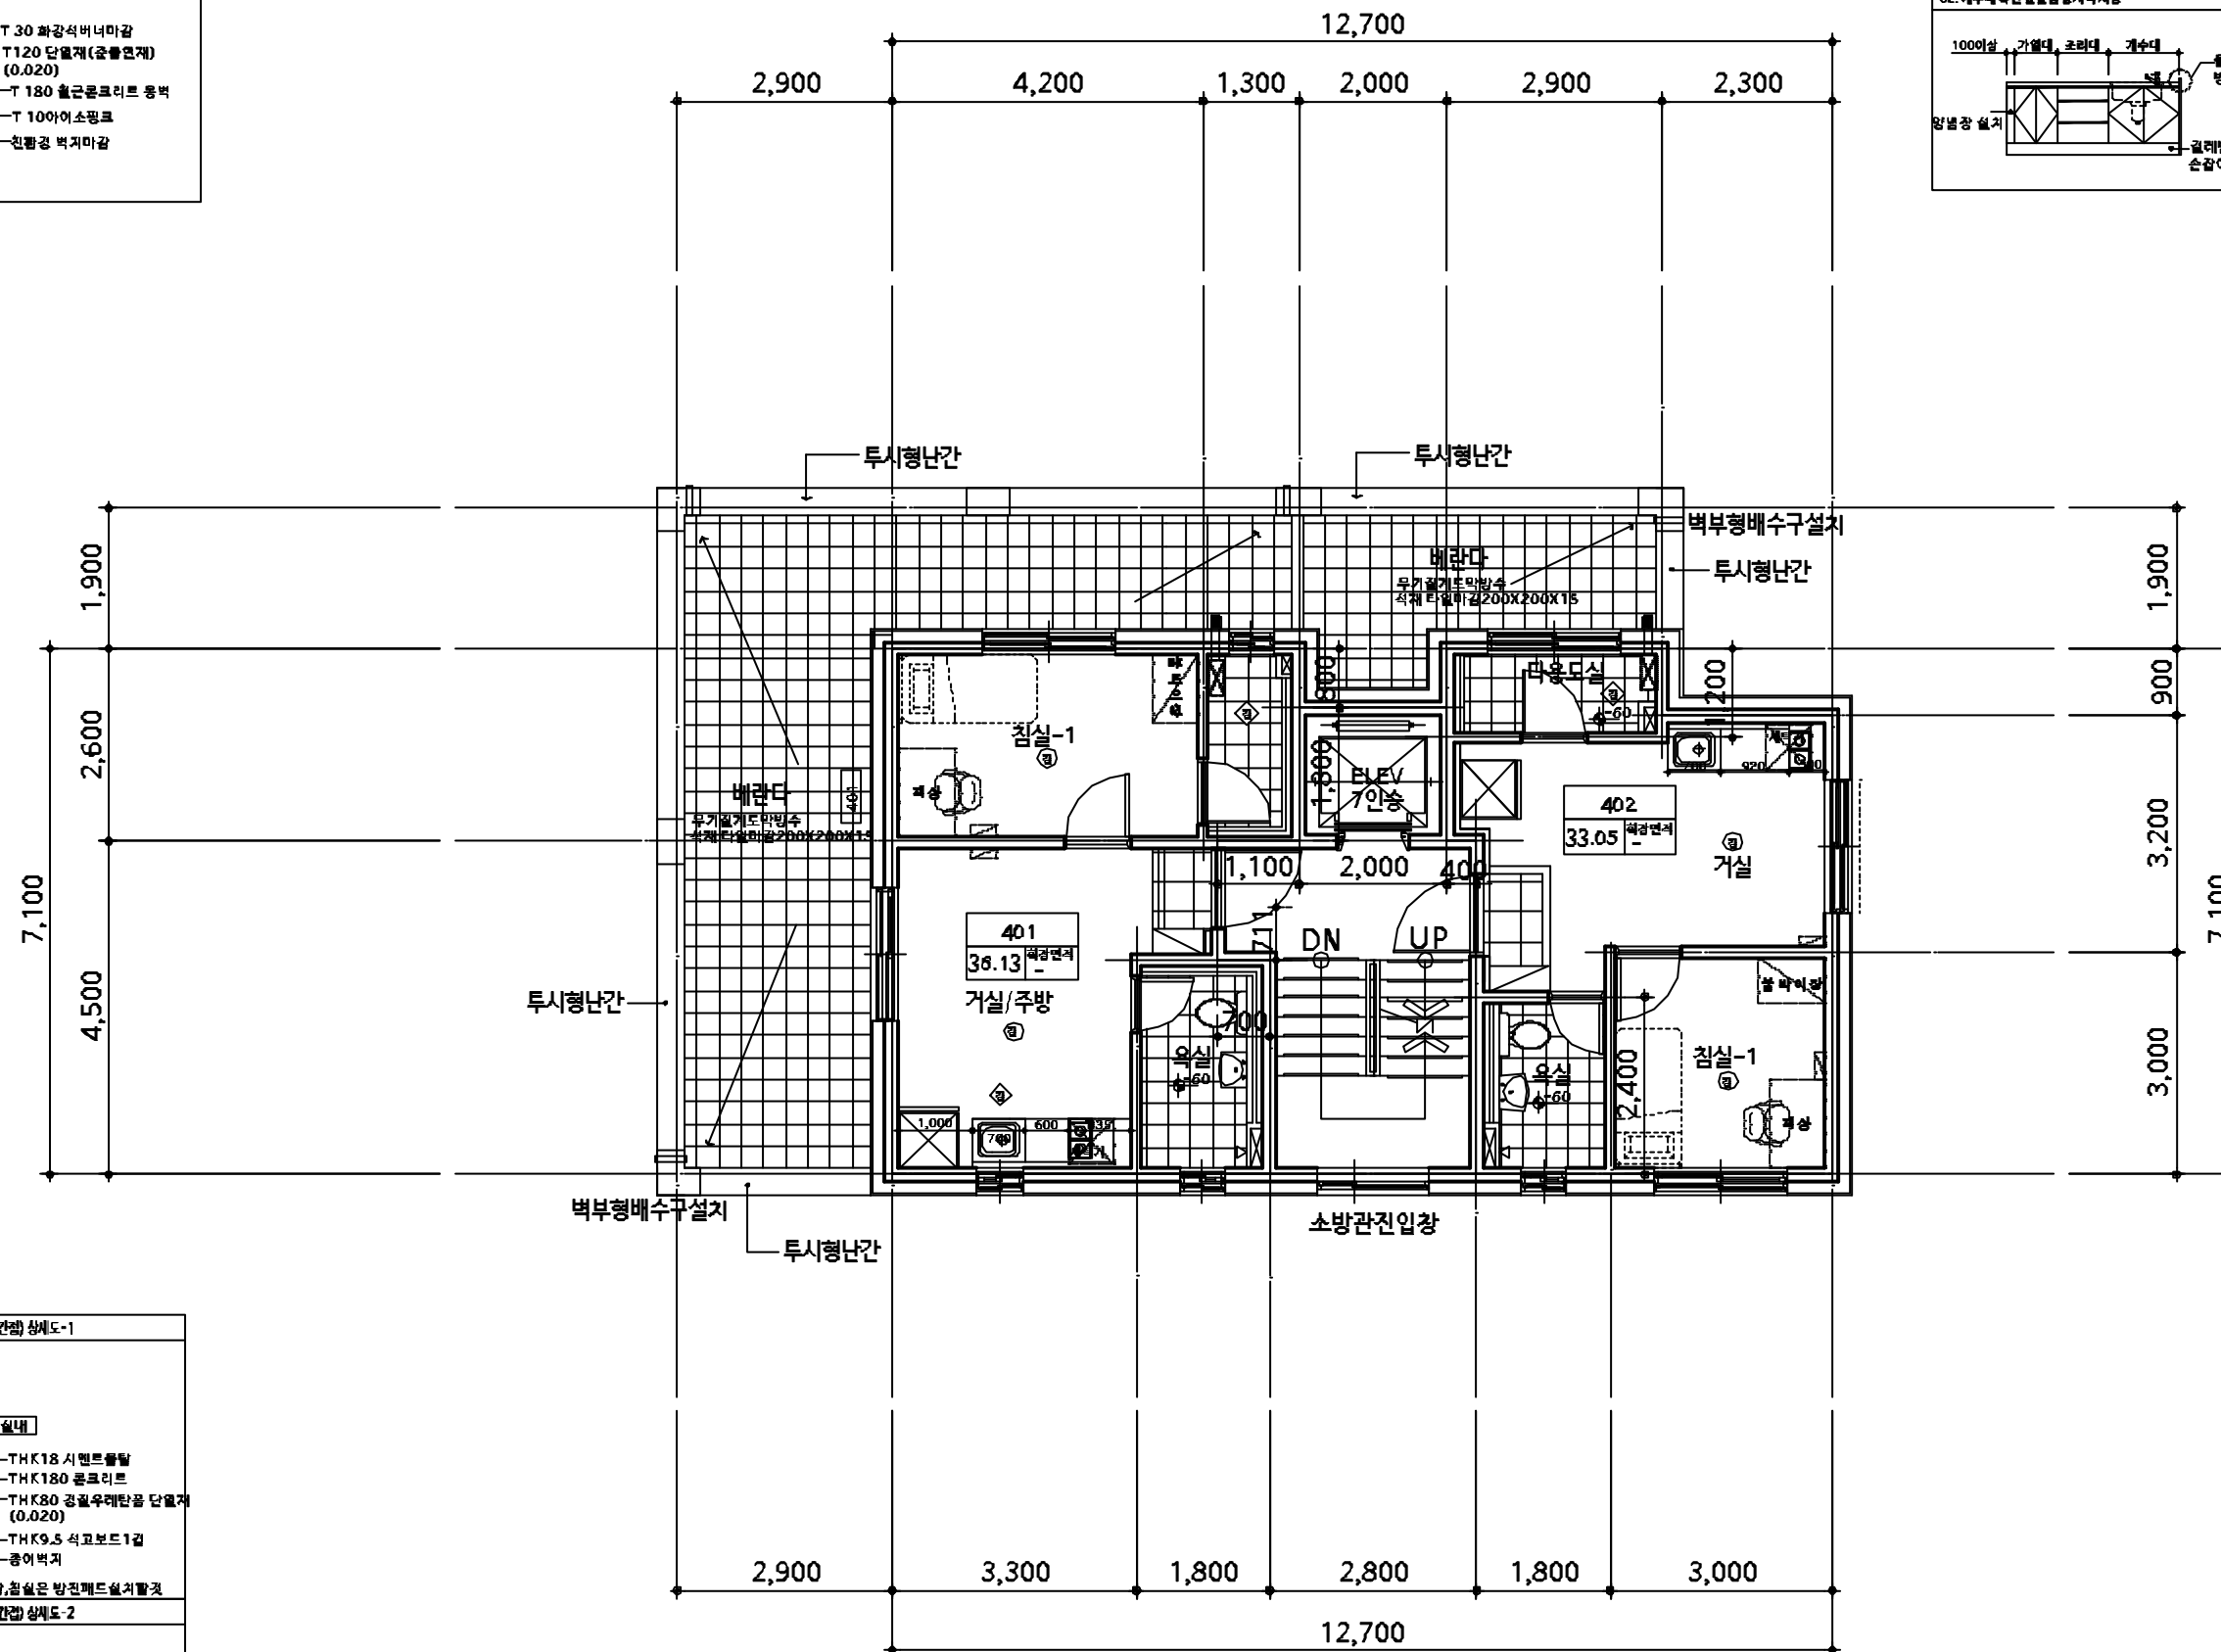

4 층 평면도

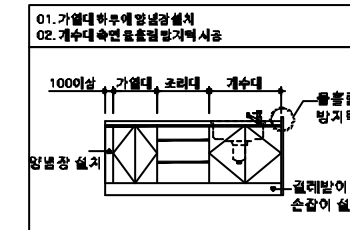

암사동 493-15
도시형생활주택
신축공사 (청년)

[illegible]

NOTE

- ① 단독경보감지기(연기)
- ② 단독경보감지기(열)
- ③ ABC분말소화기(3.3KG)

----- 차면시설

	보일러 (설비도면우선)
	에어컨 (설비도면우선)

※구조일반사항※


1. 콘크리트: $f_c = 24 \text{Mpa}$
2. 철근: $f_y = 400 \text{Mpa}$
3. 세디내벽두께: 150mm(복배근)
4. 외벽두께: 180mm(복배근)
5. 코아벽두께: 180mm(복배근)
6. 세디간벽두께: 180mm(복배근)
7. 스킵벽두께: 210mm(복배근)
(중간소출)

Structure

Mechanical

Electrical

Fire Protection

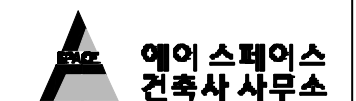

서울시 송파구 올림픽로 151-1 부경빌딩 2층
(주)부경테크노시스템
TEL 02) 417-0606 FAX 02) 516-1852

Drawing Title

5층 평면도

Scale 1/100



Date 2021

Approved By

Checked By

In Charge

Drawn By A- 23

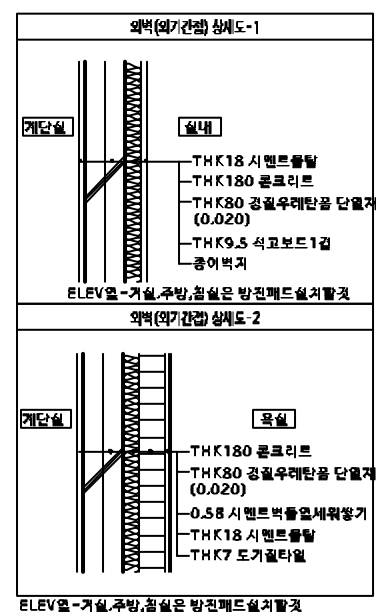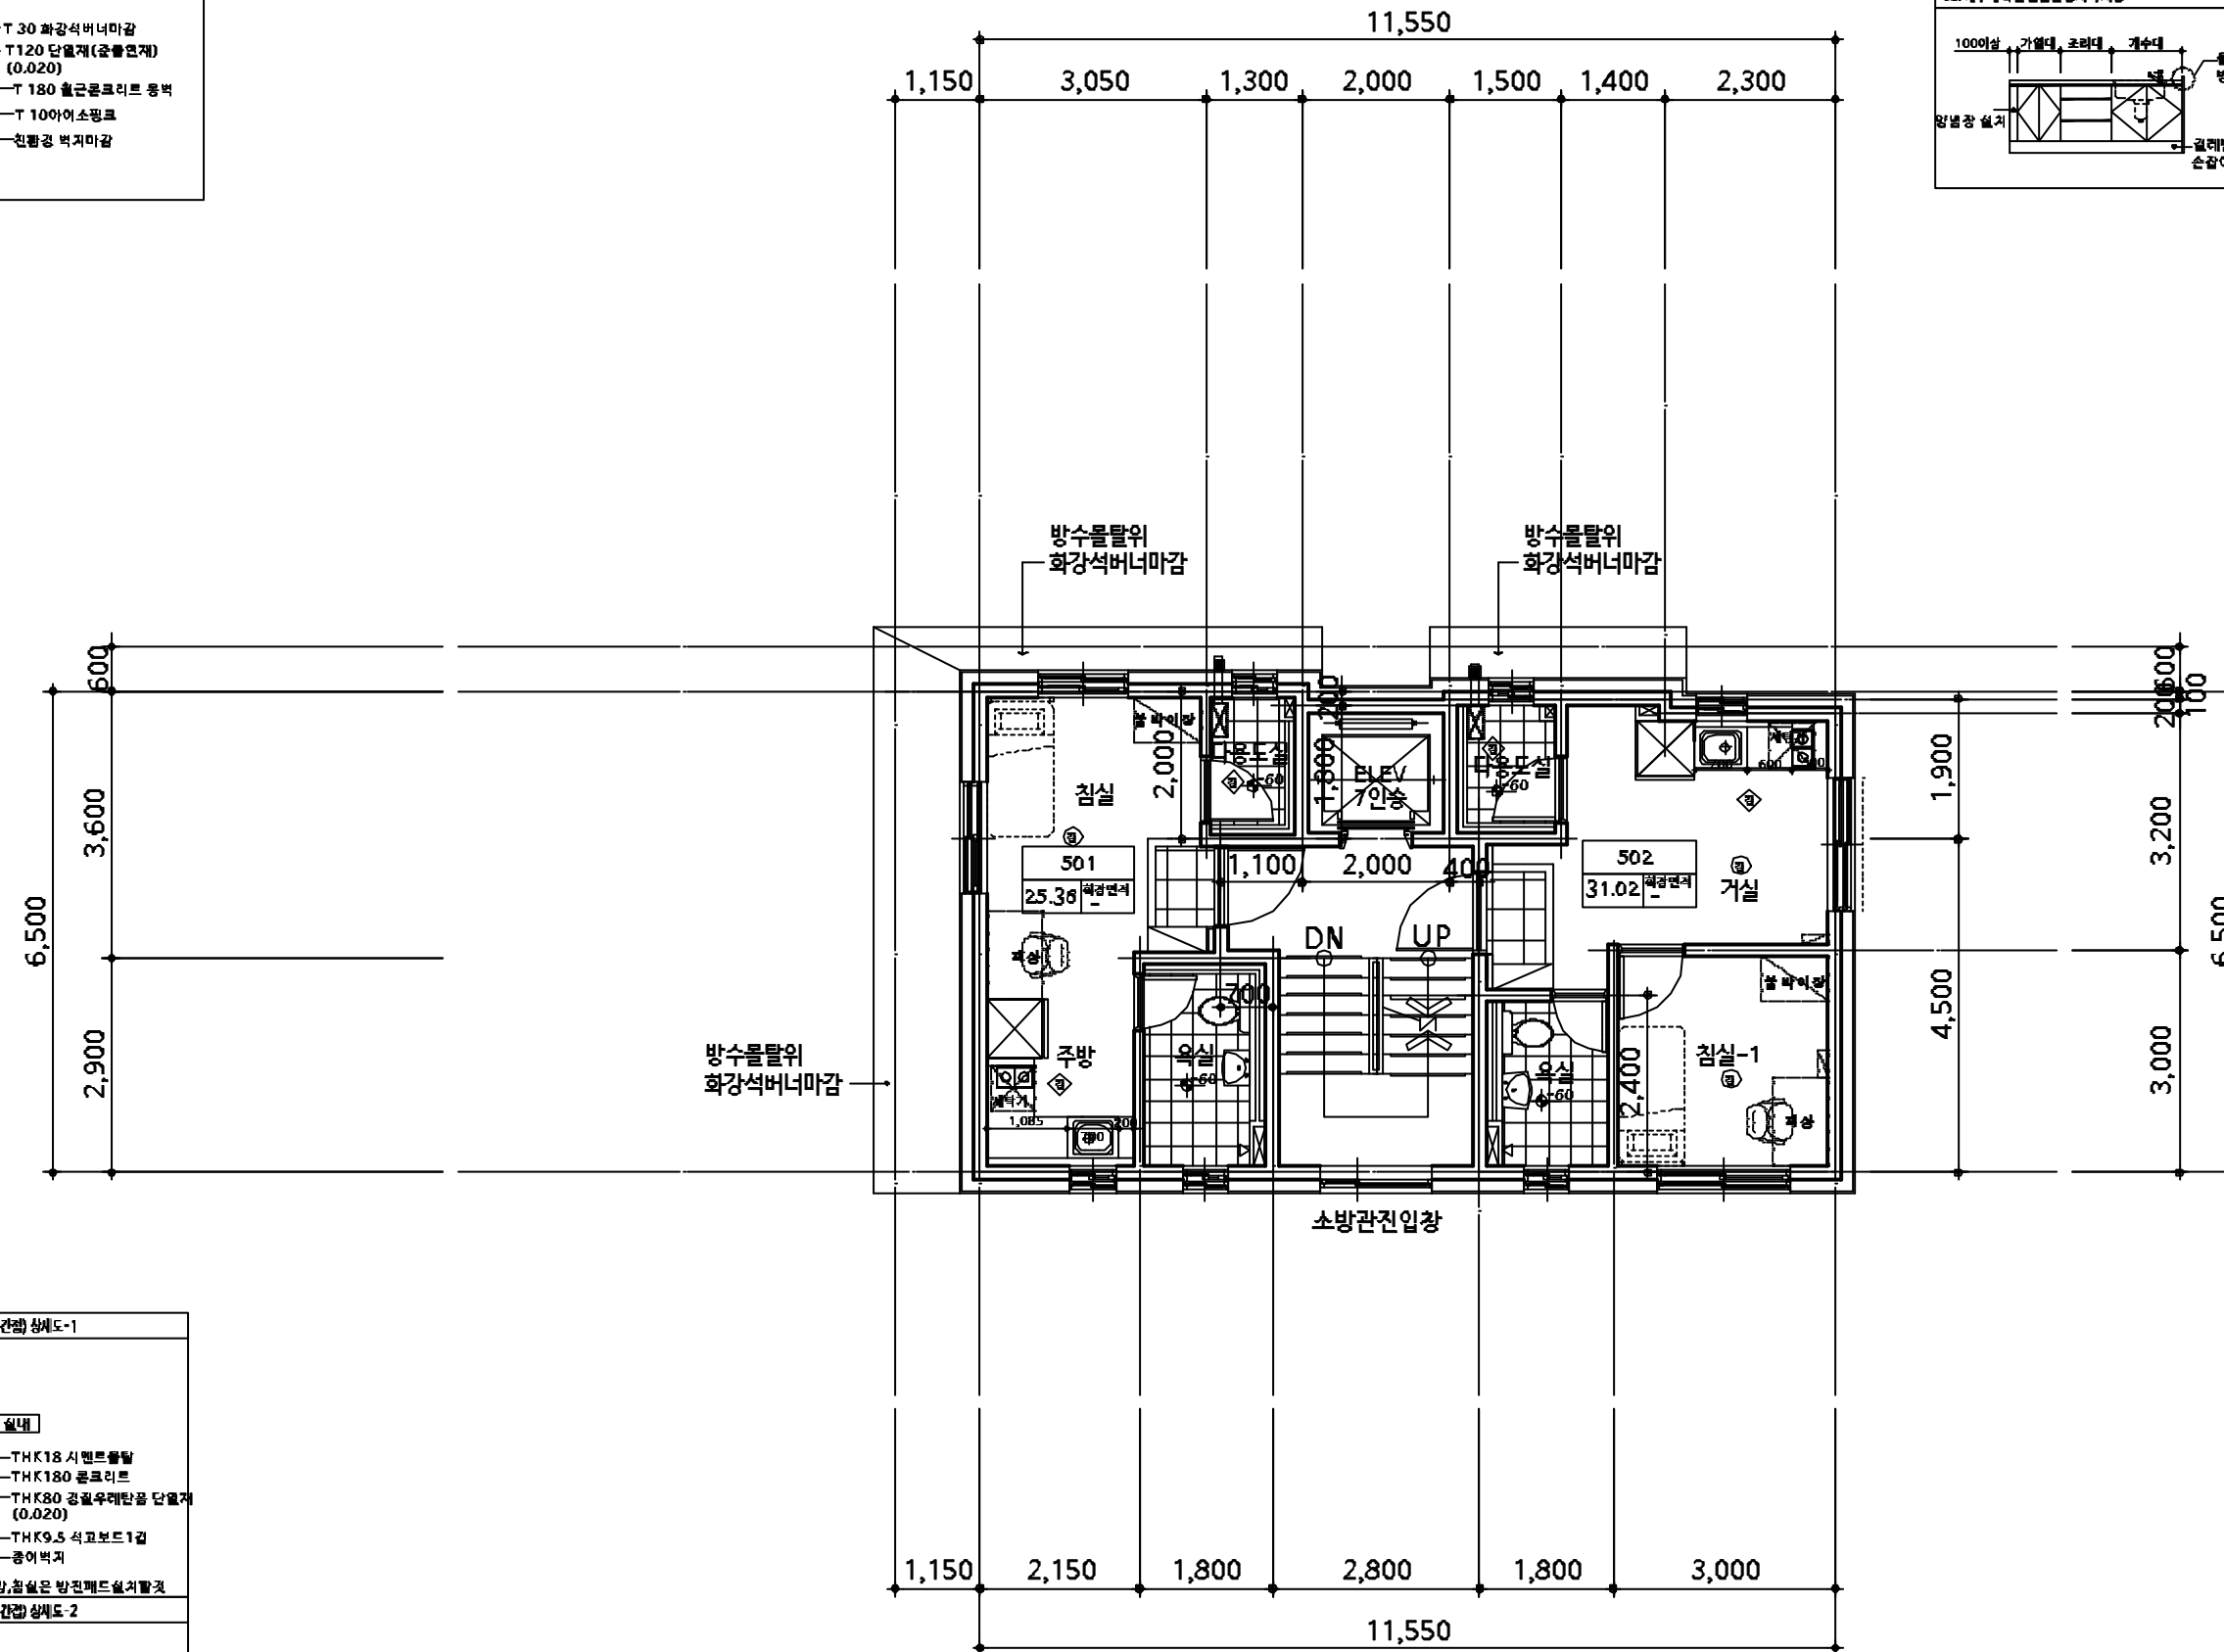

5층 평면도

Project Title

암사동 493-15
도시형생활주택
신축공사 (청년)

No.	Revised

NOTE
 ⑧ 단독경보감지기(연기)
 ⑨ 단독경보감지기(열)
 ⑩ ABC분말소화기(3.3KG)

----- 차면시설

☒ 보일러
 ☒ 에어컨

※구조일반사항※
 1.콘크리트:fc k=24Mpa
 2.철근:fy=400Mpa
 3.사다리내벽두께:150mm(복배근)
 4.외벽두께:180mm(복배근)
 5.코어벽두께:180mm(복배근)
 6.사디간벽두께:180mm(복배근)

Structure

Mechanical

Electrical

Fire Protection

에이스터스
건축사 사무소

서울시 송파구 암사동 151-1 부도원빌딩 2층
 TEL. 02-417-0808 FAX 02-516-1862

Drawing Title

지붕 & 옥탑 평면도

Scale 1/100


Date 2021.

Approved by

Checked by

In Charge

Drawing No. A- 24

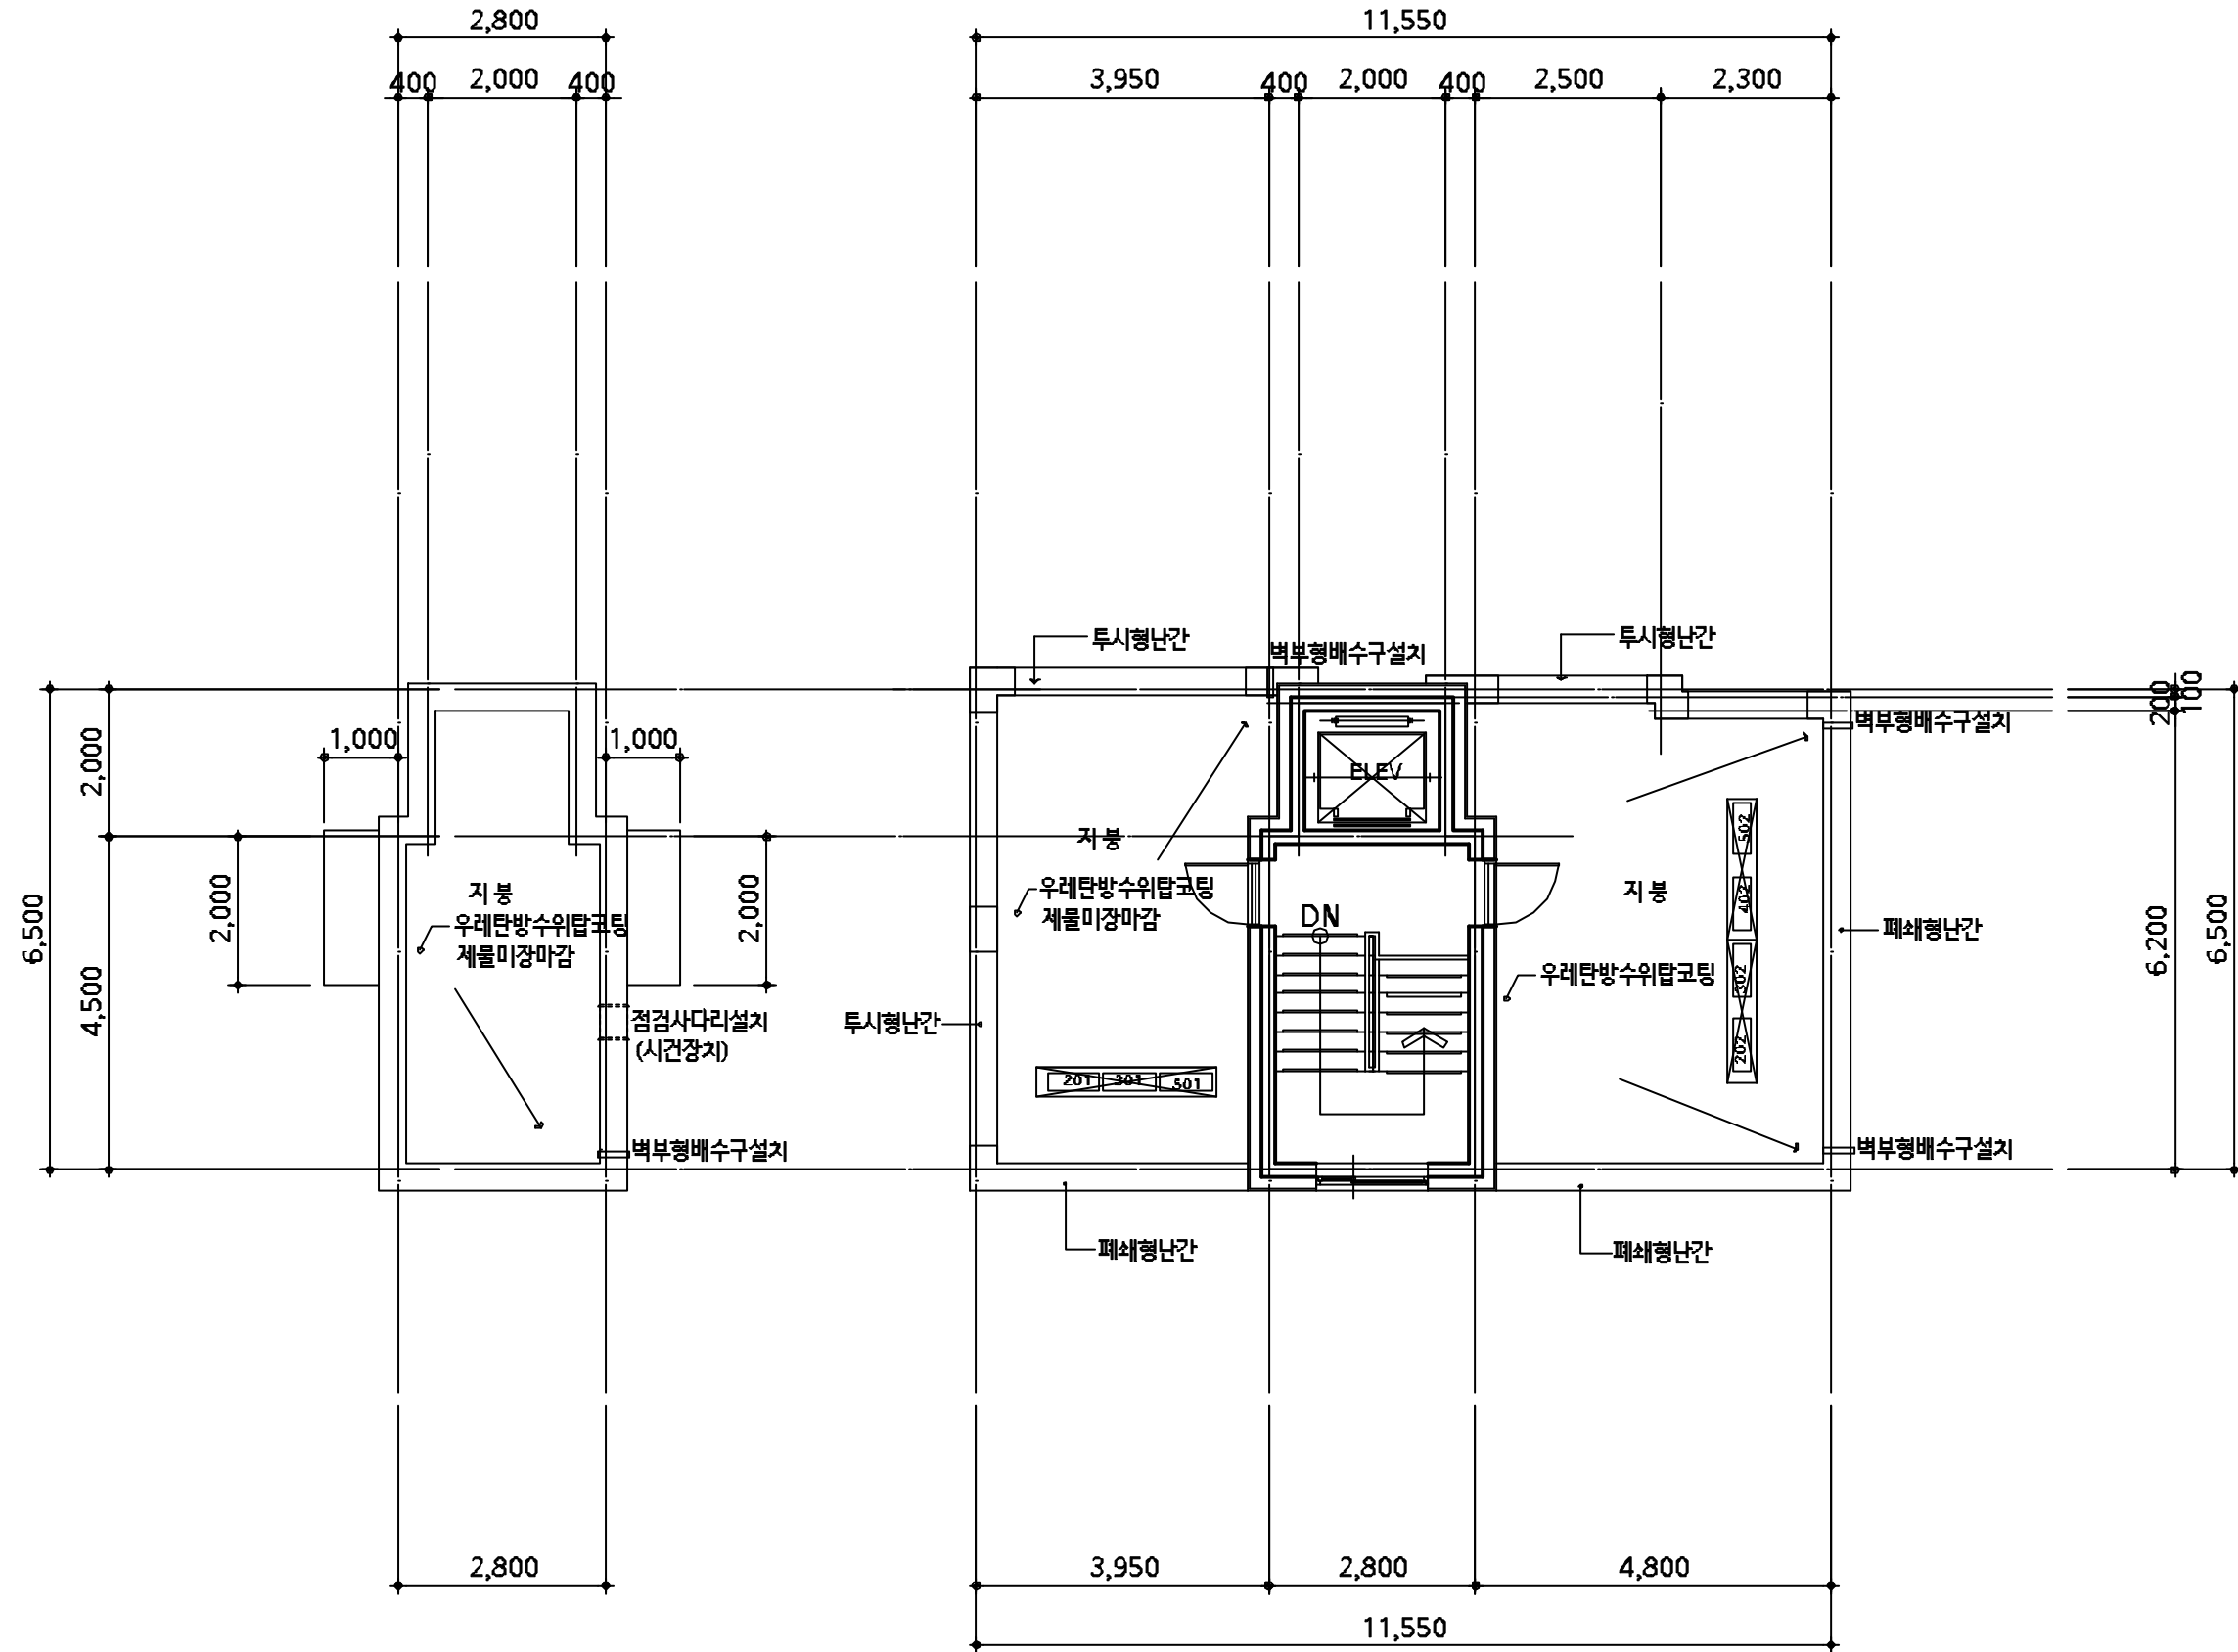

1 지붕 & 옥탑 평면도
 축척: 1/ 100

암사동 493-15
도시형생활주택
신축공사 (청년)

Structure


Mechanical

Electrical

Fire Protection



Drawing Title	
정 면 도 우 측 면 도	
Scale	1/100 A4:150
Date	2021.
Apprentice	건축사 박남권
Client	
in Charge	
Drawing	A- 25

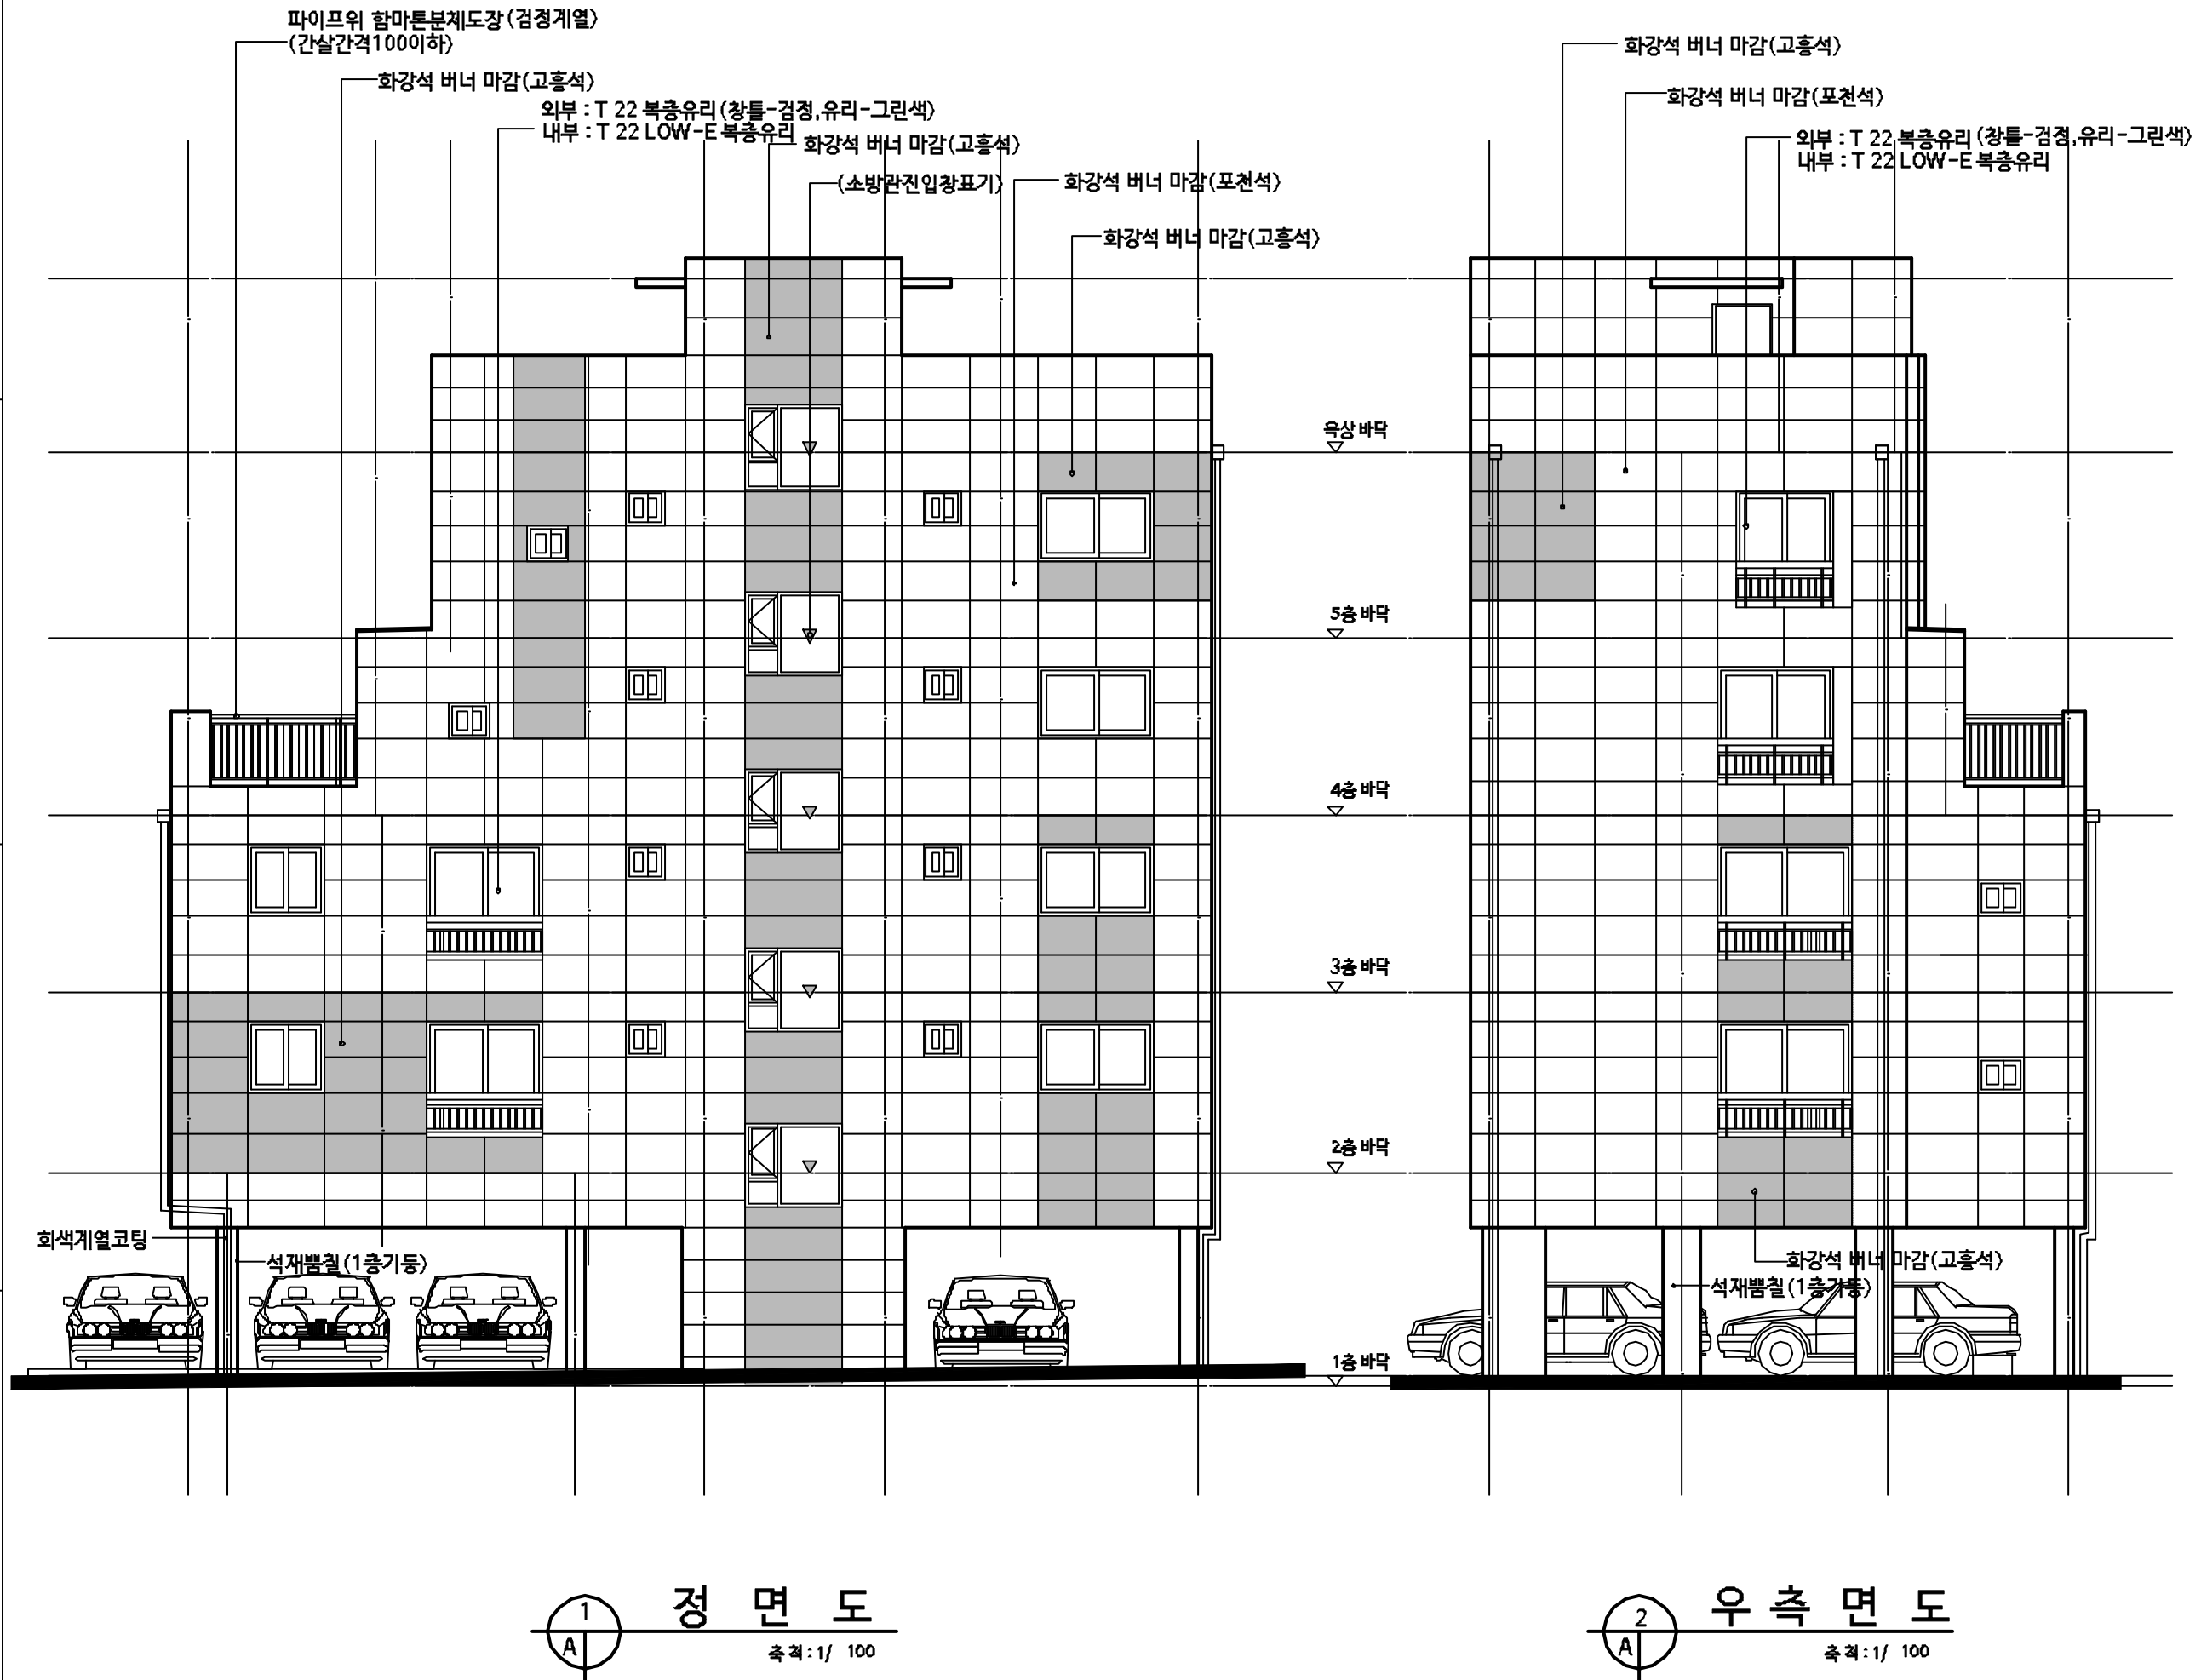

암사동 493-15
도시형생활주택
신축공사 (청년)

Structure

Mechanical

Electrical

Fire Protection



좌측면도

Scale	1/100 A4:150
Date	2021.
Approved By	건축사 박남권
Checked By	
In Charge	
Project	A- 26

