



1. 투시도



2. 건축개요 및 현황도

건 축 개 요

- 설 계 명 : 천호동 00 오피스텔 신축공사
- 대 지 위 치 : 서울특별시 강동구 천호동 541번지외 6필지
- 지 역 · 지 구 : 제1종지구단위계획구역(천호지구)
- 건 물 용 도 : 업무시설(오피스텔)
지하 2층 / 지상 10층
- 건 물 규 모 : 4M이상 3M 도로에
약 17.1M /14.2M 접합
- 대 지 면 적 : 455.00㎡
- 건 축 면 적 : 251.68㎡
- 연 면 적 : 1,982.88㎡
- 건 폐 율 : 55.31%
- 용 적 율 : 386.73%
- 최 고 높 이 : 29.95m
- 건 물 구 조 : 철근콘트리트조
- 주 차 대 수 : 30대(법정), 32대(계획)



■ 위치도



■ 주변현황도

3. 입면도



■ 정면도



■ 우측면도



■ 배면도



■ 좌측면도

※ 본 상기도면은(조감도포함)은 디자인심의시 제출된 심의도면으로서 설계도면과 일부 상이한 참조용이며 설계도면이 우선함.

4. 입면계획

※ 입면의 수직성을 강조하기 위해 주조색과 보조색을 수직으로 분할 입면계획 함.



※ 입면의 수직성을 강조하기 위해 주조색과 보조색을 수직으로 분할 입면계획 함.



5. 재료계획



*. 실내,외부에 사용되는 모든 마감재료는 친환경 인증제품을 사용하여 입주자의 정신적,신체적 안정감을취하도록 함




*. 보일러,조면기기등 전력소비가 많은 제품을 고효율기자재를 채택하여 에너지절약효과를 극대화 함.



*. 고기능,고효율 창호를 채택하여 에너지절약효과를 극대화 함.

6. 색채계획

1. 주조색 자재

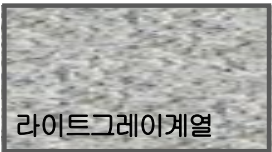




2. 보조색 자재



3. 보조색 자재






※ 본 상기도면은(조감도포함)은 디자인심의회 제출된 심의도면으로서 설계도면과 일부 상이한 참조용이며 설계도면이 우선함.

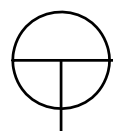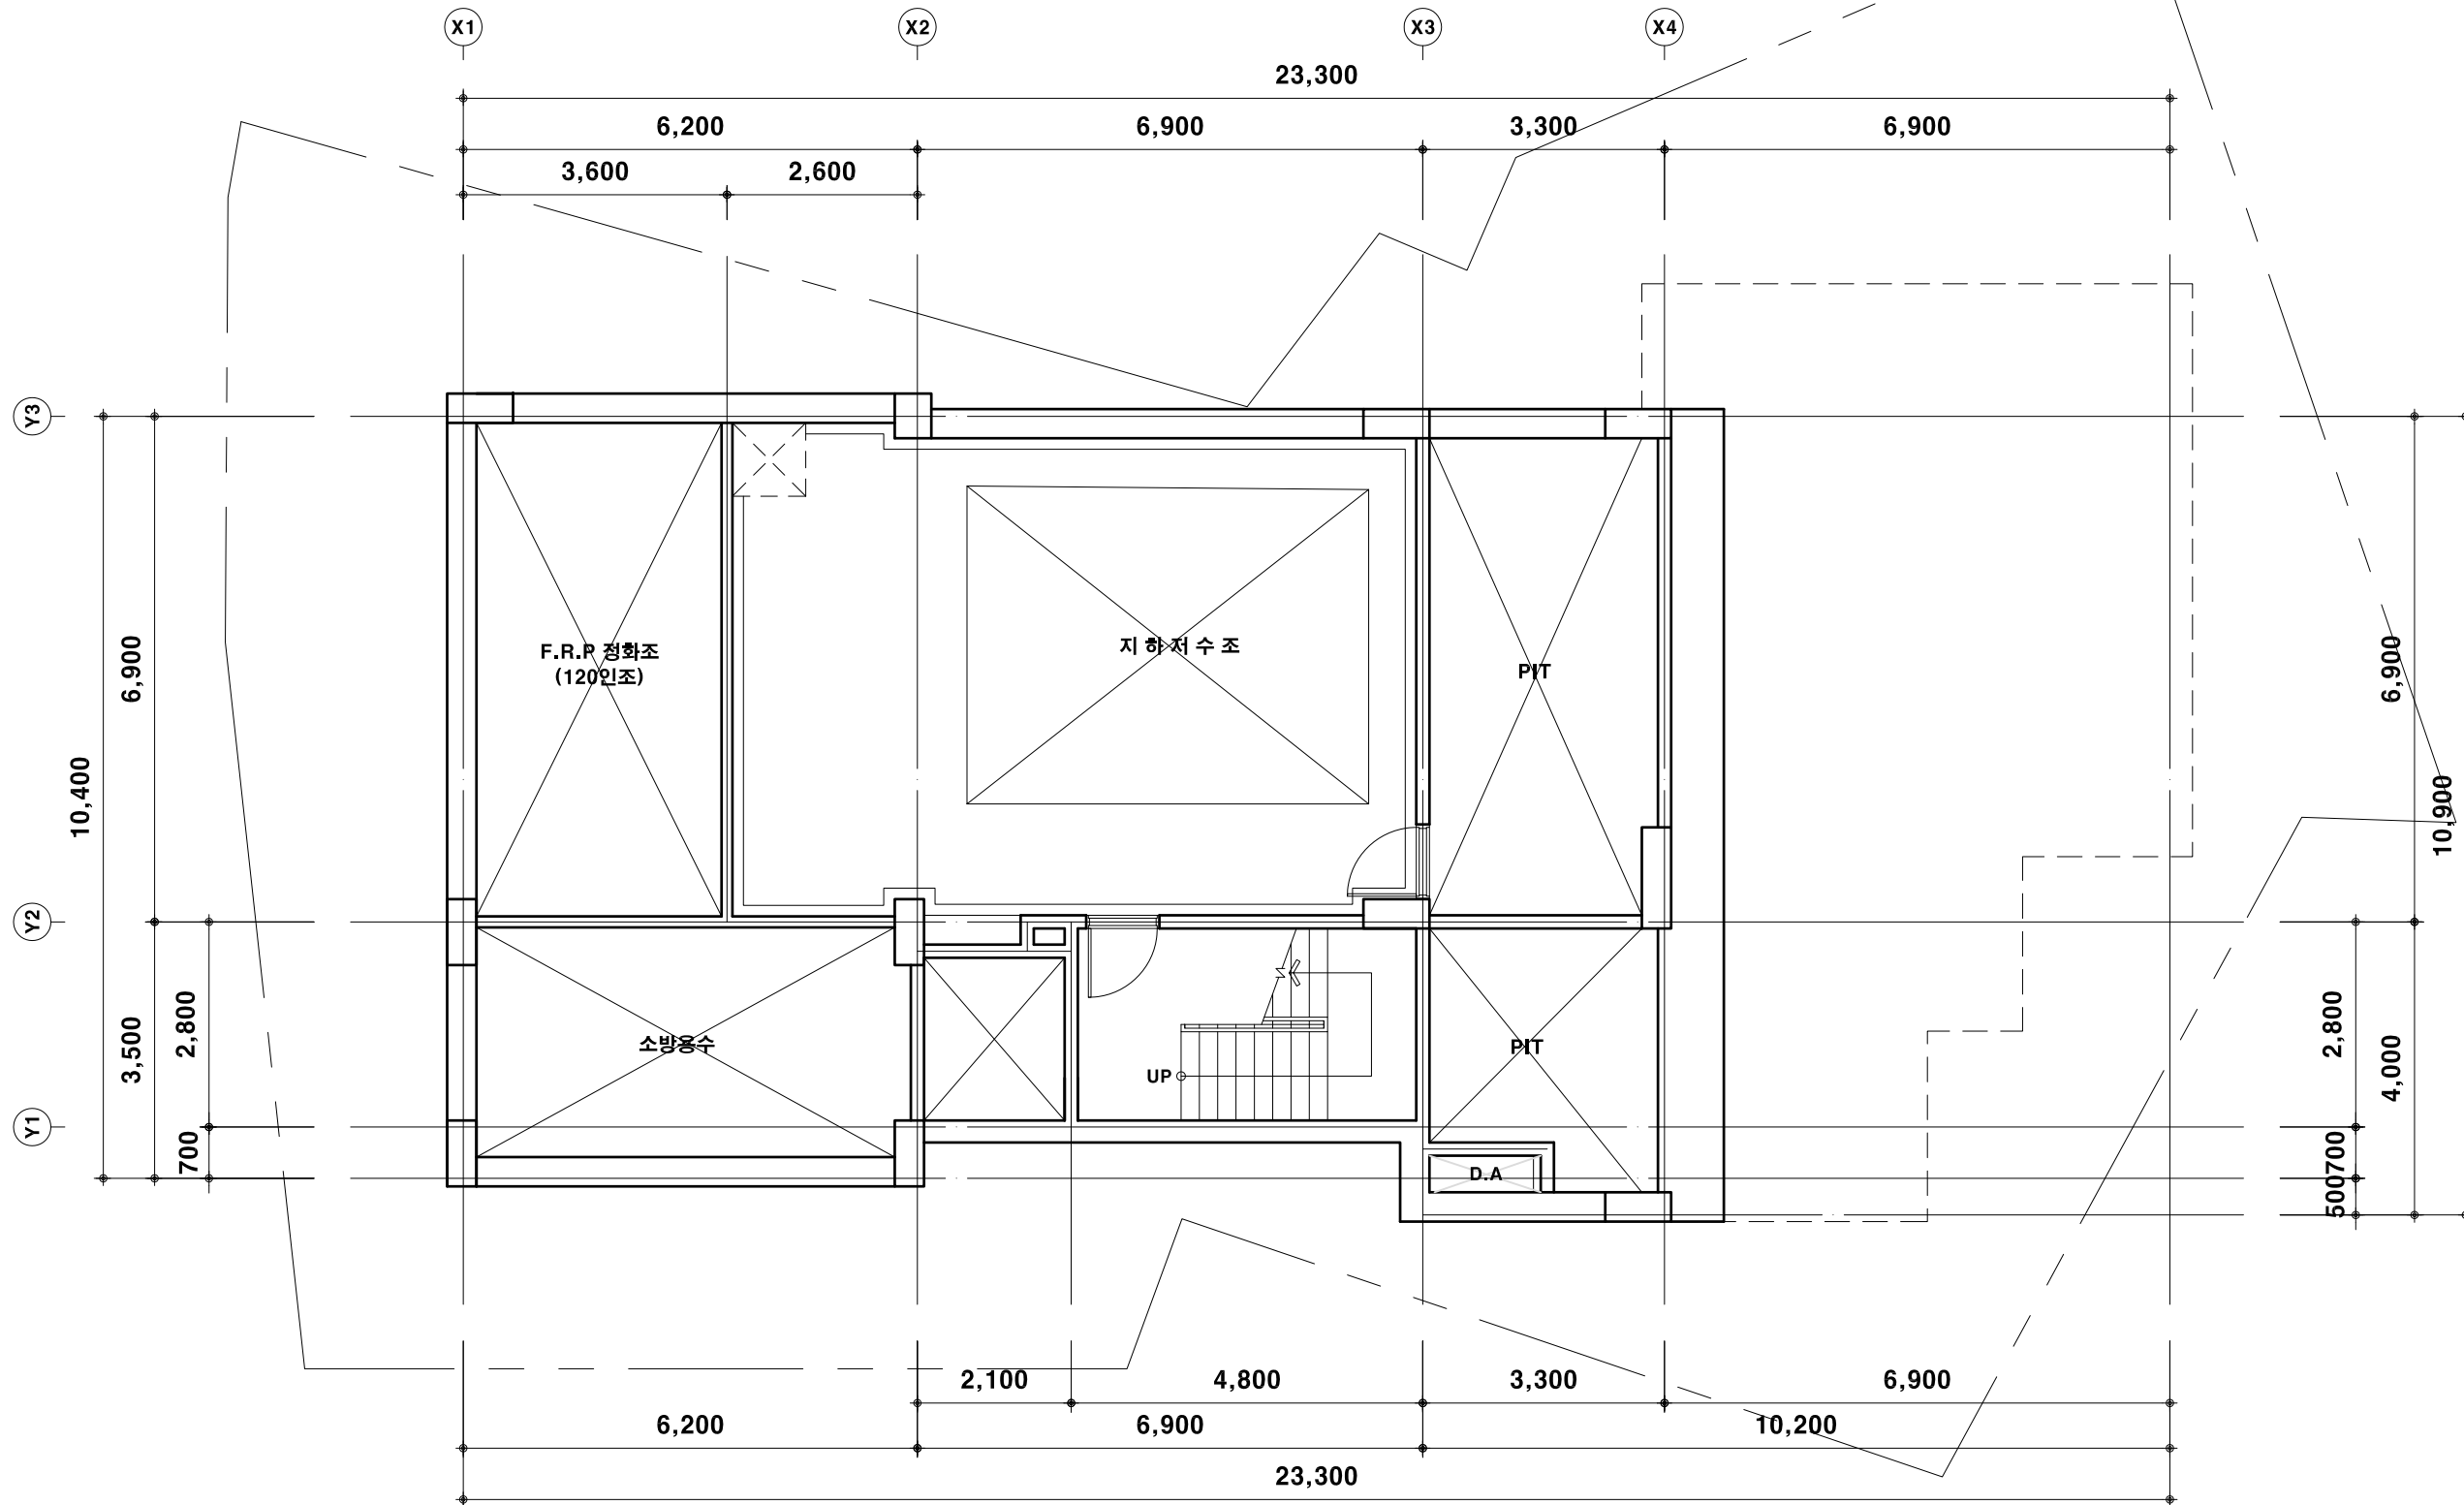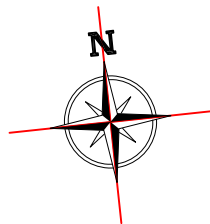


지하2층 평면도

SCALE : 1/100

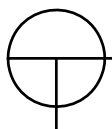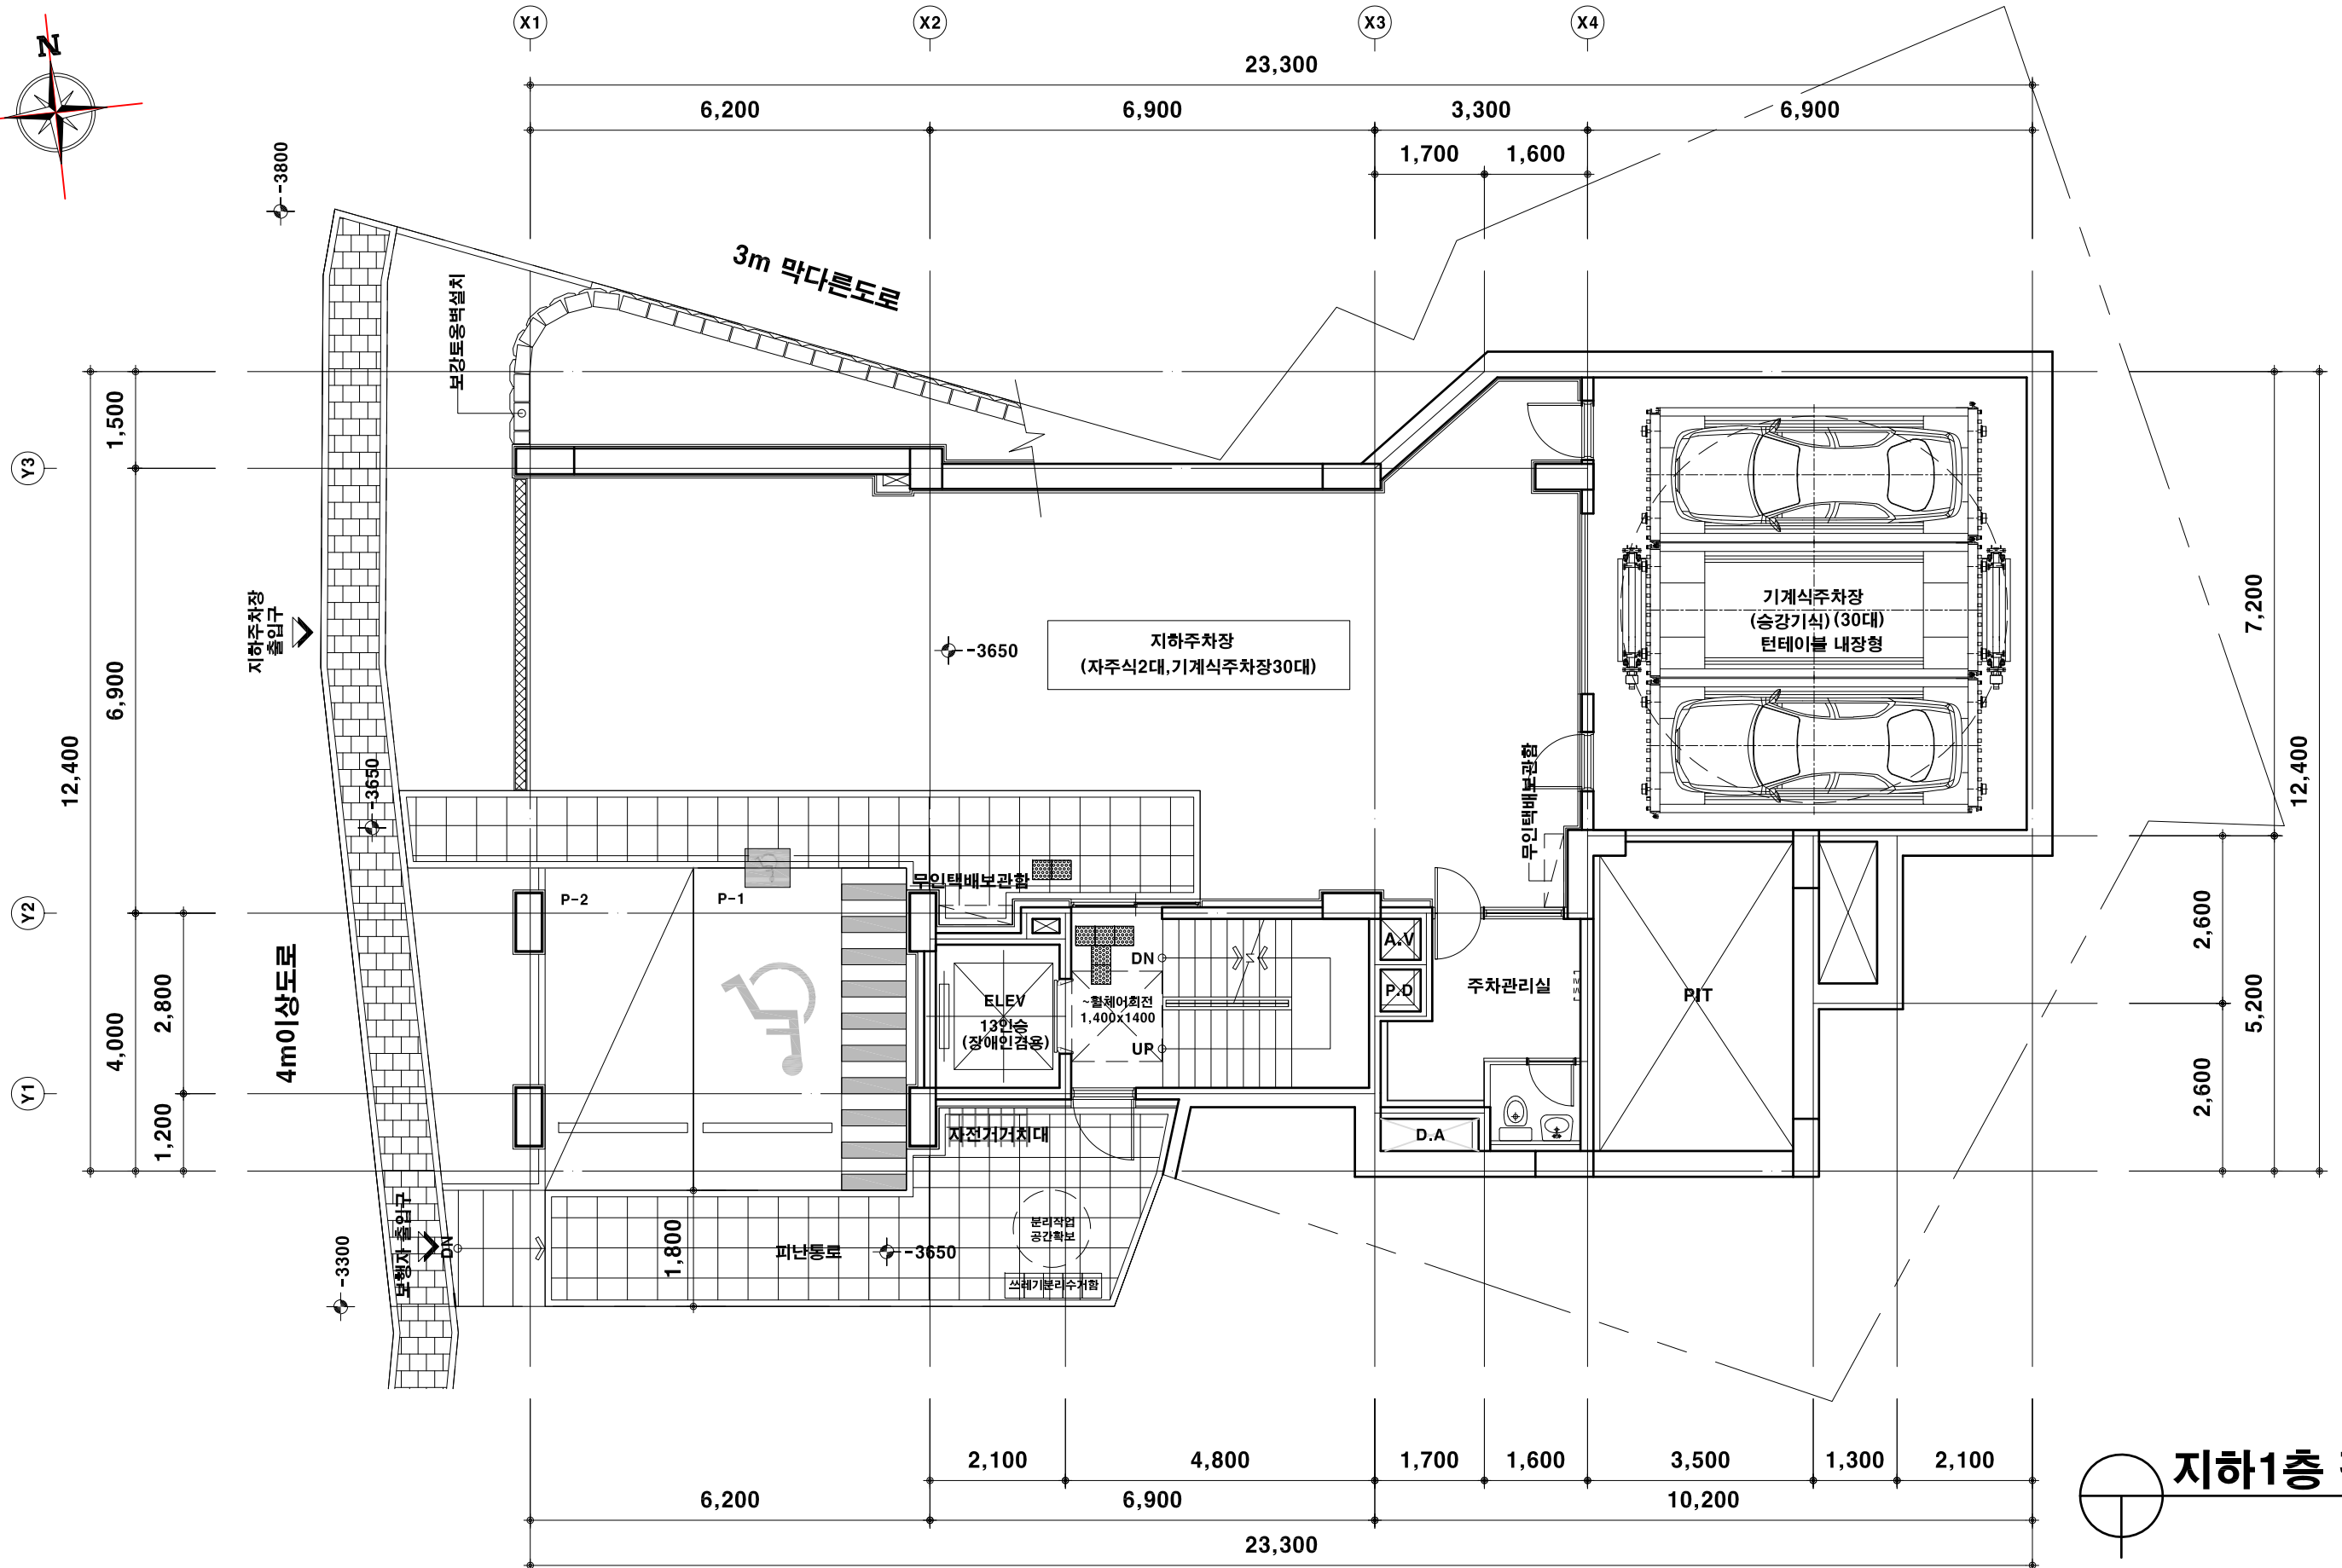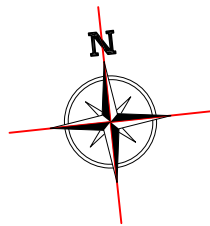


지하1층 평면도

SCALE : 1/100

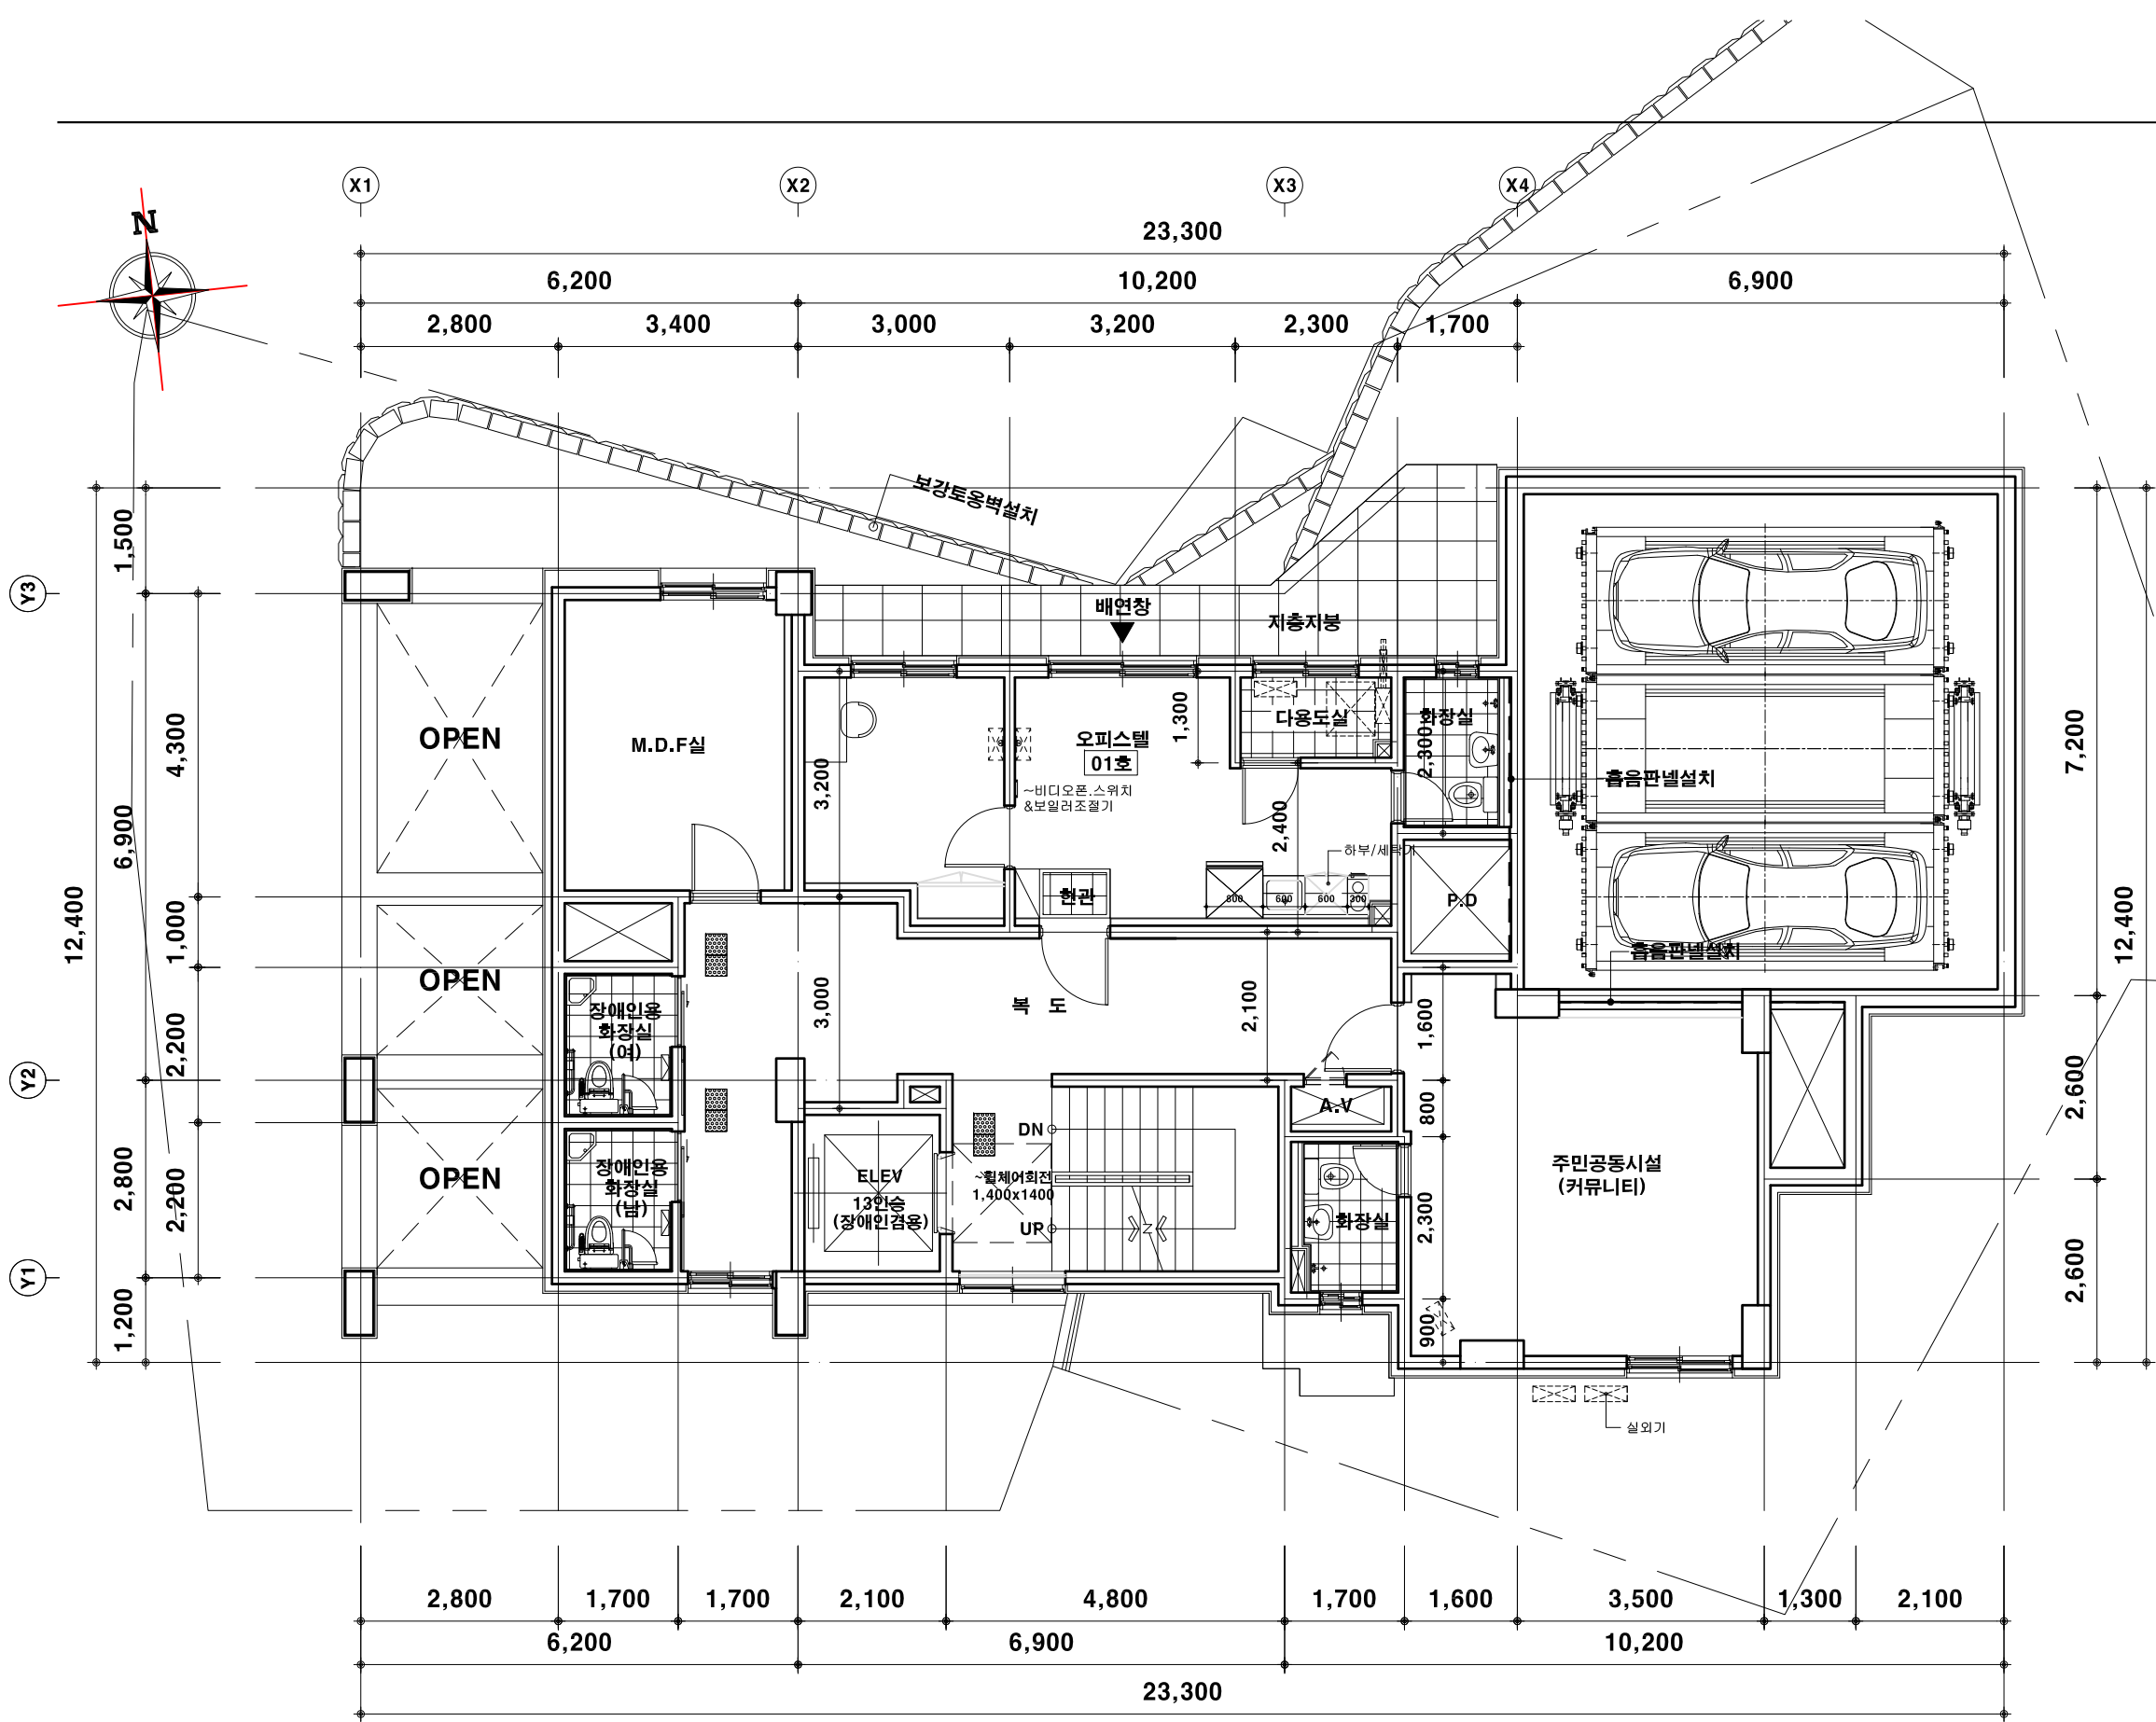




1층 평면도
SCALE : 1/100

주 기			
건 축	1 (외부)	주차장내 CCTV,쓰레기분리수거,자전거보관대 설치	
		우편함 설치 (세대전용, 공용, 반송용, 폐건전지함 구분 설치)	
		테라스 창호 PL이중창 설치	
		세대 테라스 설치시 세대간 분리벽 계획	
		세대 발코니 설치시 차양시설 설치	
	2 (계단실)	세대 현관문 도어체크 설치	
	계단참의 현관과 계단 이격거리 (최소600mm이상)		
	3 (내부)	세대내 욕실, 휴지걸이 매립형 설치	
	4 (시공)	콘크리트 폼타이 제거 후 마감공사 시공 (방수, 단열재 시공 등)	
		욕실 & 다용도실 스위치 : 문 열리는 방향으로 시공	
		주차장 차량 진출입구간 무소음트렌치 시공	
5 (마감)	-직접외기(외벽)에 면한 실내벽면 단열재		
	[아이소핑크(10mm) + 석고보드 마감도면 표기]		
	-간접외기(계단실,복도)에 면한 실내벽면 단열재		
	[경질우레탄폼(80mm) + 석고보드 마감도면 표기]		
	*기타 실내 벽면 시멘트 미장 마감		
구 조	1	철근 : fy=400Mpa	
		콘크리트 : fck=24Mpa	
	2	스라브두께 : 210mm (복배근)	
		외벽두께 : 180mm (복배근)	
		코아벽두께 : 180mm (복배근)	
		세대간벽두께 : 180mm (복배근)	
	내벽두께 : 150mm (복배근)		
전 기	1	-콘센트 설치 (바닥 마감선 기준)	
		[거실] 천정매립형 에어컨 :	
		[안방] 벽걸이형 에어컨 : 1900	
		[화장실] 양변기 옆 : 900	
		[주방] 조리대 : 중앙 / 냉장고 : 350 / 후드 : 2100	
	2	-비디오폰 (VP),보일러온도조절기(B), 스위치(S) 설치 (거실 아트홀 위치)	VP S B
	3	-위치 표기	
		에어컨 실외기	
		에어컨 콘센트	
	냉매, 배수관 (배수관수직매립)		
비 고			
	세대현관문 ## 규격"틀"포함 : 1000X2200		



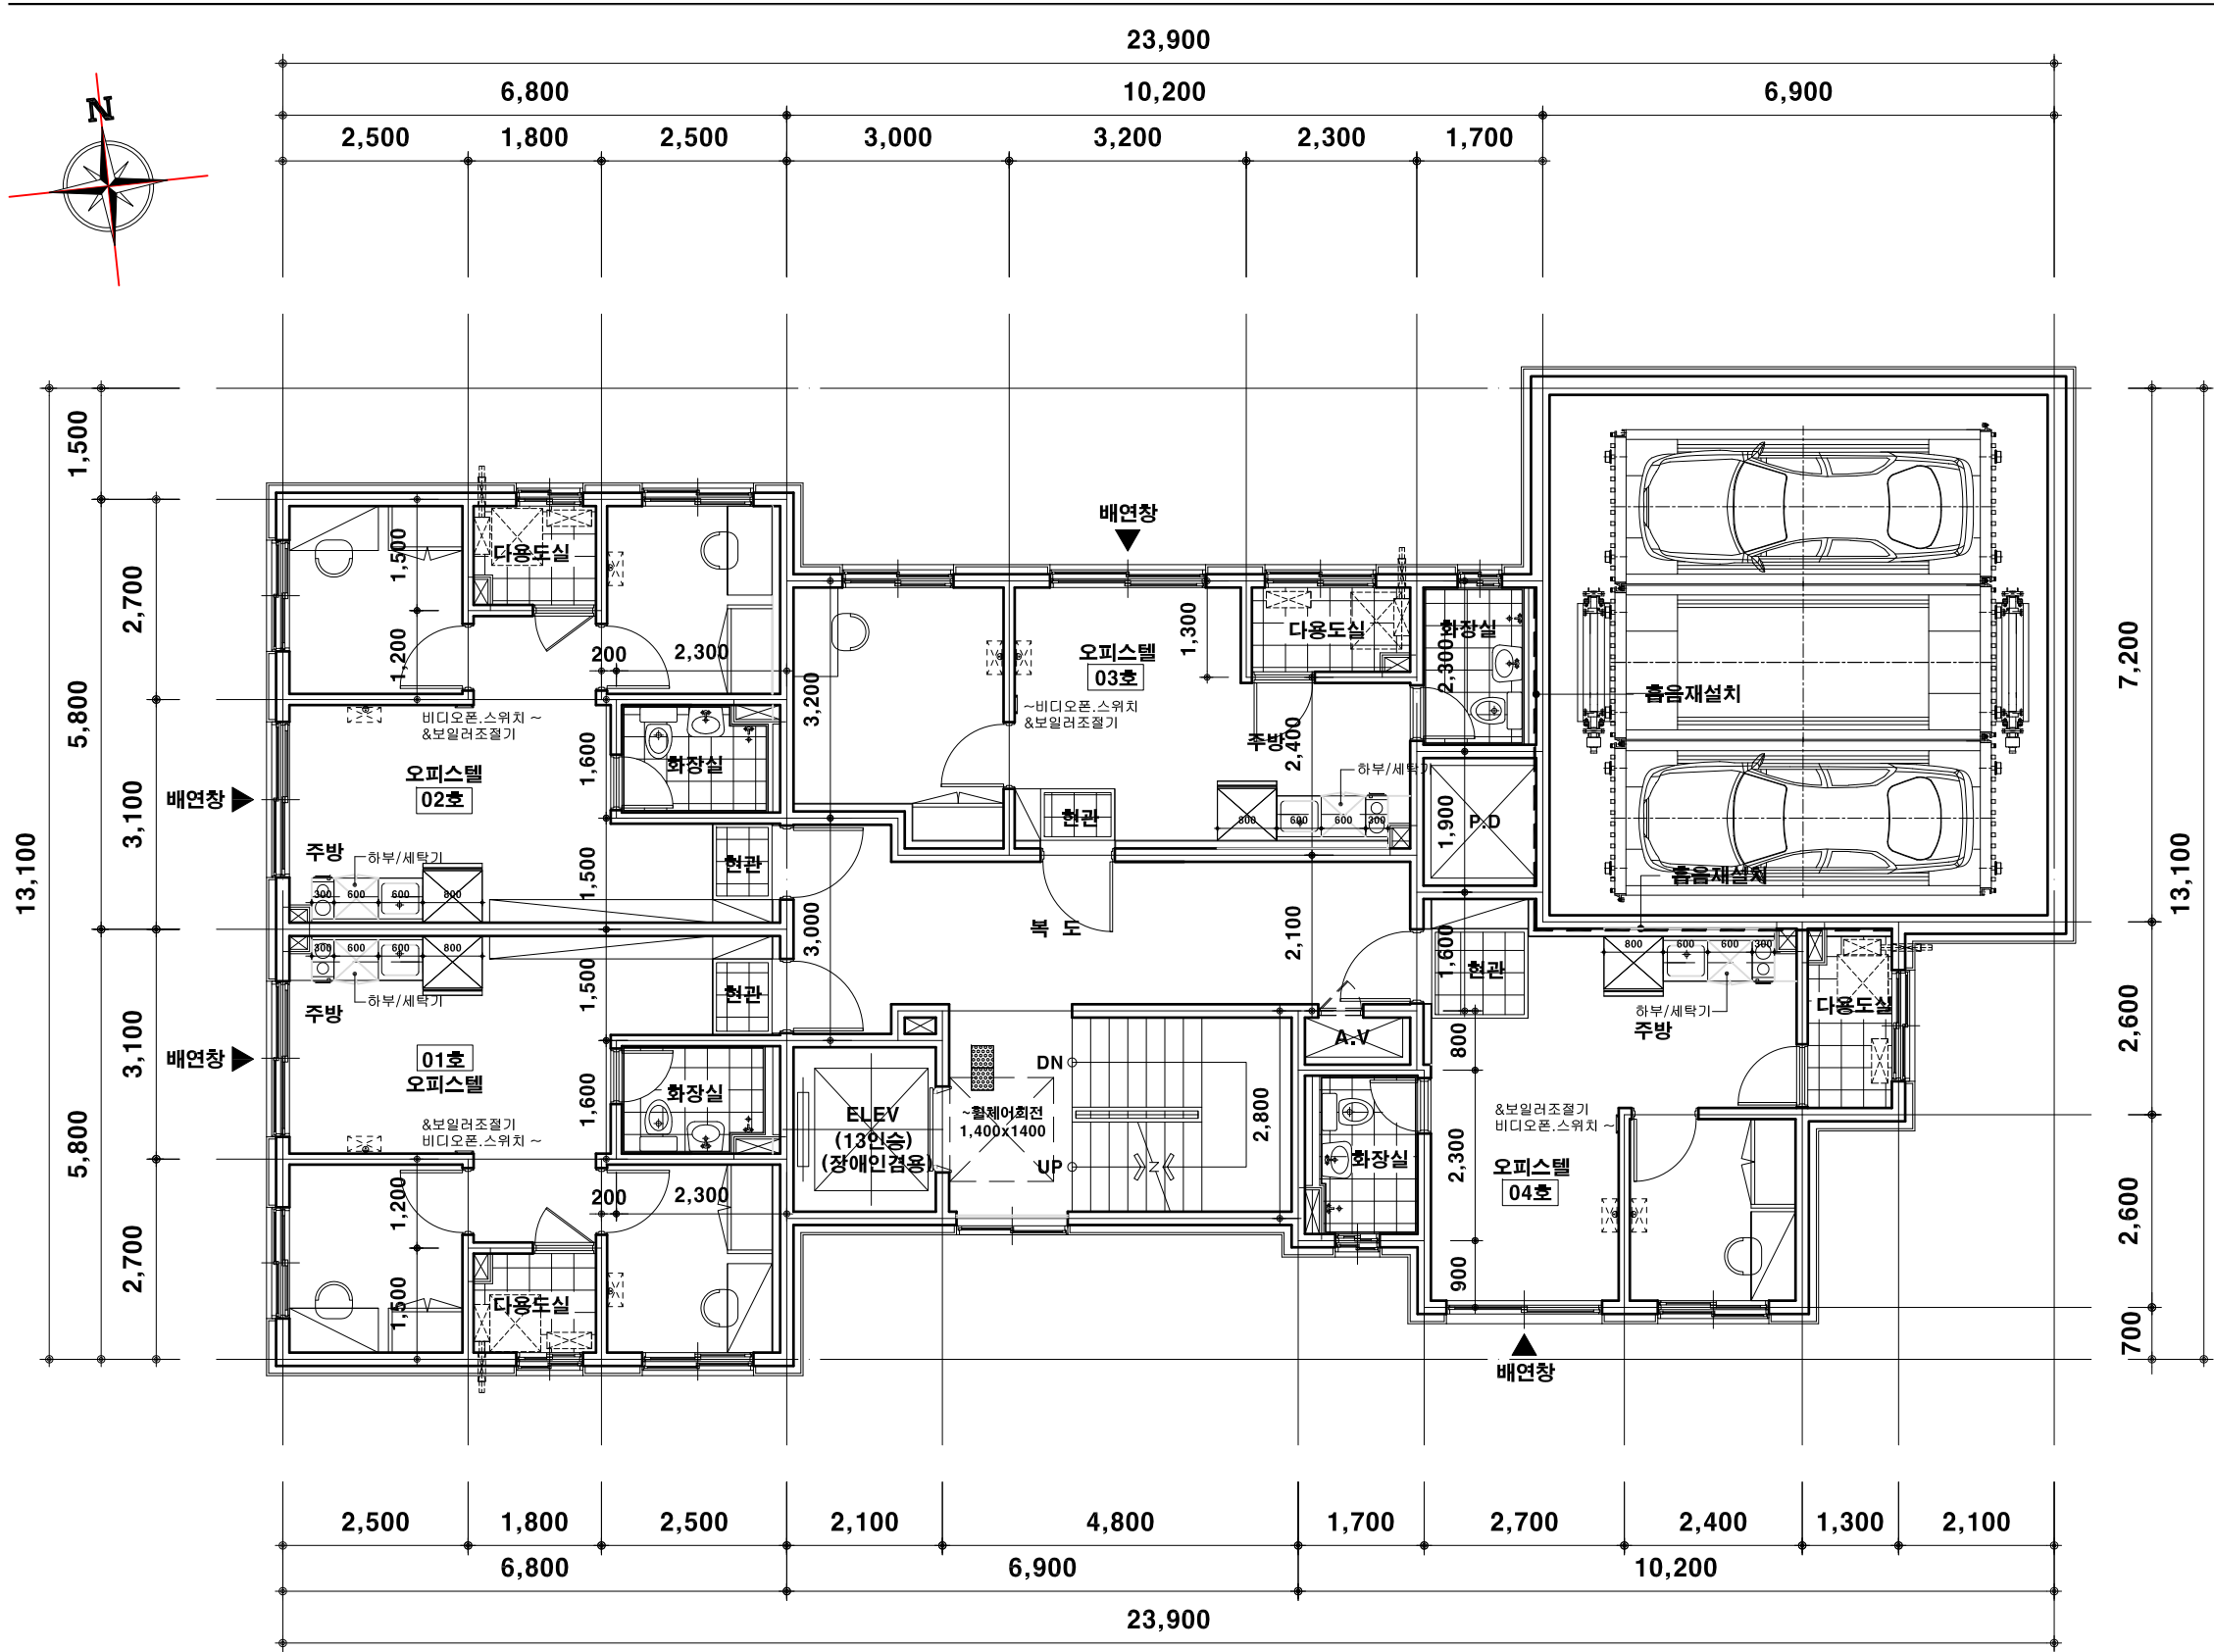


2~10층 평면도
SCALE : 1/100

주 기		
건 축	1 (외부)	주차장내 CCTV,쓰레기분리수거,자전거보관대 설치
		우편함 설치 (세대전용, 공용, 반송용, 폐건전지함 구분 설치)
		테라스 창호 PL이중창 설치
		세대 테라스 설치시 세대간 분리벽 계획
		세대 발코니 설치시 차양시설 설치
구 조	2 (계단실)	세대 현관문 도어체크 설치
		계단참의 현관과 계단 이격거리 (최소600mm이상)
		세대내 욕실, 휴지걸이 매립형 설치
		콘크리트 폴타이 제거 후 마감공사 시공 (방수, 단열재 시공 등)
		욕실 & 다용도실 스위치 : 문 열리는 방향으로 시공
전 기	3 (내부)	주차장 차량 진출입구간 무소음트렌치 시공
		-직접외기(외벽)에 면한 실내벽면 단열재
		[아이소핑크(10mm) + 석고보드 마감도면 표기]
		-간접외기(계단실,복도)에 면한 실내벽면 단열재
		[경질우레탄폼(80mm) + 석고보드 마감도면 표기]
비 고	5 (마감)	*기타 실내 벽면 시멘트 미장 마감
	1	철근 : fy=400Mpa
		콘크리트 : fck=24Mpa
		스라브두께 : 210mm (복배근)
		외벽두께 : 180mm (복배근)
		코아벽두께 : 180mm (복배근)
전 기	2	세대간벽두께 : 180mm (복배근)
		내벽두께 : 150mm (복배근)
	1	-콘센트 설치 (바닥 마감선 기준)
		[거실] 천정매립형 에어컨 :
		[안방] 벽걸이형 에어컨 : 1900
		[화장실] 양변기 열 : 900
		[주방] 조리대 : 중앙 / 냉장고 : 350 / 후드 : 2100
비 고	2	-비디오폰(VP),보일러온도조절기(B),스위치(S) 설치 (거실 아트홀 위치)
		-위치 표기
		에어컨 실외기
		에어컨 콘센트
		냉매, 배수관 (배수관수직매립)
비 고	3	세대현관문
		## 규격"틀"포함 : 1000X2200
	1	

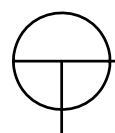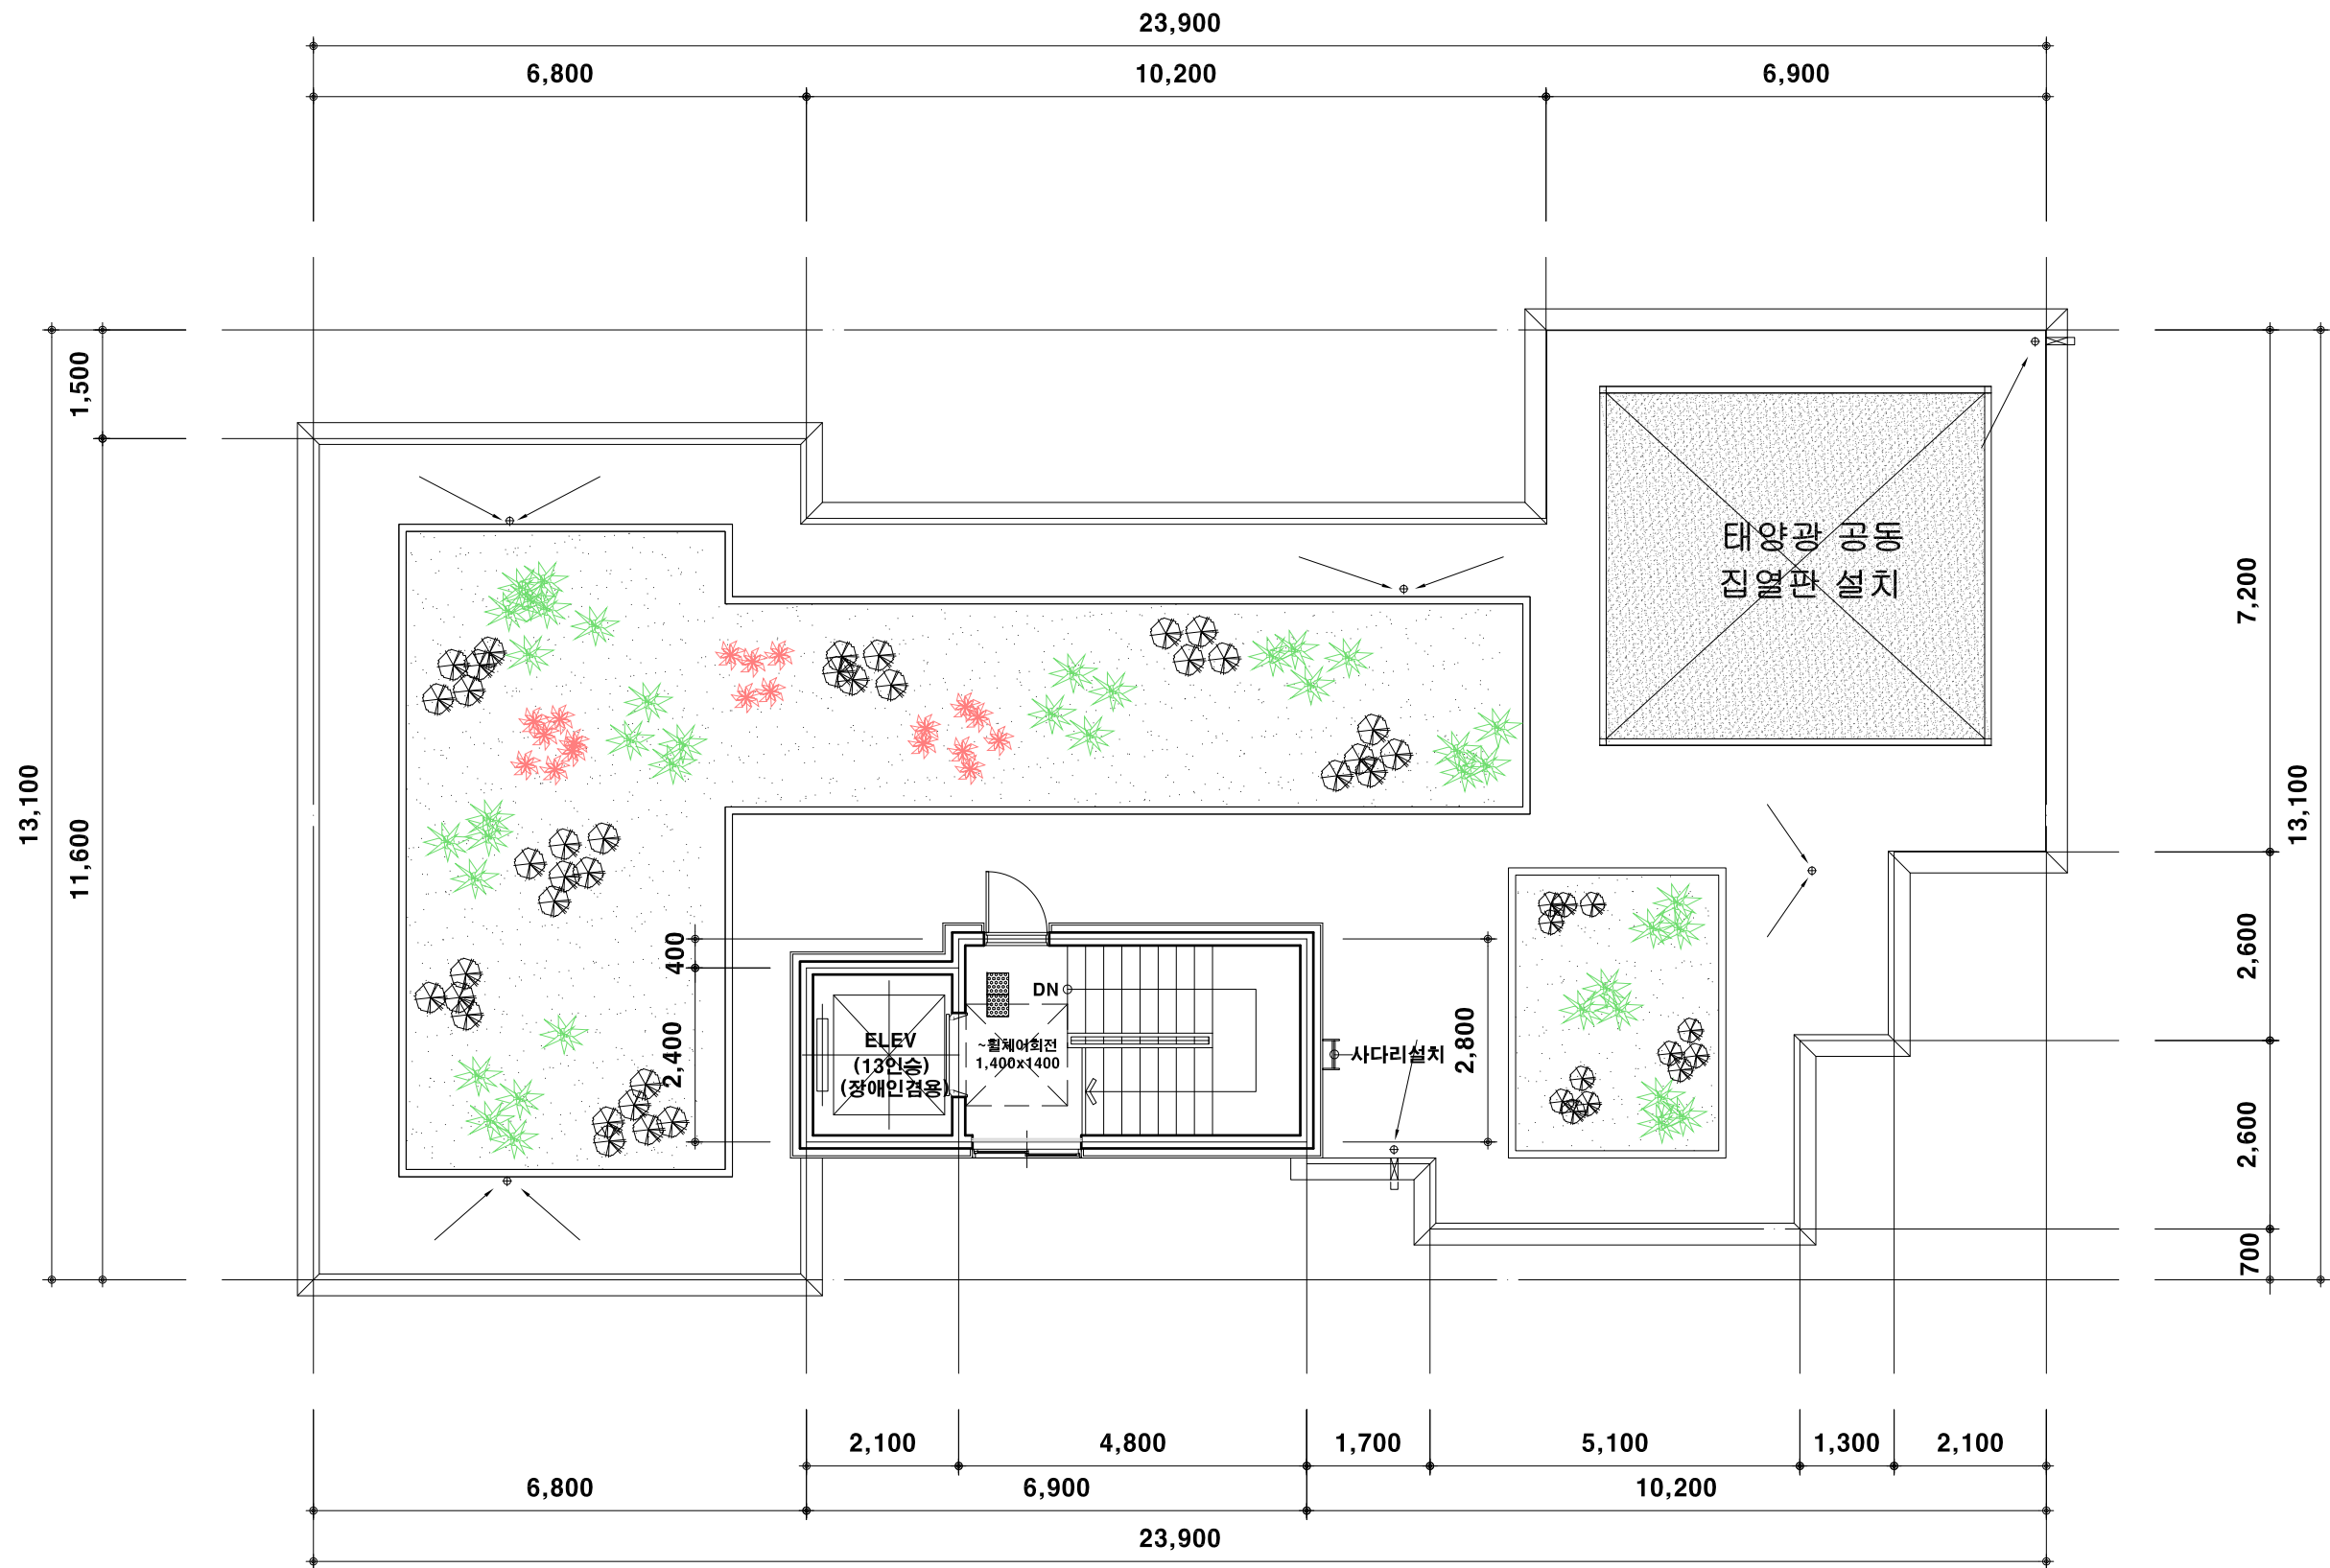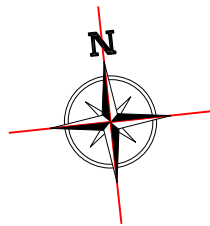

지붕 평면도
SCALE : 1/100

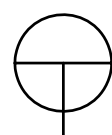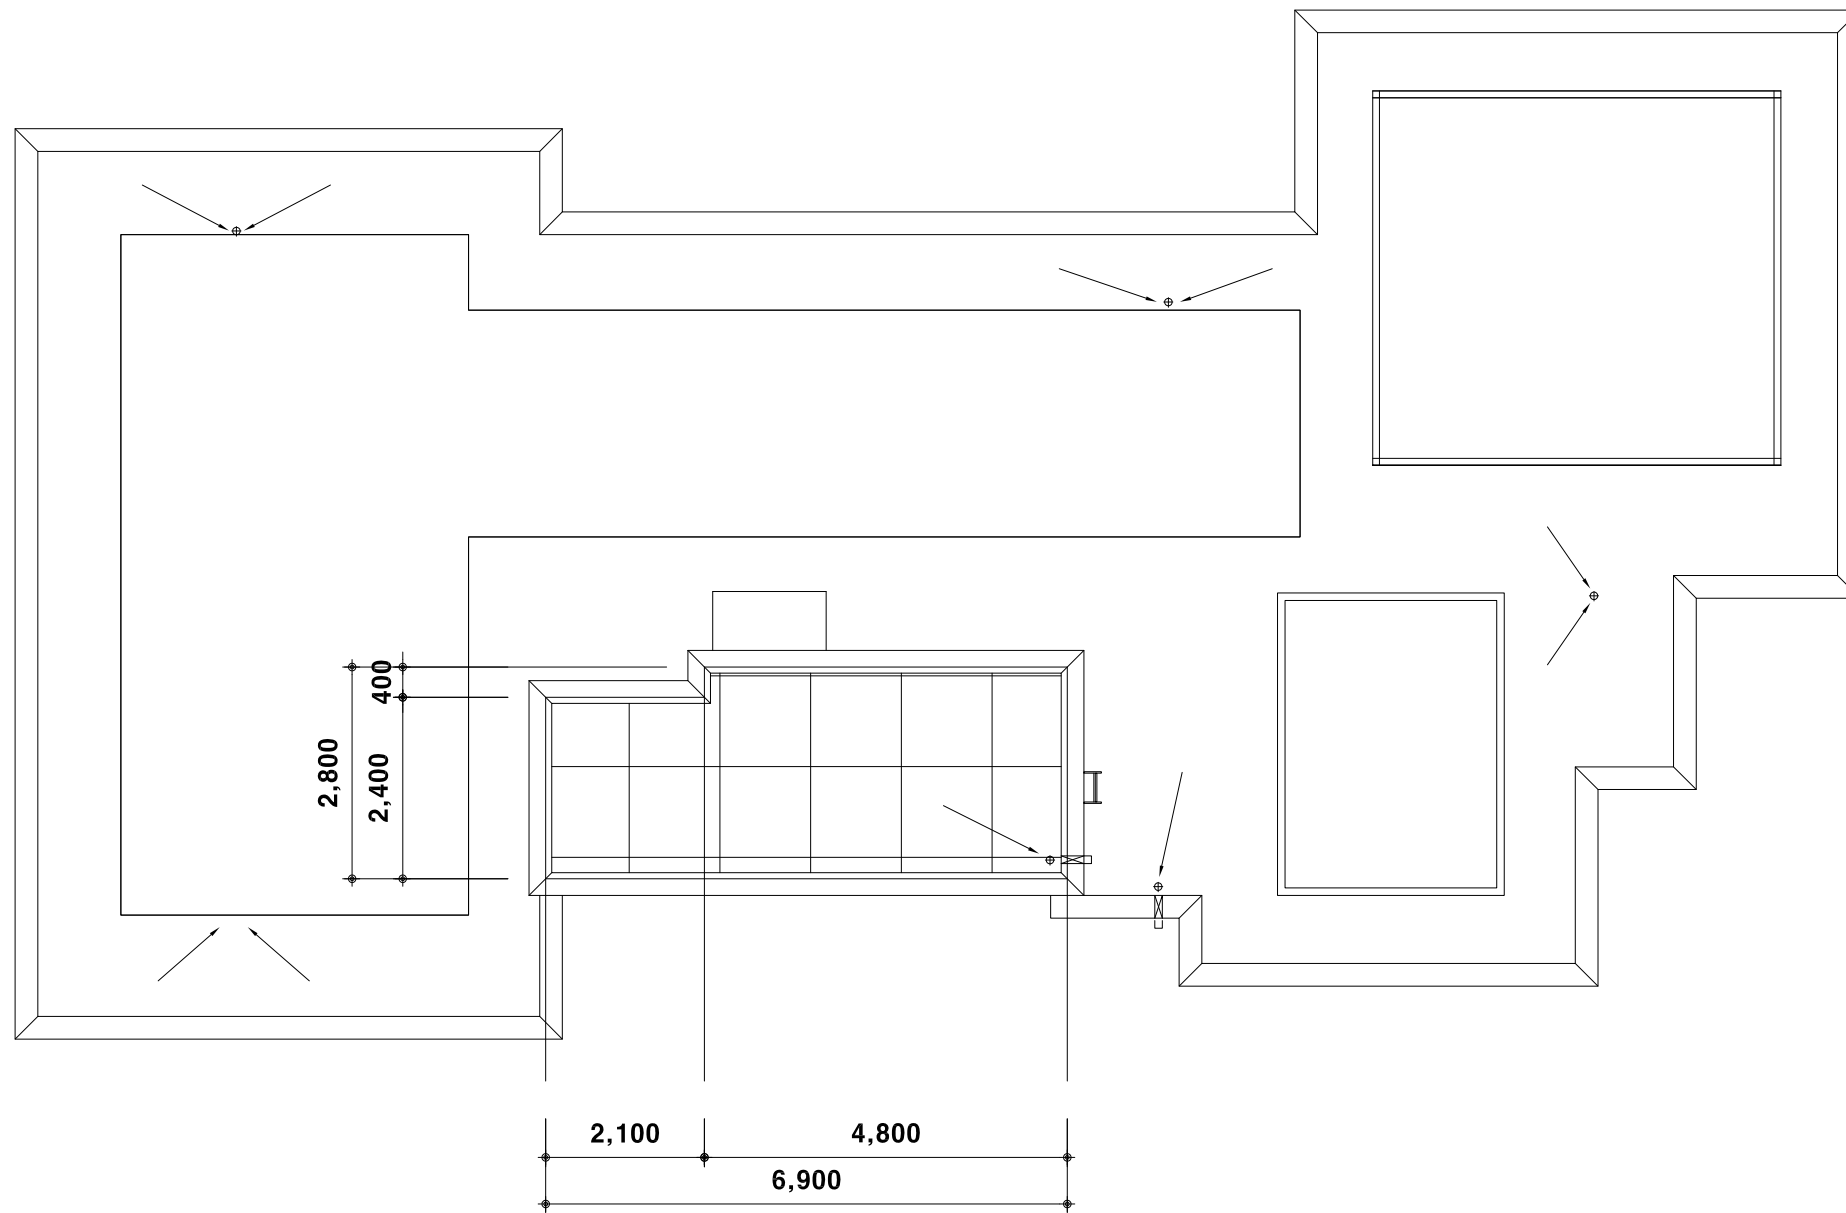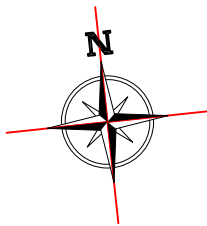

옥탑지붕 평면도

SCALE : 1/100







【본건전경】



【주위 환경】