


NO.	DATE	REVISION DESCRIPTION	BY	APP.
-----	------	----------------------	----	------

PROJECT TITLE
천호동 도시형생활주택 신축계획안

DATE	SCALE A1 : 1/ 50 A3 : 1/100
APPROVED	
CHECKED 2	DRAWING NO A - 101
CHECKED 1	
DRAWING	

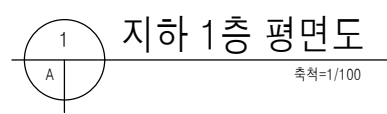

*NOTE:

■ 출입문 버튼 설치(인터폰 설치시)

비밀번호 버튼은 그 중심이 바닥면으로부터 0.8~1.2m 높이에 위치하도록 설치한다.

시각장애인이 구분할 수 있게 돌출물 부착 등

출입구 비밀번호 및 카드버튼

1층 평면도

축척=1/100



NO.	DATE	REVISION DESCRIPTION	BY	APP.



PROJECT TITLE
천호동 도시형생활주택 신축계획안

DRAWING TITLE
1층 평면도



DATE	SCALE A1 : 1/ 50 A3 : 1/100
APPROVED	
CHECKED 2	DRAWING NO A - 102
CHECKED 1	
DRAWING	

NO.	DATE	REVISION DESCRIPTION	BY	APP.
-----	------	----------------------	----	------

PROJECT TITLE
하수처리 시설개선사업에 따른 수질개선에

DRAWING TITLE
2~3층 평면도

DATE	SCALE A1 : 1/ 50 A3 : 1/100
APPROVED	
CHECKED 2	DRAWING NO A - 103
CHECKED 1	
DRAWING	

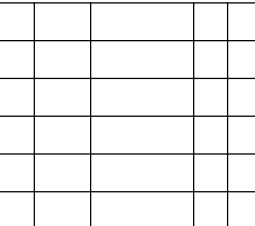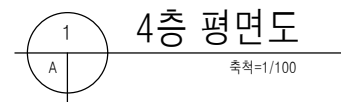

CheonSan
Architects / Development Co., Ltd.
제주특별자치도 제주시 양정로14, 3층(건일빌, 역신빌)
Tel. 064-745-0641 Fax. 064-745-0642

DRAWING TITLE
4층 평면도

DATE	SCALE A1 : 1/ 50 A3 : 1/100
APPROVED	
CHECKED 2	DRAWING NO A - 104
CHECKED 1	
DRAWING	

NO.	DATE	REVISION DESCRIPTION	BY	APP.
-----	------	----------------------	----	------


PROJECT TITLE
천호동 도시형생활주택 신축계획안




DATE	SCALE A1 : 1/ 50 A3 : 1/100
APPROVED	
CHECKED 2	DRAWING NO A - 105
CHECKED 1	
DRAWING	

NO.	DATE	REVISION DESCRIPTION	BY	APP.
-----	------	----------------------	----	------

PROJECT TITLE

DRAWING TITLE

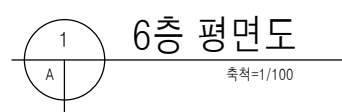

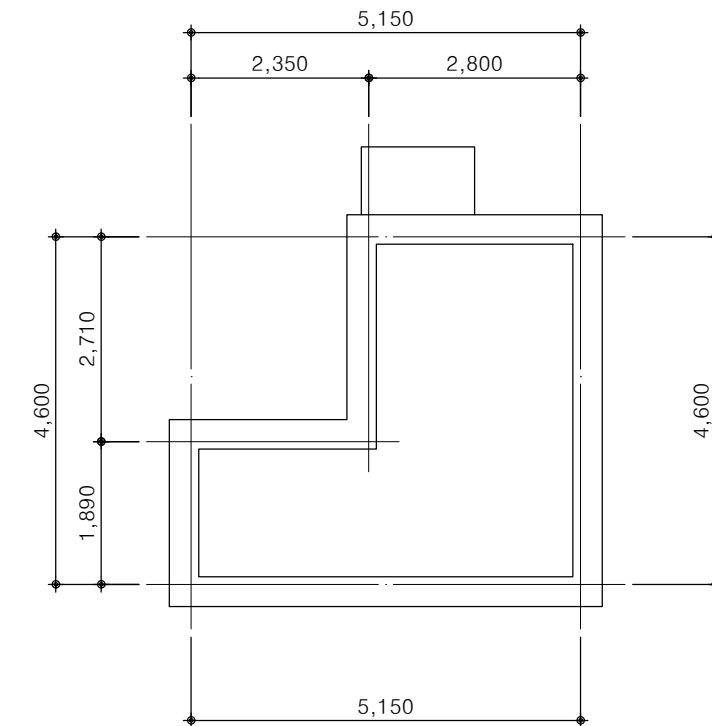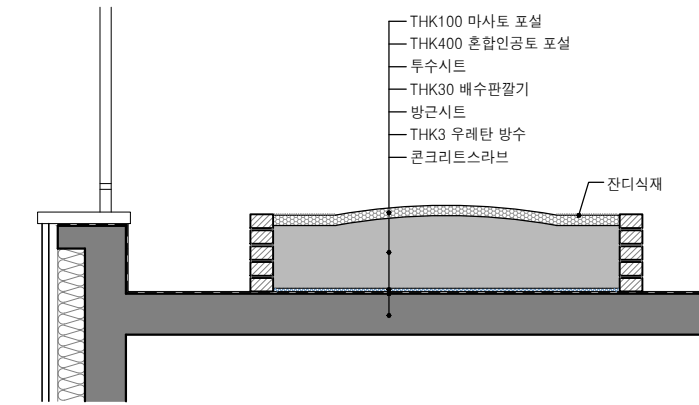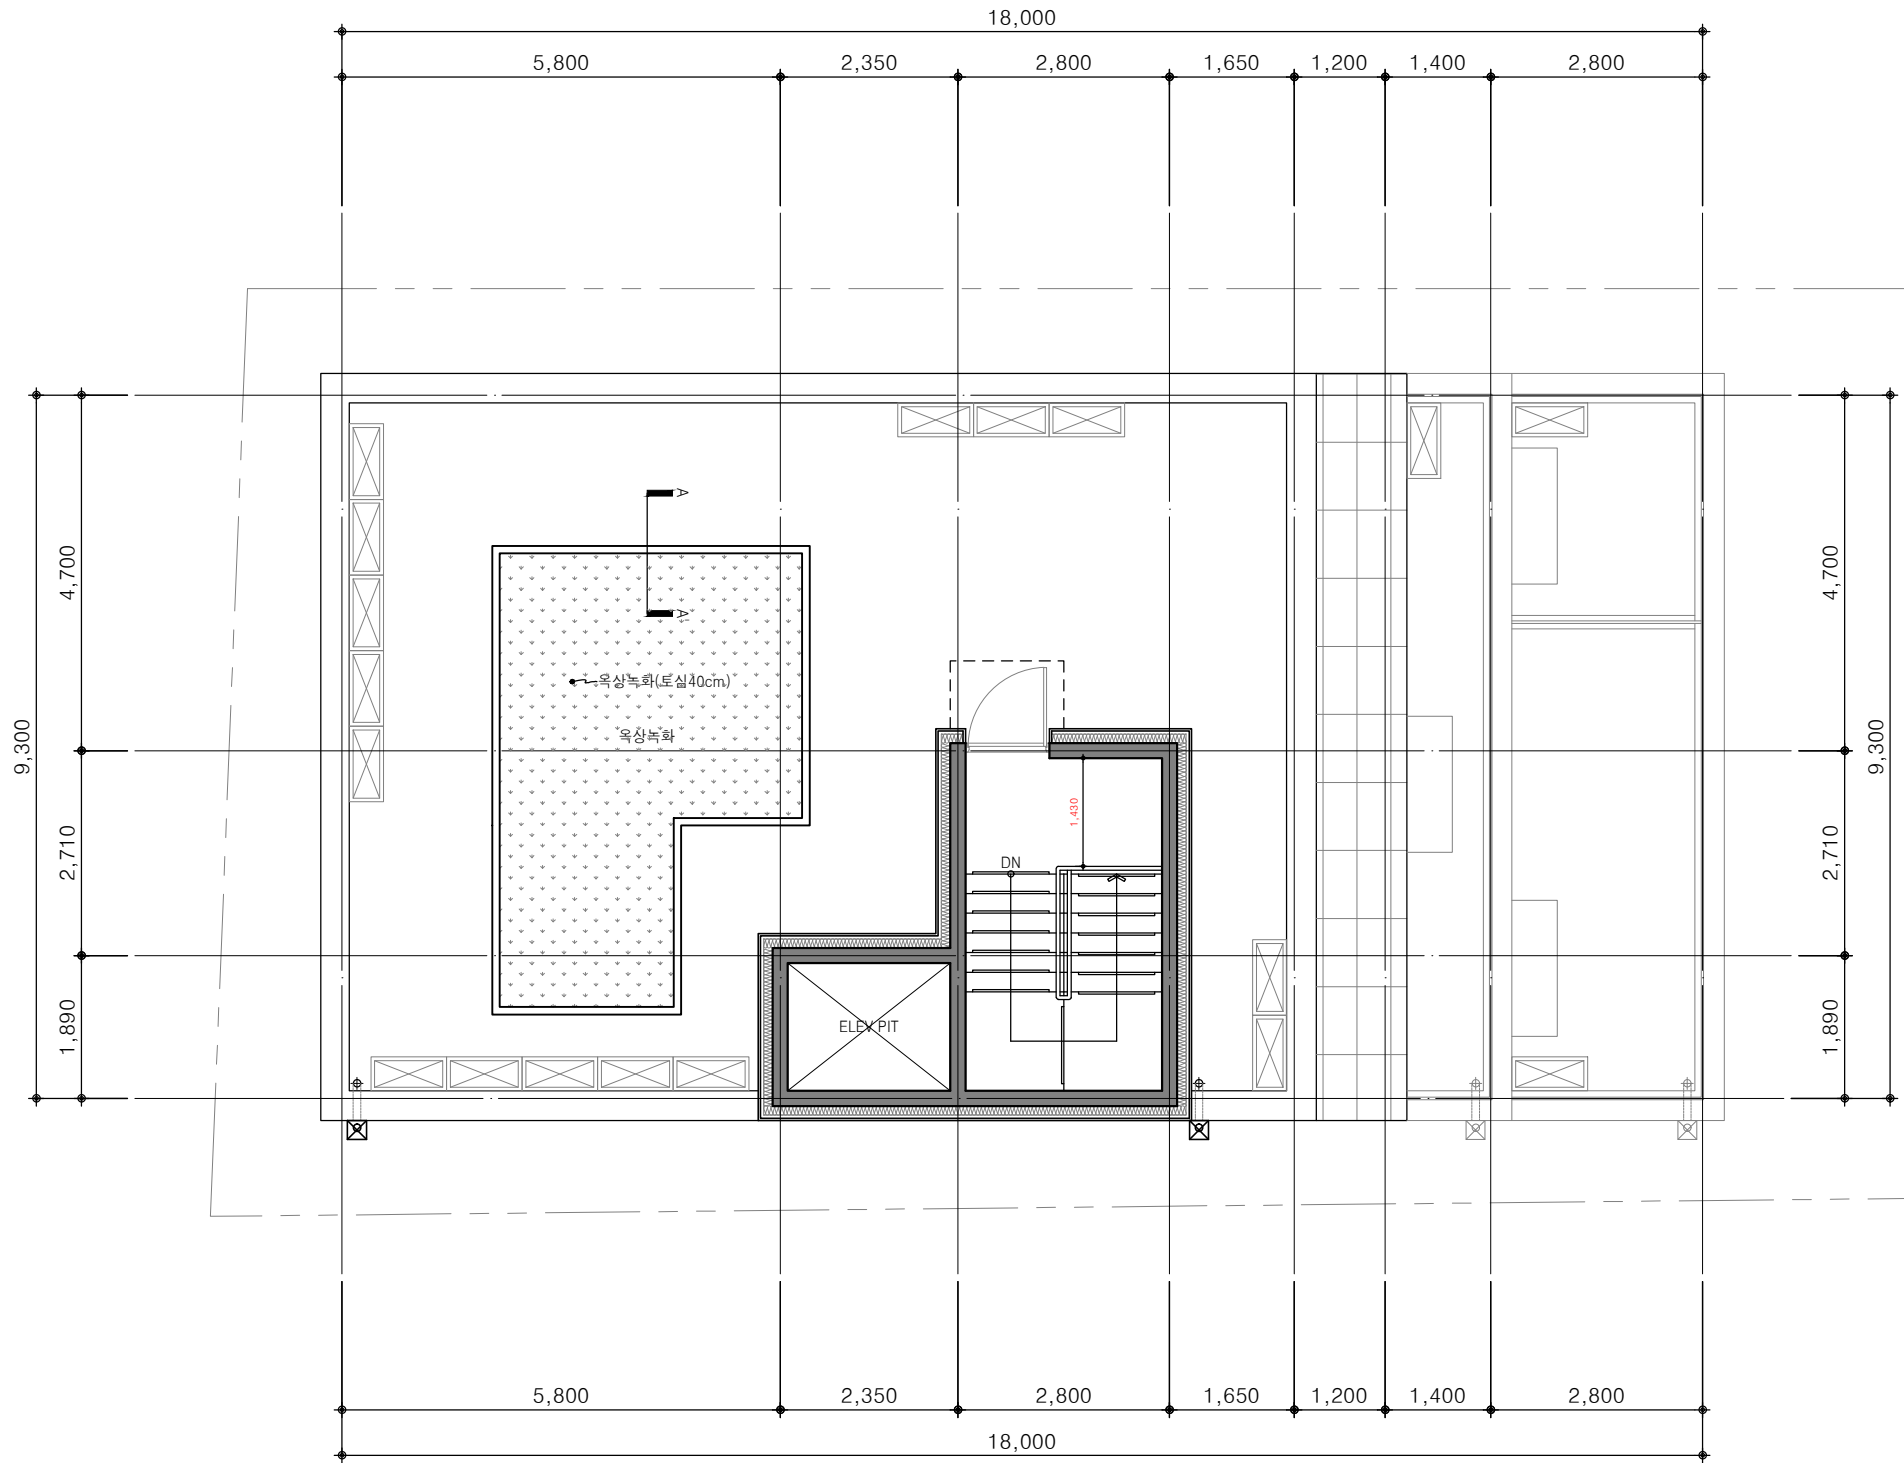

*NOTE:



NO.	DATE	REVISION DESCRIPTION	BY	APP.

CheonSan
Architects / Development Co., Ltd.
제주시청지하도 지하 3층(안양동, 국민빌딩)
Tel. 064-745-0641 Fax. 064-745-0642

PROJECT TITLE
천호동 도시형생활주택 신축계획안

DRAWING TITLE
지붕층 평면도

DATE	SCALE
APPROVED	A1 : 1/ 50 A3 : 1/100
CHECKED 2	DRAWING NO
CHECKED 1	A - 107
DRAWING	

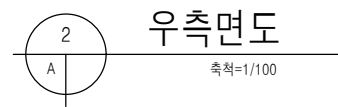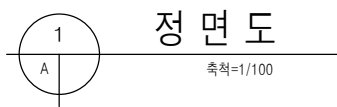

NO.	DATE	REVISION DESCRIPTION	BY	APP.



PROJECT TITLE
천호동 도시형생활주택 신축계획안

입면도-1

DATE	SCALE A1 : 1/ 50 A3 : 1/ 100
APPROVED	
CHECKED 2	DRAWING NO A - 201
CHECKED 1	
DRAWING	



NO.	DATE	REVISION DESCRIPTION	BY	APP.
-----	------	----------------------	----	------



PROJECT TITLE
천호동 도시형생활주택 신축계획안

DRAWING TITLE
입면도-2

DATE	SCALE
APPROVED	A1 : 1/ 50 A3 : 1/100
CHECKED 2	DRAWING NO
CHECKED 1	A - 201
DRAWING	