




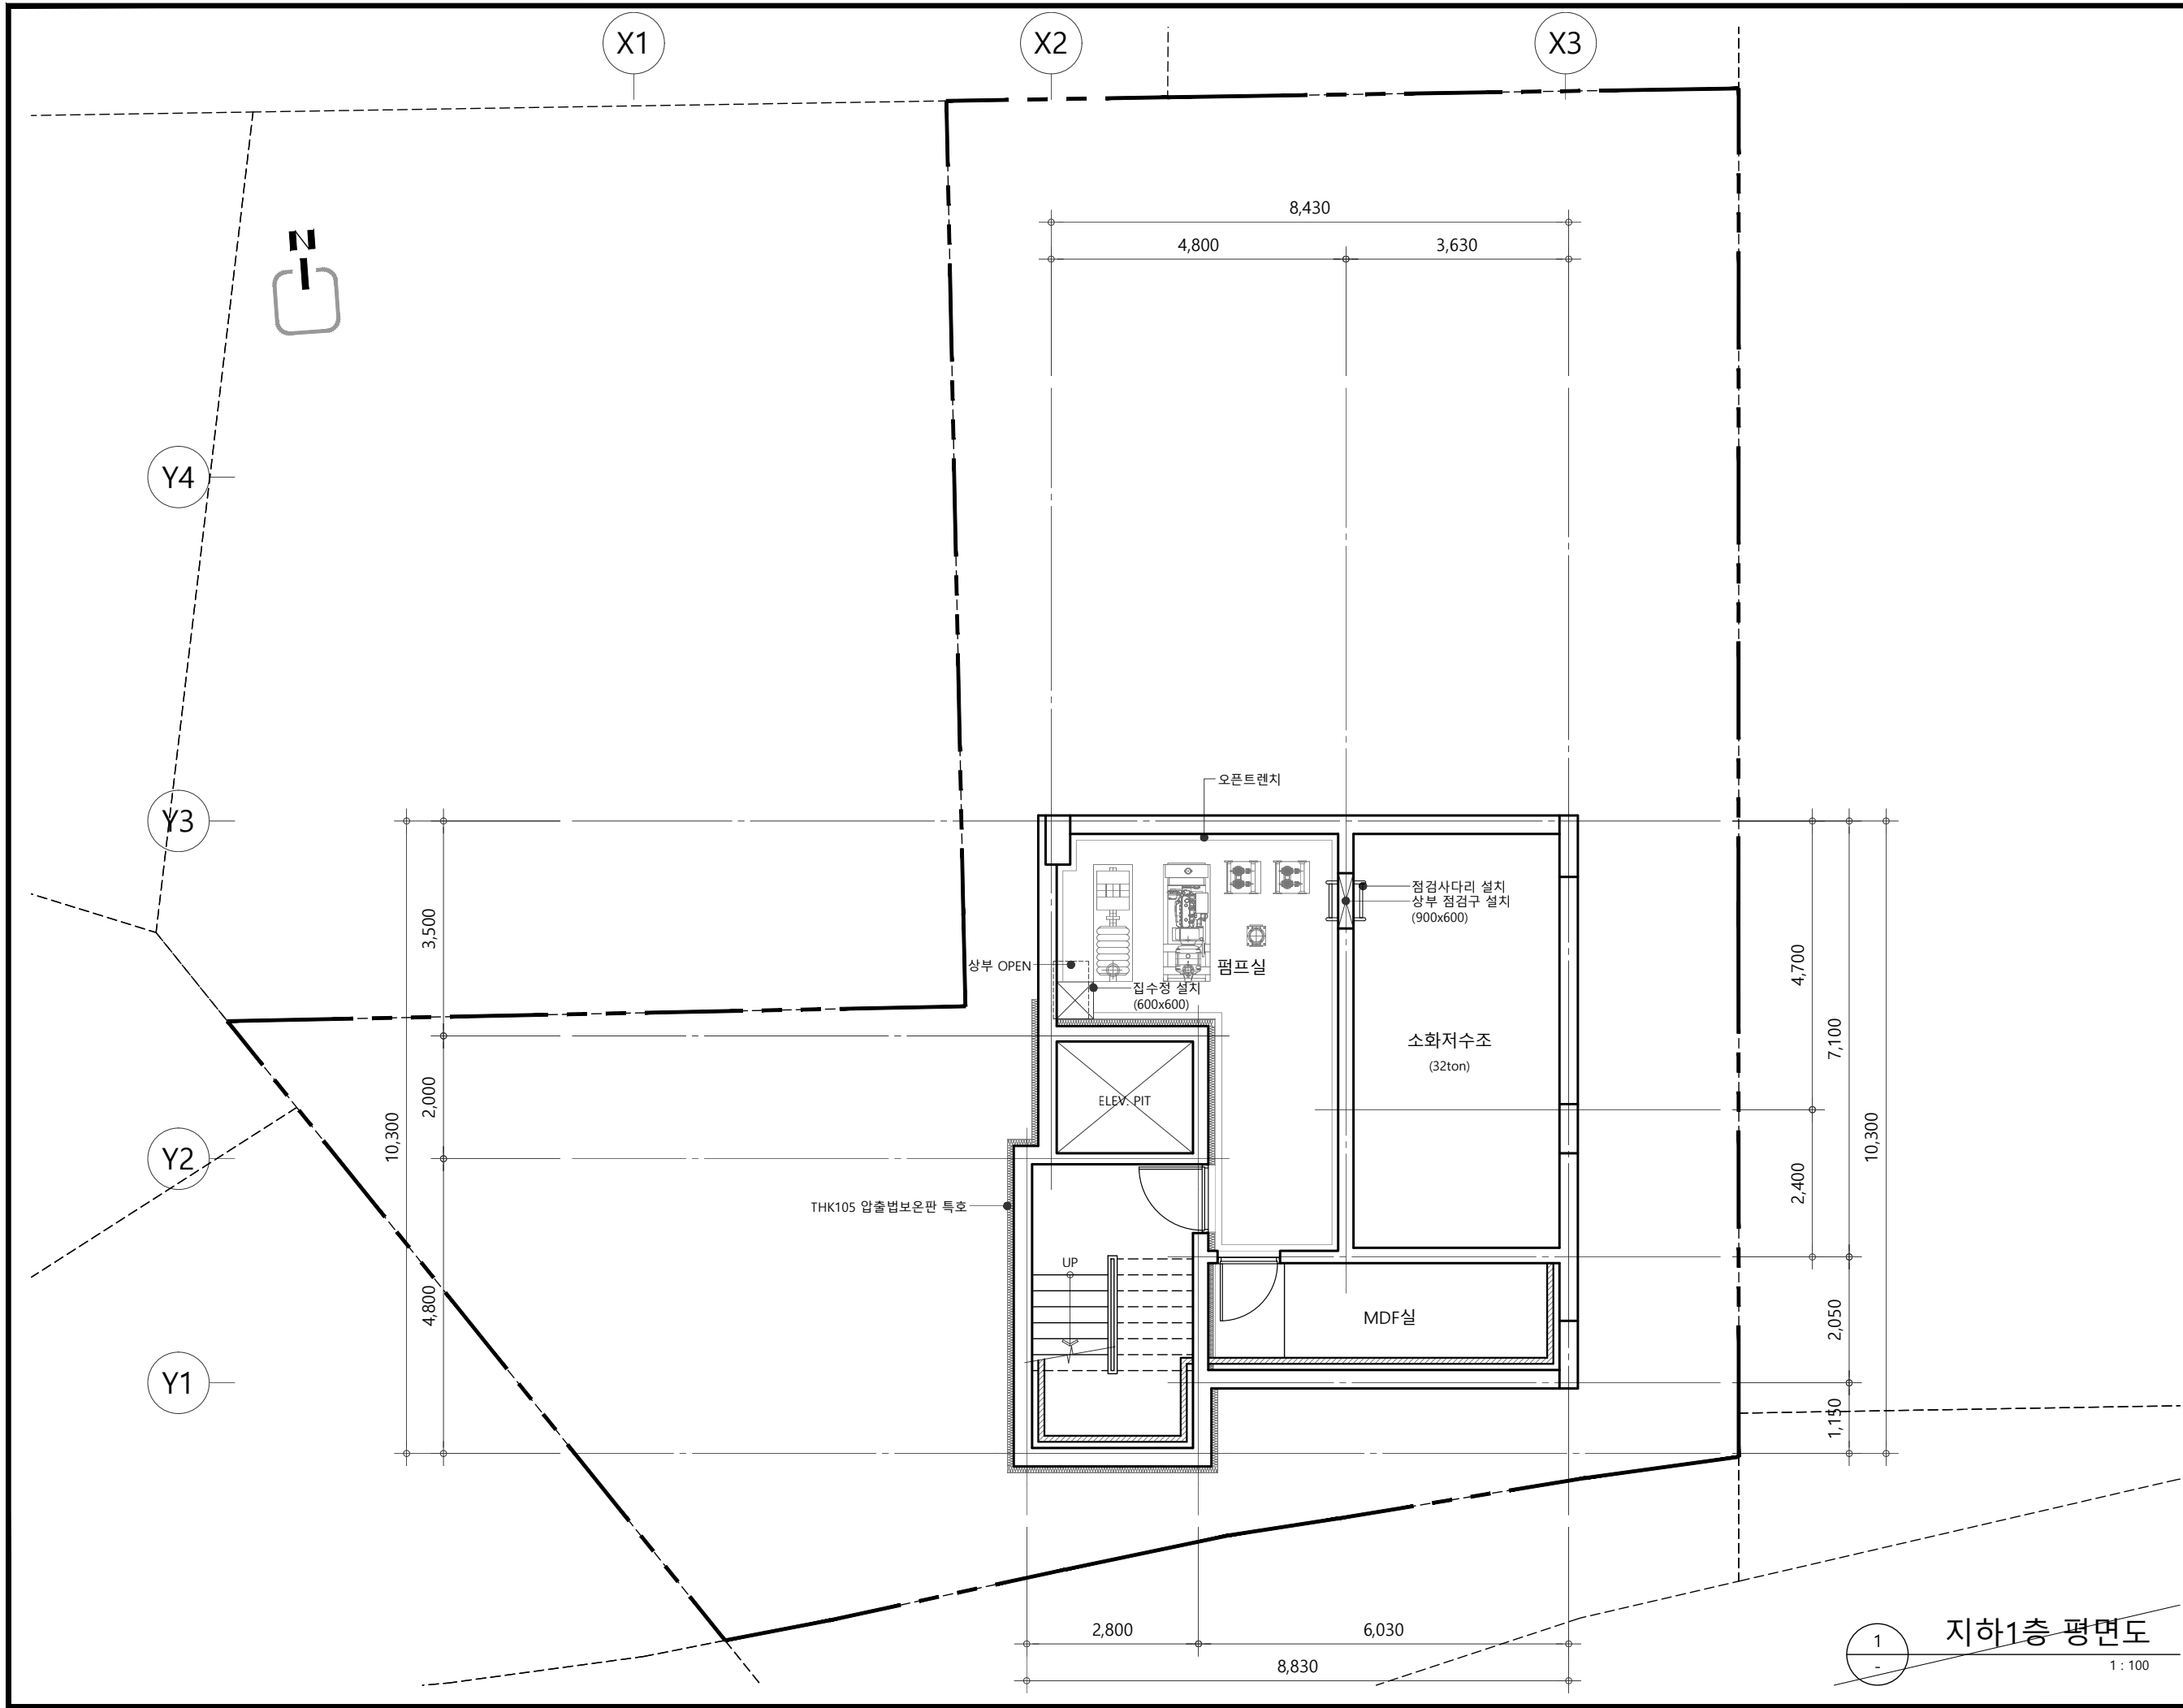

PROJECT TITLE			천호동 도시형생활주택 및 오피스텔 신축공사
KEY-MAP			
NOTES			
DESCRIPTION			
Rev.			Issue & Date
CONSULTANT			Check
ESIN ARCHITECTS			건축사사무소이신
4F - #401 Wonil Bldg, 42, Cheonho-daero 170-gil, Gangdong-gu, Seoul, Korea 05381			
TEL 070. 7767. 1546 FAX 0504. 322. 1546			
E-MAIL esinarchi@gmail.com			
Drawing			지하1층 평면도
Scale			1 : 100
Drawn by			Checked by
Approved by			
Drawing number			A31 - 101
PROJECT CODE			ESIN2203-001

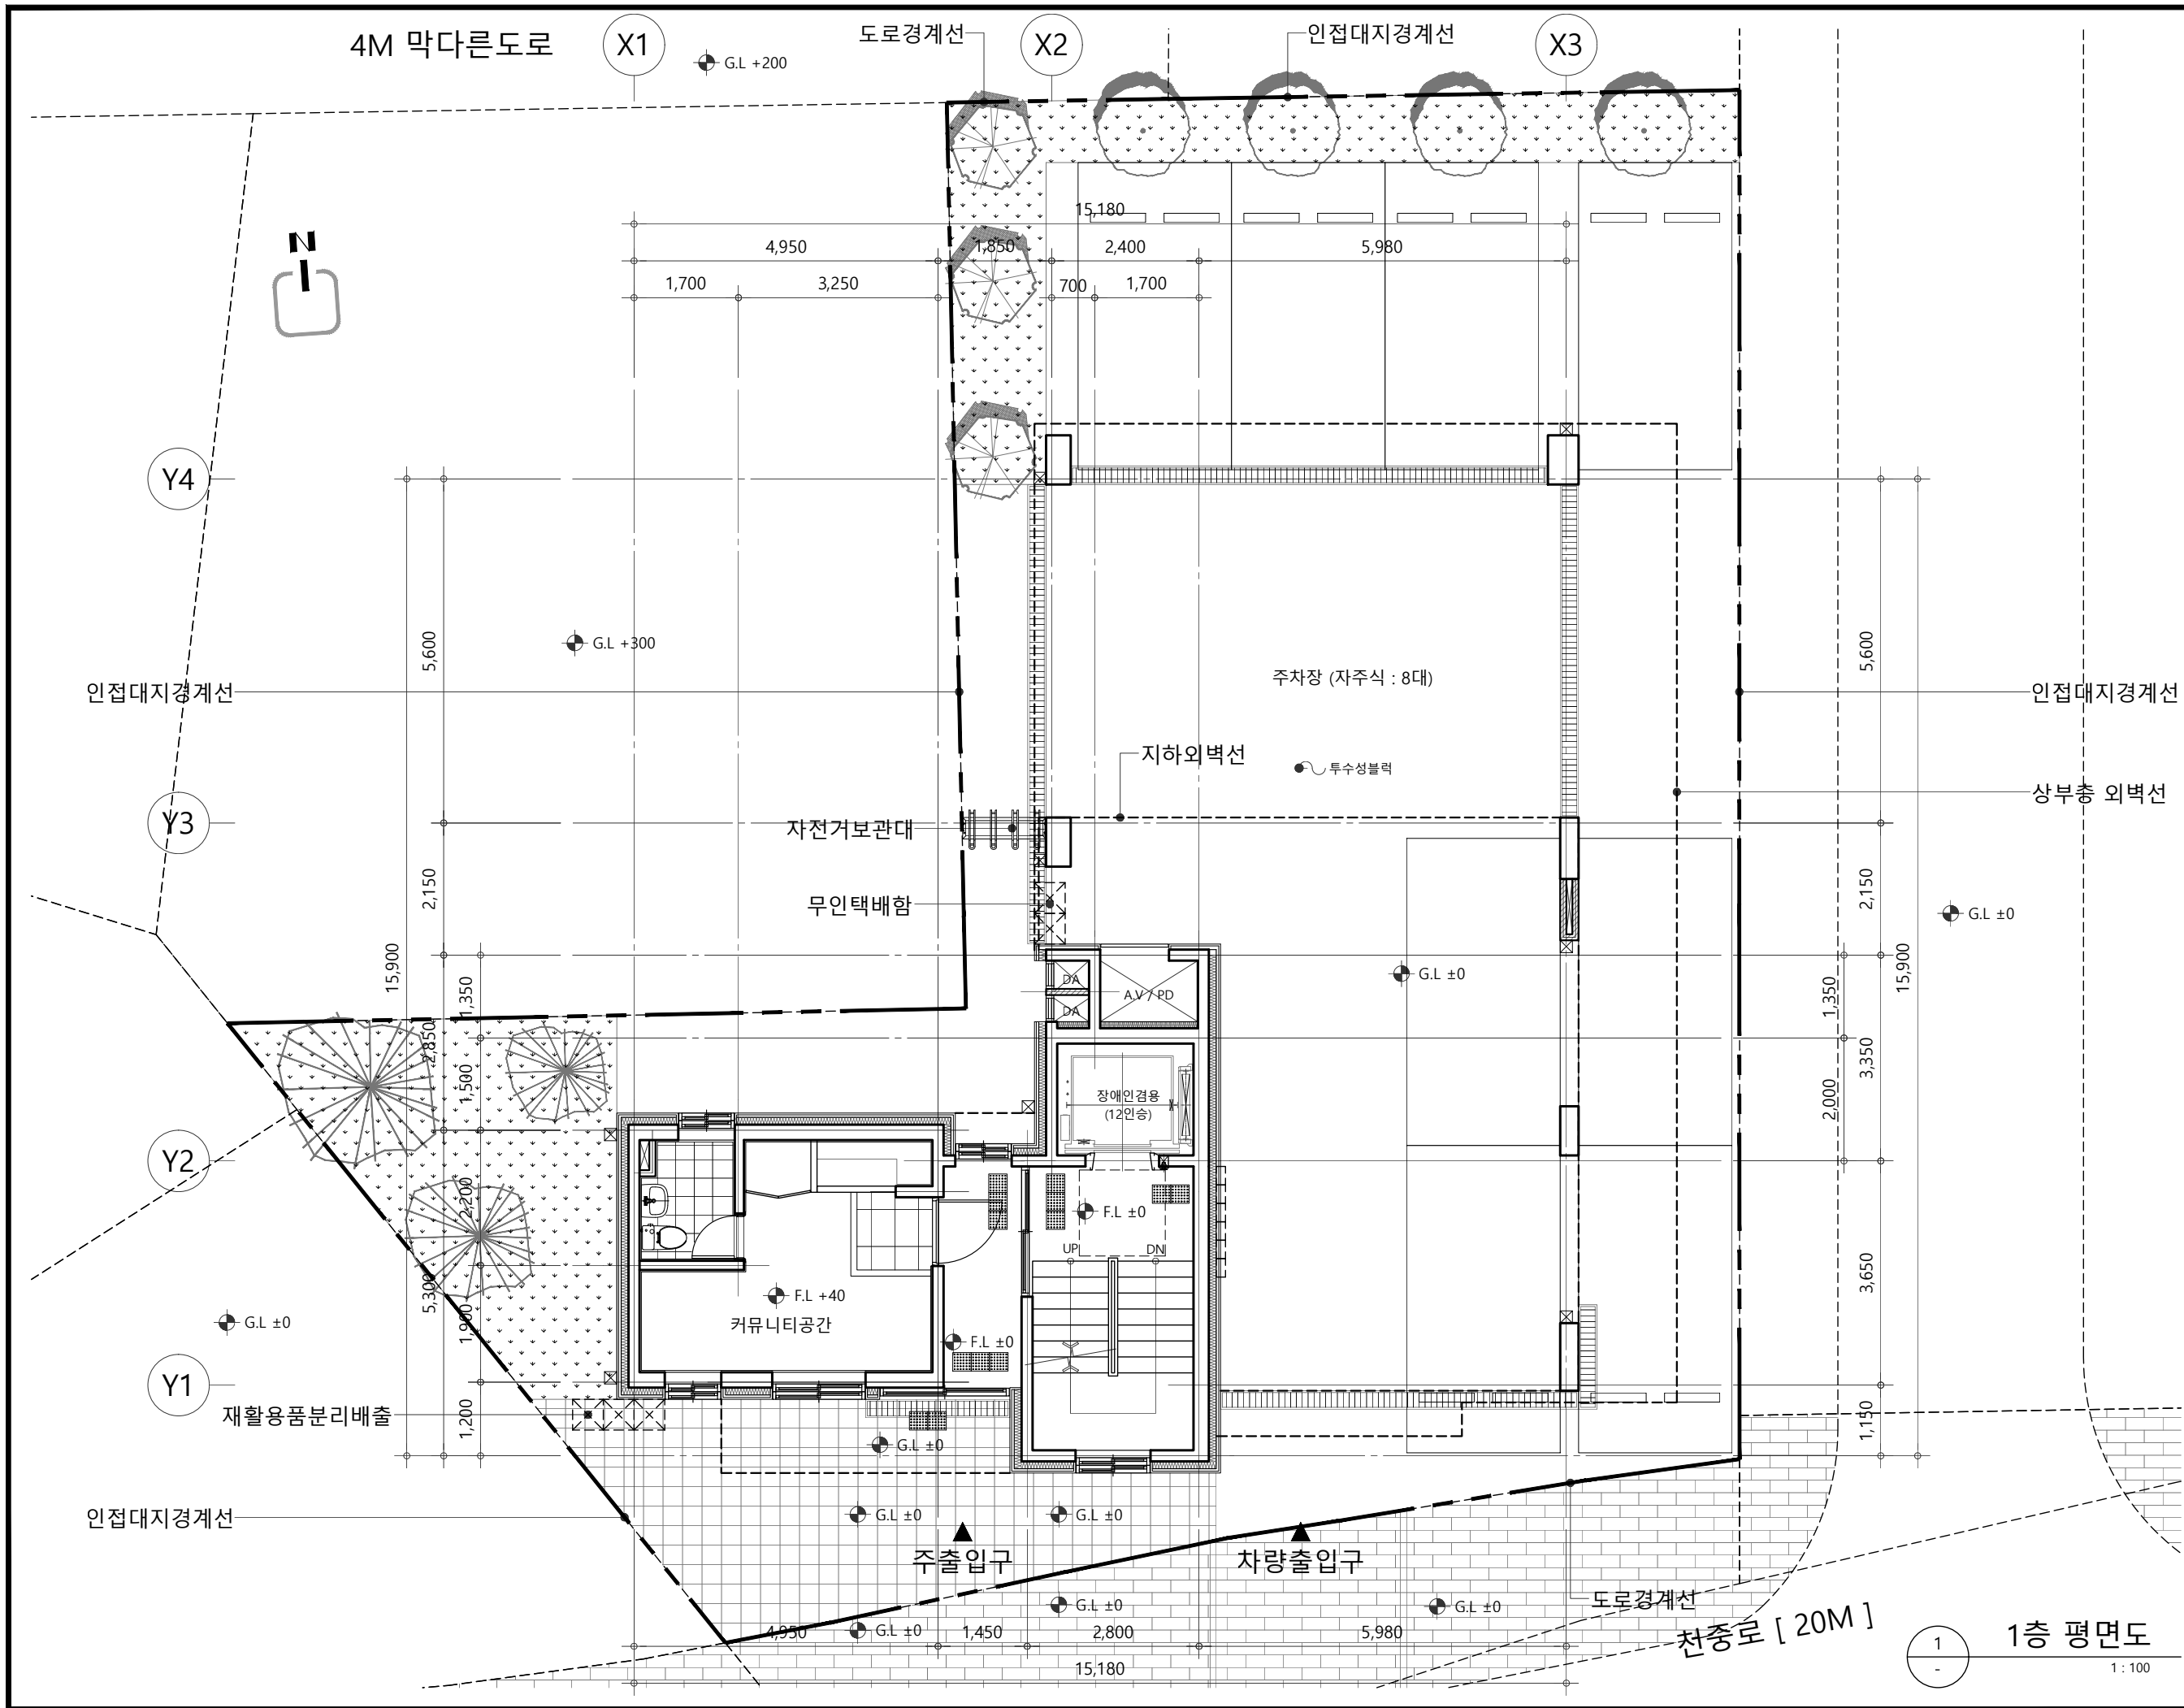


PROJECT TITLE			천호동 도시형생활주택 및 오피스텔 신축공사
KEY-MAP			
NOTES			
DESCRIPTION			
Rev.			Issue & Date
CONSULTANT			Check
ESIN ARCHITECTS			건축사사무소이신
4F - #401 Wonil Bldg, 42, Cheonho-daero 170-gil, Gangdong-gu, Seoul, Korea 05381 TEL 070.7767.1546 FAX 0504.322.1546 E-MAIL esinarchi@gmail.com			
Drawing			1층 평면도
Scale			1 : 100
Drawn by			Checked by
Approved by			
Drawing number			A31 - 102
PROJECT CODE			ESIN2203-001

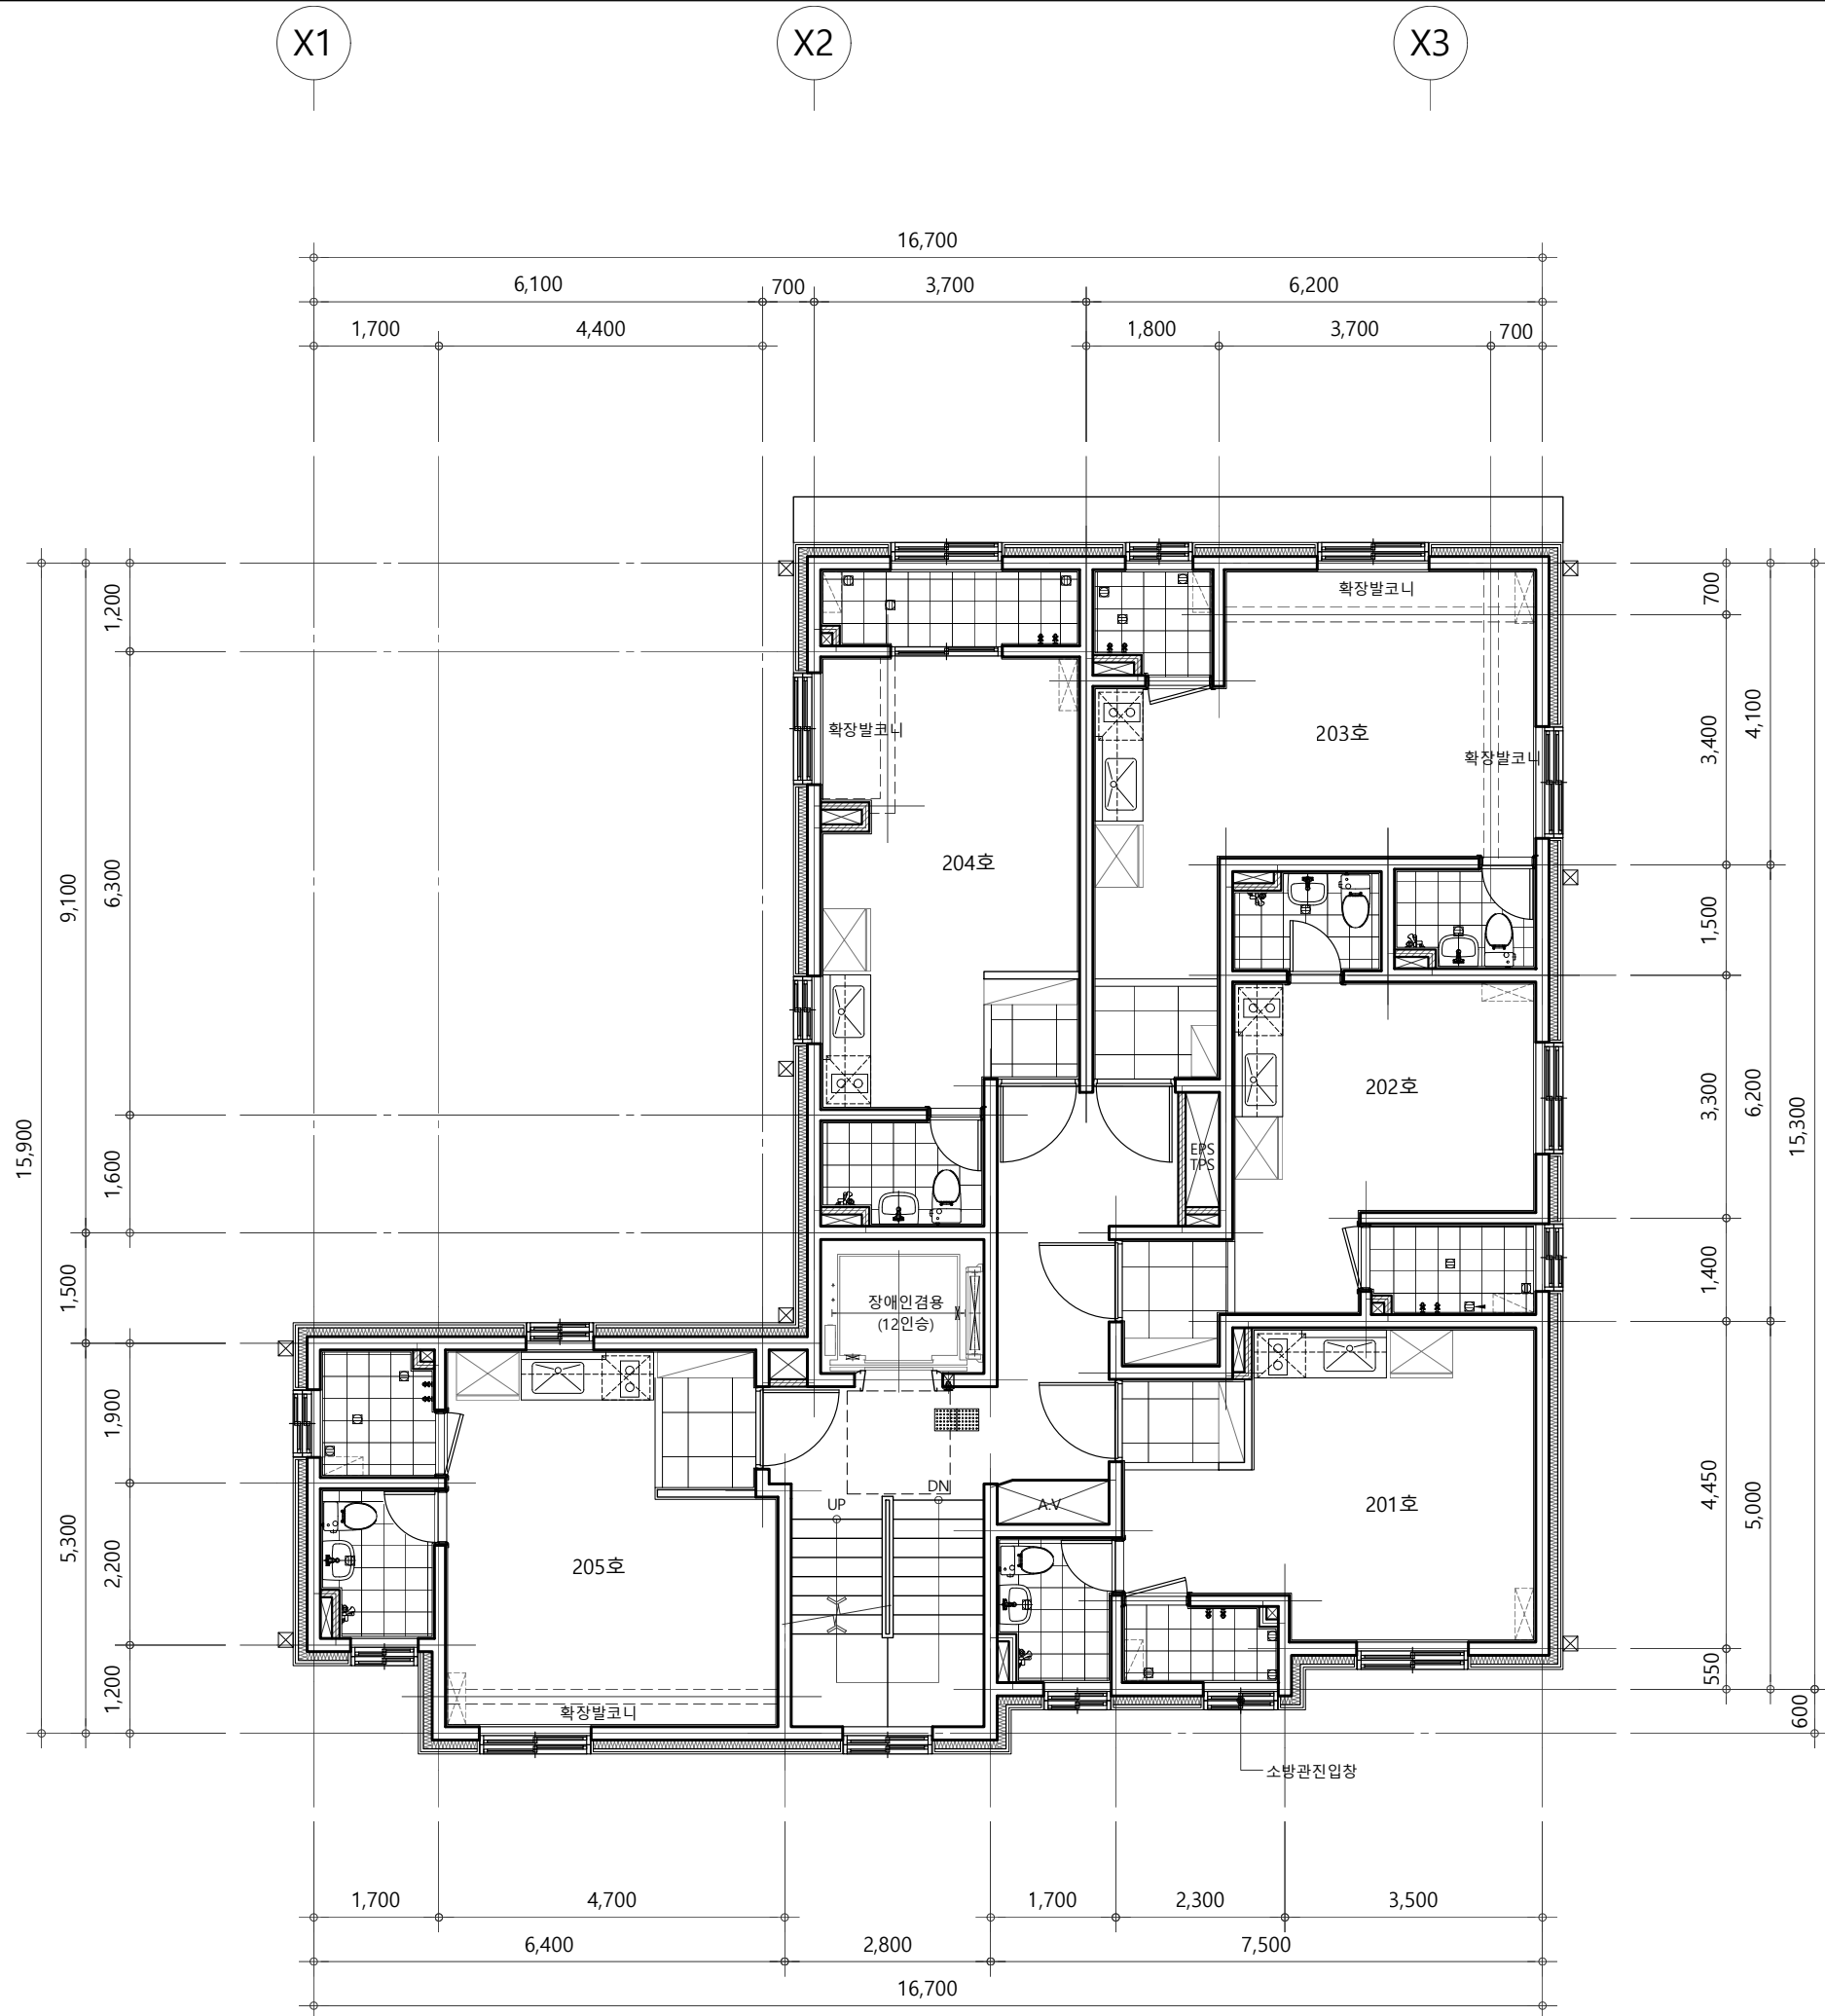

1
-


2층 평면도
1 : 100

PROJECT TITLE	천호동 도시형생활주택 및 오피스텔 신축공사
KEY-MAP	
NOTES	
DESCRIPTION	
Rev.	Issue & Date
CONSULTANT	Check
ESIN ARCHITECTS 건축사사무소 이신	
4F - #401 Wonil Bldg, 42, Cheonho-daero 170-gil, Gangdong-gu, Seoul, Korea 05381 TEL 070.7767.1546 FAX 0504.322.1546 E-MAIL esinarchi@gmail.com	
Drawing	2층 평면도
Scale	1 : 100
Drawn by	Checked by
Approved by	
Drawing number	A31 - 103
PROJECT CODE	ESIN2203-001

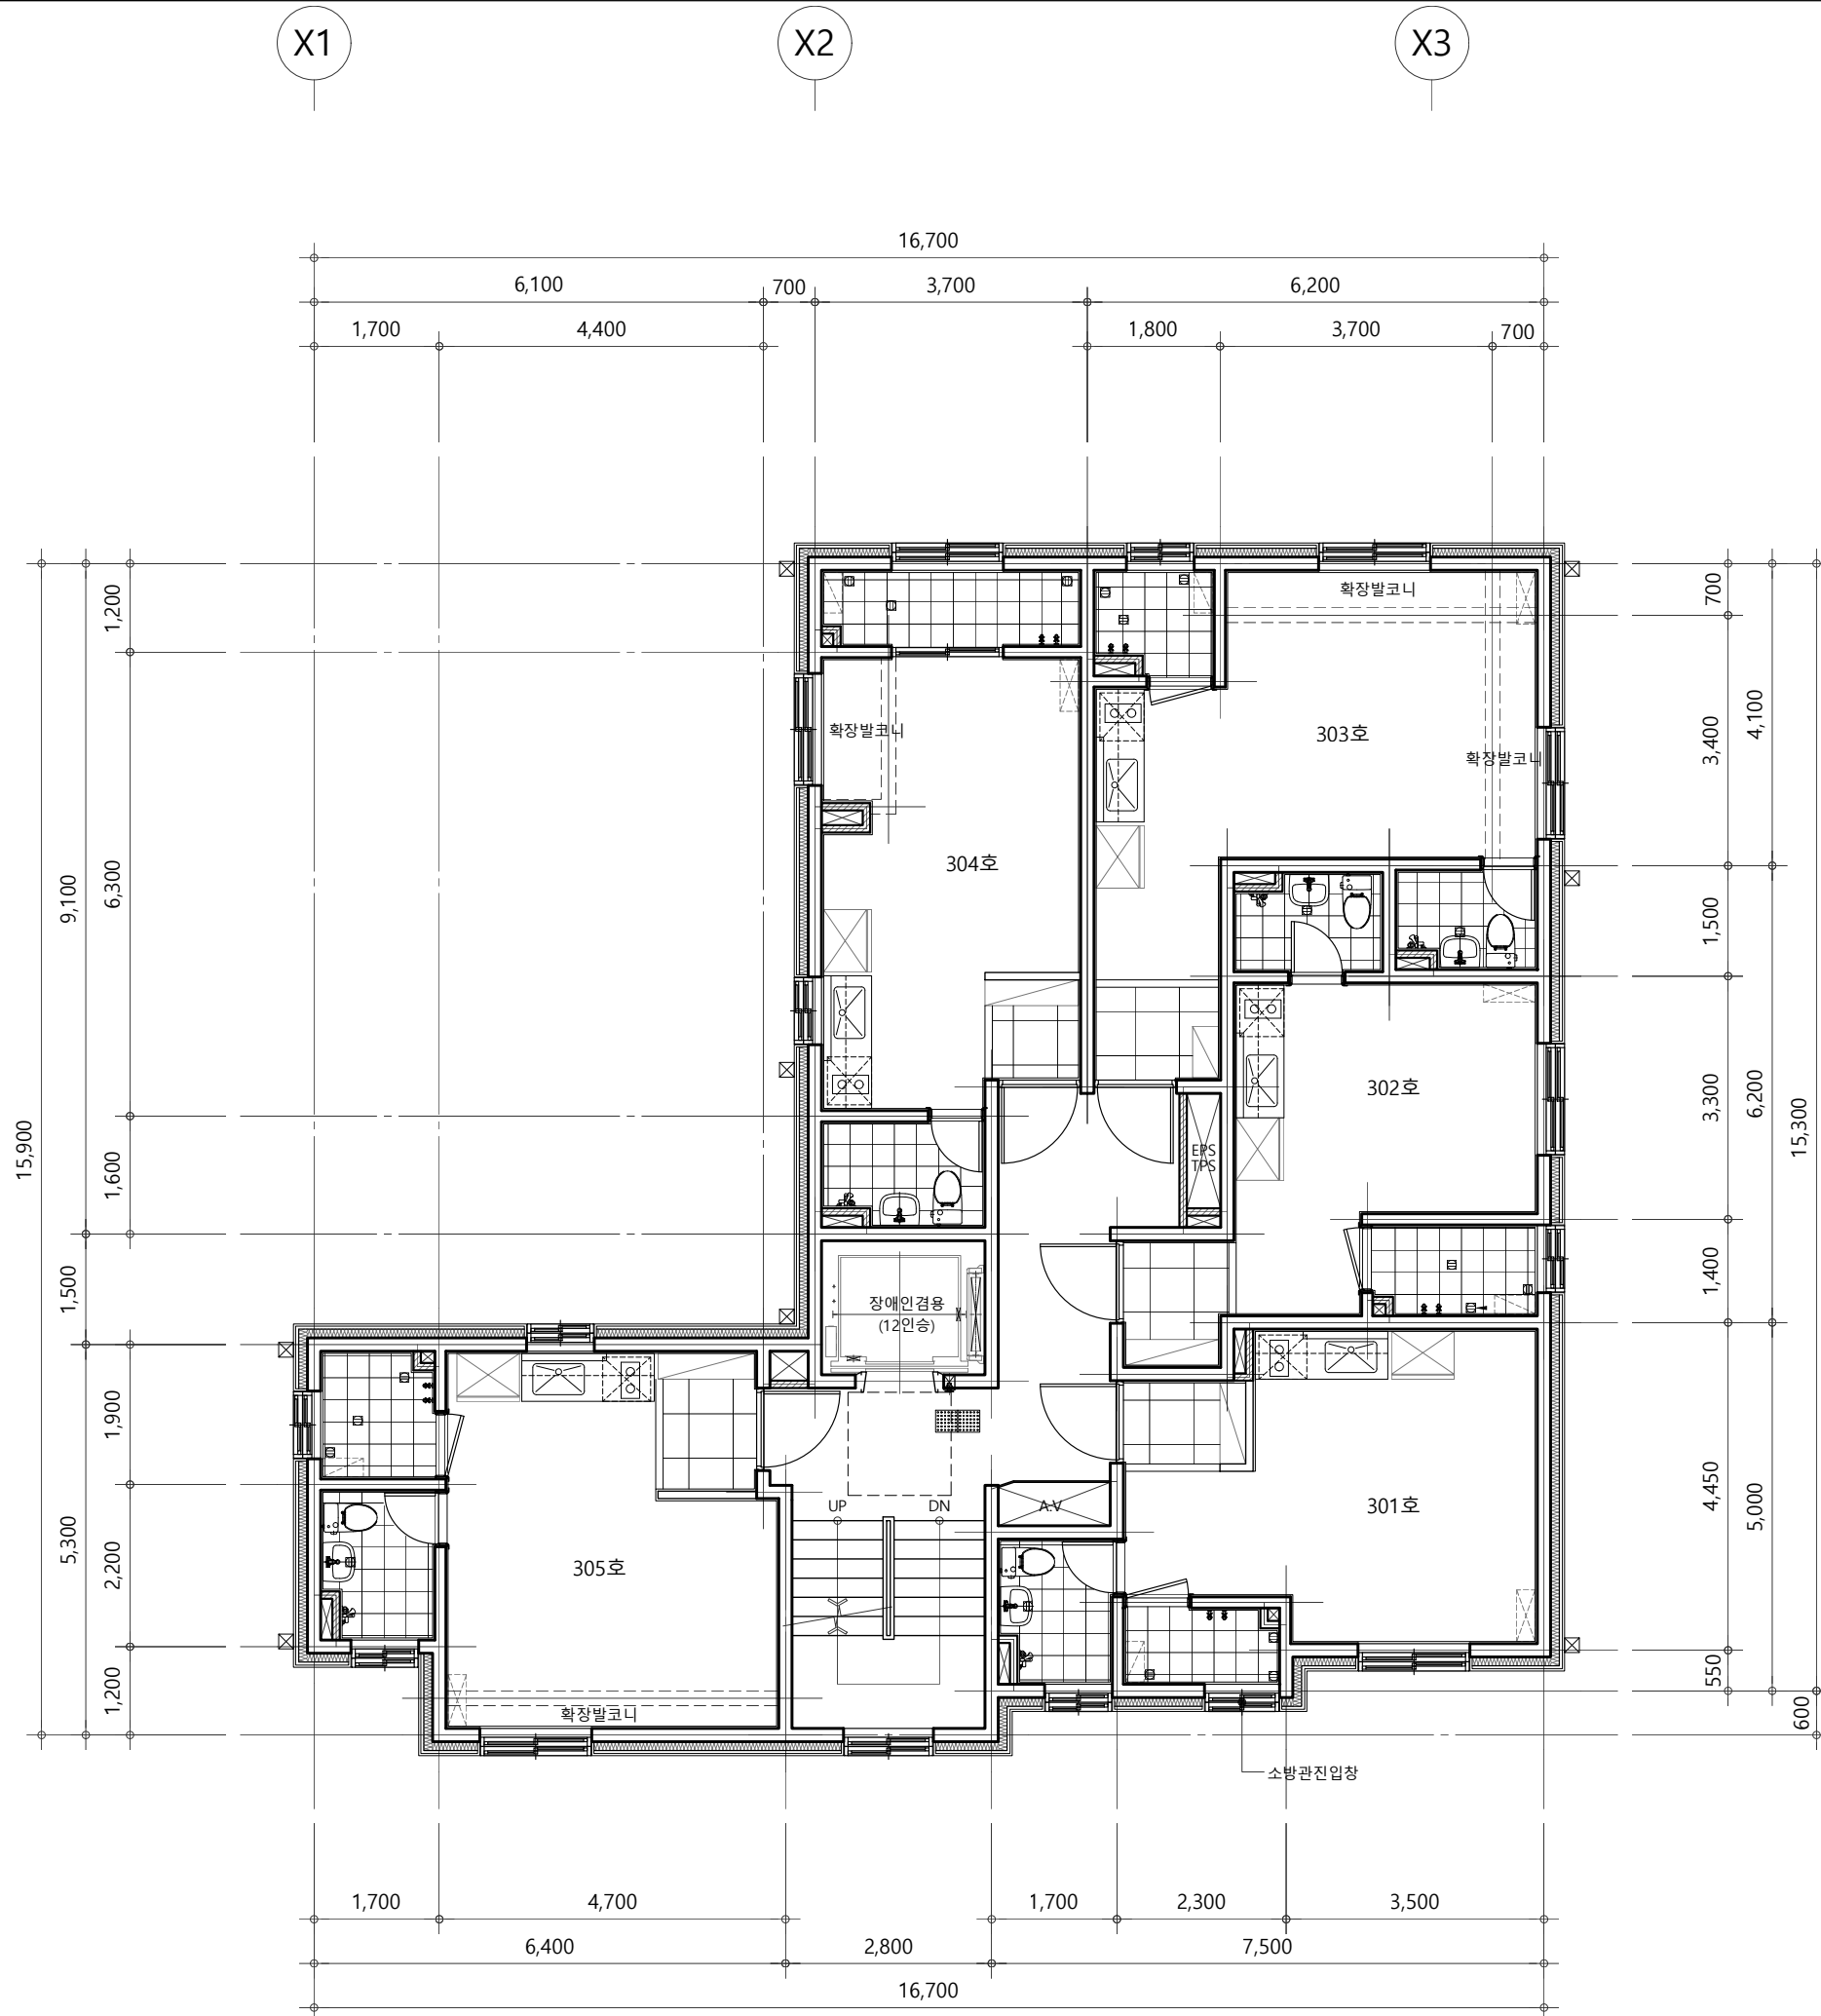


1
-
3층 평면도
1 : 100

PROJECT TITLE		
천호동 도시형생활주택 및 오피스텔 신축공사		
KEY-MAP		
NOTES		
DESCRIPTION		
Rev.		
Issue & Date		
Check		
CONSULTANT		
ESIN ARCHITECTS 건 축 사 사 무 소 이 신 4F - #401 Wonil Bldg, 42, Cheonho-daero 170-gil, Gangdong-gu, Seoul, Korea 05381 TEL 070. 7767. 1546 FAX 0504. 322. 1546 E-MAIL esinarchi@gmail.com		
Drawing		
3층 평면도		
Scale		
1 : 100		
Drawn by		
Checked by		
Approved by		
Drawing number		
A31 - 104		
PROJECT CODE		
ESIN2203-001		

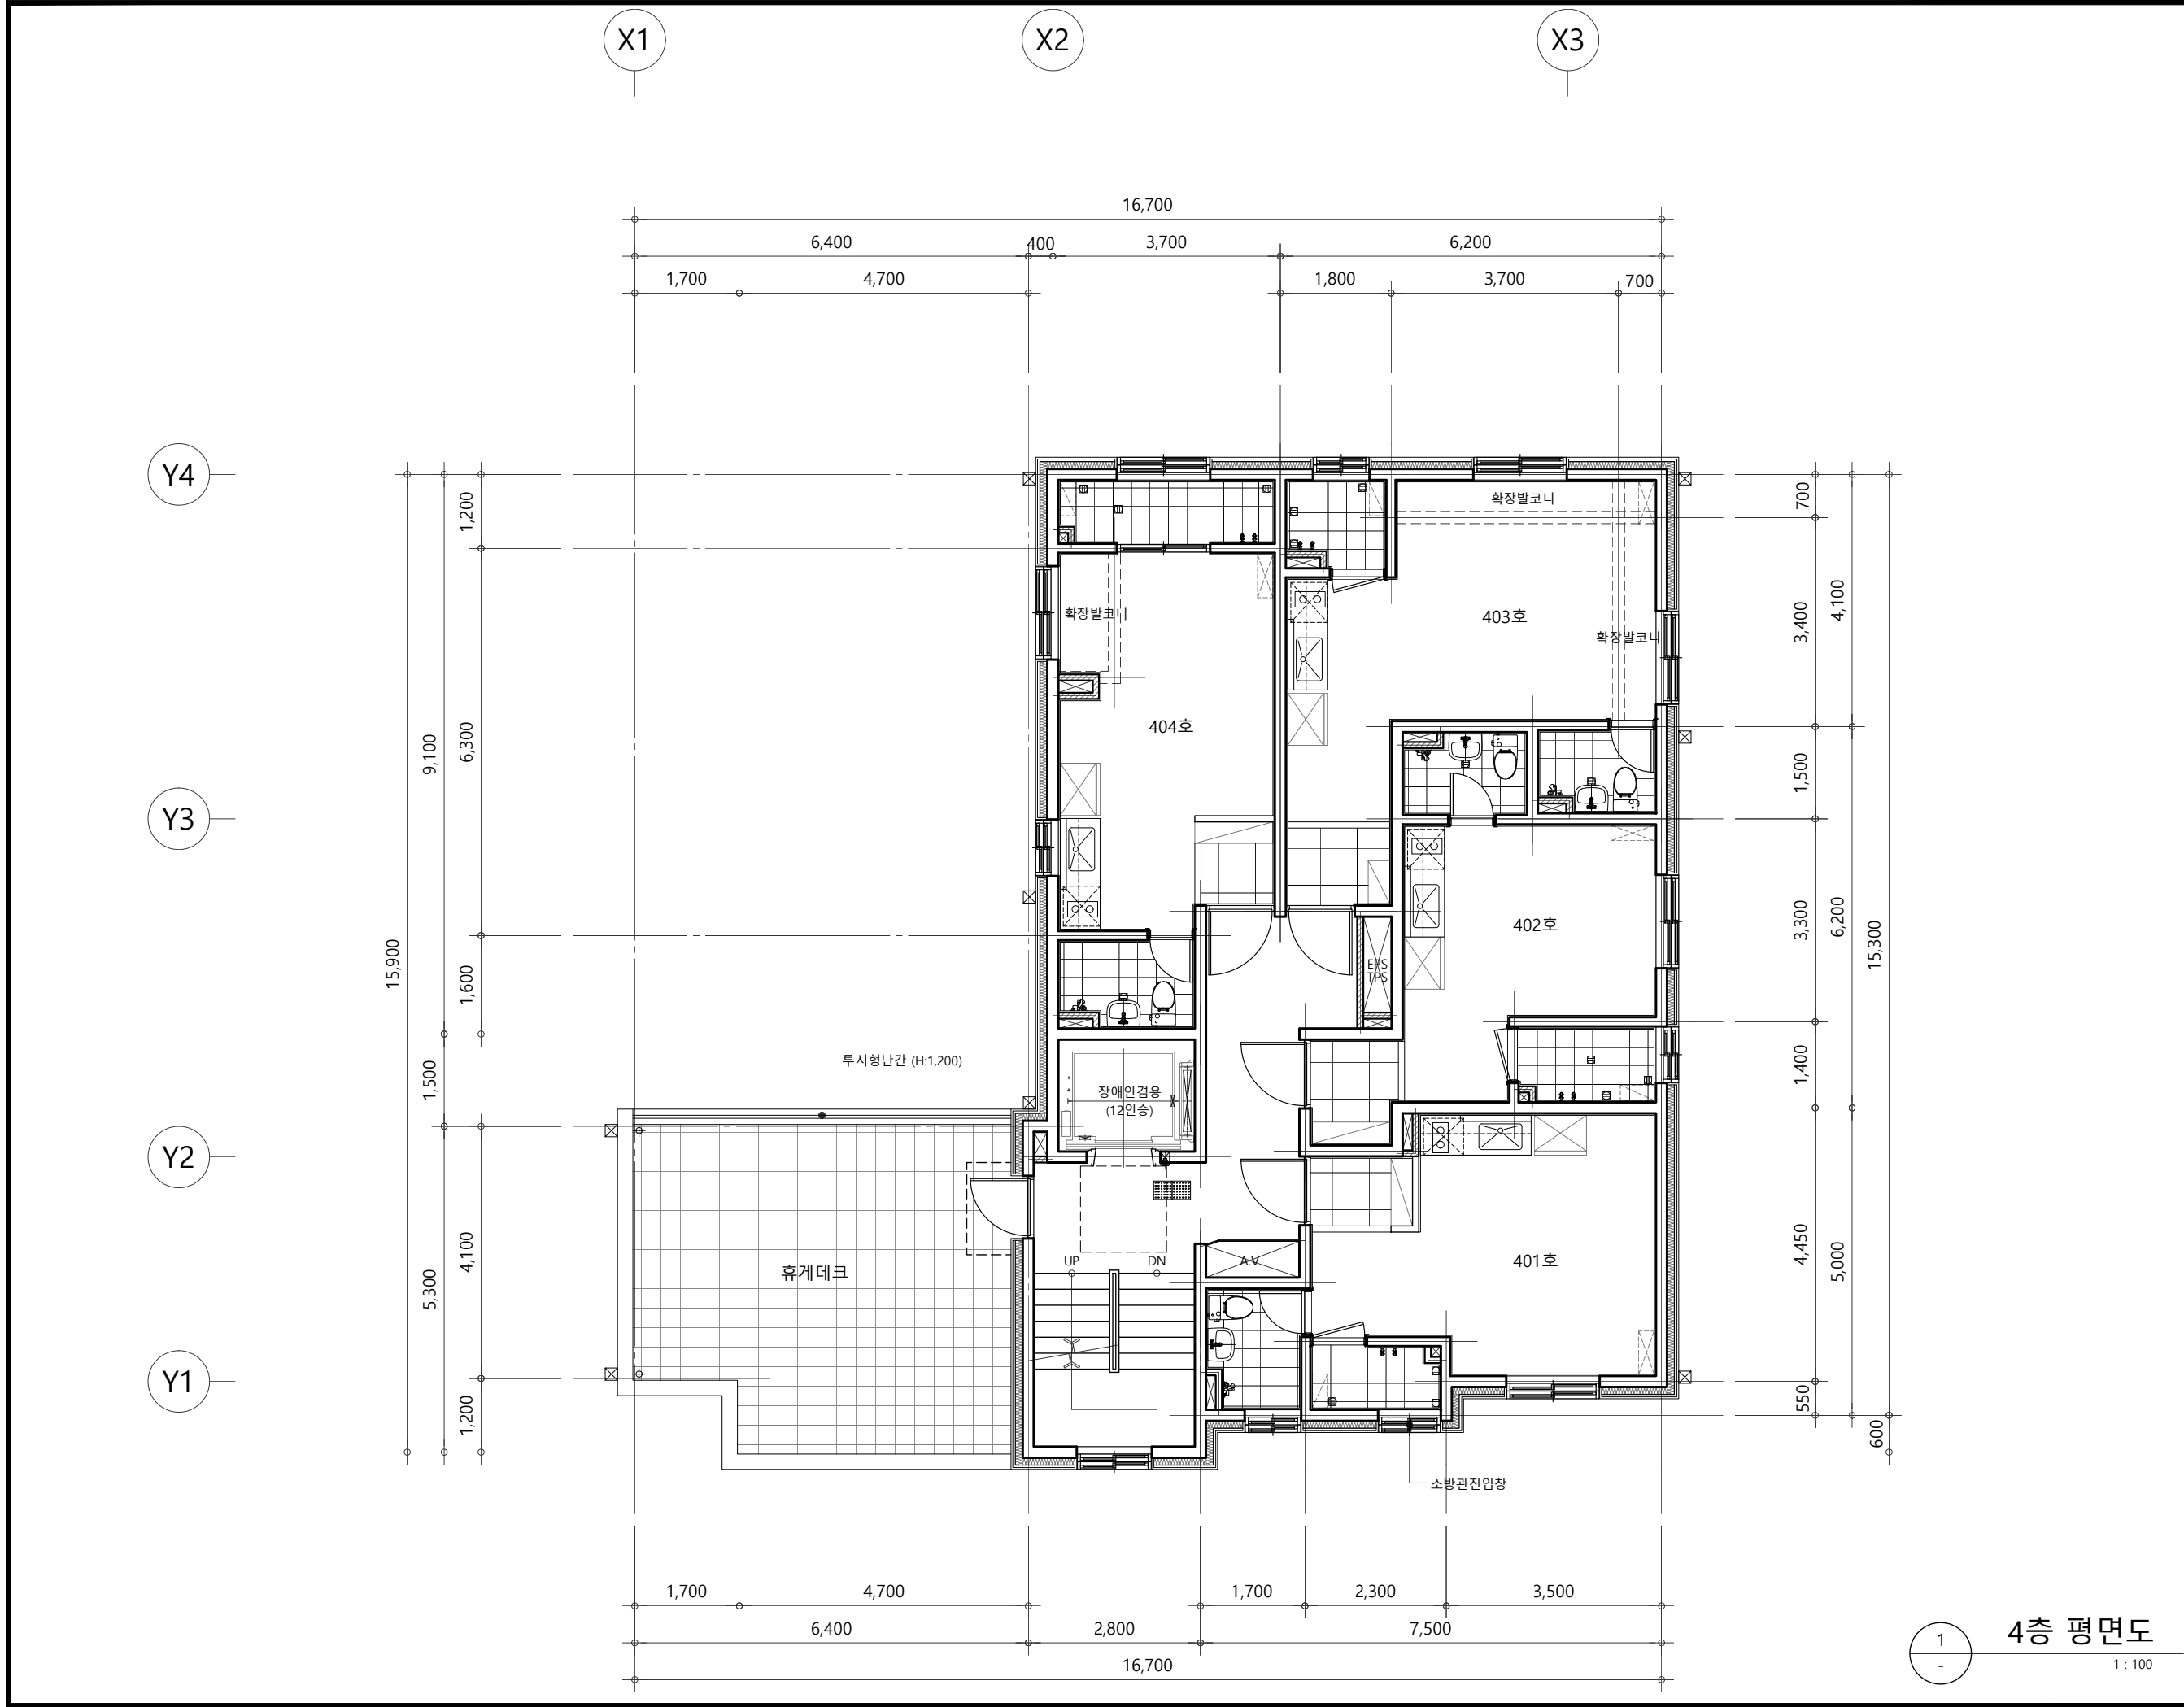


PROJECT TITLE			천호동 도시형생활주택 및 오피스텔 신축공사
KEY-MAP			
NOTES			
DESCRIPTION			
Rev.			Issue & Date
CONSULTANT			Check
ESIN ARCHITECTS			건축사사무소 이신
4F - #401 Wonil Bldg, 42, Cheonho-daero 170-gil, Gangdong-gu, Seoul, Korea 05381			
TEL 070. 7767. 1546 FAX 0504. 322. 1546			
E-MAIL esinarchi@gmail.com			
Drawing			4층 평면도
Scale			1 : 100
Drawn by			Checked by
Approved by			
Drawing number			A31 - 105
PROJECT CODE			ESIN2203-001

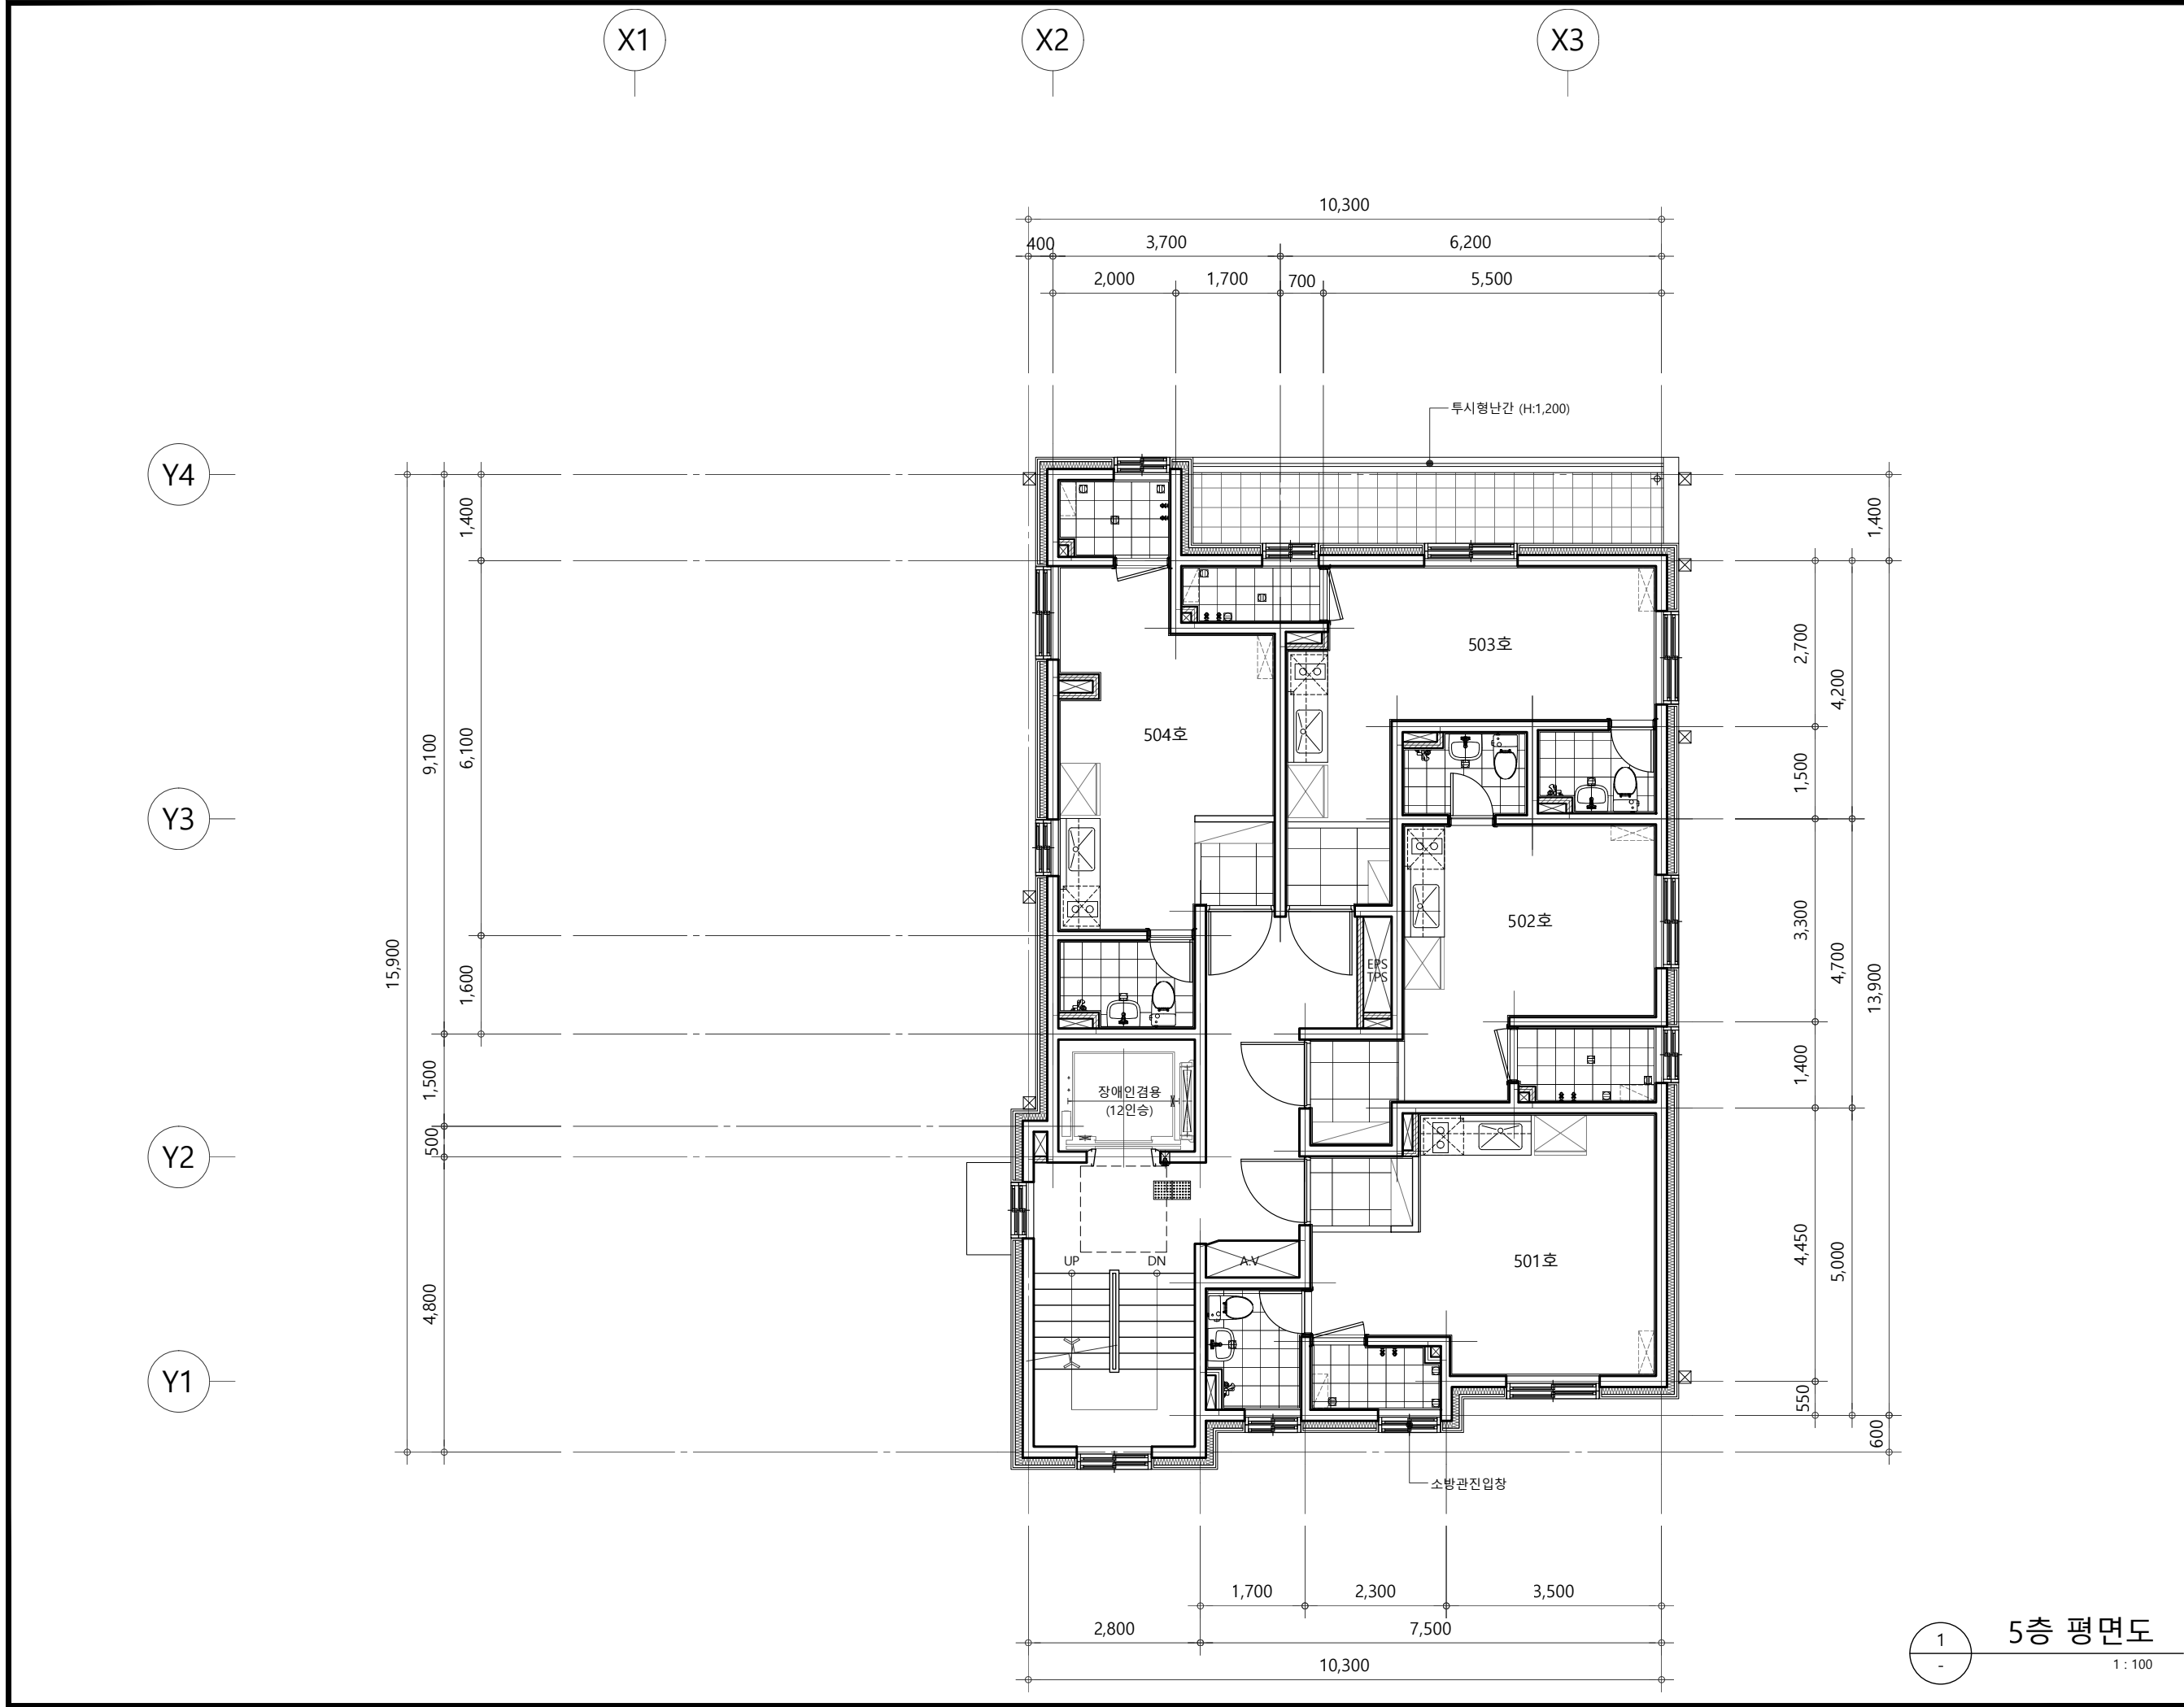


PROJECT TITLE			천호동 도시형생활주택 및 오피스텔 신축공사
KEY-MAP			
NOTES			
DESCRIPTION			
Rev.			Issue & Date
CONSULTANT			Check
ESIN ARCHITECTS			건축사사무소이신
4F - #401 Wonil Bldg, 42, Cheonho-daero 170-gil, Gangdong-gu, Seoul, Korea 05381			
TEL 070.7767.1546 FAX 0504.322.1546			
E-MAIL esinarchi@gmail.com			
Drawing			5층 평면도
Scale			1 : 100
Drawn by			Checked by
Approved by			
Drawing number			A31 - 106
PROJECT CODE			ESIN2203-001




PROJECT TITLE			천호동 도시형생활주택 및 오피스텔 신축공사
KEY-MAP			
NOTES			
DESCRIPTION			
Rev.			Issue & Date
CONSULTANT			Check
ESIN ARCHITECTS			건축사사무소이신
4F - #401 Wonil Bldg, 42, Cheonho-daero 170-gil, Gangdonggu, Seoul, Korea 05381			
TEL 070. 7767. 1546 FAX 0504. 322. 1546			
E-MAIL esinarchi@gmail.com			
Drawing			6층 평면도
Scale			1 : 100
Drawn by			Checked by
Approved by			
Drawing number			A31 - 107
PROJECT CODE			ESIN2203-001

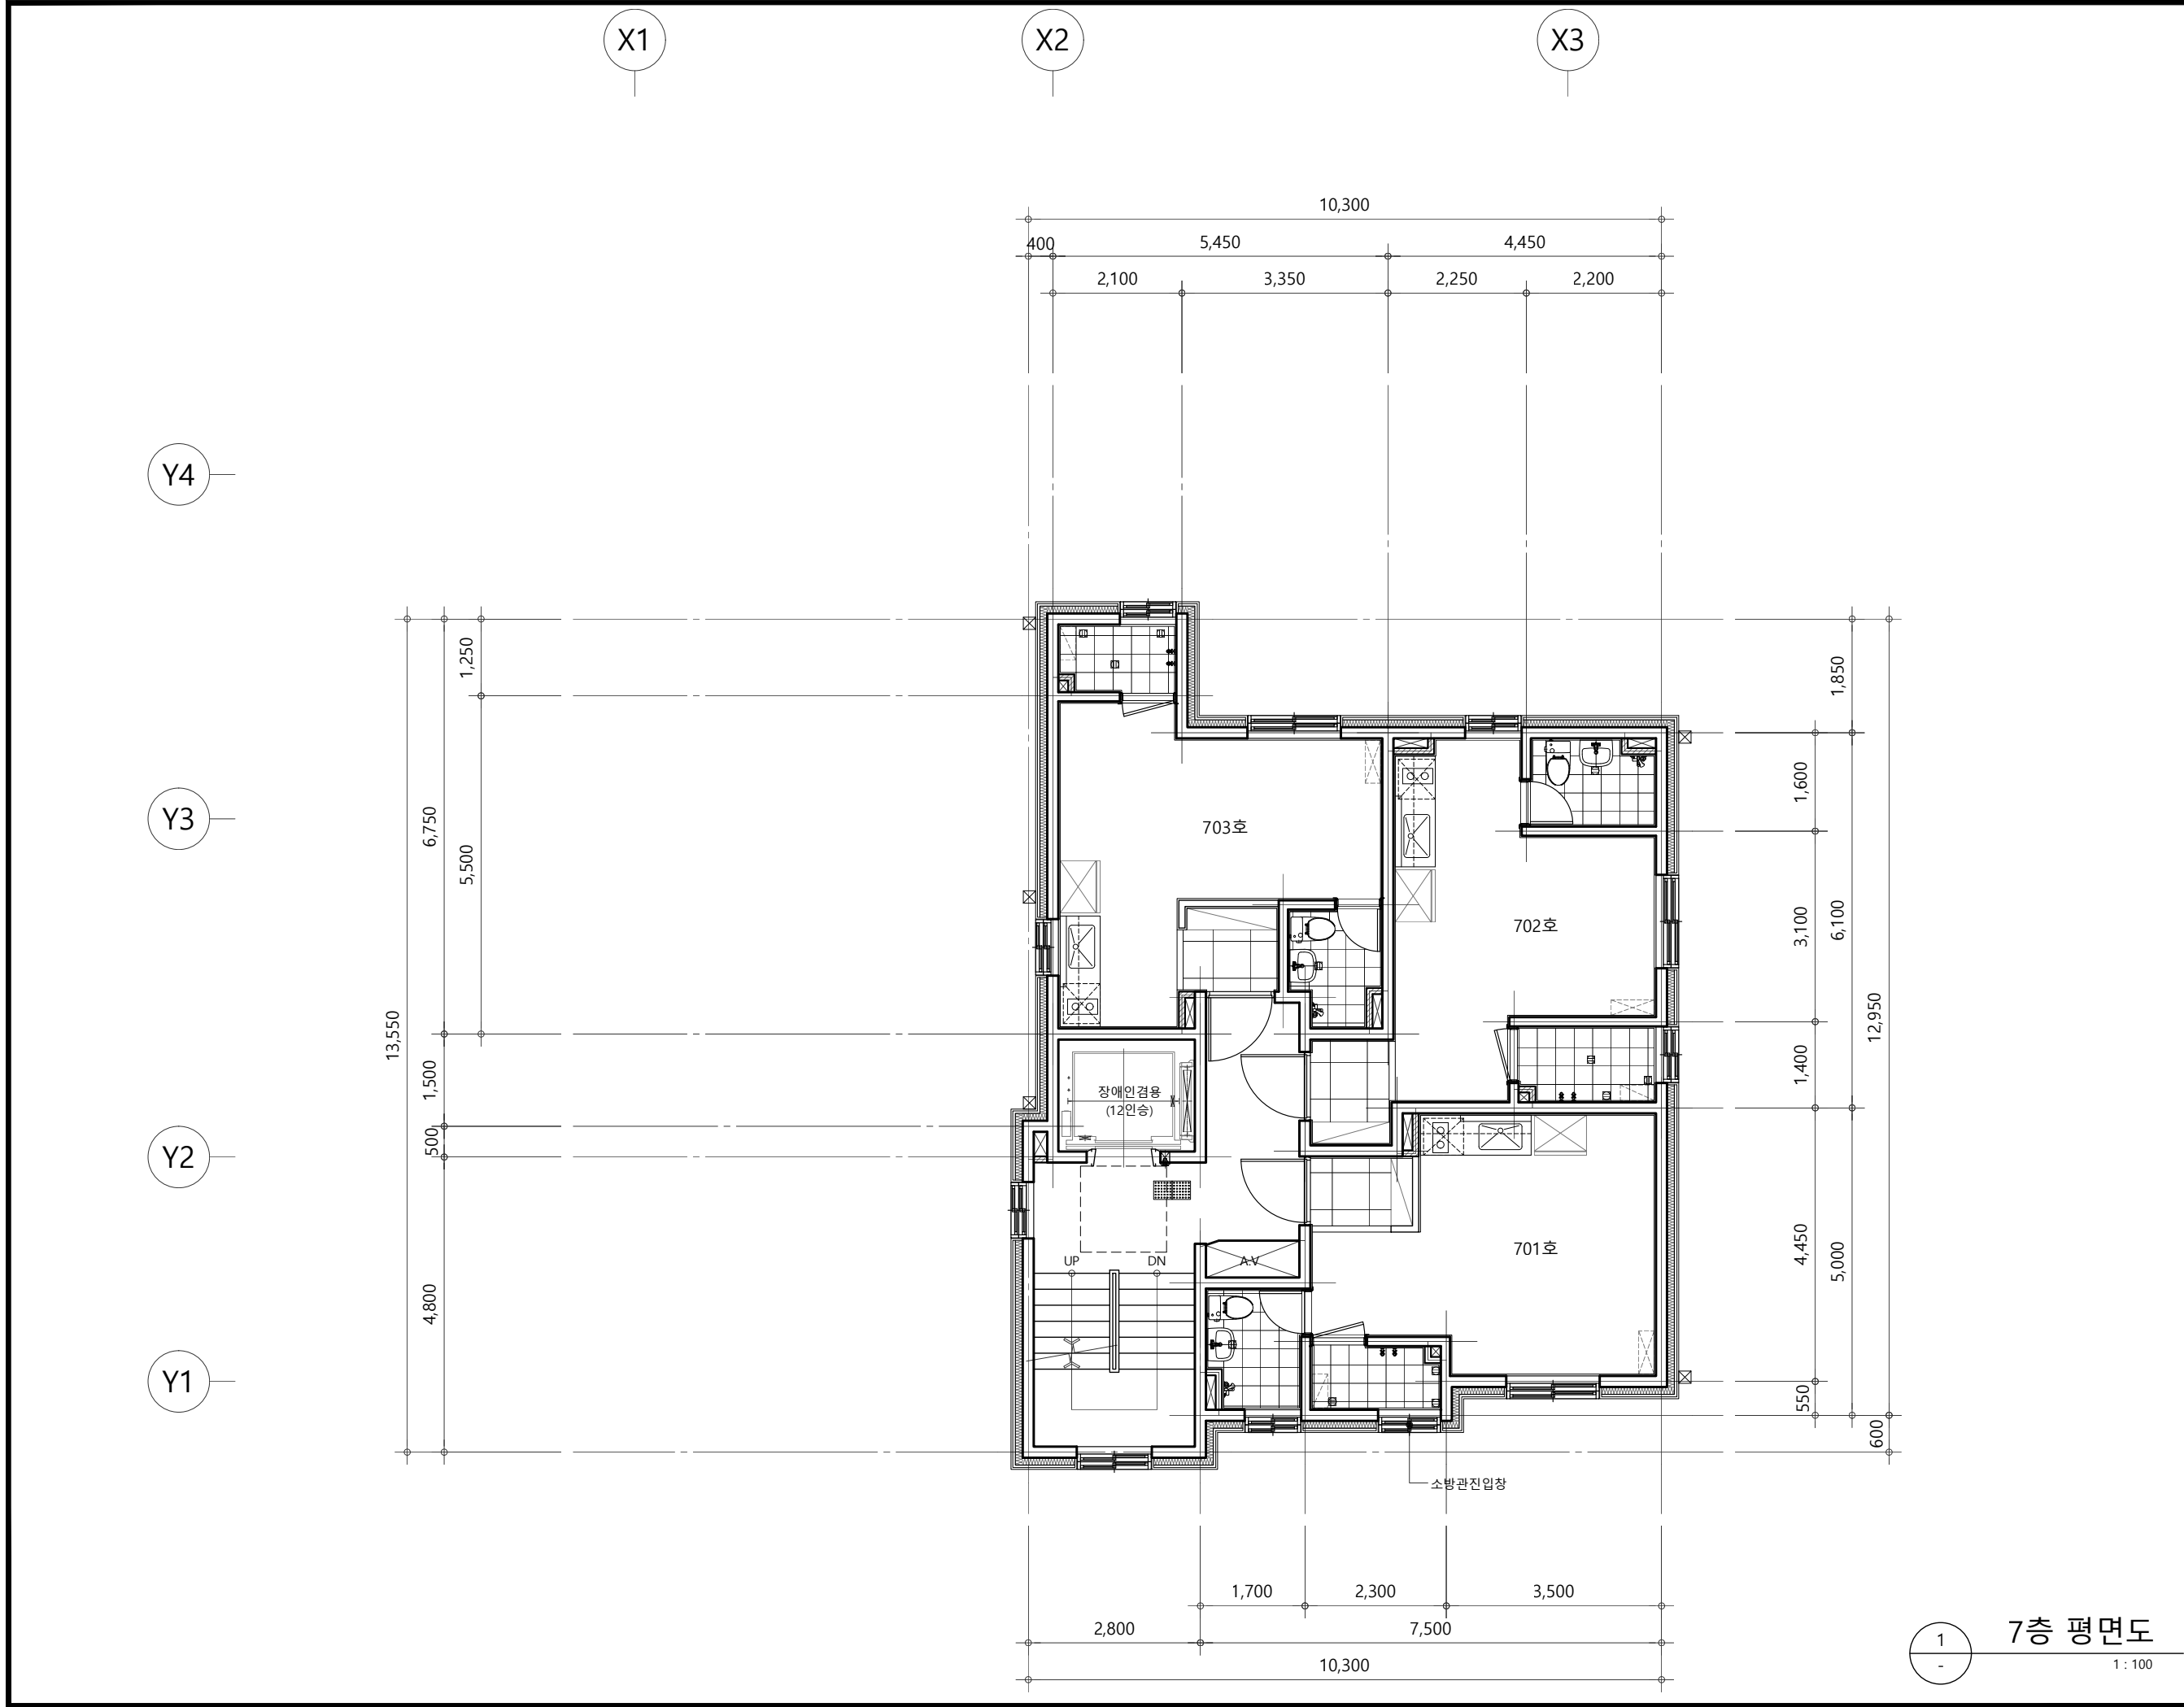

PROJECT TITLE			천호동 도시형생활주택 및 오피스텔 신축공사
KEY-MAP			
NOTES			
DESCRIPTION			
Rev.			Issue & Date
CONSULTANT			Check
ESIN ARCHITECTS			건축사사무소이신
4F - #401 Wonil Bldg, 42, Cheonho-daero 170-gil, Gangdonggu, Seoul, Korea 05381			
TEL 070. 7767. 1546 FAX 0504. 322. 1546			
E-MAIL esinarchi@gmail.com			
Drawing			7층 평면도
Scale			1 : 100
Drawn by			Checked by
Approved by			
Drawing number			A31 - 108
PROJECT CODE			ESIN2203-001

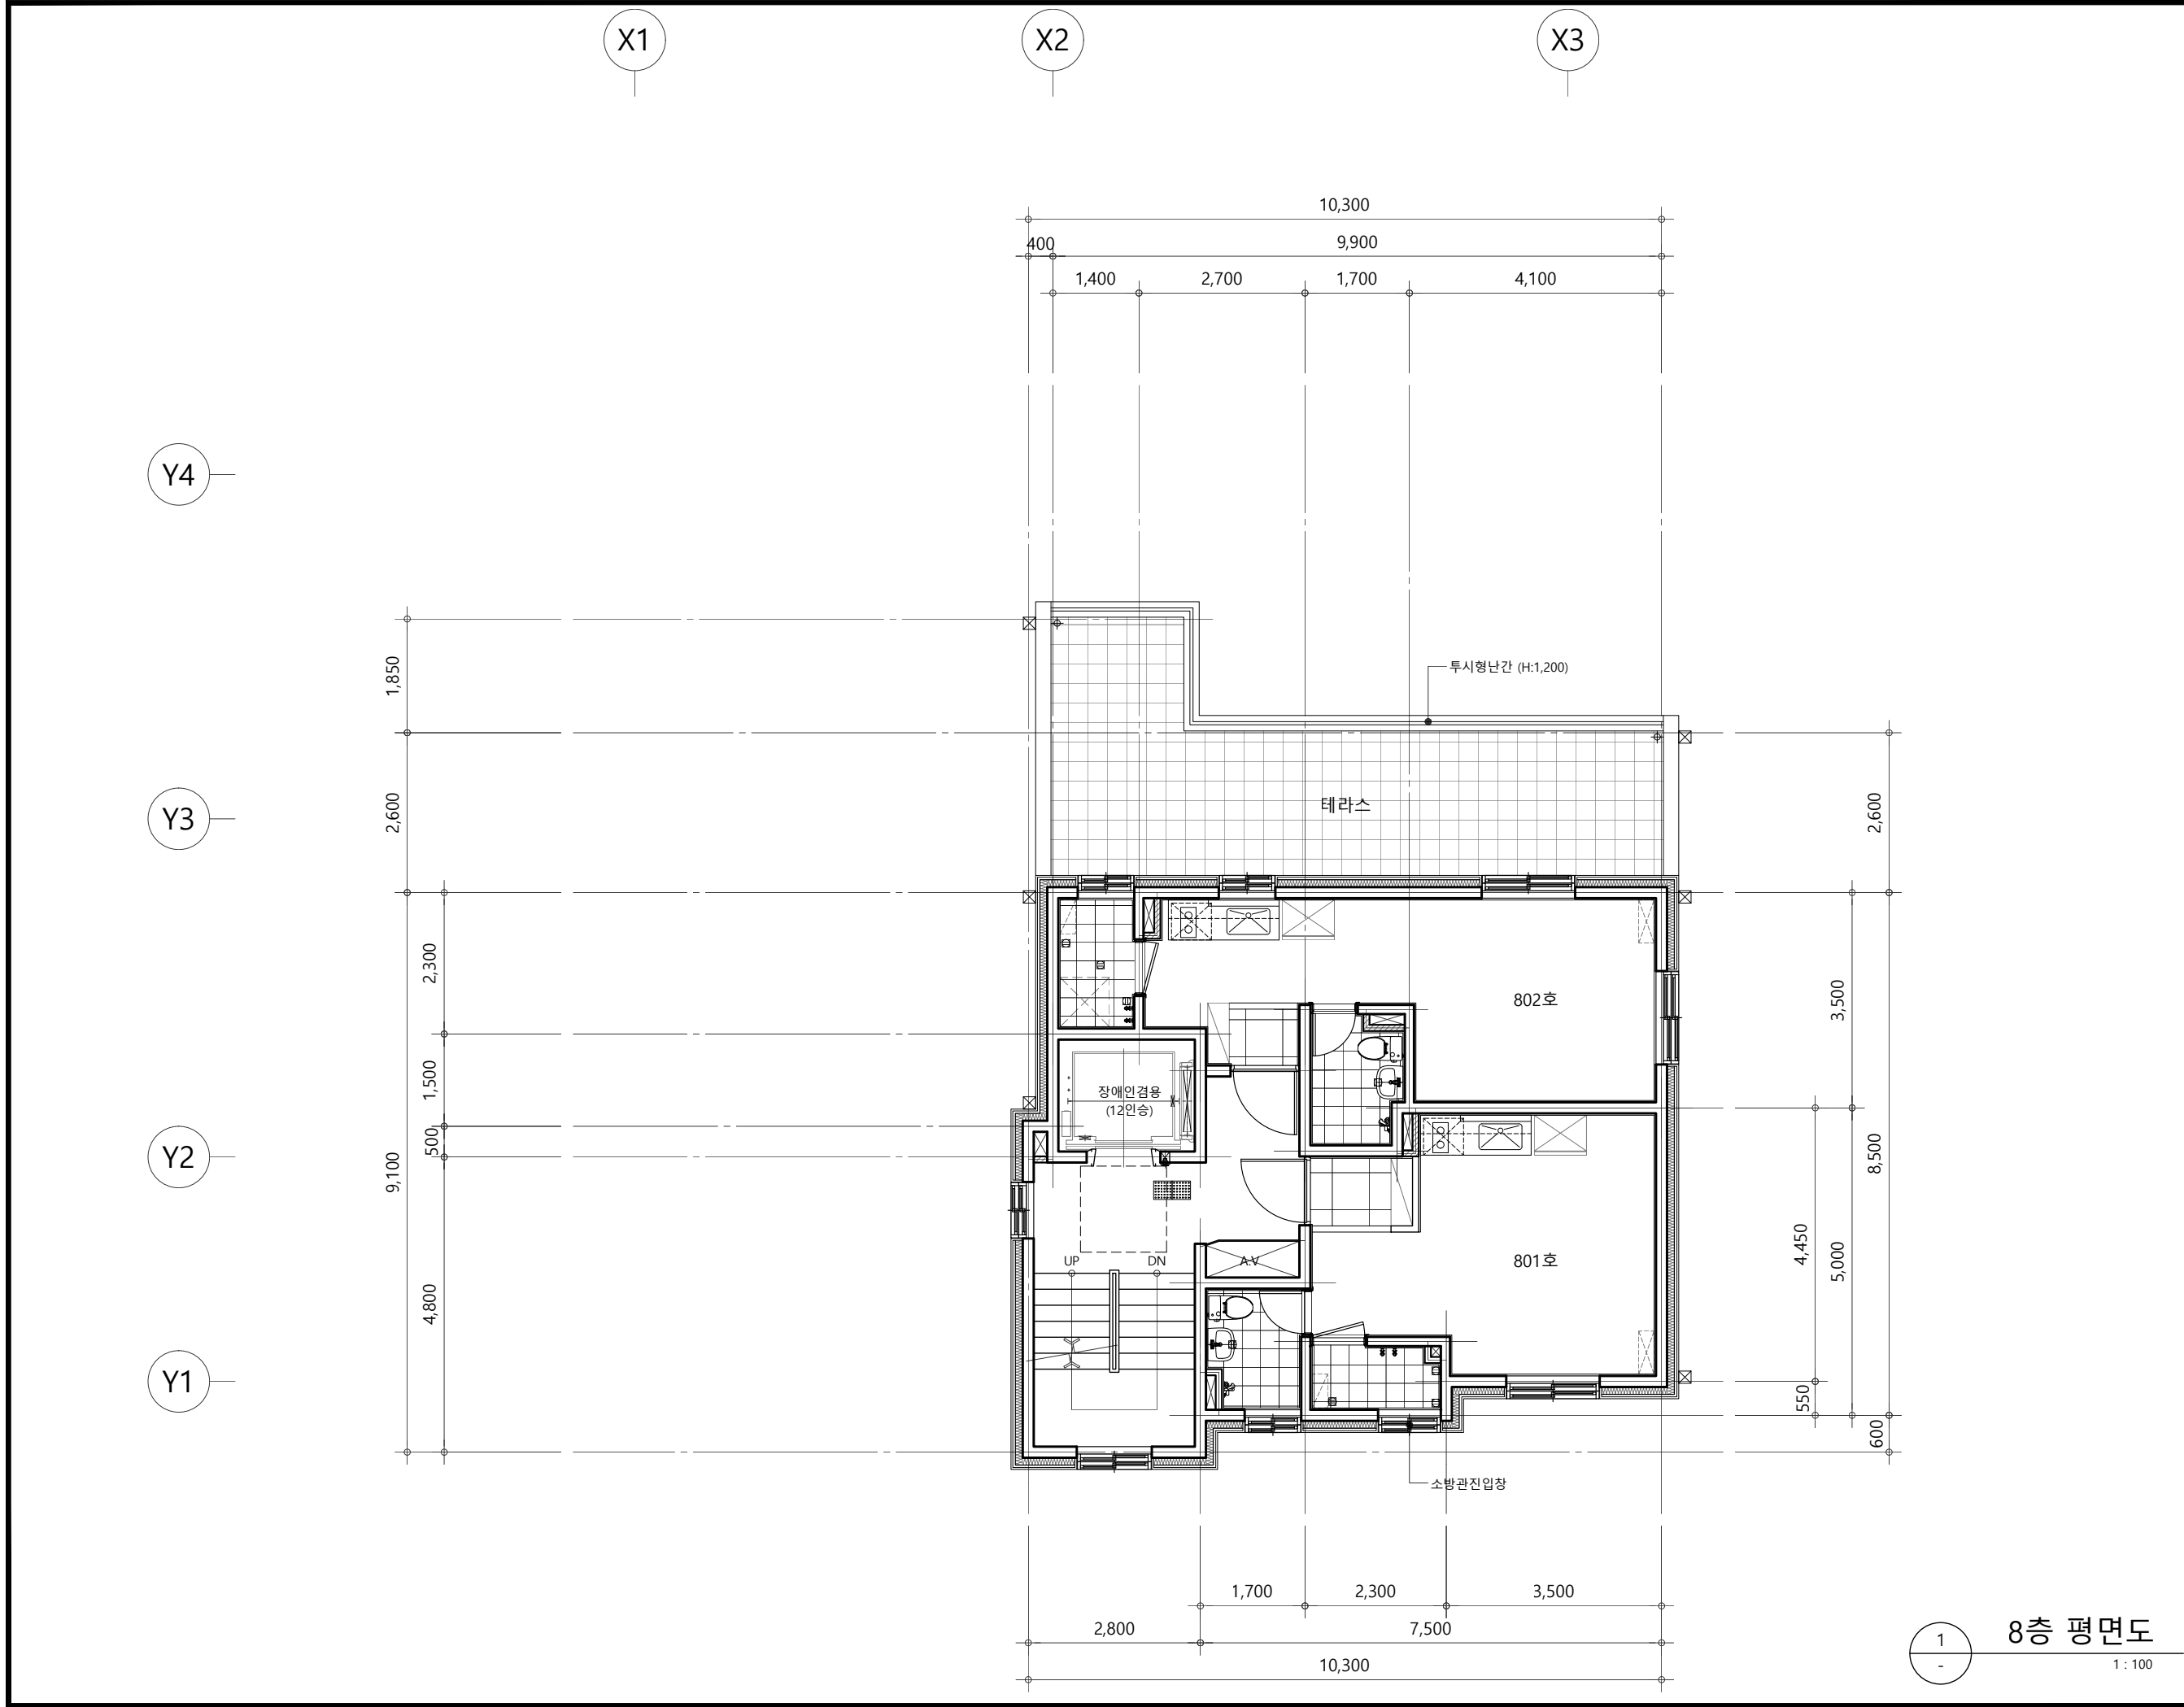

PROJECT TITLE			천호동 도시형생활주택 및 오피스텔 신축공사
KEY-MAP			
NOTES			
DESCRIPTION			
Rev.			Issue & Date
CONSULTANT			Check
ESIN ARCHITECTS			건축사사무소이신
4F - #401 Wonil Bldg, 42, Cheonho-daero 170-gil, Gangdong-gu, Seoul, Korea 05381			
TEL 070. 7767. 1546 FAX 0504. 322. 1546			
E-MAIL esinarchi@gmail.com			
Drawing			8층 평면도
Scale			1 : 100
Drawn by			Checked by
Approved by			
Drawing number			A31 - 109
PROJECT CODE			ESIN2203-001

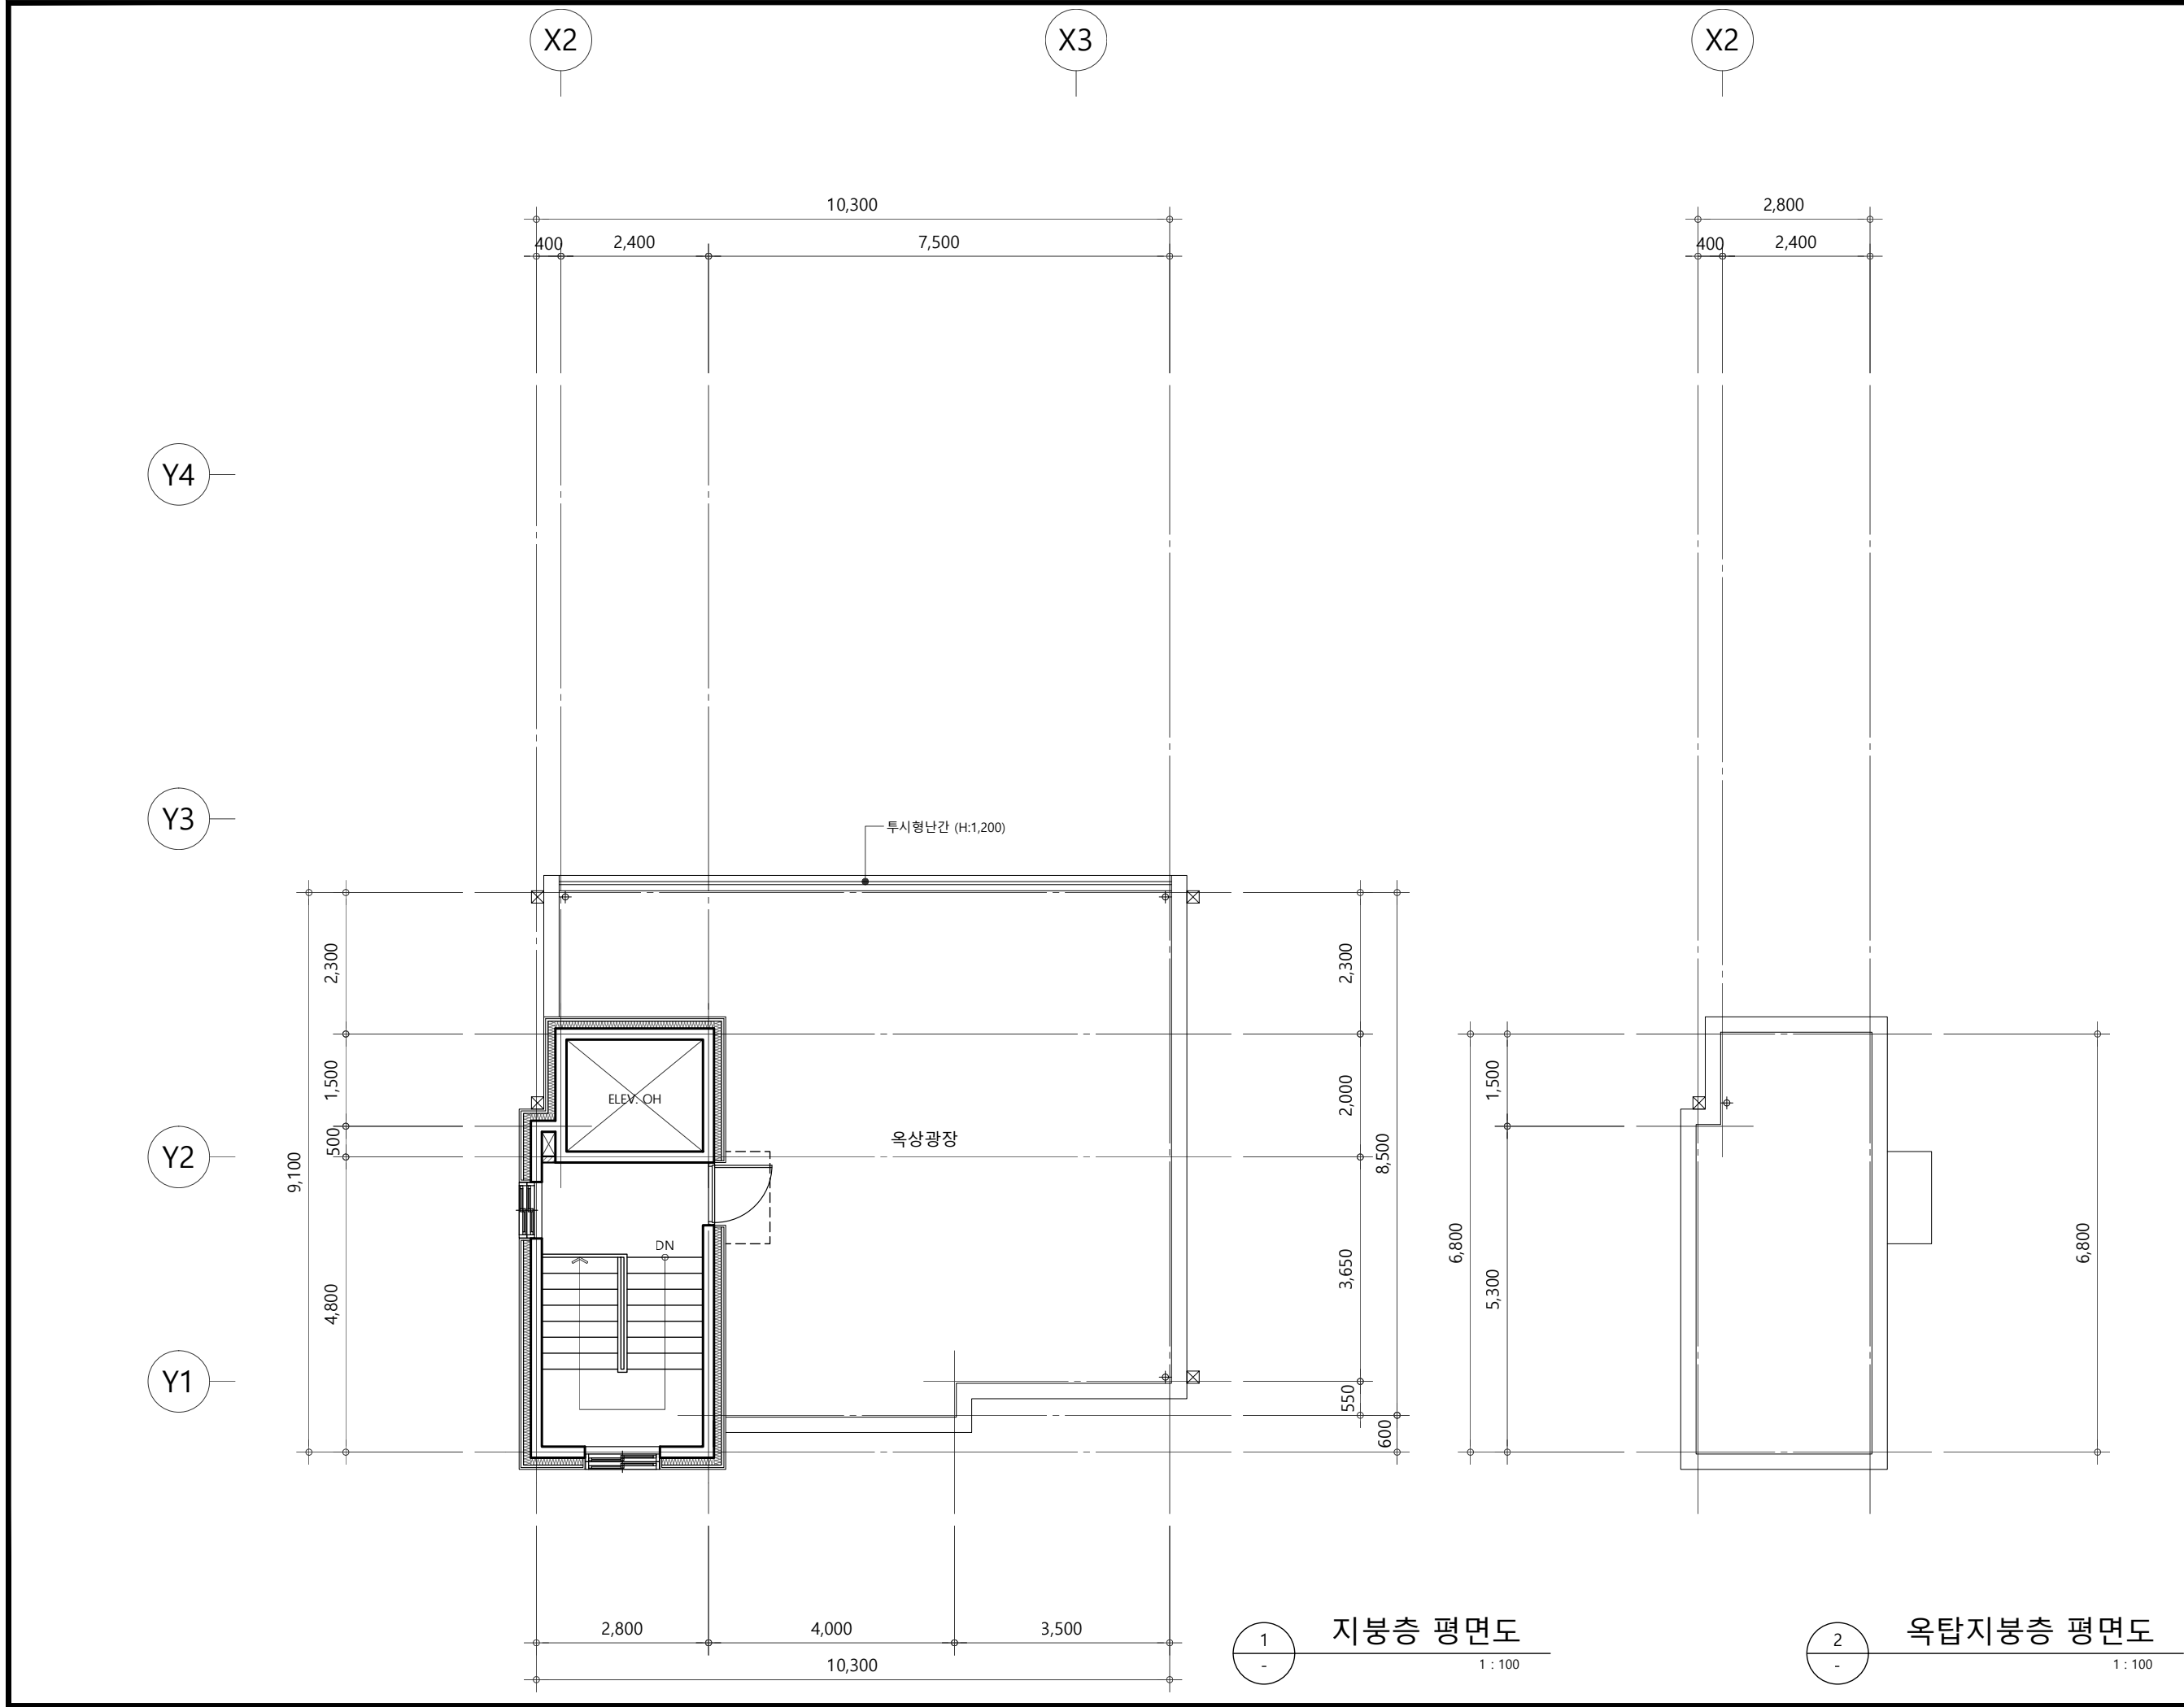


PROJECT TITLE			천호동 도시형생활주택 및 오피스텔 신축공사
KEY-MAP			
NOTES			
DESCRIPTION			
Rev.			Issue & Date
CONSULTANT			Check
ESIN ARCHITECTS			건축사사무소이신
4F - #401 Wonil Bldg, 42, Cheonho-daero 170-gil, Gangdong-gu, Seoul, Korea 05381			
TEL 070. 7767. 1546 FAX 0504. 322. 1546			
E-MAIL esinarchi@gmail.com			
Drawing			지붕층 평면도 옥탑지붕층 평면도
Scale			1 : 100
Drawn by			Checked by
Approved by			
Drawing number			A31 - 110
PROJECT CODE			ESIN2203-001

PROJECT TITLE

천호동
도시재생활동주택 및
오피스텔 신축공사

NOTES

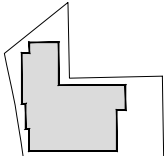

DESCRIPTION

Rev.	Issue & Date	Check
CONSULTANT		

ESIN ARCHITECTS
건축사사무소 이신
4F #401 Wonil Bldg. 42, Oryong-dong 170-gil,
Gangbyeong-gu, Seoul, Korea | 05381
TEL. 070-7767-1546 FAX 0504-322-1546
E-MAIL esinarch@gmail.com

Drawing

정면도

Scale 1 : 100

Drawn by Checked by


Approved by

Drawing number

PROJECT CODE

ESIN2203-001

Copy rights © 2022 ESIN ARCHITECTS. All rights reserved.

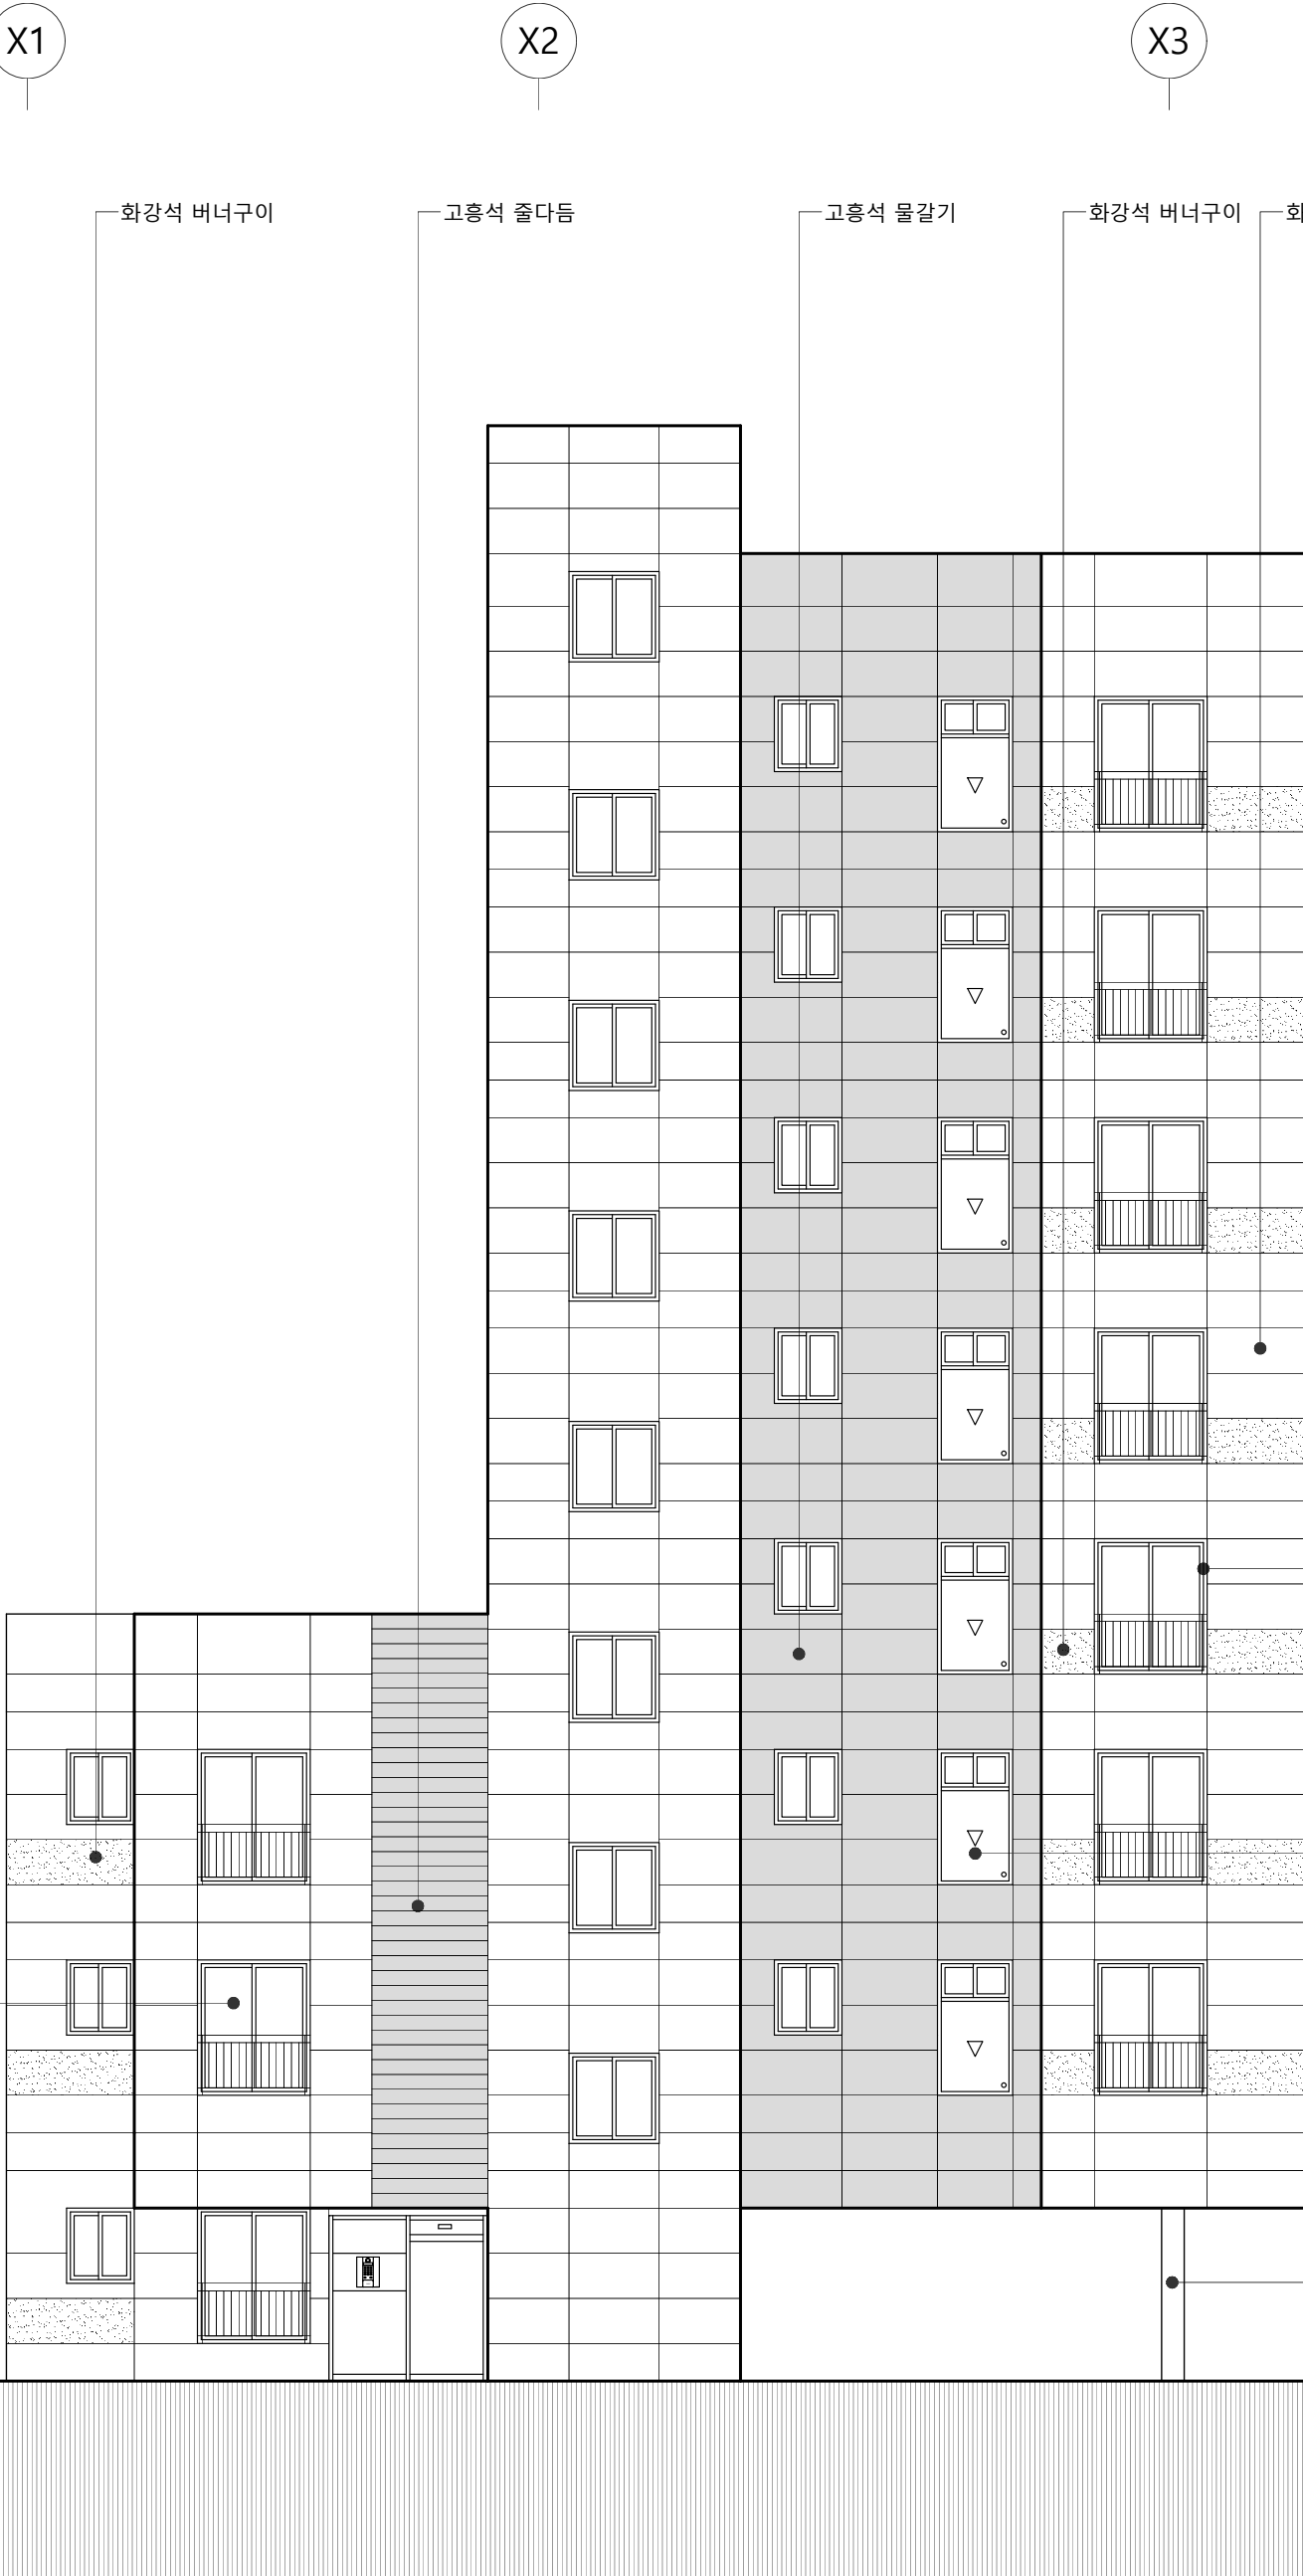

X1

X2

X3

▼ 옥탑지붕층
EL +25,800

▼ 지붕층
EL +23,100

▼ 지상8층
EL +20,200

▼ 지상7층
EL +17,400

▼ 지상6층
EL +14,600

▼ 지상5층
EL +11,800

▼ 지상4층
EL + 9,000

▼ 지상3층
EL +6,200

THK22 로이복층유리

▼ 지상2층
EL +3,400

▼ 지상1층
EL ±0 (G.L -100)


1
-

정면도
1 : 100

PROJECT TITLE

천호동
도시영생활주택 및
오피스텔 신축공사

KEYMAP

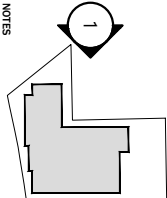

NOTES

DESCRIPTION

Rev.	Issue & Date	Check
CONSULTANT		

ESIN ARCHITECTS
건축사사무소 이진
4F #401 Wonil Bldg. 42, Oryong-dong 170-gil,
Gangdonggu, Seoul, Korea | 05381
TEL. 070-7767-1546 FAX 0504-322-1546
E-MAIL esinarch@gmail.com

Drawing

건축면도

Scale 1 : 100

Drawn by Checked by

Approved by

Drawing number

PROJECT CODE

ESIN2203-001

Copy rights © 2022 ESIN ARCHITECTS. All rights reserved.

1
-

건축면도
1 : 100

▼ 옥탑지붕층
EL +25,800

▼ 지붕층
EL +23,100

▼ 지상8층
EL +20,200

▼ 지상7층
EL +17,400

▼ 지상6층
EL +14,600

▼ 지상5층
EL +11,800

▼ 지상4층
EL + 9,000

▼ 지상3층
EL +6,200

▼ 지상2층
EL +3,400

▼ 지상1층
EL ±0 (G.L -100)

우수선희통

PVC창호(블랙)

THK22 로이복층유리

석재뿔칠

THK22 로이복층유리

화강석 물갈기

THK22 로이복층유리

화강석 물갈기

화강석 버너구이

Y1

Y2

Y3

Y4

화강석 물갈기

화강석 버너구이

고흥석 물갈기

▼ 옥탑지붕층
EL +25,800

▼ 지붕층
EL +23,100

▼ 지상8층
EL +20,200

▼ 지상7층
EL +17,400

▼ 지상6층
EL +14,600

▼ 지상5층
EL +11,800

▼ 지상4층
EL + 9,000

▼ 지상3층
EL +6,200

▼ 지상2층
EL +3,400

▼ 지상1층
EL ±0 (G.L -100)

투시형난간

우수선흡통


석재뿔칠

PVC창호(블랙)

THK22 로이복층유리

1
-

우측면도
1 : 100

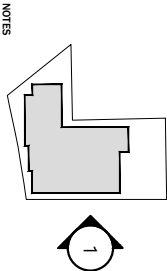

NOTES

전호동
도시영생활주택 및
오피스텔 신축공사

KEYMAP

DESCRIPTION

Rev.	Issue & Date	Check
CONSULTANT		

ESIN ARCHITECTS
건축사사무소 이진
4F #401 Wonil Bldg. 42, Oryong-dong 170-gil,
Gangdong-gu, Seoul, Korea | 05381
TEL. 070-7767-1546 FAX 0504-322-1546
E-MAIL esinarch@gmail.com

Drawing

우측면도

Scale
1 : 100

Drawn by
Checked by

Approved by

Drawing number

PROJECT CODE


ESIN2203-001

Copy rights © 2022 ESIN ARCHITECTS. All rights reserved.

PROJECT TITLE

천호동
도시재생활동주택 및
오피스텔 신축공사

KEY MAP

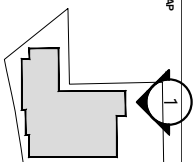

NOTES

DESCRIPTION

Rev.	Issue & Date	Check
CONSULTANT		

ESIN ARCHITECTS
건축사사무소 이진
4F #401 Wonil Bldg. 42, Orehob-danro 170-gil,
Gangdonggu, Seoul, Korea | 05381
TEL. 070-7767-1546 FAX 0504-322-1546
E-MAIL esinarch@gmail.com

Drawing

배면도

Scale

1 : 100

Drawn by

Checked by

Approved by

Drawing number

A32 - 004

PROJECT CODE

ESIN2203-001

Copy rights © 2022 ESIN ARCHITECTS. All rights reserved.

1
-

배면도

1 : 100

X3

X2

X1

고흥석 물갈기

투시형난간

화강석 버너구이

화강석 물갈기

▼ 옥탑지붕층
EL +25,800

▼ 지붕층
EL +23,100

▼ 지상8층
EL +20,200

▼ 지상7층
EL +17,400

▼ 지상6층
EL +14,600

▼ 지상5층
EL +11,800

PVC창호(블랙)

▼ 지상4층
EL + 9,000

THK22 로이복층유리

▼ 지상3층
EL +6,200

▼ 지상2층
EL +3,400

석재뿔칠

▼ 지상1층
EL ±0 (G.L -100)