

1. 조감도



2. 건축개요 및 현황도

■ 건축개요

- 설 계 명 : 강동구 길동 349-9 도시형생활주택 (원룸형-청년주택) 신축공사
- 대 지 위 치 : 서울특별시 강동구 길동 349-9
- 지 역 지 구 : 제3종일반주거지역
- 건 물 용 도 : 도시형생활주택 원룸형(다세대)
- 건 물 규 모 : 지상5층
- 대 지 면 적 : 248.00m²
- 건 축 면 적 : 123.84m²
- 연 면 적 : 512.70m²
- 건 폐 율 : 50%(법정) / 49.94%
- 용 적 율 : 250.00%(법정) / 206.73%
- 최 고 높 이 : 14.40m
- 건 물 구 조 : 철근콘크리트구조
- 주 차 대 수 : 전용면적 30m² 미만 0.4대 / 원룸형 세대당 0.5대 (법정)
5.9대 / 자주식 6대
- 조 경 면 적 : 12.40m² 이상 5%(법정)




■ 위치도




■ 주변현황도

3. 입면도

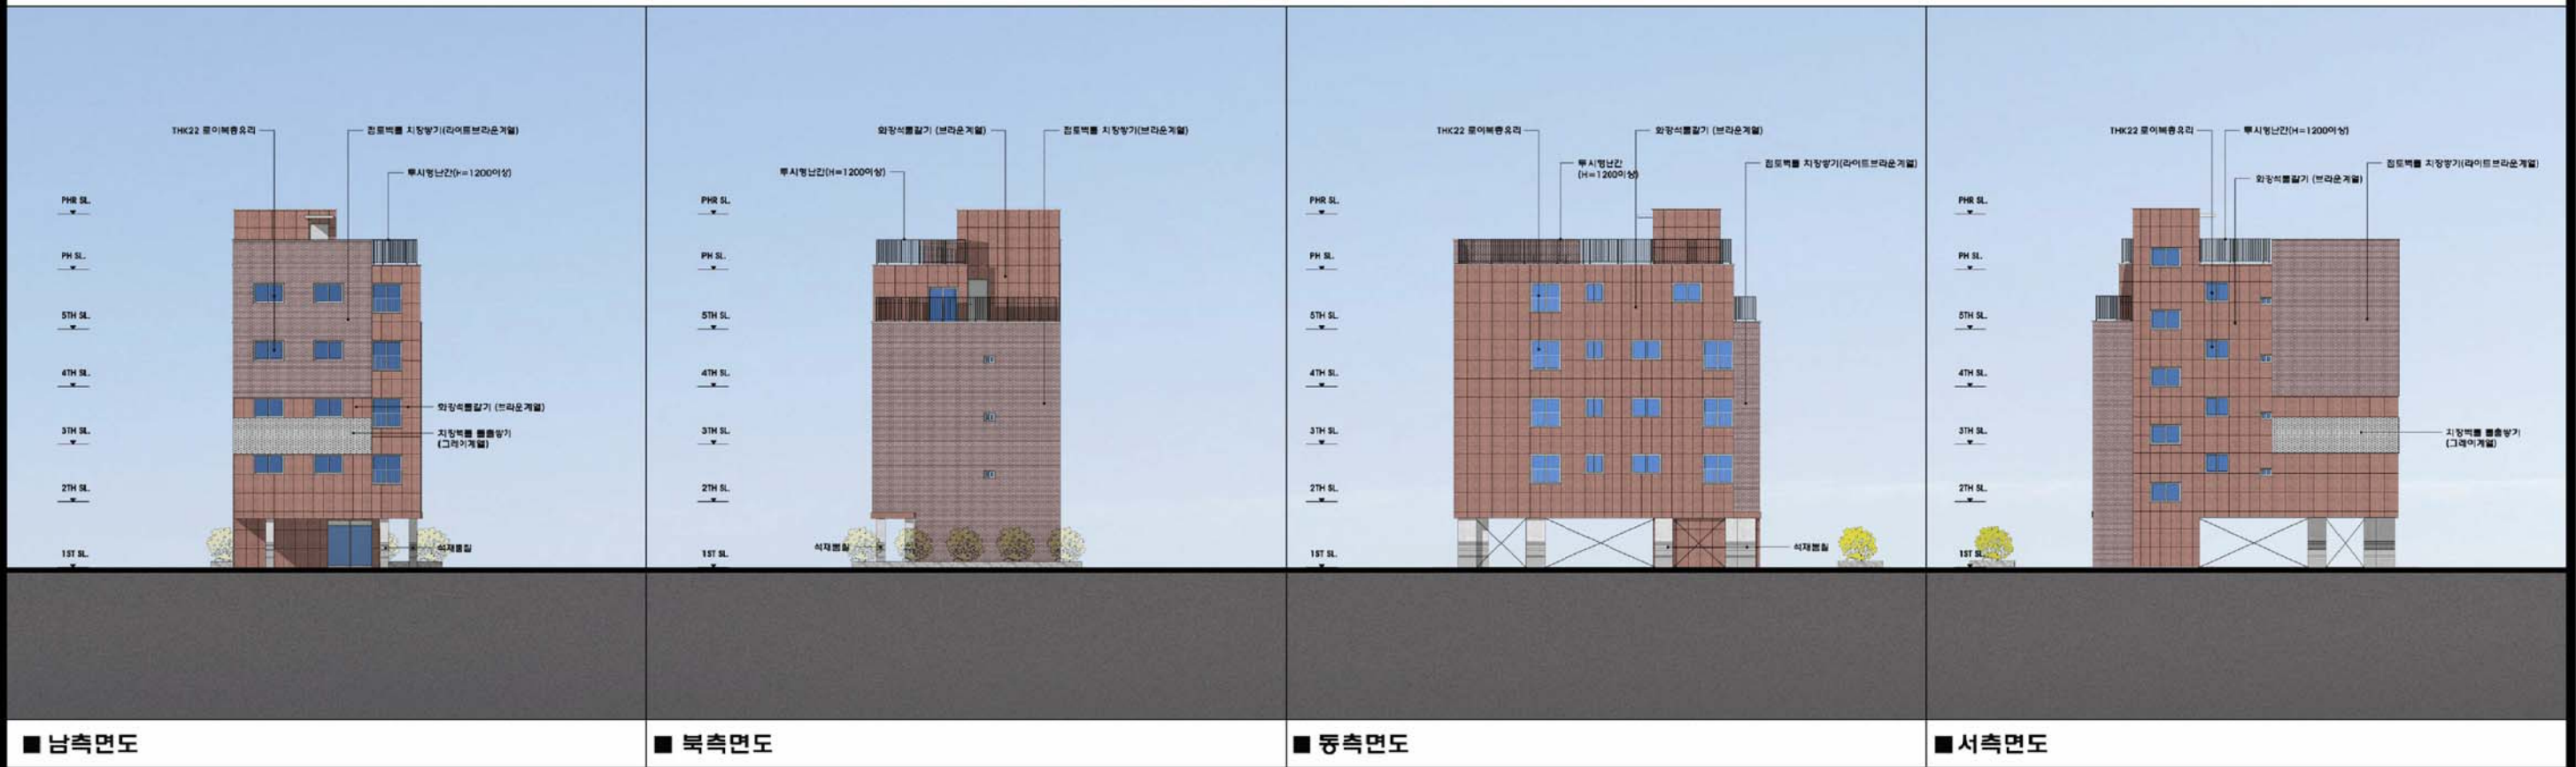

본 상기도면은 디자인심의회 제출된 심의도면이며 설계도면과 일부 상이한 참조용이며 설계도면이 우선함

4. 설계자 의도

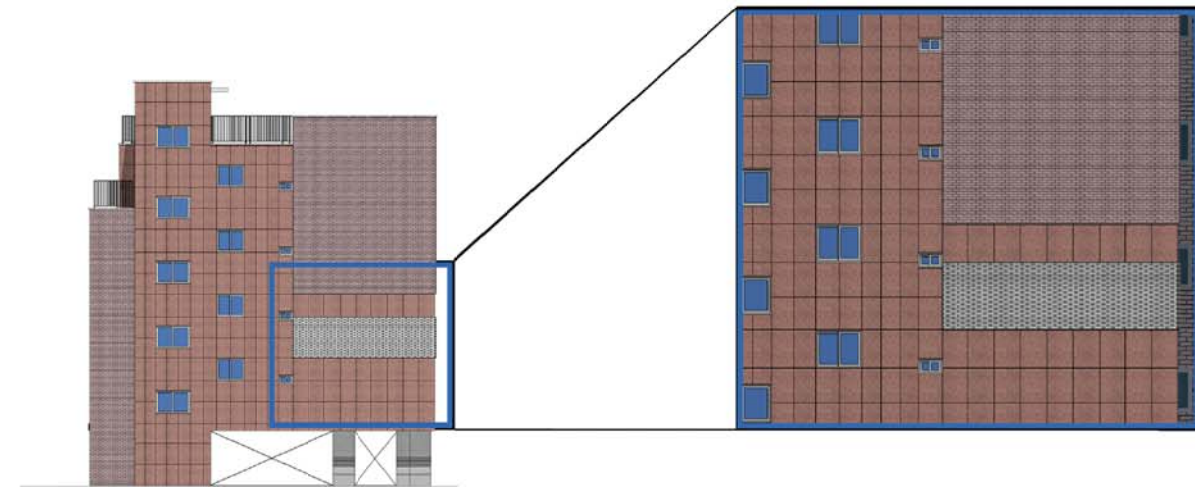



- Ⓐ 화강석물갈기 ± 0
- Ⓑ 점토벽돌 치장쌓기 ± 30
- Ⓒ 치장벽돌 돌출쌓기 ± 30

- Ⓐ 브라운계열의 화강석물갈기 기본외장재로 사용하고 점토벽돌쌓기로 변화를 주어 시각적 다양성을 주고 MASS감을 향상시킨 디자인
- Ⓑ 점토벽돌 돌출쌓기는 DESIGN POINT ITEM으로 색상의 변화와 질감의 변화를 함께 사용하여 시각성을 높이고 건물의 인지성을 향상

기본 외장재 점토벽돌(브라운 계열) 치장쌓기 위주 / 화강석물갈기 (브라운계열) 시공

5. 재료계획

1. 점토벽돌_주변도시 경관과 이질감이 적고 세련된 재료

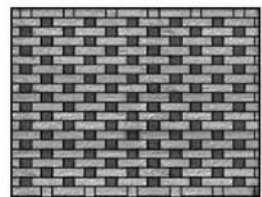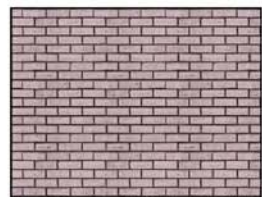

외장재-점토벽돌 치장쌓기 (라이트 브라운계열) 외장재 - 점토벽돌 돌출쌓기 (다크그레이계열)

2. 석재_시선의 흐름과 인지성을 고려한 재료



외장재-화강석물갈기(브라운계열)

3. 기둥_안정감이 느껴지는 색상의 재료



외장재-석재붙칠마감


■ 외장재

구분	실명	재료명
1층	피로티 주차장	바닥 : THK100칼라무늬 CON' C 천정 : AL천장재
2~5층	현관	폴리싱타일
	방	바닥 : 데코타일 무늬목 마감 벽 : 진완경실크벽지 천정 : 진완경천정재
	거실	바닥 : 데코타일 무늬목 마감 벽 : 진완경실크벽지 천정 : 진완경천정재
	계단실	바닥 : THK30 화강석 물갈기 벽 : 다채무늬도로


■ 내장재

6. 색채계획

주조색 / 보조색 / 강조색

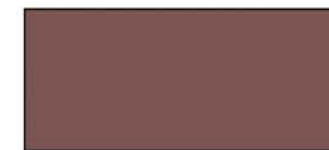

BROWN

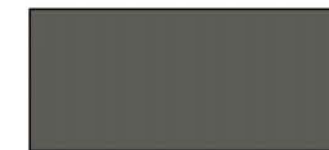

DARK GREY





GREY



- 브라운계열의 기본색상과 그레이계열의 대비색을 사용하여 조화로운 이미지를 부각시킨 무난하고 편안한 디자인 연출

본 상기도면은 디자인심의회 제출된 심의도면이며 설계도면과 일부 상이한 참조용이며 설계도면이 우선함

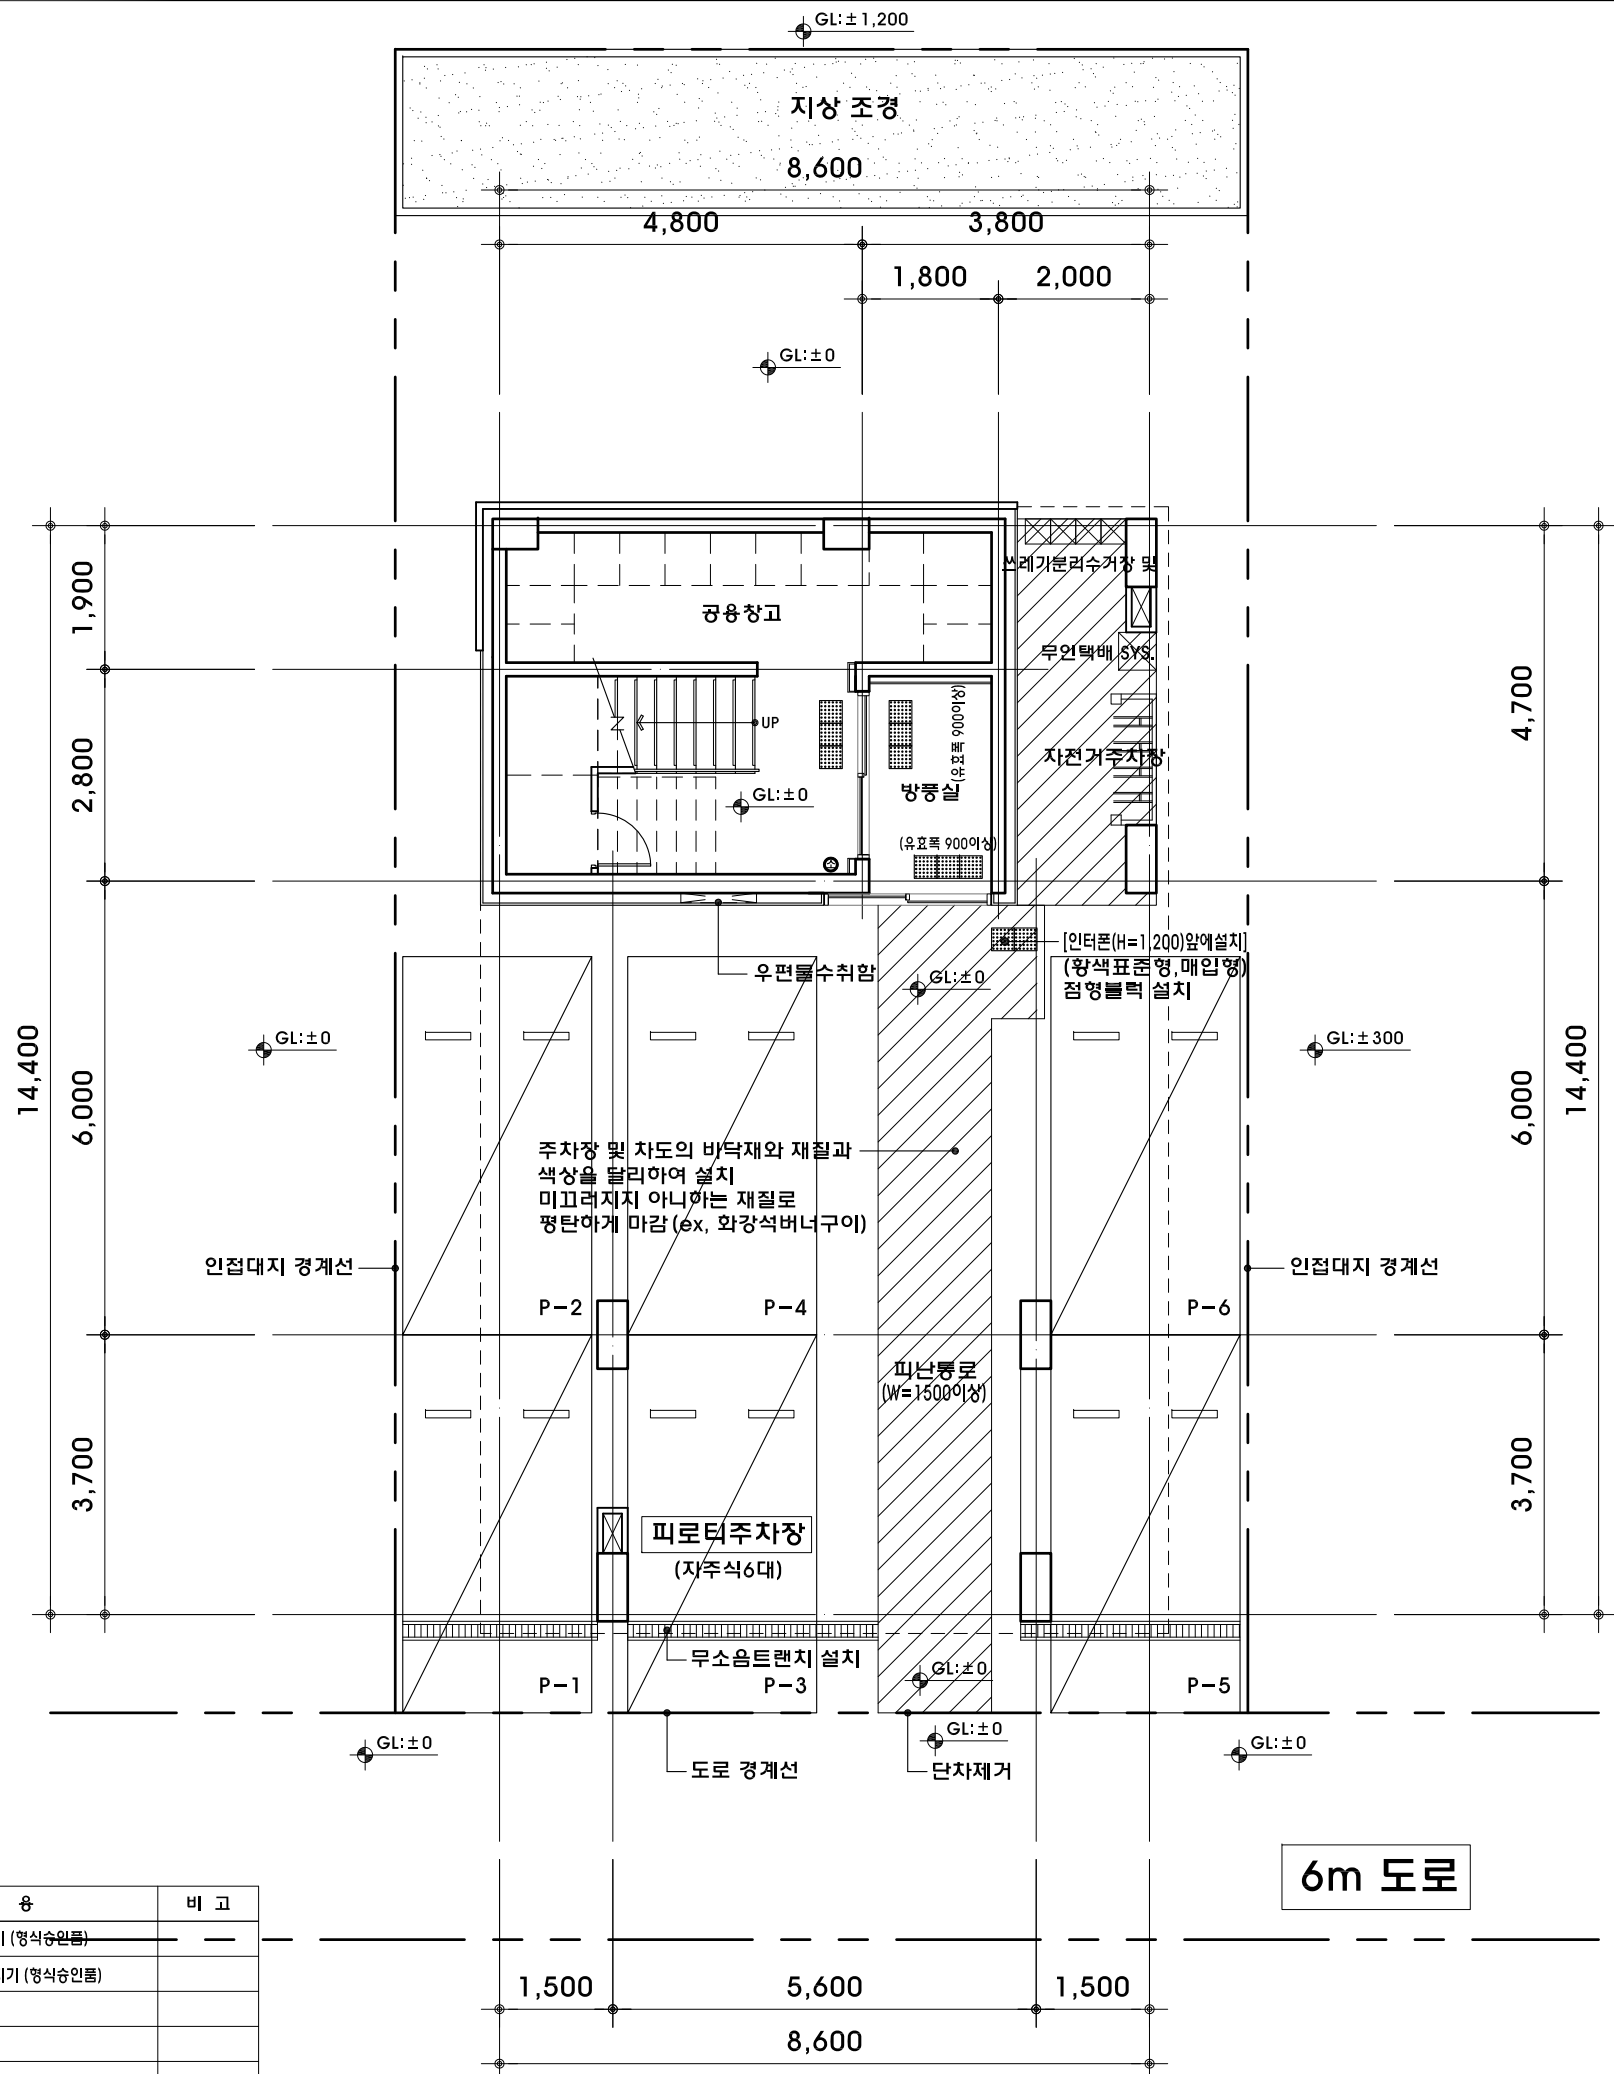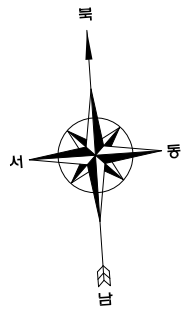


* 주 기 *		
상 표	내 용	비 고
	열식 단독경보형 감지기 (형식승인품)	
	연기식 단독경보형 감지기 (형식승인품)	
	ABC 분말 소화기	
	차면시설	
	소방관 진입창	



■ 주 기

건 축	1	주차장내 CCTV,쓰레기분리수거,자전거보관대 설치
		우편함 설치 (세대전용, 공용, 반송용, 폐건전지함 구분 설치)
		우편함 규격은 현장 여건에 맞추어 25x16x32 or 32x25x16
		이상으로 하고 세대전용,공용,반송용,폐건전지함으로 구분 설치한다.
	(외부)	세대 테라스 설치시 세대간 분리벽 계획
		세대 발코니 설치시 차양시설 설치
	2 (계단실)	세대 현관문 도어체크 및 스토퍼 설치
		계단참의 현관과 계단 이격거리 (최소600mm이상)
	3 (내부)	세대내 욕실, 휴지걸이 매립형 설치
		불박이 가구 내부 다용도 수납가능토록 수평 이동 칸막이 설치
구 조	4 (시공)	에어컨 실외기 설치위치 및 에어컨 콘센트 도면 표기 ☹ - 에어컨 콘센트 표기
		거실-스탠드형, 침실-벽걸이형
		콘크리트 폴타이 제거 후 마감공사 시공 (방수, 단열재 시공 등)
		욕실 & 다용도실 스위치 : 문 열리는 방향으로 시공
	5 (마감)	주차장 차량 진출입구간,화장실 무소음트랜치 시공
		-직접외기(외벽)에 면한 실내벽면 단열재
		[아이소핑크(10mm) + 석고보드 마감도면 표기]
		-간접외기(계단실,복도)에 면한 실내벽면 단열재
	1	[경질우레탄보드(80mm) + 석고보드 마감도면 표기]
		*기타 실내 벽면 시멘트 미장 마감
전 기	2	철근 : fy=400Mpa
		콘크리트 : fck=24Mpa
		스라브벽두께 : 210mm (복배근)
		외벽벽두께 : 180mm (복배근)
	1	코아벽두께 : 180mm (복배근)
		세대벽두께 : 180mm (복배근)
		-콘센트 설치 (바닥 마감선 기준)
		[거실] 스탠드형 에어컨 : 350
	2	[안방] 벽걸이형 에어컨 : 1900
		[화장실] 양변기 옆 : 900
		[주방] 조리대 : 중양 / 냉창고 : 350 / 후드 : 2100
비 고	3	-비디오폰(VP),보일러온도조절기(B), 스위치(S) 설치 (거실 아트홀 위치)
	1	-위치 표기
		에어컨 실외기
		에어컨 콘센트
	2	

사업명칭 PROJECT TITLE	강동구 길동 349-9 도시형생활주택(원룸형) 신축공사-청년주택-
사업번호 PROJECT NO.	
변경사항 ISSUER & REVISIONS	
제 도 DRAWN BY	
설 계 DESIGNED BY	
심 사 CHECKED BY	
승 인 APPROVED BY	건축사 이선영
주기사항 NOTE	
협동설계 CONSULTANTS	
일 자 DATE	
도면번호 DRAWING NO.	A - 101
축 척 SCALE	A3 : 1 / 100
도면명 NAME OF DRAWING	지상1층 평면도

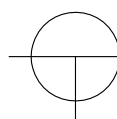

지상1층 평면도
SCALE = 1/100

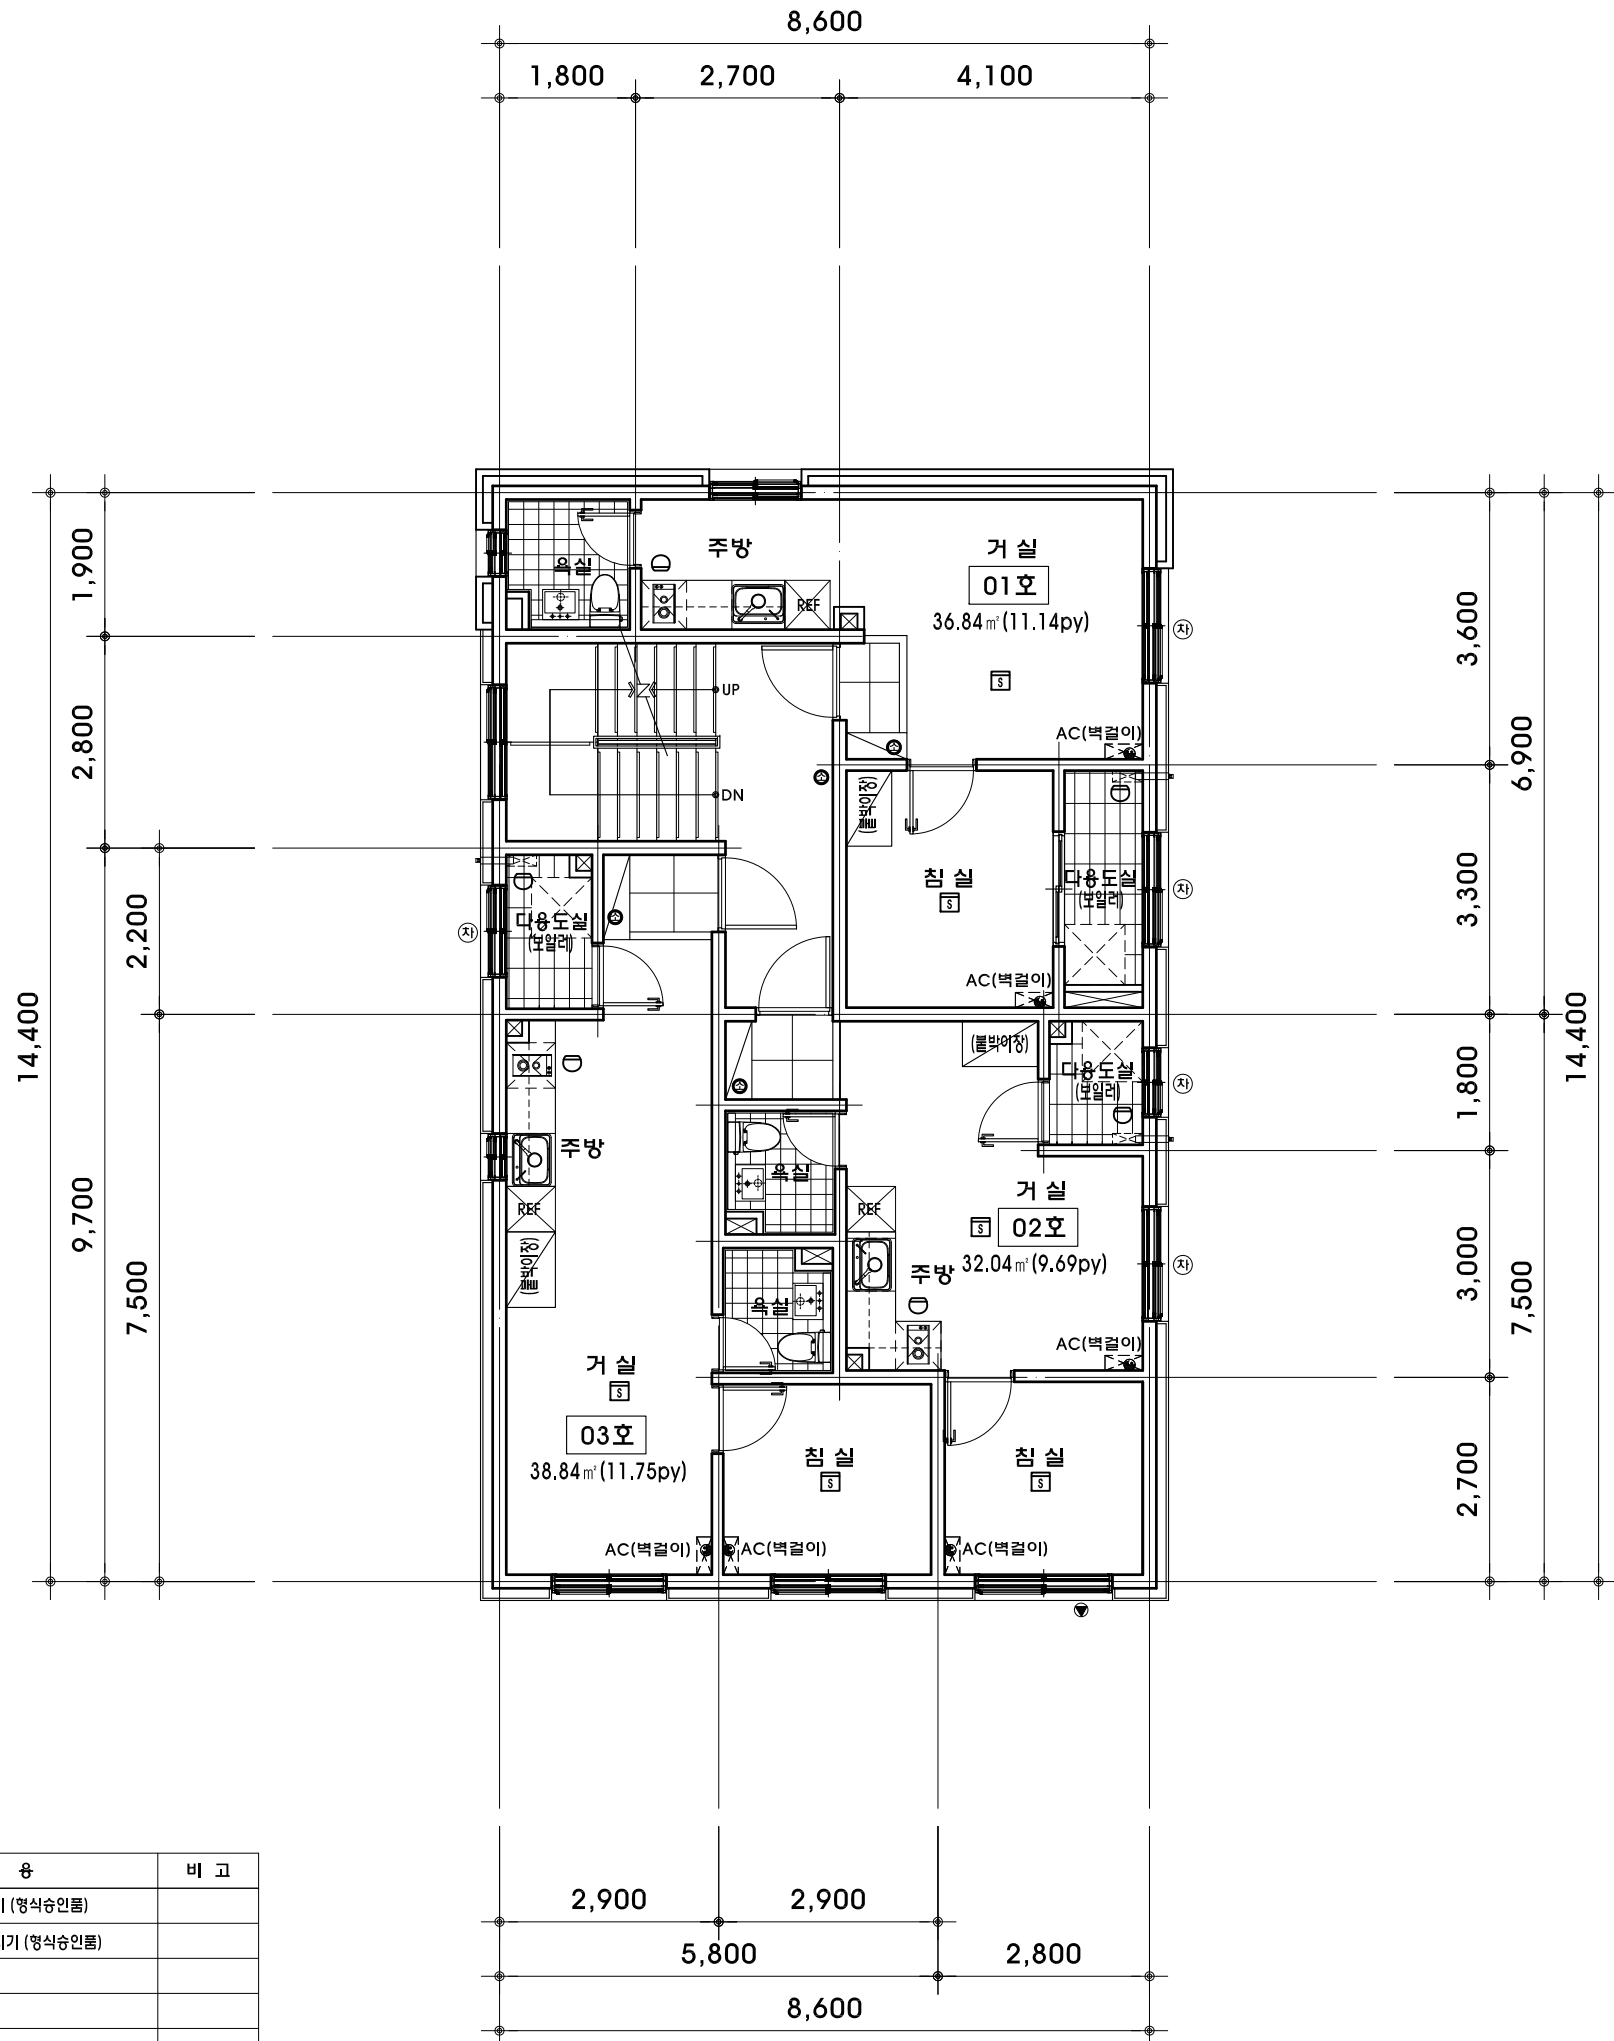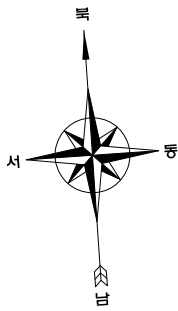


* 주 기 *

상 표	내 용	비 고
	열식 단독경보형 감지기 (형식승인품)	
	연기식 단독경보형 감지기 (형식승인품)	
	ABC 분말 소화기	
	차면시설	
	소방관 진입창	

■ 주 기



구 조	1	주차장내 CCTV,쓰레기분리수거,자전거보관대 설치
		우편함 설치 (세대전용, 공용, 반송용, 폐건전지함 구분 설치)
		우편함 규격은 현장 여건에 맞추어 25x16x32 or 32x25x16
		이상으로 하고 세대전용,공용,반송용,폐건전지함으로 구분
		설치한다.
	(외부)	세대 테라스 설치시 세대간 분리벽 계획
		세대 발코니 설치시 차양시설 설치
		세대내 비디오폰 설치
	2 (계단실)	세대 현관문 도어체크 및 스톱퍼 설치
		계단참의 현관과 계단 이격거리 (최소600mm이상)
	3 (내부)	세대내 욕실, 휴지걸이 매립형 설치
		불박이 가구 내부 다용도 수납가능토록 수평 이동 칸막이 설치
		에어컨 실외기 설치위치 및 에어컨 콘센트 도면 표기 ☺ - 에어컨 콘센트 표기
	4 (시공)	콘크리트 폴타이 제거 후 마감공사 시공 (방수, 단열재 시공 등)
		욕실 & 다용도실 스위치 : 문 열리는 방향으로 시공 주차장 차량 진출입구간,화장실 무소음트랜치 시공
전 기	5 (마감)	- 직접외기(외벽)에 면한 실내벽면 단열재
		[아이소핑크(10mm) + 석고보드 마감도면 표기]
		- 간접외기(계단실,복도)에 면한 실내벽면 단열재
		[경질우레탄보드(80mm) + 석고보드 마감도면 표기]
		*기타 실내 벽면 시멘트 미장 마감
	1	철근 : fy=400Mpa
		콘크리트 : fck=24Mpa
		스라브벽두께 : 210mm (복배근)
		외벽벽두께 : 180mm (복배근)
	2	코아벽두께 : 180mm (복배근)
		세대벽두께 : 180mm (복배근)
		-콘센트 설치 (바닥 마감선 기준)
	1	[거실] 스탠드형 에어컨 : 350
		[안방] 벽걸이형 에어컨 : 1900
		[화장실] 양변기 옆 : 900
		[주방] 조리대 : 중양 / 냉창고 : 350 / 후드 : 2100
	2	-비디오폰(VP),보일러온도조절기(B), 스위치(S) 설치 (거실 아트홀 위치)
	3	-위치 표기
		에어컨 실외기
		에어컨 콘센트
비 고		

사업명 PROJECT TITLE		강동구 길동 349-9 도시형생활주택(원룸형) 신축공사-청년주택-
사업번호 PROJECT NO.		
변경사항 ISSUER & REVISIONS		
	△	
	△	
	△	
	△	
	△	
 한판건축사 연구소 설립로55번길 6-12 T.032,464,6775 F.032,881,9102		
제 도 DRAWN BY		
설 계 DESIGNED BY		
심 사 CHECKED BY		
승 인 APPROVED BY		건축사 이선영
주기사항 NOTE		
협동업체 CONSULTANTS		
일 자 DATE		
도면번호 DRAWING NO.		A - 102
축 척 SCALE		A3 : 1 / 100
도 면 명 NAME OF DRAWING		지상2~4층 평면도

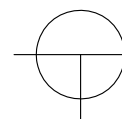

지상2~4층 평면도

SCALE = 1/100

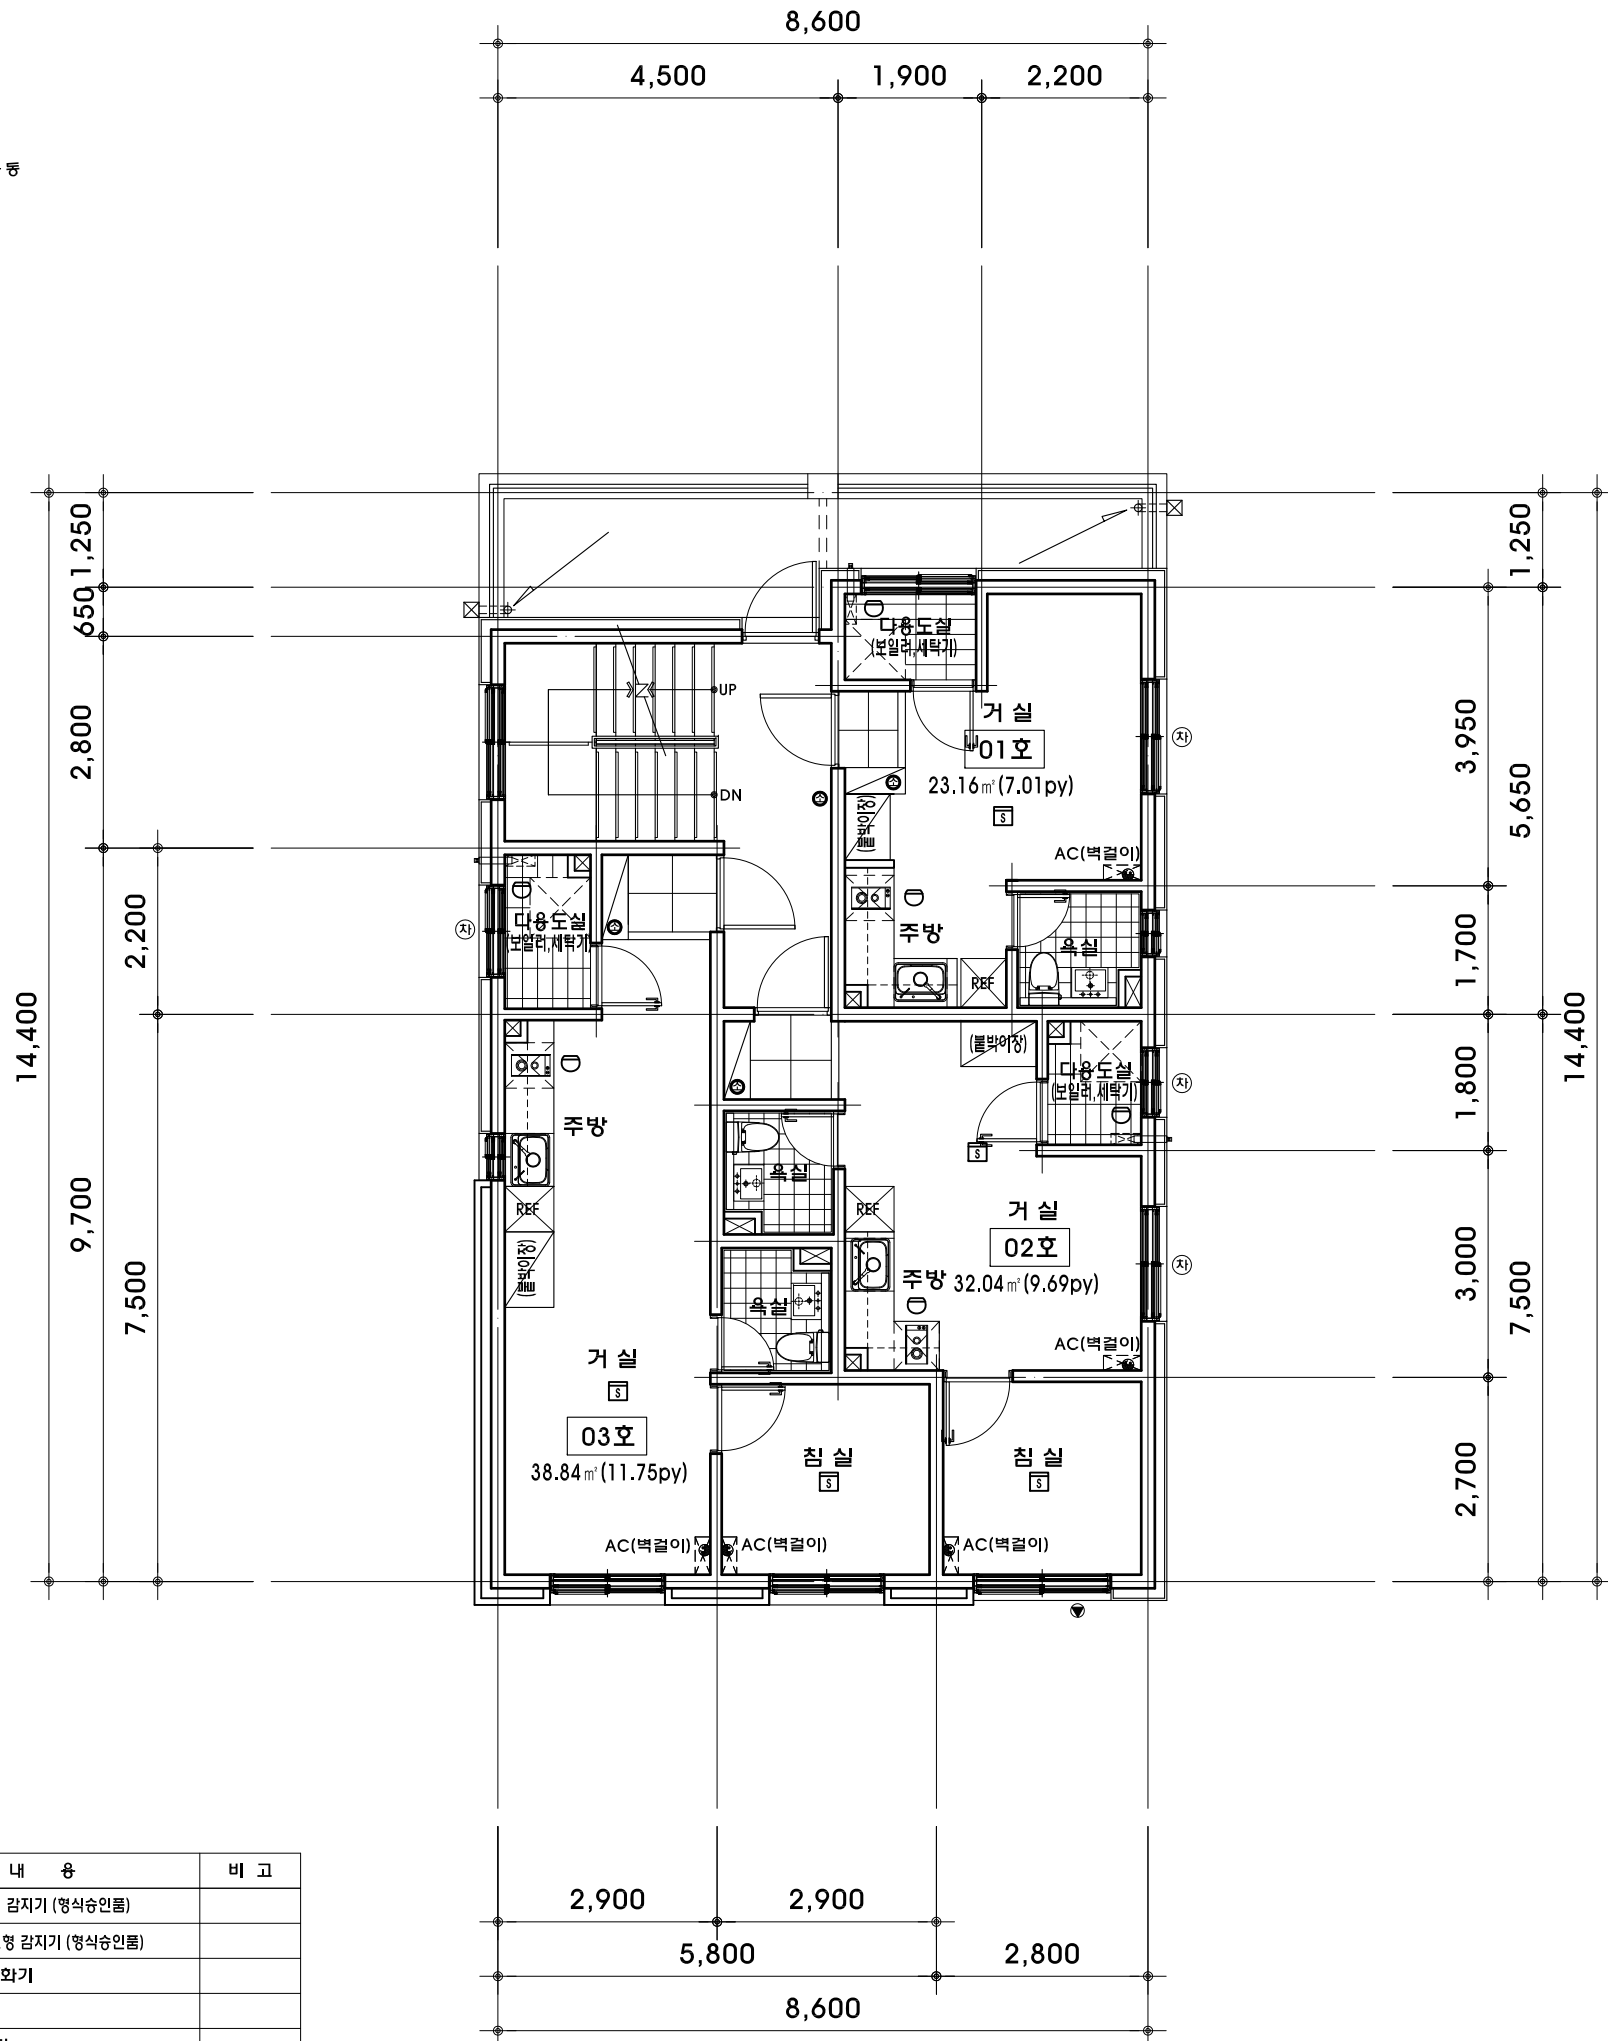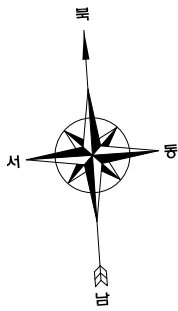


* 주 기 *

상 표	내 용	비 고
☐	열식 단독경보형 감지기 (형식승인품)	
☐	연기식 단독경보형 감지기 (형식승인품)	
⊙	ABC 분말 소화기	
Ⓜ	차면시설	
▼	소방관 진입창	

■ 주 기




구 조	1	주차장내 CCTV,쓰레기분리수거,자전거보관대 설치
		우편함 설치 (세대전용, 공용, 반송용, 폐건전지함 구분 설치)
		우편함 규격은 현장 여건에 맞추어 25x16x32 or 32x25x16
		이상으로 하고 세대전용,공용,반송용,폐건전지함으로 구분
		설치한다.
	(외부)	세대 테라스 설치시 세대간 분리벽 계획
		세대 발코니 설치시 차양시설 설치
		세대내 비디오폰 설치
	2 (계단실)	세대 현관문 도어체크 및 스톱퍼 설치
		계단참의 현관과 계단 이격거리 (최소600mm이상)
	3 (내부)	세대내 욕실, 휴지걸이 매립형 설치
		불박이 가구 내부 다용도 수납가능토록 수평 이동 칸막이 설치
		에어컨 실외기 설치위치 및 에어컨 콘센트 도면 표기 ☺ - 에어컨 콘센트 표기
	4 (시공)	거실-스탠드형, 침실-벽걸이형
		콘크리트 폴타이 제거 후 마감공사 시공 (방수, 단열재 시공 등)
전 기	5 (마감)	욕실 & 다용도실 스위치 : 문 열리는 방향으로 시공
		주차장 차량 진출입구간,화장실 무소음트랜치 시공
		-직접외기(외벽)에 면한 실내벽면 단열재
		[아이소핑크(10mm) + 석고보드 마감도면 표기]
		-간접외기(계단실,복도)에 면한 실내벽면 단열재
	1	[경질우레탄보드(80mm) + 석고보드 마감도면 표기]
		*기타 실내 벽면 시멘트 미장 마감
		철근 : fy=400Mpa
	2	콘크리트 : fck=24Mpa
		스라브벽두께 : 210mm (복배근)
		외벽벽두께 : 180mm (복배근)
		코아벽두께 : 180mm (복배근)
	3	세대벽두께 : 180mm (복배근)
		-콘센트 설치 (바닥 마감선 기준)
		[거실] 스탠드형 에어컨 : 350
		[안방] 벽걸이형 에어컨 : 1900
비 고	1	[화장실] 양변기 옆 : 900
		[주방] 조리대 : 중양 / 냉창고 : 350 / 후드 : 2100
	2	-비디오폰(VP),보일러온도조절기(B),
		스위치(S) 설치 (거실 아트홀 위치)
	3	-위치 표기
		에어컨 실외기
		에어컨 콘센트

사업명칭 PROJECT TITLE		강동구 길동 349-9 도시형생활주택(원룸형) 신축공사-청년주택-
사업번호 PROJECT NO.		
변경사항 ISSUER & REVISIONS		
△		
 한한건축사 연구소 설립로55번길 6-12 T.032,464,6775 F.032,881,9102		
제 도 DRAWN BY		
설 계 DESIGNED BY		
심 사 CHECKED BY		
승 인 APPROVED BY		건축사 이선영
주기사항 NOTE		
협동업체 CONSULTANTS		
일 자 DATE		
도면번호 DRAWING NO.		A - 103
축 척 SCALE		A3 : 1 / 100
도 면 명 NAME OF DRAWING		지상5층 평면도

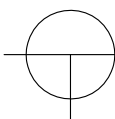


지상5층 평면도

SCALE = 1/100

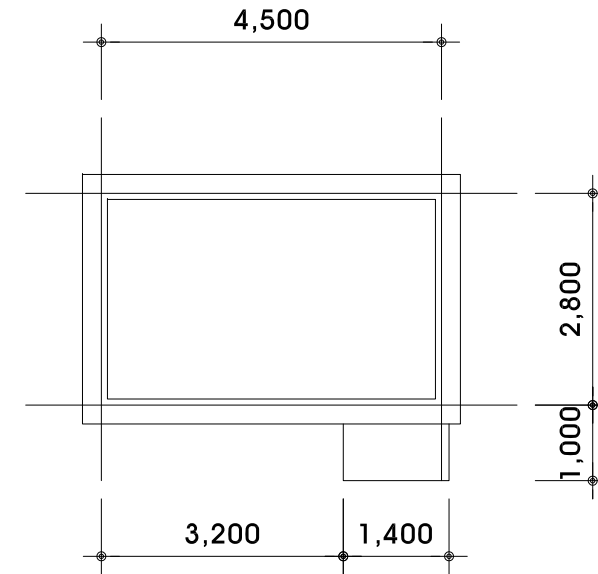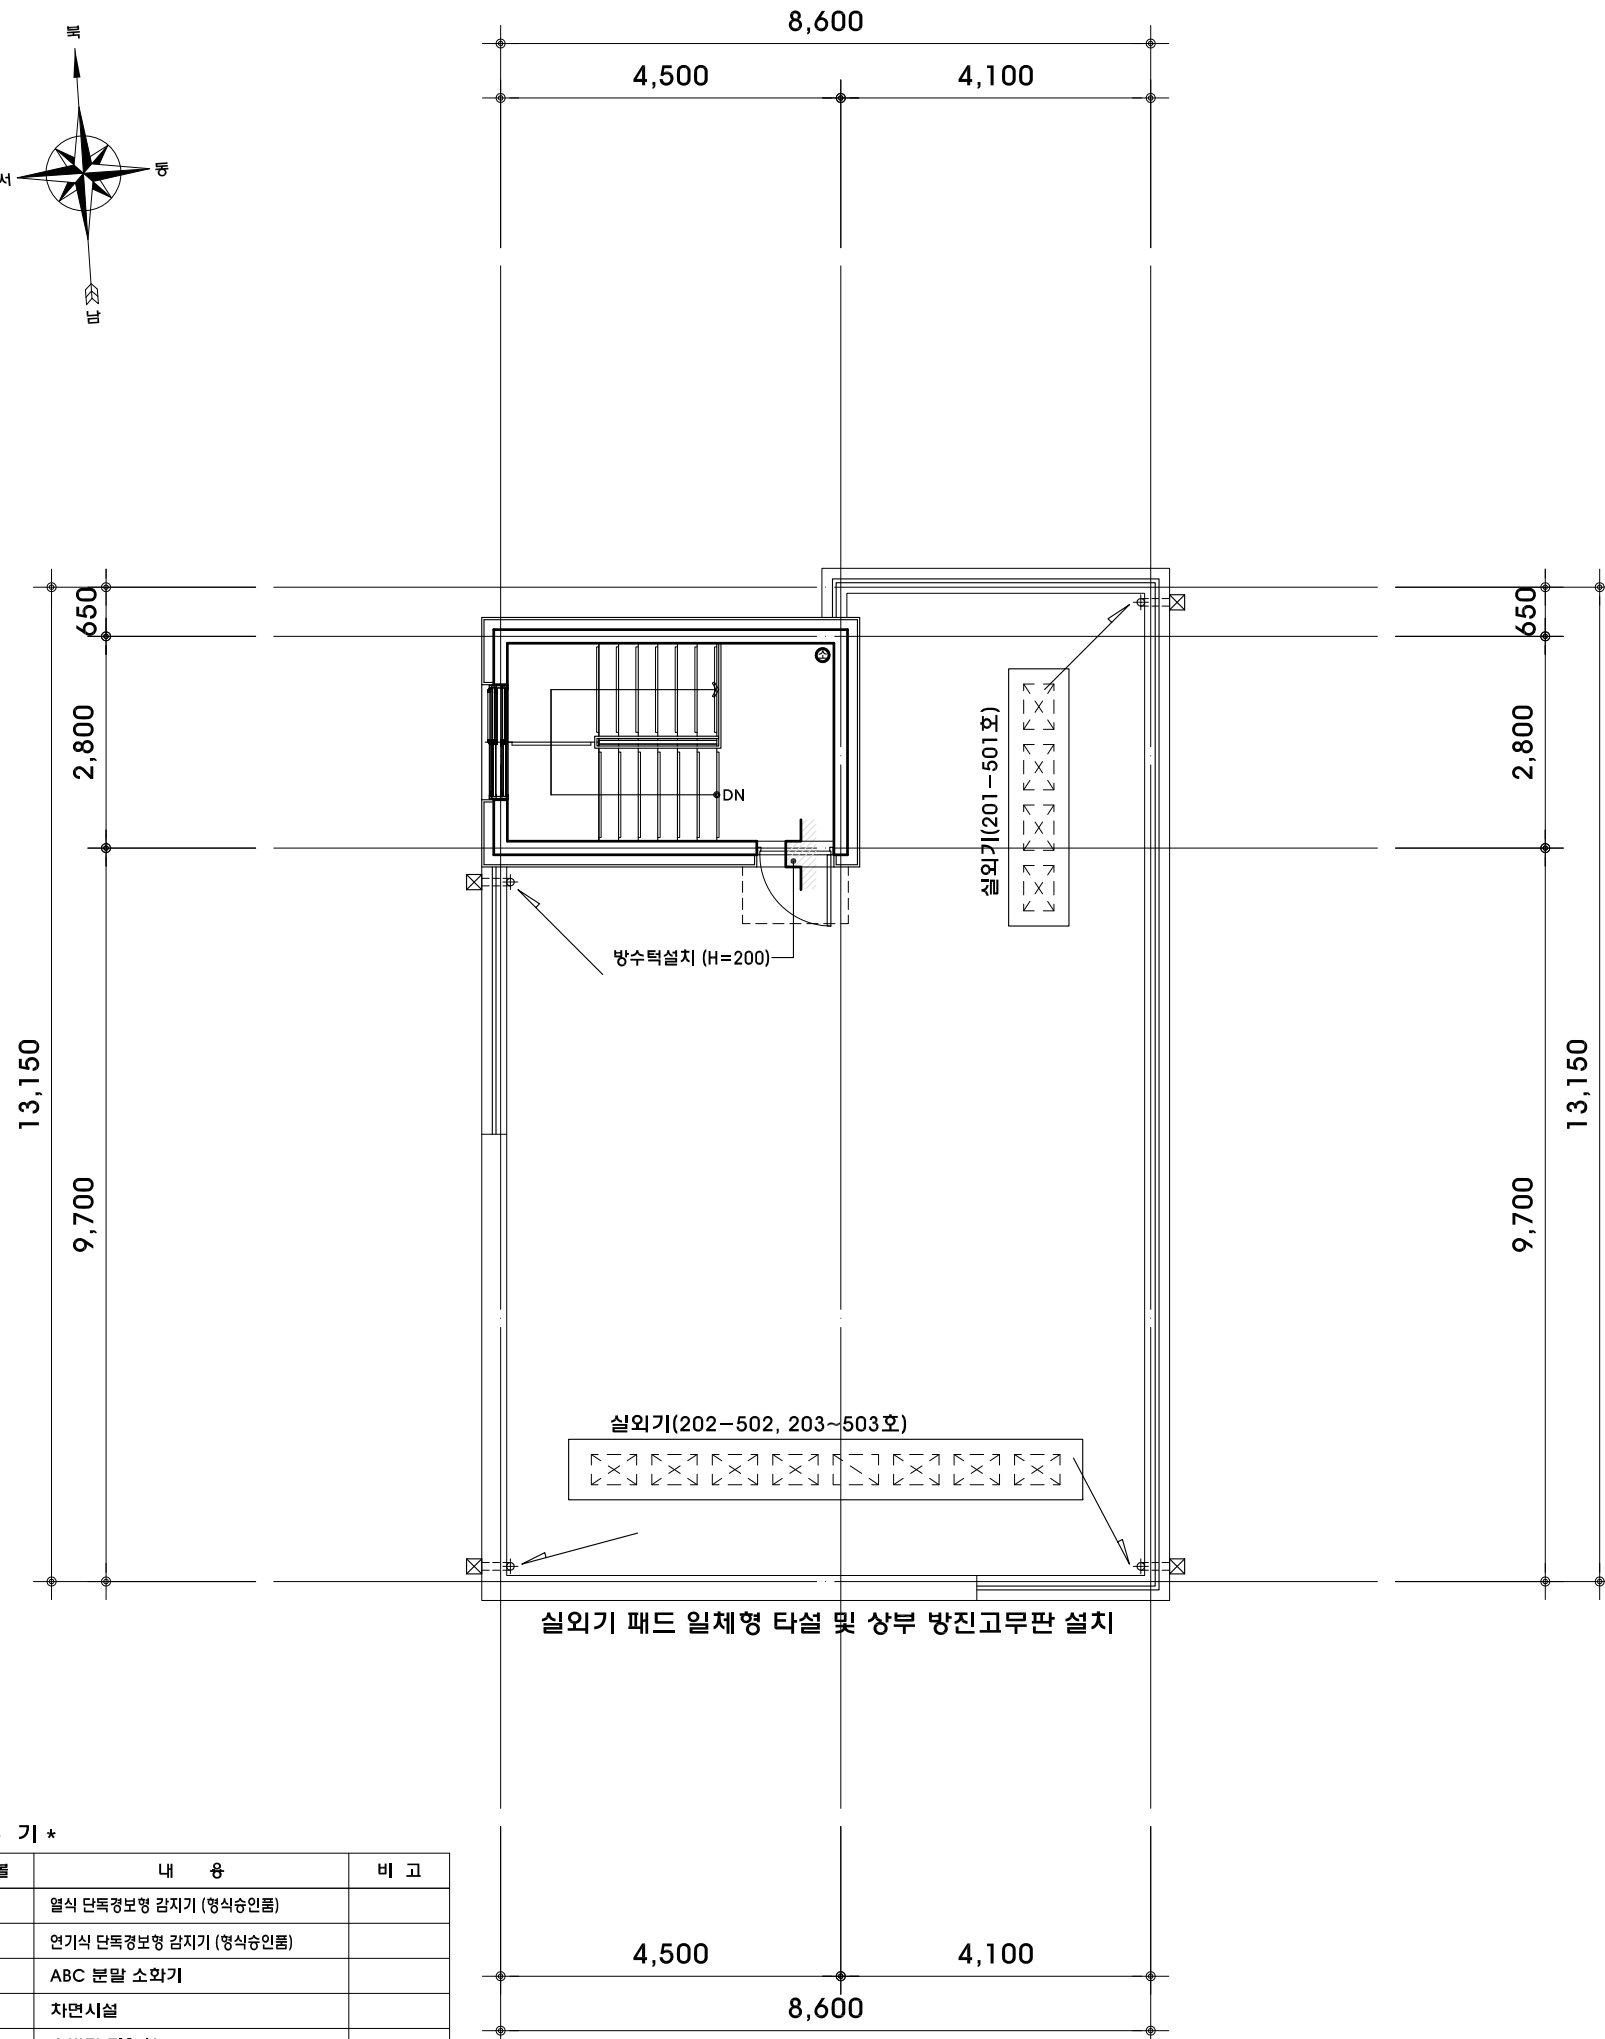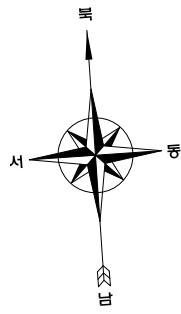

* 주 기 *

심볼	내용	비고
☐	열식 단독경보형 감지기 (형식승인품)	
☐	연기식 단독경보형 감지기 (형식승인품)	
⊕	ABC 분말 소화기	
⊙	차면시설	
▼	소방관 진입창	

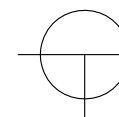

지붕층 및 옥탑지붕층 평면도

SCALE = 1/100

사업명칭
PROJECT TITLE

강동구 길동 349-9
도시형생활주택(원룸형)
신축공사-청년주택-

사업번호
PROJECT NO.

변경사항
ISSUER & REVISIONS



hanndas
architects & interiors
안전광역시 연수구 남달로55번길 6-12
T.032,464,6775 F.032,881,9102

제 도
DRAWN BY

설 계
DESIGNED BY

심 사
CHECKED BY

승 인
APPROVED BY
건축사 이선영

주기사장
NOTE

협동업체
CONSULTANTS

일 자
DATE

도면번호
DRAWING NO.


A - 104

축척
SCALE


A3 : 1 / 100

도면명
NAME OF DRAWING

지붕층 및
옥탑지붕층 평면도

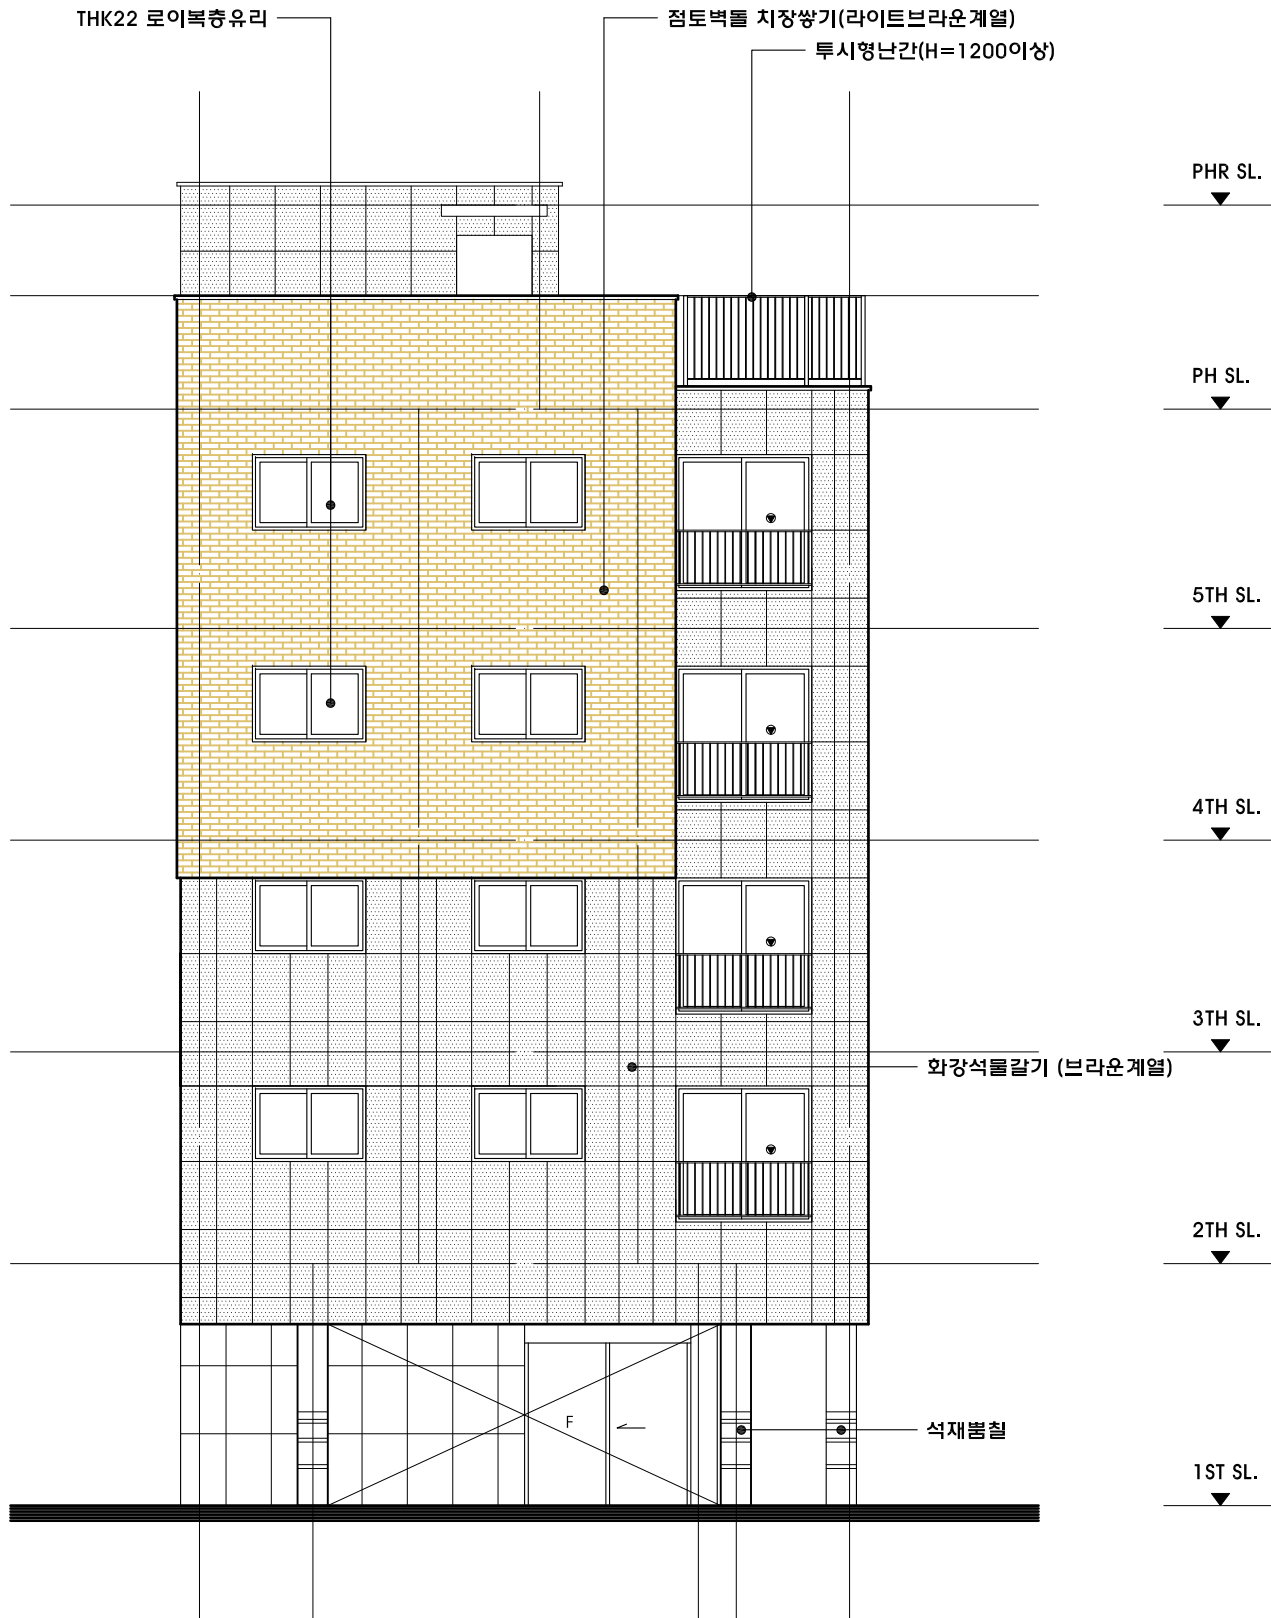

남 측 면 도
SCALE = 1/100

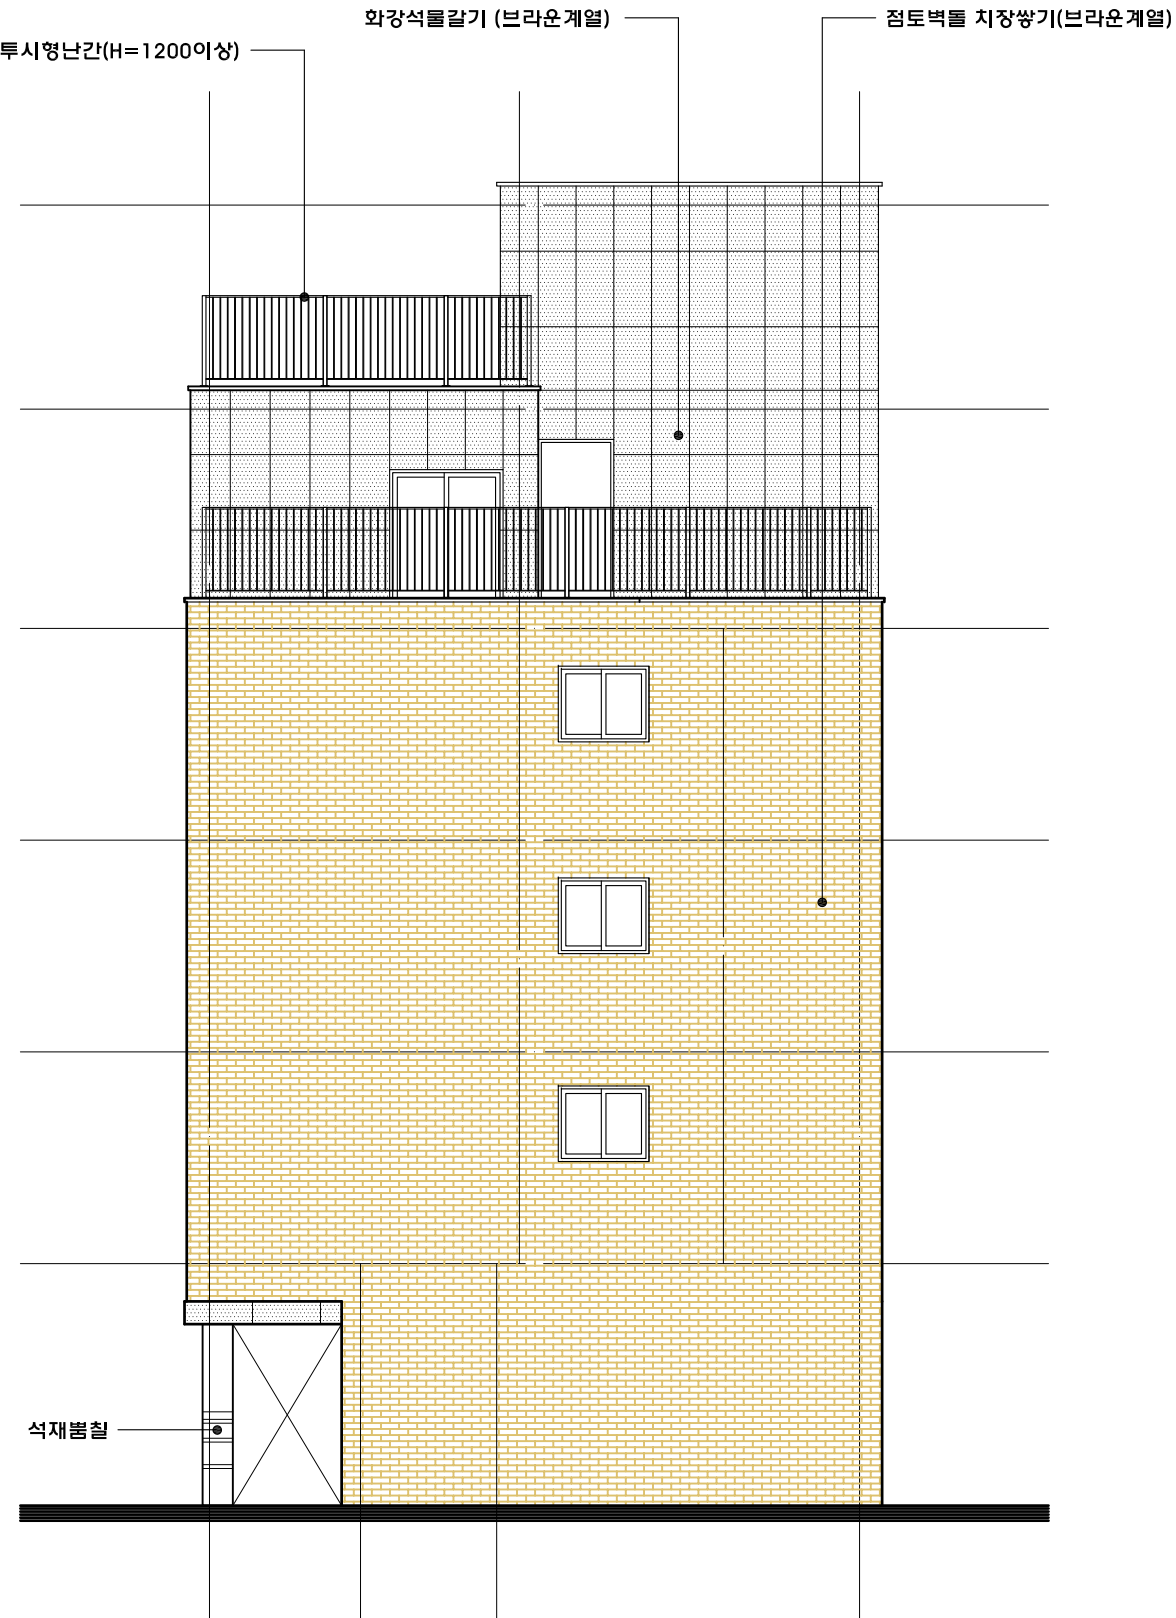


북 측 면 도
SCALE = 1/100

사업명 PROJECT TITLE	
강동구 길동 349-9 도시형생활주택(원룸형) 신축공사-청년주택-	
사업번호 PROJECT NO.	
변경사항 ISSUER & REVISIONS	
△	
△	
△	
△	
△	
 Architects & Interiors 안전광역시 연수구 남달로55번길 6-12 T.032.464.6775 F.032.881.9102	
제 도 DRAWN BY	
설 계 DESIGNED BY	
심 사 CHECKED BY	
승 인 APPROVED BY 건축사 이선영	
주기사항 NOTE	
연동업체 CONSULTANTS	
일 자 DATE	
도면번호 DRAWING NO. A - 105	
축 척 SCALE A3 : 1 / 100	
도면명 NAME OF DRAWING 남측면도, 북측면도	



사업명 PROJECT TITLE	
강동구 길동 349-9 도시형생활주택(원룸형) 신축공사-청년주택-	
사업번호 PROJECT NO.	
변경사항 ISSUER & REVISIONS	
△	
△	
△	
△	
△	
 architects & interiors 안전행복도시 연구개발55번길 6-12 T.032.464.6775 F.032.881.9102	
제 도 DRAWN BY	
설 계 DESIGNED BY	
심 사 CHECKED BY	
승 인 APPROVED BY 건축사 이선영	
주기사항 NOTE	
연동업체 CONSULTANTS	
일 자 DATE	
도면번호 DRAWING NO. A - 106	
축 척 SCALE A3 : 1 / 100	
도면명 NAME OF DRAWING 동측면도	

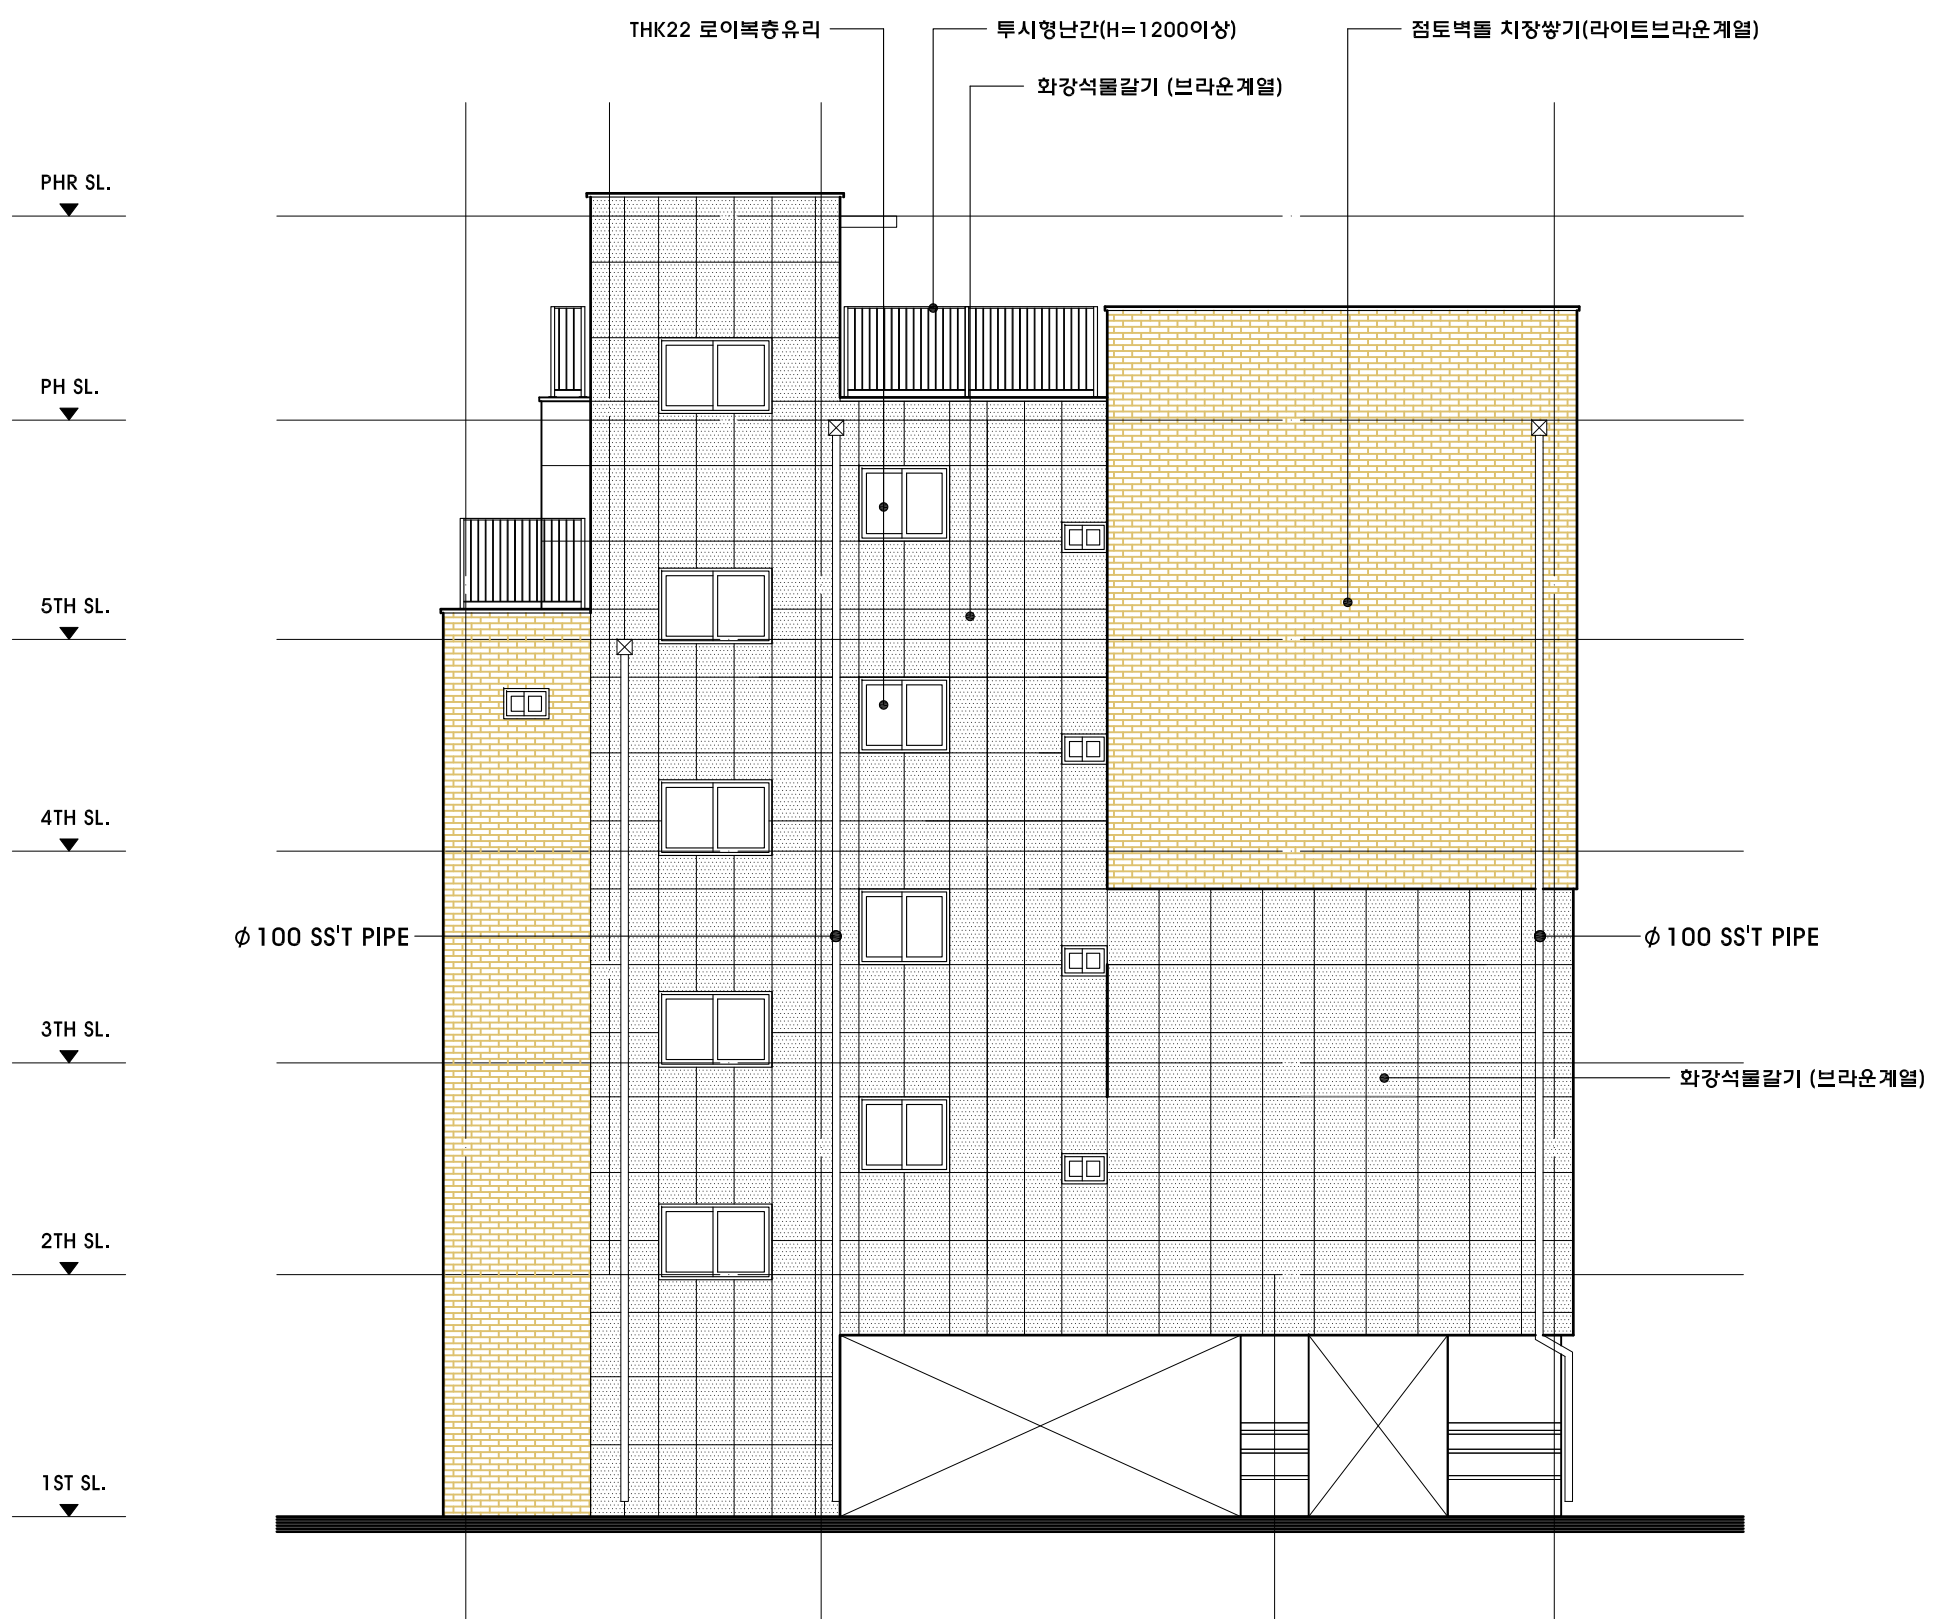

서 측 면 도
SCALE = 1/100

사업명 PROJECT TITLE	
강동구 길동 349-9 도시형생활주택(원룸형) 신축공사-청년주택-	
사업번호 PROJECT NO.	
변경사항 ISSUER & REVISIONS	
△	
△	
△	
△	
△	
 architects & interiors 안전광역시 연수구 남달로55번길 6-12 T.032.464.6775 F.032.881.9102	
제 도 DRAWN BY	
설 계 DESIGNED BY	
심 사 CHECKED BY	
승 인 APPROVED BY 건축사 이선영	
주기사항 NOTE	
연동업체 CONSULTANTS	
일 자 DATE	
도면번호 DRAWING NO. A - 107	
축 척 SCALE A3 : 1 / 100	
도면명 NAME OF DRAWING 서측면도	