


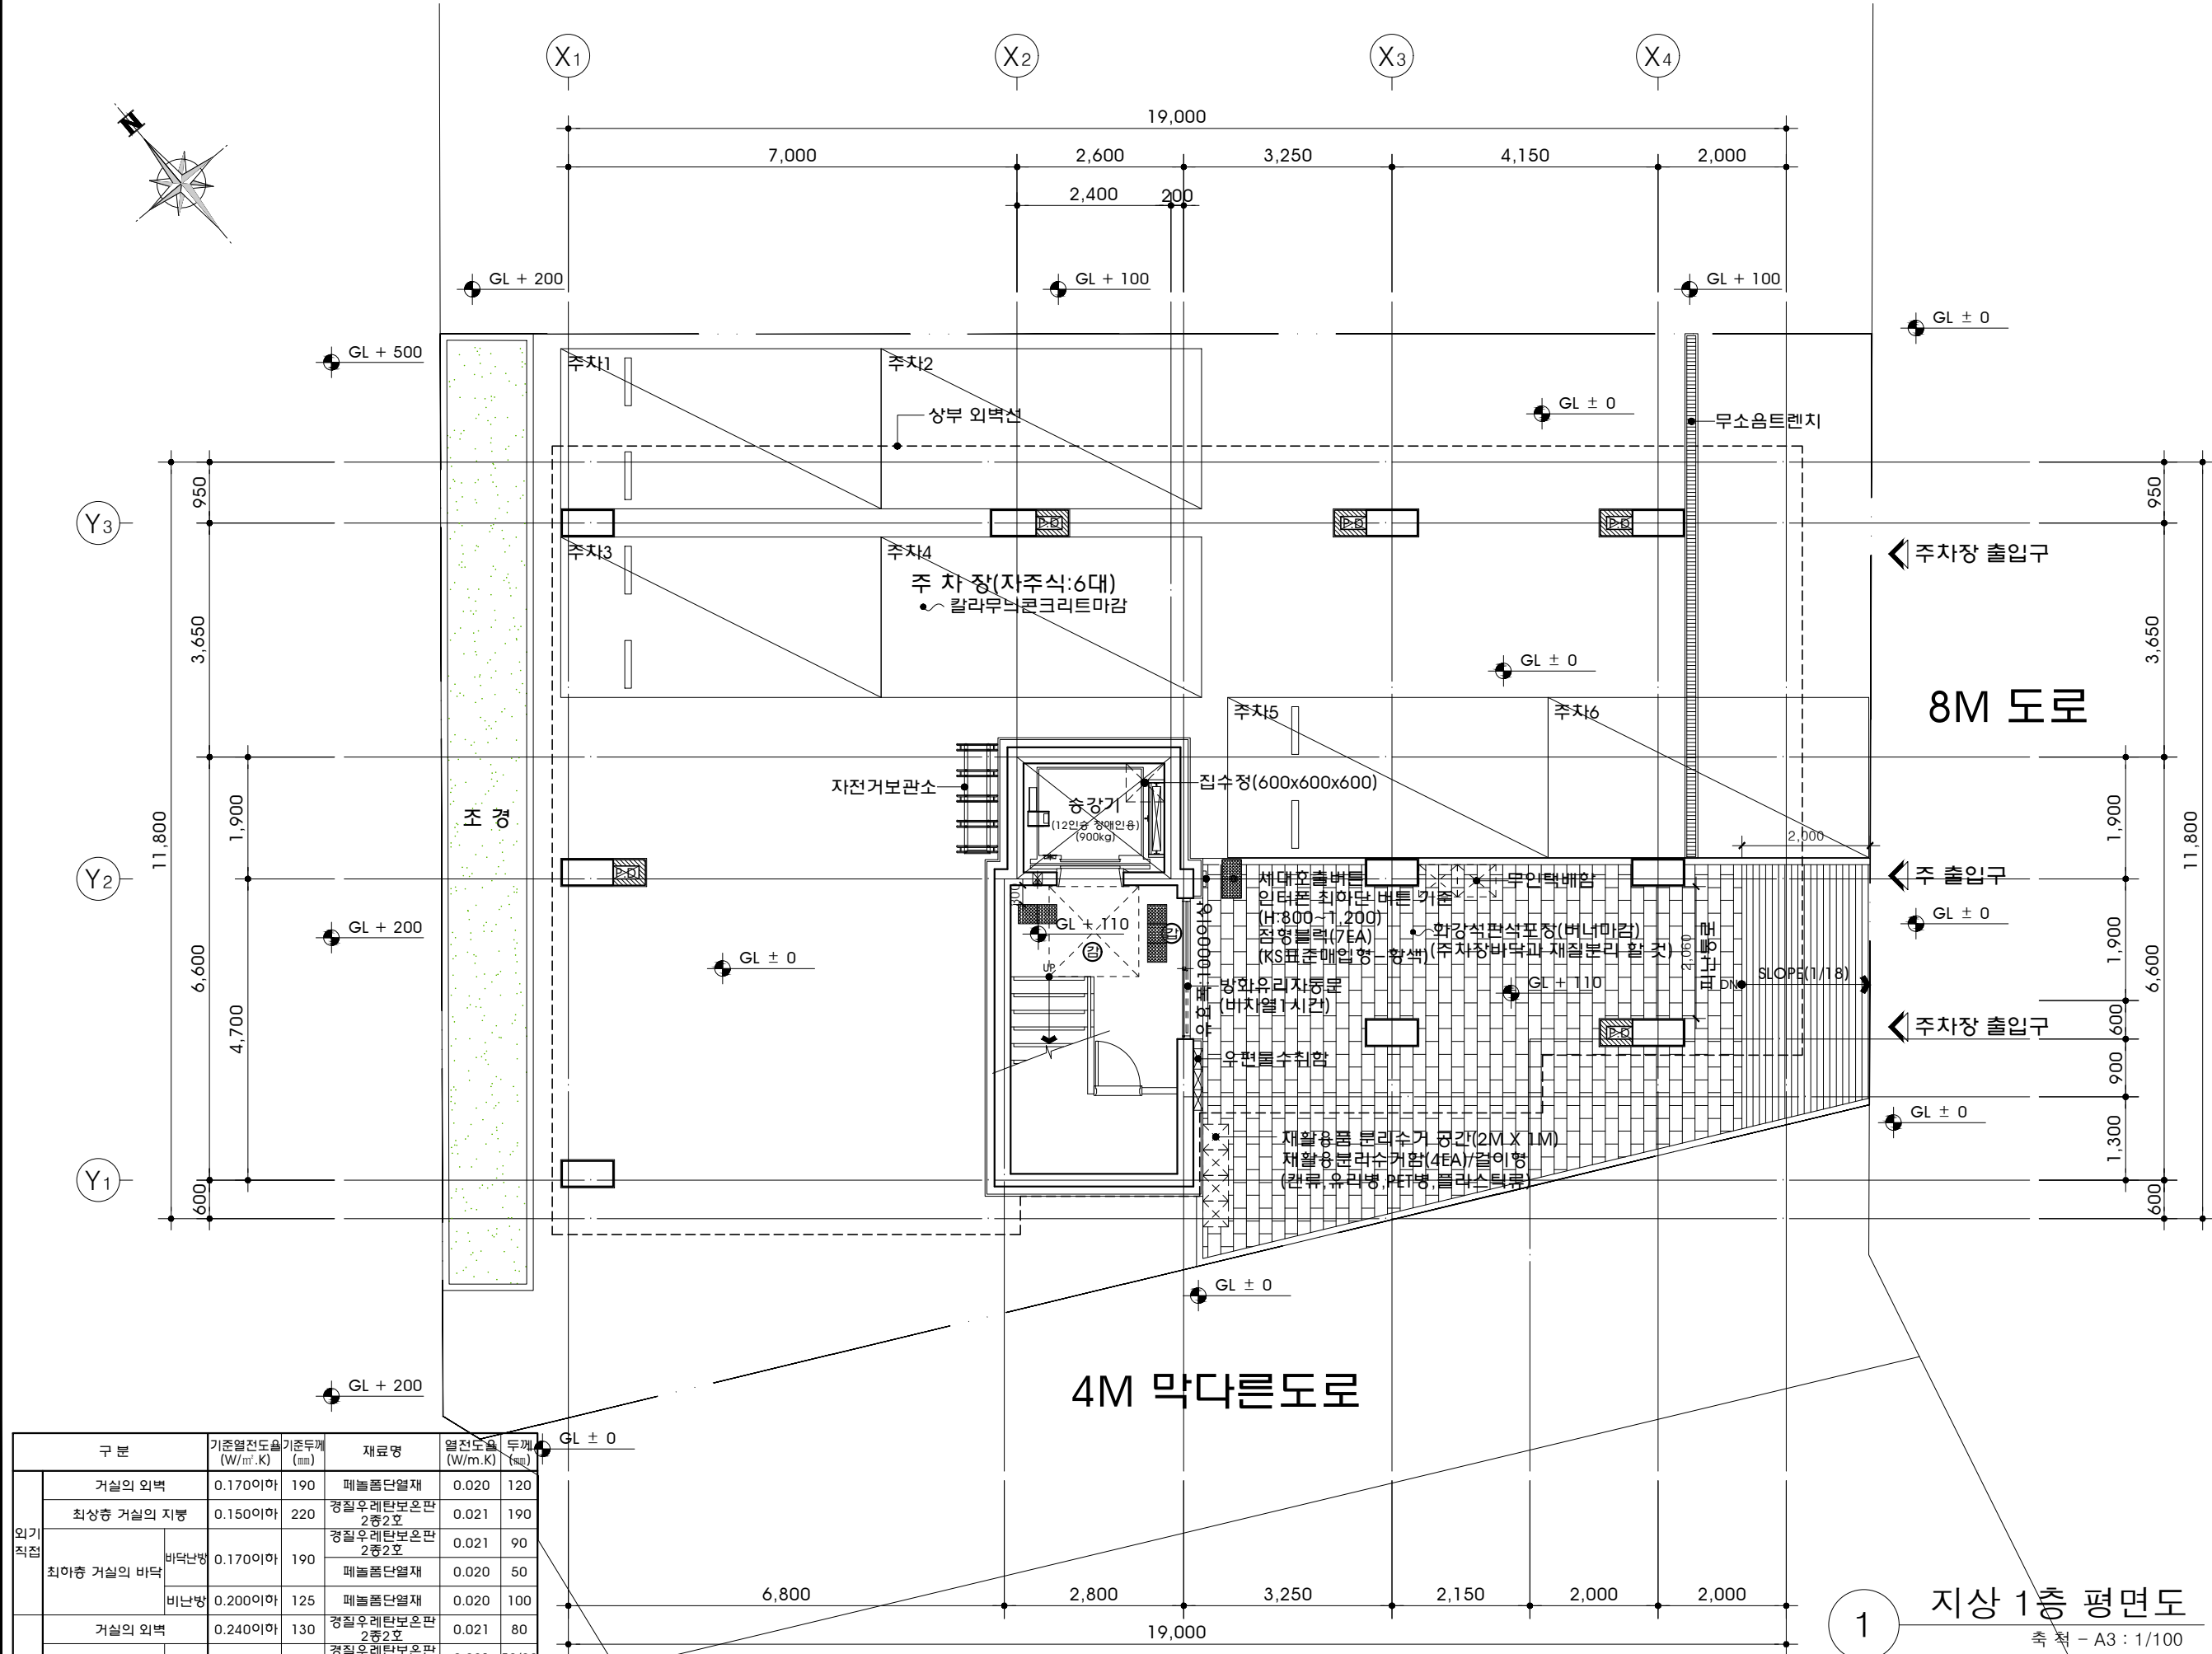


구 분		기준열전도율 (W/m ² .K)	기준두께 (mm)	재료명	열전도율 (W/m.K)	두께 (mm)
외기 직접	거실의 외벽	0.170이하	190	페놀폼단열재	0.020	120
	최상층 거실의 지붕	0.150이하	220	경질우레탄보온판 2중2호	0.021	190
	최하층 거실의 바닥	비단난방 0.170이하	190	경질우레탄보온판 2중2호	0.021	90
				페놀폼단열재	0.020	50
		비단난방 0.200이하	125	페놀폼단열재	0.020	100
외기 간접	거실의 외벽	0.240이하	130	경질우레탄보온판 2중2호	0.021	80
	최하층 거실의 바닥	비단난방 0.240이하	125	경질우레탄보온판 2중2호	0.021	50/20
				비드법보온판 완충재	0.031	30
		비단난방 0.290이하	110	경질우레탄보온판 2중2호	0.021	70

NO.	DATE	REVISION
7		
6		
5		
4		
3		
2		
1		

* NOTE

- 발트인
- 세탁기, 냉장고, 에어컨
- 냉장고 위 전자렌지 설치
- 책상, 불박이장이이동식옷장

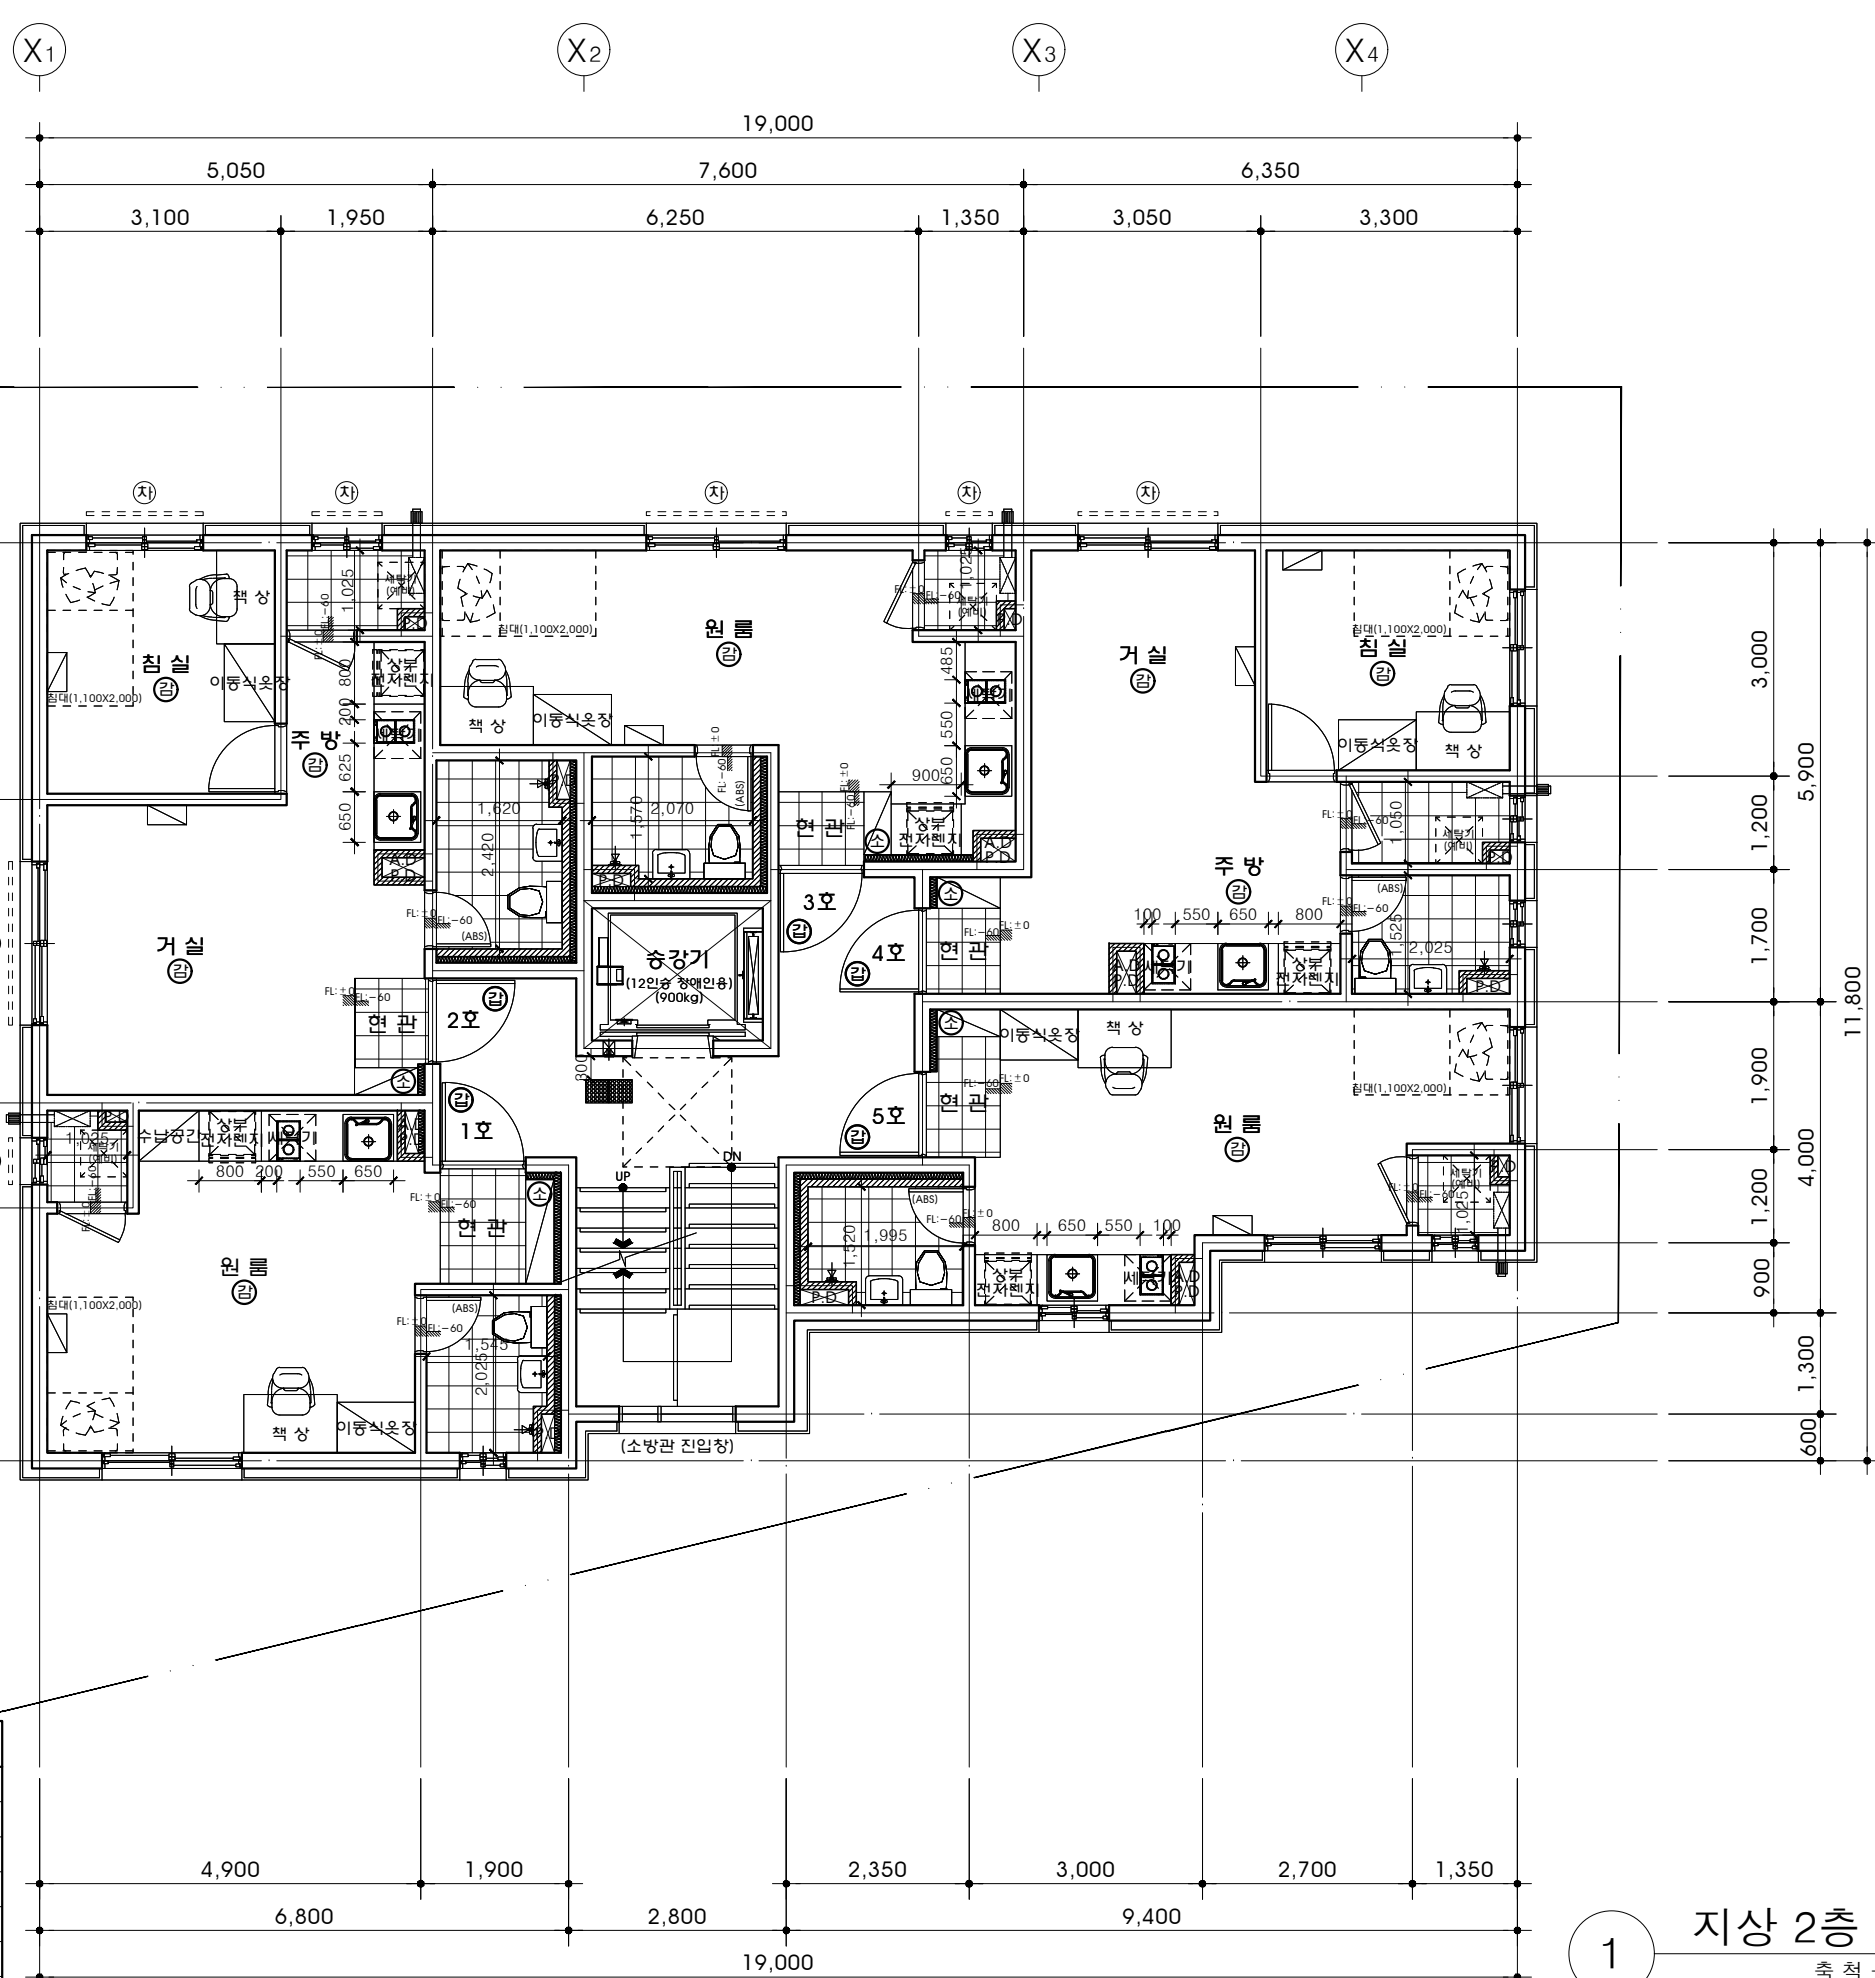

구 분		기준열전도율 (W/m ² .K)	기준두께 (mm)	재료명	열전도율 (W/m.K)	두께 (mm)	
외기 직접	거실의 외벽	0.170이하	190	페놀폼단열재	0.020	120	
	최상층 거실의 지붕	0.150이하	220	경질우레탄보온판 2중2호	0.021	190	
	최하층 거실의 바닥	바닥난방	0.170이하	190	경질우레탄보온판 2중2호	0.021	90
		비난방	0.200이하	125	페놀폼단열재	0.020	50
					페놀폼단열재	0.020	100
외기 간접	거실의 외벽	0.240이하	130	경질우레탄보온판 2중2호	0.021	80	
	최하층 거실의 바닥	바닥난방	0.240이하	125	경질우레탄보온판 2중2호	0.021	50/20
		비난방	0.290이하	110	비드법보온판 완충재	0.031	30
					경질우레탄보온판 2중2호	0.021	70

1 지상 2층 평면도
축척 - A3 : 1/100



사업명칭
PROJECT TITLE
강동구 성내동 521-3, 14번지
도시형생활주택
(청년주택)신축공사

사업번호
PROJECT NO.

NOTE

- ㉔ 단독경보감지기
- ㉕ ABC분말소화기(3.3KG)
- ㉖ 60분+ 방화문, 60분 방화문

- 보일러
- 에어컨
- 실외기

차면시설
*기둥 주위에 차량 보호대 설치
*각세대 거실난간 국기꽃이 설치
*승강기에 면한 침실 및 거실,
주방 방진패드 설치

* 구 조 *

- 콘크리트: fck = 27 MPa
- 철근: fy = 400 MPa
- 세대벽두께: 200mm(북배근)
- 세대내벽두께: 150mm(북배근)
- 외벽두께: 200mm(북배근)
- 코아벽두께: 200mm(북배근)
- 스라브두께: 210mm(3~5층)
- 스라브두께: 180mm(2층, 지붕)

9.세대현관문 규격 (틀포함)
1100x2200

ISSUES & REVISIONS

NO.	DATE	REVISION
7		
6		
5		
4		
3		
2		
1		

제도
DRAWN BY 전유구

심사
CHECKED BY 정우열

승인
APPROVED BY 김재형

도면명
NAME OF DRAWING

지상 2층 평면도

일자
DATE 2024. 10 .

축척
SCALE A3: 1/100

건축사사무소
에코플랜
Total Architecture
Engineers Group

서울특별시 송파구 삼학사로 25-1
신영빌딩 2층 (삼전동 182-4)
TEL: (02)418-7902 / FAX: (02)418-7907
E-mail: ecoplan01@hanmail.net

도면번호
SHEET NO.

A-102


- * NOTE

- 발트인

- 세탁기, 냉장고, 에어컨

- 냉장고 위 전자렌지 설치

- 책상, 불박이장이이동식옷장

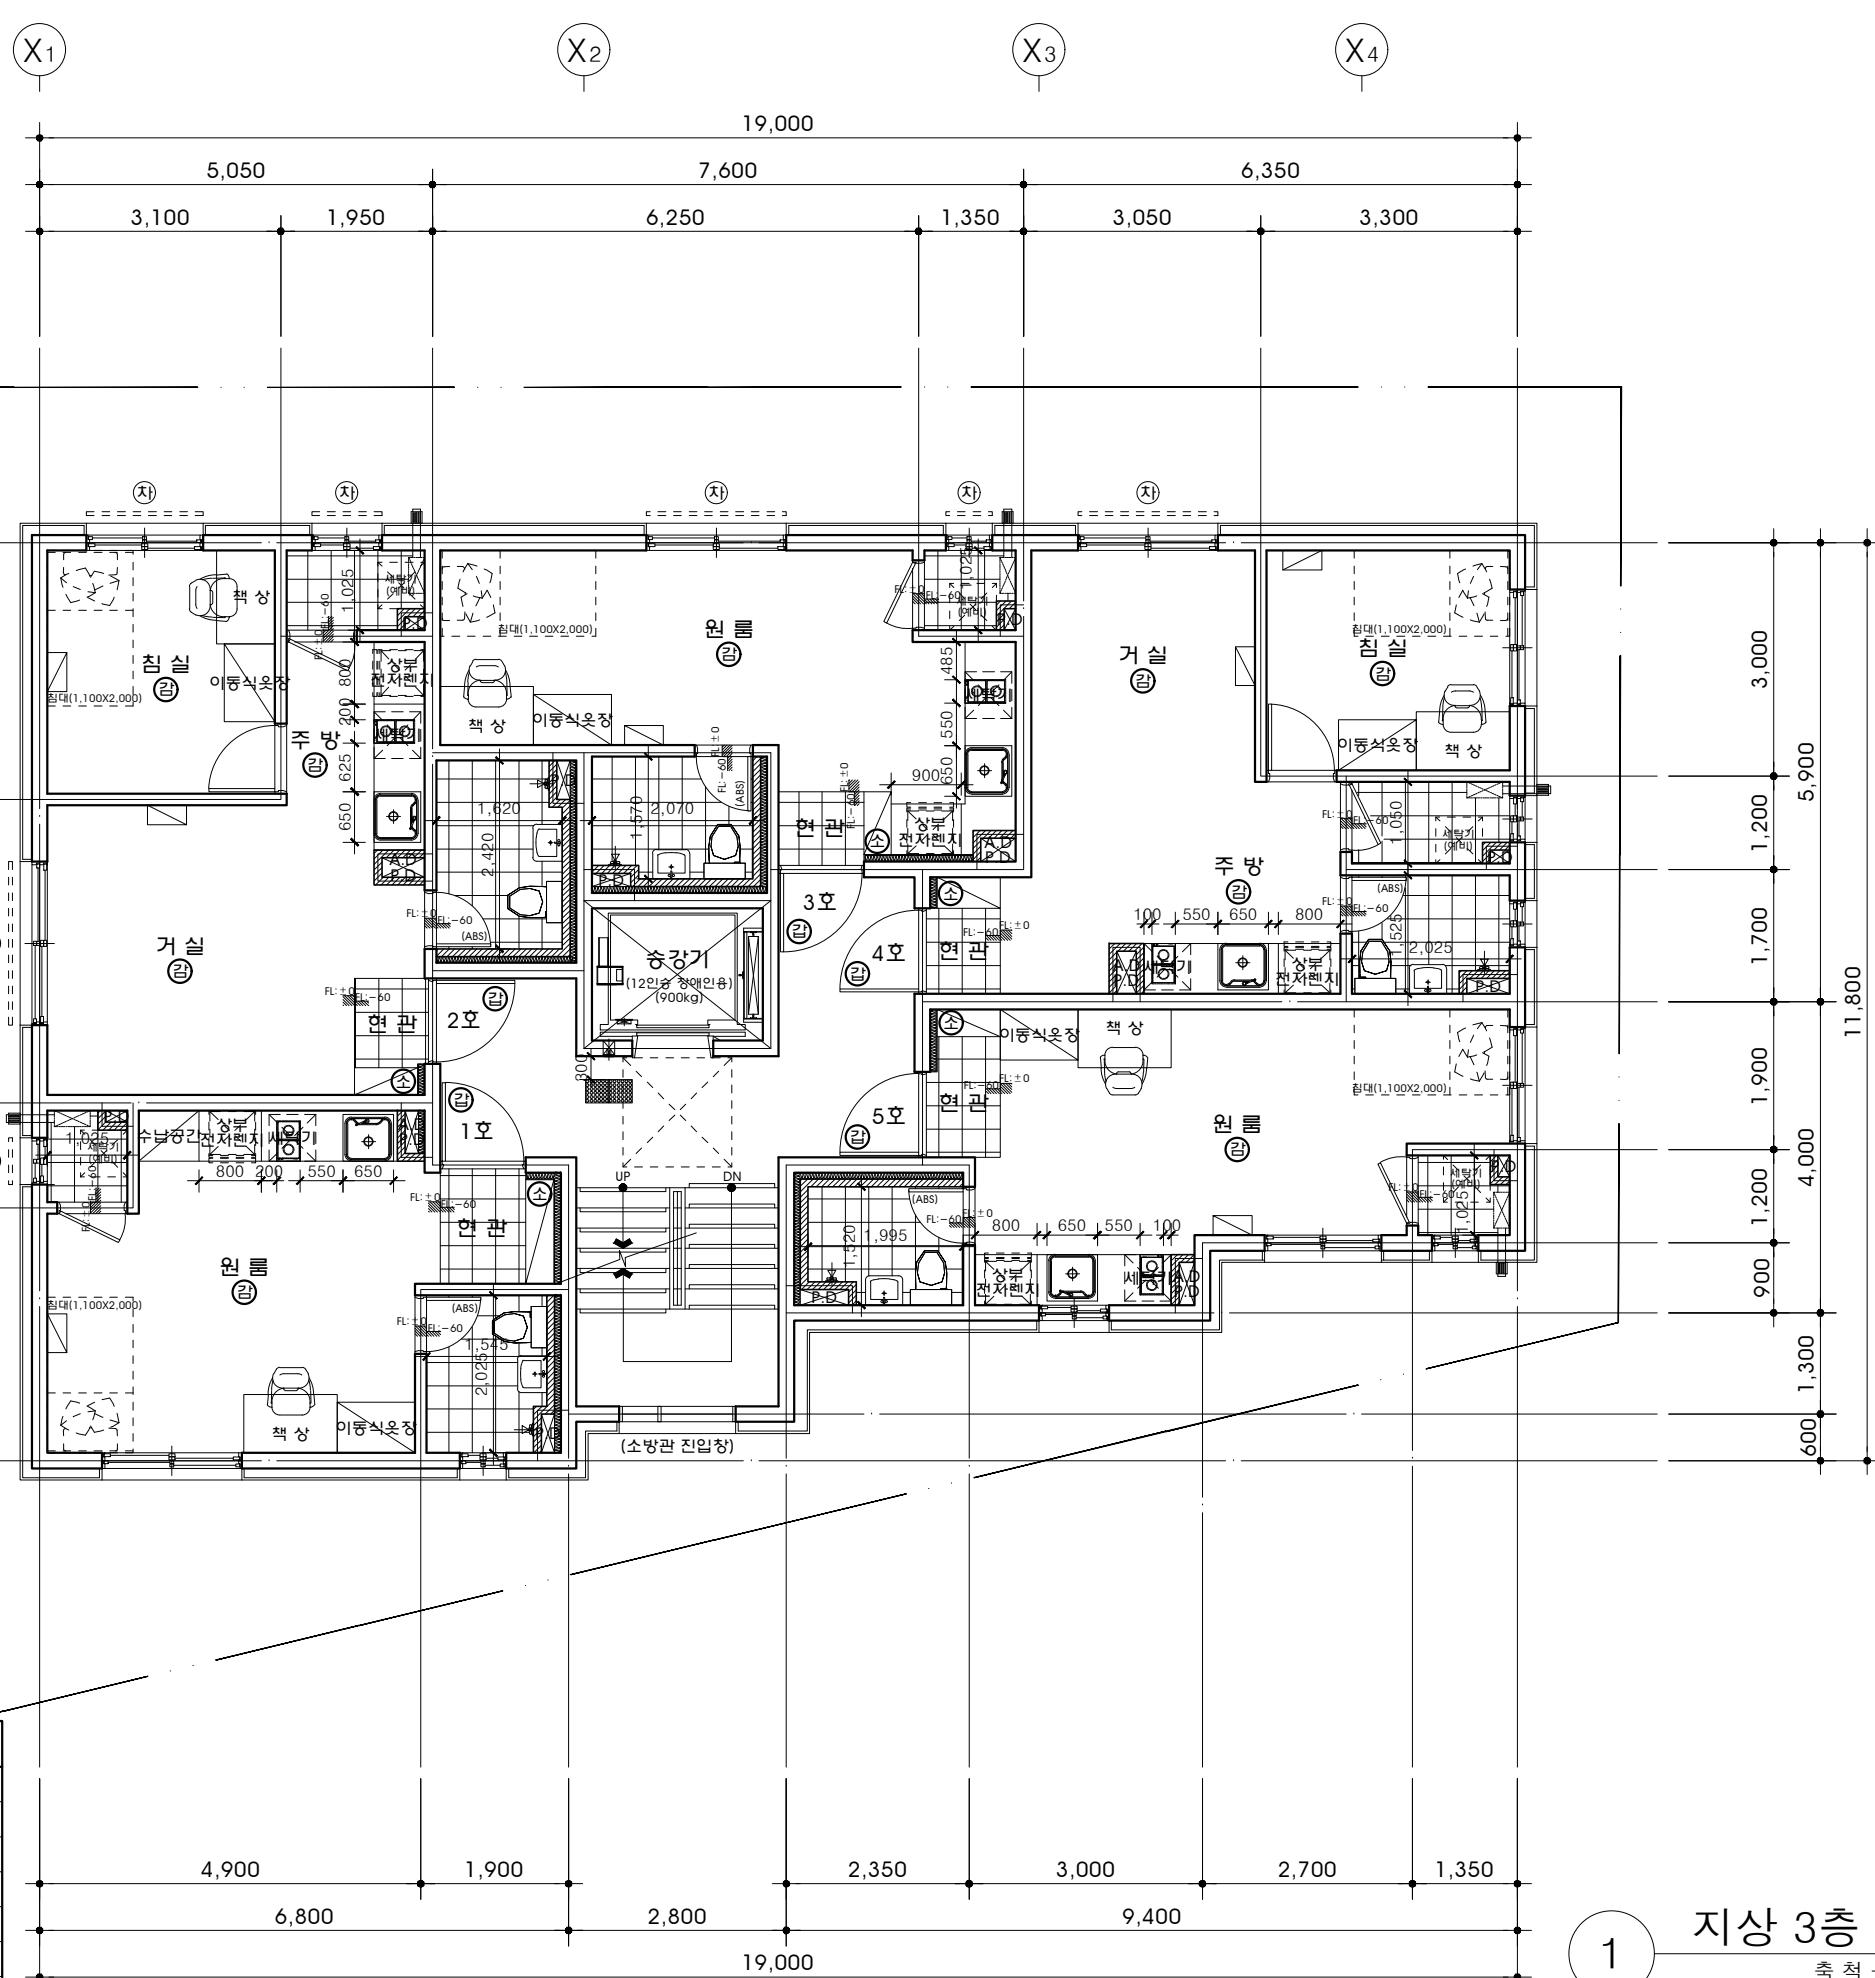

구 분		기준열전도율 (W/m ² .K)	기준두께 (mm)	재료명	열전도율 (W/m.K)	두께 (mm)	
외기 직접	거실의 외벽	0.170이하	190	페놀폼단열재	0.020	120	
	최상층 거실의 지붕	0.150이하	220	경질우레탄보온판 2중2호	0.021	190	
	최하층 거실의 바닥	바닥난방	0.170이하	190	경질우레탄보온판 2중2호	0.021	90
		비난방	0.200이하	125	페놀폼단열재	0.020	50
					페놀폼단열재	0.020	100
외기 간접	거실의 외벽	0.240이하	130	경질우레탄보온판 2중2호	0.021	80	
	최하층 거실의 바닥	바닥난방	0.240이하	125	경질우레탄보온판 2중2호	0.021	50/20
		비난방	0.290이하	110	비드법보온판 완충재	0.031	30
					경질우레탄보온판 2중2호	0.021	70

EpA

ECO-PLAN

ARCHITECTURE

사업명칭

PROJECT TITLE

강동구 성내동 521-3,14번지

도시형생활주택

(청년주택)신축공사

사업번호

PROJECT NO.

NOTE

Ⓢ 단독경보감지기

Ⓢ ABC분말소화기(3.3KG)

Ⓢ 60분+ 방화문, 60분 방화문

☐ 보일러

☐ 에어컨

☐ 실외기

----- 차면시설

*기둥 주위에 차량 보호대 설치

*각세대 거실난간 국기꽃이 설치

*승강기에 면한 침실 및 거실, 주방 방진패드 설치

* 구 조 *

1.콘크리트: fck = 27 MPa

2.철근 : fy = 400 MPa

3.세대벽두께:200mm(북배근)

4.세대내벽두께:150mm(북배근)

5.외벽두께:200mm(북배근)

6.코아벽두께:200mm(북배근)

7.스라브두께:210mm(3~5층)

8.스라브두께:180mm(2층,지붕)

9.세대현관문 규격 (틀포함) 1100x2200

ISSUES & REVISIONS

7		
6		
5		
4		
3		
2		
1		

NO.

DATE

REVISION

제도

DRAWN BY

전유구

심사

CHECKED BY

정우열

승인

APPROVED BY

김재형

도면명

NAME OF DRAWING

지상 3층 평면도

일자

DATE

2024. 10 .

축척

SCALE

A3: 1/100

건축사사무소

에코플랜

Total Architecture

Engineers Group

서울특별시 송파구 삼학사로 25-1

신영빌딩 2층 (삼전동 182-4)

TEL: (02)418-7902 / FAX: (02)418-7907

E-mail: ecoplan01@hanmail.net

도면번호

SHEET NO.


A-103

1

지상 3층 평면도

축척 - A3 : 1/100

- * NOTE
- 빌트인
- 세탁기, 냉장고, 에어컨
- 냉장고 위 전자렌지 설치
- 책상, 불박이장이이동식옷장

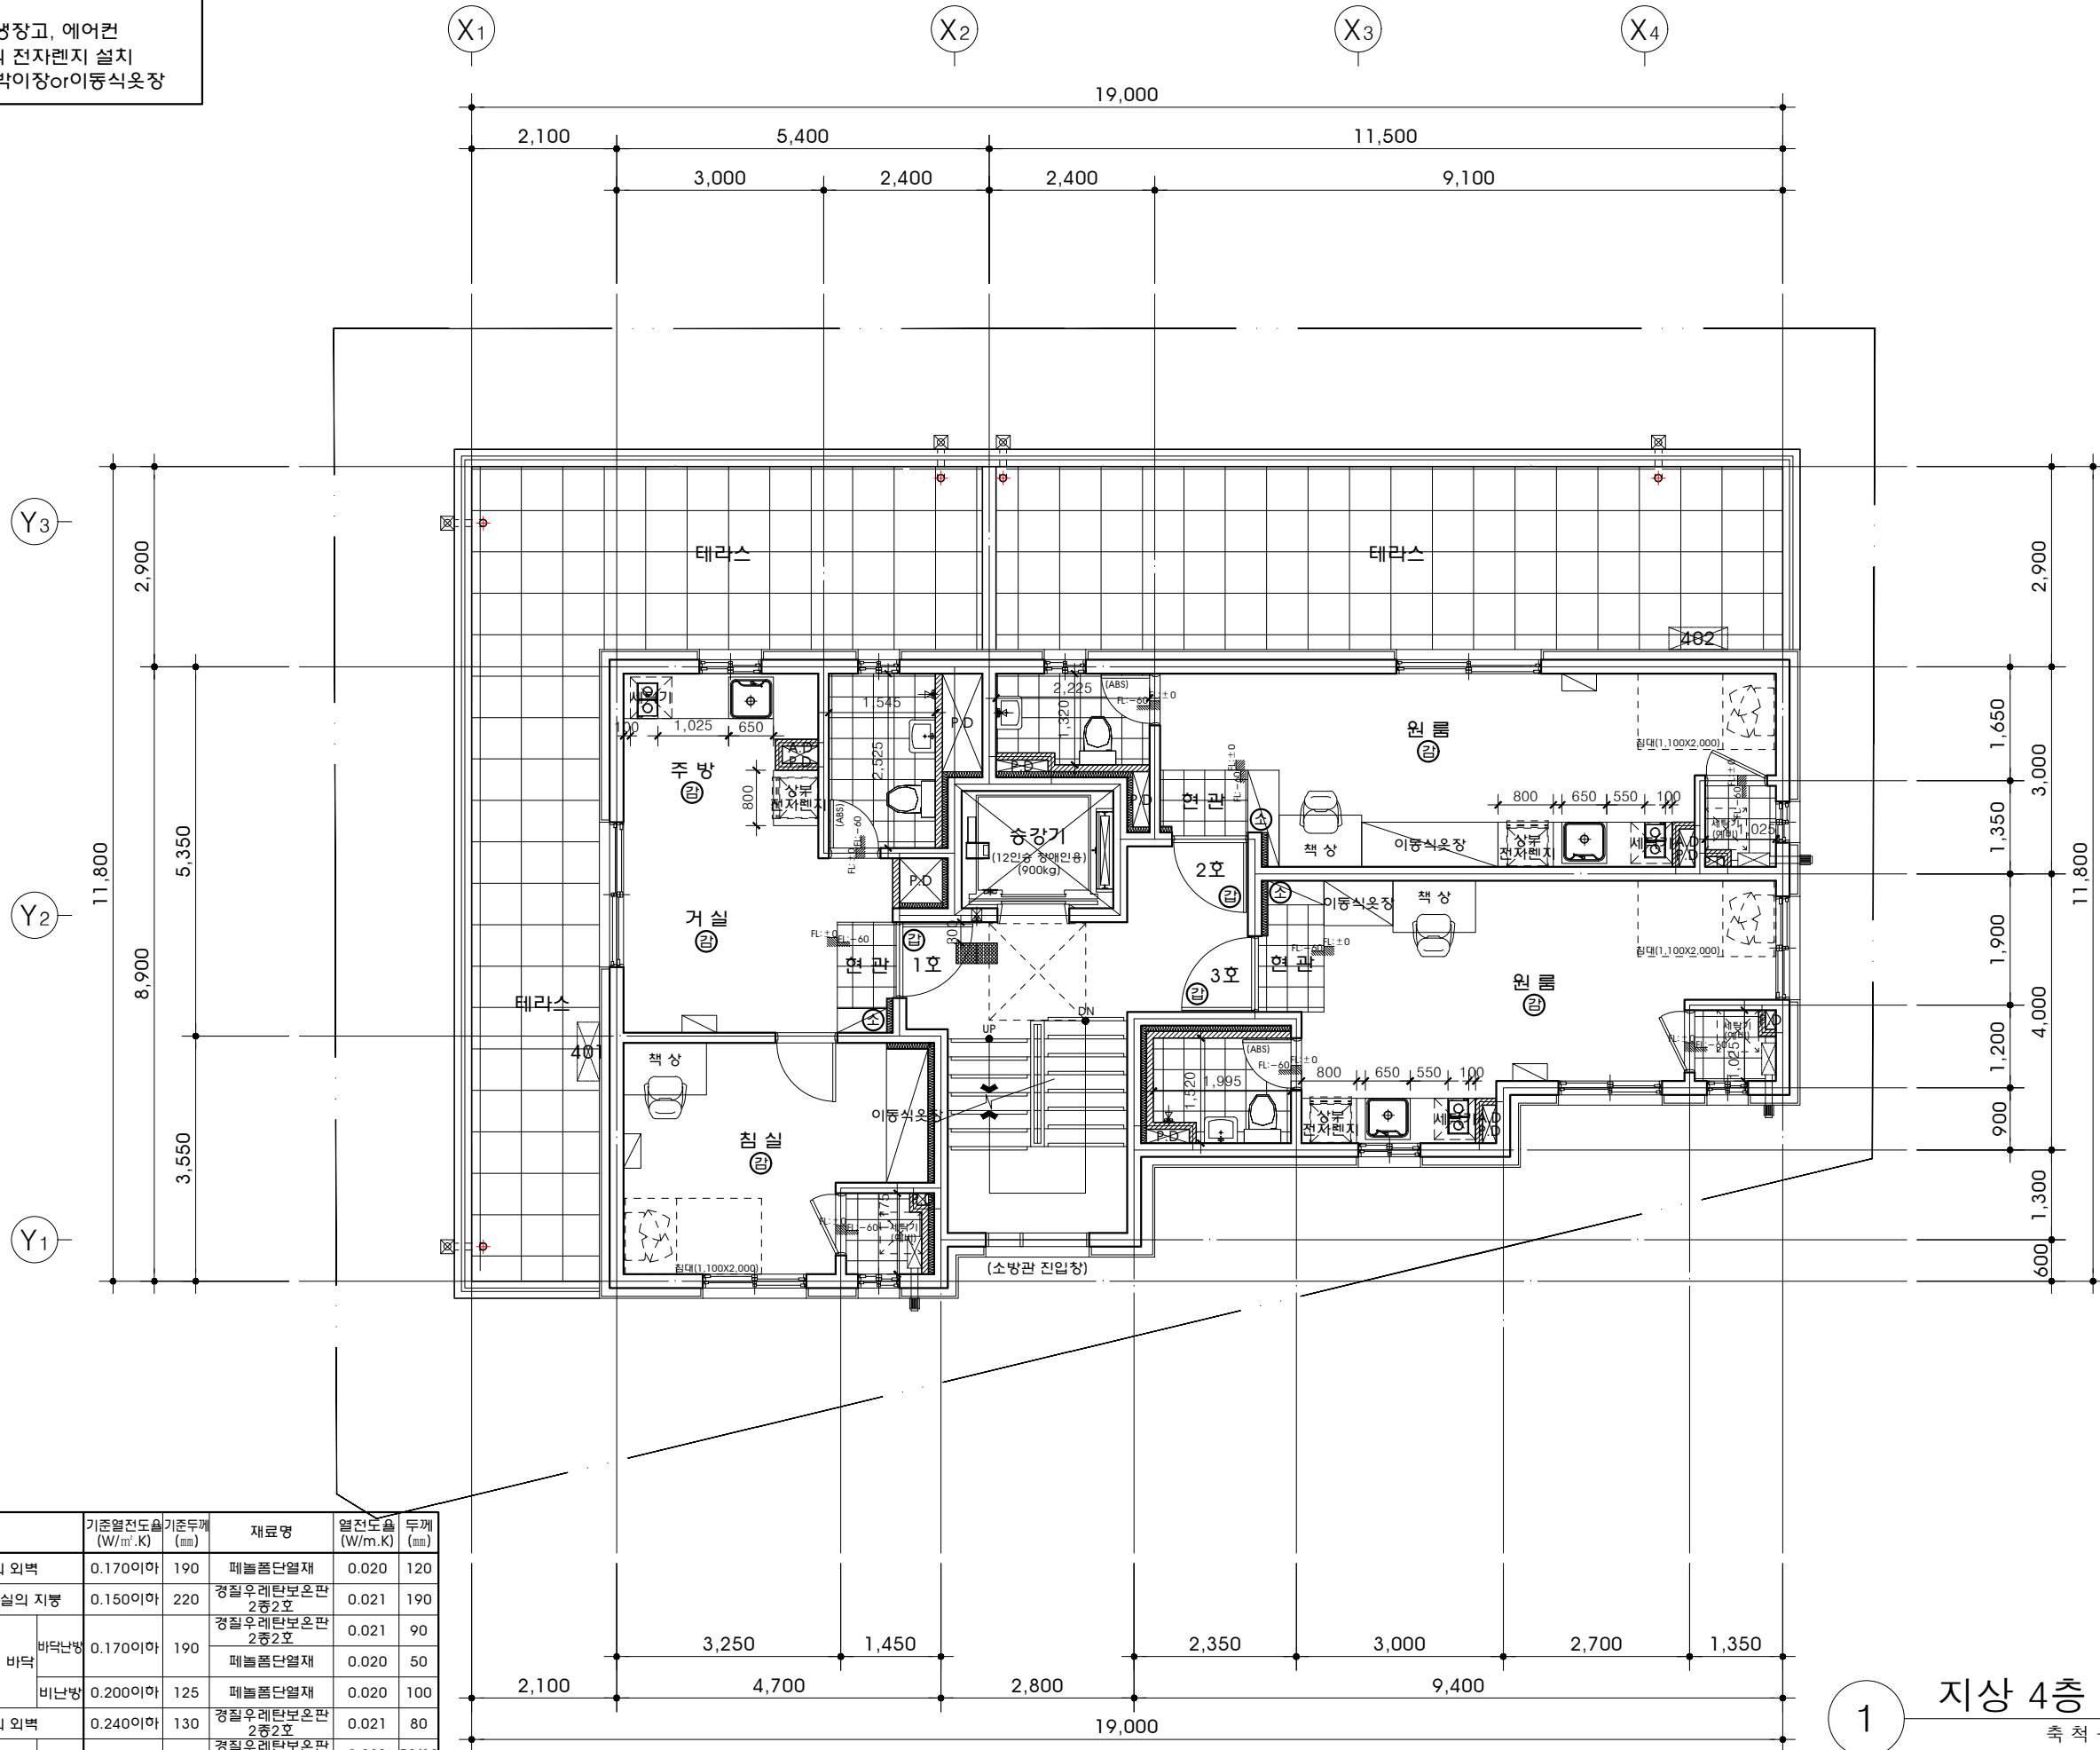

구 분		기준열전도율 (W/m ² .K)	기준두께 (mm)	재료명	열전도율 (W/m.K)	두께 (mm)
외기 직접	거실의 외벽	0.170이하	190	페놀폼단열재	0.020	120
	최상층 거실의 지붕	0.150이하	220	경질우레탄보온판 2중2호	0.021	190
	최하층 거실의 바닥	비단난방	0.170이하	경질우레탄보온판 2중2호	0.021	90
				페놀폼단열재	0.020	50
		비난방	0.200이하	페놀폼단열재	0.020	100
외기 간접	거실의 외벽	0.240이하	130	경질우레탄보온판 2중2호	0.021	80
	최하층 거실의 바닥	비단난방	0.240이하	경질우레탄보온판 2중2호	0.021	50/20
				비드법보온판 완충재	0.031	30
		비난방	0.290이하	경질우레탄보온판 2중2호	0.021	70

1

지상 4층 평면도

축척 - A3 : 1/100

사업명칭
PROJECT TITLE

강동구 성내동 521-3, 14번지
도시형생활주택
(청년주택)신축공사

사업번호
PROJECT NO.

NOTE

- Ⓢ

단독경보감지기
- Ⓢ

ABC분말소화기(3.3KG)
- Ⓢ

60분+ 방화문, 60분 방화문

Ⓢ

보일러

Ⓢ

에어컨

Ⓢ

실외기

차면시설

- *기둥 주위에 차량 보호대 설치
- *각세대 거실난간 국기꽃이 설치
- *승강기에 면한 침실 및 거실,
주방 방진패드 설치

* 구 조 *

1.콘크리트: fck = 27 MPa

2.철근 : fy = 400 MPa

3.세대벽두께:200mm(북배근)

4.세대내벽두께:150mm(북배근)

5.외벽두께:200mm(북배근)

6.코아벽두께:200mm(북배근)

7.스라브두께:210mm(3~5층)

8.스라브두께:180mm(2층,지붕)

9.세대현관문 규격 (틀포함)

1100x2200

ISSUES & REVISIONS

7		
6		
5		
4		
3		
2		
1		
NO.	DATE	REVISION

제도
DRAWN BY

전유구

심사
CHECKED BY

정우열

승인
APPROVED BY

김재형

도면명
NAME OF DRAWING

지상 4층 평면도

일자
DATE

2024. 10.

축척
SCALE

A3: 1/100

건축사사무소

에코플랜

Total Architecture


Engineers Group

서울특별시 송파구 삼학사로 25-1
신영빌딩 2층 (삼전동 182-4)
TEL: (02)418-7902 / FAX: (02)418-7907
E-mail: ecoplan01@hanmail.net

도면번호
SHEET NO.

A-104

- * NOTE
- 빌트인
- 세탁기, 냉장고, 에어컨
- 냉장고 위 전자렌지 설치
- 책상, 불박이장이이동식옷장

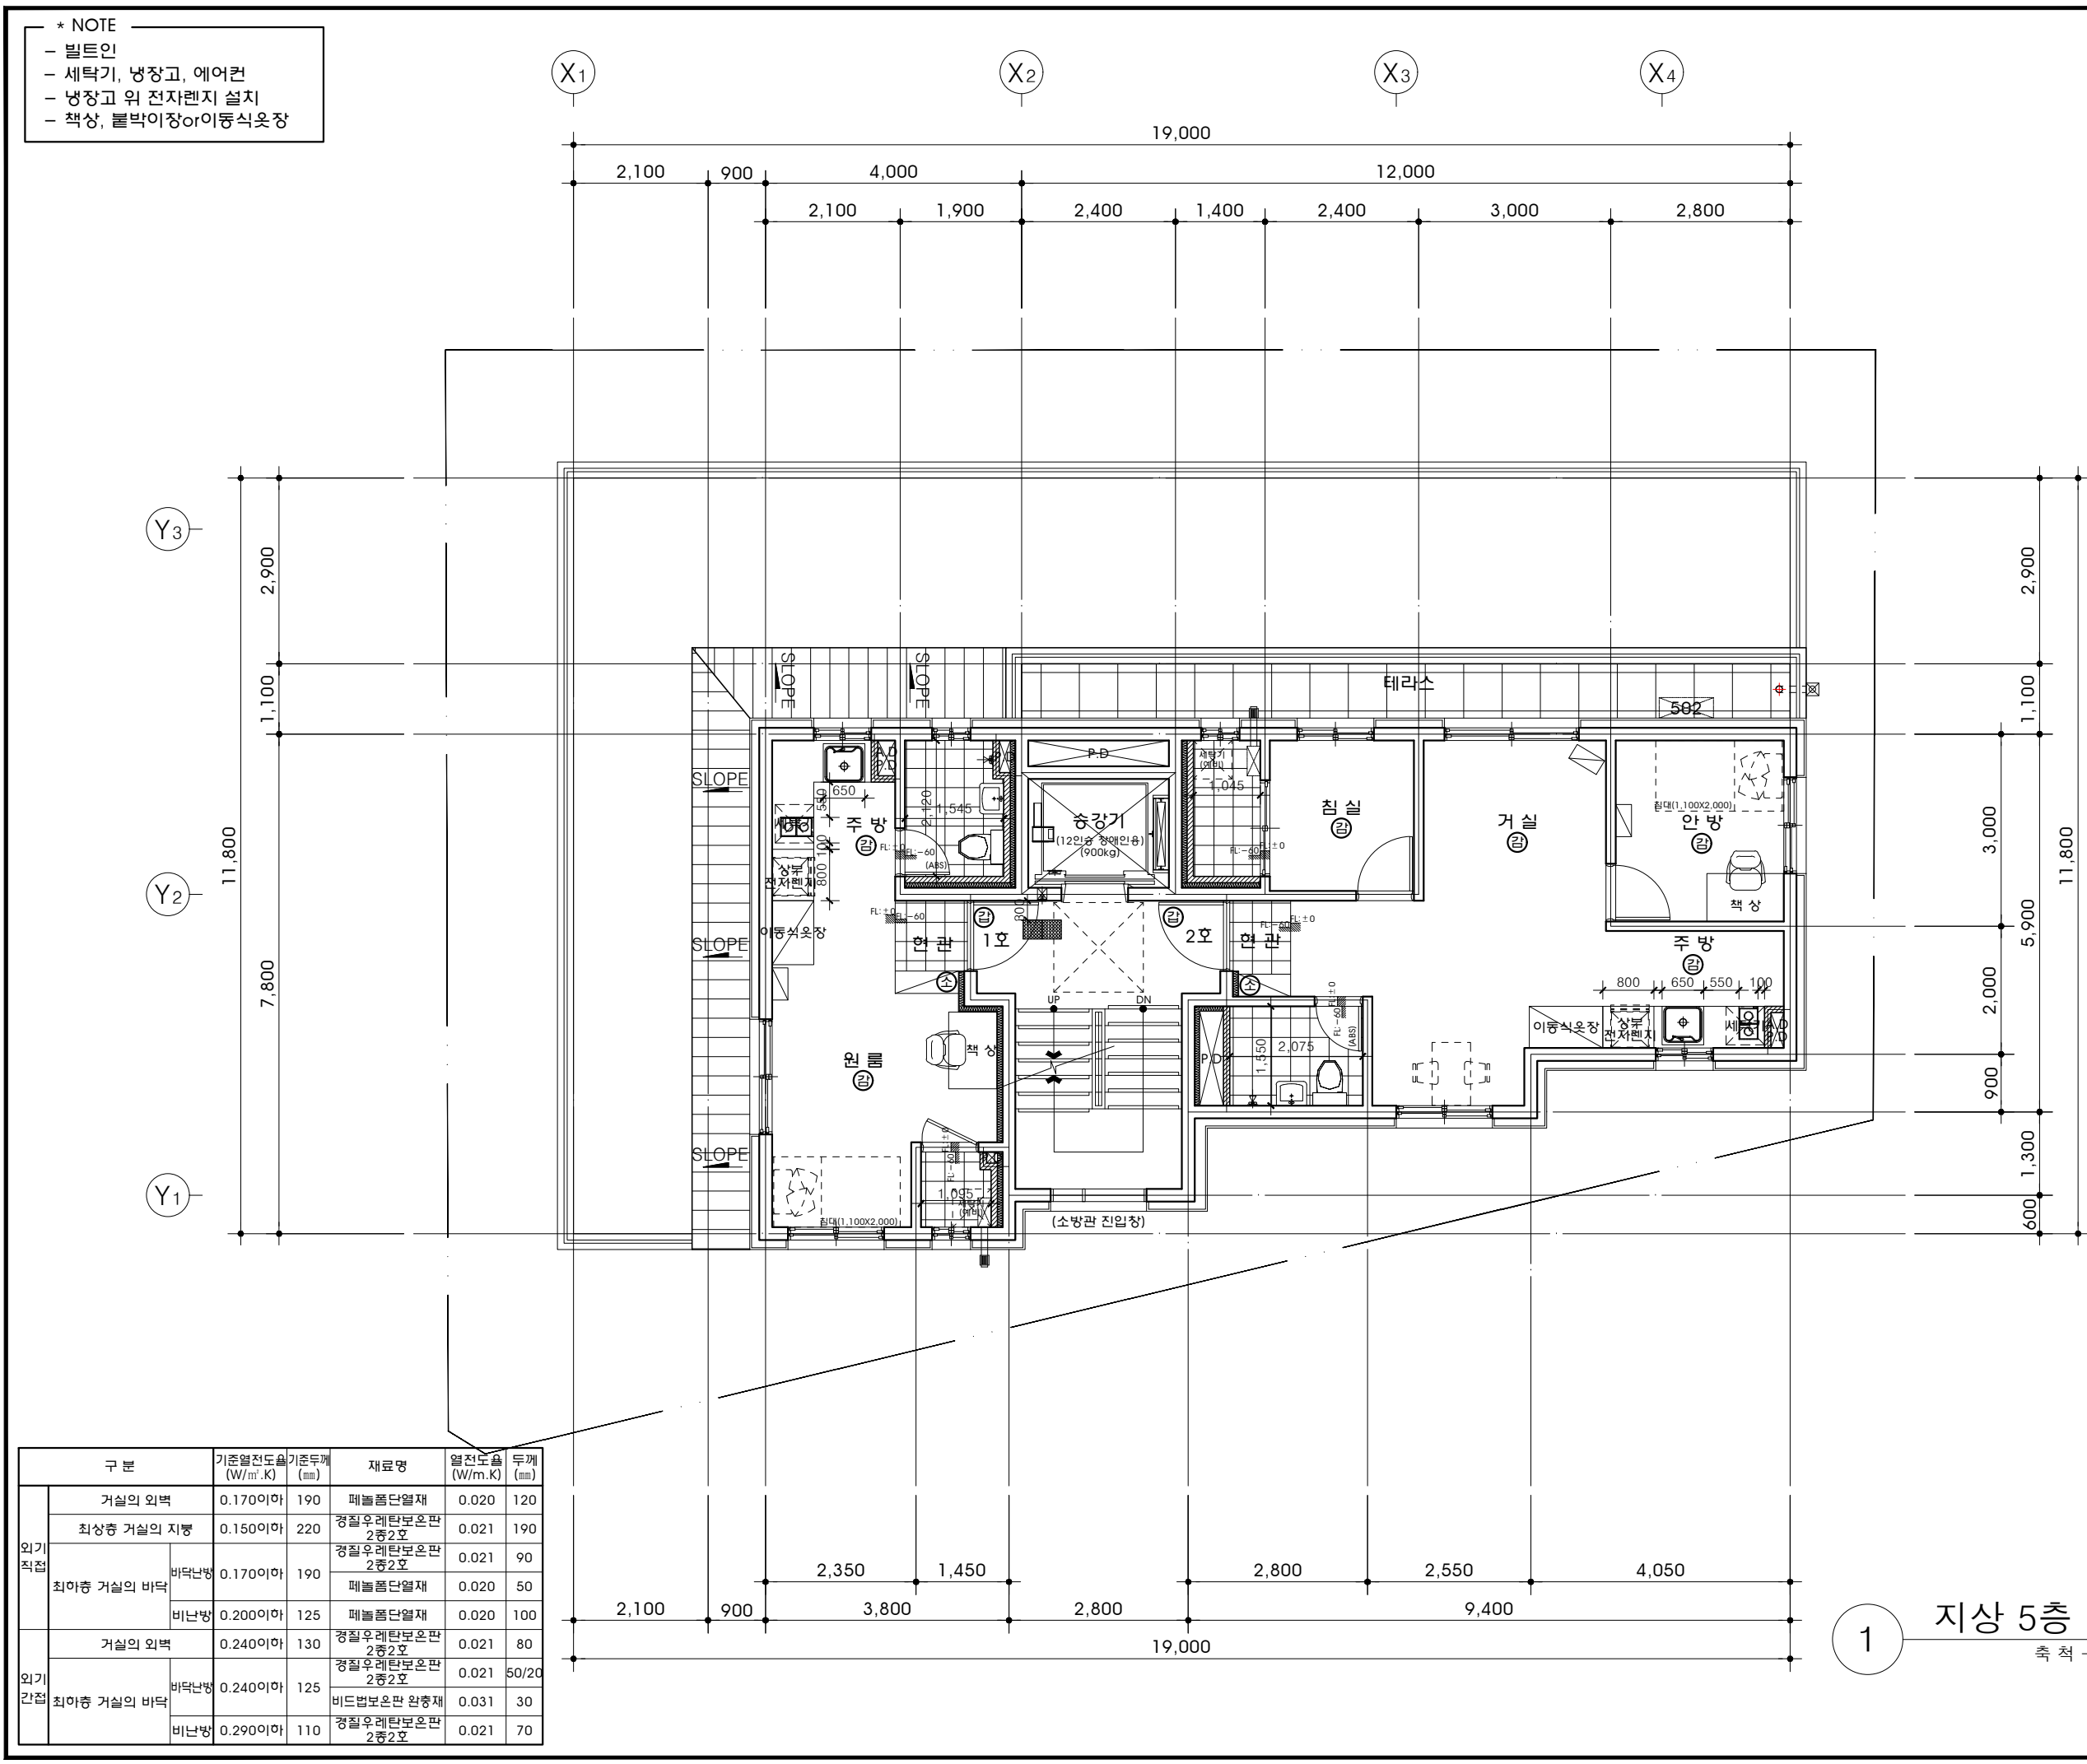

사업명칭
PROJECT TITLE

강동구 성내동 521-3,14번지
도시형생활주택
(청년주택)신축공사

사업번호
PROJECT NO.

NOTE

- Ⓢ

단독경보감지기
- Ⓢ

ABC분말소화기(3.3KG)
- Ⓢ

60분+ 방화문, 60분 방화문

☐

보일러

☐

에어컨

☐

실외기

차면시설

- *기둥 주위에 차량 보호대 설치
- *각세대 거실난간 국기꽃이 설치
- *승강기에 면한 침실 및 거실,
주방 방진패드 설치

* 구 조 *

1.콘크리트: fck = 27 MPa

2.철근 : fy = 400 MPa

3.세대벽두께:200mm(북배근)

4.세대내벽두께:150mm(북배근)

5.외벽두께:200mm(북배근)

6.코아벽두께:200mm(북배근)

7.스라브두께:210mm(3~5층)

8.스라브두께:180mm(2층,지붕)

9.세대현관문 규격 (틀포함)

1100x2200

ISSUES & REVISIONS

7		
6		
5		
4		
3		
2		
1		
NO.	DATE	REVISION

제도
DRAWN BY

전유구

심사
CHECKED BY

정우열

승인
APPROVED BY

김재형

도면명
NAME OF DRAWING

지상 5층 평면도

일자
DATE

2024. 10.

축척
SCALE

A3: 1/100

건축사무소

에코플랜

Total Architecture

Engineers Group

서울특별시 송파구 삼학사로 25-1

신영빌딩 2층 (삼전동 182-4)

TEL: (02)418-7902 / FAX: (02)418-7907


E-mail: ecoplan01@hanmail.net

도면번호
SHEET NO.

A-105

* NOTE

- 발트인
- 세탁기, 냉장고, 에어컨
- 냉장고 위 전자렌지 설치
- 책상, 불박이장이동식옷장

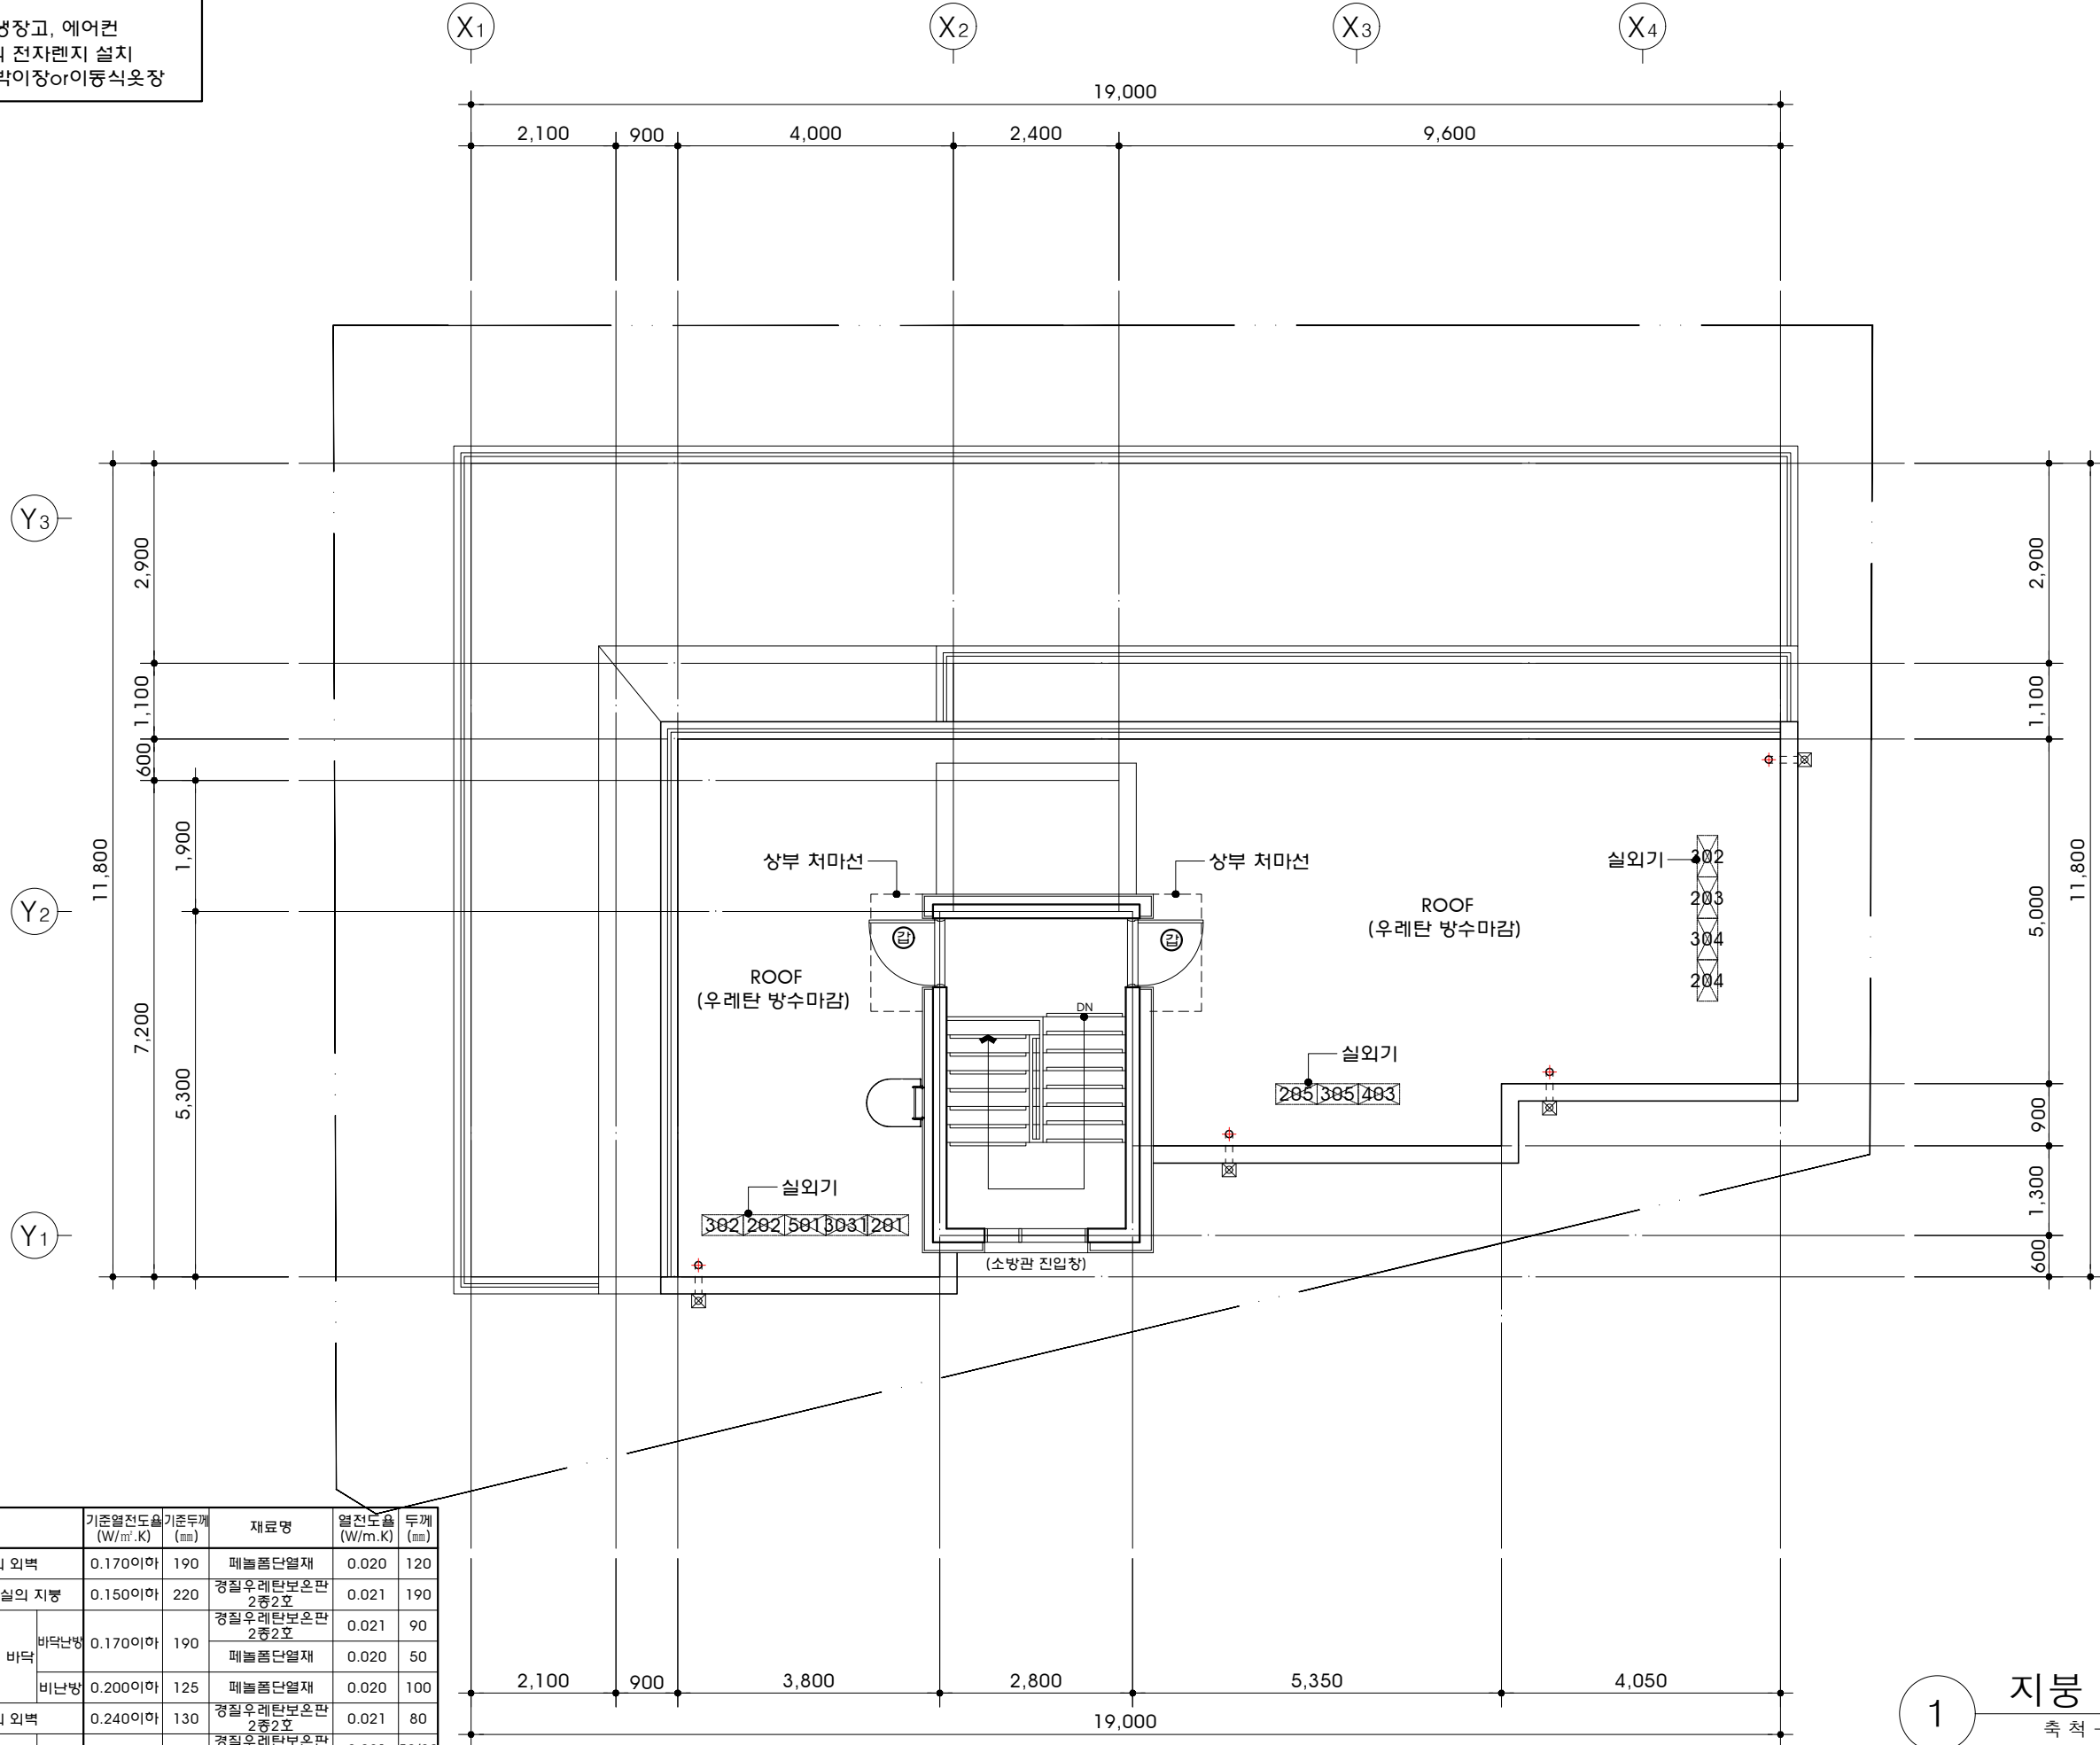

구 분		기준열전도율 (W/m ² .K)	기준두께 (mm)	재료명	열전도율 (W/m.K)	두께 (mm)
외기 직접	거실의 외벽	0.170이하	190	페놀폼단열재	0.020	120
	최상층 거실의 지붕	0.150이하	220	경질우레탄보온판 2중2호	0.021	190
	최하층 거실의 바닥	비단난방	0.170이하	경질우레탄보온판 2중2호	0.021	90
				페놀폼단열재	0.020	50
		비난방	0.200이하	페놀폼단열재	0.020	100
외기 간접	거실의 외벽	0.240이하	130	경질우레탄보온판 2중2호	0.021	80
	최하층 거실의 바닥	비단난방	0.240이하	경질우레탄보온판 2중2호	0.021	50/20
				비드법보온판 완충재	0.031	30
		비난방	0.290이하	경질우레탄보온판 2중2호	0.021	70

1 지붕 평면도
축척 - A3 : 1/100



사업명칭
PROJECT TITLE
강동구 성내동 521-3, 14번지
도시형생활주택
(청년주택)신축공사

사업번호
PROJECT NO.
NOTE

- 단독경보감지기
- ABC분말소화기(3.3KG)
- 60분+ 방화문, 60분 방화문
- 보일러
- 에어컨
- 실외기

차면시설
*기둥 주위에 차량 보호대 설치
*각세대 거실난간 국기꽃이 설치
*승강기에 면한 침실 및 거실,
주방 방진패드 설치
* 구 조 *

- 콘크리트: fck = 27 MPa
- 철근: fy = 400 MPa
- 세대벽두께: 200mm(복배근)
- 세대내벽두께: 150mm(복배근)
- 외벽두께: 200mm(복배근)
- 코아벽두께: 200mm(복배근)
- 스라브두께: 210mm(3~5층)
- 스라브두께: 180mm(2층, 지붕)

9.세대현관문 규격 (틀포함)
1100x2200

ISSUES & REVISIONS		
7		
6		
5		
4		
3		
2		
1		
NO.	DATE	REVISION

제도
DRAWN BY
전유구
심사
CHECKED BY
정우열
승인
APPROVED BY
김재형
도면명
NAME OF DRAWING

지붕 평면도

일자
DATE
2024. 10 .
축척
SCALE
A3: 1/100

건축사무소
에코플랜
Total Architecture
Engineers Group

서울특별시 송파구 삼학사로 25-1
신영빌딩 2층 (삼전동 182-4)
TEL: (02)418-7902 / FAX: (02)418-7907
E-mail: ecoplan01@hanmail.net


도면번호
SHEET NO.
A-106

- * NOTE
- 발트인

- 세탁기, 냉장고, 에어컨

- 냉장고 위 전자렌지 설치

- 책상, 불박이장아이동식옷장

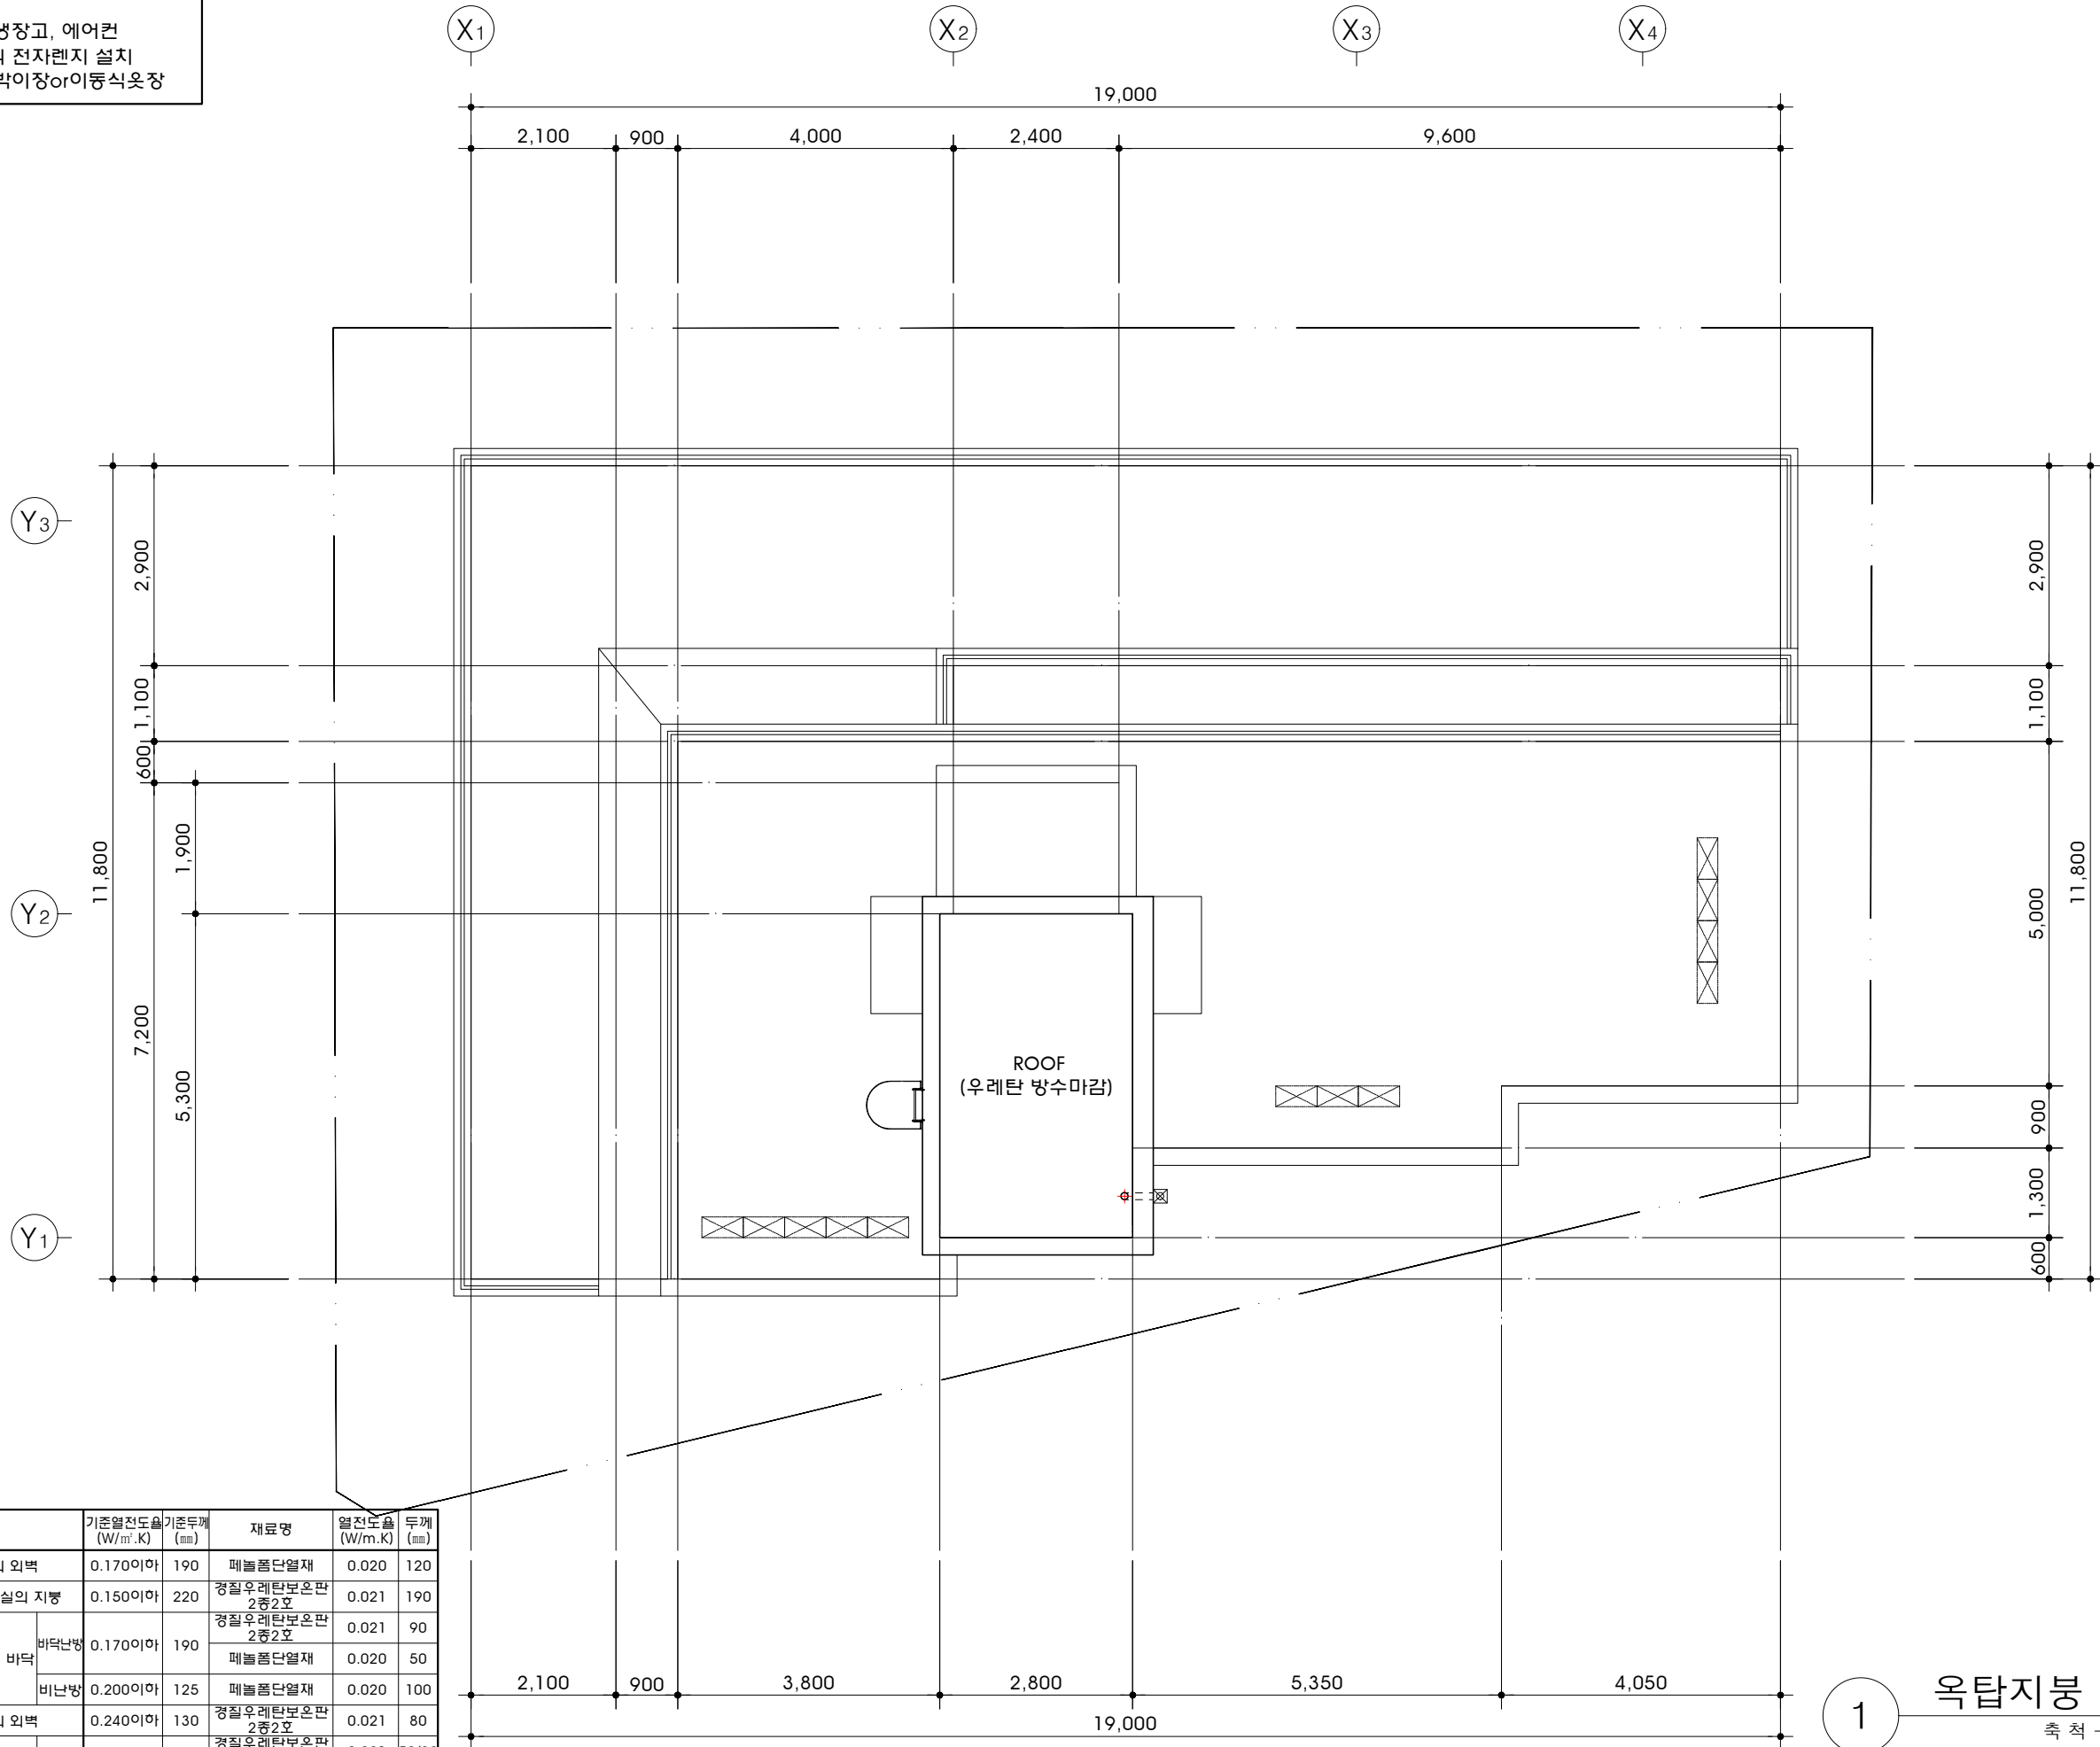

구 분		기준열전도율 (W/m ² .K)	기준두께 (mm)	재료명	열전도율 (W/m.K)	두께 (mm)
외기 직접	거실의 외벽	0.170이하	190	페놀폼단열재	0.020	120
	최상층 거실의 지붕	0.150이하	220	경질우레탄보온판 2중2호	0.021	190
	최하층 거실의 바닥	비단난방	0.170이하	경질우레탄보온판 2중2호	0.021	90
				페놀폼단열재	0.020	50
		비난방	0.200이하	페놀폼단열재	0.020	100
외기 간접	거실의 외벽	0.240이하	130	경질우레탄보온판 2중2호	0.021	80
	최하층 거실의 바닥	비단난방	0.240이하	경질우레탄보온판 2중2호	0.021	50/20
				비드법보온판 완충재	0.031	30
		비난방	0.290이하	경질우레탄보온판 2중2호	0.021	70



사업명칭
PROJECT TITLE

강동구 성내동 521-3,14번지
도시형생활주택
(청년주택)신축공사

사업번호
PROJECT NO.

NOTE

Ⓜ 단독경보감지기

Ⓢ ABC분말소화기(3.3KG)

Ⓜ 60분+ 방화문, 60분 방화문

☐ 보일러

☐ 에어컨

☐ 실외기

----- 차면시설

*기둥 주위에 차량 보호대 설치

*각세대 거실난간 국기꽃이 설치

*승강기에 면한 침실 및 거실,
주방 방진패드 설치

* 구 조 *

1.콘크리트: fck = 27 MPa

2.철근 : fy = 400 MPa

3.세대벽두께:200mm(복배근)

4.세대내벽두께:150mm(복배근)

5.외벽두께:200mm(복배근)

6.코아벽두께:200mm(복배근)

7.스라브두께:210mm(3~5층)

8.스라브두께:180mm(2층,지붕)

9.세대현관문 규격 (틀포함)
1100x2200

ISSUES & REVISIONS

7		
6		
5		
4		
3		
2		
1		
NO.	DATE	REVISION

제도
DRAWN BY

전유구

심사
CHECKED BY

정우열

승인
APPROVED BY

김재형

도면명
NAME OF DRAWING

옥탑지붕 평면도

일자
DATE

2024. 10 .

축척
SCALE

A3: 1/100

건축사무소


에코플랜

Total Architecture
Engineers Group

서울특별시 송파구 삼학사로 25-1
신영빌딩 2층 (삼전동 182-4)
TEL: (02)418-7902 / FAX: (02)418-7907
E-mail: ecoplan01@hanmail.net

도면번호
SHEET NO.


A-107

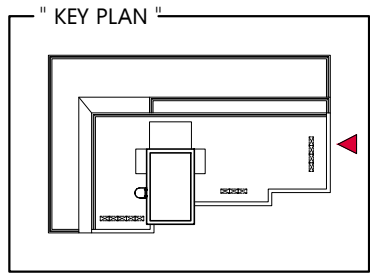

Y1

Y2


Y3

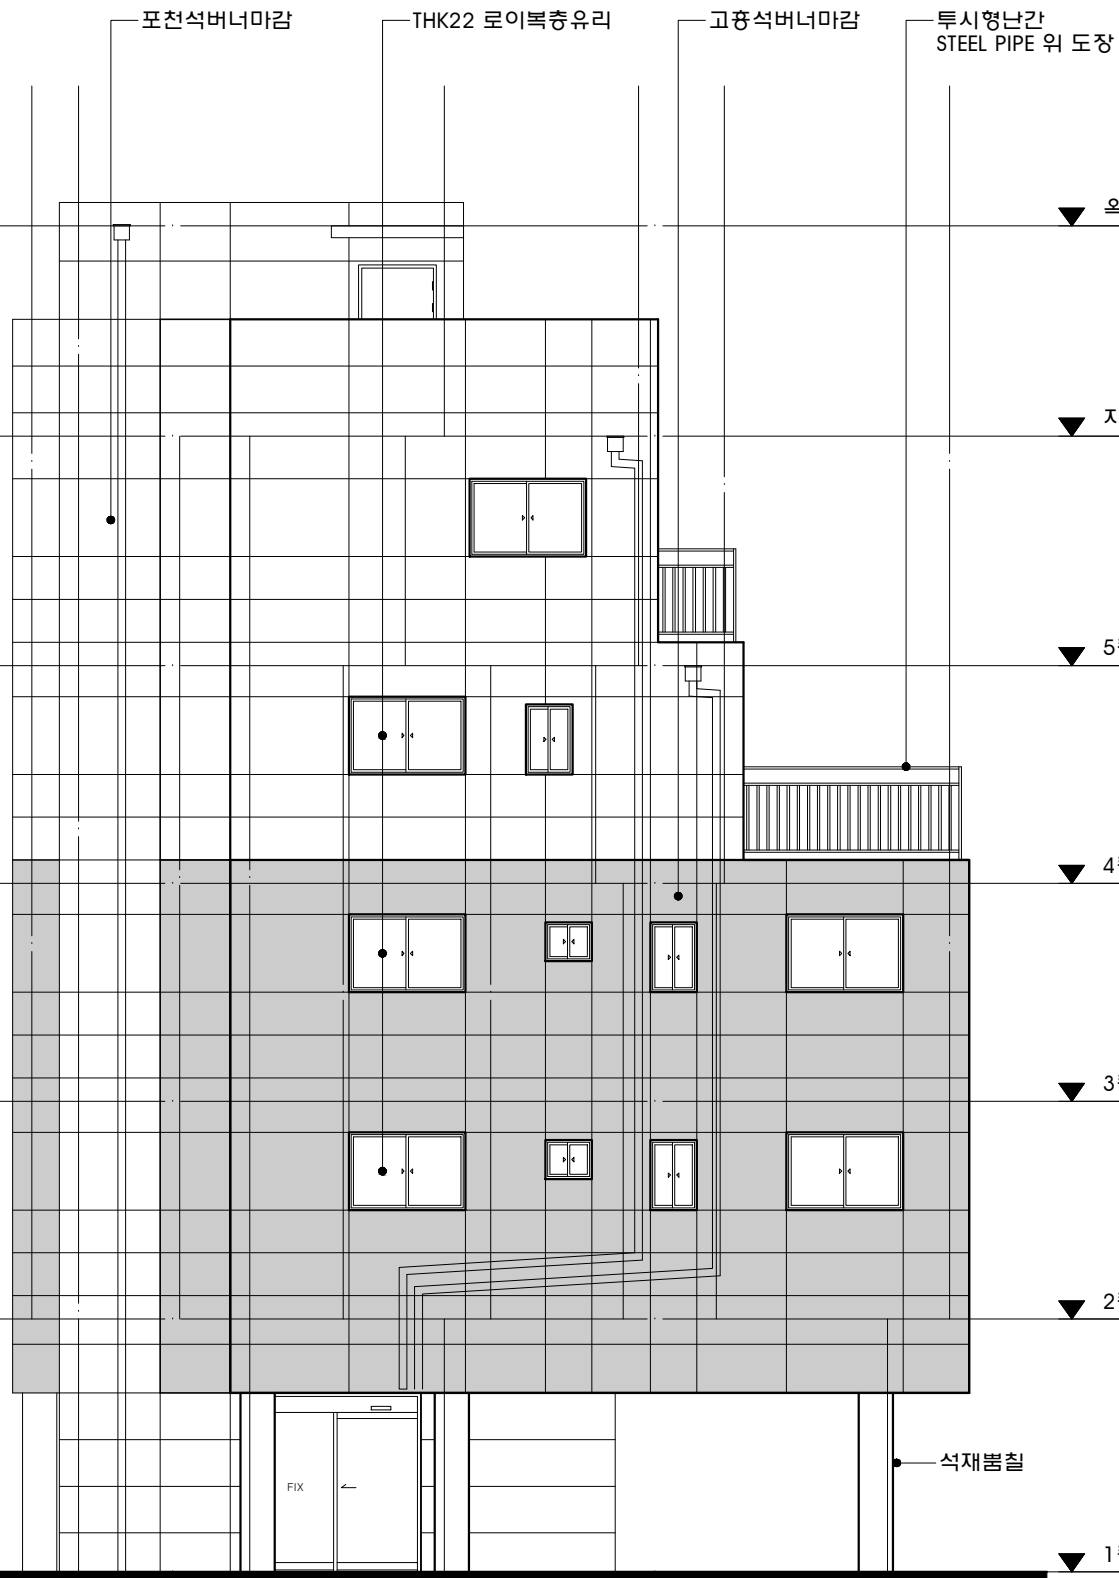

1

정면도


축척 - A3 : 1/100

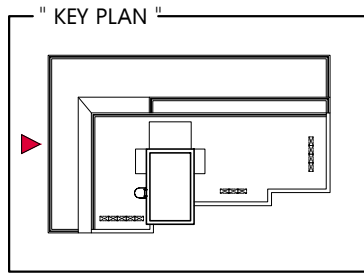

Y3

Y2

Y1


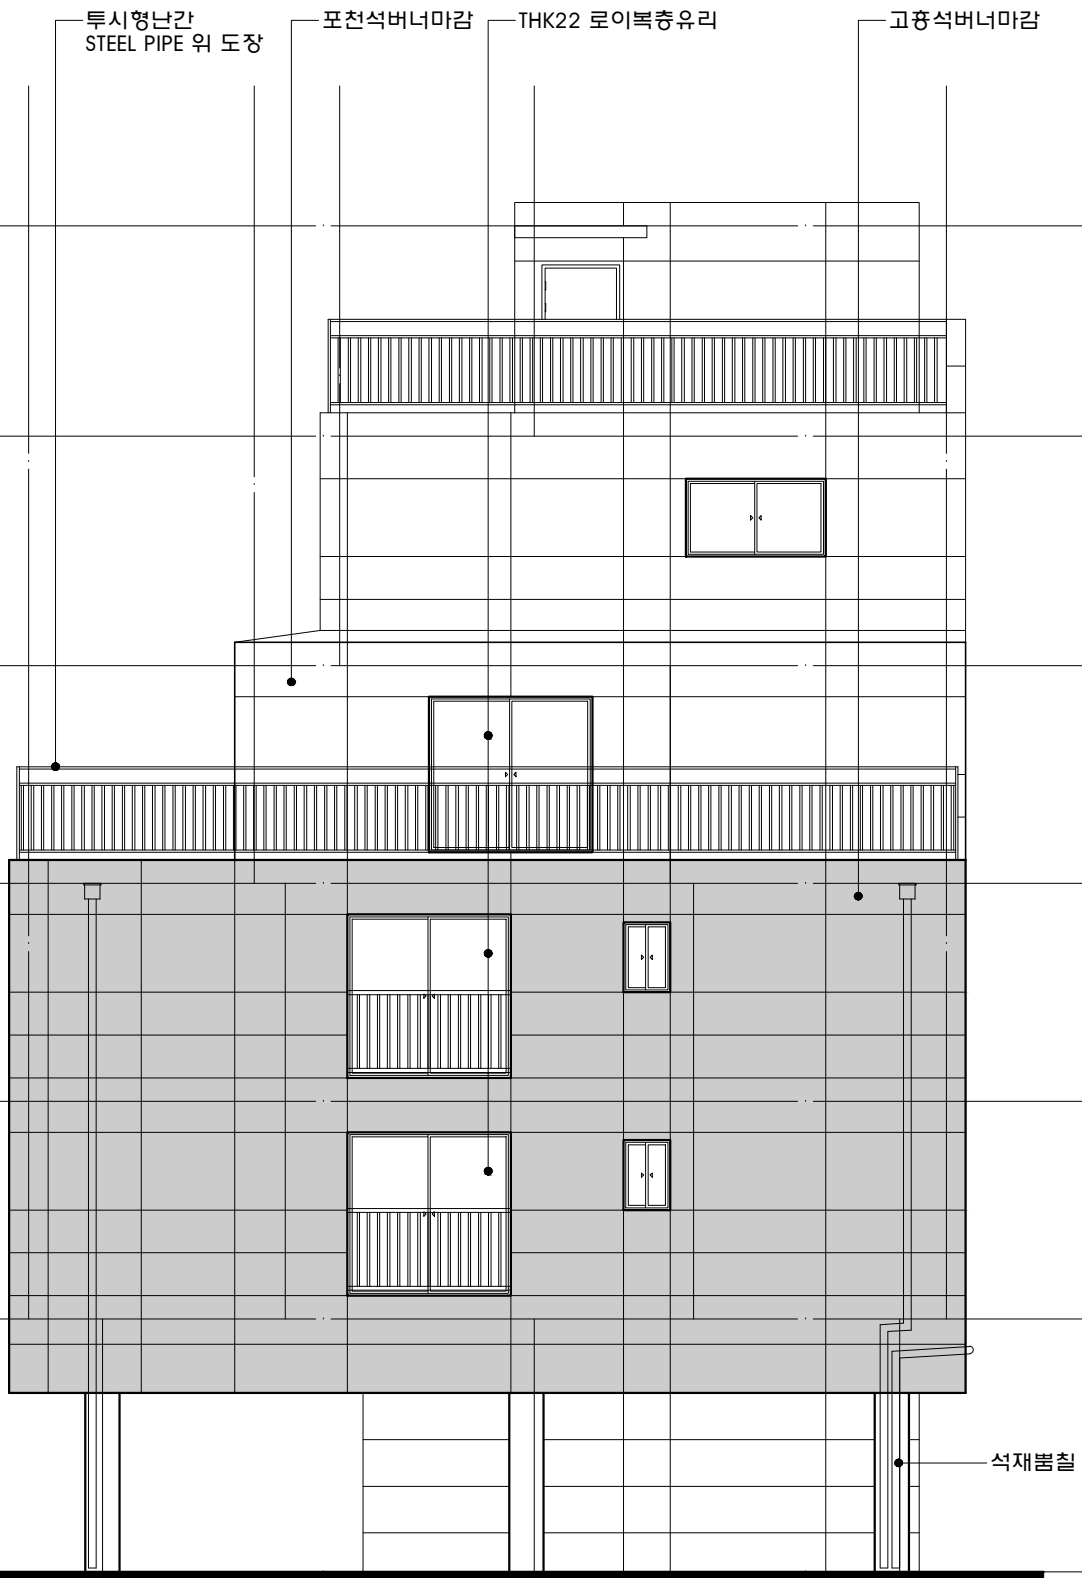


2

배면도

축척 - A3 : 1/100

7		
6		
5		
4		
3		
2		
1		
NO.	DATE	REVISION

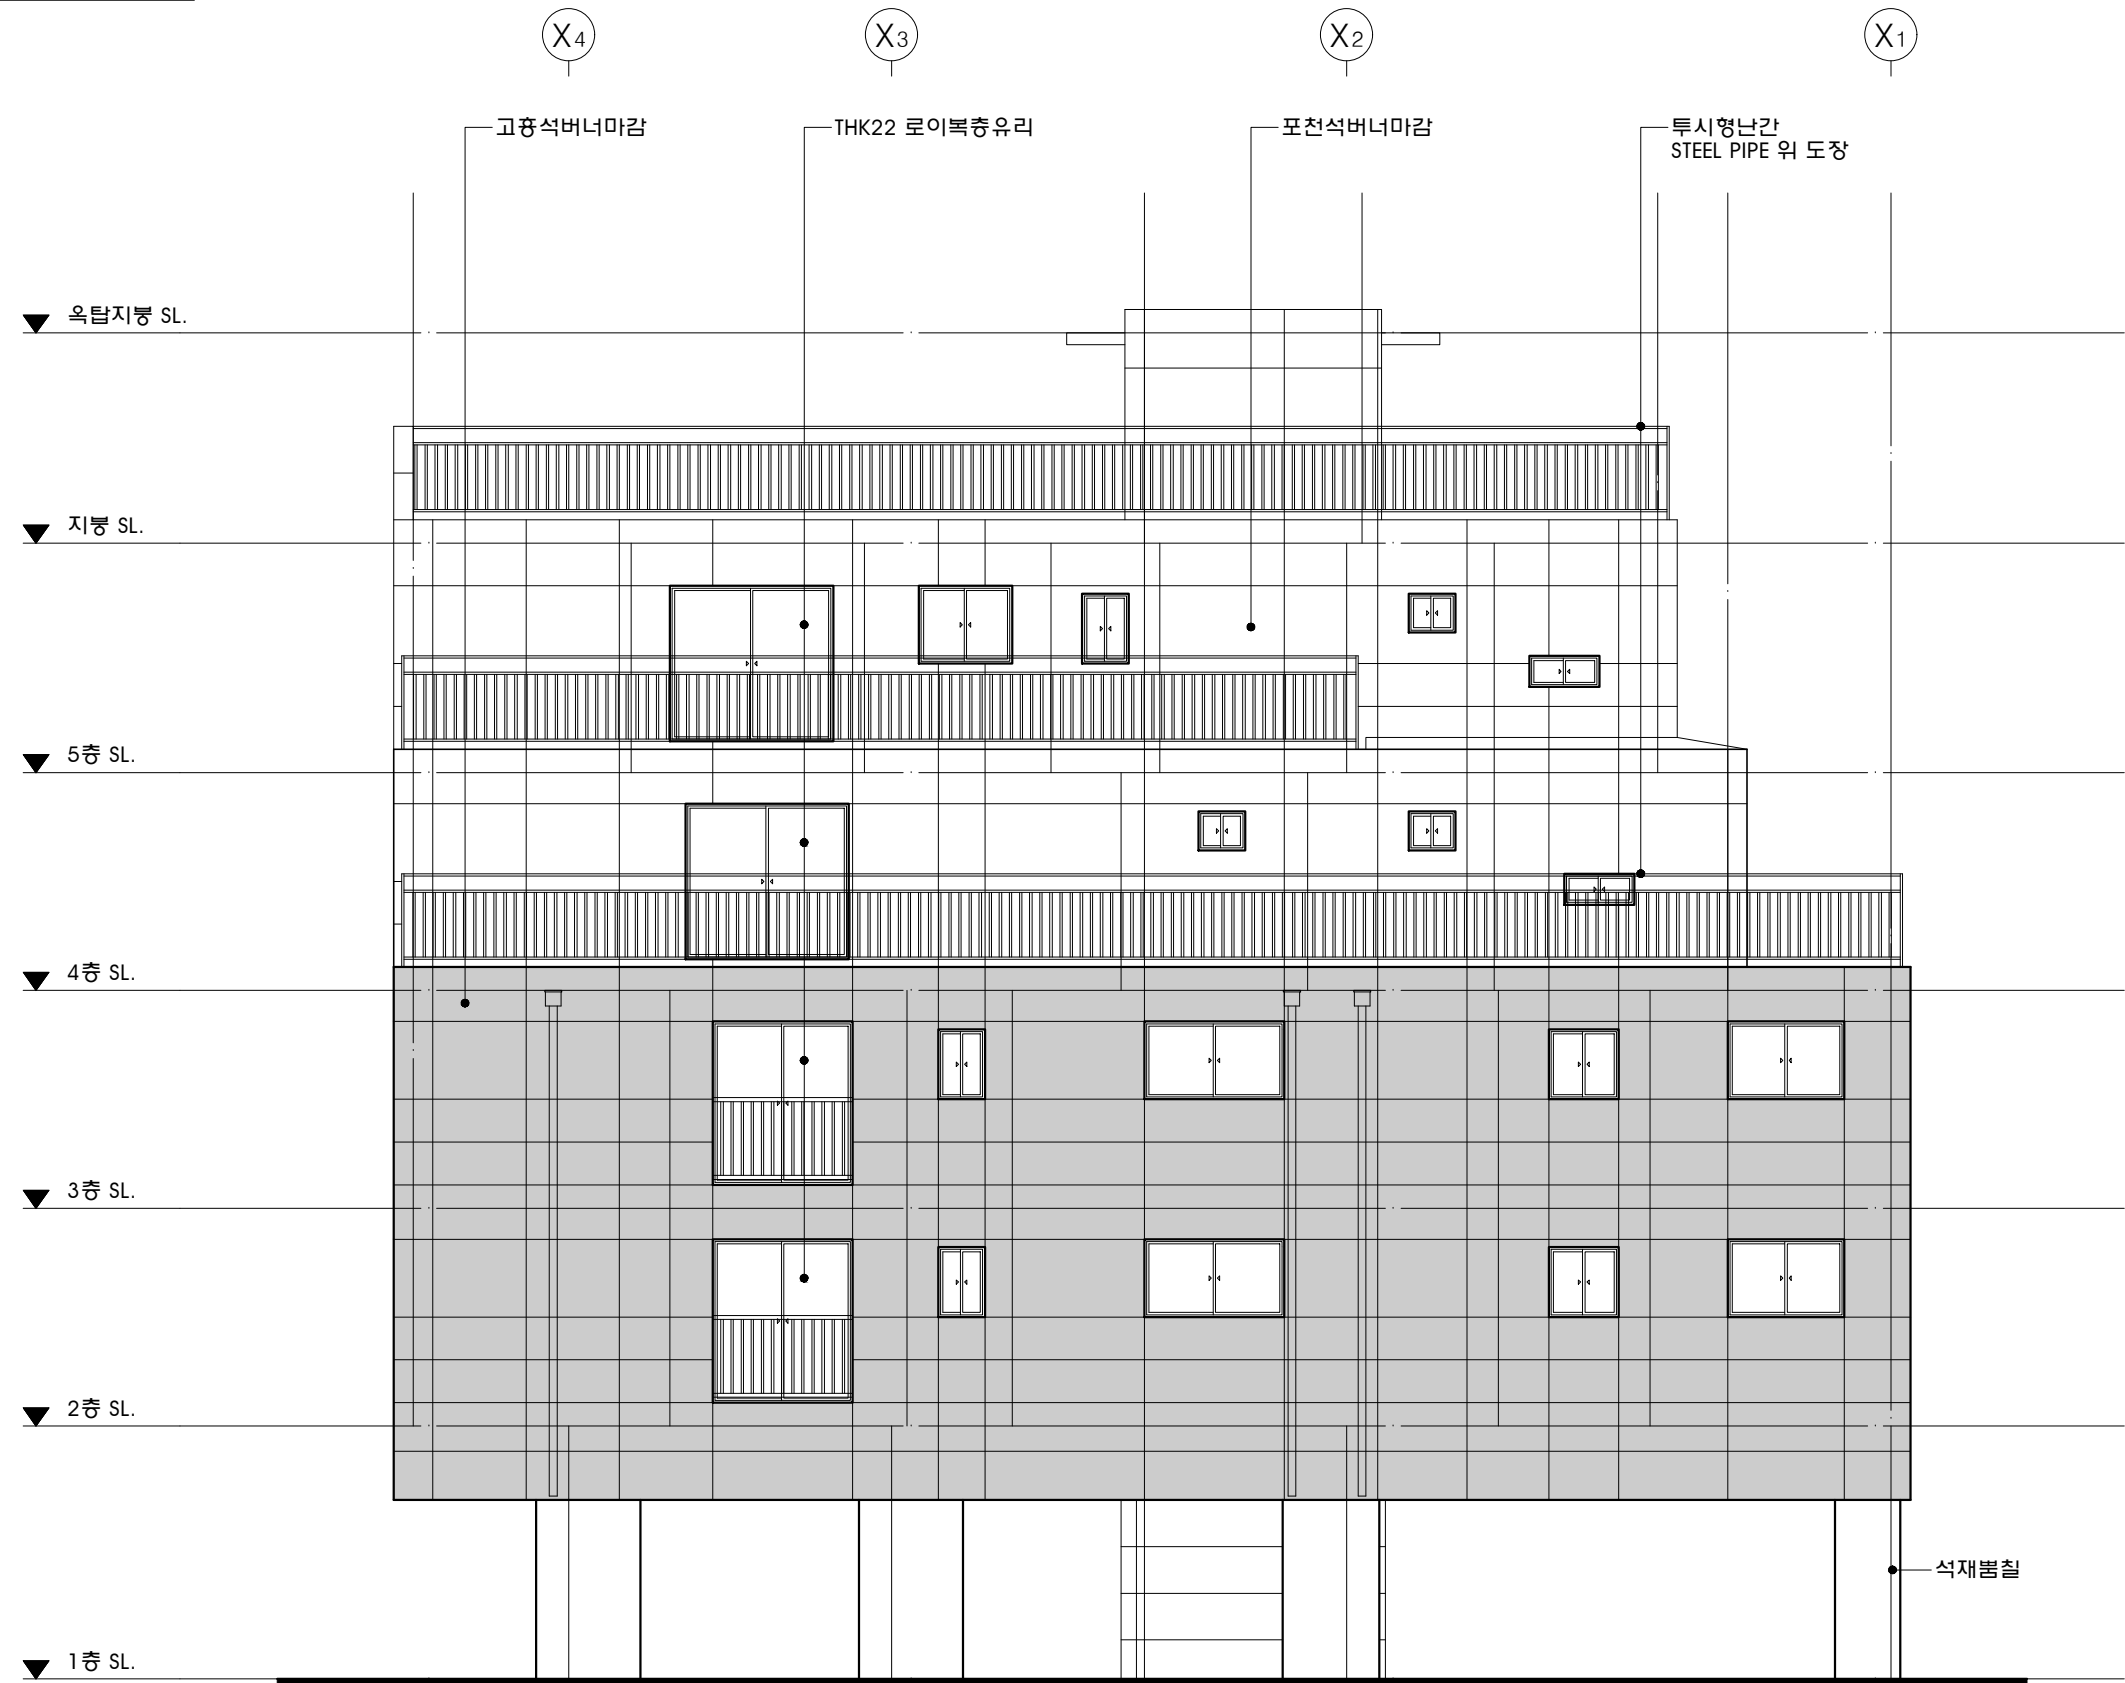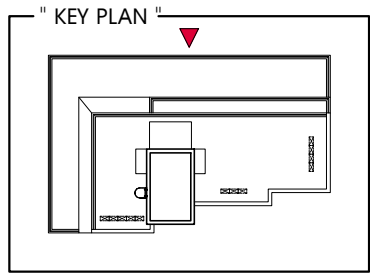

1 우측면도
축척 - A3 : 1/100

ISSUES & REVISIONS		
7		
6		
5		
4		
3		
2		
1		
NO.	DATE	REVISION

제도
DRAWN BY
전유구

심사
CHECKED BY
정우열

승인
APPROVED BY
김재형

도면명
NAME OF DRAWING

우측면도

일자
DATE
2024. 10 .



축척
SCALE
A3: 1/100

건축사사무소
에코플랜
Total Architecture
&
Engineers Group

서울특별시 송파구 삼학사로 25-1
신영빌딩 2층 (삼전동 182-4)
TEL: (02)418-7902 / FAX: (02)418-7907
E-mail: ecoplan01@hanmail.net

도면번호
SHEET NO.

A-202

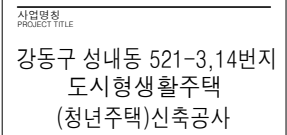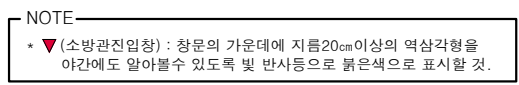

사업번호
PROJECT NO

NOTE

ISSUES & REVISIONS		
7		
6		
5		
4		
3		
2		
1		
NO.	DATE	REVISION

제도
DRAWN BY 전유구

심사
CHECKED BY 정우열

승인
APPROVED BY 김재형

NAME OF DRAWING

좌측면도

일자
DATE 2024. 10

축척
SCALE A3: 1/100

건축사사무소
에코플랜
Total Architecture
&
Engineers Group

서울특별시 송파구 삼학사로 25-1
신영빌딩 2층 (삼전동 182-4)
TEL: (02) 418-7902 / FAX: (02) 418-7907
E-mail: ecoplan01@hanmail.net

도면번호
SHEET NO.

A-203

