
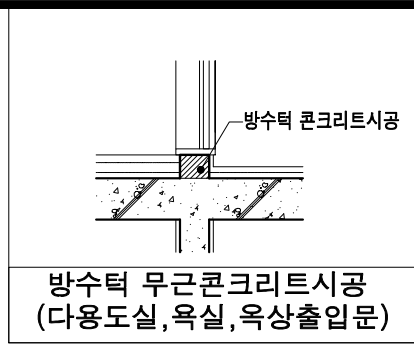


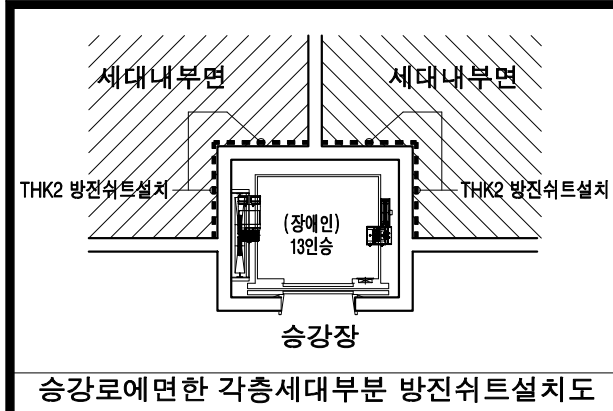

PROJECT TITLE
사업명칭

미아동214-70,71
도시형생활주택
(단지형다세대)신축공사

사업번호 PROJECT NO.
도면명

2024-1004

NOTE

- ⑧ 단독경보감지기(연기식)
⑨ 단독경보감지기(열감지)
㉔ ABC분말소화기(3.3KG)
㉕ 가스누설경보기

차면시설
보일러
에어컨 실외기
* 구조 *

1. 냉장고
2. 벽걸이 에어컨(거실&주방)
(침실 : 에어컨 배관설치)
3. 세탁기(싱크대 하부설치)
4. 전자레인지(냉장고 상부설치)
에너지효율등급 상위 제품 우선 적용
(제품생산현황 등에 따른 사전협의 가능)
5. 불박이장 (W:900이상)
- * 주의사항
매입임대주택 품질기준
도면: A-021~034 참조할것.
1. 콘크리트: fck = 24 MPa
2. 철근: fy = 400 MPa
3. 세대간벽두께: 180mm(복배근)
(미장마감포함 210mm이상)
4. 외벽두께: 180mm(복배근)
5. 코아벽두께: 180mm(복배근)
6. 스라브두께: 210mm(복배근)

NO. ▲ REVISIONS ▲ DATE
번호 수정 일자

DESIGNED BY
설계

CHECKED BY
심사

APPROVED BY
승인

CONSULTANTS
협동설계

SCALE
축척

1/100

DATE
일자

2024. 05 .

DWG NO.
도면번호

A-303



NAME OF DRAWING
도면명

2,3층 평면도

(주)에이이플러스
건축사무소
Architecture + Environment
AE+
TEL. 02 - 745 - 8511
FAX. 0505-070-6511



2,3층 평면도
SCALE : 1/100

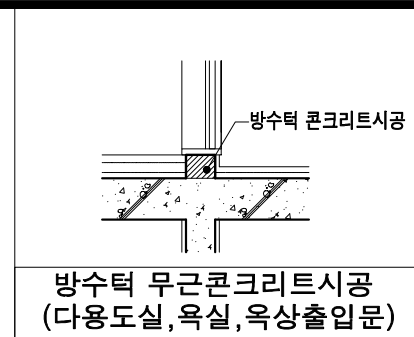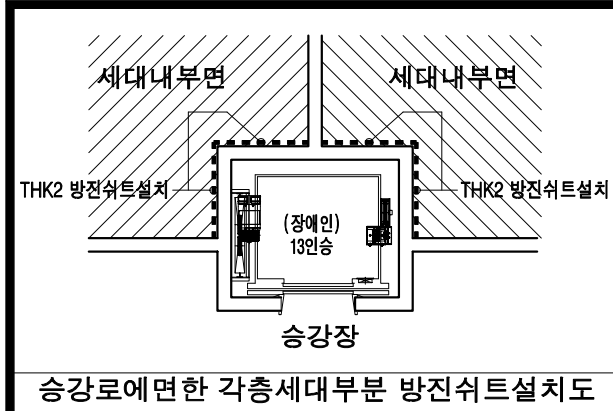

- 주방및 가구등 빌트인
- 청년주택 :
- 1.냉장고
 - 2.벽걸이 에어컨(거실&주방)
(침실 : 에어컨 배관설치)
 - 3.세탁기(싱크대 하부설치)
 - 4.전자레인지(냉장고 상부설치)
- 에너지효율등급 상위 제품 우선 적용
(제품생산현황 등에 따른 사전협의 가능)
- 5.불박이장 (W:900이상)
- * 주의사항 *
- 매입임대주택 품질기준
도면: A-021~034 참조할것.

PROJECT TITLE
사업명칭

미아동214-70,71
도시형생활주택
(단지형다세대)신축공사

사업번호 PROJECT NO.
도면명

2024-1004

NOTE

- ⑧ 단속경보감지기(연기식)
- ⑨ 단속경보감지기(열감지)
- ③ ABC분말소화기(3.3KG)
- ④ 가스누설경보기

차면시설

- 보일러
- 에어컨 실외기

* 구 조 *

- 1.콘크리트: fck = 24 MPa
- 2. 철근: fy = 400 MPa
- 3. 세대간벽두께:180mm(복배근)
- (미장마감포함 210mm이상)
- 4. 외벽두께:180mm(복배근)
- 5. 코아벽두께:180mm(복배근)
- 6. 스라브두께:210mm(복배근)

NO. 번호	REVISIONS 수정	DATE 일자
-----------	-----------------	------------

DESIGNED BY
설계

CHECKED BY
심사

APPROVED BY
승인

CONSULTANTS
협동설계

SCALE
축척

1/100

DATE
일자

2024. 05 .

DWG NO.
도면번호

A-304


NAME OF DRAWING
도면명

4층 평면도

(주)에이이플러스
건축사사무소
Architecture + Environment
AE+
TEL. 02 - 745 - 8511
FAX. 0505-070-6511

4층 평면도

SCALE : 1/100

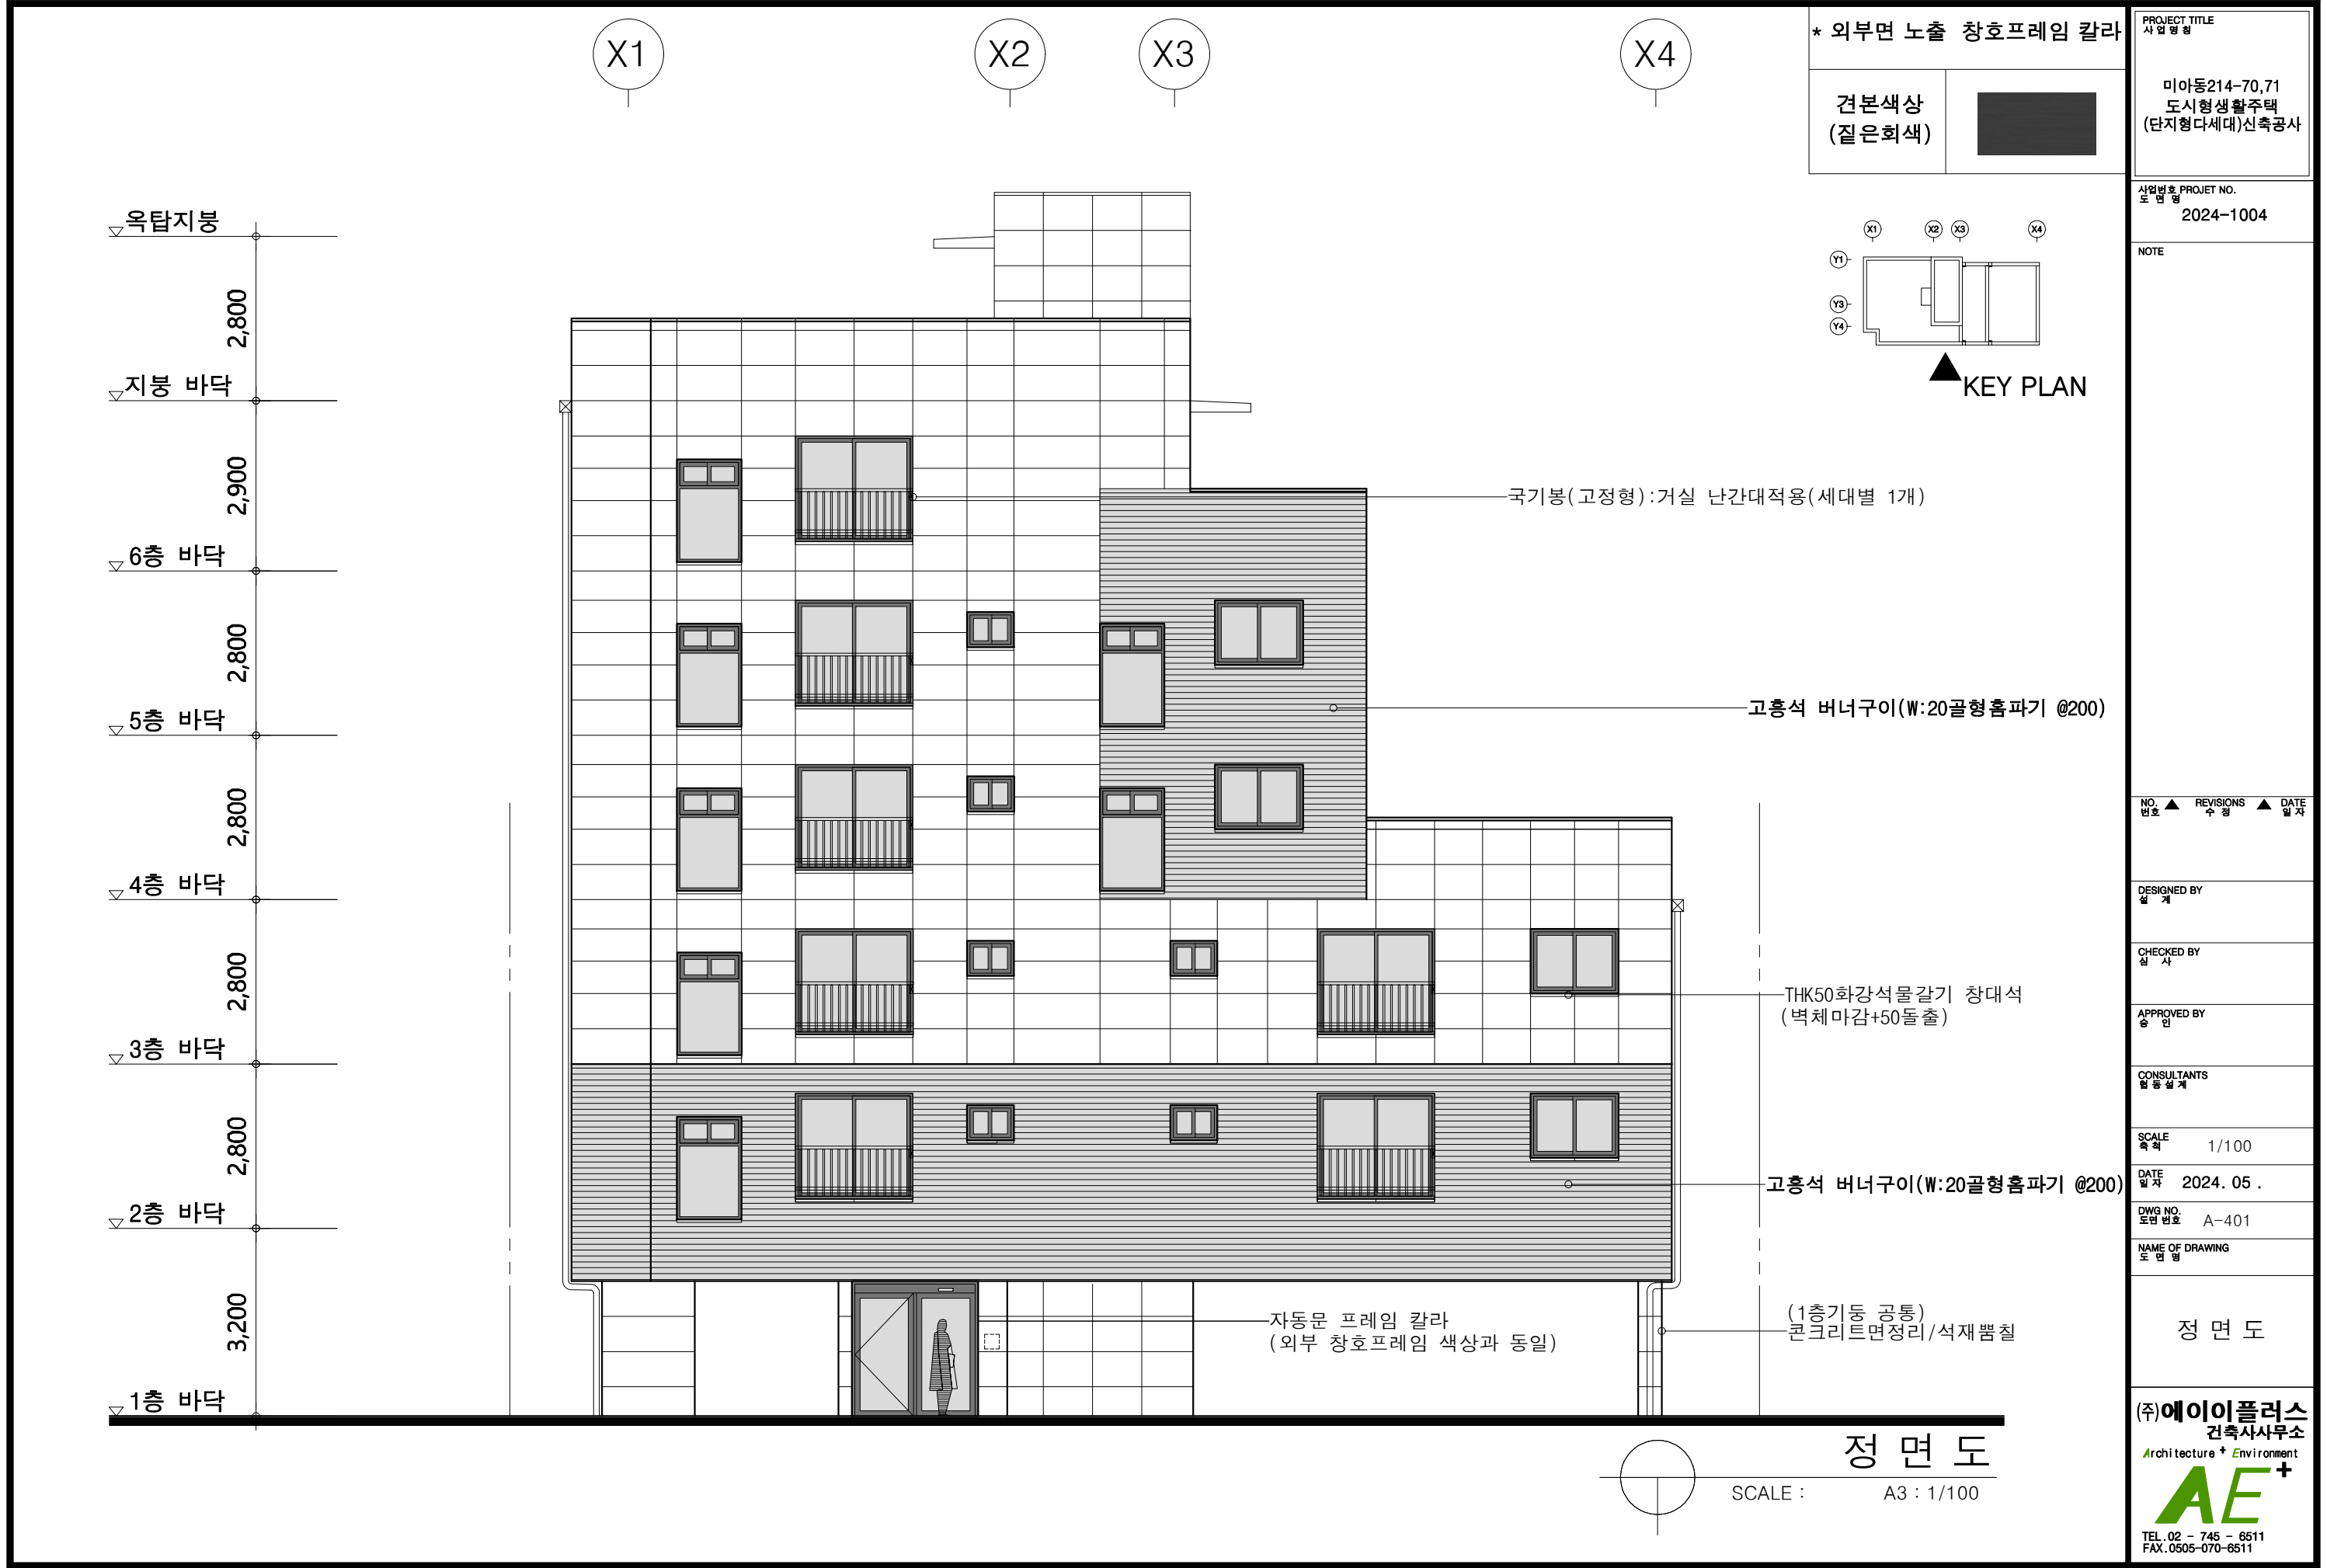

PROJECT TITLE
사업명칭
미아동214-70,71
도시형생활주택
(단지형다세대)신축공사

사업번호 PROJECT NO.
도면명
2024-1004

NOTE

NO. ▲ REVISIONS ▲ DATE
번호 수정 일자

DESIGNED BY
설계

CHECKED BY
심사

APPROVED BY
승인

CONSULTANTS
협동설계

SCALE
축척
1/100

DATE
일자
2024. 05 .

DWG NO.
도면번호
A-401

NAME OF DRAWING
도면명

정 면 도

(주)에이이플러스
건축사무소
Architecture + Environment
AE+
TEL. 02 - 745 - 8511
FAX. 0505-070-6511


옥탑지붕
2,800
지붕 바닥
2,900
6층 바닥
2,800
5층 바닥
2,800
4층 바닥
2,800
3층 바닥
2,800
2층 바닥
3,200
1층 바닥

Y4

Y3

Y2

Y1

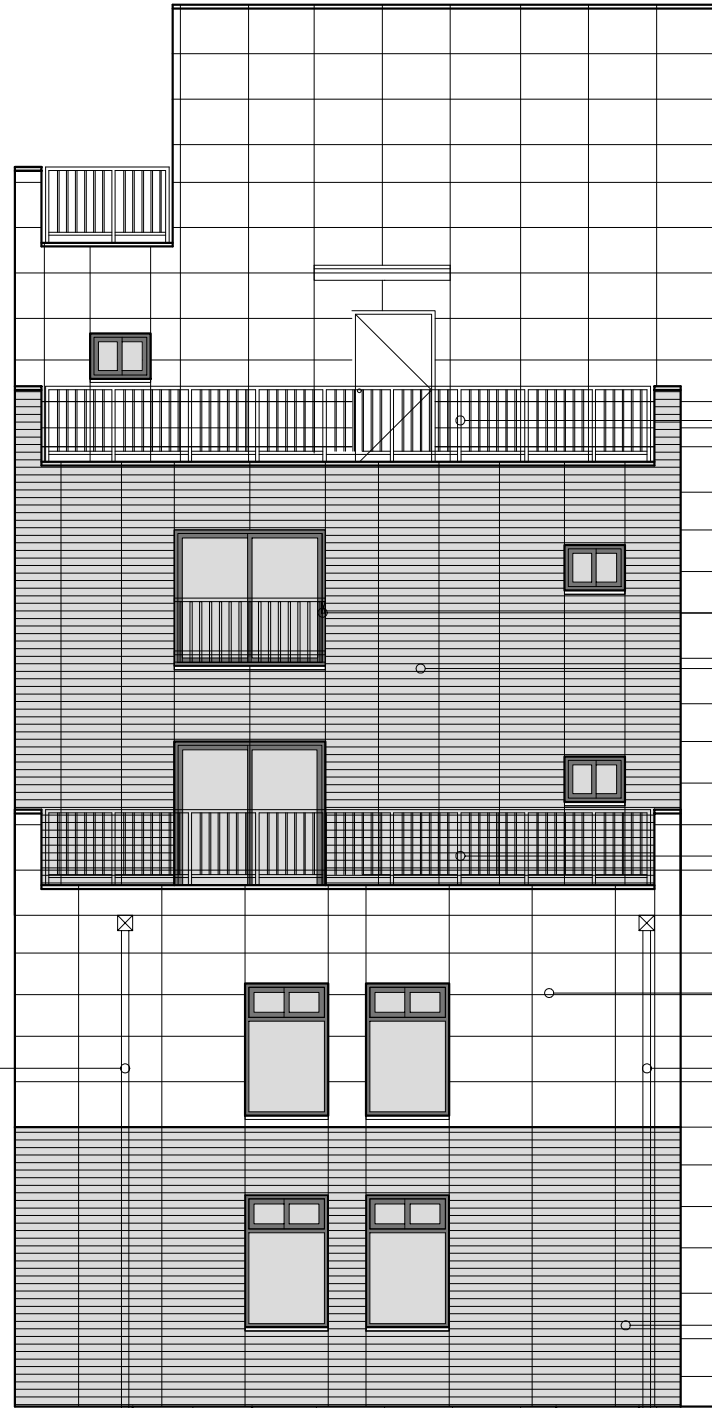

(난간동자 1000 이하)
수직형 철재 난간(상세도 S-501참조)
(H:옥상두겹상단+1200)

국기봉(고정형):거실 난간대적용(세대별 1개)
고흥석 버너구이(W:20골형흠파기 @200)

(난간동자 1000 이하)
수직형 철재 난간(상세도 S-501참조)
(H:옥상두겹상단+1200)


화강석(진주화 물갈기)

Ø100 SST선출통
(도장:외벽마감재동일색상)

고흥석 버너구이(W:20골형흠파기 @200)

* 외부면 노출 창호프레임 칼라

견본색상
(질은회색)

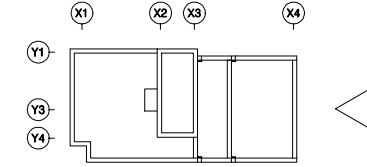

KEY PLAN

PROJECT TITLE
사업명칭
미아동214-70,71
도시형생활주택
(단지형다세대)신축공사

사업번호 PROJCT NO.
도면명
2024-1004

NOTE

NO. ▲ REVISIONS ▲ DATE
번호 수정 일자

DESIGNED BY
설계

CHECKED BY
심사

APPROVED BY
승인

CONSULTANTS
협동설계

SCALE
축척 1/100


DATE
일자 2024. 05 .

DWG NO.
도면번호 A-402

NAME OF DRAWING
도면명

우측면도


(주)에이이플러스
건축사무소
Architecture + Environment
AE+
TEL. 02 - 745 - 6511
FAX. 0505-070-6511

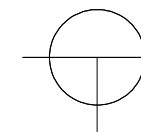

우측면도

SCALE : A3 : 1/100


Y1 Y2 Y3 Y4

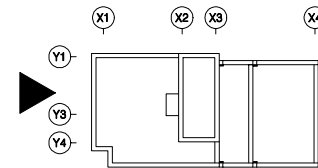

KEY PLAN

* 외부면 노출 창호프레임 칼라

견본색상
(질은회색)

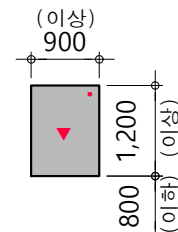

설치위치: 도로면 입면
소방관 진입창 범례

PROJECT TITLE
사업명칭
미아동214-70,71
도시형생활주택
(단지형태세대)신축공사

사업번호 PROJ. NO.
도면명 2024-1004

NOTE

NO. ▲ REVISIONS ▲ DATE
번호 수정 일자

DESIGNED BY
설계

CHECKED BY
심사

APPROVED BY
승인

CONSULTANTS
협동설계

SCALE
축척 1/100

DATE
일자 2024. 05 .

DWG NO.
도면번호 A-403

NAME OF DRAWING
도면명

좌측면도

(주)에이이플러스
건축사무소
Architecture + Environment
AE+
TEL. 02 - 745 - 6511
FAX. 0505-070-6511

옥탑지붕

2,800

지붕 바닥

2,900

6층 바닥

Ø100 SST선출통
(도장:외벽마감재동일색상)

2,800

5층 바닥

2,800

4층 바닥

2,800

3층 바닥

2,800

2층 바닥

3,200

1층 바닥

Ø100 SST선출통
(도장:외벽마감재동일색상)

화강석(진주화 물갈기)

소방창

THK50화강석물갈기 창대석
(벽체마감+50돌출)

고흥석 버너구이(W:20골형홈파기 @200)

좌측면도

SCALE : A3 : 1/100

X4

X3

X2


X1

* 외부면 노출 창호프레임 칼라

견본색상
(질은회색)PROJECT TITLE
사업명칭

미아동214-70,71
도시형생활주택
(단지형다세대)신축공사사업번호 PROJECT NO.
도면명
2024-1004

NOTE

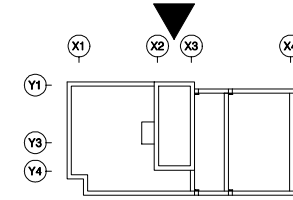

KEY PLAN

옥탑지붕
2,800
지붕 바닥
2,900
6층 바닥
2,800
5층 바닥
2,800
4층 바닥
2,800
3층 바닥
2,800
2층 바닥
3,200
1층 바닥

Ø100 SST선출통
(도장:외벽마감재동일색상)
고흥석 버너구이(W:20골형흙파기 @200)

Ø100 SST선출통
(도장:외벽마감재동일색상)

국기봉(고정형):거실 난간대적용(세대별 1개)
수직형 주물철재 난간

화강석(진주화 물갈기)

THK50화강석물갈기 창대석
(벽체마감+50돌출)

고흥석 버너구이(W:20골형흙파기 @200)

(1층기둥 공통)
콘크리트면정리/석재땜칠

배 면 도

SCALE : A3 : 1/100

NO. ▲ REVISIONS ▲ DATE
번호 수정 일자DESIGNED BY
설계CHECKED BY
심사APPROVED BY
승인CONSULTANTS
협동설계SCALE
축척 1/100DATE
일자 2024. 05 .DWG NO.
도면번호 A-404NAME OF DRAWING
도면명


배 면 도

(주)에이이플러스
건축사사무소


Architecture + Environment

AE+

TEL. 02 - 745 - 6511
FAX. 0505-070-6511

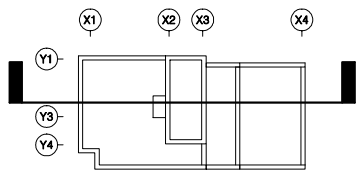

KEY PLAN

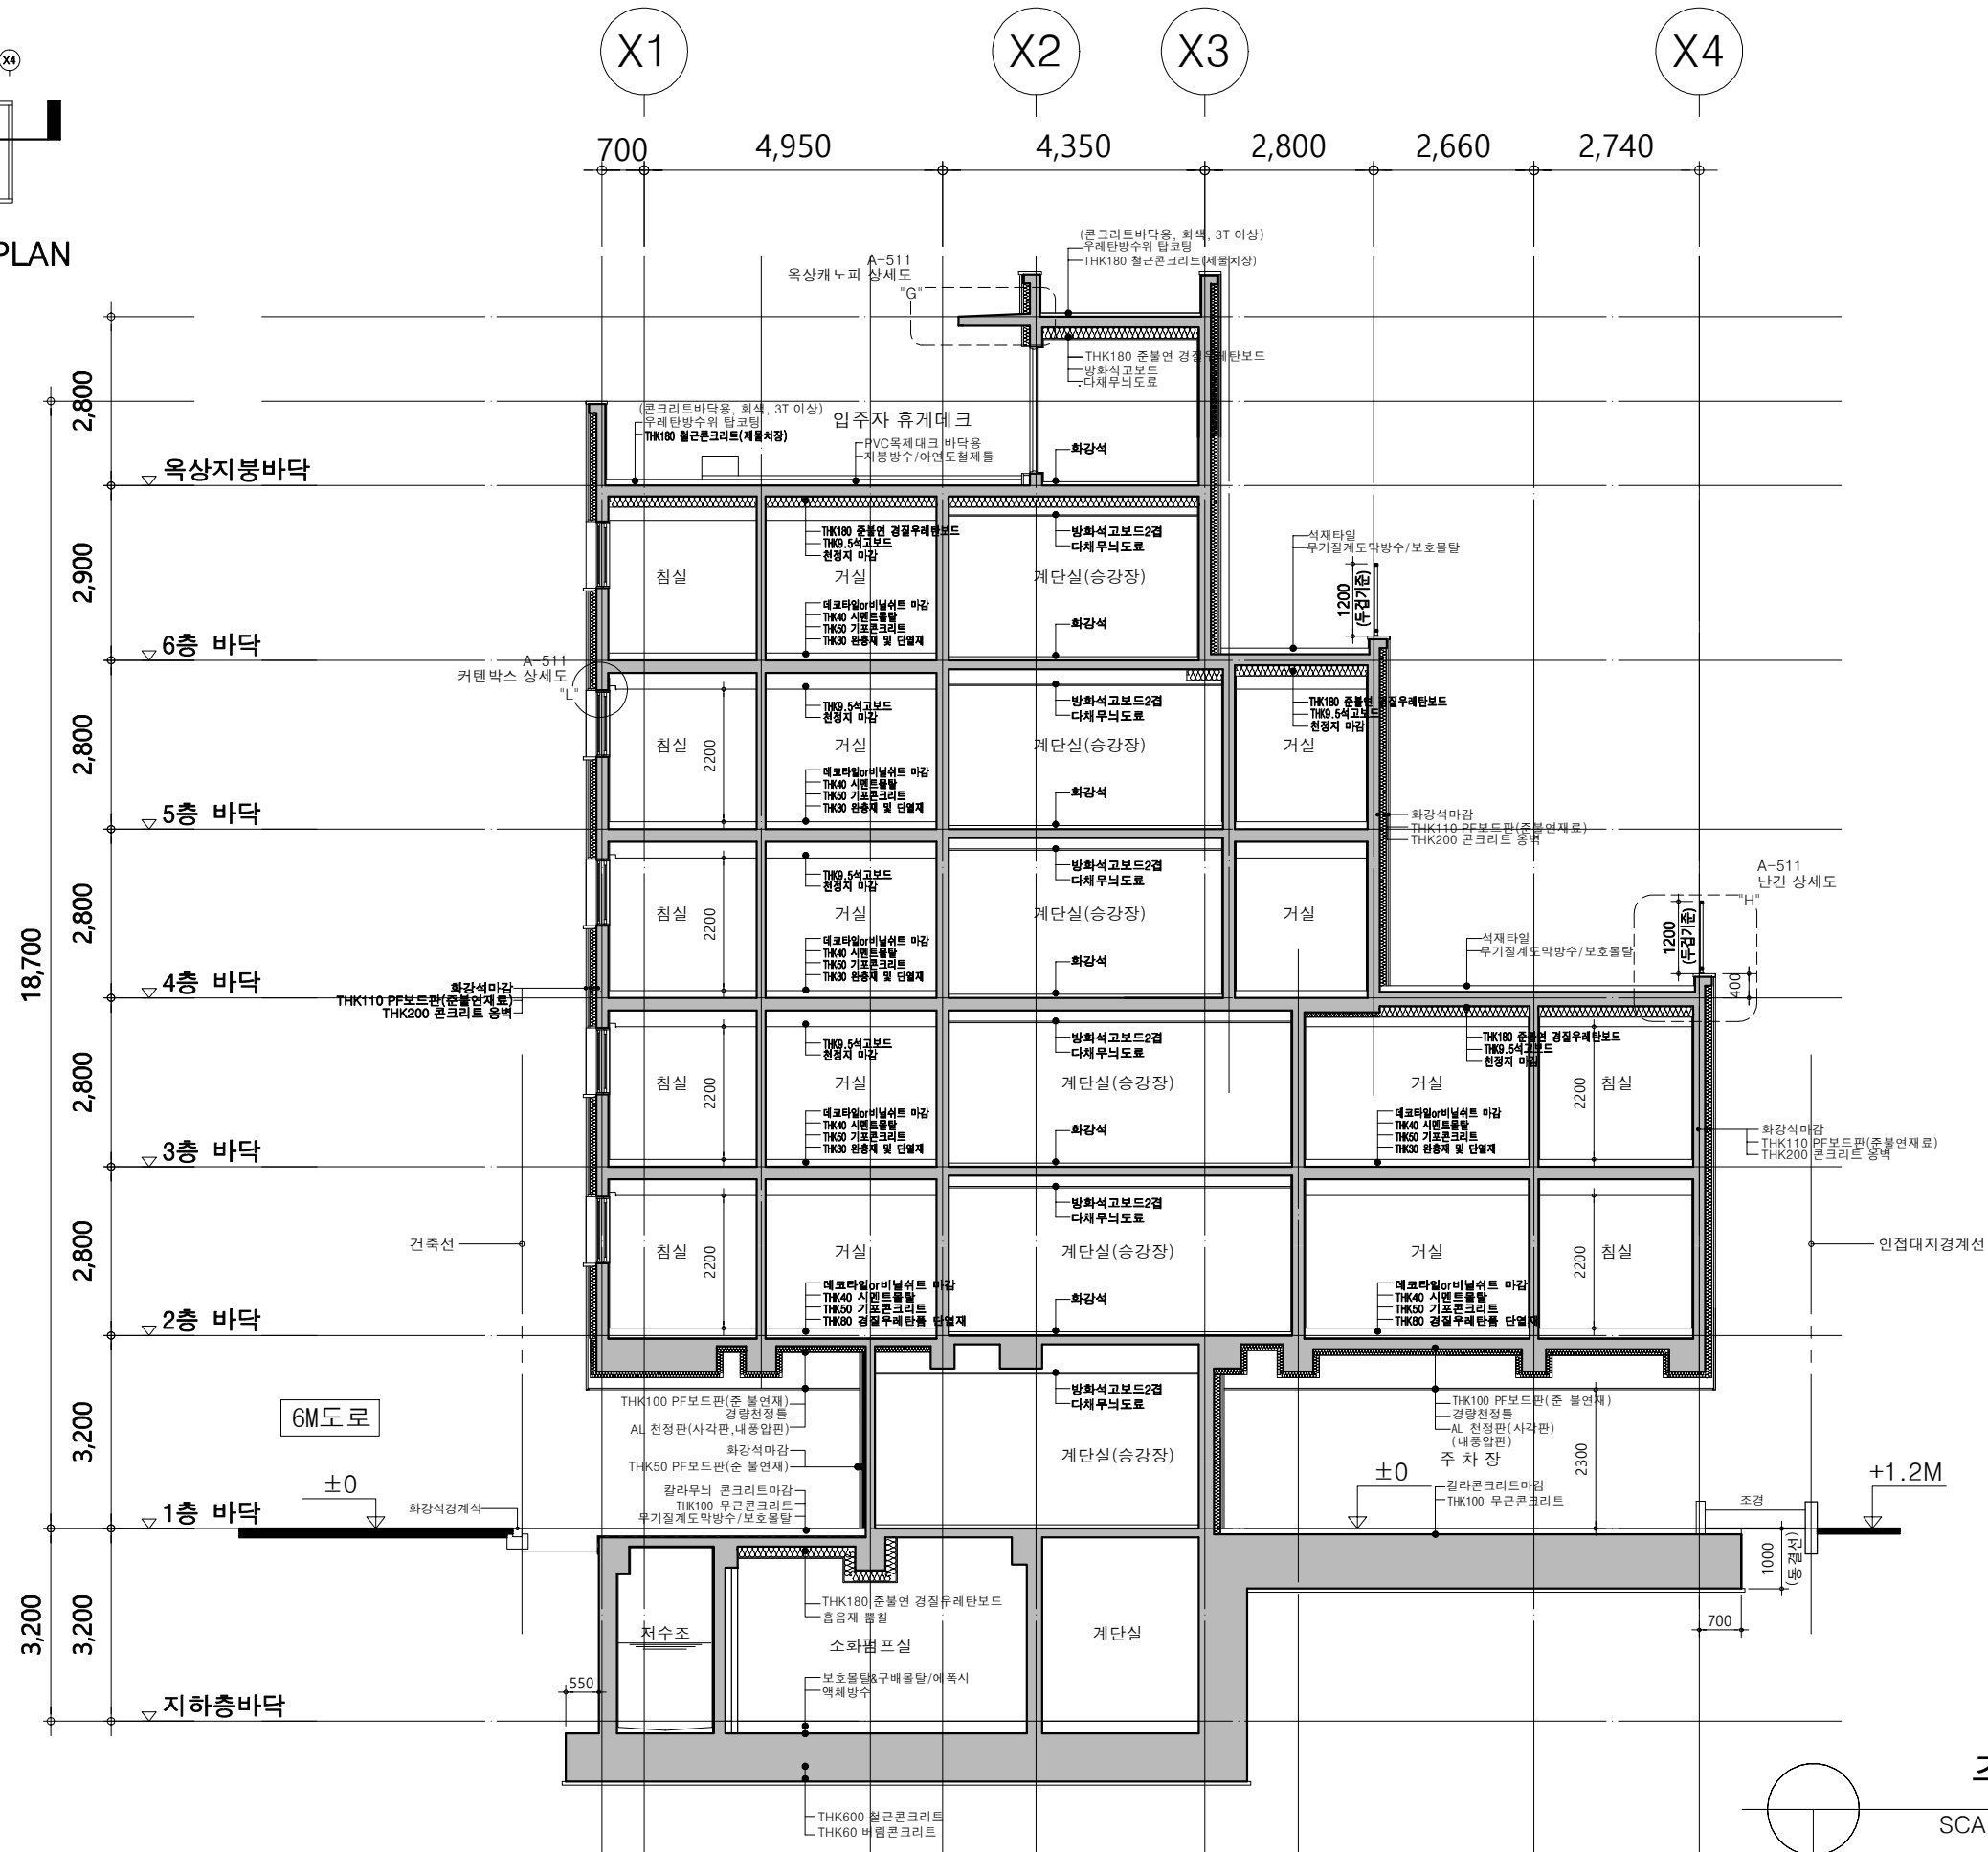

PROJECT TITLE
사업명칭

미아동214-70,71
도시형생활주택
(단지형태세대)신축공사

PROJECT NO.
도면명
2024-1004

NOTE
1. 단열재, 창호 등 단열
및 기밀성관련 사항은
에너지관련도서 (형별성능
내역서, 외피전개도, 단열
계획도 등)를 우선하여
적용한다.

NO. REVISIONS DATE
번호 수정 일자

DESIGNED BY
설계

CHECKED BY
심사

APPROVED BY
승인

CONSULTANTS
협동설계

SCALE
축척 1/120




DATE
일자 2024. 05 .

DWG NO.
도면번호 A-501

NAME OF DRAWING
도면명

주 단 면 도

(주)에이플러스
건축사무소
Architecture + Environment
AE+
TEL. 02 - 745 - 8511
FAX. 0505-070-6511

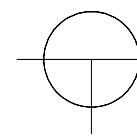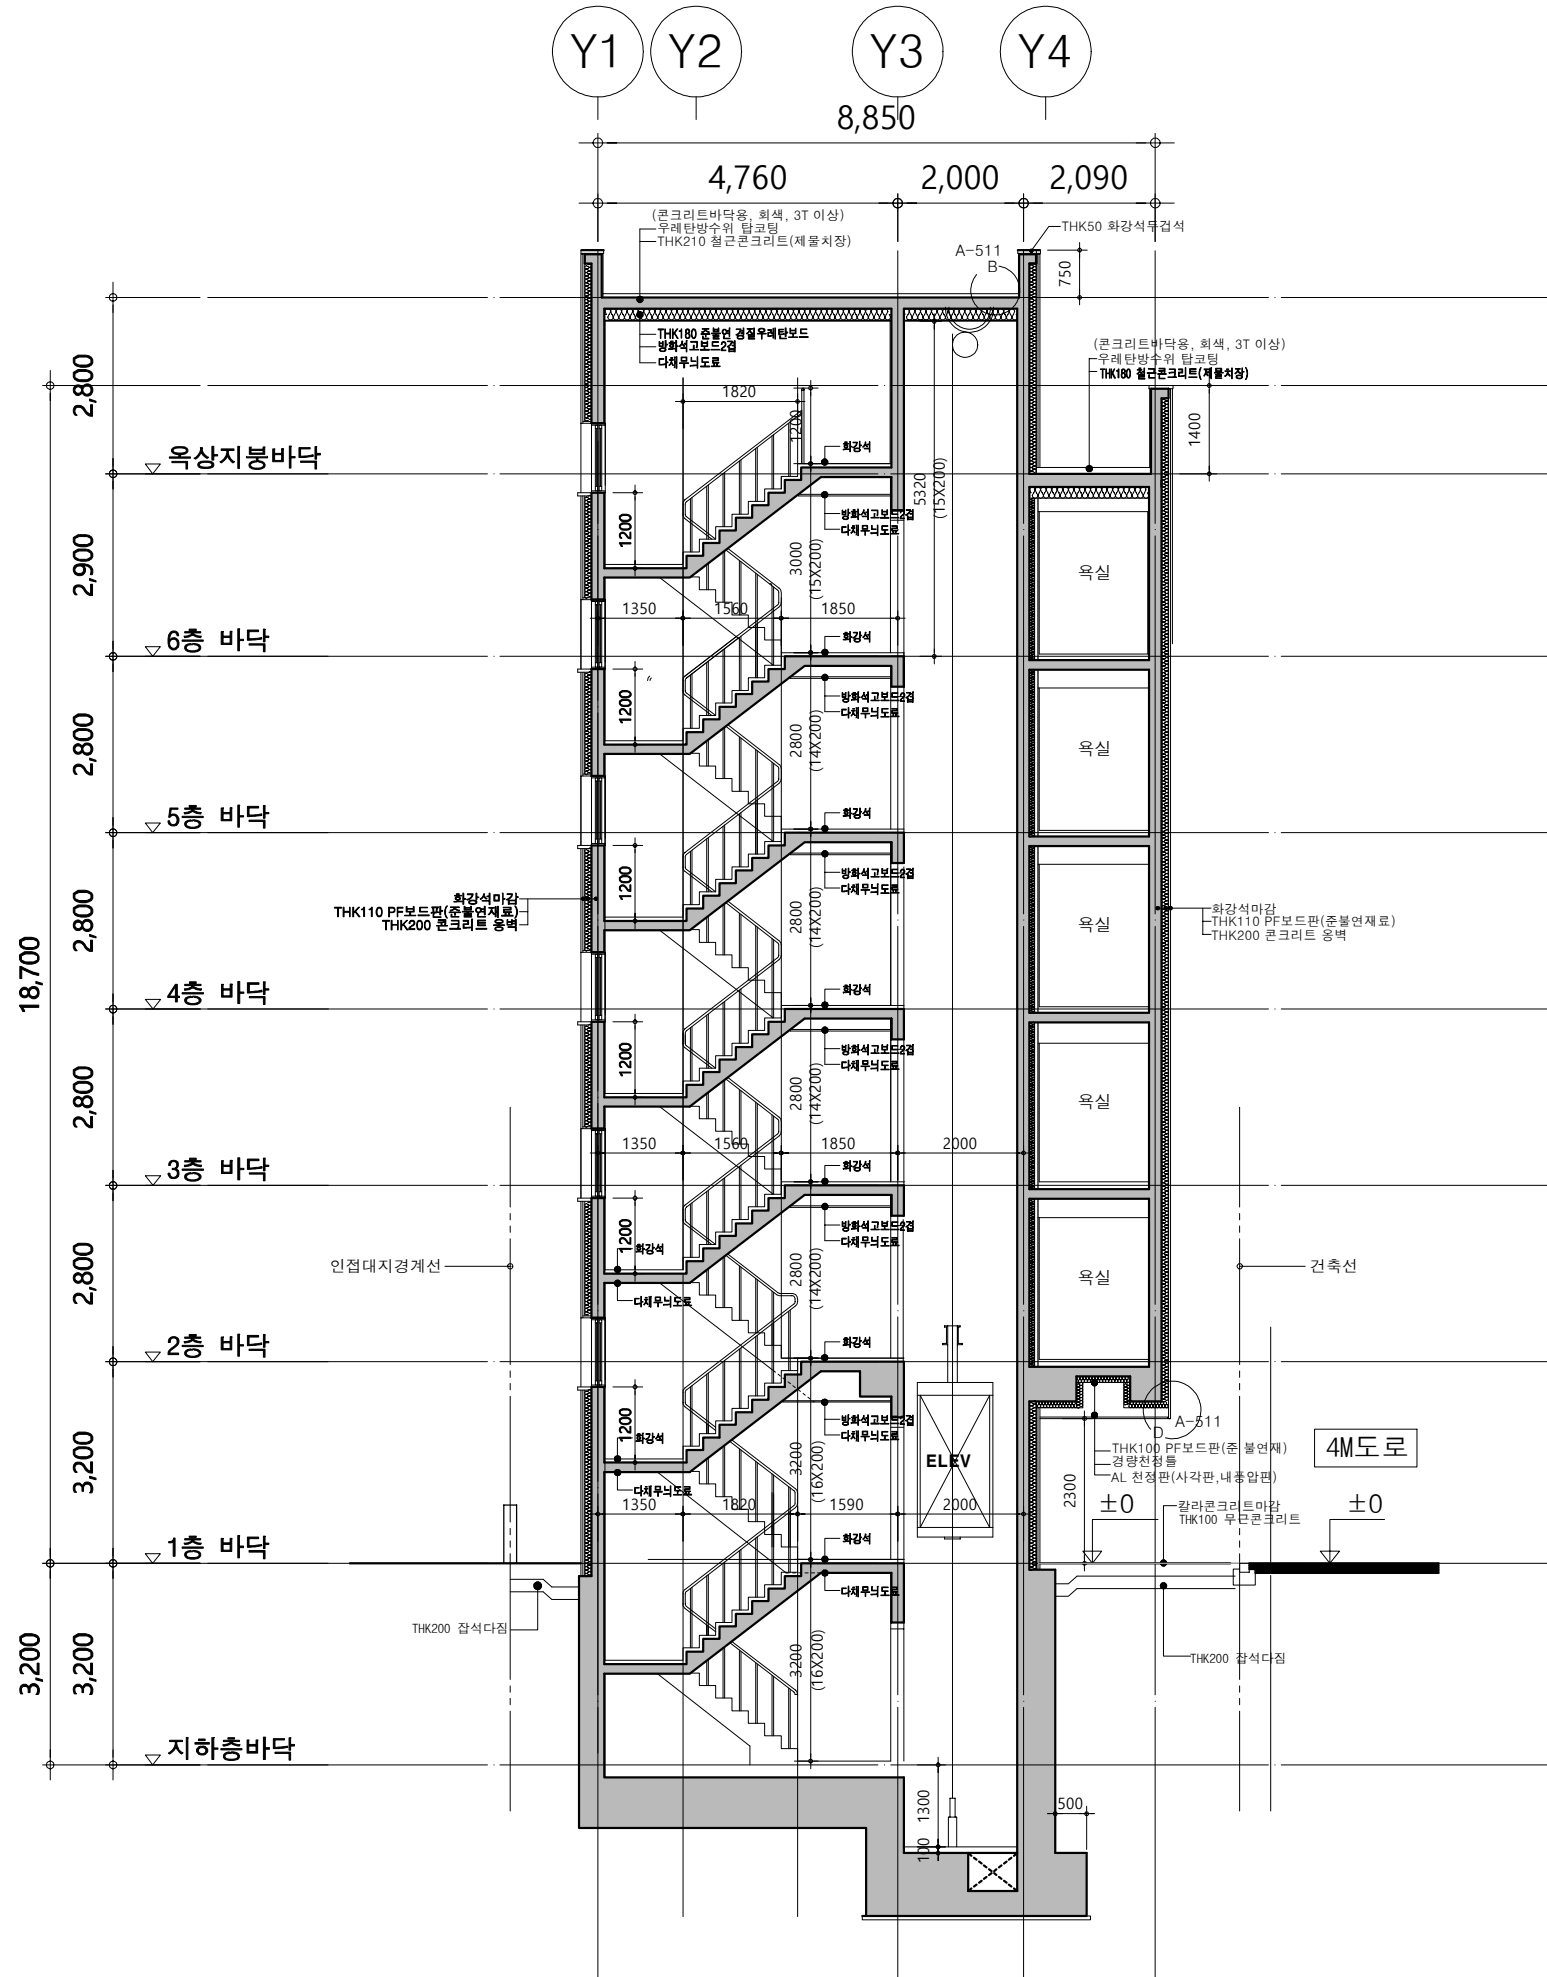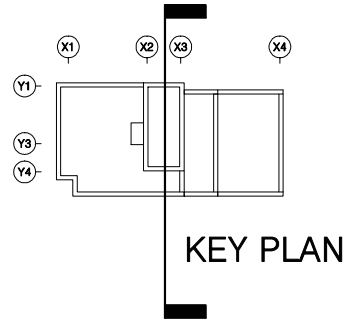

계단단면도
SCALE : 1/150

PROJECT TITLE
사업명칭

미아동214-70,71
도시형생활주택
(단지형다세대)신축공사

사업번호 PROJ. NO.
도면명
2024-1004

NOTE
1. ELE PIT 깊이는
사양에 따라 다를 수
있으니 시공시 유의할 것

2. 단열재, 창호 등 단열
및 기밀성관련 사항은
에너지관련도서 (형별성능
내역서, 외피전개도, 단열
계획도 등)를 우선하여
적용한다.

NO. 번호	REVISIONS 수정	DATE 일자
-----------	-----------------	------------

DESIGNED BY
설계

CHECKED BY
심사

APPROVED BY
승인



CONSULTANTS
협동설계

SCALE
축척 1/120

DATE
일자 2024. 05 .

DWG NO.
도면번호 A-502

NAME OF DRAWING
도면명

계단단면도

(주)에이이플러스
건축사사무소
Architecture + Environment
AE+
TEL. 02 - 745 - 6511
FAX. 0505-070-6511