


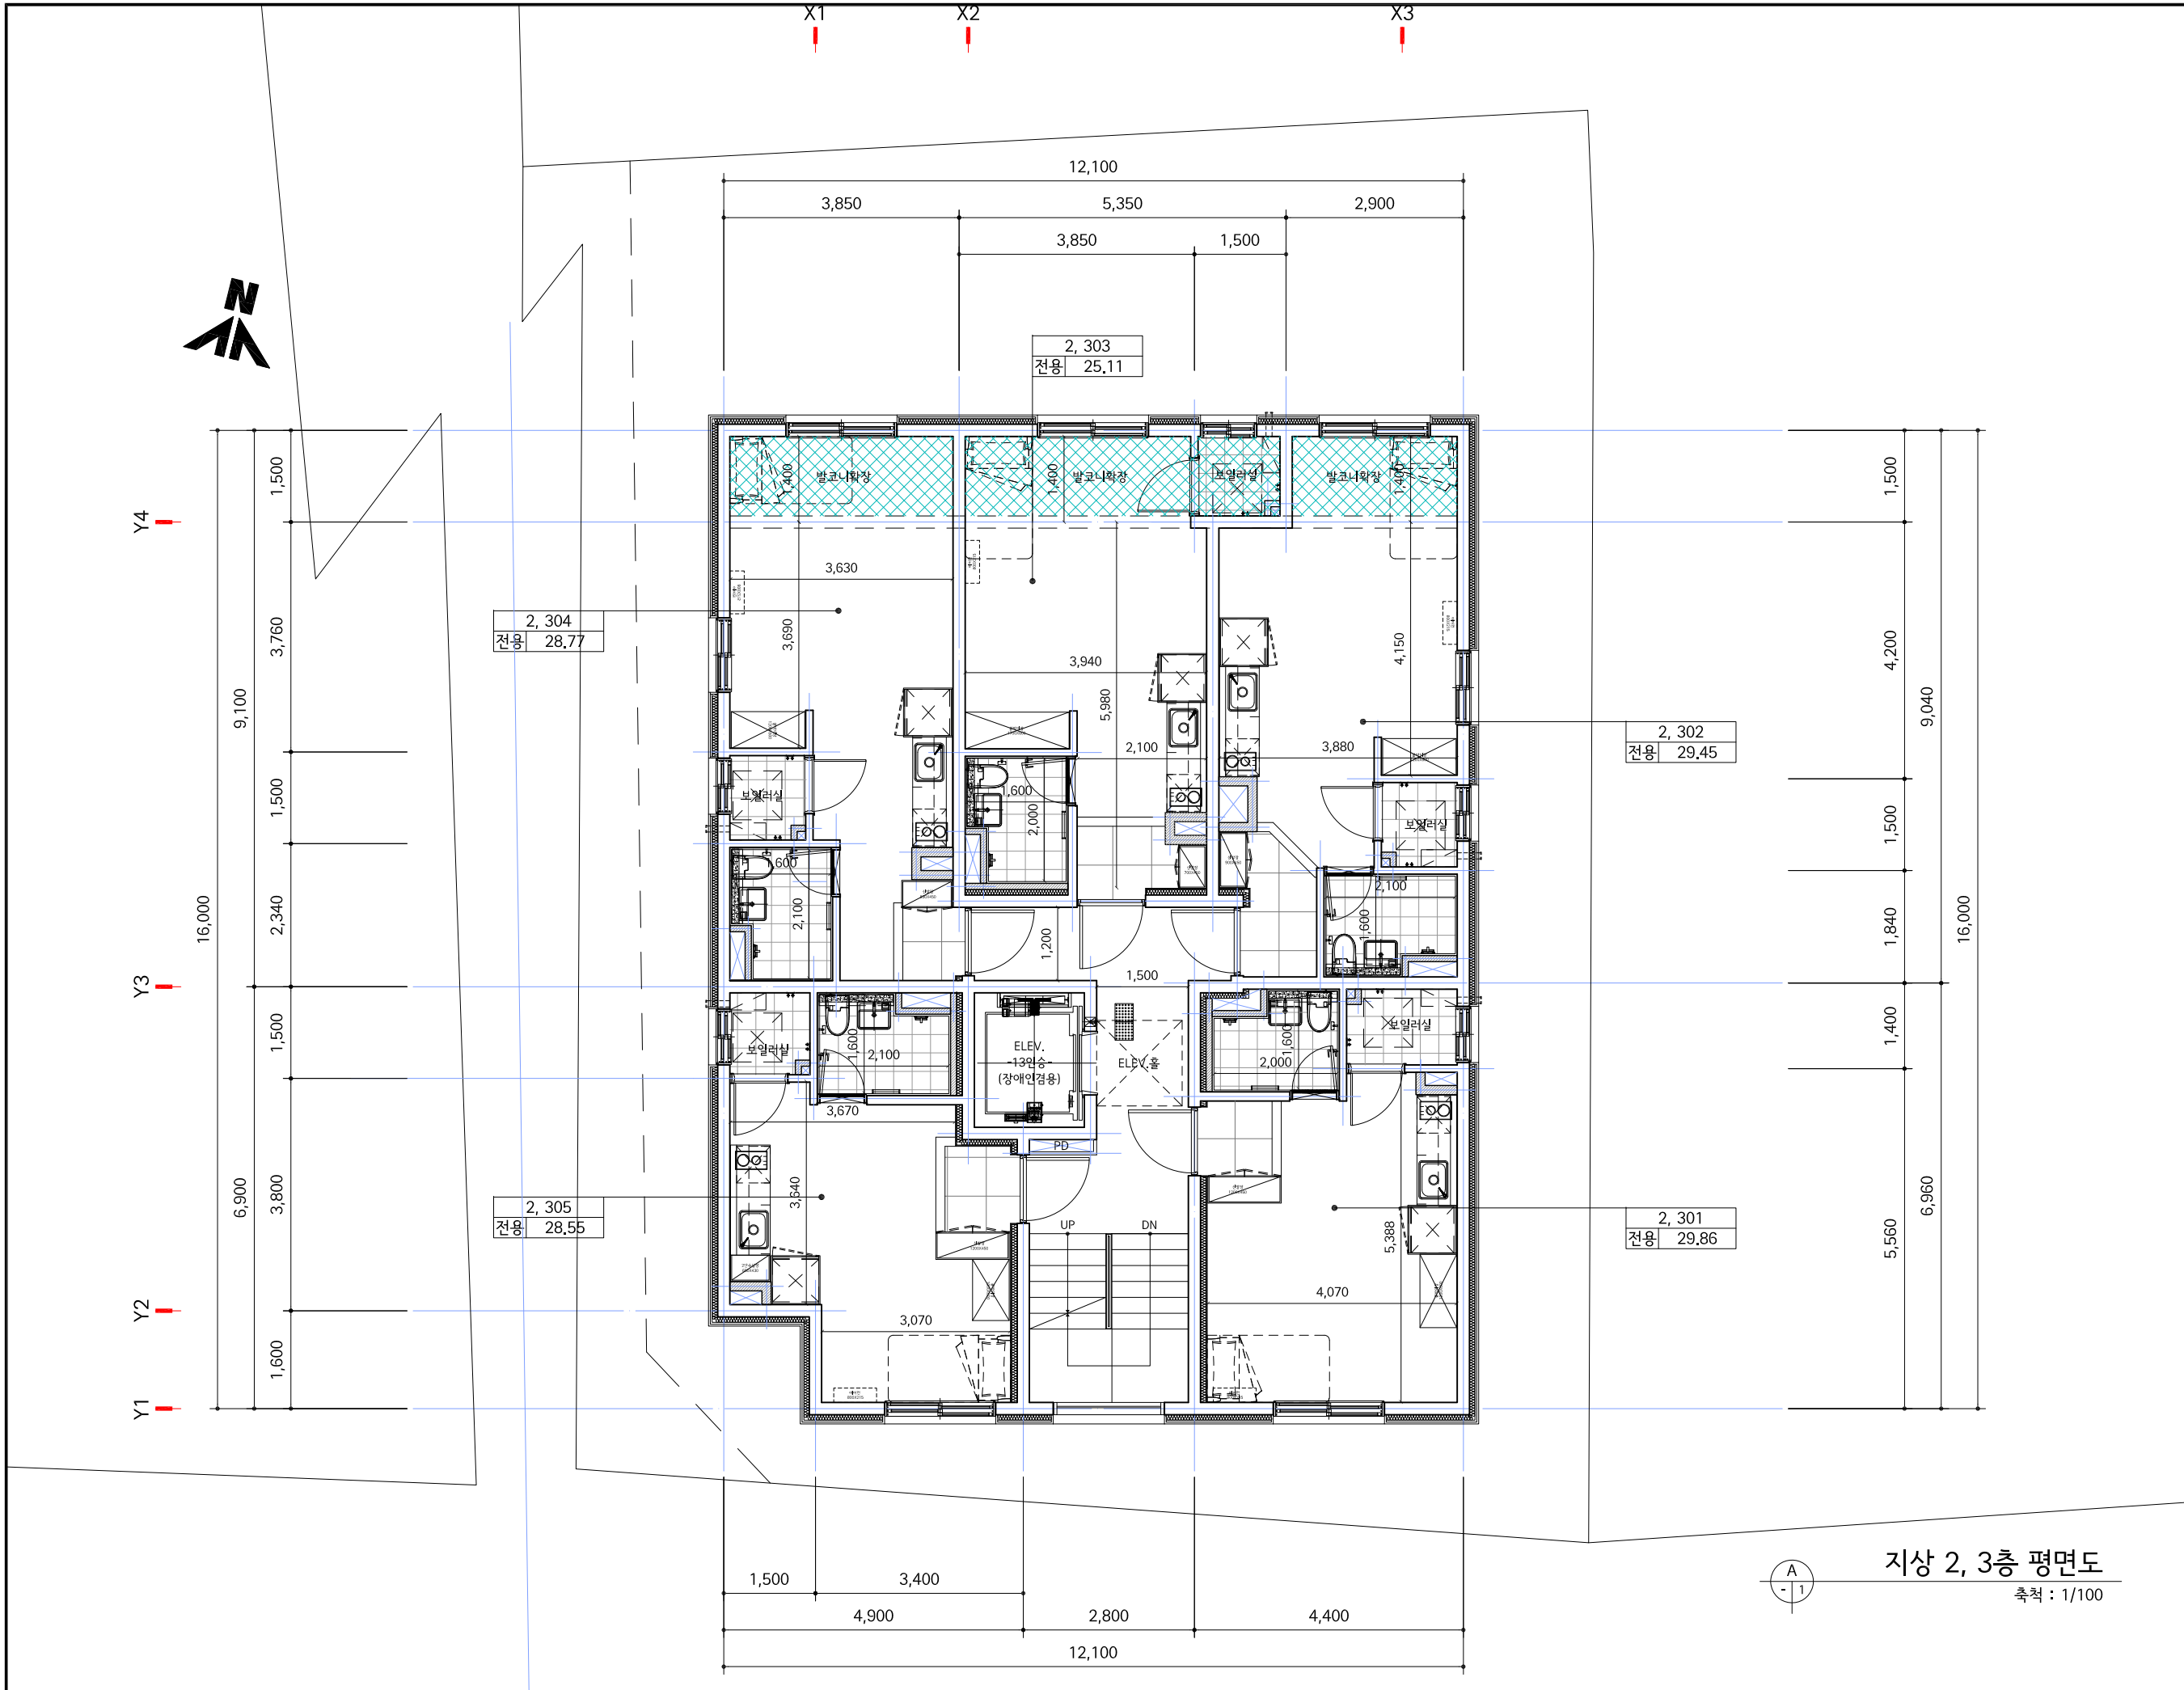

지상 2, 3층 평면도
축척 : 1/100

PROJECT TITLE
공사명

강북구 수유동
391-26 외 1필지
단지형다세대주택
신축공사

NOTE

1층 바닥높이 : GL ±0.00
2~5층 반자높이 : 2,300
슬래브 : THK 210
2층슬래브 : THK 180
내벽 : THK 150
외벽,세대간벽 : THK 200
콘크리트 fck = 27 MPa


△					
△					
△					
△					
△					
NO	DATE	REVISION DESCRIPTION	DRAWN	DATE	DATE

건축사 사무소
하늘건축
Architects & Engineers

TEL : 02) 928 ~ 4484
FAX : 02) 928 ~ 4487

APPROVED 승인	DATE
ARCHITECT 설계	
CHKD 1 검토	
CHKD 2 검토	
DRAWN 당	
DATE 작성일	2025. 12.

SCALE 축척	A3 : 1/100
TITLE 도면명	지상 2, 3층 평면도
DRWG NO. 도면번호	A - 102
B.C.C.NO. 분류번호	SHEET NO. 일반번호
JOB NO. 작업번호	REV NO.

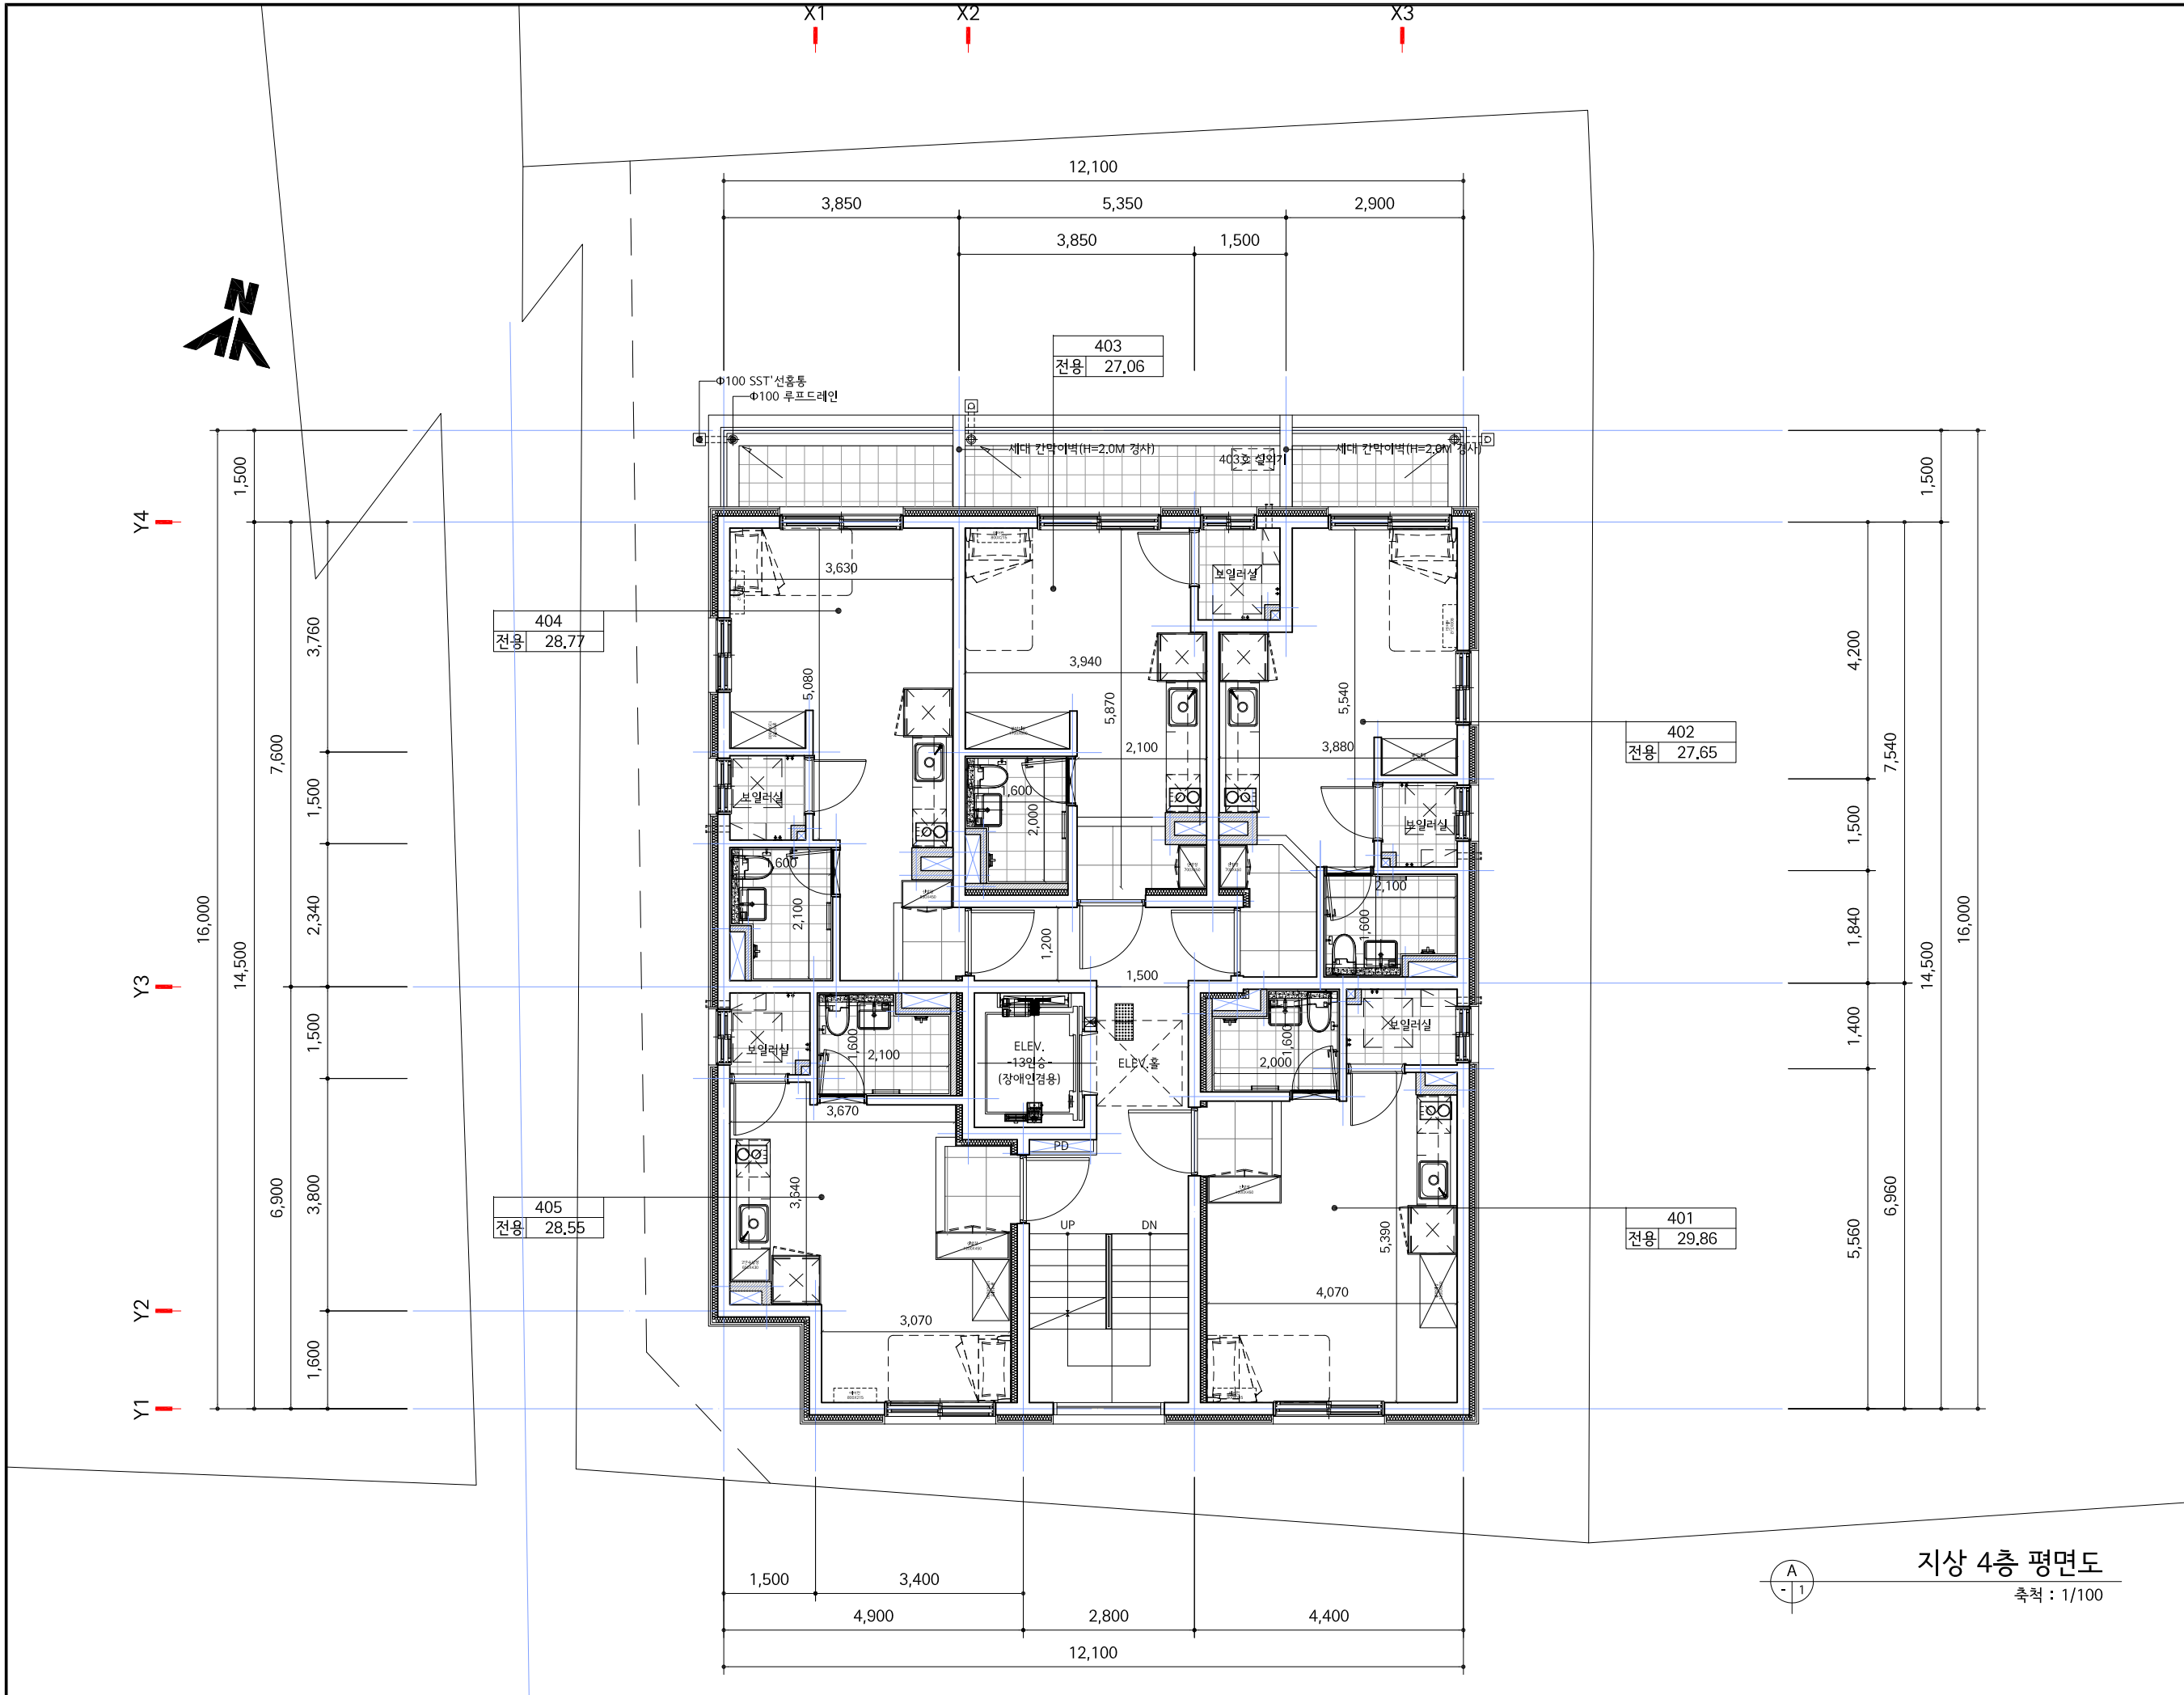

지상 4층 평면도
축척 : 1/100


PROJECT TITLE
공사명
강북구 수유동
391-26 외 1필지
단지형다세대주택
신축공사

NOTE
1층 바닥높이 : GL ±0.00
2~5층 반자높이 : 2,300
슬래브 : THK 210
2층슬래브 : THK 180
내벽 : THK 150
외벽,세대간벽 : THK 200
콘크리트 fck = 27 MPa

△							
△							
△							
△							
△							
NO	DATE	REVISION	DESCRIPTION	DRAWN	DATE	DATE	

건축사 사무소
하늘건축
Architects & Engineers
TEL : 02) 928 ~ 4484
FAX : 02) 928 ~ 4487

APPROVED 승인 인	DATE
ARCHITECT 설계	
CHKD 1 검토	
CHKD 2 검토	
DRAWN 당	
DATE 작성일	2025. 12.
SCALE 축척	A3 : 1/100
TITLE 도면명	지상 4층 평면도
DRWG NO. 도면번호	A - 103
B.C.C.NO. 분류번호	SHEET NO. 일련번호
JOB NO. 작업번호	REV NO.

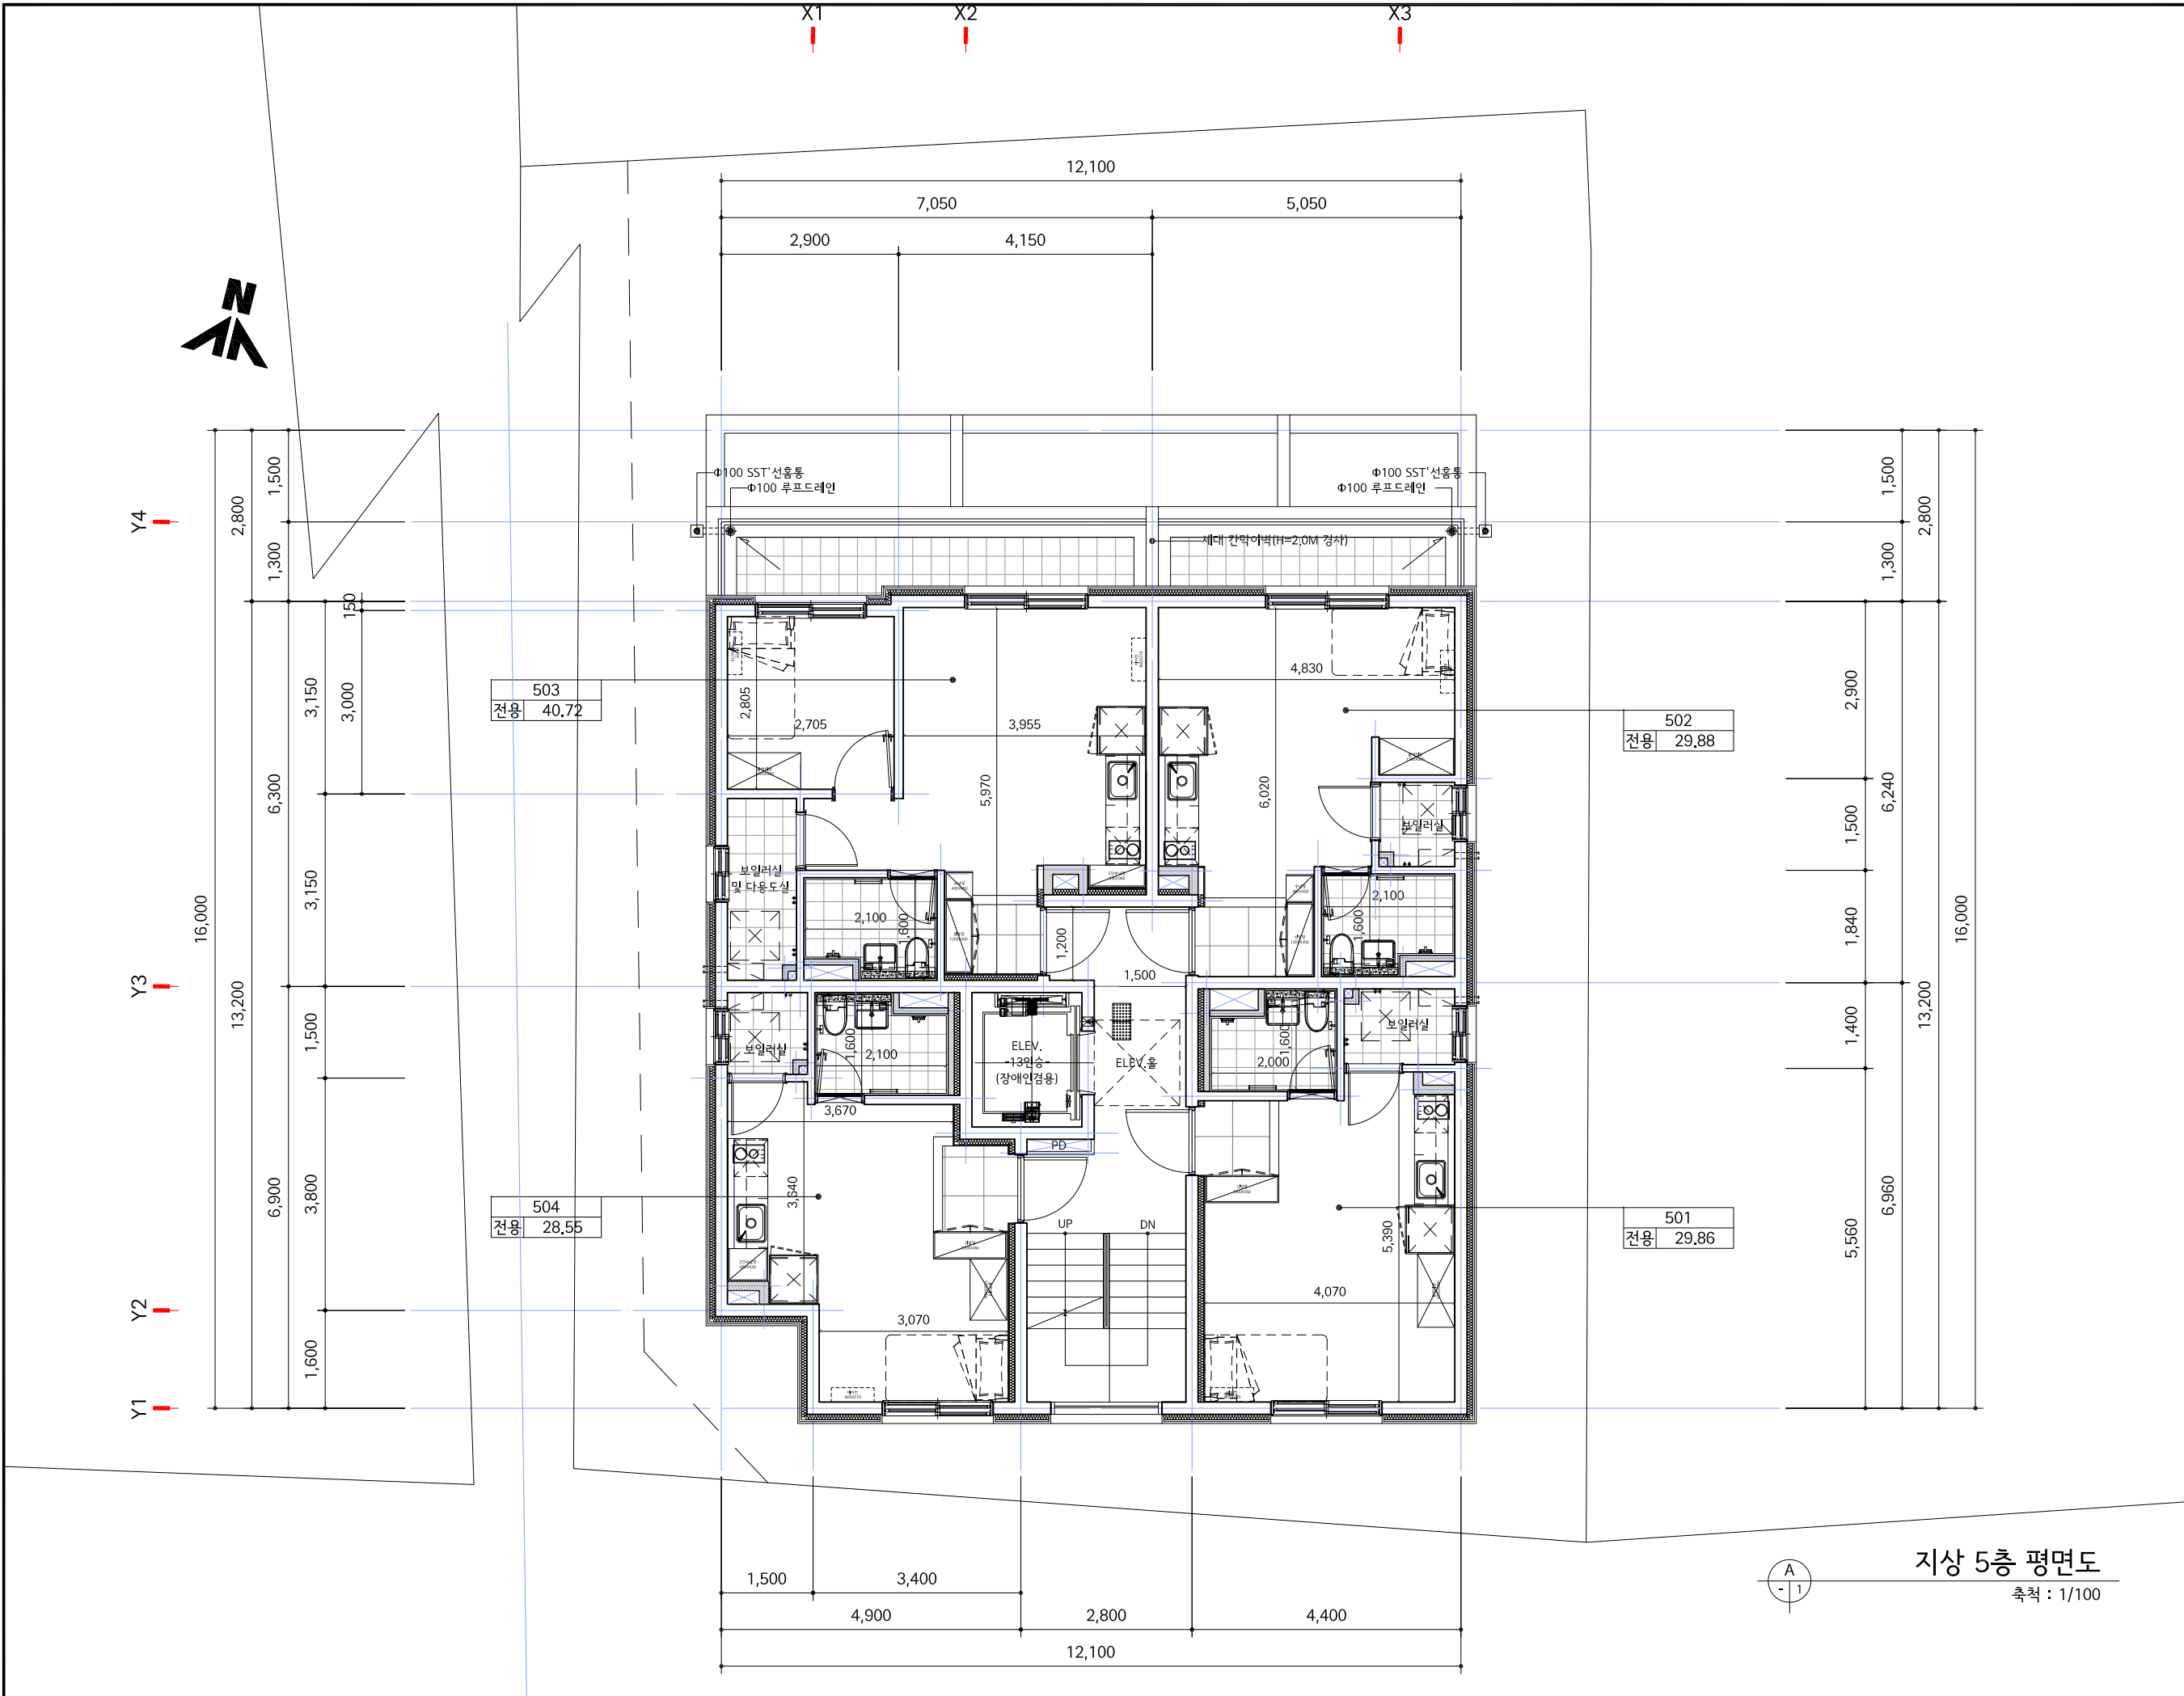

지상 5층 평면도
축척 : 1/100

PROJECT TITLE
공 사 명

강북구 수유동
391-26 외 1필지
단지형다세대주택
신 축 공 사

NOTE

1층 바닥높이 : GL ±0.00
2~5층 반자높이 : 2,300
슬래브 : THK 210
2층슬래브 : THK 180
내벽 : THK 150
외벽,세대간벽 : THK 200
콘크리트 fck = 27 MPa

△					
△					
△					
△					
△					
NO	DATE	REVISION DESCRIPTION	DRAWN	DATE	DATE

건축사 사무소
하늘 건축
Architects & Engineers

TEL : 02) 928 ~ 4484
FAX : 02) 928 ~ 4487

APPROVED 승 인	DATE
ARCHITECT 설 계	
CHKD 1 검 토	
CHKD 2 검 토	
DRAWN 당	
DATE 작성일	2025. 12.



SCALE
축 척

A3 : 1/100



TITLE
도면명

지상 5층 평면도


DRWG NO. 도면번호	A - 104
B.C.C.NO. 분류번호	SHEET NO. 일반번호
JOB NO. 작업번호	REV NO. △

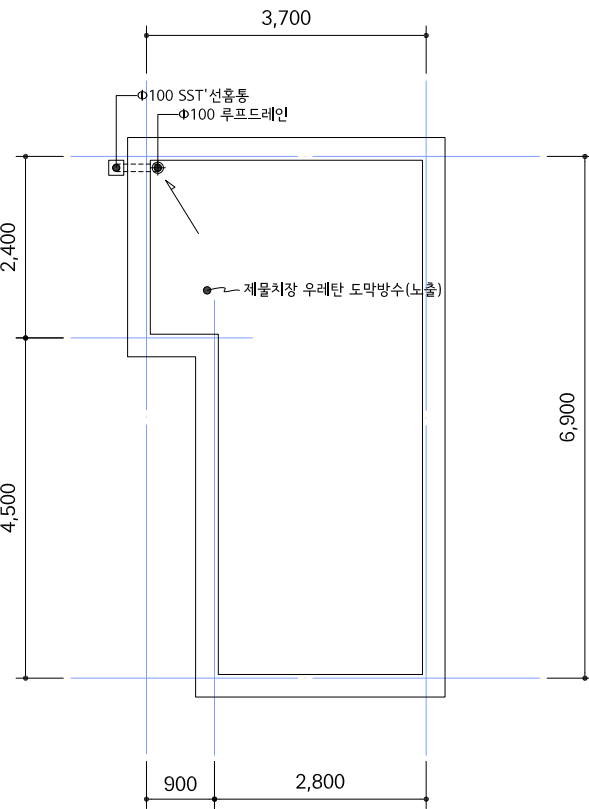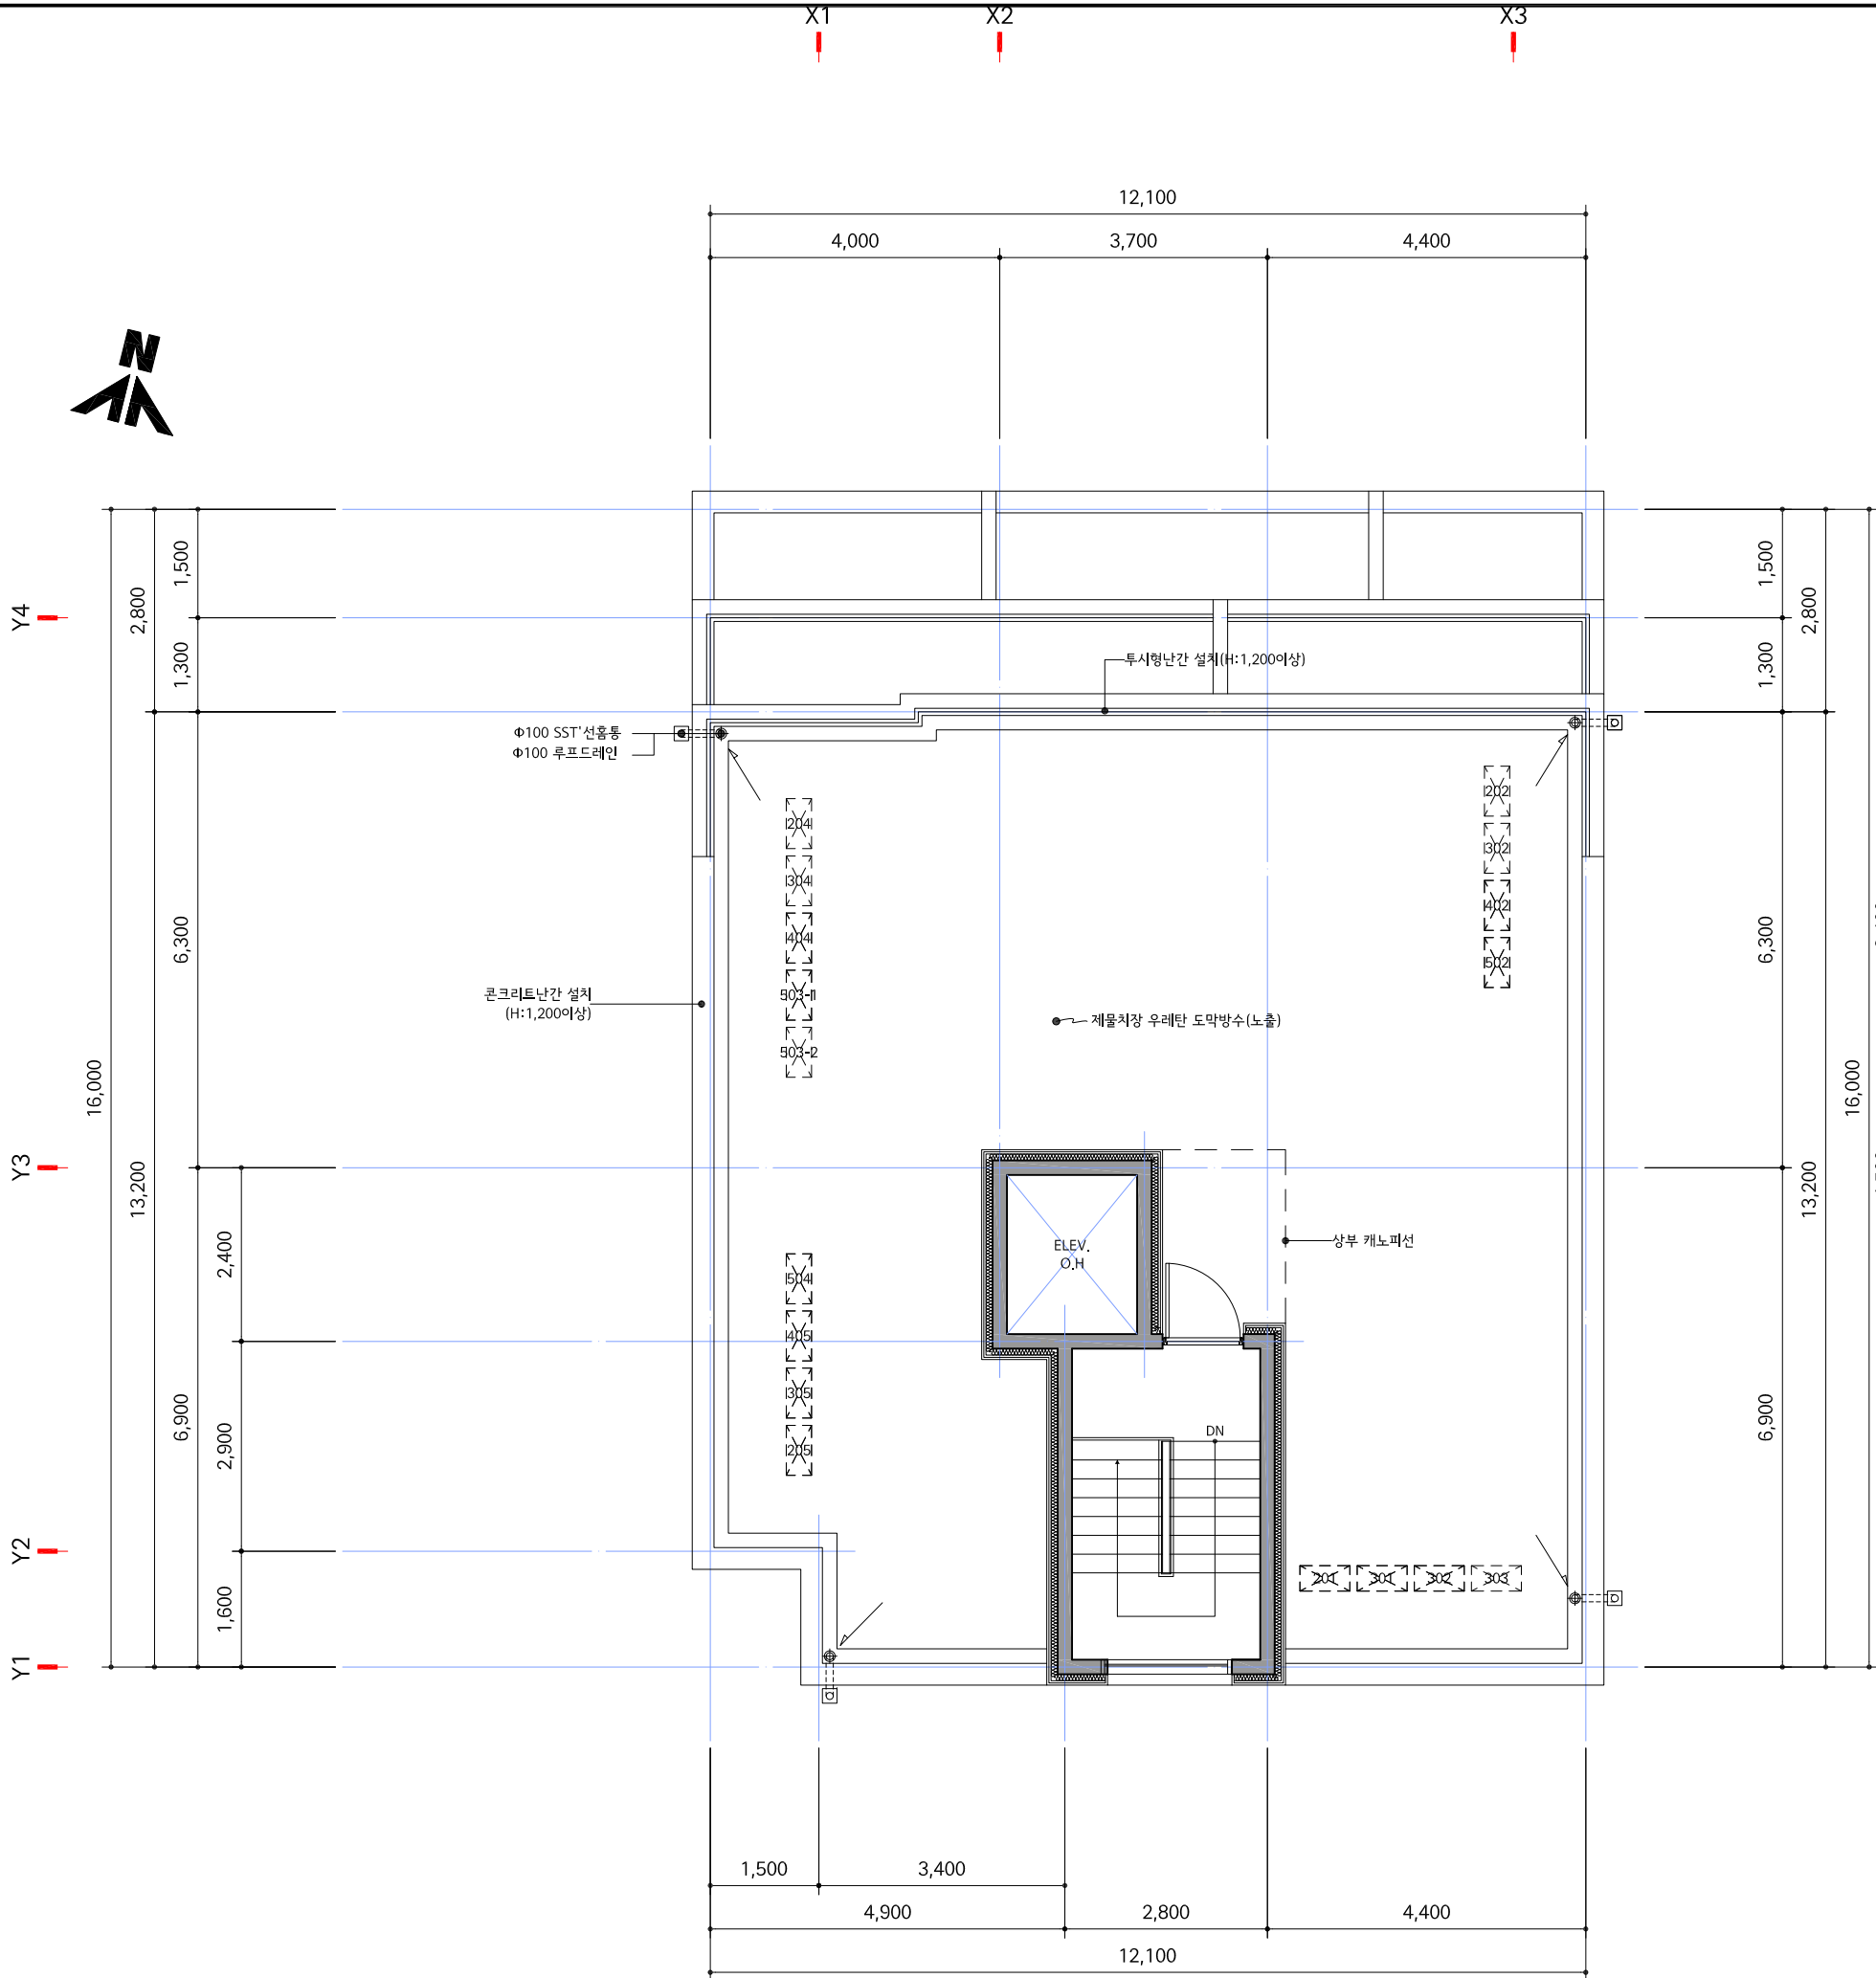

옥탑지붕 평면도
축척 : 1/100

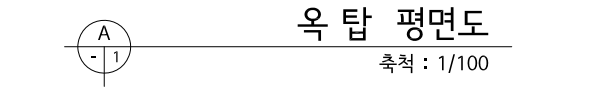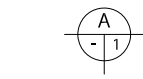

옥 탑 평면도
축척 : 1/100

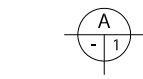

PROJECT TITLE
공 사 명

강북구 수유동
391-26 외 1필지
단지형다세대주택
신 축 공 사



NOTE

1층 바닥높이 : GL ±0.00
2~5층 반자높이 : 2,300
슬래브 : THK 210
2층슬래브 : THK 180
내벽 : THK 150
외벽,세대간벽 : THK 200
콘크리트 fck = 27 MPa

△					
△					
△					
△					
△					
NO	DATE	REVISION DESCRIPTION	DRAWN	DATE	DATE

건축사 사무소
하늘 건축
Architects & Engineers
TEL : 02) 928 ~ 4484
FAX : 02) 928 ~ 4487

APPROVED 승 인	DATE
ARCHITECT 설 계	
CHK D 1 검 토	
CHK D 2 검 토	
DRAWN 당	
DATE 작성일	2025. 12.
SCALE 축 척	A3 : 1/100
TITLE 도면명	옥탑 및 옥탑지붕 평면도
DRWG NO. 도면번호	A - 105
B.C.C.NO. 분류번호	SHEET NO. 일반번호
JOB NO. 작업번호	REV NO.

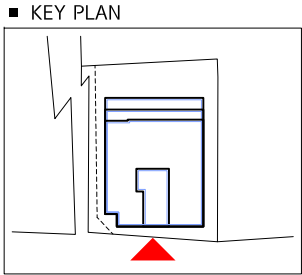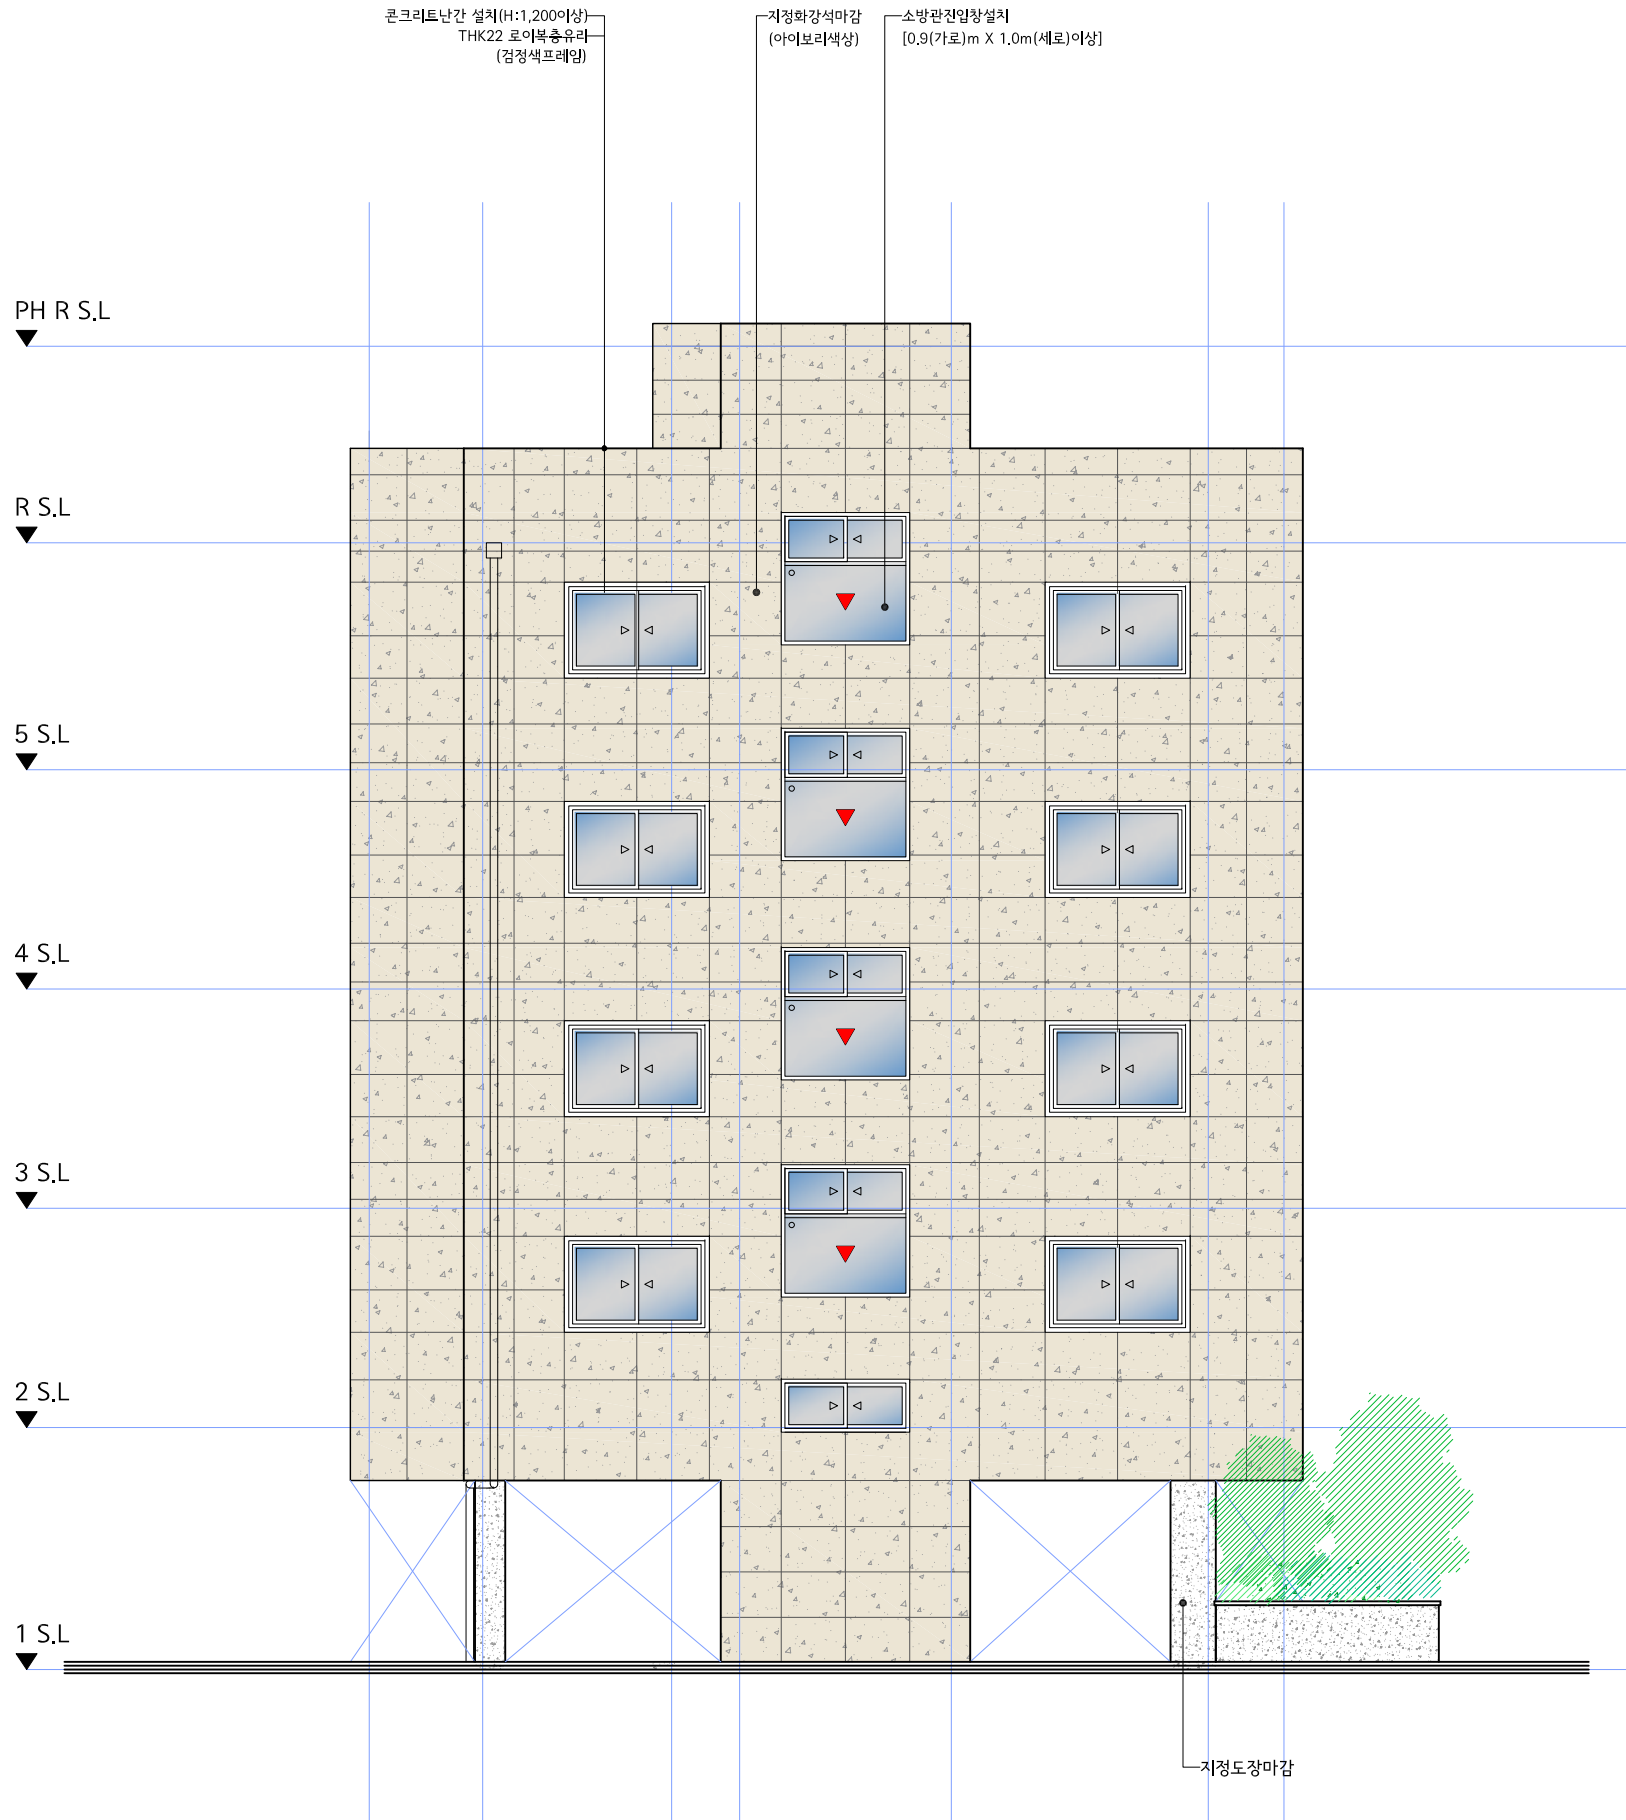

소방관 진입장 설치.
(건축법 제49조, 시행령 제 51조,
건축물의 피난·방화구조 등의 기준에 관한 규칙 제 18조 2)

타격지점 스티커	30
소방관 진입장 스티커 (빨간색)	200이상
소방관진입장규격 0.9(가로)m X 1.0m(세로)이상 바닥마감에서 하단부 0.8m이내 (난간이 설치된 노대 등에 설치시 1.2m이내)	



정 면 도(남측면도)
축척 : 1/100

PROJECT TITLE
공 사 명
강북구 수유동
391-26 외 1필지
단지형다세대주택
신 축 공 사

NOTE


△					
△					
△					
△					
△					
NO	DATE	REVISION DESCRIPTION	DRAWN	DATE	DATE




건축사 사무소
하늘 건축
Architects & Engineers

TEL : 02) 928 ~ 4484
FAX : 02) 928 ~ 4487

APPROVED 승 인	DATE
ARCHITECT 설 계	
CHKD 1 검 토	
CHKD 2 검 토	
DRAWN 담 당	
DATE 작성일	2025. 12.
SCALE 축 척	A3 : 1/100
TITLE 도면명	정 면 도(남측면도)
DRWG NO. 도면번호	A - 231
B.C.C.NO. 분류번호	SHEET NO. 일반번호
JOB NO. 작업번호	REV NO. △

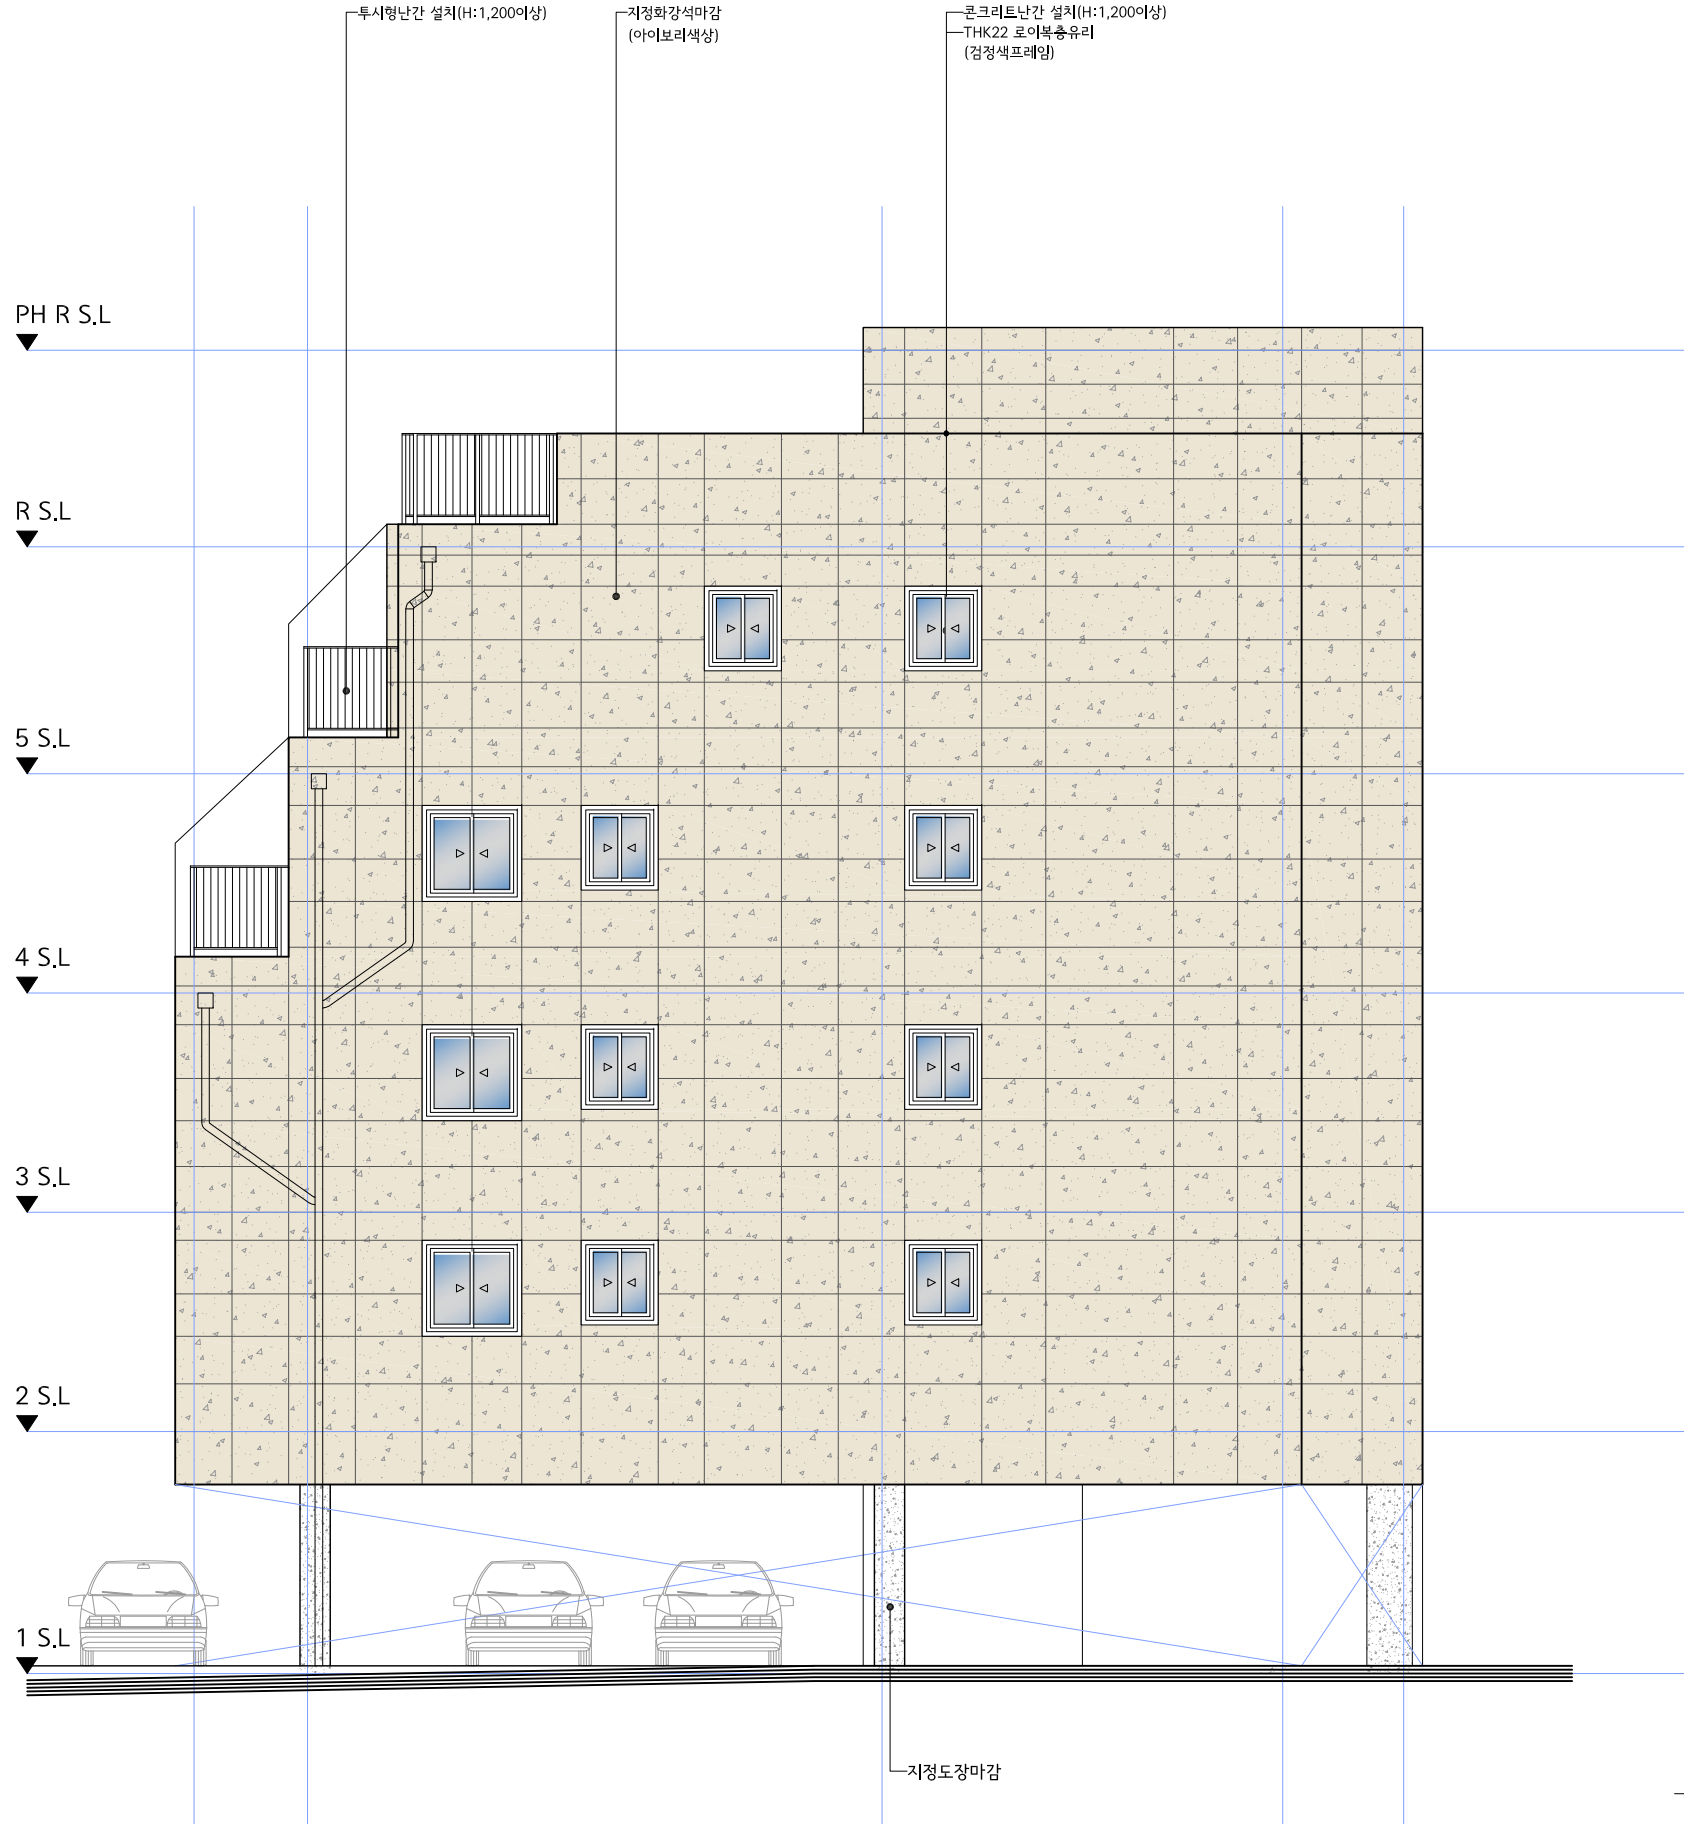

KEY PLAN

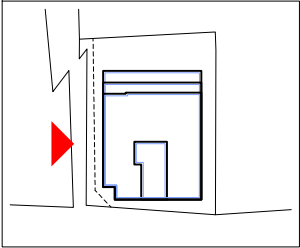

PROJECT TITLE
공 사 명
강북구 수유동
391-26 외 1필지
단지형다세대주택
신 축 공 사

NOTE

△					
△					
△					
△					
△					
NO	DATE	REVISION DESCRIPTION	DRAWN	DATE	DATE



건축사 사무소
하늘 건축
Architects & Engineers

TEL : 02) 928 ~ 4484
FAX : 02) 928 ~ 4487


APPROVED 승 인	DATE
ARCHITECT 설 계	
CHKD 1 검 토	
CHKD 2 검 토	
DRAWN 담 당	
DATE 작성일	2025. 12.
SCALE 축 척	A3 : 1/100
TITLE 도면명	좌측면도(서측면도)
DRWG NO. 도면번호	A - 232
B.C.C NO. 분류번호	SHEET NO. 일련번호
JOB NO. 작업번호	REV NO.

좌측면도(서측면도)

축척 : 1/100



■ KEY PLAN

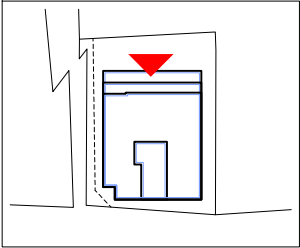

PROJECT TITLE

공 사 명

강북구 수유동
391-26 외 1필지
단지형다세대주택
신 축 공 사

NOTE


△					
△					
△					
△					
△					
NO	DATE	REVISION DESCRIPTION	DRAWN	DATE	DATE



건축사 사무소
하늘 건축
Architects & Engineers


TEL : 02) 928 ~ 4484
FAX : 02) 928 ~ 4487

APPROVED 승 인	DATE
ARCHITECT 설 계	
CHKD 1 검 토	
CHKD 2 검 토	
DRAWN 담 당	
DATE 작성일	2025. 12.
SCALE 축 척	A3 : 1/100
TITLE 도면명	배 면 도(북측면도)
DRWG NO. 도면번호	A - 233
B.C.C NO. 분류번호	SHEET NO. 일련번호
JOB NO. 작업번호	REV NO.

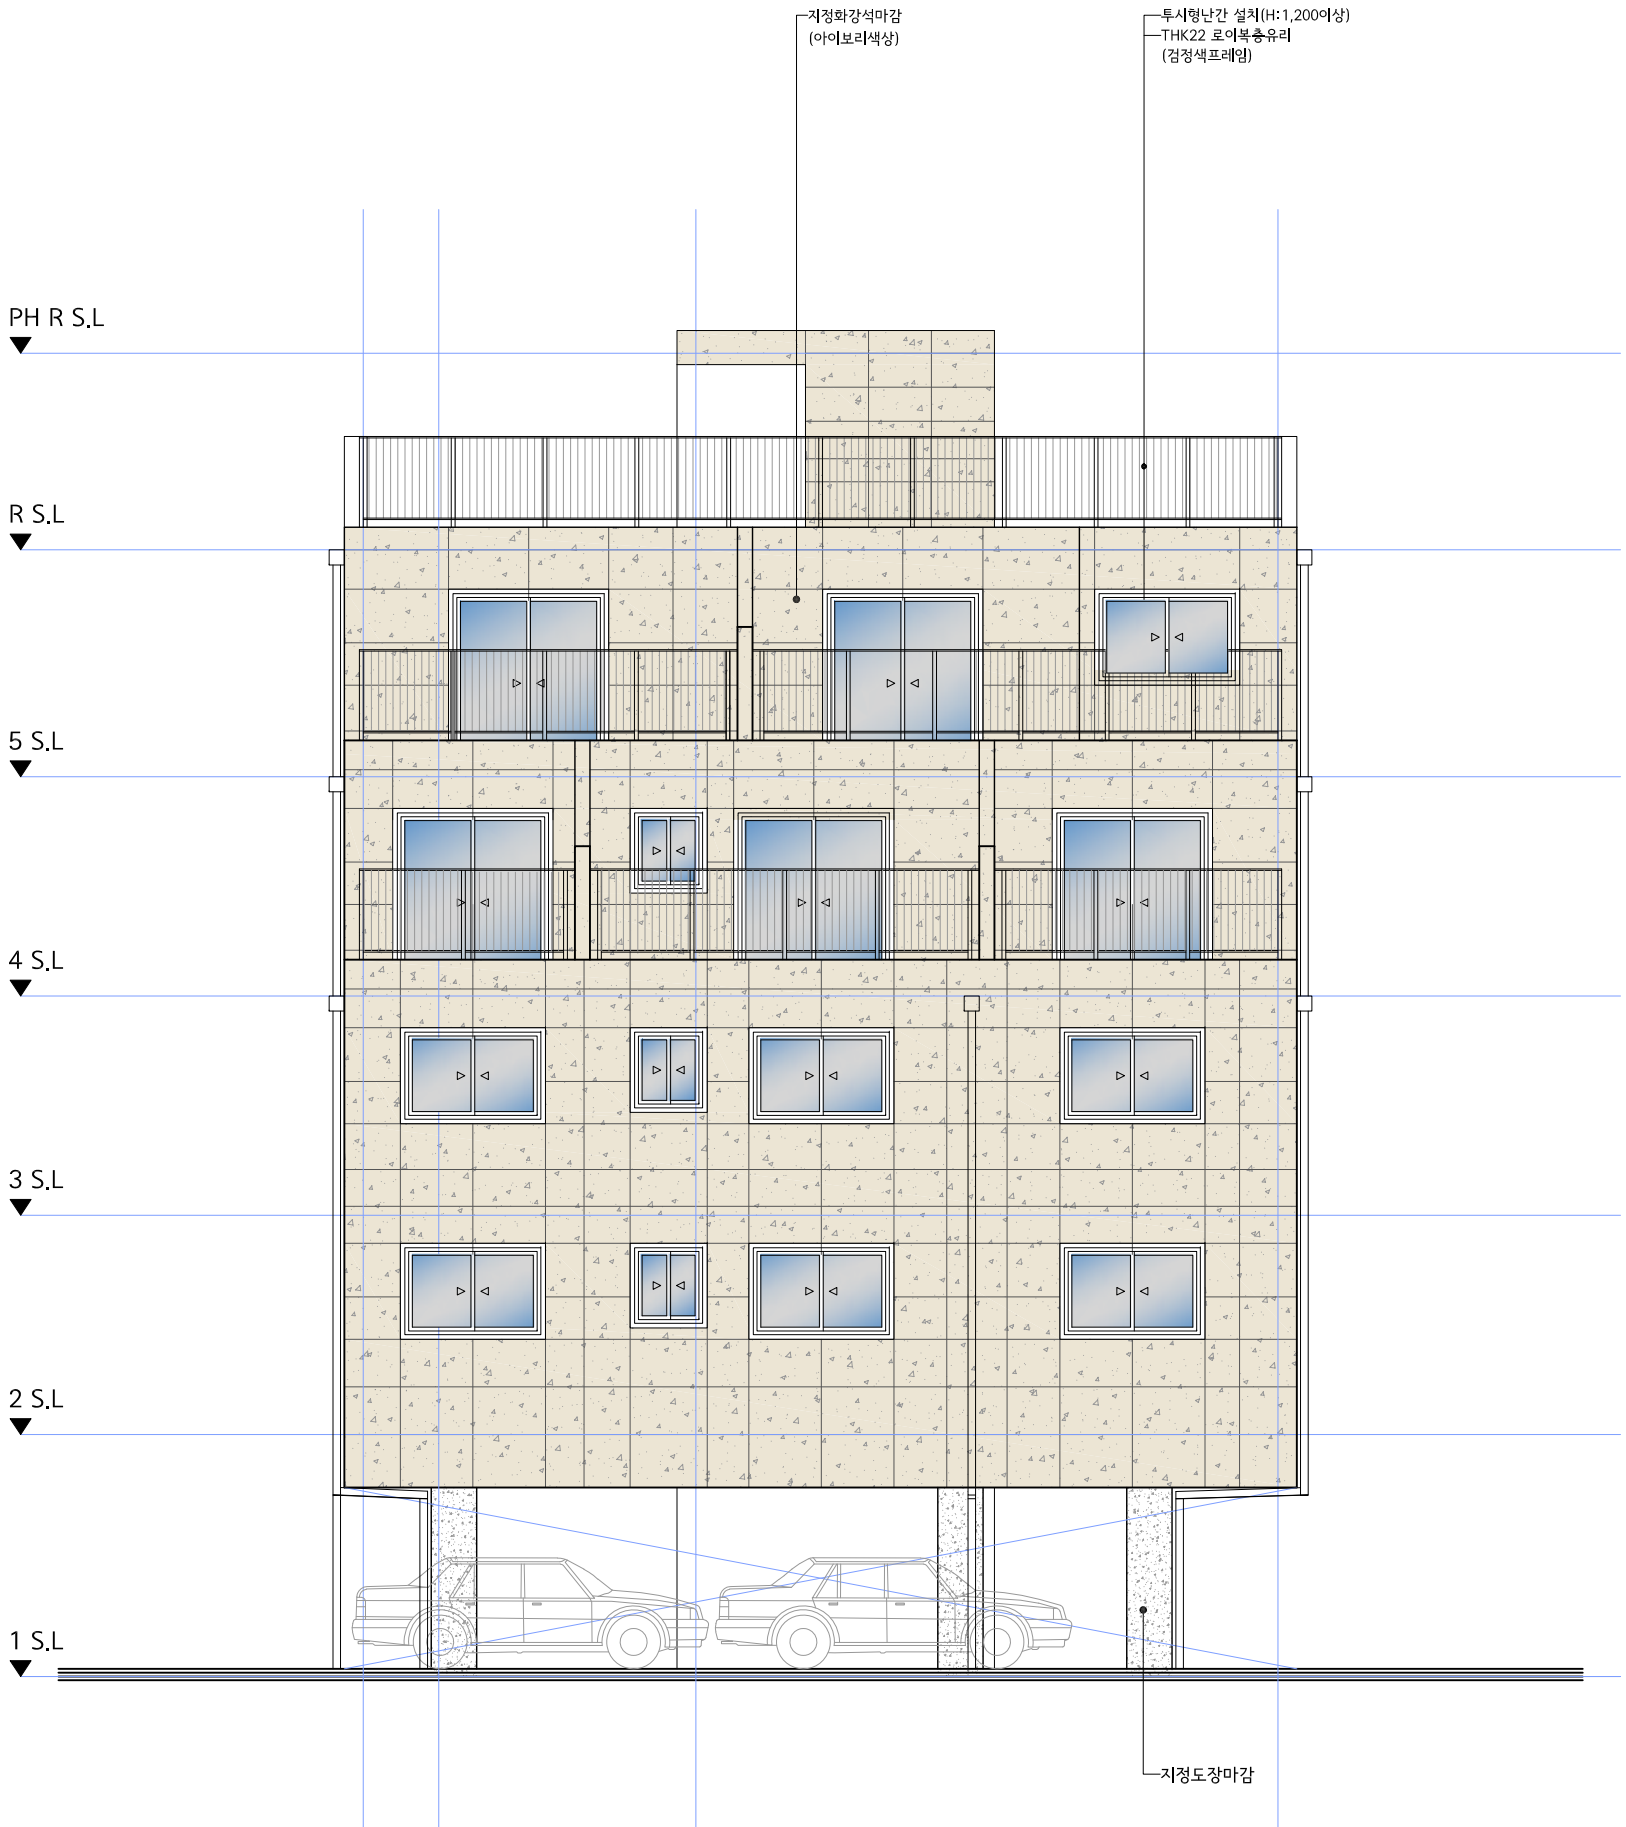


배 면 도(북측면도)

축척 : 1/100

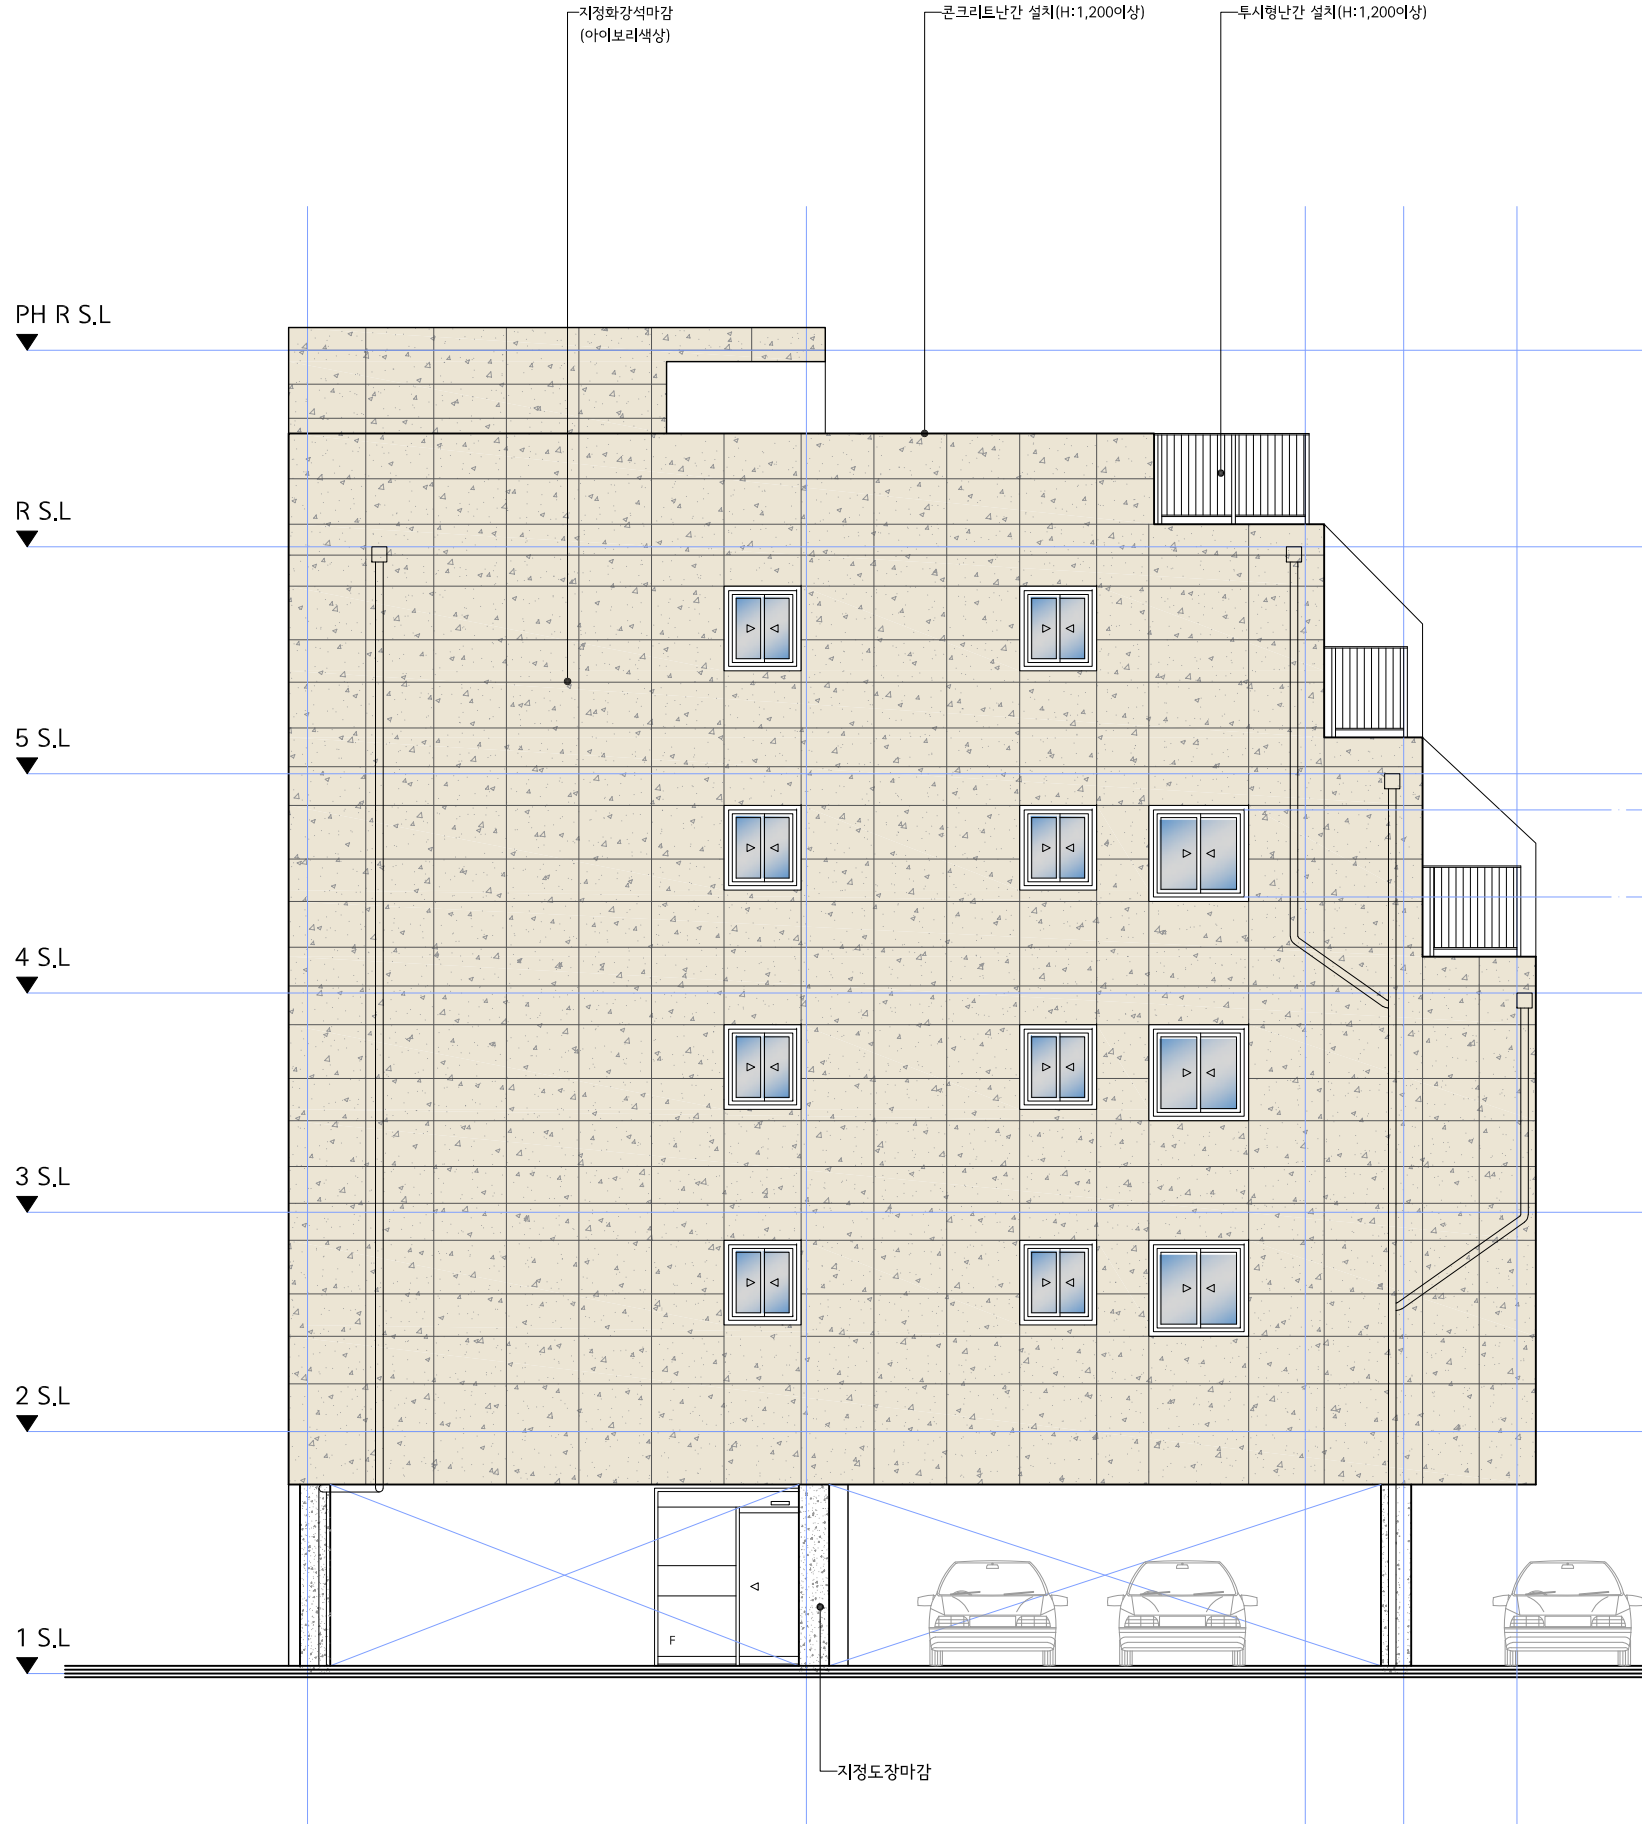

■ KEY PLAN

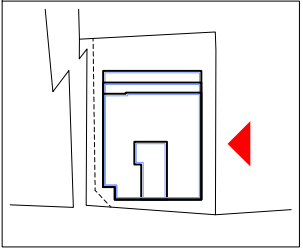

PROJECT TITLE

공 사 명

강북구 수유동
391-26 외 1필지
단지형다세대주택
신 축 공 사

NOTE

△					
△					
△					
△					
△					
NO	DATE	REVISION DESCRIPTION	DRAWN	DATE	DATE



건축사 사무소
하늘 건축
Architects & Engineers


TEL : 02) 928 ~ 4484
FAX : 02) 928 ~ 4487

APPROVED 승 인	DATE
ARCHITECT 설 계	
CHKD 1 검 토	
CHKD 2 검 토	
DRAWN 담 당	
DATE 작 성 일	2025. 12.
SCALE 축 척	A3 : 1/100
TITLE 도 면 명	우측면도(동측면도)
DRWG NO. 도 면 번 호	A - 234
B.C.C NO. 분류번호	SHEET NO. 일반번호
JOB NO. 작업번호	REV NO.




우측면도(동측면도)


축척 : 1/100

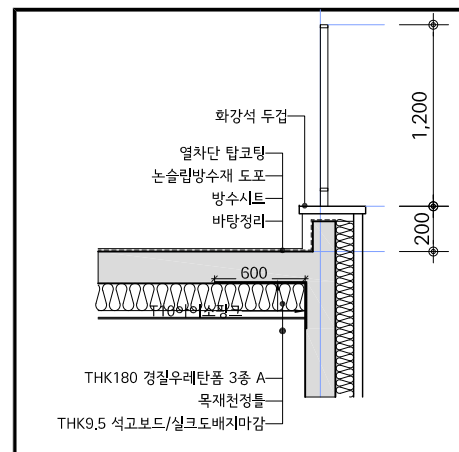


1	파라펫 상세도
---	---------

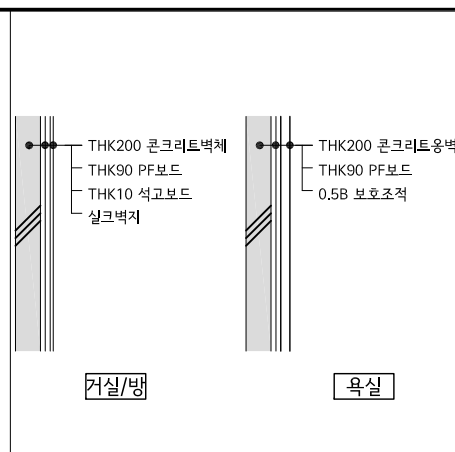


5 | 간접외기벽체상세도

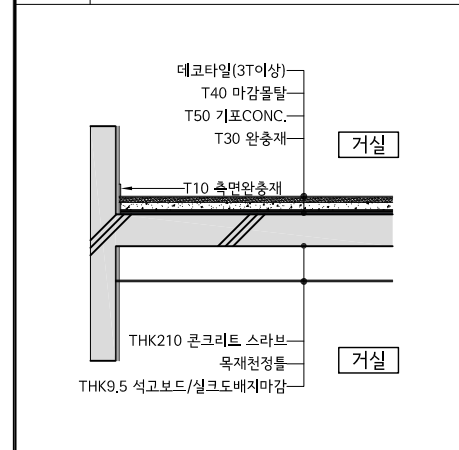


2 표준바닥마감상세도

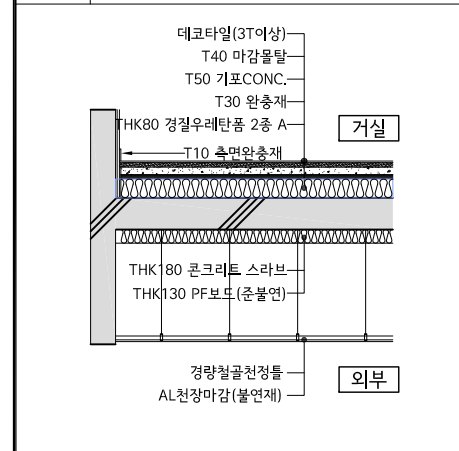


3 | 2층바닥마감상세도

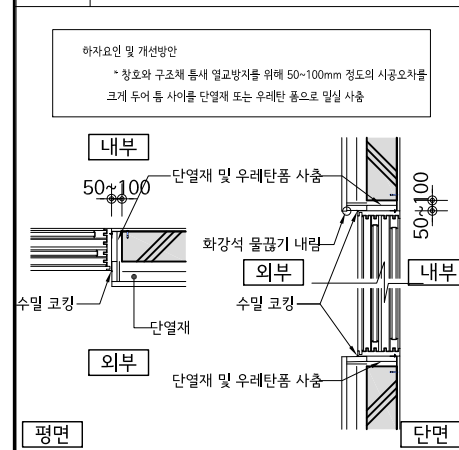

4 창호설치 단면상세도 - 석재마감

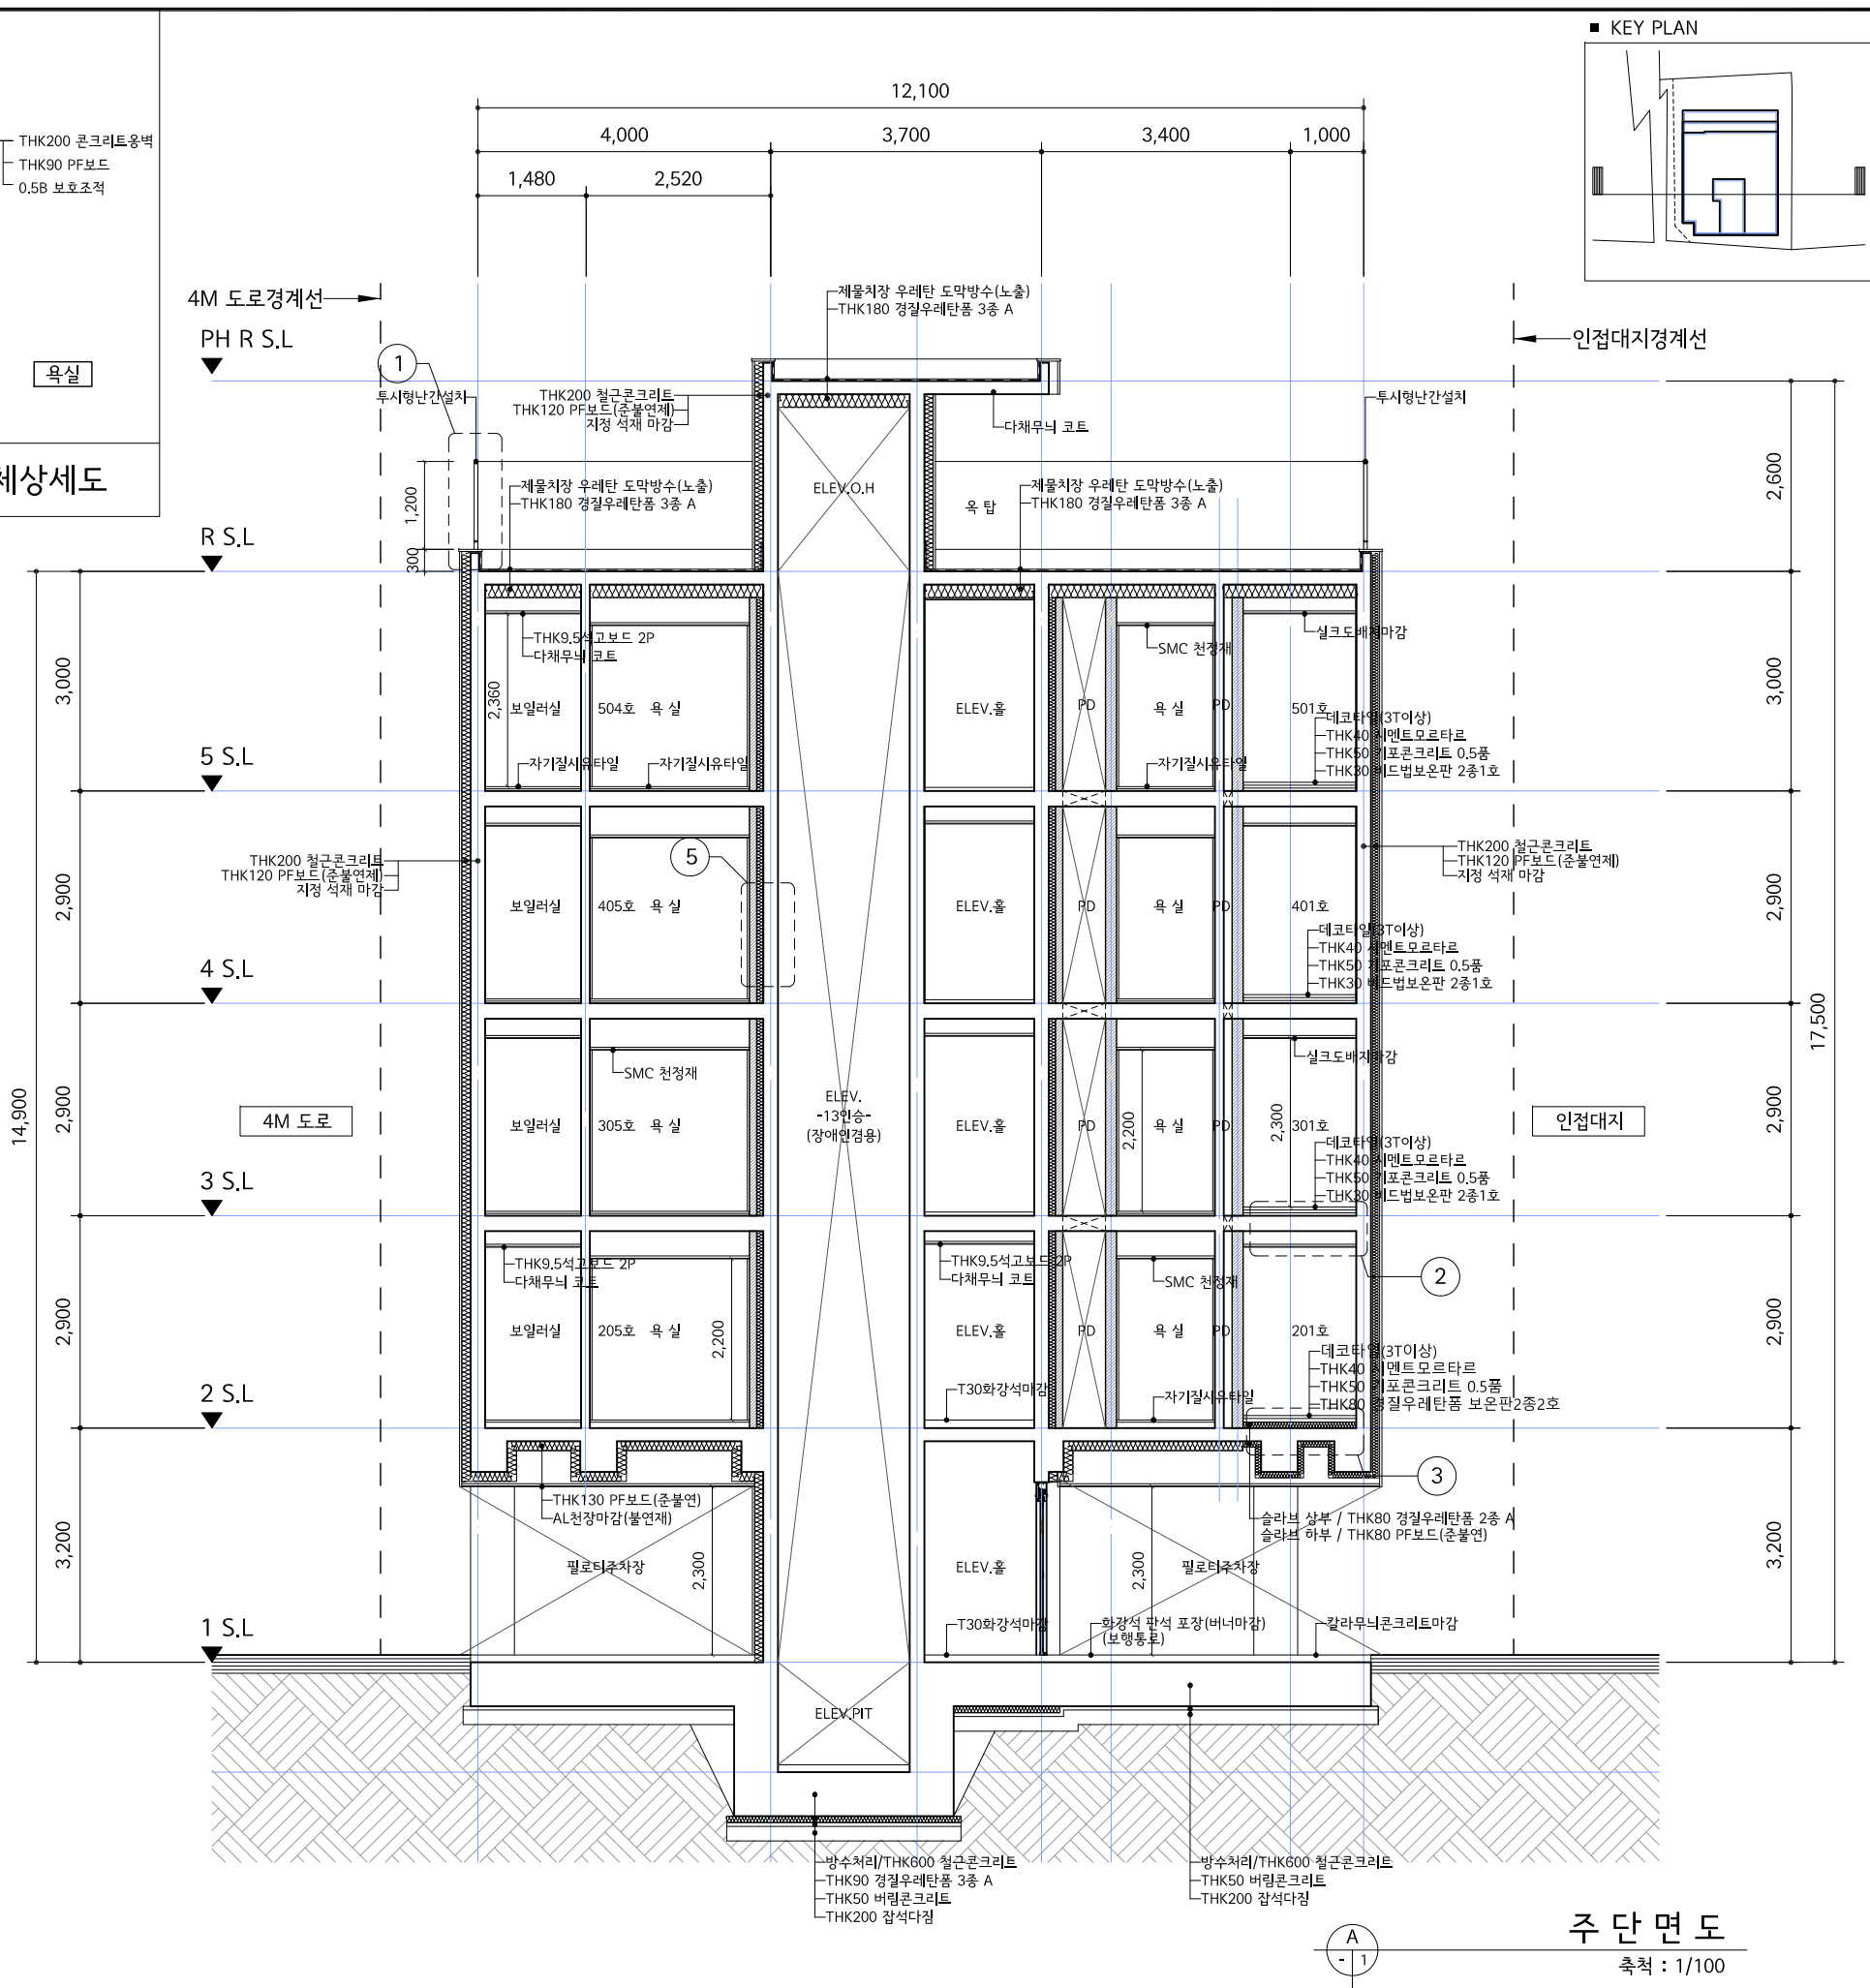


주 단 면 도
축척 : 1/100

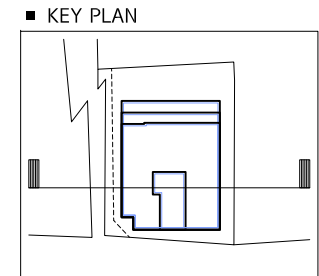

PROJECT TITLE
공 사 명
강북구 수유동
391-26 외 1필지
단지형다세대주택
신 축 공 사

NOTE
※외부 단열재 : 준불연

						
NO	DATE	REVISION DESCRIPTION	DRAWN	DATE	DATE	

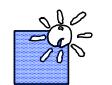

건축사 사무소
하늘 건축
Architects & Engineers

TEL : 02) 928 ~ 4484
FAX : 02) 928 ~ 4487

APPROVED 승 인	DATE
ARCHITECT 설 계	
CHKD 1 검 토	
CHKD 2 검 토	
DRAWN 담 당	

2025. 12.

SCALE
축척
A3 : 1/100

TITLE
도면명

주 단 면 도

DRWG NO.
도면번호

A - 251

분류번호

JOB NO.
작업번호

PROJECT TITLE 공 사 명 강북구 수유동 391-26 외 1필지 단지형다세대주택 신 축 공 사				
NOTE ※외부 단열재 : 준불연				
△			△	
△			△	
△			△	
△			△	
△			△	
NO	DATE	REVISION DESCRIPTION	DRAW DATE	DATE
 건축사 사무소 아 늘 건 축 Architects & Engineers TEL : 02) 928 ~ 4484 FAX : 02) 928 ~ 4487				
APPROVED 승 인 ARCHITECT 설 계 C H K D 1 검 토 C H K D 2 검 토			DATE	
D R A W N 담 당				
DATE 작성일 2025. 12.				
SCALE 축 적 A3 : 1/100				
TITLE 도 면 명 계 단 단 면 도				
DRWG NO. 도 원 번호 A - 252				
B.C.C.NO. 부류번호			SHEET NO. 일련번호	
JOB NO. 작업번호			REV NO. 	