

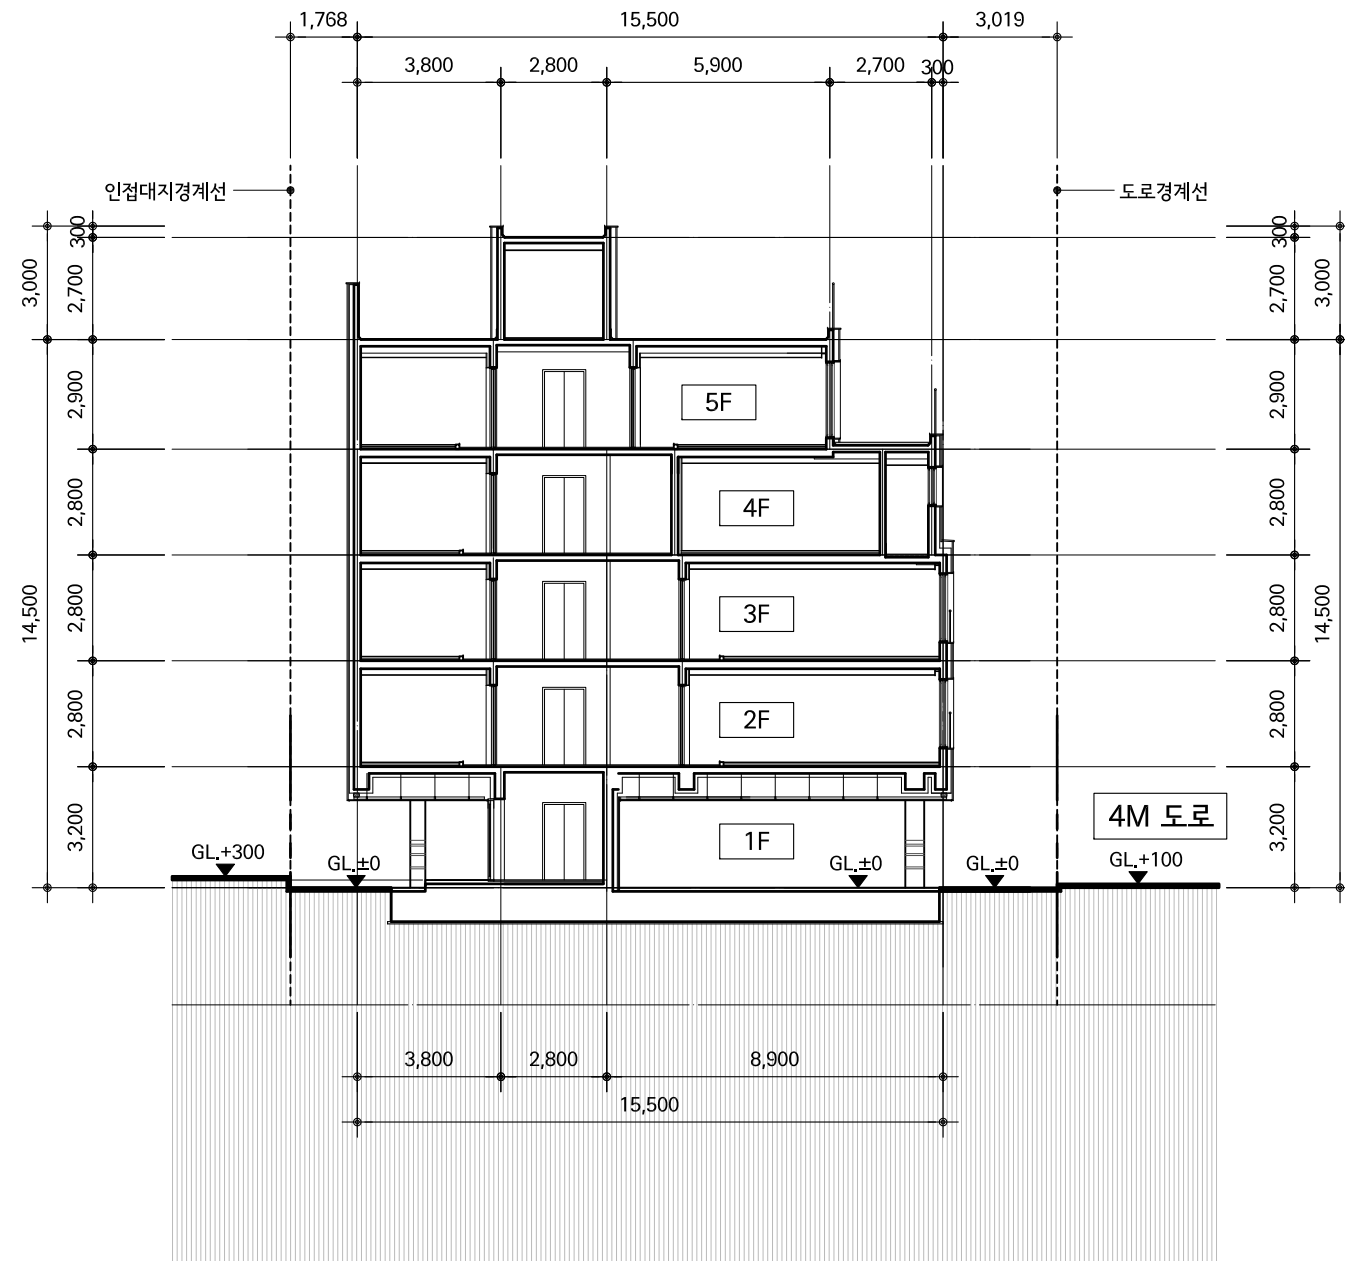


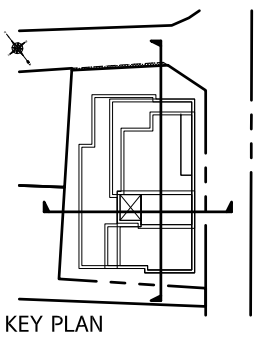


PHR SL.
▼
PH SL.
▼
5TH SL.
▼
4TH SL.
▼
3RD SL.
▼
2ND SL.
▼
1ST SL.
▼

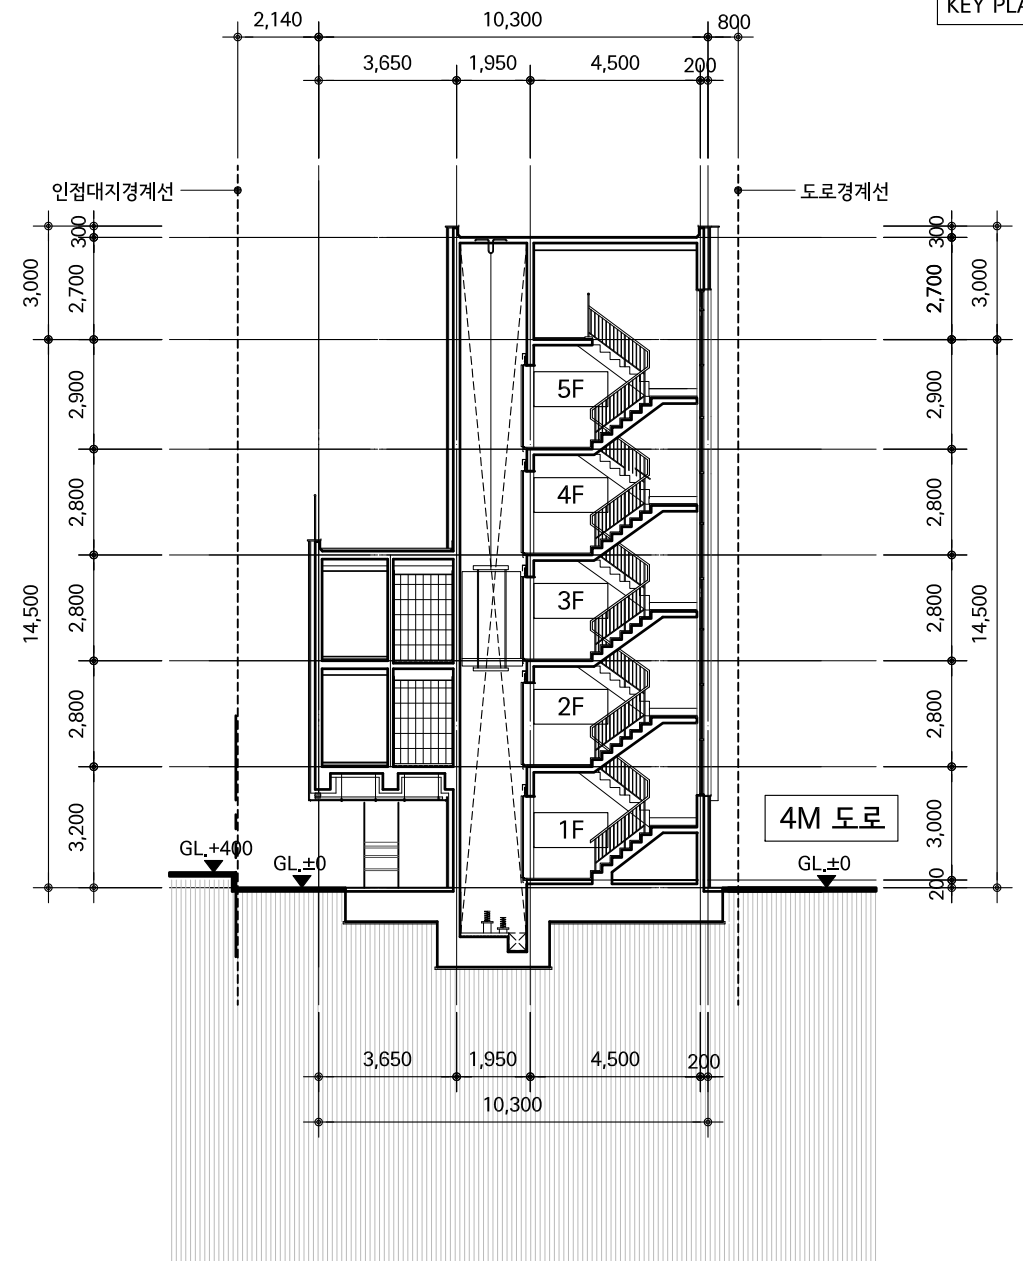

대지 '종' 단면도
SCALE = 1/200

대지 '횡' 단면도
SCALE = 1/200

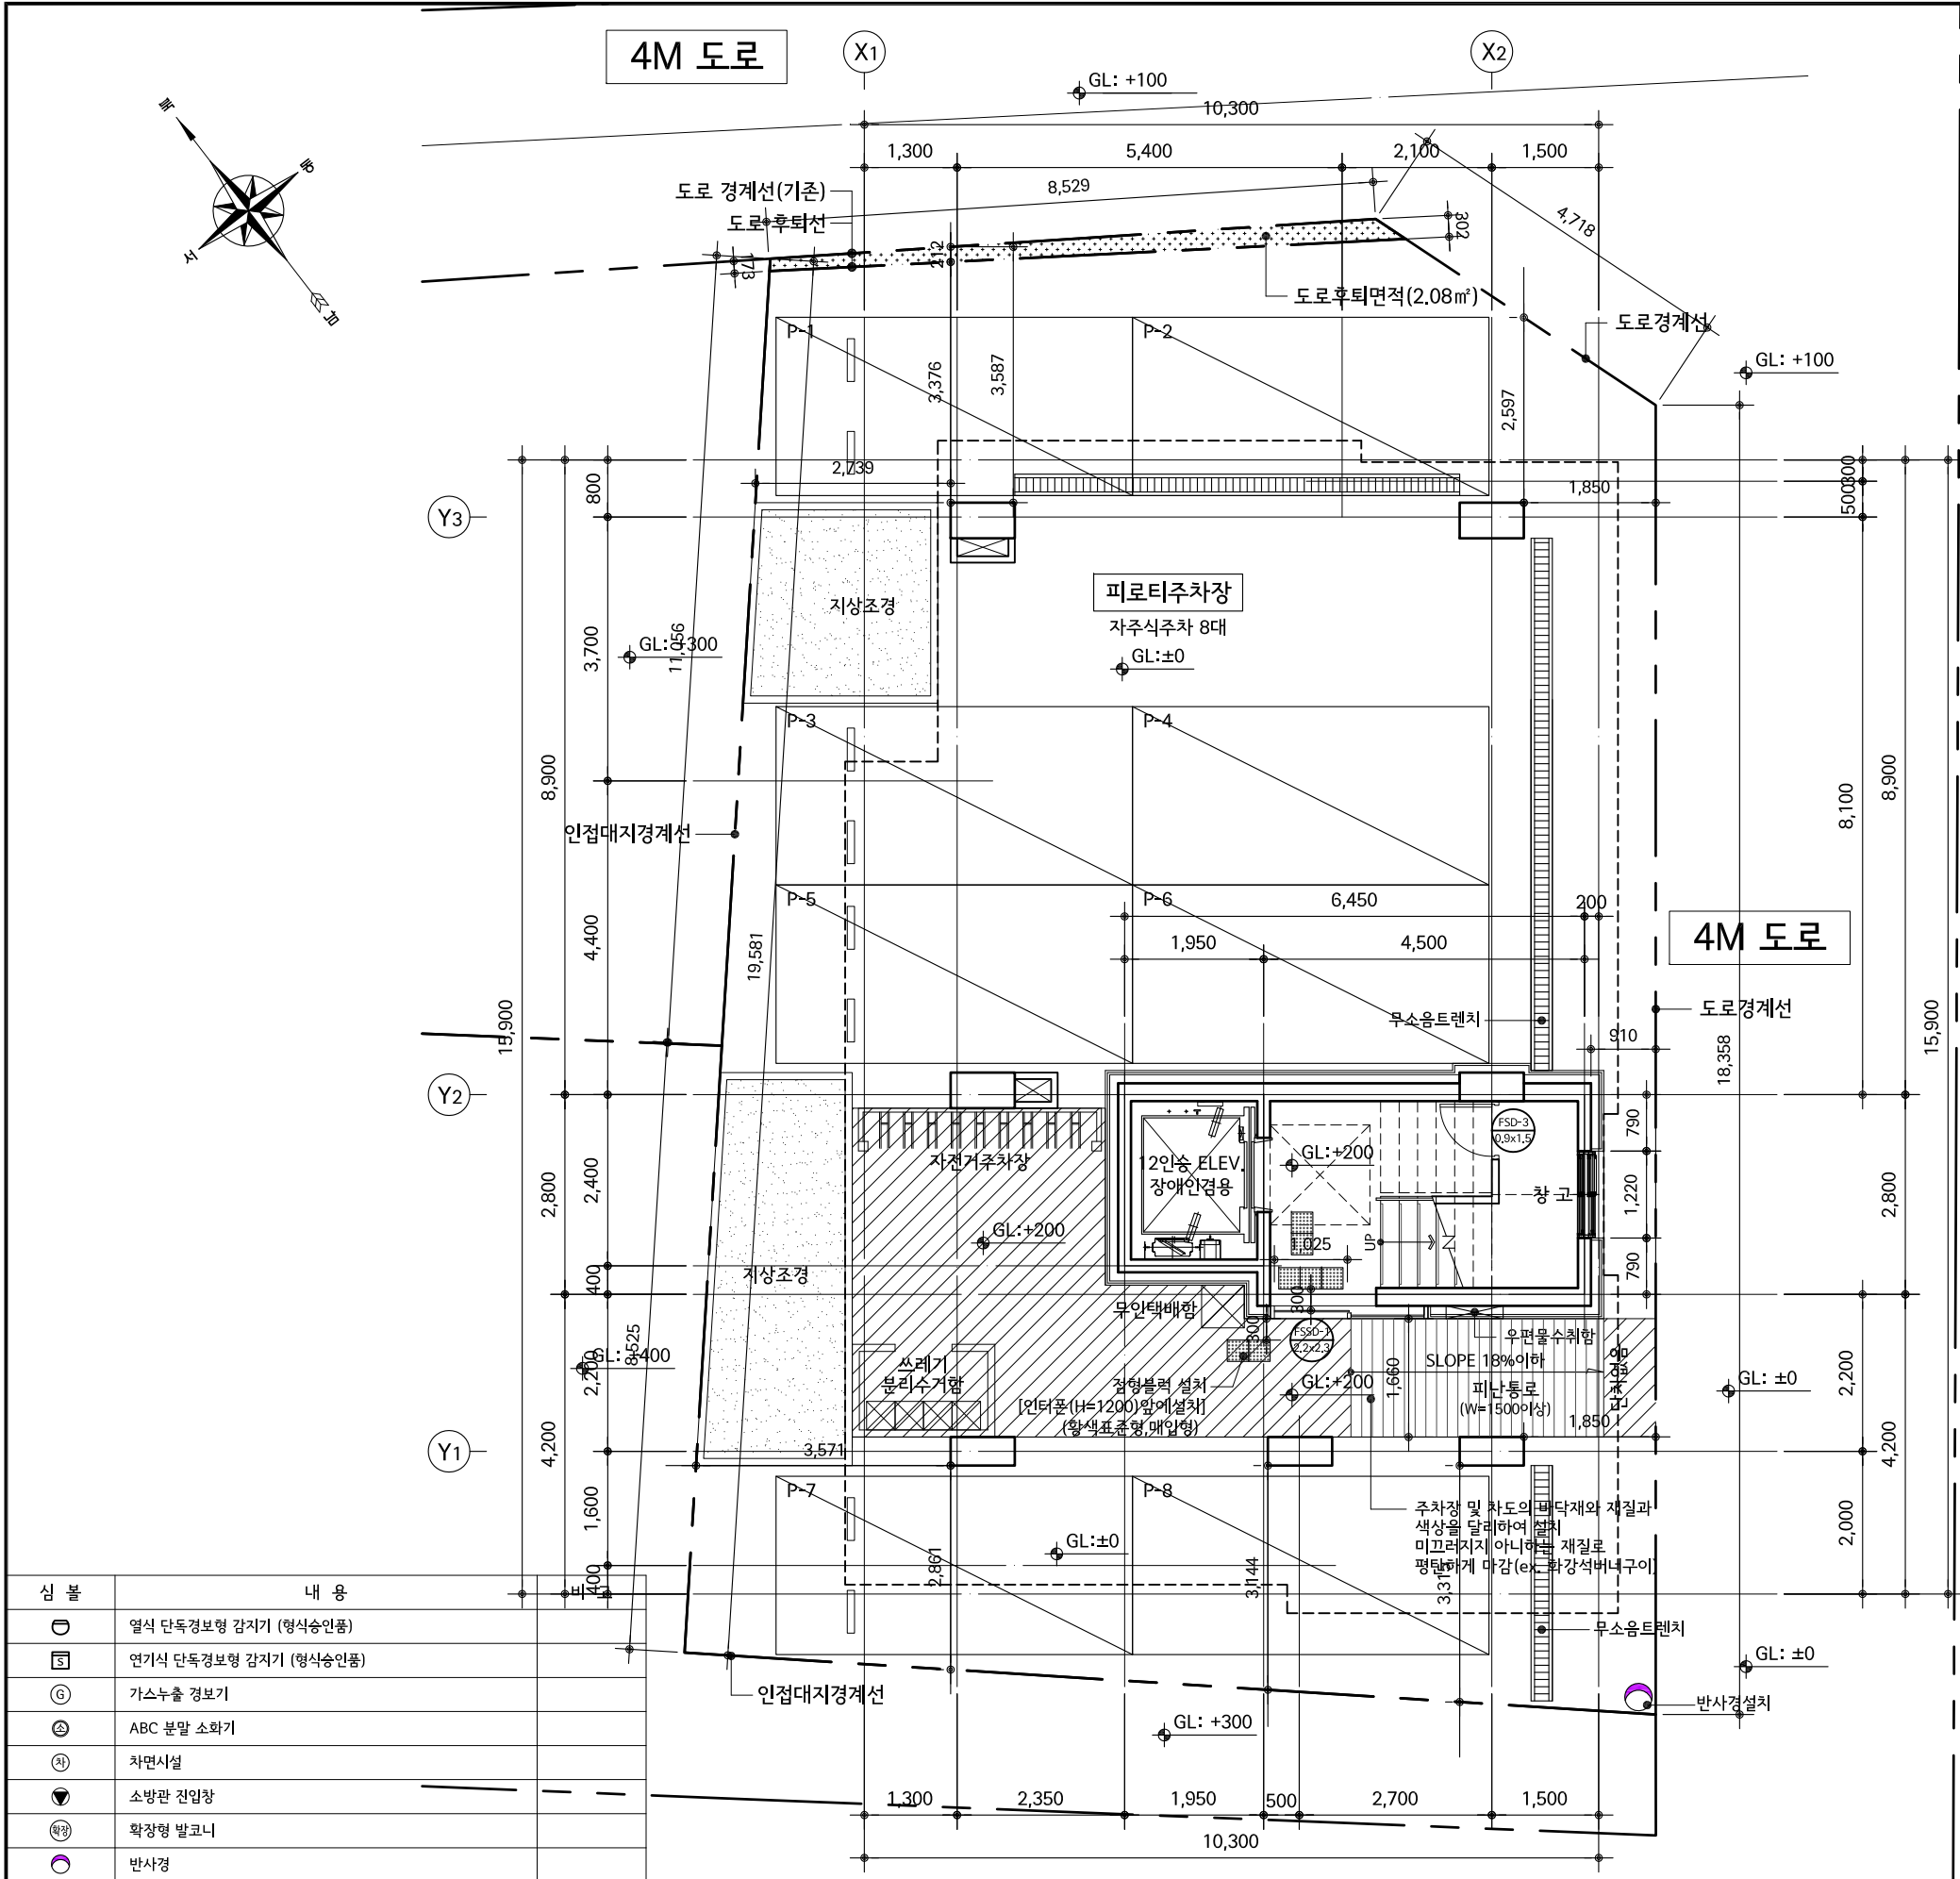


심볼	내용
⊖	열식 단독경보형 감지기 (형식승인품)
☐	연기식 단독경보형 감지기 (형식승인품)
⊙	가스누출 경보기
⊕	ABC 분말 소화기
④	차면시설
☑	소방관 진입창
Ⓢ	확장형 발코니
○	반사경

주 기

건	1 (외부)	주차장내 CCTV,쓰레기분리수거,자전거보관대 설치 우편함 설치 (세대전용, 공용, 반송용, 폐전지함 구분 설치) 세대 테라스 설치시 세대간 분리벽 계획 세대 발코니 설치시 차양시설 설치 세대내 비디오폰 설치
	2 (계단실)	세대 현관문 도어체크 및 스토퍼 설치 계단창의 현관과 계단 이격거리 (최소600mm이상)
	3 (내부)	Built in 가구(불박이장, 책상) 설치 전자제품(벽걸이에어컨, 냉장고, 세탁기) 설치 에어컨 실외기 설치위치 및 에어컨 콘센트, 냉매 및 배수관 위치 도면표기(배수관 수직으로 매립) ● - 에어컨 콘센트 표기
	4 (시공)	콘크리트 톱타이 제거 후 마감공사 시공 (방수, 단열재 시공 등) 욕실 & 다용도실 스위치 : 문 열리는 방향으로 시공 주차장 차량 진출입구간,화장실 무소음트렌치 시공
	5 (마감)	-직접외기(외벽)에 면한 실내벽면 단열재 [아이소핑크(10mm) + 석고보드 마감도면 표기] -계단실,복도에 면한 실내벽면 단열재(방풍설치시) [아이소핑크(20mm) + 석고보드 마감도면 표기] *기타 실내 벽면 시멘트 미장 마감
구 조	1	철근 : $f_y=400\text{Mpa}$ (HD16이하), $f_y=500\text{Mpa}$ (HD19이상) 콘크리트 : $f_{ck}=30\text{Mpa}$
	2	스라브두께 : 210mm (복배근) 이상 외벽벽두께 : 180mm (복배근) 이상 내벽두께 : 150mm (복배근) 이상 비내력벽두께 : 100mm (단배근) 이상
전 기	1	-콘센트 설치 (바닥 마감선 기준) 스탠드형 에어컨 : 350 벽걸이형 에어컨 : 1900 [화장실] 양변기 옆 : 900 [주방] 조리대 : 중앙 / 냉장고 : 350 / 후드 : 2100
	2	-비디오폰(VP),보일러온도조절기(B), 스위치(S) 설치 (거실 아트홀 위치)
	3	-위치 표기 에어컨 실외기 에어컨 콘센트 냉매, 배수관 (배수관수직매립)
비 고		우편함 규격은 관련법규에 맞추어 적절한 위치에 설치하고 세대전용,공용,반송용,폐전지함으로 구분 설치한다. 난간대에 국기봉을 설치한다


지상1층 평면도
SCALE = 1/100

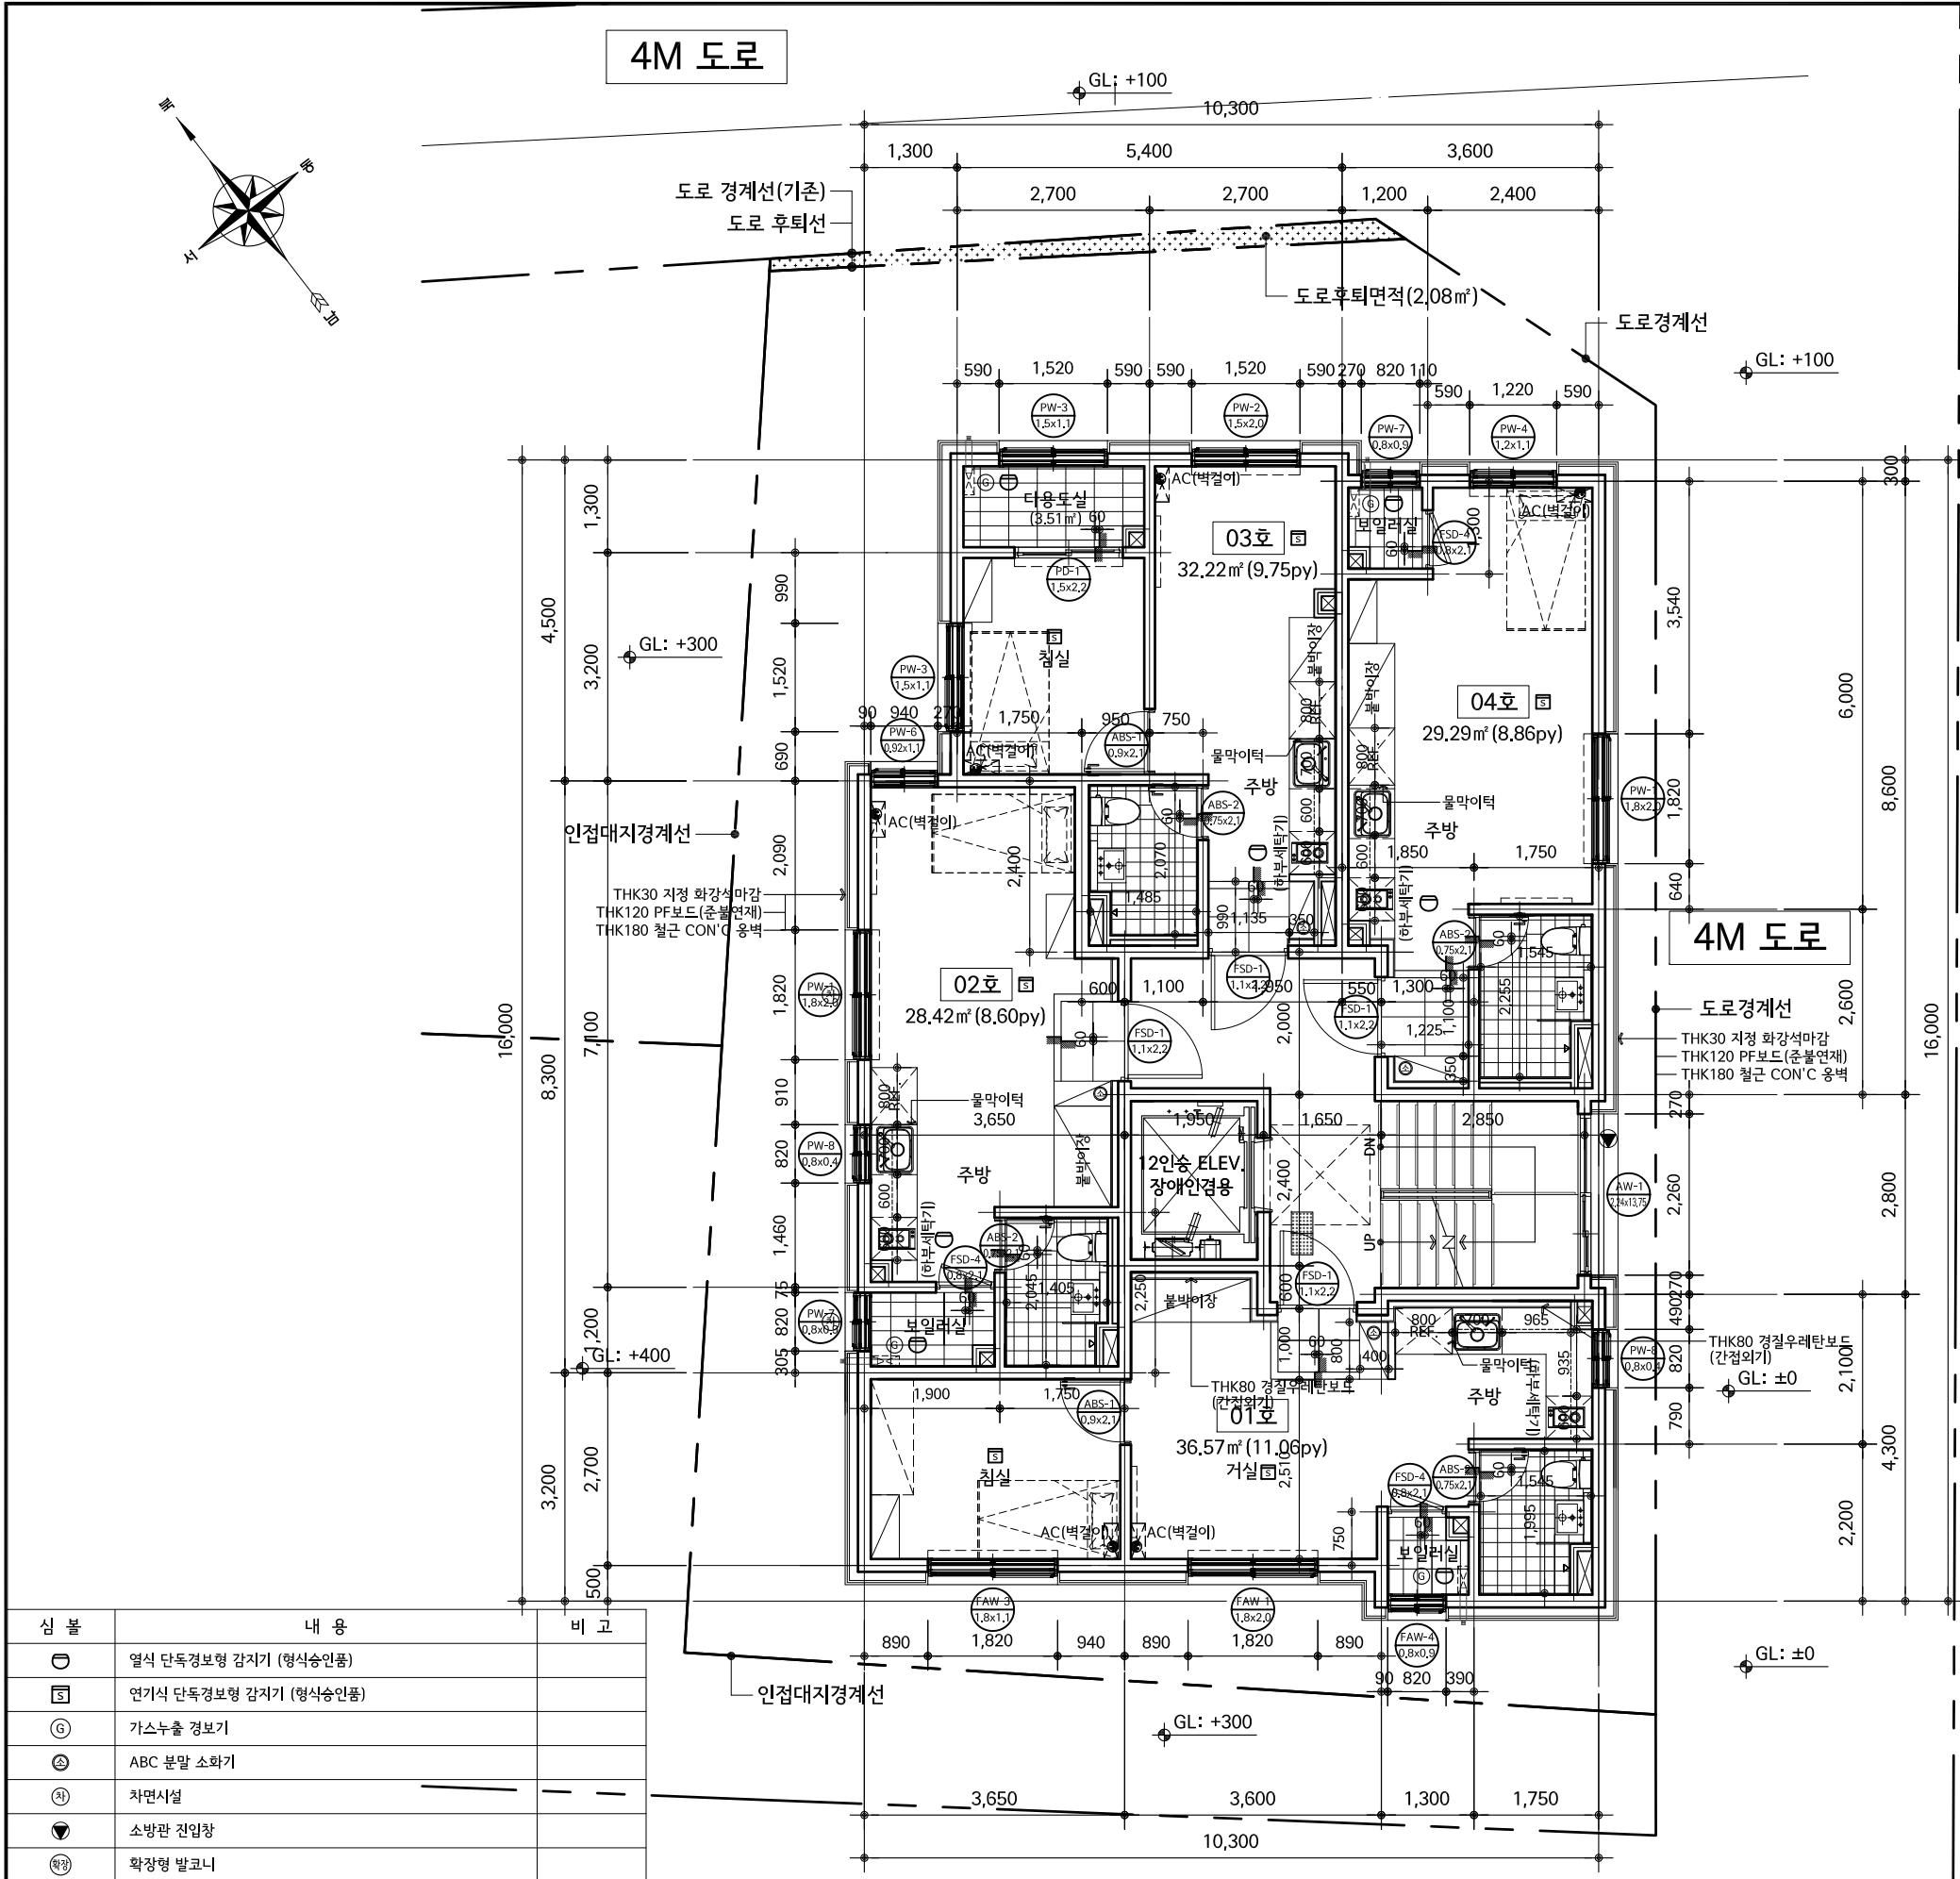

심볼	내용	비고
⊖	열식 단독경보형 감지기 (형식승인품)	
⊞	연기식 단독경보형 감지기 (형식승인품)	
⊙	가스누출 경보기	
⊗	ABC 분말 소화기	
차	차면시설	
▼	소방관 진입창	
확	확장형 발코니	

주 기


건	1 (외부)	주차장내 CCTV,쓰레기분리수거,자전거보관대 설치 우편함 설치 (세대전용, 공용, 반송용, 폐전지함 구분 설치) 세대 테라스 설치시 세대간 분리벽 계획 세대 발코니 설치시 차양시설 설치 세대내 비디오폰 설치
	2 (계단실)	세대 현관문 도어체크 및 스토퍼 설치 계단참의 현관과 계단 이격거리 (최소600mm이상)
	3 (내부)	Built in 가구(불박이장, 책상) 설치 전자제품(벽걸이에어컨, 냉장고, 세탁기) 설치 에어컨 실외기 설치위치 및 에어컨 콘센트, 냉매 및 배수관 위치 도면표기(배수관 수직으로 매립) ● - 에어컨 콘센트 표기
	4 (시공)	콘크리트 토탈이 제거 후 마감공사 시공 (방수, 단열재 시공 등) 욕실 & 다용도실 스위치 : 문 열리는 방향으로 시공 주차장 차랑 진출입구간,화장실 무소음트렌치 시공
	5 (마감)	-직접외기(외벽)에 면한 실내벽면 단열재 [아이소핑크(10mm) + 석고보드 마감도면 표기] -계단실,복도에 면한 실내벽면 단열재(방풍설치시) [아이소핑크(20mm) + 석고보드 마감도면 표기] *기타 실내 벽면 시멘트 미장 마감
구 조	1	철근 : fy=400Mpa(HD16이하),fy=500Mpa(HD19이상) 콘크리트 : fck=30Mpa
	2	스라브두께 : 210mm (복배근) 이상 외벽벽두께 : 180mm (복배근) 이상 내벽두께 : 150mm (복배근) 이상 비내력벽두께 : 100mm (단배근) 이상
전 기	1	-콘센트 설치 (바닥 마감선 기준) 스탠드형 에어컨 : 350 벽걸이형 에어컨 : 1900 [화장실] 양변기 옆 : 900 [주방] 조리대 : 중앙 / 냉장고 : 350 / 후드 : 2100
	2	-비디오폰(VP),보일러온도조절기(B), 스위치(S) 설치 (거실 아트홀 위치)
	3	-위치 표기 에어컨 실외기 에어컨 콘센트 냉매, 배수관 (배수관수직매립)
비 고		우편함 규격은 관련법규에 맞추어 적절한 위치에 설치하고 세대전용,공용,반송용,폐전지함으로 구분 설치한다. 난간대에 국기봉을 설치한다

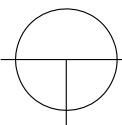


지상2~3층 평면도

SCALE = 1/100

 hanndas Architects & Interiors 안방광역시 연수구 남달로59번길 6-12, 2층 T_032-404-8775 F_032-881-9102	PROJECT TITLE 수유동 270-114 도시형생활주택(소형주택) 신축공사 -청년주택-	NAME OF DRAWING. 지상2~3층 평면도	제 도 DRAWN BY 설 계 DESIGNED BY 사 사 CHECKED BY 승 인 APPROVED BY 건축사 이선영	발행사항 ISSUER & REVISIONS	주 기 사항 NOTE	SCALE. A3: 1 / 100 DATE.	DRAWING NUMBER A - 1 0 2

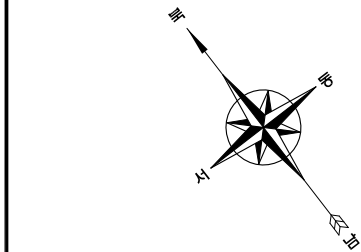

4M 도로

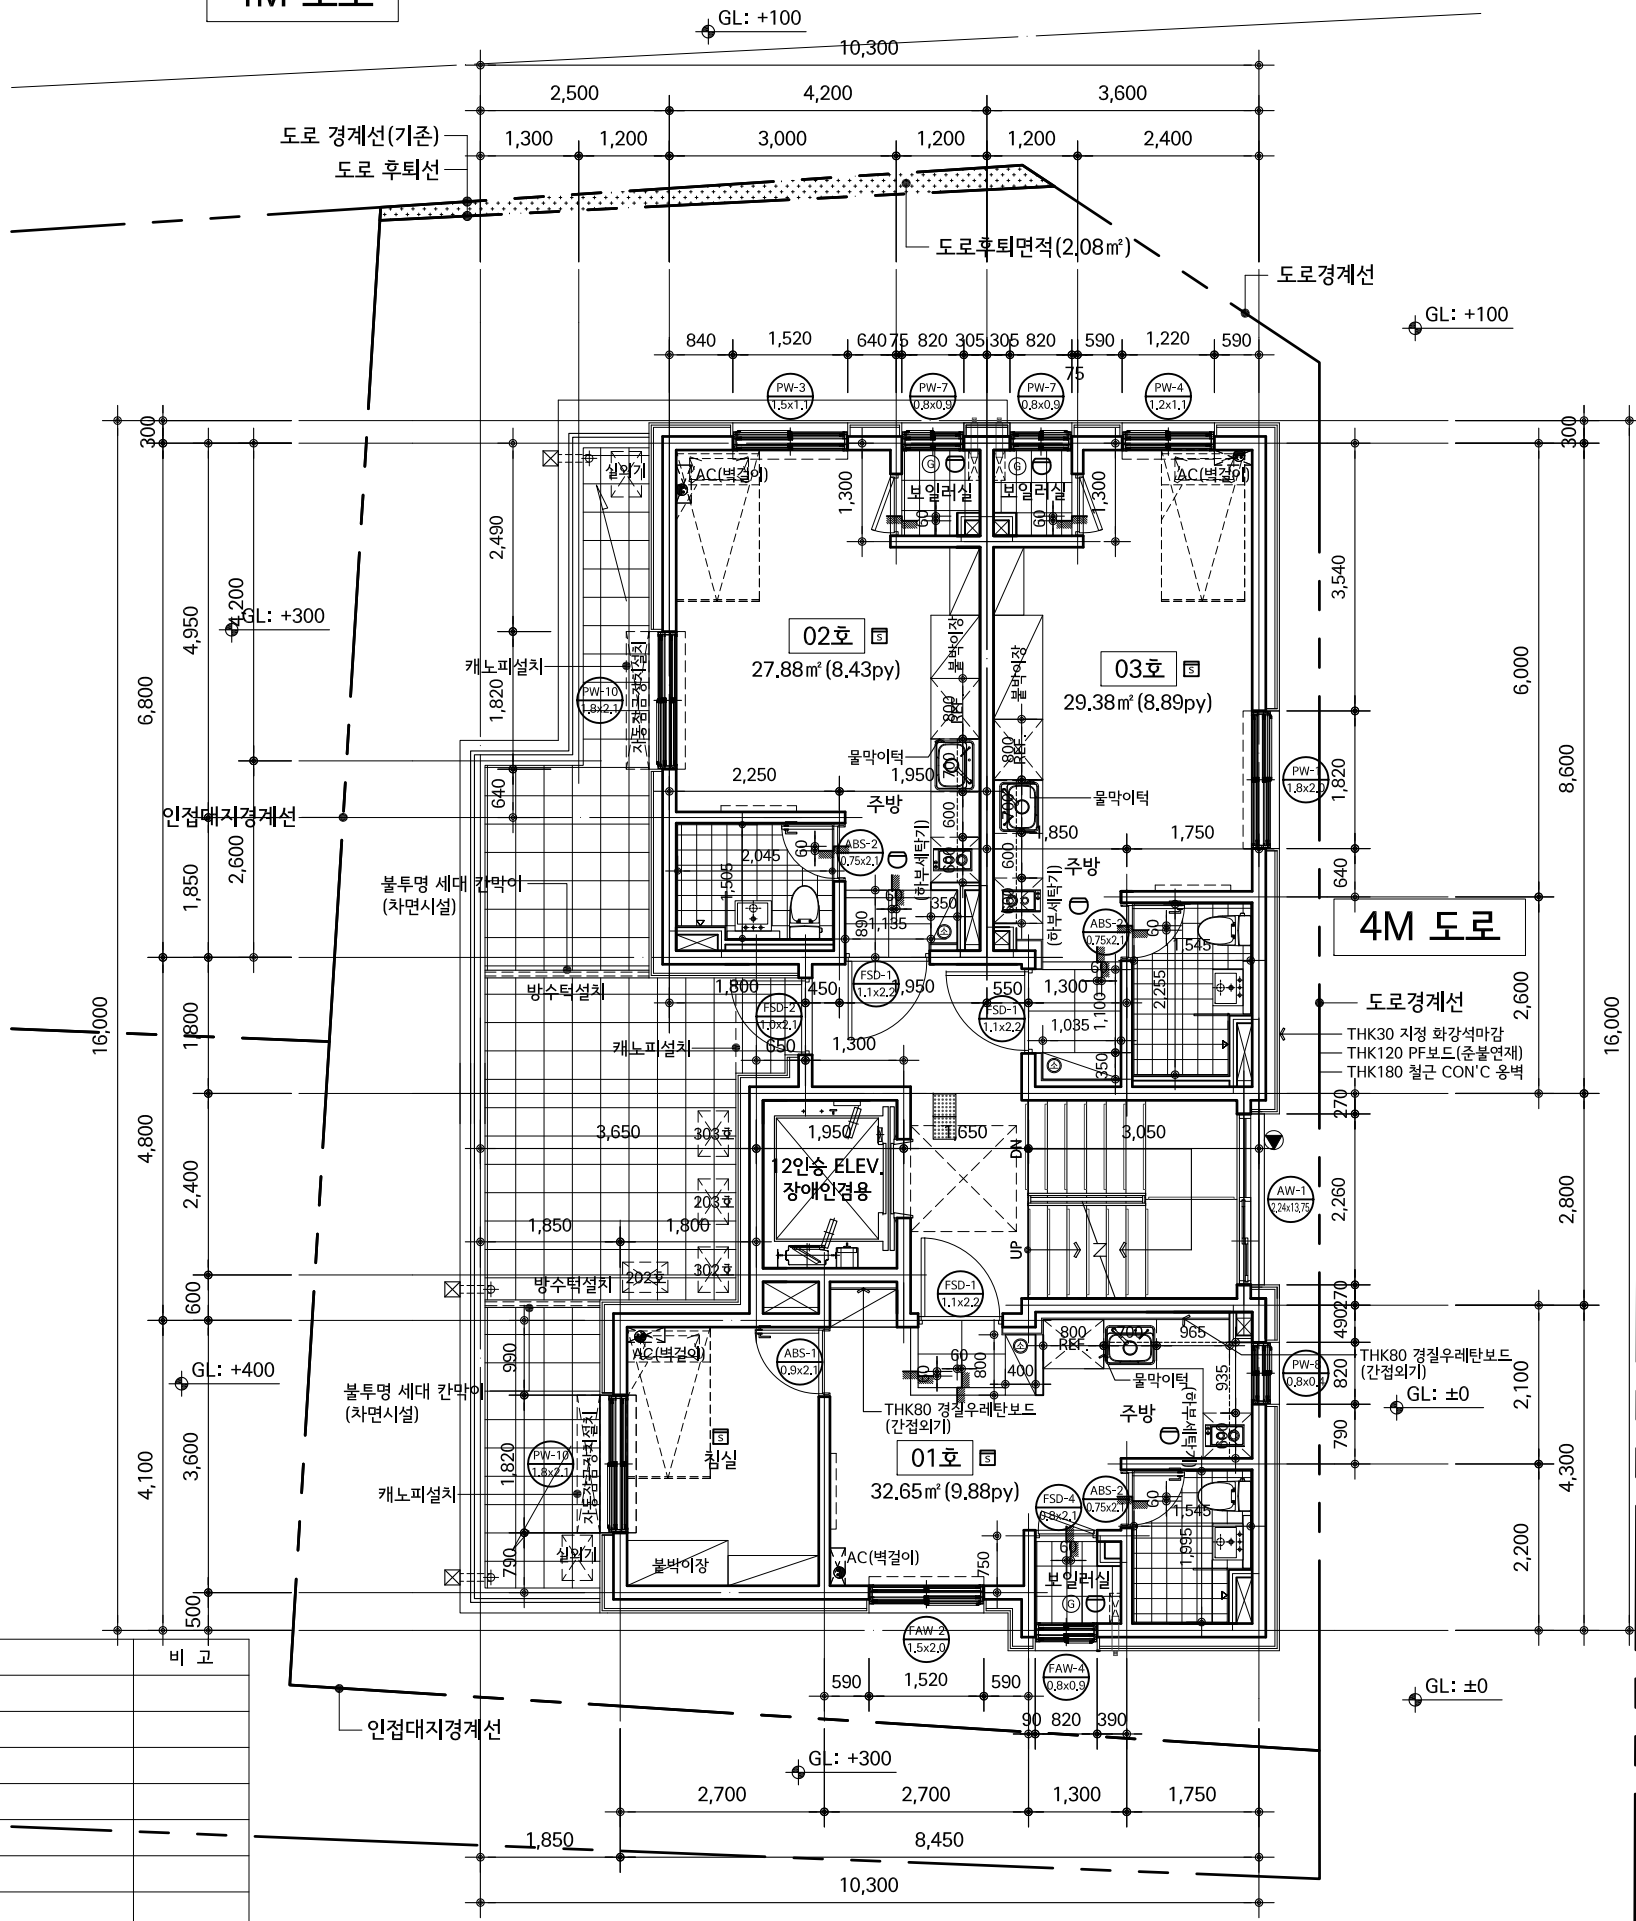


주 기

건	1 (외부)	주차장내 CCTV,쓰레기분리수거,자전거보관대 설치
		우편함 설치 (세대전용, 공용, 반송용, 폐전지함 구분 설치)
		세대 테라스 설치시 세대간 분리벽 계획
		세대 발코니 설치시 차양시설 설치
		세대내 비디오폰 설치
축	2 (계단실)	세대 현관문 도어체크 및 스토퍼 설치
		계단참의 현관과 계단 이격거리 (최소600mm이상)
	3 (내부)	Built in 가구(불박이장, 책상) 설치
		전자제품(벽걸이에어컨, 냉장고, 세탁기) 설치
		에어컨 실외기 설치위치 및 에어컨 콘센트, 냉매 및 배수관 위치 도면표기(배수관 수직으로 매립) ● - 에어컨 콘센트 표기
구	4 (시공)	콘크리트 토타이 제거 후 마감공사 시공 (방수, 단열재 시공 등)
		욕실 & 다용도실 스위치 : 문 열리는 방향으로 시공
	5 (마감)	주차장 차량 진출입구간,화장실 무소음트렌치 시공
		-직접외기(외벽)에 면한 실내벽면 단열재
		[아이소핑크(10mm) + 석고보드 마감도면 표기]
전	1	-계단실,복도에 면한 실내벽면 단열재(방풍실설치시)
		[아이소핑크(20mm) + 석고보드 마감도면 표기]
	2	*기타 실내 벽면 시멘트 미장 마감
		철근 : fy=400Mpa(HD16이하),fy=500Mpa(HD19이상)
		콘크리트 : fck=30Mpa
기	3	스라브두께 : 210mm (복배근) 이상
		외벽벽두께 : 180mm (복배근) 이상
	4	내벽두께 : 150mm (복배근) 이상
		비내력벽두께 : 100mm (단배근) 이상
		-콘센트 설치 (바닥 마감선 기준)
비	1	스탠드형 에어컨 : 350
		벽걸이형 에어컨 : 1900
	2	[화장실] 양변기 옆 : 900
		[주방] 조리대 : 중앙 / 냉장고 : 350 / 후드 : 2100
		-비디오폰(VP),보일러온도조절기(B), 스위치(S) 설치 (거실 아트홀 위치)
고	3	-위치 표기
		에어컨 실외기
	4	에어컨 콘센트
		냉매, 배수관 (배수관수직매립)
		우편함 규격은 관련법규에 맞추어 적절한 위치에 설치하고
대	1	세대전용,공용,반송용,폐전지함으로 구분 설치한다.
		난간대에 국기봉을 설치한다
	2	

심	볼	내	용	비	고
○		열식 단독경보형 감지기 (형식승인품)			
□		연기식 단독경보형 감지기 (형식승인품)			
⊙		가스누출 경보기			
⊗		ABC 분말 소화기			
차		차면시설			
▼		소방관 진입창			
확		확장형 발코니			

지상4층 평면도
SCALE = 1/100

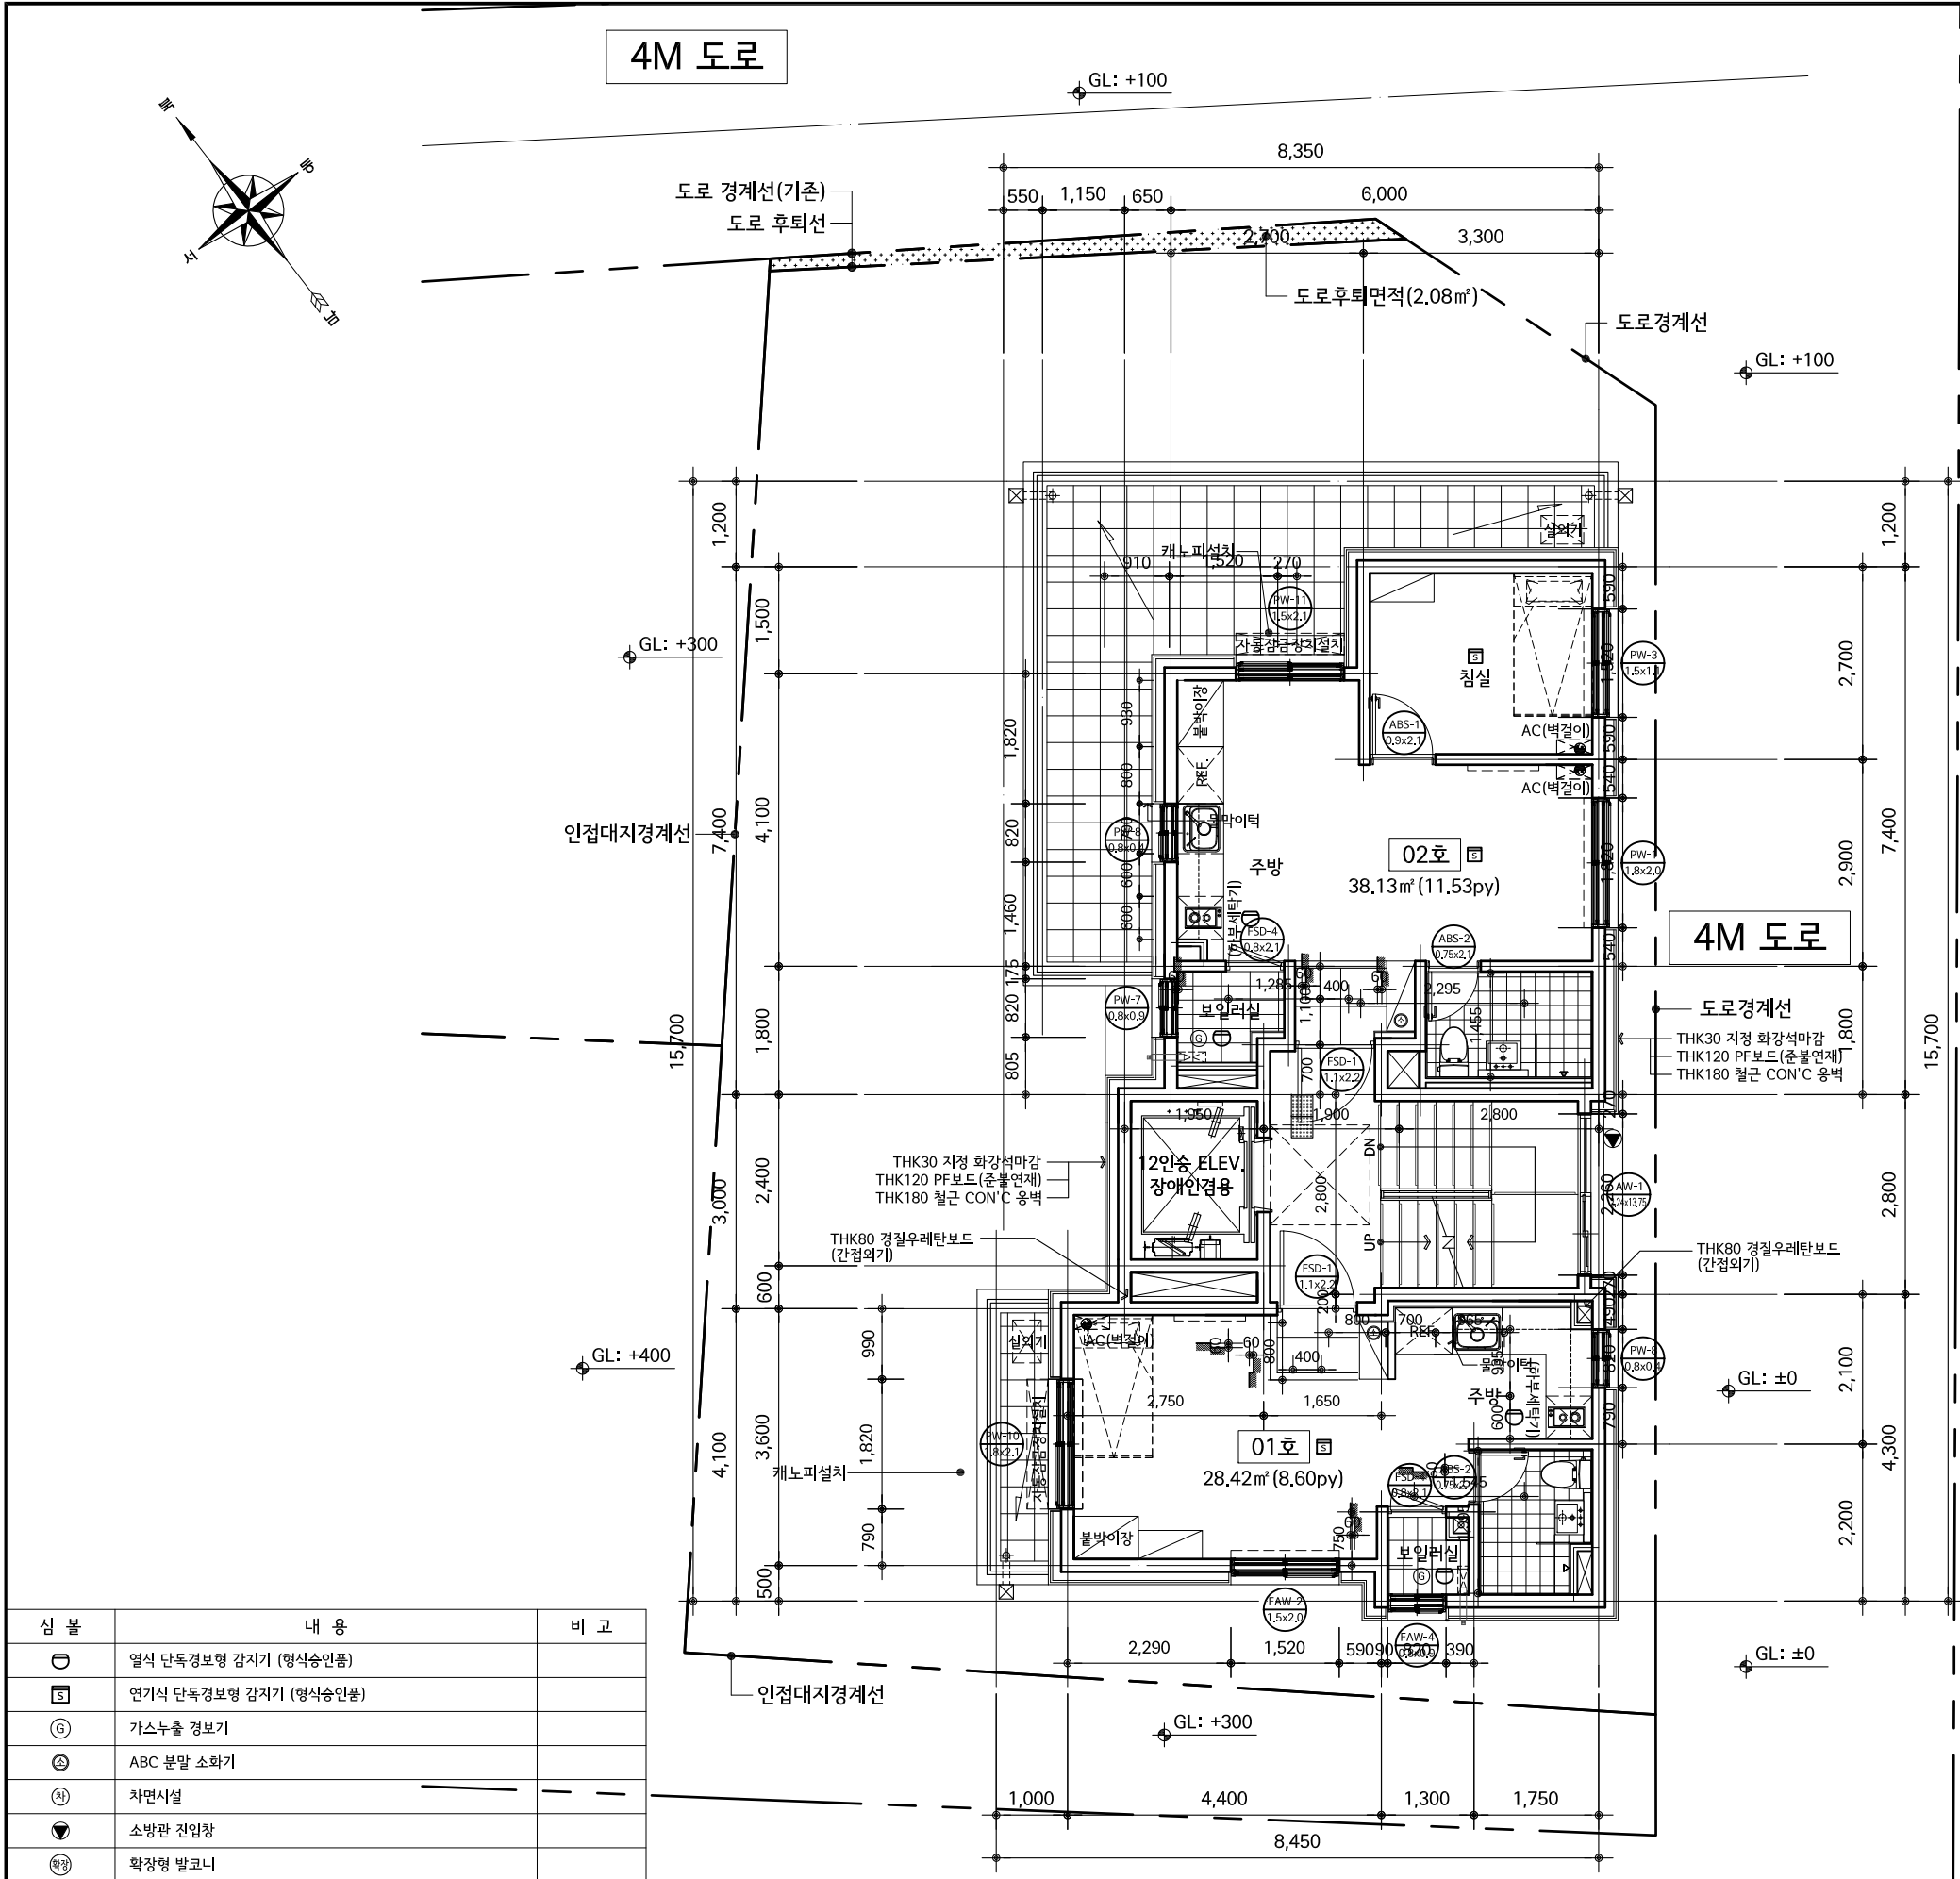




심볼	내용	비고
⊖	열식 단독경보형 감지기 (형식승인품)	
㉔	연기식 단독경보형 감지기 (형식승인품)	
㉔	가스누출 경보기	
㉔	ABC 분말 소화기	
차	차면시설	
●	소방관 진입창	
확	확장형 발코니	

주 기

건	1 (외부)	주차장내 CCTV,쓰레기분리수거,자전거보관대 설치 우편함 설치 (세대전용, 공용, 반송용, 폐전지함 구분 설치) 세대 테라스 설치시 세대간 분리벽 계획 세대 발코니 설치시 차양시설 설치 세대내 비디오폰 설치
	2 (계단실)	세대 현관문 도어체크 및 스토퍼 설치 계단참의 현관과 계단 이격거리 (최소600mm이상)
	3 (내부)	Built in 가구(불박이장, 책상) 설치 전자제품(벽걸이에어컨, 냉장고, 세탁기) 설치 에어컨 실외기 설치위치 및 에어컨 콘센트, 냉매 및 배수관 위치 도면표기(배수관 수직으로 매립) ● - 에어컨 콘센트 표기
	4 (시공)	콘크리트 톱타이 제거 후 마감공사 시공 (방수, 단열재 시공 등) 욕실 & 다용도실 스위치 : 문 열리는 방향으로 시공 주차장 차랑 진출입구간,화장실 무소음트렌치 시공
	5 (마감)	-직접외기(외벽)에 면한 실내벽면 단열재 [아이소핑크(10mm) + 석고보드 마감도면 표기] -계단실,복도에 면한 실내벽면 단열재(방풍실설치시) [아이소핑크(20mm) + 석고보드 마감도면 표기] *기타 실내 벽면 시멘트 미장 마감
구 조	1	철근 : fy=400Mpa(HD16이하),fy=500Mpa(HD19이상) 콘크리트 : fck=30Mpa
	2	스라브두께 : 210mm (복배근) 이상 외벽벽두께 : 180mm (복배근) 이상 내벽두께 : 150mm (복배근) 이상 비내력벽두께 : 100mm (단배근) 이상
전 기	1	-콘센트 설치 (바닥 마감선 기준) 스탠드형 에어컨 : 350 벽걸이형 에어컨 : 1900 [화장실] 양변기 옆 : 900 [주방] 조리대 : 중앙 / 냉장고 : 350 / 후드 : 2100
	2	-비디오폰(VP),보일러온도조절기(B), 스위치(S) 설치 (거실 아트홀 위치)
	3	-위치 표기 에어컨 실외기 에어컨 콘센트 냉매, 배수관 (배수관수직매립)
비 고	우편함 규격은 관련법규에 맞추어 적절한 위치에 설치하고 세대전용,공용,반송용,폐전지함으로 구분 설치한다. 난간대에 국기봉을 설치한다	

지상5층 평면도
SCALE = 1/100

안방광역시 연수구 남달로55번길 6-12, 2층 T_032-464-8775 F_032-881-9102	PROJECT TITLE 수유동 270-114 도시형생활주택(소형주택) 신축공사 -청년주택-	NAME OF DRAWING. 지상5층 평면도	제 도 DRAWN BY 설 계 DESIGNED BY 사 사 CHECKED BY 승 인 APPROVED BY 건축사 이선영	변경사항 ISSUER & REVISIONS	추가사항 NOTE	SCALE. A3: 1 / 100	DRAWING NUMBER A - 1 0 4
						DATE.	

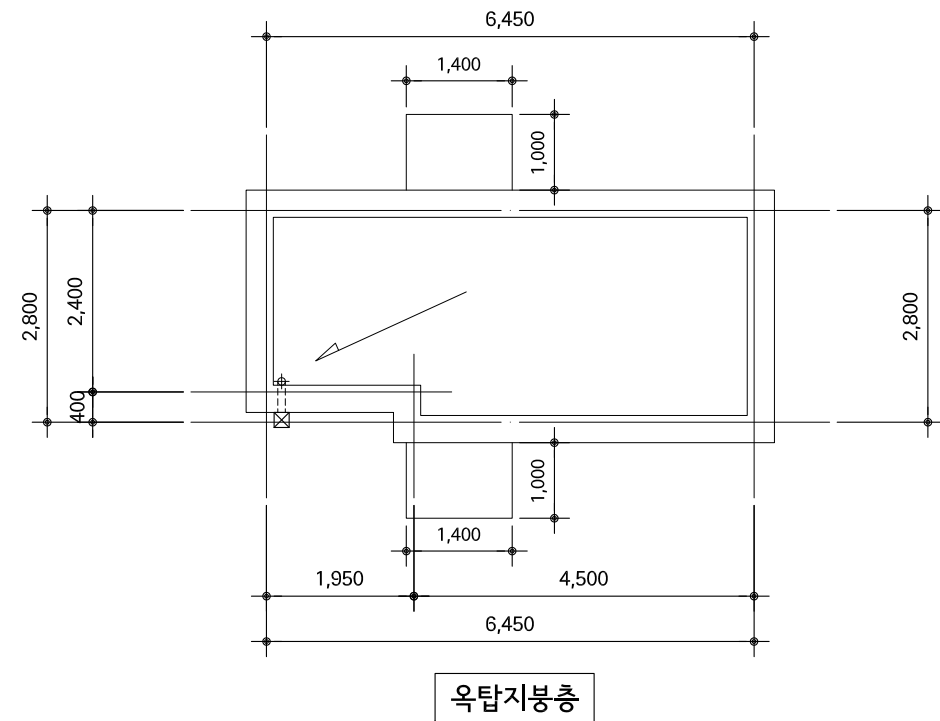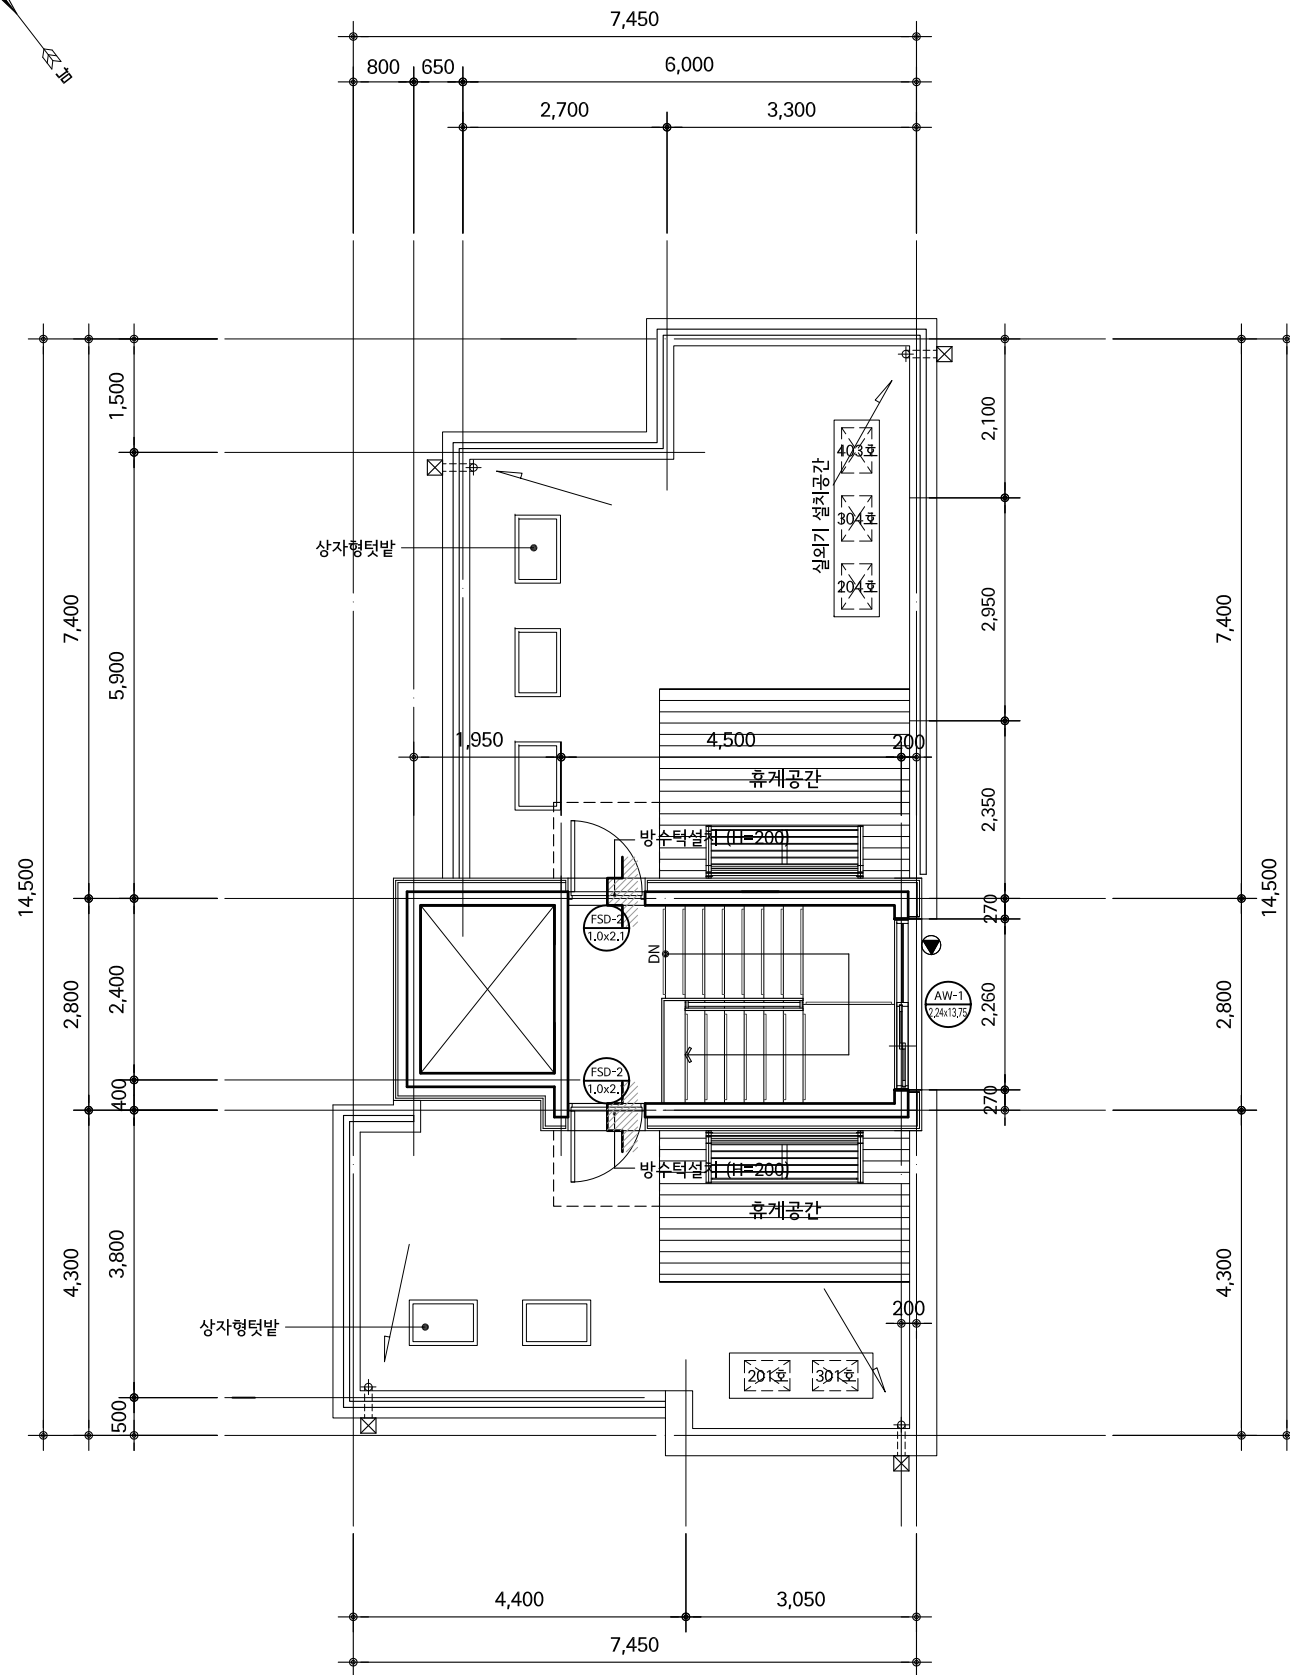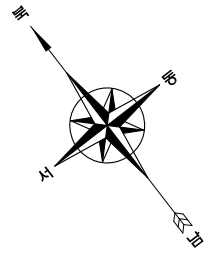

지붕층 및 옥탑지붕층 평면도
SCALE = 1/100