


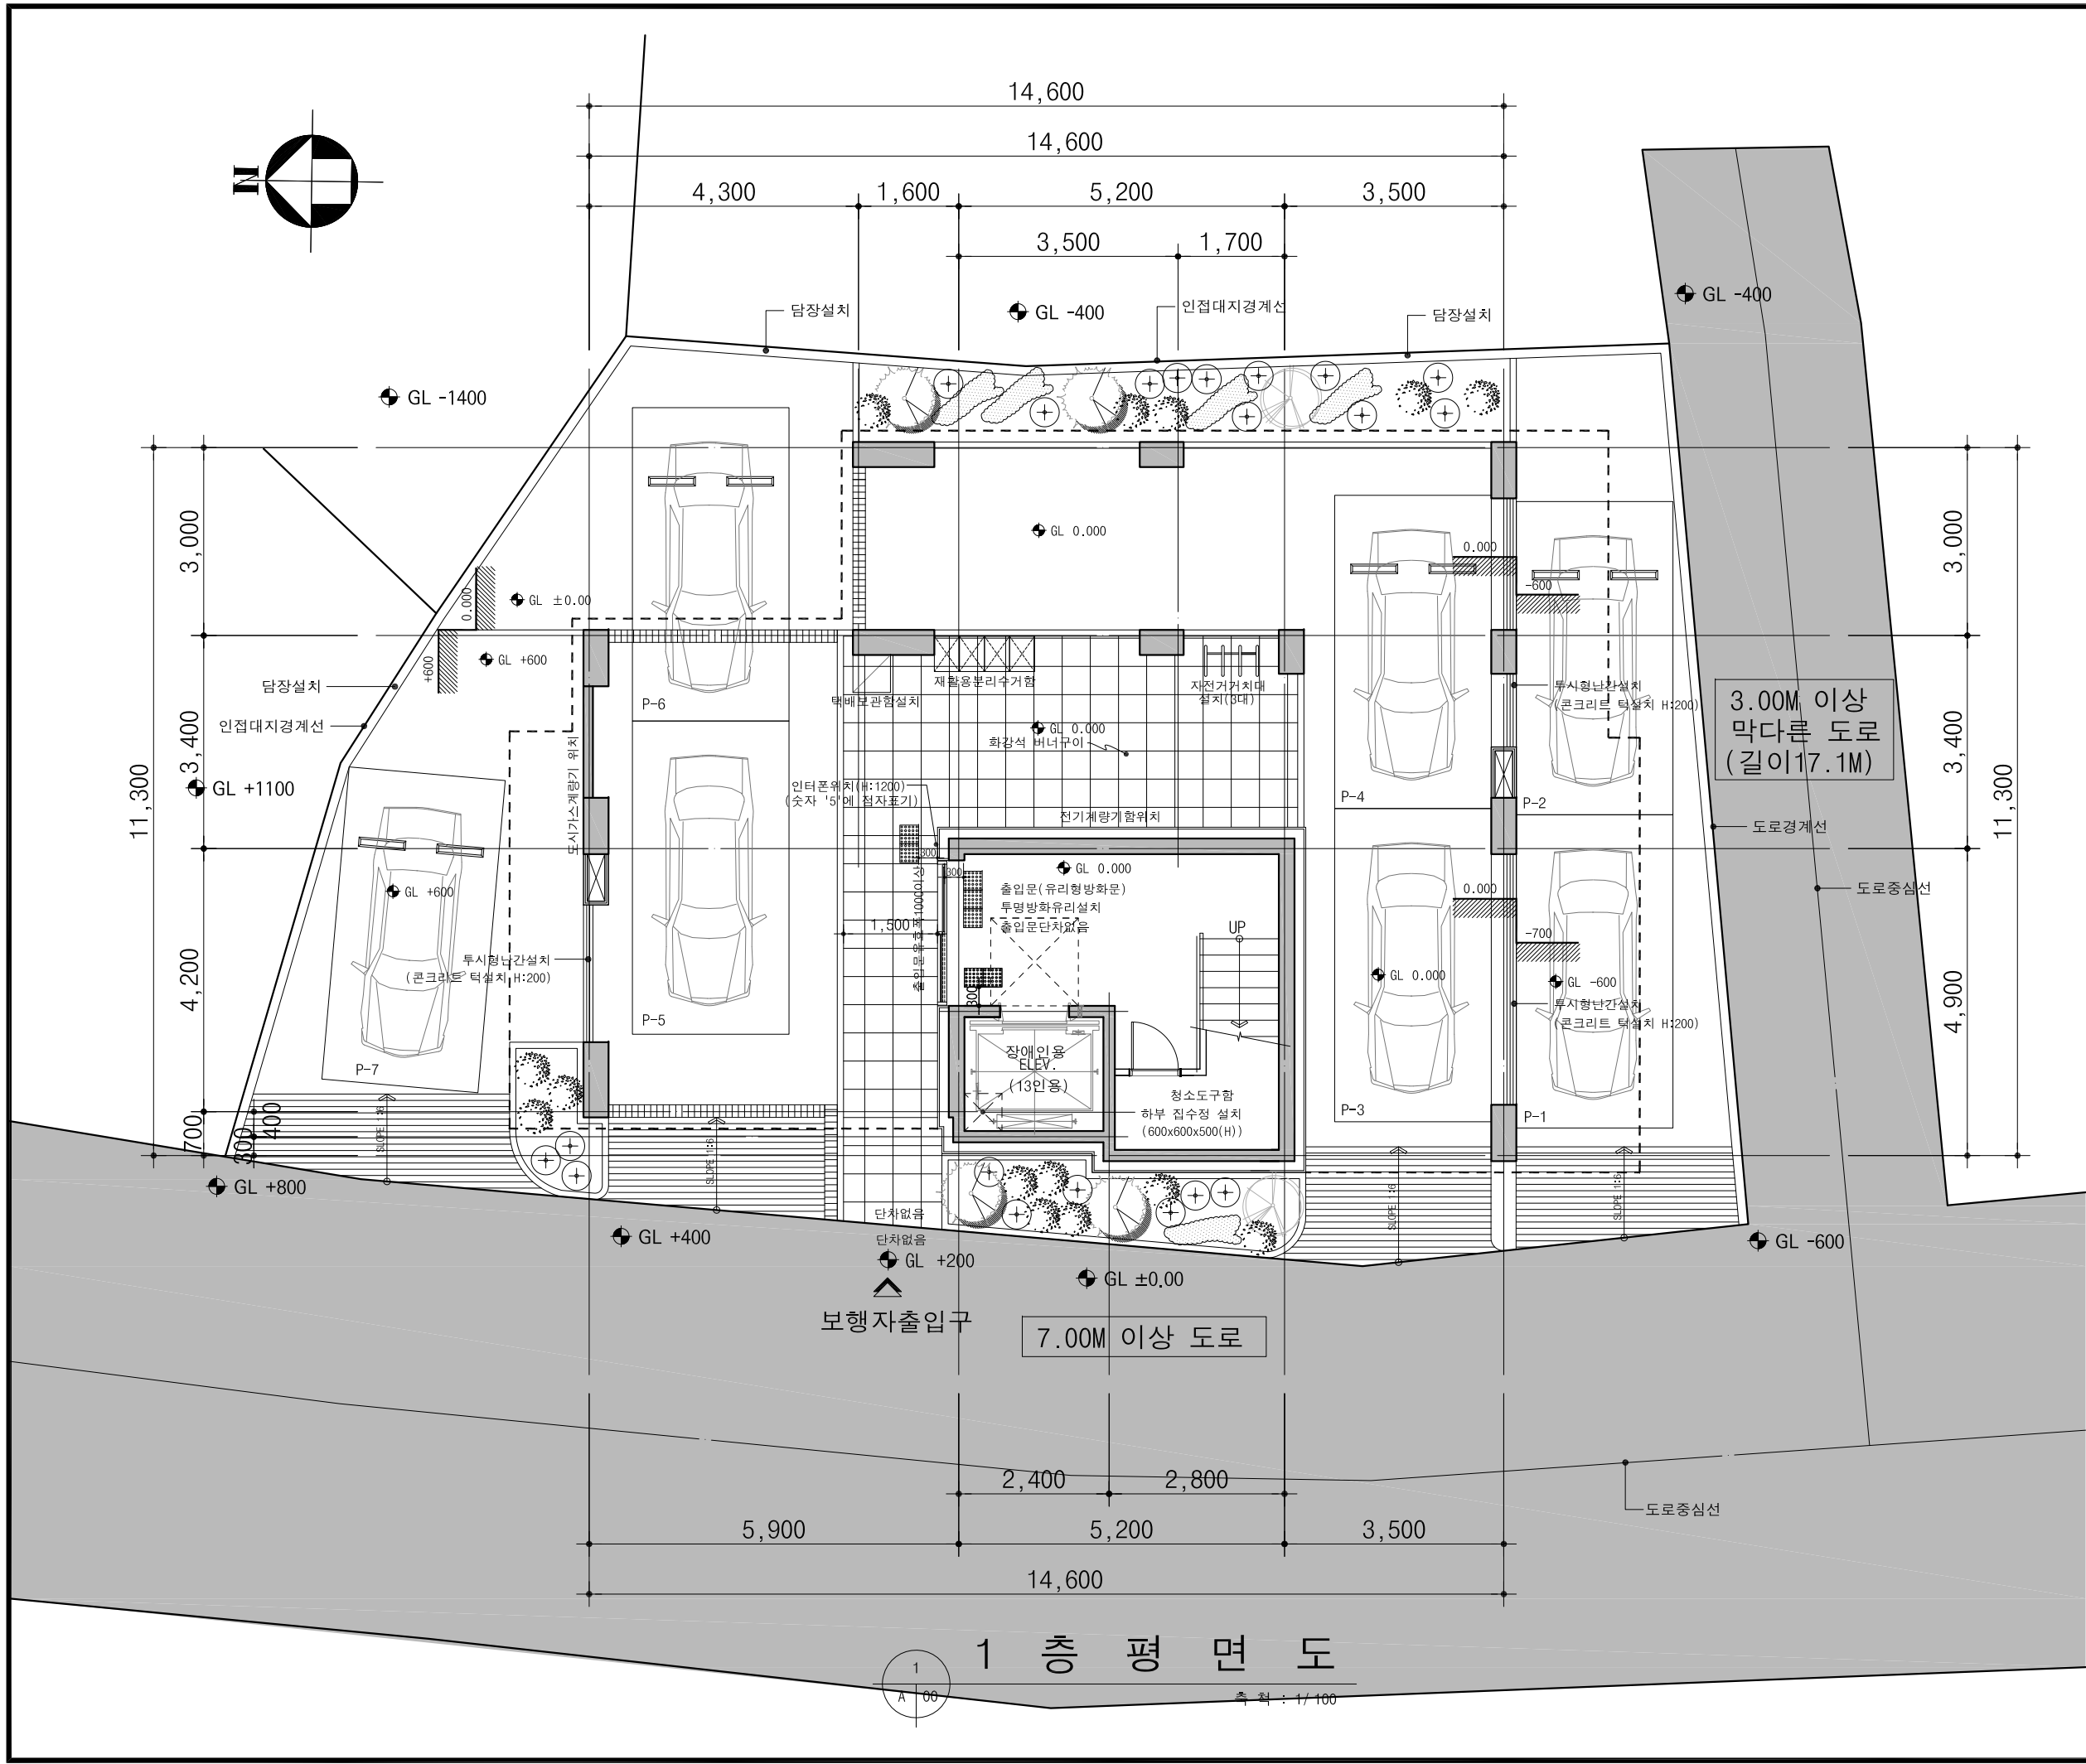

주 기	
1	접근로의 유효폭 1.2미터 이상 확보
2	접근로의 기울기는 1/18 이하로 설치
3	대지 내를 연결하는 주접근로에 단차가 있을 경우 그 높이는 2cm 이하가 되도록 설치
4	접근로는 차도와 색상과 재질을 달리하여 반드시 보차분리를 명확히 해주어야 함
5	접근로의 바닥표면은 잘미끄러지지 않는 재료로 평탄하게 마감하여야 함
6	블록 등으로 접근로를 포장하는 경우에는 이음새의 틈이 벌어지지 아니하도록 하여 면이 평탄하게 시공하여야 함
7	덮개를 설치할 경우 덮개에 격자구멍 또는 틈새의 양방향 간격이 2cm 이하가 되도록 설치
8	점형블록은 매립형으로 설치함(황색KS제품)

계단실 추출입문

유리폭, 유리높이=1,000X2,100
샷시, 문틀, 부속철물일체(방화용)

* 점형블록

KS표준 황색매입형
우레탄재질로 설치 한다

NOTE:

PROJECT 강북구 우이동 32-3번지
도시형생활주택 (원룸형) 청년주택 신축공사



APPROVED BY 건축사 구 연 목

ARCHITECTURE & ENGINEERING 건축사사무소 유일엔지니어링
서울특별시 서초구 반포대로 14길71(서초동)
[6서초에클라트(1904호)]
TEL : 02) 540-1546, FAX : 02) 540-1576

TITLE 1층 평면도

날짜 DATE: 2022. 09. .

SCALE	1/ 100	DWG NO.	A - 008	REV.

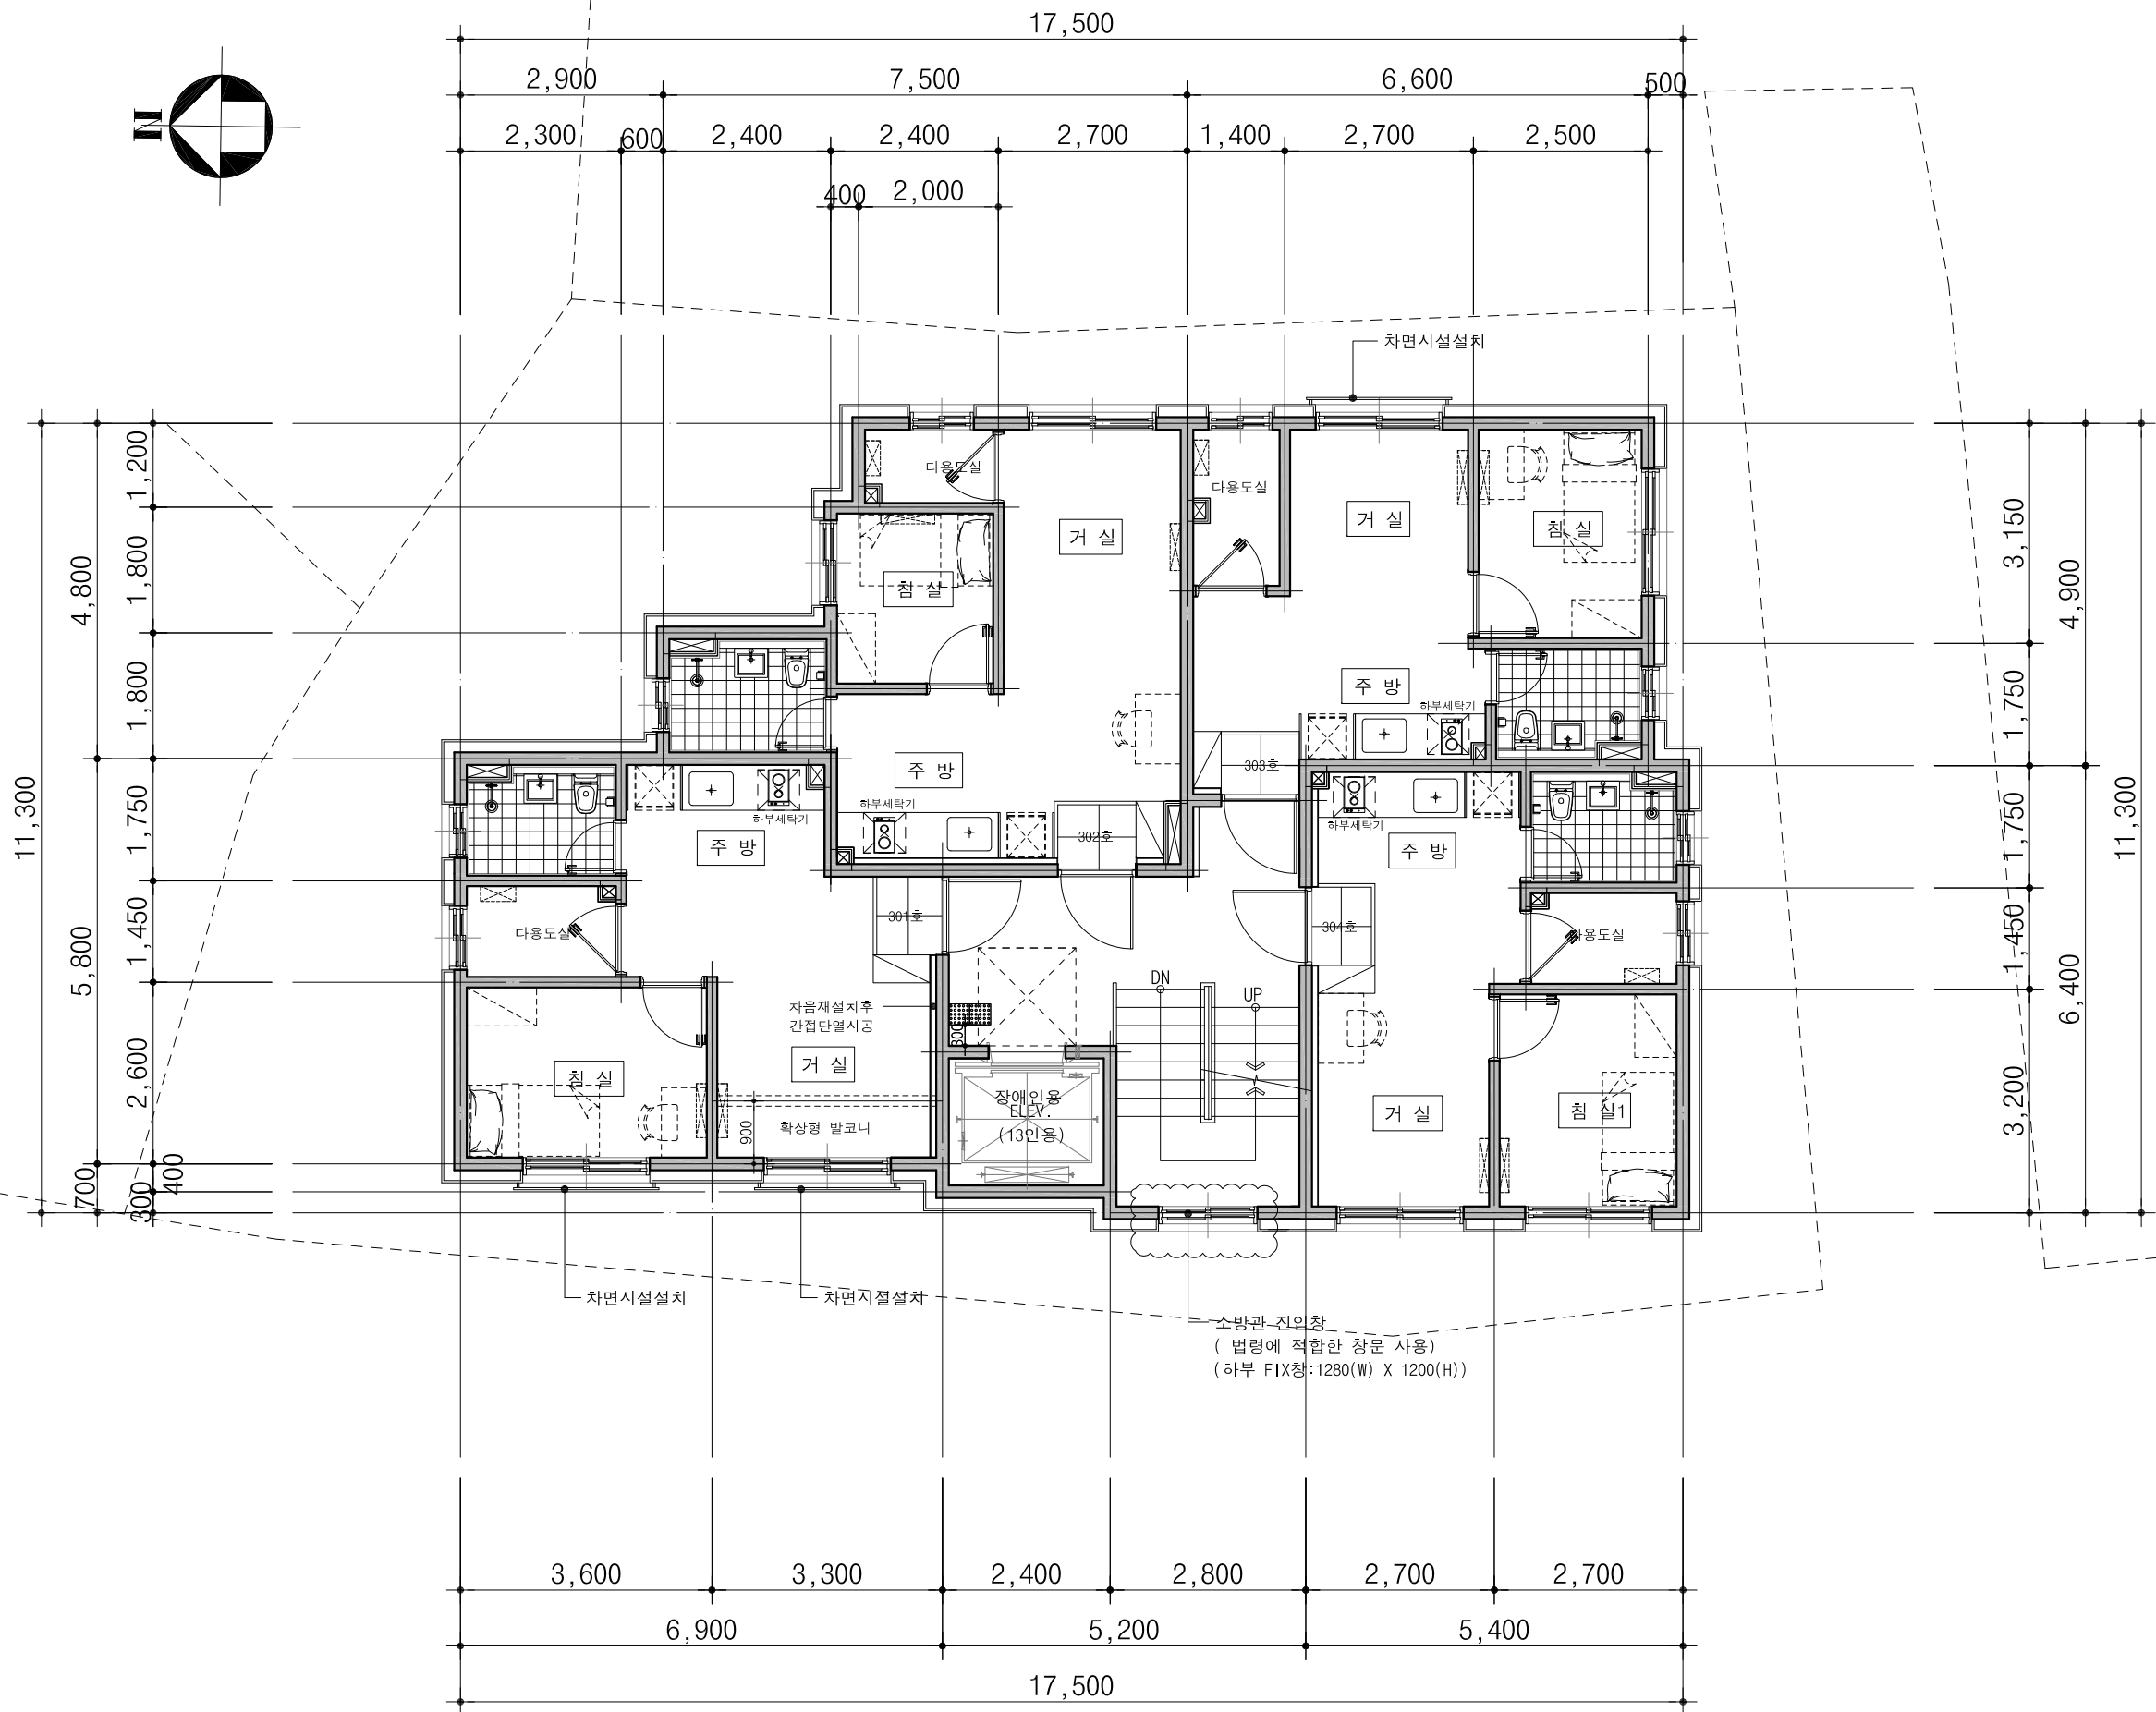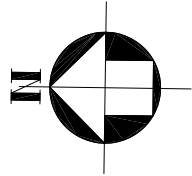

3 층 평 면 도
축척 : 1/100

주 기			
1	세대 현관문 도어체크 및 스토퍼 계획		
2	세대 발코니 설치시 세대간 분리벽 계획		
3	세대내 비디오폰 설치		
4	주차장내 CCTV 설치		
5	외벽	직접 외기에 면한 실내벽면은 단열재 (아이소핑크10mm+석고보드 마감도면 표기)	
	계단실 /복도	간접 외기에 면한 실내벽면은 단열재 (경질우레탄80mm+석고보드 마감도면 표기)	
6	에어콘 실외기 설치위치 및 에어콘 도면표기)		
7	불박이 가구 내부 다용도 수납가능토록 수평이동 칸막이 설치		
8	콘크리트 폼타이 제거후 마감공사 시공(방수 및 단열재 시공등)		
9	구조	콘크리트	fck=24Mpa
		철근	fy=400Mpa
		세대 벽두께	150mm(복배근)
		외벽 벽두께	180mm(복배근)
		코아 벽두께	180mm(복배근)
		2층 슬라브 두께: 180mm(복배근) 3~5층 슬라브 두께: 210mm(복배근)	
10	기타 실내 벽면은 시멘트 미장마감		
11	욕실 & 다용도실 스위치 : 문열리는 방향으로 시공		
12	공동주택 바닥충격음 차단구조기준		
3층, 4층, 5층			
13	소방관 진입창의 기준 건축물의 피난방화구조등의 기준에 관한규칙 제18조의2에 의거 1. 2층이상 11층이하인 층에 각각 1개소 이상설치 2. 소방차진입로또는 소방차 진입이 가능한 공터에 면할것 3. 창문 가운에 Ø200이상의 역삼각형을 야간에 식별가능하도록 설치.(반사 등으로 붉은색으로 표시) 4. 창문 한쪽 모서리에 타격지점 표시 (Ø30 이상의 원형) 5. 창문크기 : 폭900 높이1,200이상 (바닥에서 창아랫부분 높이800이내로 설치) 6. 다음 각 목의 어느 하나에 해당하는 유리 사용할 것 가. 플로트판유리로서 두께6mm이하인것 나. 강화유리/배강도유리로서 두께5mm이하인것 다. 위의 유리로 구성된 이중유리로서 두께24mm 이하인것		
14	외기에 간접면하는 부분 : THK80 결질우렌타폼 2중2호 설치		

NOTE:

PROJECT강북구 우이동 32-3번지
도시형생활주택 (원룸형) 청년주택 신축공사

APPROVED BY건축사 구 연 목



건축사사무소 유일엔지니어링
ARCHITECTURE & ENGINEERING
서울특별시 서초구 반포대로 14길71(서초동)
[0서초에클라트(1904호)]
TEL : 02) 540-1546, FAX : 02)540-1576

TITLE3층 평면도

날짜
DATE:2022. 09. .

SCALE1/ 100 DWG NO. A - 010 REV.



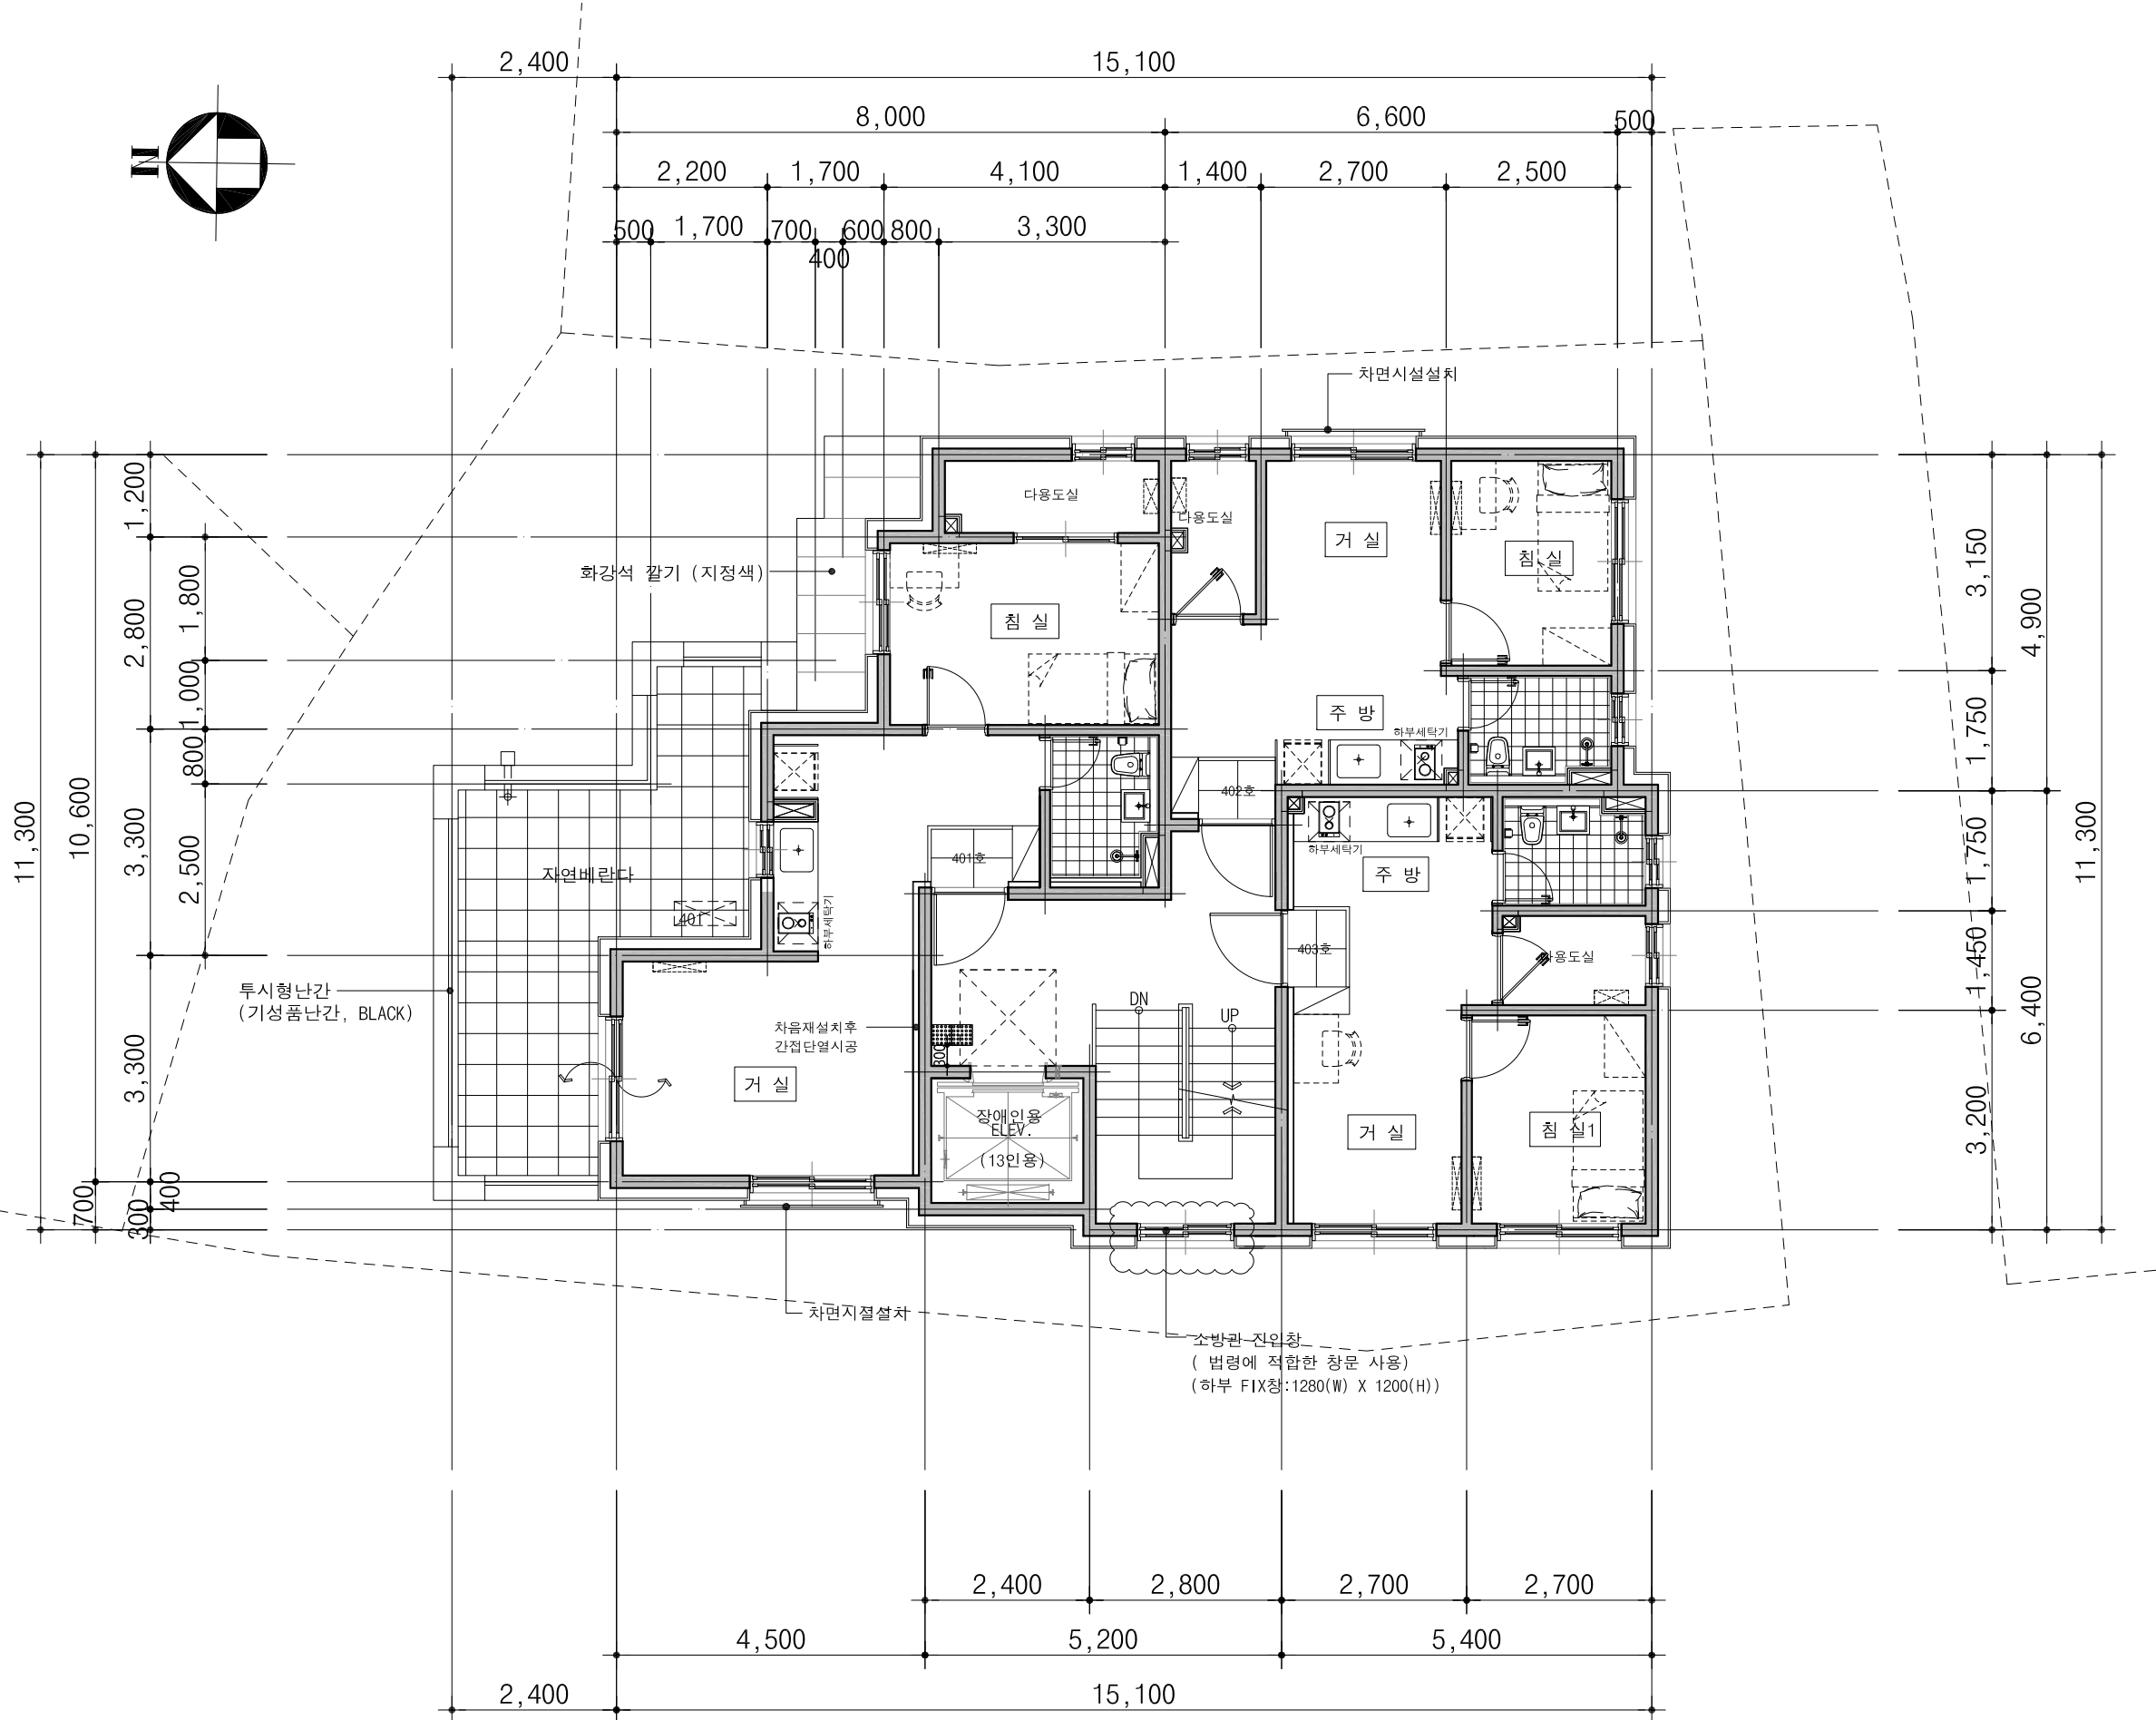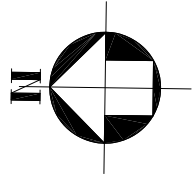

4 층 평 면 도

축척 : 1/100

주 기

- 세대 현관문 도어체크 및 스토퍼 계획
- 세대 발코니 설치시 세대간 분리벽 계획
- 세대내 비디오폰 설치
- 주차장내 CCTV 설치
- | | | |
|----|---------|--|
| 벽체 | 외벽 | 직접 외기에 면한 실내벽면은 단열재 (아이소핑크10mm+석고보드 마감도면 표기) |
| | 계단실 /복도 | 간접 외기에 면한 실내벽면은 단열재 (경질우레탄80mm+석고보드 마감도면 표기) |
- 에어콘 실외기 설치위치 및 에어콘 도면표기)
- 불박이 가구 내부 다용도 수납가능토록 수평이동 칸막이 설치
- 콘크리트 폼타이 제거후 마감공사 시공(방수 및 단열재 시공등)
- | | | |
|------|--------|--------------|
| 구조 | 콘크리트 | : fck=24Mpa |
| | 철근 | : fy=400Mpa |
| | 세대 벽두께 | : 150mm(복배근) |
| | 외벽 벽두께 | : 180mm(복배근) |
| | 코아 벽두께 | : 180mm(복배근) |
| 2층 | 스라브 두께 | : 180mm(복배근) |
| 3~5층 | 스라브 두께 | : 210mm(복배근) |
- 기타 실내 벽면은 시멘트 미장마감
- 욕실 & 다용도실 스위치 : 문열리는 방향으로 시공
- 공동주택 바닥충격음 차단구조기준
- | | | |
|------------|-----------|--------------------|
| 3층, 4층, 5층 | 결재방이(PVC) | 데크타일마감(2.2t이상) |
| | T=40 | 시멘트충진(1:3, 평창채 혼입) |
| | T=40 | 경질우레탄80mm |
| | T=30 | 완충재(EPS계열) |
| | T=20 | 콘크리트슬라브 |
- 소방관 진입창의 기준

건축물의 피난방화구조등의 기준에 관한규칙 제18조의2에 의거

 - 2층이상 11층이하인 층에 각각 1개소 이상설치
 - 소방차진입로또는 소방차 진입이 가능한 공터에 면할것
 - 창문 가운데 $\varnothing 200$ 이상의 역삼각형을 야간에 식별가능하도록 설치.(반사 등으로 붉은색으로 표시)
 - 창문 한쪽 모서리에 타격지점 표시 ($\varnothing 30$ 이상의 원형)
 - 창문크기 : 폭900 높이1,200이상 (바닥에서 창아랫부분 높이800이내로 설치)
 - 다음 각 목의 어느 하나에 해당하는 유리 사용할 것
가. 플로트판유리로서 두께6mm이하인것
나. 강화유리/배강도유리로서 두께5mm이하인것
다. 위의 유리로 구성된 이중유리로서 두께24mm 이하인것
- | | |
|--------------------|----|
| T80경질폴리우레탄폼단열재2중2호 | 호실 |
| | |
| T180철콘크리트벽 | 호실 |



NOTE:

PROJECT강북구 우이동 32-3번지
도시형생활주택 (원룸형) 청년주택 신축공사

APPROVED BY건축사 구 연 목

건축사사무소 유일엔지니어링
ARCHITECTURE & ENGINEERING
서울특별시 서초구 반포대로 14길71(서초동)
L(서초에클라트)1904호
TEL : 02) 540-1546, FAX : 02)540-1576

TITLE	4층 평면도		
날짜 DATE:	2022. 09. .		
SCALE	1/ 100	DWG NO. A - 011	REV.

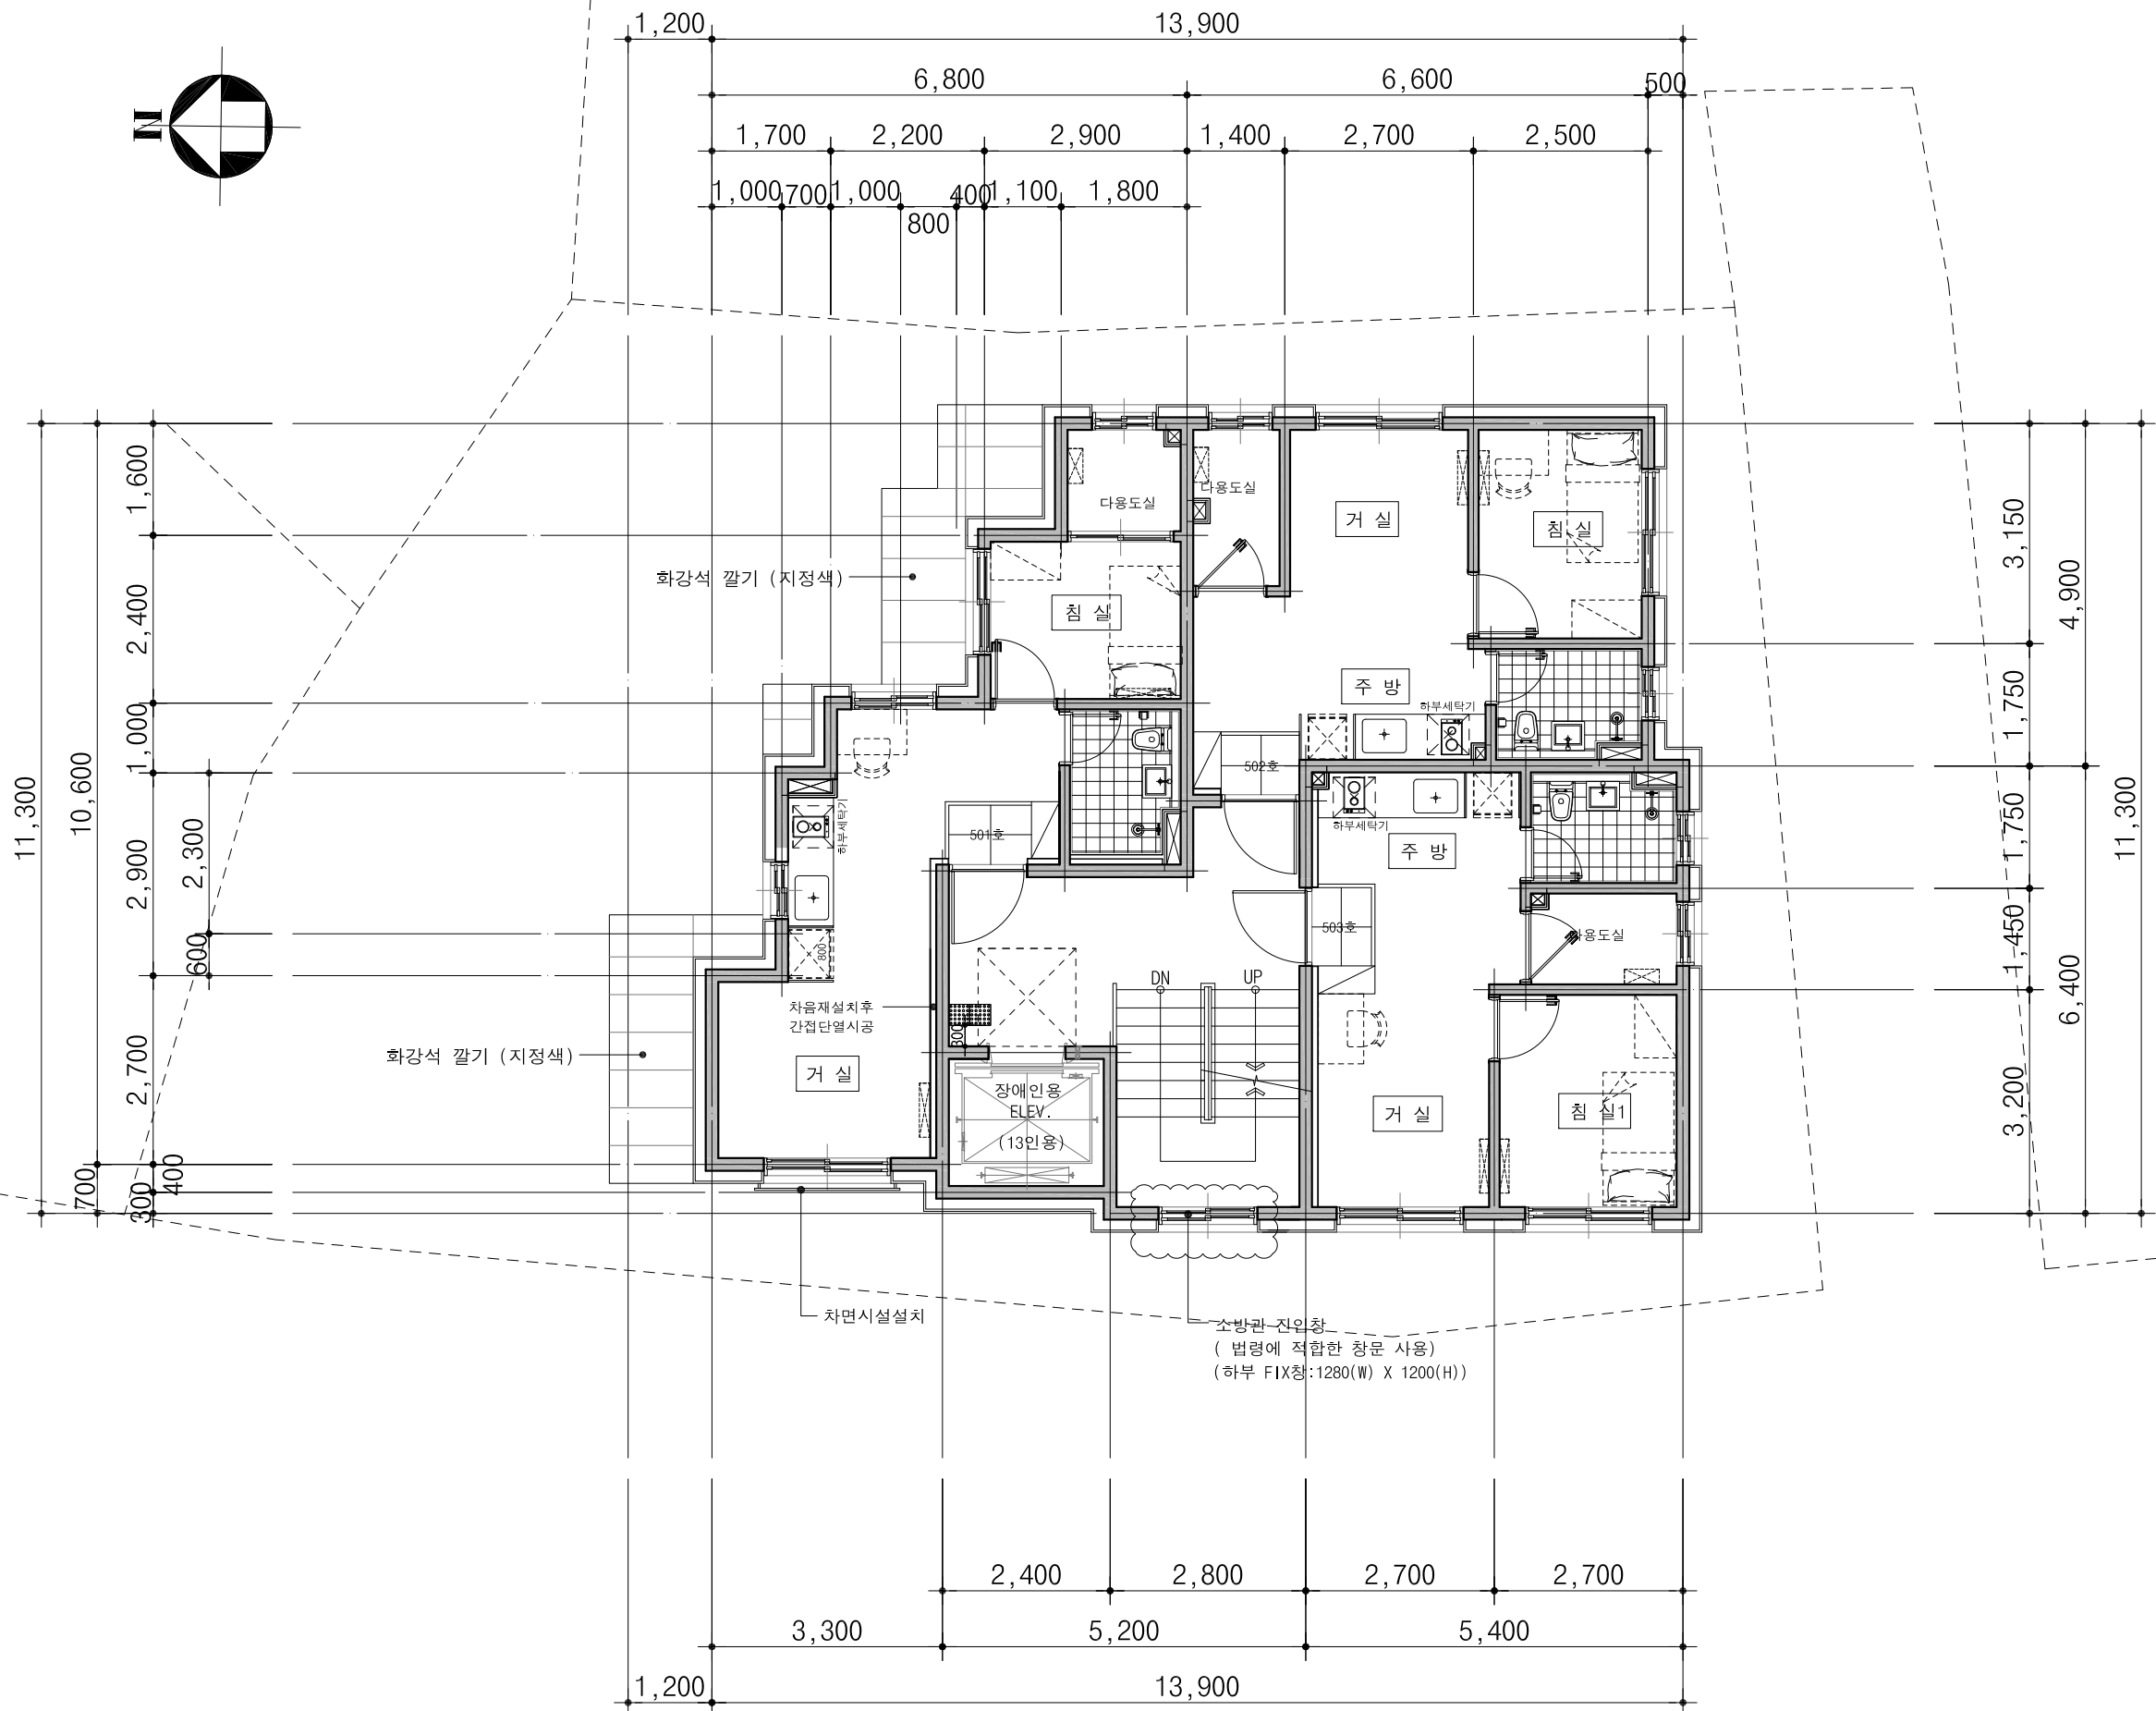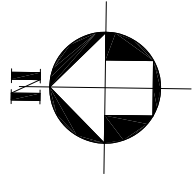


5 층 평 면 도




축척 : 1/100

주 기

- 세대 현관문 도어체크 및 스토퍼 계획
- 세대 발코니 설치시 세대간 분리벽 계획
- 세대내 비디오폰 설치
- 주차장내 CCTV 설치
- | 벽체 | 외벽 | 직접 외기에 면한 실내벽면은 단열재 (아이소핑크10mm+석고보드 마감도면 표기) |
|-----|-------------------------|--|
| 계단실 | 간접 외기에 면한 실내벽면은 단열재 /복도 | (경질우레탄80mm+석고보드 마감도면 표기) |
- 에어콘 실외기 설치위치 및 에어콘 도면표기)
- 불박이 가구 내부 다용도 수납가능토록 수평이동 칸막이 설치
- 콘크리트 폼타이 제거후 마감공사 시공(방수 및 단열재 시공등)
- | 구조 | 콘크리트 : fck=24Mpa |
|--------------------------|---------------------|
| | 철근 : fy=400Mpa |
| | 세대 벽두께 : 150mm(복배근) |
| | 외벽 벽두께 : 180mm(복배근) |
| | 코아 벽두께 : 180mm(복배근) |
| 2층 슬라브 두께 : 180mm(복배근) | |
| 3-5층 슬라브 두께 : 210mm(복배근) | |
- 기타 실내 벽면은 시멘트 미장마감
- 욕실 & 다용도실 스위치 : 문열리는 방향으로 시공
- 공동주택 바닥충격음 차단구조기준


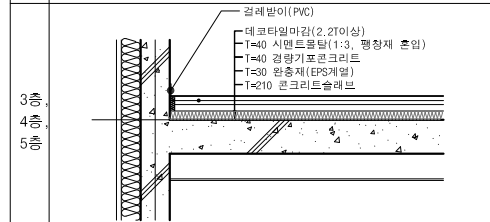


- 소방관 진입창의 기준
건축물의 피난방화구조등의 기준에 관한규칙 제18조의2에 의거
1. 2층이상 11층이하인 층에 각각 1개소 이상설치
2. 소방차진입로또는 소방차 진입이 가능한 공터에 면할것
3. 창문 가운데 $\varnothing 200$ 이상의 역삼각형을 야간에 식별가능하도록 설치.(반사 등으로 붉은색으로 표시)
4. 창문 한쪽 모서리에 타격지점 표시 ($\varnothing 30$ 이상의 원형)
5. 창문크기 : 폭900 높이1,200이상
(바닥에서 창아랫부분 높이800이내로 설치)
6. 다음 각 목의 어느 하나에 해당하는 유리 사용할 것
가. 플로트판유리로서 두께6mm이하인것
나. 강화유리/배강도유리로서 두께5mm이하인것
다. 위의 유리로 구성된 이중유리로서 두께24mm 이하인것
- 외기에 간접면하는 부분 : THK80 경질우레탄폼 2중2호 설치

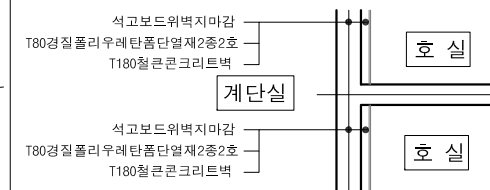

NOTE:

PROJECT	강북구 우이동 32-3번지 도시형생활주택 (원룸형) 청년주택 신축공사
APPROVED BY	건축사 구 연 목
	
	건축사사무소 유일엔지니어링 ARCHITECTURE & ENGINEERING 서울특별시 서초구 반포대로 14길71(서초동) [0서초에클라트(1904호)] TEL : 02) 540-1546, FAX : 02)540-1576
TITLE	5층 평면도
날짜 DATE:	2022. 09. .
SCALE	1/ 100
DWG NO.	A - 012
REV.	

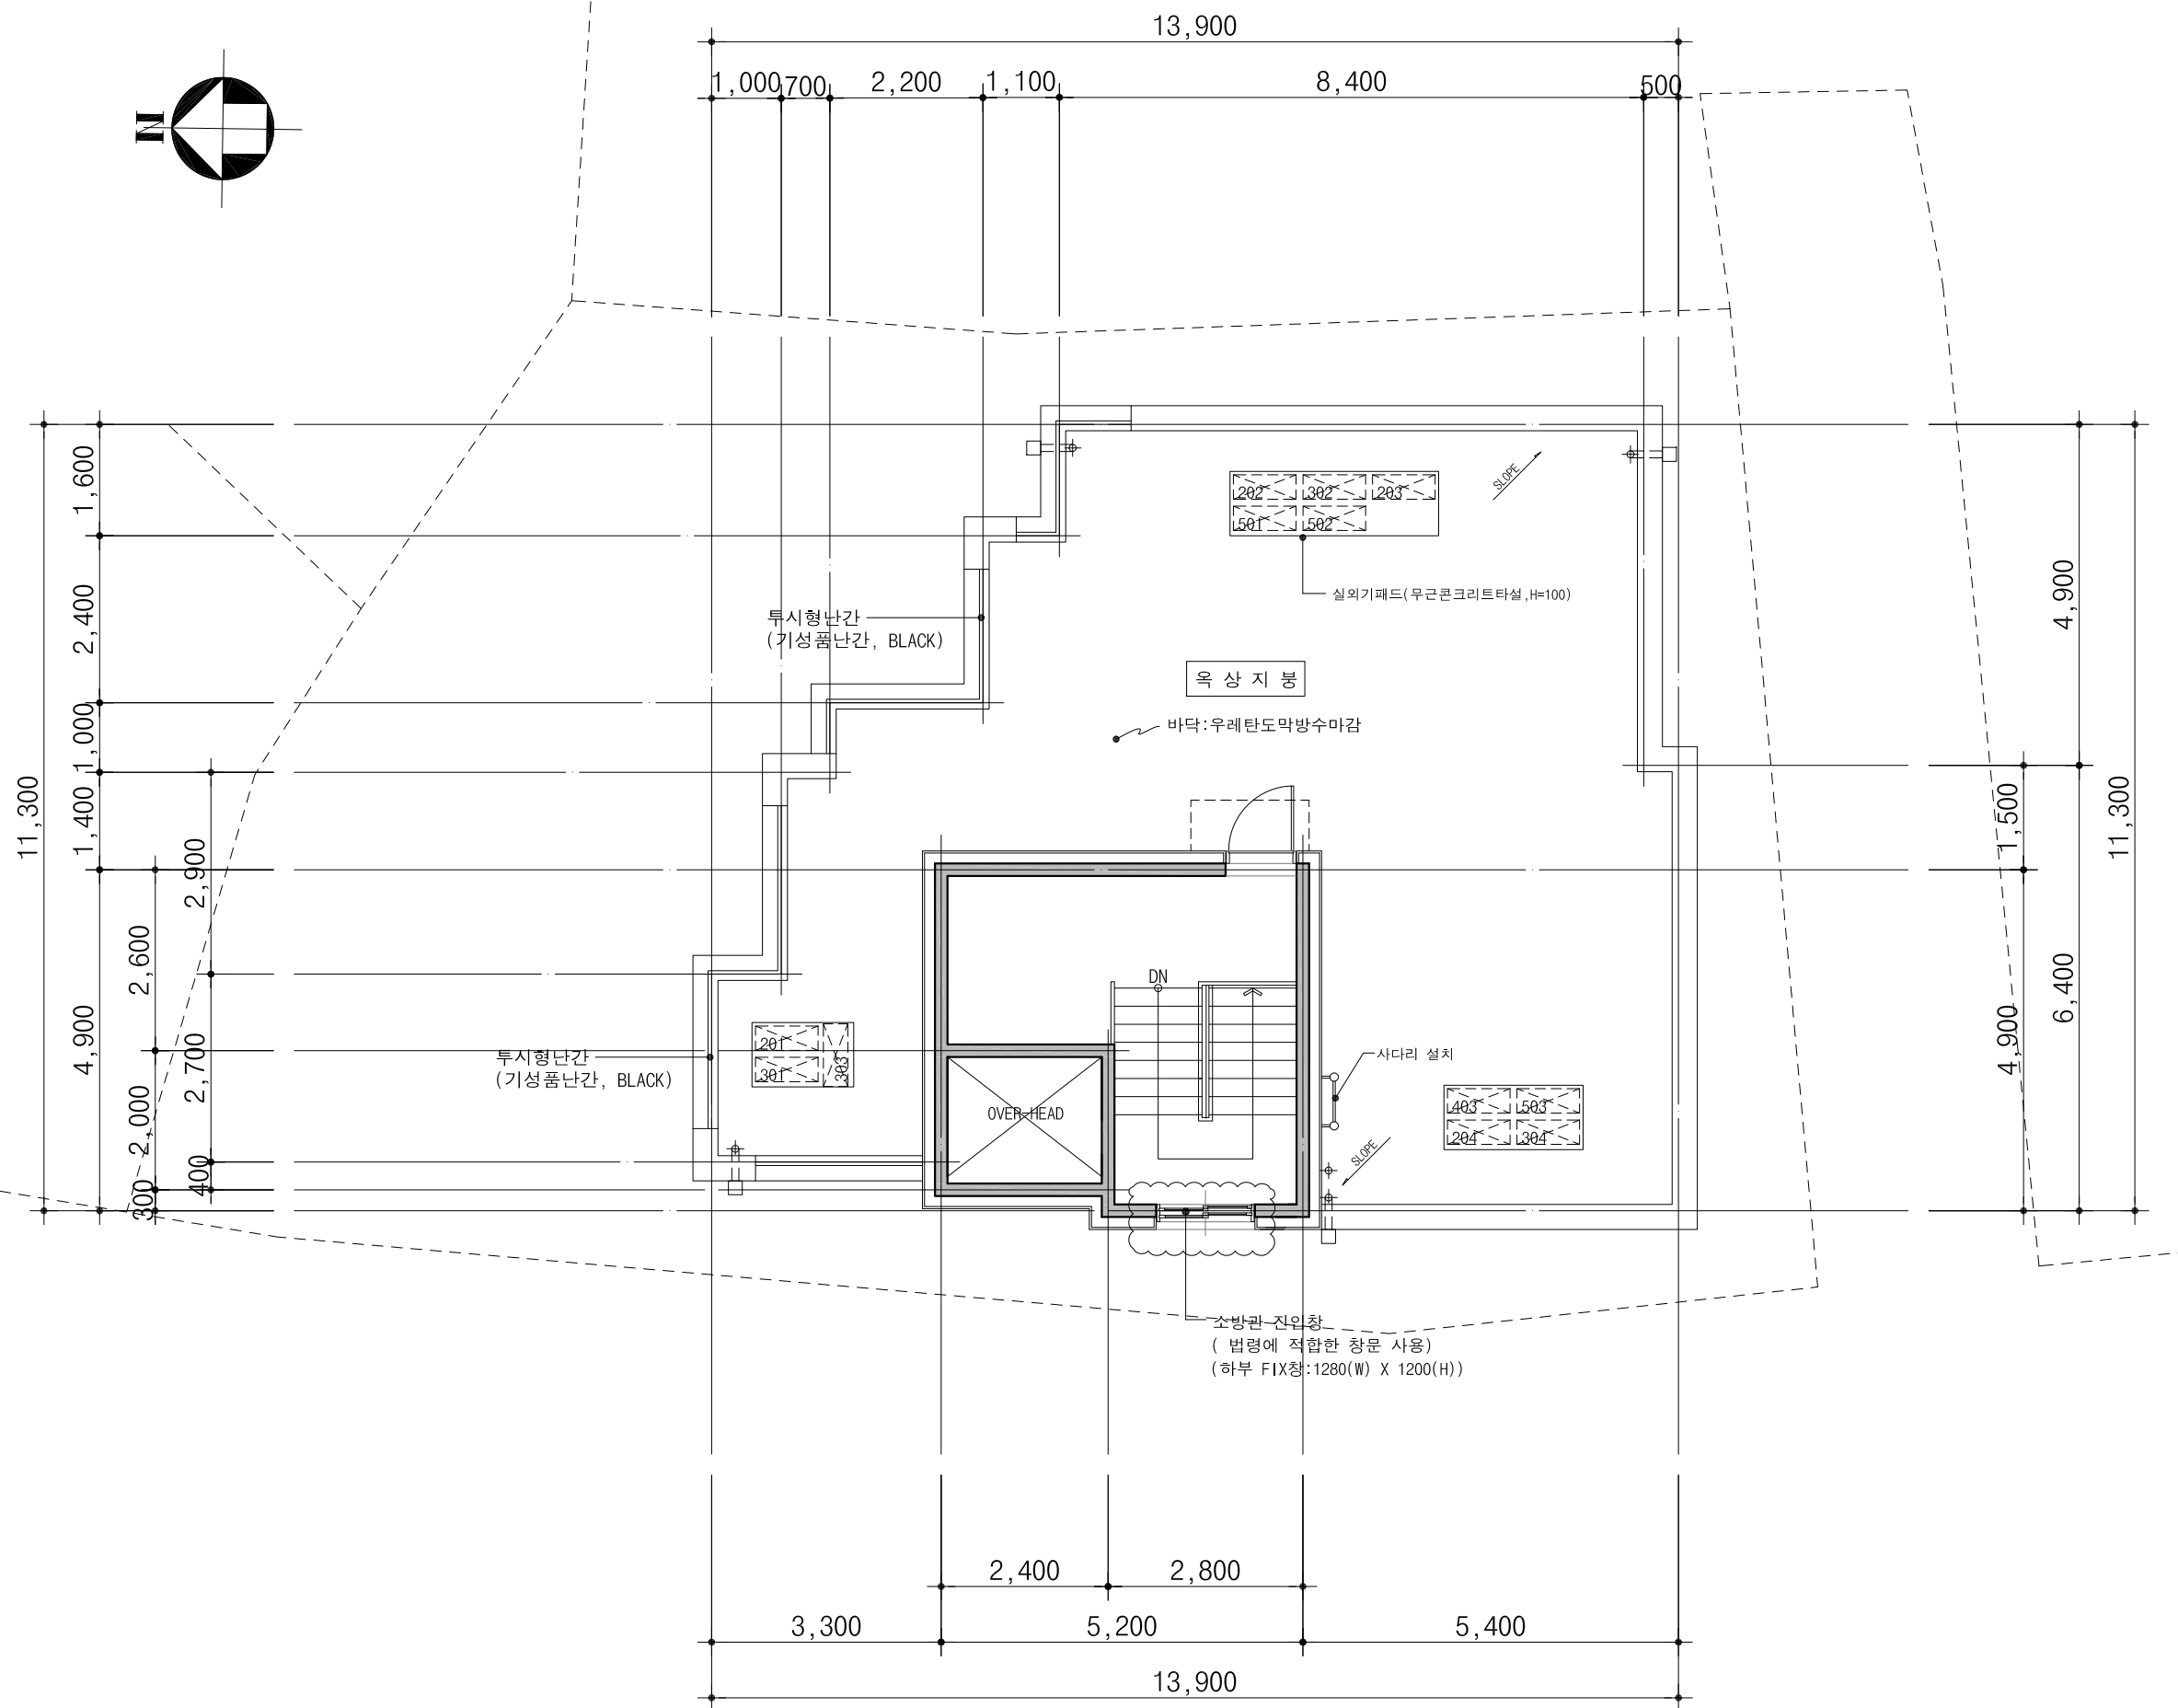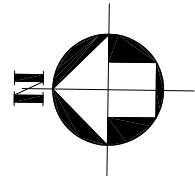

옥탑층 평면도



축척: 1/100



NOTE:

PROJECT 강북구 우이동 32-3번지
도시형생활주택 (원룸형) 청년주택 신축공사
APPROVED BY 건축사 구연목
건축사사무소 유일엔지니어링
서울특별시 서초구 반포대로 14길71(서초동)
[0서초에클라트(1904호)]
TEL : 02) 540-1546, FAX : 02)540-1576

TITLE 옥탑층 평면도

날짜 DATE: 2022. 09. .

SCALE	1/ 100	DWG NO.	A - 013	REV.
-------	--------	---------	---------	------

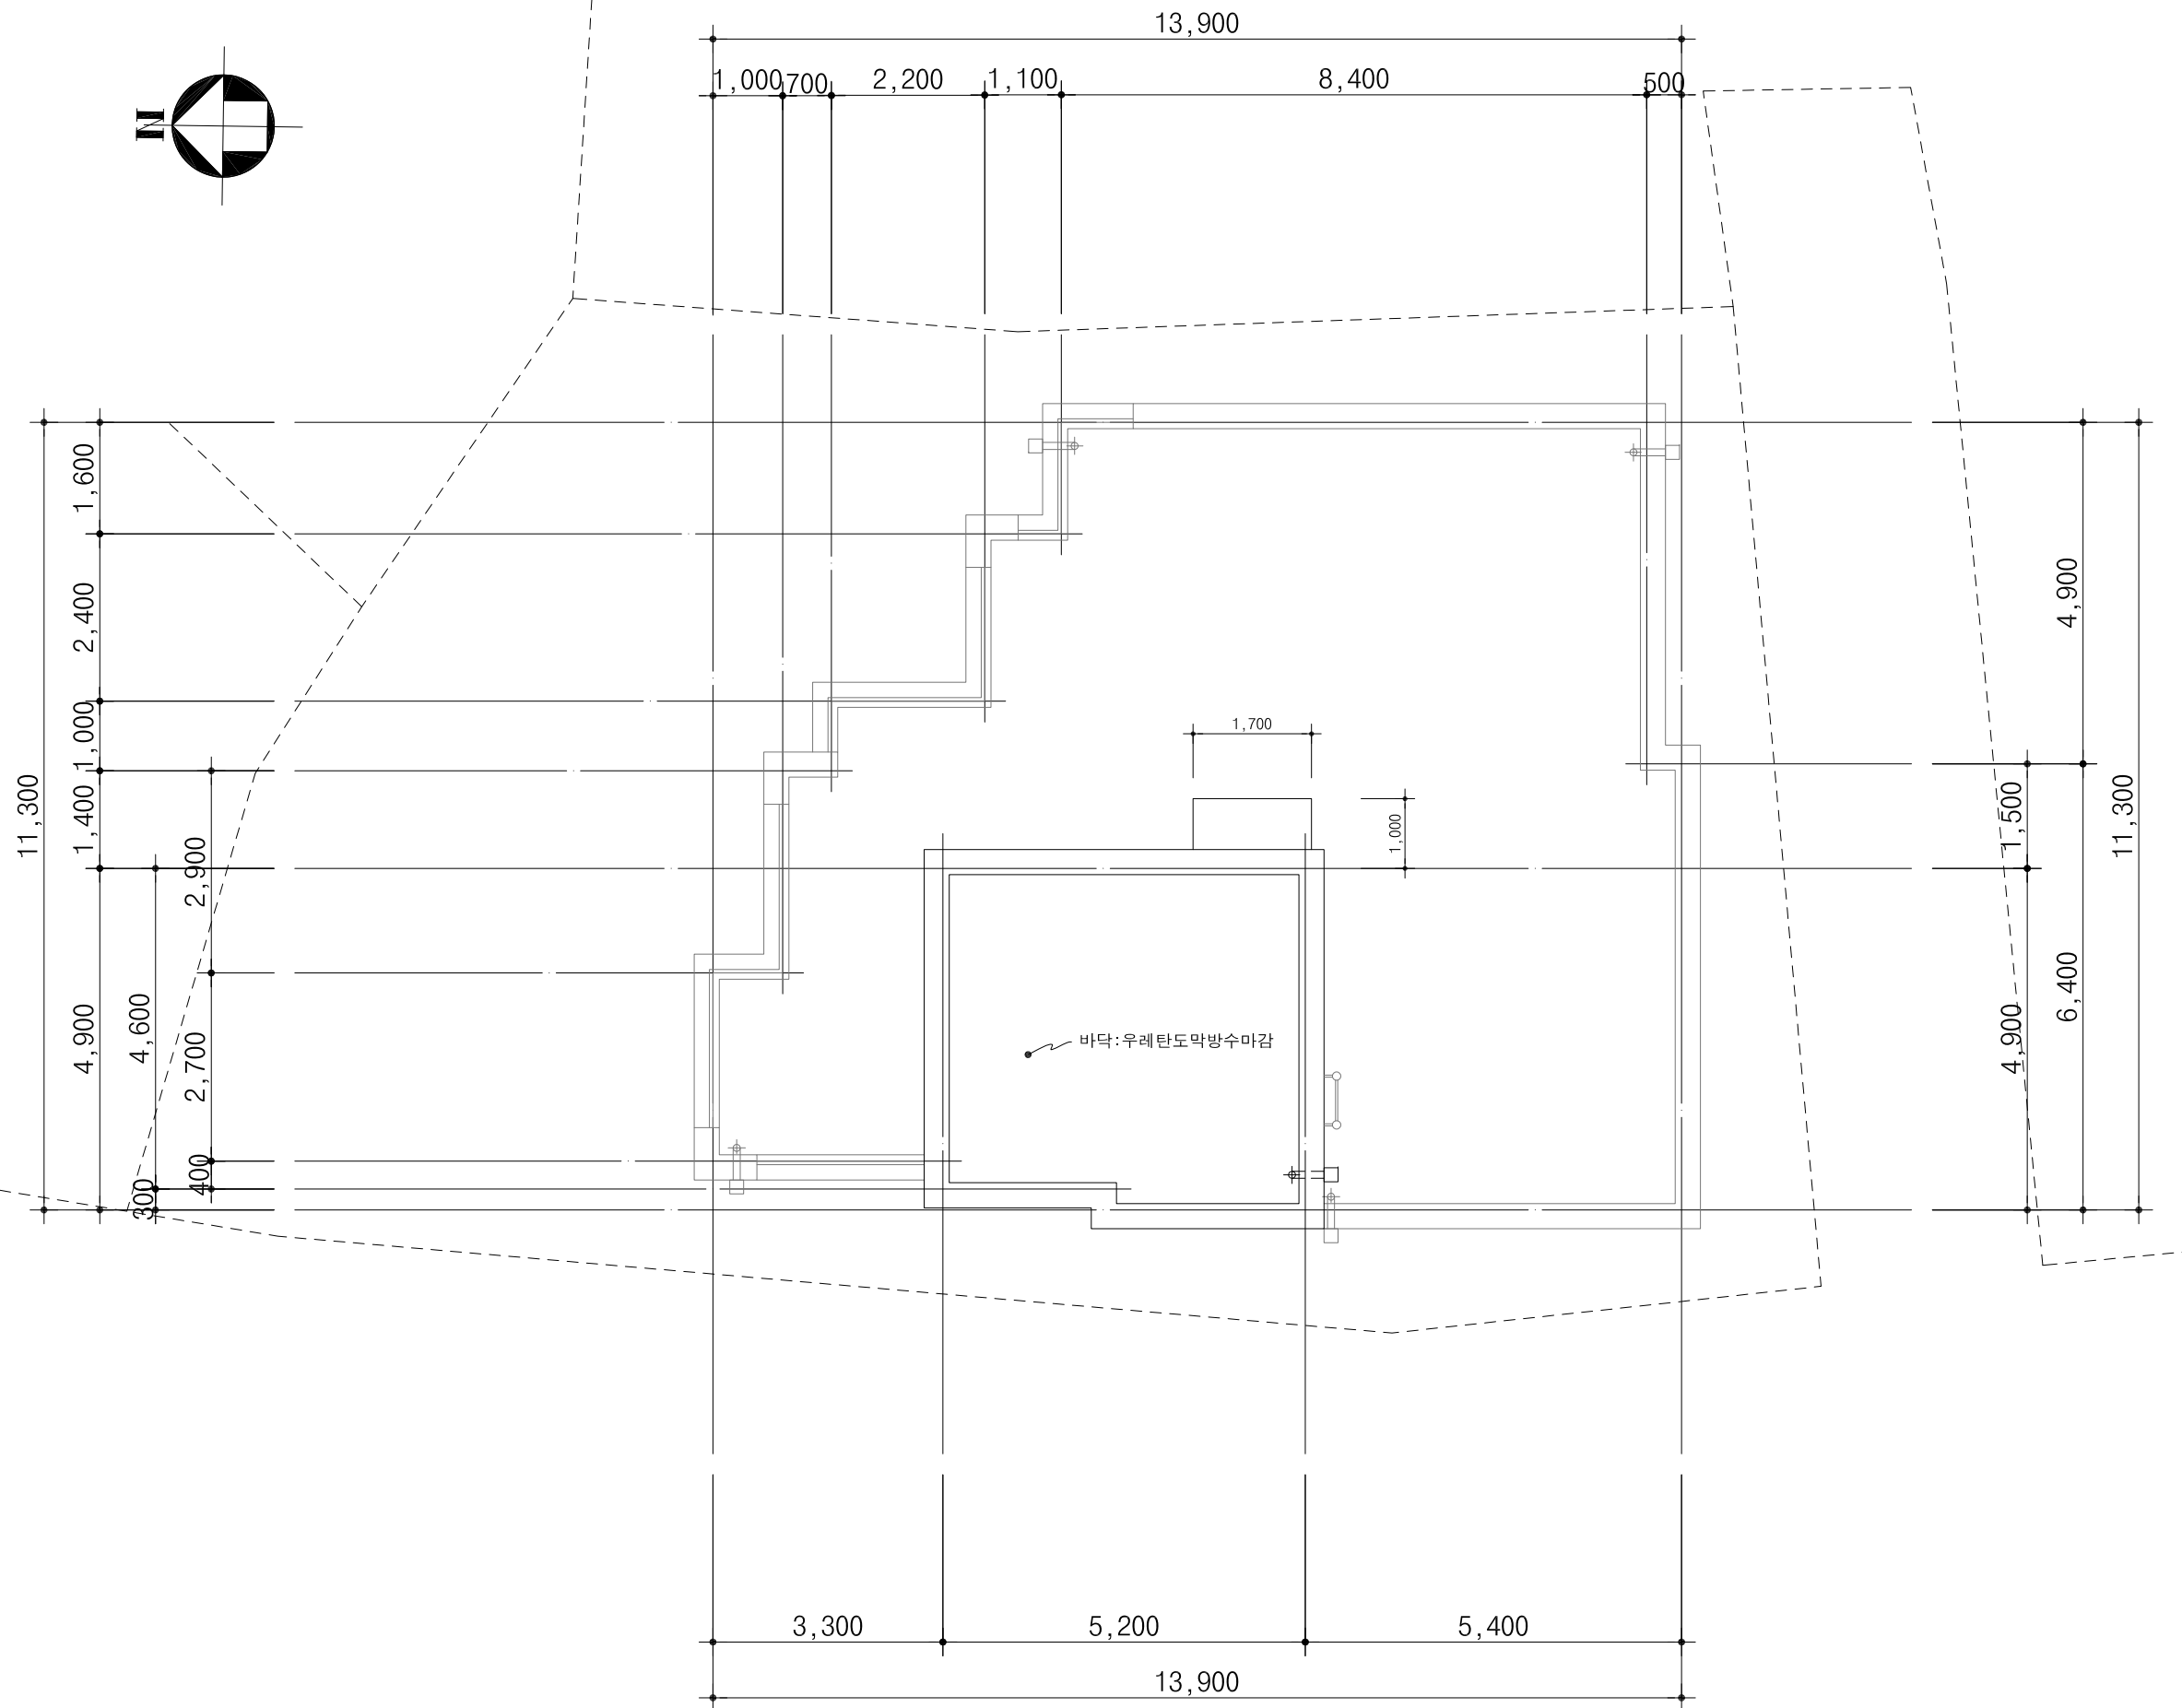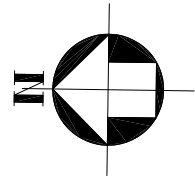

옥탑지붕 평면도



축척: 1/100

NOTE:

PROJECT 강북구 우이동 32-3번지
도시형생활주택 (원룸형) 청년주택 신축공사

APPROVED BY 건축사 구연목




건축사사무소 유일엔지니어링
서울특별시 서초구 반포대로 14길71(서초동)
[0서초에클라트(1904호)]
TEL : 02) 540-1546, FAX : 02) 540-1576

TITLE 옥탑지붕 평면도

날짜 DATE: 2022. 09. .

SCALE	1/ 100	DWG NO.	A - 014	REV.
-------	--------	---------	---------	------

KEY - PLAN

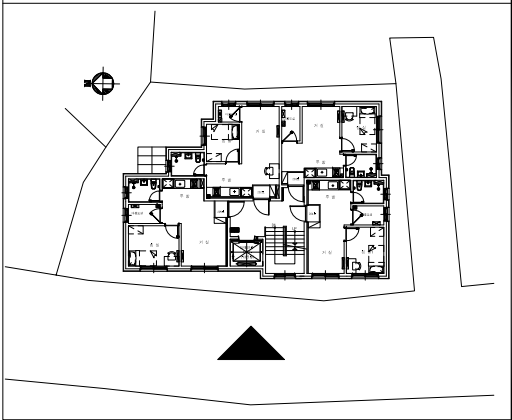

투시형난간(기성품난간, BLACK)
석재뿔철마감(기둥)

T30 라임스톤
T22 복층유리 이중창
투시형난간(기성품난간, BLACK)
T30 화강석 (버터플라이화이트)

▼ PH1 SL

▼ ROOF SL

▼ 5TH SL

▼ 4TH SL

▼ 3TH SL

▼ 2ND SL

▼ 1ST SL

3.00M 이상
막다른 도로

GL +1300

AL천장마감(준불연재)

GL ±0.00

GL -700

정면도

축척 : 1/100



NOTE:

PROJECT 강북구 우이동 32-3번지
도시형생활주택 (원룸형) 청년주택 신축공사

APPROVED BY 건축사 구연목




건축사사무소 유일엔지니어링
서울특별시 서초구 반포대로 14길71(서초동)
(0서호에클라트(1904호))
TEL : 02) 540-1546, FAX : 02) 540-1576

TITLE 정면도

날짜 DATE: 2022. 09. .

SCALE	1/ 100	DWG NO.	A - 015	REV.
-------	--------	---------	---------	------

KEY - PLAN

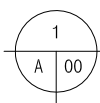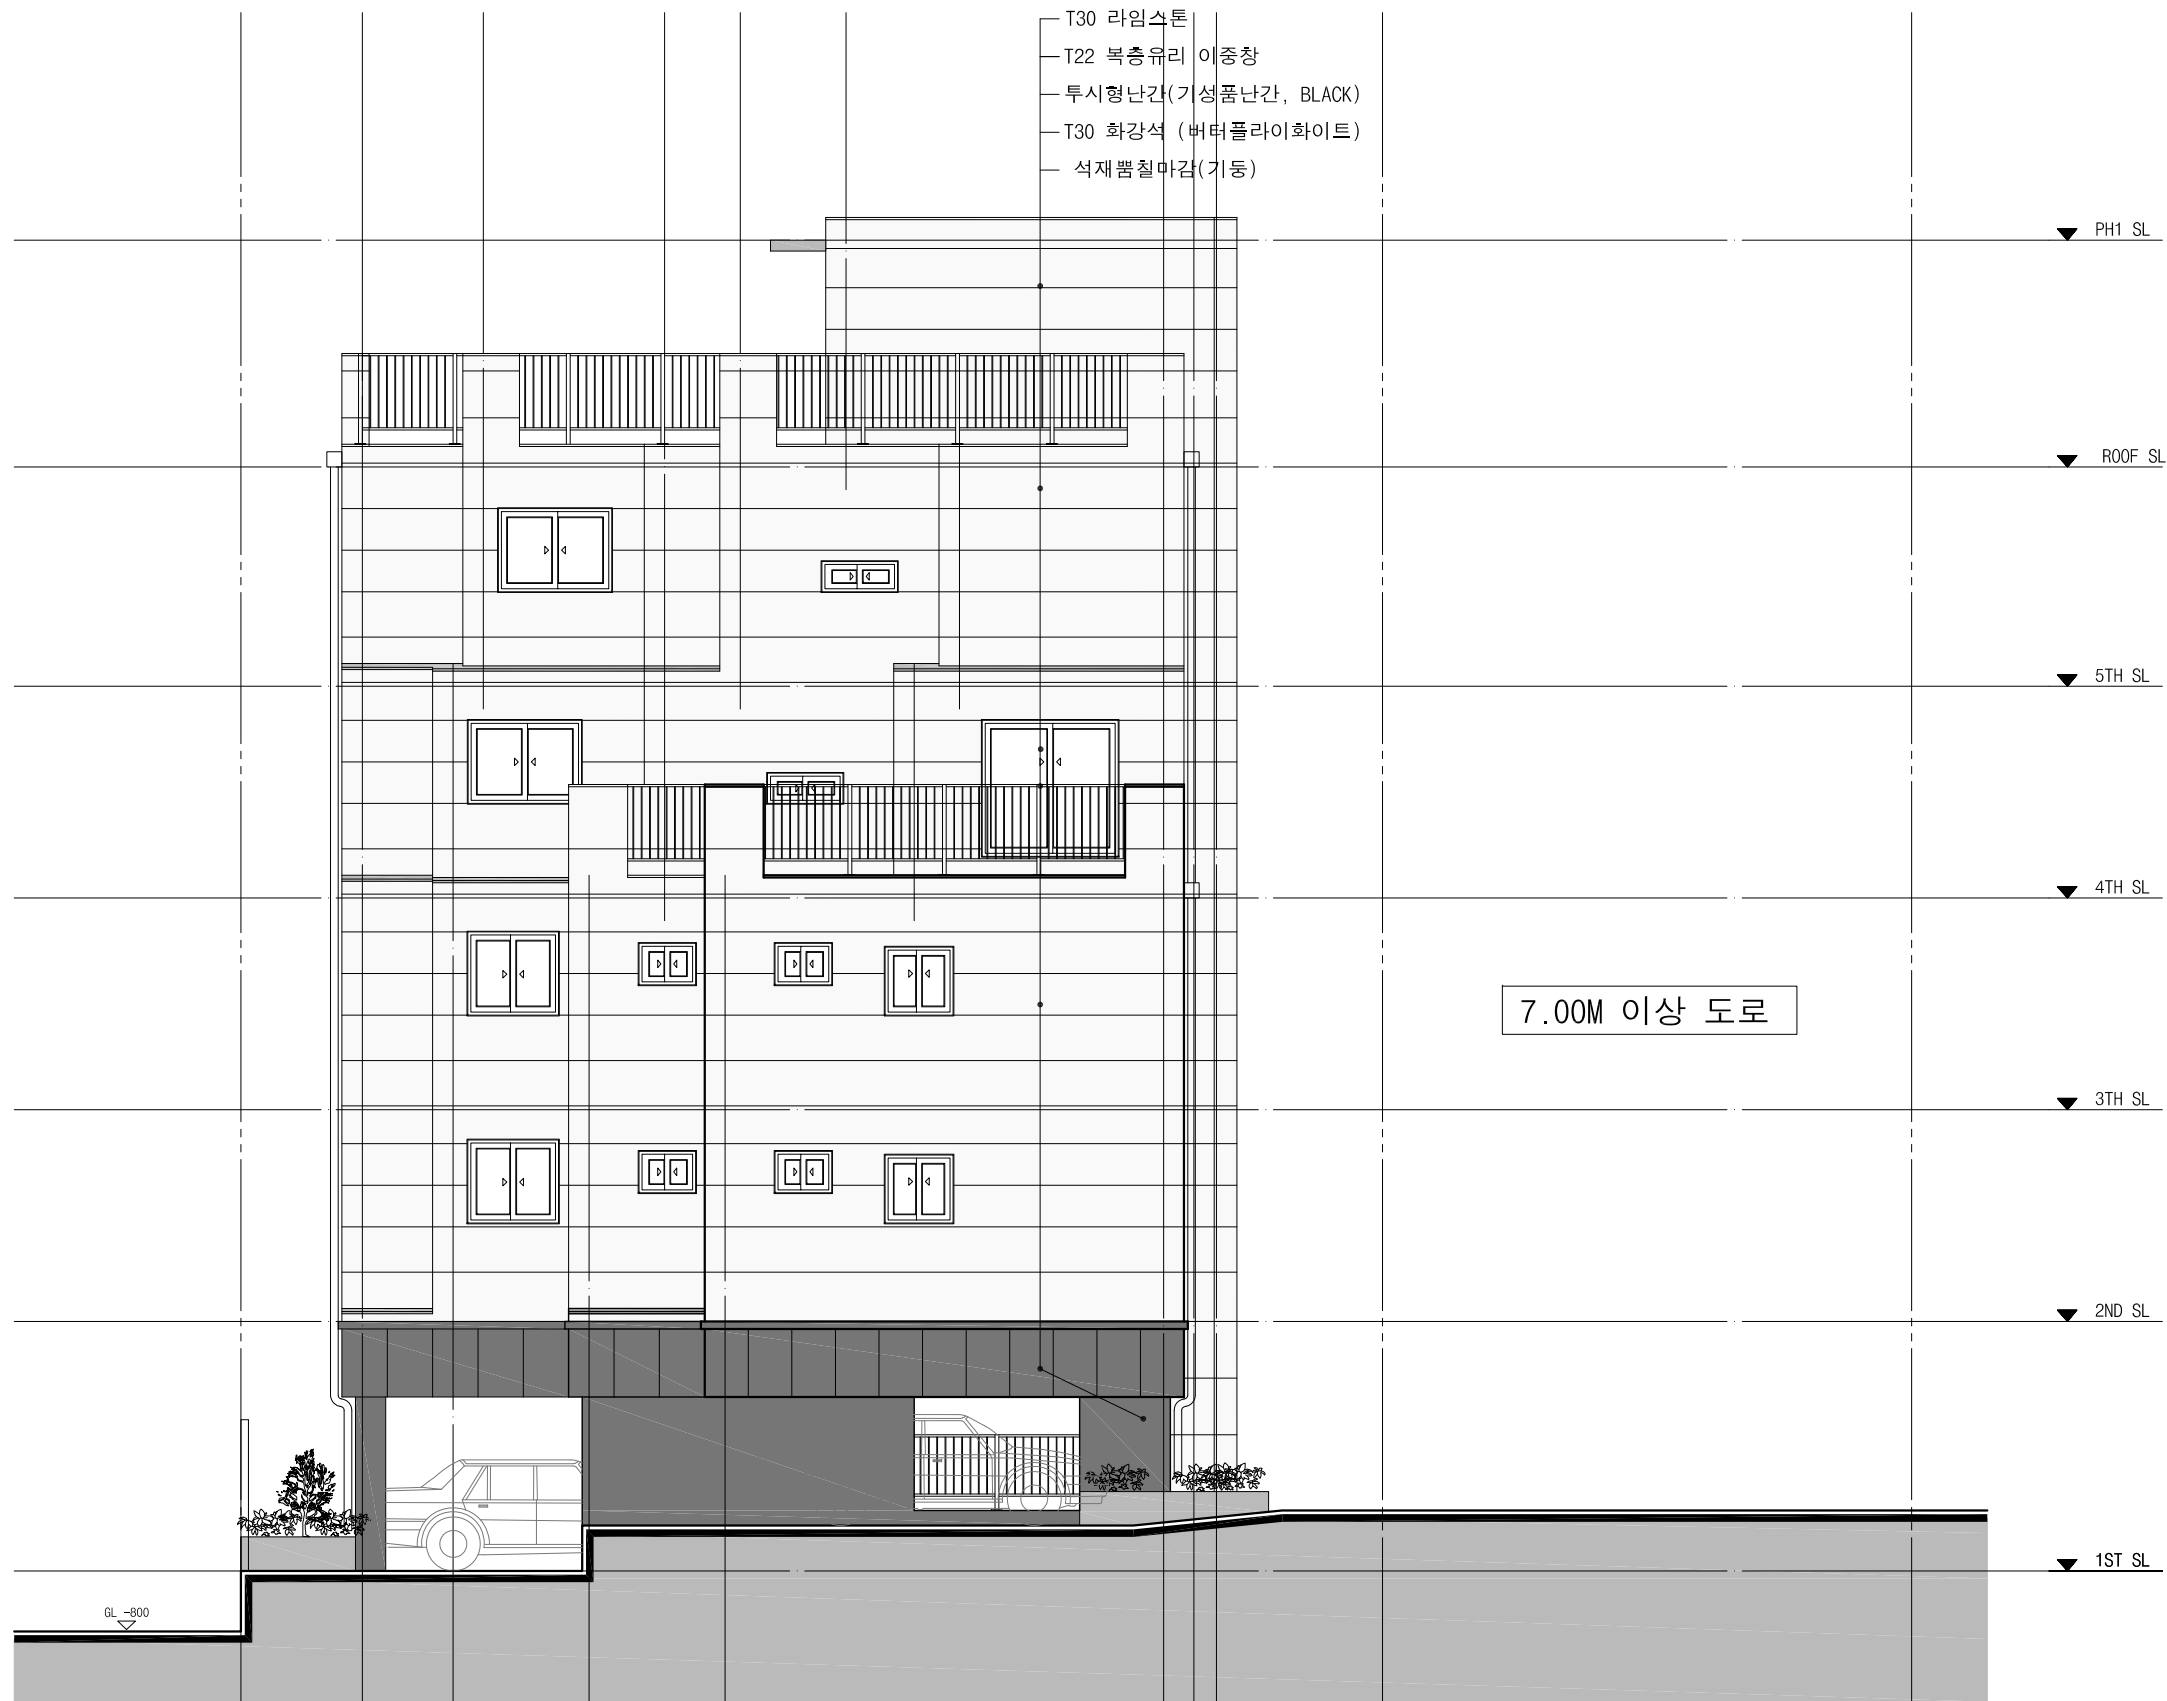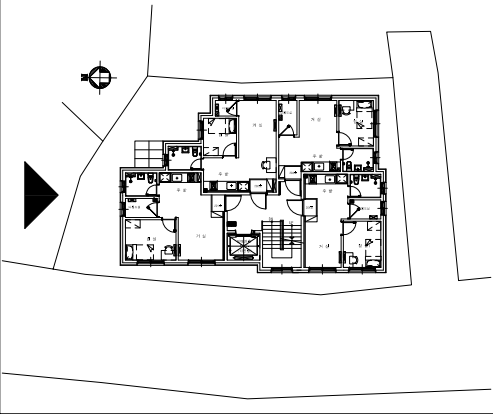

좌측면도

축척 : 1/100

NOTE:

PROJECT 강북구 우이동 32-3번지
도시형생활주택 (원룸형) 청년주택 신축공사

APPROVED BY

건축사 구연목



건축사사무소 유일엔지니어링

서울특별시 서초구 반포대로 14길71(서초동)
[0서초에클라트(1904호)]
TEL : 02) 540-1546, FAX : 02) 540-1576

TITLE

좌측면도

날짜

DATE:

2022. 09. .

SCALE



1/ 100

DWG NO.

A - 016

REV.

KEY - PLAN

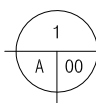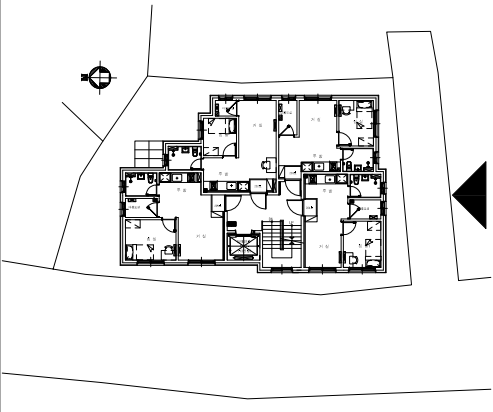

우 측 면 도

축척 : 1/100

NOTE:

PROJECT 강북구 우이동 32-3번지
도시형생활주택 (원룸형) 청년주택 신축공사

APPROVED BY 건축사 구 연 목

ARCHITECTURE & ENGINEERING
서울특별시 서초구 반포대로 14길71(서초동)
[0서초에클라트(1904호)]
TEL : 02) 540-1546, FAX : 02)540-1576

TITLE 우측면도

날짜
DATE: 2022. 09. .

SCALE	1/ 100	DWG NO.	A - 017	REV.
-------	--------	---------	---------	------