

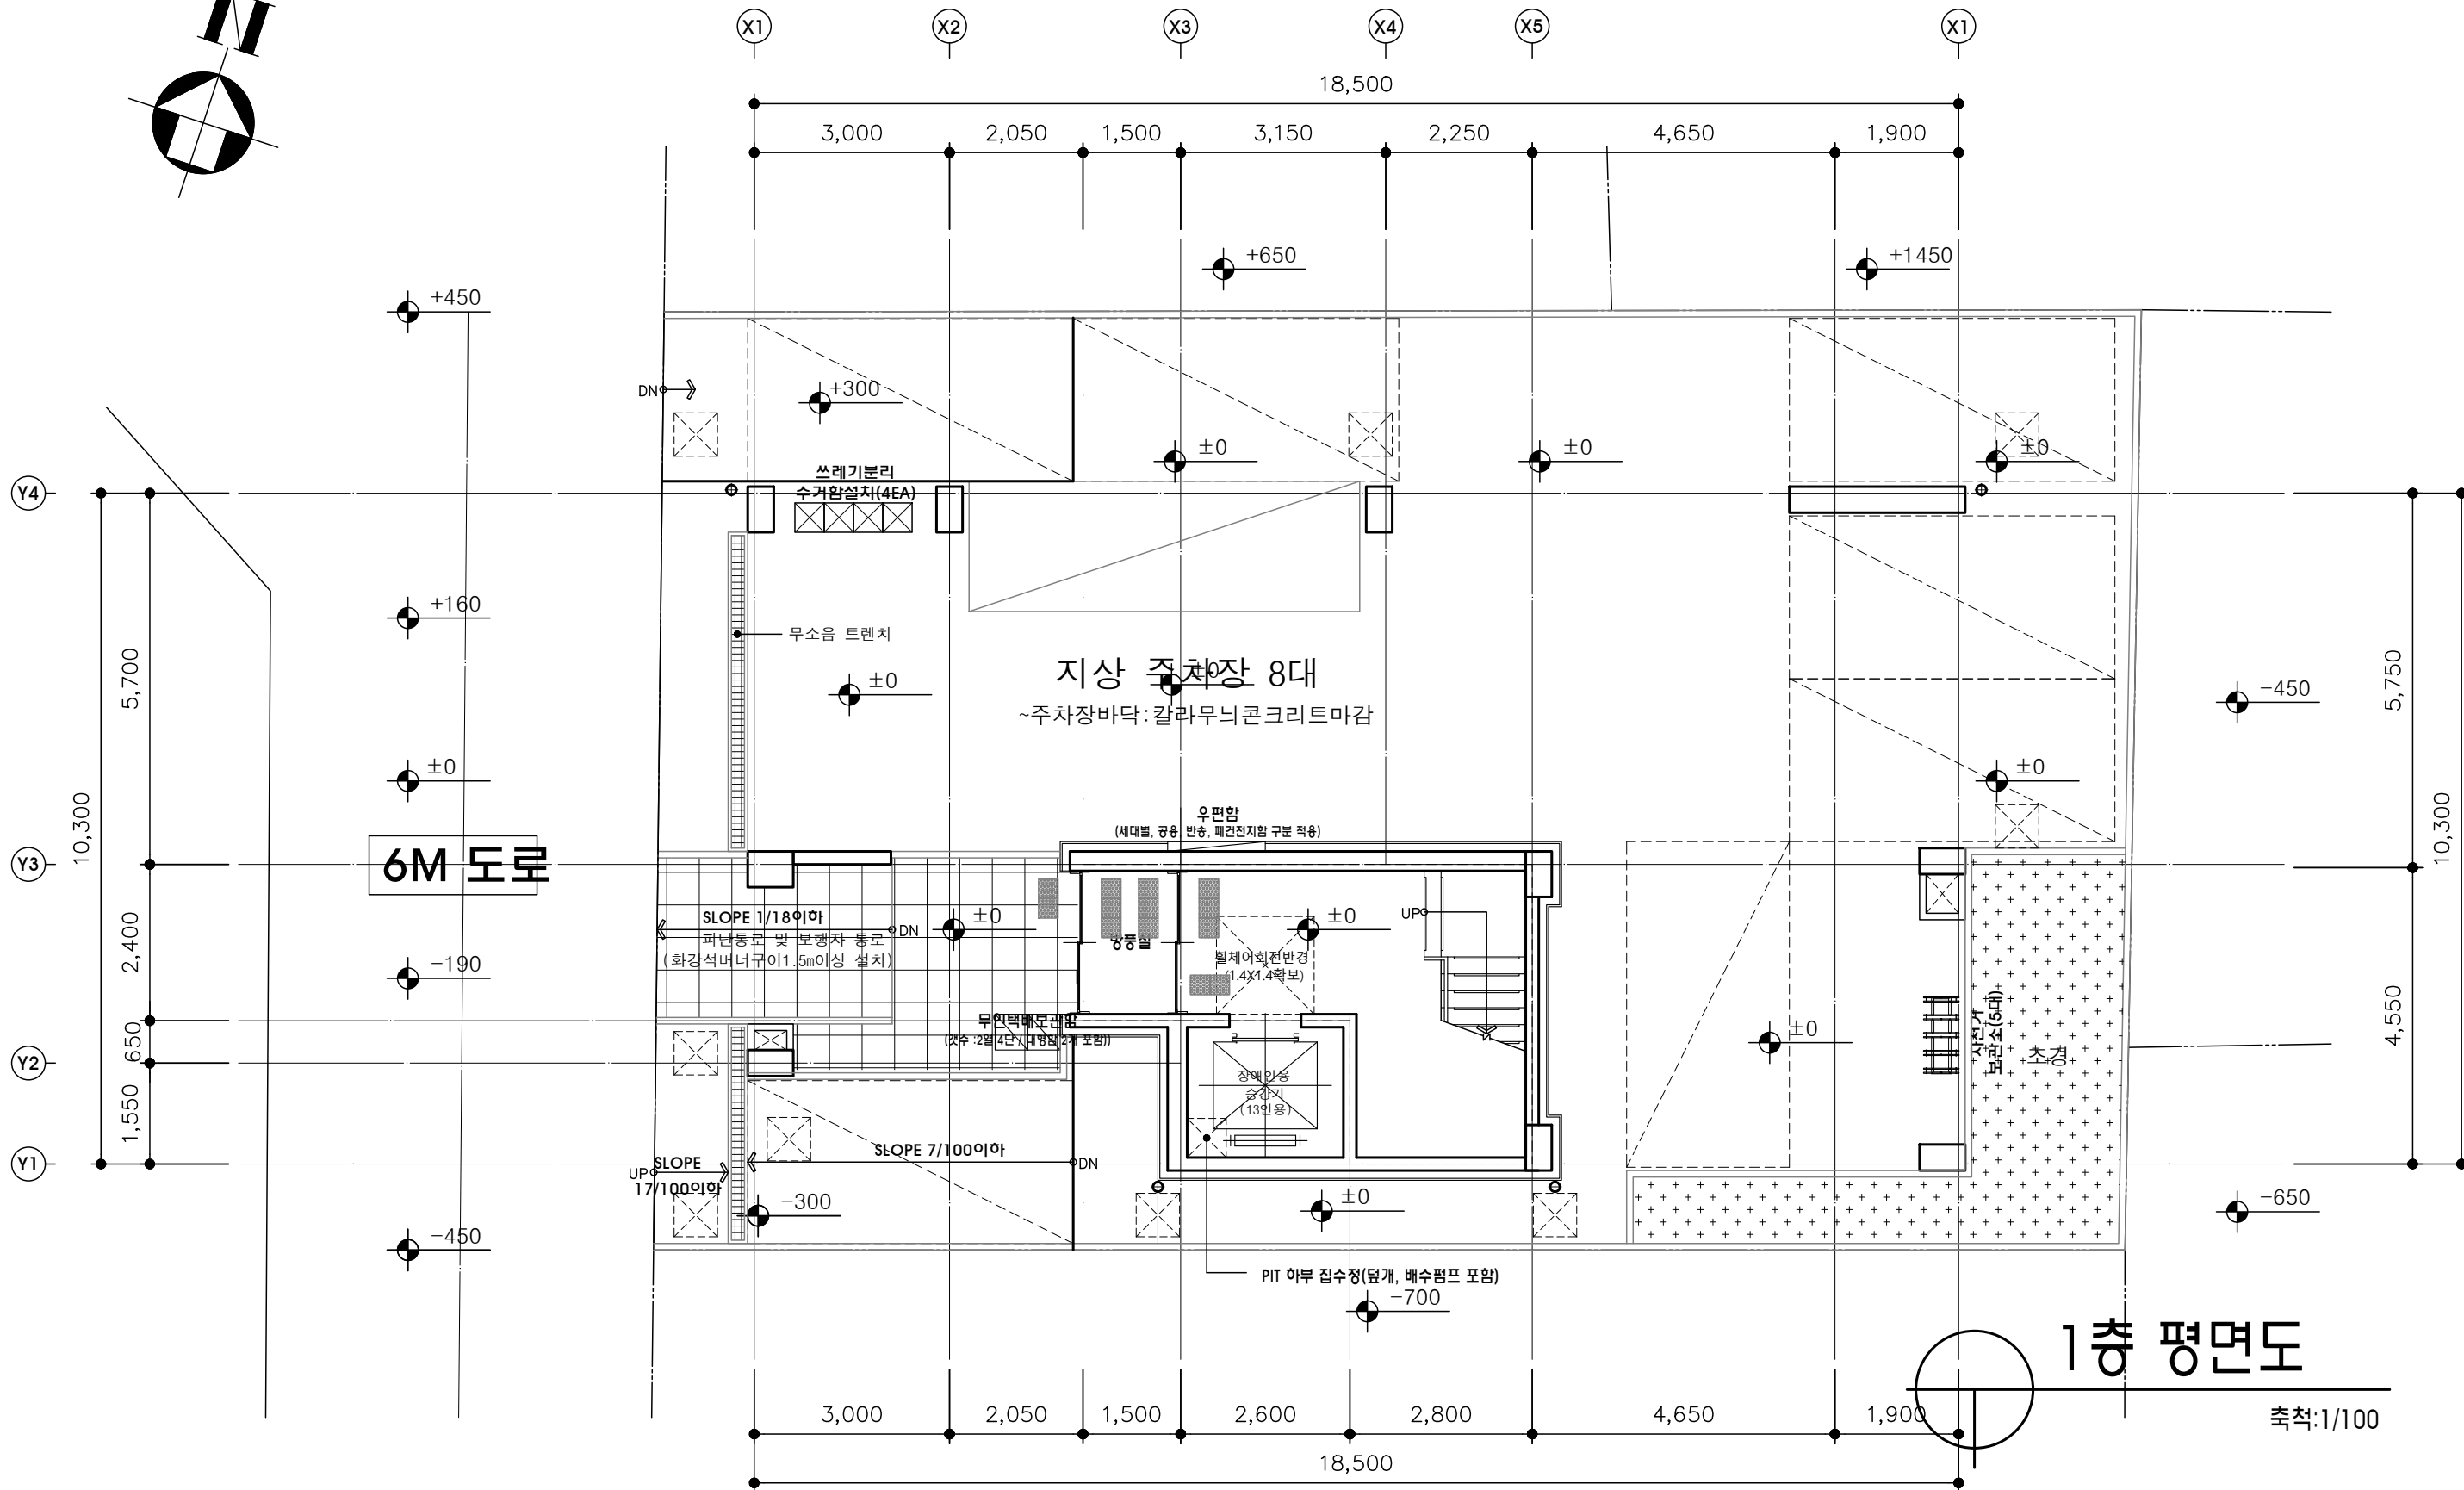
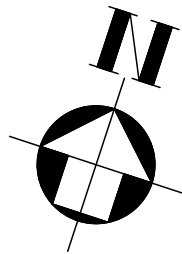



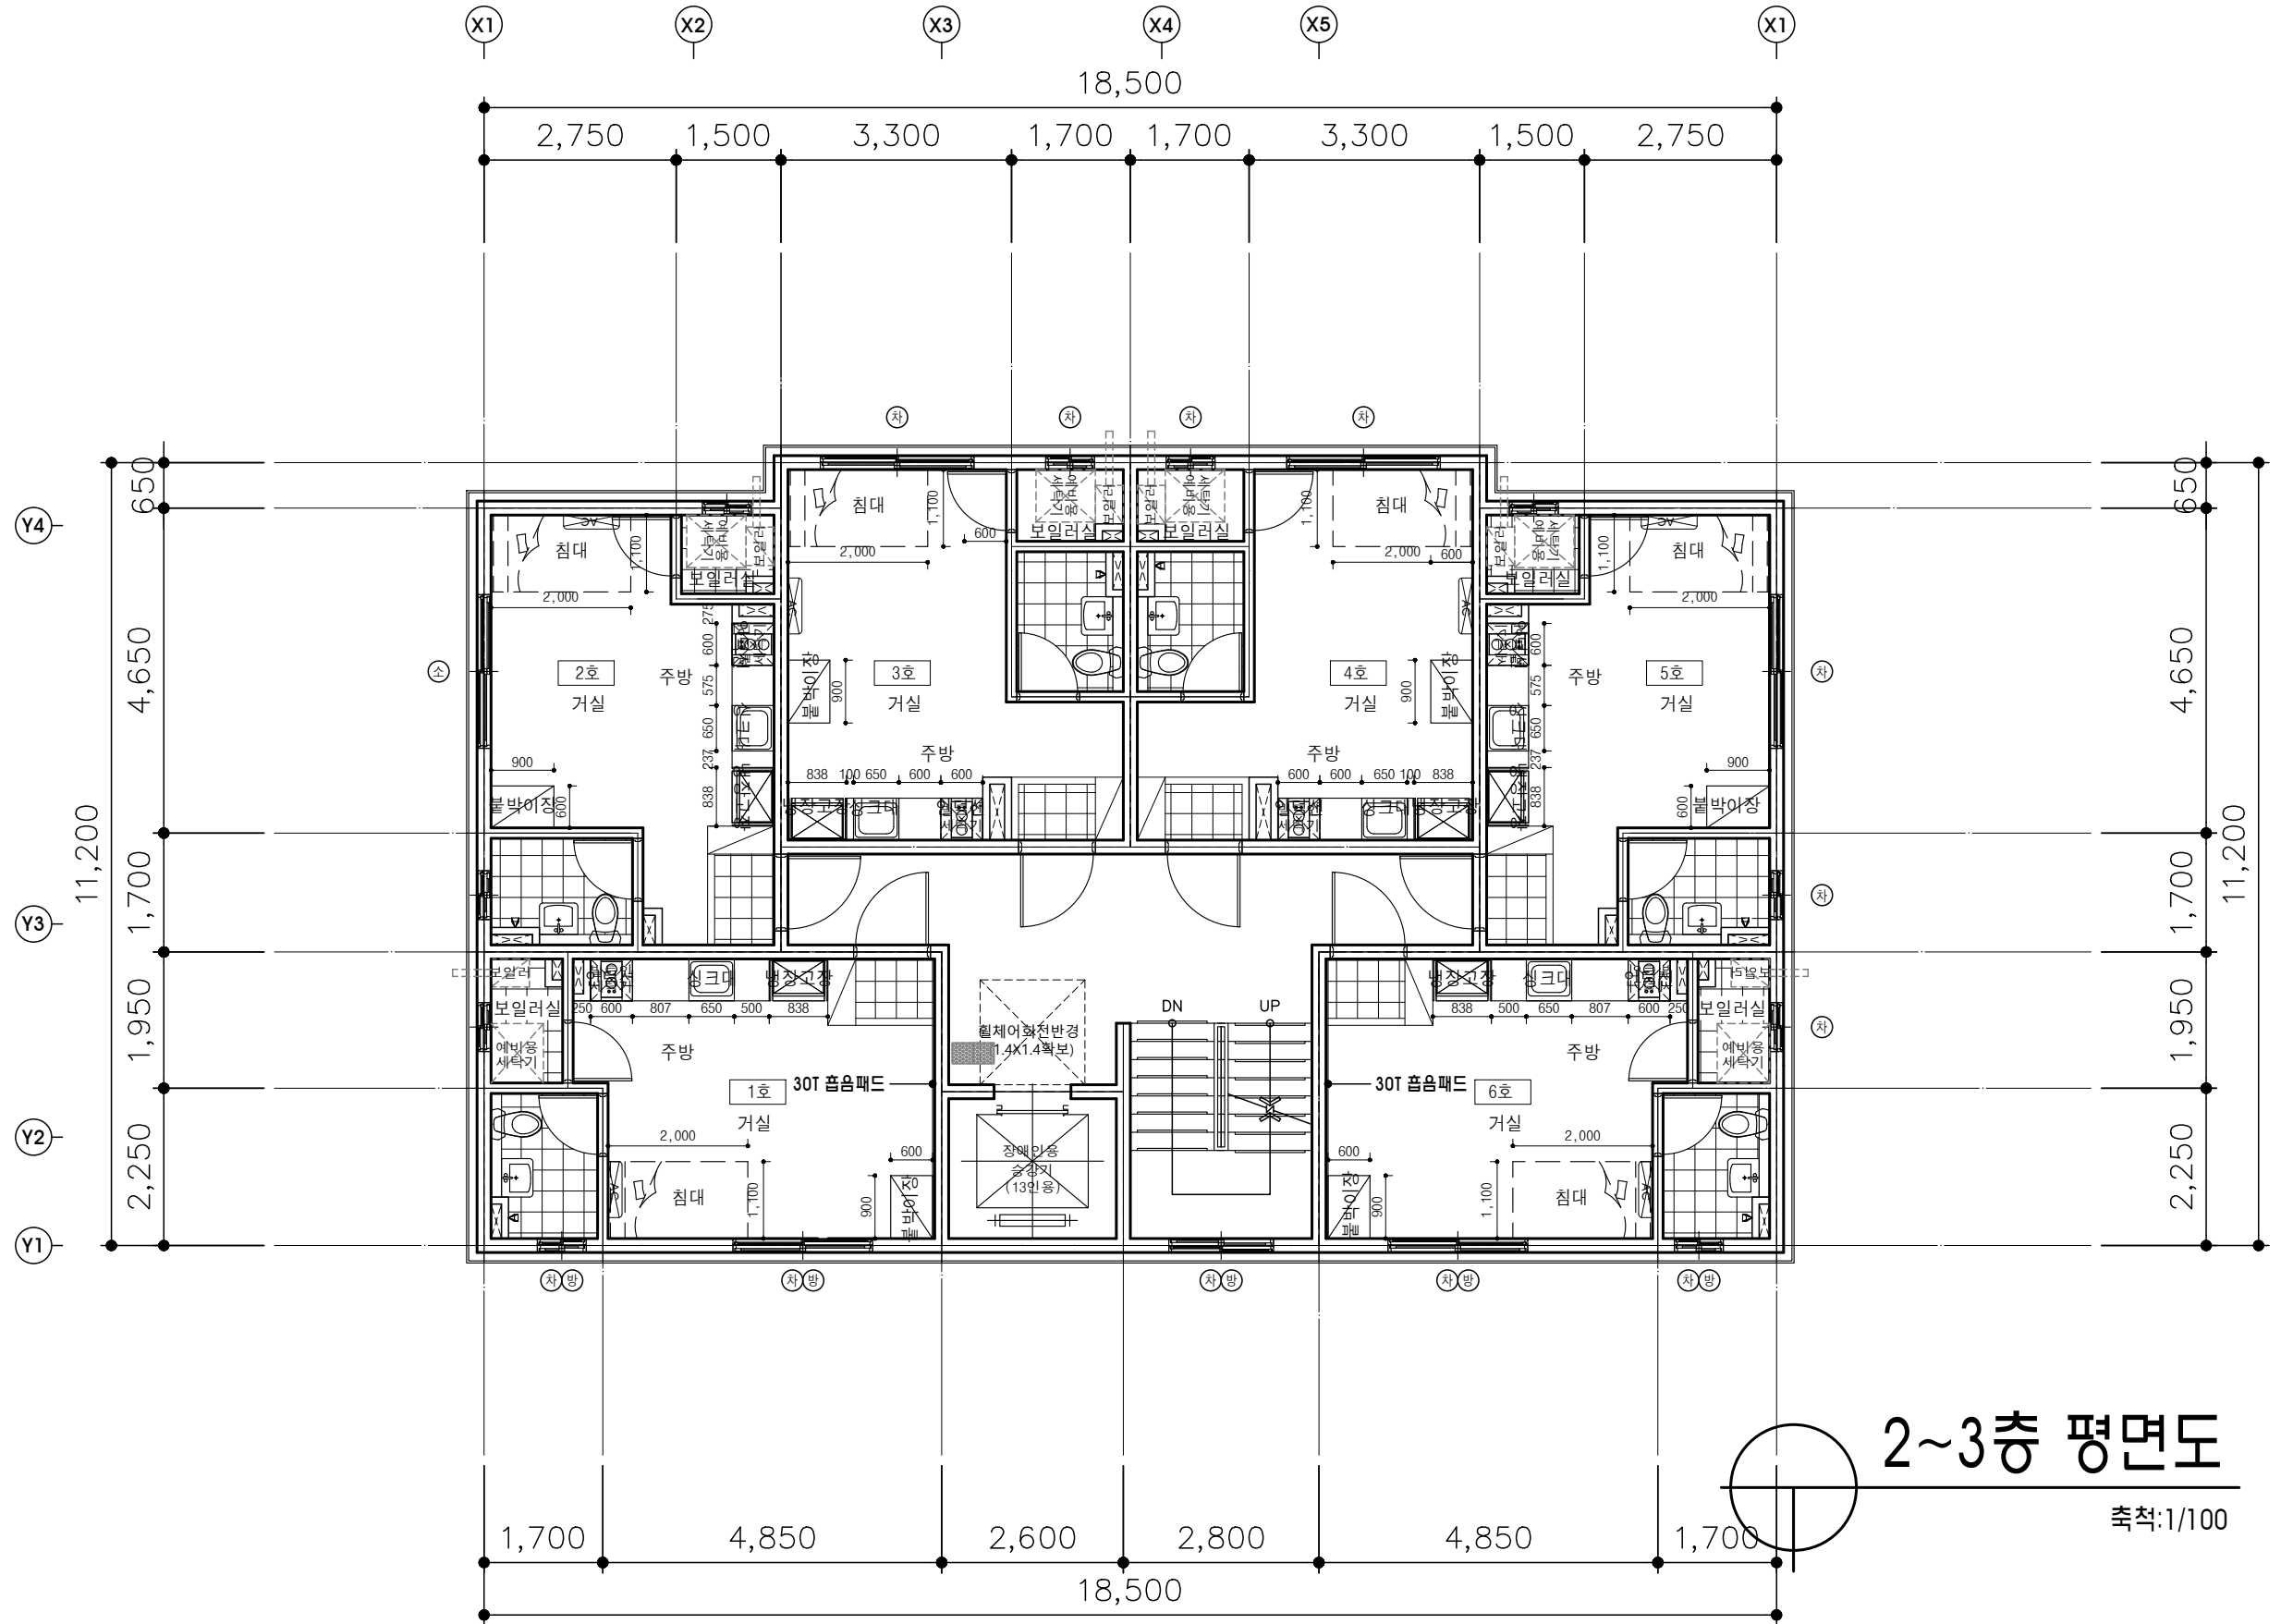


1층 평면도

축척: 1/100


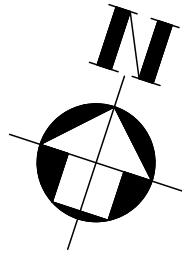


2~3층 평면도
축척: 1/100

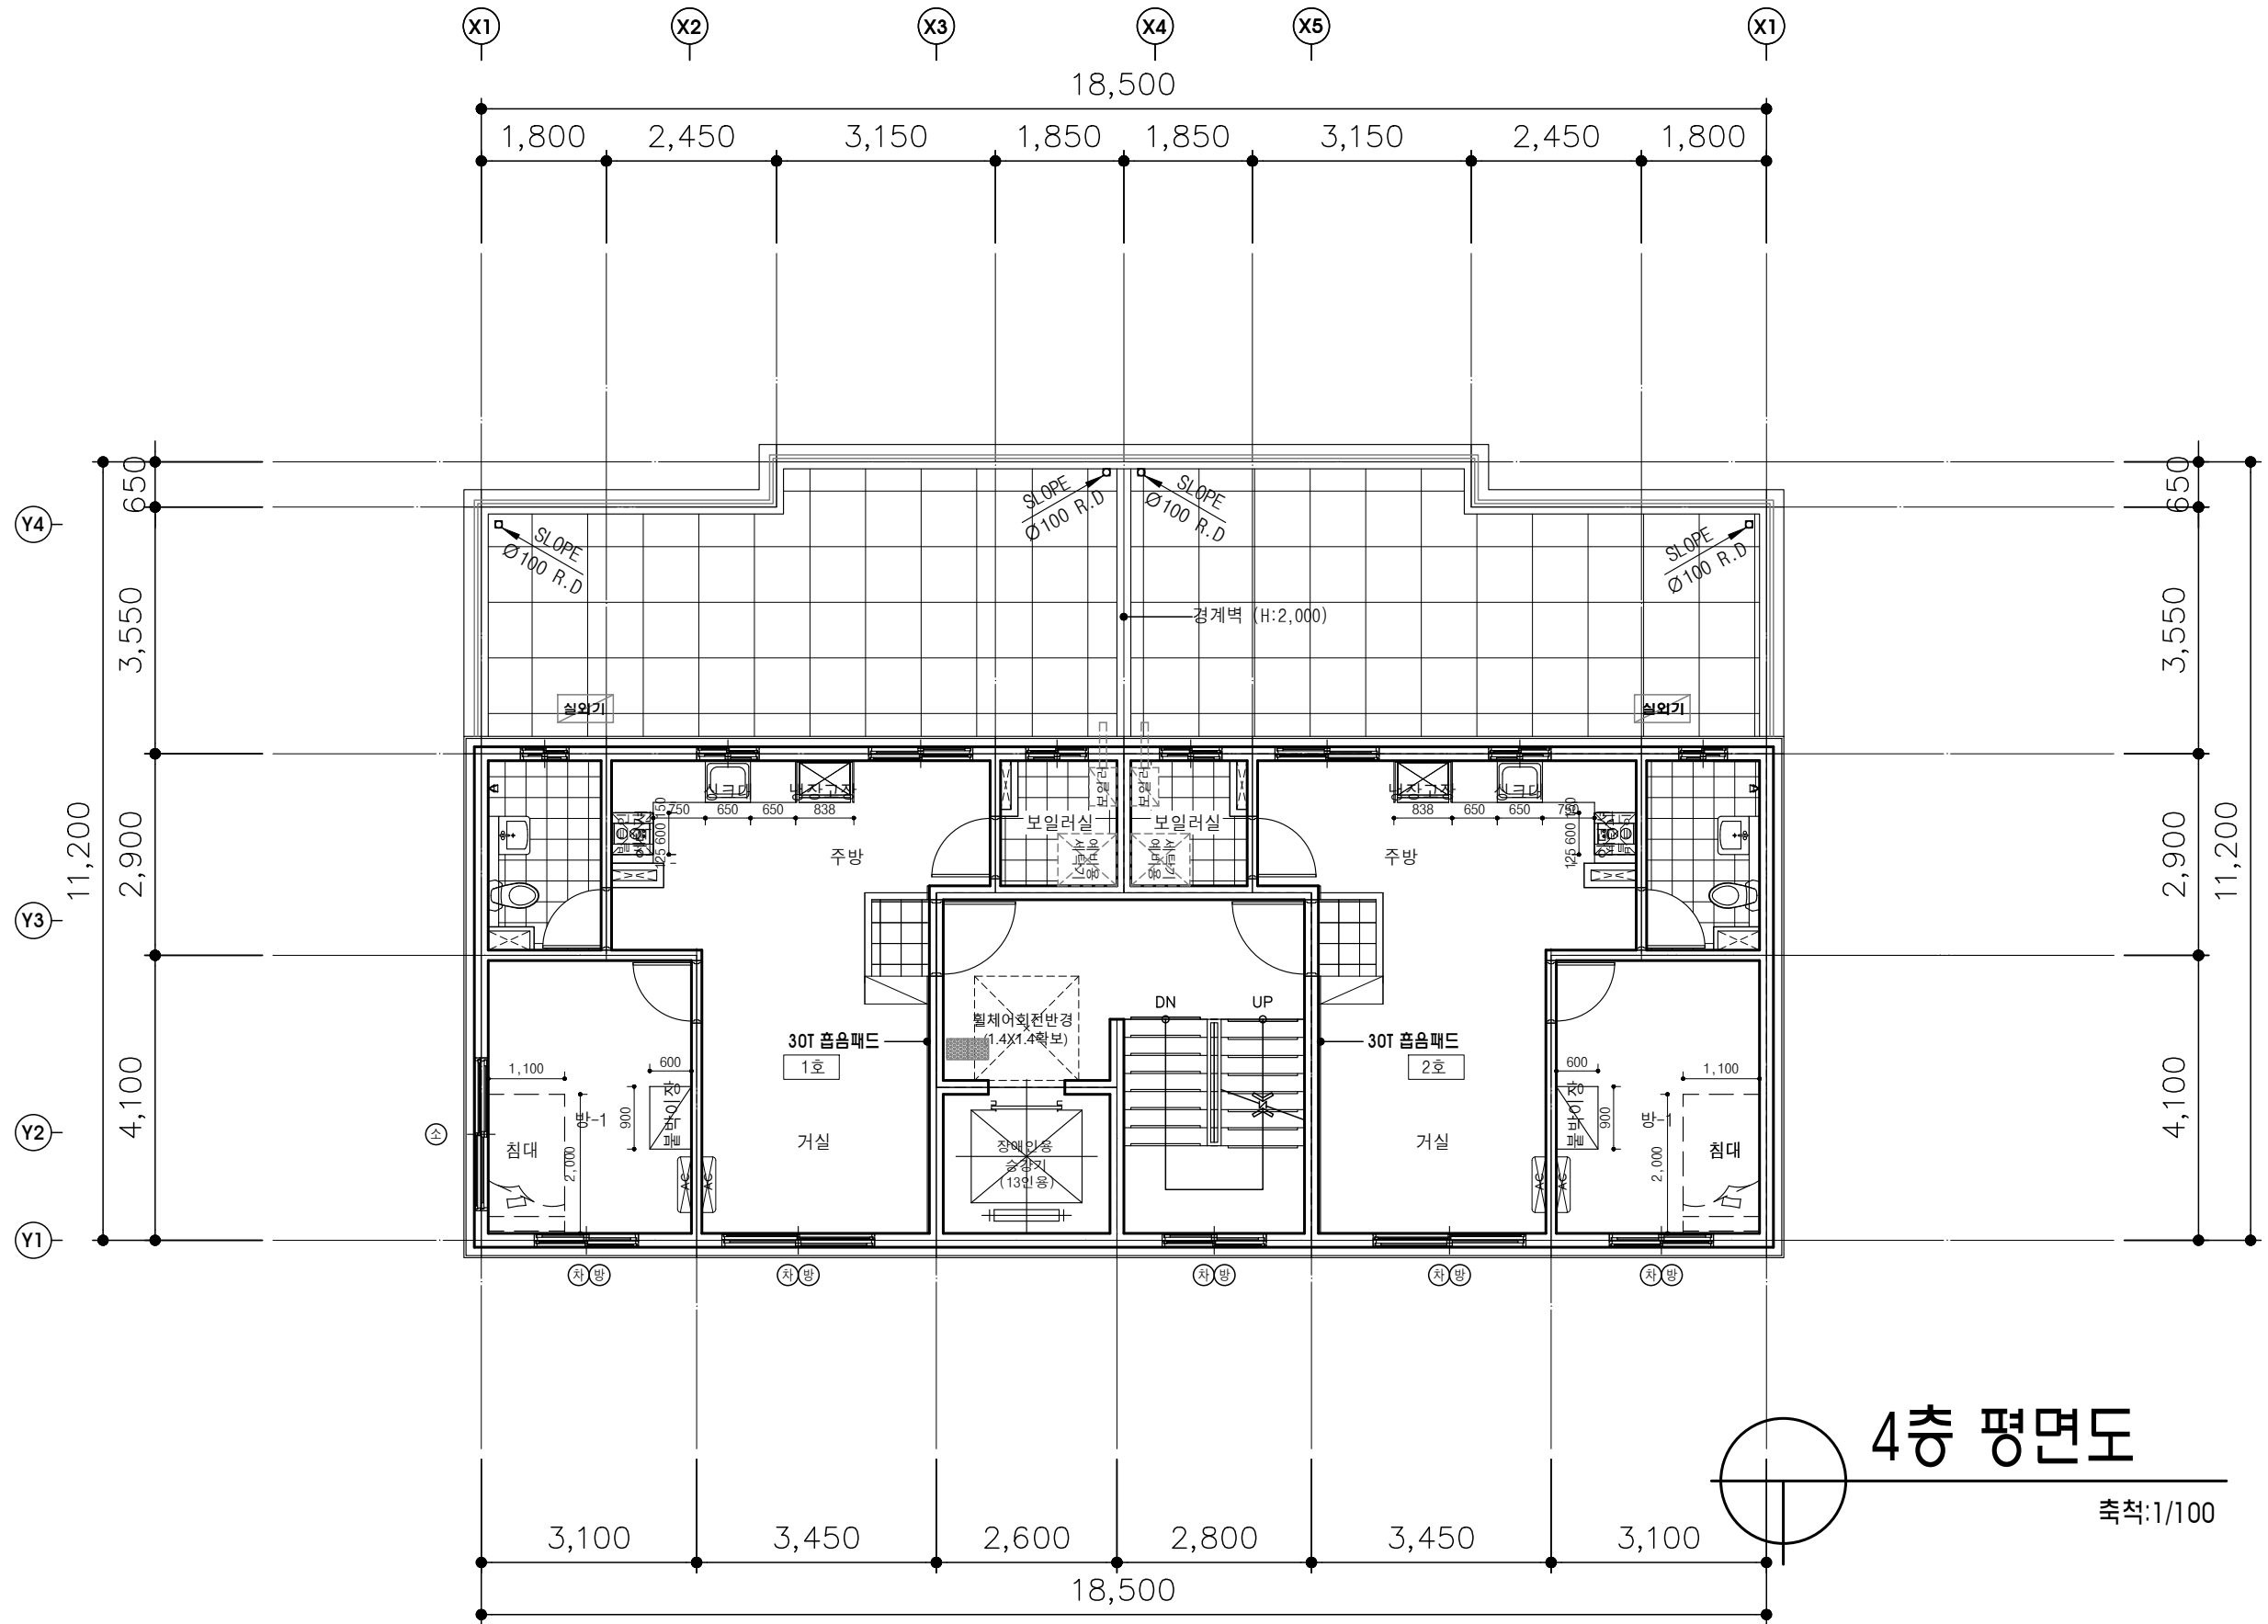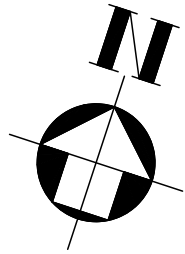




4층 평면도
축척: 1/100

비밀 생활 건축사 사무소 서울특별시 도봉구 마들로684-9 상가동 311호 T. 02 - 725 - 3491 F. 070 - 4337 - 0902	설계명 PROJECT TITLE 미아동 223-4 신축공사	노트 NOTE 다용도실 전열교환기 점검구 설치 (배관 점검 가능 해야 함.) 1. 청년 유형 가전 및 가구 -냉장고, 세탁기, 벽걸이에어컨, 불박이장 또는 이동식 옷장, 책상	설계구분 PROJECT KINDS 계획 설계	담당 DRAWN BY : 담당 DRAWN BY : 최 재 평	축척 SCALE	도면명칭 DRAWING TITLE
			설계번호 PROJECT NO. 20220248	검토 CHECKED BY : PIC APPROVED BY : 최 재 평	날짜 DATE 23년 09월	도면번호 SHEET NO. 14

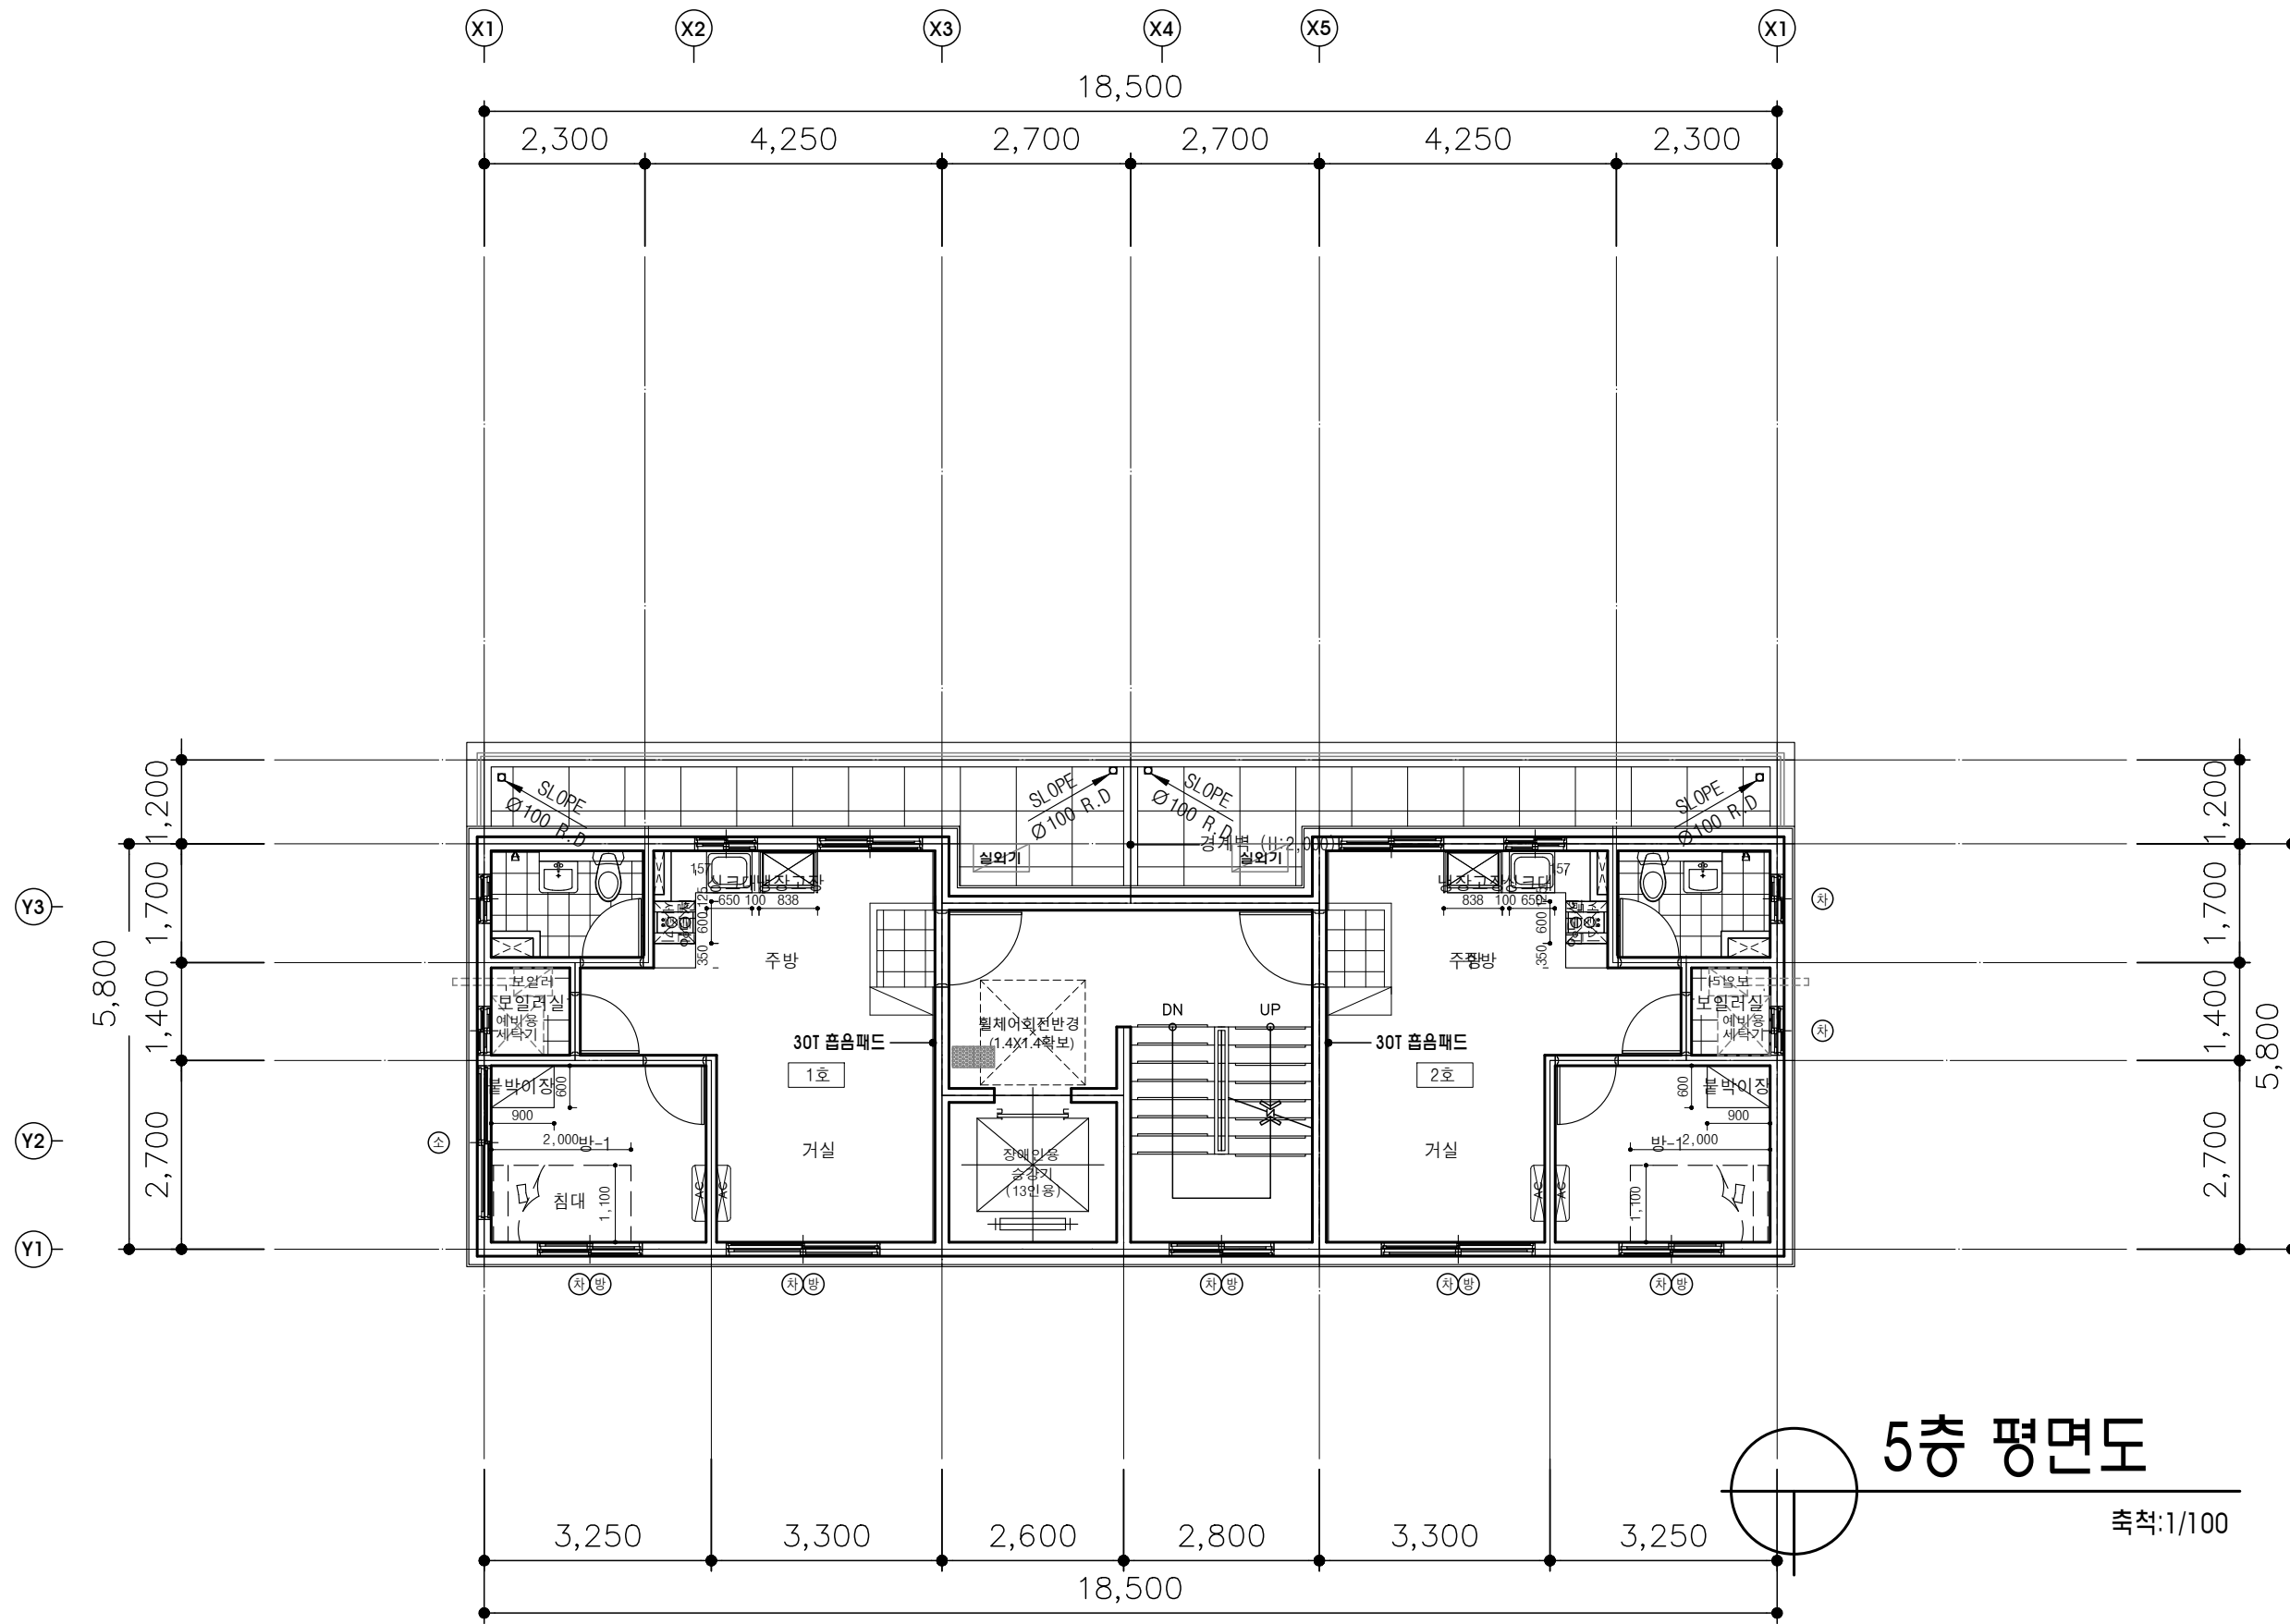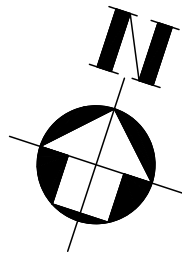


5층 평면도
축척: 1/100

비밀 생활 건축사 사무소 서울특별시 도봉구 마들로684-9 상가동 311호 T. 02 - 725 - 3491 F. 070 - 4337 - 0902	설계명 PROJECT TITLE 미아동 223-4 신축공사	노트 NOTE 다용도실 전열교환기 점검구 설치 (배관 점검 가능 해야 함.) 1. 청년 유형 가전 및 가구 -냉장고, 세탁기, 벽걸이에어컨, 불박이장 또는 이동식 옷장, 책상	설계구분 PROJECT KINDS 계획 설계	담당 DRAWN BY : 담당 DRAWN BY : 최 재 평	축척 SCALE	도면명칭 DRAWING TITLE
			설계번호 PROJECT NO. 20220248	검토 CHECKED BY : PIC APPROVED BY : 최 재 평	날짜 DATE 23년 09월	도면번호 SHEET NO. 16

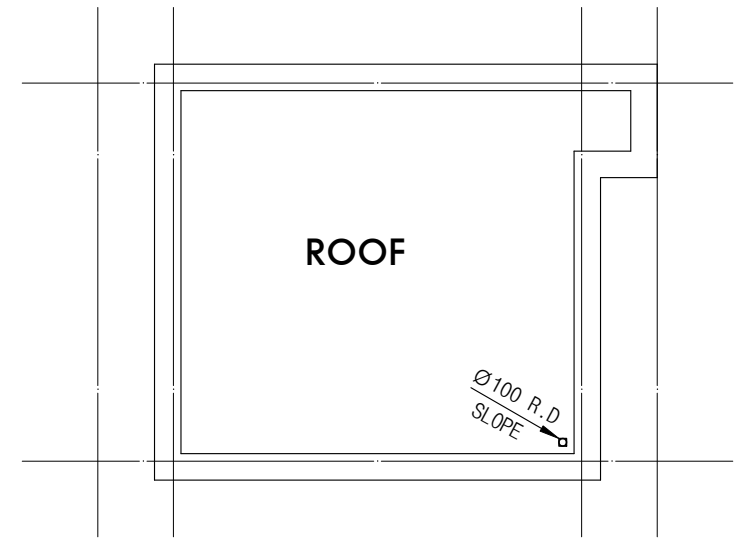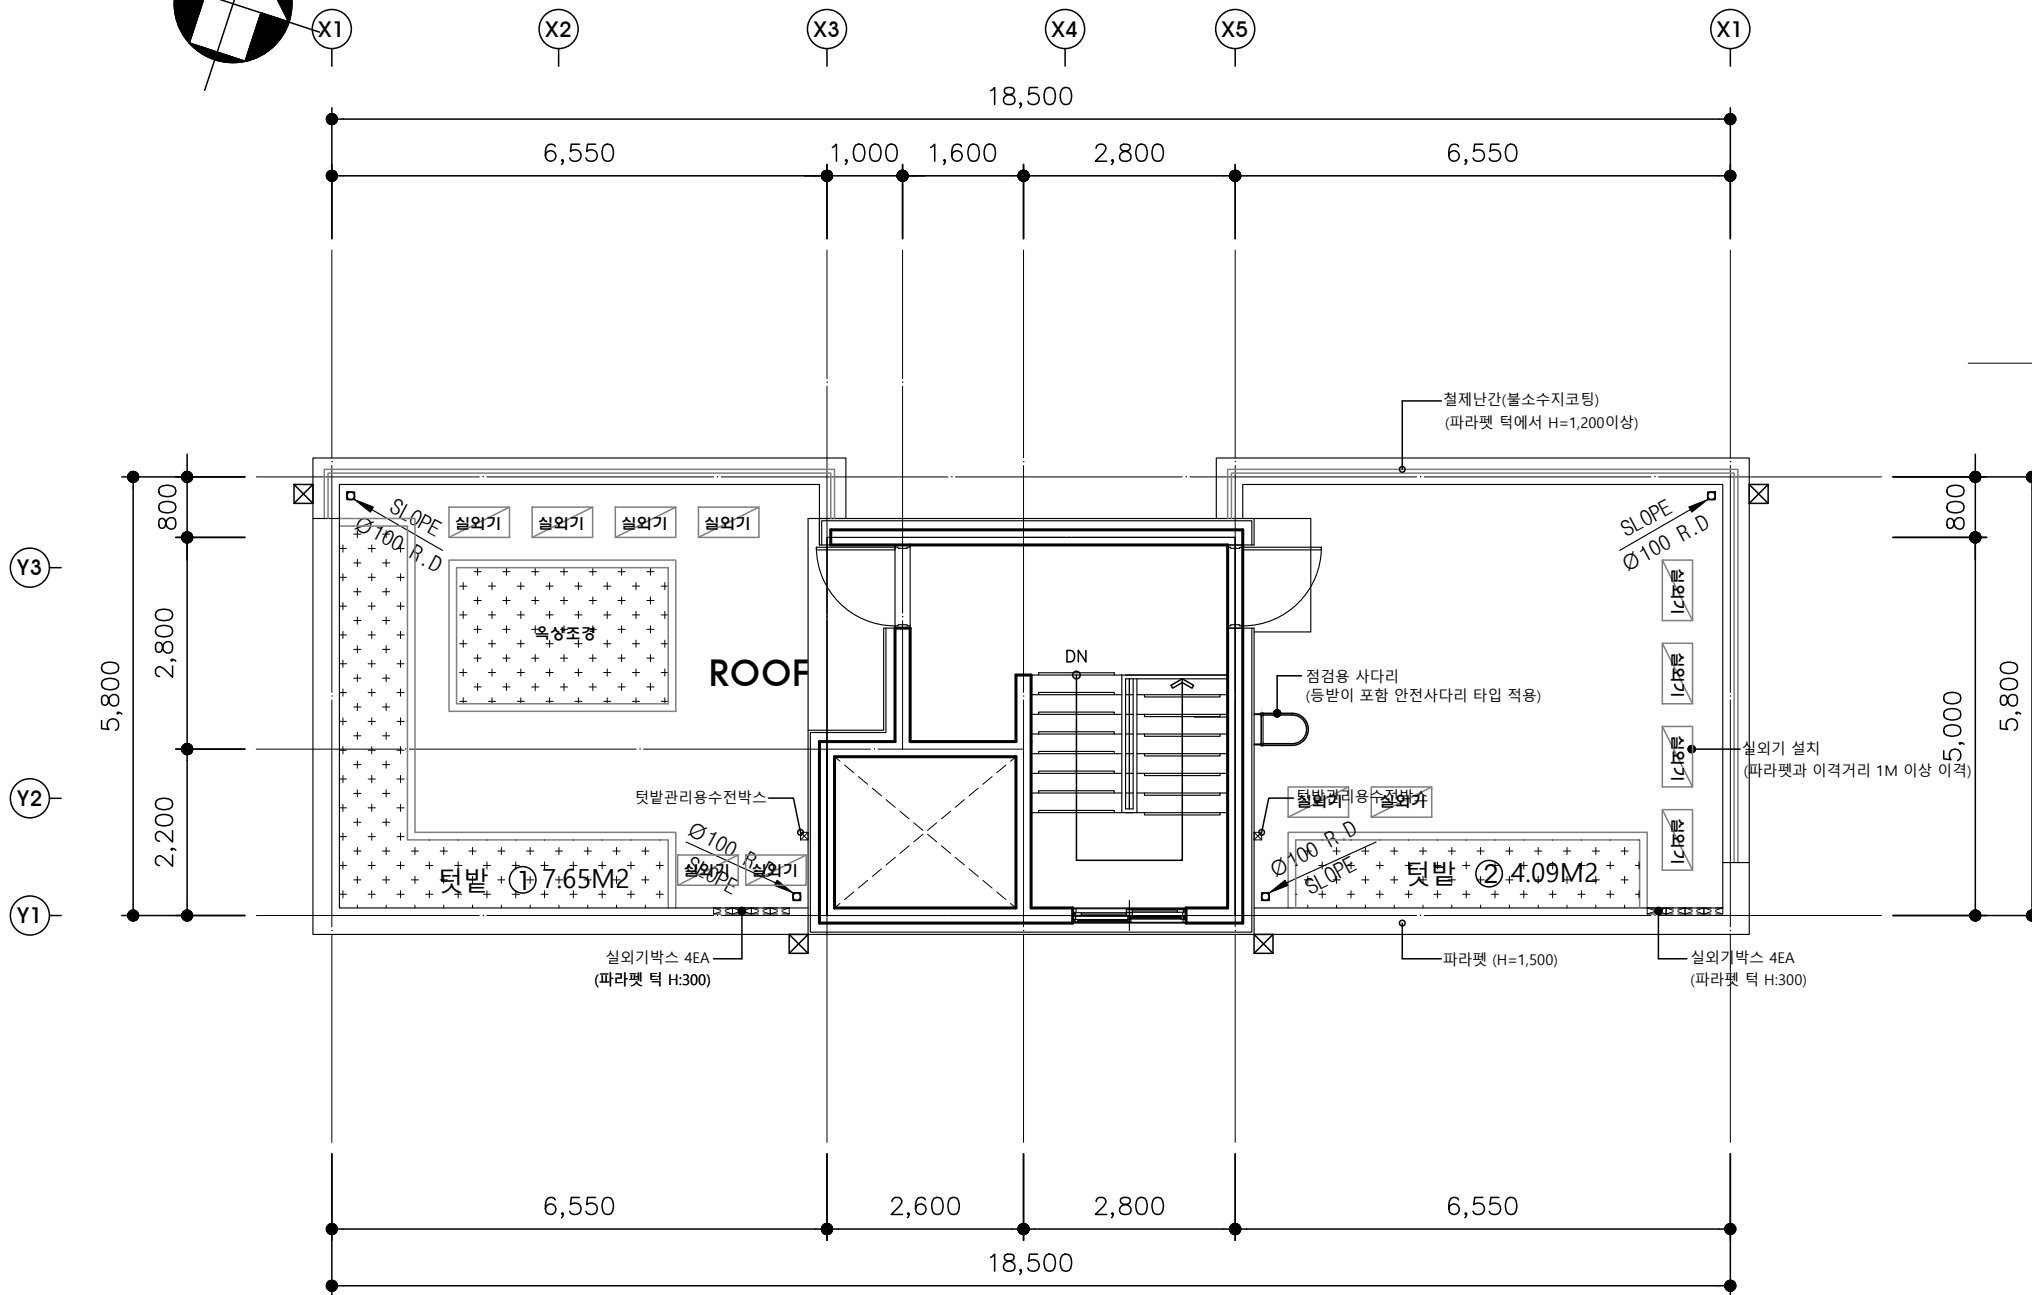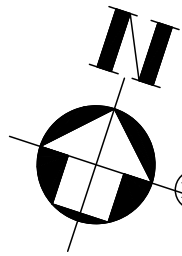

옥탑지붕 평면도

축척:1/100

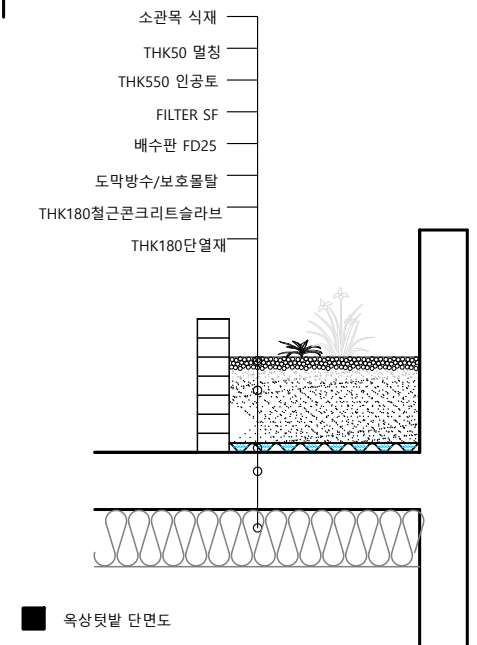


커뮤니티시설 개요

옥상면적	75.98 m ²
터발면적	①+② = 11.74 m ²
터발비율	11.74 m ² (15.45%) / 설계 < 11.397m ² (옥상면적의 15.0%) / 권장
옥상조경	5.04 m ² (30.78%) / 설계 > 4.91 m ² (법정 조경 설치 면적의 30%) / 권장


옥탑 평면도

축척:1/100

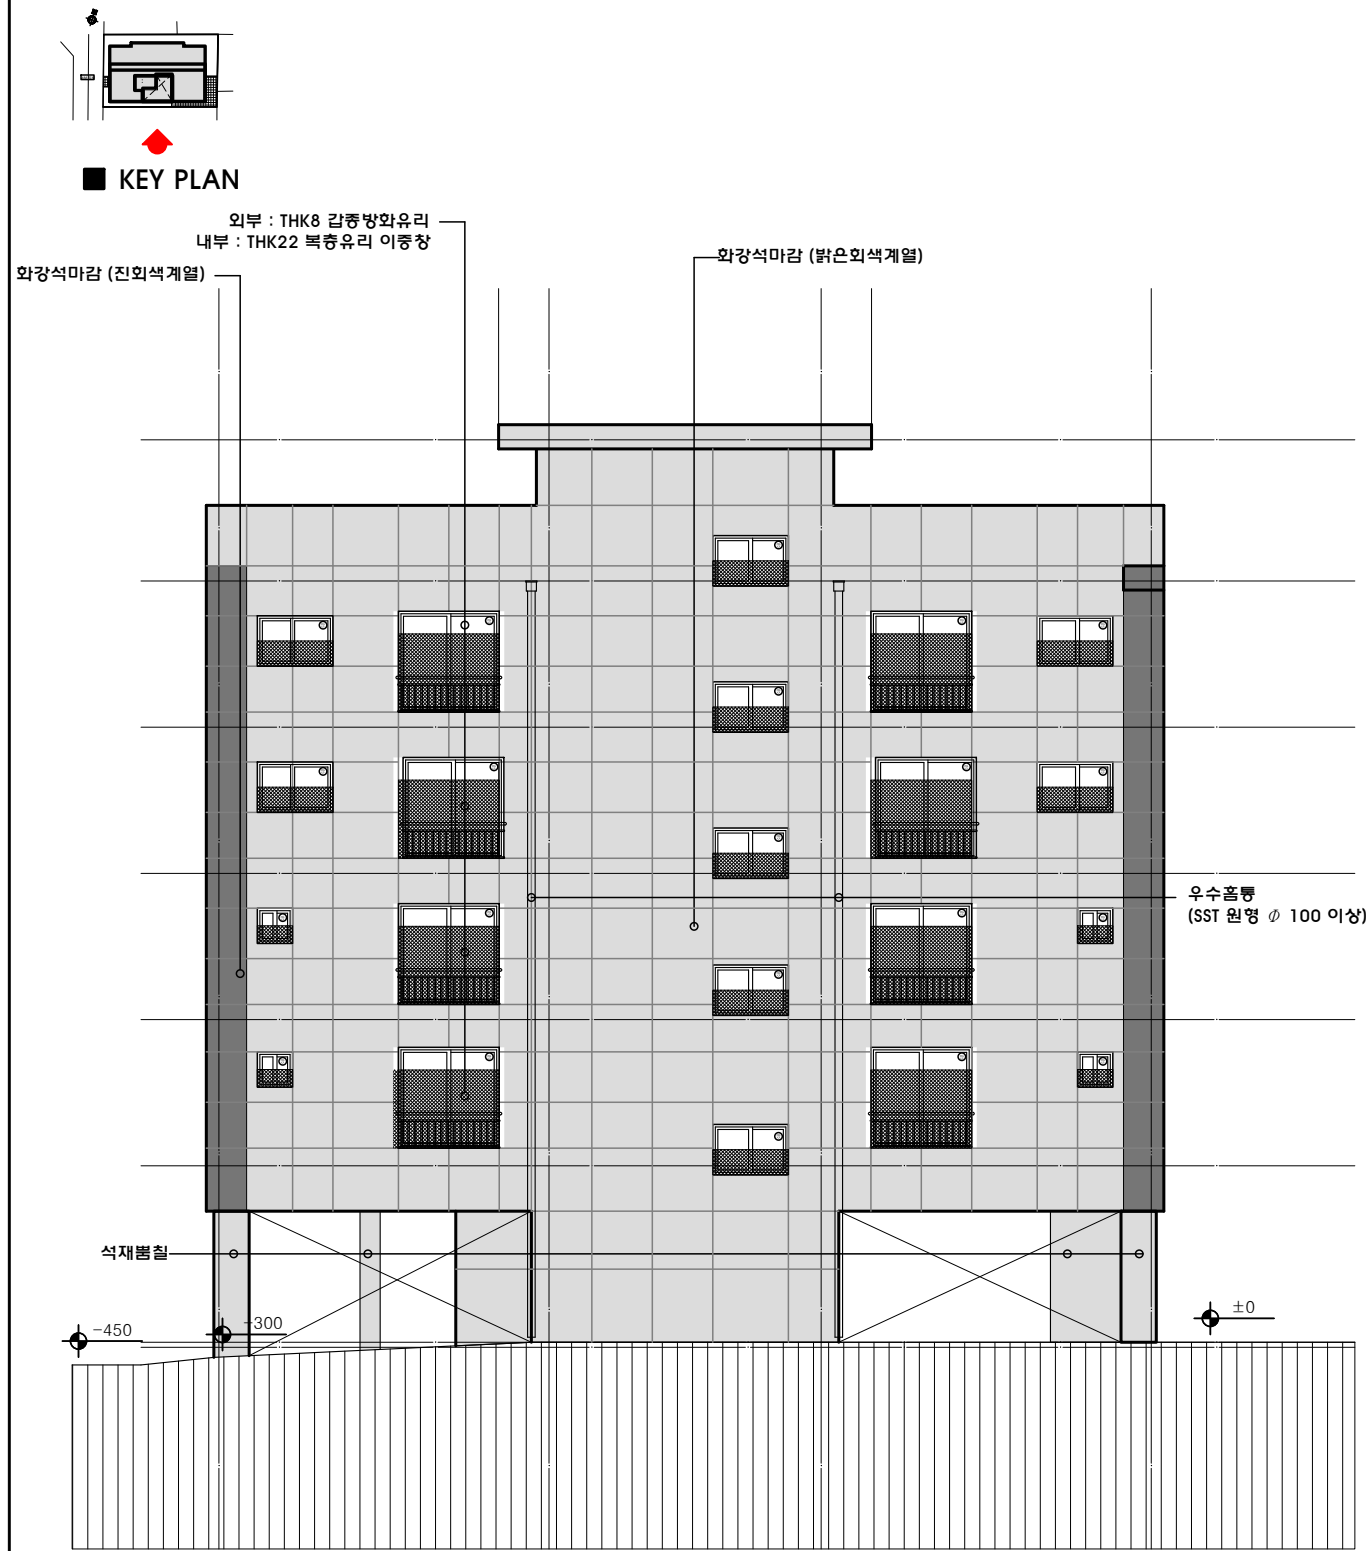


남측면도

축척:1/150

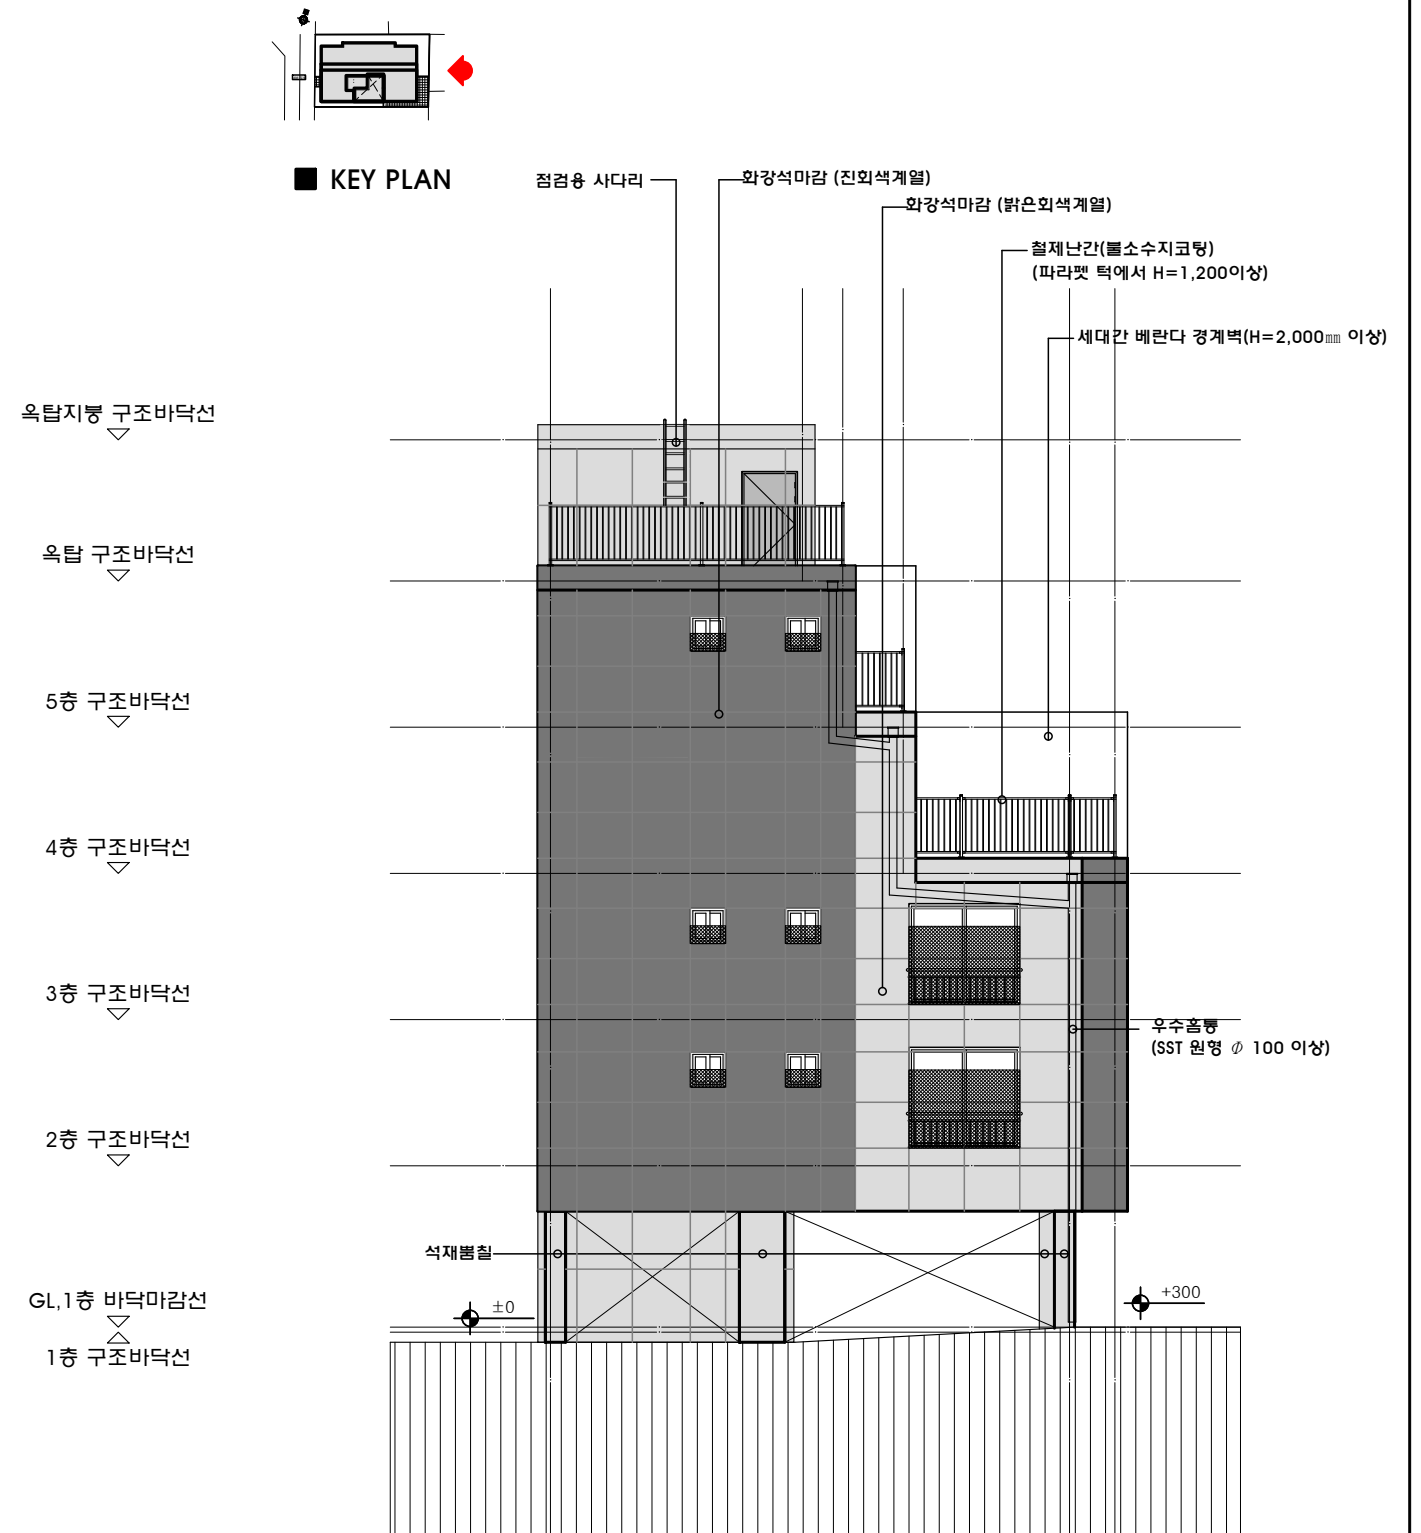


동측면도


축척:1/150

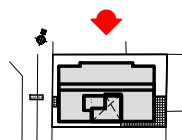


KEY PLAN

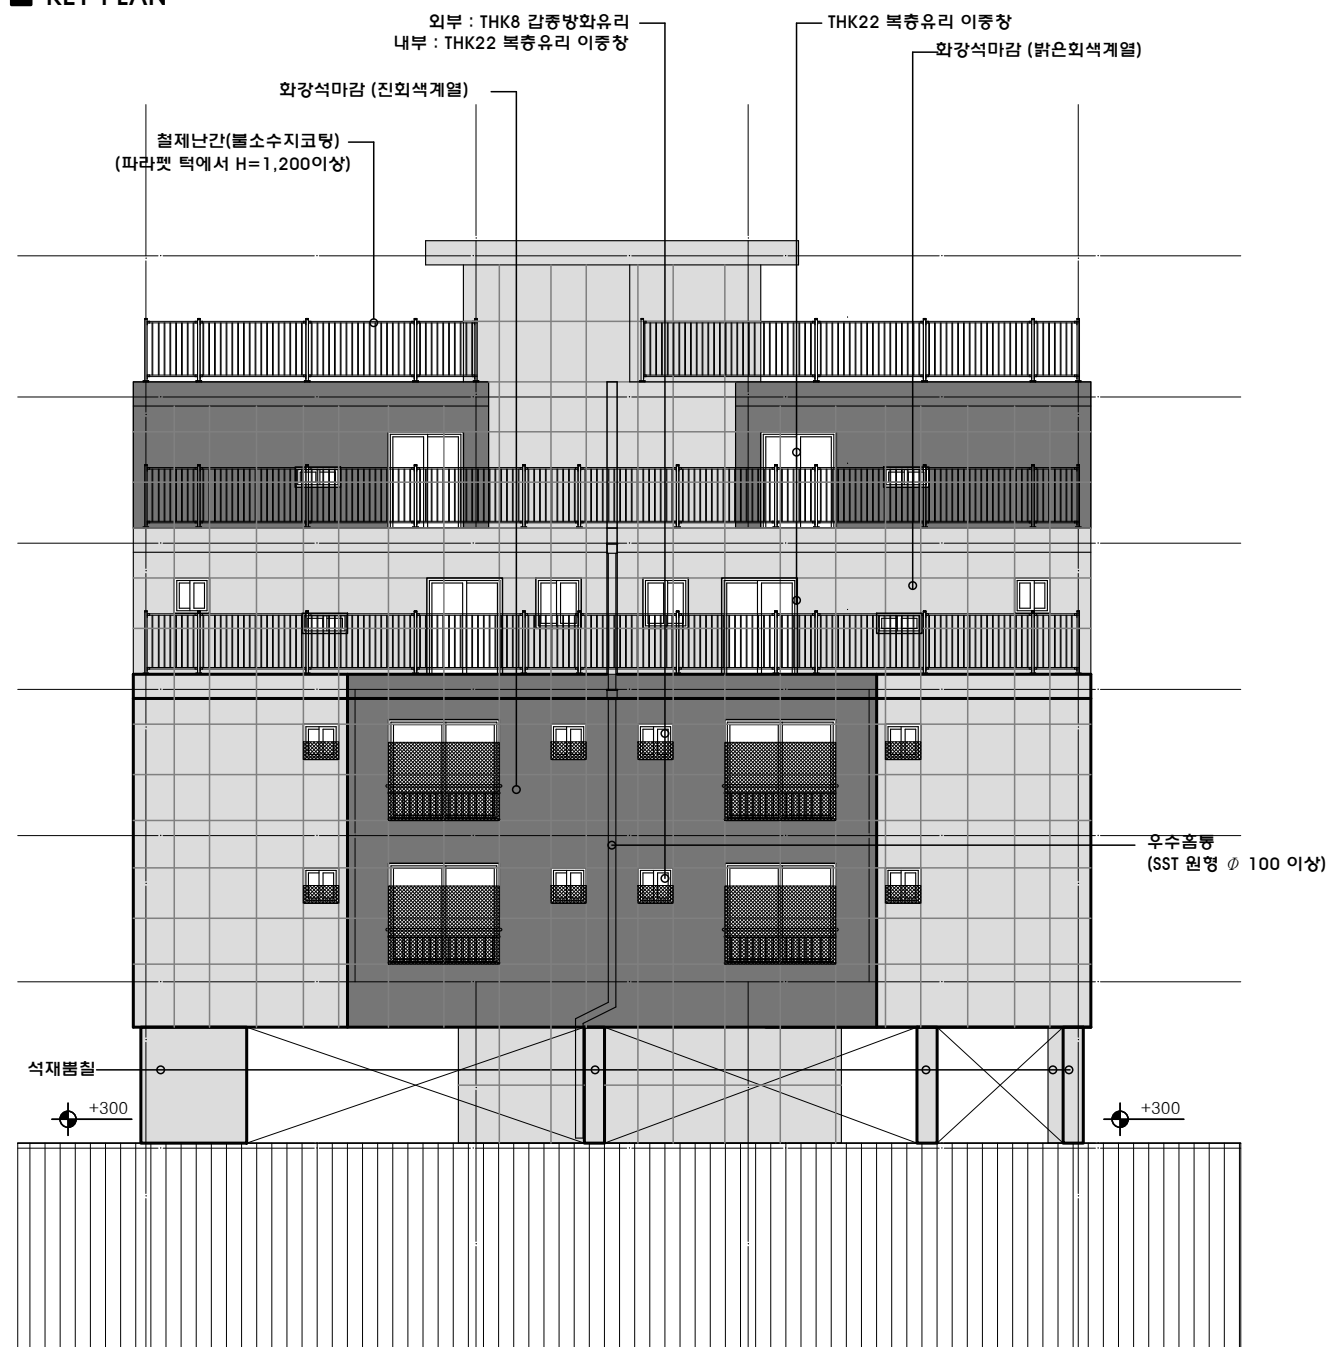

북측면도
축척:1/150

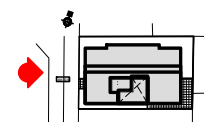

KEY PLAN

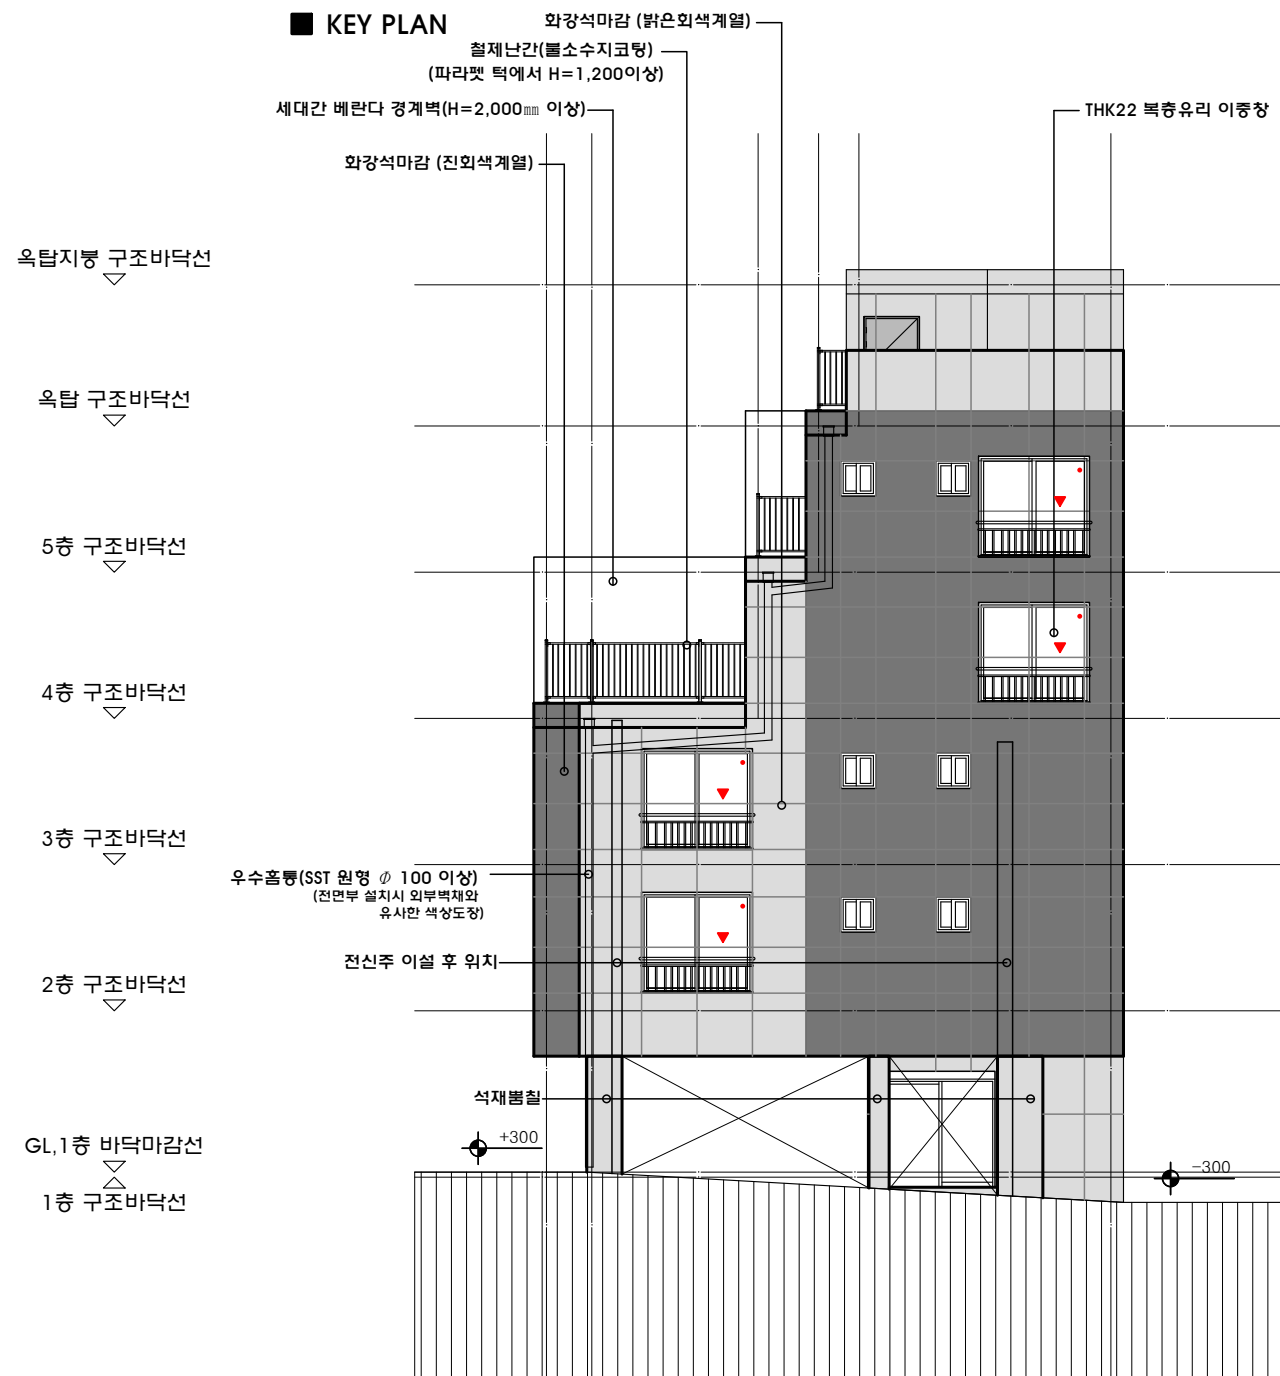

서측면도
축척:1/150