
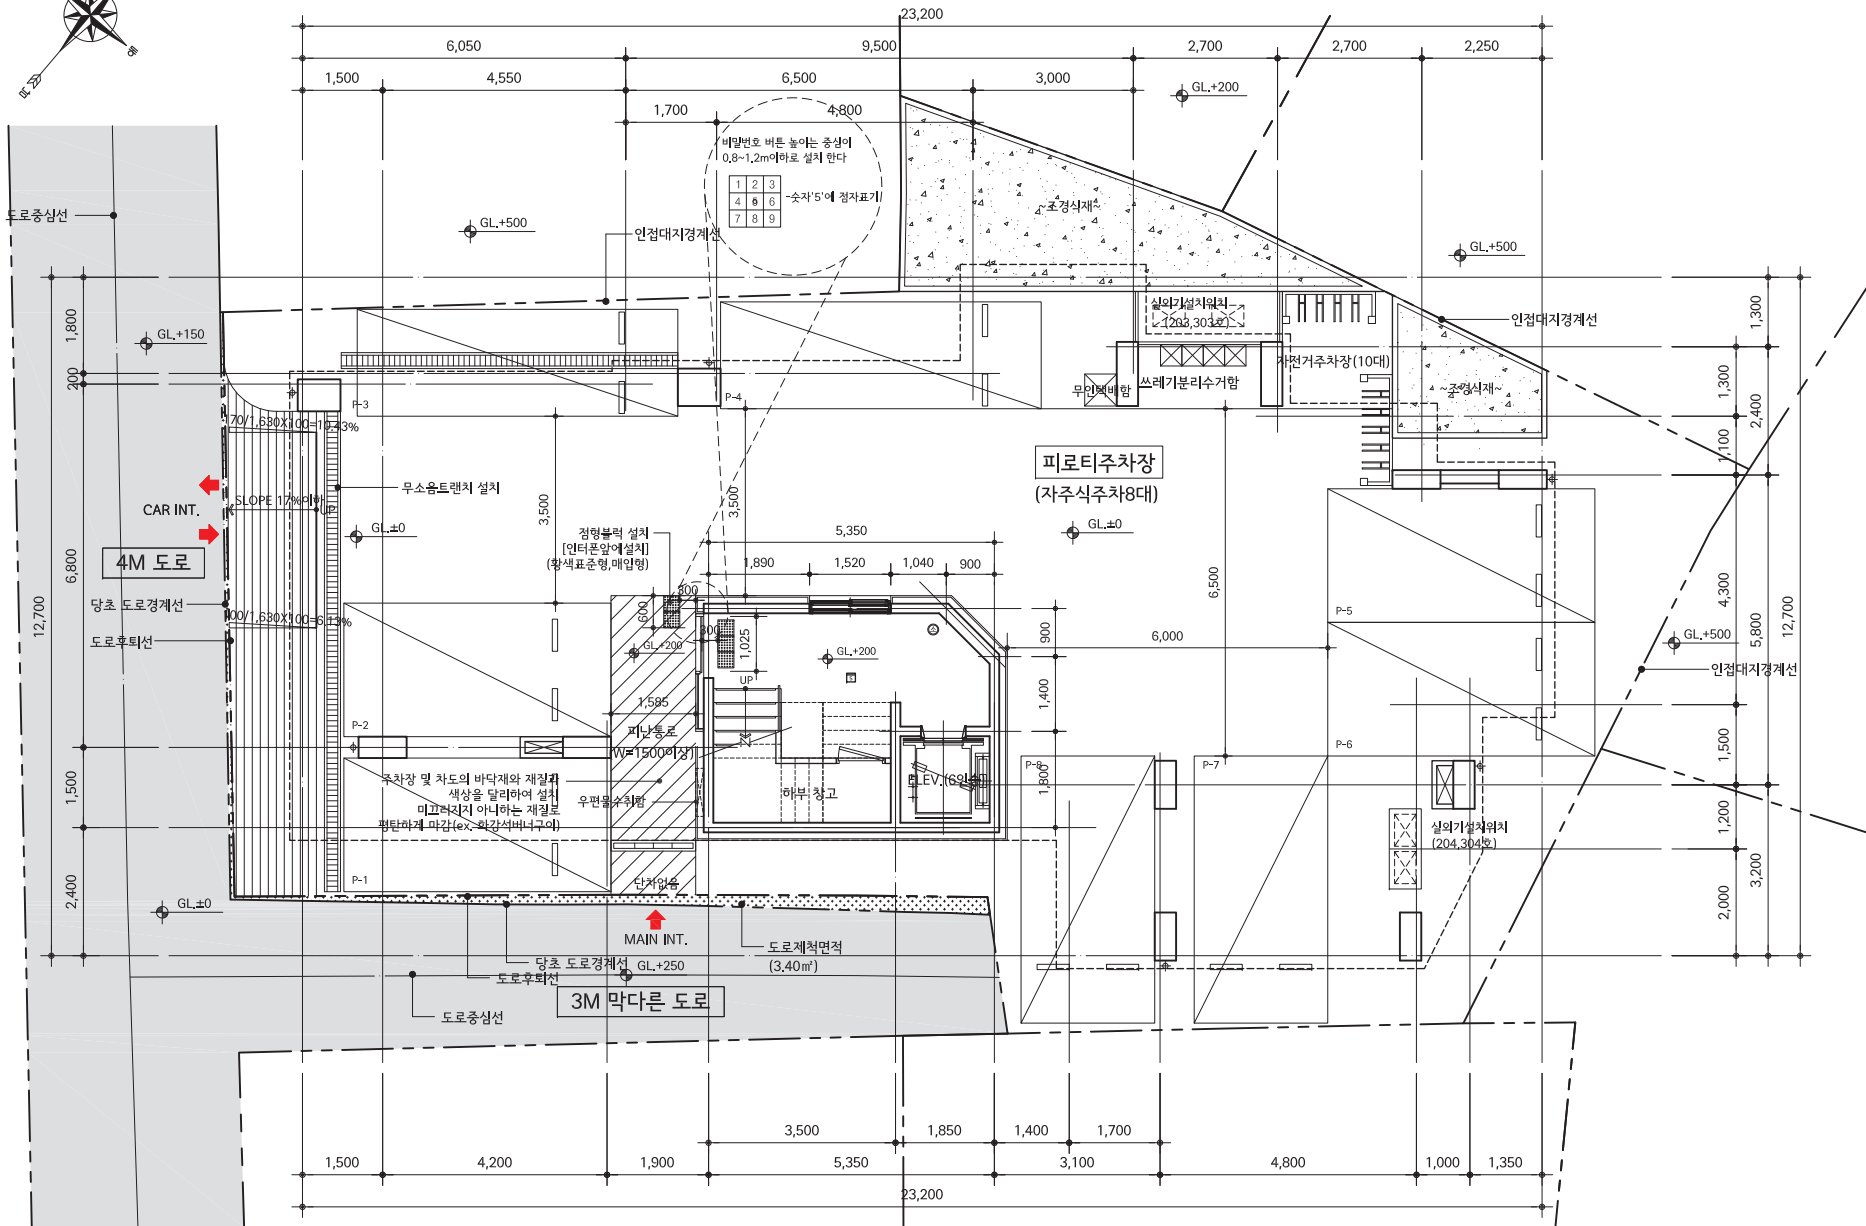


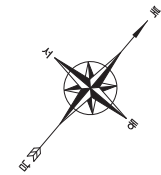

작업명
PROJECT TITLE

강북구 수유동 134-44외1
도시형생활주택(원룸형)
신축공사 (청년주택)

사업번호
PROJECT NO.

변경사항
ISSUES & REVISIONS

△
△
△
△
△

hanndas
Architects & Interiors
영남대학교 건축·환경디자인학과
T.052.464.8775 F.052.889.9102

제 도
DRAWN BY

설 계
DESIGNED BY

검 사
CHECKED BY

승 인
APPROVED BY

건축사 이선영

추가사항
NOTE

■ 출입로 버튼 설치(엔터콘 설치)

비밀번호 버튼은 그 앞선이 비커면으로 부터

중심이 0.8~1.2m 이내에 위치하도록 설치한다.

시각장애인의 구분할수있게 돌출물 부착

출입구 비밀번호 및 카드버튼 설치

1 2 3
4 5 6
7 8 9

엔터콘 설치

엔터콘 설치시 화강블록은 엔터콘 전면

0.3m이하여야 2장, 후면엔터콘 후면에

0.3m이하여야 문턱만큼 설치하여야함.

협동설계
CONSULTANTS

일 자
DATE

도면번호
DRAWING NO.

A - 101



중 적
SCALE

A3 : 1 / 100

도면명
NAME OF DRAWING

지상1층 평면도

지상1층 평면도
SCALE = 1/100

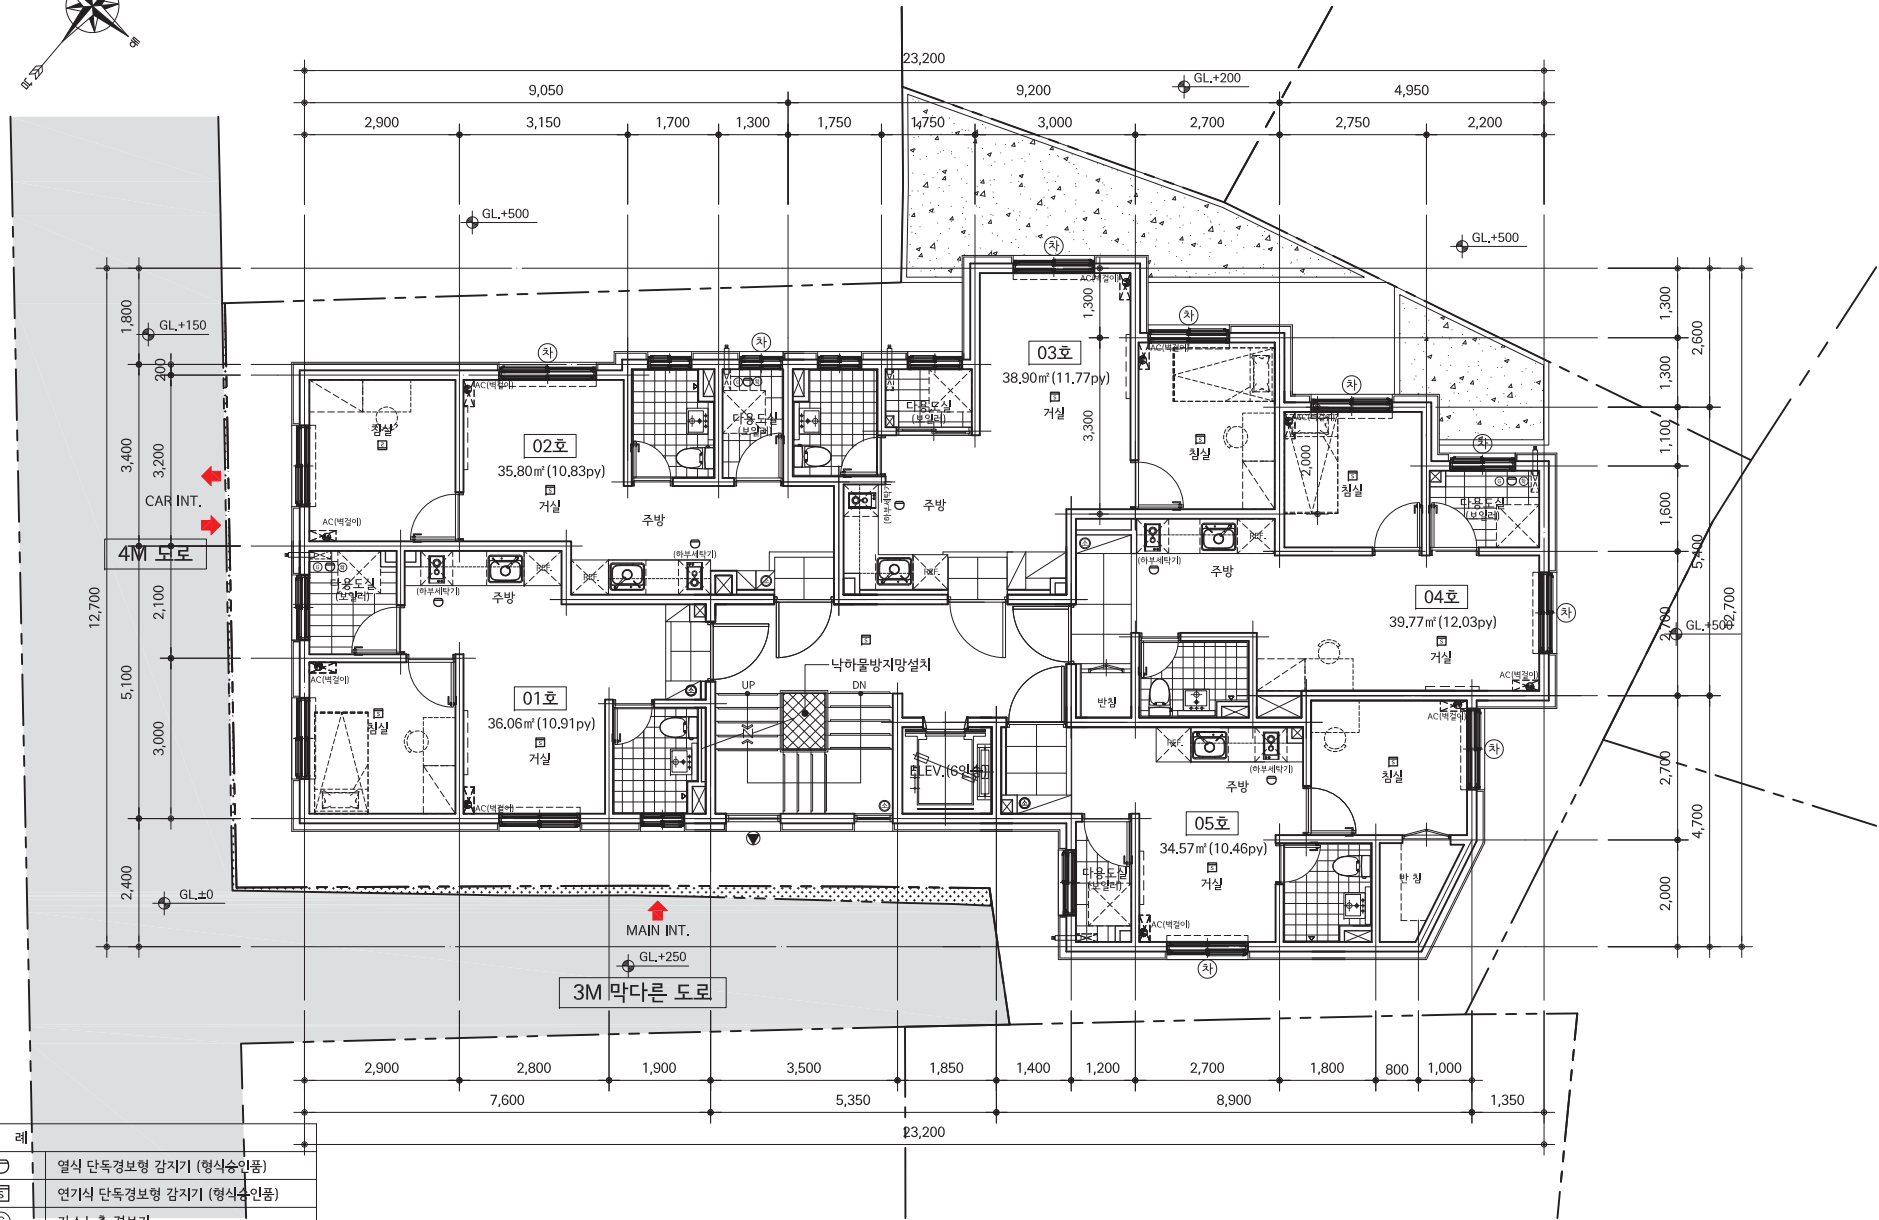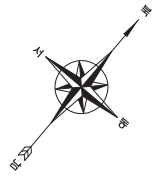



범	례	
㉠	열식 단독경보형 감지기 (형식승인품)	
㉡	연기식 단독경보형 감지기 (형식승인품)	
㉢	가스누출 경보기	
㉣	확산소화기	
㉤	ABC 분말 소화기	
㉥	차연시설	
㉦	소방관 진입창	



지상2~3층 평면도
SCALE = 1/100

작업명 PROJECT TITLE 강북구 수유동 134-44외1 도시형생활주택(원룸형) 신축공사 (청년주택)	
사업번호 PROJECT NO. 	
변경사항 ISSUER & REVISIONS 	
 hanndas Architects & Interiors 영등포구 영등동 1-10-11 4F~2F T.02-464-8775 F.02-881,9102	
제도 DRAWN BY	
설계 DESIGNED BY	
심사 CHECKED BY	
승인 APPROVED BY 건축사 이선영	
추가사항 NOTE	
협동설계 CONSULTANTS	
날짜 DATE	
도면번호 DRAWING NO. A - 102	
축척 SCALE A3 : 1 / 100	
도면명 NAME OF DRAWING 지상2~3층 평면도	

지상5층 평면도
SCALE = 1/100

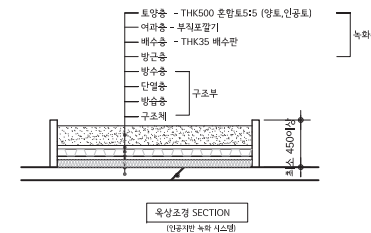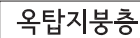

SCALE = 1/100

PROJECT TITLE

강북구 수유동 134-44외1
도시형생활주택(원룸형)
신축공사 (청년주택)

사업번호
PROJECT NO.

ISSUER & REVISIONS



제 도
DRAWN BY

DESIGNED BY

심사
CHECKED BY

승인
APPROVED

건축사 이선영

주기사항
NOTE

협동설계
CONSULTANTS

DATE

도면번호
DRAWING NO.


A - 105

측척
SCALE

A3 : 1 / 100

NAME OF DRAWING

지붕층 및
옥탑지붕층 평면도

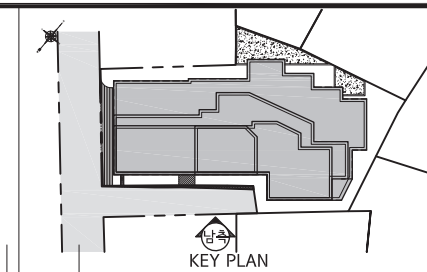

사업명
 PROJECT TITLE
 강북구 수유동 134-44외1
 도시형생활주택(원룸형)
 신축공사 (청년주택)

사업번호
 PROJECT NO.

변경사항
 ISSUER & REVISIONS

△	
△	
△	
△	
△	



제 도
 DRAWN BY

설계
 DESIGNED BY

검토
 CHECKED BY

승인
 APPROVED BY
 건축사 이선영

추가사항
 NOTE

협동설계
 CONSULTANTS


일자
 DATE

도면번호
 DRAWING NO.
 A - 106

축척
 SCALE
 A3 : 1 / 100

도면명
 NAME OF DRAWING

남 측 면 도

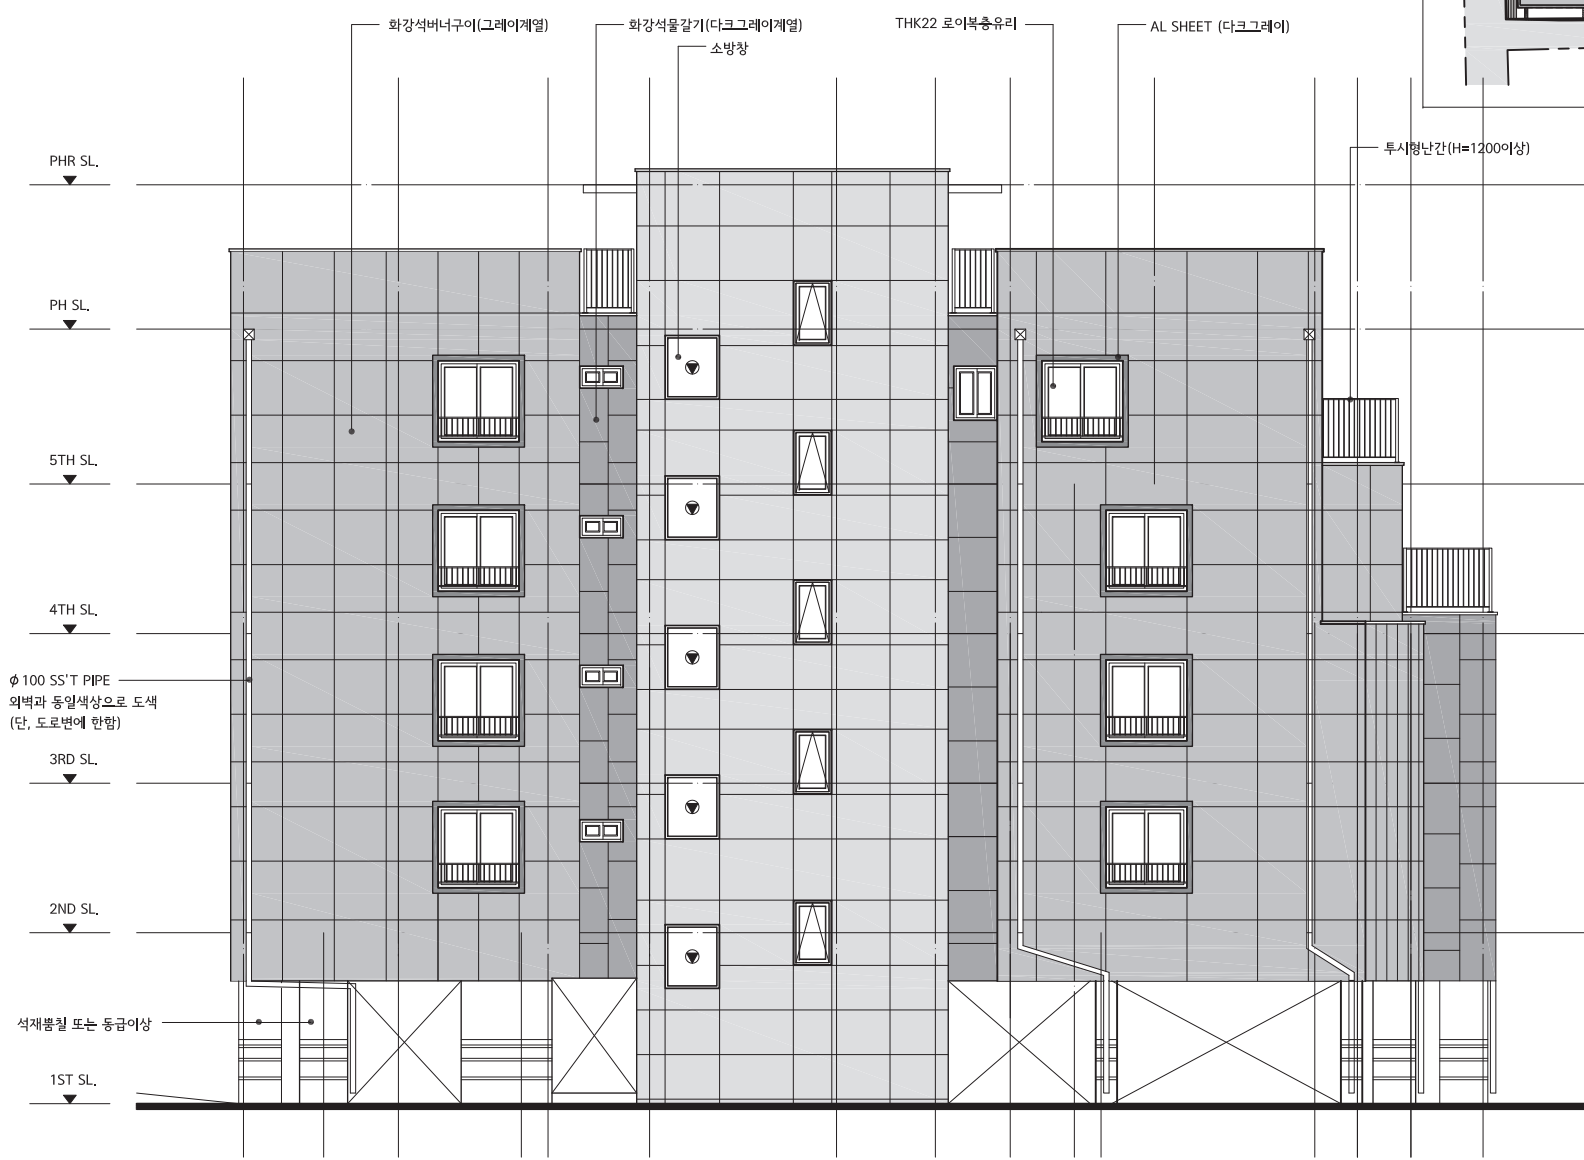

남 측 면 도
 SCALE = 1/100

시안명칭
PROJECT TITLE
강북구 수유동 134-44외1
도시형생활주택(원룸형)
신축공사 (청년주택)

사안번호
PROJECT NO.

변경사항
ISSUER & REVISIONS



제 도
DRAWN BY

설 계
DESIGNED BY

검 사
CHECKED BY

승 인
APPROVED BY
건축사 이선영

추가사항
NOTE

협동설계
CONSULTANTS

일 자
DATE

도면번호
DRAWING NO.


A - 107

축 척
SCALE

A3 : 1 / 100

도면명
NAME OF DRAWING

북 측 면 도

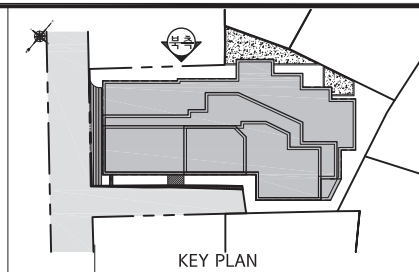

화강석물갈기(다크그레이계열)

화강석버너구이(그레이계열)

THK22 로어복층유리

투시형난간(H=1200이상)

PHR SL.

PH SL.

5TH SL.

4TH SL.

3RD SL.

2ND SL.


1ST SL.

석재폼칠 또는 동급이상




북 측 면 도

SCALE = 1/100

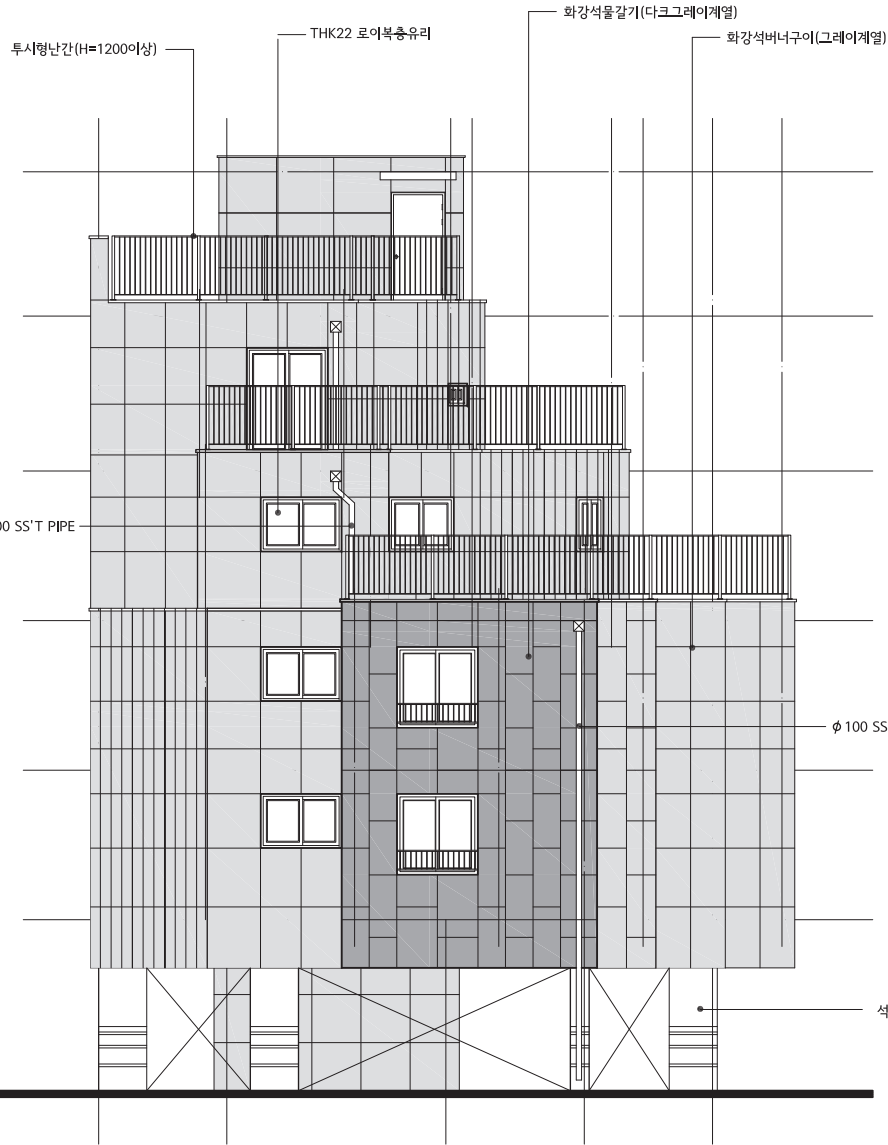


동 측 면 도

SCALE = 1/100

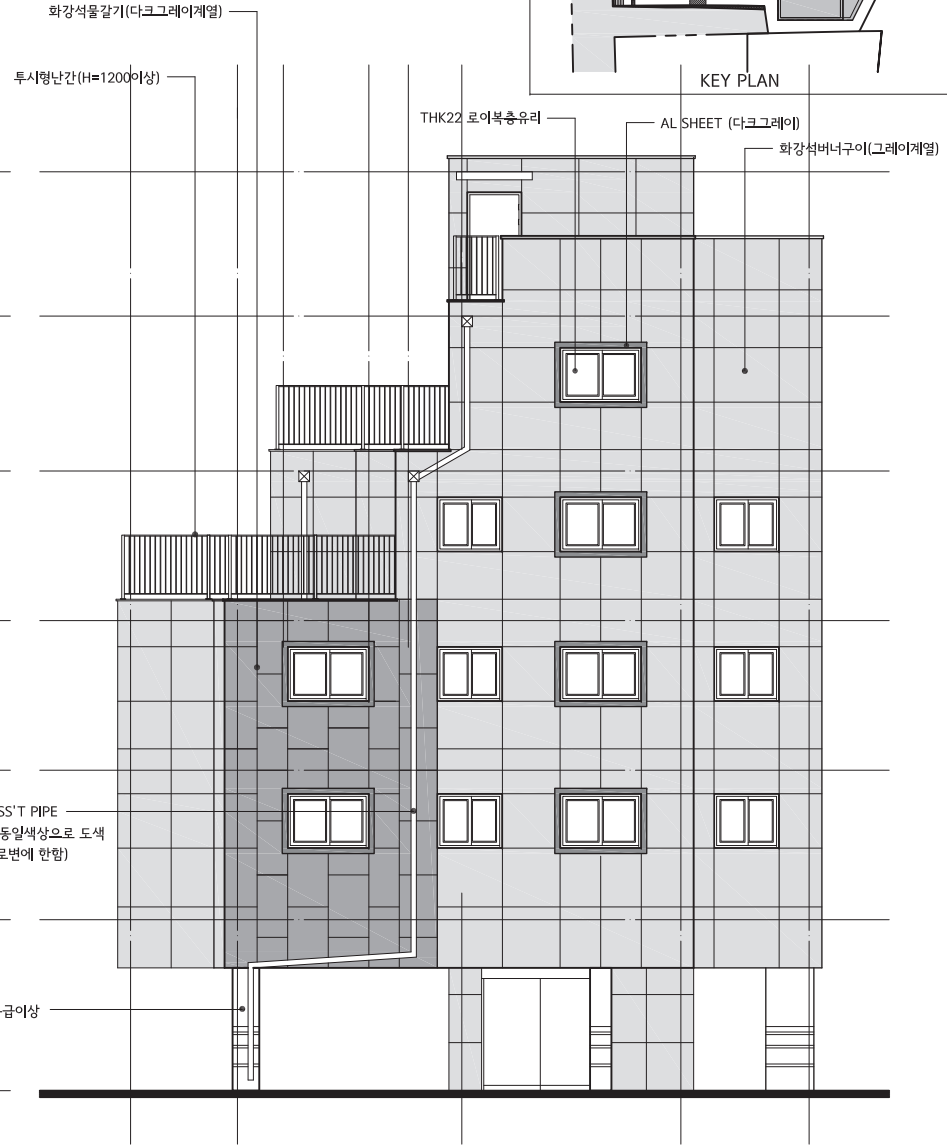

서 측 면 도

SCALE = 1/100

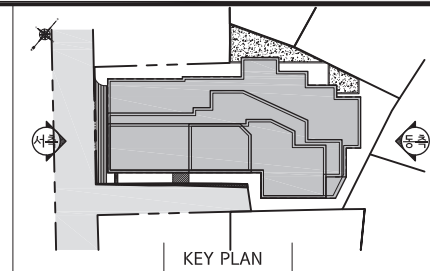

사업명
PROJECT TITLE
강북구 수유동 134-44외1
도시형생활주택(원룸형)
신축공사 (청년주택)

사업번호
PROJECT NO.

발주처
ISSUER & REVISIONS

△	
△	
△	
△	
△	

hanndas
Architects & Interiors
영남대학교 건축·환경디자인학과
T.052.464.8775 F.052.881.9102

제 도
DRAWN BY

검 제
DESIGNED BY

심 사
CHECKED BY

승 인
APPROVED BY

건축사 이선영
추가사항
NOTE

협동설계
CONSULTANTS

일 자
DATE

도면번호
DRAWING NO.

A - 108

중 적
SCALE

A3 : 1 / 100

도면명
NAME OF DRAWING

동측면도, 서측면도