

PROJECT TITLE
공 사 명
강북구 수유동
560-2호
다세대주택
신 축 공 사

NOTE
1층 바닥높이 : GL ±0.00
2~5층 반자높이 : 2200
슬래브 : THK 210
2층슬래브 : THK 150
내벽 : THK 150
외벽,세대간벽 : THK 200
콘크리트 fck = 27 MPa


- ELEV. 내측벽 : THK20 방진패드
- 코아 내측벽 : THK60 단열재

△					
△					
△					
△					
△					
NO	DATE	REVISION	DESCRIPTION	DRAWN	DATE


건축사 사무소
하늘건축
Architects & Engineers
TEL : 02) 928 ~ 4484
FAX : 02) 928 ~ 4487

APPROVED 인	
ARCHITECT 설	
CHKD 1 승	
CHKD 2 승	
DRAWN 당	

DATE 작성일	2024. 10.
SCALE 축척	A3 : 1/100
TITLE 도면명	지상1층 평면도
DRWG NO. 도면번호	A - 101
B.C.C NO. 분류번호	SHEET NO. 시트번호
JOB NO. 작업번호	REV NO.

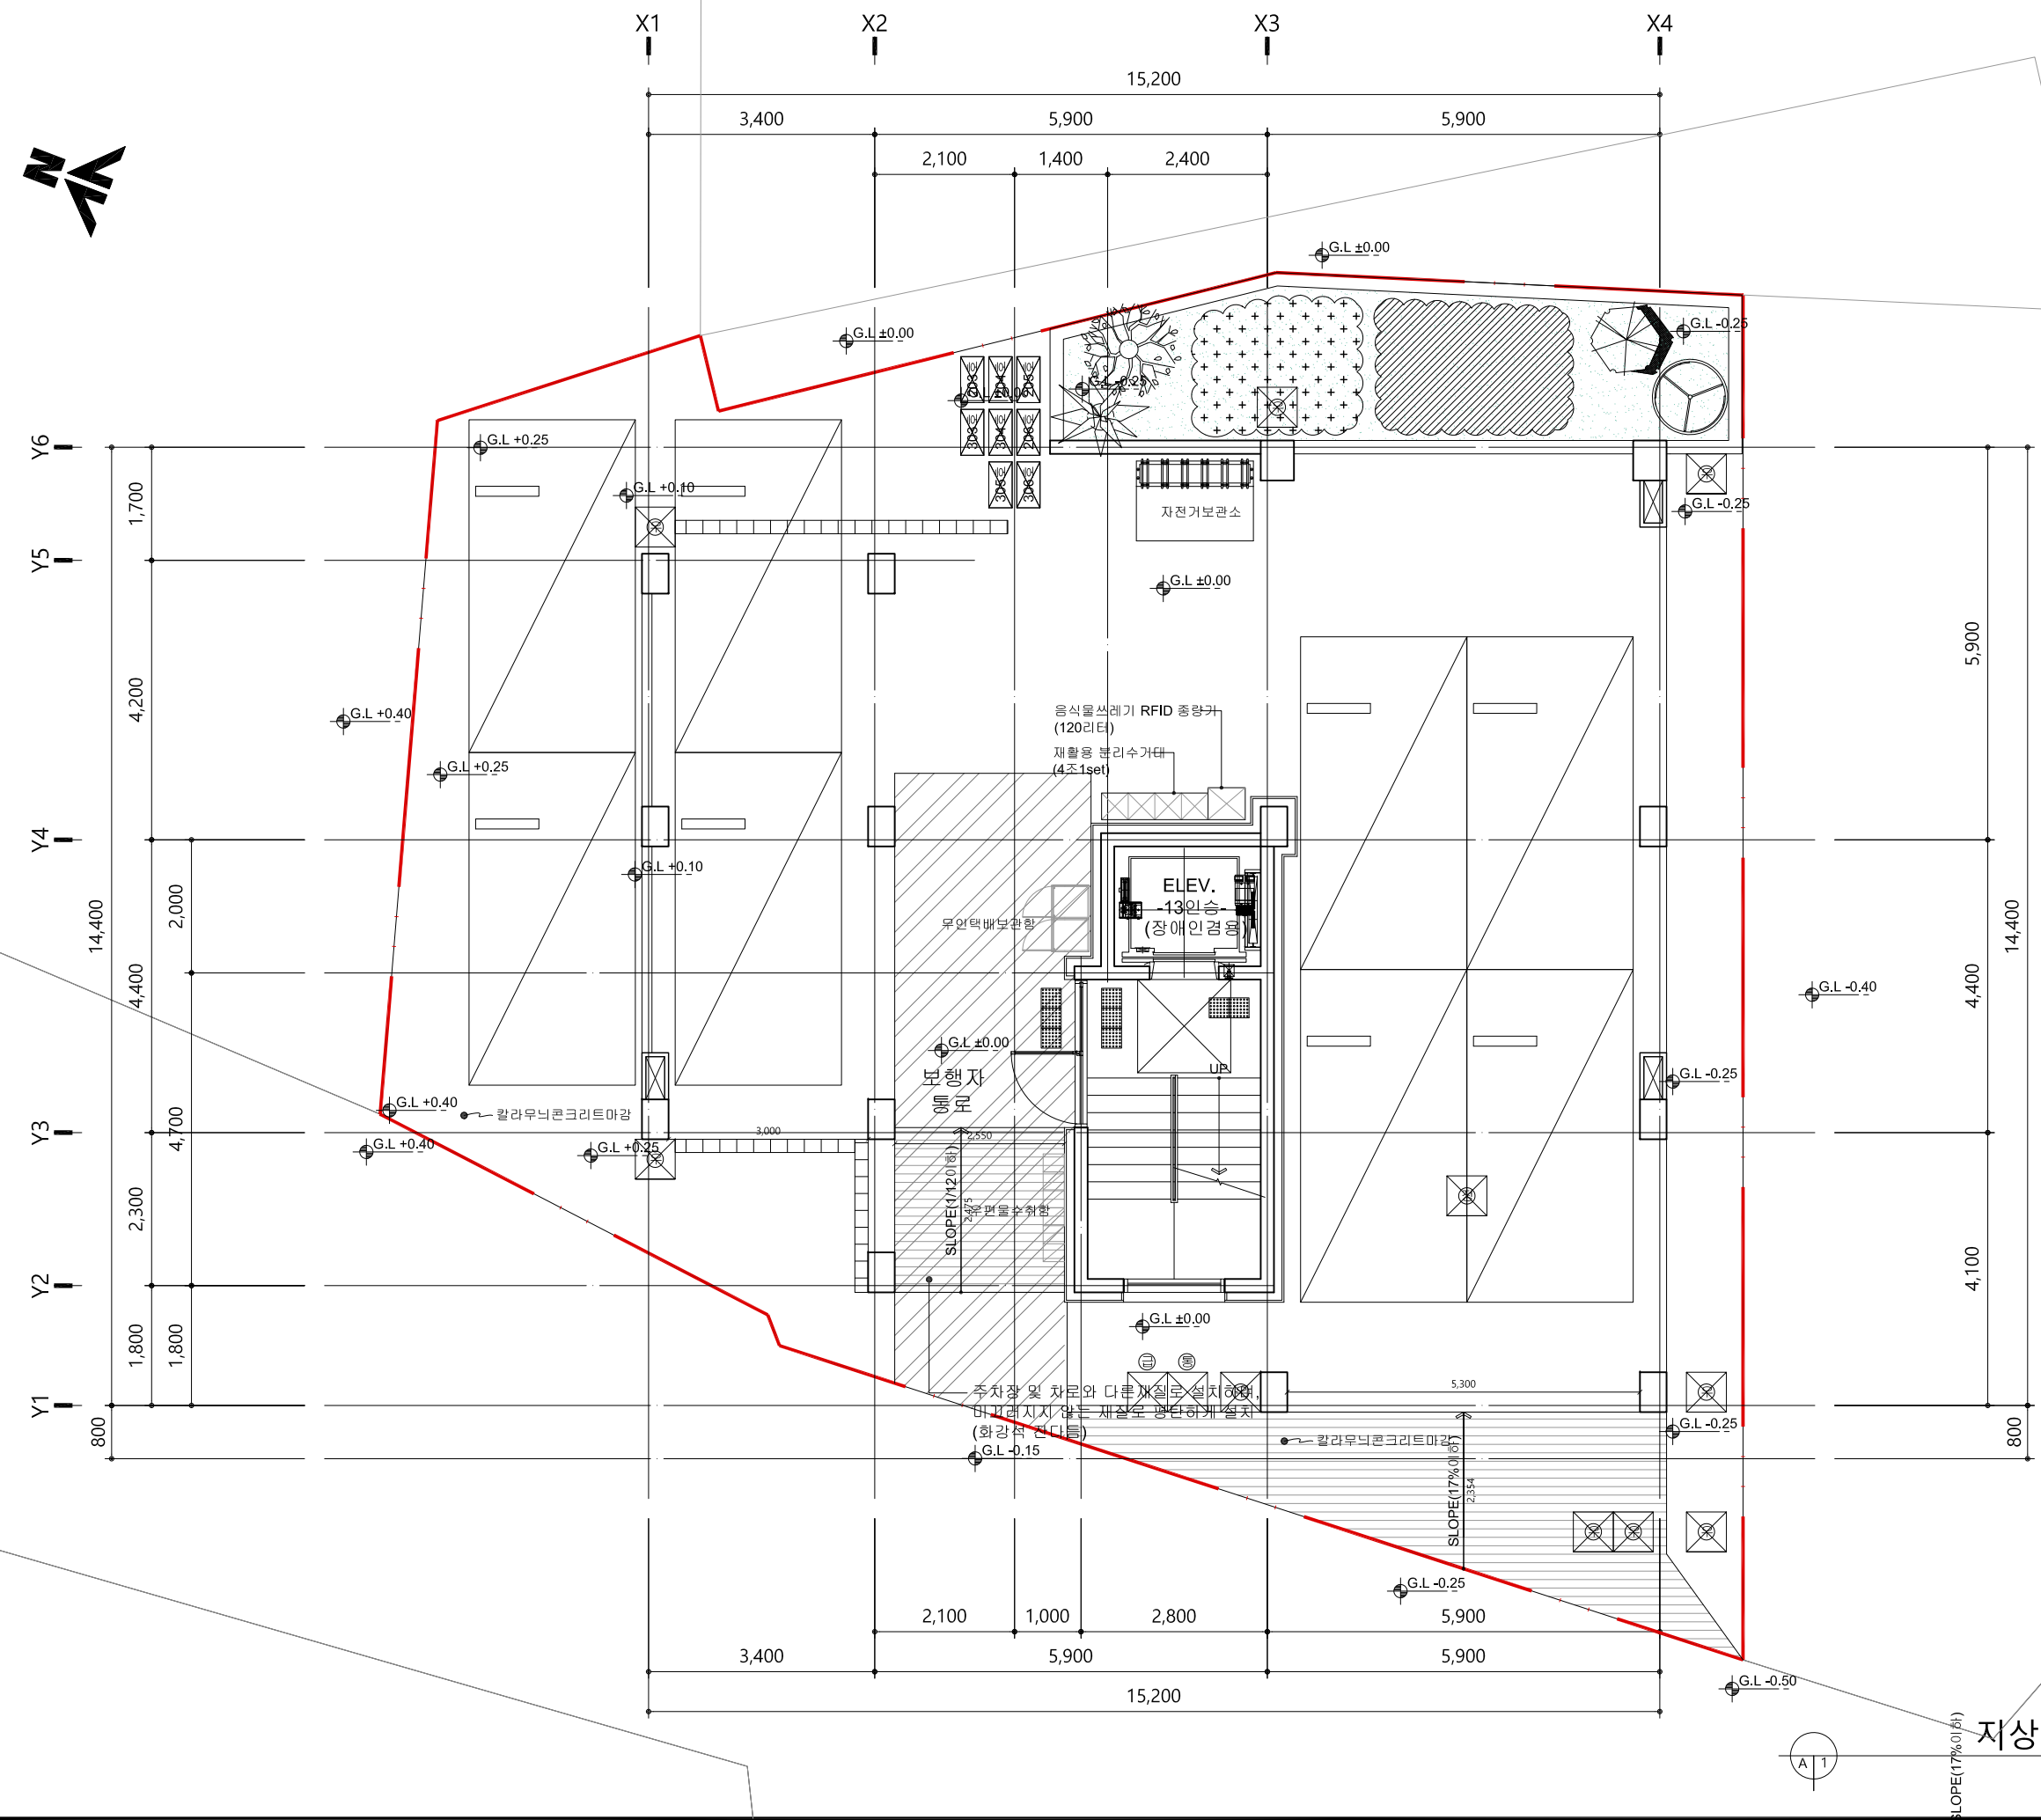

지상1층 평면도
SCALE A3 : 1/100

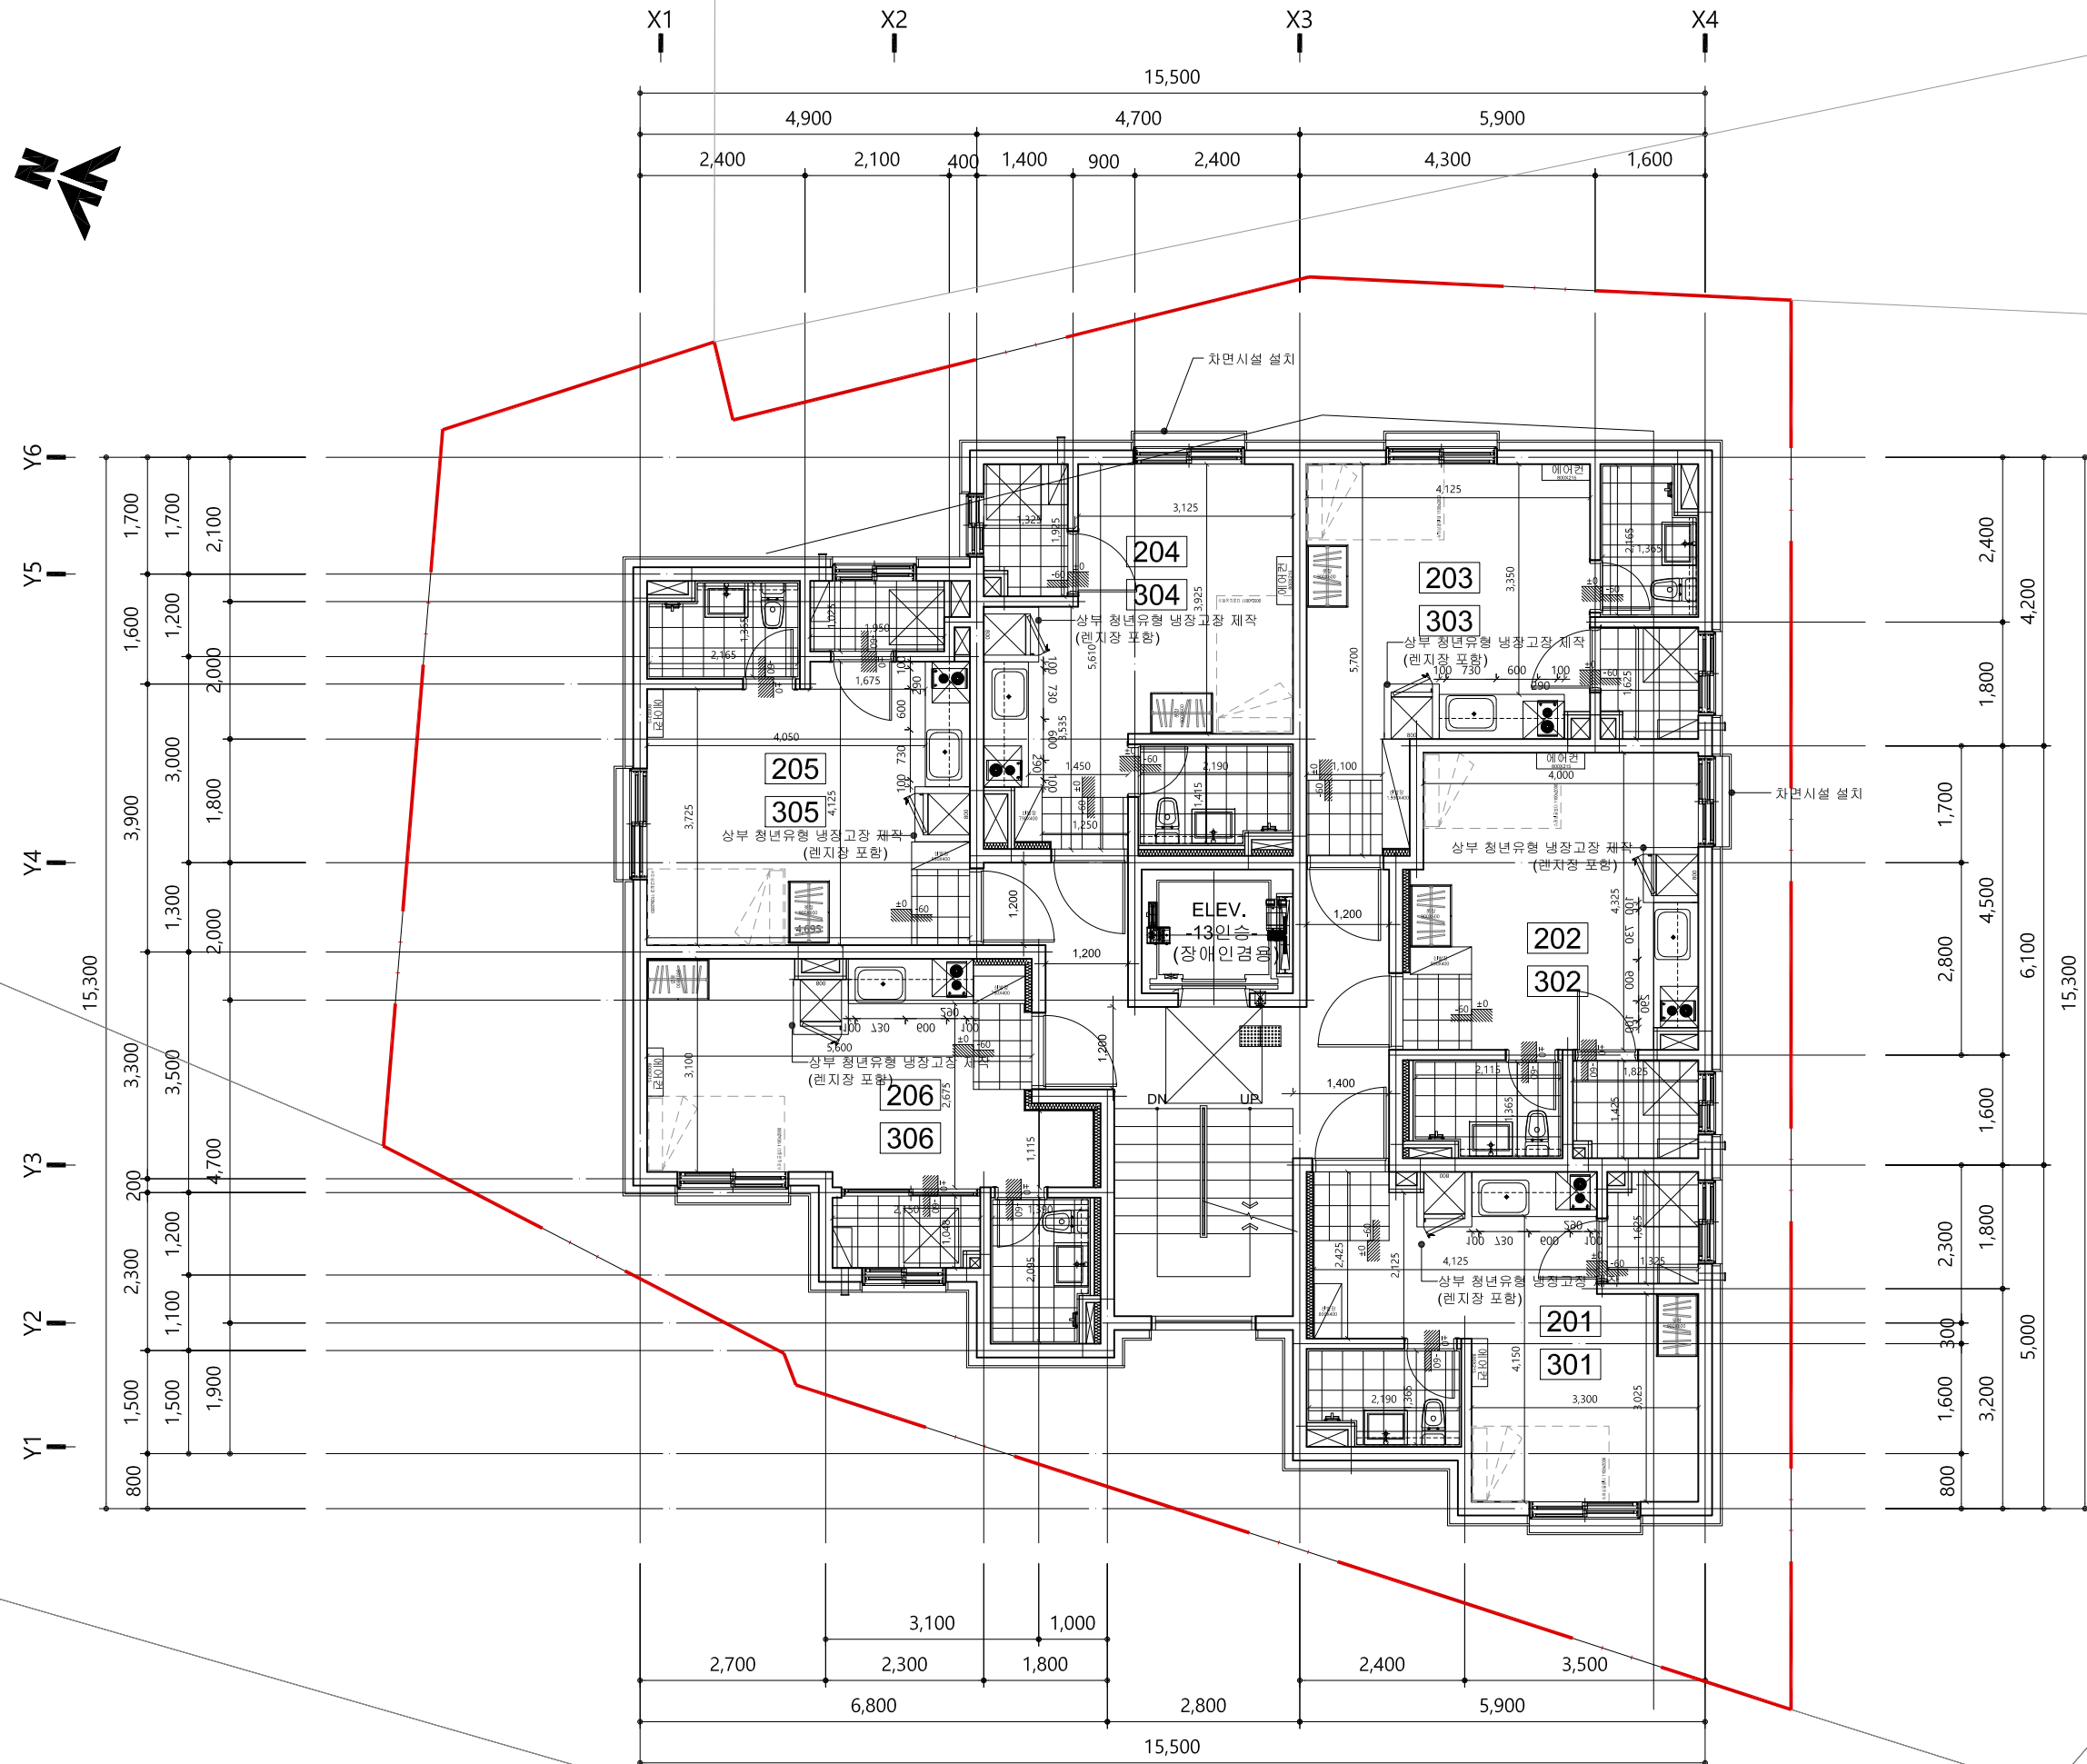

B.C.C.NO. 분류번호	SHEET NO. 일련번호
JOB NO. 작업번호	REV NO. △

NO. 번호	REV NO. 
-----------	--

PROJECT TITLE
공 사 명
강북구 수유동
560-2호
다세대주택
신 축 공 사

NOTE
1층 바닥높이 : GL ±0.00
2~5층 반자높이 : 2200
슬래브 : THK 210
2층슬래브 : THK 150
내벽 : THK 150
외벽,세대간벽 : THK 200
콘크리트 fck = 27 MPa

- ELEV. 내측벽 : THK20 방진패드
- 코아 내측벽 : THK60 단열재

△					
△					
△					
△					
△					
NO	DATE	REVISION	DESCRIPTION	DRAWN	DATE

건축사 사무소
하늘건축
Architects & Engineers
TEL : 02) 928 ~ 4484
FAX : 02) 928 ~ 4487

APPROVED
인
ARCHITECT
설 계
CHKD 1
승 인
CHKD 2
승 인
DRAWN
담 당
DATE
작성일
2024. 10.


SCALE
축척
A3 : 1/100

TITLE
도면명
지상 4층 평면도

DRWG. NO.
도면번호
A - 103

B.C.C. NO.
분류번호
SHEET NO.
시트번호

JOB NO.
작업번호
REV NO.
REV. NO.

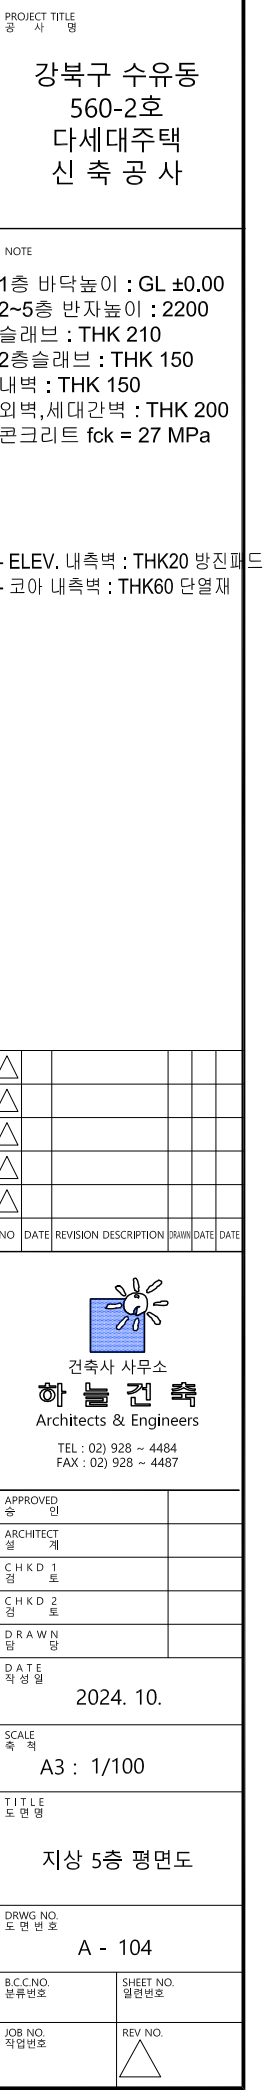

지상 5층 평면도

SCALE A3 : 1/100

PROJECT TITLE
공사명

강북구 수유동
560-2호
다세대주택
신축공사

NOTE

1층 바닥높이 : GL ±0.00
2~5층 반자높이 : 2200
슬래브 : THK 210
2층슬래브 : THK 150
내벽 : THK 150
외벽, 세대간벽 : THK 200
콘크리트 fck = 27 MPa

- ELEV. 내측벽 : THK20 방진패드
- 코아 내측벽 : THK60 단열재

△					
△					
△					
△					
△					
NO	DATE	REVISION	DESCRIPTION	DRAWN	DATE



건축사 사무소
하늘건축
Architects & Engineers
TEL : 02) 928 ~ 4484
FAX : 02) 928 ~ 4487

APPROVED 인	
ARCHITECT 설계	
CHKD 1 승인	
CHKD 2 승인	
DRAWN 담당	



DATE
작성일 2024. 10.

SCALE
축척 A3 : 1/100

TITLE
도면명 옥탑층, 옥탑지붕 평면도

DRWG. NO.
도면번호 A - 105

B.C.C. NO. 분류번호	SHEET NO. 절단번호
JOB NO. 작업번호	REV NO. 개정

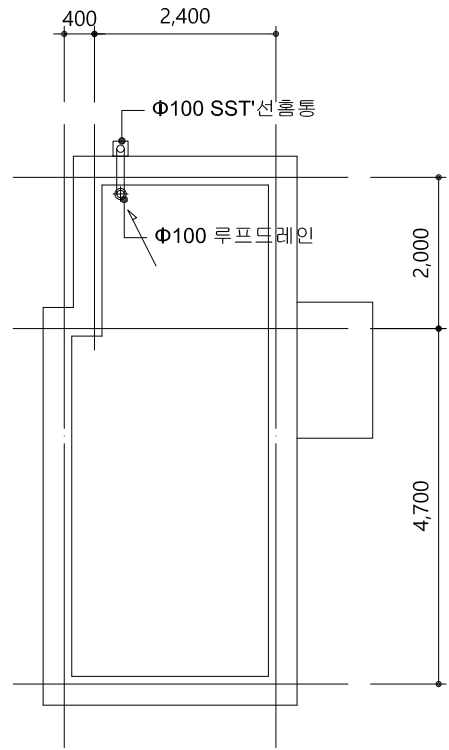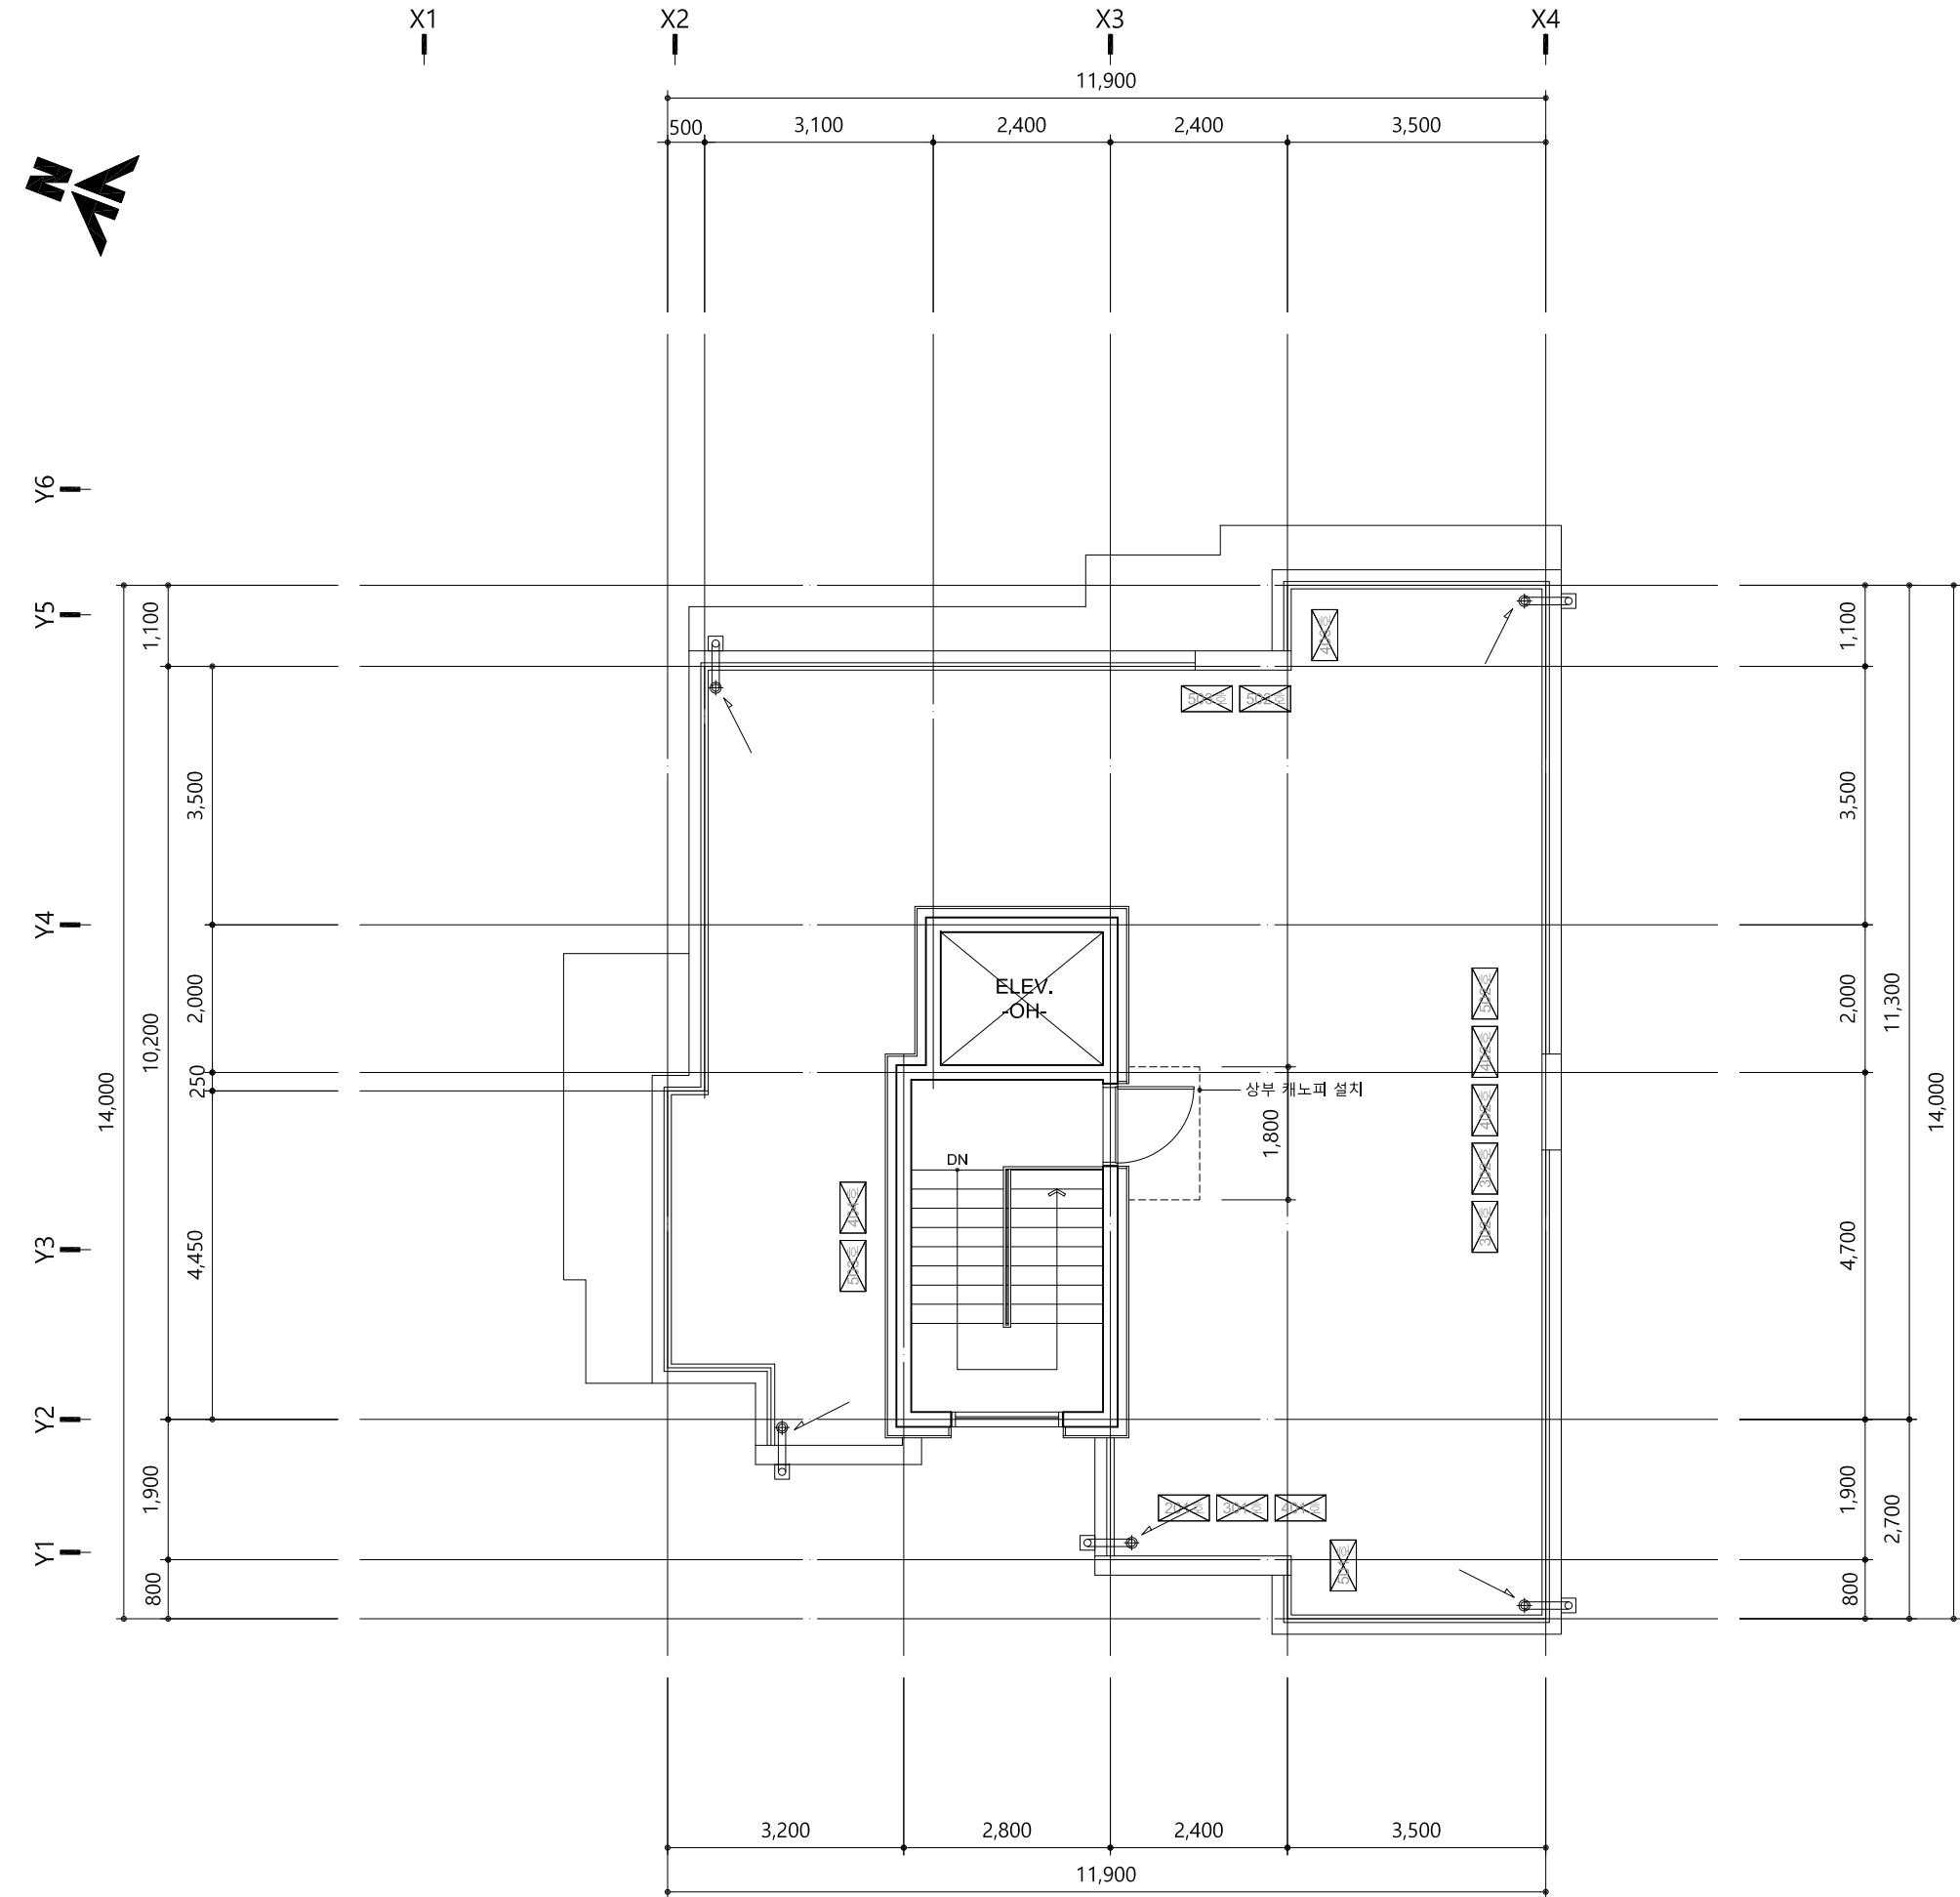


옥탑 지붕 평면도
SCALE A3 : 1/100



옥탑층 평면도
SCALE A3 : 1/100

KEY PLAN

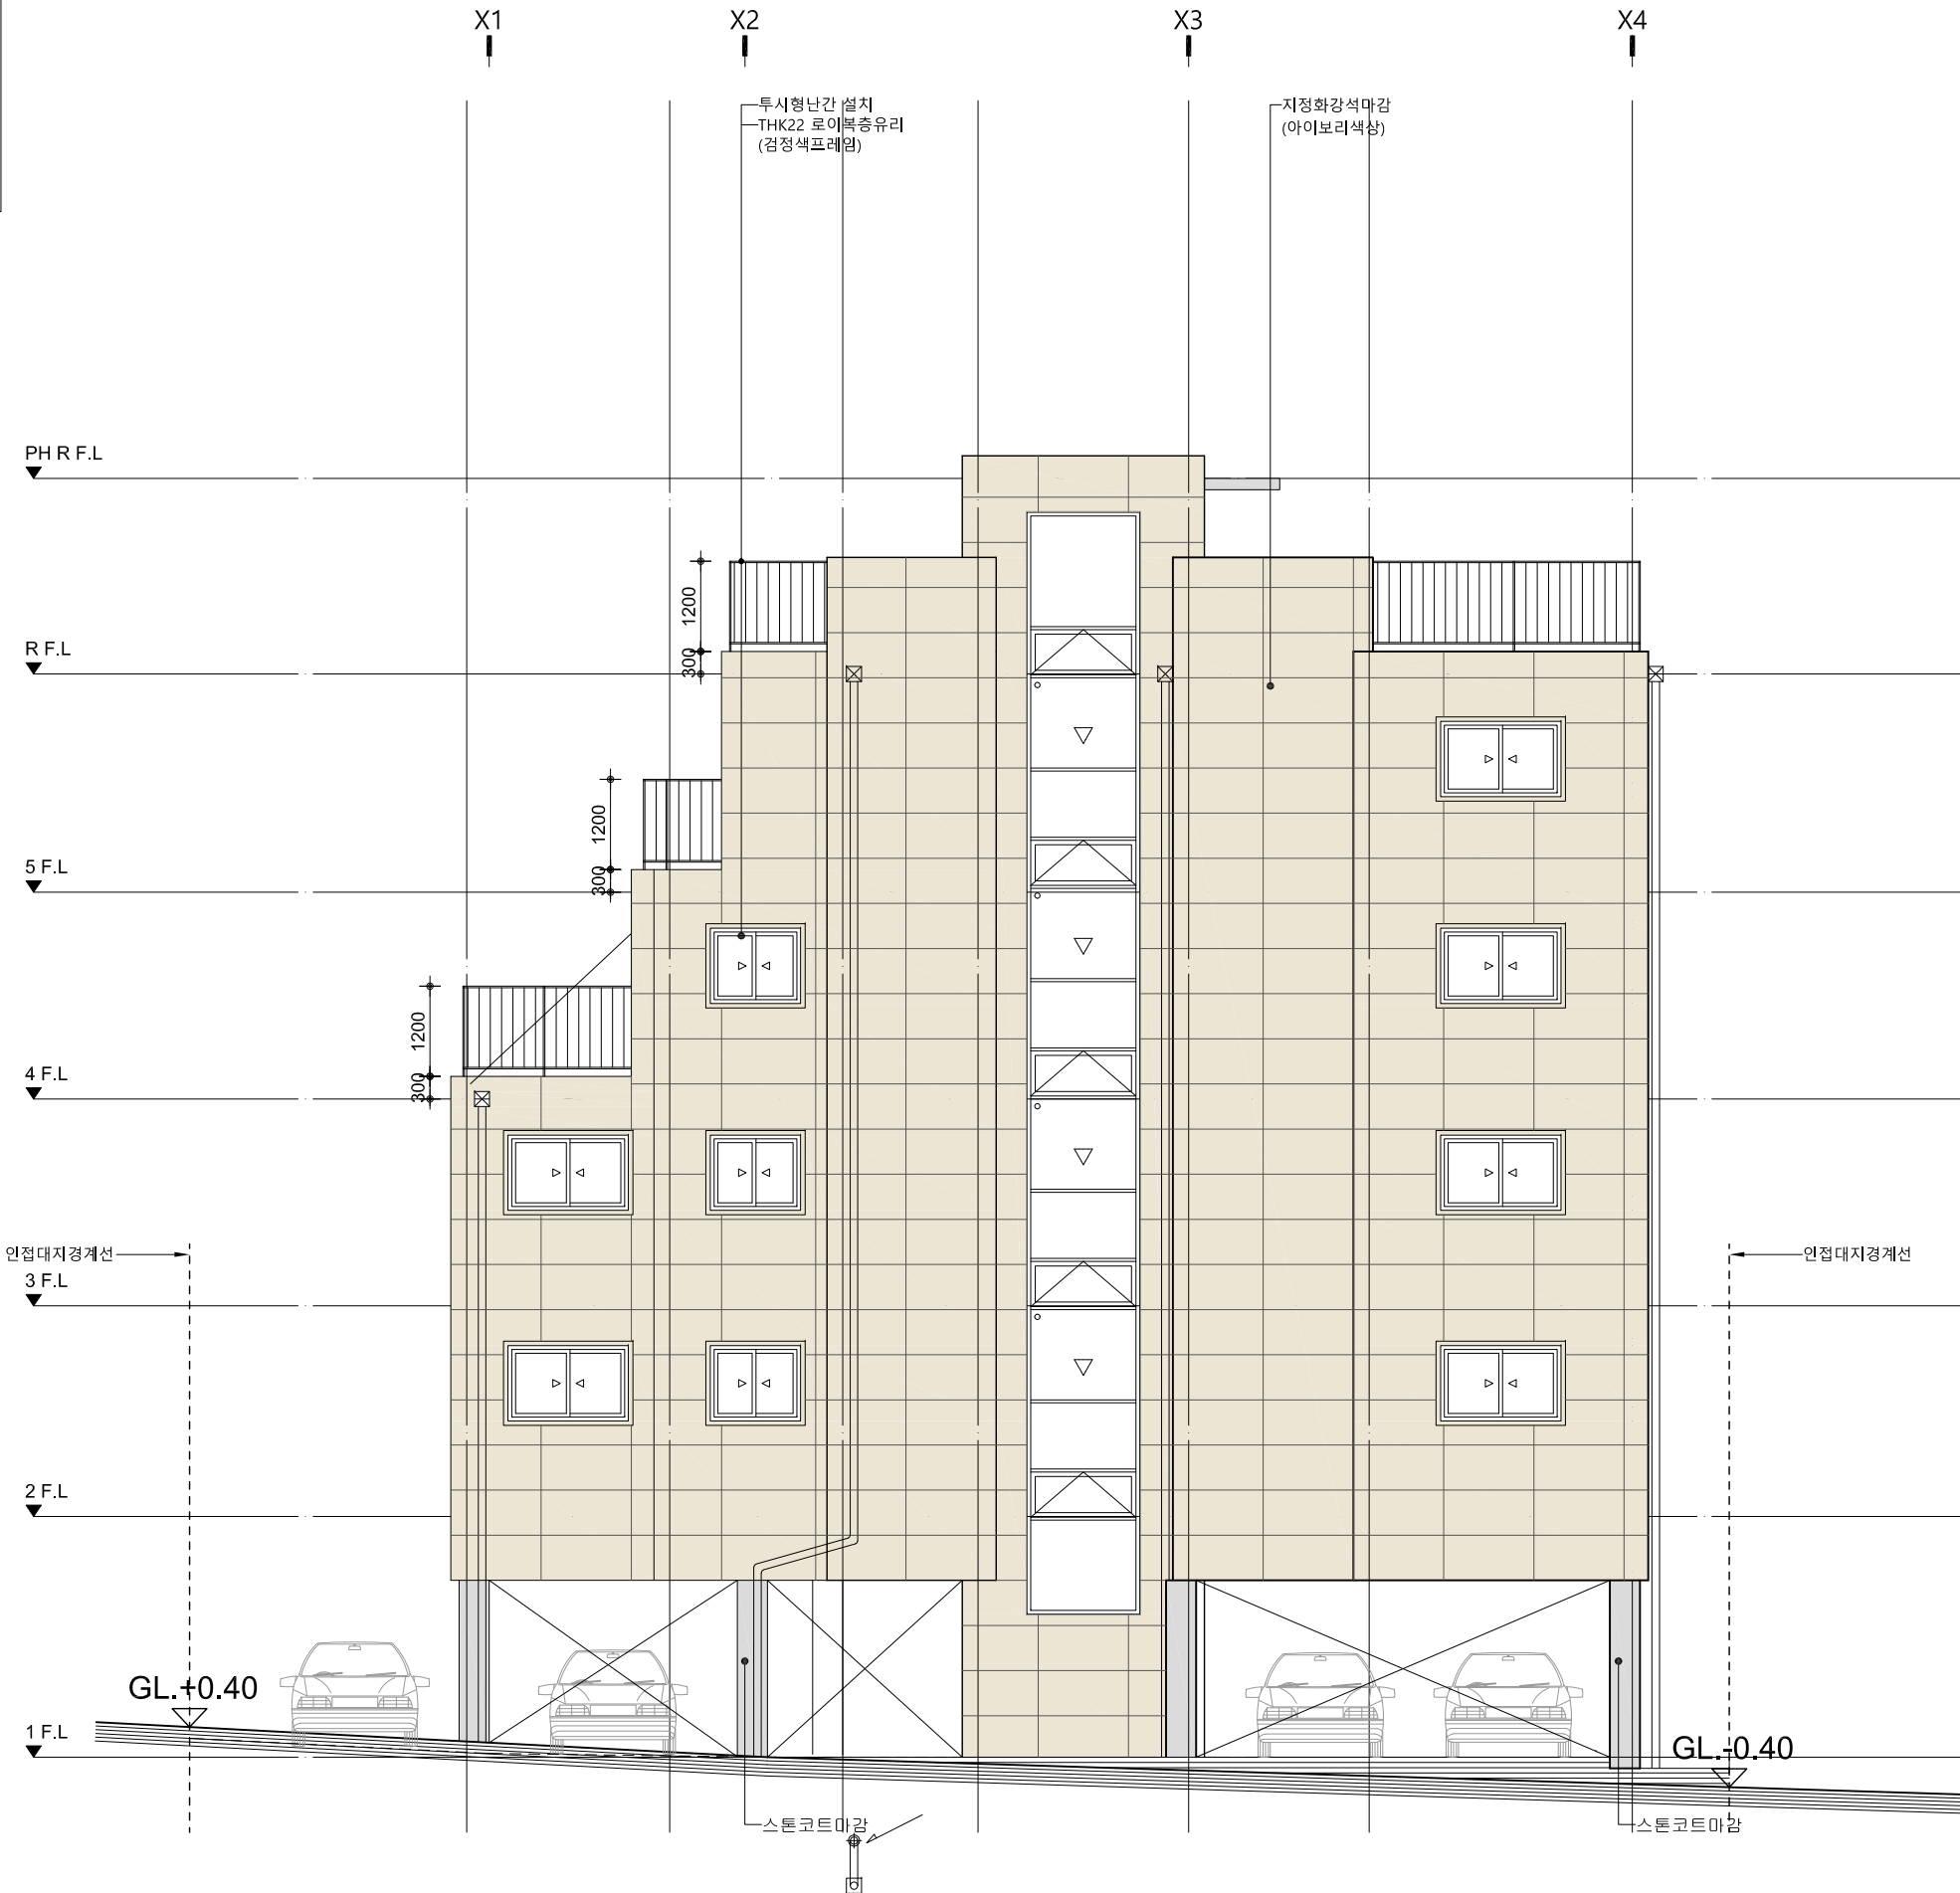

정면도(서측면도)
SCALE A3 : 1/100

PROJECT TITLE
공사명

강북구 수유동
560-2호
다세대주택
신축공사

NOTE

1층 바닥높이 : GL ±0.00
2~5층 반자높이 : 2200
슬래브 : THK 210
2층슬래브 : THK 150
내벽 : THK 150
외벽, 세대간벽 : THK 200
콘크리트 fck = 27 MPa

- ELEV. 내측벽 : THK20 방진패드
- 코아 내측벽 : THK60 단열재

△					
△					
△					
△					
△					
NO	DATE	REVISION	DESCRIPTION	DRAWN	DATE





건축사 사무소
하늘건축
Architects & Engineers

TEL : 02) 928 ~ 4484
FAX : 02) 928 ~ 4487

APPROVED 인	
ARCHITECT 설계	
CHKD 1 검토	
CHKD 2 검토	
DRAWN 당	
DATE 작성일	2024. 10.
SCALE 축척	A3 : 1/100
TITLE 도면명	정면도(서측면도)
DRWG. NO. 도면번호	A - 201
B.C.C. NO. 분류번호	SHEET NO. 시트번호
JOB NO. 작업번호	REV NO. 개정번호

KEY PLAN

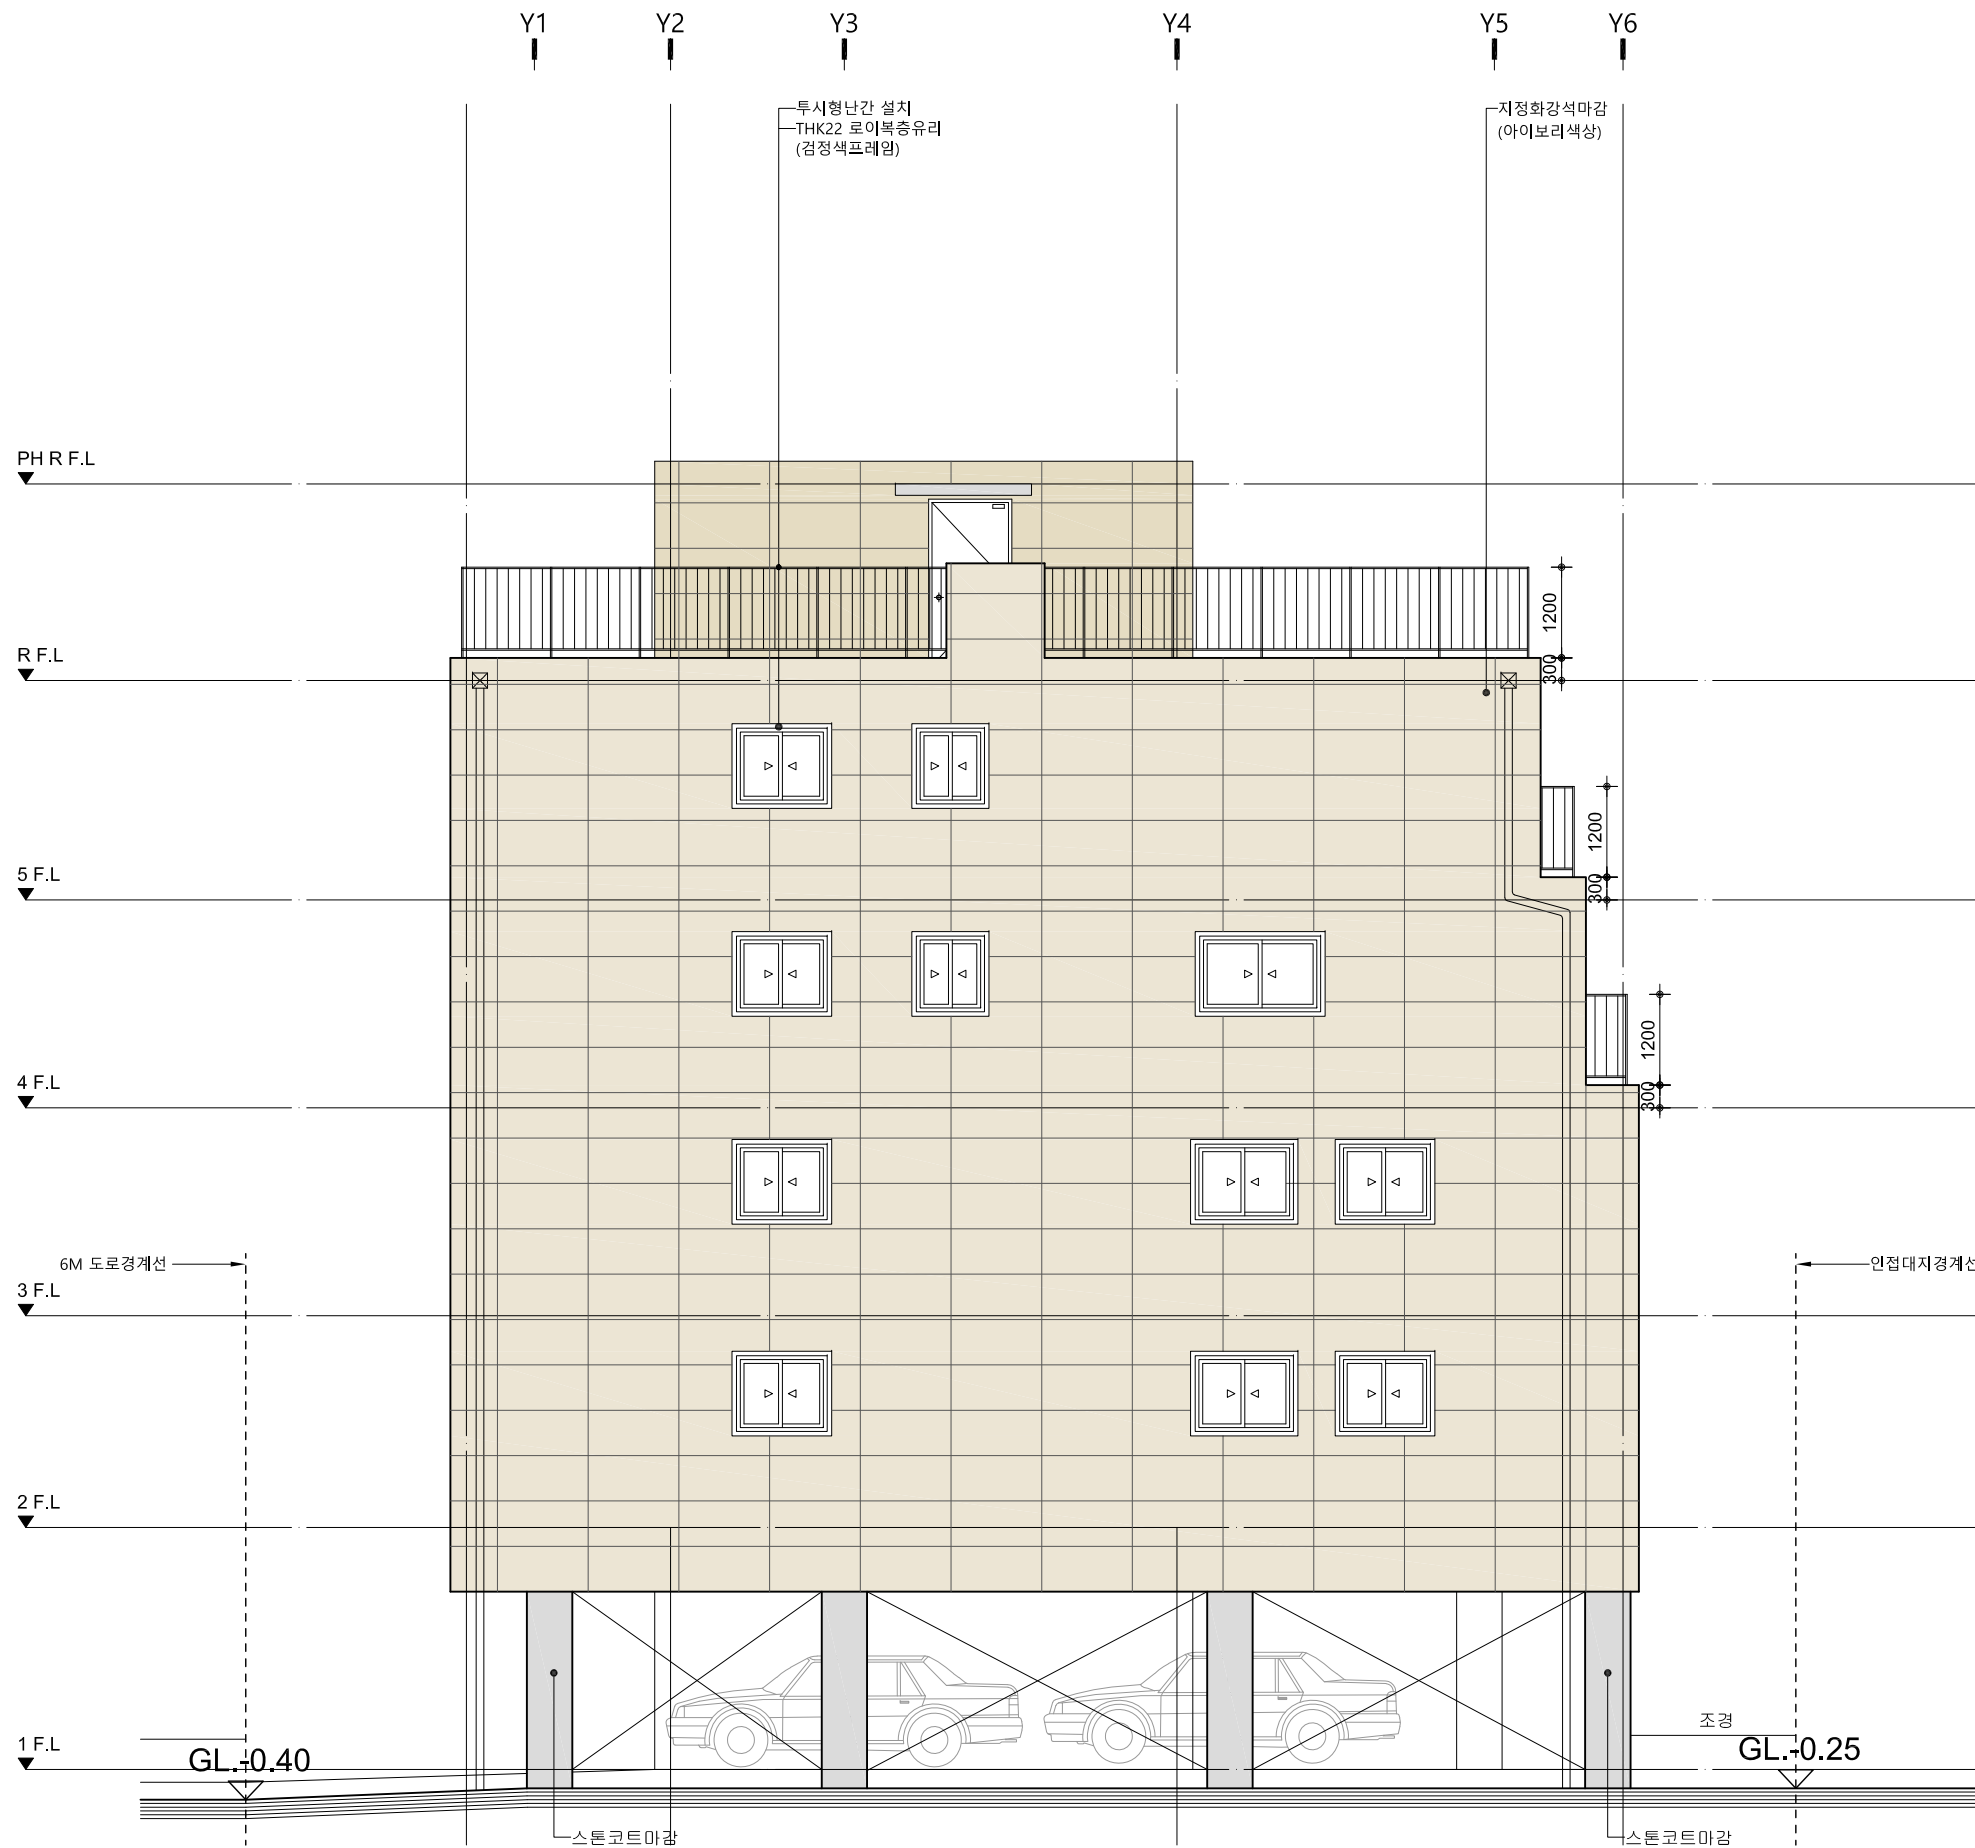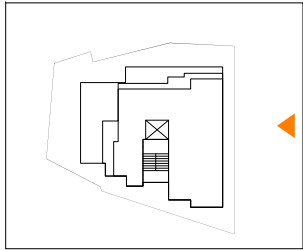

우측면도(남측면도)
SCALE A3 : 1/100

PROJECT TITLE
공사명

강북구 수유동
560-2호
다세대주택
신축공사

NOTE

1층 바닥높이 : GL ±0.00
2~5층 반자높이 : 2200
슬래브 : THK 210
2층슬래브 : THK 150
내벽 : THK 150
외벽, 세대간벽 : THK 200
콘크리트 fck = 27 MPa

- ELEV. 내측벽 : THK20 방진패드
- 코아 내측벽 : THK60 단열재

△					
△					
△					
△					
△					
NO	DATE	REVISION	DESCRIPTION	DRAWN	DATE





건축사 사무소
하늘건축
Architects & Engineers

TEL : 02) 928 ~ 4484
FAX : 02) 928 ~ 4487

APPROVED 인	
ARCHITECT 설계	
CHKD 1 검토	
CHKD 2 검토	
DRAWN 당	
DATE 작성일	2024. 10.
SCALE 축척	A3 : 1/100
TITLE 도면명	우측면도(남측면도)
DRWG NO. 도면번호	A - 202
B.C.C NO. 분류번호	SHEET NO. 결판번호
JOB NO. 작업번호	REV NO.

KEY PLAN

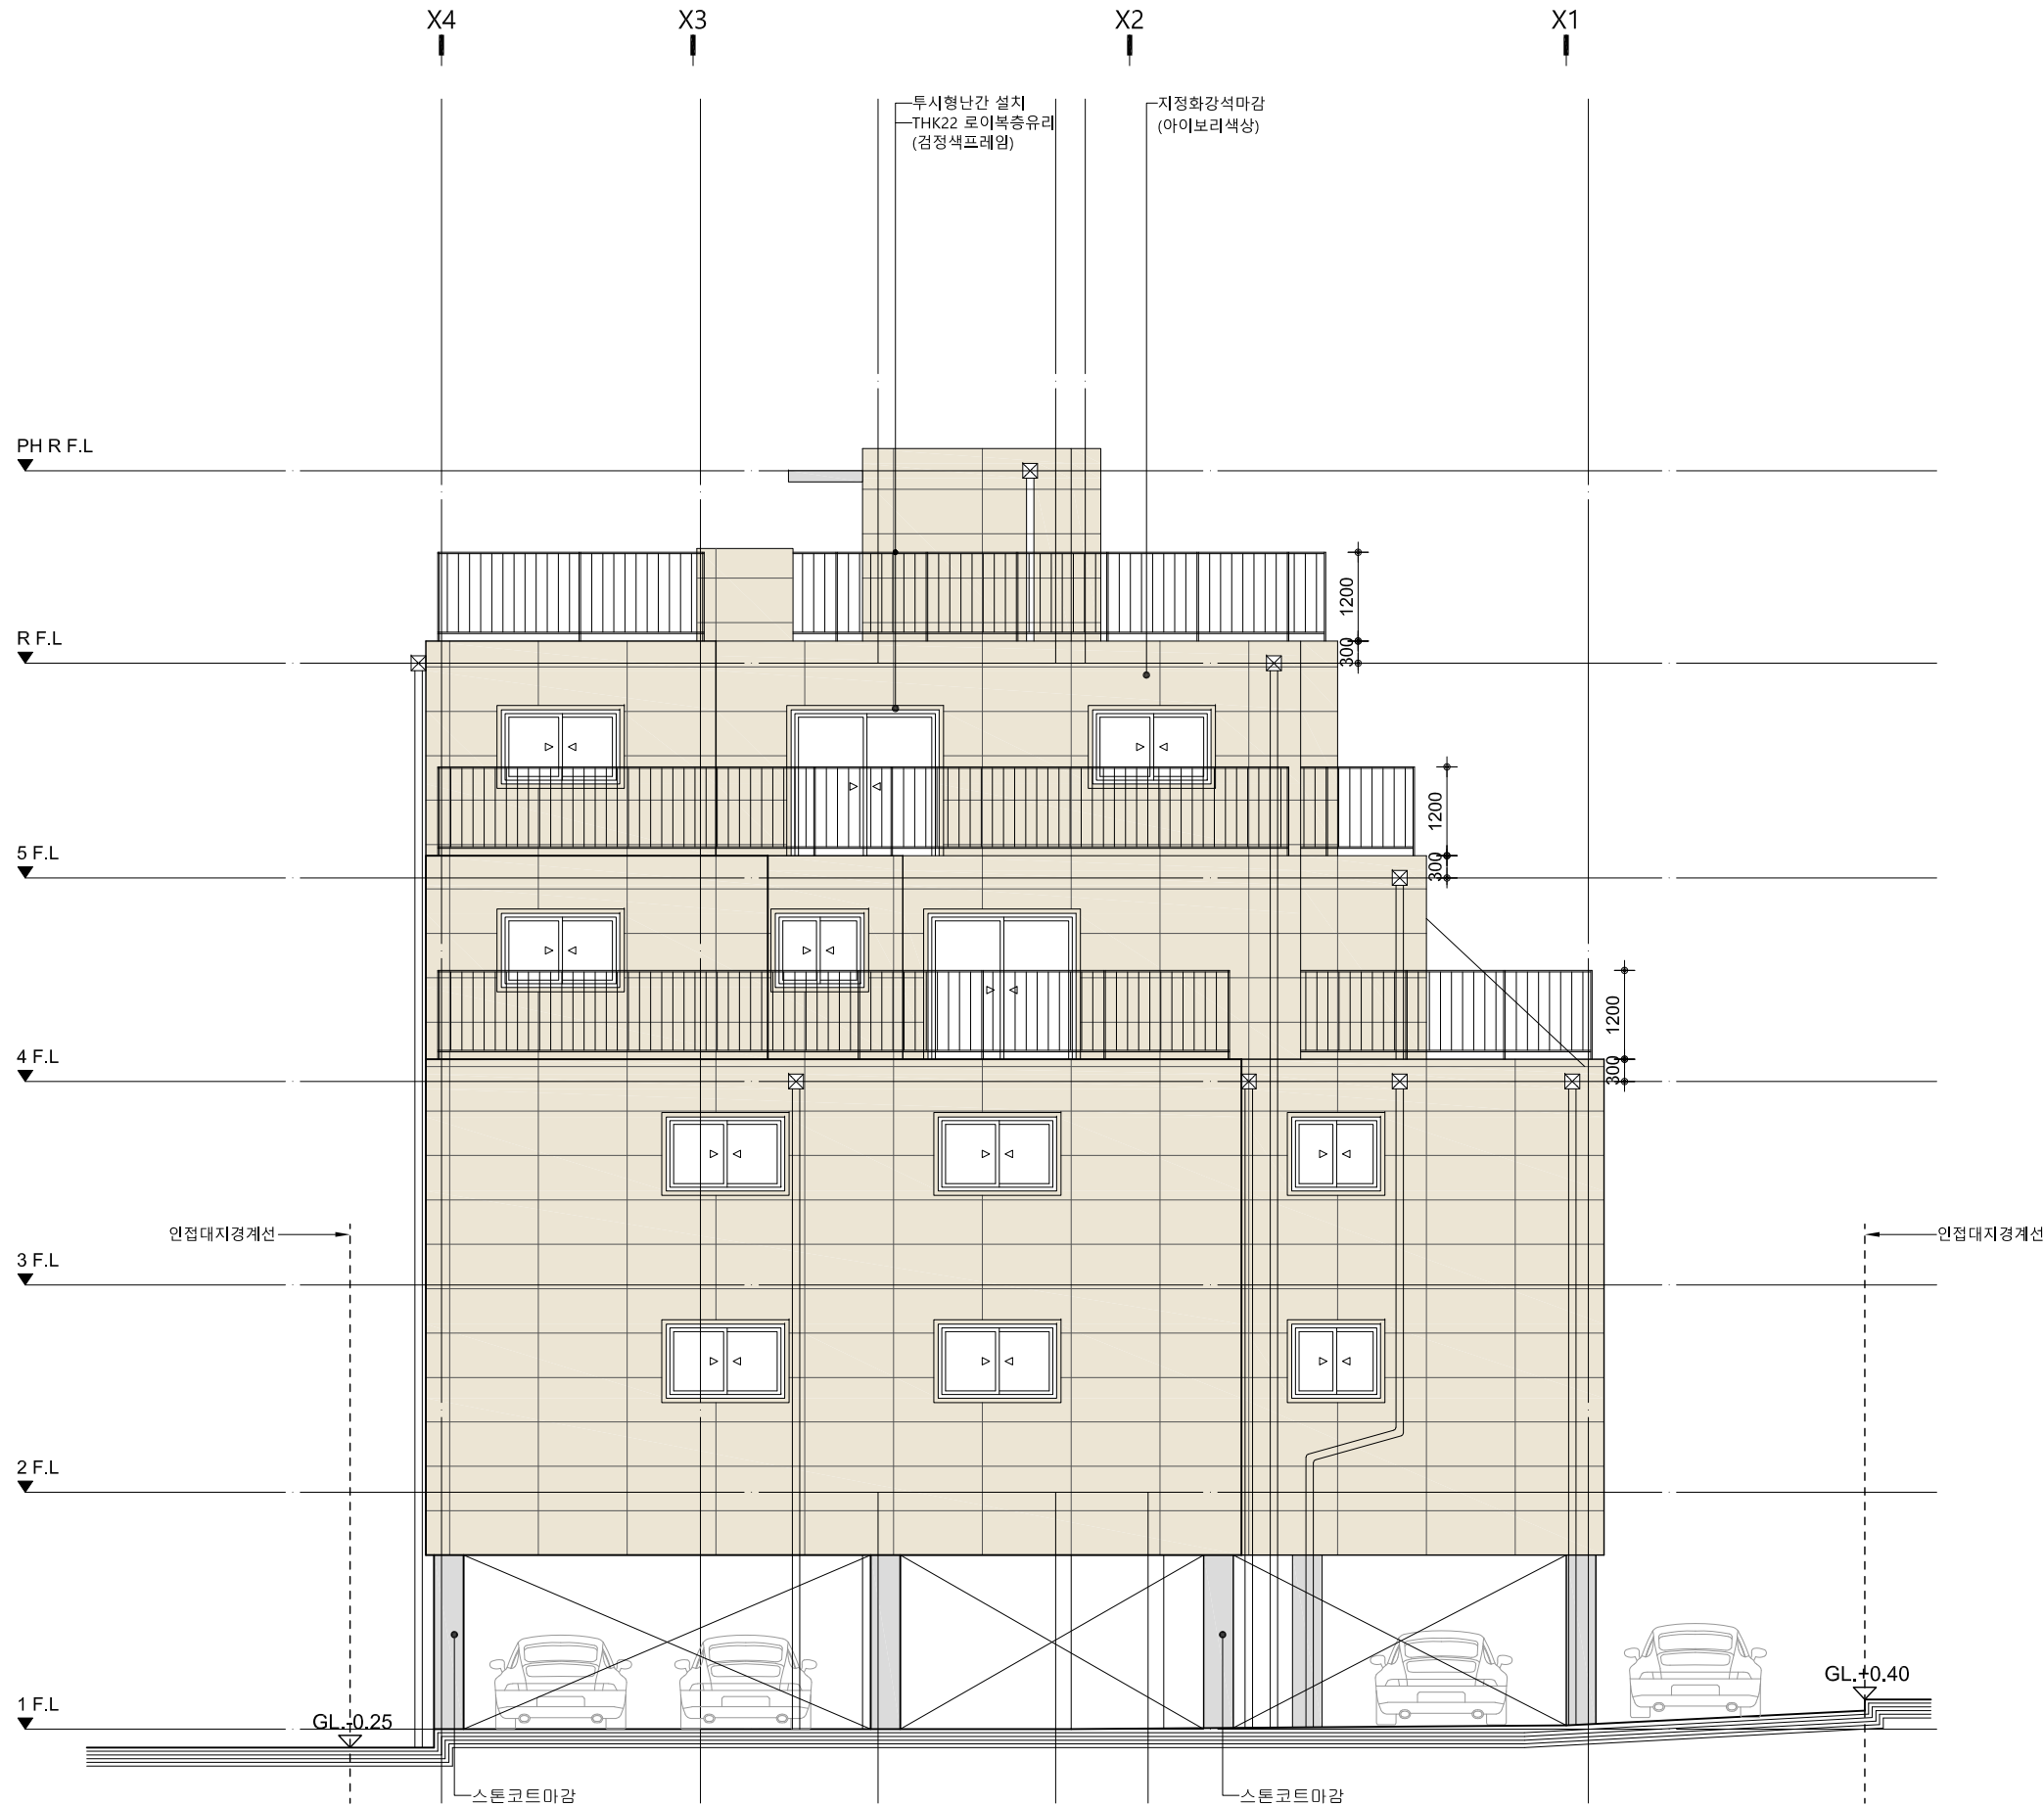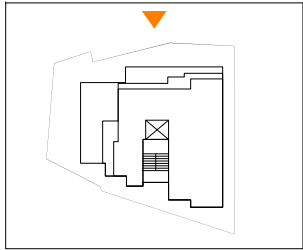

배면도(동측면도)
SCALE A3 : 1/100

PROJECT TITLE
공 사 명

강북구 수유동
560-2호
다세대주택
신 축 공 사

NOTE

1층 바닥높이 : GL ±0.00
2~5층 반자높이 : 2200
슬래브 : THK 210
2층슬래브 : THK 150
내벽 : THK 150
외벽, 세대간벽 : THK 200
콘크리트 fck = 27 MPa

- ELEV. 내측벽 : THK20 방진패드
- 코아 내측벽 : THK60 단열재

△					
△					
△					
△					
△					
NO	DATE	REVISION	DESCRIPTION	DRWN	DATE



건축사 사무소
하늘 건축
Architects & Engineers

TEL : 02) 928 ~ 4484
FAX : 02) 928 ~ 4487

APPROVED 인	
ARCHITECT 설	
CHKD 1 검	
CHKD 2 검	
DRAWN 당	

DATE
작성일
2024. 10.

SCALE
축척
A3 : 1/100

TITLE
도면명
배면도(동측면도)

DRWG NO.
도면번호
A - 203



B.C.C NO.
분류번호

SHEET NO.
시트번호

JOB NO.
작업번호

REV NO.
개정번호

KEY PLAN

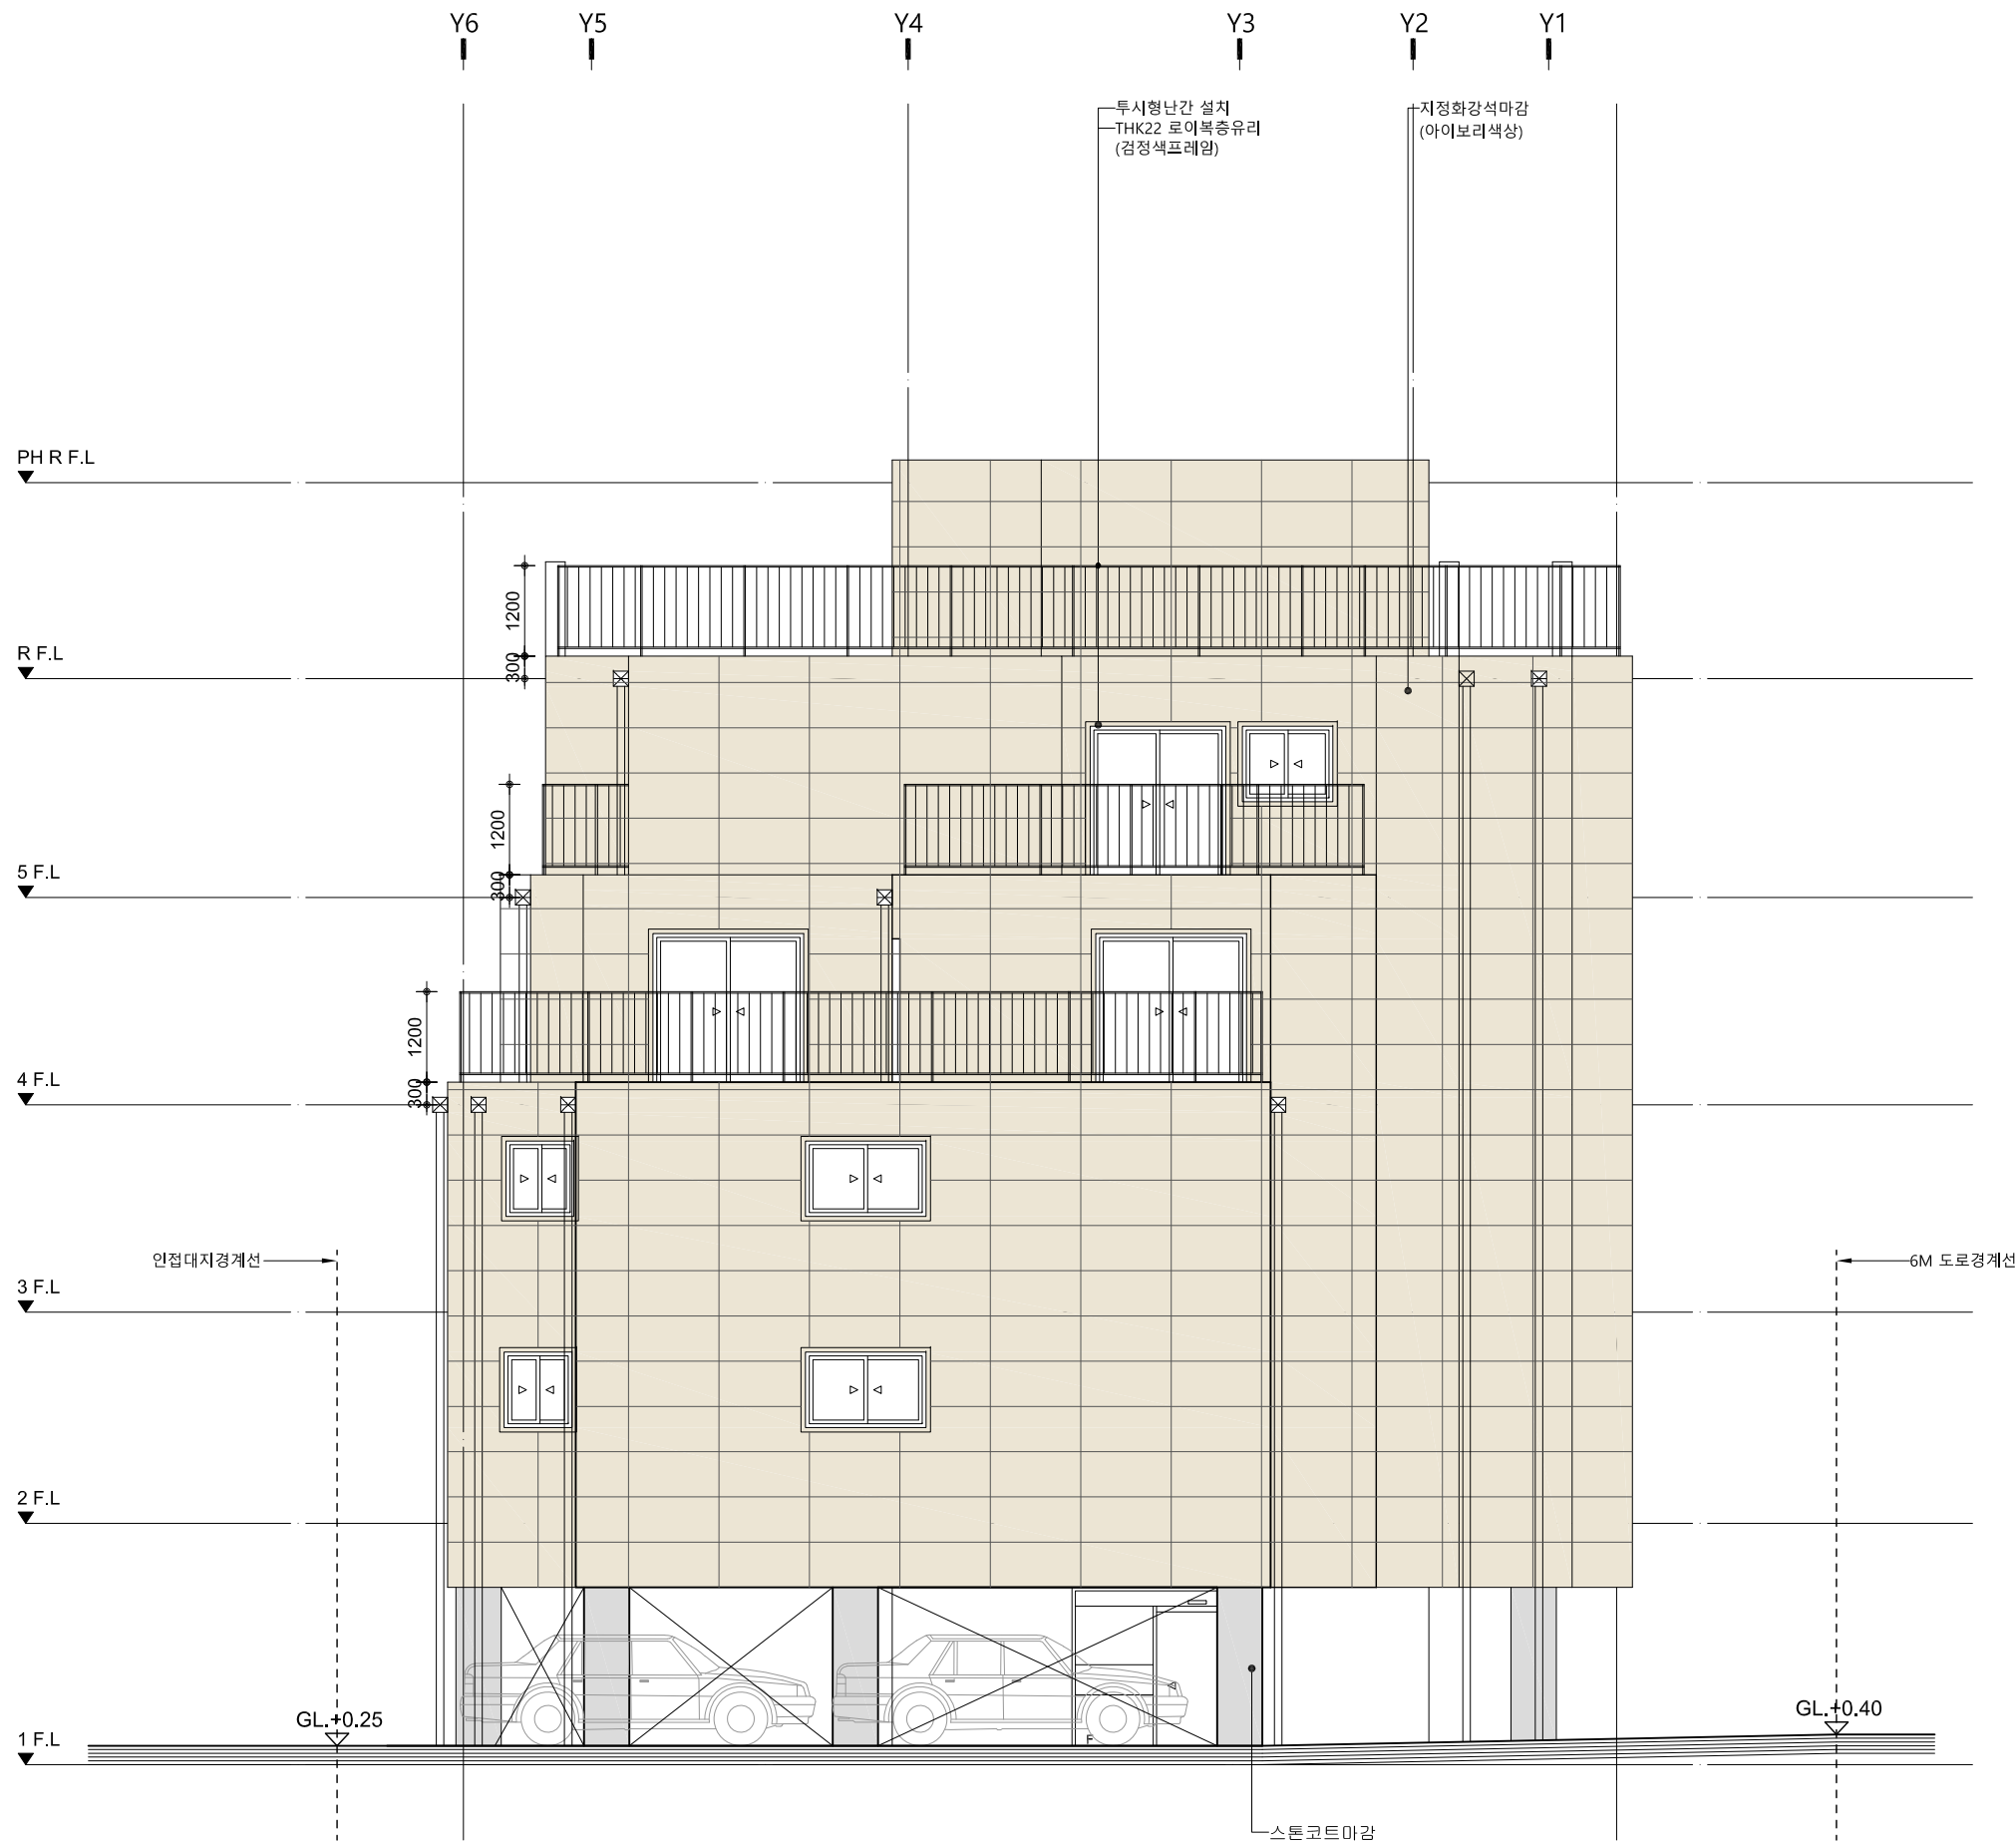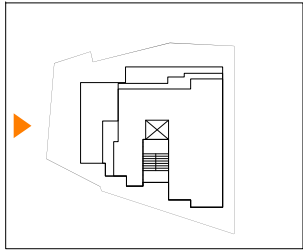

좌측면도(북측면도)
SCALE A3 : 1/100

PROJECT TITLE
공사명

강북구 수유동
560-2호
다세대주택
신축공사

NOTE

1층 바닥높이 : GL ±0.00
2~5층 반자높이 : 2200
슬래브 : THK 210
2층슬래브 : THK 150
내벽 : THK 150
외벽, 세대간벽 : THK 200
콘크리트 fck = 27 MPa

- ELEV. 내측벽 : THK20 방진패드
- 코아 내측벽 : THK60 단열재

△					
△					
△					
△					
△					
NO	DATE	REVISION	DESCRIPTION	DRAWN	DATE



건축사 사무소
하늘건축
Architects & Engineers

TEL : 02) 928 ~ 4484
FAX : 02) 928 ~ 4487

APPROVED 인	
ARCHITECT 설계	
CHKD 1 검토	
CHKD 2 검토	
DRAWN 담당	

DATE
작성일
2024. 10.

SCALE
축척
A3 : 1/100

TITLE
도면명
좌측면도(북측면도)

DRWG NO.
도면번호
A - 204

B.C.C NO. 분류번호	SHEET NO. 절단번호
JOB NO. 작업번호	REV NO. 개정