
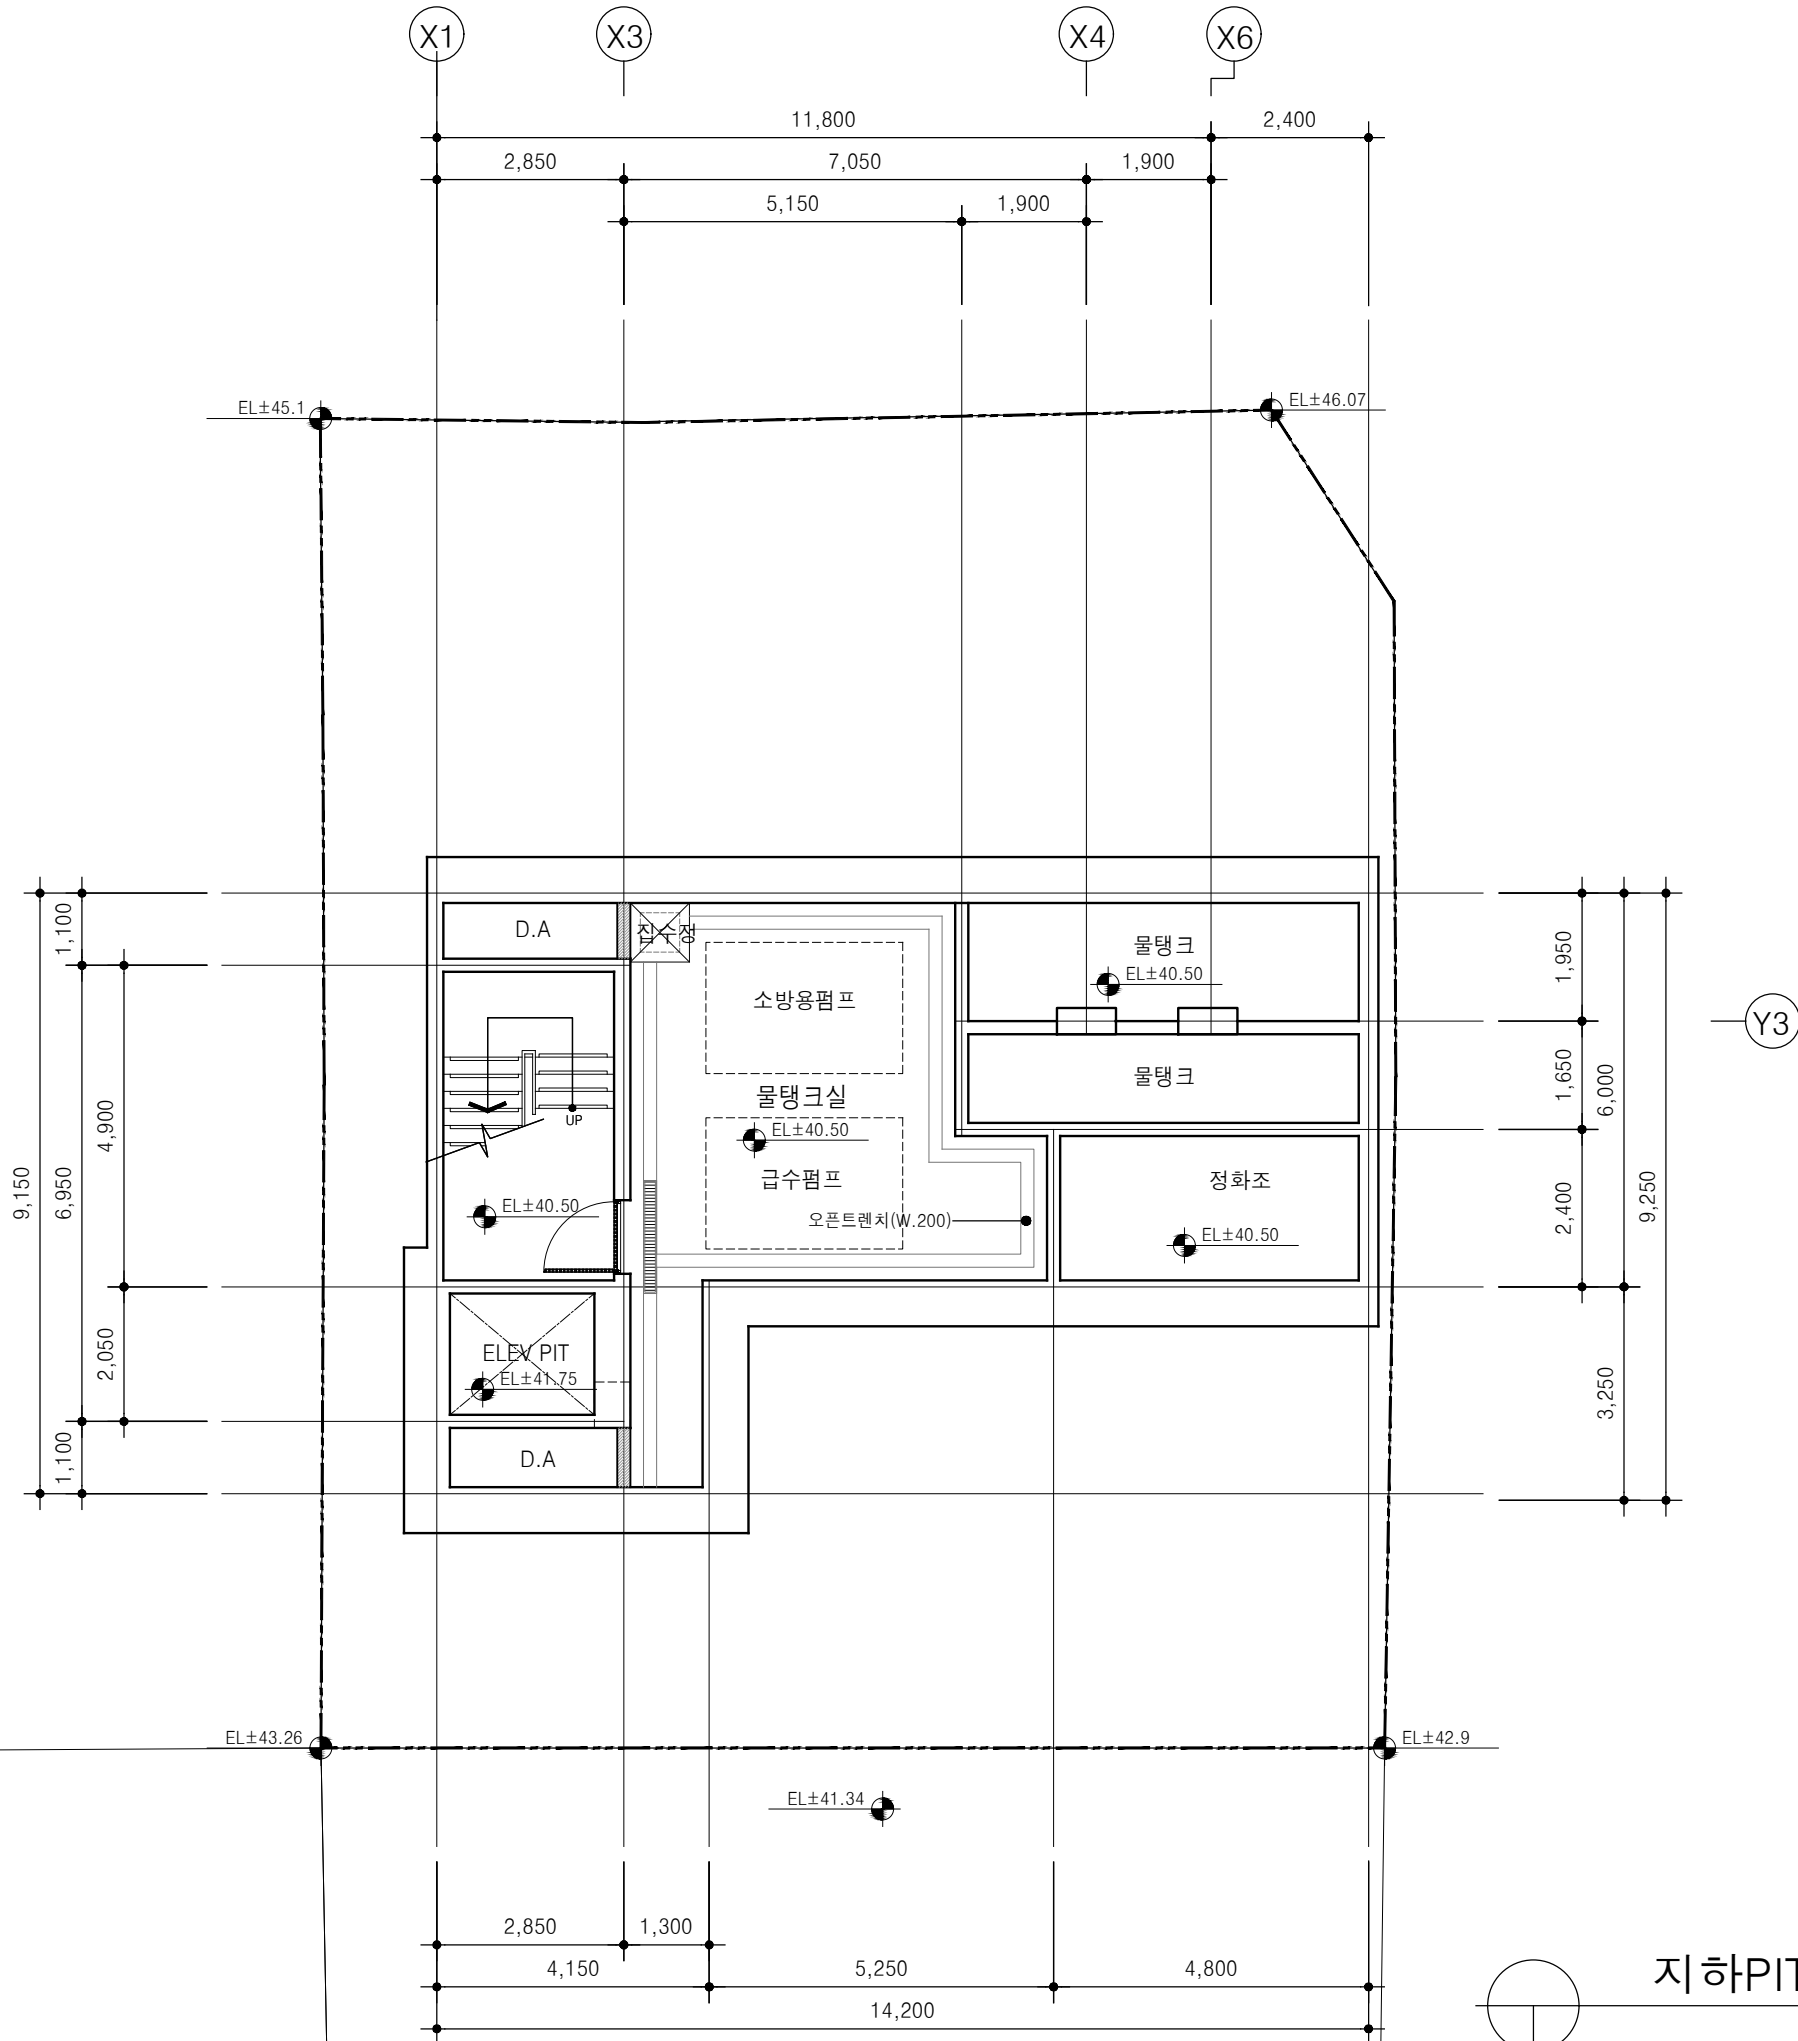


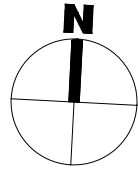

지하PIT 평면도

* NOTE

변경사항 REVISION

수정번호	수정내용		
	설 계	검 토	승 인
20		20	20
수정번호	수정내용		
	설 계	검 토	승 인
20		20	20
수정번호	수정내용		
	설 계	검 토	승 인
20		20	20

합동설계 CONSULTANTS

토목	CIVIL - ENGINEERING	
구조	CONSTRUCTION	
기계	MECHANICAL EQUIPMENT	
전기	ELECTRICAL EQUIPMENT	
방재	PREVENTION	
조경	LANDSCAPING	

KEY PLAN

설 계 번 호 PROJECT NO.

2024-0502

설 계 명 PROJECT NAME

화곡동 155-22 도시형생활주택
신축공사



유아이
건축사사무소(주)

06649 서울시 서초구 반포대로24길 42-6 태진빌딩 1층
TEL. 02 6348 1575 FAX. 02 6280 1576
http://www.ui-architects.com

승 인 APPROVE

심 사 SUBMIT

설 계 DRAWN

도 면 명

지하PIT 평면도

축 척

파일명 FILE NAME


A1

A3

1/120


도면번호 SHEETNO.

A - 000

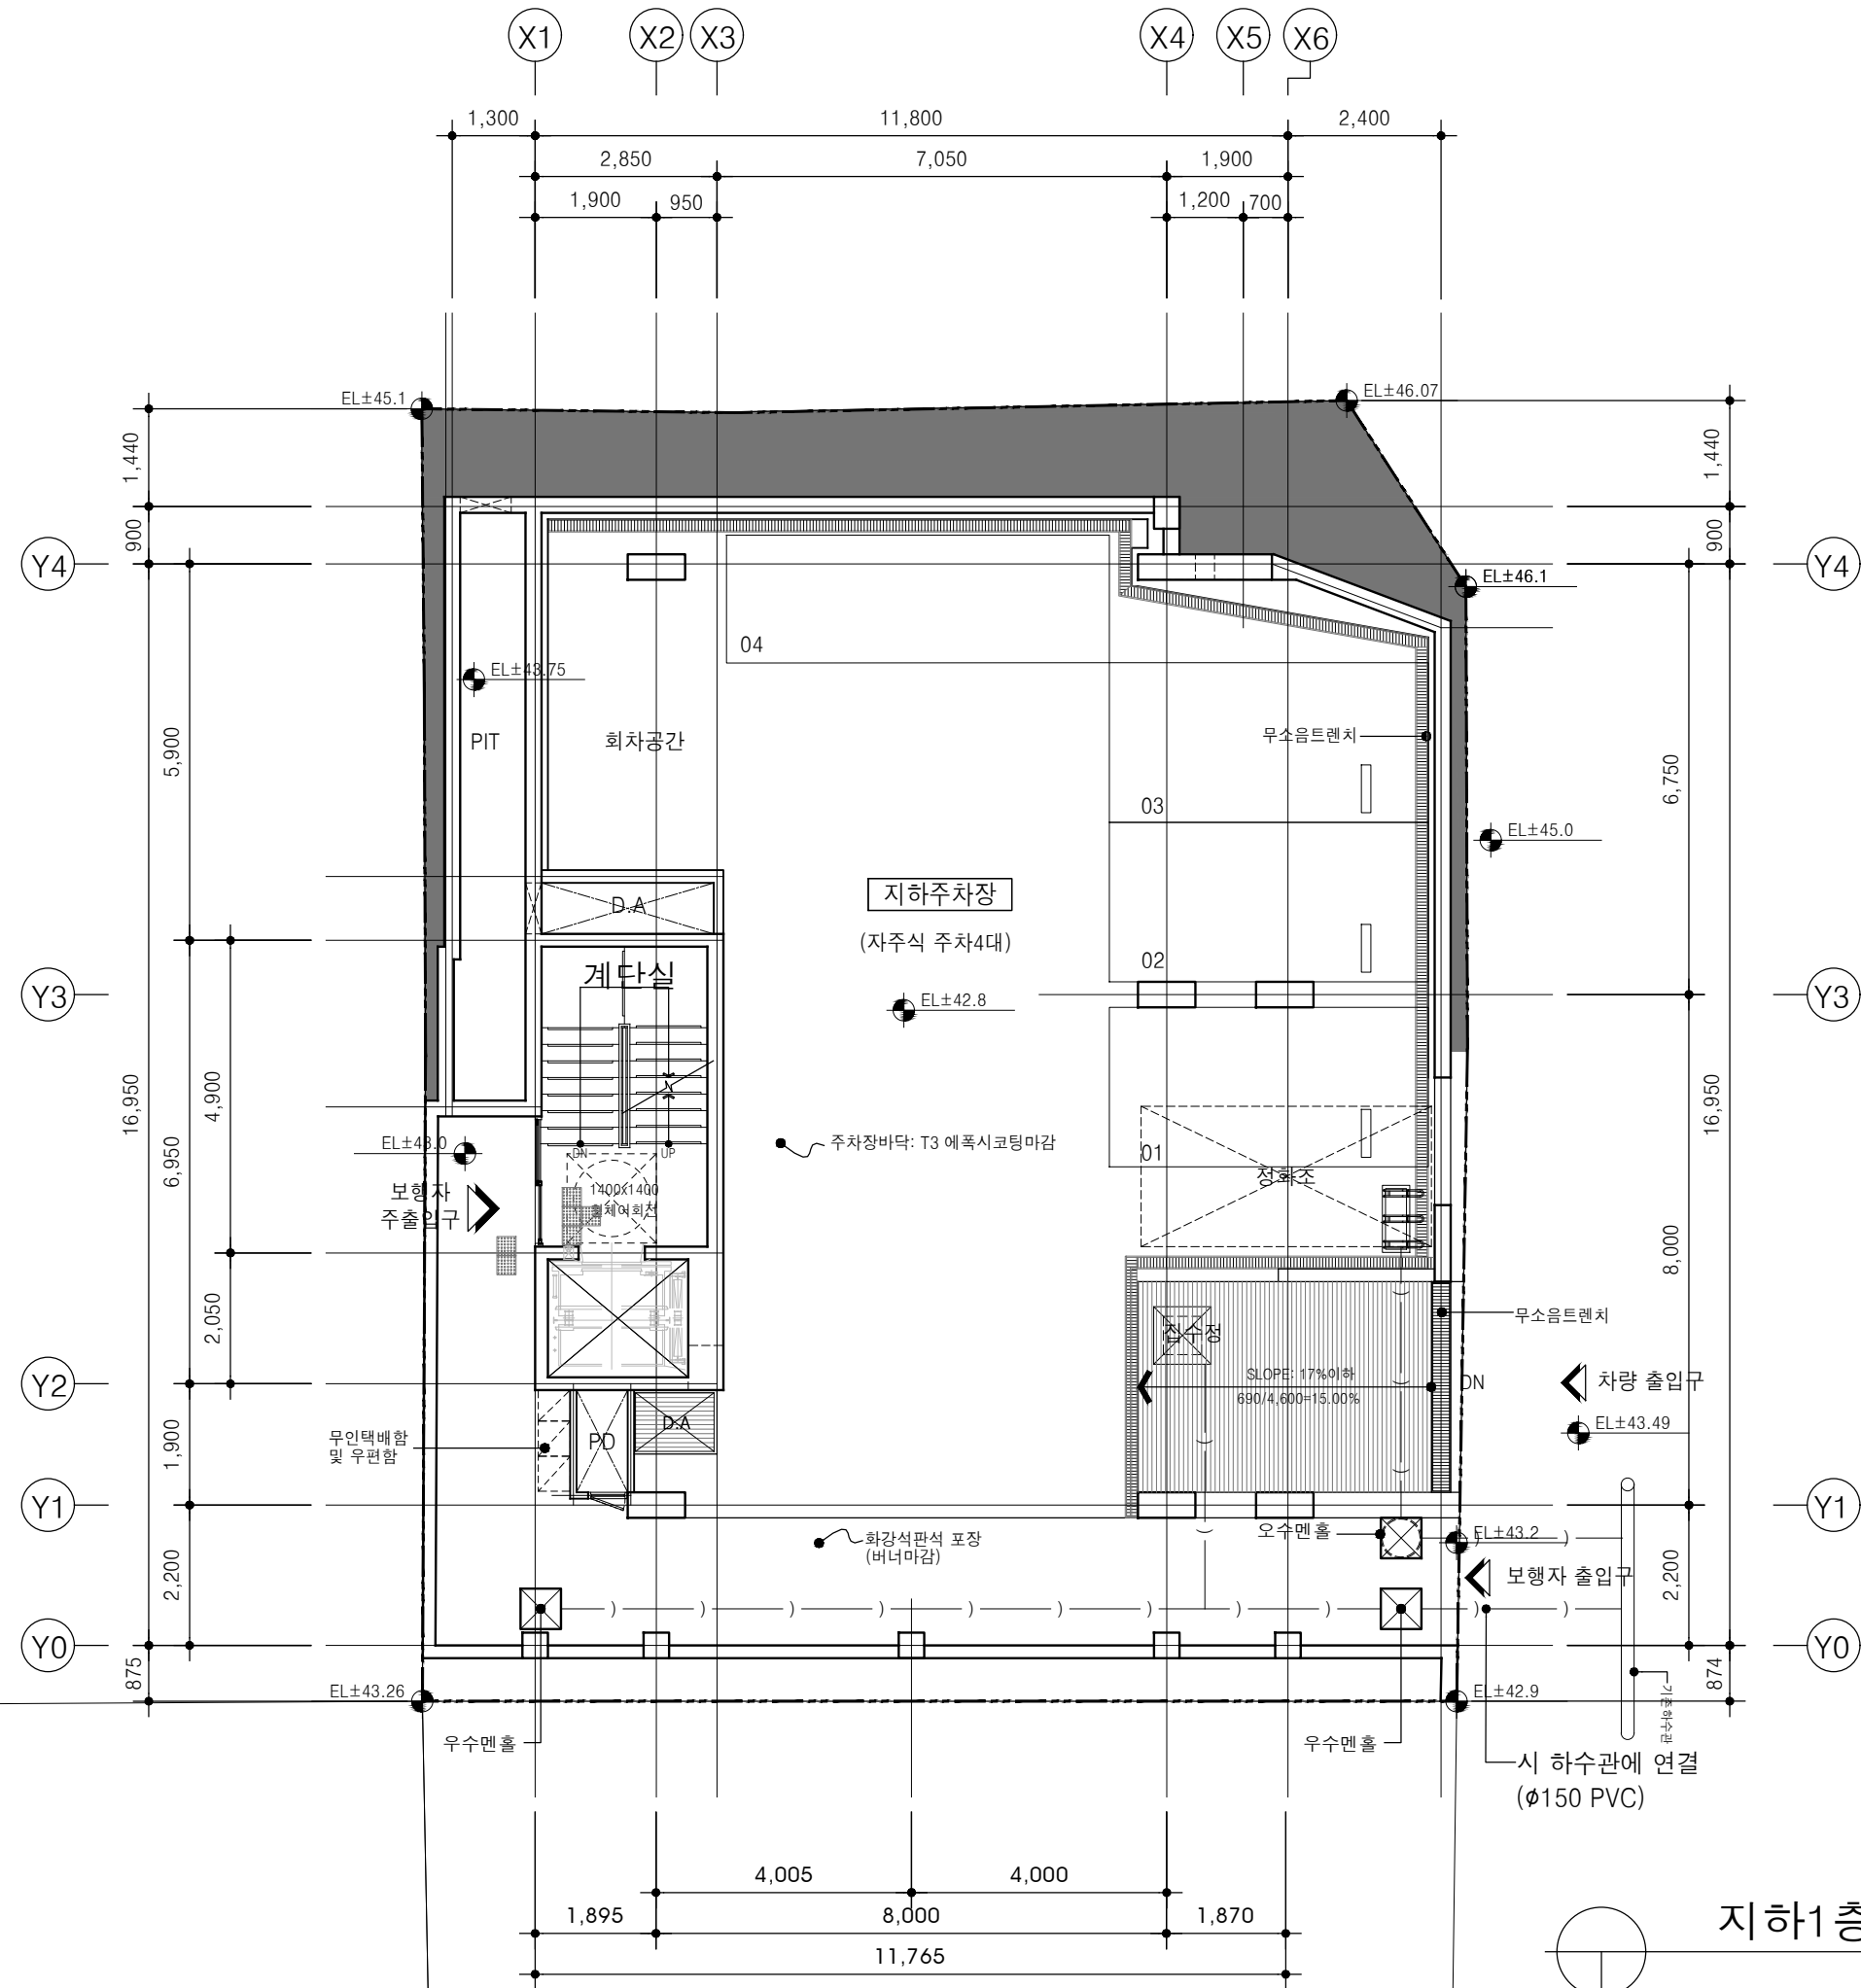

지하1층 평면도

A - 000

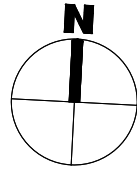

4M 도로

Y4

Y3

Y2

Y1

X1

X2

X3

X4

X5

X6

차량 출입구

차량출입 안내용 경광등 설치

차량진출입 안전용 반사경 설치

보행자 출입구

필로티 주차장

(자주식 주차8대)

보행자
주출입구

(휴게공간)

쓰레기분리장

8M 도로

지상 1층 평면도

* NOTE

변경사항 REVISION

수정번호	수정내용		
	설 계	검 토	승 인
20	...	20	...
20	...	20	...
20	...	20	...

합동설계 CONSULTANTS

토목	CIVIL - ENGINEERING	
구조	CONSTRUCTION	
기계	MECHANICAL EQUIPMENT	
전기	ELECTRICAL EQUIPMENT	
방재	PREVENTION	
조경	LANDSCAPING	

KEY PLAN

설 계 번 호 PROJECT NO.

2024-0502

설 계 명 PROJECT NAME

화곡동 155-22 도시형생활주택
신축공사



유아이
건축사무소(주)

06649 서울시 서초구 반포대로24길 42-6 태진빌딩 1층
TEL. 02 6348 1575 FAX. 02 6280 1576
http://www.ui-architects.com

승 인 APPROVE

심 사 SUBMIT

설 계 DRAWN

도면명

지상 1층 평면도

축척



파일명 FILE NAME

A1


A3 1/120

도면번호 SHEETNO.

A - 000

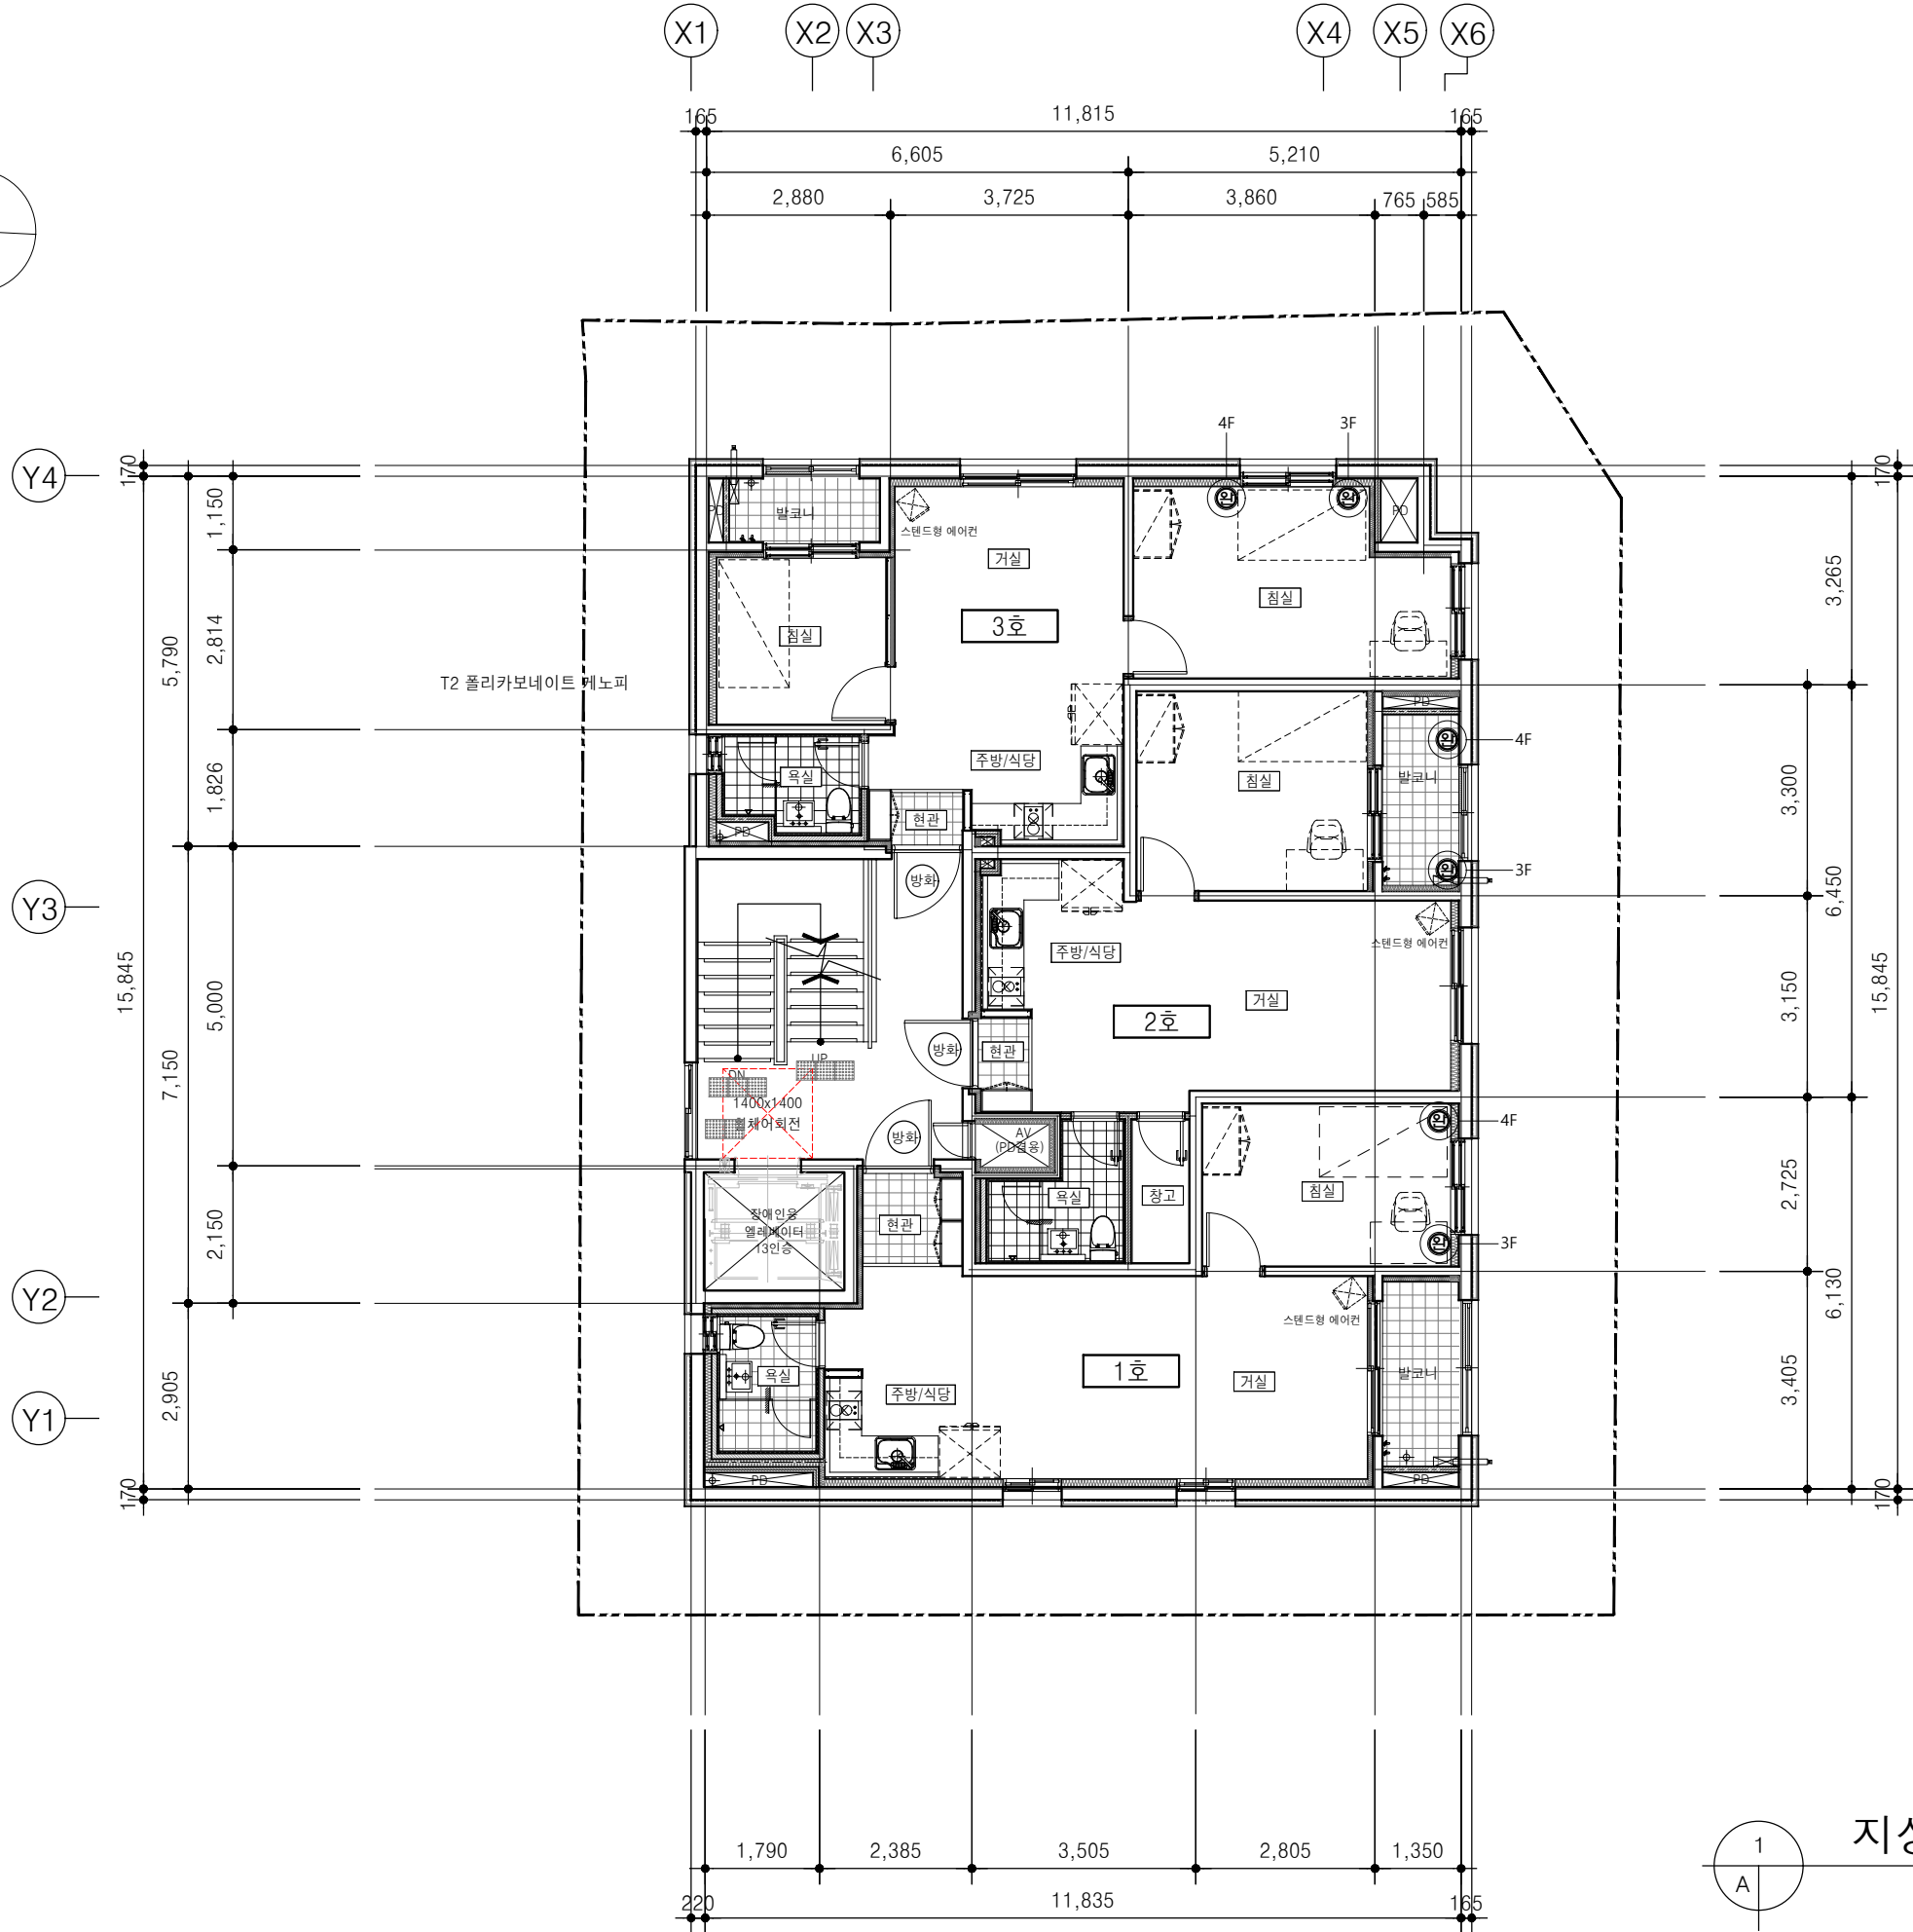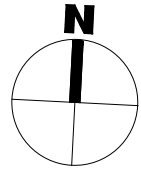

②	완강기	수량
	난간높이 1.2M이상 고정식발판 설치	3

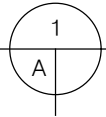

지상 2~4층 평면도

축척 : 1 / 120 (A3)

* NOTE

- 내력벽(철근콘크리트)
- 비내력벽(경량벽체)
- 조적벽(0.5B)

변경사항 REVISION

수정번호	수정내용
①	설계 검토 승인
20	20
20	20
20	20
②	수정내용
설계 검토 승인	
20	20
20	20
20	20
③	수정내용
설계 검토 승인	
20	20
20	20
20	20

합동설계 CONSULTANTS

토목	CIVIL ENGINEERING
구조	CONSTRUCTION
기계	MECHANICAL EQUIPMENT
전기	ELECTRICAL EQUIPMENT
방재	PREVENTION
조경	LANDSCAPING

KEY PLAN

설계번호 PROJECT NO.
2024-0502

설계명 PROJECT NAME
화곡동 155-22 도시형생활주택
신축공사

UI 유아이
건축사사무소(주)
06649 서울시 서초구 반포대로24길 42-6 태진빌딩 1층
TEL. 02 6348 1575 FAX. 02 6280 1576
http://www.ui-architects.com

승인 APPROVE 심사 SUBMIT

설계 DRAWN

도면명
지상 2~4층 평면도

축척
A1

파일명 FILE NAME


A3 1/120

도면번호 SHEETNO.

A - 000



완강기	수량
난간높이 1.2M이상 고정식발판 설치	3

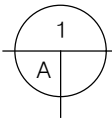

지상 5층 평면도

축척 : 1 / 120 (A3)

* NOTE

- 내력벽(철근콘크리트)
- 비내력벽(경량벽체)
- 조적벽(0.5B)
- 확장형 발코니

변경사항 REVISION

수정내용	설 계	검 토	승 인
20	20	20	20
수정내용	설 계	검 토	승 인
20	20	20	20
수정내용	설 계	검 토	승 인
20	20	20	20

합동설계 CONSULTANTS

토목	CIVIL - ENGINEERING	
구조	CONSTRUCTION	
기계	MECHANICAL EQUIPMENT	
전기	ELECTRICAL EQUIPMENT	
방재	PREVENTION	
조경	LANDSCAPING	

KEY PLAN

설 계 번 호 PROJECT NO.
2024-0502

설 계 명 PROJECT NAME
화곡동 155-22 도시형생활주택
신축공사

UI 유아이
건축사사무소(주)
06649 서울시 서초구 반포대로24길 42-6 태진빌딩 1층
TEL. 02-6348-1575 FAX. 02-6280-1576
http://www.ui-architects.com

승 인 APPROVE	심 사 SUBMIT
설 계 DRAWN	


도면명
지상 5층 평면도

축척	파일명 FILE NAME
A1	
A3	1/120

도면번호 SHEETNO.
A - 000



②	완강기	수량
	난간높이 1.2M이상 고정식발판 설치	3

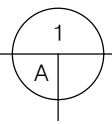

지상 6층 평면도

축척 : 1 / 120 (A3)

* NOTE

- 내력벽(철근콘크리트)
- 비내력벽(경량벽체)
- 조적벽(0.5B)
- 확장형 발코니

변경사항 REVISION

수정번호	수정내용		
	설계	검토	승인
20	20	20	20
수정번호	수정내용		
	설계	검토	승인
20	20	20	20
수정번호	수정내용		
	설계	검토	승인
20	20	20	20

합동설계 CONSULTANTS

토목	CIVIL ENGINEERING	
구조	CONSTRUCTION	
기계	MECHANICAL EQUIPMENT	
전기	ELECTRICAL EQUIPMENT	
방재	PREVENTION	
조경	LANDSCAPING	

KEY PLAN

설계번호 PROJECT NO.
2024-0502

설계명 PROJECT NAME
화곡동 155-22 도시형생활주택
신축공사



UI 유아이
건축사사무소(주)
06649 서울시 서초구 반포대로24길 42-6 태진빌딩 1층
TEL. 02 6348 1575 FAX. 02 6280 1576
http://www.ui-architects.com

승인 APPROVE	심사 SUBMIT
설계 DRAWN	

도면명
지상 6층 평면도

축척	파일명 FILE NAME
A1	
A3	1/120

도면번호 SHEETNO.
A - 000

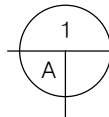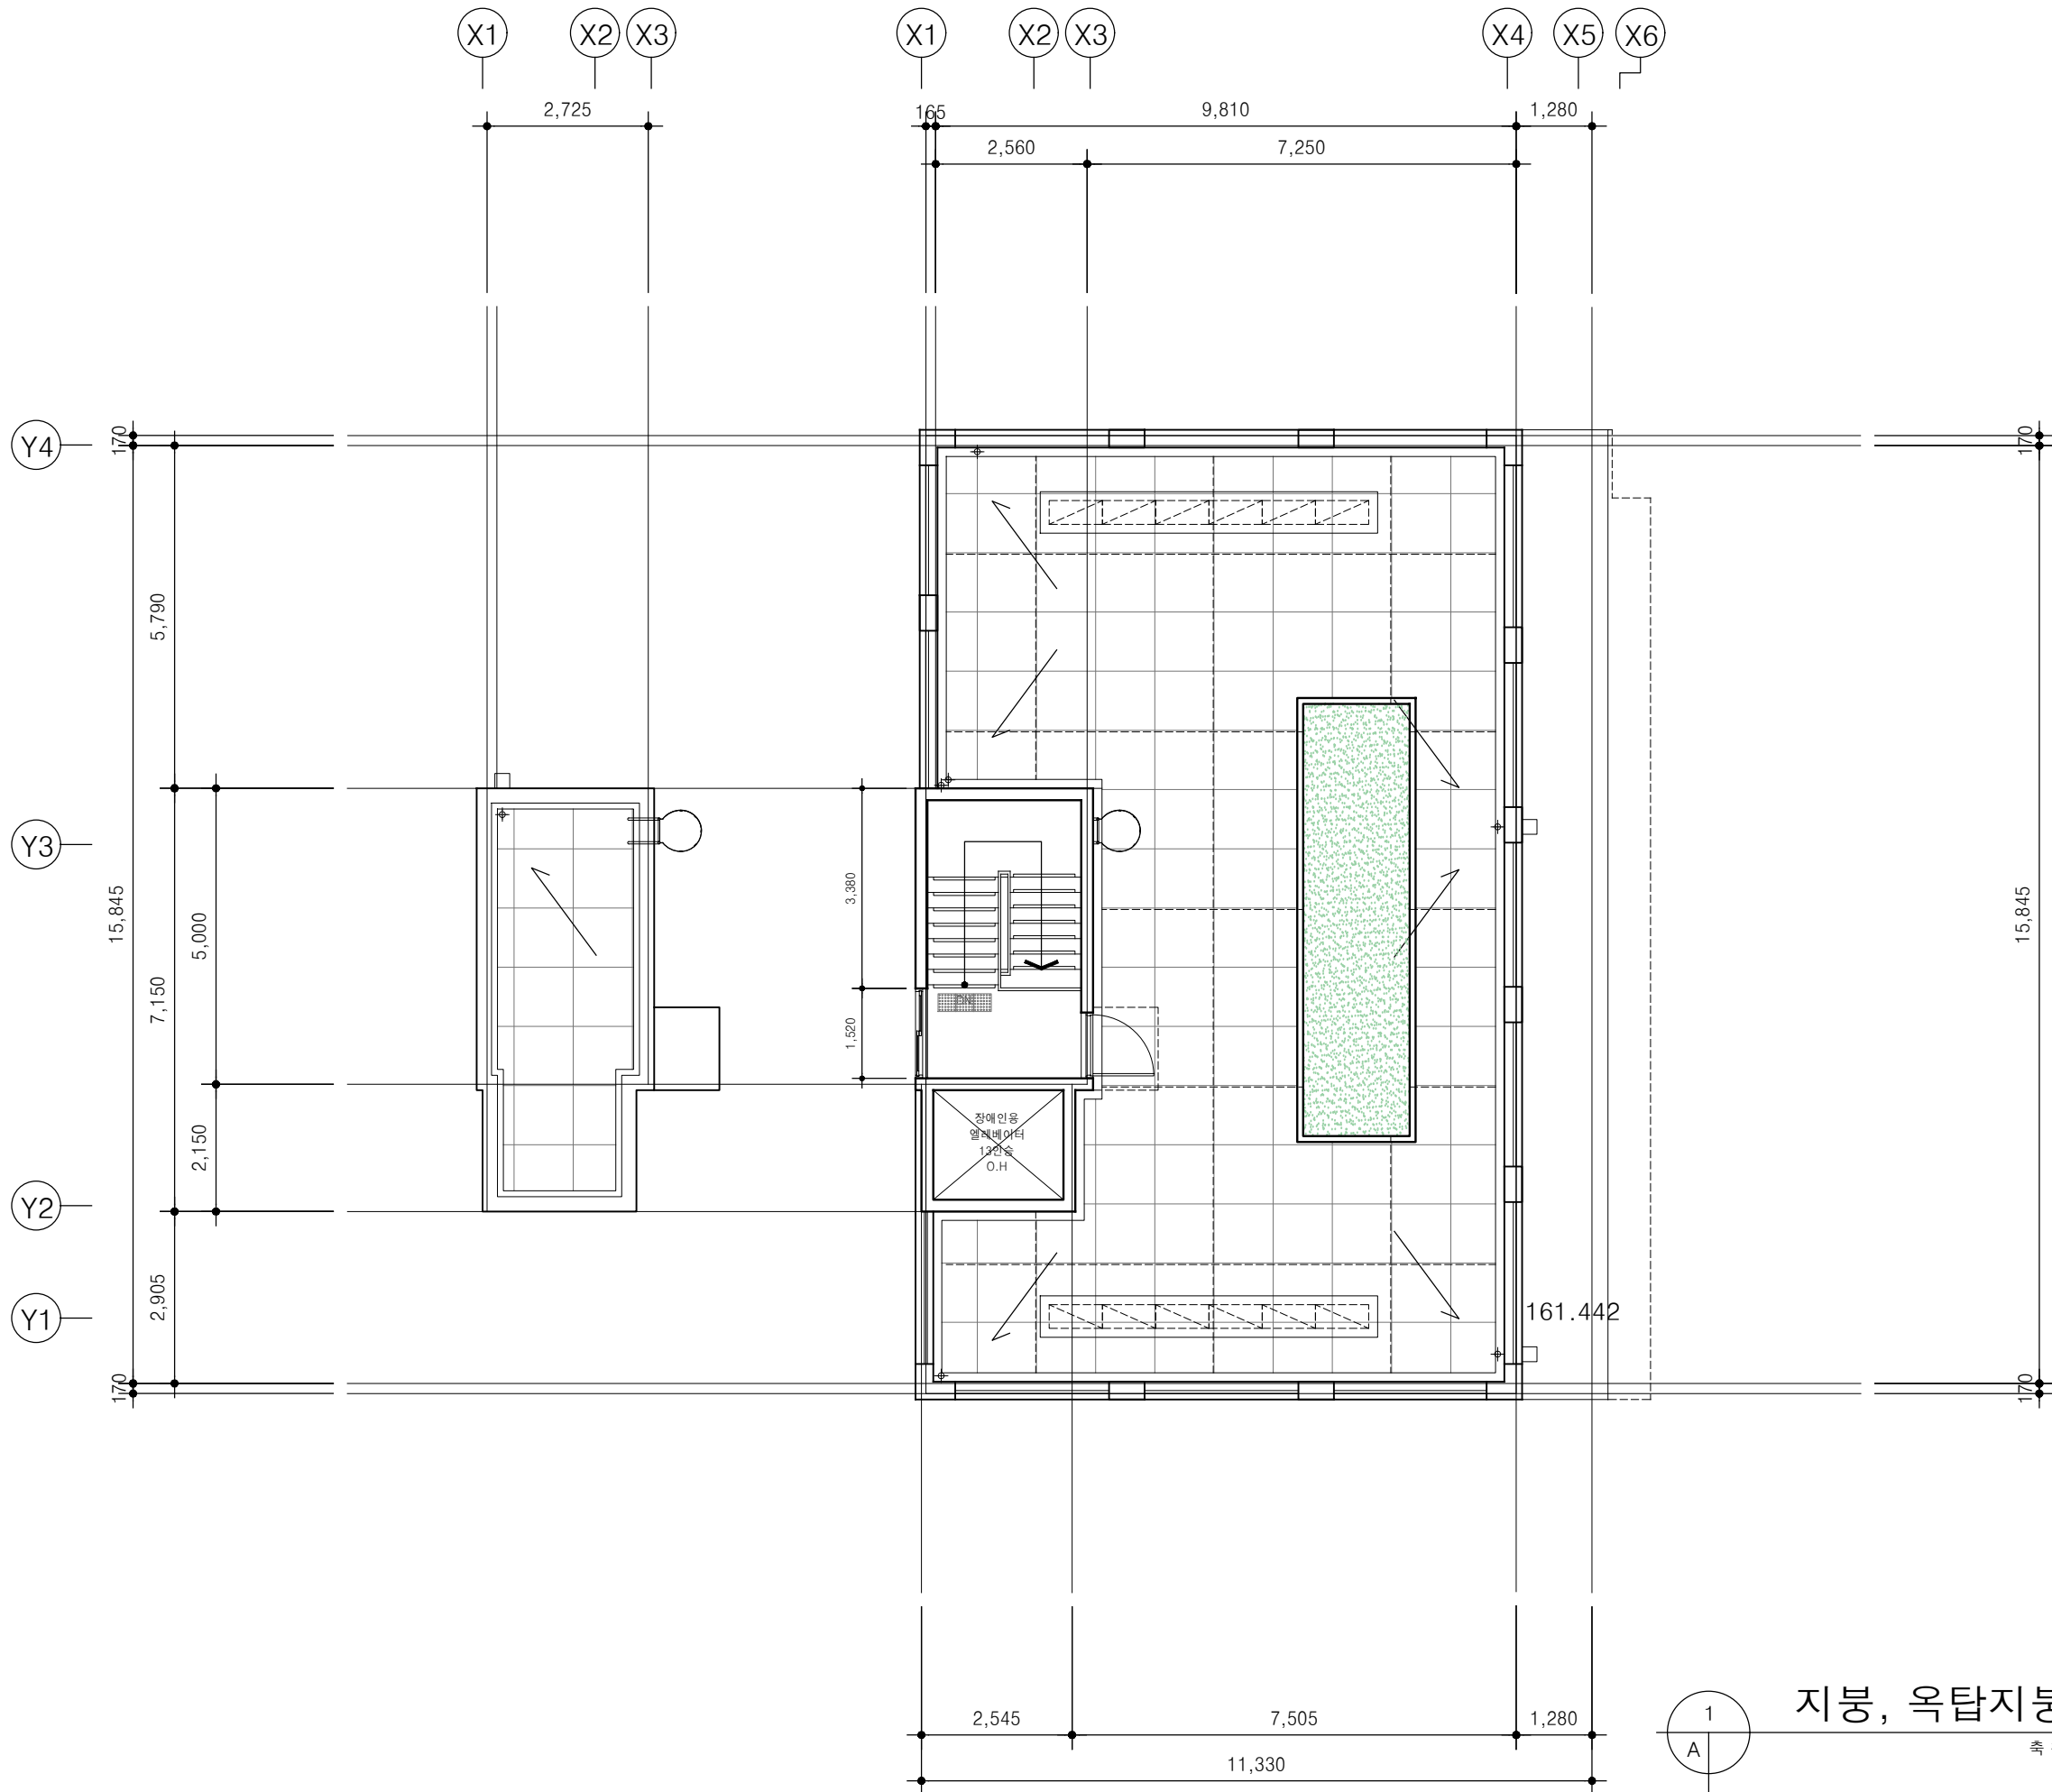

지붕, 옥탑지붕 평면도

축척 : 1 / 120 (A3)

* NOTE

- 내력벽(철근콘크리트)
- 비내력벽(경량벽체)
- 조적벽(0.5B)
- 확장형 발코니

변경사항 REVISION

수정번호	수정내용		
	설계	검토	승인
20	20	20	20
수정번호	수정내용		
	설계	검토	승인
20	20	20	20
수정번호	수정내용		
	설계	검토	승인
20	20	20	20

합동설계 CONSULTANTS

토목	CIVIL ENGINEERING	
구조	CONSTRUCTION	
기계	MECHANICAL EQUIPMENT	
전기	ELECTRICAL EQUIPMENT	
방재	PREVENTION	
조경	LANDSCAPING	

KEY PLAN

설계번호 PROJECT NO.
2024-0502

설계명 PROJECT NAME
화곡동 155-22 도시형생활주택
신축공사

UI 유아이
건축사사무소(주)
06649 서울시 서초구 반포대로24길 42-6 태진빌딩 1층
TEL. 02 6348 1575 FAX. 02 6280 1576
http://www.ui-architects.com

승인 APPROVE

심사 SUBMIT

설계 DRAWN

도면명
지붕, 옥탑지붕 평면도

축척

파일명 FILE NAME

A1

A3 1/120

도면번호 SHEETNO.

A - 000



* NOTE

변경사항 REVISION

수정번호	수정내용		
	설 계	검 토	승 인
20	20	20	20

수정번호	수정내용		
	설 계	검 토	승 인
20	20	20	20

수정번호	수정내용		
	설 계	검 토	승 인
20	20	20	20

합동설계 CONSULTANTS

토목	CIVIL ENGINEERING	
구조	CONSTRUCTION	
기계	MECHANICAL EQUIPMENT	
전기	ELECTRICAL EQUIPMENT	
방재	PREVENTION	
조경	LANDSCAPING	

KEY PLAN

설 계 번 호 PROJECT NO.
2024-0502

설 계 명 PROJECT NAME
화곡동 155-22 도시형생활주택
신축공사

UI 유아이 건축사무소(주)
06649 서울시 서초구 반포대로24길 42-6 태진빌딩 1층
TEL. 02 6348 1575 FAX. 02 6280 1576
http://www.ui-architects.com

승 인 APPROVE	심 사 SUBMIT
설 계 DRAWN	
도면명 동측면도 (정면도)	
축척	파일명 FILE NAME
A1	
A3	1/120

도면번호 SHEETNO.
A - 201



* NOTE

변경사항 REVISION

수정번호

설 계

검 토

승 인

20

20

20

수정번호

수정내용

설 계

검 토

승 인

20

20

20

수정번호

수정내용

설 계

검 토

승 인

20

20

20

합동설계 CONSULTANTS

토목 CIVIL - ENGINEERING

구조 CONSTRUCTION

기계 MECHANICAL EQUIPMENT

전기 ELECTRICAL EQUIPMENT

방재 PREVENTION

조경 LANDSCAPING

KEY PLAN

설 계 번 호 PROJECT NO.

2024-0502

설 계 명 PROJECT NAME

화곡동 155-22 도시형생활주택 신축공사

유아이 건축사사무소(주)

06649 서울시 서초구 반포대로24길 42-6 태진빌딩 1층

TEL. 02 6348 1575 FAX. 02 6280 1576

http://www.ui-architects.com

승 인 APPROVE

심 사 SUBMIT

설 계 DRAWN

도면명

북측면도 (우측면도)

축척

파일명 FILE NAME


A1

A3

1/120

도면번호 SHEETNO.

A - 202

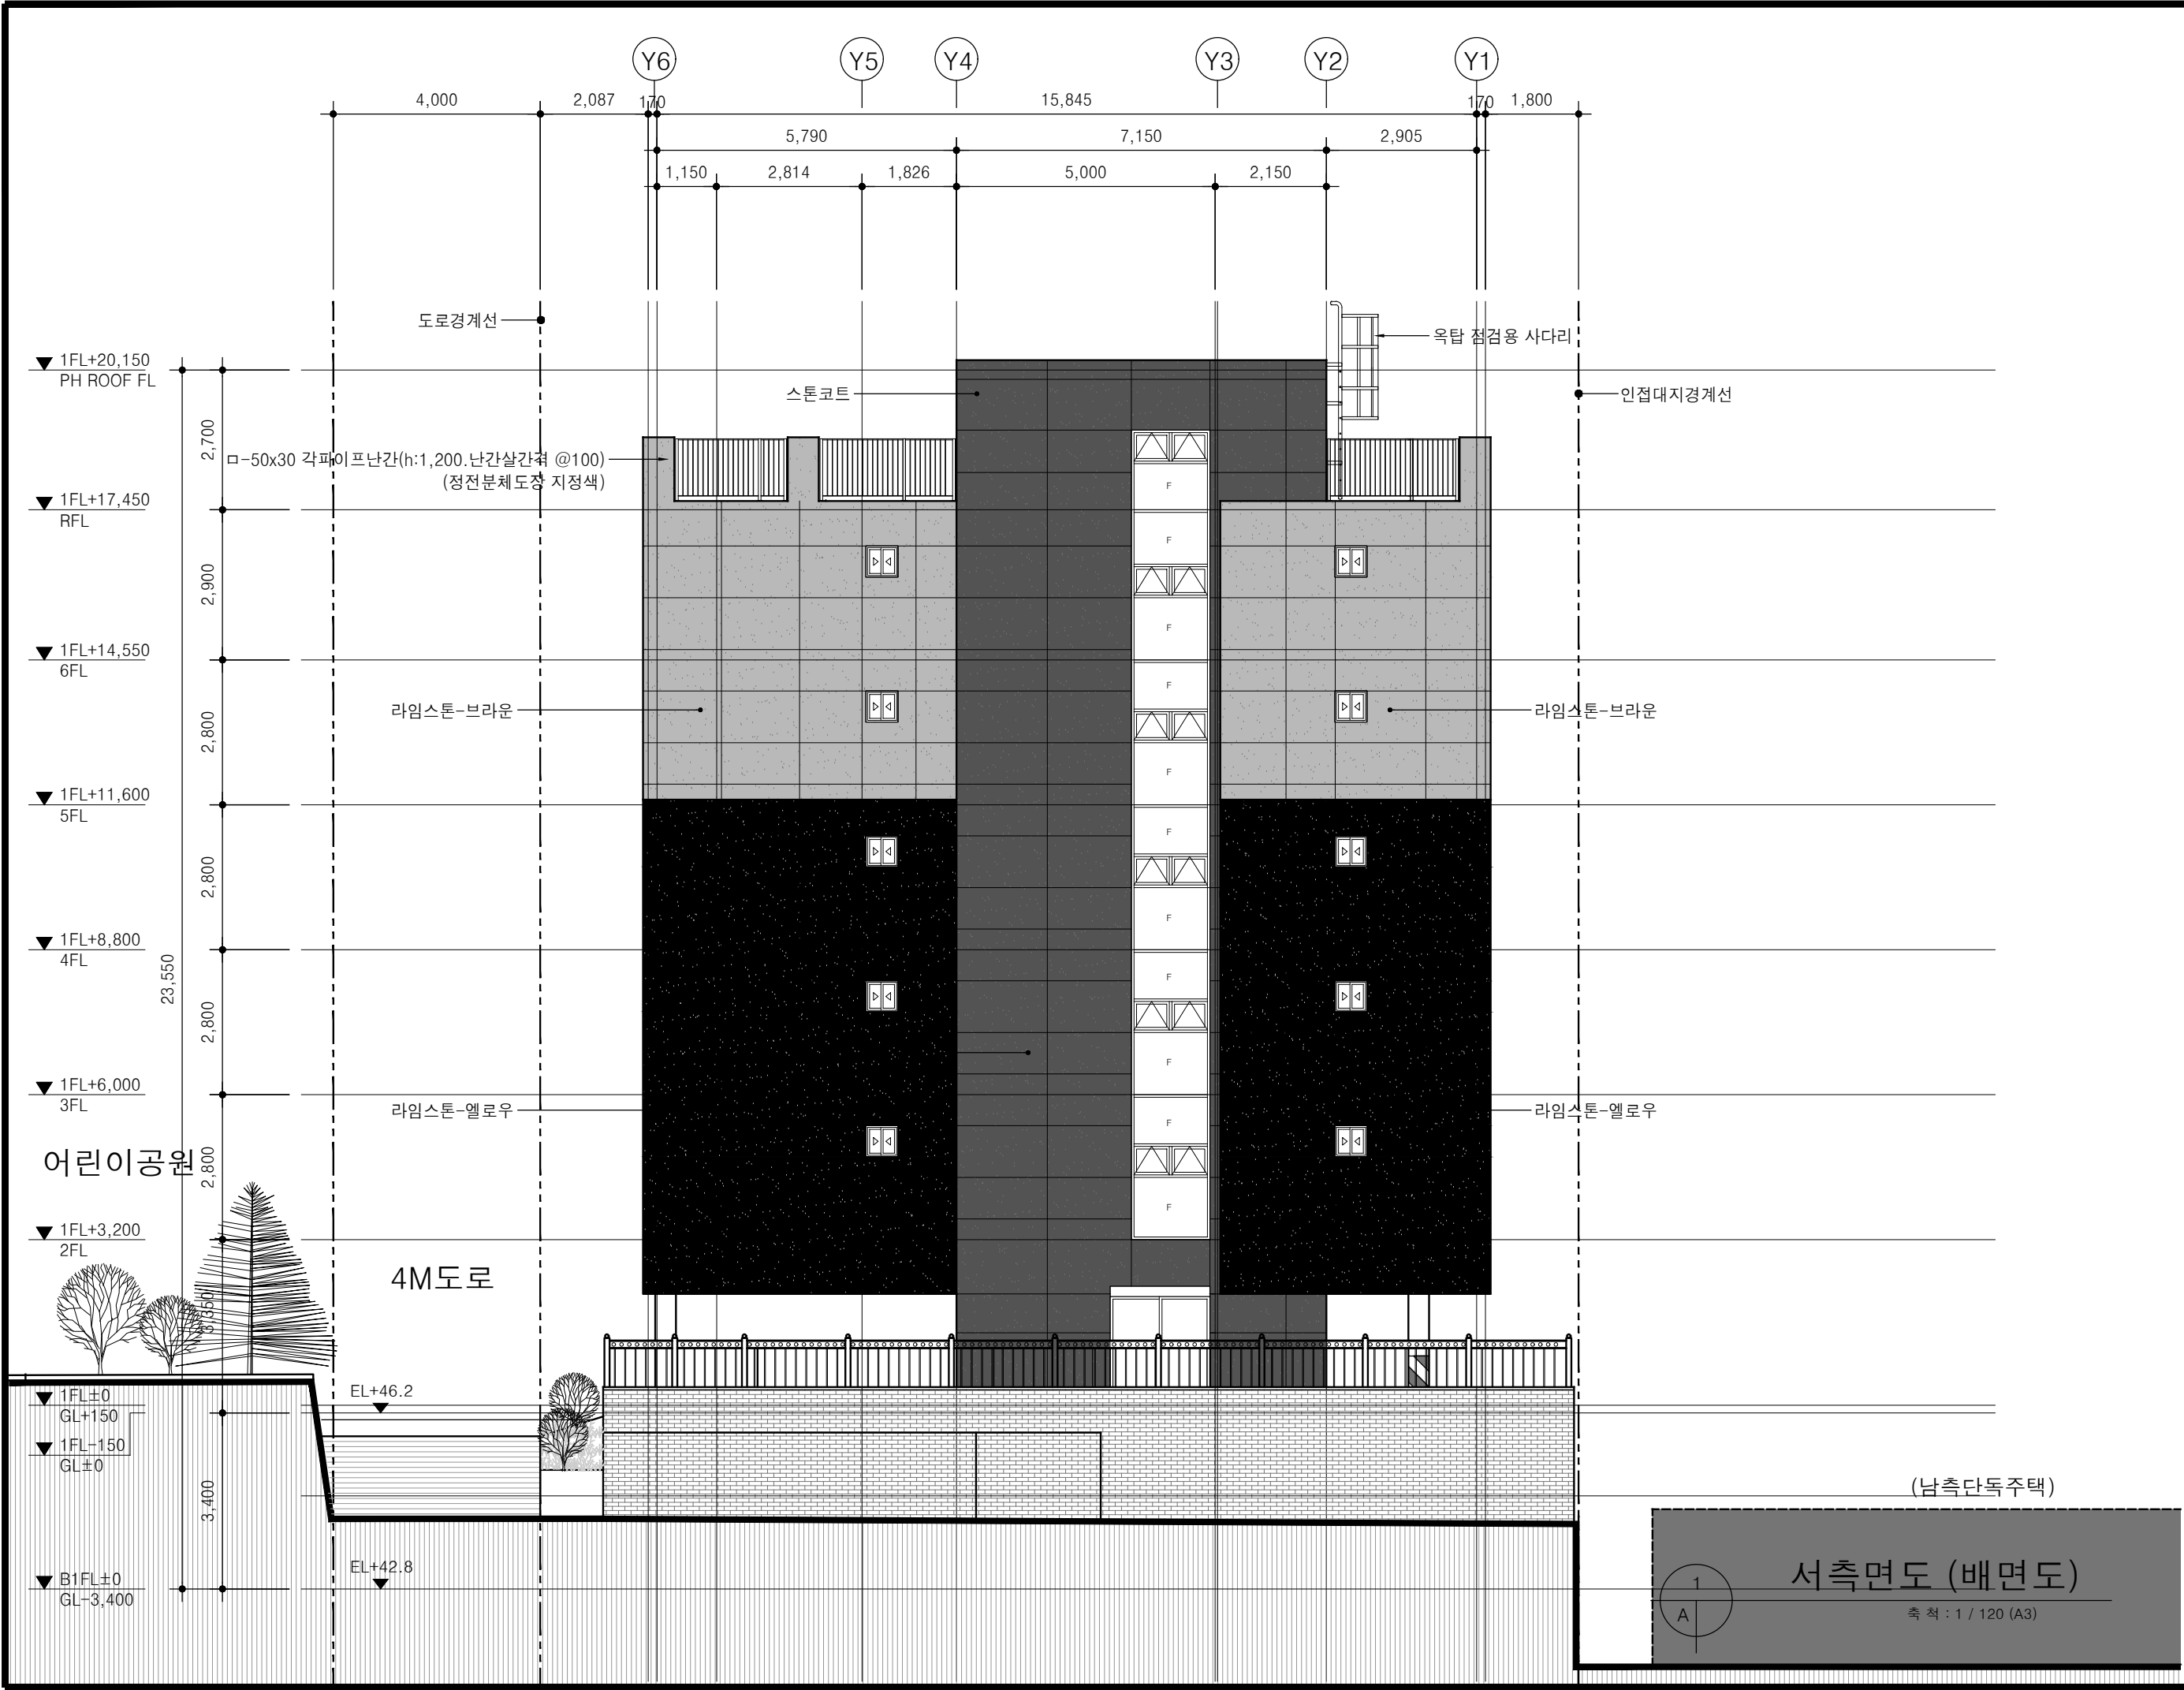

* NOTE

변경사항 REVISION

수정번호	수정내용		
	설 계	검 토	승 인
20	20	20	20

수정번호

수정내용		
설 계	검 토	승 인
20	20	20

수정번호

수정내용		
설 계	검 토	승 인
20	20	20

합동설계 CONSULTANTS

토목 CIVIL ENGINEERING	
구조 CONSTRUCTION	
기계 MECHANICAL EQUIPMENT	
전기 ELECTRICAL EQUIPMENT	
방재 PREVENTION	
조경 LANDSCAPING	

KEY PLAN

설 계 번 호 PROJECT NO.
2024-0502

설 계 명 PROJECT NAME
화곡동 155-22 도시형생활주택
신축공사

UI

유아이 건축사사무소(주)


06649 서울시 서초구 반포대로24길 42-6 태진빌딩 1층
TEL. 02 6348 1575 FAX. 02 6280 1576
http://www.ui-architects.com

승 인 APPROVE	심 사 SUBMIT
설 계 DRAWN	
도면명 서측면도 (배면도)	
축척	파일명 FILE NAME
A1	
A3	1/120
도면번호 SHEETNO. A - 203	

(남측단독주택)

서측면도 (배면도)

축척 : 1 / 120 (A3)

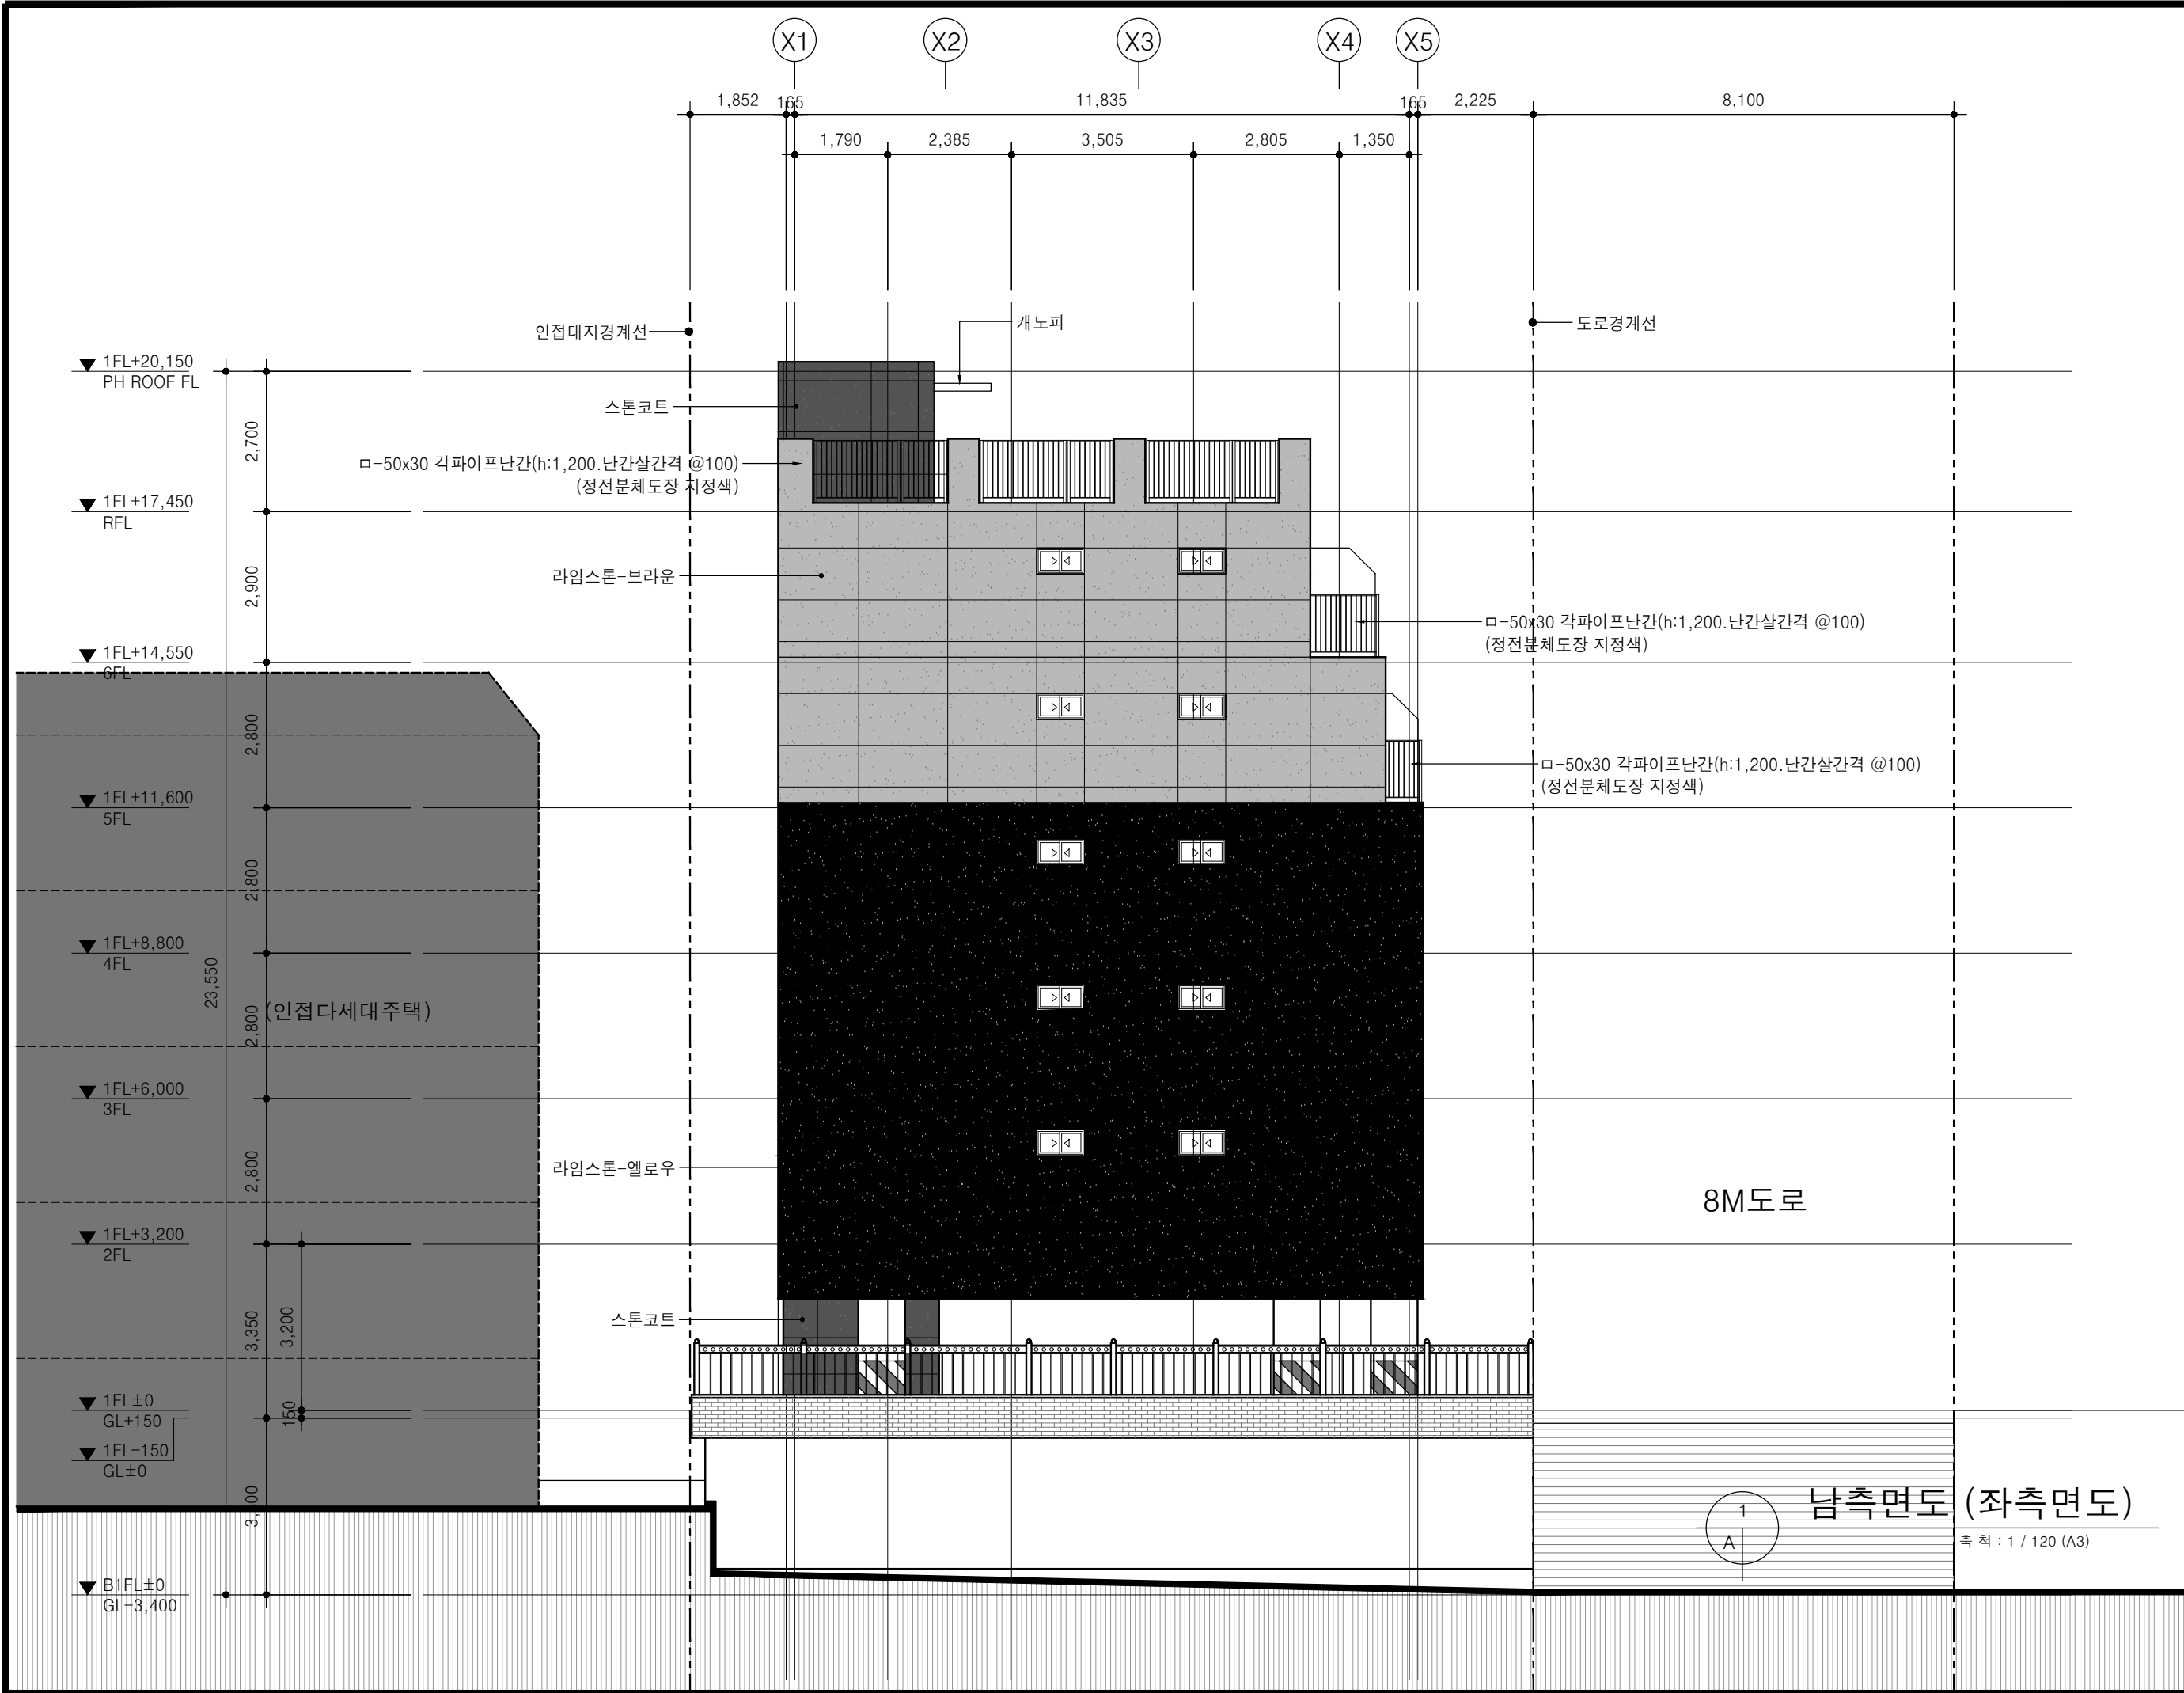

* NOTE

변경사항 REVISION

수정번호	수정내용		
	설 계	검 토	승 인
20		20	20
수정번호	수정내용		
	설 계	검 토	승 인
20		20	20
수정번호	수정내용		
	설 계	검 토	승 인
20		20	20

합동설계 CONSULTANTS

토목	CIVIL - ENGINEERING	
구조	CONSTRUCTION	
기계	MECHANICAL EQUIPMENT	
전기	ELECTRICAL EQUIPMENT	
방재	PREVENTION	
조경	LANDSCAPING	

KEY PLAN

설 계 번 호 PROJECT NO.
2024-0502

설 계 명 PROJECT NAME
화곡동 155-22 도시형생활주택
신축공사

UI 유아이 건축사사무소(주)
06649 서울시 서초구 반포대로24길 42-6 태진빌딩 1층
TEL. 02 6348 1575 FAX. 02 6280 1576
http://www.ui-architects.com

승 인 APPROVE

심 사 SUBMIT

설 계 DRAWN

도면명 남측면도 (좌측면도)

축척

파일명 FILE NAME



A1
A3 1/120

도면번호 SHEETNO.

A - 204

거실-상부발코니 단열재 반영

1. 각층 거실과 상부발코니 (외기직접.간접)사이 단열재
--> T15진공단열재(불연.열전도율 0.00181)
2. 각층 발코니(간접)와 상부발코니 (외기직접.간접)사이 단열재
--> T15진공단열재(불연.열전도율 0.00181)

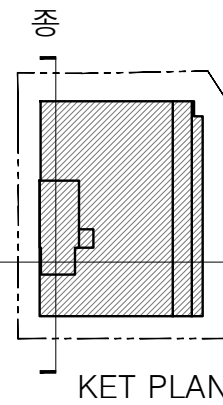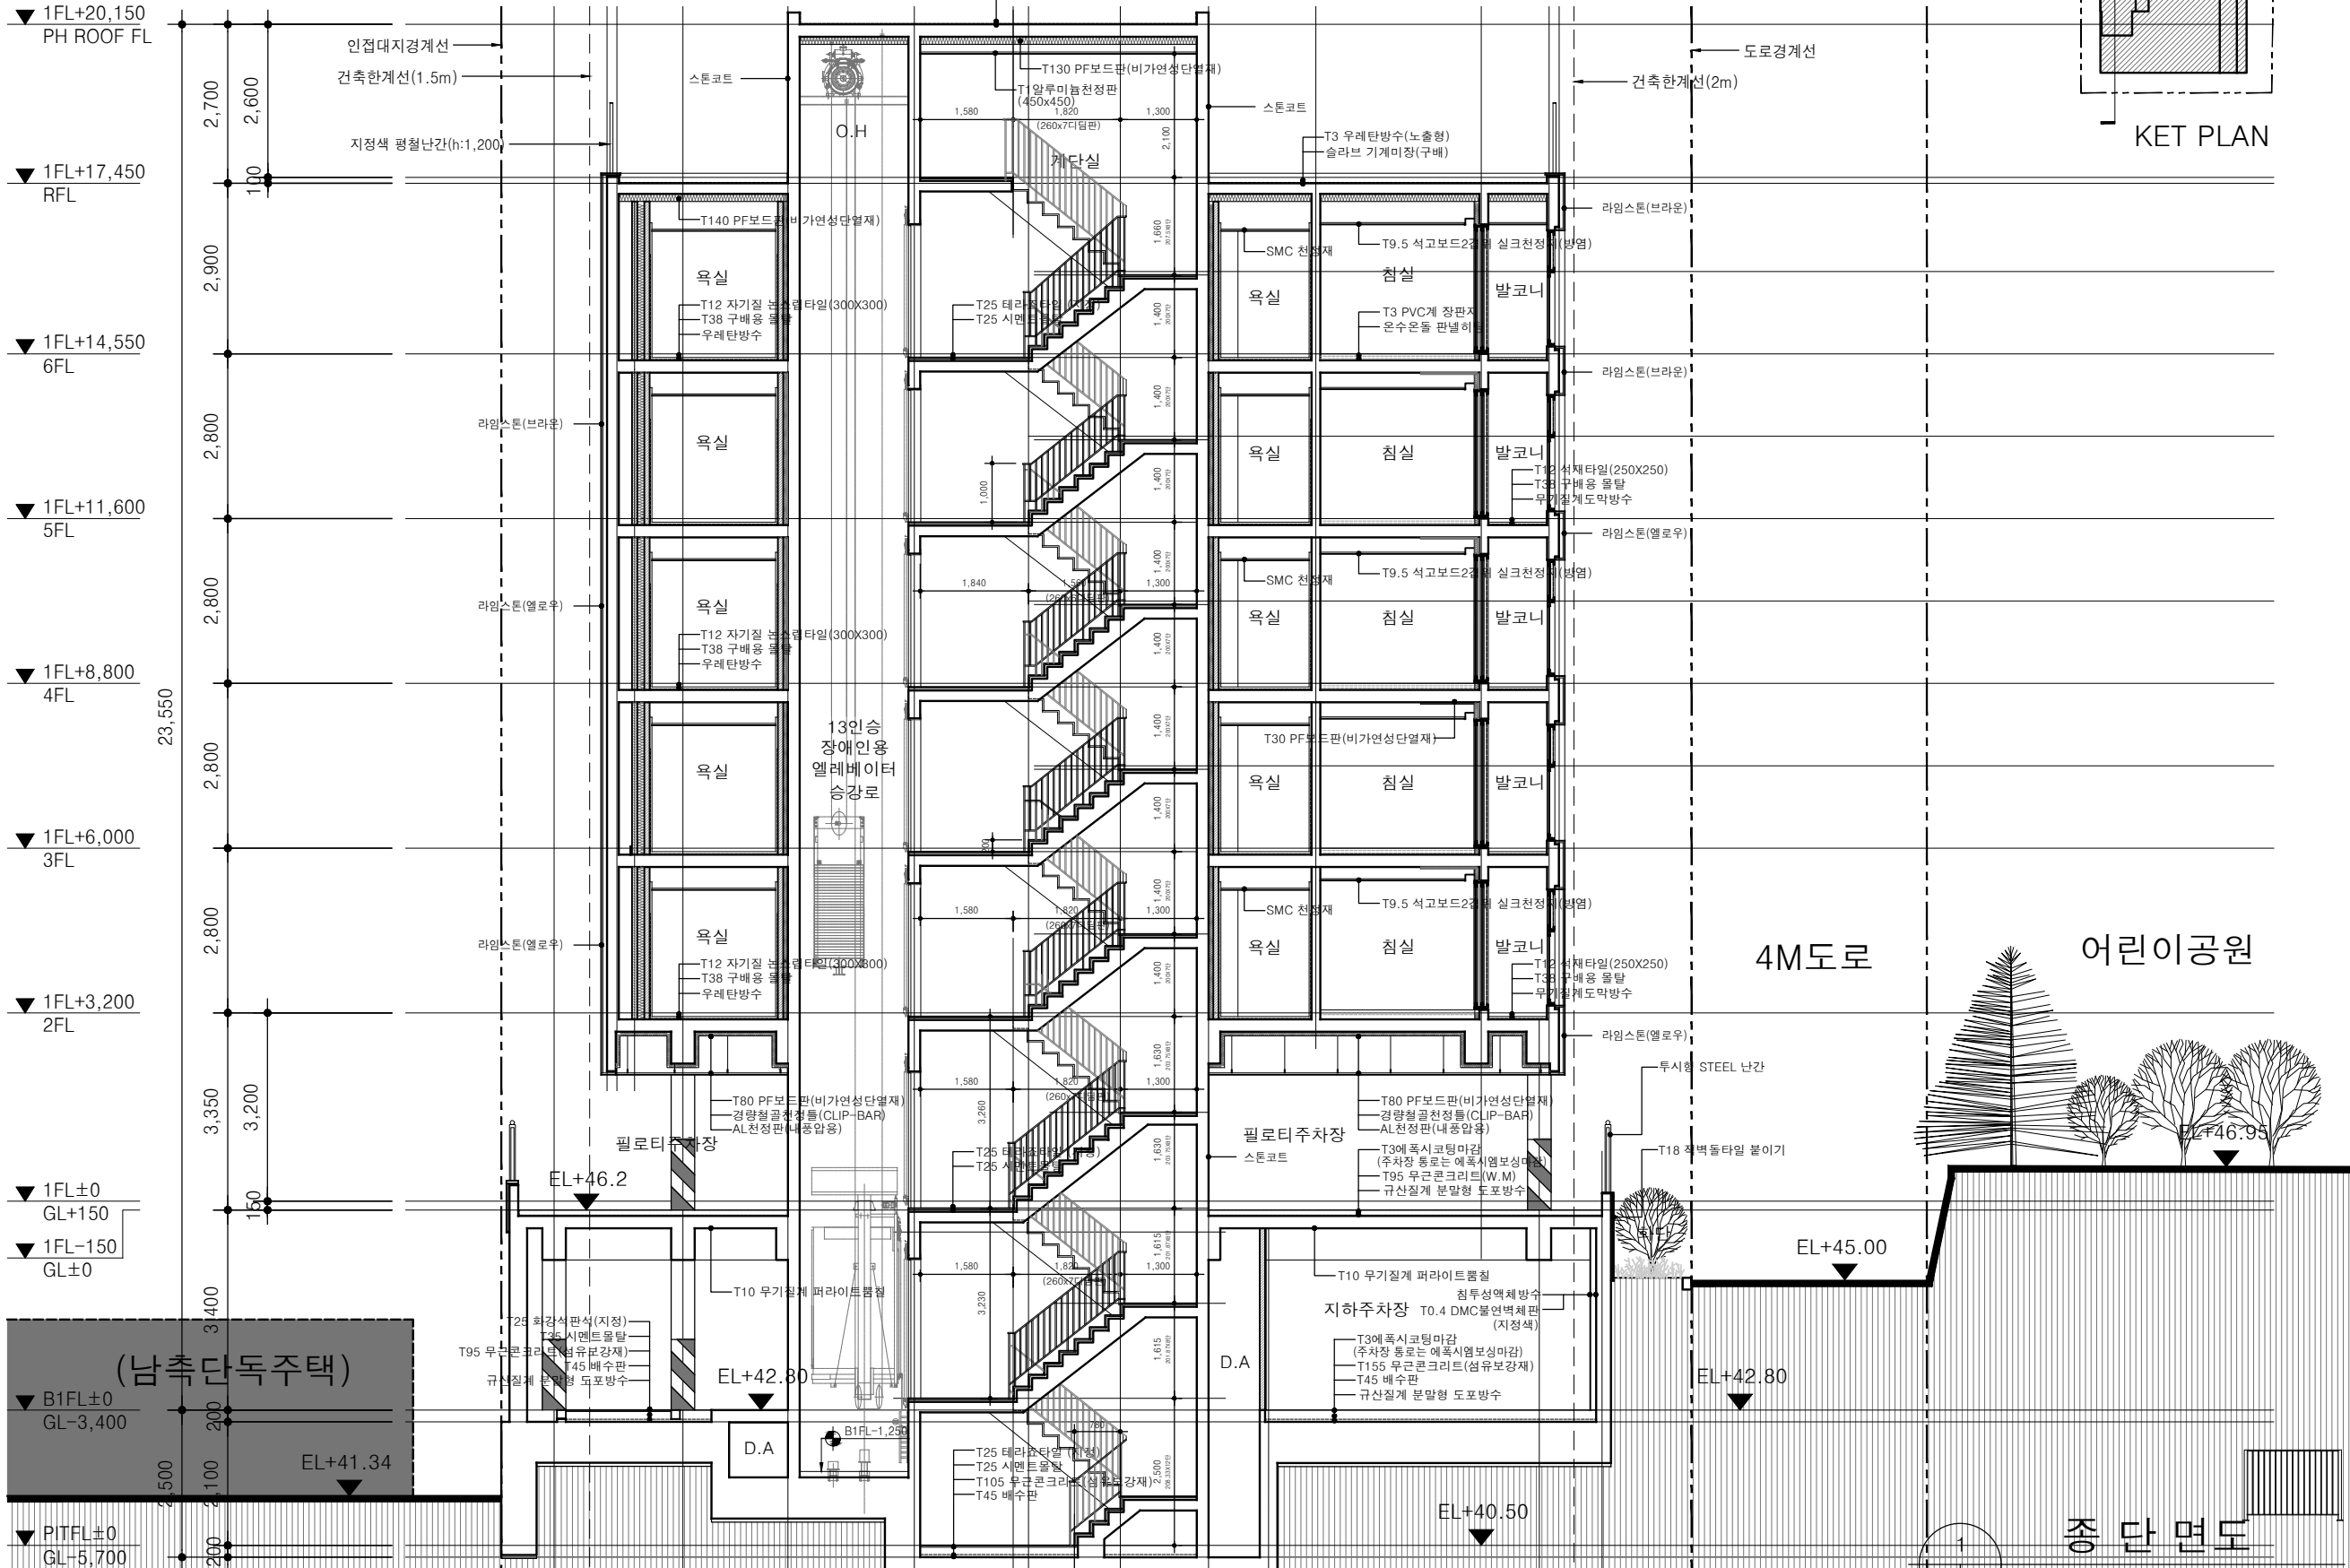

* NOTE

변경사항 REVISION

수정번호	수정내용
1	설계
2	검토
3	승인

합동설계 CONSULTANTS

구분	내용
토목	CIVIL ENGINEERING
구조	CONSTRUCTION
기계	MECHANICAL EQUIPMENT
전기	ELECTRICAL EQUIPMENT
방재	PREVENTION
조경	LANDSCAPING

KEY PLAN

설 계 번 호 PROJECT NO.
2024-0502

설 계 명 PROJECT NAME
화곡동 155-22 도시형생활주택
신축공사

유아이 건축사사무소(주)
06649 서울시 서초구 반포대로24길 42-6 태진빌딩 1층
TEL. 02 6348 1575 FAX. 02 6280 1576
http://www.ui-architects.com

승 인 APPROVE

심 사 SUBMIT

설 계 DRAWN

도 면 명

중 단 면도

축척 1 / 120 (A3)

도면번호 SHEET NO.
A - 301

거실-상부발코니 단열재 반영

1. 각층 거실과 상부발코니 (외기직접.간접)사이 단열재
--> T15진공단열재(불연.열전도율 0.00181)
2. 각층 발코니(간접)와 상부발코니 (외기직접.간접)사이 단열재
--> T15진공단열재(불연.열전도율 0.00181)

▼ 1FL+20,150
PH ROOF FL

▼ 1FL+17,450
RFL

▼ 1FL+14,550
6FL

▼ 1FL+11,600
5FL

▼ 1FL+8,800
4FL

▼ 1FL+6,000
3FL


▼ 1FL+3,200
2FL

▼ 1FL±0
GL+150

▼ 1FL-150
GL±0

▼ B1FL±0
GL-3,400

▼ PITFL±0
GL-5,700

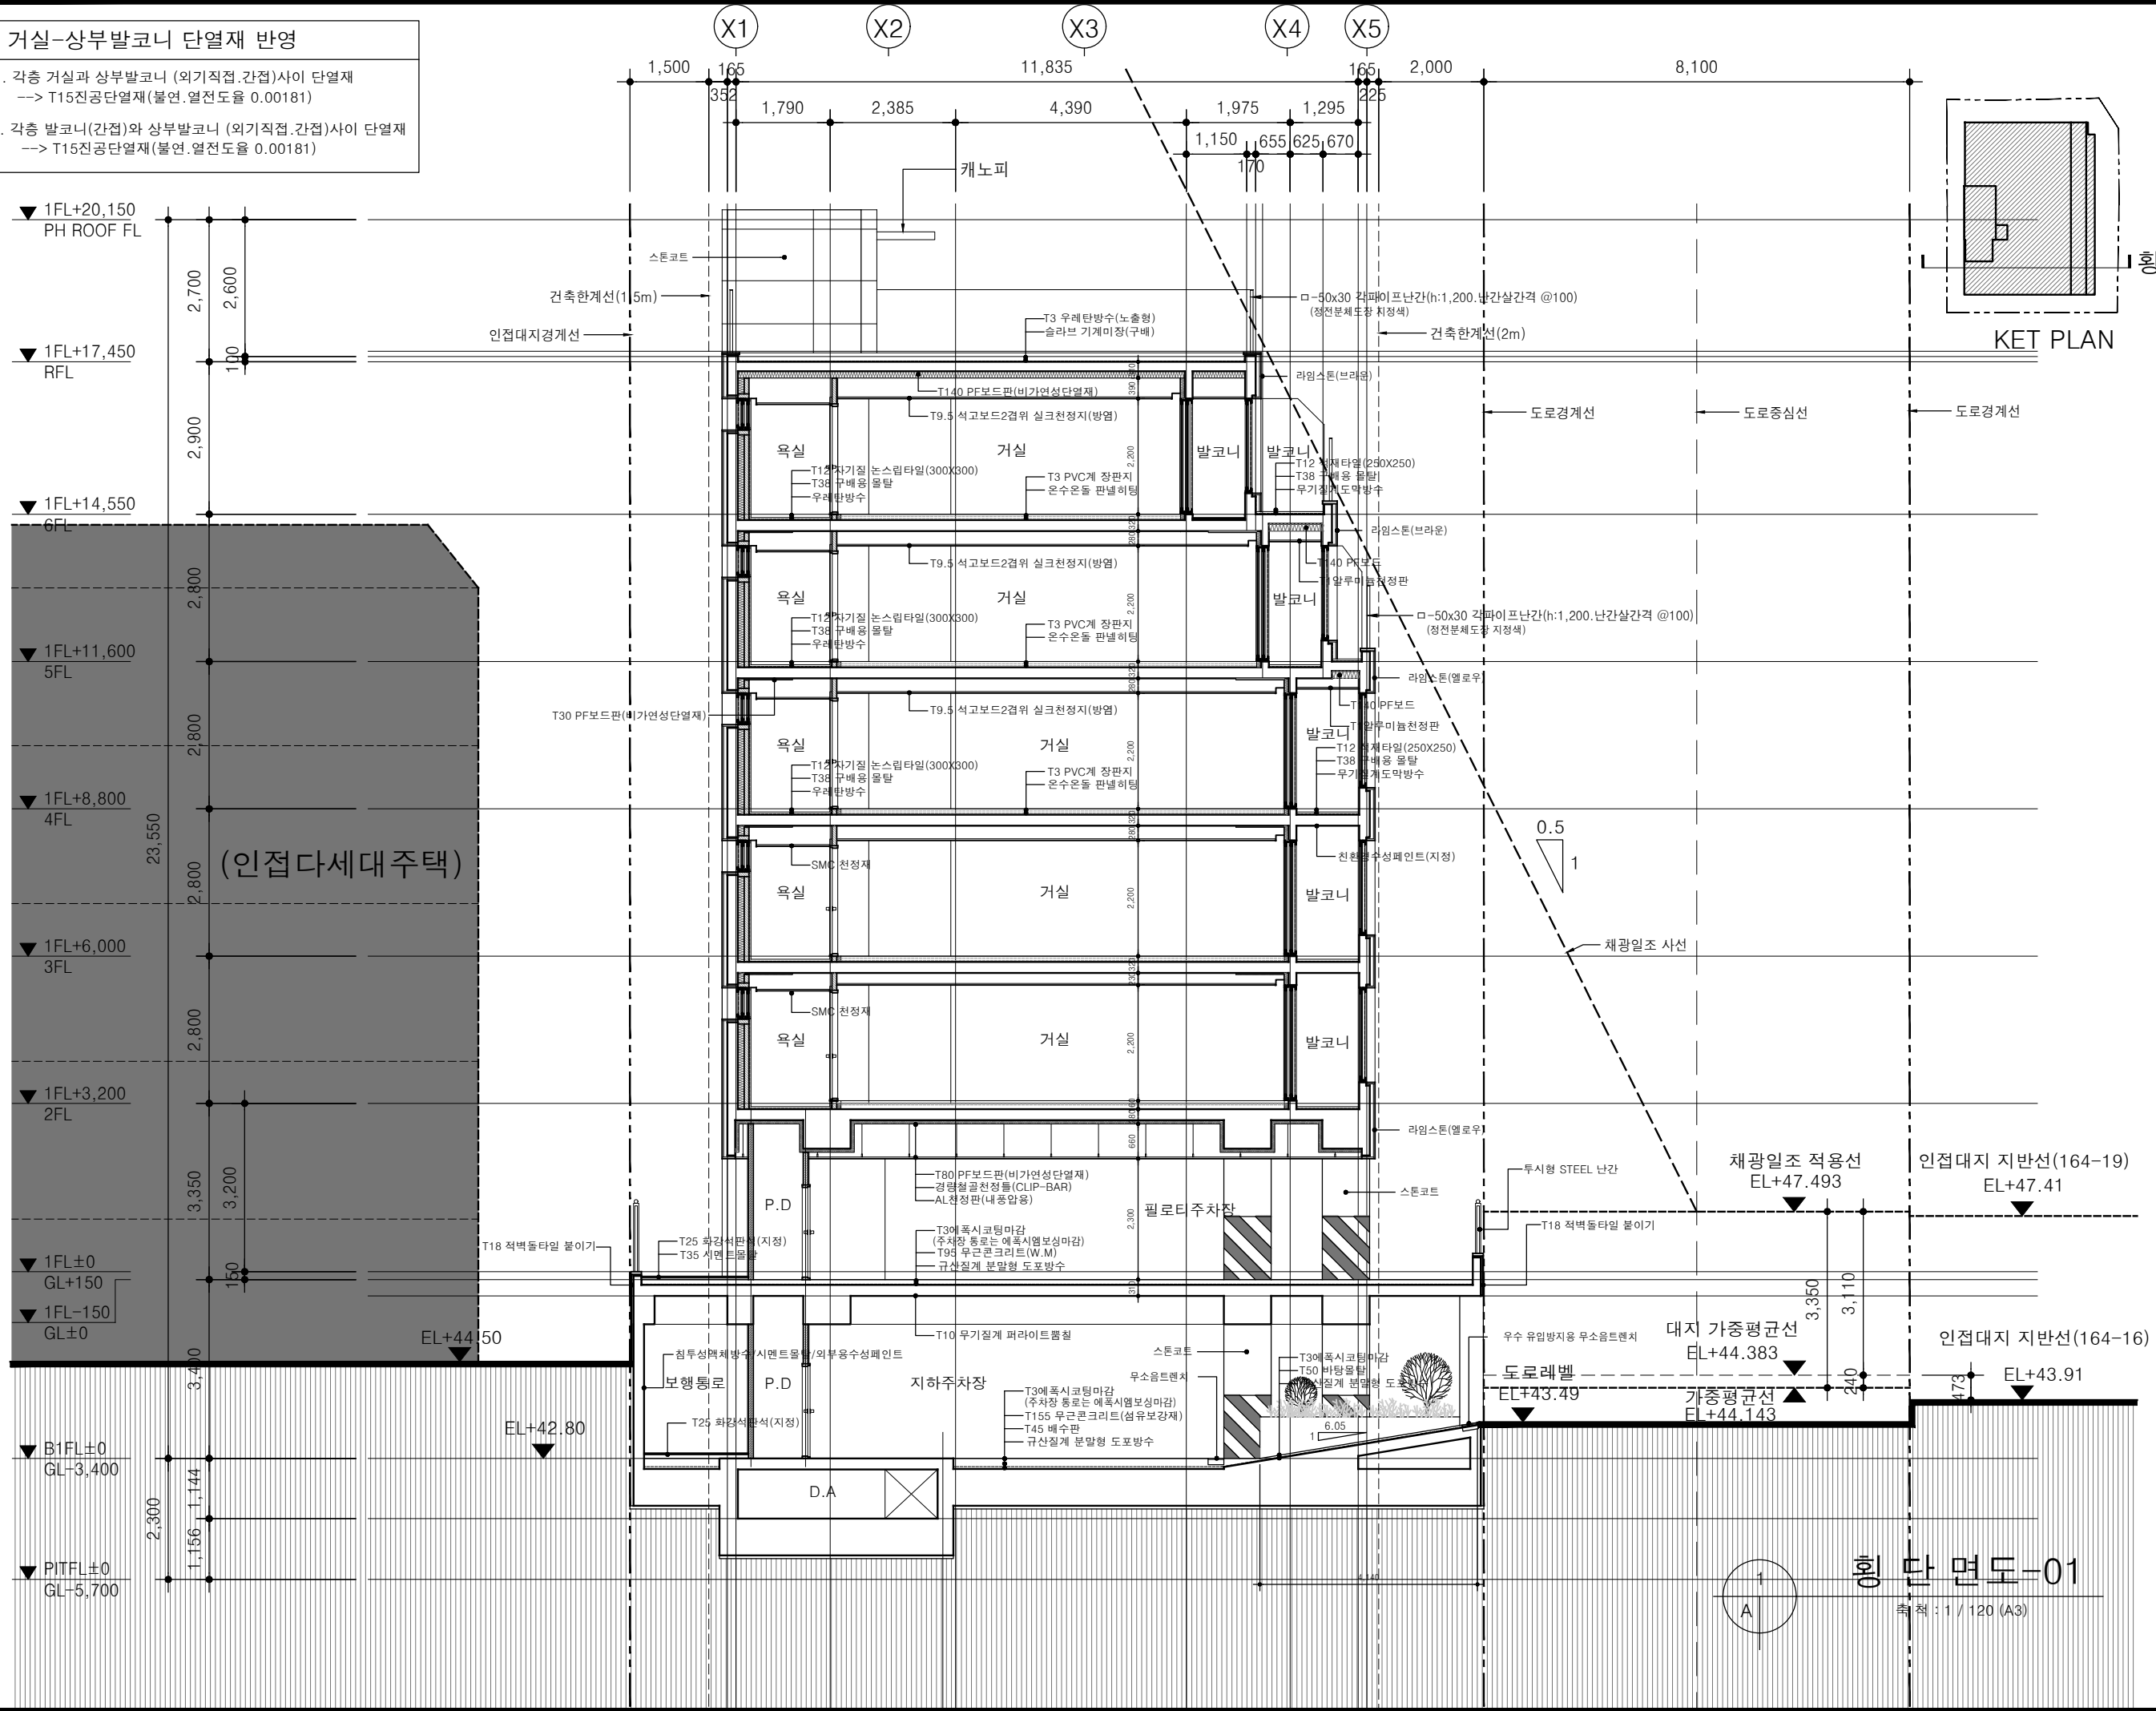

* NOTE

변경사항 REVISION

수정번호	수정내용		
	설 계	검 토	승 인
20	...	20	...
20	...	20	...
20	...	20	...

합동설계 CONSULTANTS

토목	CIVIL ENGINEERING	
구조	CONSTRUCTION	
기계	MECHANICAL EQUIPMENT	
전기	ELECTRICAL EQUIPMENT	
방재	PREVENTION	
조경	LANDSCAPING	

KEY PLAN

설 계 번 호 PROJECT NO.

2024-0502

설 계 명 PROJECT NAME

화곡동 155-22 도시형생활주택
신축공사

UI 유아이
건축사사무소(주)
06649 서울시 서초구 반포대로24길 42-6 태진빌딩 1층
TEL. 02 6348 1575 FAX. 02 6280 1576
http://www.ui-architects.com

승 인 APPROVE

심 사 SUBMIT

설 계 DRAWN

도 면 명
형 단 면도-01

축 척
A1

파일명 FILE NAME

A3
1/120

도면번호 SHEETNO.

A - 302


형 단 면도-01

축 척 : 1 / 120 (A3)

거실-상부발코니 단열재 반영

1. 각층 거실과 상부발코니 (외기직접.간접)사이 단열재
--> T15진공단열재(불연.열전도율 0.00181)

2. 각층 발코니(간접)와 상부발코니 (외기직접.간접)사이 단열재
--> T15진공단열재(불연.열전도율 0.00181)

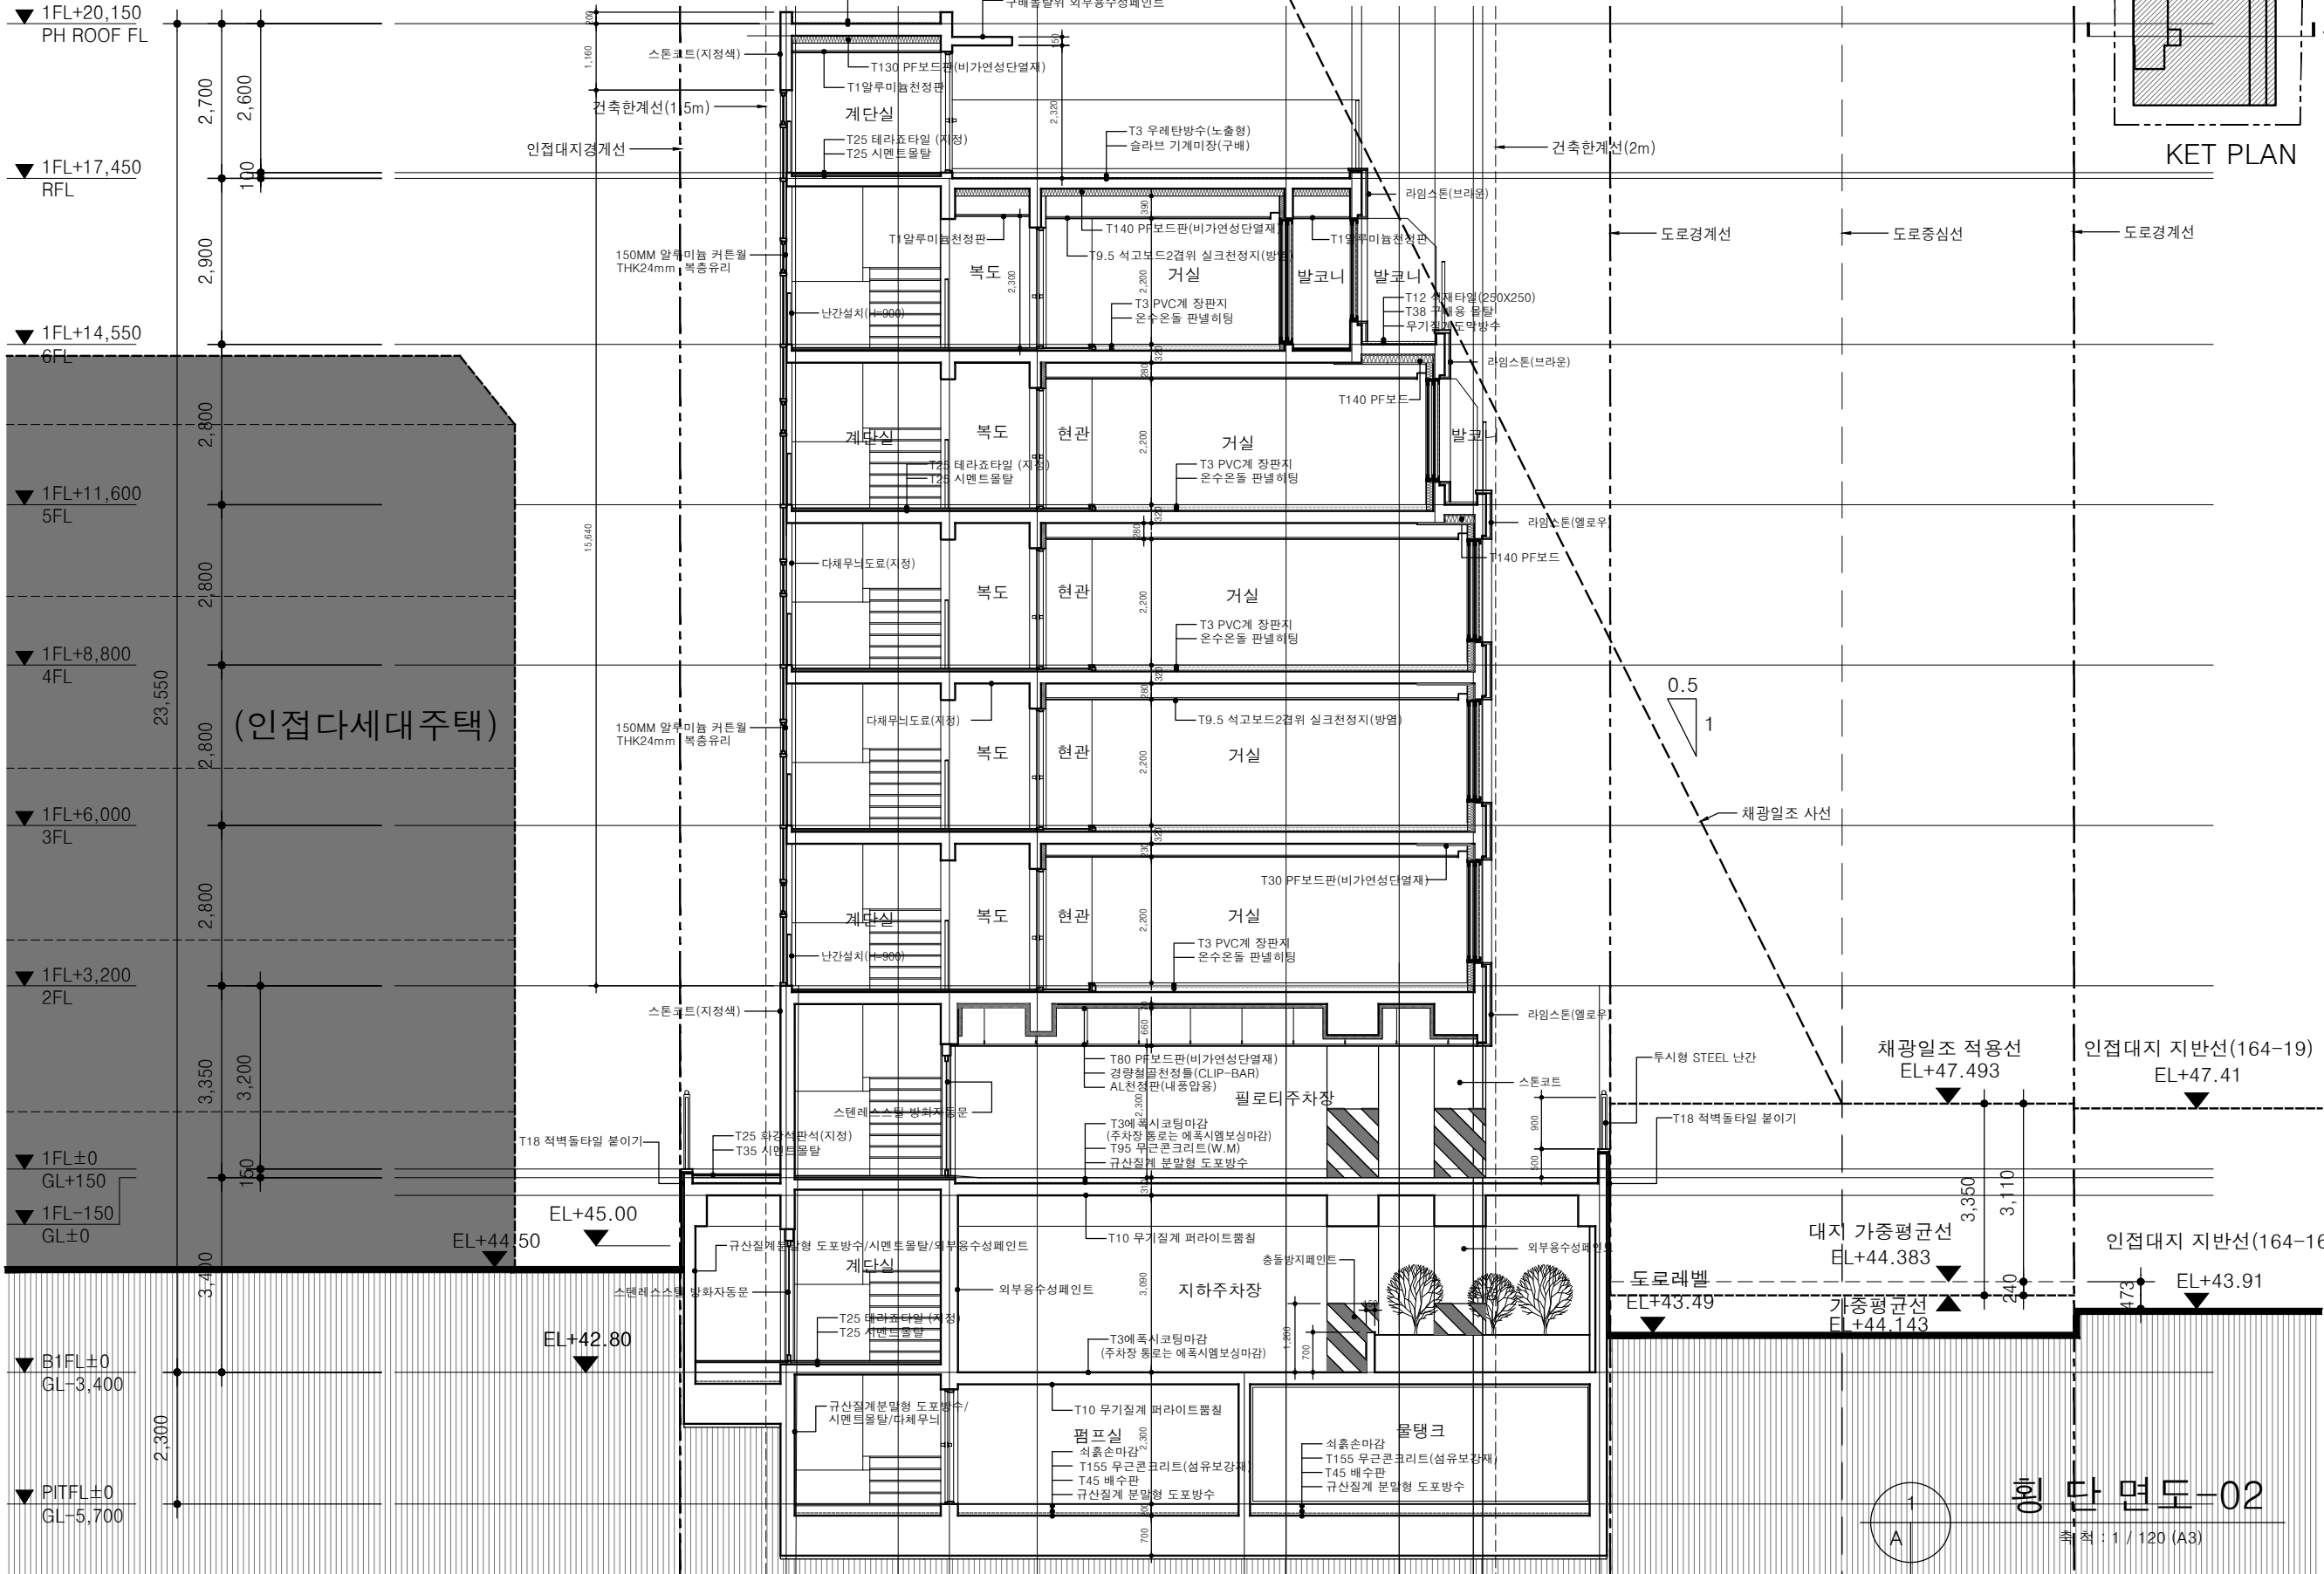

* NOTE

변경사항 REVISION

수정번호	수정내용
1	설계
2	검토
3	승인

수정번호

수정번호	수정내용
1	설계
2	검토
3	승인

수정번호

수정번호	수정내용
1	설계
2	검토
3	승인

합동설계 CONSULTANTS

구분	내용
토목	CIVIL ENGINEERING
구조	CONSTRUCTION
기계	MECHANICAL EQUIPMENT
전기	ELECTRICAL EQUIPMENT
방재	PREVENTION
조경	LANDSCAPING

KEY PLAN

설계번호 PROJECT NO.

2024-0502

설계명 PROJECT NAME

화곡동 155-22 도시형생활주택 신축공사

UI 유아이 건축사사무소(주)

06649 서울시 서초구 반포대로24길 42-6 태진빌딩 1층
TEL. 02 6348 1575 FAX. 02 6280 1576
http://www.ui-architects.com

승인 APPROVE

심사 SUBMIT

설계 DRAWN

도면명

횡단면도-02

축척

파일명 FILE NAME

A1

A3

1/120

도면번호 SHEETNO.

A - 303