

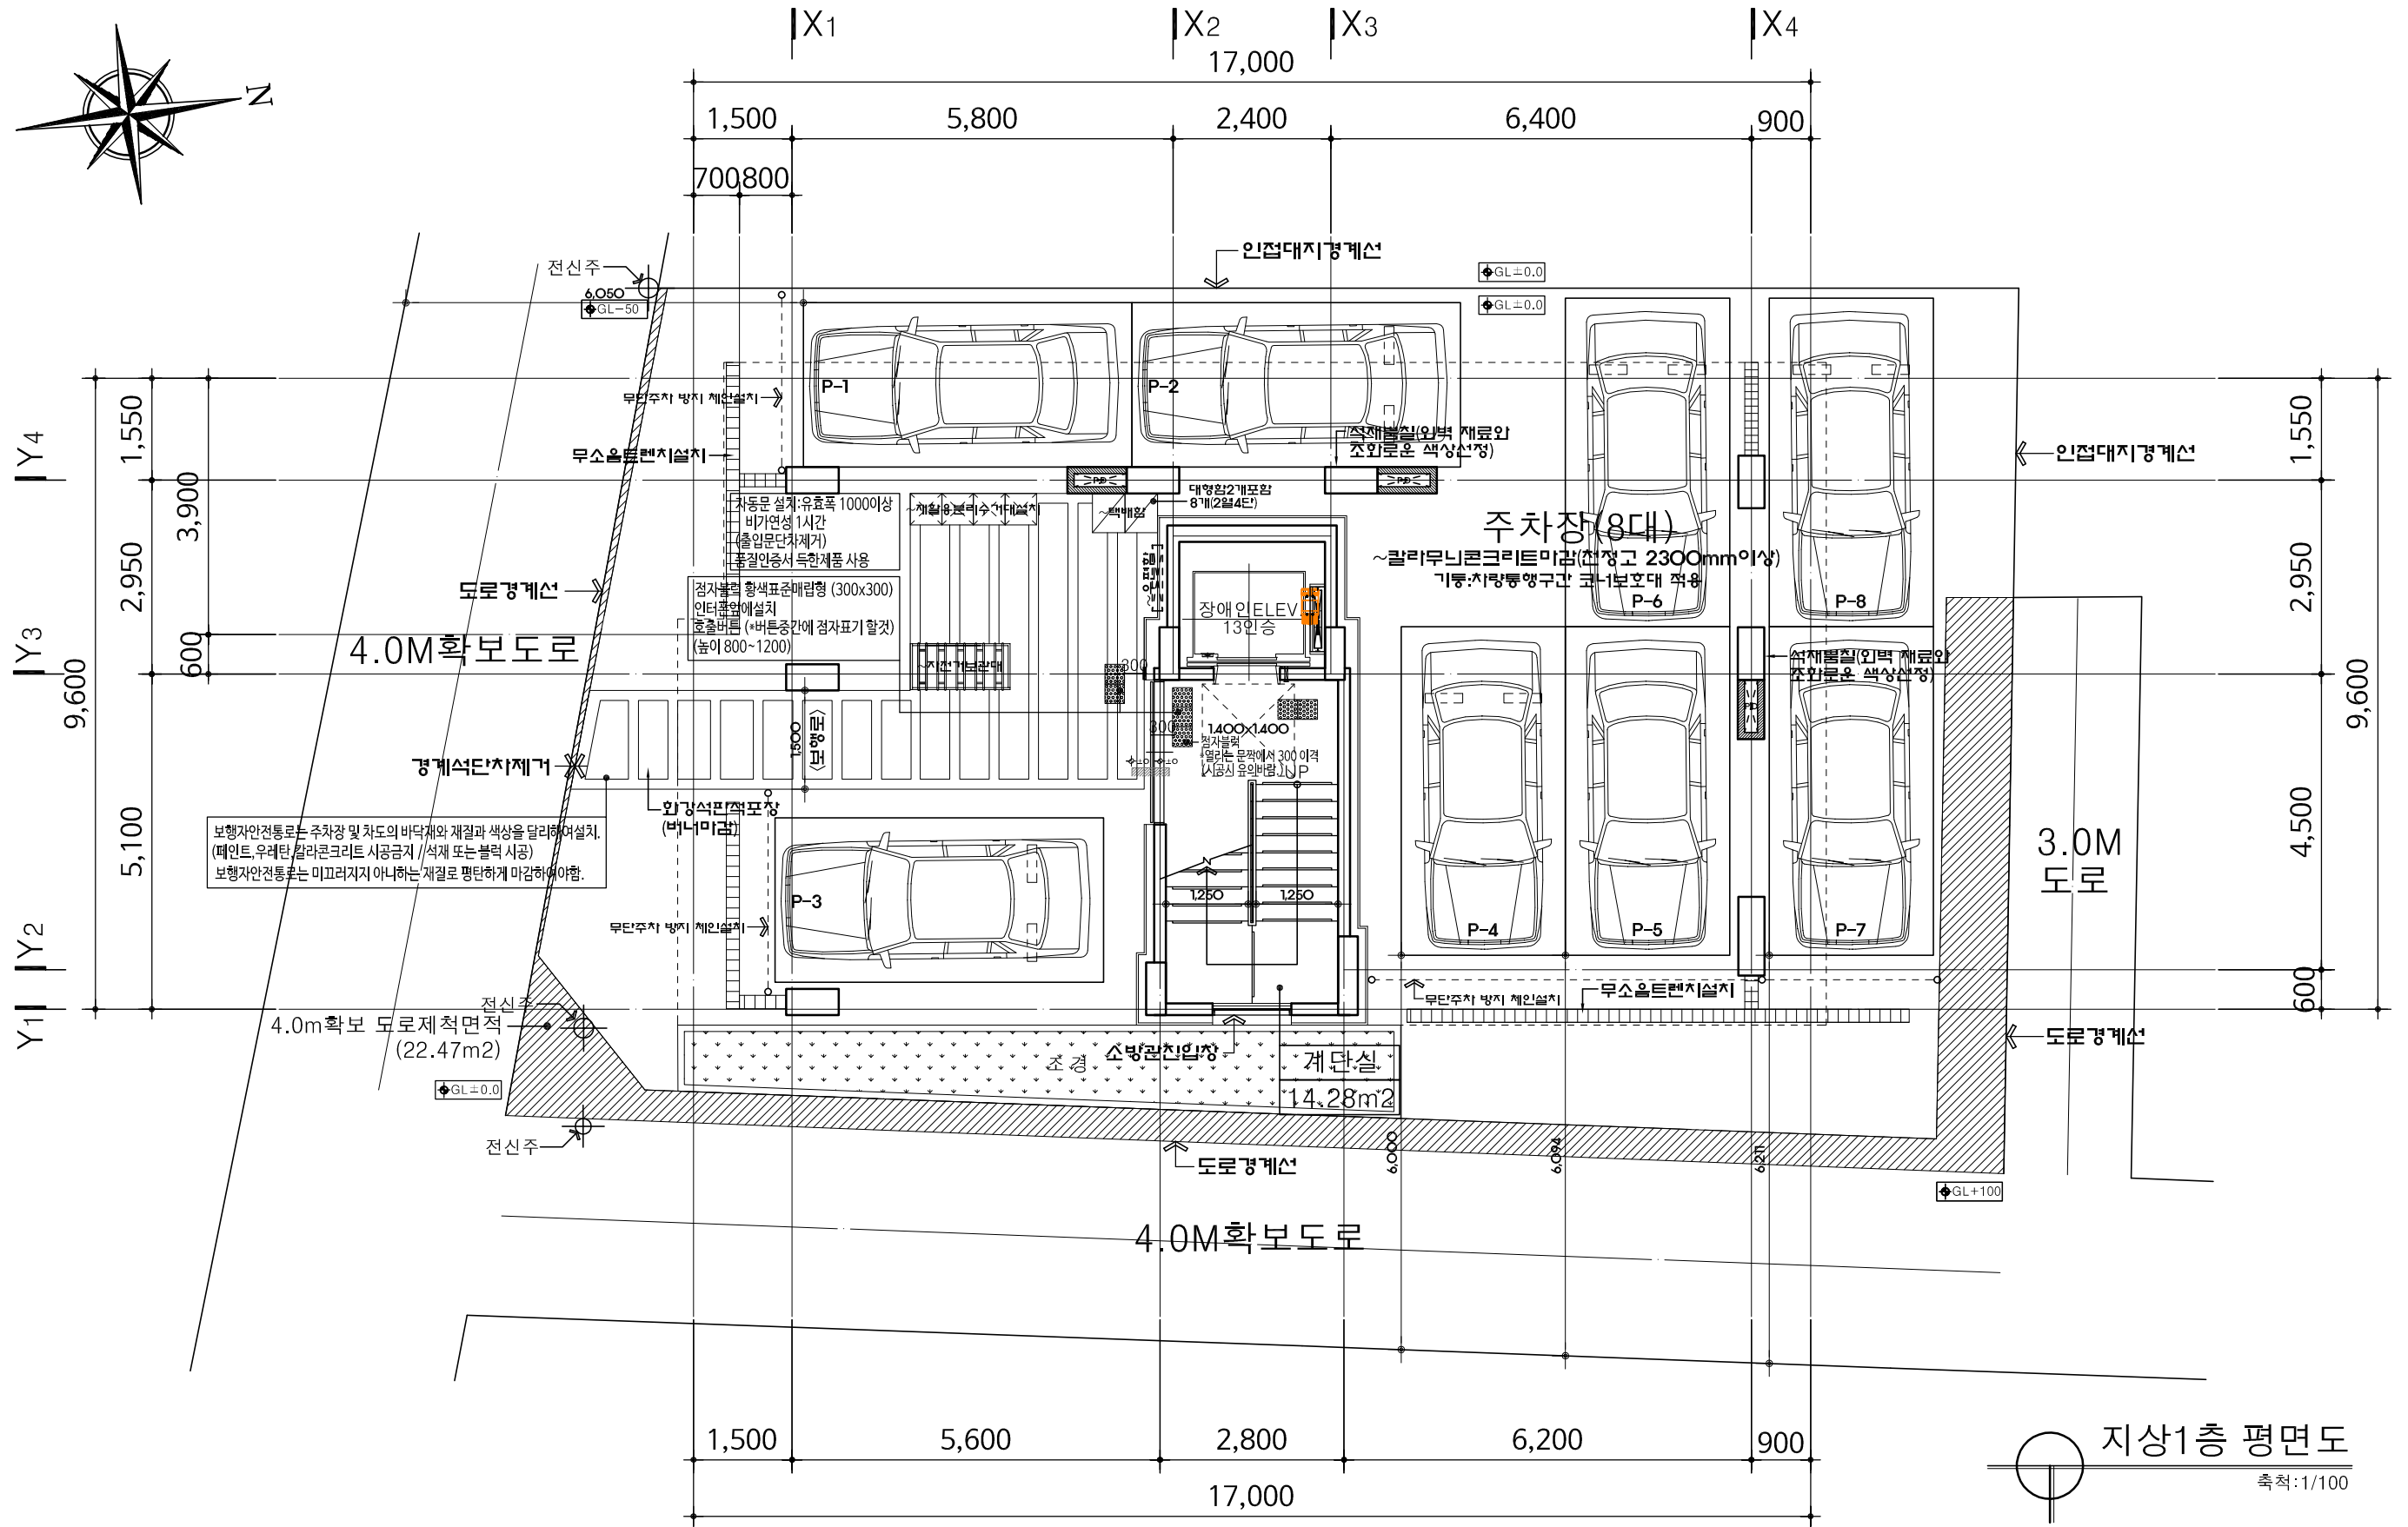
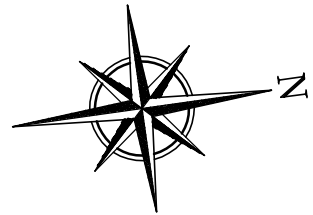


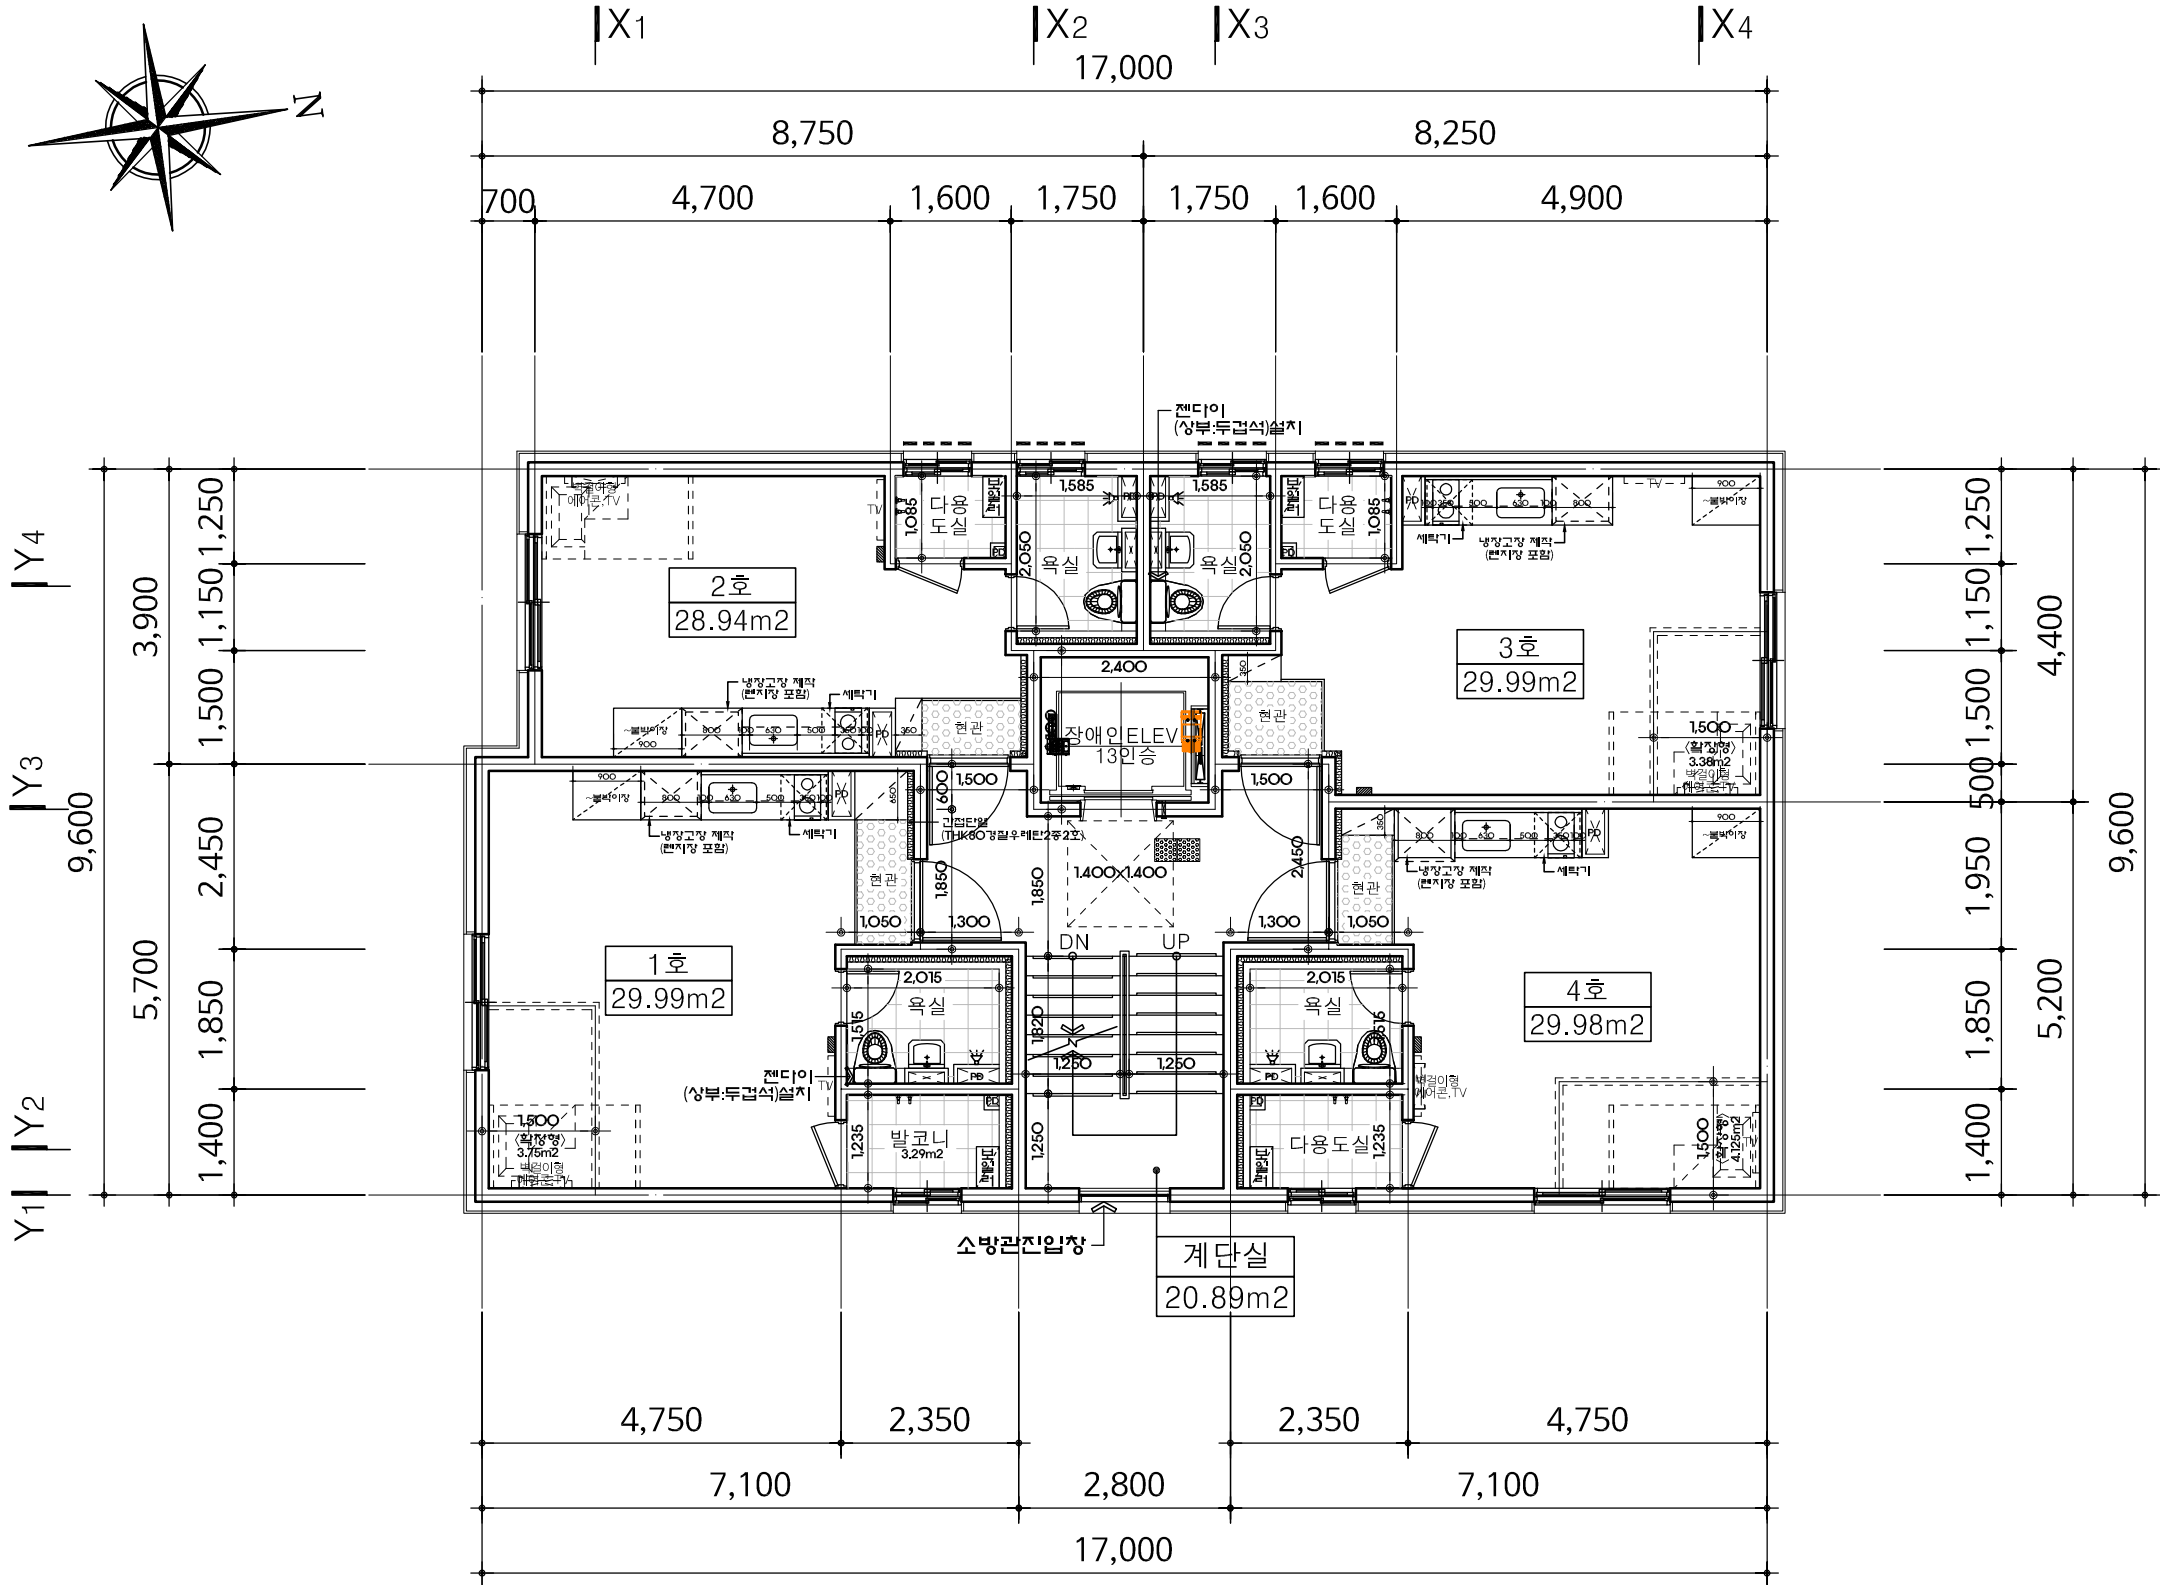


지상1층 평면도
축척: 1/100

 다원 건축사무소	서울시 송파구 석촌동 294-5, 신세계빌딩 302호 TEL: 449-9106 FAX: 449-9107 E-mail: jaesuki2@naver.com	NOTE	----- 차면시설 (창높이 1/2이상)	REVISION	PROJECT KINDS	PROJECT TITLE	DRAWN BY:		DRAWING TITLE	지상1층평면도			DRAWING NO.
						신림동 1609-18호 다세대주택 신축공사	CHECKED BY:						
							DESIGNED BY:		SCALE	1/100	DATE	2025. 09.	A - 009

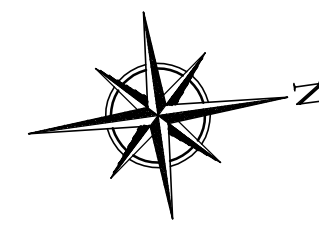


지상2~3층 평면도
축척: 1/100

주 기							
건 축	1 (외부)	주차장내 CCTV,쓰레기분리수거,지진거보관대 설치					
		우편함 설치 (세대전용, 공용, 반송용, 폐전지함 구분 설치)					
		테라스 창호 PL이중창 설치					
		세대 테라스 설치시 세대간 분리벽 계획					
		세대 발코니 설치시 차양시설 설치					
	2 (계단실)	세대 현관문 도어체크 설치					
		계단참의 현관간 계단 이격거리 (최소600mm이상)					
	3 (내부)	세대내 욕실, 휴지걸이 매립형 설치					
	4 (시공)	콘크리트 폴타이 제거 후 미감공사 시공 (방수, 단열재 시공 등)					
		욕실 & 다용도실 스위치 : 문 열리는 방향으로 시공					
		주차장 차량 진출입구간 무소음트랜지 시공					
		욕실,다용도실 슬라브 30mm 낮춤 (거실바닥마감기준:욕실,다용도실바닥 60mm이상 낮춤)					
	5 (미감)	-직접입기(외벽)에 면한 실내벽면 단열재					
[아이소핑크(10mm) + 석고보드 미감도면 표기]							
-간접입기(계단실,복도)에 면한 실내벽면 단열재							
일반내부 : [경질우레탄폼(80mm) + 석고보드 미감도면 표기]							
욕실,다용도실 : [단열재판넬(80mm) 시공]							
욕실,다용도실 : 고품방지 단열재 적용							
	*기타 실내 벽면 시멘트 미장 마감						
구 조	1	철근 : fy=400Mpa					
		콘크리트 : fck=24Mpa이상					
	2	스라브두께 : 210mm (복배근)					
		외벽두께 : 180mm (복배근)					
		코어벽두께 : 180mm (복배근)					
		세대간벽두께 : 180mm (복배근)					
	내벽두께 : 150mm (복배근)						
전 기	1	-콘센트 설치 (바닥 마감선 기준)					
		벽걸이형 에어컨 : 1900					
		[환풍실] 양면기 옆 : 900					
		[보일러실] : 1500					
		[주방] 조리대 : 중앙 1300 / 냉장고 : 350 / 후드 : 2000					
	2	-비디오폰(VP),보일러온도조절기(B), 스위치(S), 전열교환기스위치(E) (거실이트홀 위치)					
		<table><tr><td colspan="3">VP</td></tr><tr><td>S</td><td>E</td><td>B</td></tr></table>	VP			S	E
	VP						
S	E	B					
3	에어컨 실외기	<table><tr><td colspan="3">[>>>]</td></tr></table>	[>>>]				
	[>>>]						
비 고		-세대현관문 ## 규격"틀"포함 : 1100X2200					
		- 반자높이 : 2,200mm 이상					
		- 청년유형 냉장고장 제작(편지장 포함)					
		- 세탁기 : 주방기구 일부장에 계획					
		- 다용도실 전정 소재구 및 점검구 설치					
		- 주방 후드 : 슬림형 또는 통후드급(기밀대 중앙설치, 램퍼설치)					
		- 국기통 고정형 설치(세대별1개)					
		- 개수대 상부 SST권조선편 설치					
		- 욕탕 점검용사다리 : 등받이 포함 안전사다리 타입 적용					
		- 필로티 출입제안을 위한 신기술 및 사슬고리 설치					
		- 개수대 앞에 냉장고가 있는 경우 물막이턱 반영					
		- 세대 환풍실 내 샤워공간 물튀김 방지막 설치					


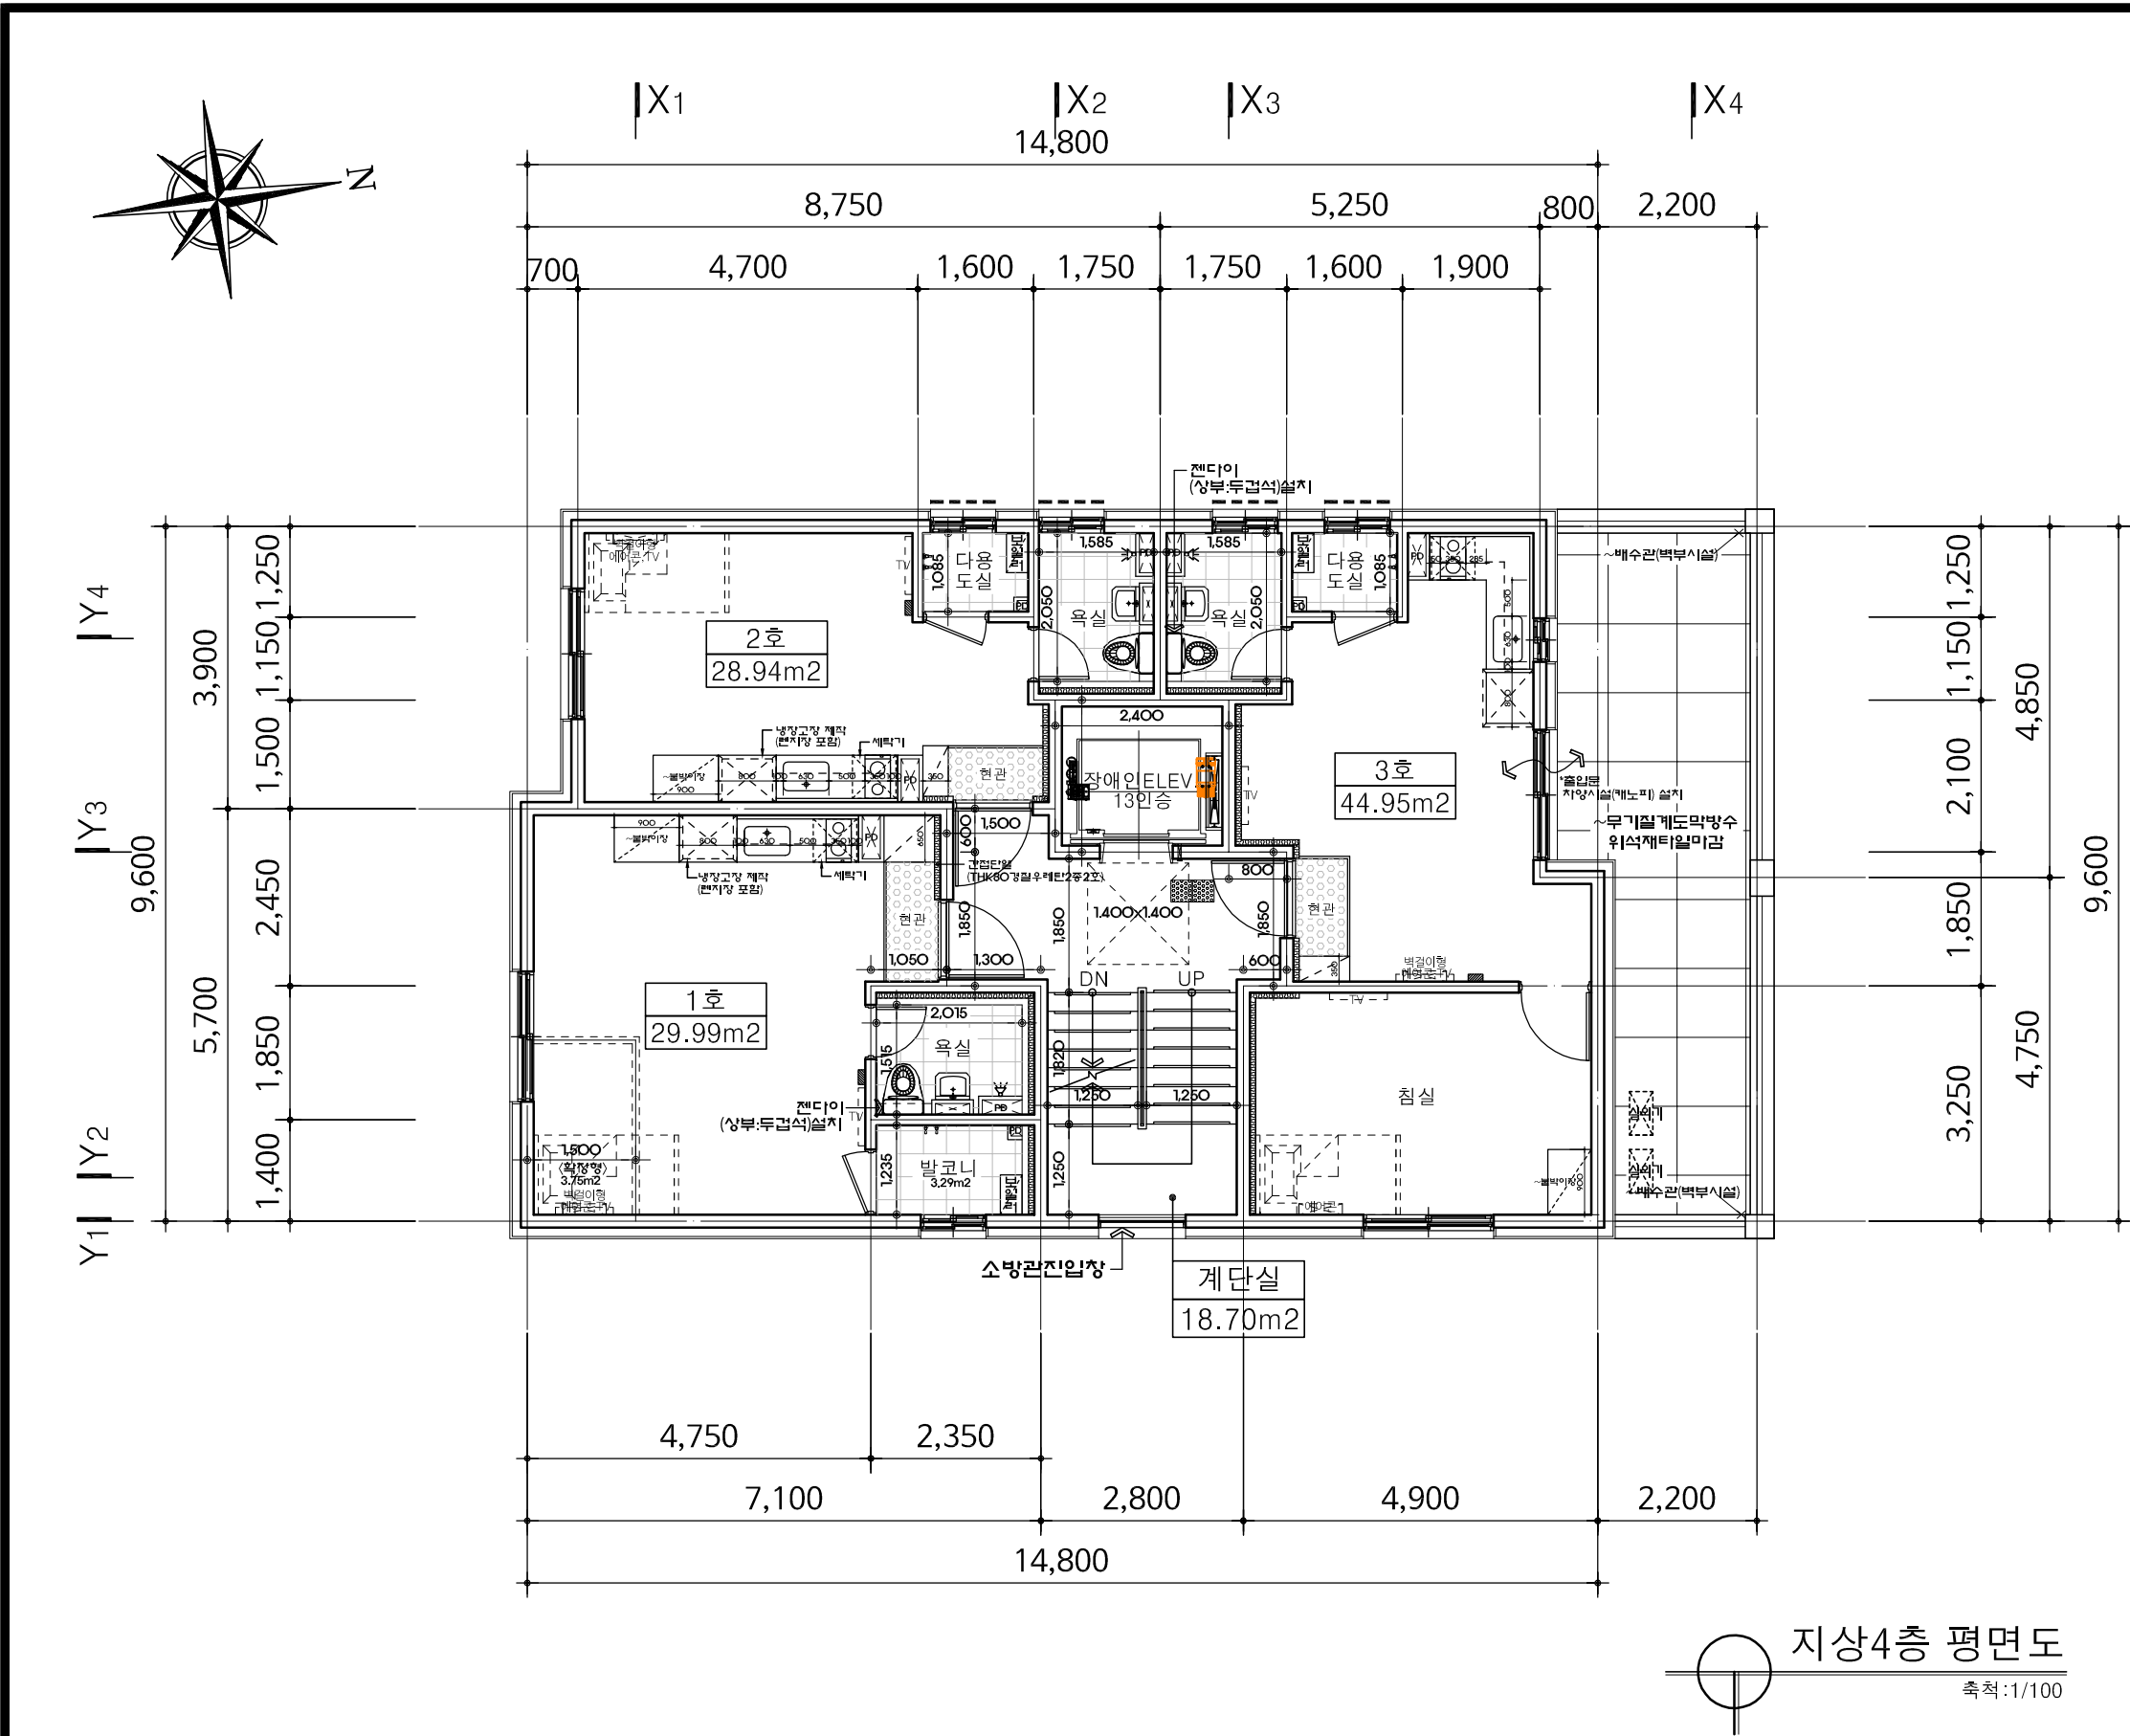


지상4층 평면도
축척:1/100


주 기			
구 조	1 (외부)	주차장내 CCTV,쓰레기분리수거,지진거보관대 설치	
		우편함 설치 (세대전용, 공용, 반송용, 폐전지함 구분 설치)	
		테라스 창호 PL이중창 설치	
		세대 테라스 설치시 세대간 분리벽 계획	
		세대 발코니 설치시 차양시설 설치	
	2 (계단실)	세대 현관문 도어체크 설치	
		계단참의 현관간 계단 이격거리 (최소600mm이상)	
	3 (내부)	세대내 욕실, 휴지걸이 매립형 설치	
	4 (시공)	콘크리트 폴타이 제거 후 미감공사 시공 (방수, 단열재 시공 등)	
		욕실 & 다용도실 스위치 : 문 열리는 방향으로 시공	
	5 (미감)	주차장 차양 진출입구간 무소음트랜지 시공	
욕실,다용도실 슬라브 30mm 낮춤 (거실바닥마감기준:욕실,다용도실바닥 60mm이상 낮춤)			
-적접외기(외벽)에 면한 실내벽면 단열재			
[아이소핑크(10mm) + 석고보드 미감도면 표기]			
-간접외기(계단실,복도)에 면한 실내벽면 단열재			
일반내부 : [경질우레탄폼(80mm) + 석고보드 미감도면 표기]			
욕실,다용도실 : [단열재판넬(80mm) 시공]			
구 조	욕실,다용도실 : 고품방지 단열재 적용		
	*기타 실내 벽면 시멘트 미장 마감		
구 조	1	철근 : fy=400Mpa	
		콘크리트 : fck=24Mpa이상	
	2	스라브두께 : 210mm (복배근)	
		외벽두께 : 180mm (복배근)	
		코어벽두께 : 180mm (복배근)	
세대간벽두께 : 180mm (복배근)			
구 조	1	내벽두께 : 150mm (복배근)	
		-콘센트 설치 (바닥 마감선 기준)	
		벽걸이형 에어컨 : 1900	
		[환풍실] 양면기 옆 : 900	
		[보일러실] : 1500	
	2	[주방] 조리대 : 중앙 1300 / 냉장고 : 350 / 후드 : 2000	
		-비디오폰(VP),보일러온도조절기(B), 스위치(S), 전열교환기스위치(E) (거실이트홀 위치)	
		VP S E B	
		3	에어컨 실외기
비 고	-세대현관문 ## 규격"틀"포함 : 1100X2200 - 반지높이 : 2,200mm 이상 - 청년유형 냉장고장 제작(냉장고 포함) - 세탁기 : 주방기구 하부장에 계획 - 다용도실 전정 소재구 및 점검구 설치 - 주방 후드 : 슬림형 또는 통후드급(기열대 중앙설치, 램퍼설치) - 국기통 고정형 설치(세대별1개) - 개수대 상부 SST관조선폰 설치 - 욕실 점검용사다리 : 등받이 포함 안전사다리 타입 적용 - 필로티 출입제안을 위한 신시슬 및 사슬고리 설치 - 개수대 옆에 냉장고가 있는 경우 물막이턱 반영 - 세대 환풍실 내 샤워공간 물튀김 방지막 설치		

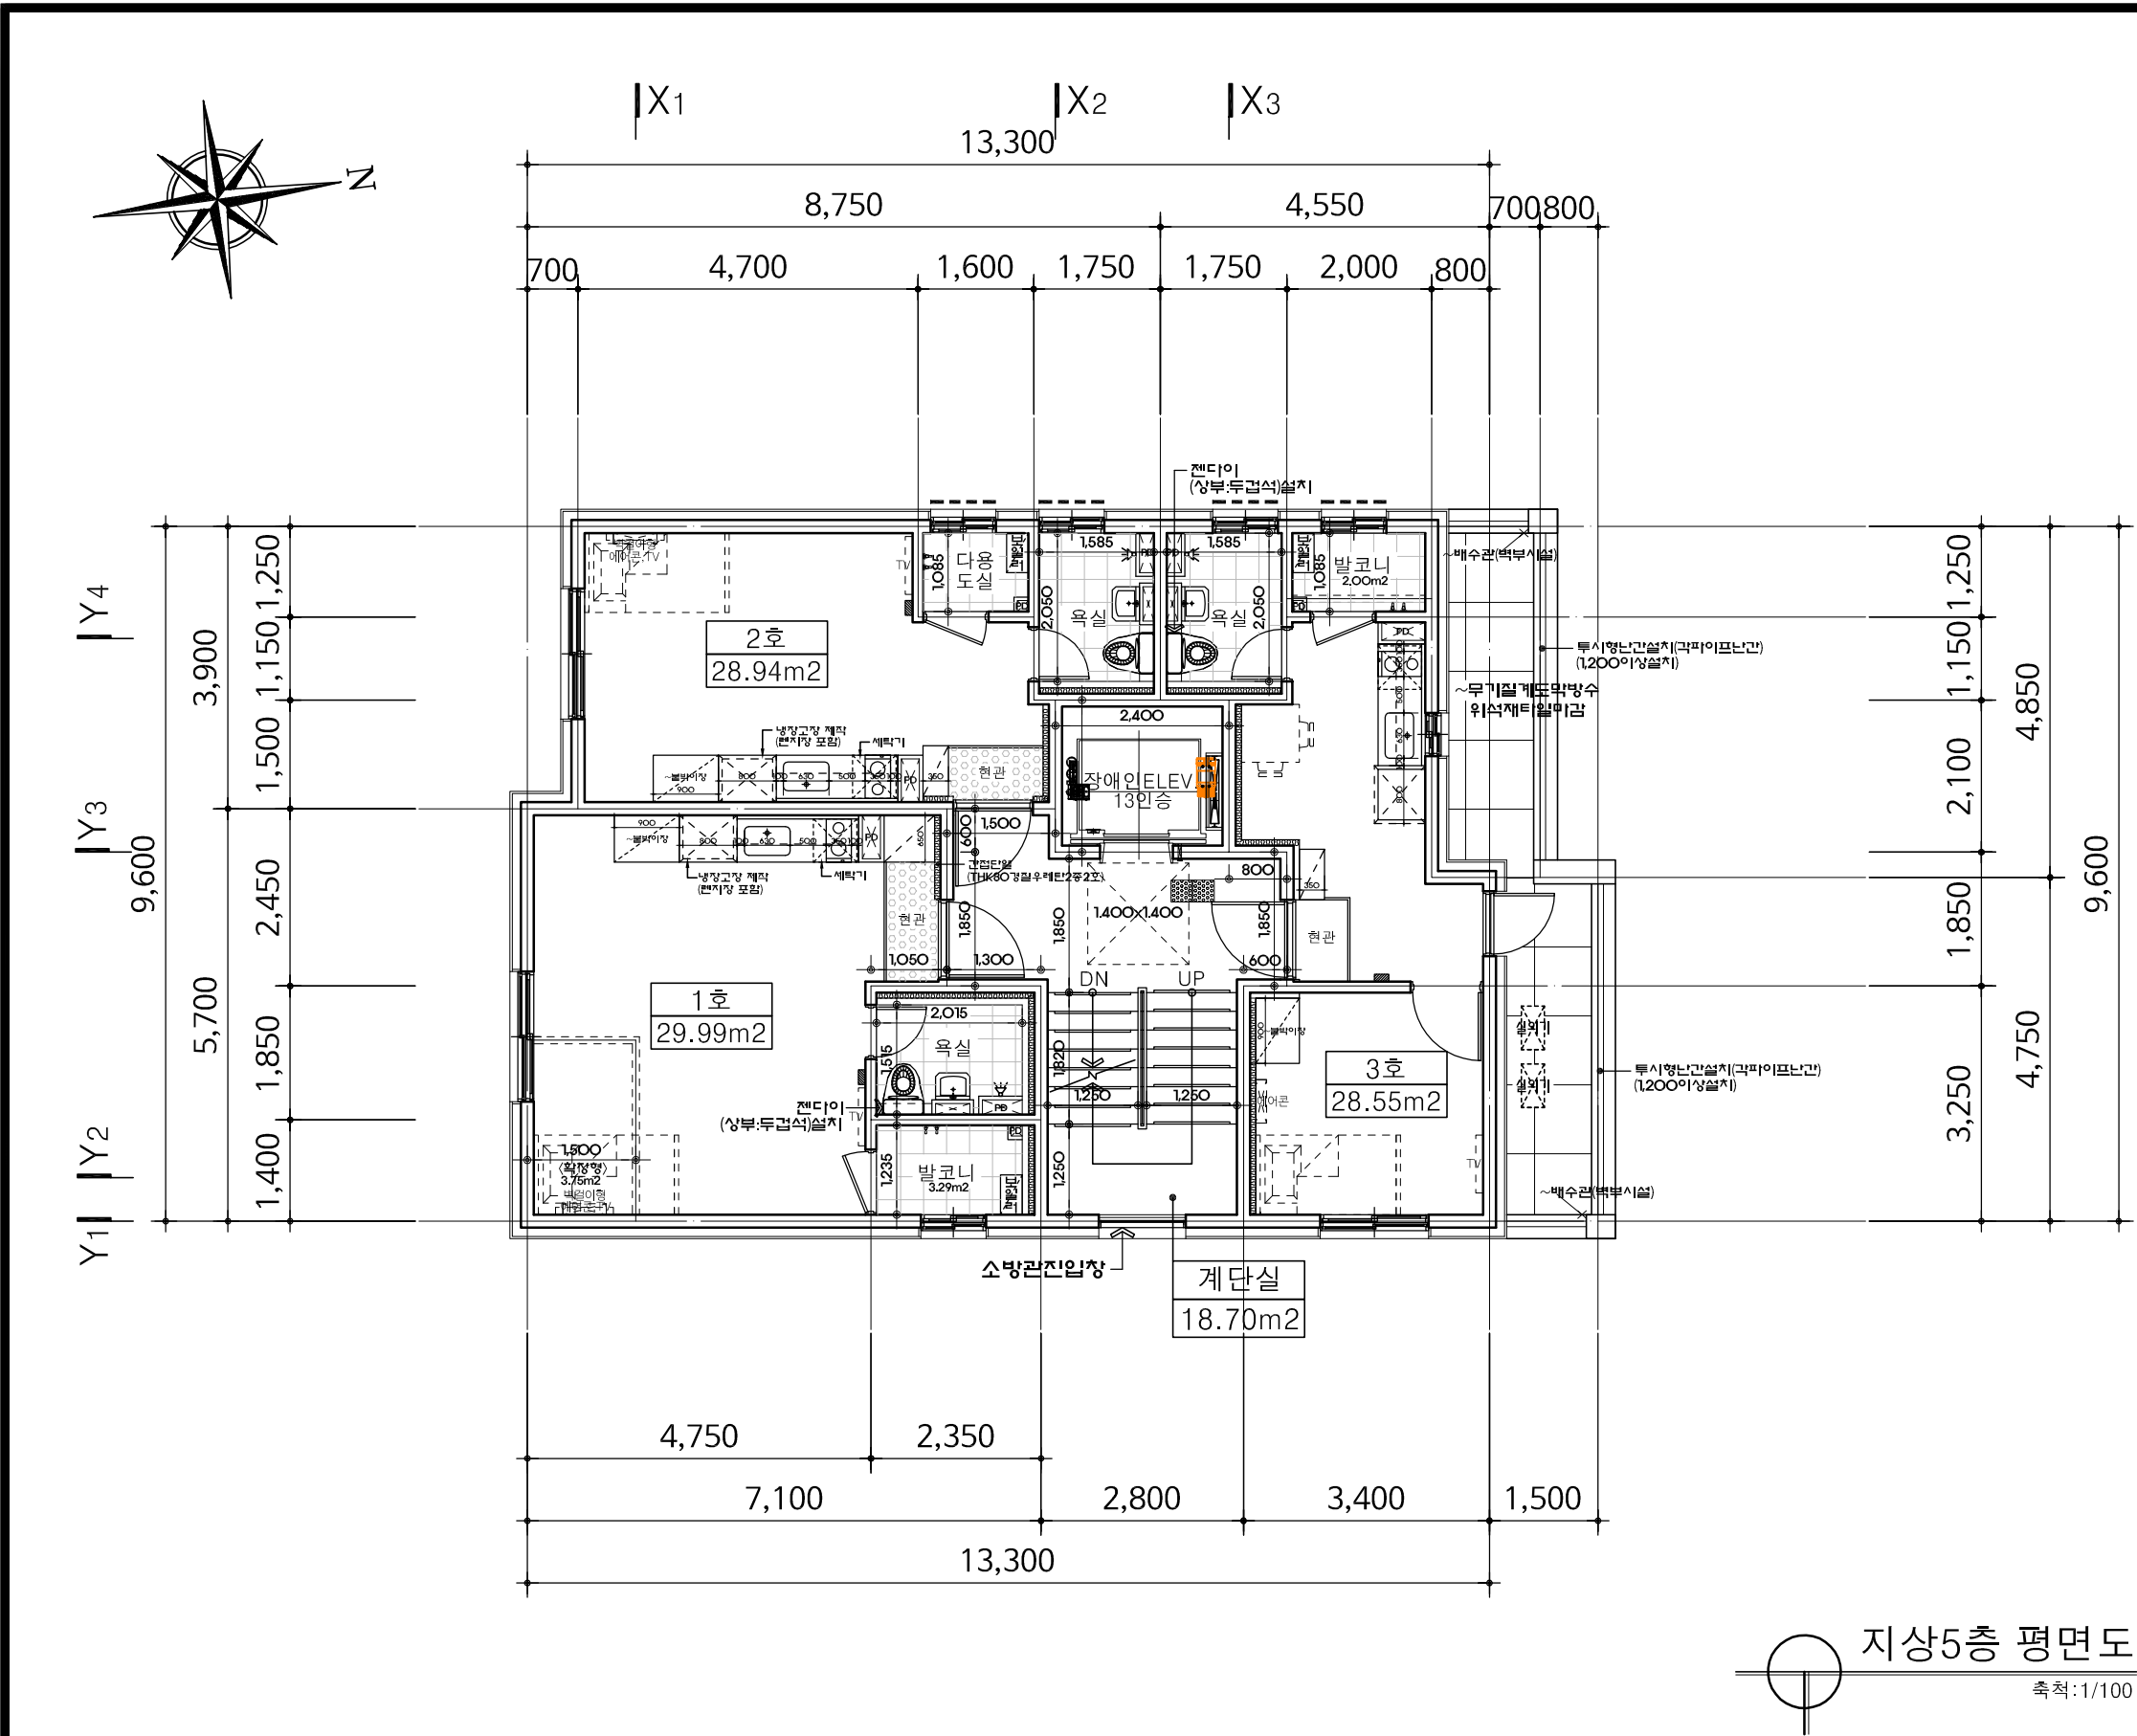

주 기		
구 조	1 (외부)	주차장내 CCTV,쓰레기분리수거,지진거보관대 설치
		우편함 설치 (세대전용, 공용, 반송용, 폐전지함 구분 설치)
		테라스 창호 PL이중창 설치
		세대 테라스 설치시 세대간 분리벽 계획
		세대 발코니 설치시 차양시설 설치
	2 (계단실)	세대 현관문 도어체크 설치
		계단참의 현관문 계단 이격거리 (최소600mm이상)
	3 (내부)	세대내 욕실, 휴지걸이 매립형 설치
		콘크리트 폴타이 제거 후 미감공사 시공 (방수, 단열재 시공 등)
	4 (시공)	욕실 & 다용도실 스위치 : 문 열리는 방향으로 시공
주차장 차량 진출입구간 무소음트랜지 시공		
기 타	5 (미감)	욕실,다용도실 슬라브 30mm 낮춤 (거실바닥마감기준:욕실,다용도실바닥 60mm이상 낮춤)
		-직접입기(외벽)에 면한 실내벽면 단열재 [아이소핑크(10mm) + 석고보드 미감도면 표기]
	-간접입기(계단실,복도)에 면한 실내벽면 단열재 일반내부 : [경질우레탄폼(80mm) + 석고보드 미감도면 표기] 욕실,다용도실 : [단열재판넬(80mm) 시공]	
	욕실,다용도실 : 고품방지 단열재 적용	
	*기타 실내 벽면 시멘트 미장 마감	
	1	철근 : fy=400Mpa
		콘크리트 : fck=24Mpa이상
2		스라브두께 : 210mm (복배근)
		인벽두께 : 180mm (복배근)
		코어벽두께 : 180mm (복배근)
	세대간벽두께 : 180mm (복배근)	
내벽두께 : 150mm (복배근)		
전 기	1	-콘센트 설치 (바닥 마감선 기준)
		벽걸이형 에어컨 : 1900
		[환풍실] 양변기 앞 : 900
		[보일러실] : 1500
	[주방] 조리대 : 중앙 1300 / 냉장고 : 350 / 후드 : 2000	
2	-비디오폰(VP),보일러온도조절기(B), 스위치(S), 전열교환기스위치(E) (거실이트홀 위치)	
	VP S E B	
3	에어컨 실외기	
비 고	-세대현관문 ## 규격"틀"포함 : 1100X2200 - 반지높이 : 2,200mm 이상 - 청년유형 냉장고장 제작(냉지장 포함) - 세탁기 : 주방기구 하부장에 계획 - 다용도실 전정 소재구 및 점검구 설치 - 주방 후드 : 슬림형 또는 통후드급(기열대 중앙설치, 램퍼설치) - 국기통 고정형 설치(세대별1개) - 개수대 상부 SST관조선헌 설치 - 욕실 점검용사다리 : 등받이 포함 안전사다리 타입 적용 - 필로티 출입제한을 위한 신시슬 및 시슬고리 설치 - 개수대 옆에 냉장고가 있는 경우 물막이턱 반영 - 세대 환풍실 내 샤워공간 물튀김 방지막 설치	

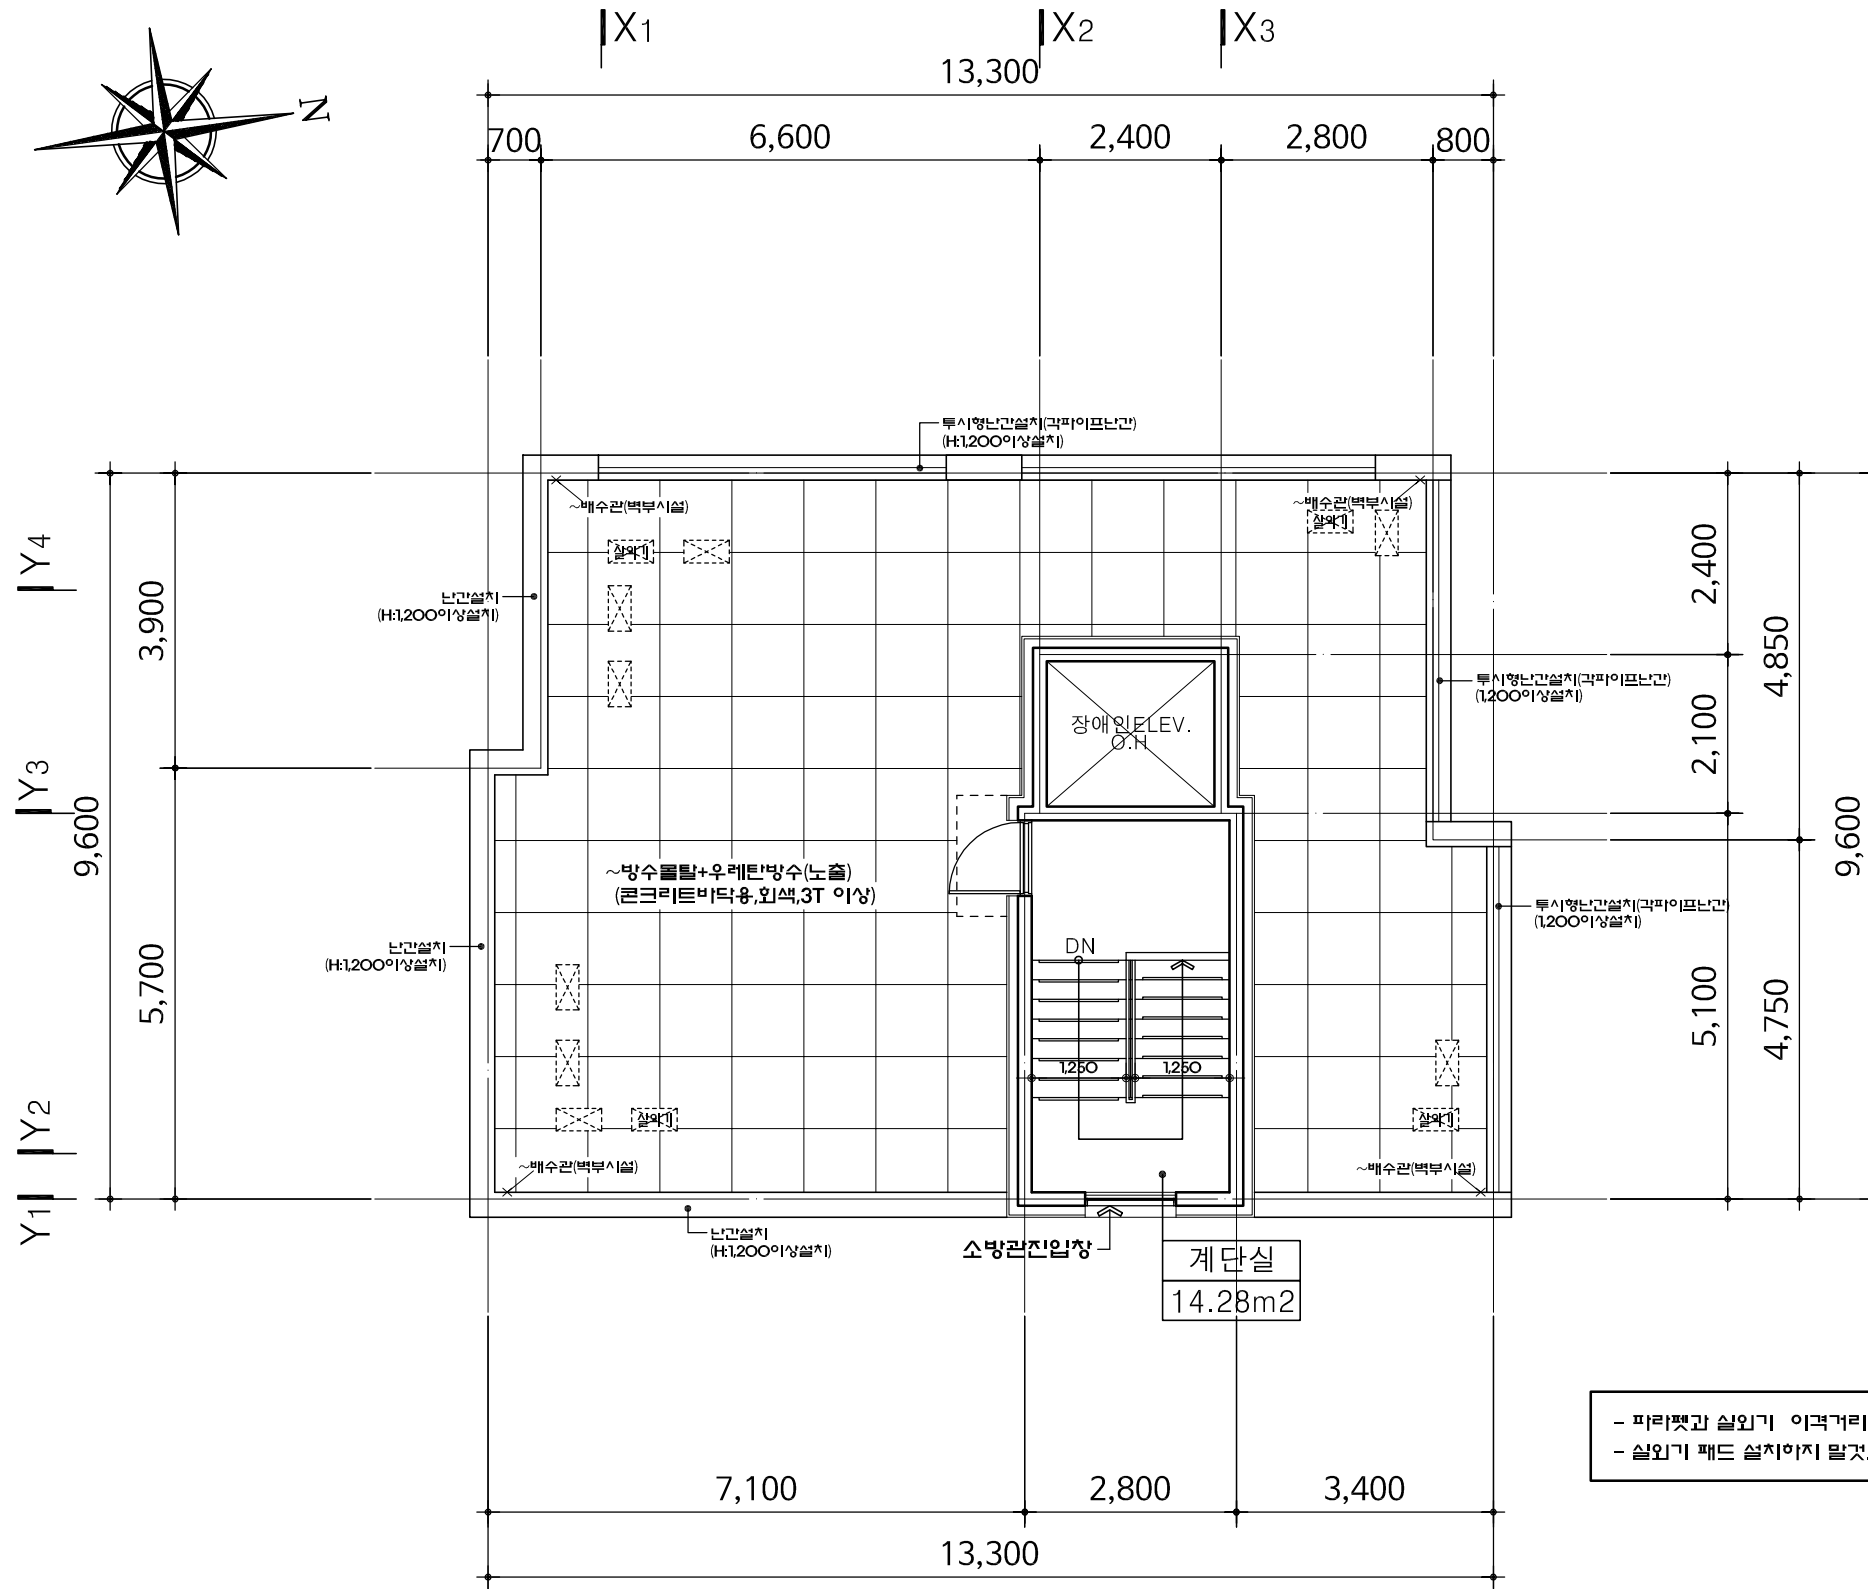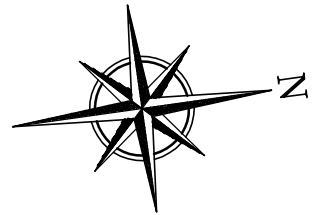

옥탑층 평면도
축척:1/100

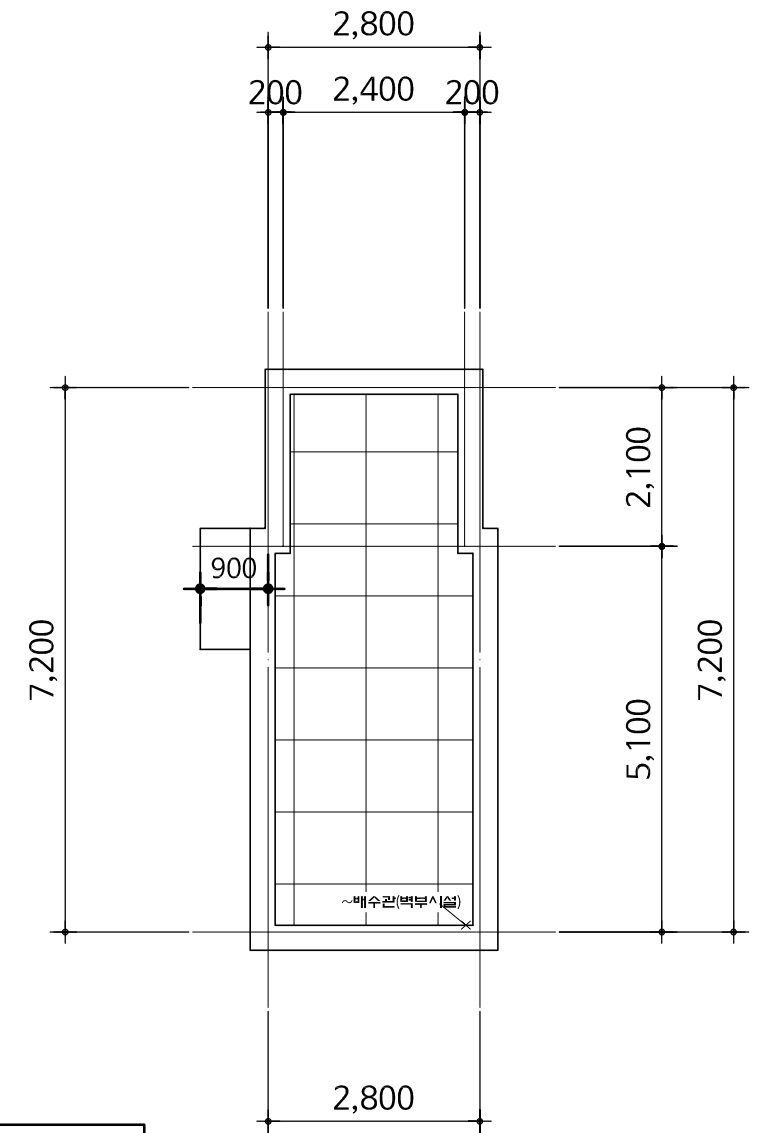


옥탑지붕 평면도
축척:1/100

- 파라펫과 실외기 이격거리 1,000mm 이상 권장
- 실외기 패드 설치하지 말것.




서울시 송파구 석촌동 294-5,
신세계빌딩 302호
TEL:449-9106 FAX:449-9107
E-mail:jaesuki2@naver.com


NOTE	REVISION	PROJECT KINDS	PROJECT TITLE	DRAWN BY:	DRAWING TITLE	DRAWING NO.		
----- 차면시설 (창높이 1/2이상)			신림동 1609-18호 다세대주택 신축공사	CHECKED BY:	SCALE	1/100	DATE	2025. 09.
				DESIGNED BY:				A - 013

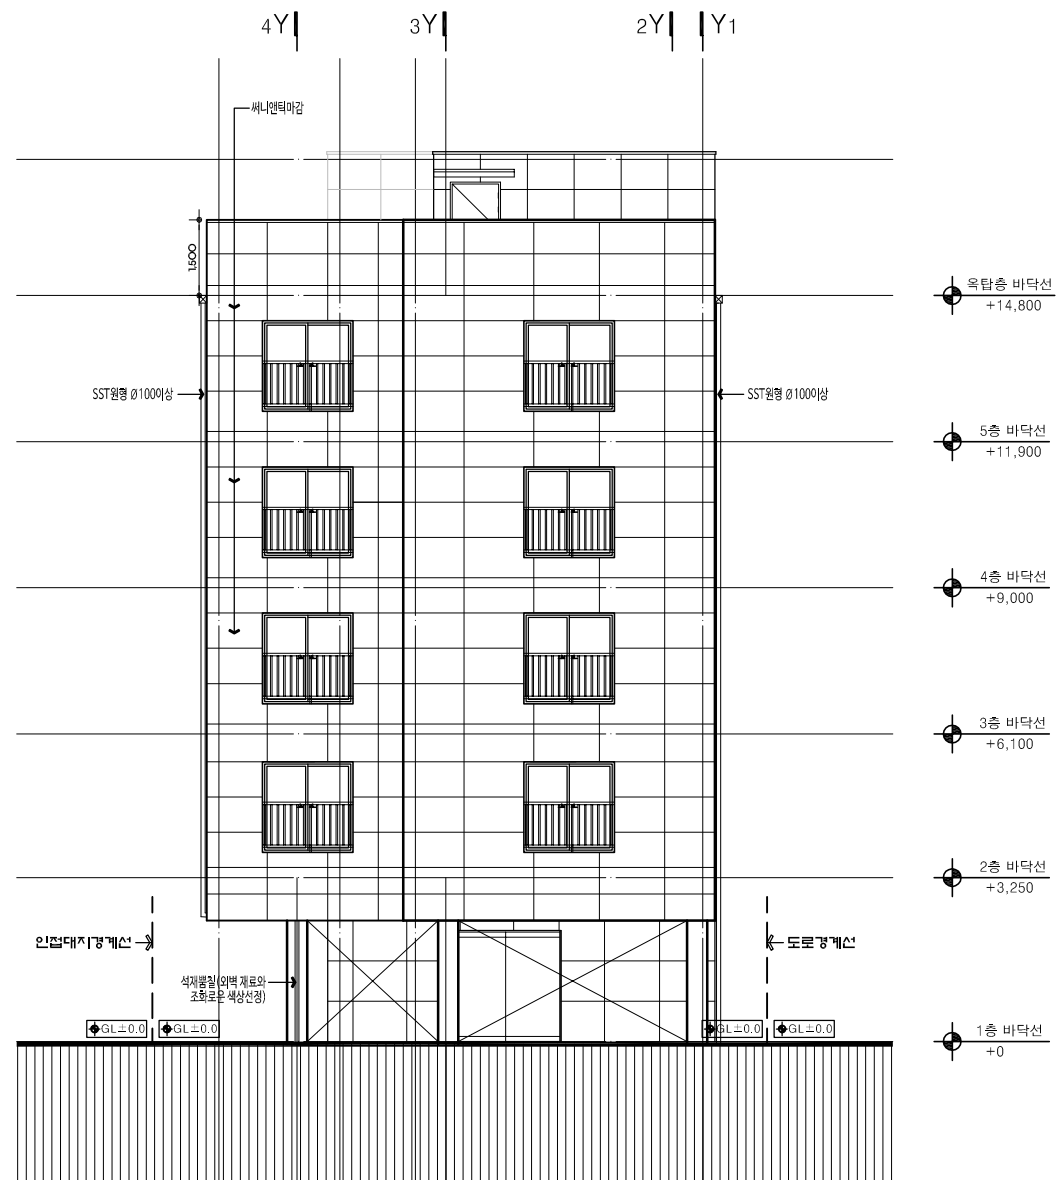

정면도
축척: 1/150

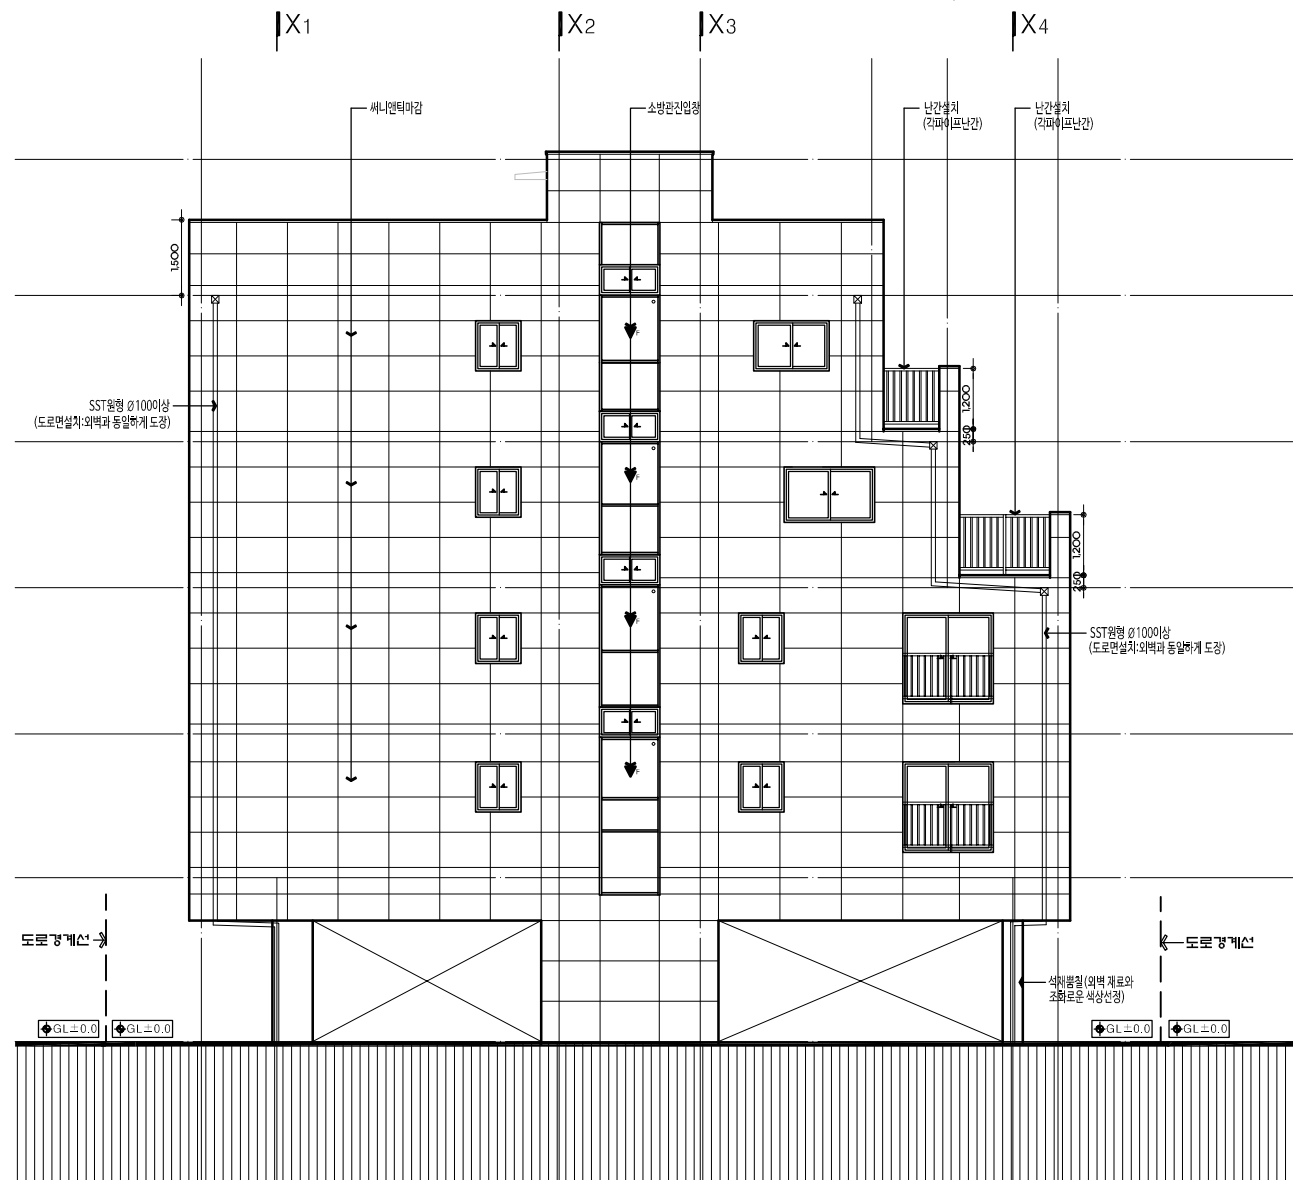


우측면도
축척: 1/150

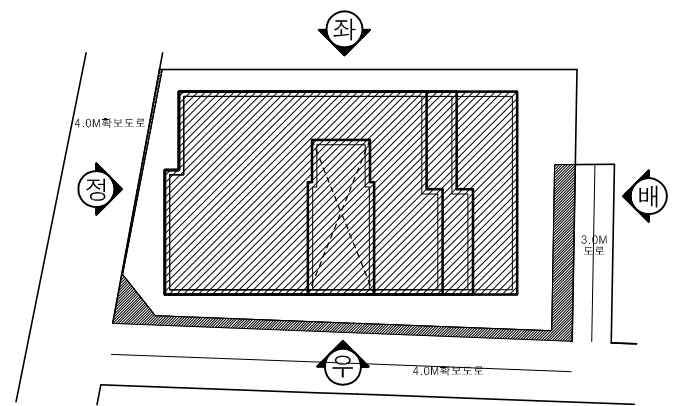


서울시 송파구 석촌동 294-5,
신세계빌딩 302호
TEL: 449-9106 FAX: 449-9107
E-mail: jaesuki2@naver.com


NOTE	REVISION	PROJECT KINDS	PROJECT TITLE	DRAWN BY:	DRAWING TITLE	SCALE	DATE	DATE	DRAWING NO.
----- 차면시설 (창높이 1/2이상)			신림동 1609-18호 다세대주택 신축공사	CHECKED BY:	정면도/우측면도	1/150	2025. 09.		A - 014
				DESIGNED BY:					

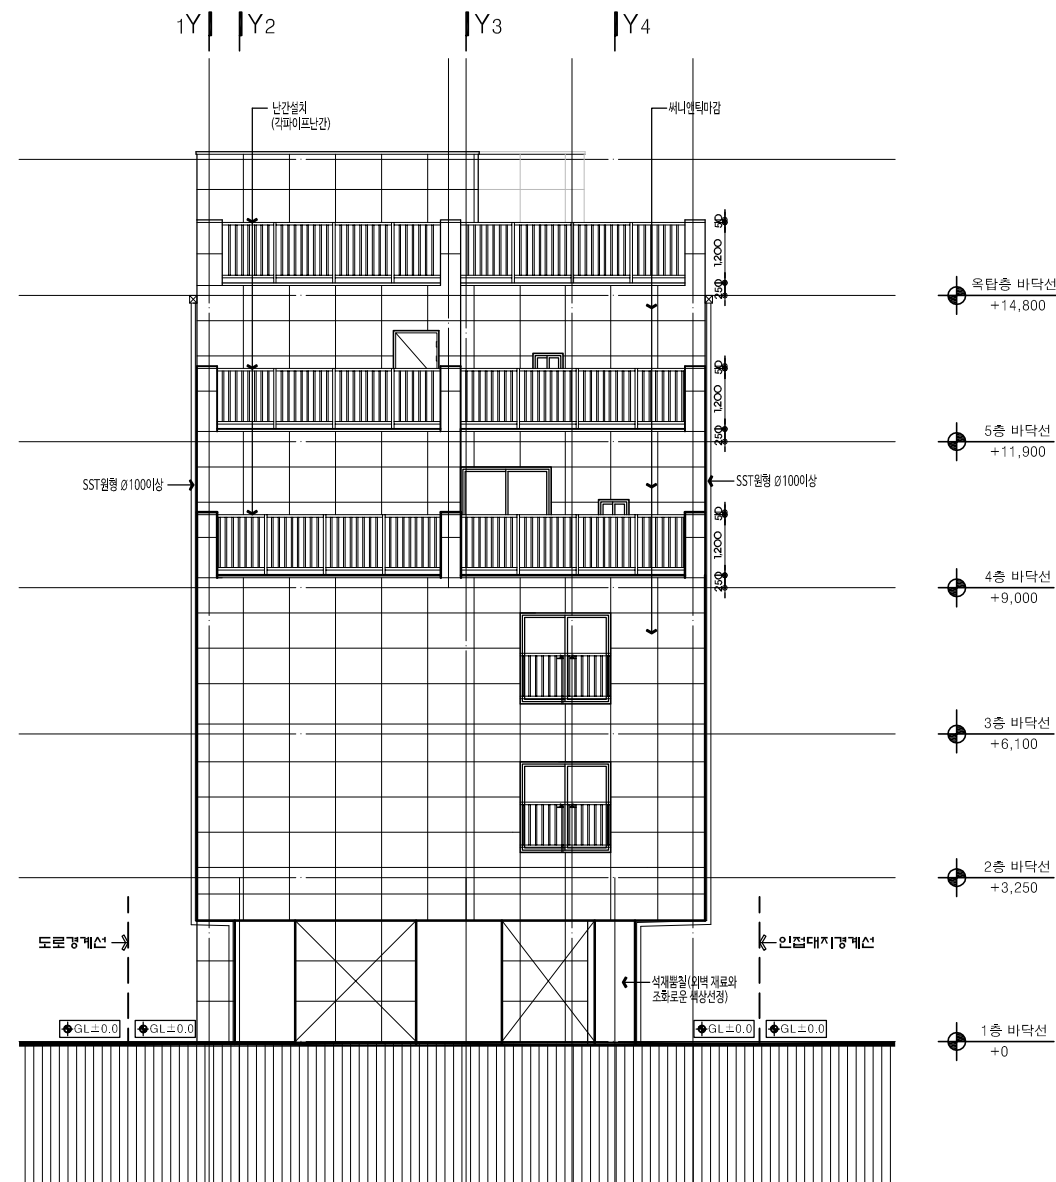

배 면 도
축척: 1/150

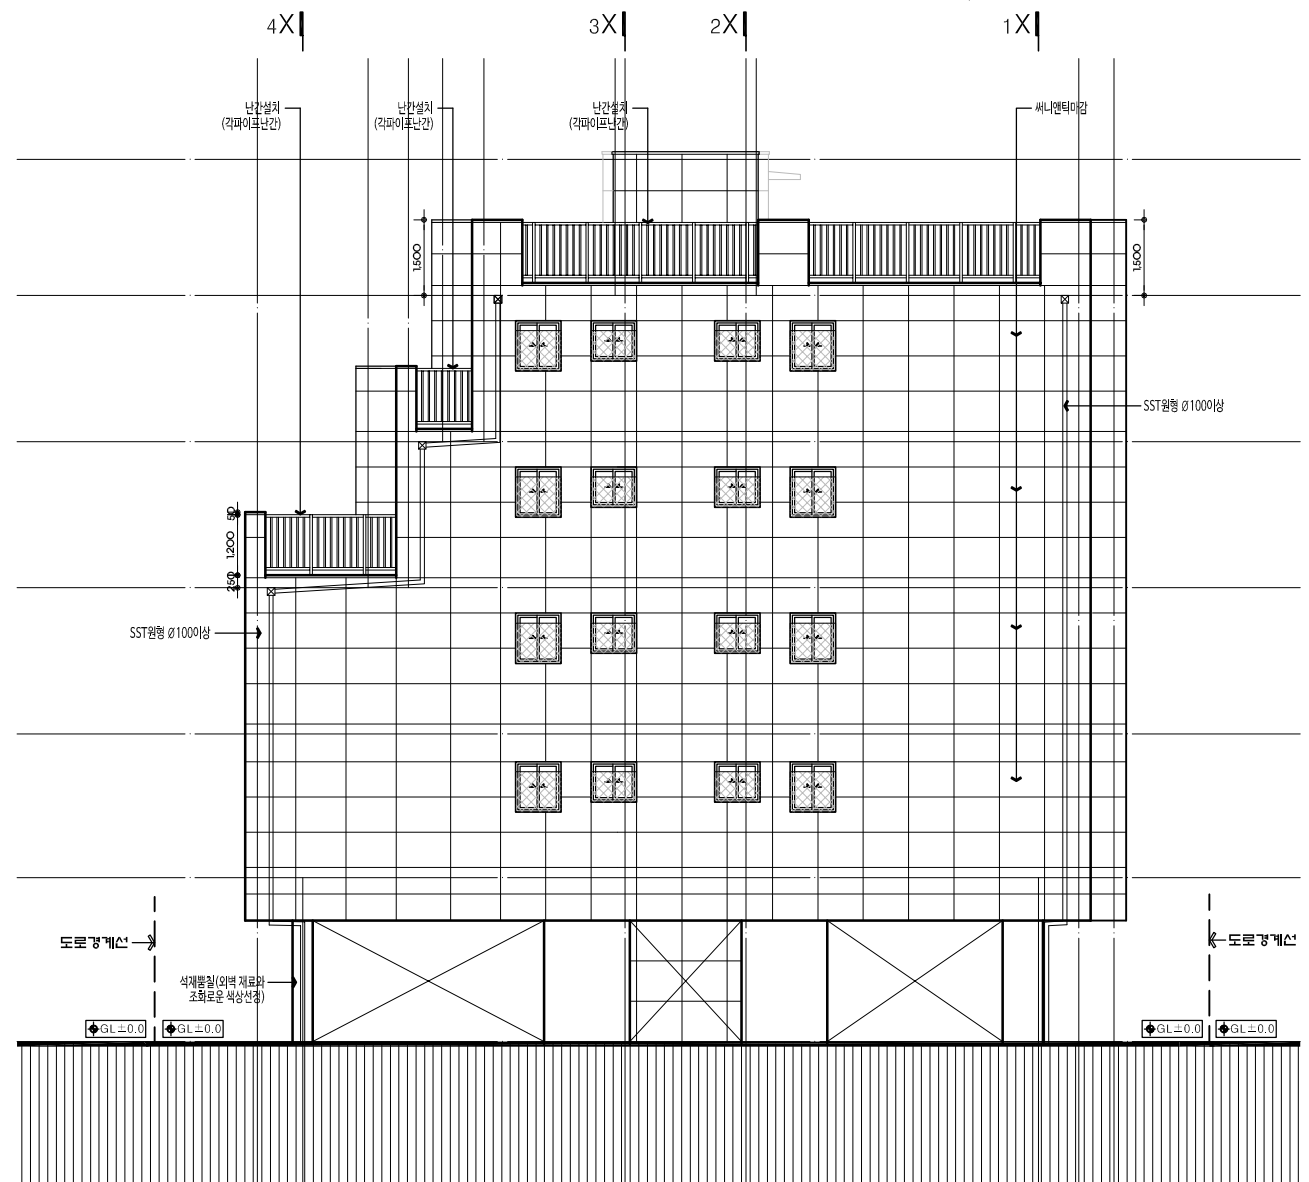


좌 측 면 도
축척: 1/150

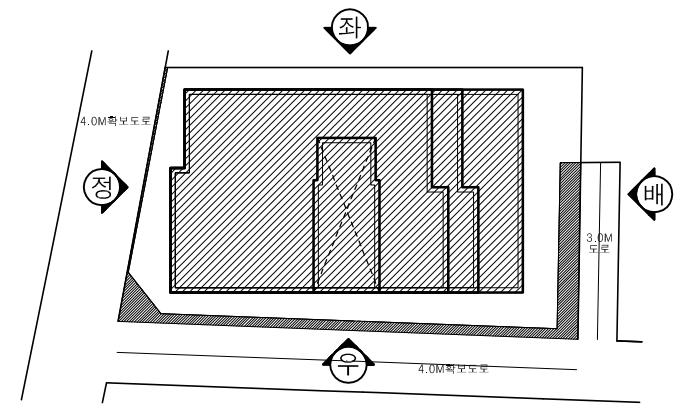


서울시 송파구 석촌동 294-5,
신세계빌딩 302호
TEL: 449-9106 FAX: 449-9107
E-mail: jaesuki2@naver.com

NOTE	REVISION	PROJECT KINDS	PROJECT TITLE	DRAWN BY:	DRAWING TITLE	DRAWING NO.
----- 차면시설 (창높이 1/2이상)			신림동 1609-18호 다세대주택 신축공사	CHECKED BY:	배면도/좌측면도	A - 015
				DESIGNED BY:	SCALE	
					1/150	
					DATE	
					2025. 09.	


<벽식루프드레인상세도>

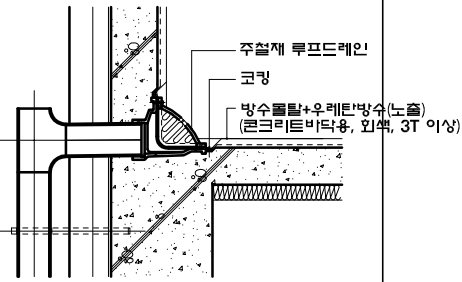


<내부방수처리시공상세도>

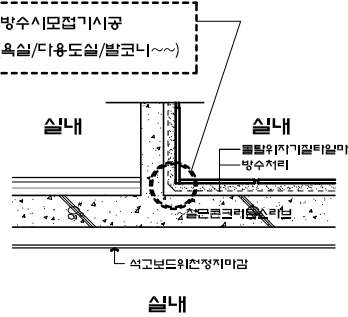


<최상층지붕 단열 단면상세>

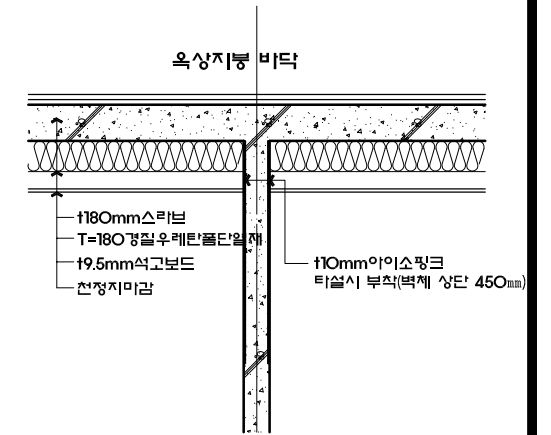


<방수처리시공&최상층결로방지단열상세>

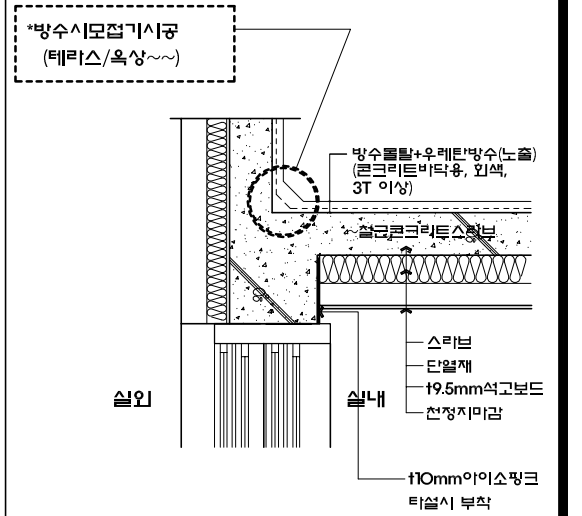

<현관~바닥상세도(벽식구조)>

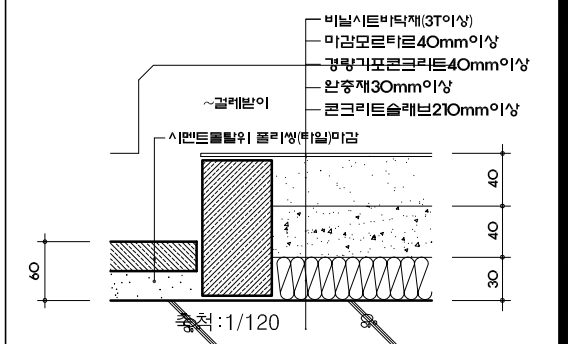

《 완충재 상능 기준참조 》

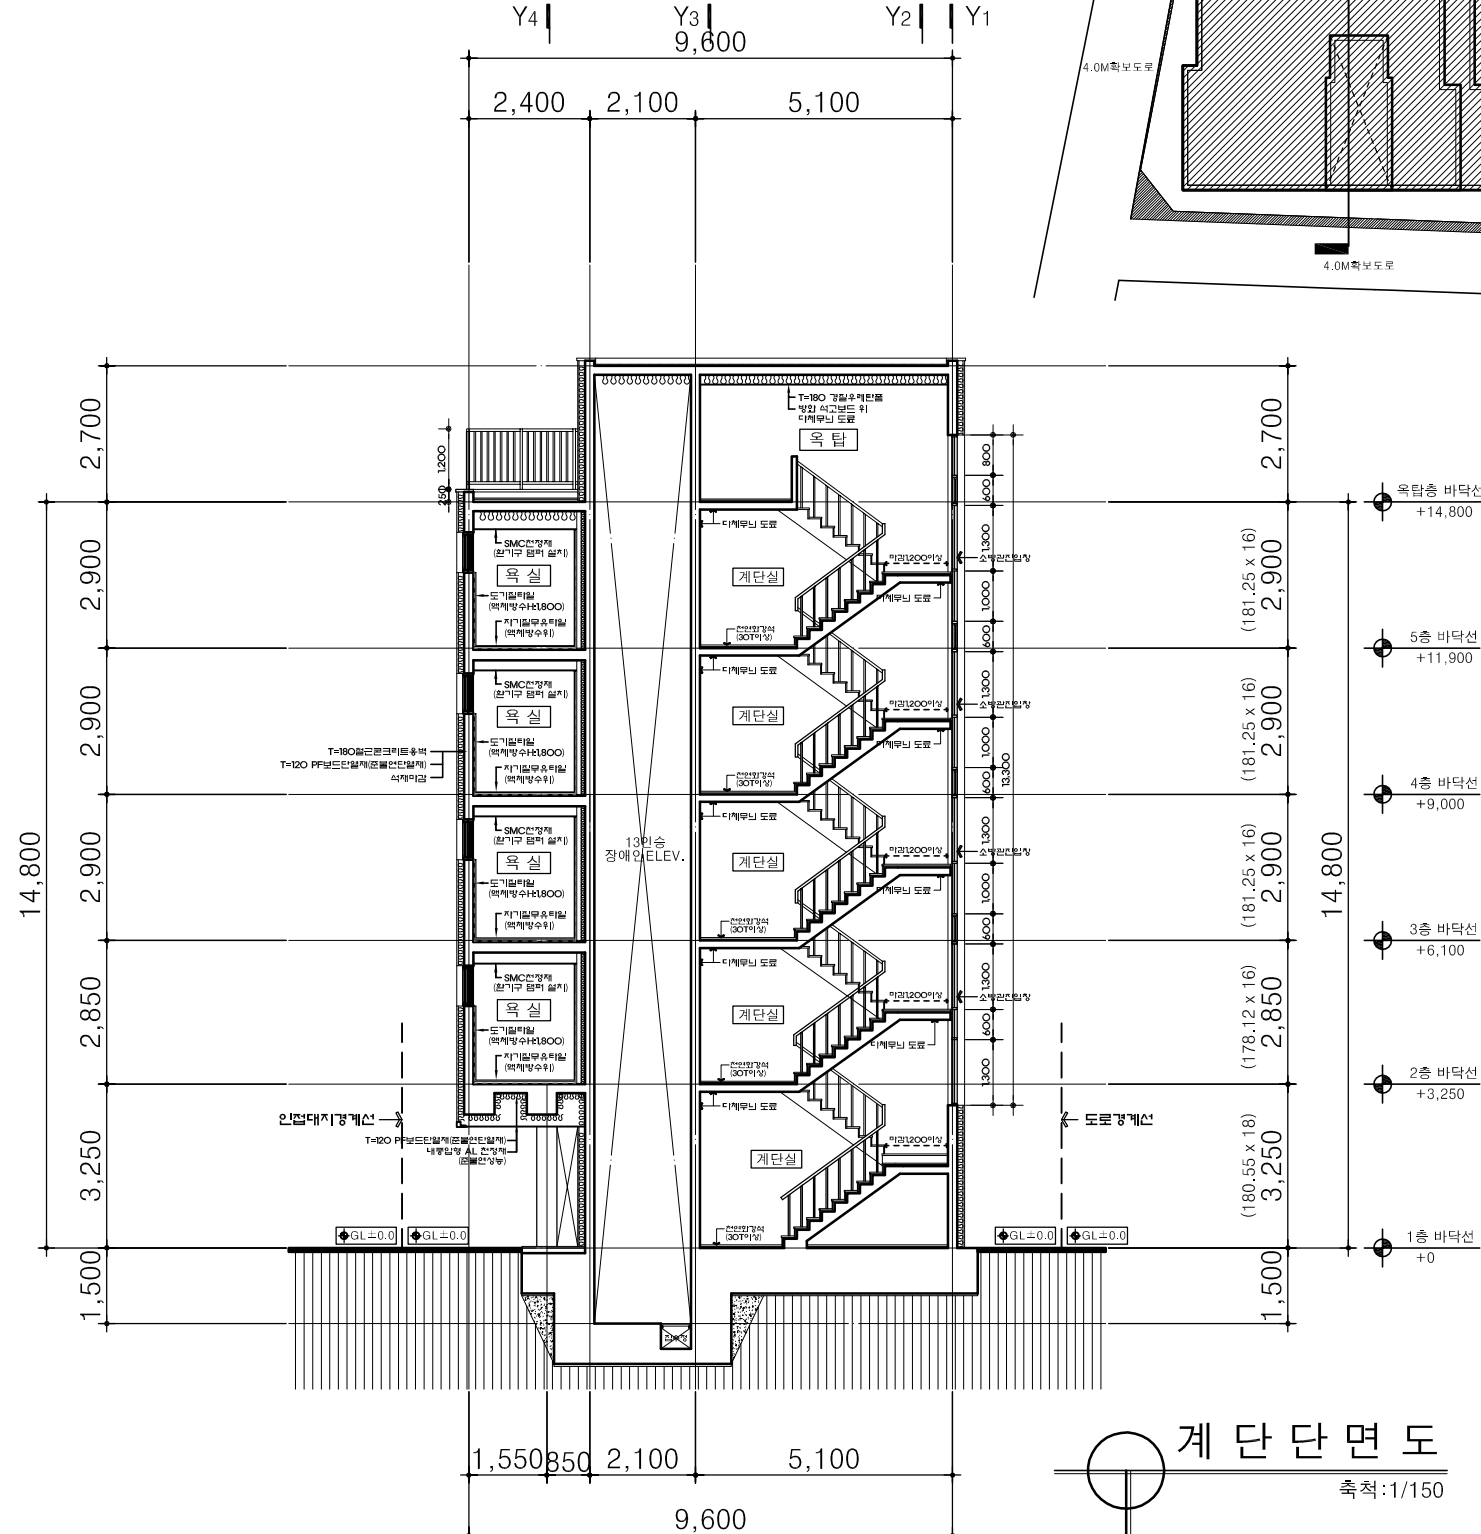

■ 단열재의 범례

건축물의 부위	두께	재질
외벽	직접 120	PF보드단열재 (준불연단열재)
	간접 80	경질우레탄폼
2층바닥 (바닥난방)	80	경질우레탄폼
지붕	180	경질우레탄폼
주차장	난방 60	PF보드단열재 (준불연단열재)
	비난방 120	PF보드단열재 (준불연단열재)

■ 계단

계단폭	1,200mm이상
단너비	260mm이상
단높이	200mm이하



서울시 송파구 석촌동 294-5,
신세계빌딩 302호
TEL:449-9106 FAX:449-9107
E-mail:jaesuk2@naver.com

NOTE	REVISION	PROJECT KINDS	PROJECT TITLE	DRAWN BY:	DRAWING TITLE	DRAWING NO.
			신림동 1609-18호 다세대주택 신축공사	CHECKED BY:	SCALE	
				DESIGNED BY:	1/150	A - 017
					DATE	2025. 09.