



PROJECT TITLE
사업명칭
(신림동 470-25호 외1필지)

도시형생활주택(소형주택)
다세대주택 신축공사

NAME OF DRAWING
도면명

조감도, 건축개요, 입면도

NOTE
주 기

▼ ▼

DATE ▲ REVISIONS ▲ NO.
일 자 수 정

DESIGNED BY
설 계

CHECKED BY
심 사

APPROVED BY
승 인

CONSULTANTS
협 동 설 계

SCALE
축 척 NONE

DATE
일 자 2023 . 11



DWG NO.
도면번호 A - 002

FILE NAME.
파일명

TECH 1 테크원
건축사무소

TECHONE ARCHITECTS & ENGINEERS
CO., LTD

TEL. 02)482-2466 (대)
FAX. 02)488-2466

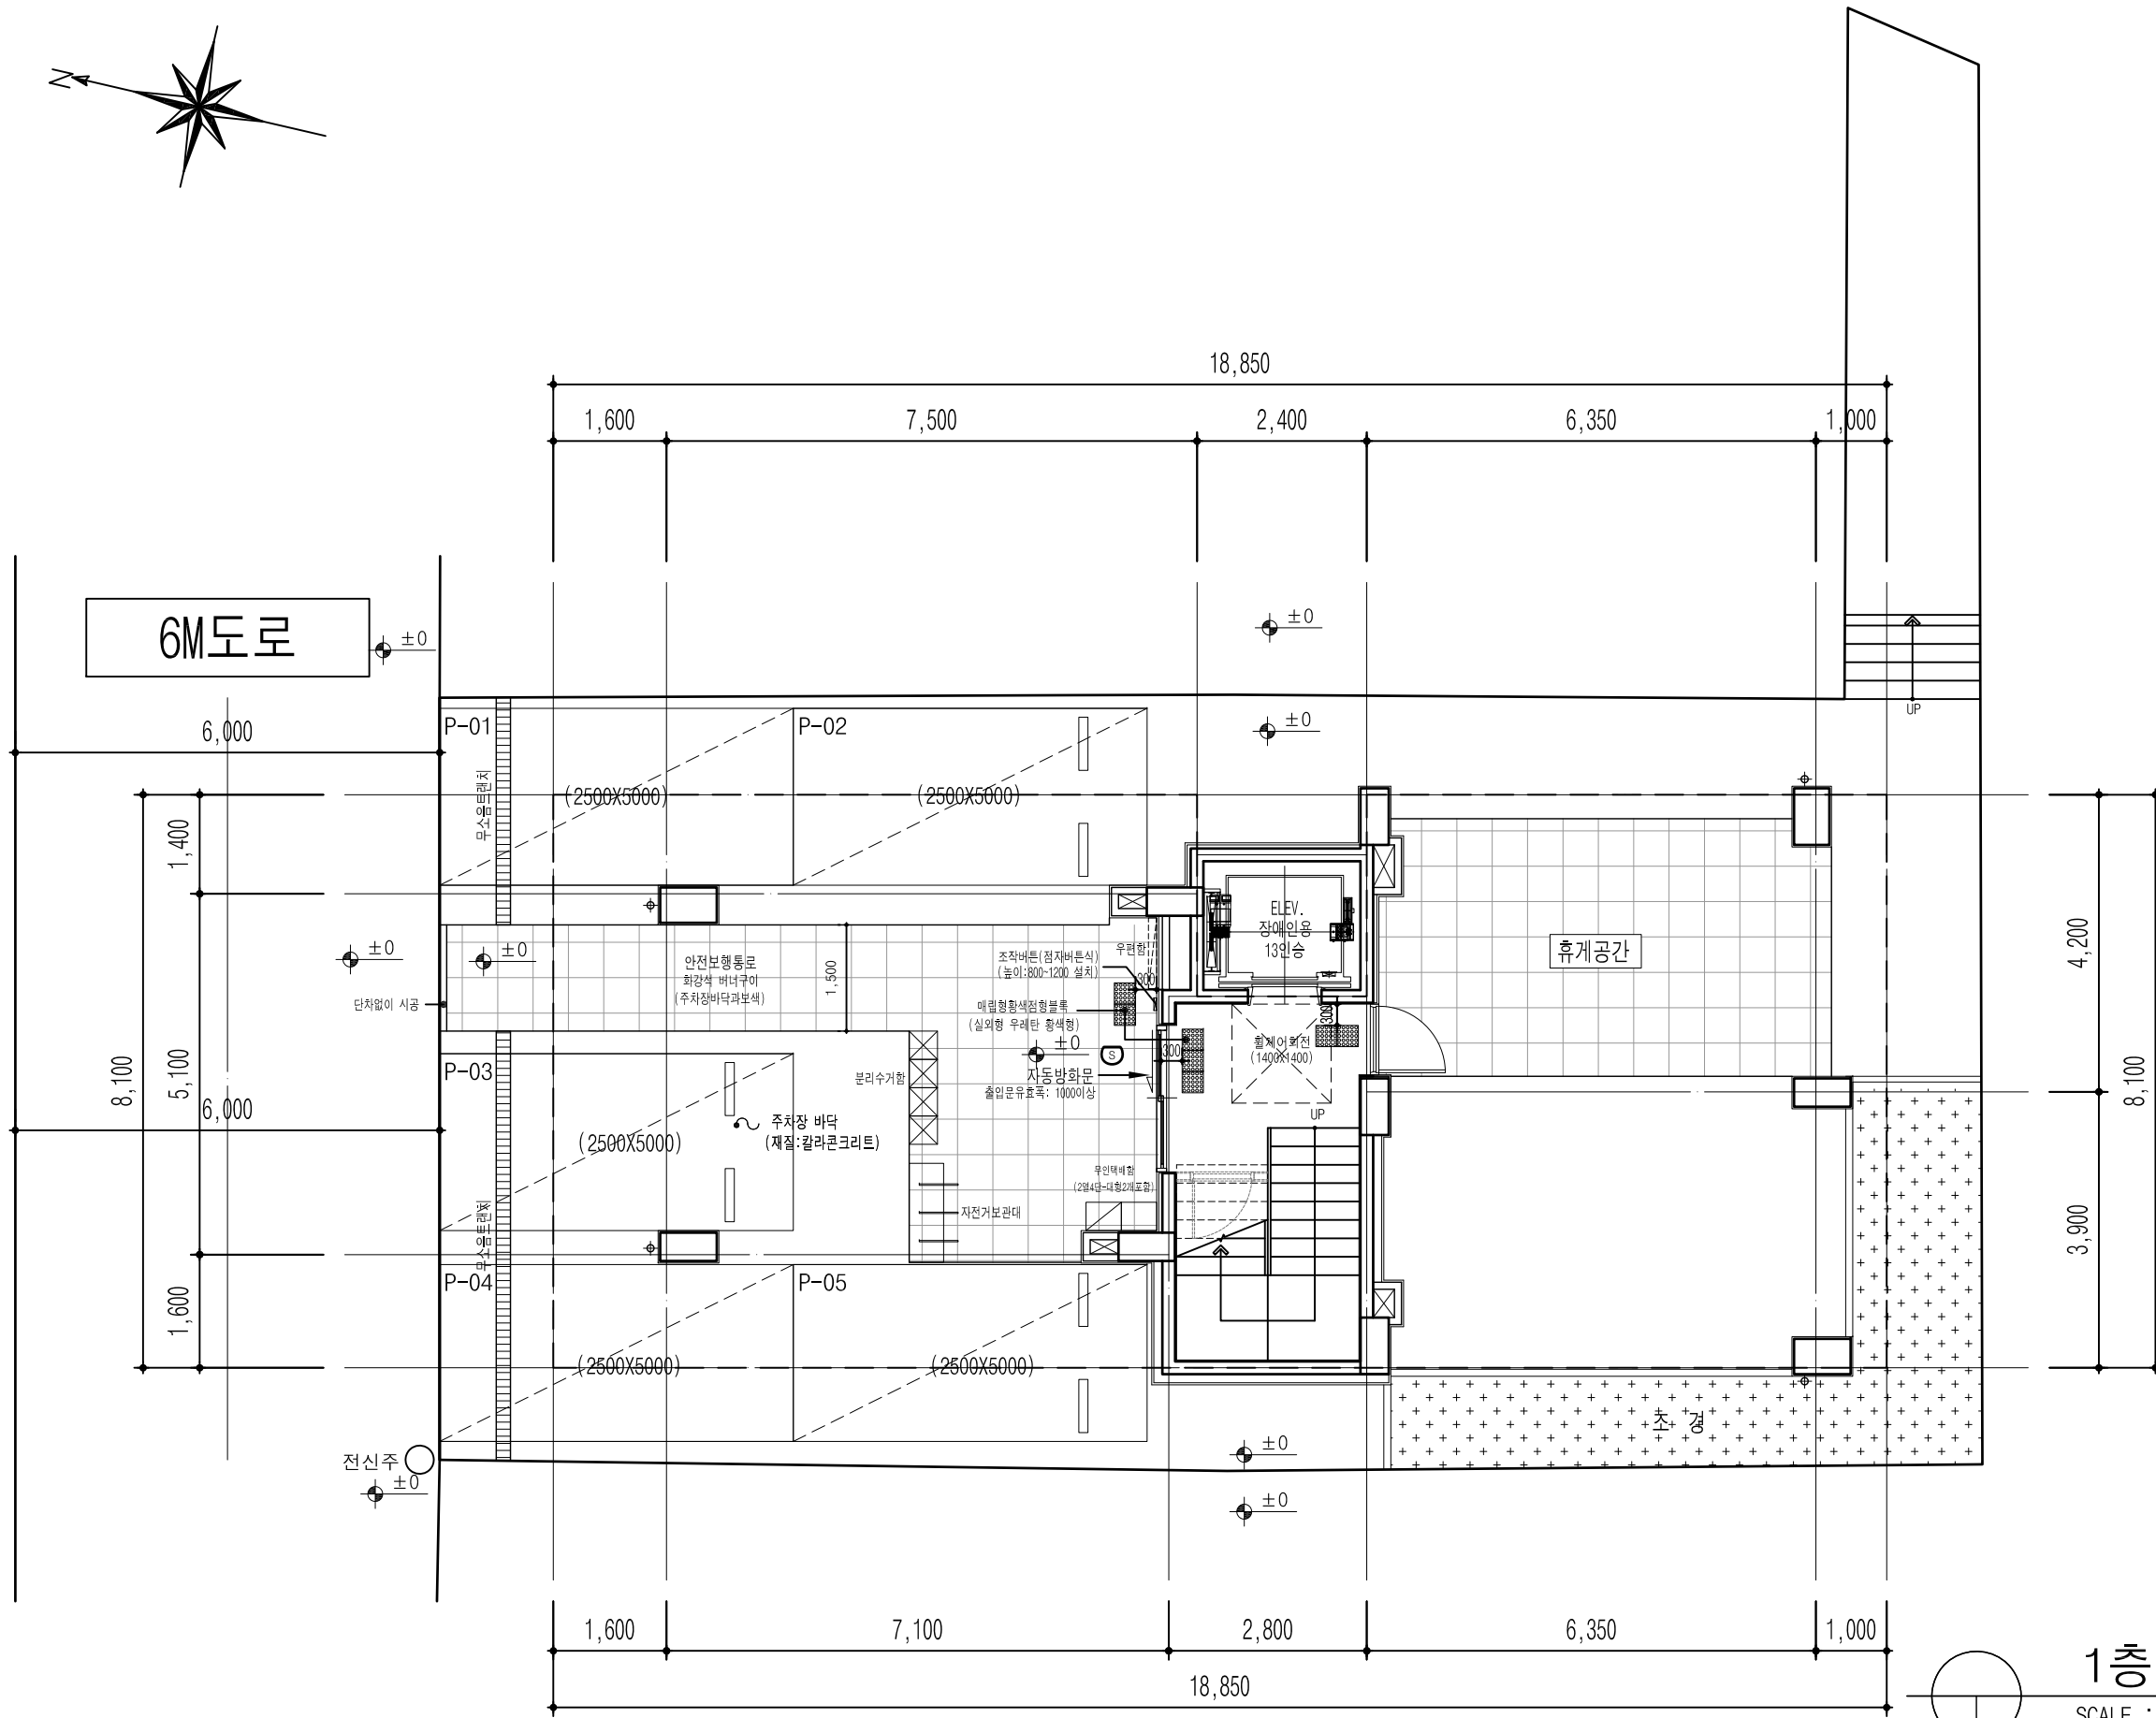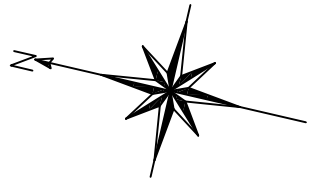

1층 평면도

SCALE : A3 : 1/100

PROJECT TITLE
사업명칭
(신림동 470-25호 외1필지)

도시형생활주택(소형주택)
다세대주택 신축공사

NAME OF DRAWING
도면명

1층 평면도

NOTE
주 기

- ③ 단독경보감지기(연기식)
- ⑤ 단독경보감지기(열감지)
- ⑧ ABC분말소화기(2.5KG)
- ⑨ 가스누설경보기
- ⑫ 일산화탄소경보기
- 차면시설
- 보일러
- 에어컨 실외기

DATE
일 자

REVISIONS
수정

NO.

DESIGNED BY
설 계

CHECKED BY
심 사

APPROVED BY
승 인


CONSULTANTS
협동설계

SCALE
축척 1 / 100




DATE
일 자 2023 . 11

DWG NO.
도면번호 A - 021

FILE NAME.
파일명

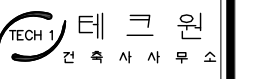

TECHONE ARCHITECTS & ENGINEERS
CO., LTD
TEL. 02)482-2466 (re)
FAX. 02)488-2466

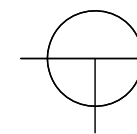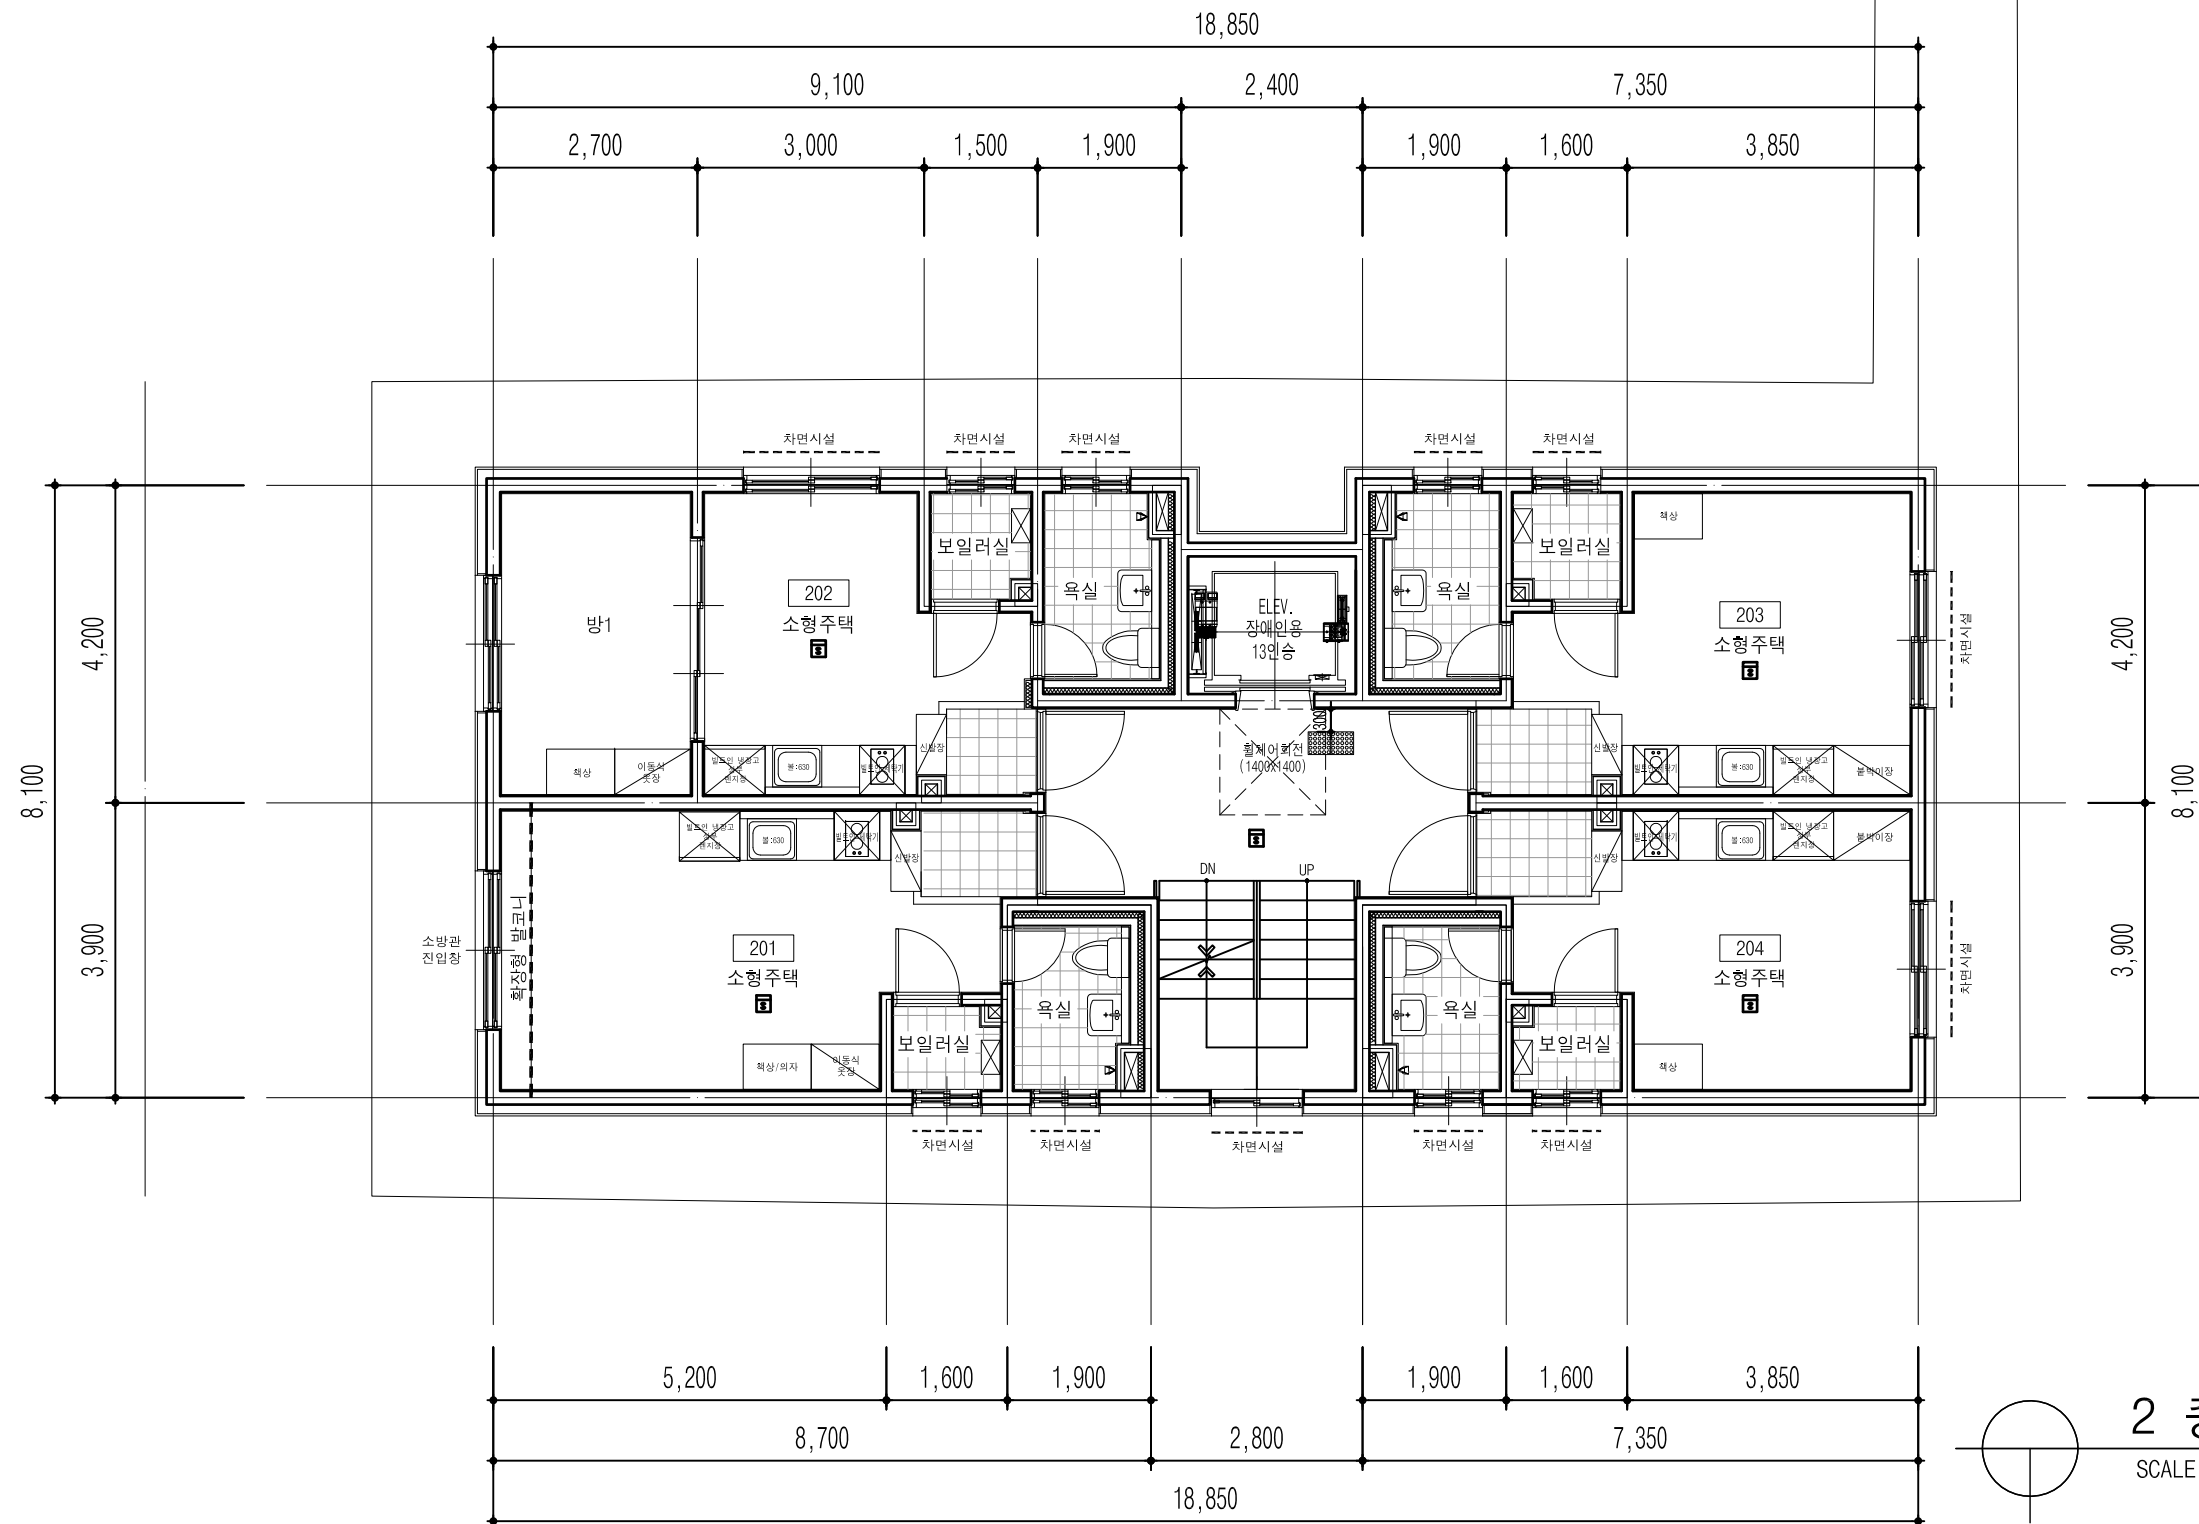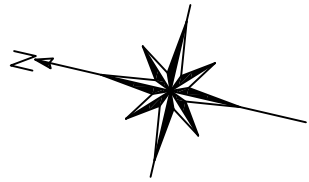

2 층 평면도

SCALE : A3 : 1/100

PROJECT TITLE
사 업 명 칭
(신림동 470-25호 외1필지)

도시형생활주택(소형주택)
다세대주택 신축공사

NAME OF DRAWING
도 면 명

2 층 평면도

NOTE
주 기

- ③ 단독경보감지기(연기식)
- ⑤ 단독경보감지기(열감지)
- ② ABC분말소화기(2.5KG)
- ⑥ 가스누설경보기
- ⑦ 일산화탄소경보기

- 차면시설
- 보일러
- 에어컨 실외기

DATE
일 자

REVISIONS
수 정

NO.

DESIGNED BY
설 계

CHECKED BY
심 사

APPROVED BY
승 인

CONSULTANTS
협 동 설 계

SCALE
축 척 1 / 100

DATE
일 자 2023 . 11




DWG NO.
도 면 번 호 A - 022

FILE NAME.
화 일 명

TECH 1 테 크 원
건축사사무소

TECHONE ARCHITECTS & ENGINEERS
CO., LTD

TEL. 02)482-2466 (대)
FAX. 02)488-2466

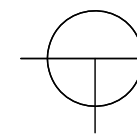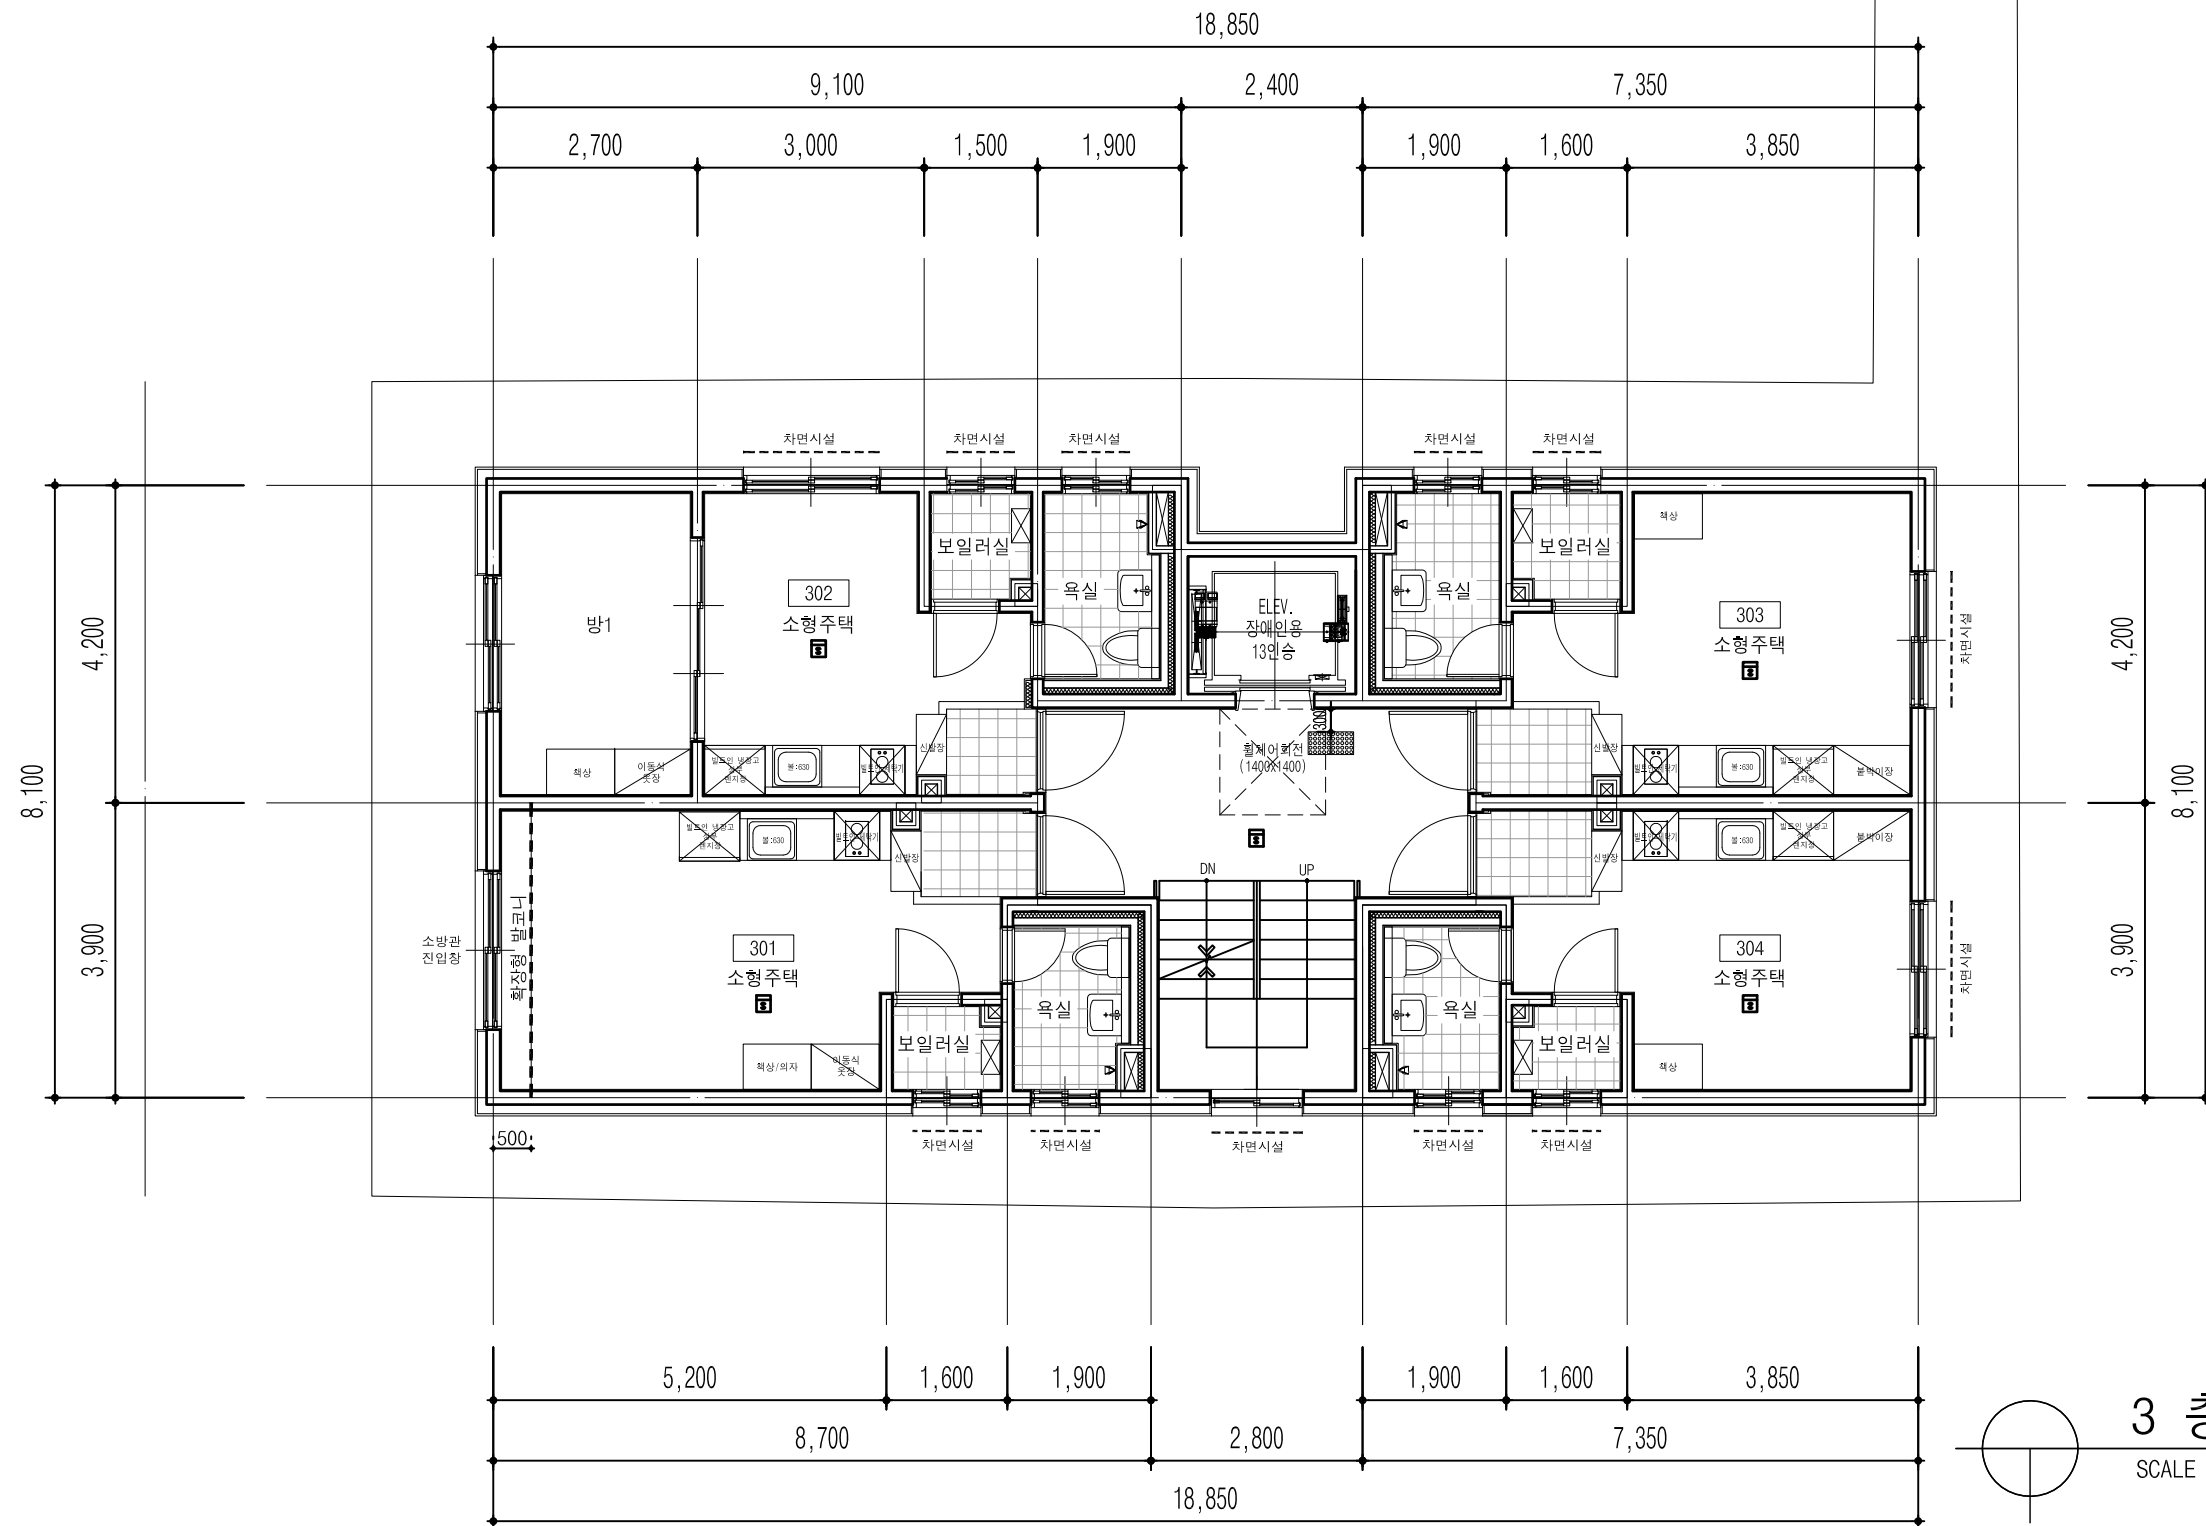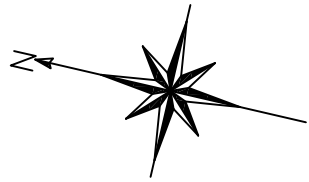

3 층 평면도

SCALE : A3 : 1/100

PROJECT TITLE
사 업 명 칭
(신림동 470-25호 외1필지)

도시형생활주택(소형주택)
다세대주택 신축공사

NAME OF DRAWING
도 면 명

3 층 평면도

NOTE
주 기

- ③ 단독경보감지기(연기식)
- ⑤ 단독경보감지기(열감지)
- ② ABC분말소화기(2.5KG)
- ⑥ 가스누설경보기
- ⑦ 일산화탄소경보기
- 차면시설
- 보일러
- 에어컨 실외기

DATE
일 자

REVISIONS
수 정

NO.

DESIGNED BY
설 계

CHECKED BY
심 사

APPROVED BY
승 인

CONSULTANTS
협 동 설 계

SCALE
축 척 1 / 100

DATE
일 자 2023 . 11




DWG NO.
도 면 번 호 A - 022

FILE NAME.
화 일 명

TECH 1 테 크 원
건축사사무소

TECHONE ARCHITECTS & ENGINEERS
CO., LTD

TEL. 02)482-2466 (re)
FAX. 02)488-2466

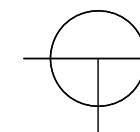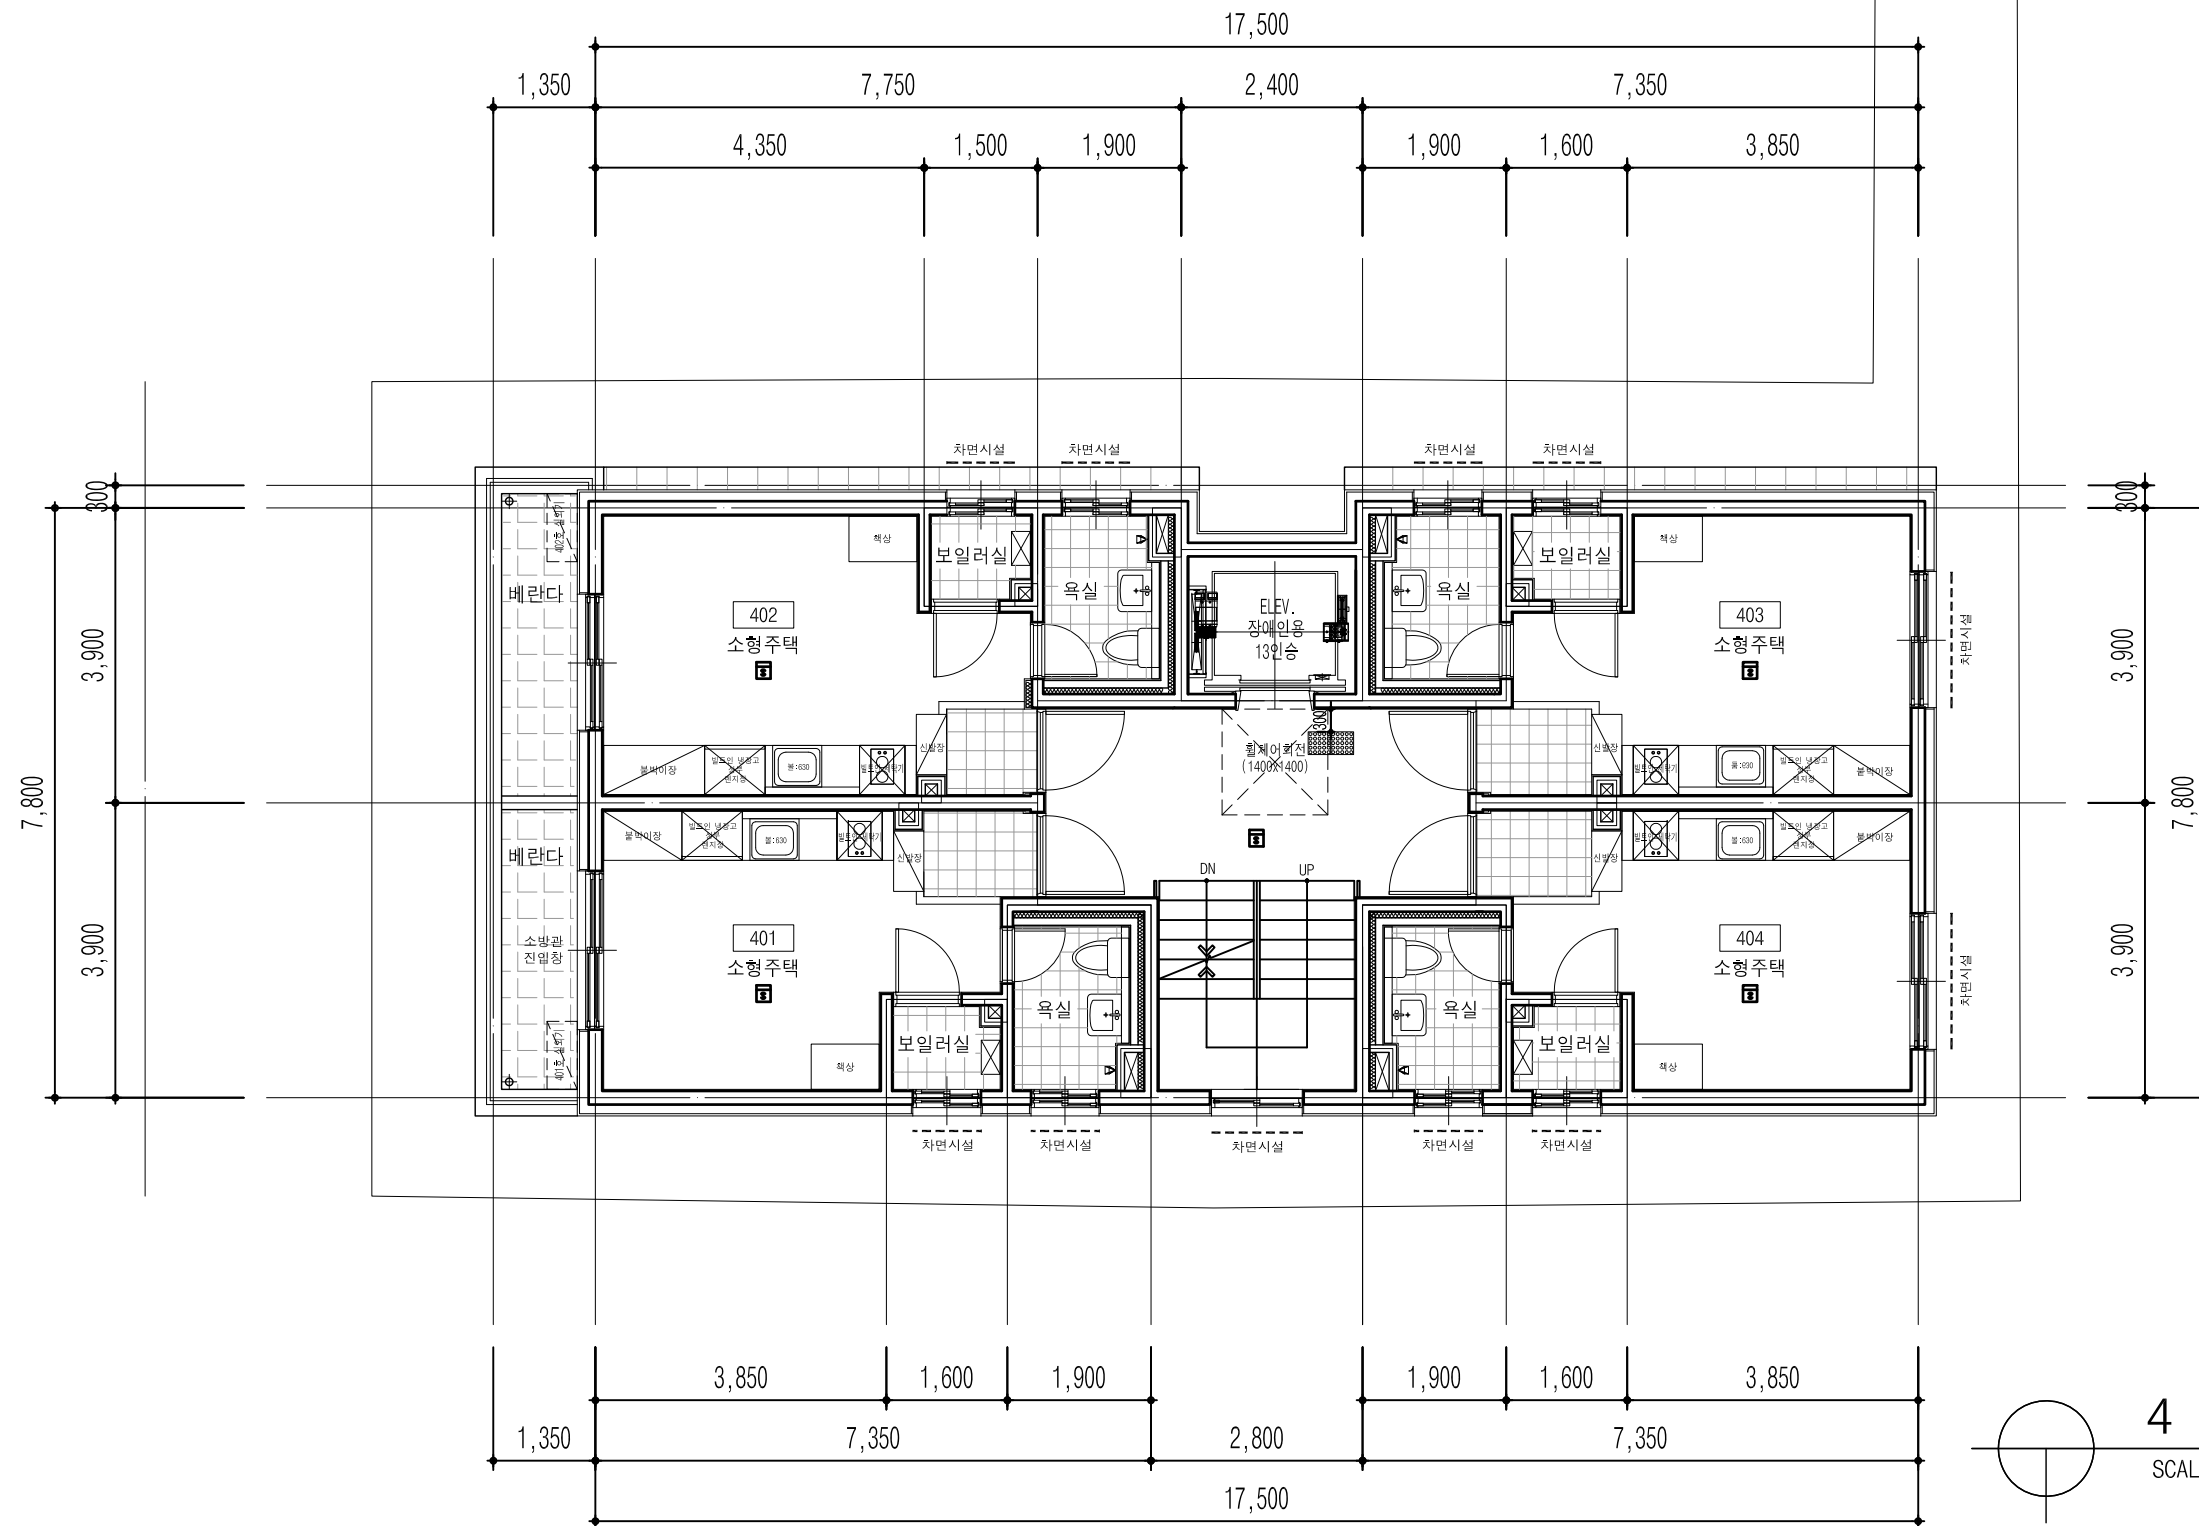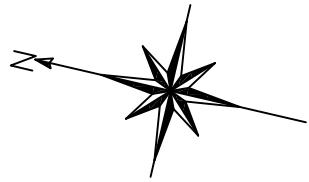

4 층 평면도

SCALE : A3 : 1/100

PROJECT TITLE
사 업 명 칭
(신림동 470-25호 외1필지)

도시형생활주택(소형주택)
다세대주택 신축공사

NAME OF DRAWING
도 면 명

4 층 평면도

NOTE
주 기

- ③ 단독경보감지기(연기식)
- ⑤ 단독경보감지기(열감지)
- ② ABC분말소화기(2.5KG)
- ⑥ 가스누설경보기
- ⑦ 일산화탄소경보기

- 차면시설
- 보일러
- 에어컨 실외기

DATE
일 자

REVISIONS
수 정

NO.

DESIGNED BY
설 계

CHECKED BY
심 사

APPROVED BY
승 인

CONSULTANTS
협 동 설 계

SCALE
축 척 1 / 100

DATE
일 자 2023 . 11




DWG NO.
도 면 번 호 A - 023

FILE NAME.
화 일 명

TECH 1 테 크 원
건축사사무소

TECHONE ARCHITECTS & ENGINEERS
CO., LTD

TEL. 02)482-2466 (대)
FAX. 02)488-2466

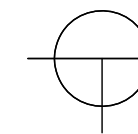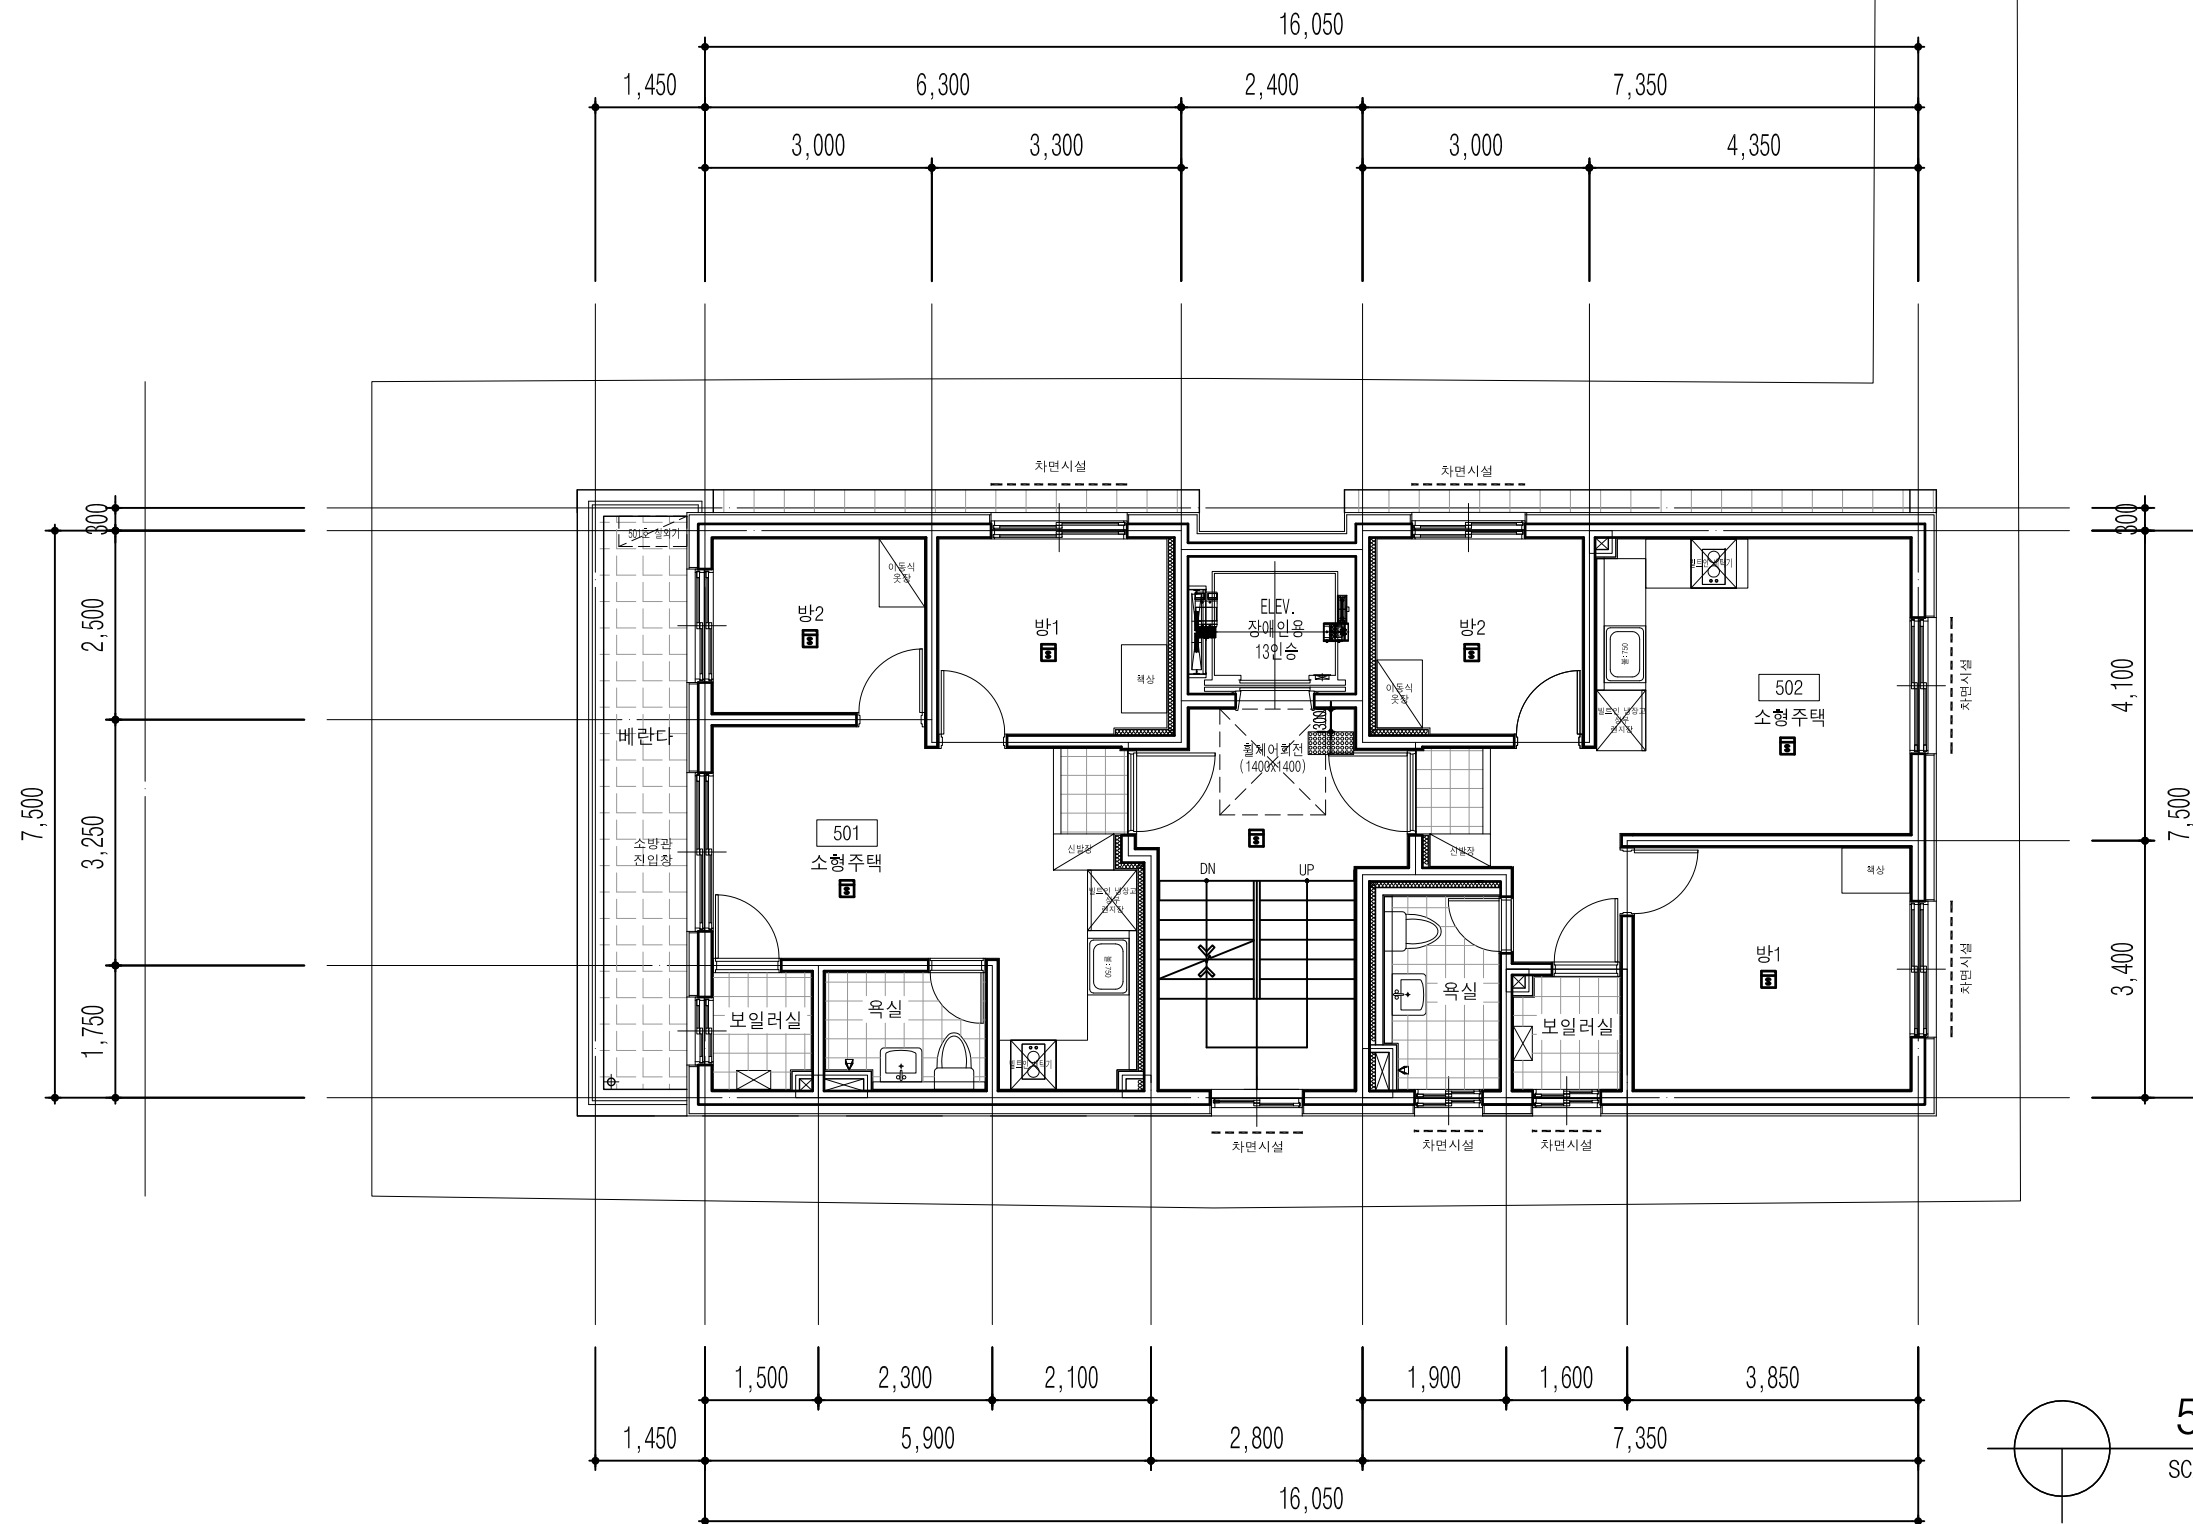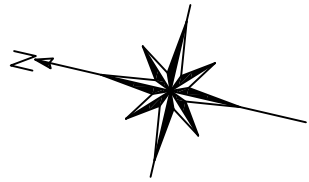

5층 평면도
SCALE : A3 : 1/100

PROJECT TITLE
사 업 명 칭
(신림동 470-25호 외1필지)

도시형생활주택(소형주택)
다세대주택 신축공사

NAME OF DRAWING
도 면 명

5층 평면도

NOTE
주 기

- 단독경보감지기(연기식)
- ⑤ 단독경보감지기(열감지)
- ② ABC분말소화기(2.5KG)
- ⑥ 가스누설경보기
- ③ 일산화탄소경보기
- 차면시설
- ☒ 보일러
- ☒ 에어컨 실외기

DATE ▲ REVISIONS ▲ NO.
일 자 수 정

DESIGNED BY
설 계

CHECKED BY
심 사

APPROVED BY
승 인


CONSULTANTS
협 동 설 계

SCALE
축 척 1 / 100



DATE
일 자 2023 . 11

DWG NO.
도 면 번 호 A - 024

FILE NAME.
화 일 명

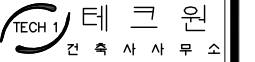

TECHONE ARCHITECTS & ENGINEERS
CO., LTD
TEL. 02)482-2466 (r)
FAX. 02)488-2466

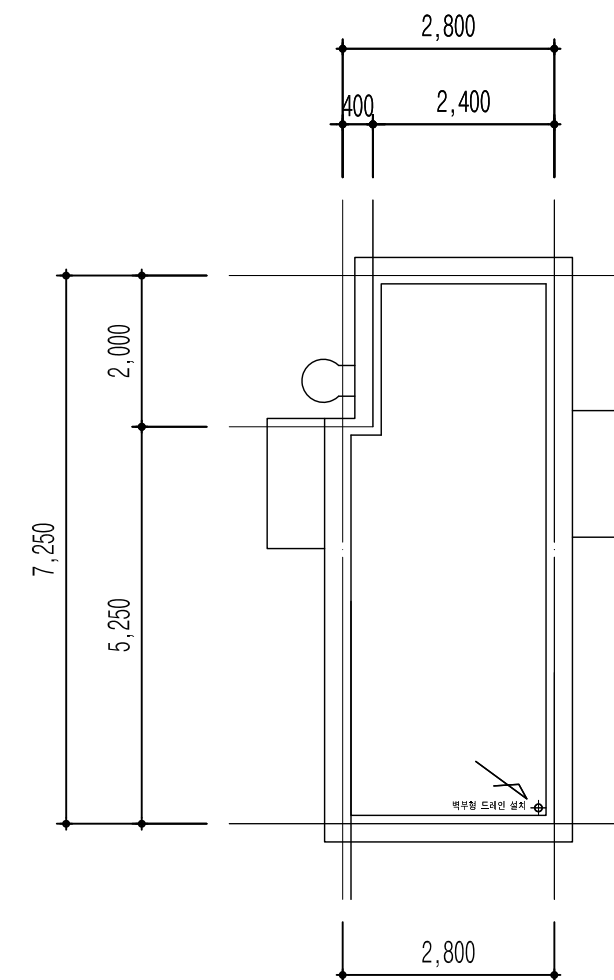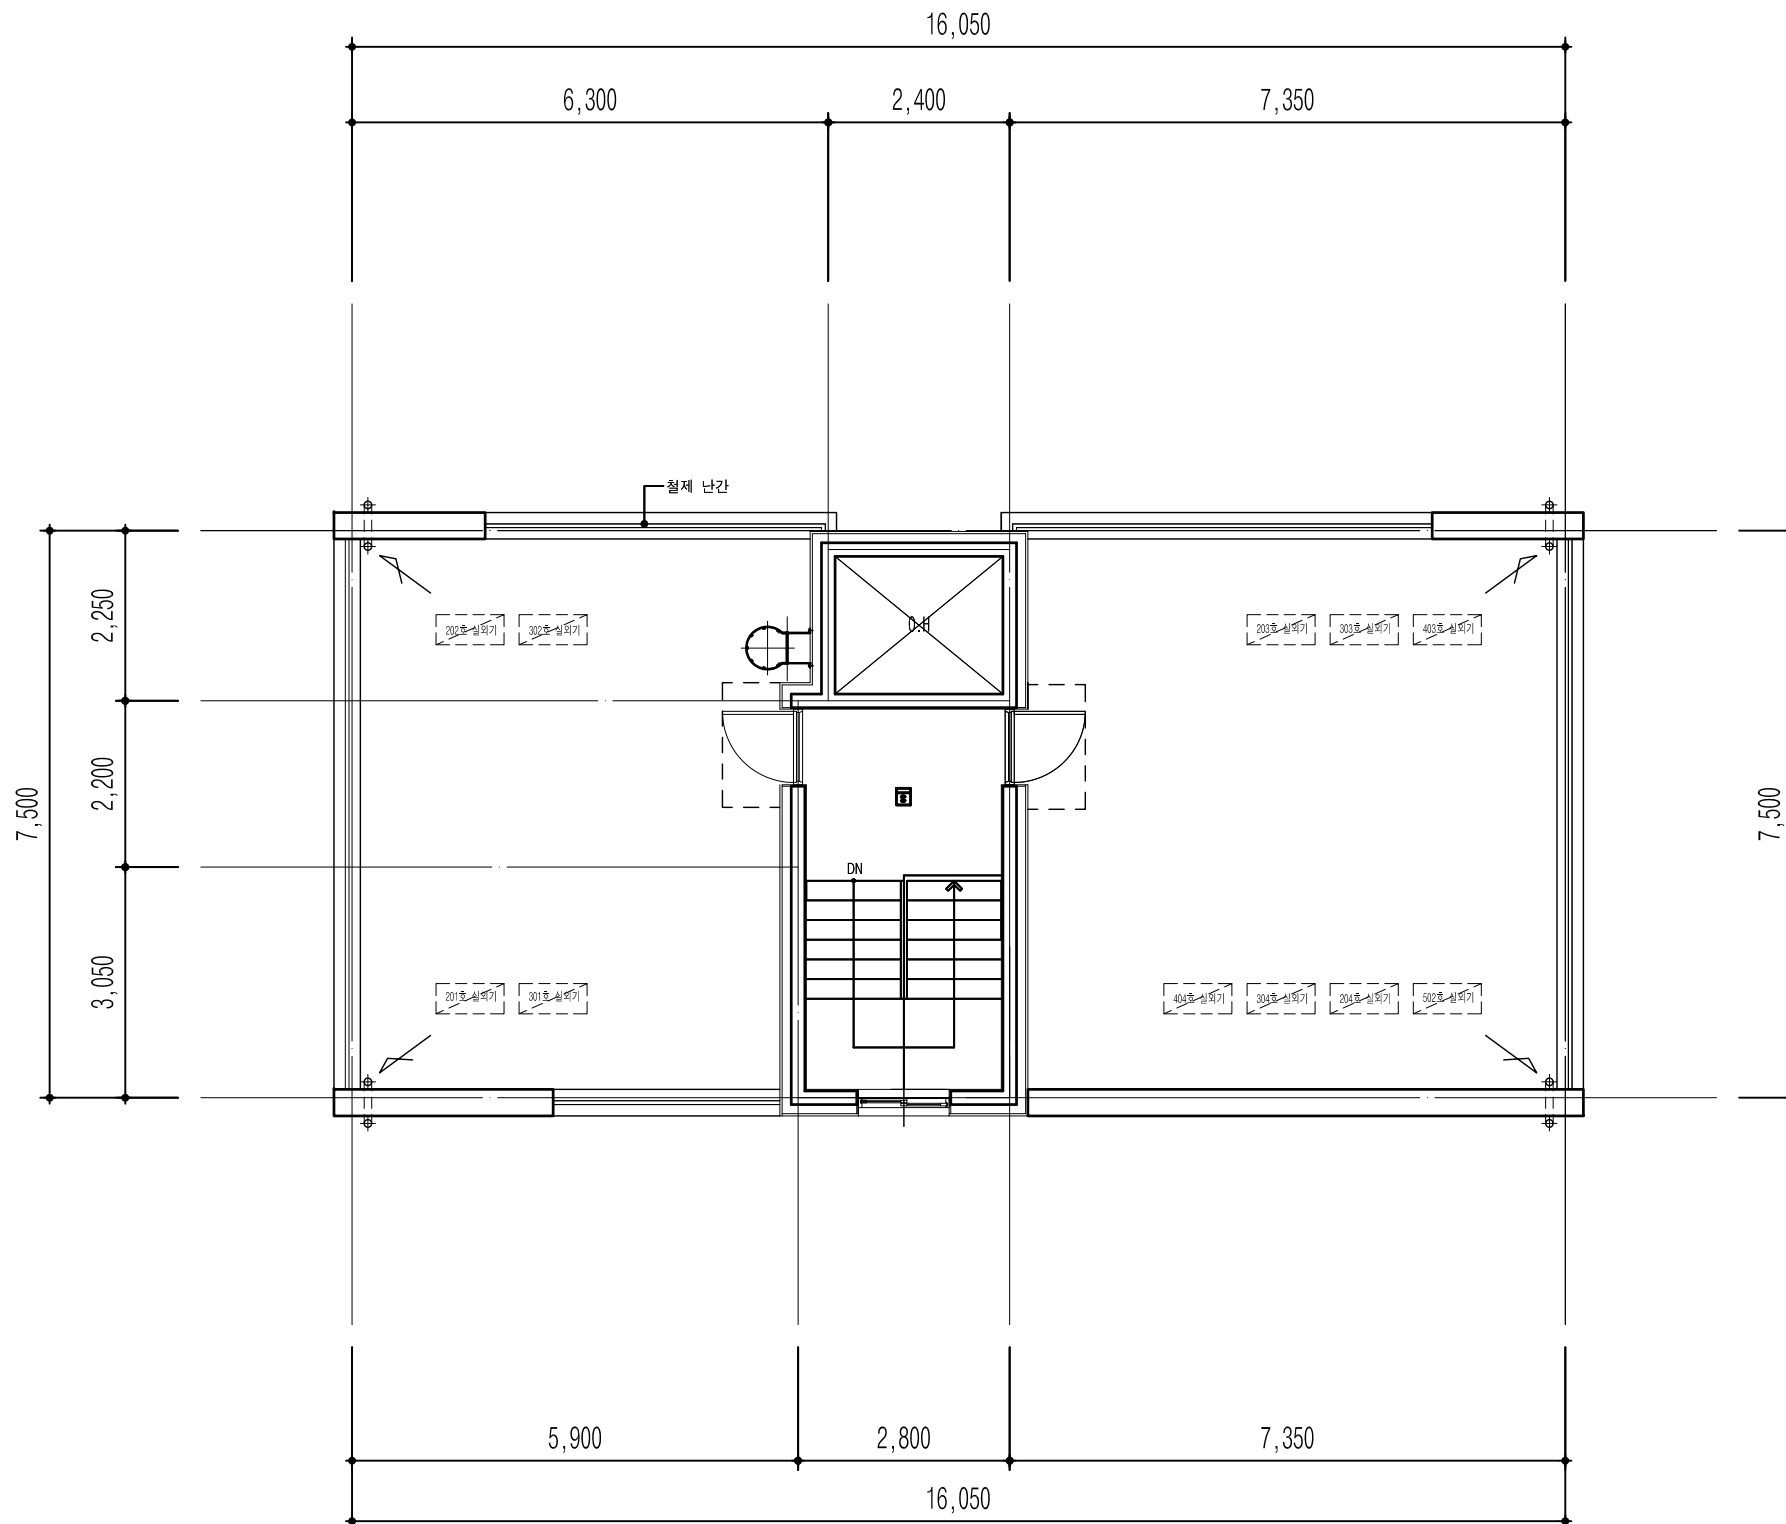

지붕 및 옥탑평면도

SCALE : A3 : 1/100

TEL. 02)482-2466 (代)
FAX. 02)488-2466

PROJECT TITLE
사 업 명 칭
(신림동 470-25호 외1필지)

도시형생활주택(소형주택)
다세대주택 신축공사

NAME OF DRAWING
도 면 명

입면도-1

NOTE
주 기

창호 PVC 블랙
소방관진입창 - 스티커부착

DATE
일 자
REVISIONS
수 정
NO.

DESIGNED BY
설 계

CHECKED BY
심 사

APPROVED BY
승 인

CONSULTANTS
협 동 설 계

SCALE
축 척
1 / 100

DATE
일 자
2023 . 11



DWG NO.
도 면 번 호
A - 031

FILE NAME
화 일 명


TECH 1 테 크 원
건축사사무소

TECHONE ARCHITECTS & ENGINEERS
CO., LTD


TEL. 02)482-2466 (대)
FAX. 02)488-2466

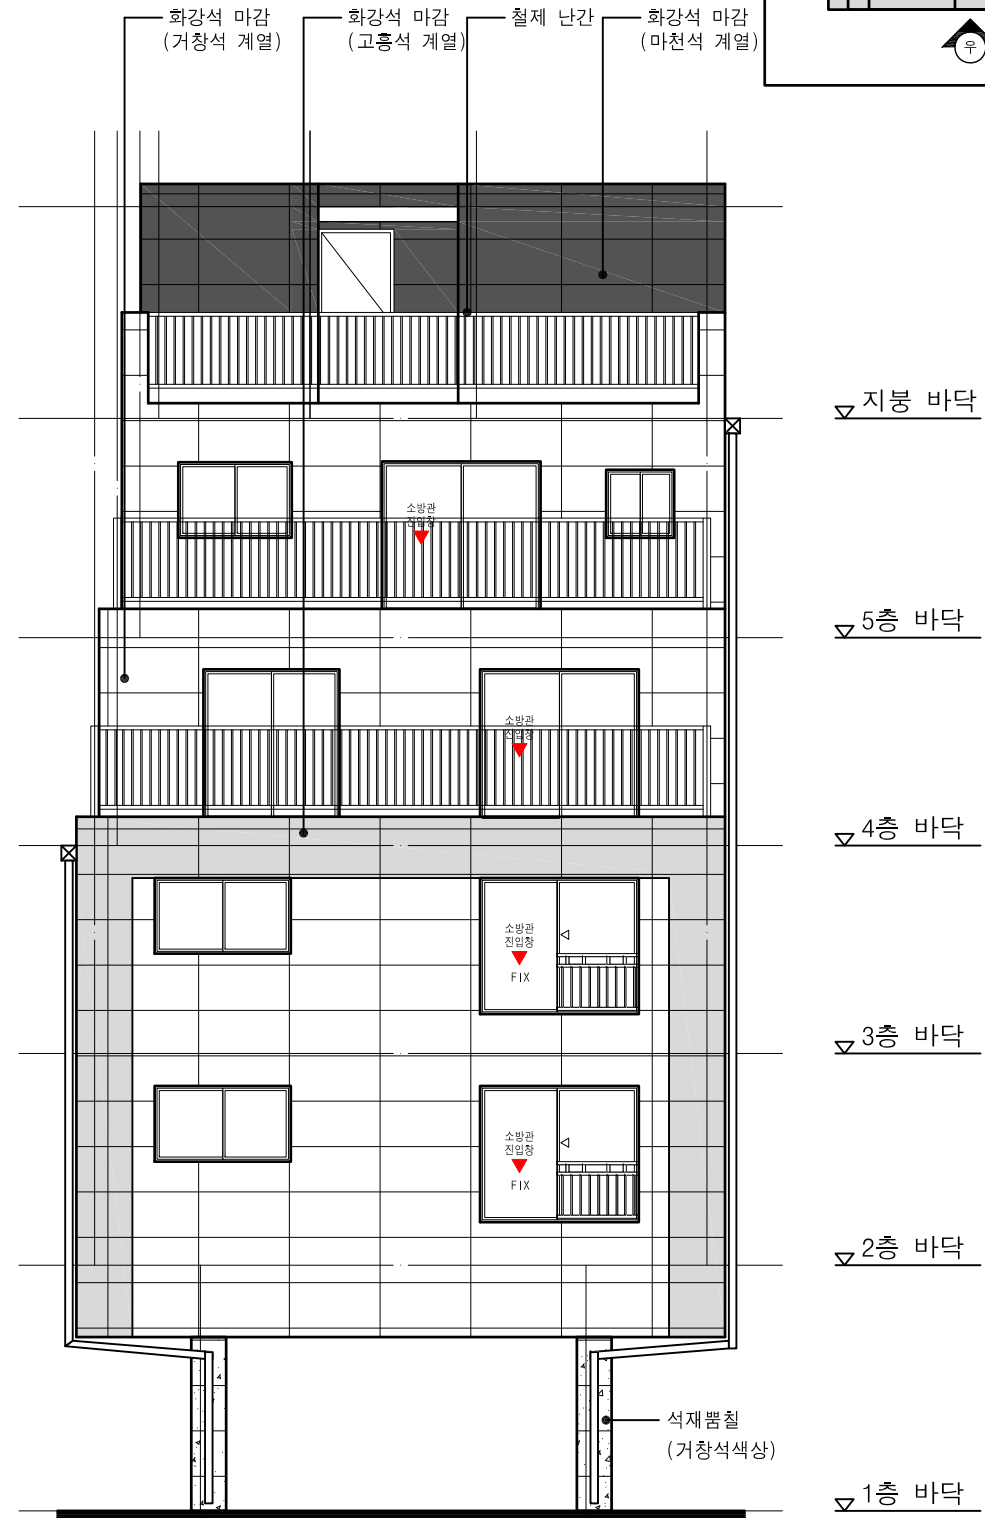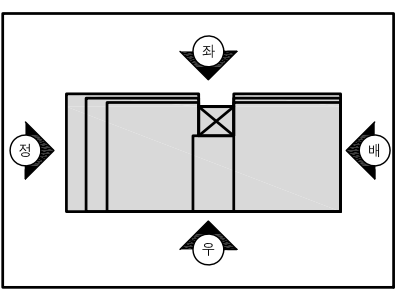

정 면 도
SCALE : A3 : 1/100

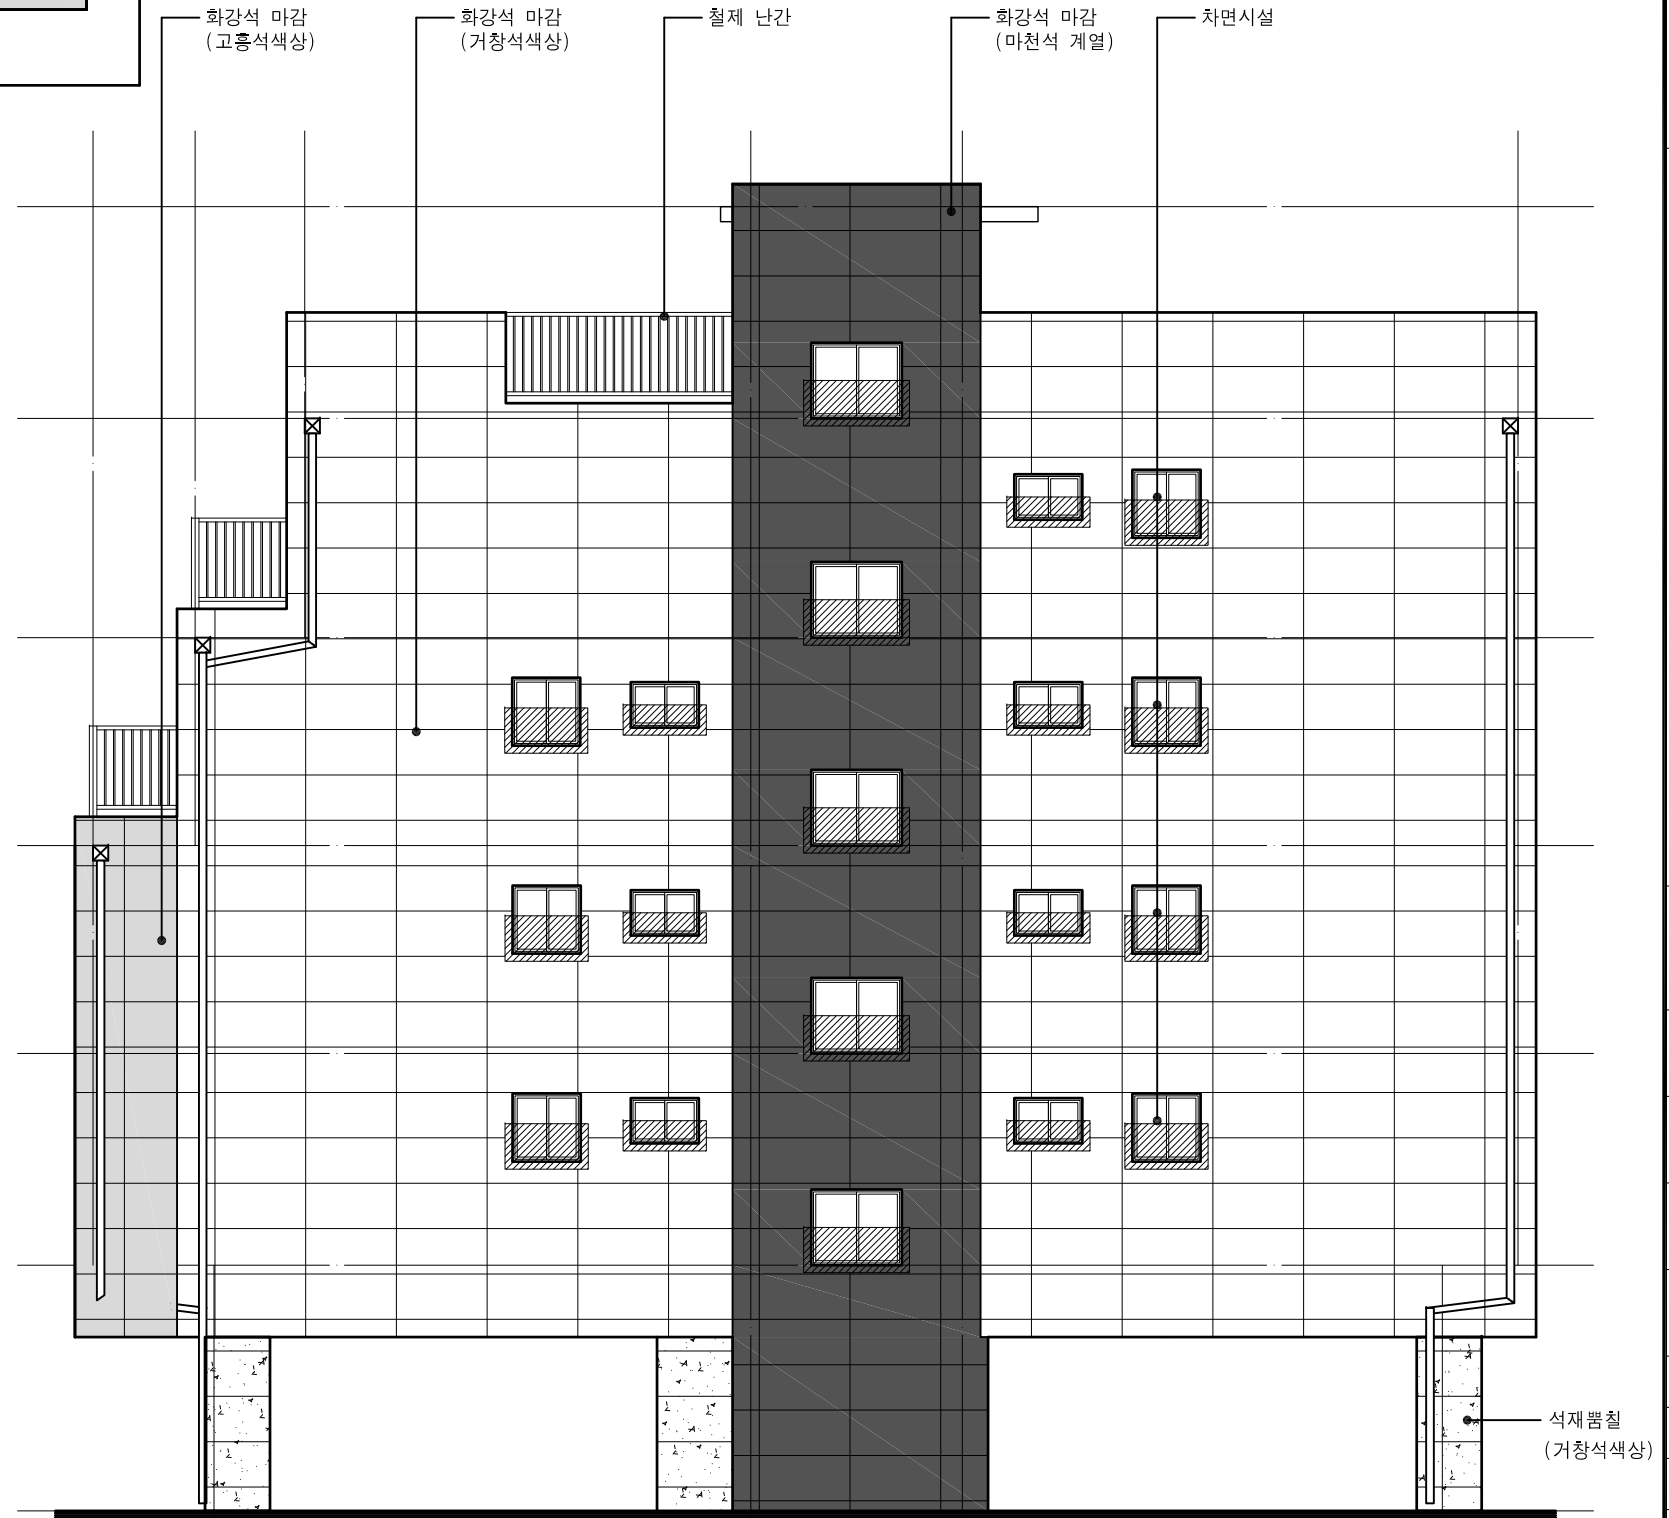

우 측 면 도
SCALE : A3 : 1/100

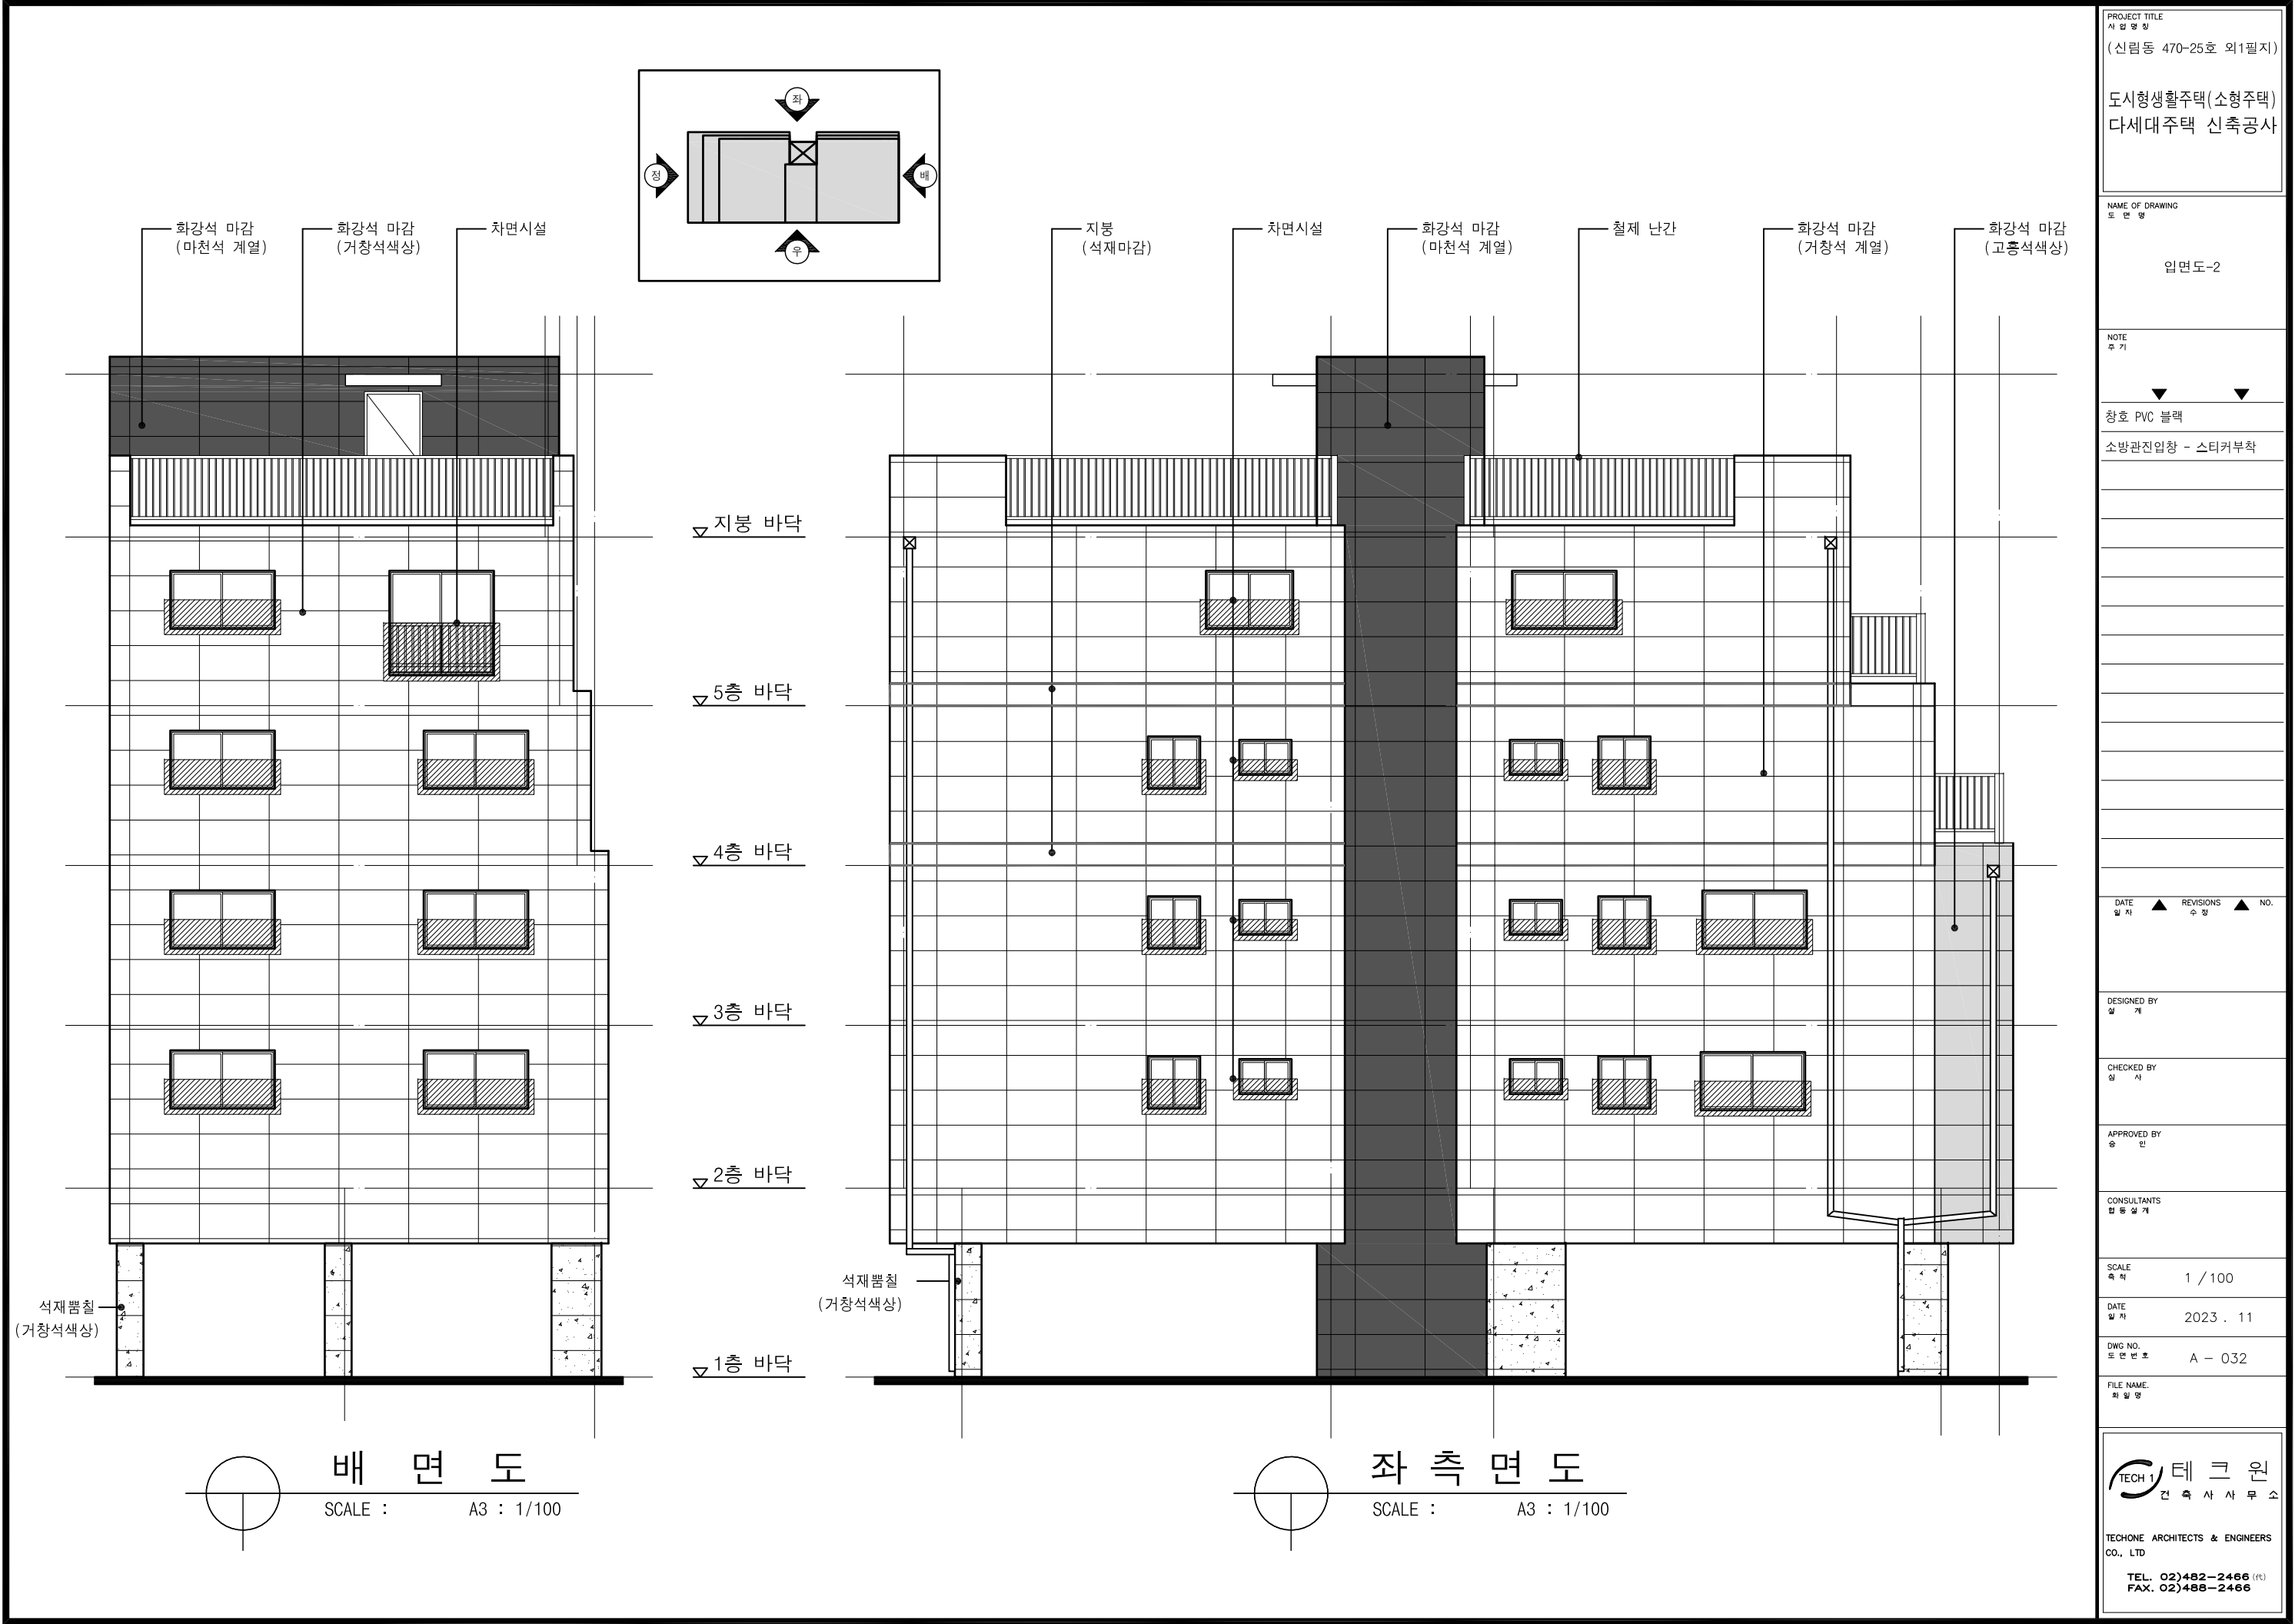

PROJECT TITLE
사업명칭
(신림동 470-25호 외1필지)

도시형생활주택(소형주택)
다세대주택 신축공사

NAME OF DRAWING
도면명

임면도-2

NOTE
주 기

창호 PVC 블랙
소방관진입창 - 스티커부착

DATE ▲ REVISIONS ▲ NO.
일 자 수정

DESIGNED BY
설 계

CHECKED BY
심 사

APPROVED BY
승 인

CONSULTANTS
협 동 설 계

SCALE
축척 1 / 100

DATE
일 자 2023 . 11

DWG NO.
도면번호 A - 032

FILE NAME.
파일명

TECH 1 테크원
건축사무소

TECHONE ARCHITECTS & ENGINEERS
CO., LTD

TEL. 02)482-2466 (대)
FAX. 02)488-2466