



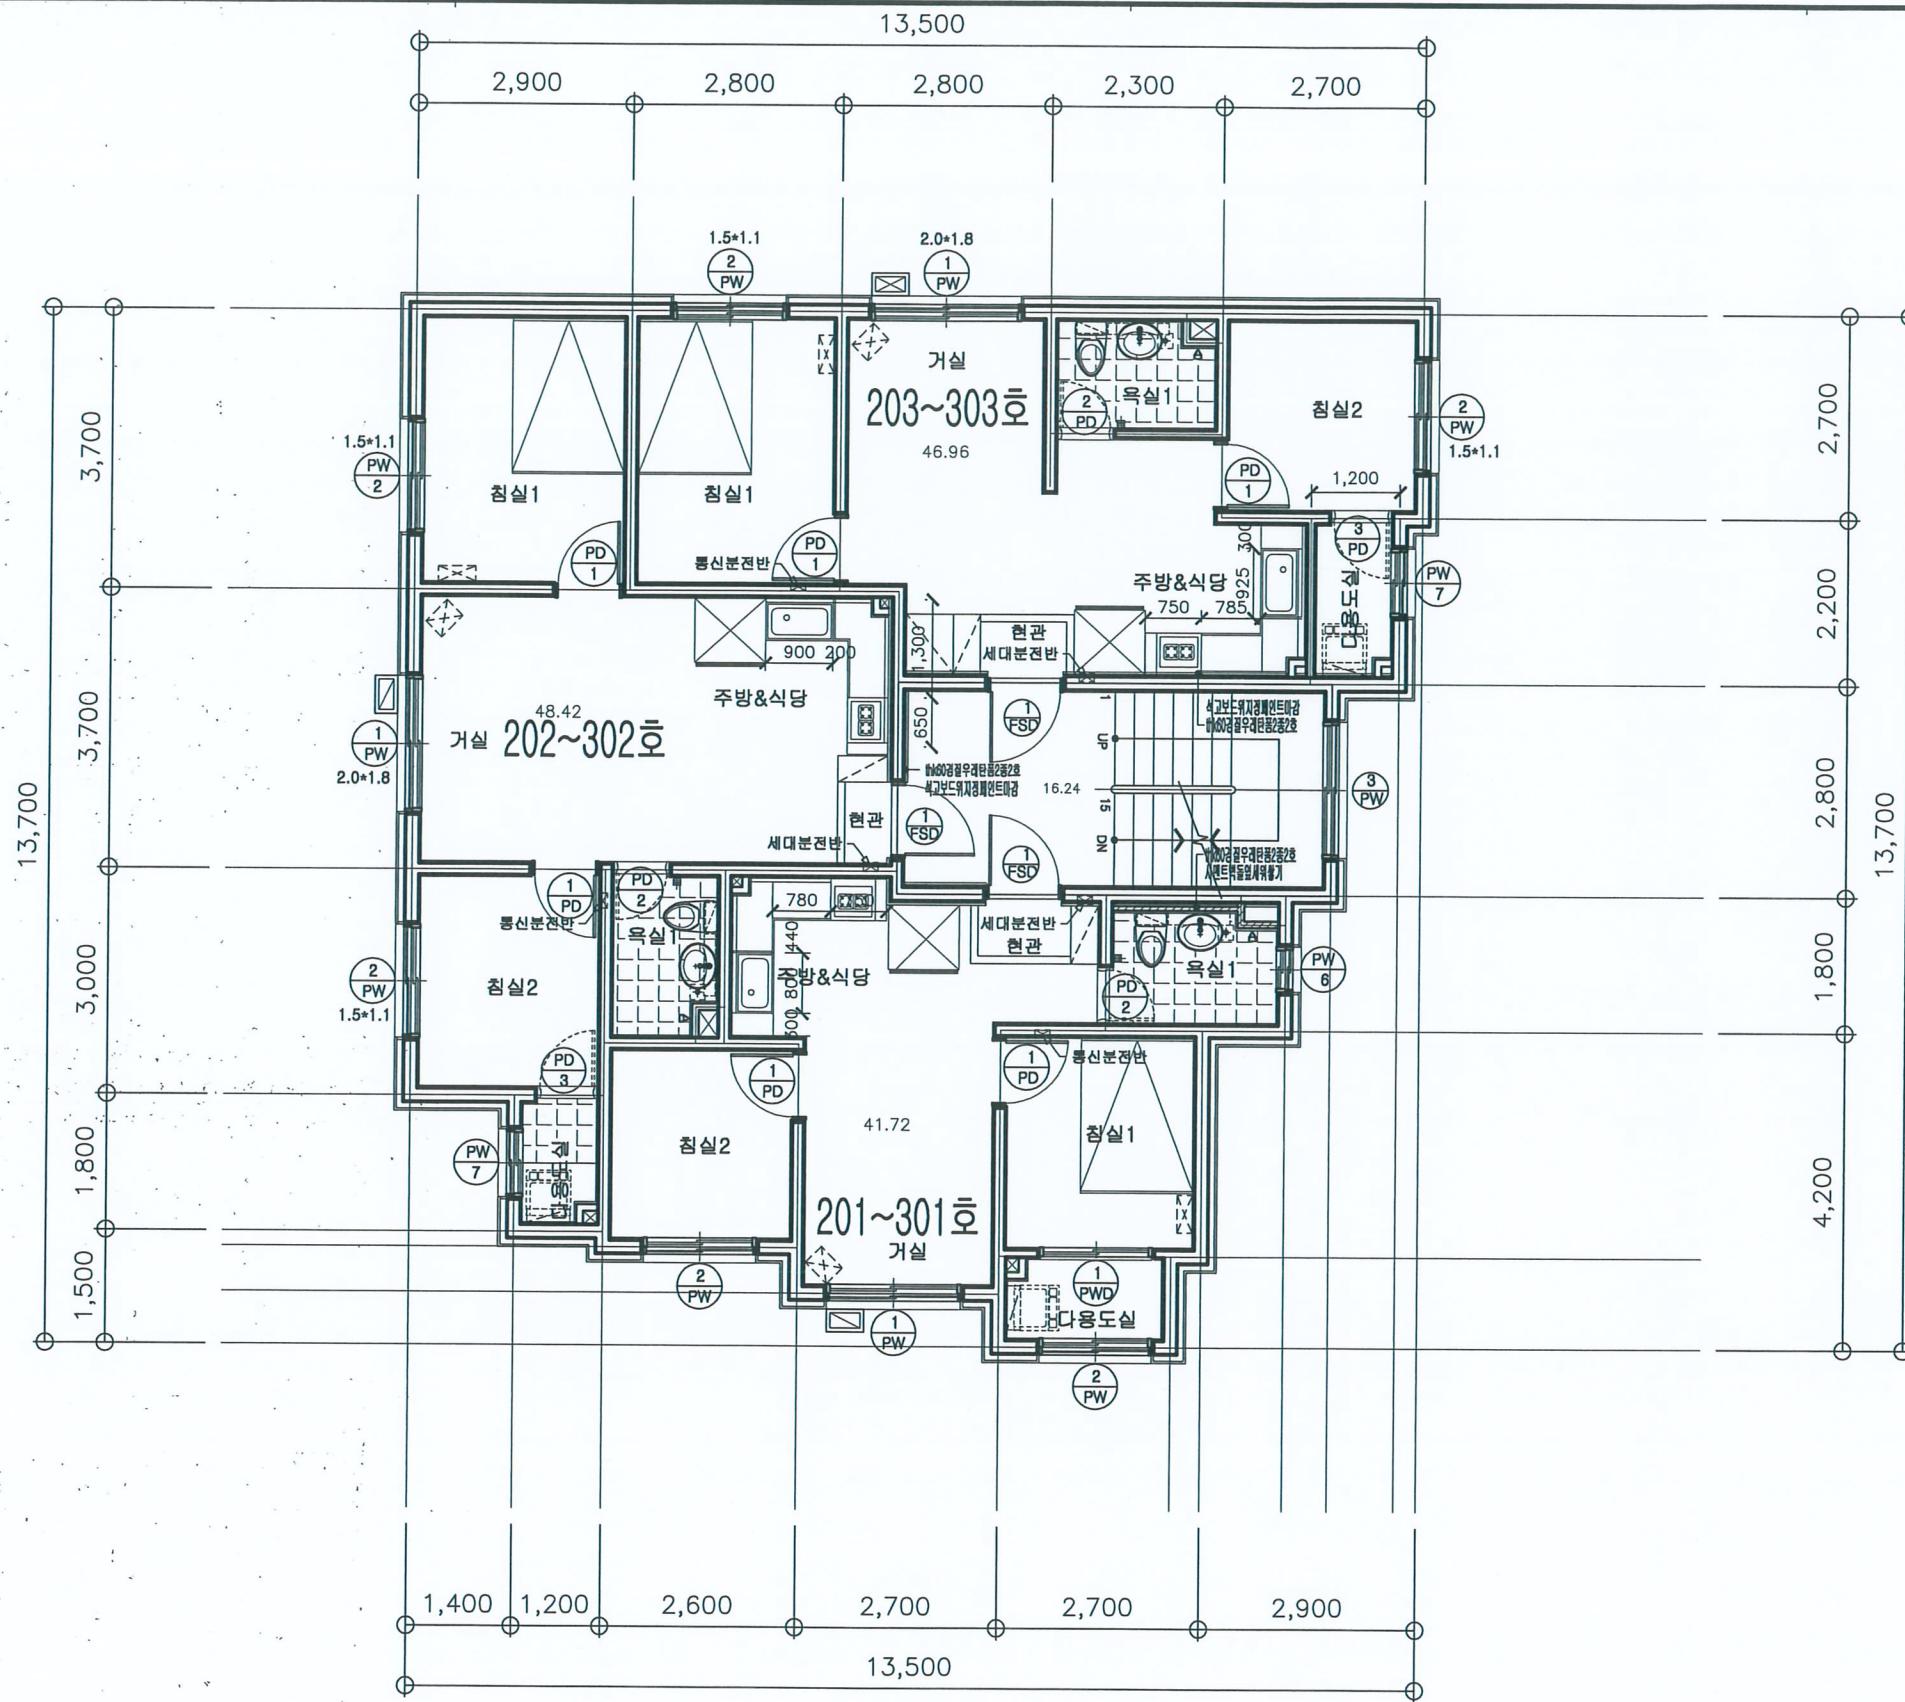

세대간 벽체마감

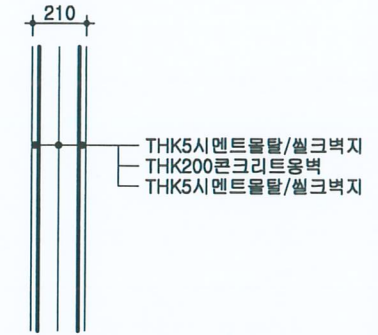

구분	항목	마감자재 적용 기준
건축	계단	W 280 * H (충고/15단) 높이를 일경하게 시공
	세대현관	W 1000 * H 2200
	창틀주변	물딩처리(창틀주변 틈 발생부분)
	창문크기	세대창문은 바닥면적 1/5이상 계단창문은 바닥면적 1/10이상
	다용도실	유효폭 1000 이상 확보할것
	단열재	직접외기 실내벽면 (얇출10 이상)
구조	철근항복강도 $f_y=400\text{Mpa}$, 콘크리트강도 $f_{ck}=24\text{Mpa}$ 이상 (철근은 KS 사용의무)	
	슬라브두께는 210 이상(필로터, 옥상바닥은 180 이상)	
	외벽, 계단실벽체두께는 180, 내부벽체는 150, 세대간벽체는 200이상	
기타	* 기준높이는 바닥마감선에서 기구 중앙 기준 적용	
	비디오존 거실아트웍 측면 1450	
	거실 에어컨콘센트용 벽걸이용 H 1800 스탠드형 H 350	
	침실 에어컨콘센트용 벽걸이용 H 1800	

A 2~3층 평면도
축척 A3:1/100

발주처 / ORDER OFFICE

사업명 / PROJECT TITLE
신림동624-34번지
다세대주택 신축공사

주기 / NOTE

NUMBER REVISIONS DATE

축척 / SCALE

1 /

일자 / DATE

2015 . . .

제도 / DRAWN BY

검토 / CHECK BY

승인 / APPROVED BY


협동설계 / CONSULTANT

美林
종합건축사 사무소
Architects Consulting Engineers


E-mail : millm67
@hanamill.net

도면명 / DRAWING TITLE

도면번호
DRAWN NO.

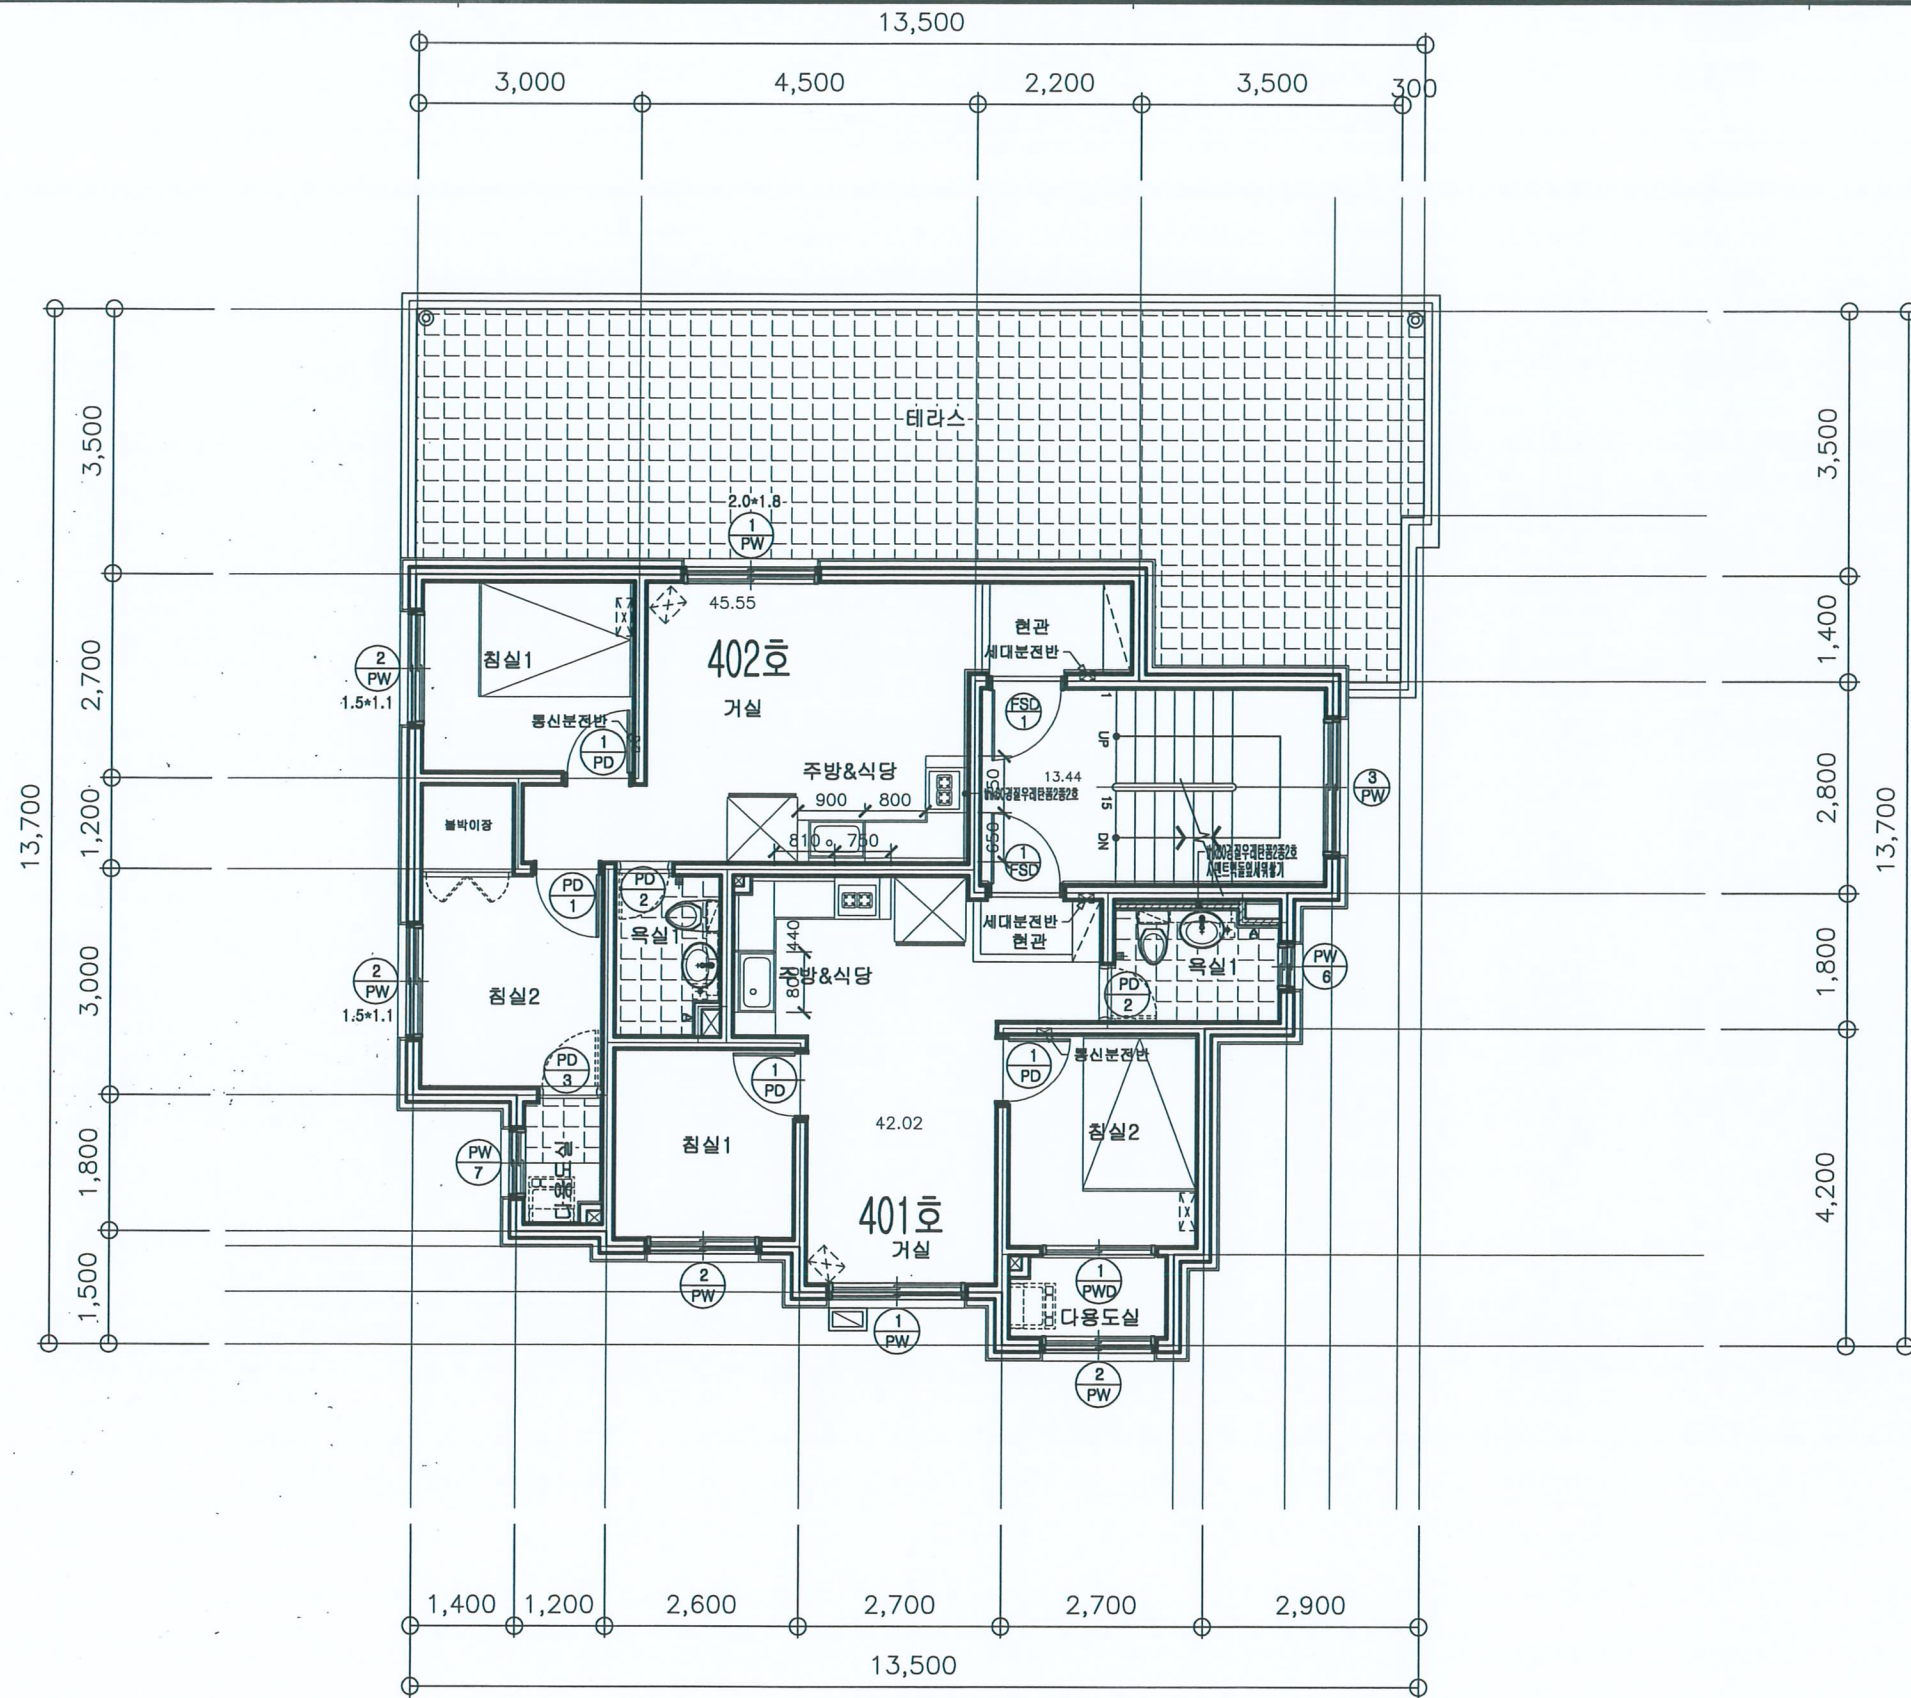

세대간 벽체마감

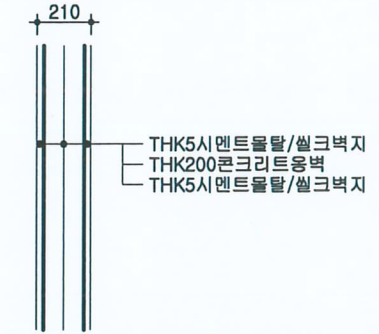

구분	항목	마감자재 적용 기준
건축	계단	W 260 * H (높고/15단) 높이를 일정하게 시공
	세대현관	W 1000 * H 2200
	창틀주변	물당치리(창틀주변 틈 발생부분)
	창문크기	세대창문은 바닥면적 1/5이상 계단창문은 바닥면적 1/10이상
	다용도실	유효폭 1000 이상 확보할것
	단열재	적정외기 실내벽면 (얇출 10 이상)
구조	철근항복강도 $f_y=400\text{Mpa}$, 콘크리트강도 $f_{ck}=24\text{Mpa}$ 이상 (철근은 KS 사용의무)	
	슬라브두께는 210 이상(필로티, 옥상바닥은 180 이상)	
	외벽, 계단실벽체두께는 180, 내부벽체는 150, 세대간벽체는 200 이상	
기타	* 기준높이는 바닥마감선에서 기구 중앙 기준 적용	
	비디오론 거실아트월 측면 1450	
	거실 에어컨콘센트용 벽걸이용 H 1800 스탠드형 H 350	
	침실 에어컨콘센트용 벽걸이용 H 1800	

4 층 평면도
축척 A3 : 1/100

발주처 / ORDER OFFICE

사업명 / PROJECT TITLE
신림동624-34번지
다세대주택 신축공사

주기 / NOTE

NUMBER REVISIONS DATE

축척 / SCALE
1 /

일자 / DATE
2015 . . .

제도 / DRAWN BY

검토 / CHECK BY

승인 / APPROVED BY


협동설계 / CONSUL TANT

美林
종합건축사 사무소
Architects Consulting Engineers


E-mail : millm67
@hanamill.net

도면명 / DRAWING TITLE

도면번호
DRAWN NO. □ - □

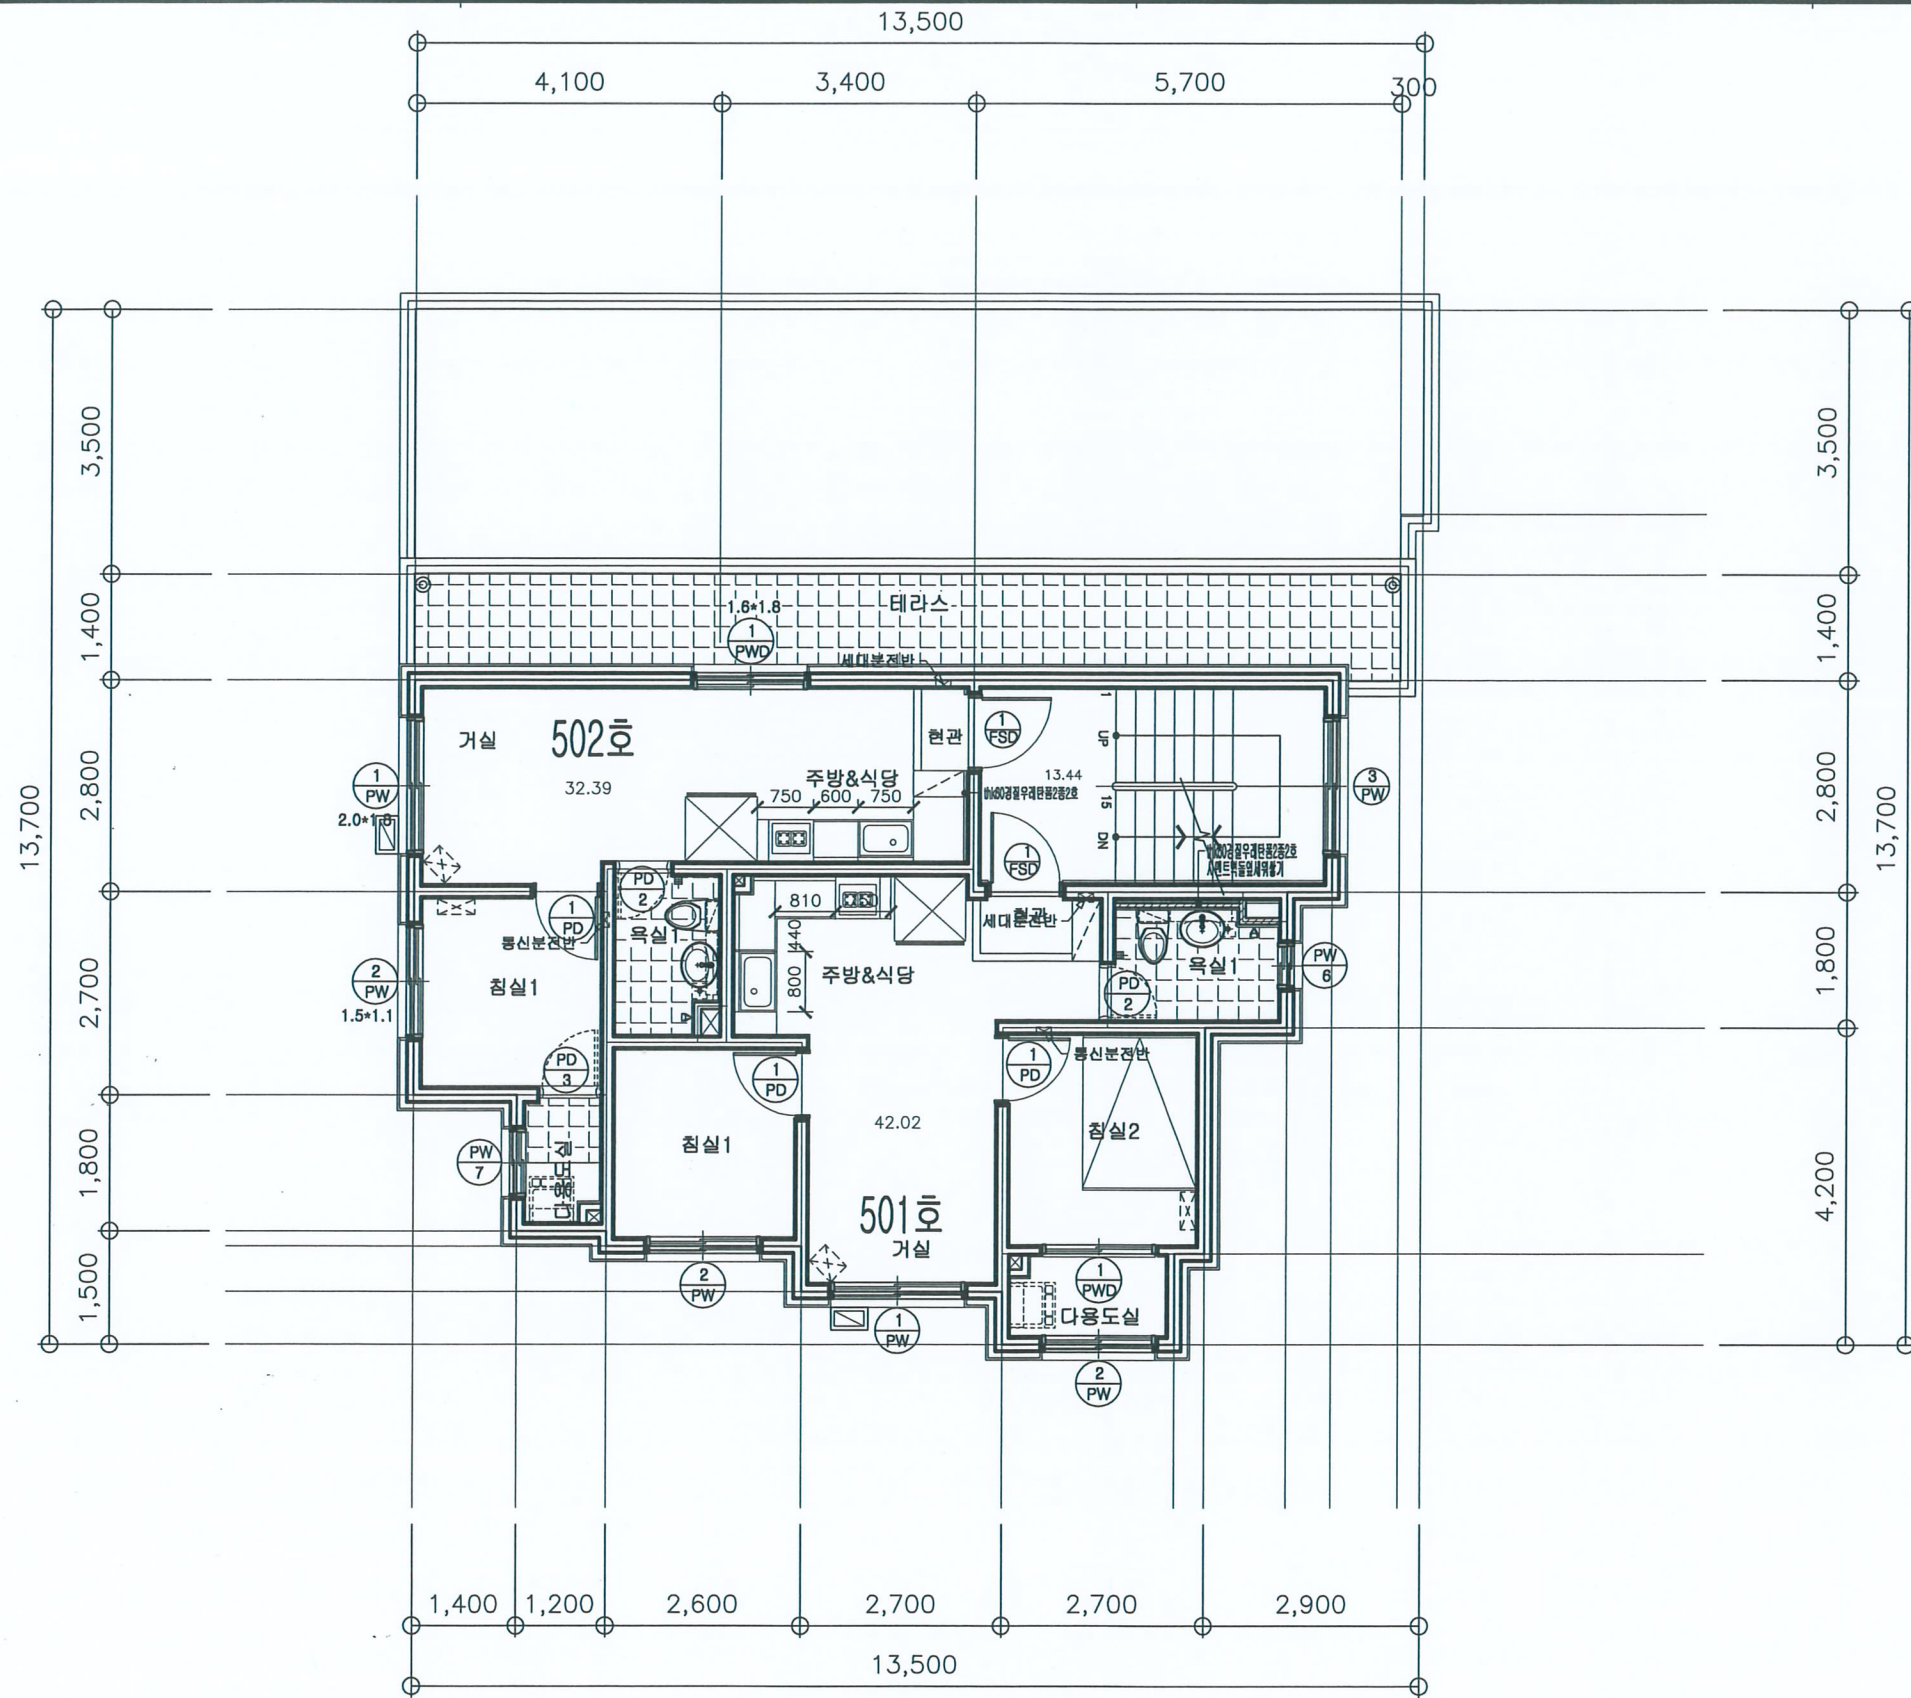

세대간 벽체마감

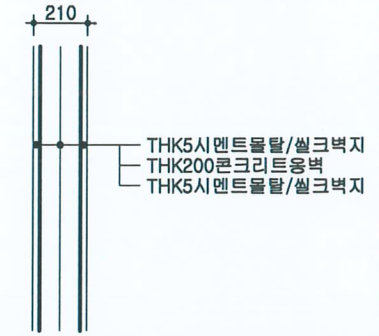

구분	항목	마감자재 적용 기준
건축	계단	W 280 * H (충고/15단) 높이를 일정하게 시공
	세대현관	W 1000 * H 2200
	창틀주변	물당처리(창틀주변 틈 발생부분)
	창문크기	세대창문은 바닥면적1/5이상 계단창문은 바닥면적1/10이상
	다용도실	유�효폭 1000 이상 확보할것
	단열재	직접외기 실내벽면 (얇을10 이상)
구조	철근항복강도 $f_y=400\text{Mpa}$, 콘크리트강도 $f_{ck}=24\text{Mpa}$ 이상 (철근은 ks 사용의무)	
	슬라브두께는 210 이상(필로티, 옥상바닥은 180 이상)	
	외벽, 계단실벽체두께는 180, 내부벽체는 150, 세대간벽체는 200이상 *.기준높이는 바닥마감선에서 기구 중앙 기준 적용	
기타	비디오존 거실아트를 측면 1450	
	거실 에어컨센트룸 벽걸이용 H 1800 스탠드형 H 350	
	침실 에어컨센트룸 벽걸이용 H 1800	

A 5 층 평면도
축척 A3 : 1/100

발주처 / ORDER OFFICE

사업명 / PROJECT TITLE
신림동624-34번지
다세대주택 신축공사

주기 / NOTE

NUMBER REVISIONS DATE

축척 / SCALE
1 /

일자 / DATE

2015 . . .

제도 / DRAWN BY

검토 / CHECK BY

승인 / APPROVED BY

협동설계 / CONSULTANT

美林
종합건축사 사무소
Architects Consulting Engineers

E-mail : millm67
@hanamll.net

도면명 / DRAWING TITLE

도면번호
DRAWN NO. □ - □