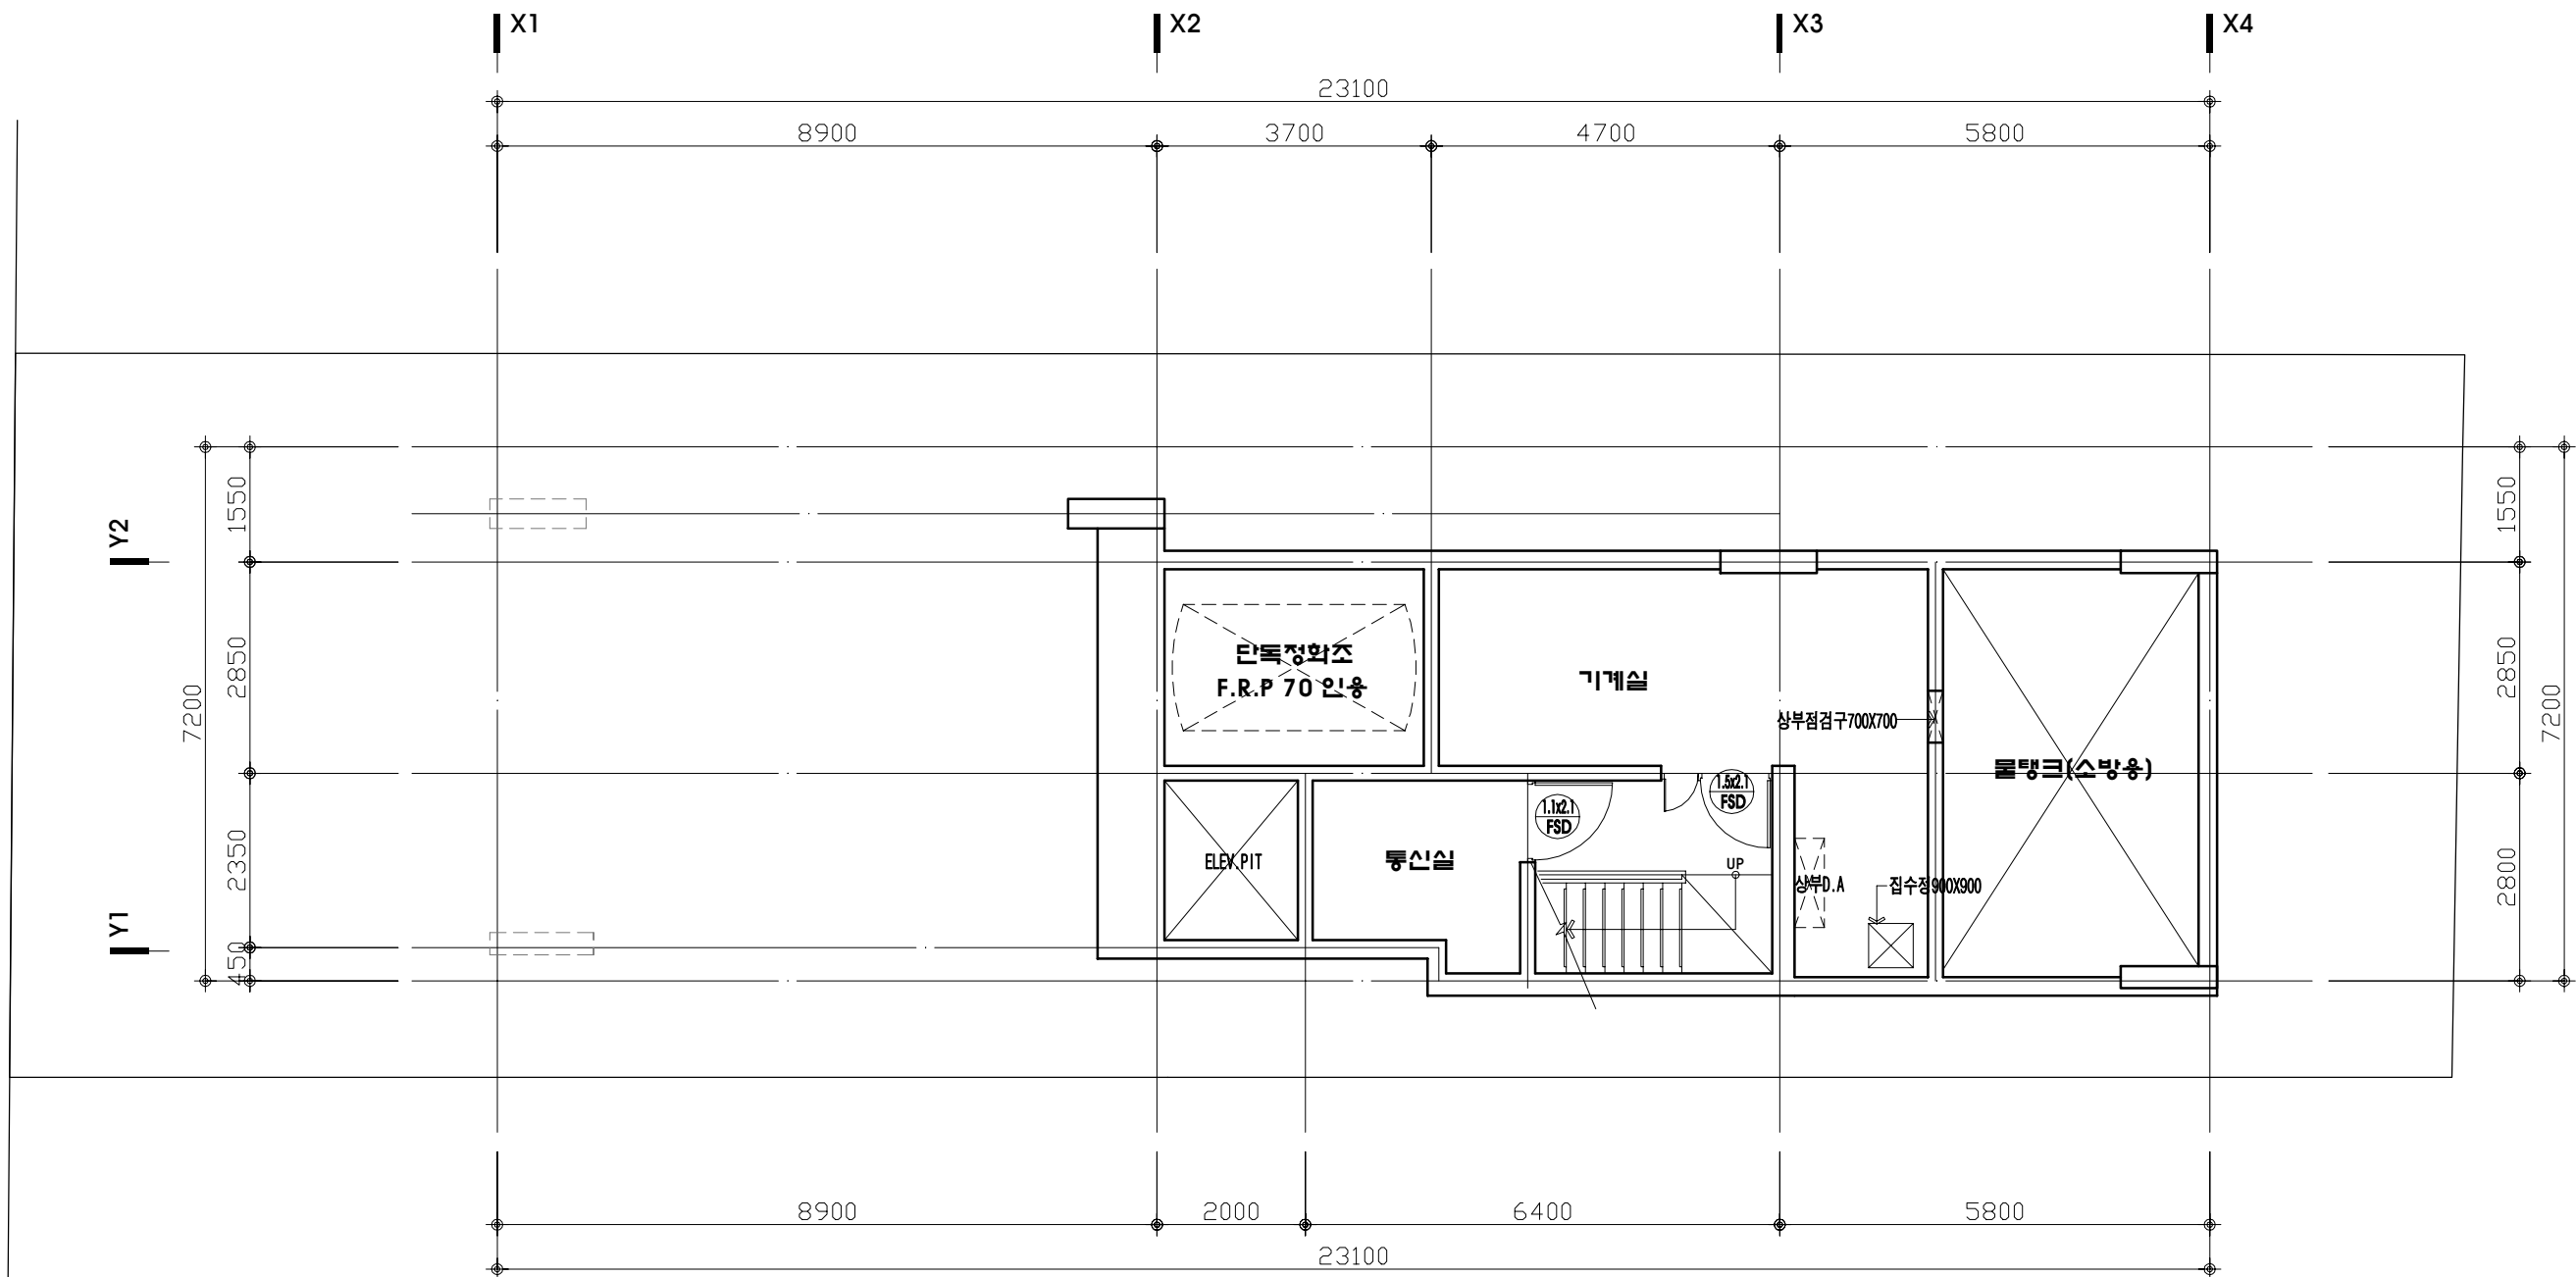
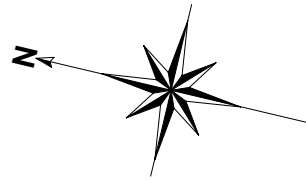


지 하 1 층 평 면 도

SCALE : 1/100

PROJECT TITLE
사 업 명 칭
(신림동1571-12)

신림동 다세대주택 신축공사
(SH 청년임대 주택)

NAME OF DRAWING
도 면 명

지하1층 평 면 도

NOTE
주 기

1. 콘크리트: $f_{ck} = 24 \text{ MPa}$
2. 철근: $f_y = 400 \text{ MPa}$
3. 세대간벽두께: 180mm(복배근)
4. 외벽두께: 200mm(복배근)
5. 코아벽두께: 180mm(복배근)
6. 슬라브두께: 210mm(복배근)
(최상층은 180mm)
7. 욕실, 다용도실-50슬라브다운

DATE ▲ REVISIONS ▲ NO.
일 자 수 장

DESIGNED BY
설 계

CHECKED BY
심 사

APPROVED BY
승 인

CONSULTANTS
합 동 설 계

SCALE
축 척 1 / 100

DATE
일 자 2021 . 10




DWG NO.
도 면 번 호 A - 201

FILE NAME.
화 일 명

TECH 1 테크원
건축사사무소

TECHONE ARCHITECTS & ENGINEERS
CO., LTD

TEL. 02)482-2466(대)
FAX. 02)488-2466

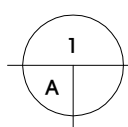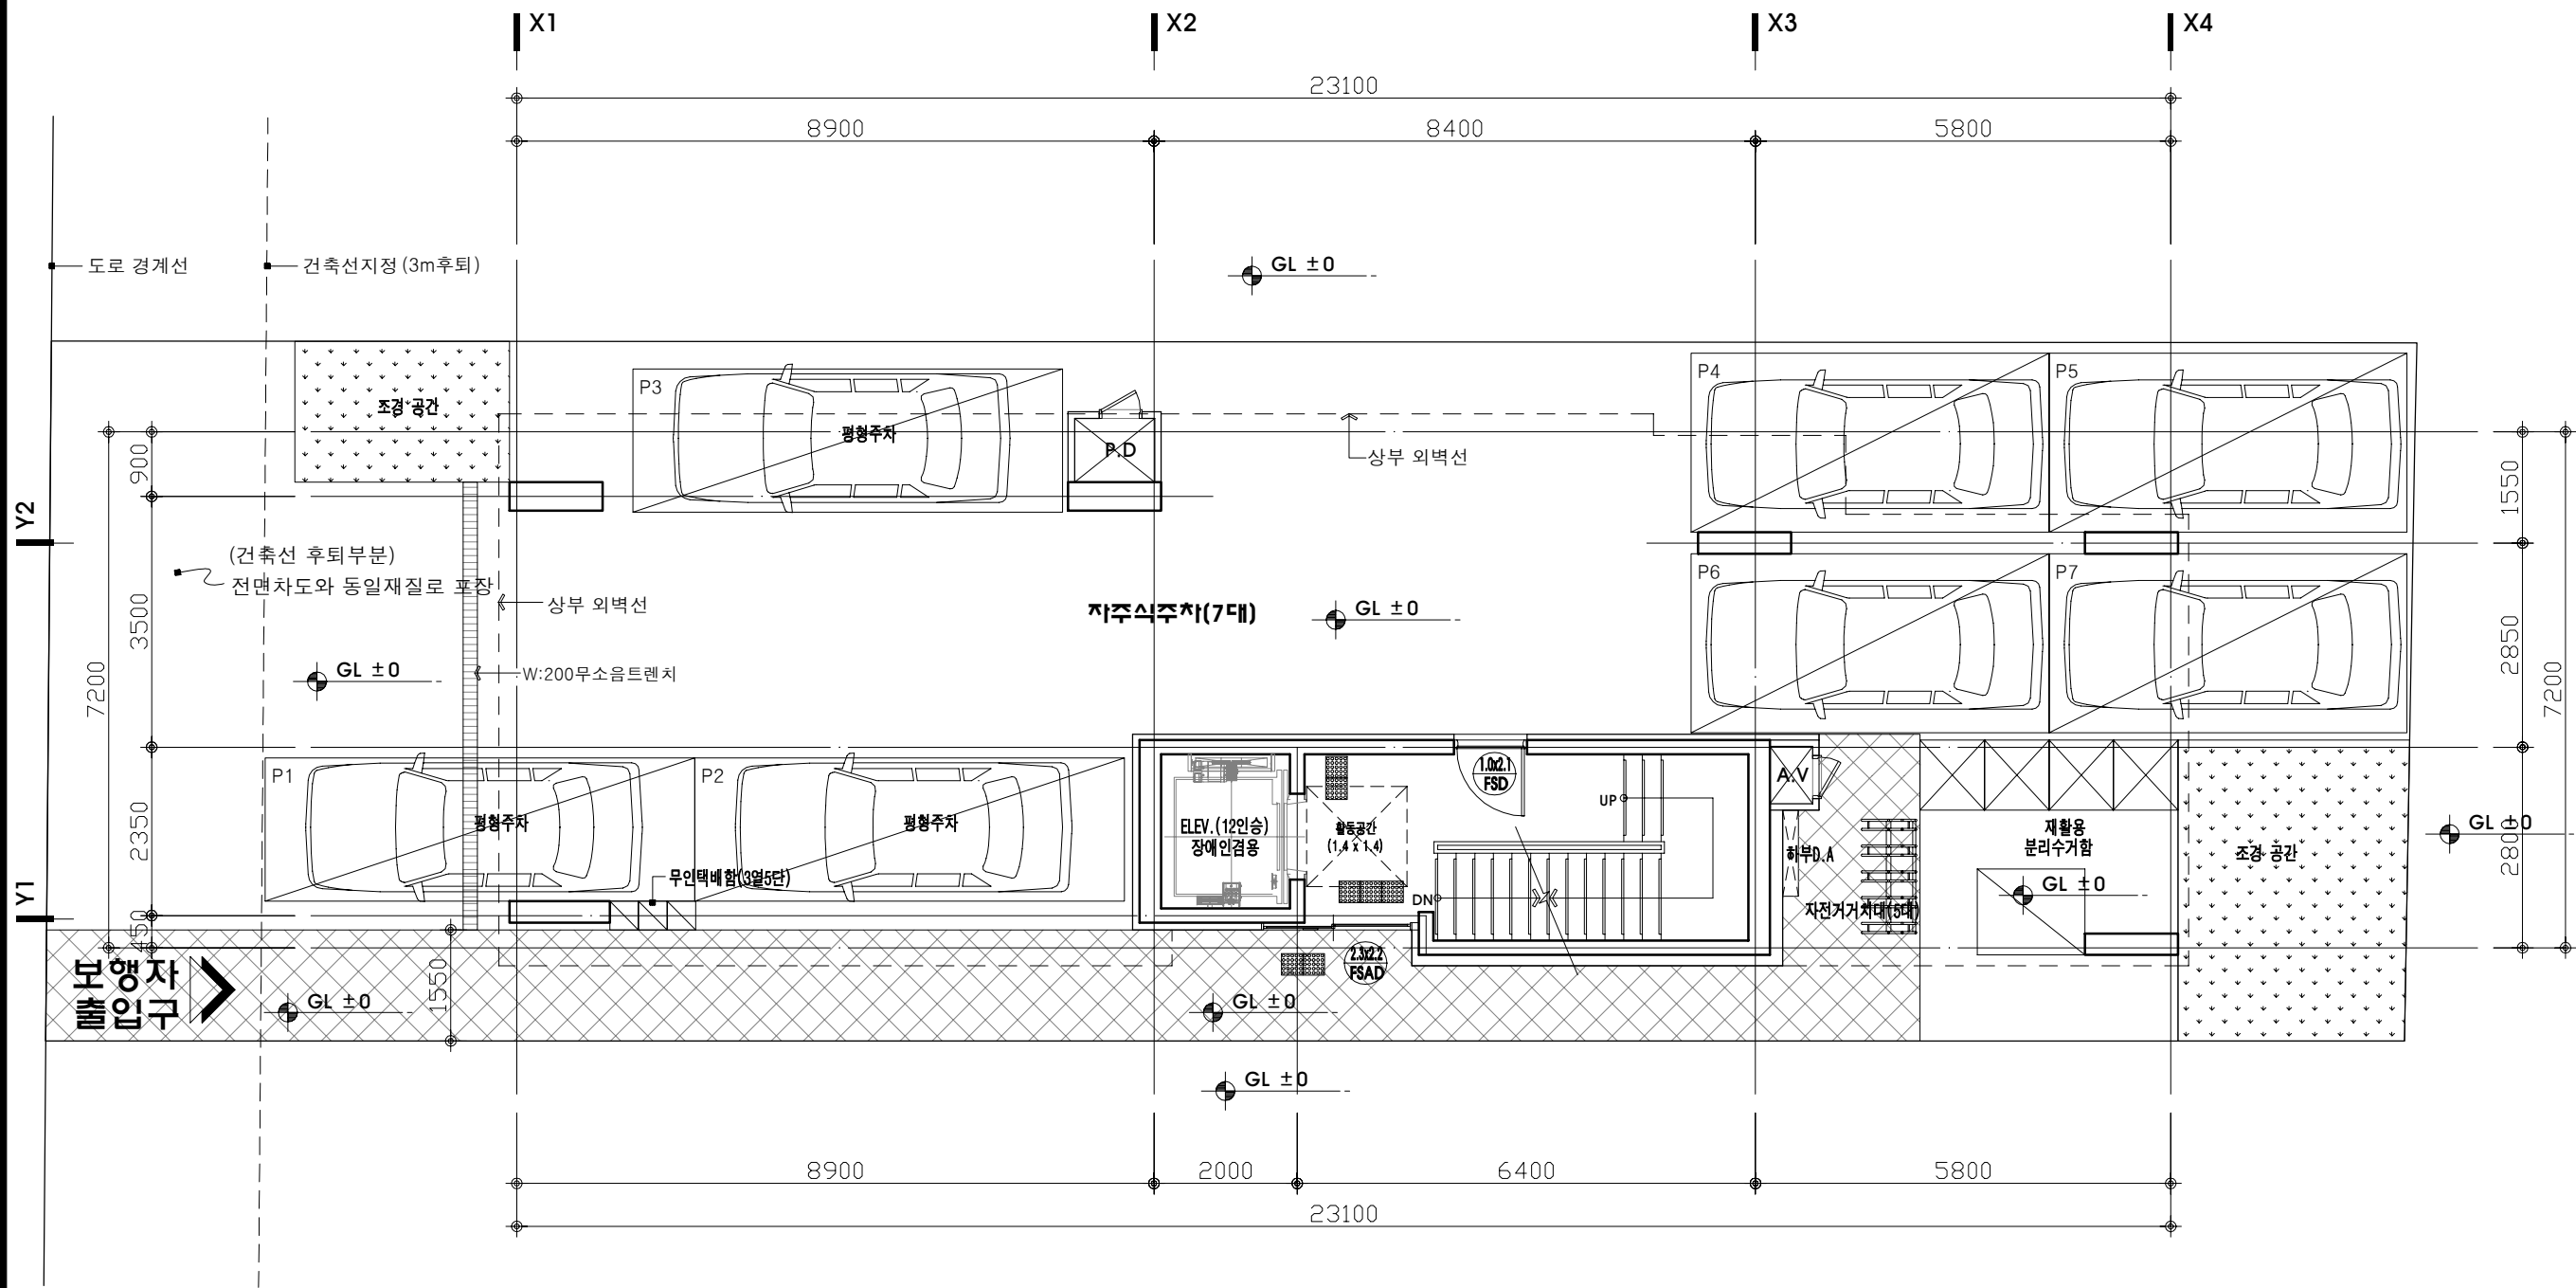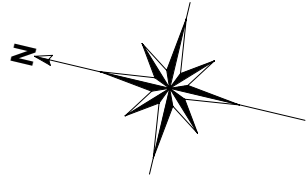

1 층 평 면 도

SCALE : 1/100

PROJECT TITLE
사 업 명 칭
(신림동 1571-12)

신림동 다세대주택 신축공사
(SH 청년임대 주택)

NAME OF DRAWING
도 면 명

1 층 평 면 도

NOTE
주 기

▼ ▼

1. 콘크리트: fck = 24 MPa

2. 철근 : fy = 400 MPa

3. 세대간벽두께: 180mm(복배근)

4. 외벽두께: 200mm(복배근)

5. 코아벽두께: 180mm(복배근)

6. 스라브두께: 210mm(복배근)
(최상층은 180mm)

7. 욕실, 다용도실-50슬라브다운

DATE
일 자

REVISIONS
수 정

NO.

DESIGNED BY
설 계

CHECKED BY
심 사

APPROVED BY
승 인

CONSULTANTS
협 동 설 계

SCALE
축 척

1 / 100

DATE
일 자

2021 . 10

DWG NO.
도 면 번 호


A - 202

FILE NAME.
화 일 명

TECH 1 테크원
건축사사무소

TECHONE ARCHITECTS & ENGINEERS
CO., LTD

TEL. 02)482-2466(대)
FAX. 02)488-2466

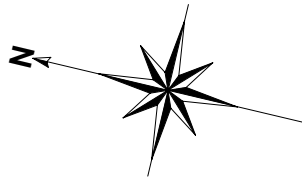

(주)
인접지와 1.5M이내에 설치된 창호는 방화
유리창으로 설치 할 것(「산업표준화법」에
따른 한국산업표준KS F 2845에 규정된 방법에
따라 비차열 20분 이상의 성능이 있을 것)
- 60cm이내에 스프링클러헤드 설치된 창 제외

PROJECT TITLE
사 업 명 칭
(신림동 1571-12)

신림동 다세대주택 신축공사
(SH 청년임대 주택)

NAME OF DRAWING
도 면 명

2 층 평 면 도

NOTE
주 기

청년주택일반형

빌트인가전기구(냉장고, 세탁기,
벽걸이에어컨, 불박이장, 책상)

☒ 보일러
☐ 에어컨 실외기
▬ 벽걸이에어컨

1. 콘크리트 : fck = 24 MPa
2. 철근 : fy = 400 MPa
3. 세대간벽두께 : 180mm(복배근)
4. 외벽두께 : 200mm(복배근)
5. 코아벽두께 : 180mm(복배근)
6. 슬라브두께 : 210mm(복배근)
(최상층은 180mm)
7. 욕실, 다용도실 - 50슬라브다운

DATE
일 자

REVISIONS
수 정

NO.
번 호

DESIGNED BY
설 계

CHECKED BY
심 사

APPROVED BY
승 인

CONSULTANTS
협 동 설 계

SCALE
축 척
1 / 100

DATE
일 자
2021 . 10



DWG NO.
도 면 번 호
A - 203

FILE NAME
화 일 명

TECH 1 테크원
건축사사무소




TECHONE ARCHITECTS & ENGINEERS
CO., LTD

TEL. 02)482-2466(대)
FAX. 02)488-2466

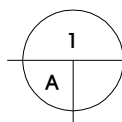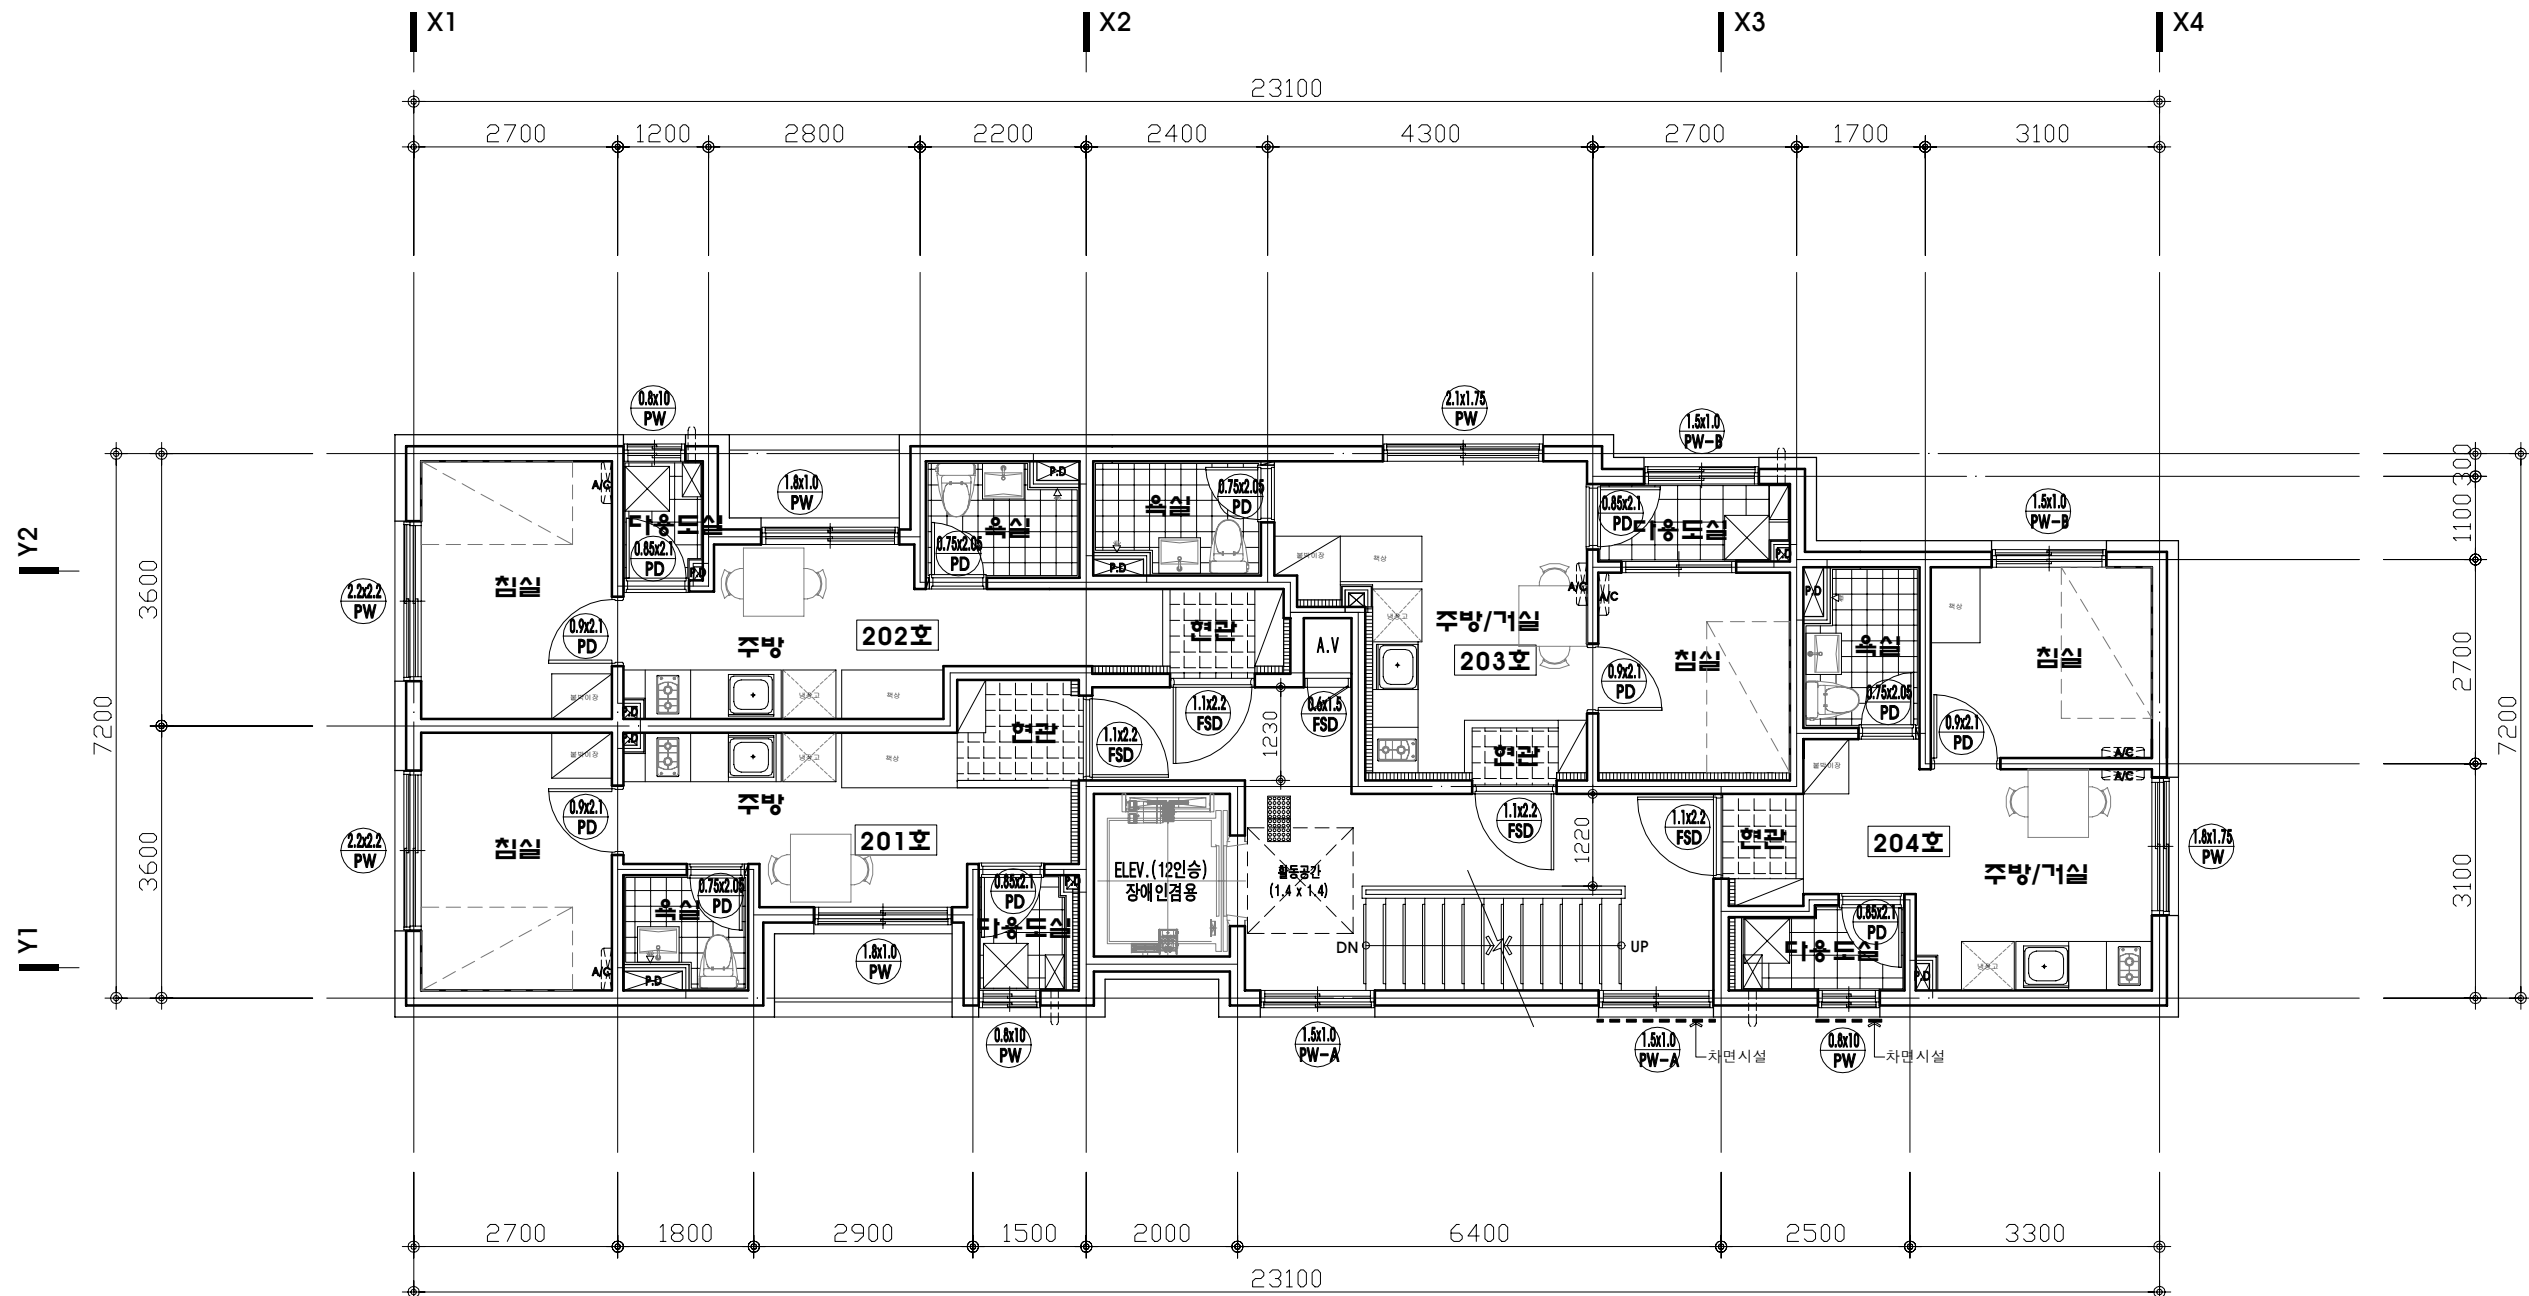

2 층 평 면 도

SCALE : 1/100

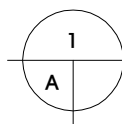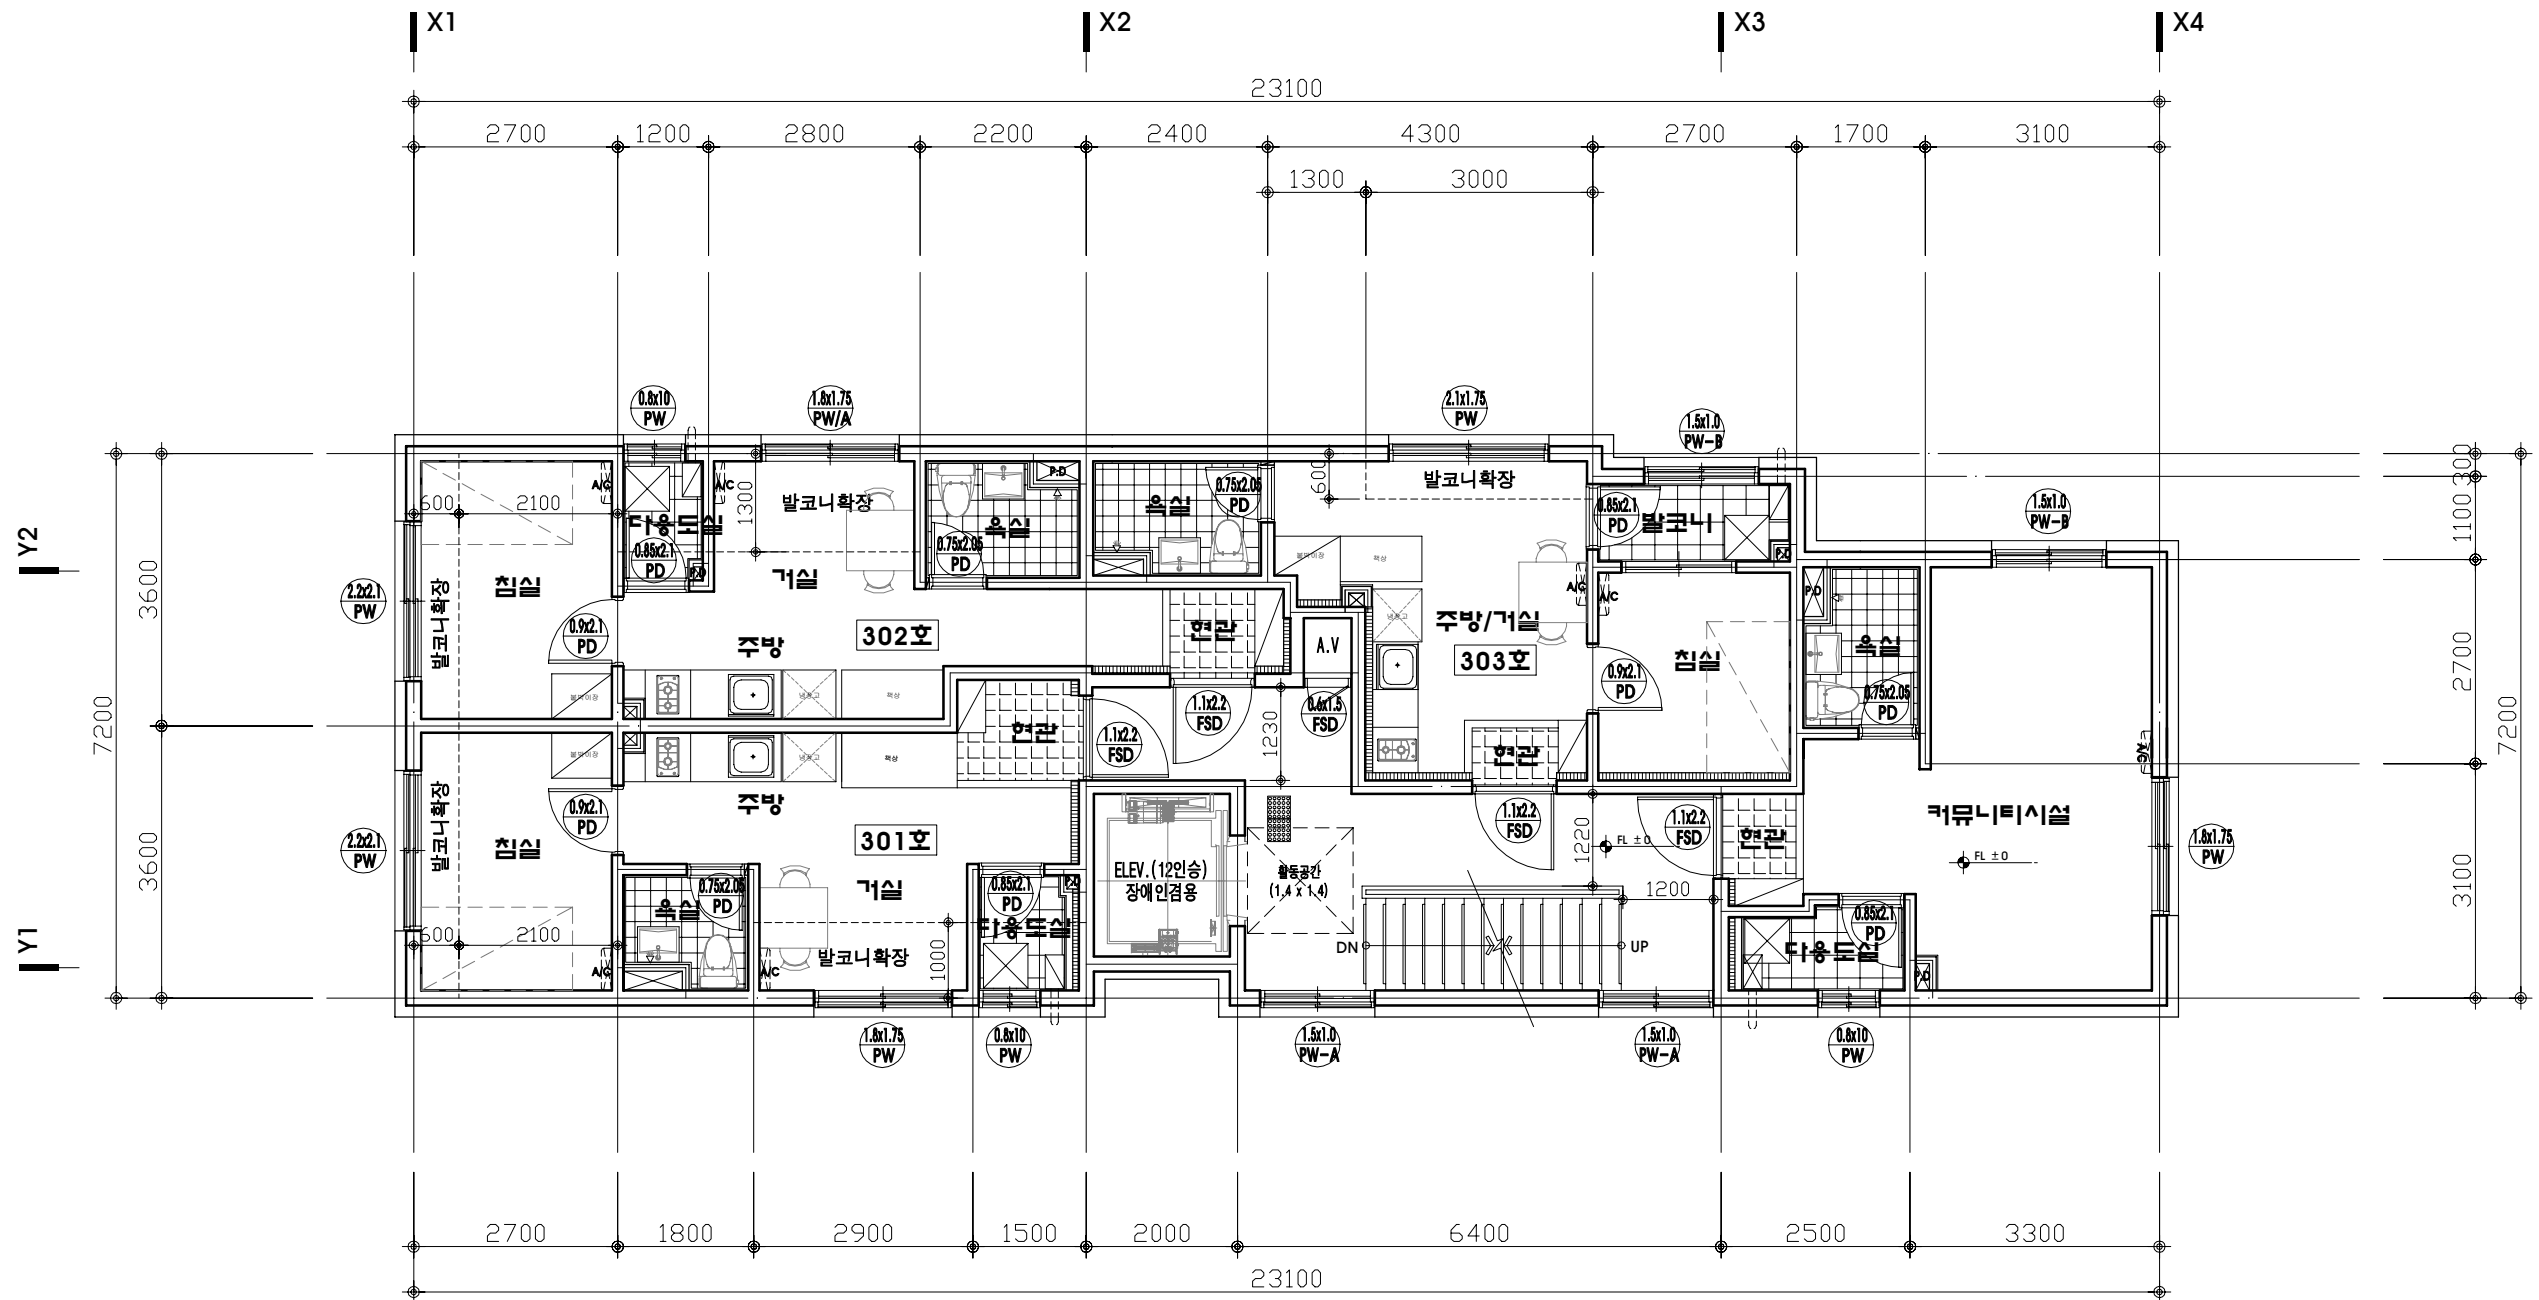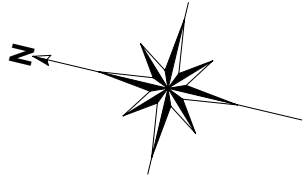


3 층 평면도

SCALE : 1/100
AREA : 132.56

(주)
인접지와 1.5M이내 설치된 창호는 방화
유리창으로 설치 할 것(「산업표준화법」에
따른 한국산업표준KS F 2845에 규정된 방법에
따라 비차열 20분 이상의 성능이 있을 것)
- 60cm이내에 스프링클러헤드 설치된 창 제외

PROJECT TITLE 사 업 명 칭 (신림동 1571-12)
신림동 다세대주택 신축공사 (SH 청년임대 주택)
NAME OF DRAWING 도 면 명 3 층 평 면 도
NOTE 주 기
청년주택일반형
빌트인가전가구(냉장고, 세탁기, 벽걸이에어컨,불박이장,책상)
☒ 보일러
☐ 에어컨 실외기
㉮㉮㉮ 벽걸이 에어컨
1.콘크리트: fck = 24 MPa
2. 철근 : fy = 400 MPa
3. 세대간벽두께:180mm(복배근)
4. 외벽두께:200mm(복배근)
5. 코아벽두께:180mm(복배근)
6. 스라브두께:210mm(복배근) (최상층은180mm)
7. 욕실, 다용도실-50슬라브다운
DATE 일 자
REVISIONS 수 정
NO.
DESIGNED BY 설 계
CHECKED BY 심 사
APPROVED BY 승 인
CONSULTANTS 협 동 설 계
SCALE 축 척 1 / 100
DATE 일 자 2021 . 10
DWG NO. 도 면 번 호 A - 204
FILE NAME. 화 일 명
TECH 1 테크원 건축사사무소 TECHONE ARCHITECTS & ENGINEERS CO., LTD TEL. 02)482-2466(대) FAX. 02)488-2466

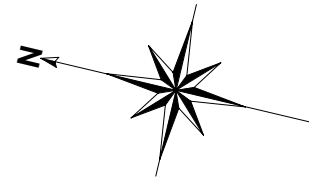

(주)
인접지와 1.5M이내에 설치된 창호는 방화
유리창으로 설치 할 것(「산업표준화법」에
따른 한국산업표준KS F 2845에 규정된 방법에
따라 비차열 20분 이상의 성능이 있을 것)
- 60cm이내에 스프링클러헤드 설치된 창 제외

PROJECT TITLE
사 업 명 칭
(신림동 1571-12)

신림동 다세대주택 신축공사
(SH 청년임대 주택)

NAME OF DRAWING
도 면 명

4~7 층 평 면 도

NOTE
주 기

청년주택일반형

빌트인가전가구(냉장고, 세탁기,
벽걸이에어컨, 불박이장, 책상)

보일러

에어컨 실외기

벽걸이에어컨

- 콘크리트: fck = 24 MPa
- 철근: fy = 400 MPa
- 세대간벽두께: 180mm(복배근)
- 외벽두께: 200mm(복배근)
- 코아벽두께: 180mm(복배근)
- 스라브두께: 210mm(복배근)
(최상층은180mm)
- 욕실, 다용도실-50슬라브다운

DATE ▲ REVISIONS ▲ NO.

DESIGNED BY
설 계

CHECKED BY
심 사

APPROVED BY
승 인

CONSULTANTS
합 동 설 계

SCALE
축 척 1 / 100

DATE
일 자 2021 . 10



DWG NO.
도 면 번 호 A - 205

FILE NAME.
화 일 명

TECH 1 테크원
건축사사무소


TECHONE ARCHITECTS & ENGINEERS
CO., LTD

TEL. 02)482-2466(대)
FAX. 02)488-2466

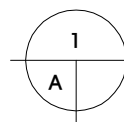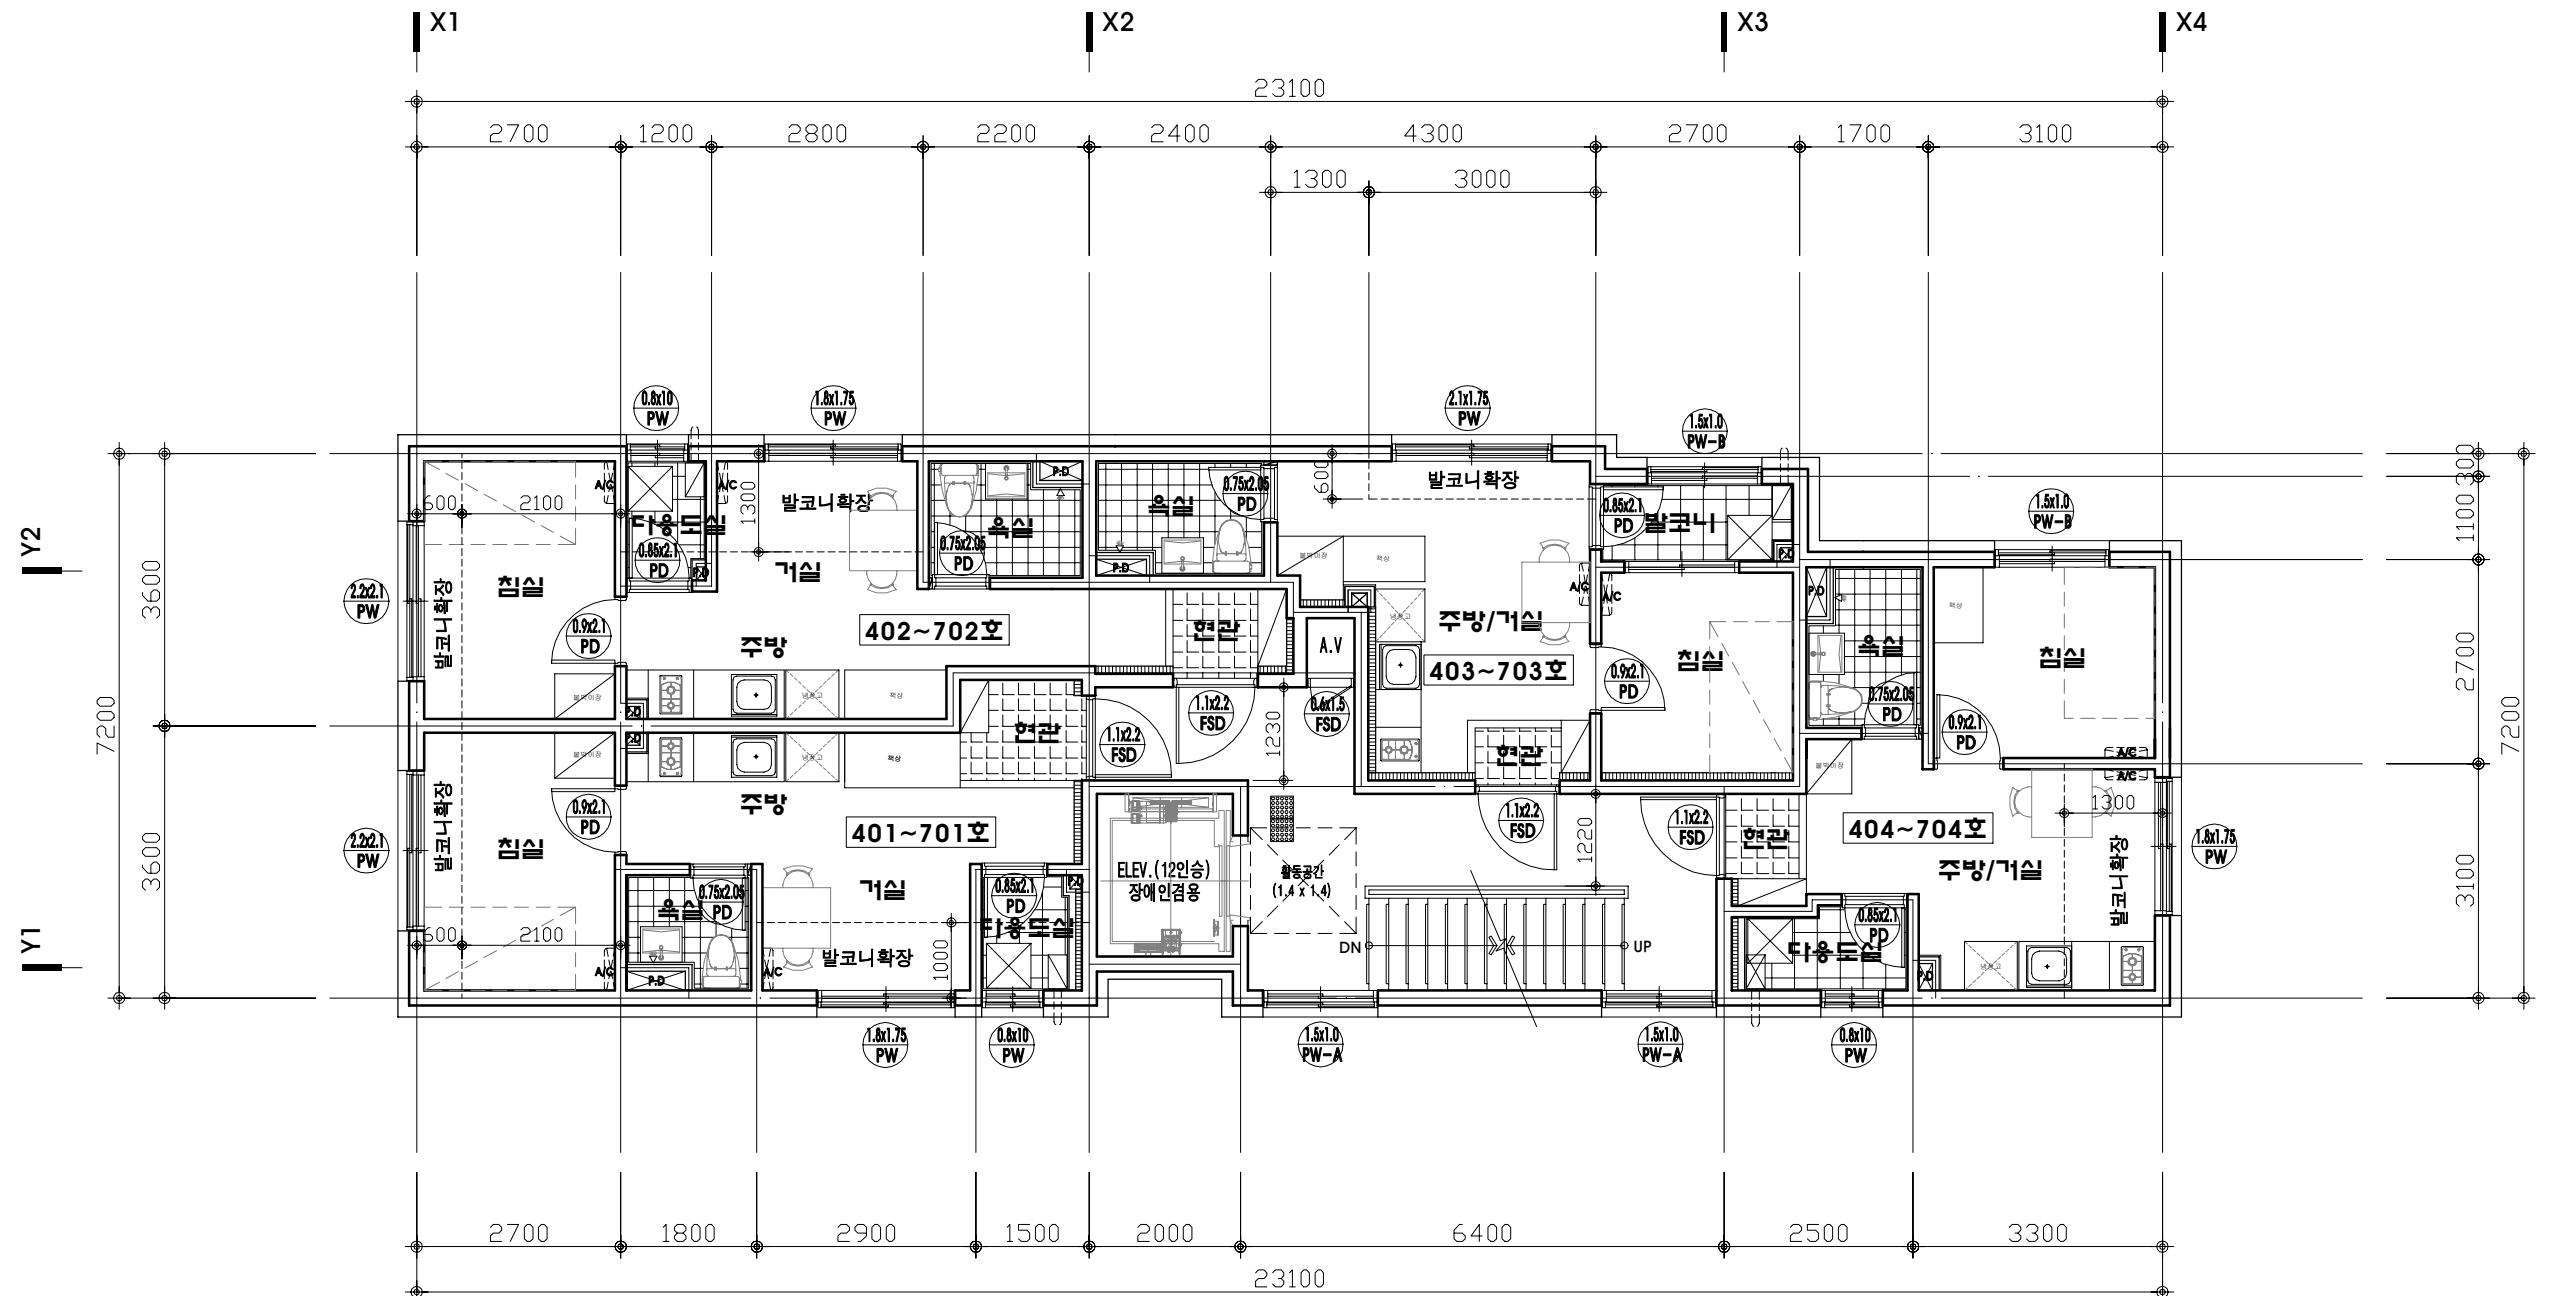


4~7 층 평 면 도

SCALE : 1/100
AREA : 127.76

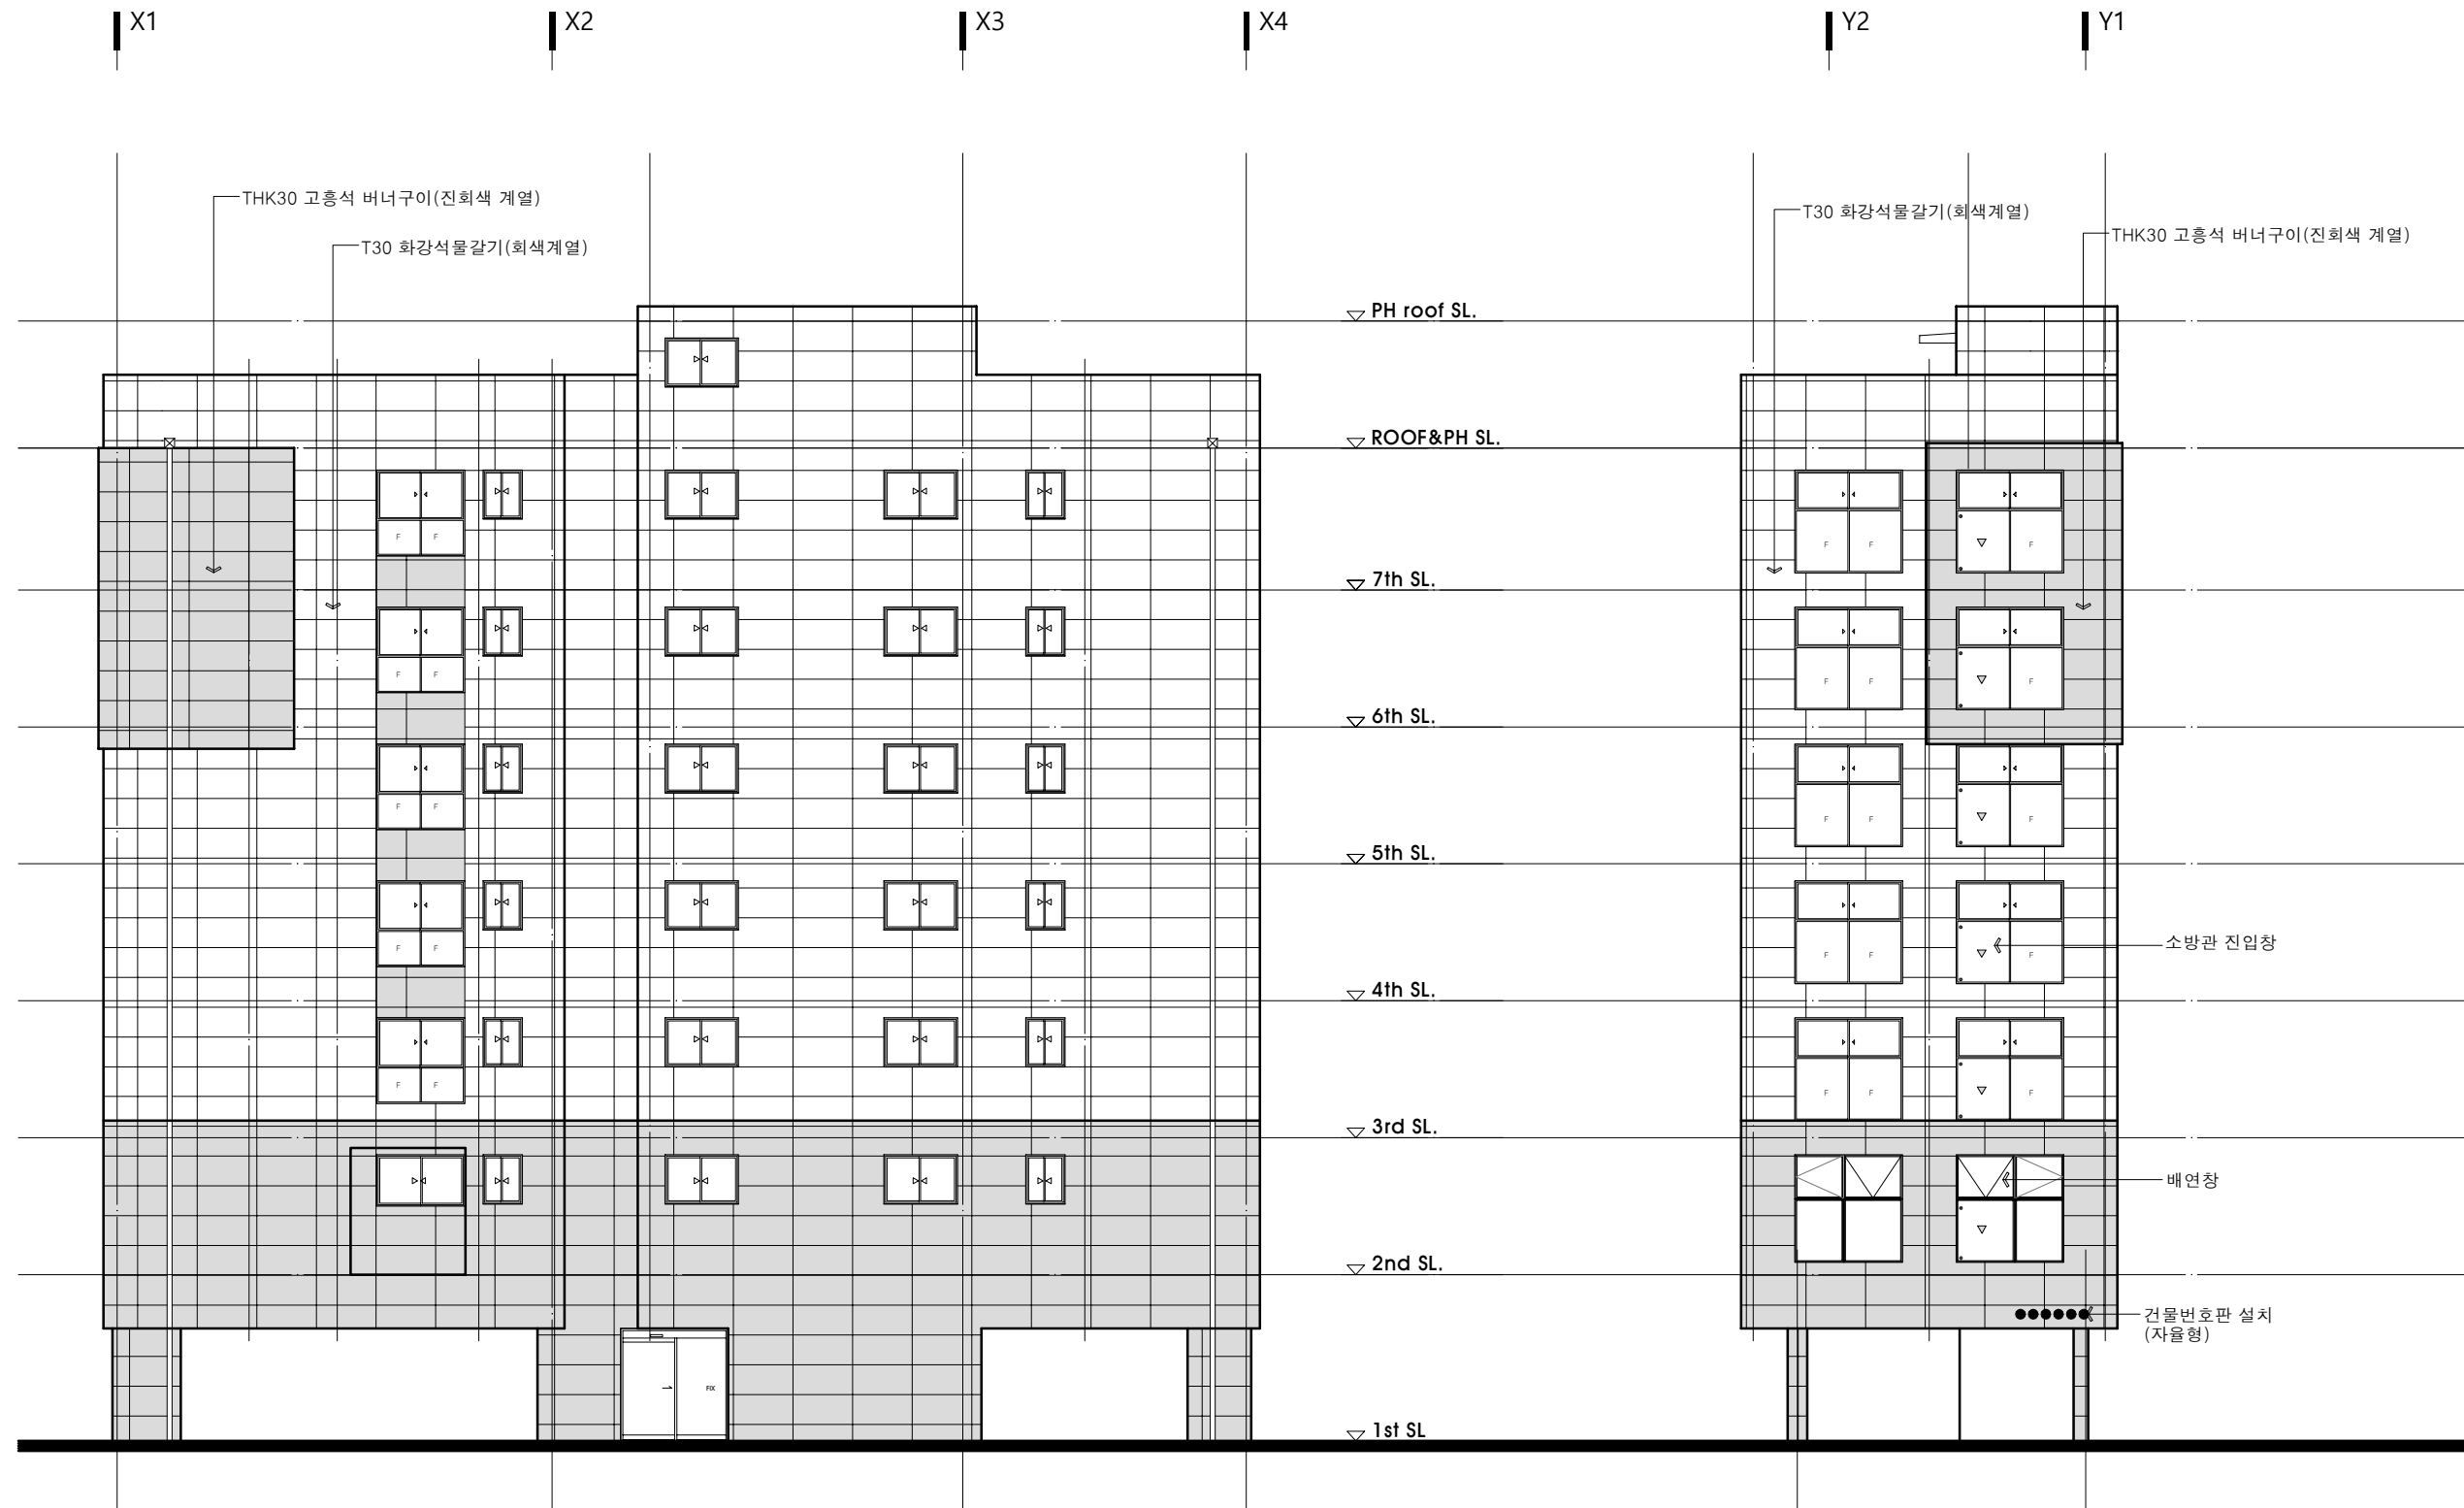

1
A
우 측 면 도
SCALE : 1/150

1
A
정 면 도
SCALE : 1/150

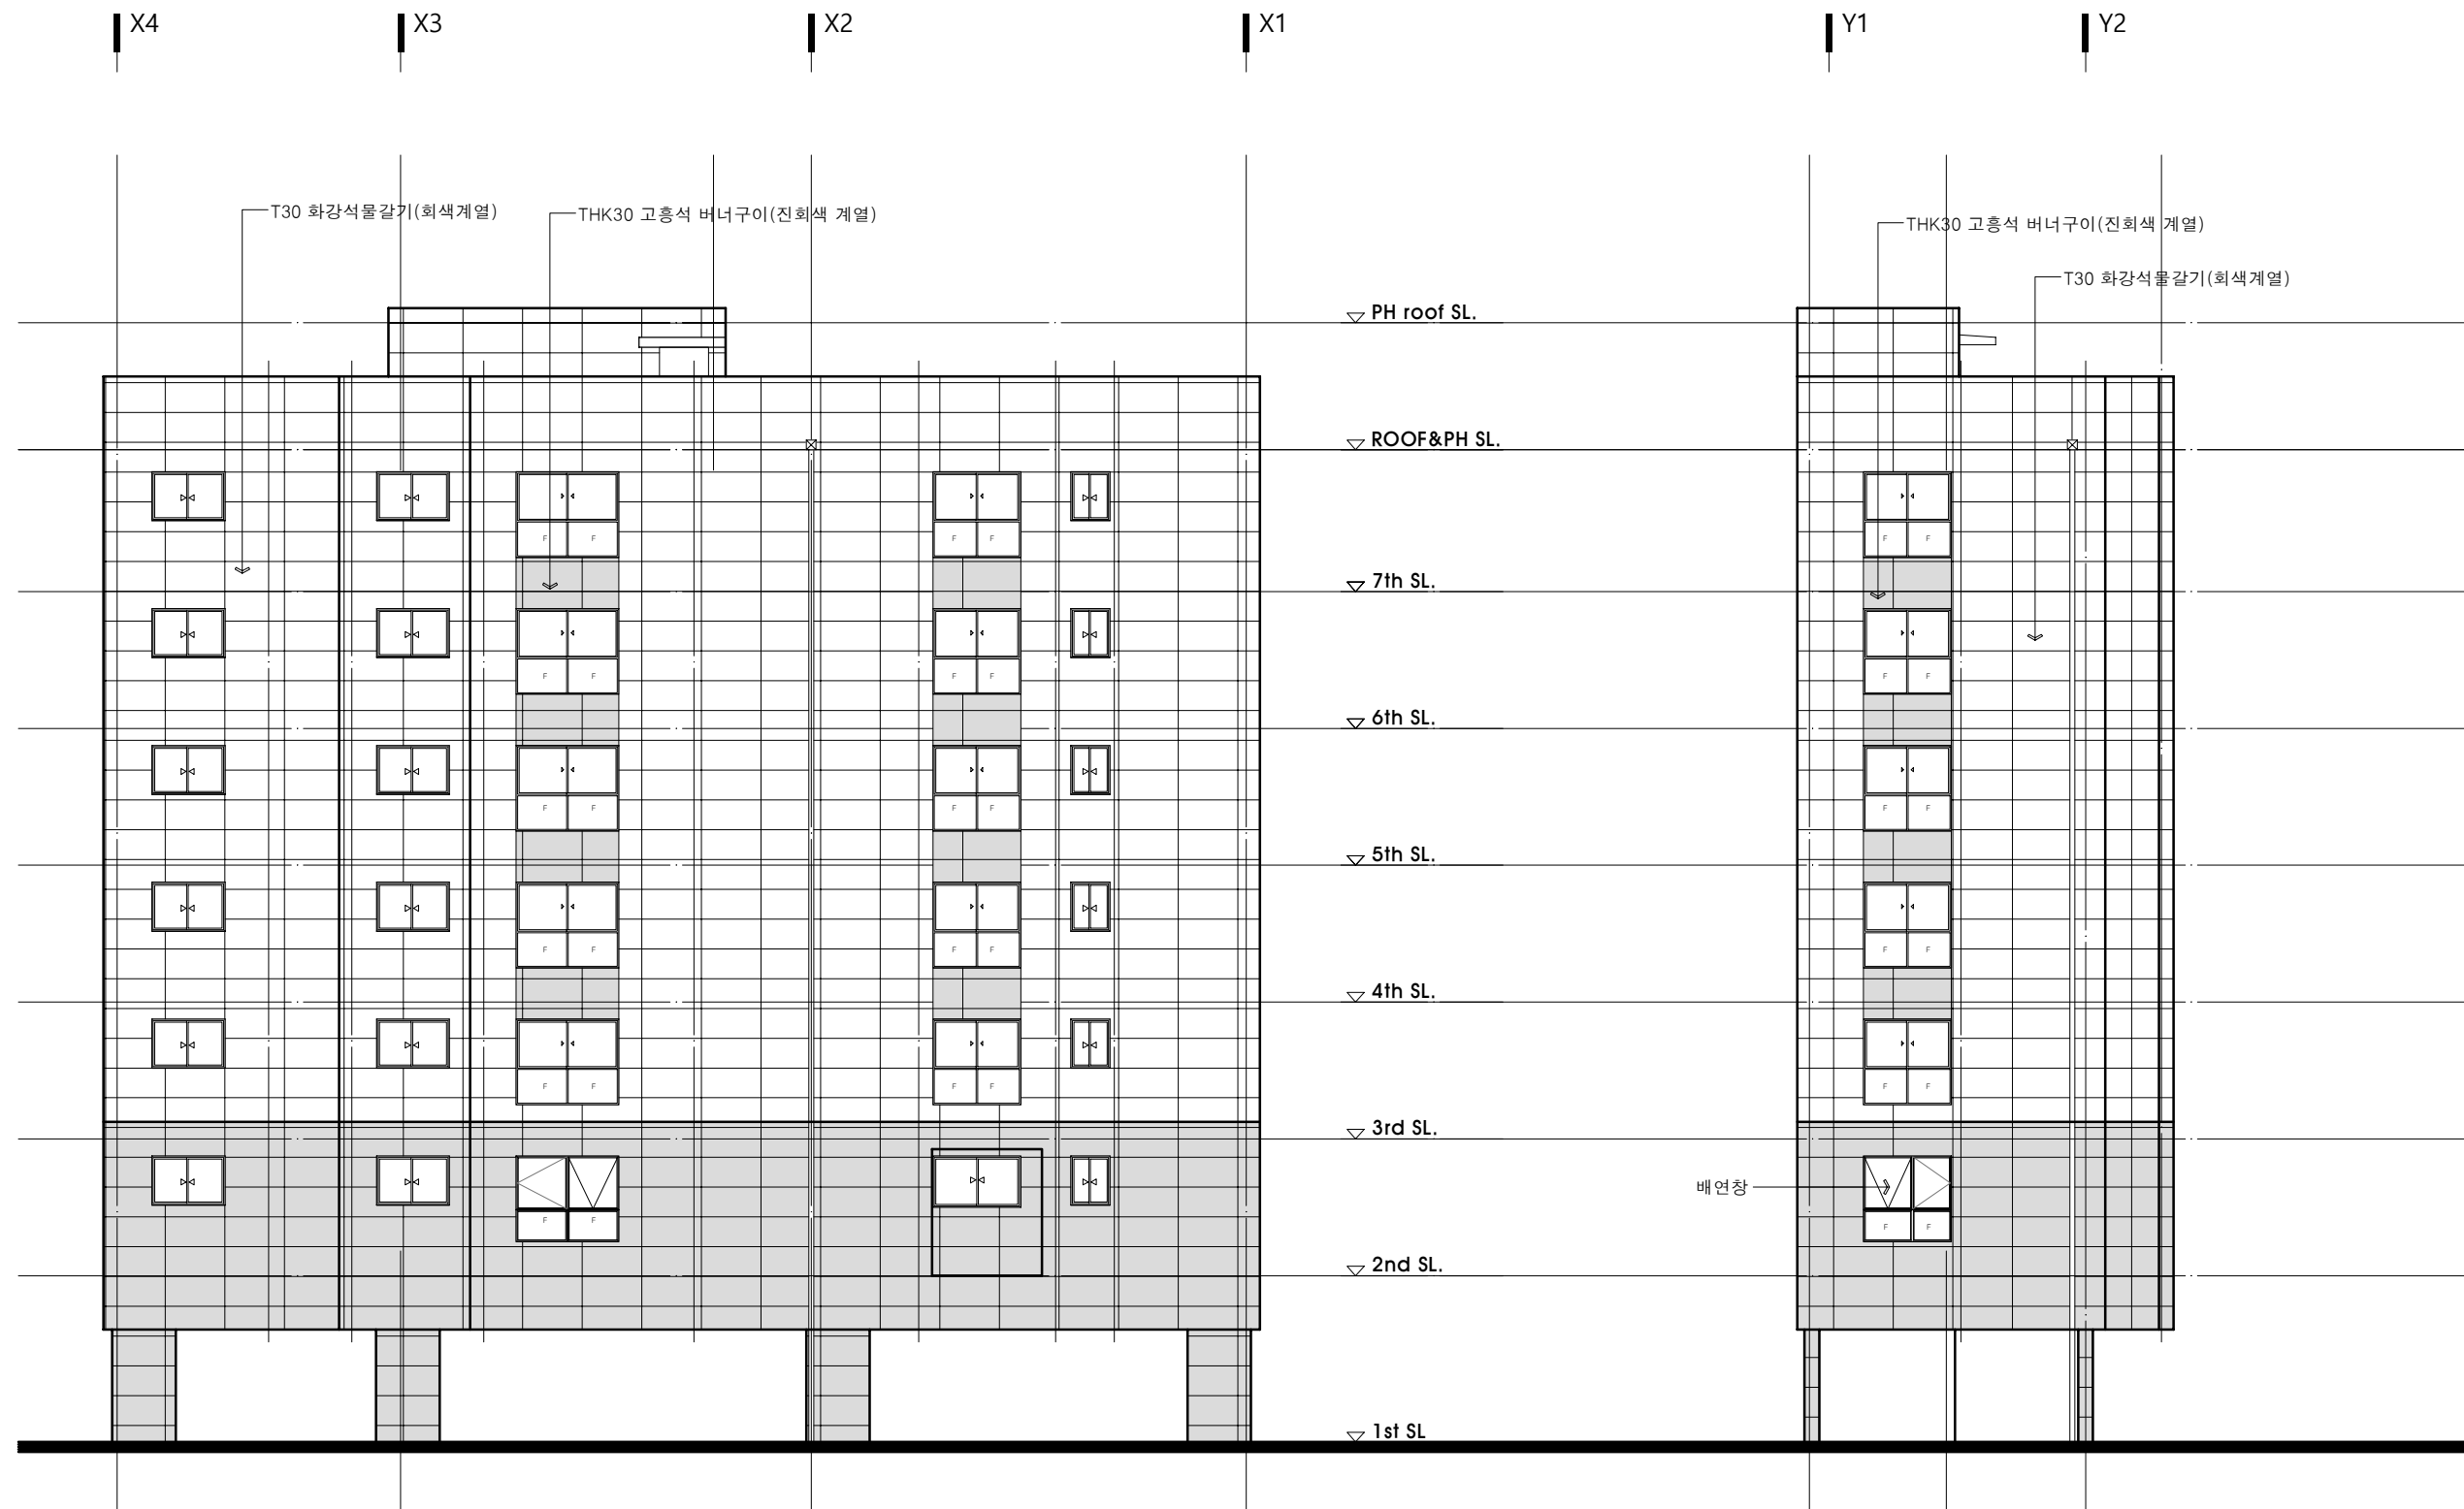

1
A
좌 측 면 도
SCALE : 1/150

1
A
배 면 도
SCALE : 1/150

PROJECT TITLE
사 업 명 칭
(관악구 신림동 1571-12)

신림동 도시형생활주택/오피스텔 신축공사
(SH 청년임대 주택)

NAME OF DRAWING
도 면 명

배면도, 좌측면도

NOTE
주 기

▼ ▼

DATE
일 자
▲ REVISIONS
수 정
▲ NO.

DESIGNED BY
설 계

CHECKED BY
심 사

APPROVED BY
승 인

CONSULTANTS
협 동 설 계

SCALE
축 척
1 / 150

DATE
일 자
2021 . 10

DWG NO.
도 면 번 호
A - 302

FILE NAME
화 일 명

테크원
건축사사무소

TECHONE ARCHITECTS & ENGINEERS
CO., LTD

TEL. 02)482-2466(대)
FAX. 02)488-2466