

1. 조감도



2. 건축개요

■ 건축개요

- 설 계 명 : 신림동 510-20호 도시형생활주택(소형주택) 신축공사
- 대 지 위 치 : 서울특별시 관악구 신림동 510-20호
- 지 역·지 구 : 제2종 일반주거지역
- 건 물 용 도 : 공동주택-도시형생활주택(소형주택)
- 건 물 규 모 : 지상 5층
- 대 지 면 적 : 330.60 m²
- 건 축 면 적 : 191.66 m²
- 연 면 적 : 659.97 m²
- 건 폐 율 : 57.97 %
- 용 적 륜 : 199.63 %
- 최 고 높 이 : 15.95 m
- 건 물 구 조 : 철근콘크리트조
- 주 차 대 수 : 7대(법정), 7대(계획)
- 조 경 면 적 : 16.53m²(법정), 20.48m²(계획)

3. 입면도



정면도

우측면도

배면도


좌측면도

[illegible]

4. 설계자 의도

■ 디자인 의도

- 보행자, 차량 출입의 원활한 계획
- 도로측에 순응한 주동 배치
- 정면성을 강조하는 디자인 계획

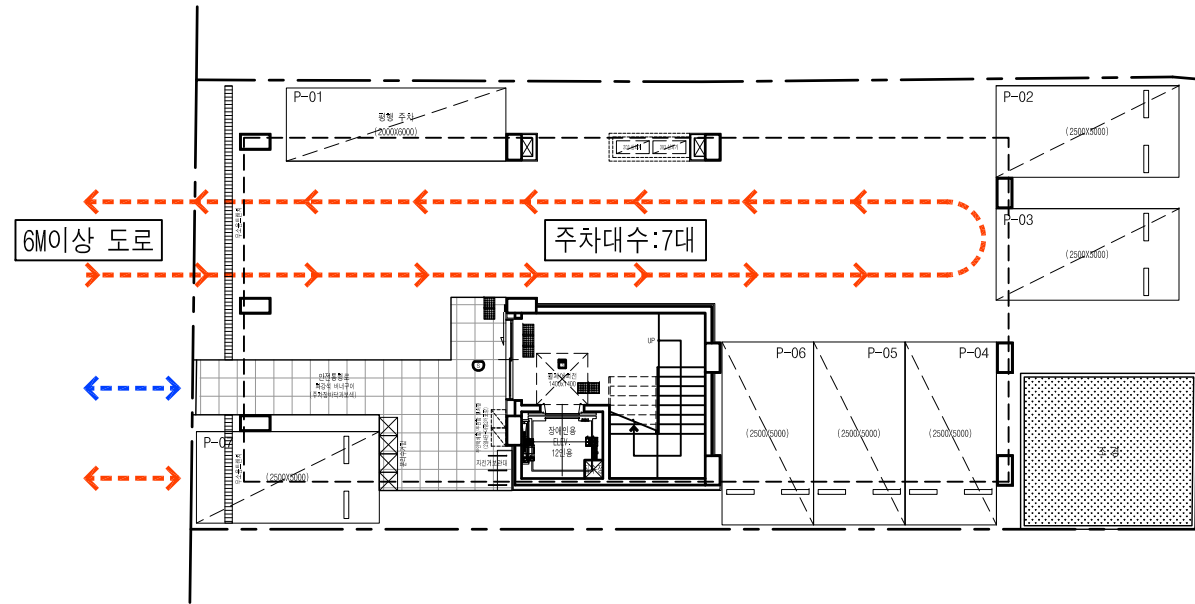

■ 입면 디자인 계획


- 창호크기 및 열을 맞추어 입면에 정돈된 이미지를 부여함.

동일한 창호 배치로 단정함과
균일성을 부여하여 통일감 표현.




5. 재료계획

1. 외벽 마감재

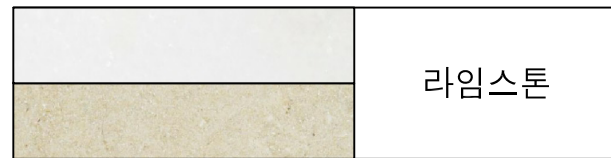

2. 주차장 바닥재

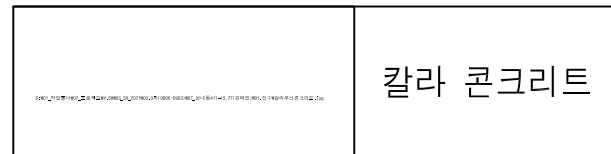

3. 옥외 난간대



■ 외장재

구분	실명	재료명
1층	필로티	바닥 : 칼라무늬콘크리트
	주차장	천정 : 내풍압형 AL 천정재
2~5층	현관	바닥 : 폴리싱타일
	방	바닥 : 데코타일 마감 천정 : 실크 또는 발포벽지
	거실	바닥 : 데코타일 마감 천정 : 실크 또는 발포벽지
	베란다	바닥 : 칼라 콘크리트 천정 : AL 천정판

■ 내장재

6. 색채계획


- 자연스러운 색상과 주변과의 조화
- 주변과 어울리는 색상을 활용한 입면 계획
- 가로경관 미관성 및 친근성





라임스톤(아이보리색상)

라임스톤(화이트색상)

PROJECT TITLE 사업명 신림동 510-20호 도시형생활주택(소형주택) 신축공사		
NAME OF DRAWING 도면명 디자인 의도		
NOTE 주 기 ▼ ▼		
NO. ▲ REVISIONS ▲ DATE 번호 수정 일자		
DESIGNED BY 설 계		
CHECKED BY 심 사		
APPROVED BY 승 인		
CONSULTANTS 협동설계		
SCALE 축척		
DATE 일 자 2023. 09.		
DWG NO. 도면 번호 A-03		
SHEET NO. 일련 번호 □-□□□		
 dawroom 건축사무소 다음건축 THE ARCHITECTS DESIGN GROUP TEL. 02.414.6061 (代) FAX. 02.414.6062		

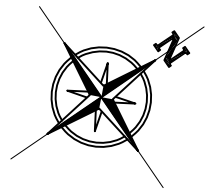

6M이상 도로

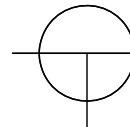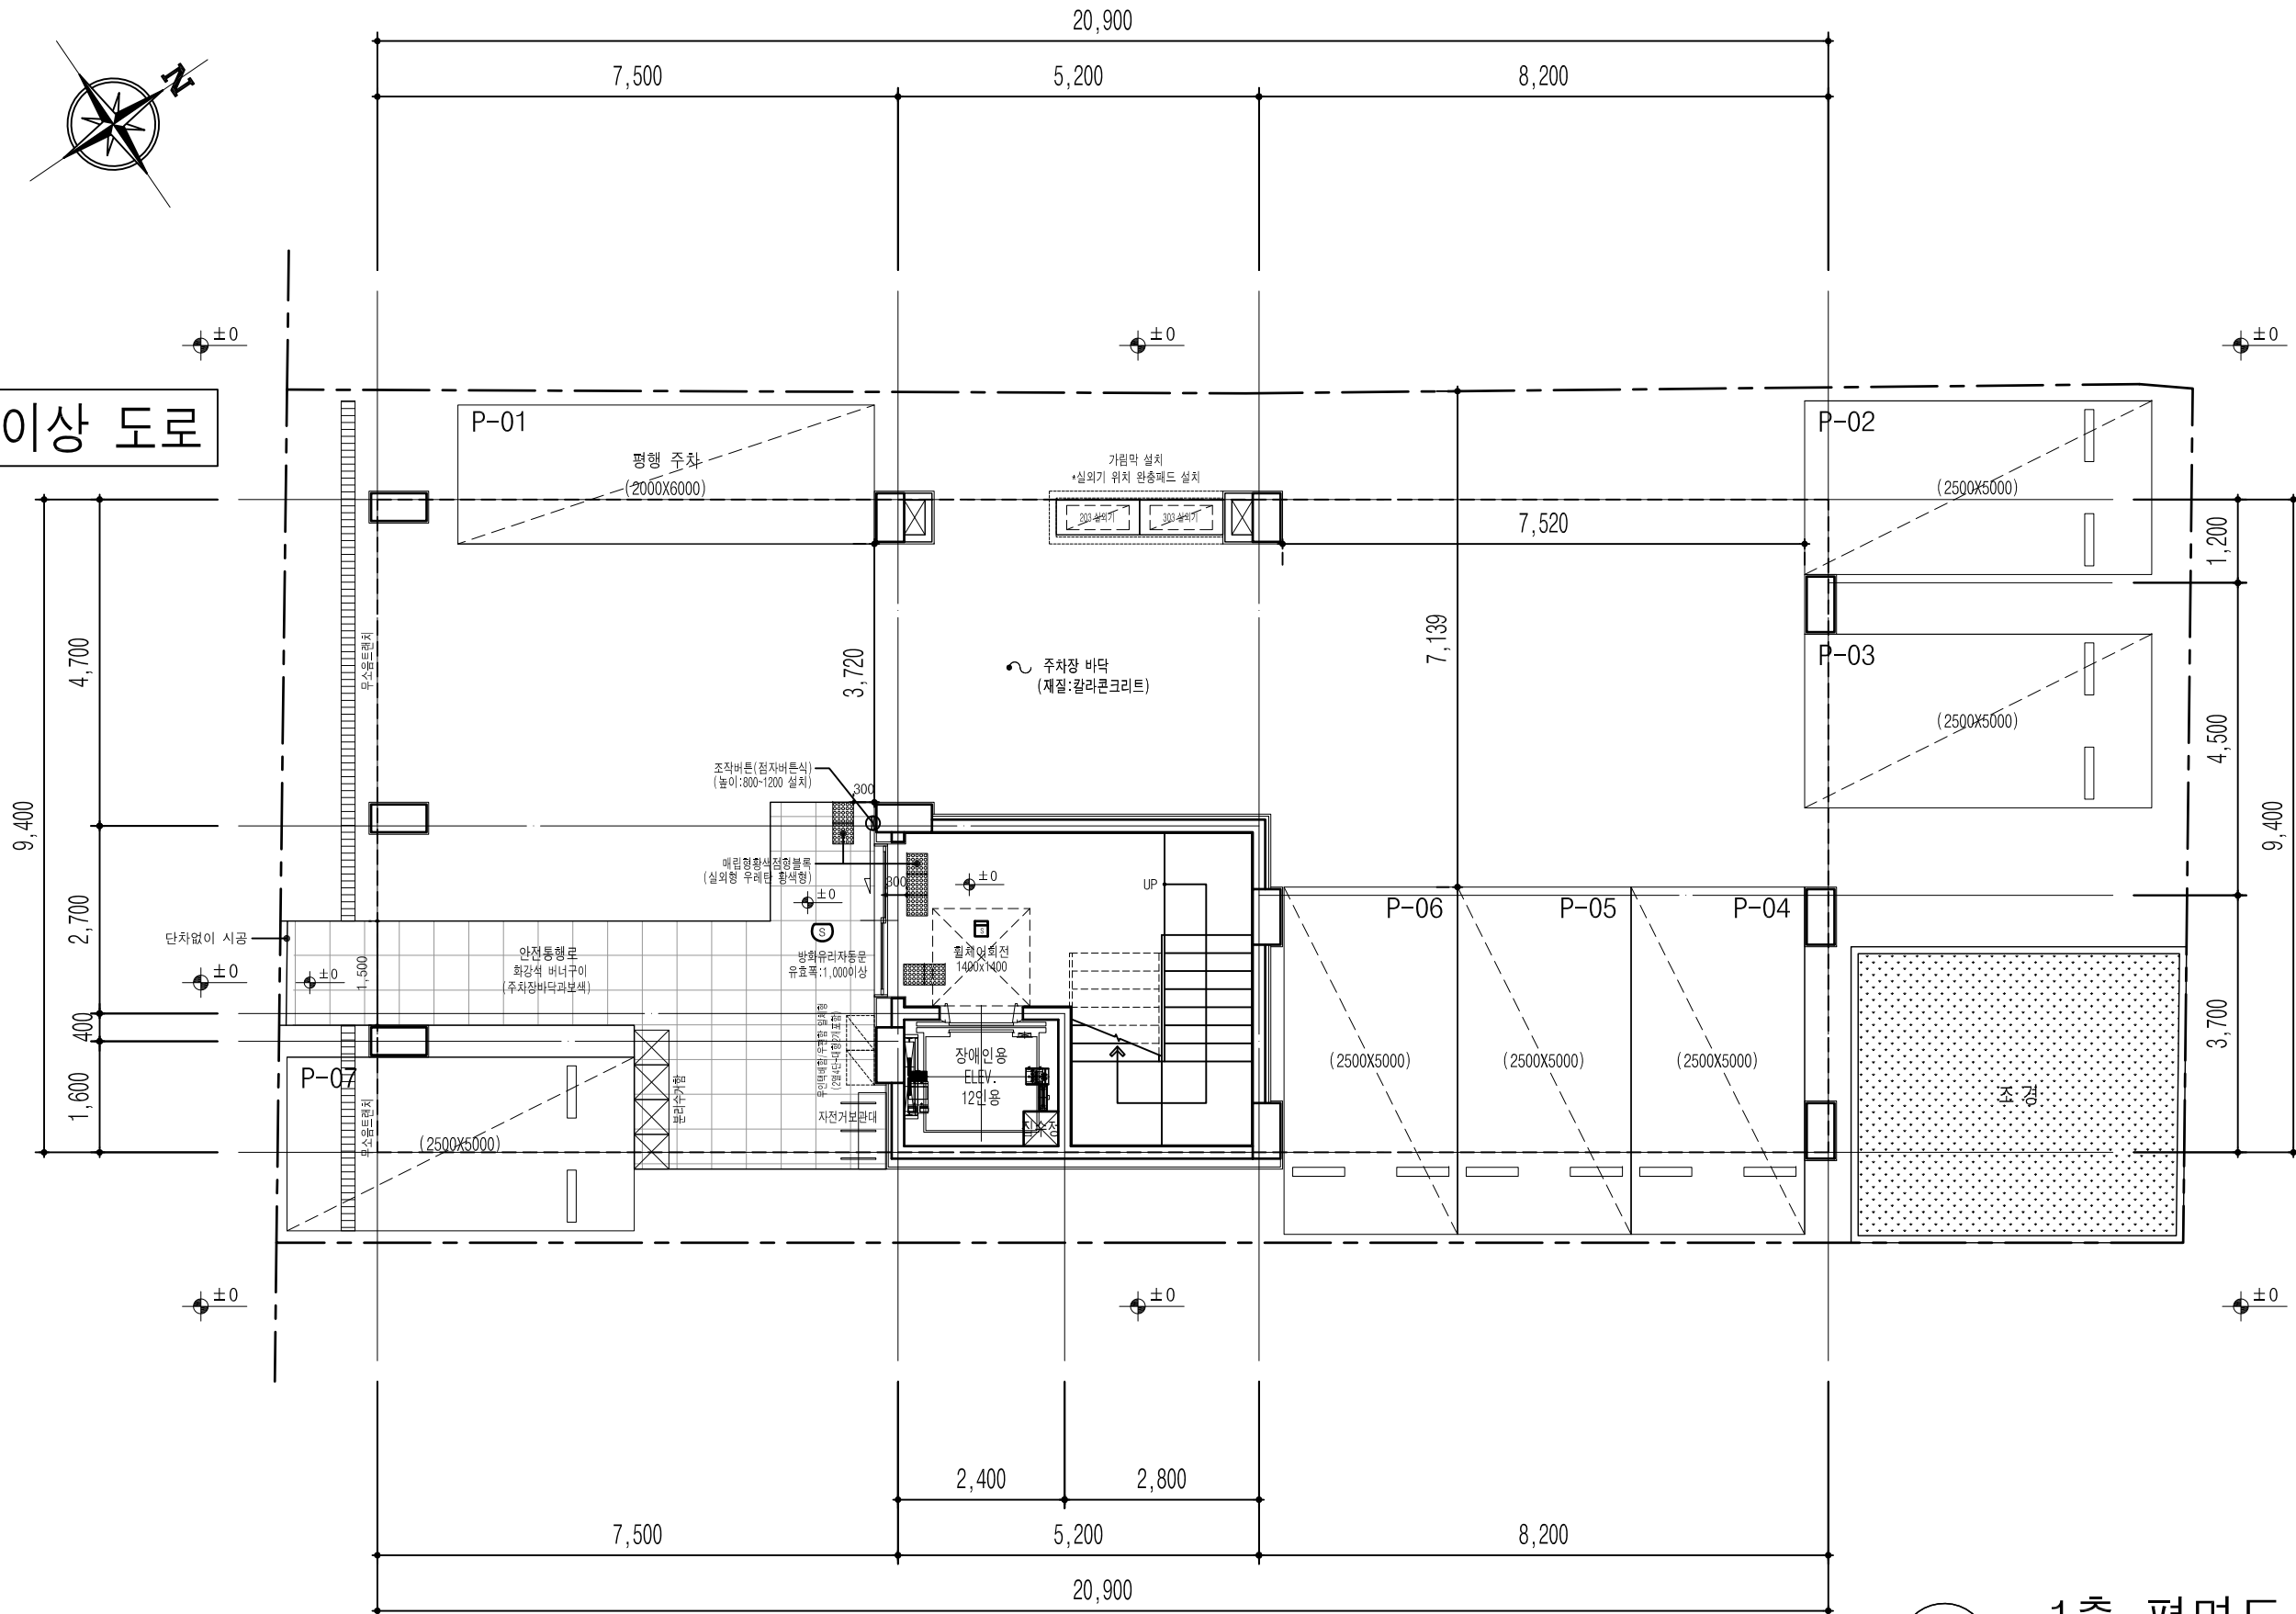

1층 평면도

SCALE : A3 : 1/100

PROJECT TITLE
사업명칭

신림동 510-20호
도시형생활주택(소형주택)
신축공사

NAME OF DRAWING
도면명

1층 평면도

NOTE
주 기

- 단독경보감지기(연기식)
- 단독경보감지기(열감지)
- ABC분말소화기(2.5KG)
- 가스누설경보기
- 일산화탄소경보기
- 차면시설
- 보일러
- 에어컨 실외기

NO. REVISIONS DATE
번호 수정 일자

DESIGNED BY
설 계

CHECKED BY
심 사

APPROVED BY
승 인

CONSULTANTS
협동설계




SCALE
축척 1/100

DATE
일 자 2023. 09.

DWG NO.
도면 번호 A-21

SHEET NO.
일련 번호

 **다룸건축**
dawroom
건축사무소 다음건축
THE ARCHITECTS DESIGN GROUP
TEL. 02.414.6061 (代)
FAX. 02.414.6062

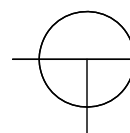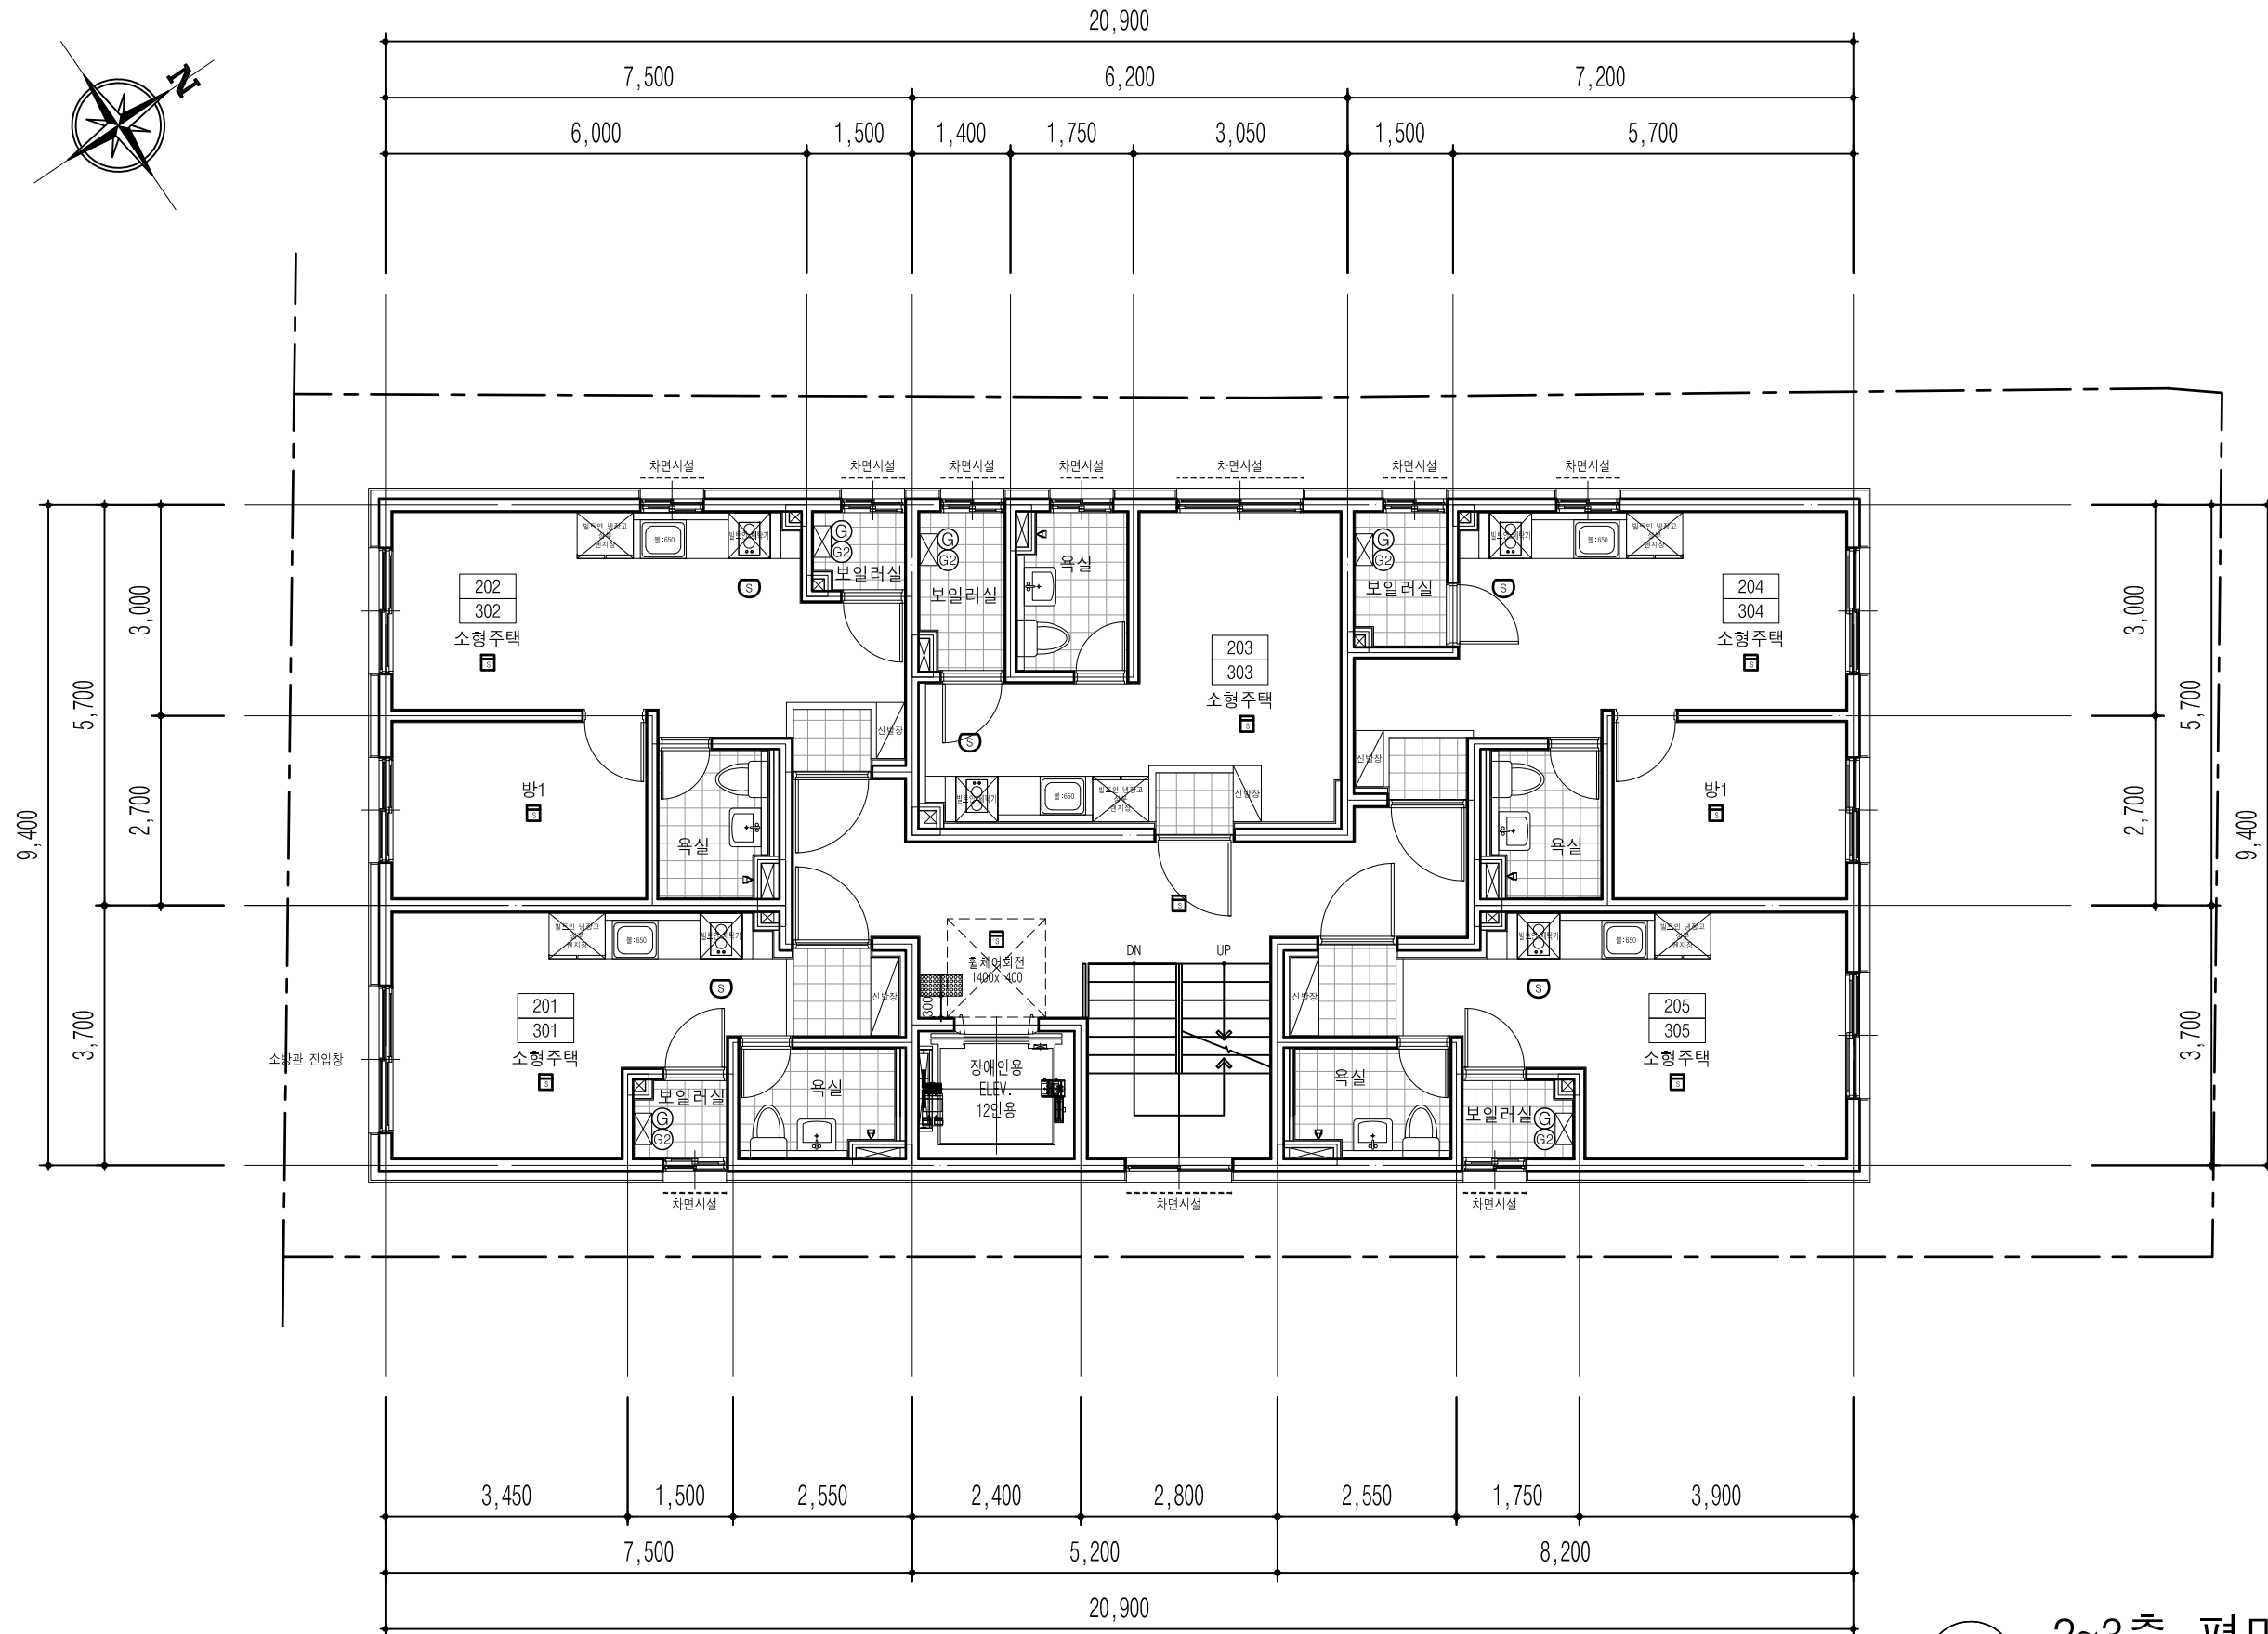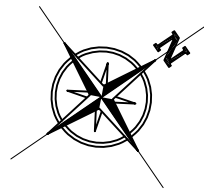

2~3층 평면도

SCALE : A3 : 1/100

PROJECT TITLE
사업명

신림동 510-20호
도시형생활주택(소형주택)
신축공사

NAME OF DRAWING
도면명

2~3층 평면도

NOTE
주 기

단독경보감지기(연기식)

단독경보감지기(열감지)

ABC분말소화기(2.5KG)

가스누설경보기

일산화탄소경보기

차면시설

보일러

에어컨 실외기

NO. REVISIONS DATE
번호 수정 일자

DESIGNED BY
설 계

CHECKED BY
심 사

APPROVED BY
승 인


CONSULTANTS
협 동 설 계

SCALE
축척 1/100

DATE
일 자 2023. 09.




DWG NO.
도면 번호 A-22

SHEET NO.
일련 번호 □-□□□

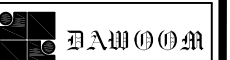

건축사무소 다음건축

THE ARCHITECTS DESIGN GROUP
TEL. 02.414.6061 (代)
FAX. 02.414.6062

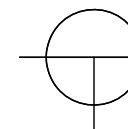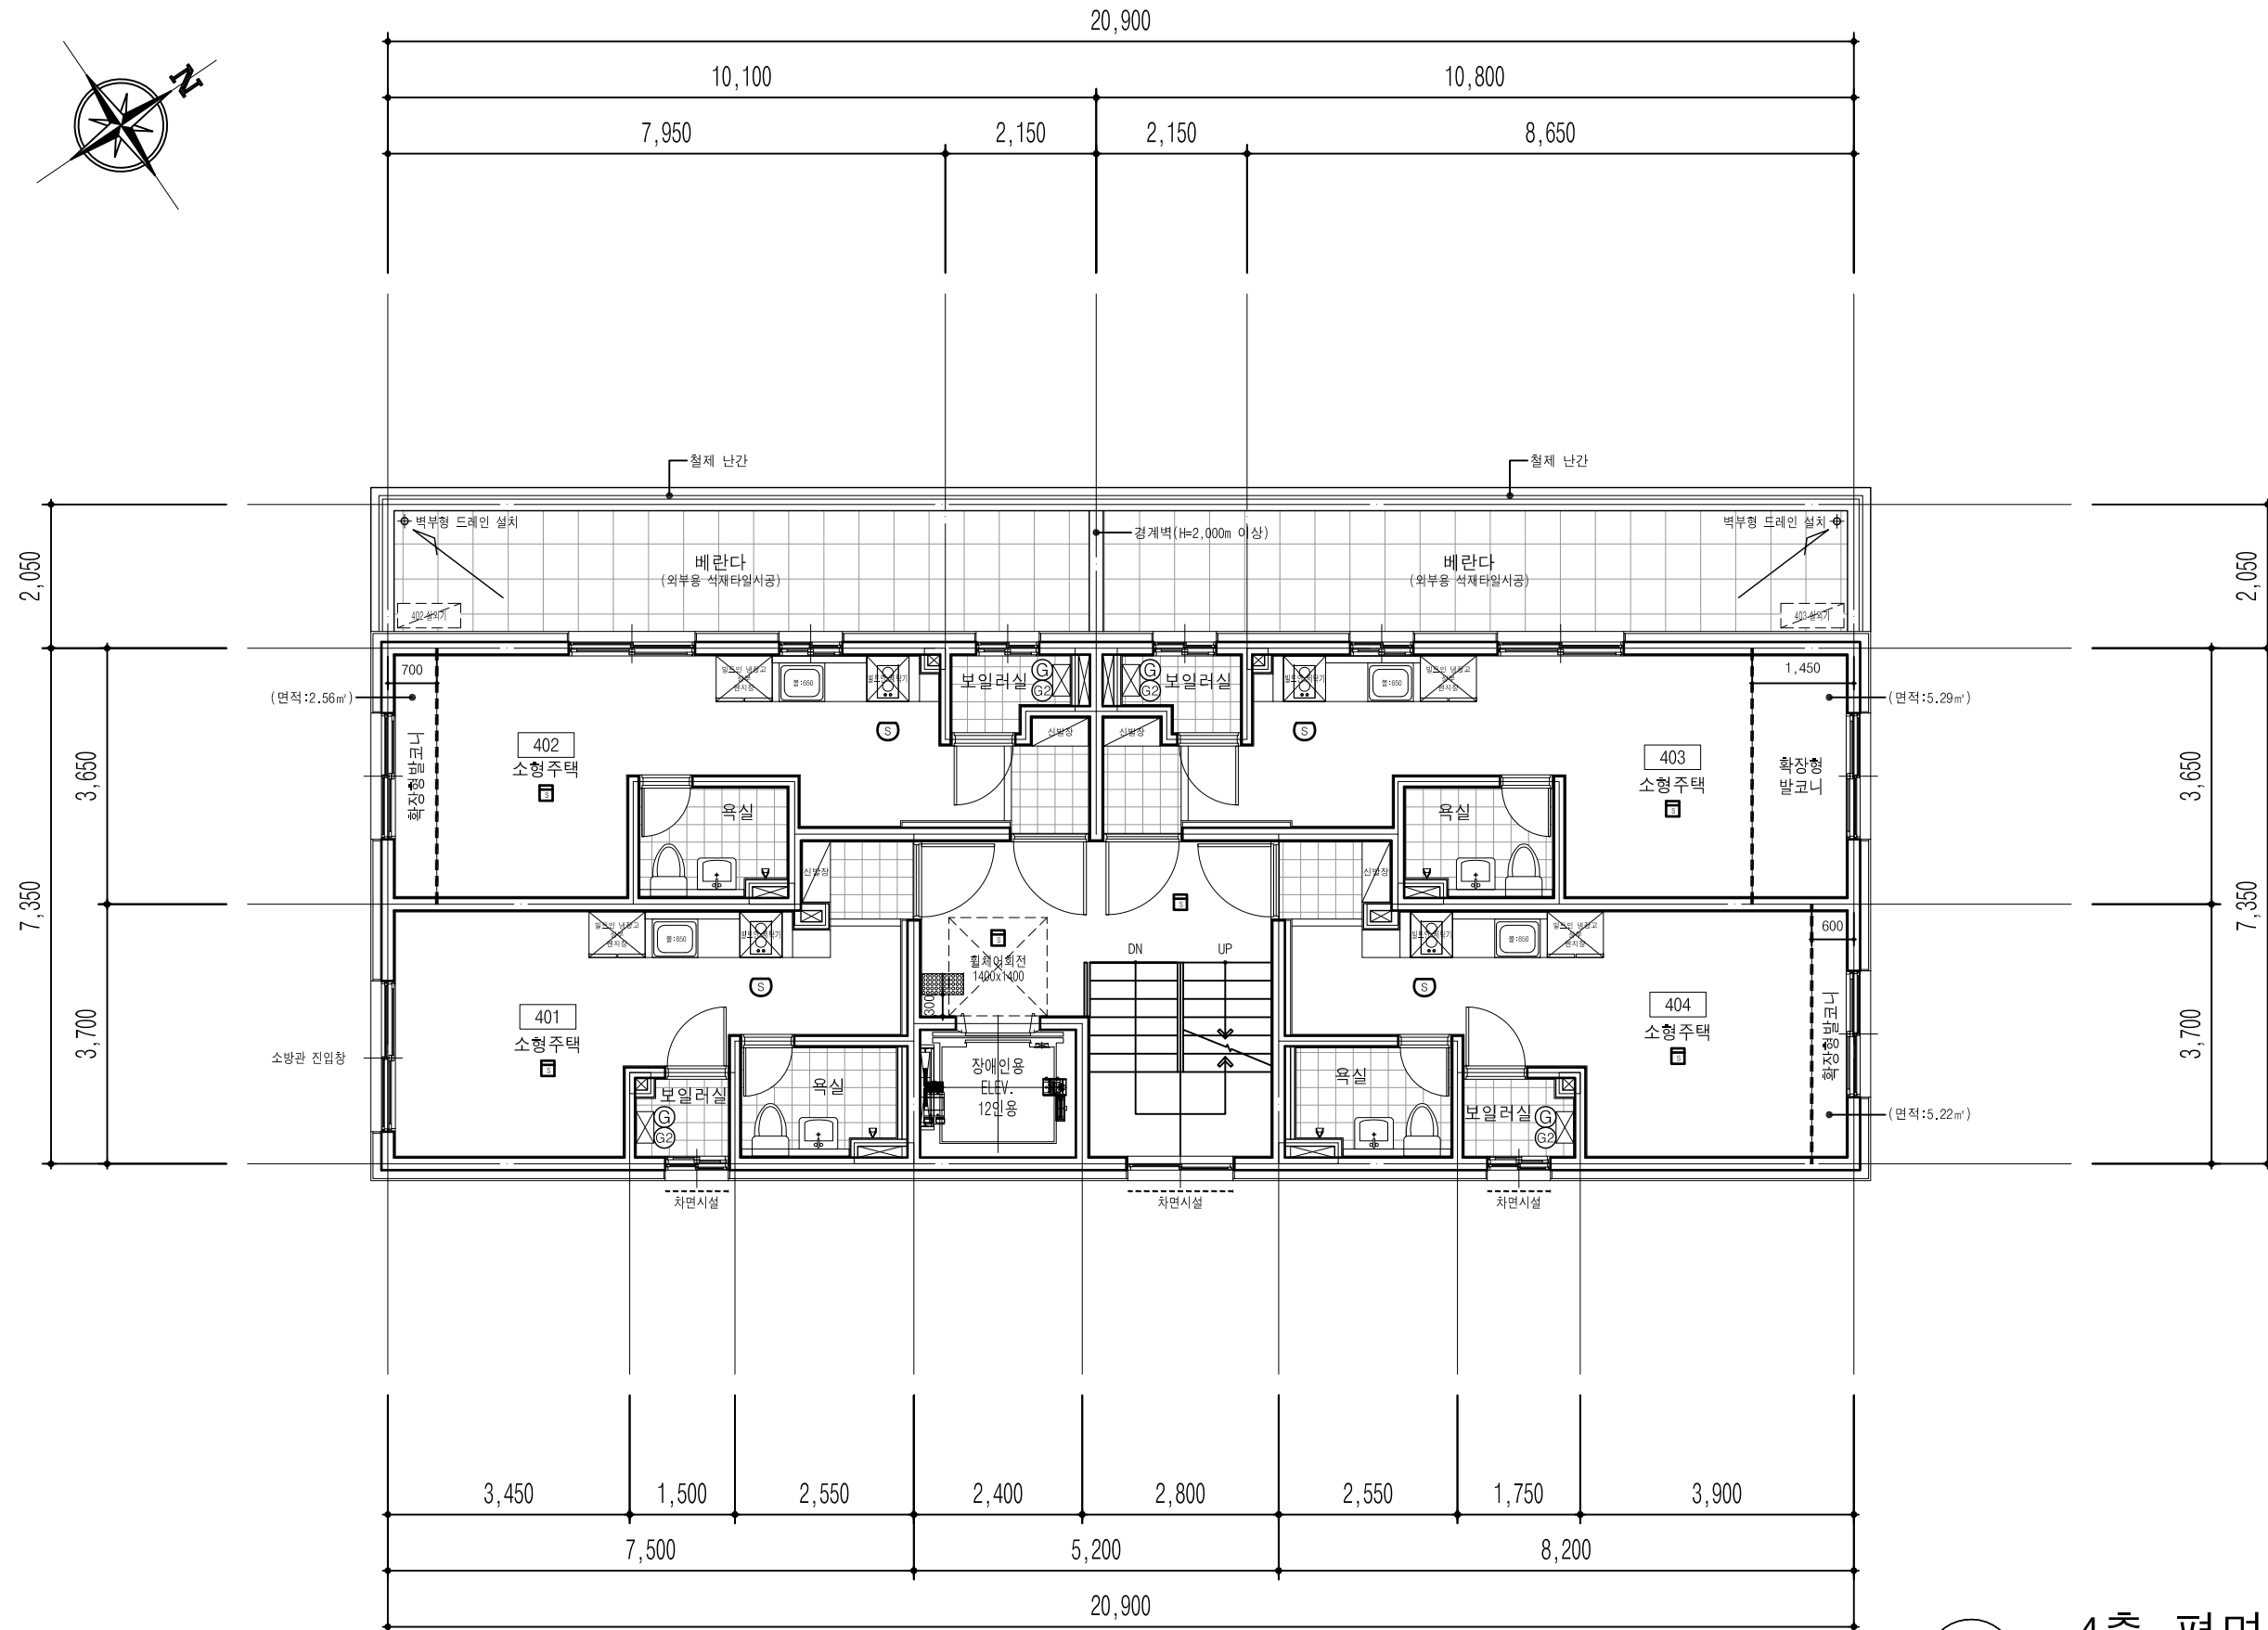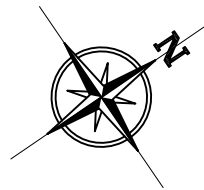

4층 평면도

SCALE : A3 : 1/100

PROJECT TITLE
사업명
신림동 510-20호
도시형생활주택(소형주택)
신축공사

NAME OF DRAWING
도면명

4층 평면도

NOTE
주 기

- 단독경보감지기(연기식)
- 단독경보감지기(열감지)
- ABC분말소화기(2.5KG)
- 가스누설경보기
- 일산화탄소경보기
- 차면시설
- 보일러
- 에어컨 실외기

NO. REVISIONS DATE
번호 수정 일자

DESIGNED BY
설 계

CHECKED BY
심 사

APPROVED BY
승 인

CONSULTANTS
협 동 설 계




SCALE
축척 1/100

DATE
일 자 2023. 09.

DWG NO.
도면 번호 A-23

SHEET NO.
일련 번호 □-□□□

다움
dawoom
건축사무소 다움건축
THE ARCHITECTS DESIGN GROUP
TEL. 02.414.6061 (代)
FAX. 02.414.6062

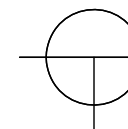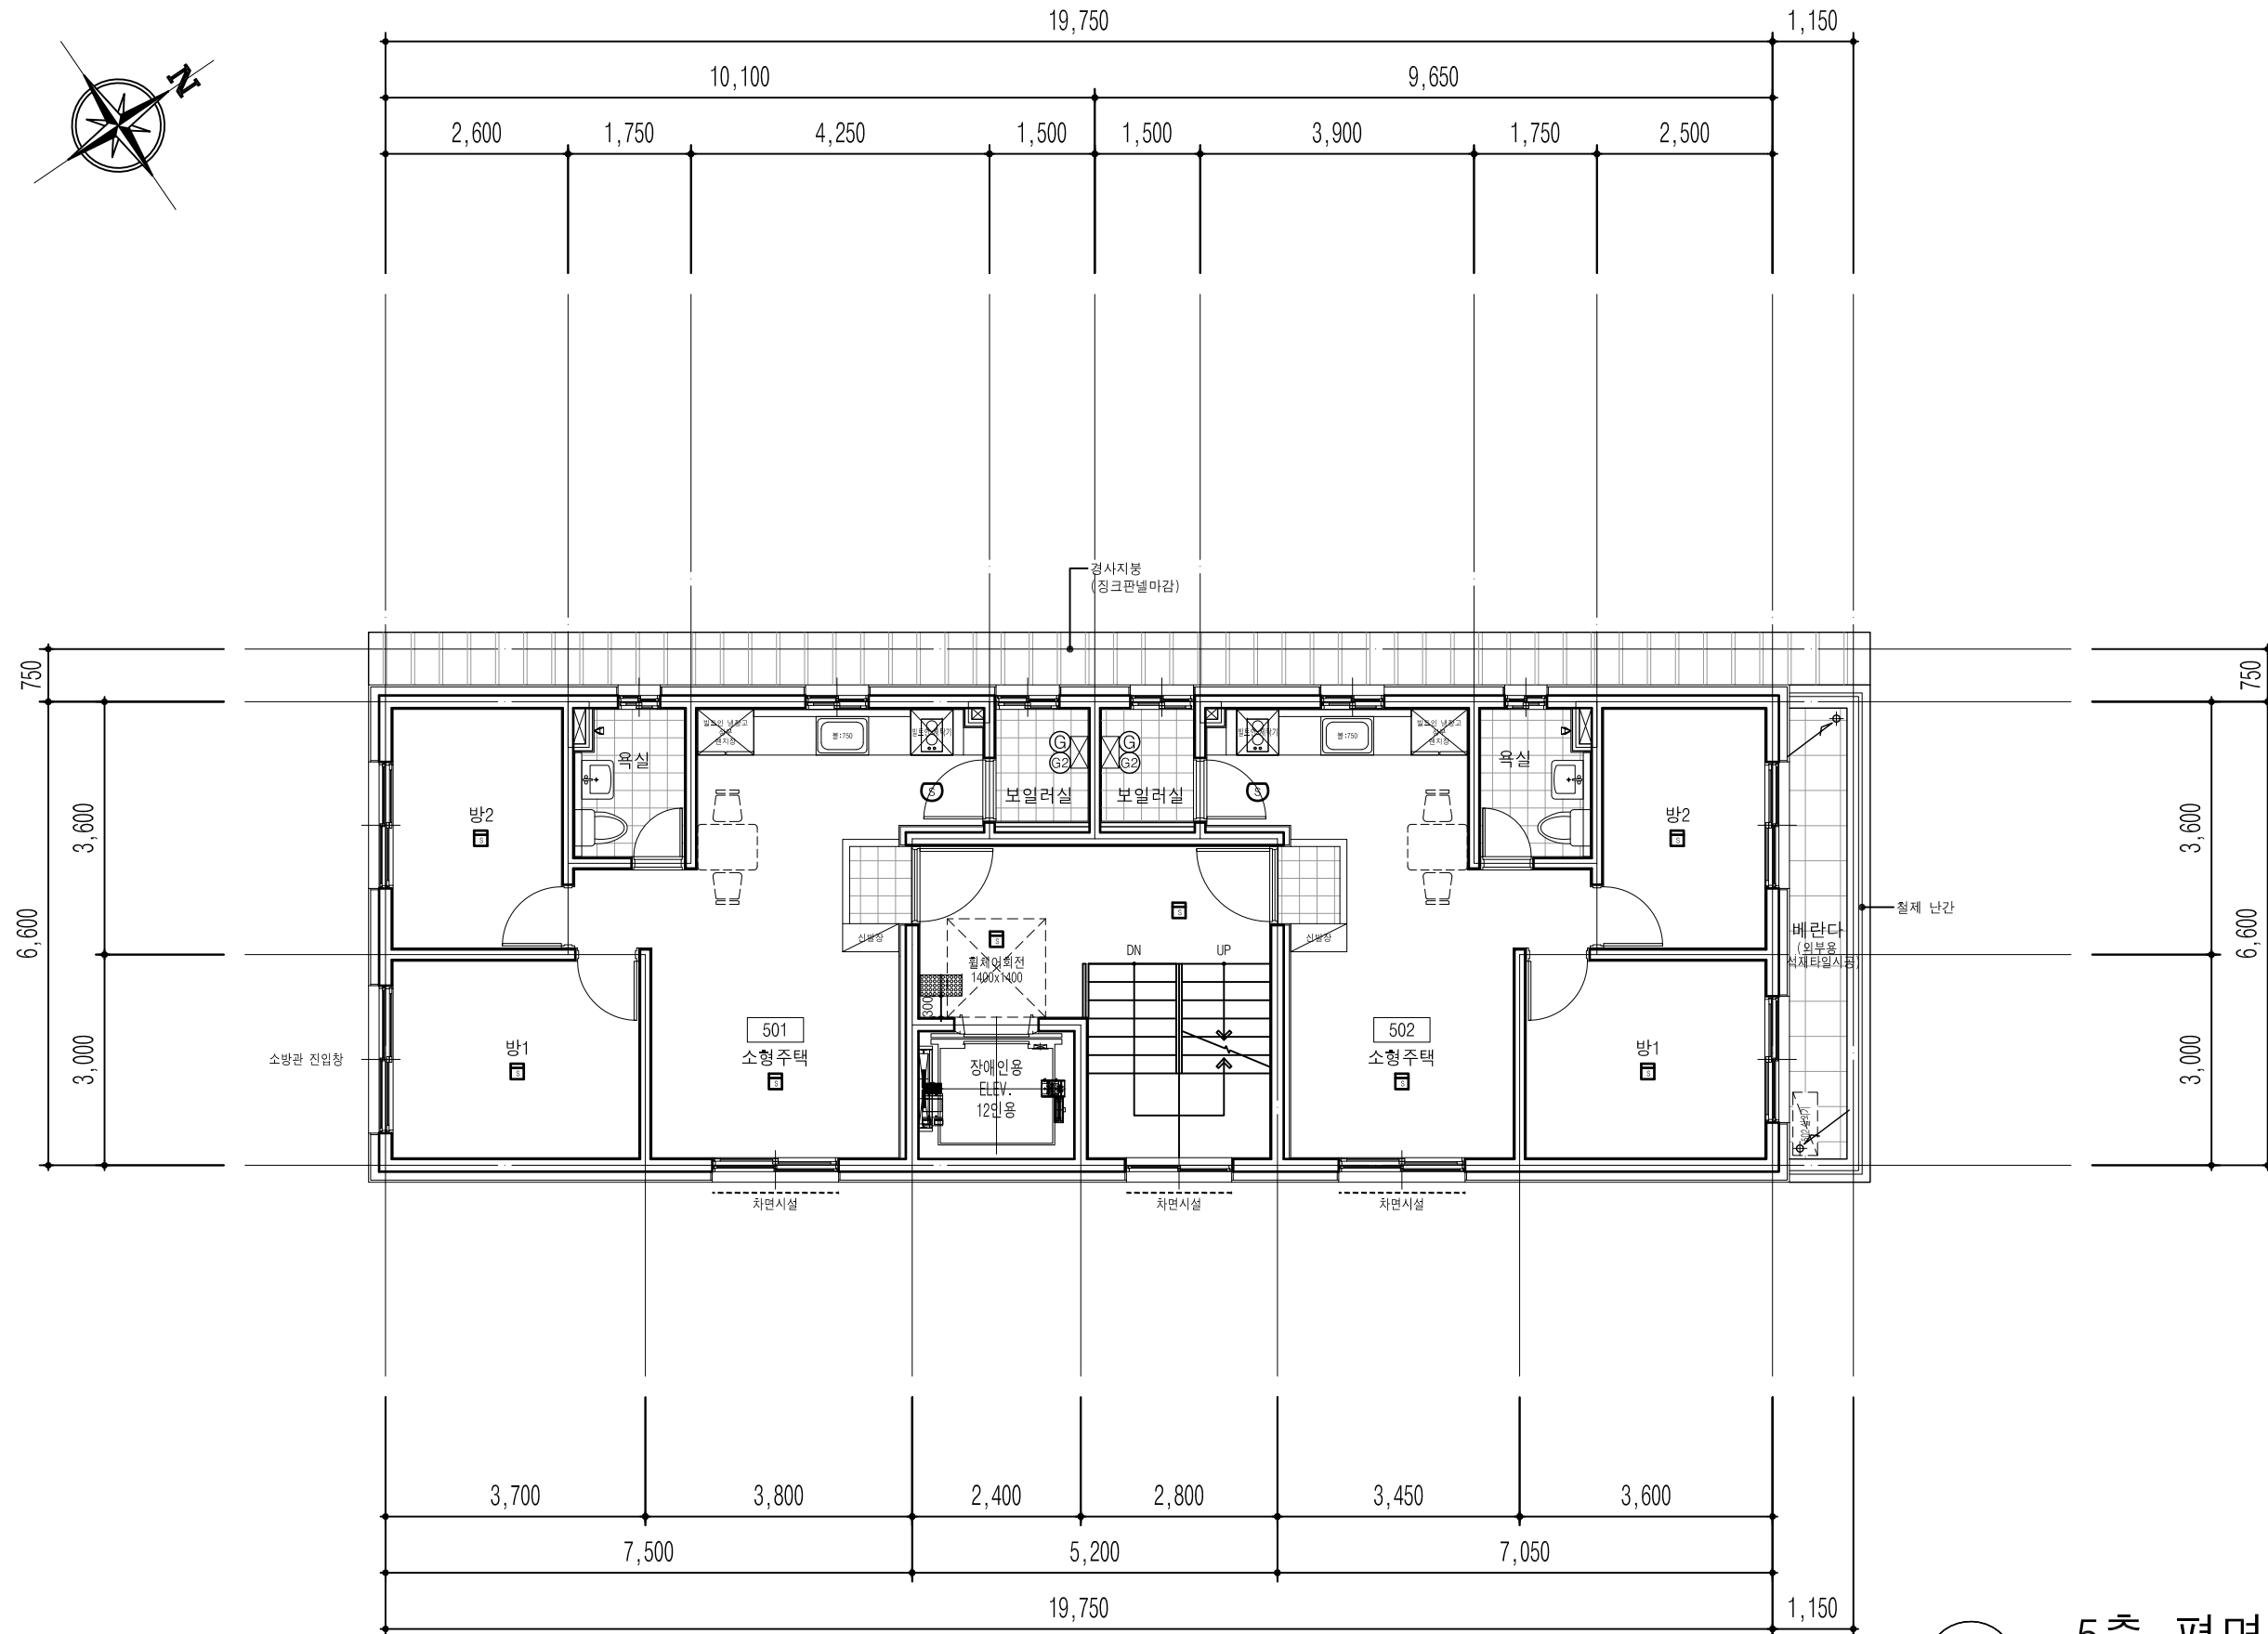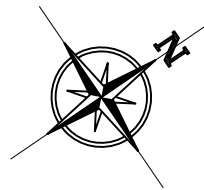

5층 평면도

SCALE : A3 : 1/100

PROJECT TITLE
사업명

신림동 510-20호
도시형생활주택(소형주택)
신축공사

NAME OF DRAWING
도면명

5층 평면도

NOTE
주 기

- 단독경보감지기(연기식)
- 단독경보감지기(열감지)
- ABC분말소화기(2.5KG)
- 가스누설경보기
- 일산화탄소경보기
- 차면시설
- 보일러
- 에어컨 실외기

NO. REVISIONS DATE
번호 수정 일자

DESIGNED BY
설 계

CHECKED BY
심 사

APPROVED BY
승 인

CONSULTANTS
협 동 설 계

SCALE
축척 1/100

DATE
일 자 2023. 09.



DWG NO.
도면 번호 A-24

SHEET NO.
일련 번호 □-□□□



건축사사무소 다음건축

THE ARCHITECTS DESIGN GROUP
TEL. 02.414.6061 (代)
FAX. 02.414.6062

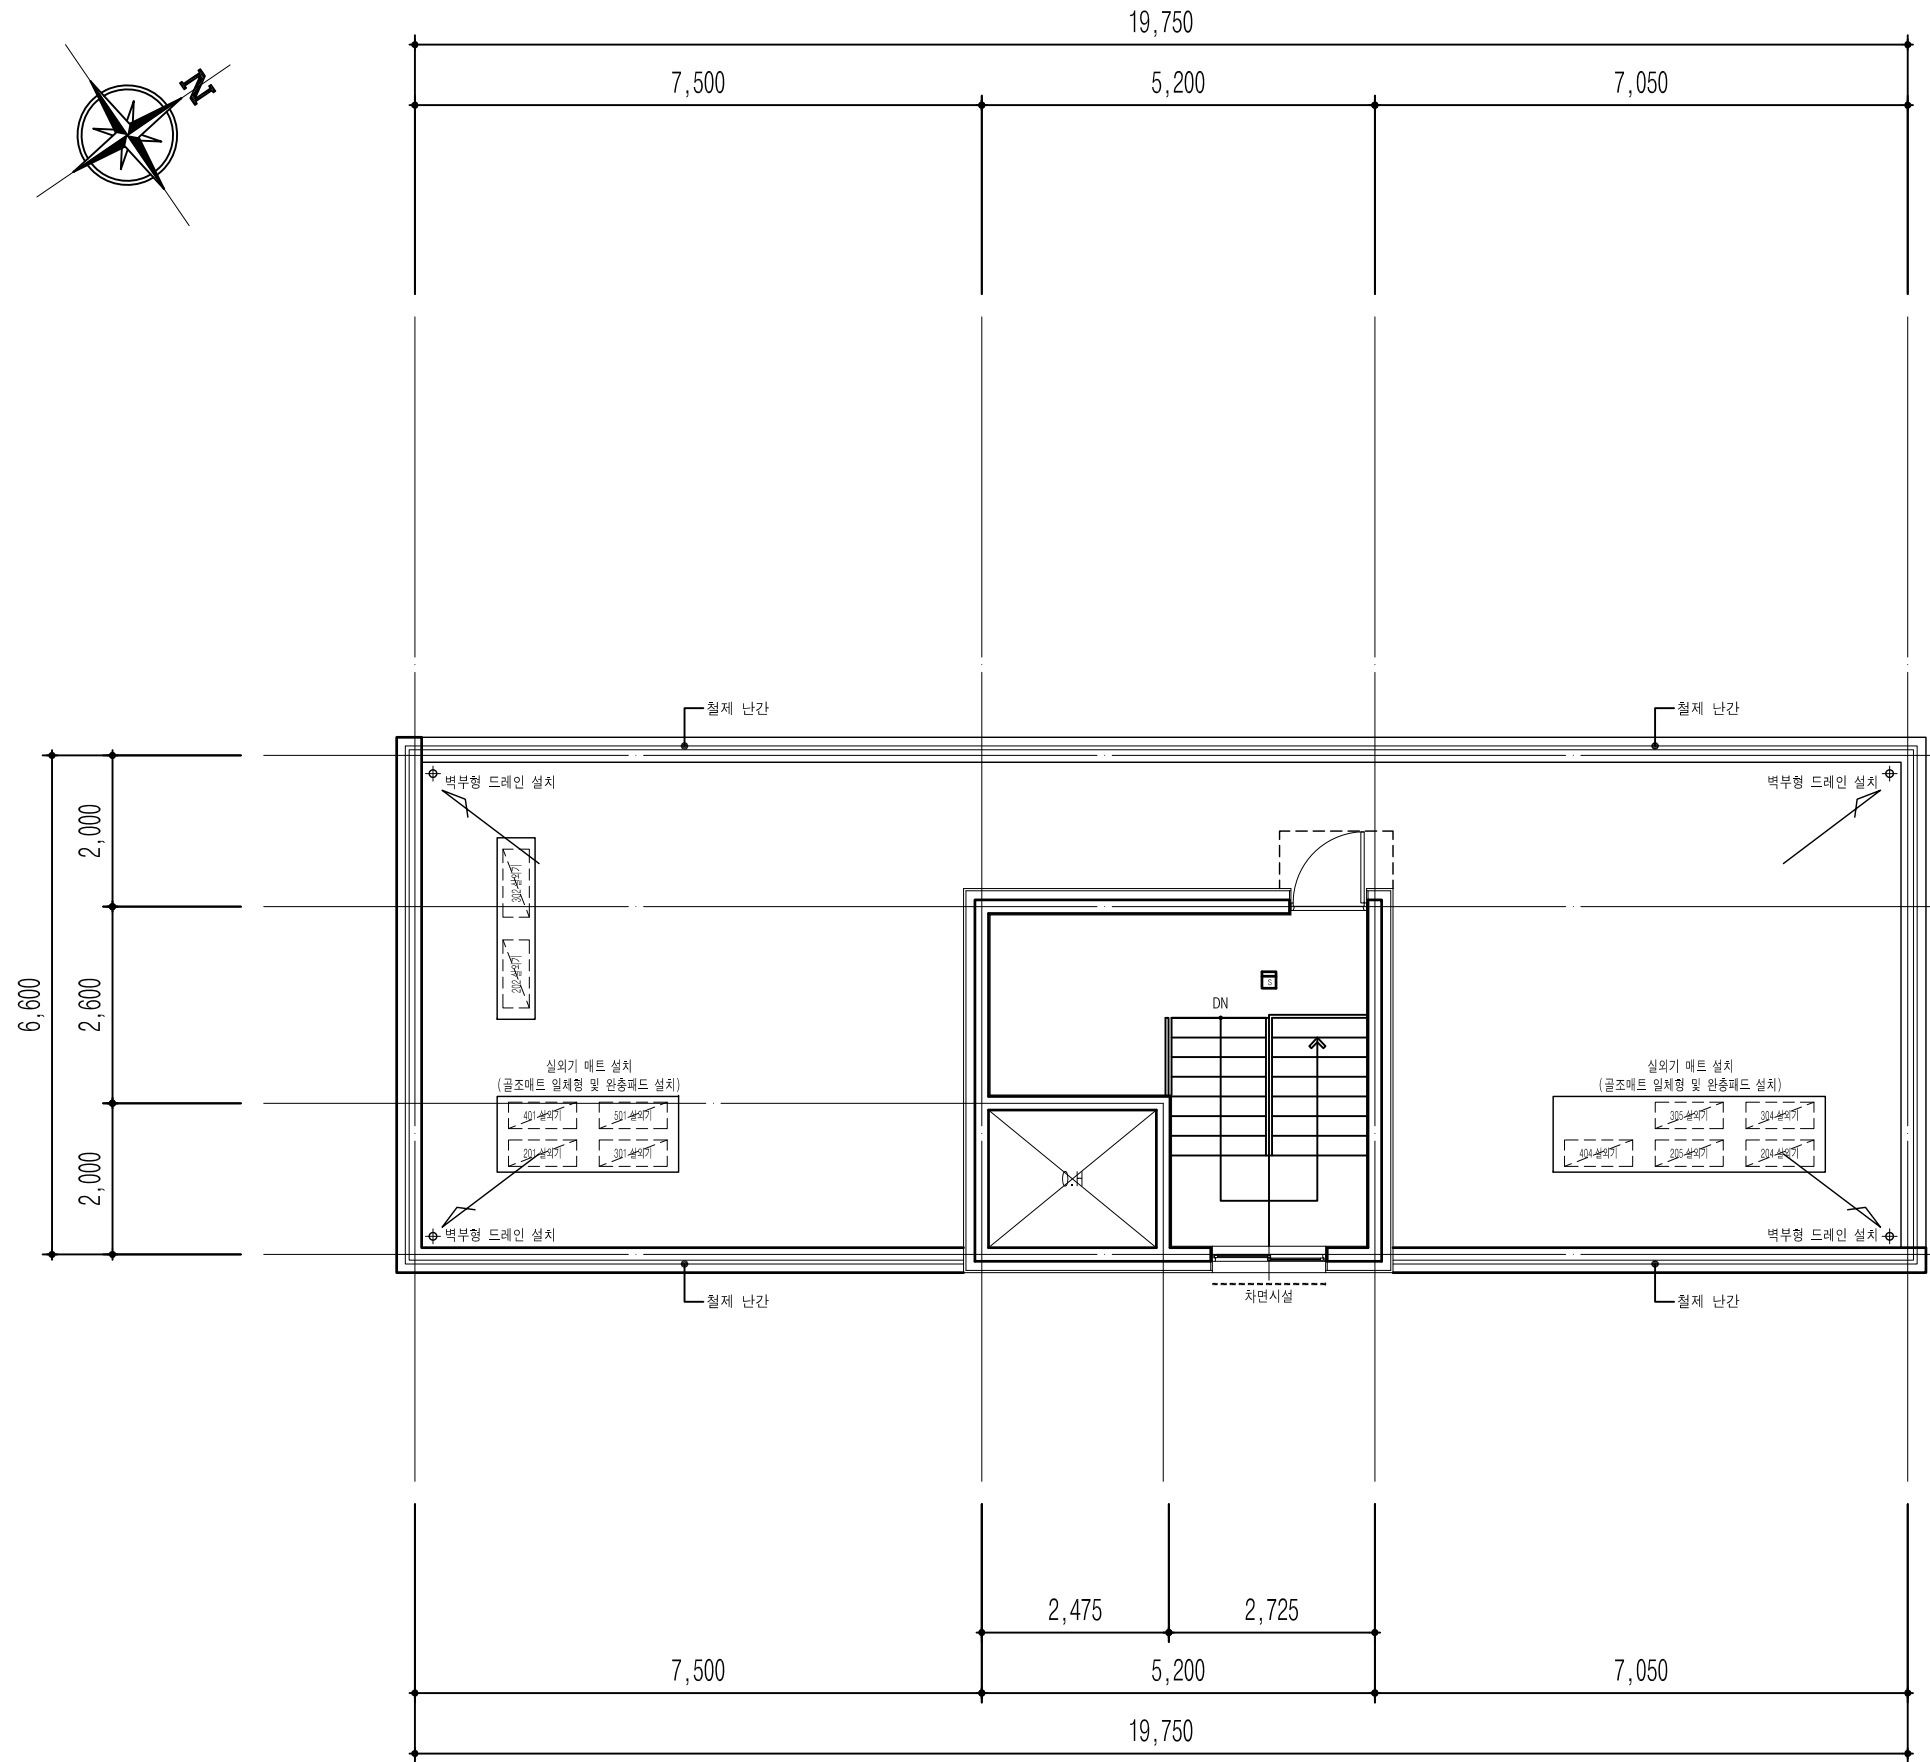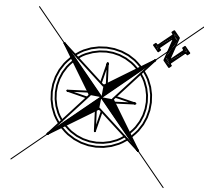

지붕및옥탑평면도
SCALE : A3 : 1/100

PROJECT TITLE
사업명칭

신림동 510-20호
도시형생활주택(소형주택)
신축공사

NAME OF DRAWING
도면명

지붕 평면도

- NOTE
주 기
- 단독경보감지기(연기식)
 - 단독경보감지기(열감지)
 - ABC분말소화기(2.5KG)
 - 가스누설경보기
 - 일산화탄소경보기
 - 차면시설
 - 보일러
 - 에어컨 실외기

NO. ▲ REVISIONS ▲ DATE
번호 수정 일자

DESIGNED BY
설 계

CHECKED BY
심 사

APPROVED BY
승 인

CONSULTANTS
협 동 설 계


SCALE
축 척 1/100

DATE
일 자 2023. 09.

DWG NO.
도면 번호 A-25

SHEET NO.
일련 번호 □—□□□

 **다움건축**
dawoom
건축사사무소 다움건축
THE ARCHITECTS DESIGN GROUP
TEL. 02.414.6061 (代)
FAX. 02.414.6062

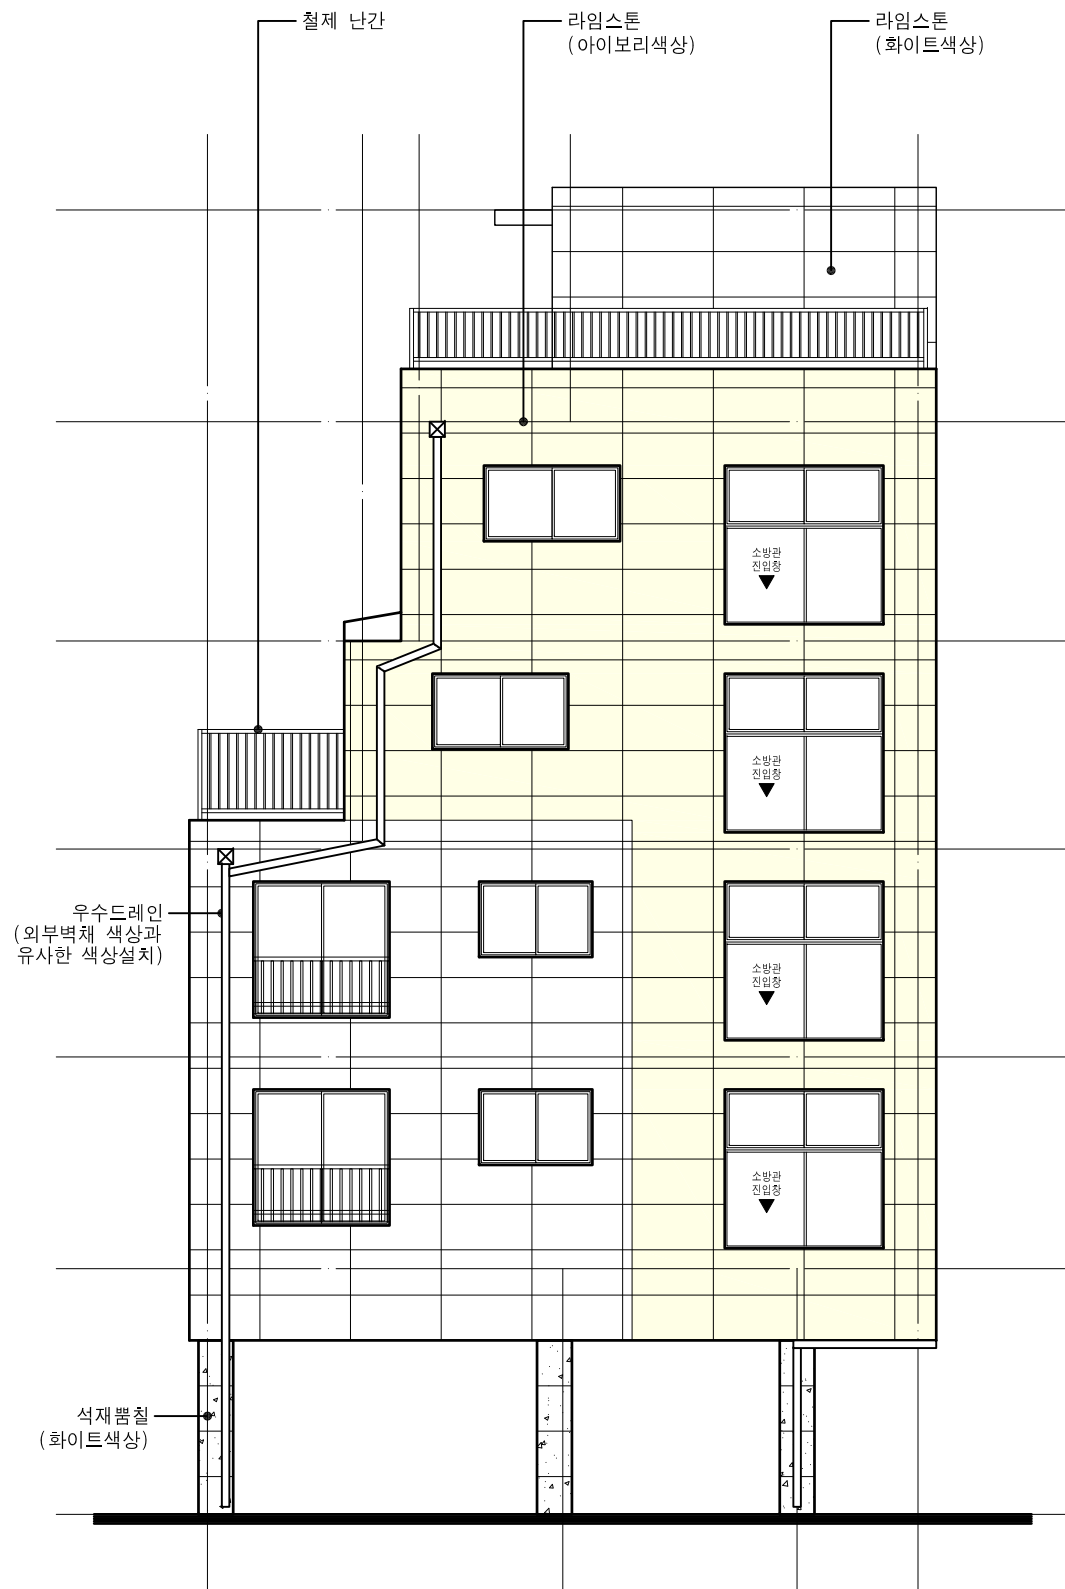

▽ 지붕 바닥

▽ 5층 바닥


▽ 4층 바닥

▽ 3층 바닥

▽ 2층 바닥

▽ 1층 바닥

정 면 도
SCALE : A3 : 1/100

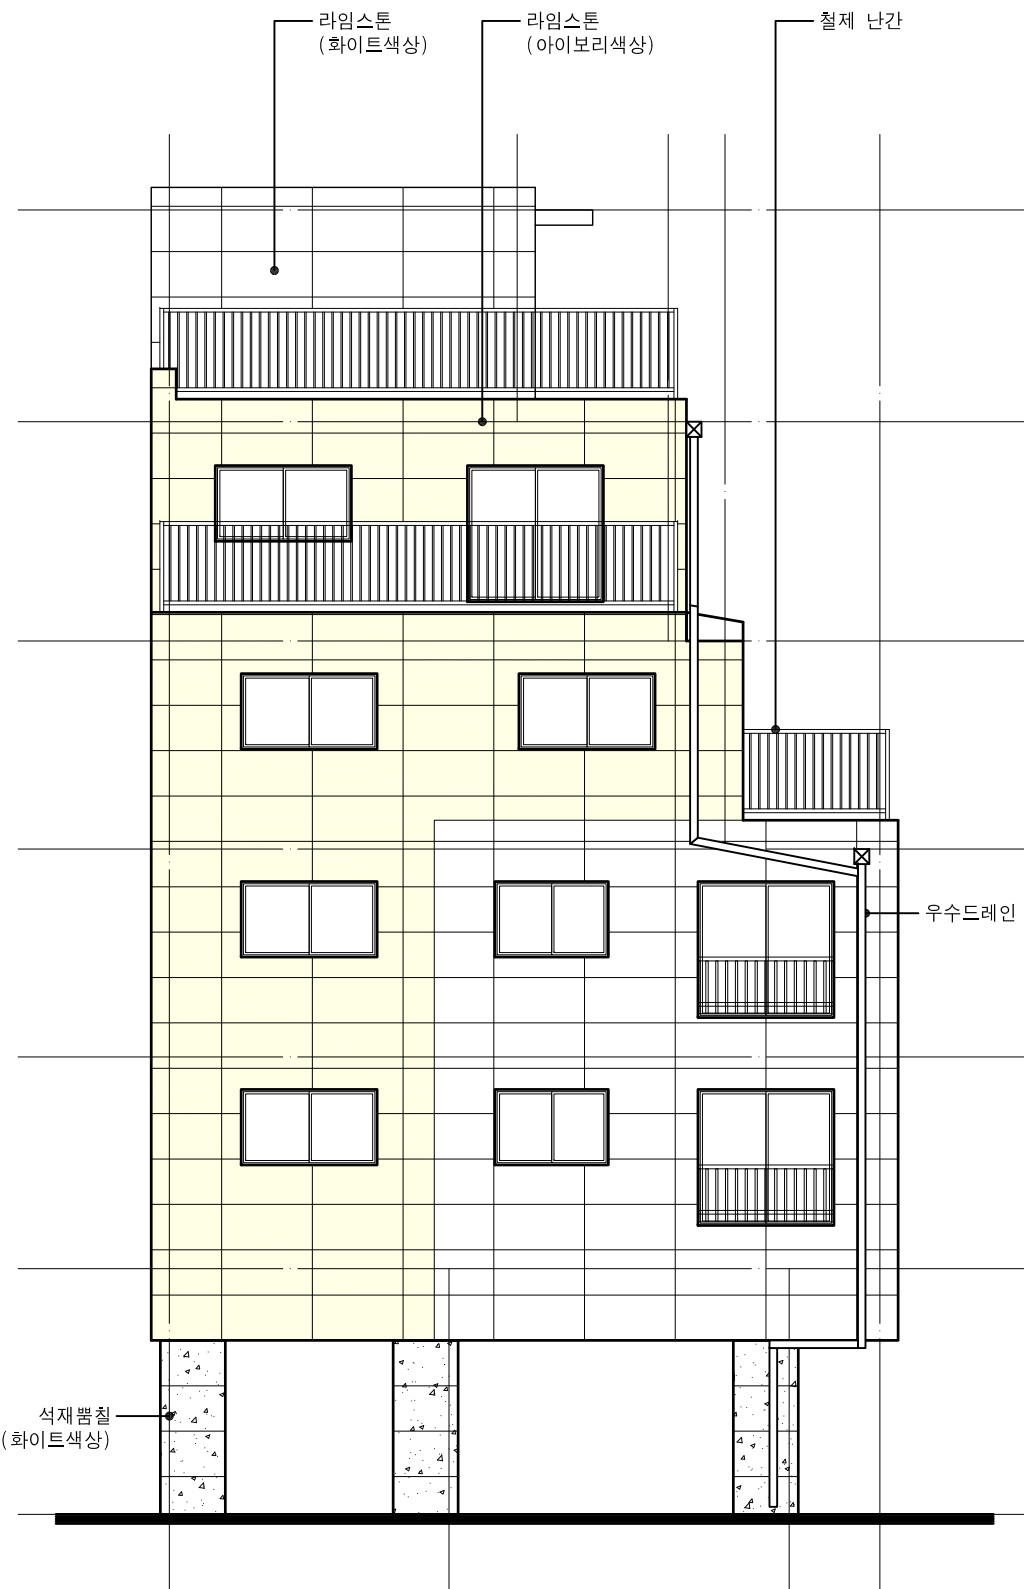

배 면 도
SCALE : A3 : 1/100

PROJECT TITLE
사업명칭

신림동 510-20호
도시형생활주택(소형주택)
신축공사

NAME OF DRAWING
도면명

입면도-1

NOTE
주 기

▼ ▼

창호 PVC 블랙
소방관진입창 - 스티커부착

NO. ▲ REVISIONS ▲ DATE
번호 수정 일자

DESIGNED BY
설 계

CHECKED BY
심 사

APPROVED BY
승 인

CONSULTANTS
협동설계


SCALE
축척 1/100

DATE
일 자 2023. 09.

DWG NO.
도면번호 A-31

SHEET NO.
일련번호 □-□□□

 **다움건축**
daum
건축사무소 다움건축
THE ARCHITECTS DESIGN GROUP
TEL. 02.414.6061 (代)
FAX. 02.414.6062

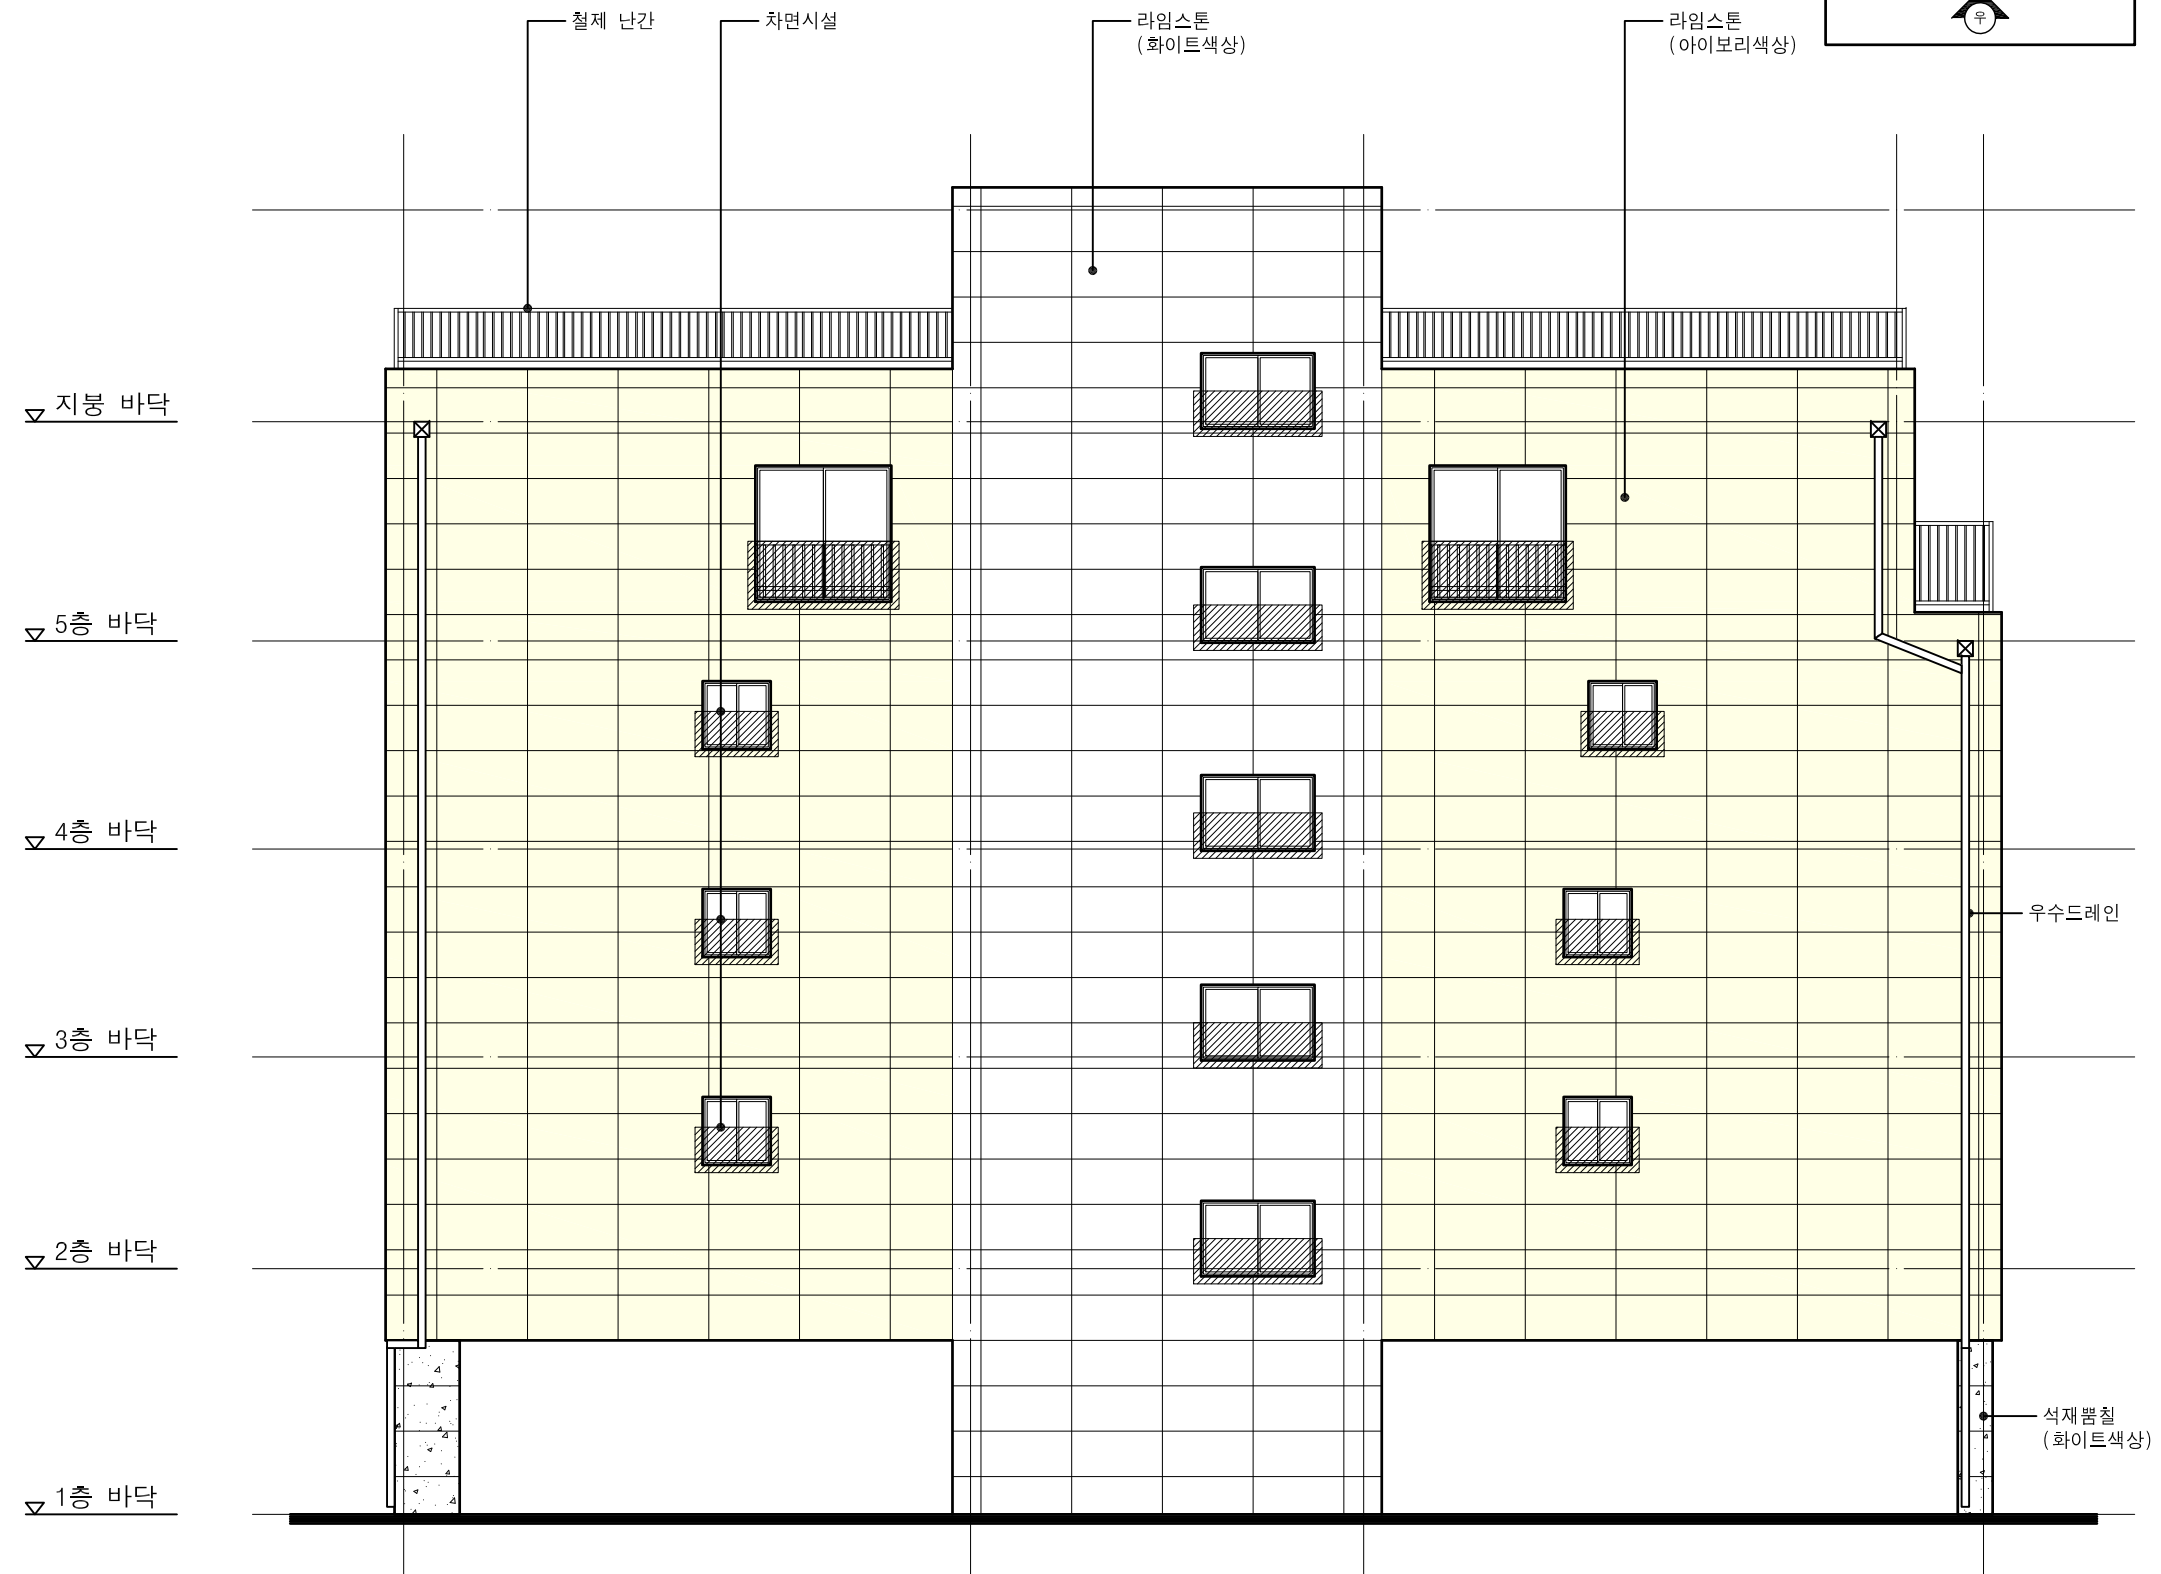

우 측 면 도
SCALE : A3 : 1/100

PROJECT TITLE
사업명칭

신림동 510-20호
도시형생활주택(소형주택)
신축공사

NAME OF DRAWING
도면명

입면도-2

NOTE
주 기

창호 PVC 블랙

NO. ▲ REVISIONS ▲ DATE
번호 수정 일자

DESIGNED BY
설 계

CHECKED BY
심 사

APPROVED BY
승 인

CONSULTANTS
협 동 설 계

SCALE
축척 1/100

DATE
일 자 2023. 09.


DWG NO.
도면 번호 A-32

SHEET NO.
일련 번호 □-□□□

 **다룸**
dawroom

건축사사무소 다룸건축

THE ARCHITECTS DESIGN GROUP
TEL. 02.414.6061 (代)
FAX. 02.414.6062

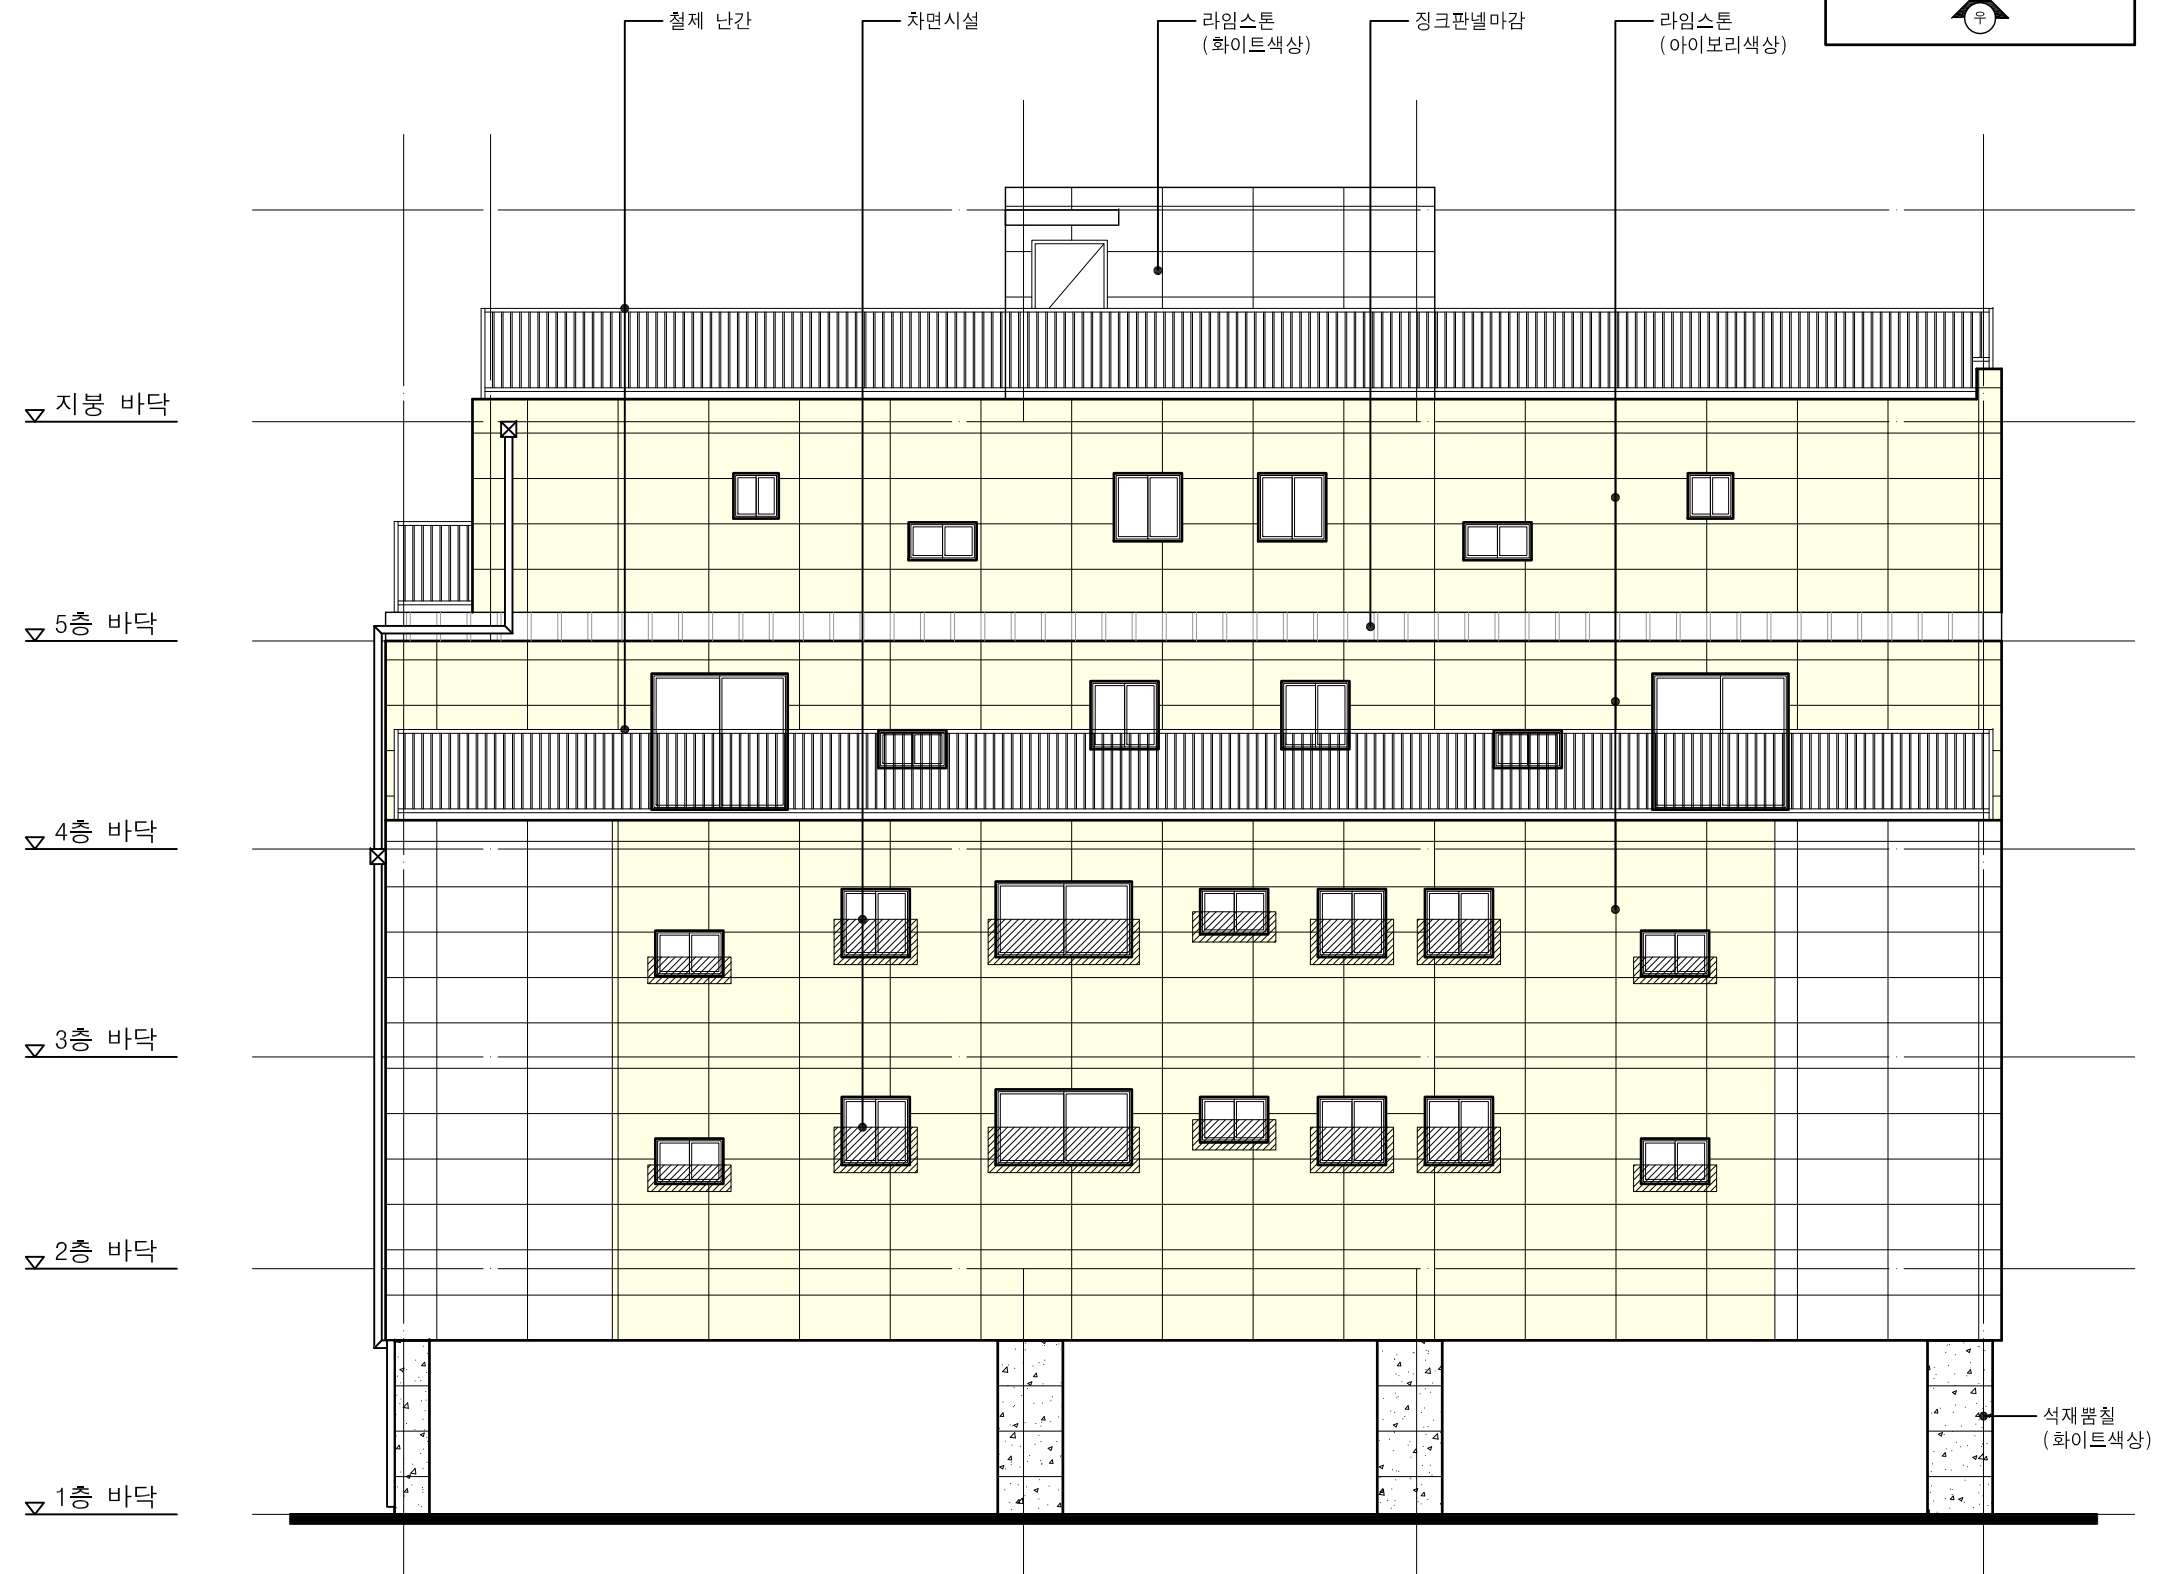

좌측면도
SCALE : A3 : 1/100

PROJECT TITLE
사업명칭

신림동 510-20호
도시형생활주택(소형주택)
신축공사

NAME OF DRAWING
도면명

입면도-3

NOTE
주 기

창호 PVC 블랙

NO.
번호

REVISIONS
수정

DATE
일자

DESIGNED BY
설계

CHECKED BY
심사

APPROVED BY
승인

CONSULTANTS
협동설계

SCALE
축척

1/100

DATE
일자

2023. 09.

DWG NO.
도면번호

A-33

SHEET NO.
일련번호

□-□□□

 **다룸**
dawroom

건축사무소 다룸건축

THE ARCHITECTS DESIGN GROUP
TEL. 02.414.6061 (代)
FAX. 02.414.6062