

1. 조감도



2. 건축개요

■ 건축개요

- 설 계 명 : 신림동 509-1호 외 1필지 도시형생활주택(소형주택) 신축공사
- 대 지 위 치 : 서울특별시 관악구 신림동 509-1호 외 1필지
- 지 역·지 구 : 제2종 일반주거지역
- 건 물 용 도 : 공동주택-도시형생활주택(소형주택)-16세대
- 건 물 규 모 : 지상 5층
- 대 지 면 적 : 330.60 m²
- 건 축 면 적 : 192.84 m²
- 연 면 적 : 659.96 m²
- 건 폐 율 : 58.33 %
- 용 적 륜 : 199.62 %
- 최 고 높 이 : 15.85 m
- 건 물 구 조 : 철근콘크리트조
- 주 차 대 수 : 8대(법정), 8대(계획)
- 조 경 면 적 : 16.53m²(법정), 20.09m²(계획)

3. 입면도



정면도

우측면도

배면도

좌측면도

PROJECT TITLE
사업명
신림동 509-1호 외 1필지
도시형생활주택(소형주택) 신축공사
다세대주택 신축공사

NAME OF DRAWING
도면명

조감도, 건축개요, 입면도

NOTE
주 기

NO. ▲ REVISIONS ▲ DATE
번호 수정 일자

DESIGNED BY
설 계

CHECKED BY
심 사

APPROVED BY
승 인

CONSULTANTS
협 동 설 계

SCALE
축 척 1/

DATE
일 자 2023. 09.

DWG NO.
도면 번호 A-02


SHEET NO.
일련 번호 □-□□□

DAWOOM
dawoom
건축사무소 다움건축
THE ARCHITECTS DESIGN GROUP
TEL. 02.414.6061 (☎)
FAX. 02.414.6062

4. 설계자 의도

■ 디자인 의도

- 보행자, 차량 출입의 원활한 계획
- 도로측에 순응한 주동 배치
- 정면성을 강조하는 디자인 계획

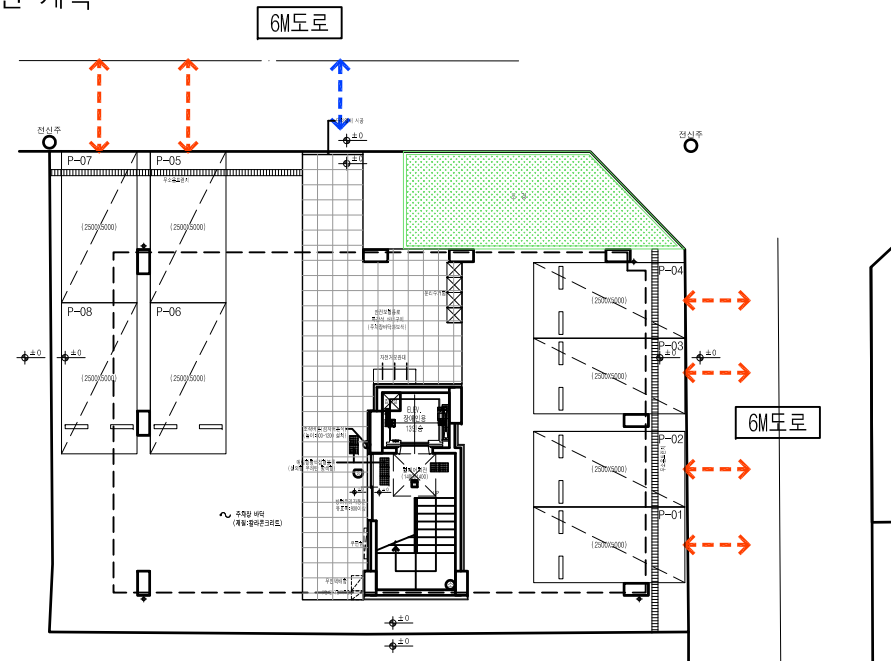


■ 입면 디자인 계획

- 창호크기 및 열을 맞추어 입면에 정돈된 이미지를 부여함.

밝은 색 돌마감으로 단정한 입면 계획.

조화로운 포인트색 돌마감으로 면분할하여 단조롭고 심심한 입면 탈피.

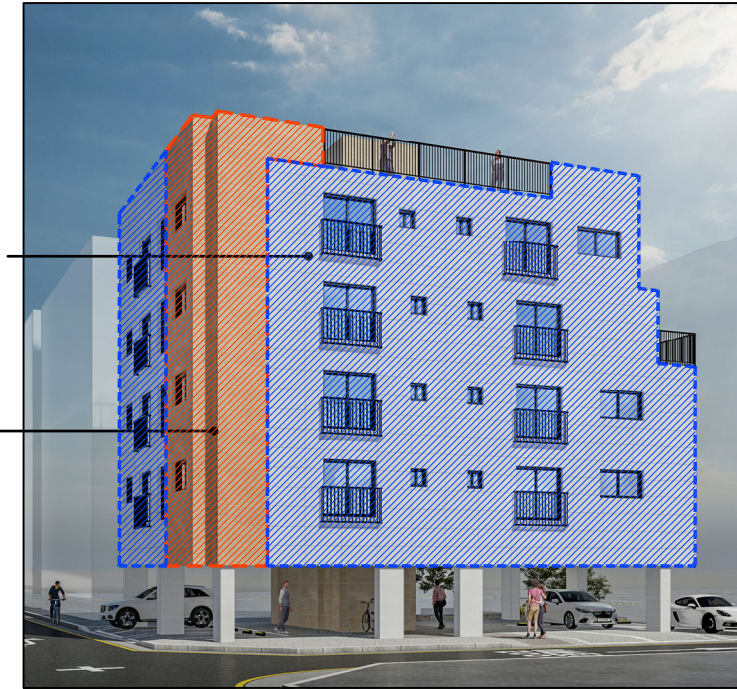

5. 재료계획

1. 외벽 마감재



2. 주차장 바닥재



3. 옥외 난간대



■ 외장재

구분	실명	재료명
1층	필로티 주차장	바닥 : 칼라무늬콘크리트 천정 : 내풍압형 AL 천정재
2~5층	현관	바닥 : 폴리싱타일
	방	바닥 : 데코타일 마감 천정 : 실크 또는 발포벽지
	거실	바닥 : 데코타일 마감 천정 : 실크 또는 발포벽지
	베란다	바닥 : 칼라 콘크리트 천정 : AL 천정판

■ 내장재

6. 색채계획

- 자연스러운 색상과 주변과의 조화
- 주변과 어울리는 색상을 활용한 입면 계획
- 가로경관 미관성 및 친근성



아이보리 계열:라임스톤

화이트 계열:라임스톤

PROJECT TITLE
사업명
신림동 509-1호 외 1필지
도시형생활주택(소형주택) 신축공사
다세대주택 신축공사

NAME OF DRAWING
도면명

디자인 의도

NOTE
주 기

NO. ▲ REVISIONS ▲ DATE
번호 수정 일자

DESIGNED BY
설 계

CHECKED BY
심 사

APPROVED BY
승 인

CONSULTANTS
협 동 설 계


SCALE
축척 1/

DATE
일 자 2023. 09.

DWG NO.
도면 번호 A-03

SHEET NO.
일련 번호 □-□□□

DAWOOM
dawoom
건축사사무소 다움건축
THE ARCHITECTS DESIGN GROUP
TEL. 02.414.6061 (代)
FAX. 02.414.6062

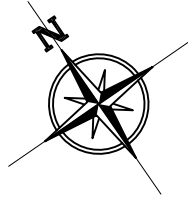

PROJECT TITLE
사업명
신림동 509-1호 외 1필지
도시형생활주택(소형주택) 신축공사
다세대주택 신축공사

NAME OF DRAWING
도면명
1층 평면도

NOTE
주 기

- 단독경보감지기(연기식)
- 단독경보감지기(열감지)
- ABC분말소화기(2.5KG)
- 가스누설경보기
- 일산화탄소경보기
- 차면시설
- 보일러
- 에어컨 실외기

NO. ▲ REVISIONS ▲ DATE
번호 수정 일자

DESIGNED BY
설 계

CHECKED BY
심 사

APPROVED BY
승 인

CONSULTANTS
협 동 설 계


SCALE
축척 1/ 100

DATE
일 자 2023. 09.




DWG NO.
도면 번호 A- 21

SHEET NO.
일련 번호 □-□□□

DAWOOM
건축사무소 다움건축
THE ARCHITECTS DESIGN GROUP
TEL. 02.414.6061 (代)
FAX. 02.414.6062

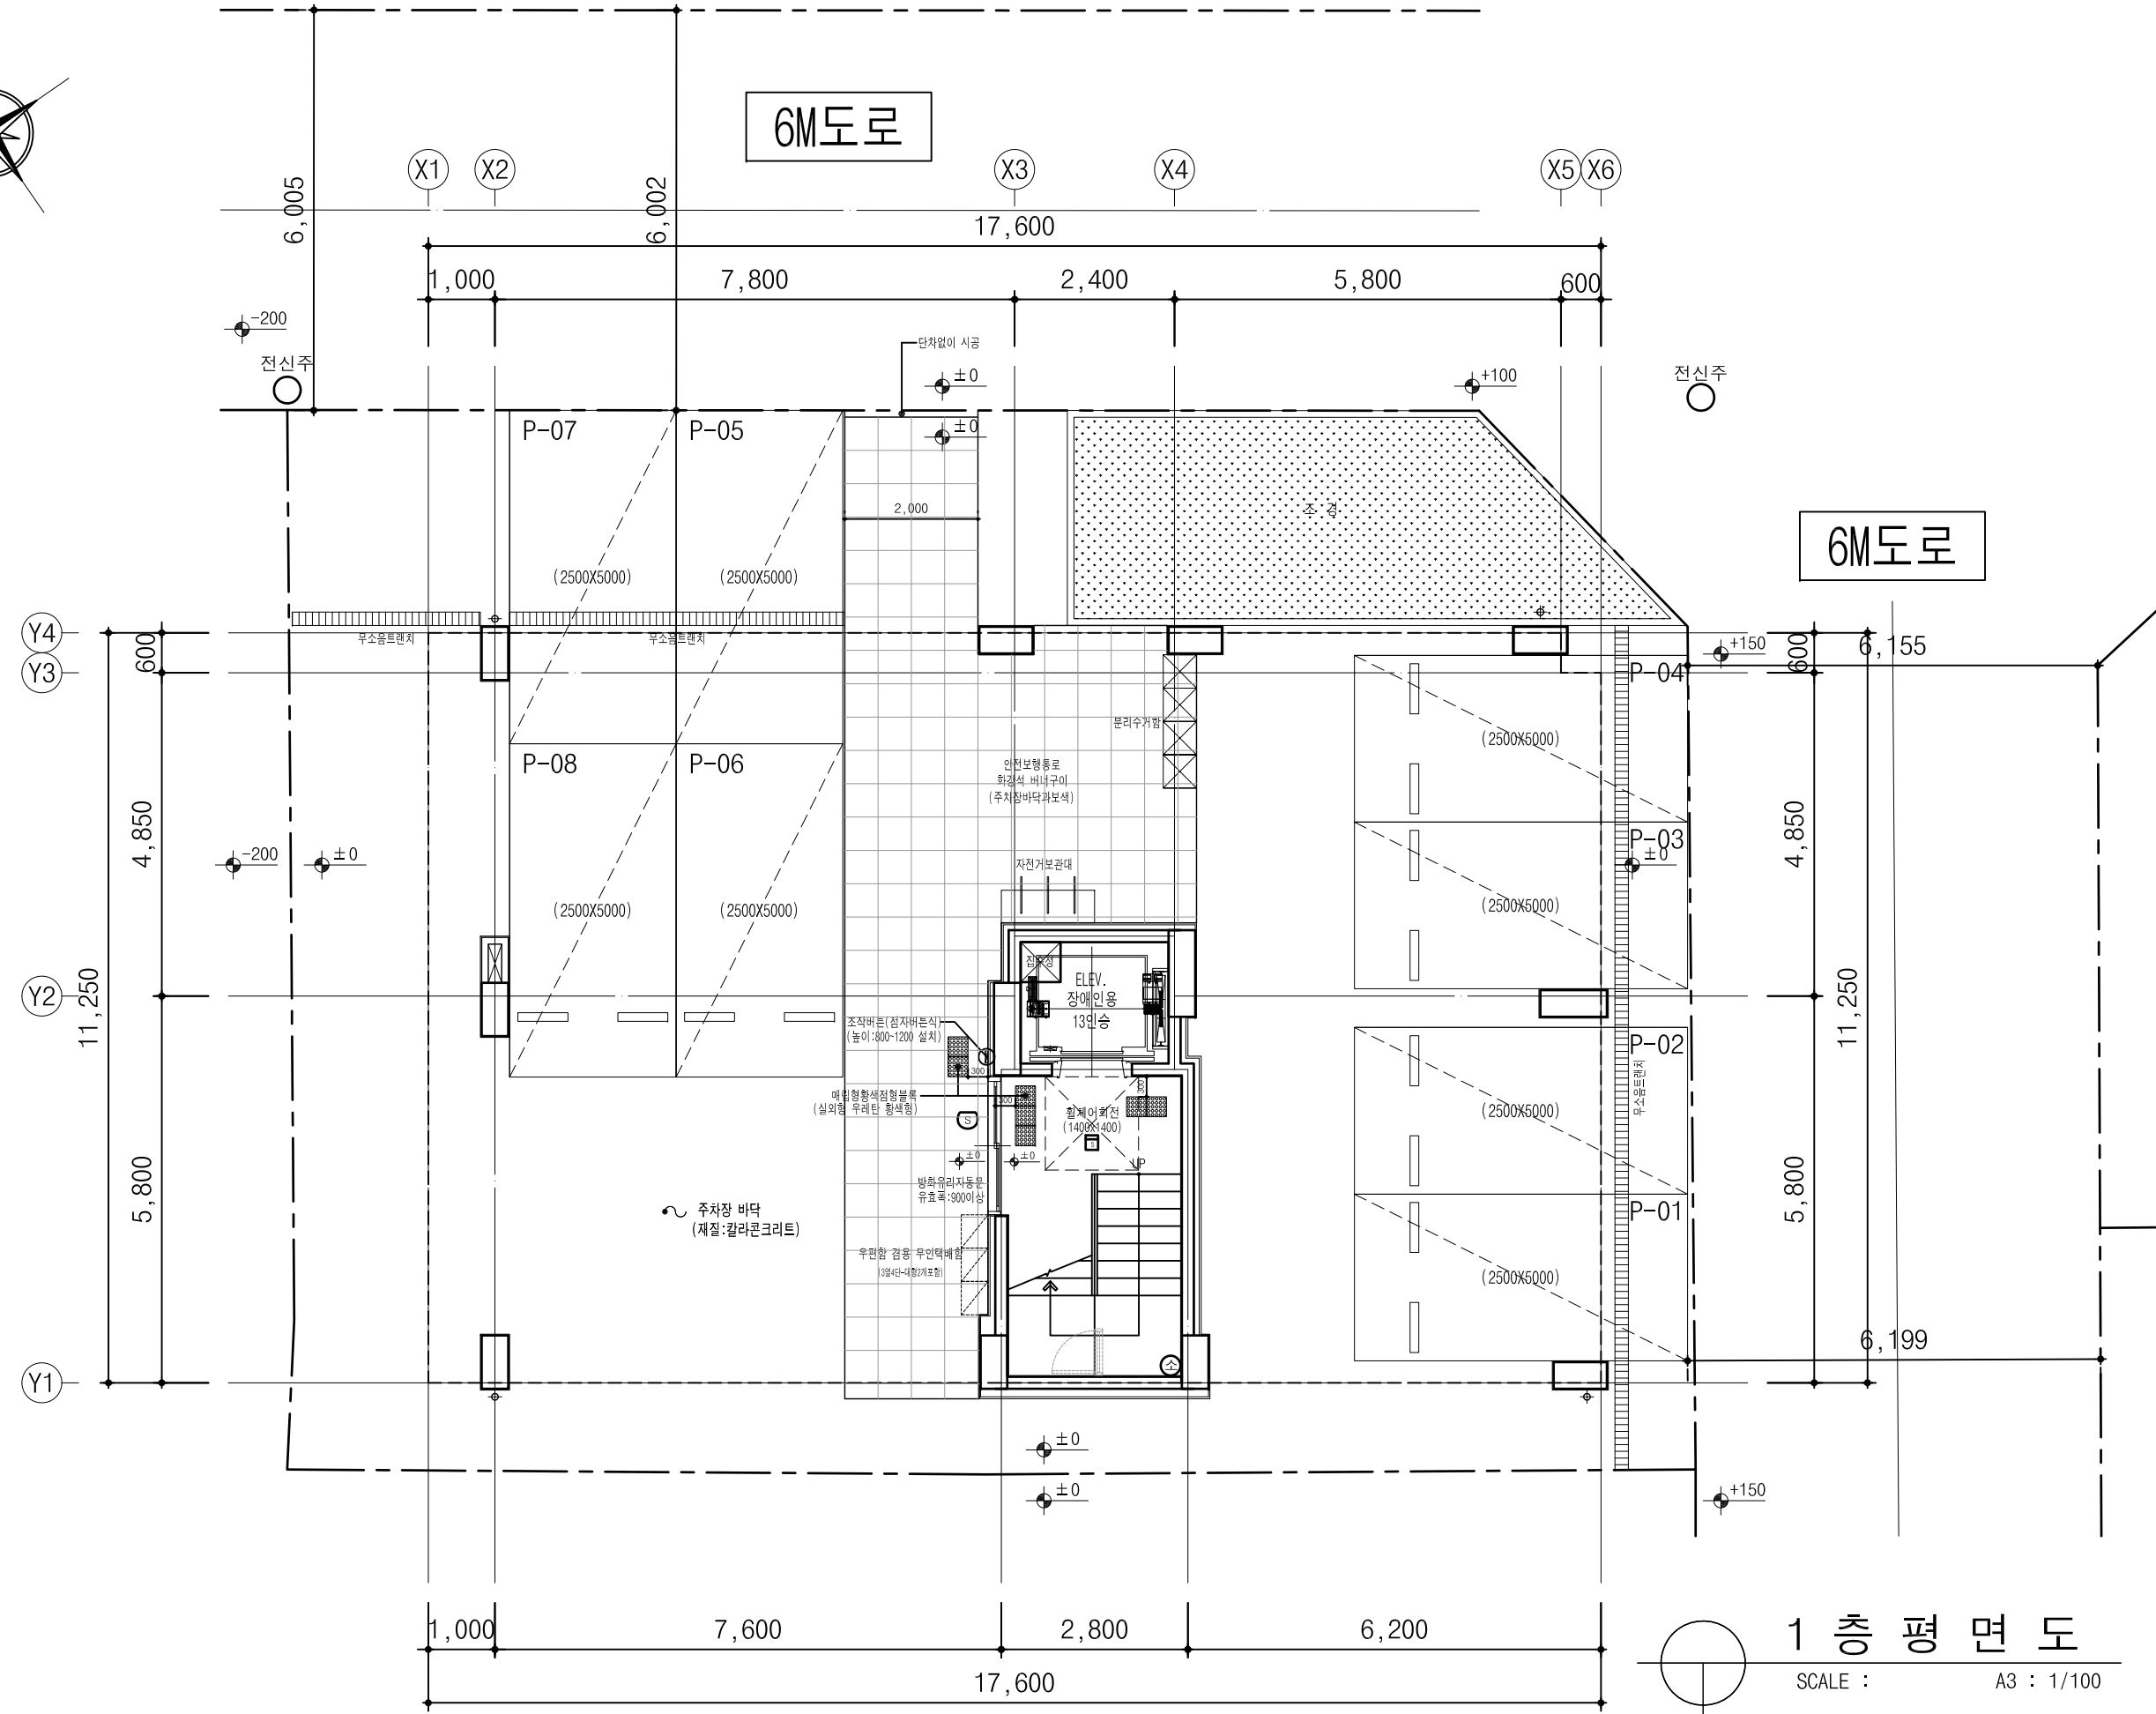

1층 평면도
SCALE : A3 : 1/100

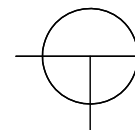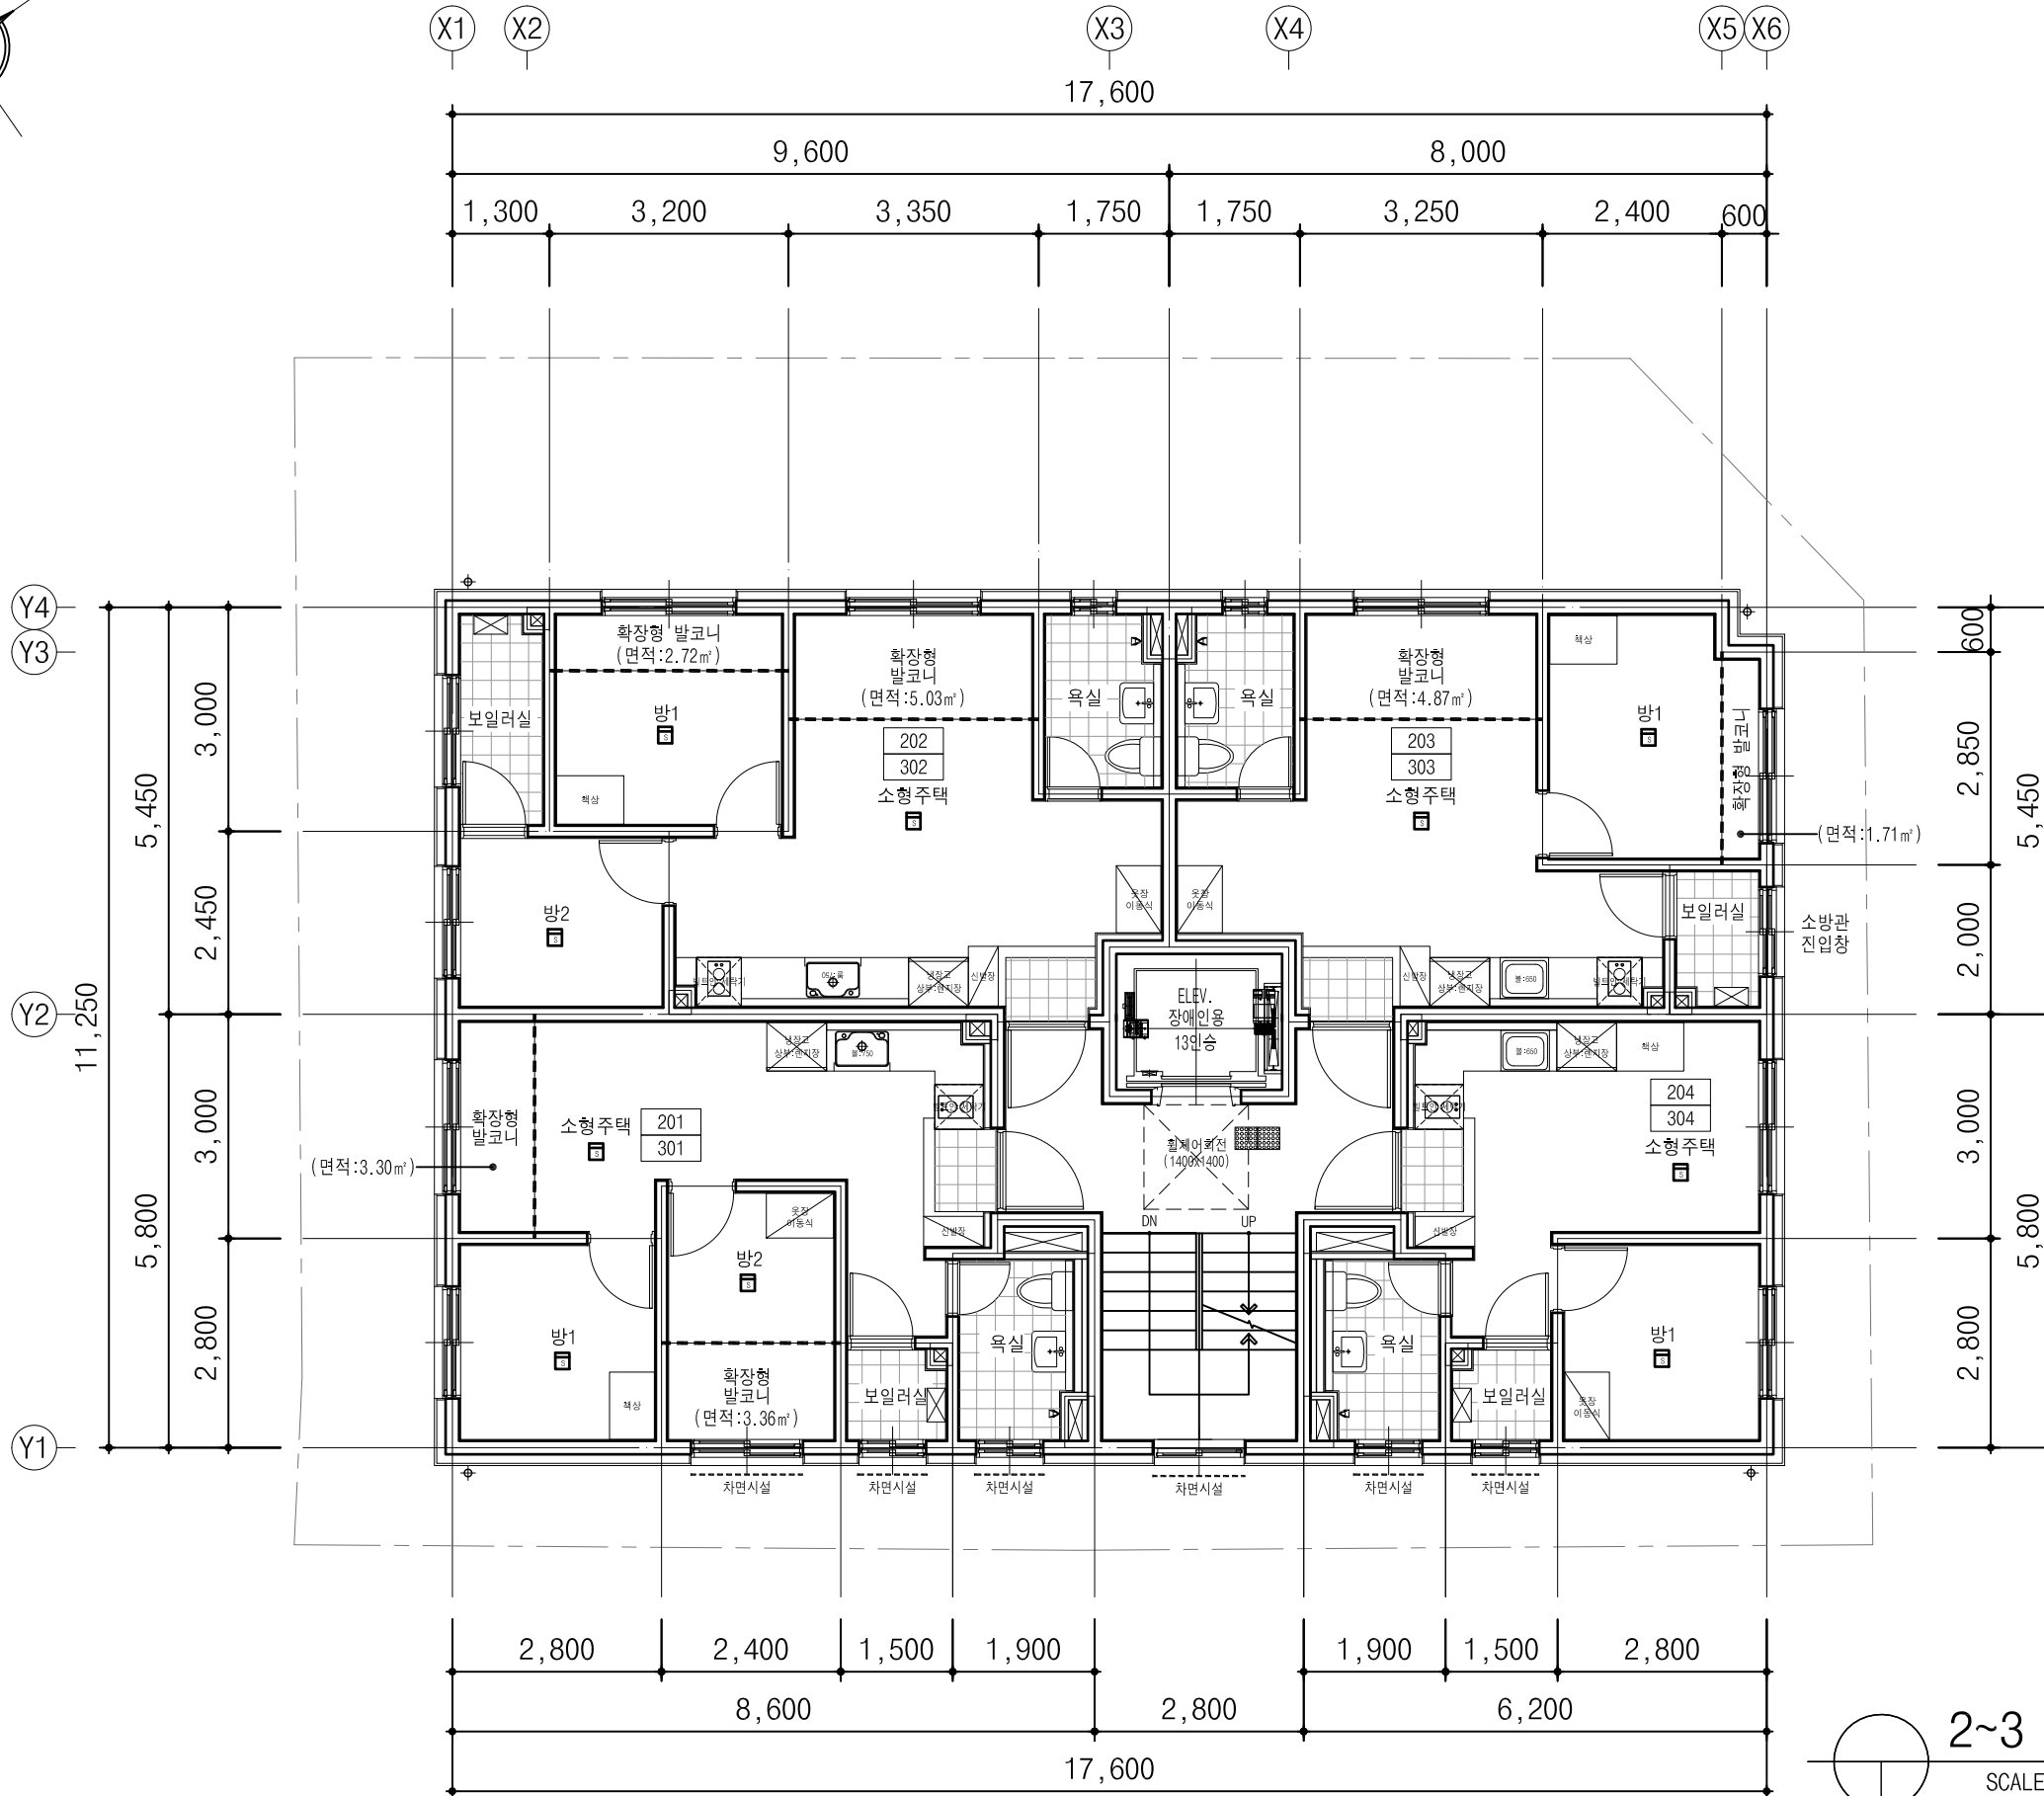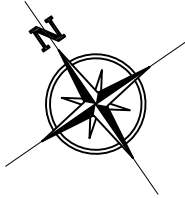

2~3 층 평면도
SCALE : A3 : 1/100

PROJECT TITLE
사업명

신림동 509-1호 외 1필지
도시형생활주택(소형주택) 신축공사
다세대주택 신축공사

NAME OF DRAWING
도면명

2~3 층 평면도

NOTE
주 기

- 단독경보감지기(연기식)
- 단독경보감지기(열감지)
- ABC분말소화기(2.5KG)
- 가스누설경보기
- 일산화탄소경보기
- 차면시설
- 보일러
- 에어컨 실외기

NO. ▲ REVISIONS ▲ DATE
번호 수정 일자

DESIGNED BY
설 계

CHECKED BY
심 사

APPROVED BY
승 인

CONSULTANTS
협 동 설 계




SCALE
축척 1/ 100

DATE
일 자 2023. 09.

DWG NO.
도면 번호 A- 22

SHEET NO.
일련 번호 □-□□□

 DAWOOM
건축사무소 다음건축
THE ARCHITECTS DESIGN GROUP
TEL. 02.414.6061 (代)
FAX. 02.414.6062

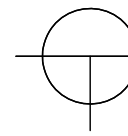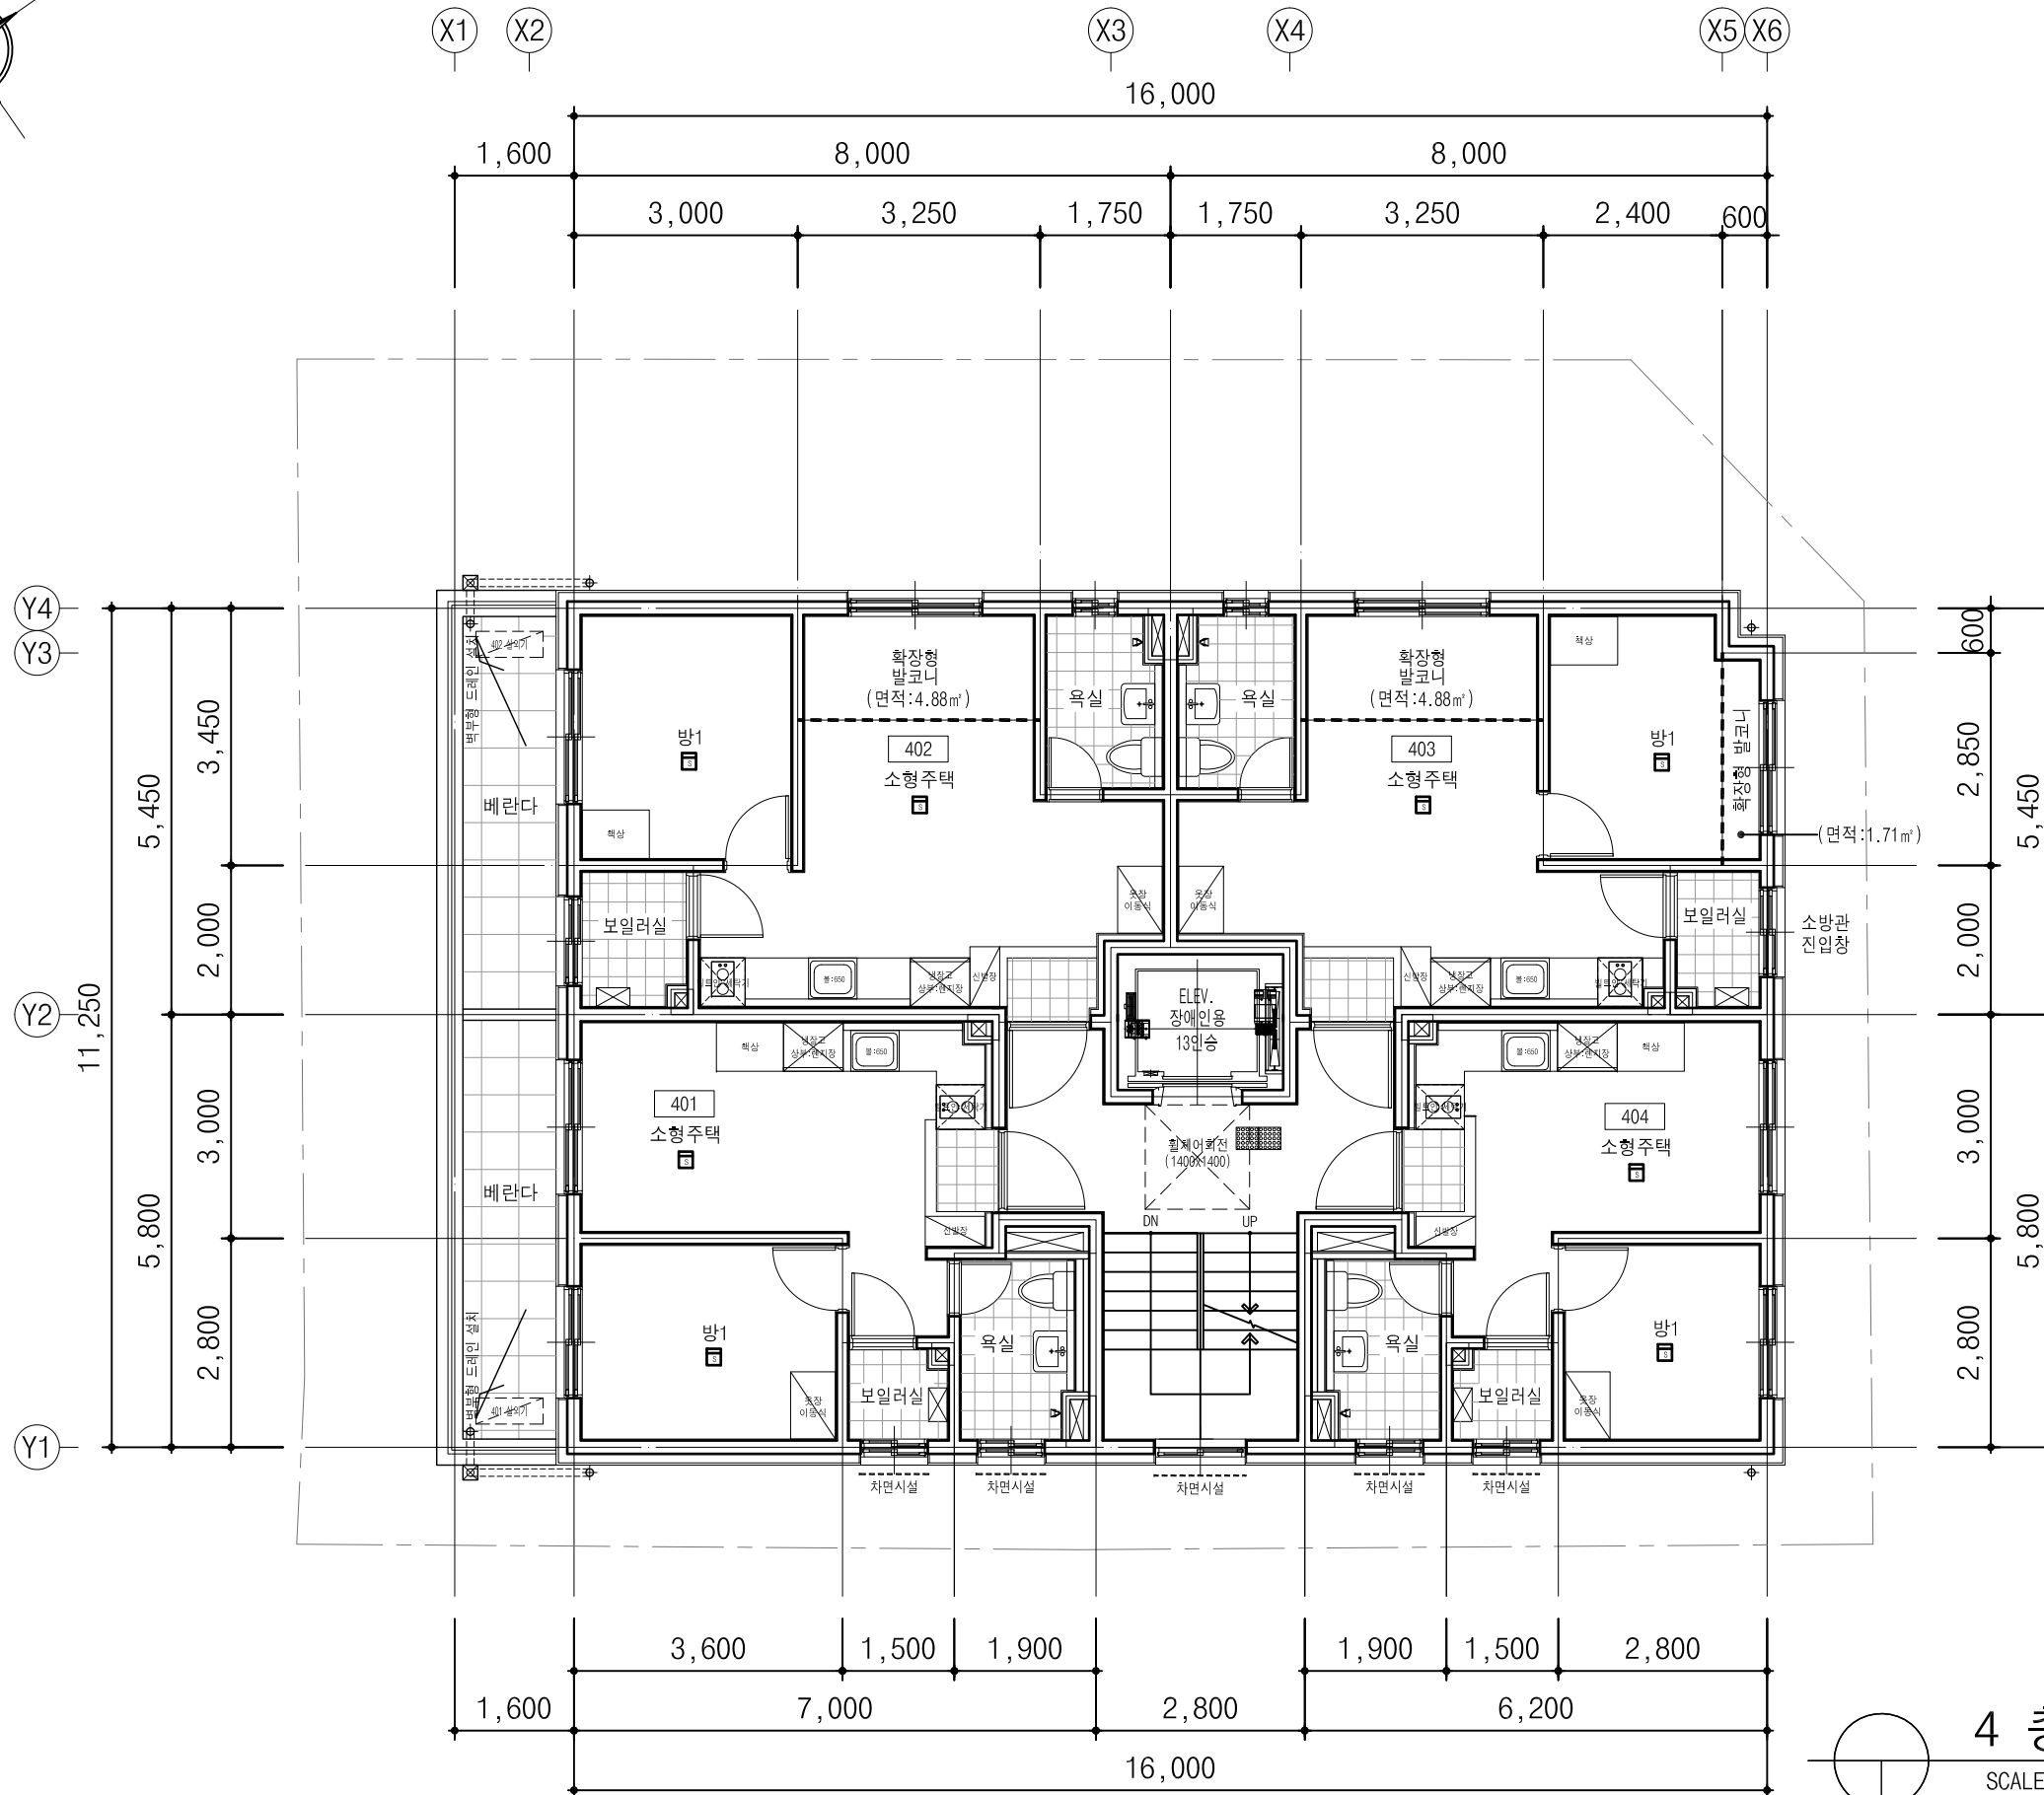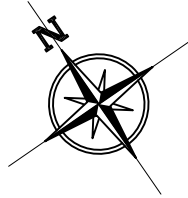

4 층 평 면 도
SCALE : A3 : 1/100

PROJECT TITLE
사업명
신림동 509-1호 외 1필지
도시형생활주택(소형주택) 신축공사
다세대주택 신축공사

NAME OF DRAWING
도면명
4 층 평 면 도

- NOTE
주 기
- 단독경보감지기(연기식)
 - 단독경보감지기(열감지)
 - ABC분말소화기(2.5KG)
 - 가스누설경보기
 - 일산화탄소경보기
 - 차면시설
 - 보일러
 - 에어컨 실외기

NO. ▲ REVISIONS ▲ DATE
번호 수정 일자

DESIGNED BY
설 계

CHECKED BY
심 사

APPROVED BY
승 인

CONSULTANTS
협 동 설 계



SCALE
축 적 1 / 100

DATE
일 자 2023. 09.

DWG NO.
도면 번호 A- 23

SHEET NO.
일련 번호 □-□□□

DAWOOM
dawoom
건축사사무소 다웬건축
THE ARCHITECTS DESIGN GROUP
TEL. 02.414.6061 (代)
FAX. 02.414.6062

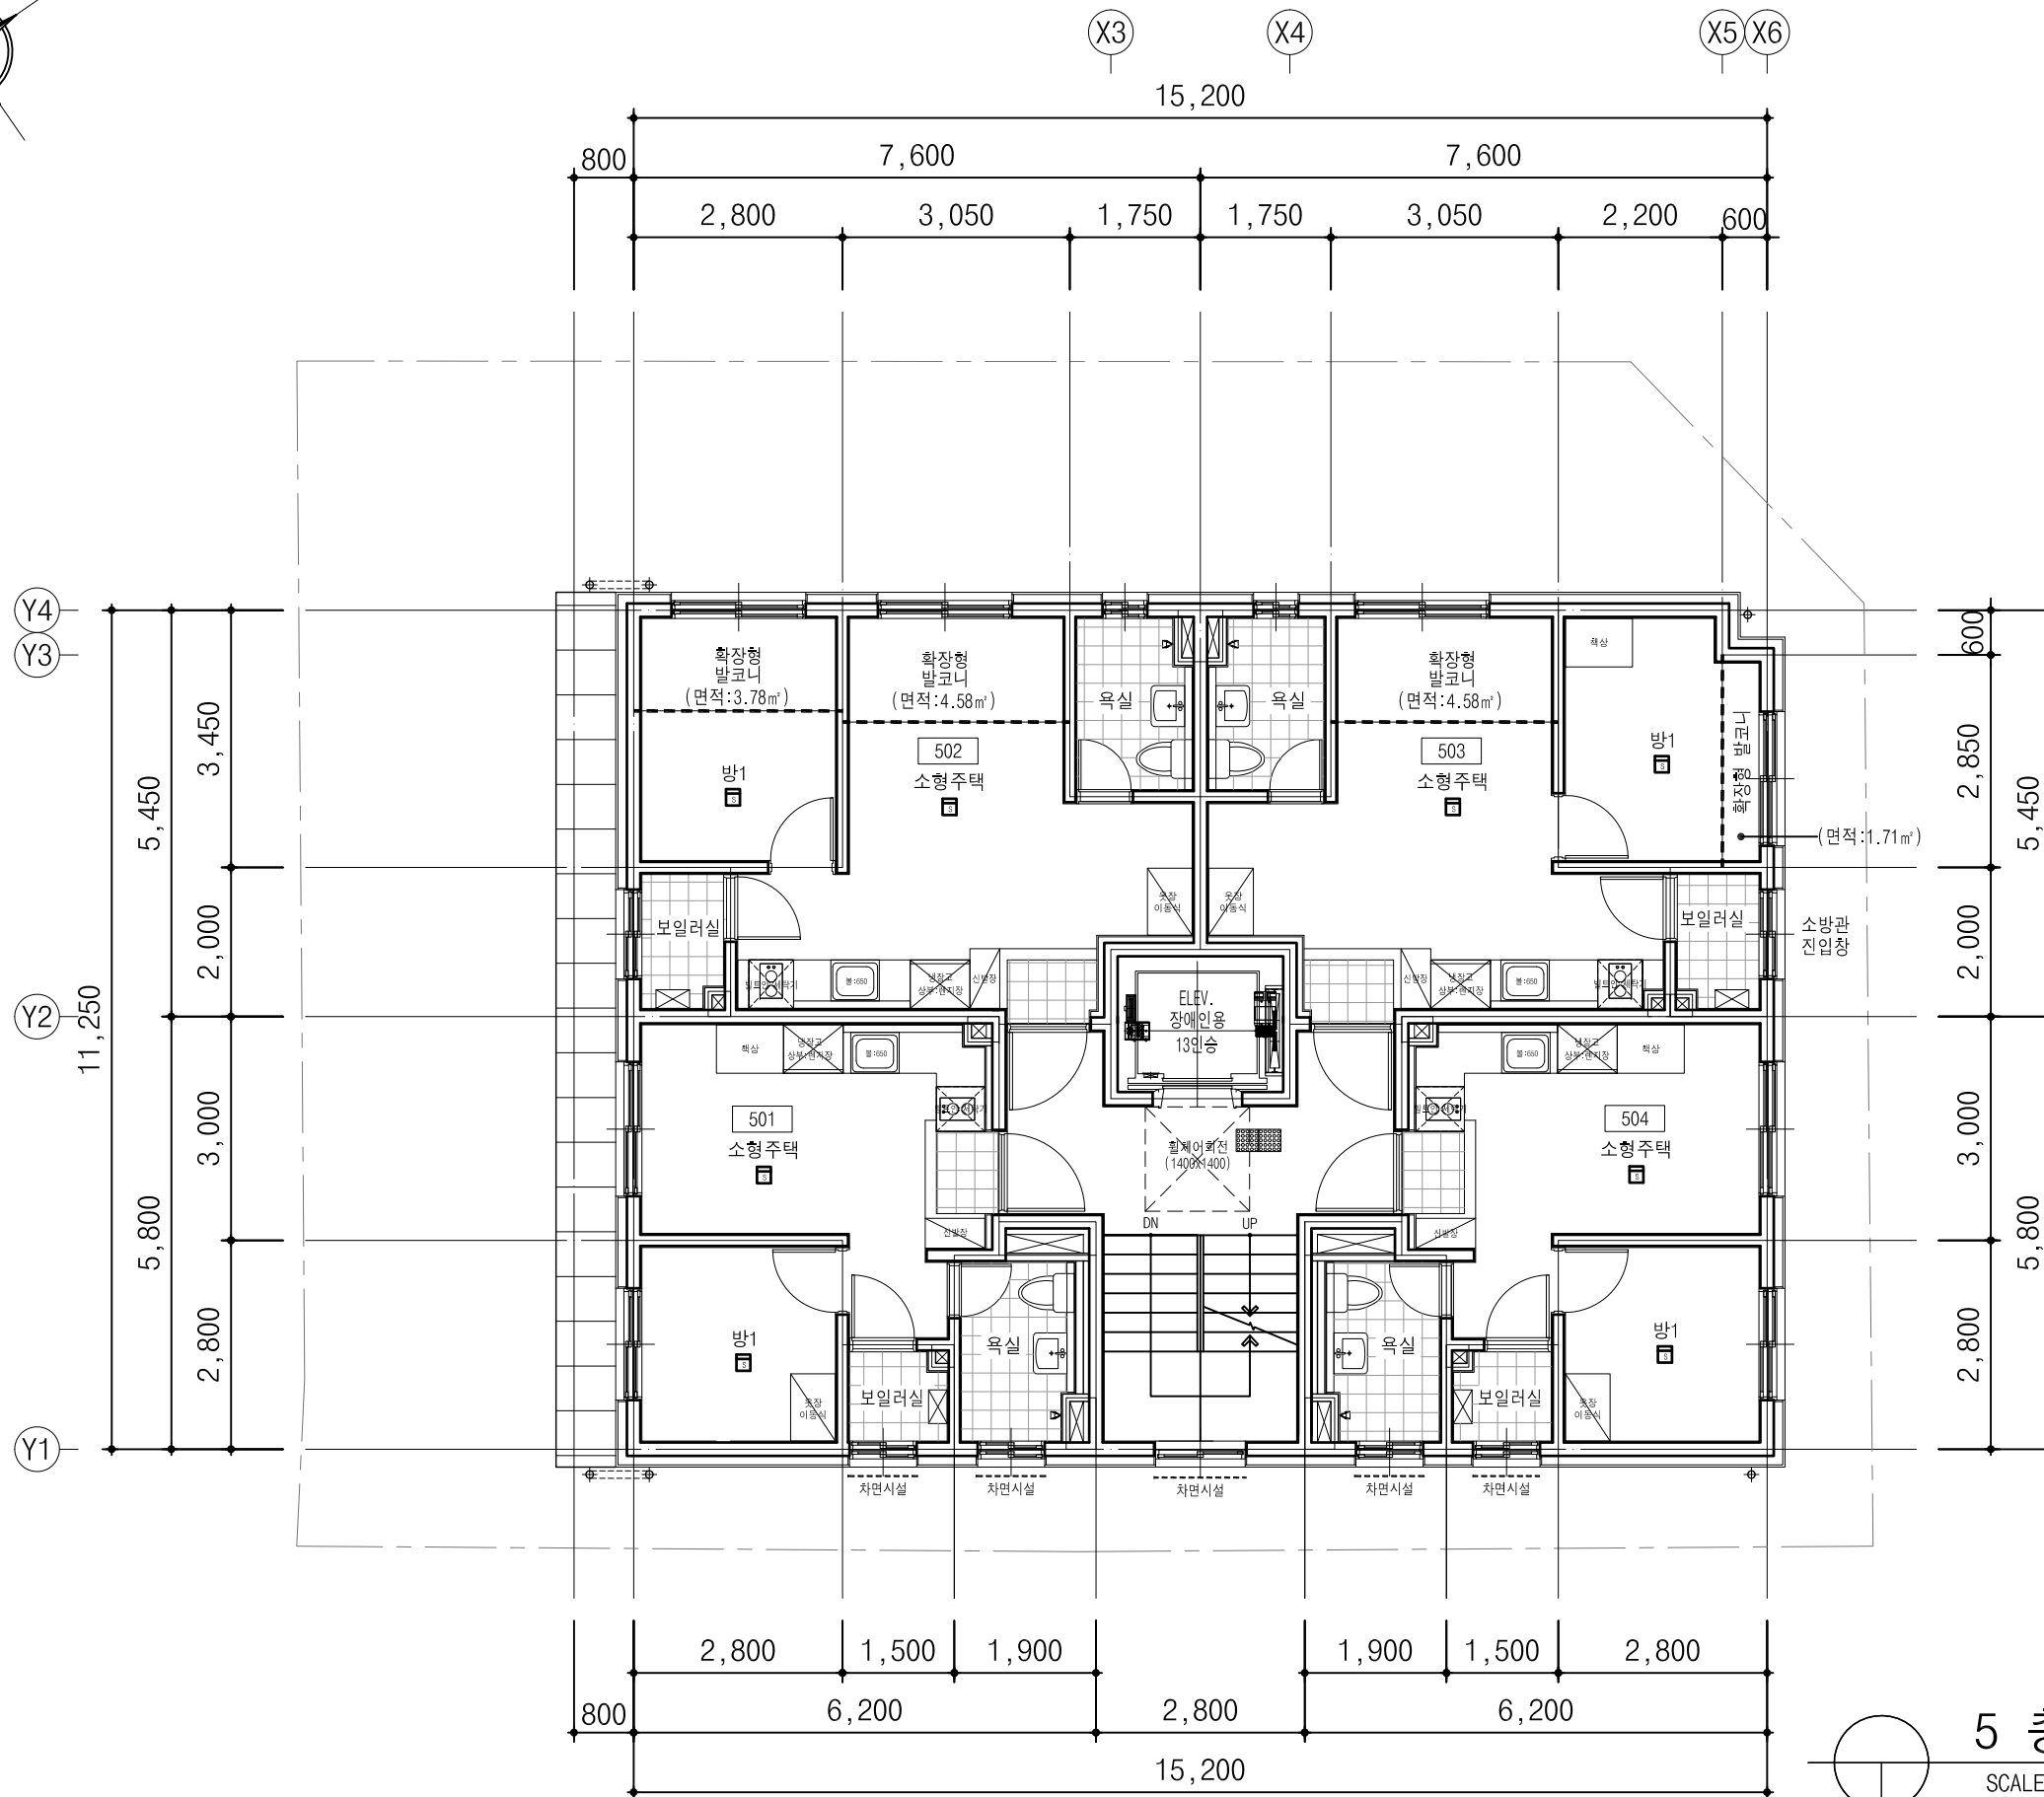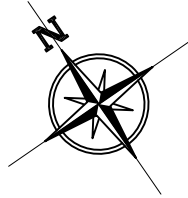

5층 평면도
SCALE : A3 : 1/100

PROJECT TITLE
사업명
신림동 509-1호 외 1필지
도시형생활주택(소형주택) 신축공사
다세대주택 신축공사

NAME OF DRAWING
도면명
5층 평면도

- NOTE
주 기
- 단독경보감지기(연기식)
 - 단독경보감지기(열감지)
 - ABC분말소화기(2.5KG)
 - 가스누설경보기
 - 일산화탄소경보기
 - 차면시설
 - 보일러
 - 에어컨 실외기

NO. ▲ REVISIONS ▲ DATE
번호 수정 일자

DESIGNED BY
설 계

CHECKED BY
심 사

APPROVED BY
승 인

CONSULTANTS
협 동 설 계




SCALE
축척 1/ 100

DATE
일 자 2023. 09.

DWG NO.
도면 번호 A- 24

SHEET NO.
일련 번호 □-□□□

 DAWOOM
dawoom
건축사사무소 다움건축
THE ARCHITECTS DESIGN GROUP
TEL. 02.414.6061 (代)
FAX. 02.414.6062

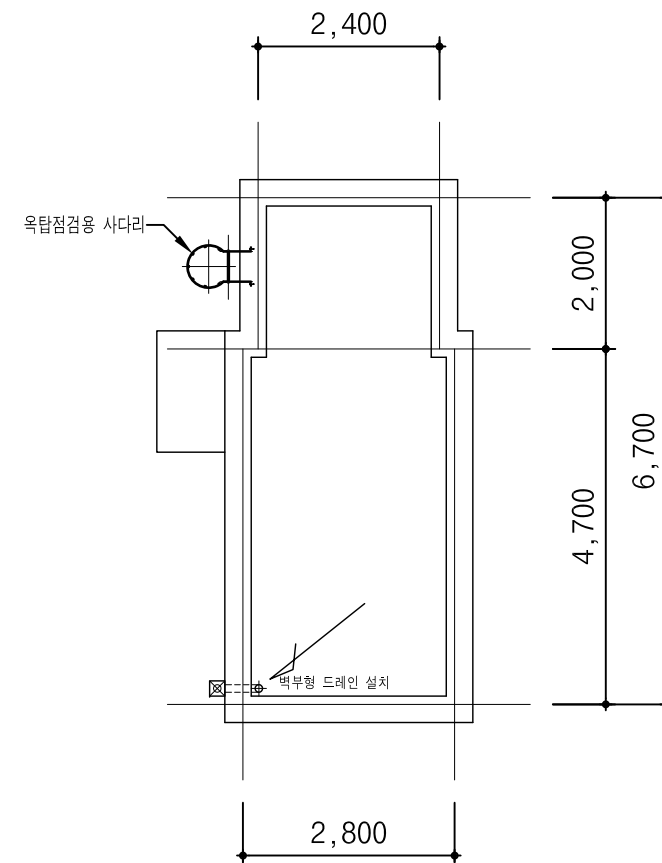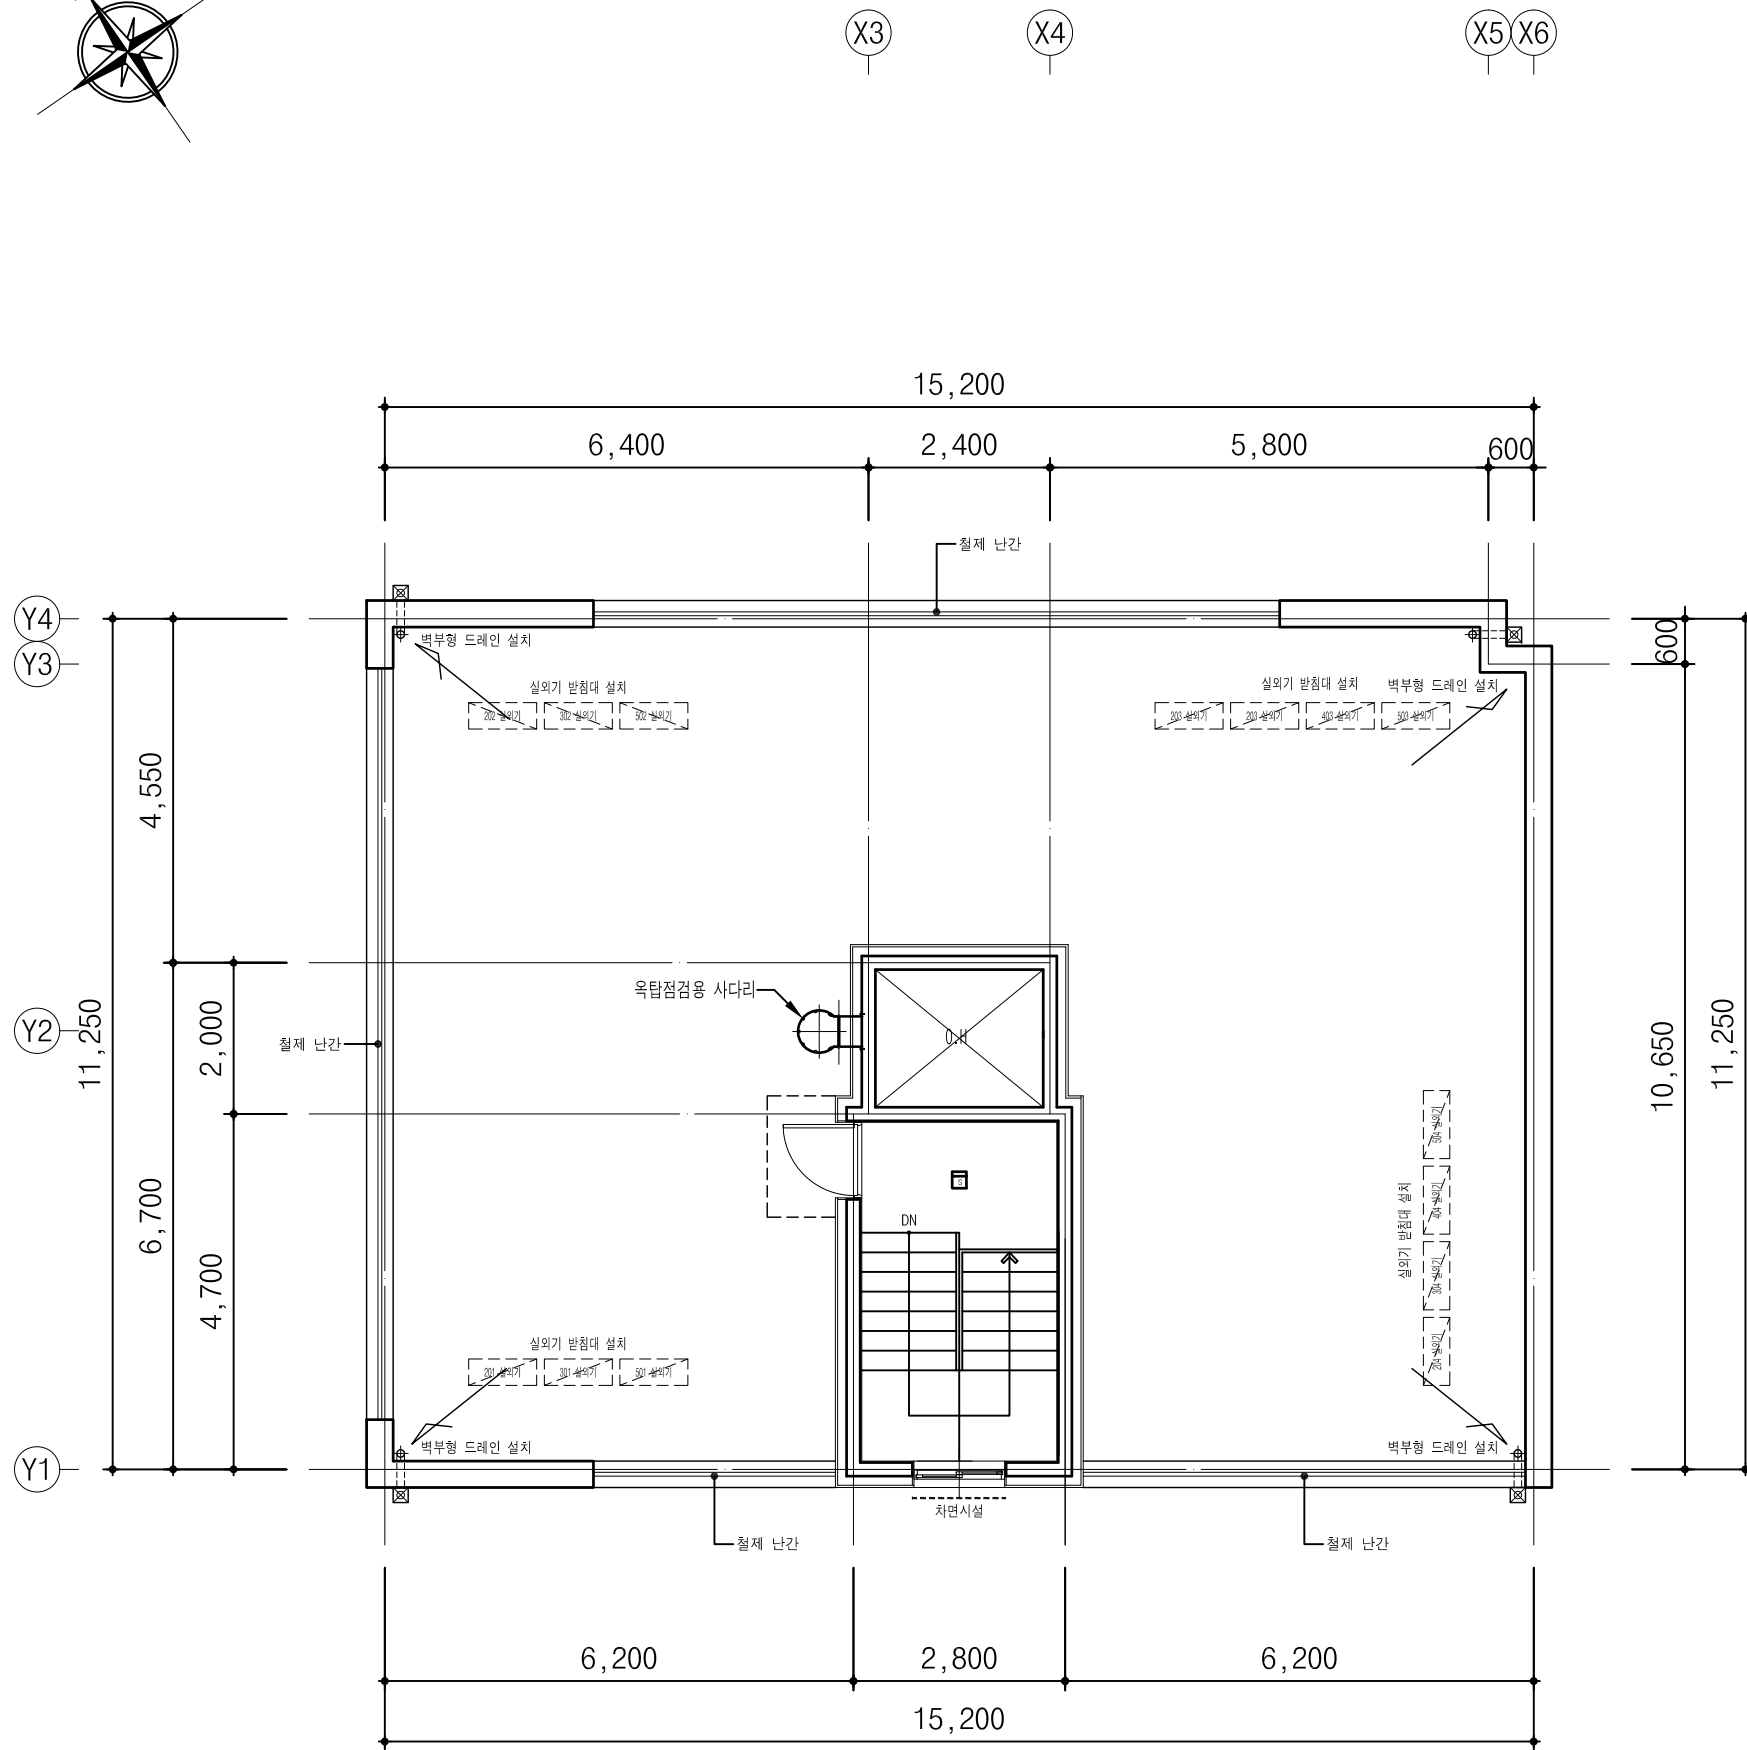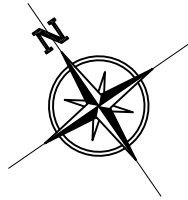

지붕및옥탑평면도
SCALE : A3 : 1/100

PROJECT TITLE
사업명
신림동 509-1호 외 1필지
도시형생활주택(소형주택) 신축공사
다세대주택 신축공사

NAME OF DRAWING
도면명
지붕및옥탑평면도

NOTE
주 기
▼ ▼

NO. ▲ REVISIONS ▲ DATE
번호 수정 일자

DESIGNED BY
설 계

CHECKED BY
심 사

APPROVED BY
승 인

CONSULTANTS
협 동 설 계


SCALE
축 적 1 / 100

DATE
일 자 2023. 09.

DWG NO.
도면 번호 A- 25

SHEET NO.
일련 번호 □ - □ □ □

DAWOOM
dawoom
건축사무소 다움건축
THE ARCHITECTS DESIGN GROUP
TEL. 02.414.6061 (代)
FAX. 02.414.6062

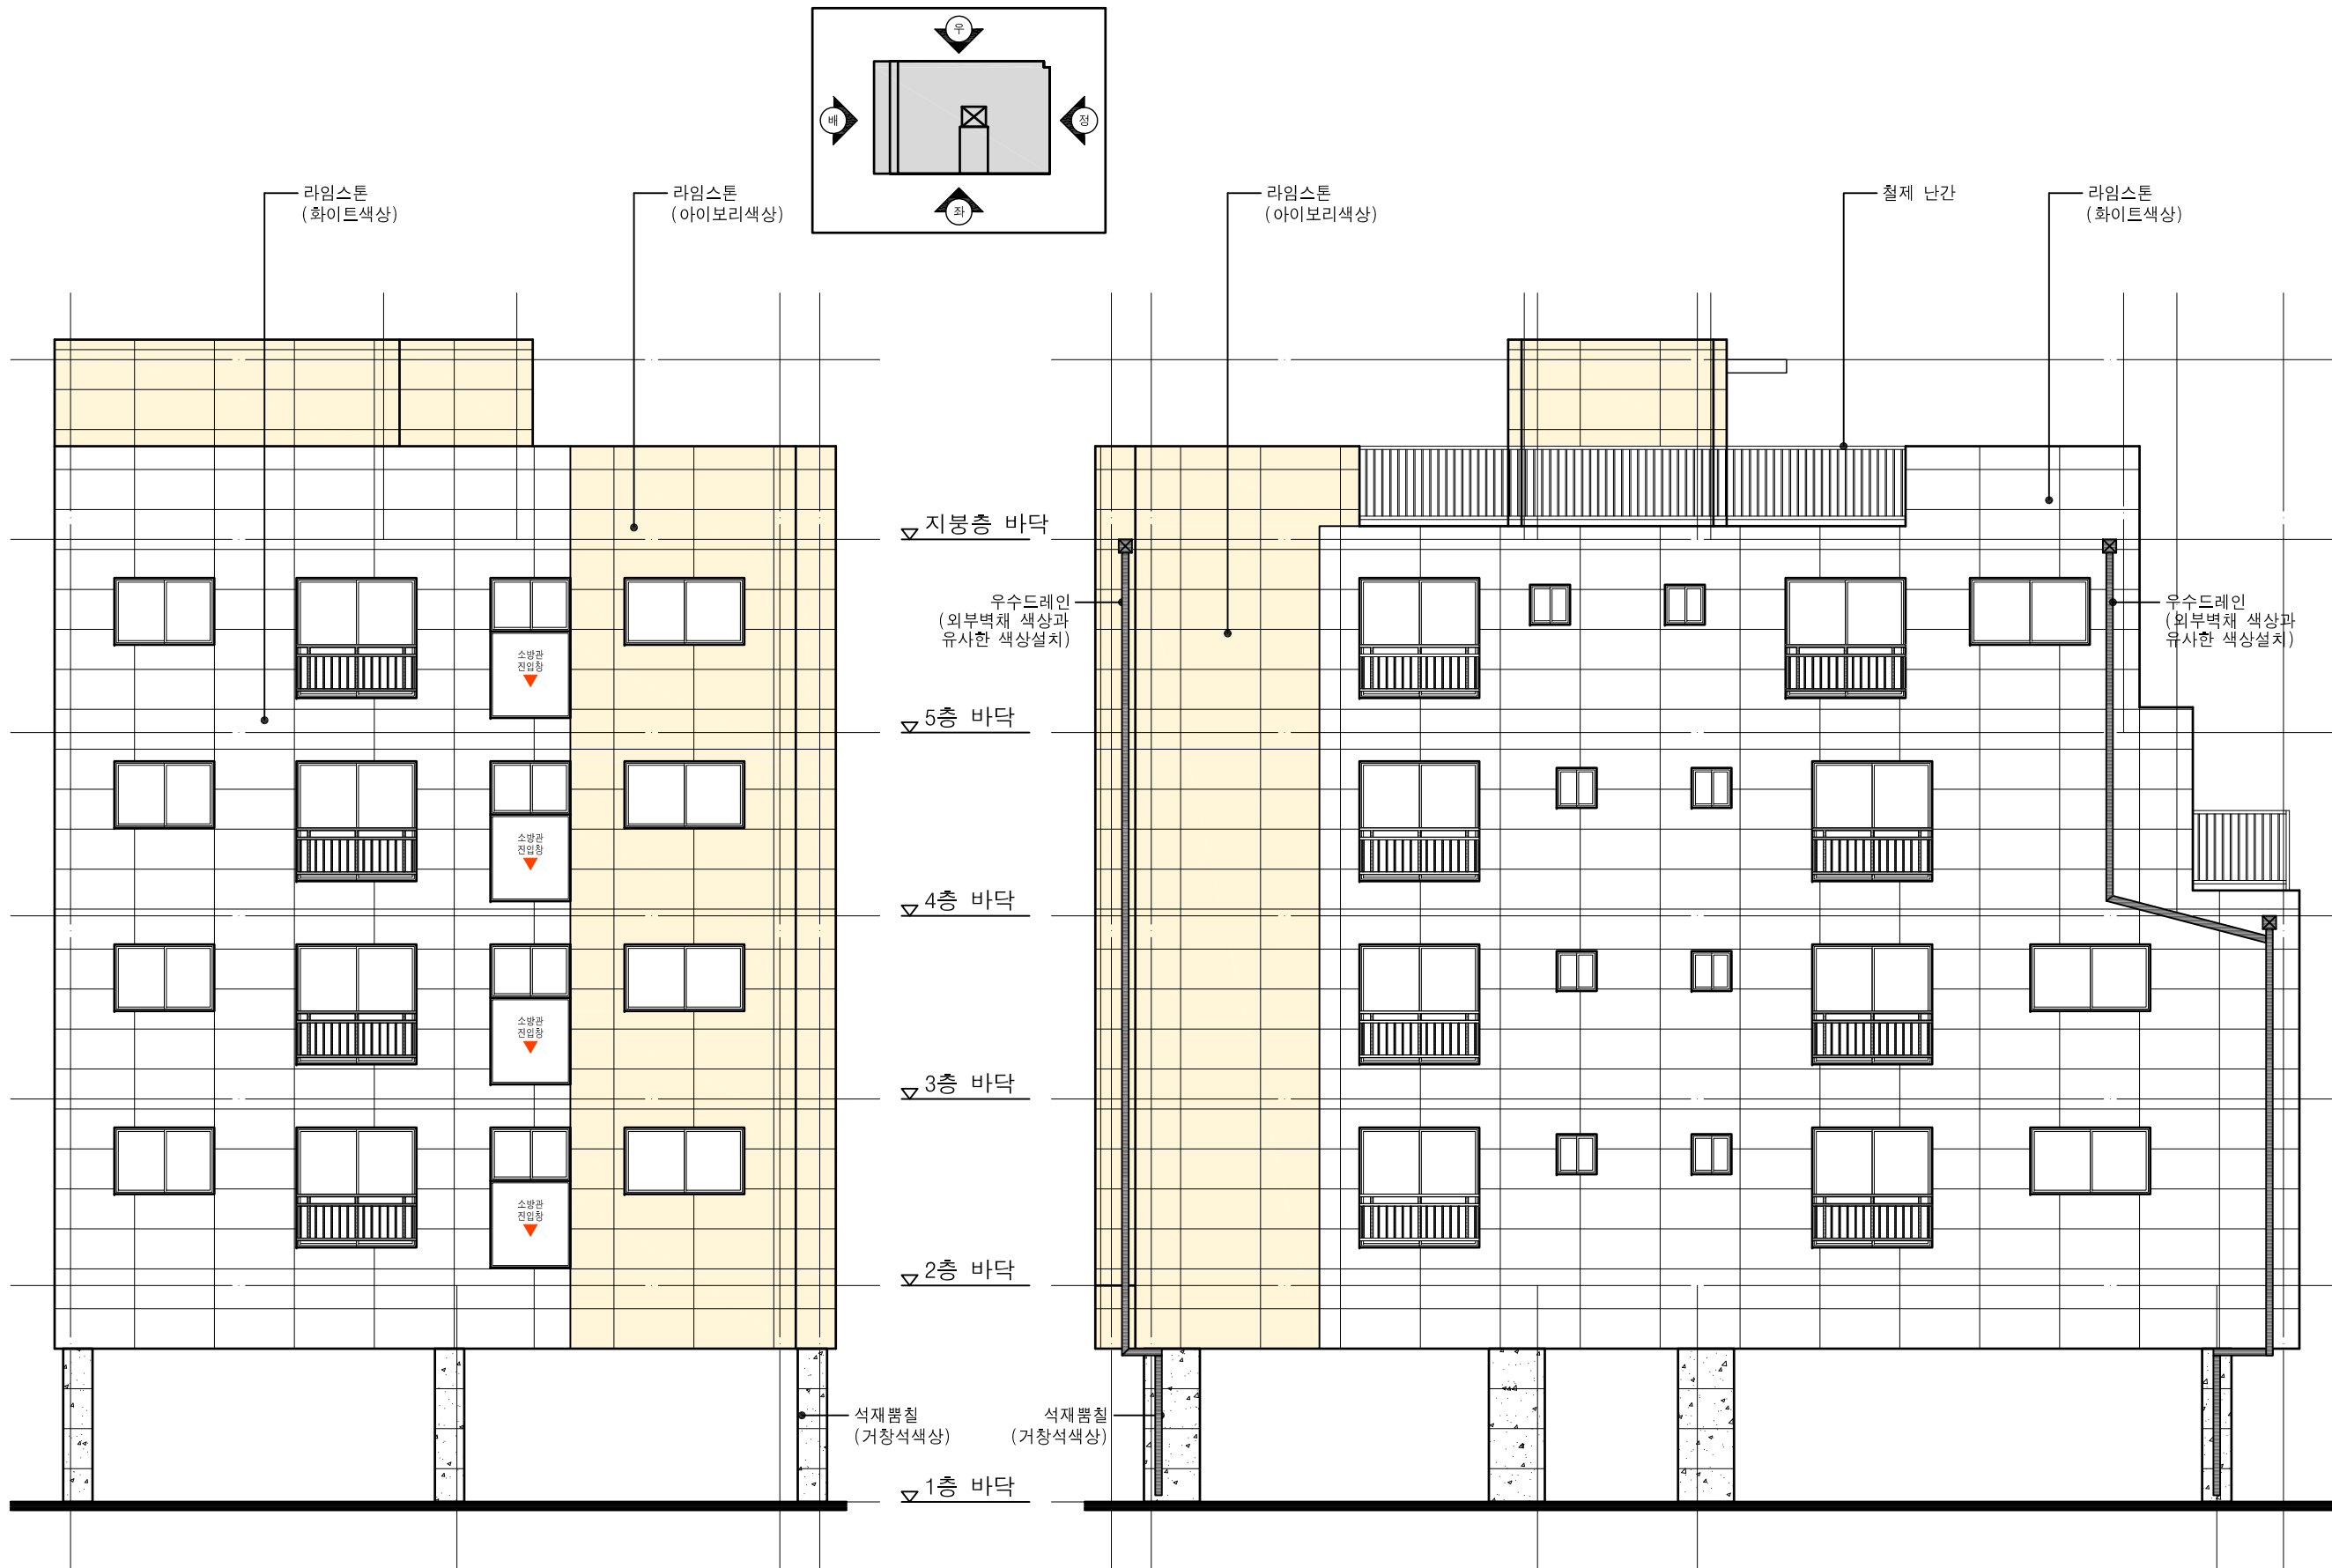

정면도
SCALE : A3 : 1/100

우측면도
SCALE : A3 : 1/100

PROJECT TITLE
사업명
신림동 509-1호 외 1필지
도시형생활주택(소형주택) 신축공사
다세대주택 신축공사

NAME OF DRAWING
도면명
입면도-1

NOTE
주 기
창호 PVC 블랙
소방관진입창 - 스티커부착

NO. ▲ REVISIONS ▲ DATE
번호 수정 일자

DESIGNED BY
설 계

CHECKED BY
검 사

APPROVED BY
승 인

CONSULTANTS
협 동 설 계


SCALE
축척 1/ 100

DATE
일 자 2023. 09.


DWG NO.
도면 번호 A- 31

SHEET NO.
일련 번호 □-□□□

DAWOOM
dawoom
건축사사무소 다움건축
THE ARCHITECTS DESIGN GROUP
TEL. 02.414.6061 (代)
FAX. 02.414.6062

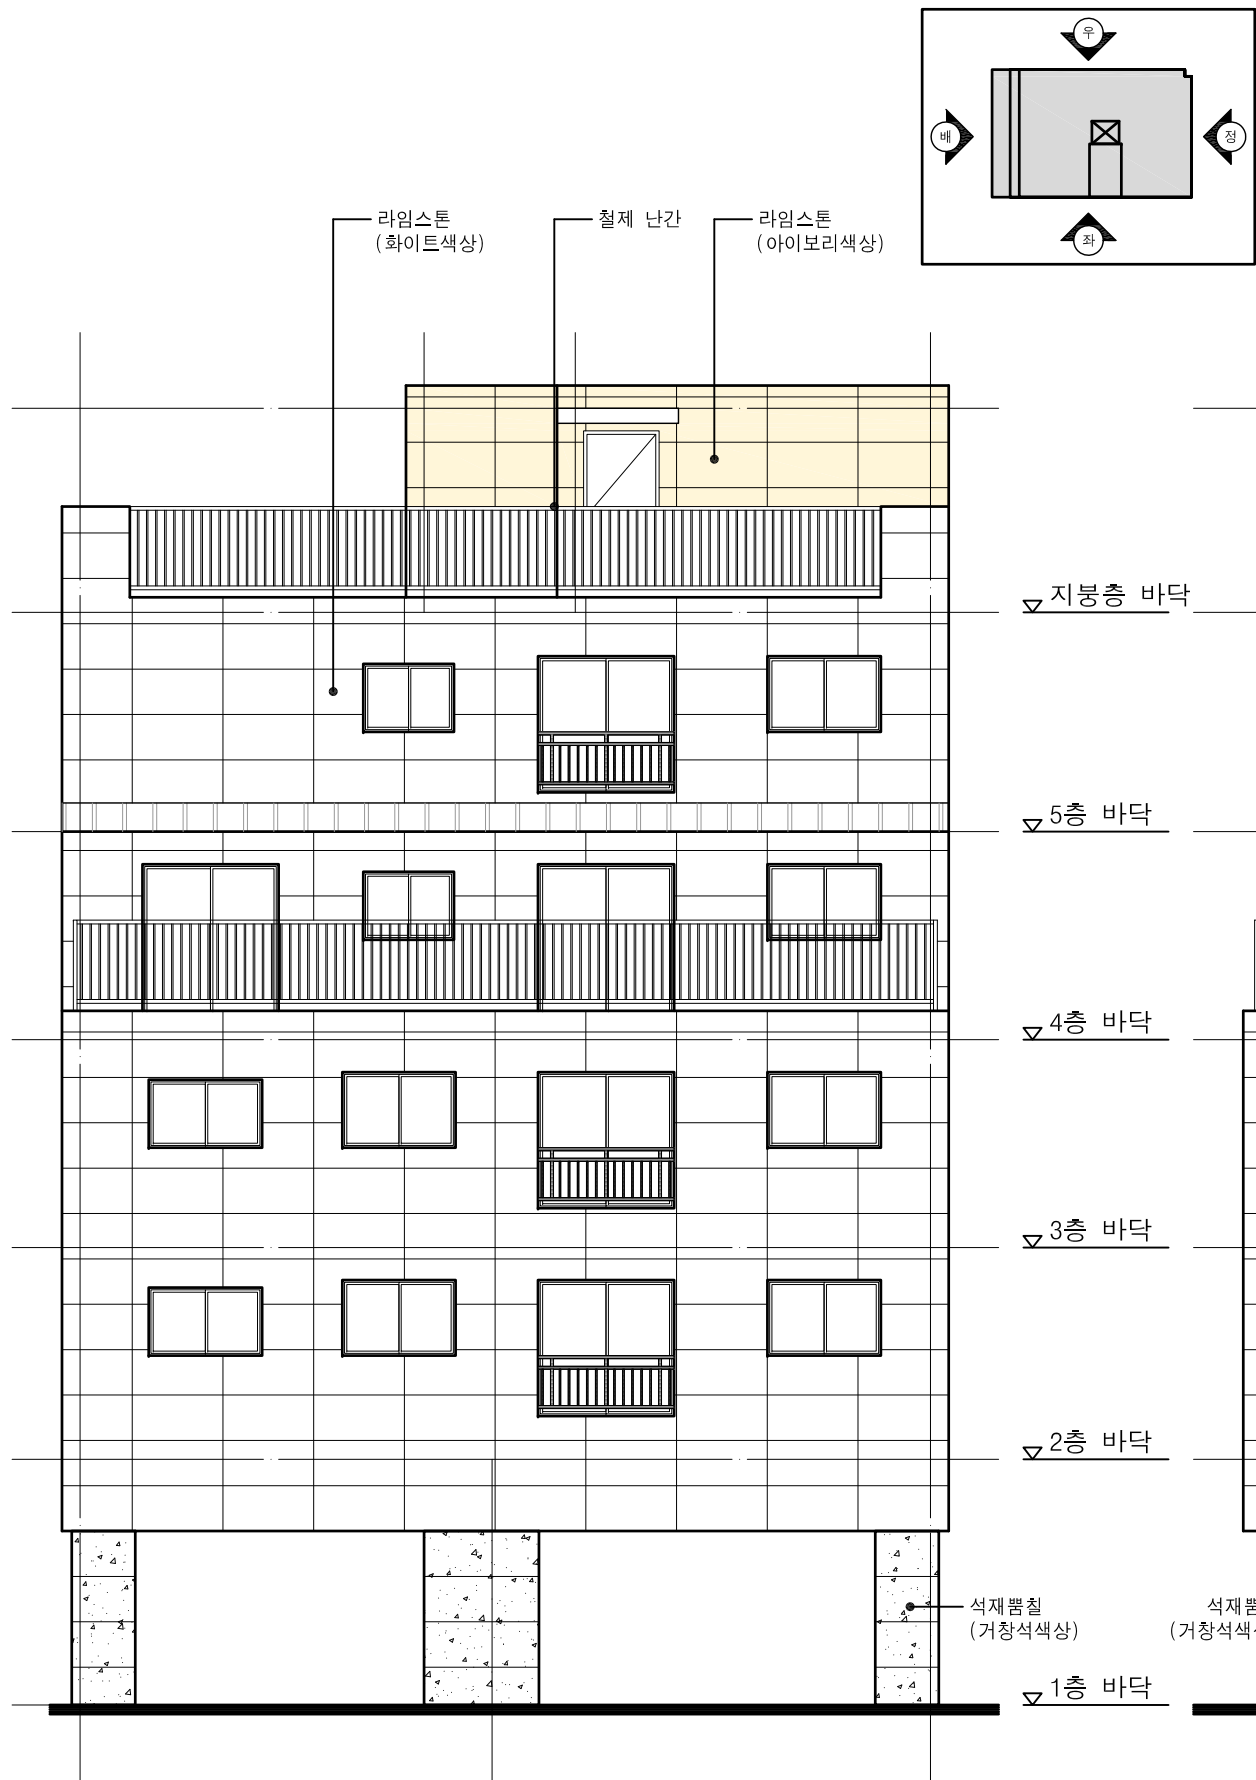

배면도
SCALE : A3 : 1/100

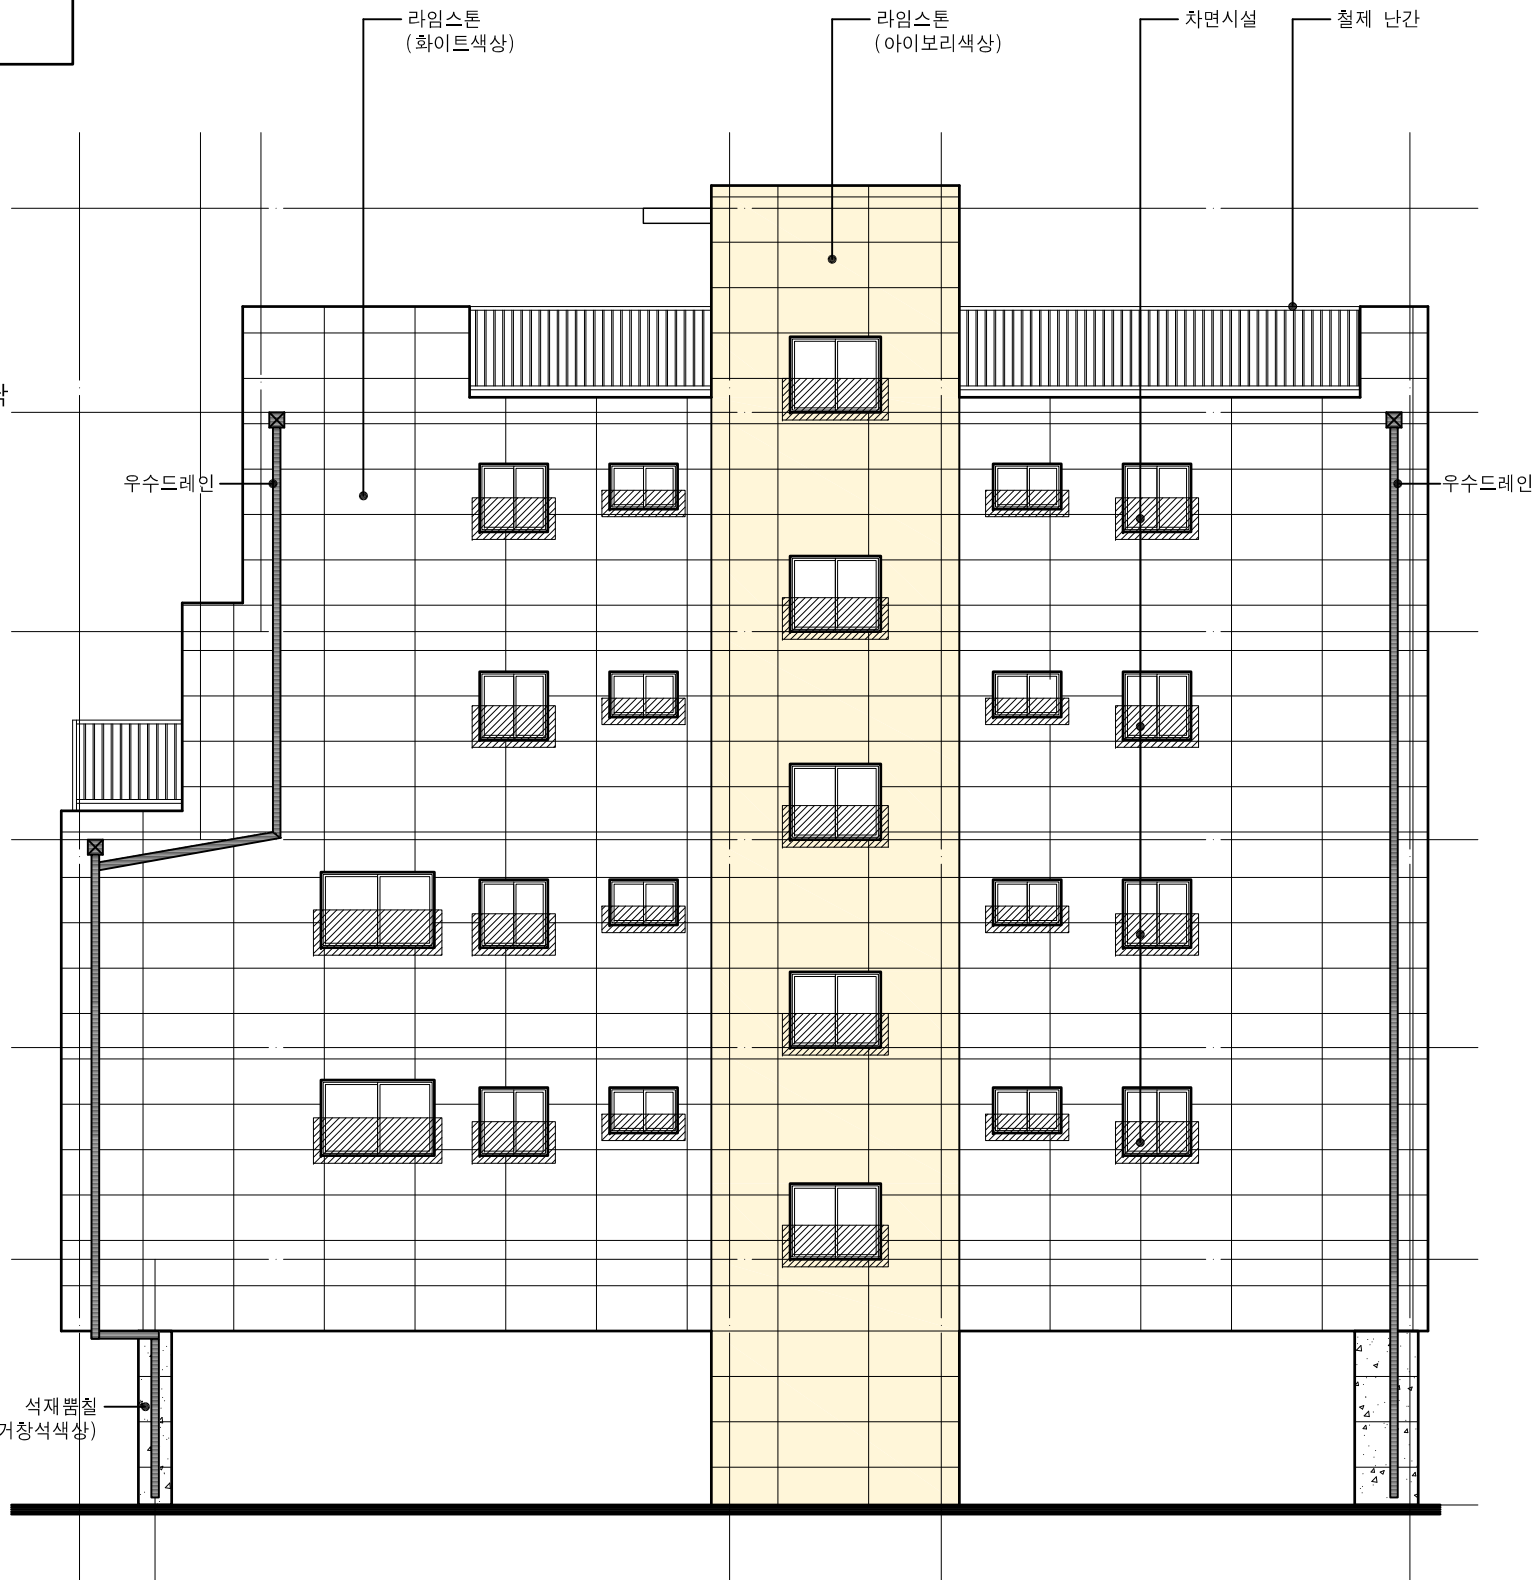

좌측면도
SCALE : A3 : 1/100

PROJECT TITLE
사업명
신림동 509-1호 외 1필지
도시형생활주택(소형주택) 신축공사
다세대주택 신축공사

NAME OF DRAWING
도면명
입면도-2

NOTE
주 기
창호 PVC 블랙

NO. ▲ REVISIONS ▲ DATE
번호 수정 일자

DESIGNED BY
설 계

CHECKED BY
검 사

APPROVED BY
승 인

CONSULTANTS
협 동 설 계

SCALE
축척 1/ 100

DATE
일 자 2023. 09.

DWG NO.
도면 번호 A- 32

SHEET NO.
일련 번호 □-□□□

 DAWOOM
dawoom
건축사사무소 다움건축
THE ARCHITECTS DESIGN GROUP
TEL. 02.414.6061 (代)
FAX. 02.414.6062