


NOTES

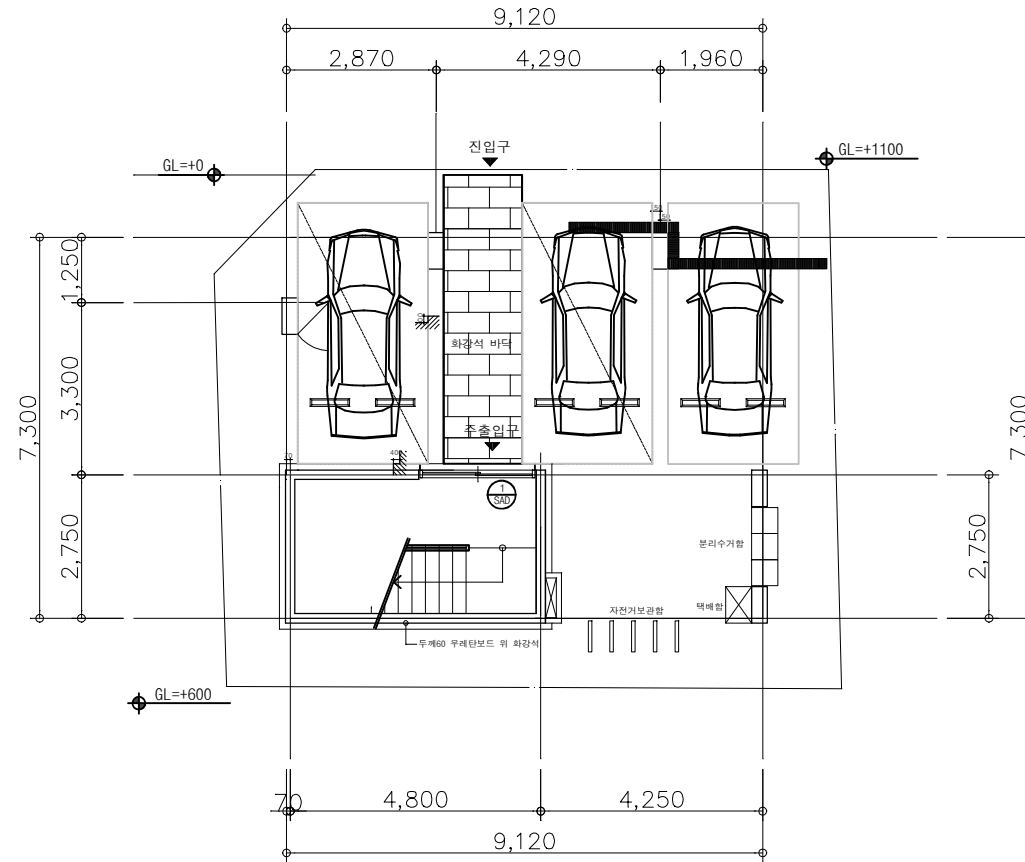

1 1층 평면도
축척 : 1/100

△			
△			
△			

신림동598-129
임대주택 계획안


승인

1층 평면도

A-22



NOTES

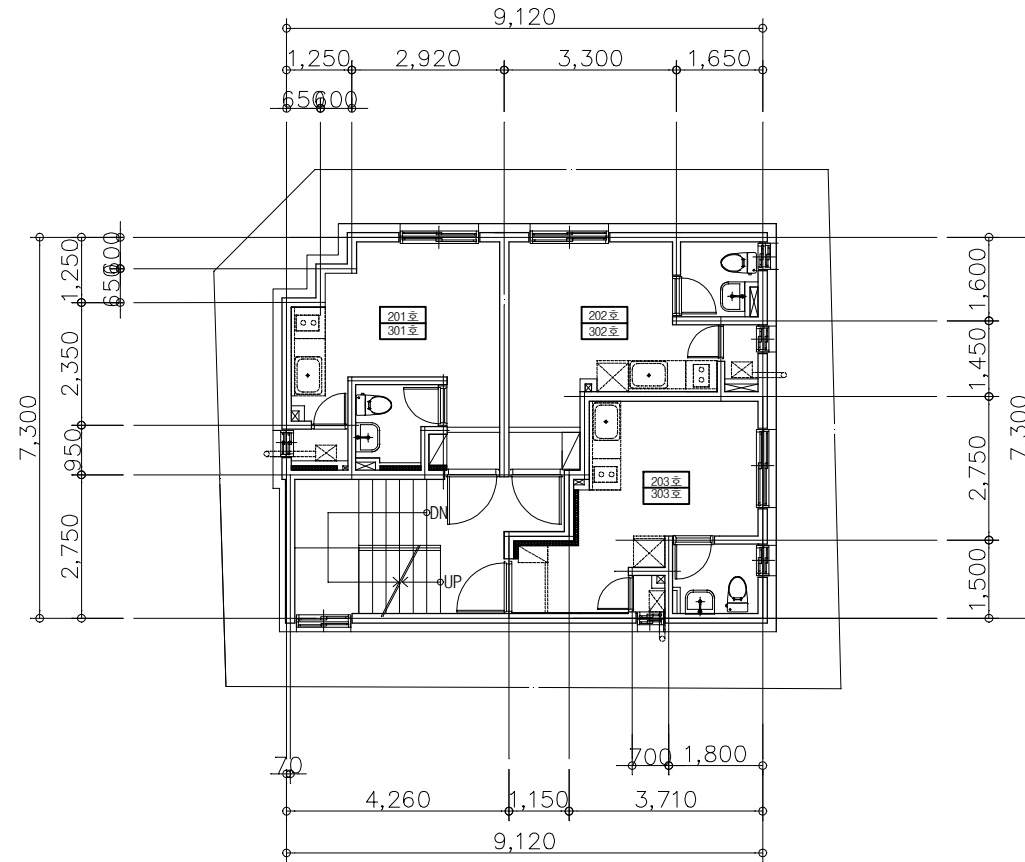

1 2,3층 평면도
축척 : 1/100

△			
△			
△			

신림동598-129
임대주택 계획안


승인

2,3층 평면도

A-23



NOTES

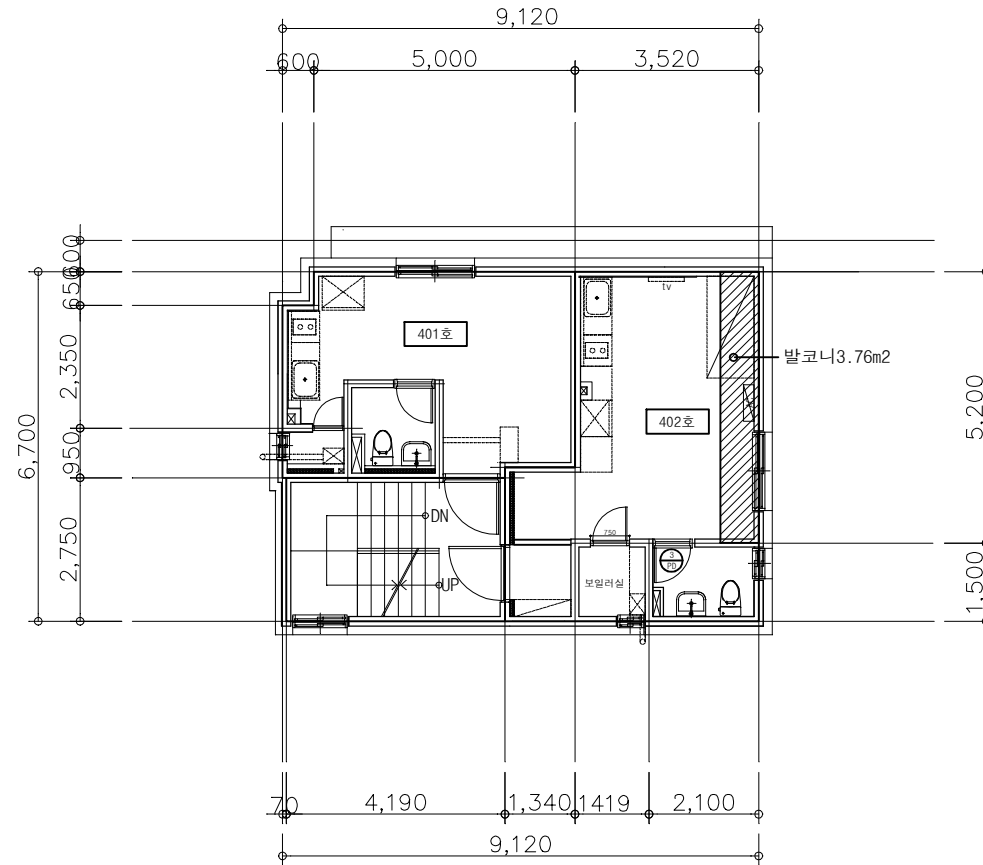

1 4층 평면도
축척 : 1/100

△			
△			
△			

신림동598-129
임대주택 계획안


승인

4층 평면도

A-24



NOTES

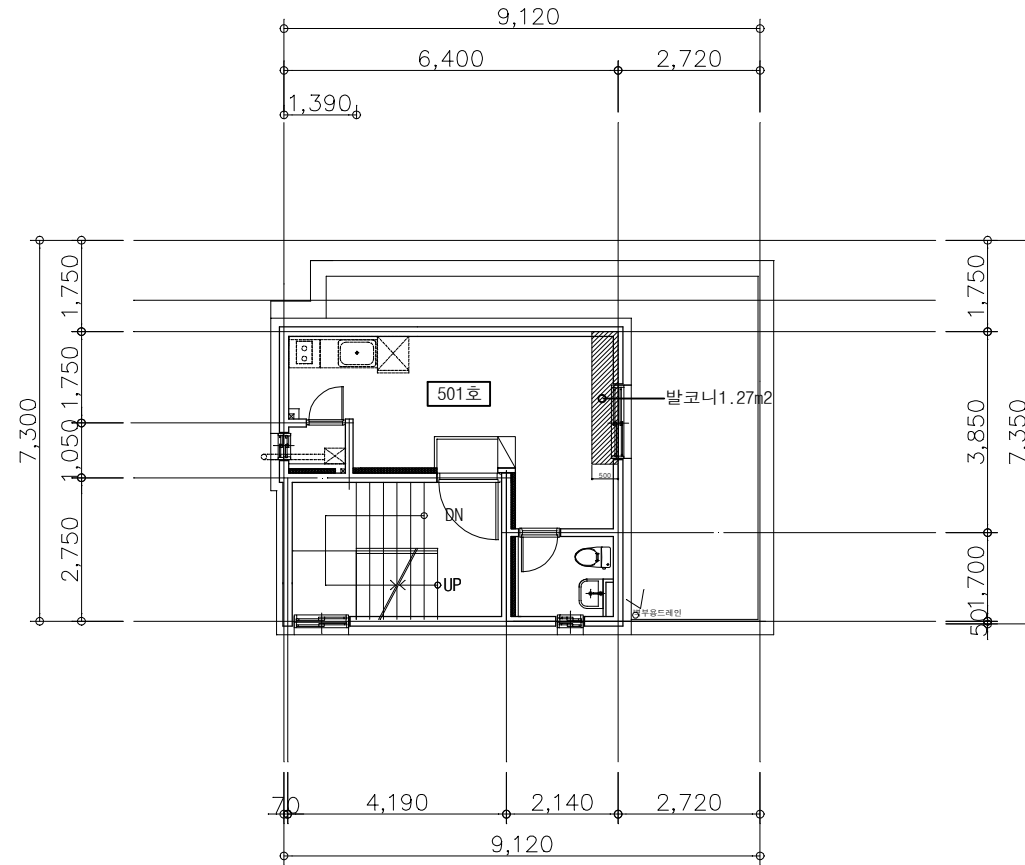

1 5층 평면도
축척 : 1/100

△			
△			
△			

신림동598-129
임대주택 계획안

	...
	...
	...
	...
	...


승인

4층 평면도

A-25



NOTES

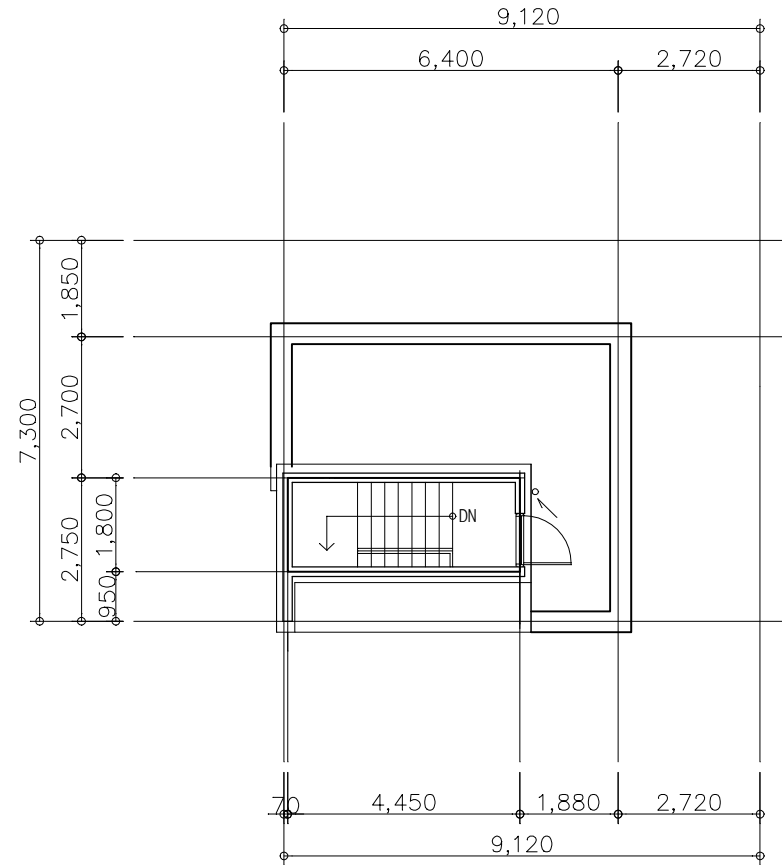

1

지붕층평면도

축척 : 1/100

8.01m²

△			
△			
△			

신림동598-129
임대주택 계획안

승인

지붕층 평면도

A- 26

△

NOTES


△			
△			
△			

신림동598-129
임대주택 계획안

승인

횡단면도

A- 32

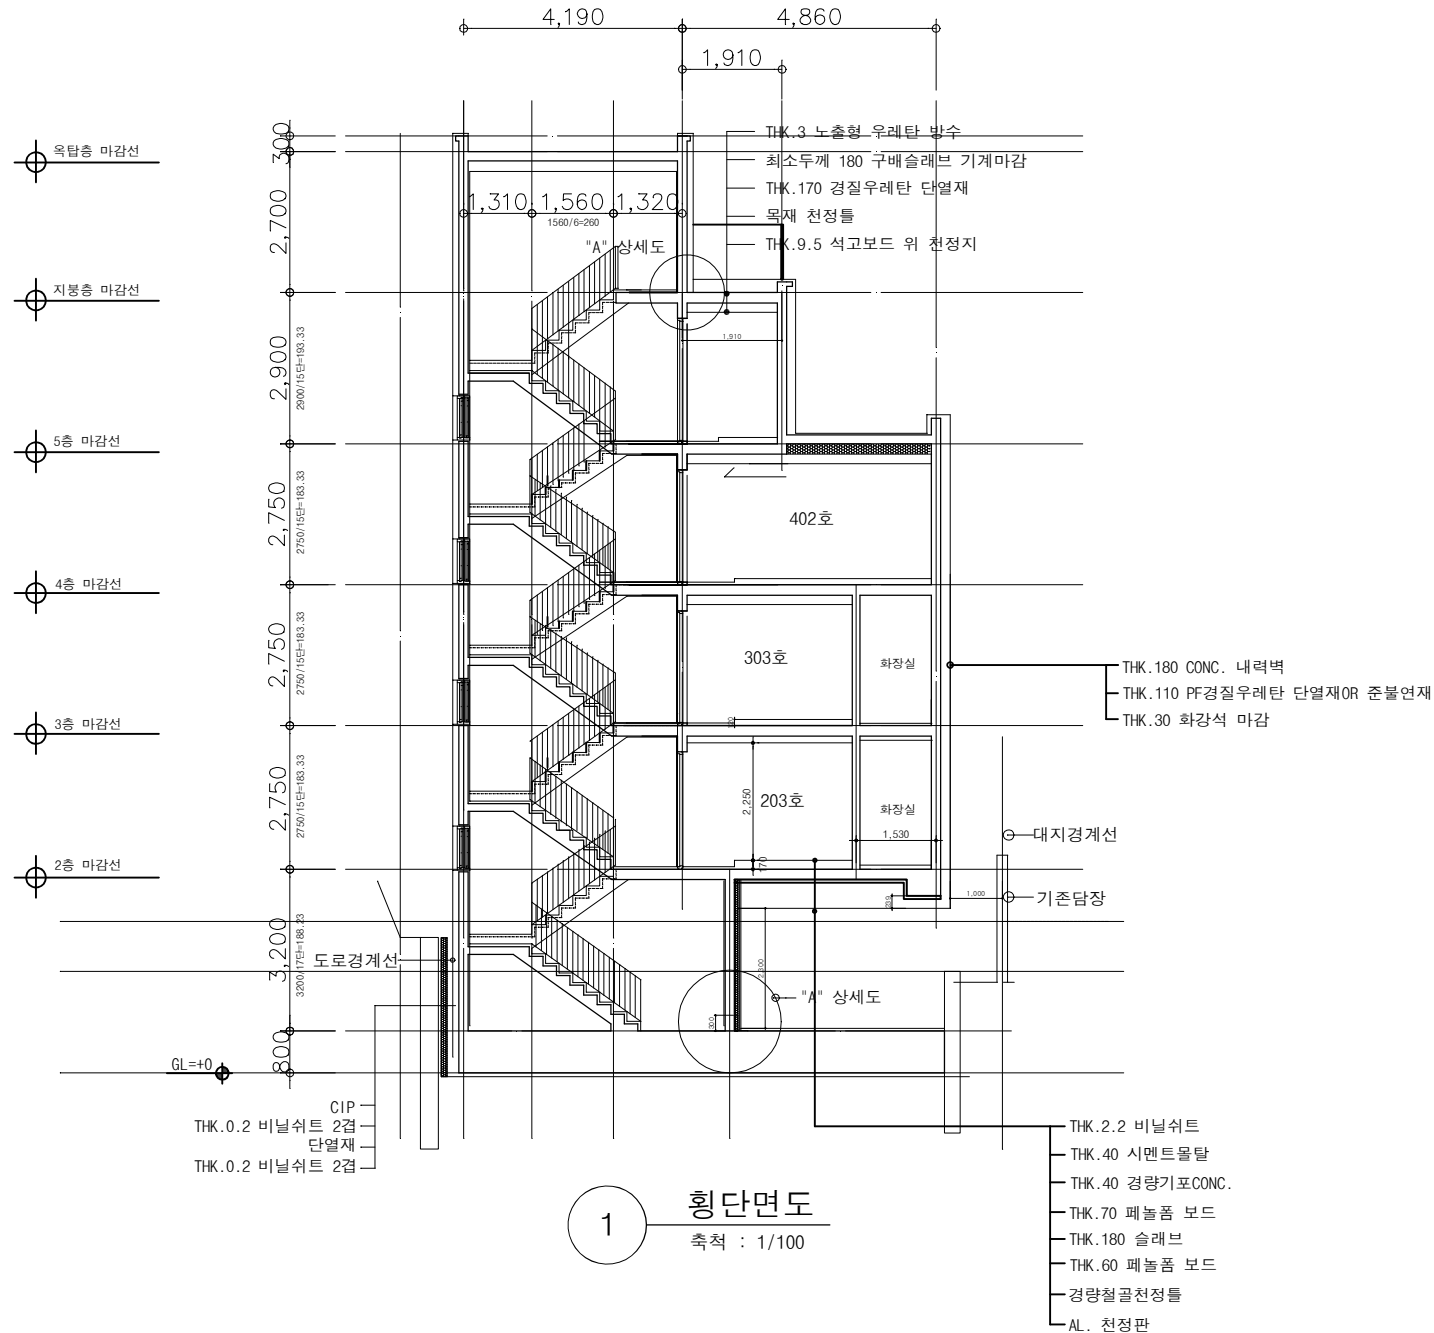

NOTES


△			
△			
△			

신림동598-129
임대주택 계획안

승인

총단면도

A- 31

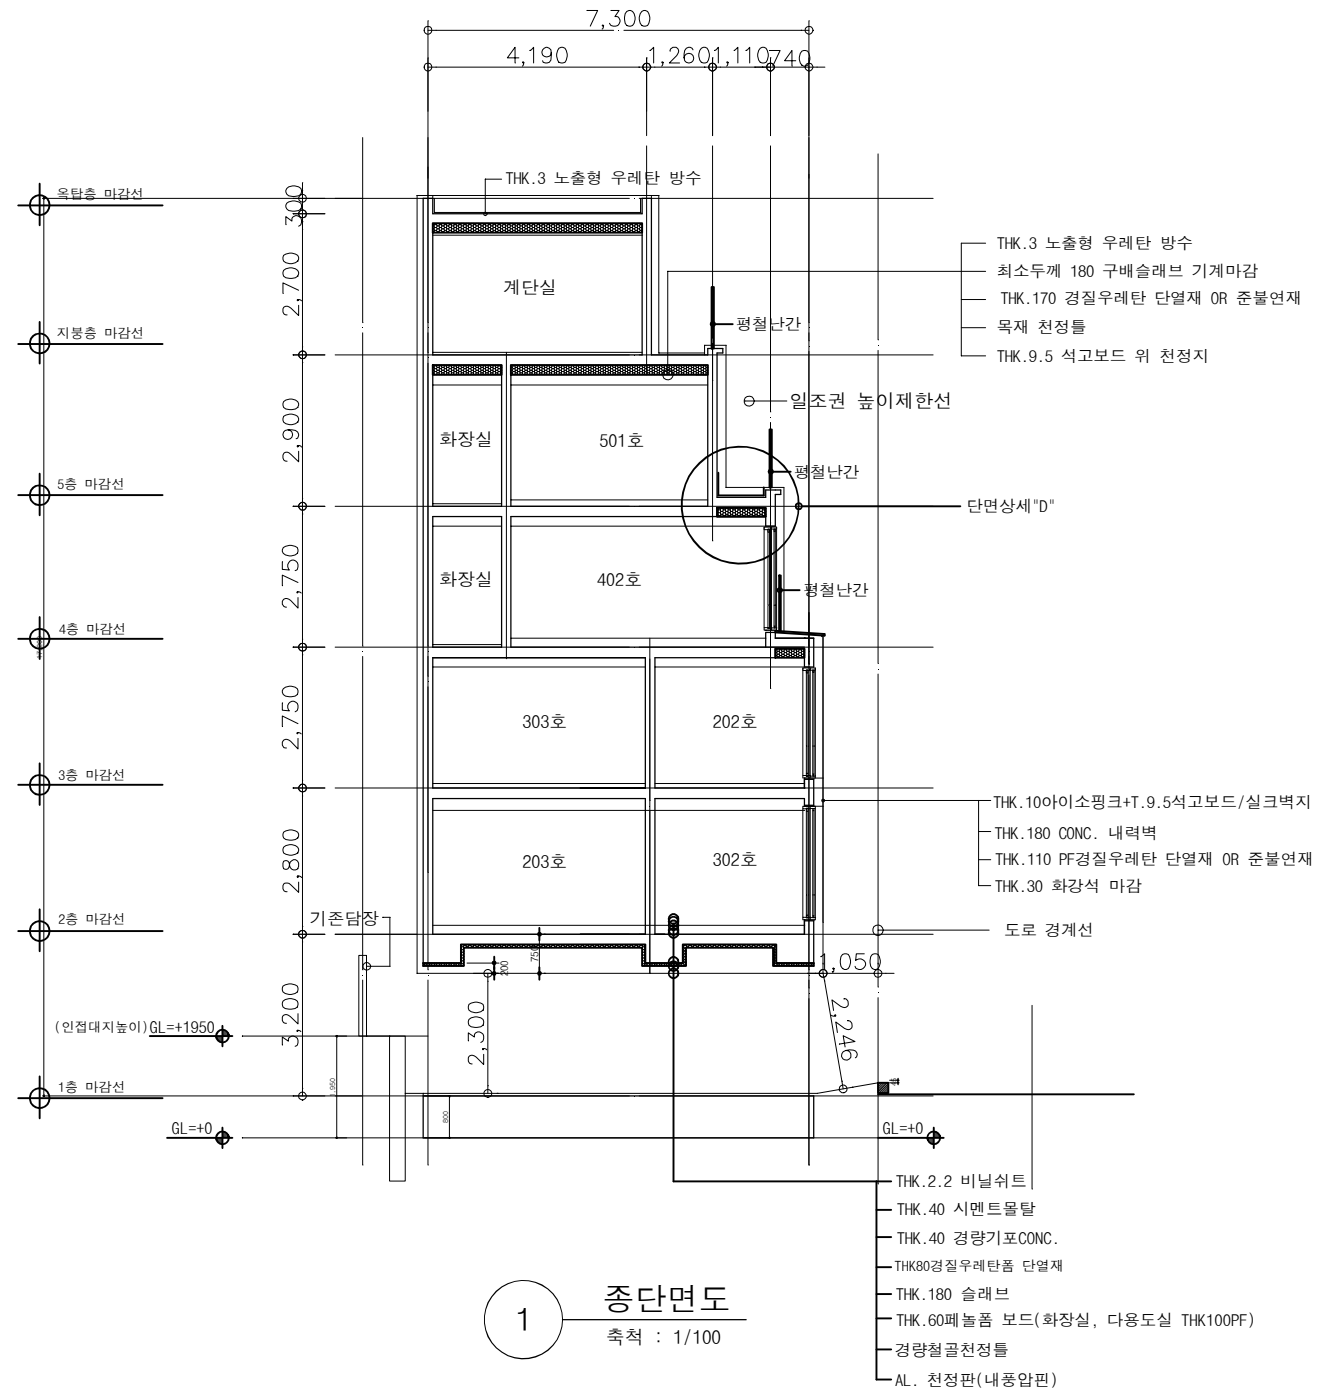

1

종단면도

축척 : 1/100

NOTES

△			
△			
△			

신림동598-129
임대주택 계획안

승인

정면도

A-28



옥탑 SL(구조)

ROOF SL(구조)


5층 SL(구조)

4층 SL(구조)

3층 SL(구조)

2층 SL(구조)

1층 SL(구조)

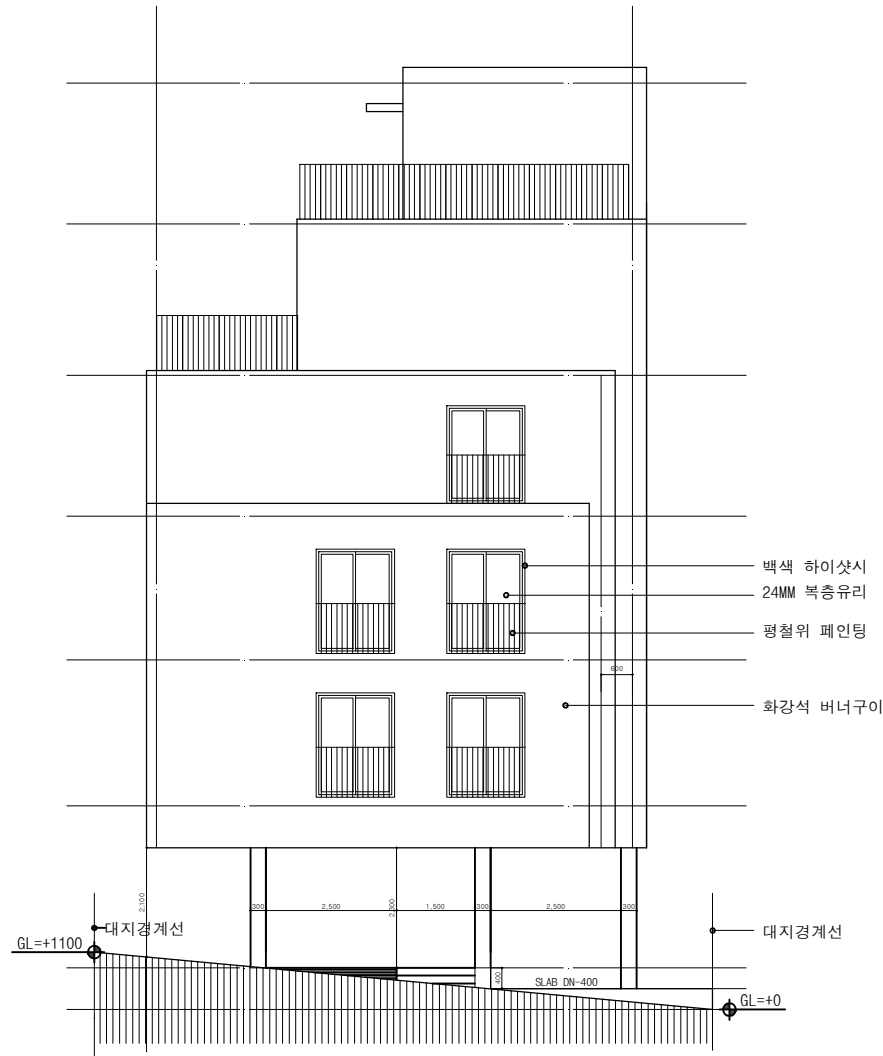

1

정면도

축척 : 1/100

NOTES

△			
△			
△			

신림동598-129
임대주택 계획안

승인

좌측면도

A-30



○ 옥탑 SL(구조)

○ ROOF SL(구조)

○ 5층 SL(구조)

○ 4층 SL(구조)

○ 3층 SL(구조)

○ 2층 SL(구조)

○ 1층 SL(구조)



1 좌측면도
축척 : 1/100

NOTES

△			
△			
△			

신림동598-129
임대주택 계획안

승인

우측면도

A-29



○ 옥탑 SL(구조)

○ ROOF SL(구조)


○ 5층 SL(구조)

○ 4층 SL(구조)

○ 3층 SL(구조)

○ 2층 SL(구조)

○ 1층 SL(구조)

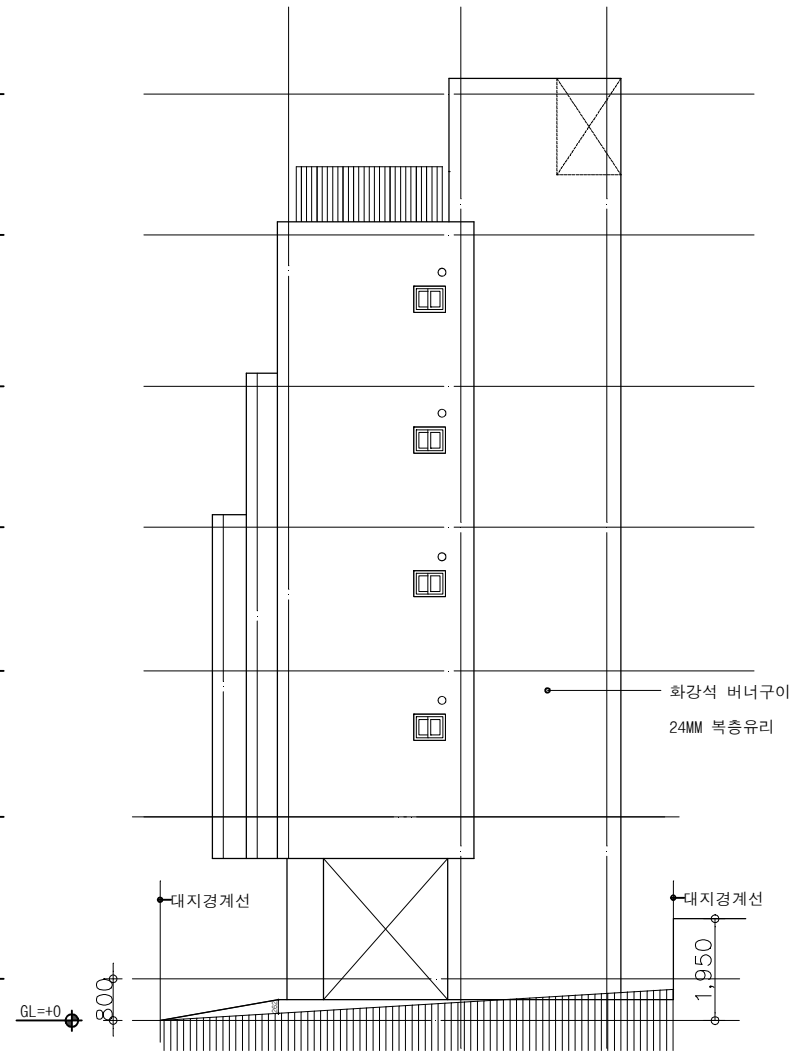

1 우측면도
축척 : 1/100

NOTES

△			
△			
△			

신림동598-129
임대주택 계획안

승인

배면도

A-27



○ 옥탑 SL(구조)

○ ROOF SL(구조)


○ 5층 SL(구조)

○ 4층 SL(구조)

○ 3층 SL(구조)

○ 2층 SL(구조)

○ 1층 SL(구조)

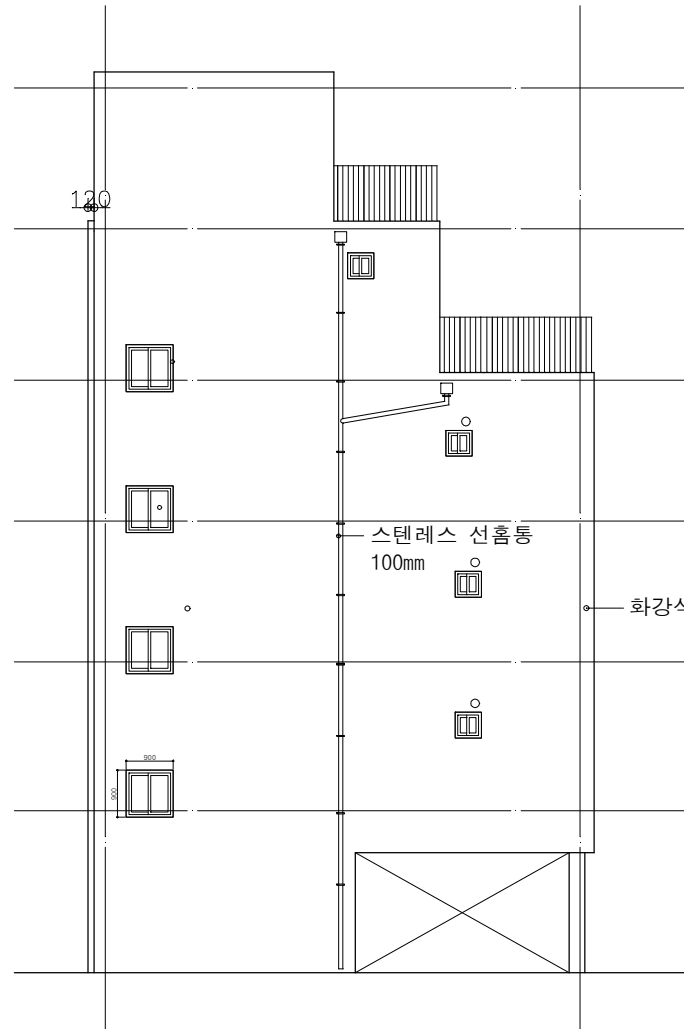

1 배면도
축척 : 1/100