

신림동 537-14
다세대주택 신축공사

설 계 코 드
PROJECT CODE

주 기 사 항
NOTE

단 계
ISSUED FOR

날 짜
DATE

2023. 03.

축 척
SCALE

A1

1/

A3

1/ 100


도 면 명
DRAWING TITLE

지상1층 평면도

SIGUN 시건 건축사무소
SIGUN ARCHITECTURE & PLANNER
TEL: 070-4772-9090, E: sigunarch@naver.com

도 면 번 호
DRAWING NO

A - 201

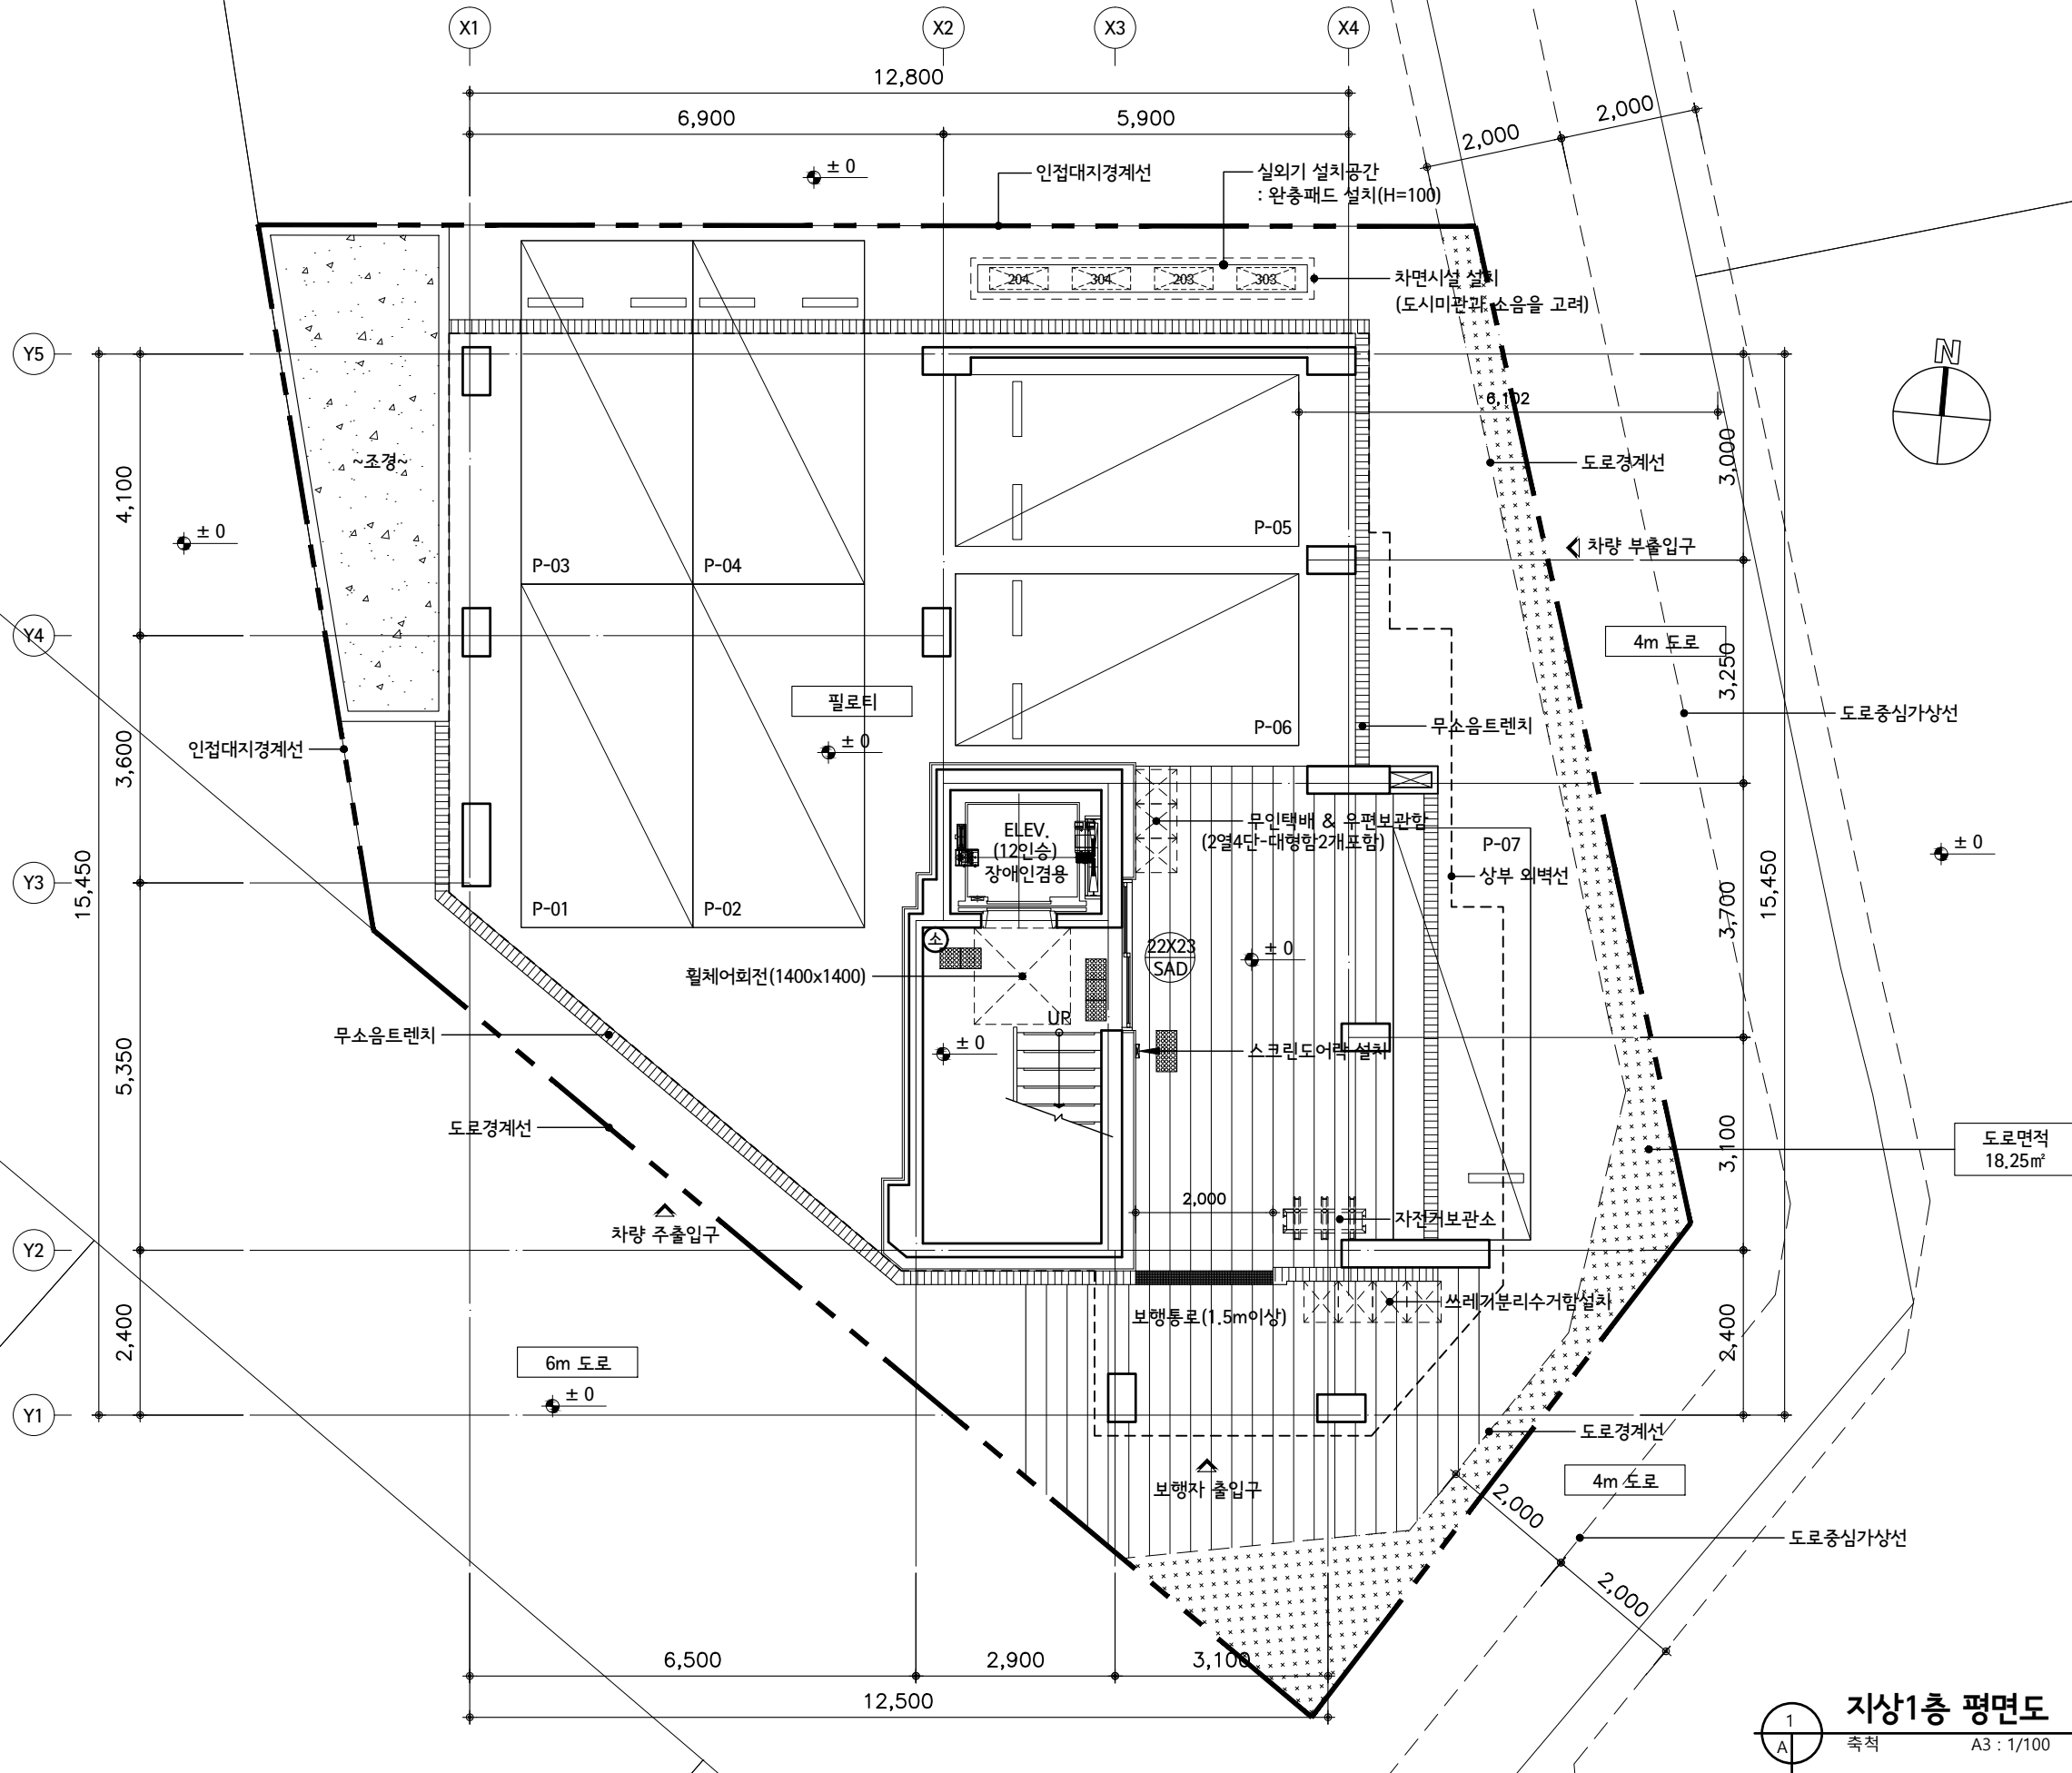

신림동 537-14
다세대주택 신축공사

설 계 코 드
PROJECT CODE

주 기 사 항
NOTE

1. 구조

구 분	내 용
강 도	콘크리트 fck = 24 MPa
철 근	fy=400 MPa(HD16이하) fy=500 MPa(HD19이상)
구 분	두 겹
외 벽	200mm(복배근)
세대내벽	150mm(복배근)
세대간벽	200mm(복배근)
코 아	200mm(복배근)
슬라브	3 ~ 5 층 210mm 2층, 지붕 180mm

2. 범위

구 분	내 용
□	단독연기감지기
⊙	ABC분말소화기(3.3KG)
⊠	보일러
⊞	벽걸이 에어컨
⊞	실외기

3. 보일러는 대기관리구역의 대기환경개선에 관한 특별법 제35조(가정용 보일러의 인증 기준 등)에 적합한 가정용 보일러를 설치할 것.

단 계
ISSUED FOR

날 짜
DATE

2023. 03.

축 척
SCALE

A1 1/

A3 1/ 100


도 면 명
DRAWING TITLE

지상2~3층 평면도

SIGUN 시건 건축사사무소
SIGUN ARCHITECTURE & PLANNER
TEL: 070-4772-9090, E: sigunarch@naver.com

도 면 번 호
DRAWING NO

A - 202

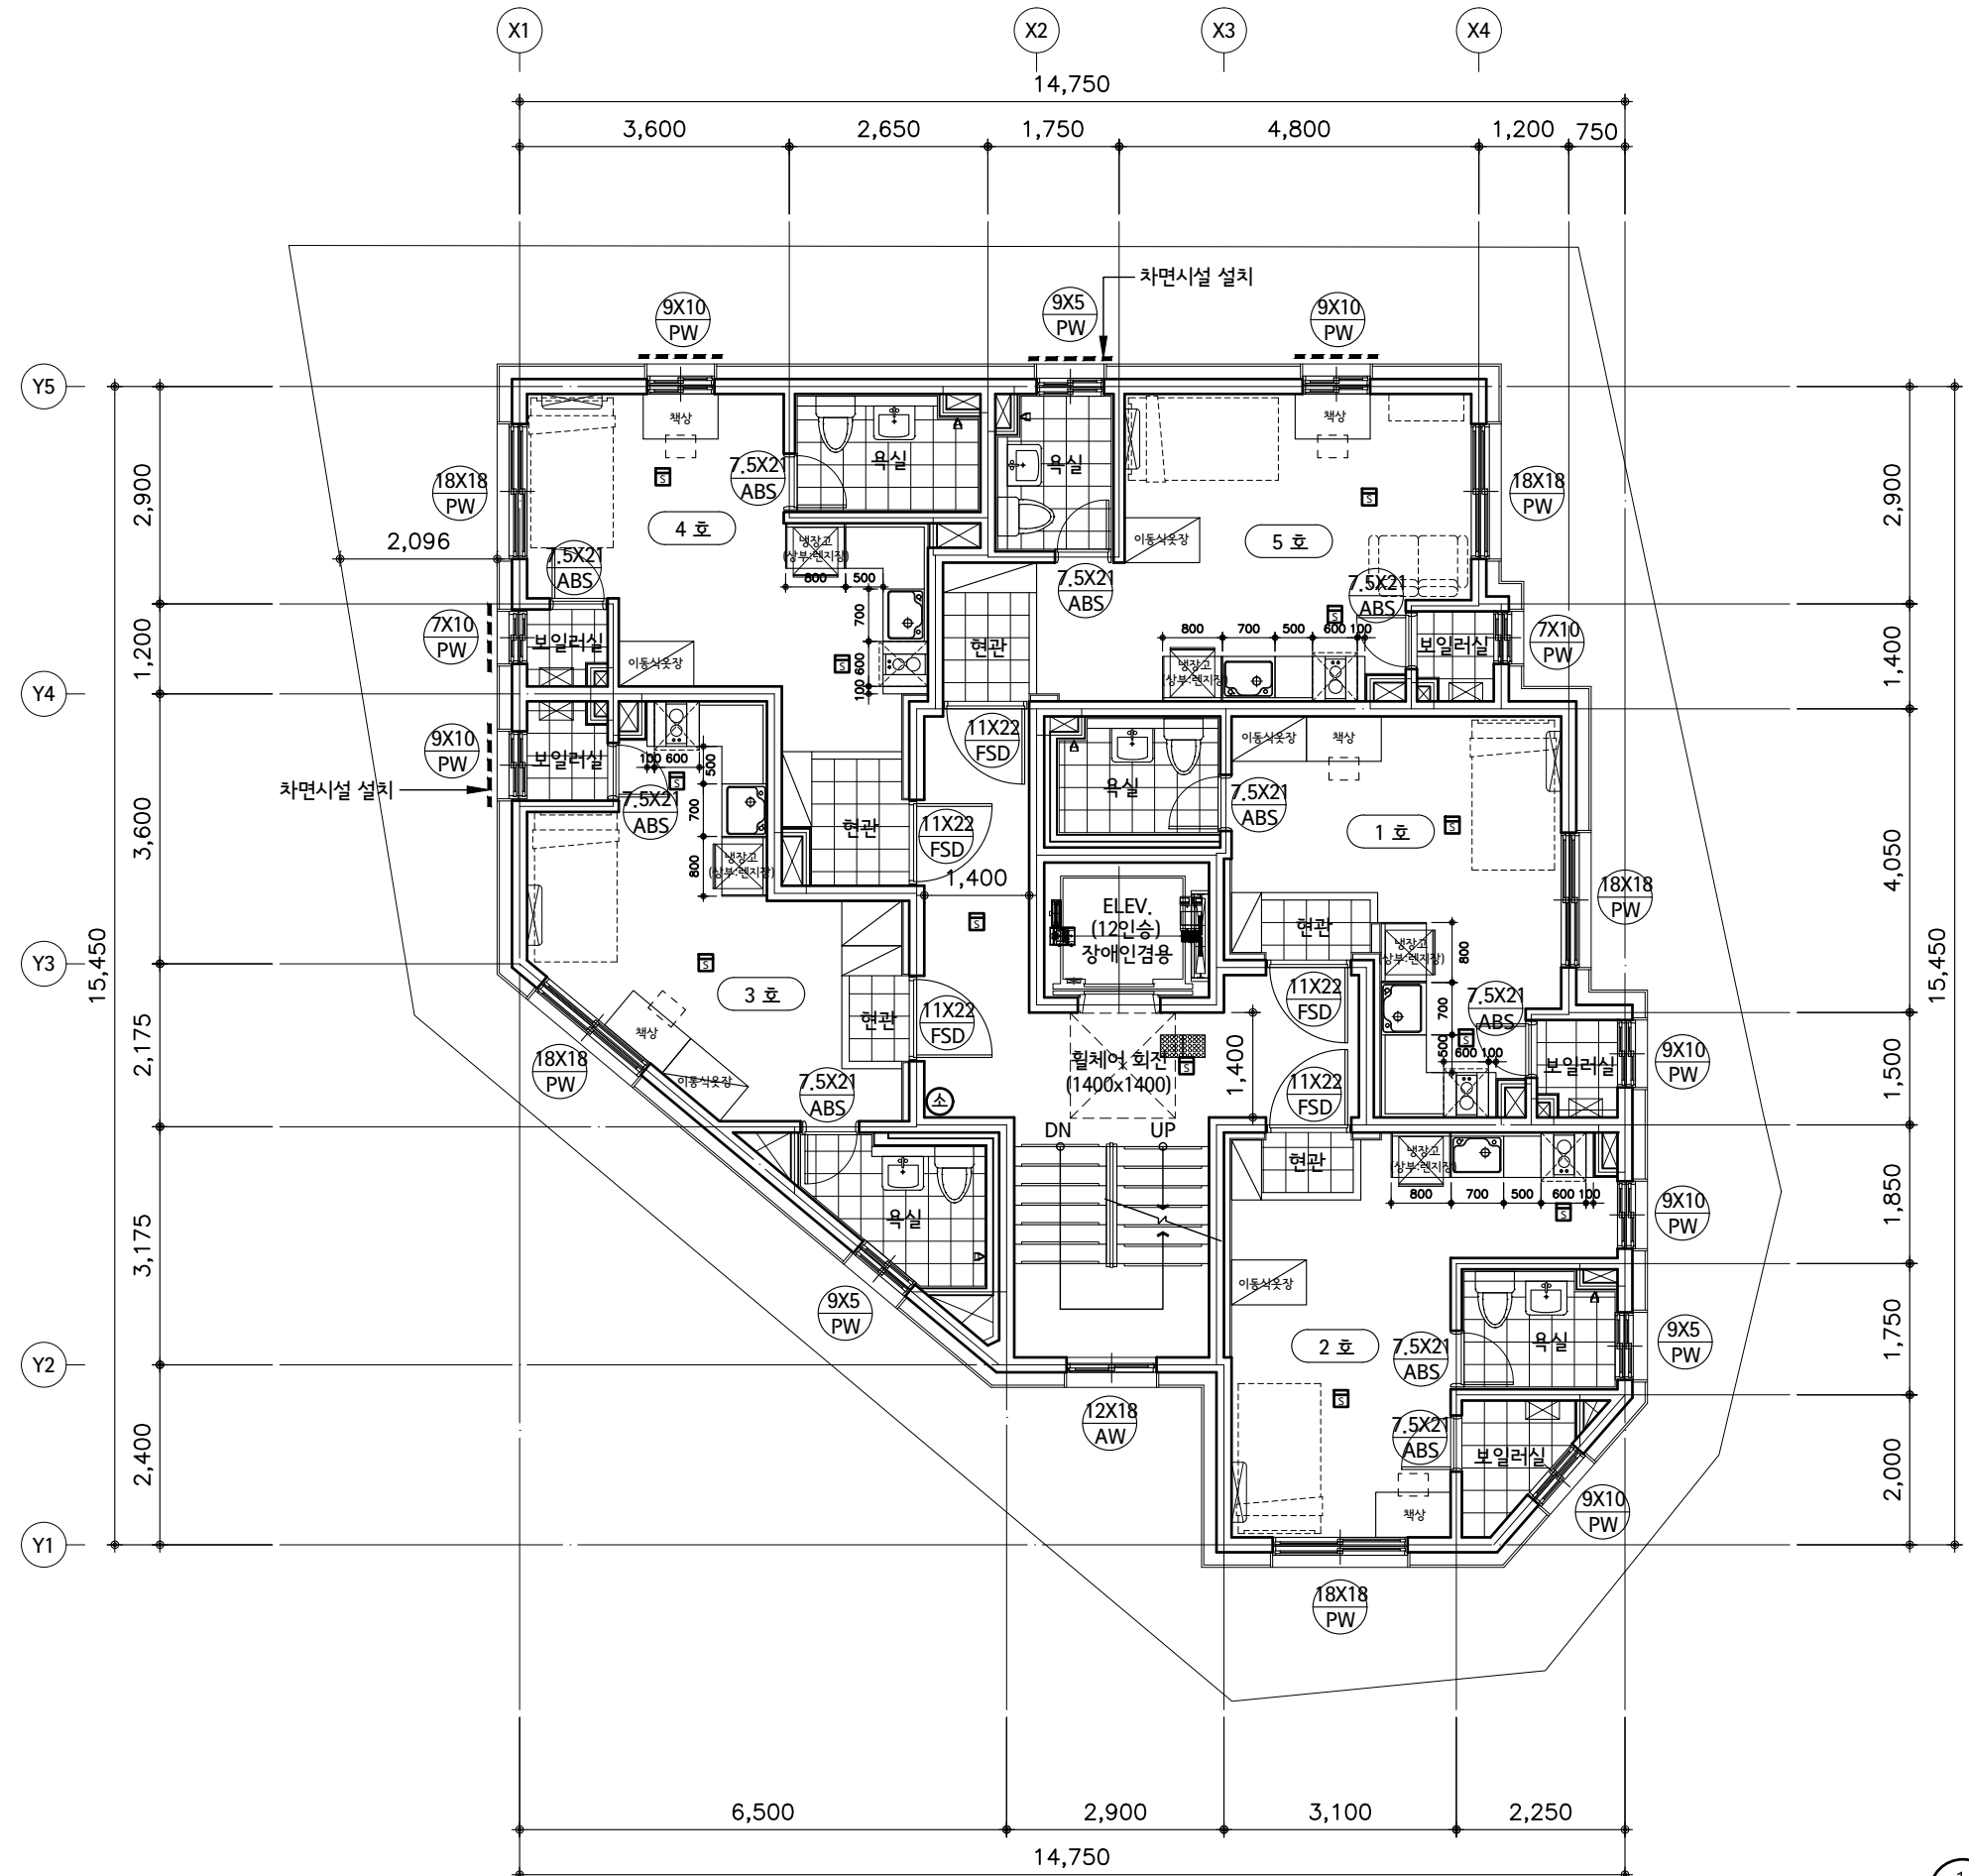

1
A
지상2~3층 평면도
축척 A3 : 1/100

설 계 코드
PROJECT CODE주 기 사 항
NOTE

구 분		내 용
강 도	콘크리트	fck = 24 MPa
	철 근	fy=400 MPa(HD16이하)
		fy=500 MPa(HD19이상)
구 분		두 겹
벽 체	외 벽	200mm(복배근)
	세대전벽	150mm(복배근)
	세단간벽	200mm(복배근)
	코 아	200mm(복배근)
슬 라브	3 ~ 5 층	210mm
	2층, 지붕	180mm

구 분	내 용
	단독연기감지기
	ABC분말소화기(3.3KG)
	보일러
	벽걸이 에어컨
	실외기

단 계
ISSUED FOR

날 짜
DATE

축척
SCALE.

A1	
----	--



A3	
----	--

도면명
DRAWING TITLE

SIGUN 시건 건축사사무소
SIGUN ARCHITECTURE & PLANNER
TEL: 070-4772-9090, E: sigunarch@naver.com

도면 번호
DRAWING NO

A - 203

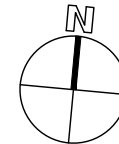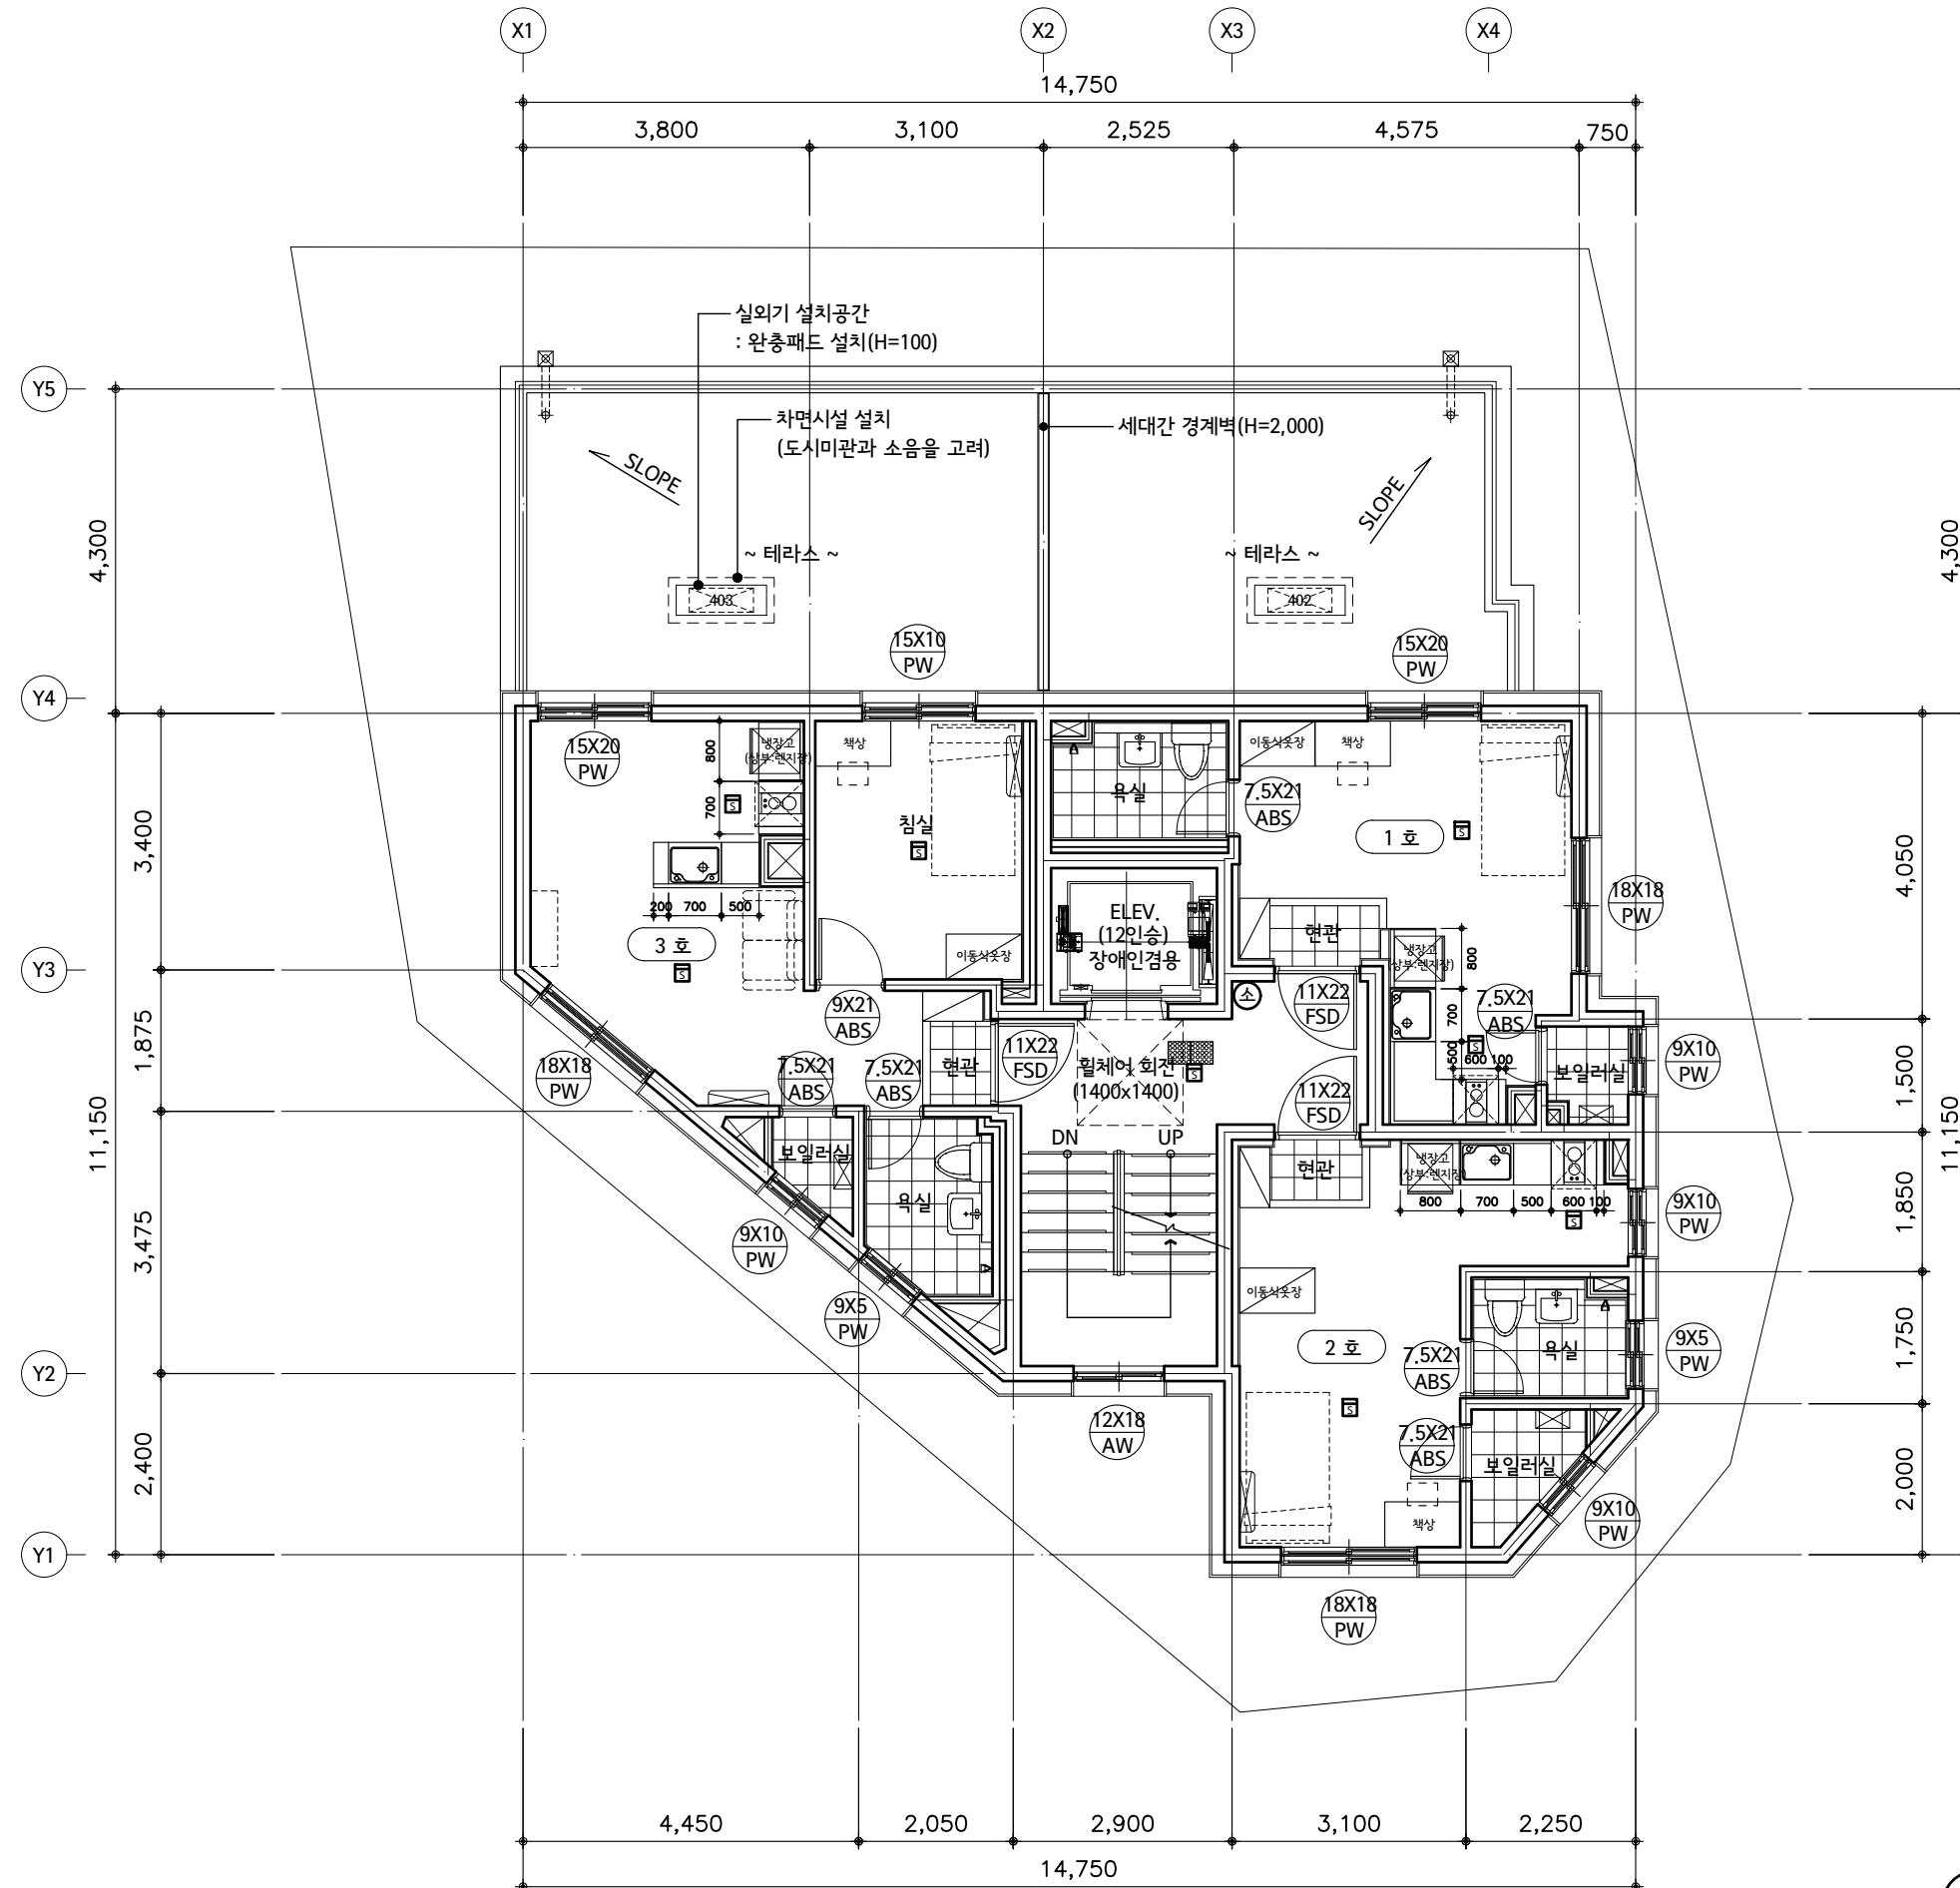

지상4층 평면도

축척 A3 : 1/100

신림동 537-14
다세대주택 신축공사

설 계 코 드
PROJECT CODE

주 기 사 항
NOTE

1. 구조

구 분	내 용
강 도	콘크리트 fck = 24 MPa
	철 근 fy=400 MPa(HD16이하) fy=500 MPa(HD19이상)
구 분	두 겜
벽 체	외 벽 200mm(복배근)
	세대내벽 150mm(복배근)
	세대간벽 200mm(복배근)
	코 아 200mm(복배근)
슬 라브	3 ~ 5 층 210mm
	2층, 지붕 180mm

2. 범위

구 분	내 용
☐	단독연기감지기
⊙	ABC분말소화기(3.3KG)
⊠	보일러
⊞	벽걸이 에어컨
⊞	실외기

3. 보일러는 대기관리권역의 대기환경개선에 관한 특별법 제35조(가정용 보일러의 인증 기준 등)에 적합한 가정용 보일러를 설치할 것.

단 계
ISSUED FOR

날 짜
DATE

2023. 03.

축 척
SCALE

A1	1/
A3	1/ 100


도 면 명
DRAWING TITLE

지상5층 평면도

SIGUN 시건 건축사사무소
SIGUN ARCHITECTURE & PLANNER
TEL: 070-4772-9090, E: sigunarch@naver.com

도 면 번 호
DRAWING NO

A - 204


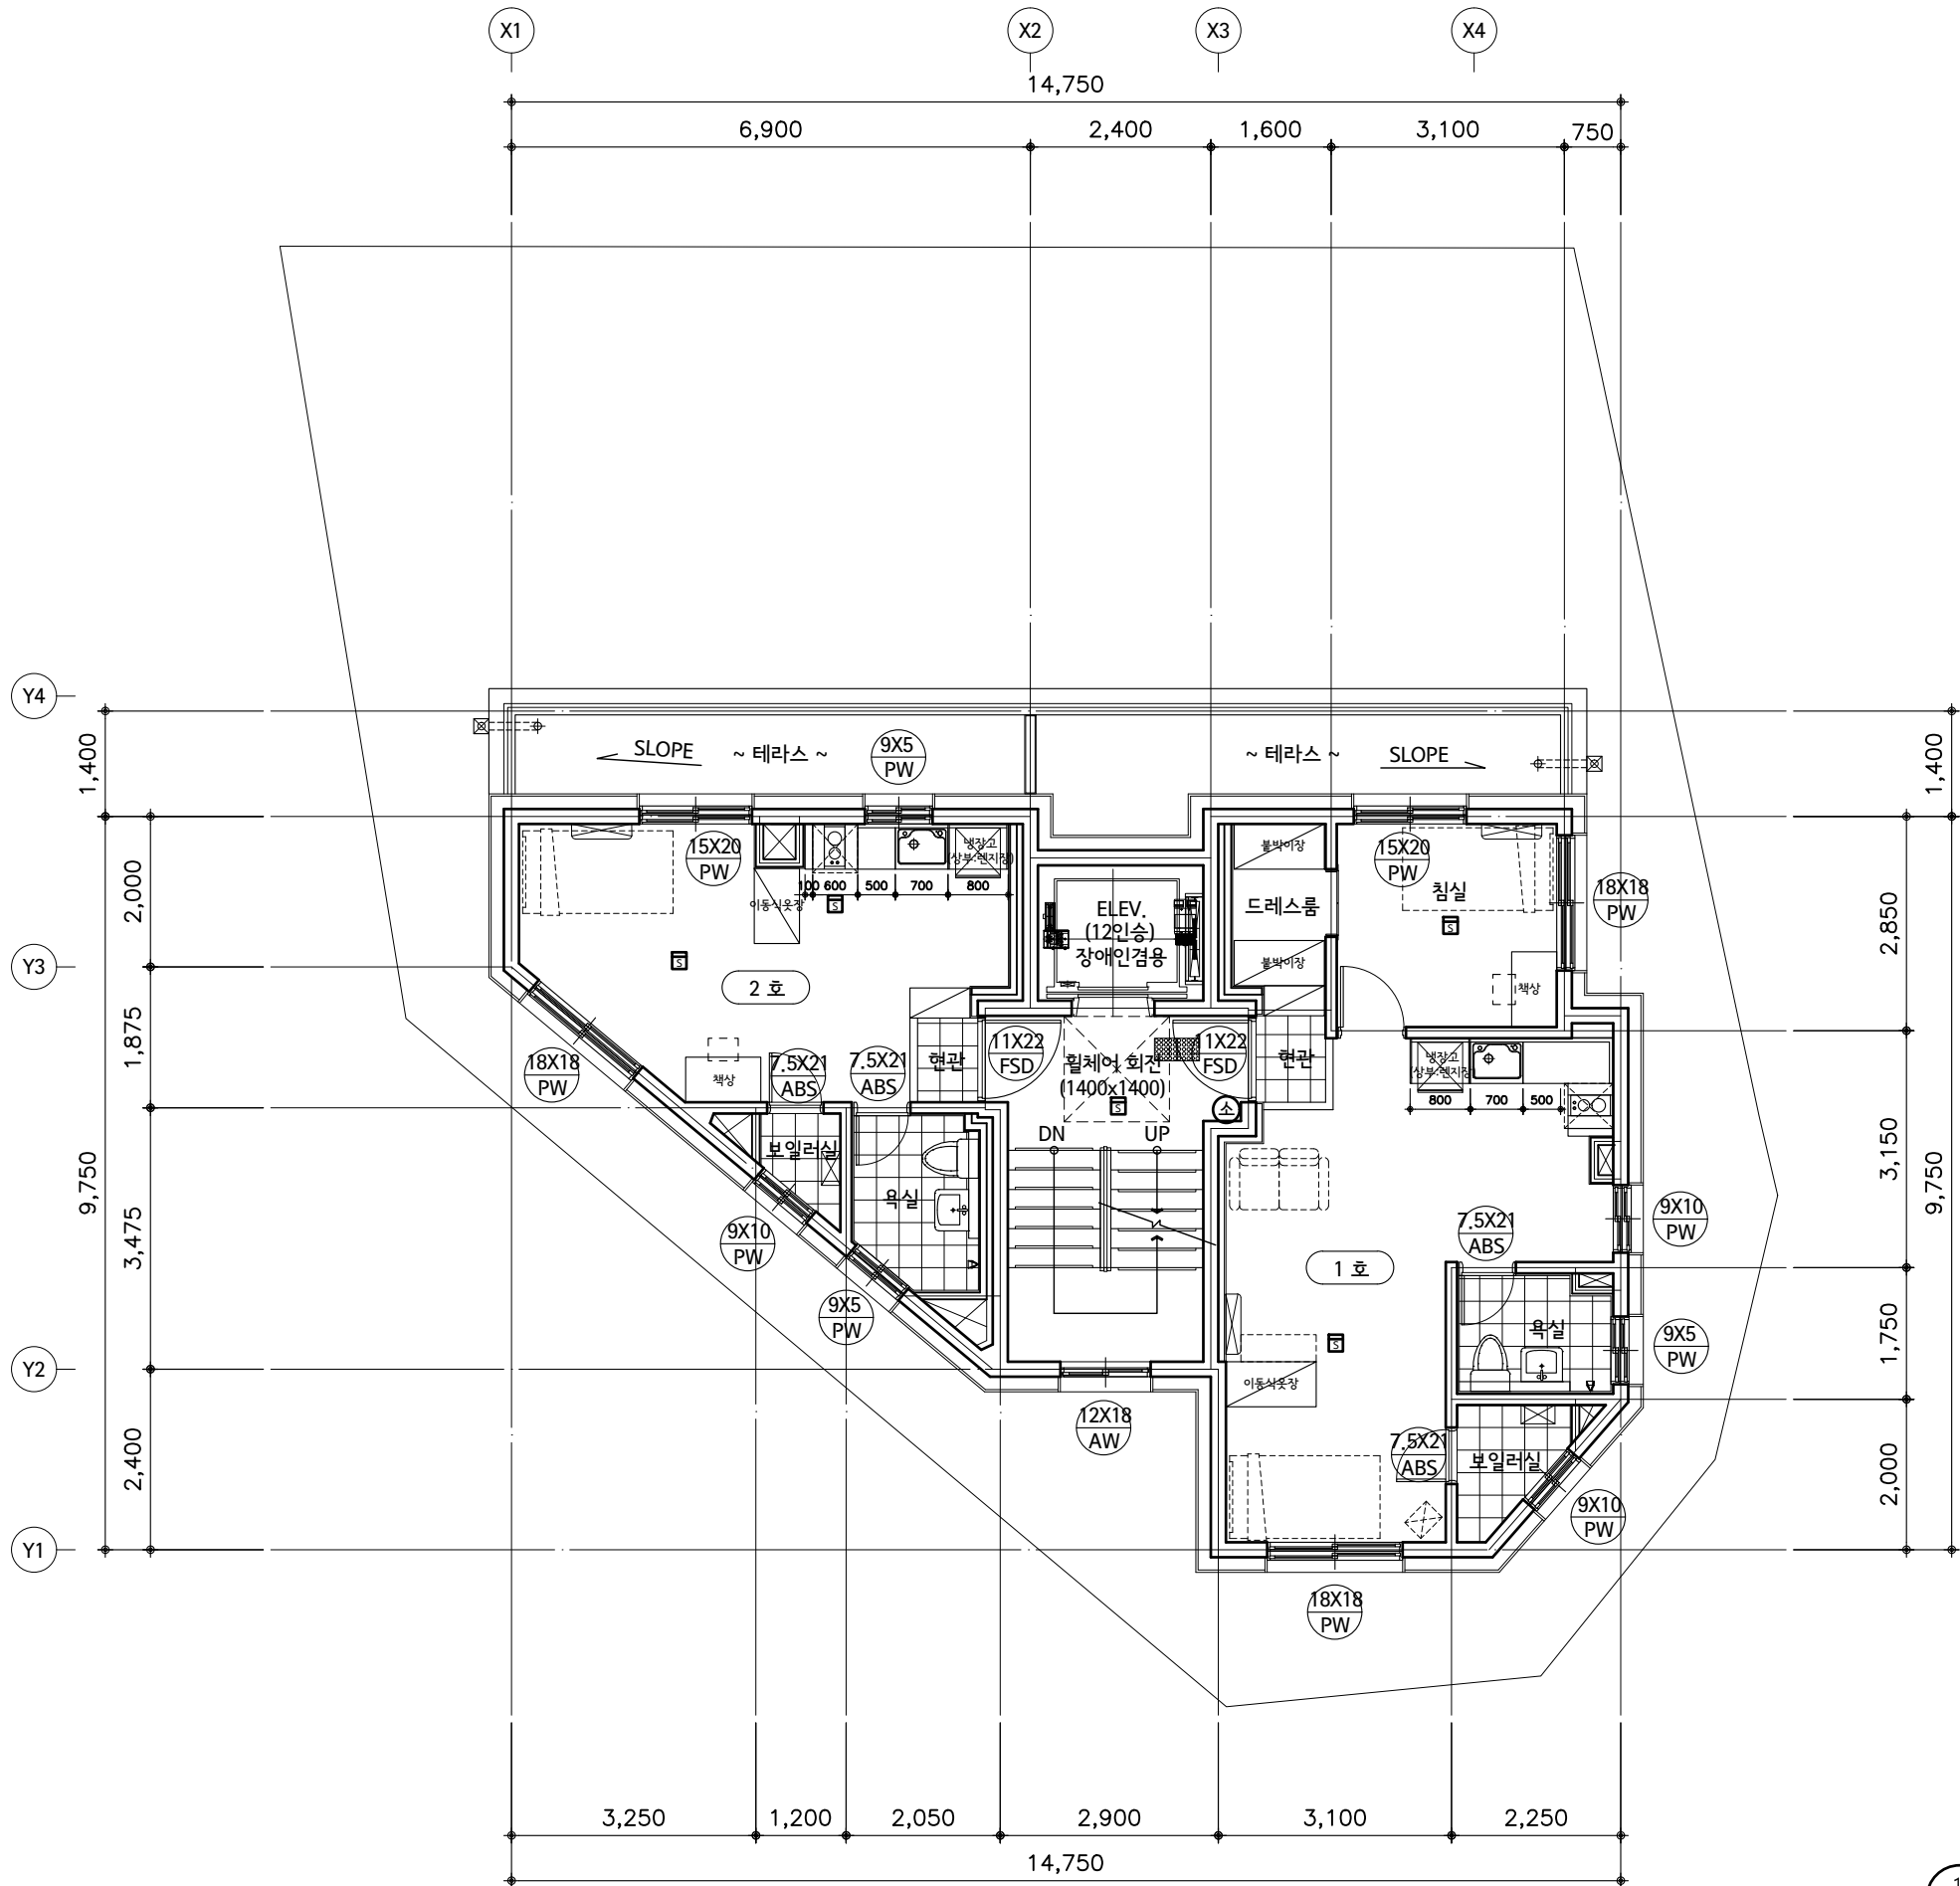


1
A 지상5층 평면도
축척 A3 : 1/100

신림동 537-14
다세대주택 신축공사

설 계 코드
PROJECT CODE

주 기 사 항
NOTE

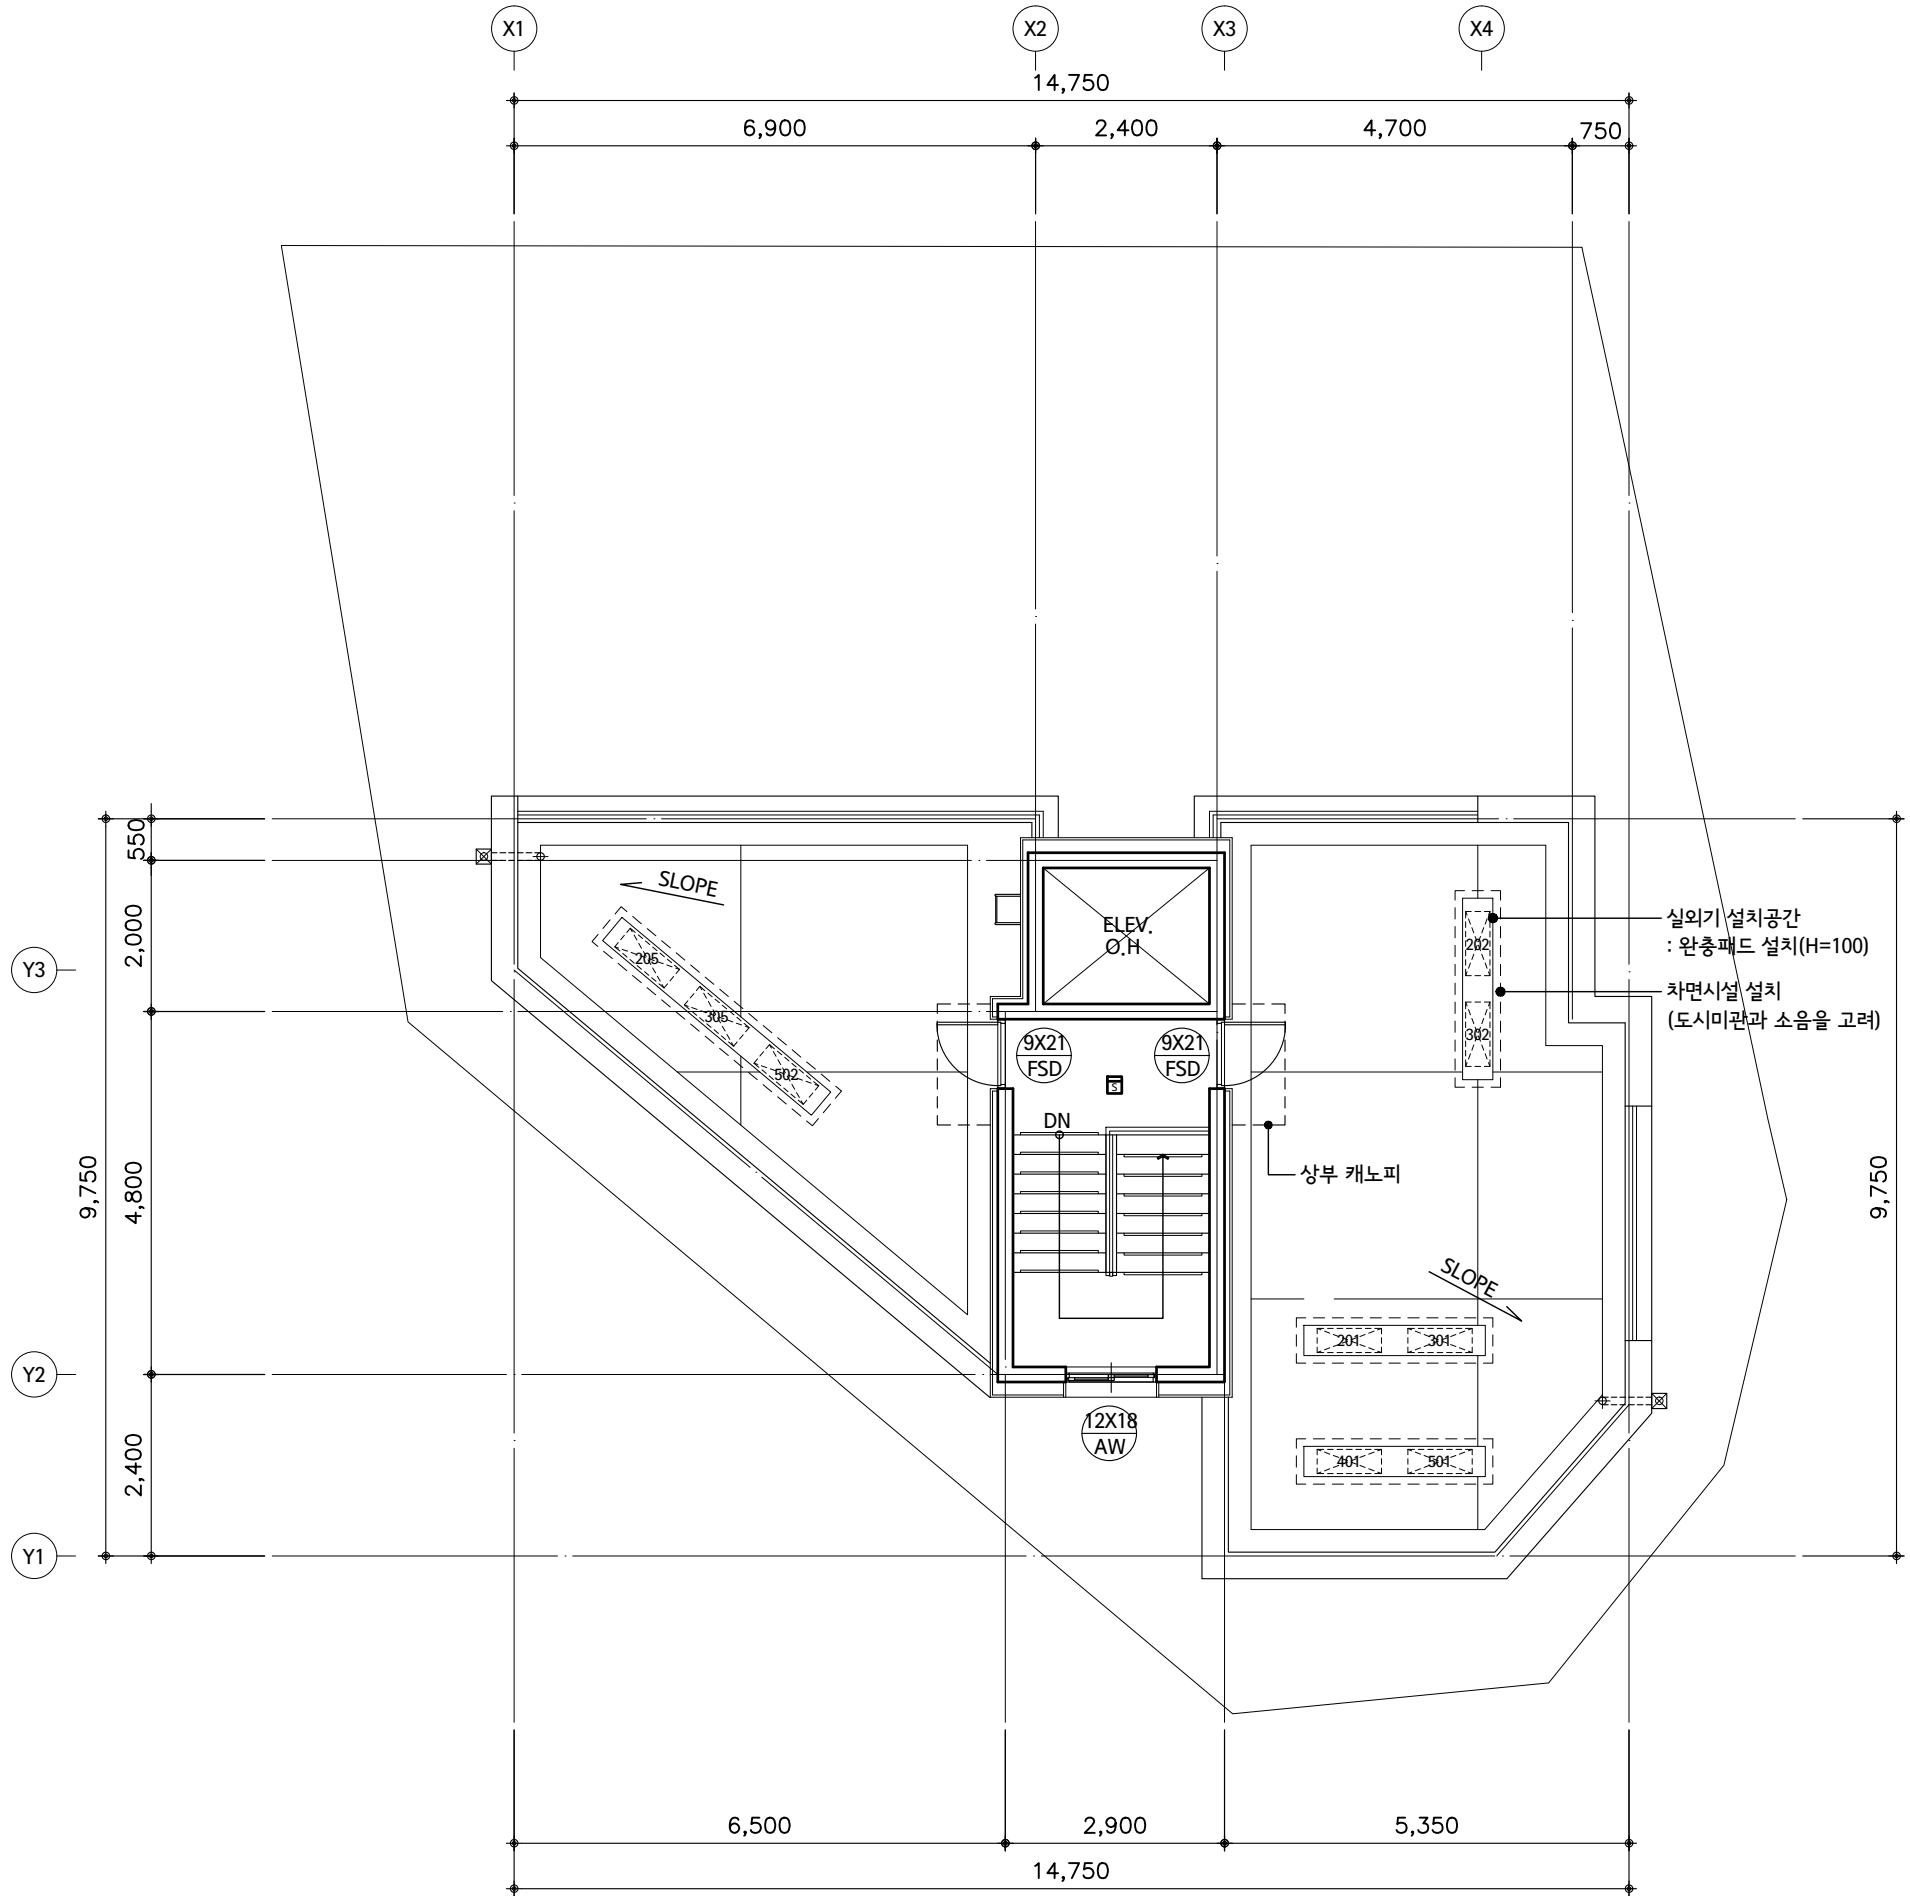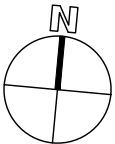

2 옥탑지붕 평면도
축척 A3 : 1/100

1 지붕 평면도
축척 A3 : 1/100

단 계
ISSUED FOR

날 짜
DATE

2023. 03.

축 척
SCALE

A1

1/

A3

1/ 100

도 면 명
DRAWING TITLE

지붕 및 옥탑평면도

SIGUN 시건 건축사사무소
SIGUN ARCHITECTURE & PLANNER
TEL: 070-4772-9090, E: sigunarch@naver.com

도 면 번 호
DRAWING NO

A - 205

신림동 537-14
다세대주택 신축공사

설 계 코드
PROJECT CODE

주 기 사 항
NOTE

1. 투시형난간
- 난간살 간격: 100mm 이하

단 계
ISSUED FOR

날 짜
DATE

2023. 03.

축 척
SCALE

A1

1/

A3

1/ 100

도 면 명
DRAWING TITLE



입면도-1 (정면도)

SIGUN 시건 건축사사무소
SIGUN ARCHITECTURE & PLANNER
TEL: 070-4772-9090, E: sigunarch@naver.com

도 면 번호
DRAWING NO


A - 301

KEY-PLAN

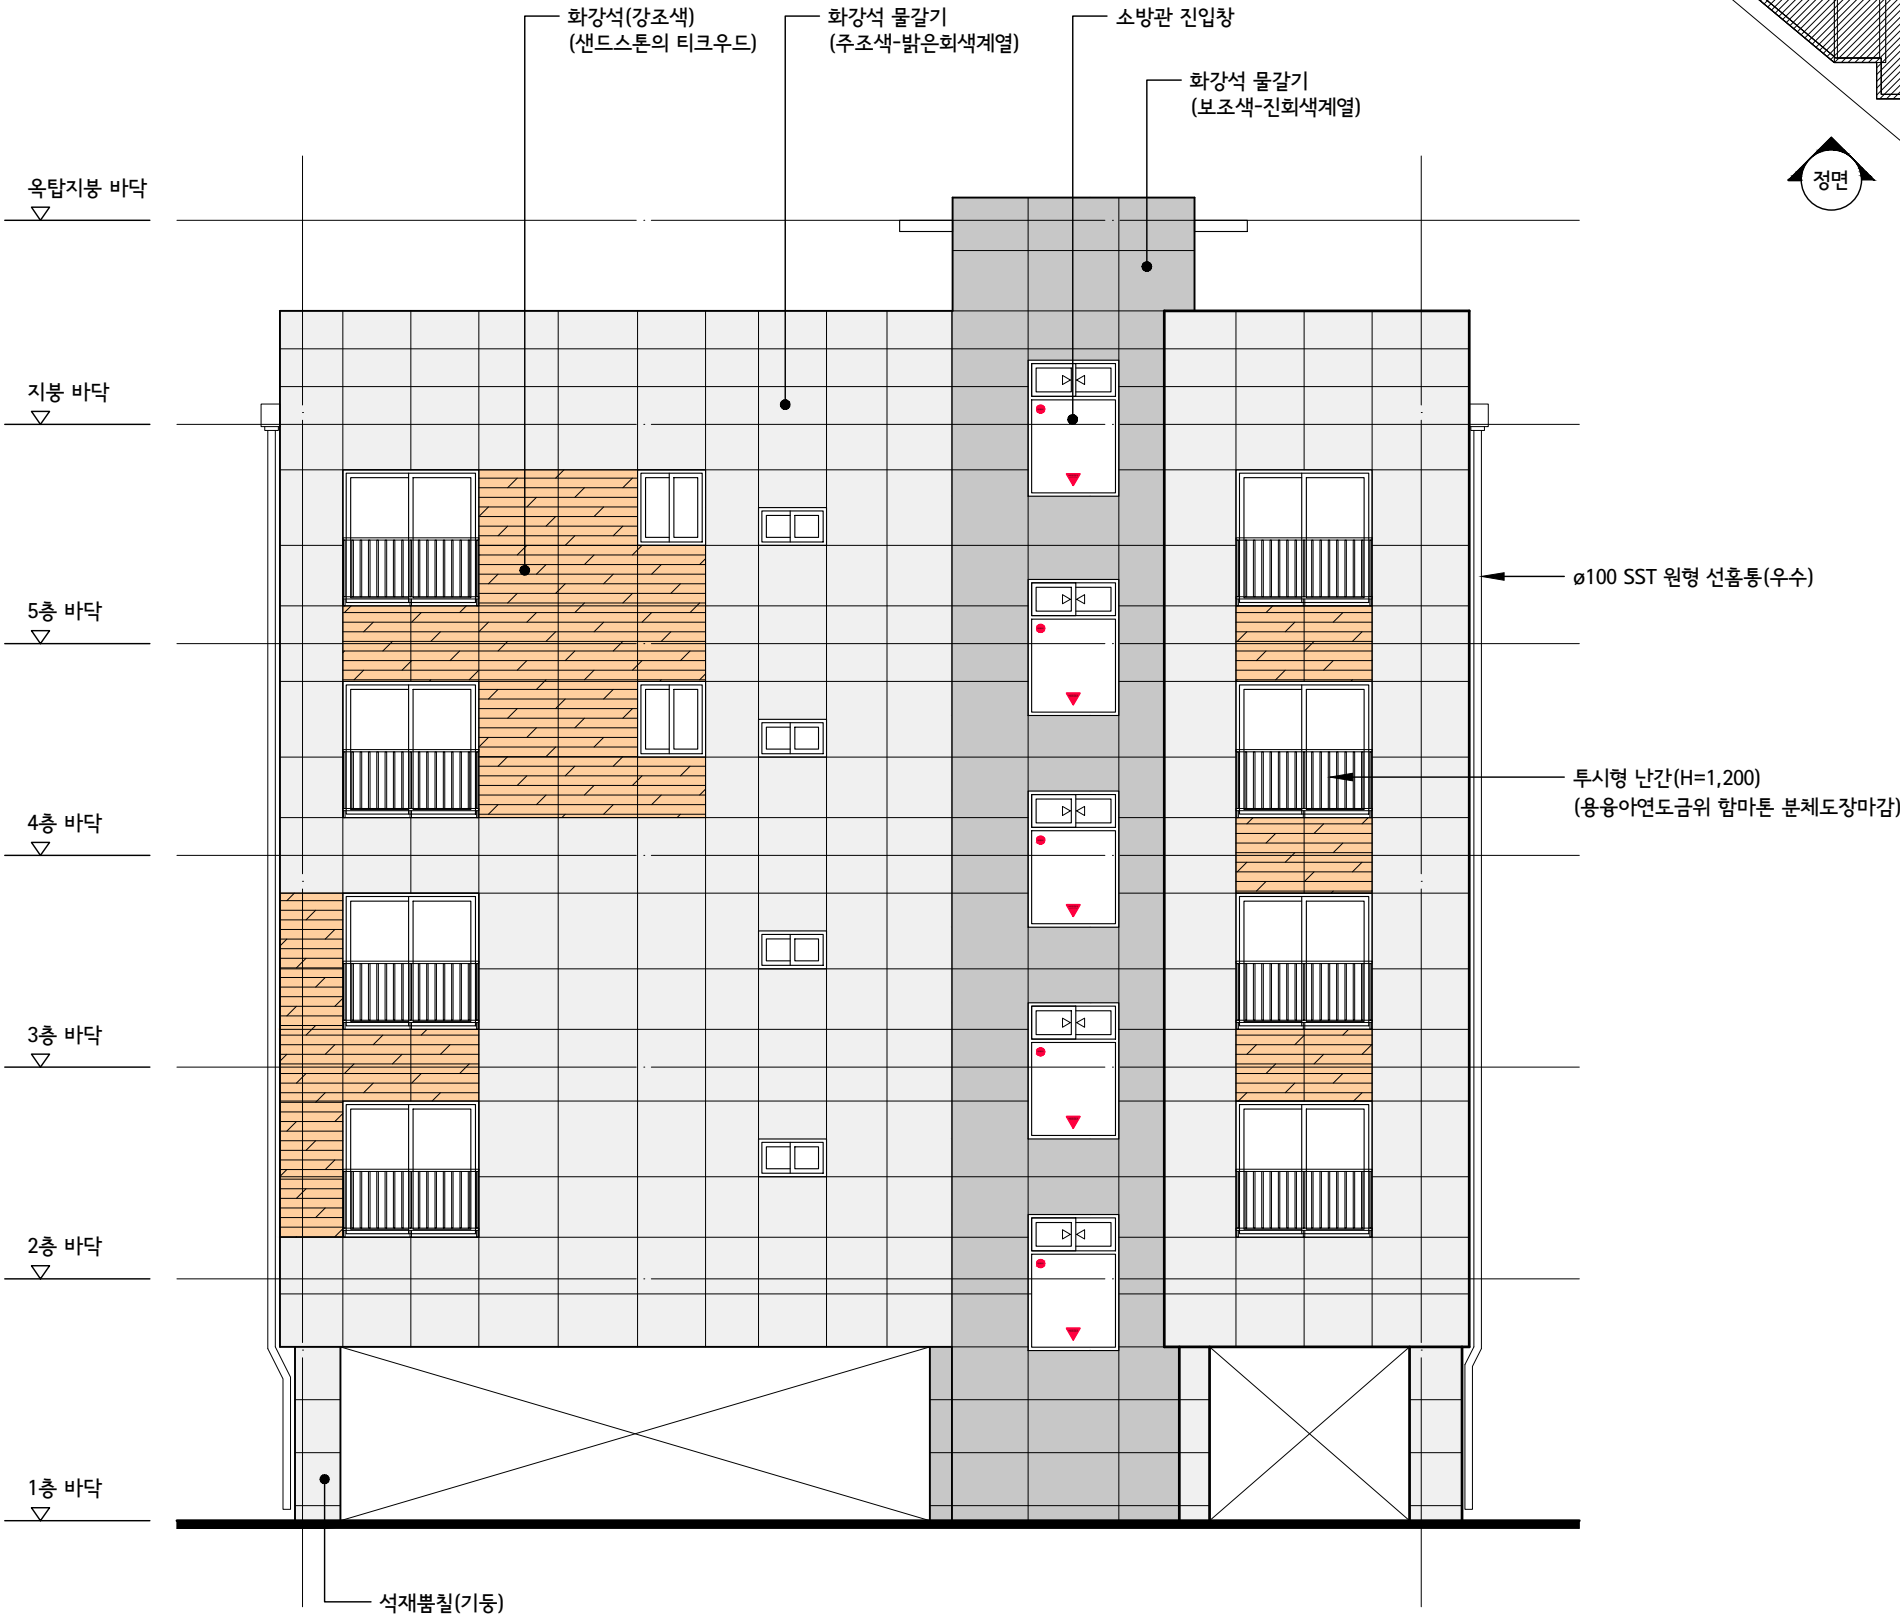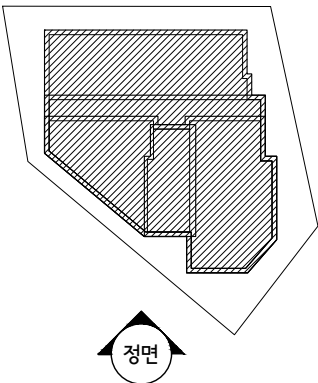

정 면 도
축척 A3 : 1/100

KEY-PLAN

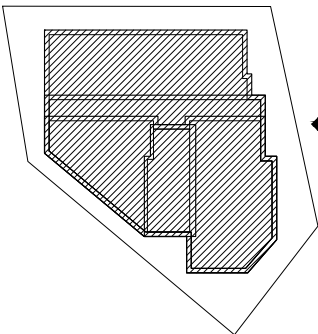

신림동 537-14
다세대주택 신축공사

설 계 코 드
PROJECT CODE

주 기 사 항
NOTE

1. 투시형난간
- 난간살 간격: 100mm 이하

단 계
ISSUED FOR

날 짜
DATE

2023. 03.

축 척
SCALE

A1

1/

A3

1/ 100


도 면 명
DRAWING TITLE

입면도-2 (우측면도)

SIGUN 시건 건축사사무소
SIGUN ARCHITECTURE & PLANNER
TEL: 070-4772-9090, E: sigunarch@naver.com

도 면 번 호
DRAWING NO

A - 302

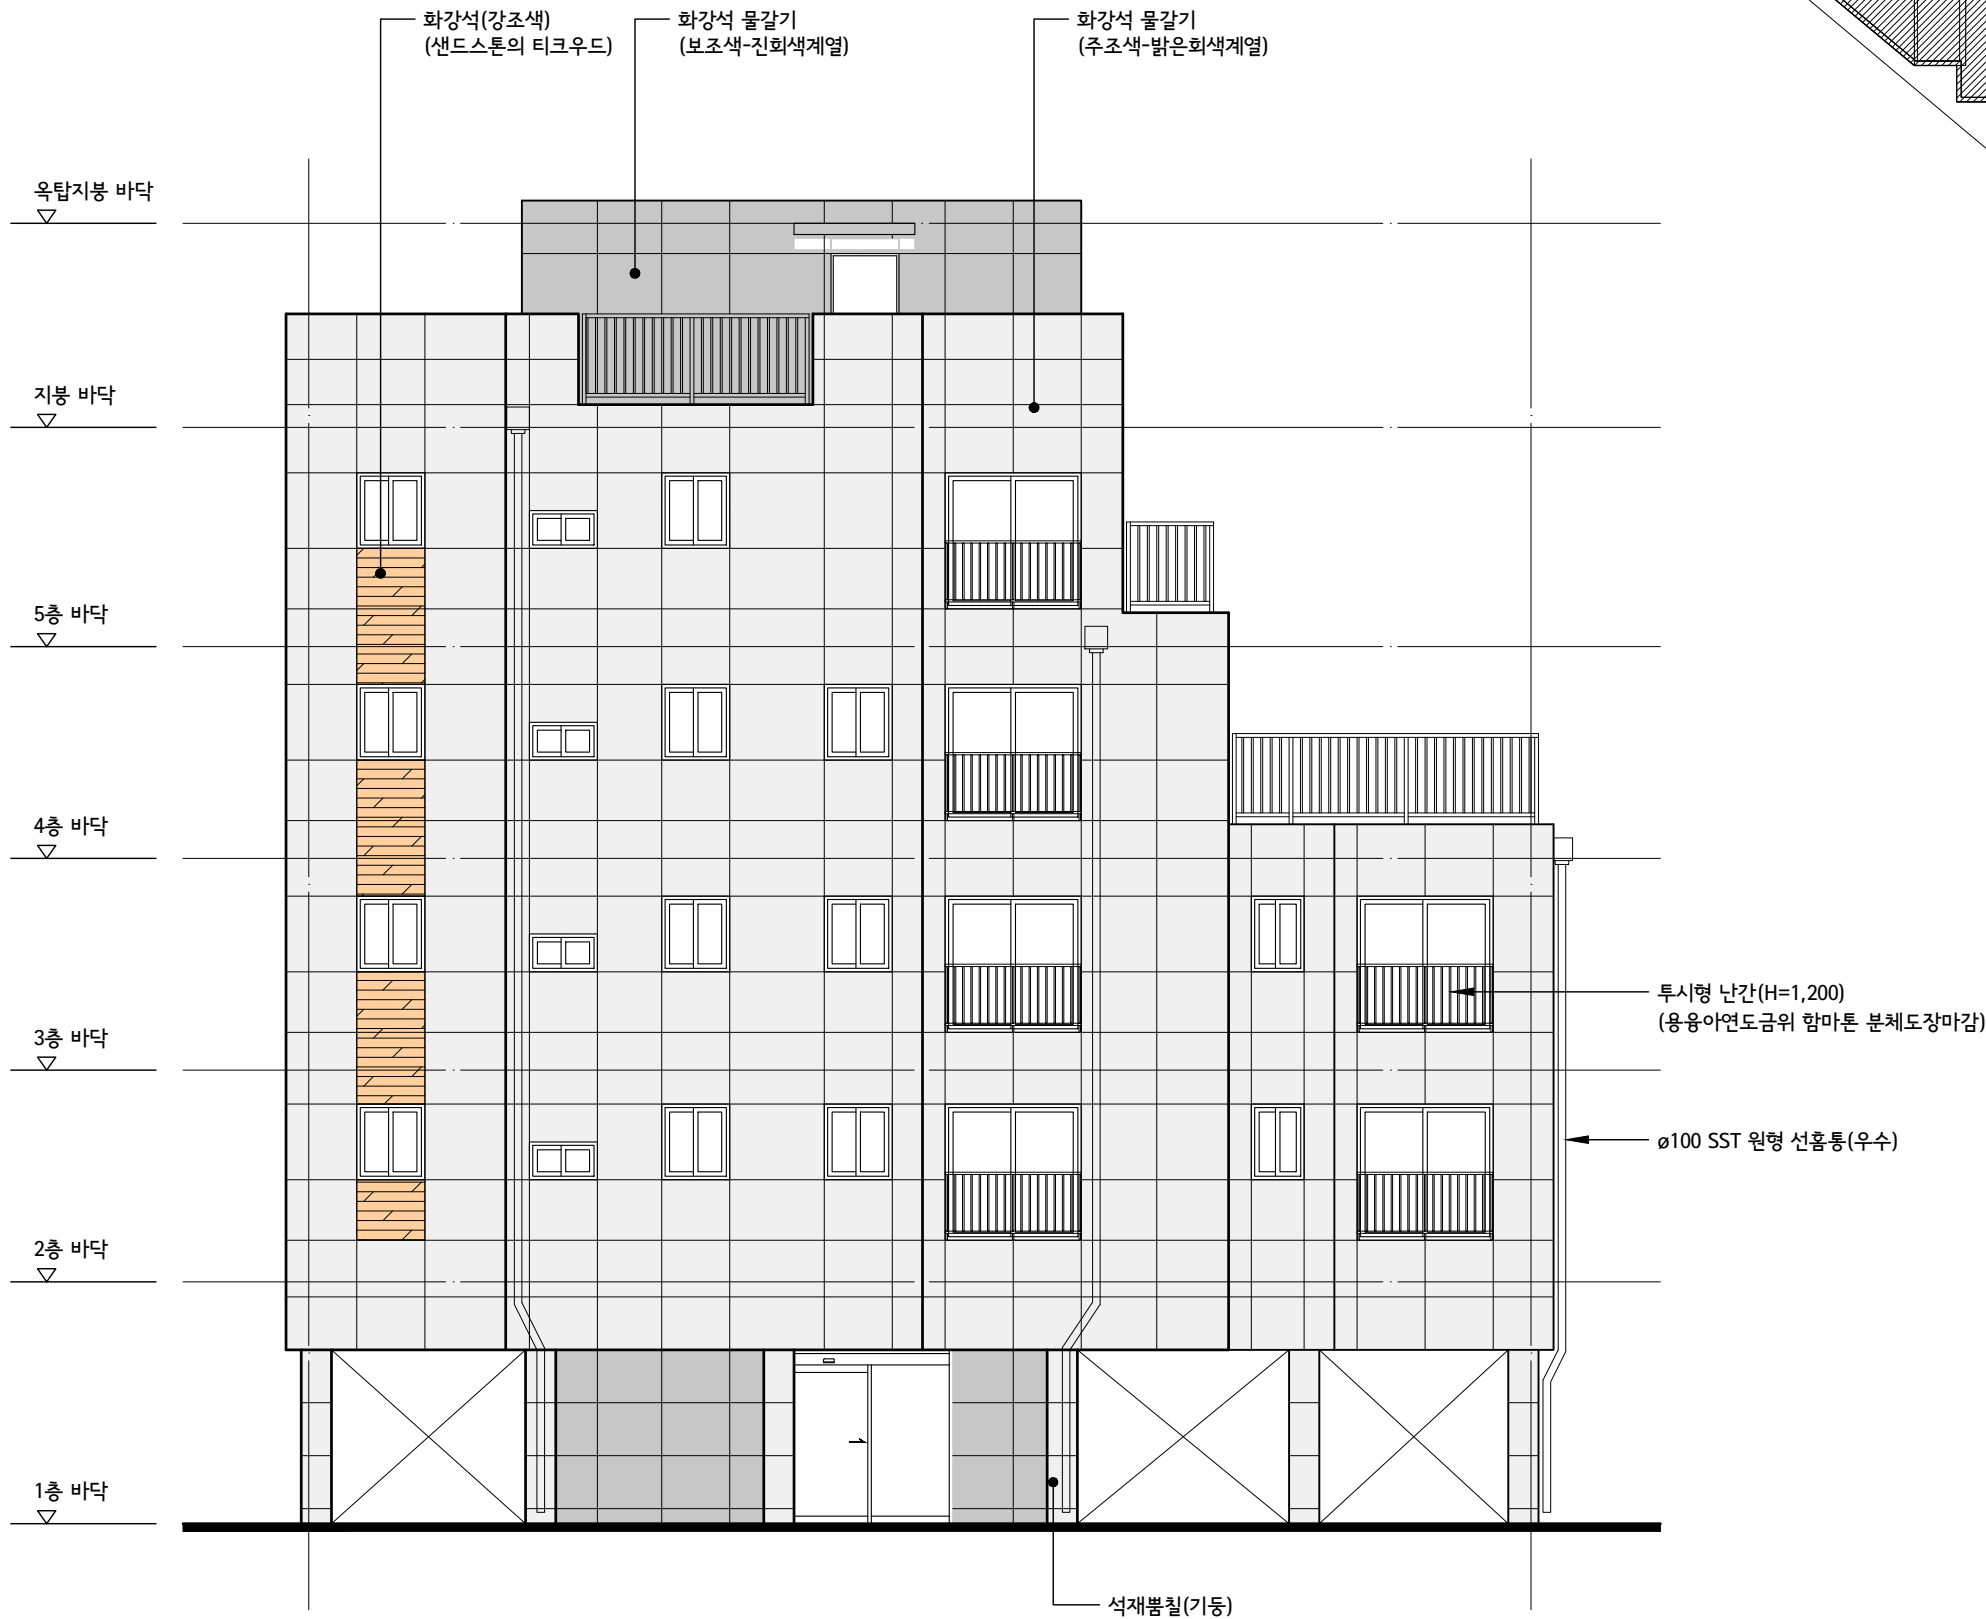

우 측 면 도

축척

A3 : 1/100

신림동 537-14
다세대주택 신축공사

설 계 코드
PROJECT CODE

주 기 사 항
NOTE

1. 투시형난간
- 난간살 간격: 100mm 이하

단 계
ISSUED FOR

날 짜
DATE

2023. 03.

축 척
SCALE

A1

1/

A3

1/ 100

도 면 명
DRAWING TITLE

입면도-3 (배면도,좌측면도)

SIGUN 시건 건축사사무소
SIGUN ARCHITECTURE & PLANNER
TEL: 070-4772-9090, E: sigunarch@naver.com

도 면 번호
DRAWING NO

A - 303

KEY-PLAN

배면

좌측면

정면도

옥탑지붕 바닥

지붕 바닥

5층 바닥

4층 바닥

투시형 난간(H=1,200)
(용융아연도금위 합마톤 분체도장마감)
3층 바닥

ø100 SST 원형 선홈통(우수)

2층 바닥

1층 바닥

화강석 물갈기
(주조색-밝은회색계열)

화강석(강조색)
(샌드스톤의 티크우드)

석재봄칠(기동)

석재봄칠(기동)

배 면 도

축척

A3 : 1/100

좌 측 면 도

축척

A3 : 1/100