


1. 조감도




2. 건축개요 및 현황도

대 지 위 치	서울특별시 관악구 신림동 1649-11호 외 1필지		
대 지 면 적	1649-11호	1649-12호	합계: 258.20 [㎡]
	133.70 [㎡]	124.50 [㎡]	
지 역 , 지 구	제3종일반주거지역		
용 적 륜	법 정	250.00 %	
	계 획	243.30 %	
건 폐 율	법 정	50.00 %	
	계 획	49.97 %	
건 축 면 적	129.03 M2		
용적률산정연면적	628.21 M2		
연 면 적	659.70 M2		
최 고 높 이	18.75 M		
건 축 규 모	지상 6층		
용 도	다세대주택-도시형생활주택(단지형다세대주택)-15세대		
조 경 면 적	법 정	258,20㎡ x 5.0% = 12.91㎡	
	계 획	17.48㎡ (6.77 %)	
정 화 조	법 정	(5세대 X 3.2 인)+(10세대 X 2.7 인) = 43.00인	
	계 획	부패탱크식 50인조	
주 차 대 수	법 정	(5세대X0.8대 + 10세대X0.3대) = 7대 = 공공주택 특별법 제43조5항 및 동법 시행령 제37조4항에 의거하여 세대당 30제곱미터 미만인 세대는 세대당 주차대수 기준 0.3대 적용함.	
	계 획	7대 설치	
비 고			

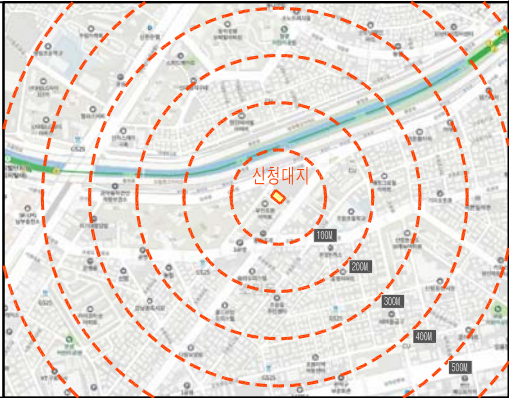


□ 위치도

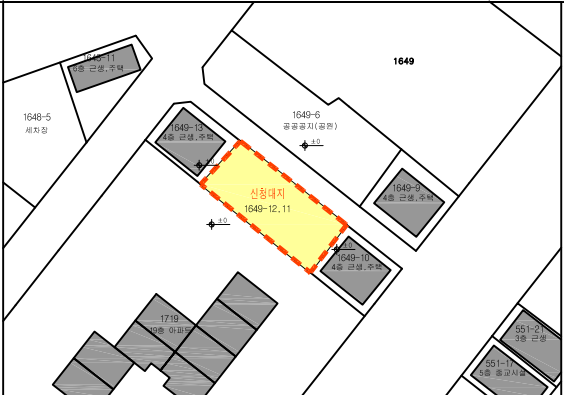

□ 주변현황도

3. 입면도

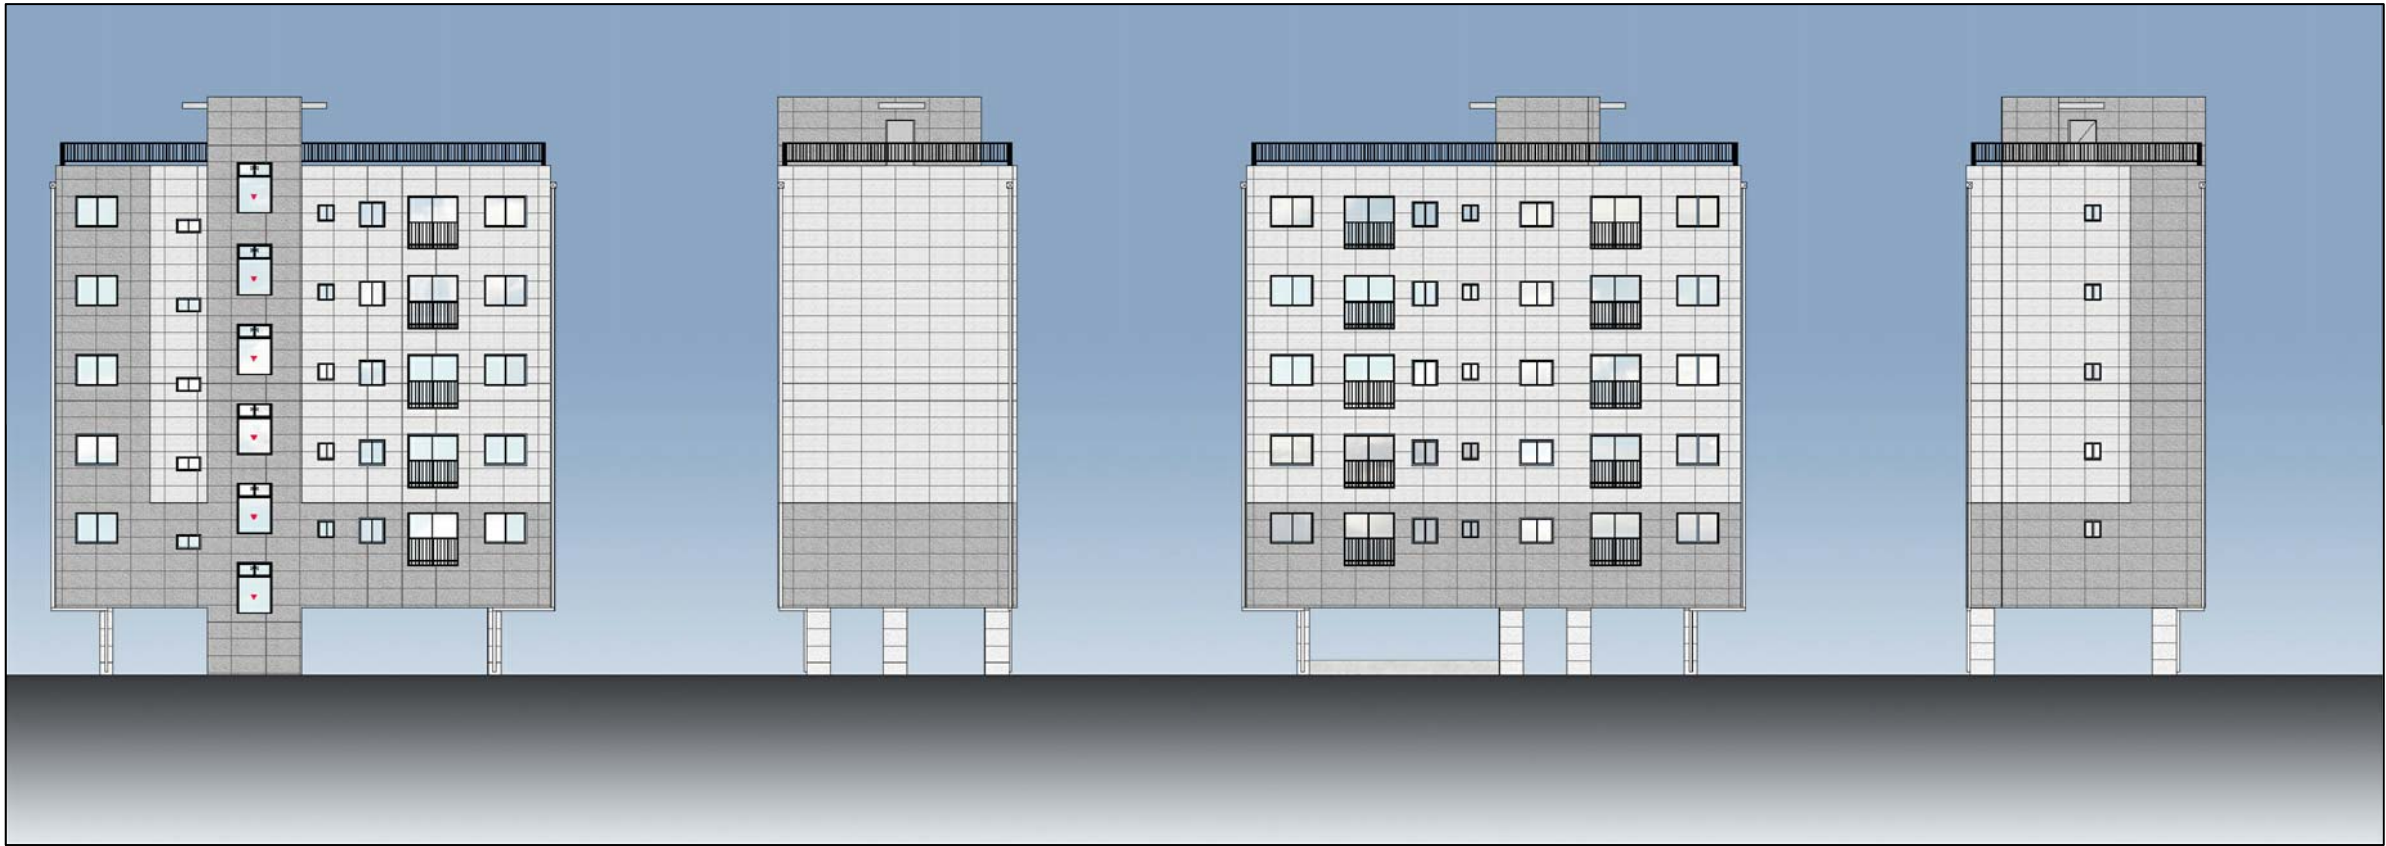

PROJECT TITLE
사 업 명 칭
관악구 신림동 1649-11호 외1필지
도시형생활주택(단지형다세대주택)
신축공사

NAME OF DRAWING
도 면 명

조감도, 입면도

NOTE
주 기

NO. ▲ REVISIONS ▲ DATE
번호 수정 일자

DESIGNED BY
설 계

CHECKED BY
심 사

APPROVED BY
승 인

CONSULTANTS
협 동 설 계

SCALE
축 측

DATE
일 자 2022. 08.

DWG NO.
도면 번호 A-02


SHEET NO.
일련 번호 □—□□□

**다움건축**
daumoo
건축사사무소 다움건축
THE ARCHITECTS DESIGN GROUP
TEL. 02.414.6061 (代)
FAX. 02.414.6062

4. 설계자 의도

■ 디자인 의도

- 보행자, 차량 출입의 원활한 계획
- 도로측에 순응한 주동 배치
- 정면성을 강조하는 디자인 계획

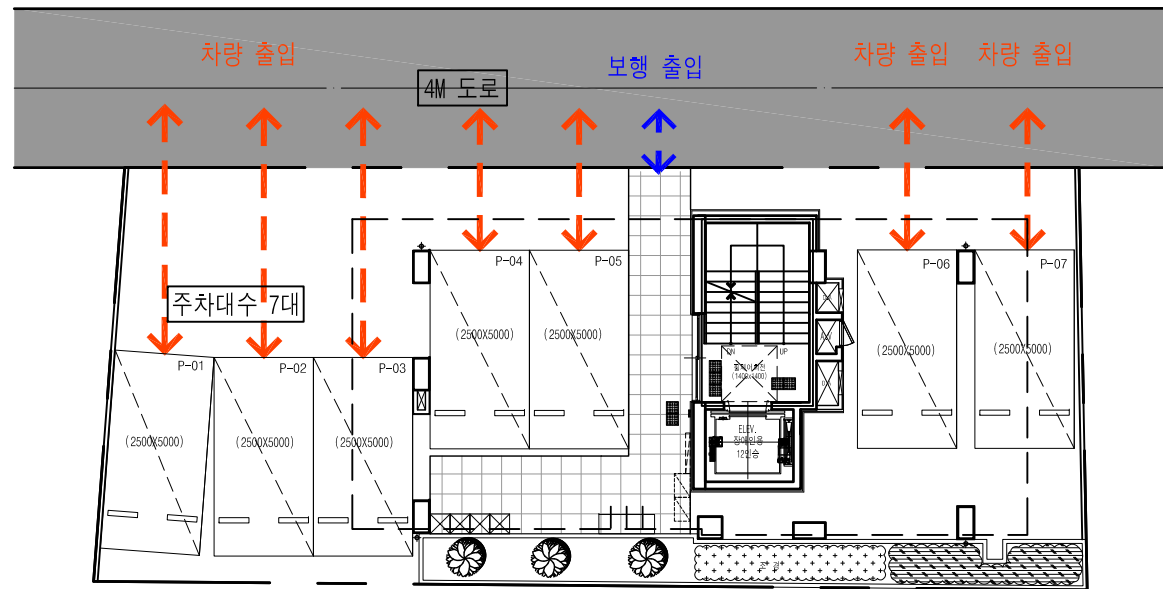

■ 입면 디자인 계획 (정면성 강조)

- 창호크기 및 열을 맞추어 입면에 정돈된 이미지를 부여함.


정면에 면분할을 통해 단정함과 균일성을 부여하고 정면성 강조함.

창호크기 및 열을 맞추어 입면에 정돈된 이미지를 부여함.



5. 재료계획

1. 외벽 마감재

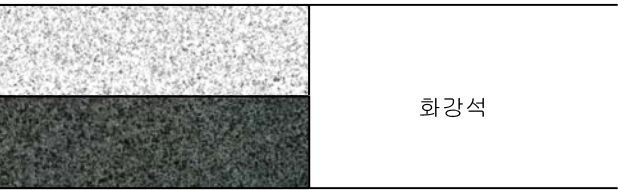

2. 주차장 바닥재



3. 옥외 난간재



□ 외장재

구분	실명	재료명
1층	필로티 주차장	바닥 : 칼라 콘크리트
		천정 : AL 천정판
2~5층	현관	바닥 : 화강석 마감
	방	바닥 : 데코타일 마감 천정 : 천정지
	거실	바닥 : 데코타일 마감 천정 : 천정지
	베란다	바닥 : 석재타일 천정 : 무기질계 도막방수

□ 내장재

6. 색채계획

- ☐ 자연스러운 색상과 주변과의 조화
- ☐ 무채색 위주의 색상 활용으로 주변과 어울리는 건물계획
- ☐ 가로경관 미관성 및 친근성



PROJECT TITLE
사업명칭

관악구 신림동 1649-11호 외1필지
도시형생활주택(단지형다세대주택)
신축공사

NAME OF DRAWING
도면명

디자인 의도, 재료계획
색채 계획도

NOTE
주 기

▼ ▼

NO. ▲ REVISIONS ▲ DATE
번호 수 일 자

DESIGNED BY
설 계

CHECKED BY
심 사

APPROVED BY
승 인

CONSULTANTS
협동설계

SCALE
축척

DATE
일 자

2023. 04.

DWG NO.
도면 번호



A-03

SHEET NO.
일련 번호

□-□□□

dawoom
건축사사무소 다움건축

THE ARCHITECTS DESIGN GROUP
TEL. 02.414.6061 (代)
FAX. 02.414.6062

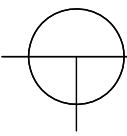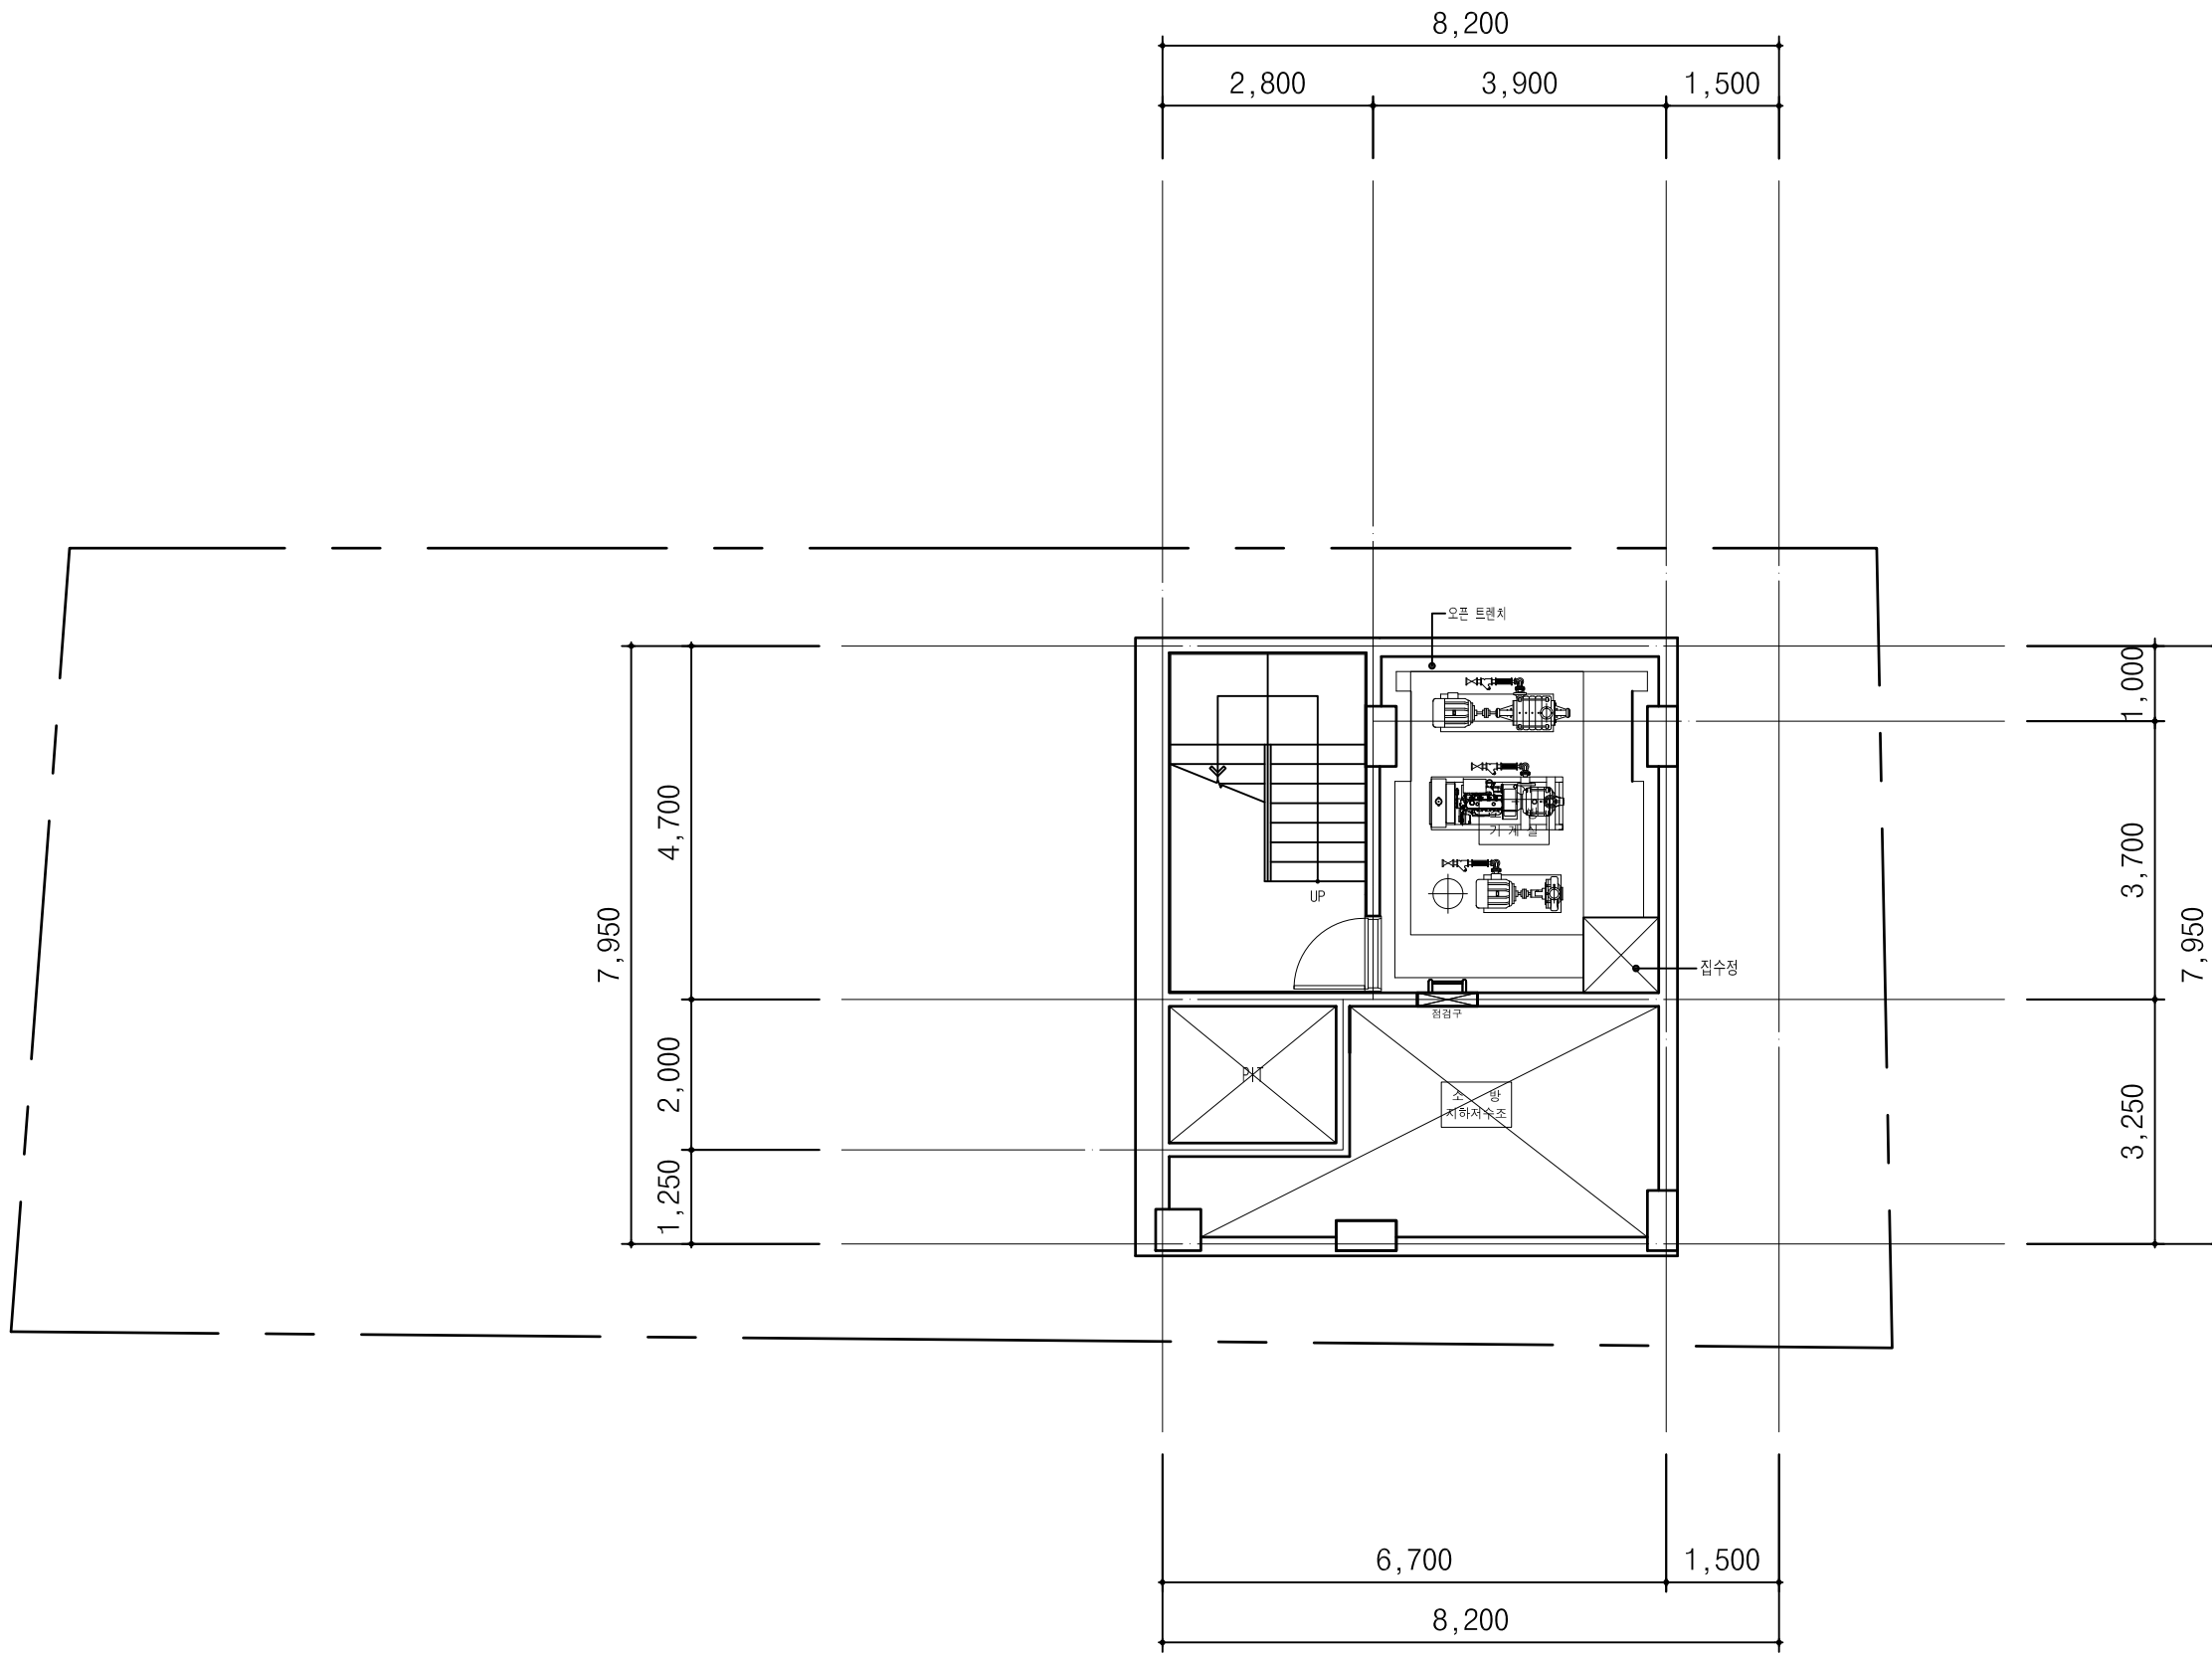

지하1층 평면도
SCALE : A3 : 1/100

PROJECT TITLE
사 업 명 칭
관악구 신림동 1649-11호 외1필지
도시형생활주택(단지형다세대주택)
신축공사

NAME OF DRAWING
도 면 명
지하1층 평면도

NOTE
주 기

- 단독경보감지기(연기식)
- 단독경보감지기(열감지)
- ABC분말소화기(2.5KG)
- 가스누설경보기
- 일산화탄소감지기

- 차면시설
- 보일러
- 에어컨 실외기

- * 구 조 *
- 1. 콘크리트: fck = 24 MPa
- 2. 철근: fy = 400 MPa
- 3. 세대간벽두께: 180mm(복배근)
(미장마감포함 210mm이상)
- 4. 외벽두께: 180mm(복배근)
- 5. 코아벽두께: 180mm(복배근)
- 6. 슬라브두께: 210mm(복배근)

NO. REVISIONS DATE
번호 수 일 자

DESIGNED BY
설 계

CHECKED BY
심 사

APPROVED BY
승 인

CONSULTANTS
협 동 설 계




SCALE
축 측

DATE
일 자 2023. 04.

DWG NO.
도면 번호 A-21

SHEET NO.
일련 번호

DAWOO
daewoom
건축사사무소 다움건축
THE ARCHITECTS DESIGN GROUP
TEL. 02.414.6061 (代)
FAX. 02.414.6062

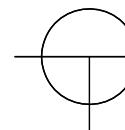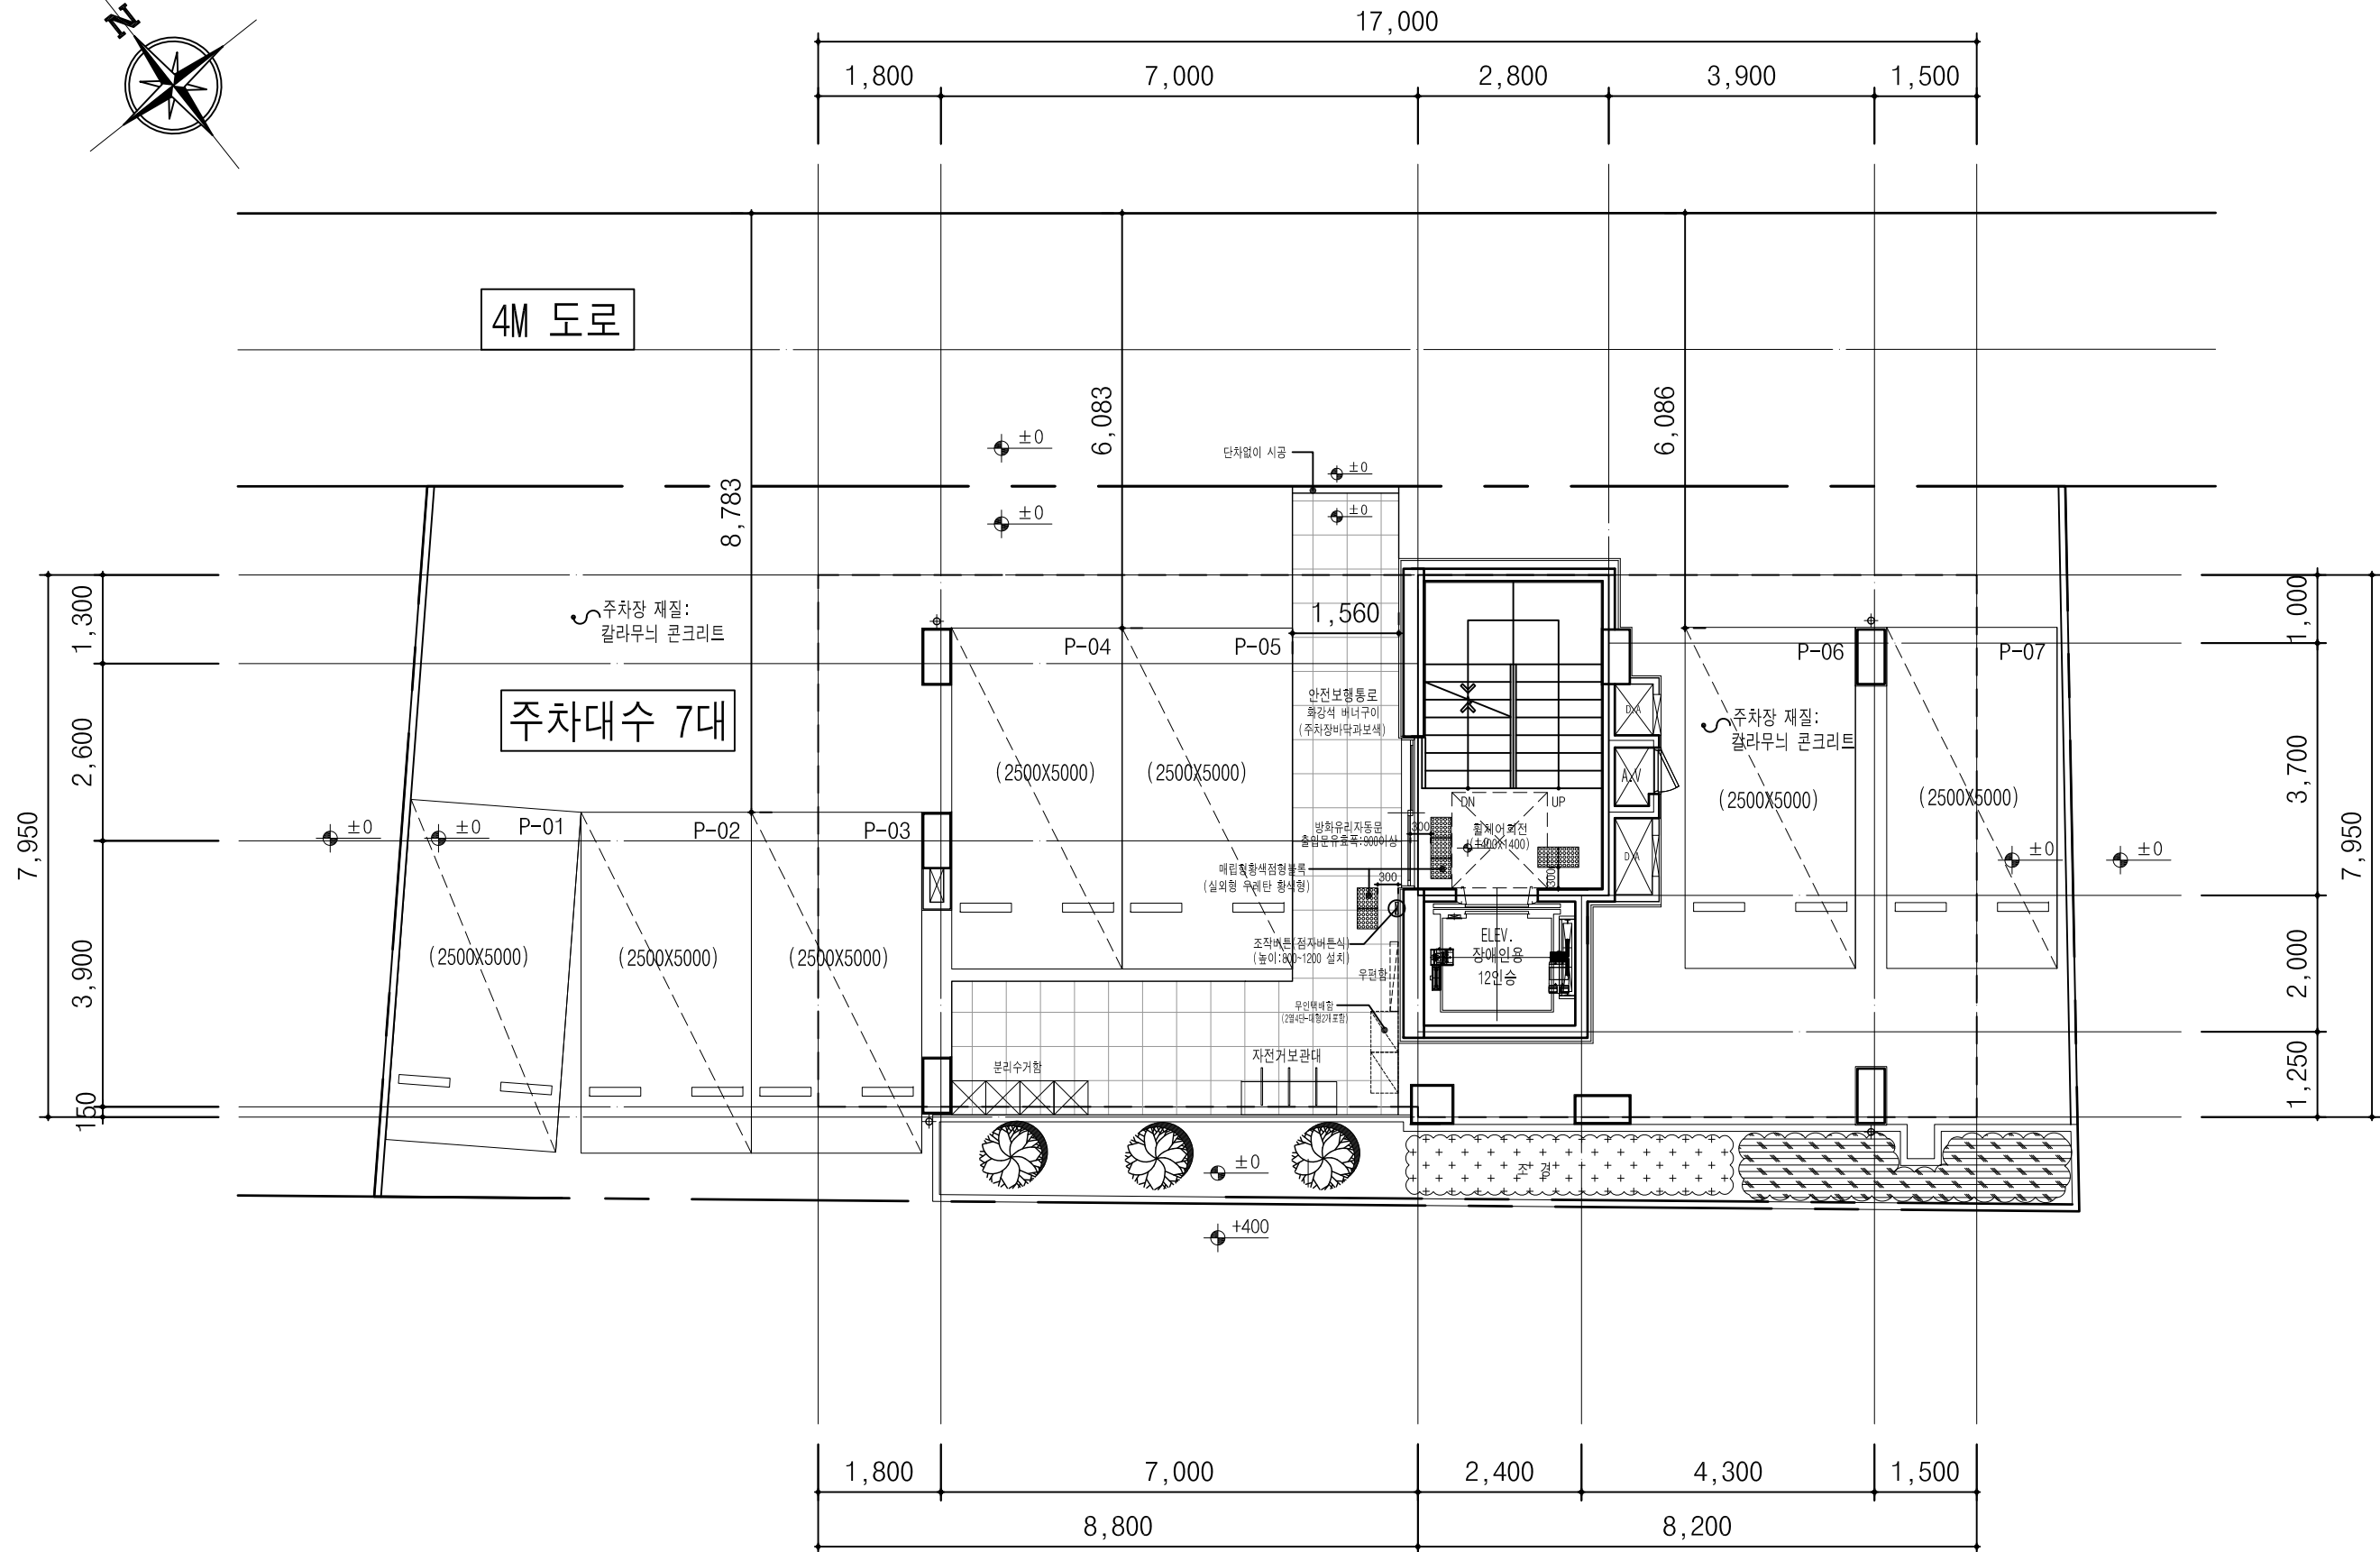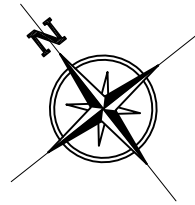

1 층 평면도

SCALE : A3 : 1/100

PROJECT TITLE
사업명칭
관악구 신림동 1649-11호 외1필지
도시형생활주택(단지형다세대주택)
신축공사

NAME OF DRAWING
도면명
1 층 평면도

NOTE
주 기

- 단독경보감지기(연기식)
- 단독경보감지기(열감지)
- ABC분말소화기(2.5KG)
- 가스누설경보기
- 일산화탄소감지기

- 차면시설
- 보일러
- 에어컨 실외기

* 구조 *

- 콘크리트: fck = 24 MPa
- 철근: fy = 400 MPa
- 세대간벽두께: 180mm(복배근)
(미장마감포함 210mm이상)
- 외벽두께: 180mm(복배근)
- 코아벽두께: 180mm(복배근)
- 스라브두께: 210mm(복배근)

NO. REVISIONS DATE
번호 수정 일자

DESIGNED BY
설계

CHECKED BY
심사

APPROVED BY
승인

CONSULTANTS
협동설계


SCALE
축척

DATE
일자 2023. 04.

DWG NO.
도면번호 A-22

SHEET NO.
일련번호 □-□□□


건축사사무소 다움건축
THE ARCHITECTS DESIGN GROUP
TEL. 02.414.6061 (代)
FAX. 02.414.6062

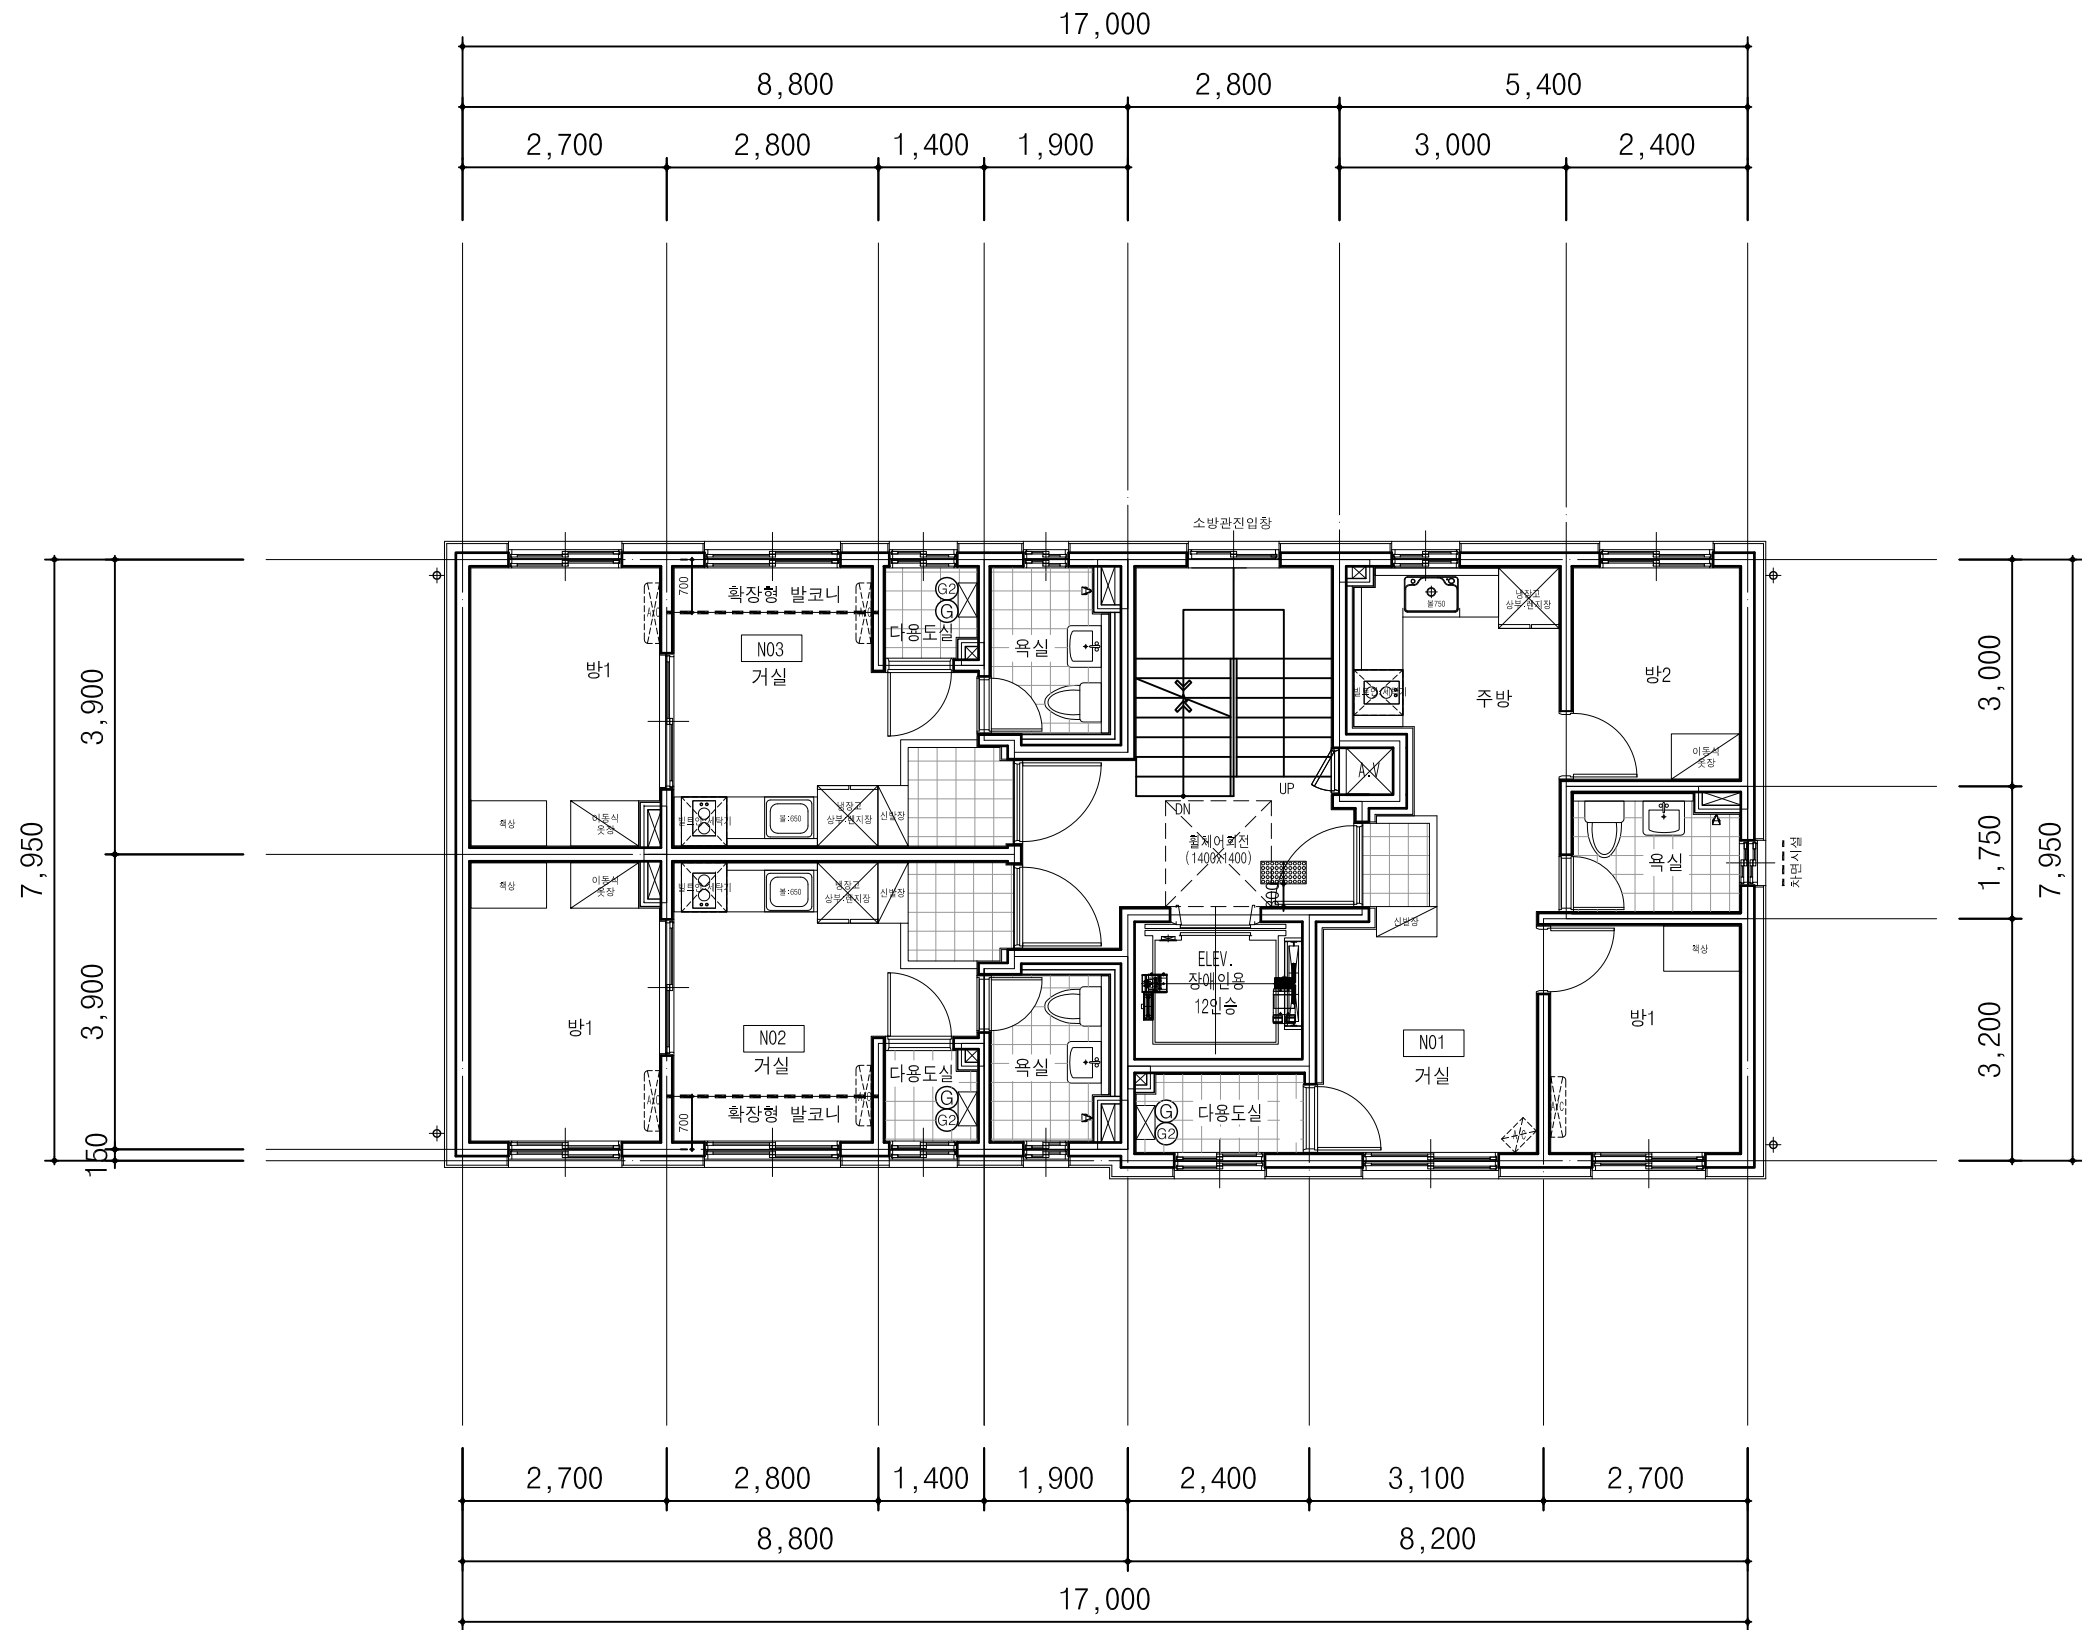

2 층 평면도
SCALE : A3 : 1/100

PROJECT TITLE
사 업 명 칭

관악구 신림동 1649-11호 외1필지
도시형생활주택(단지형다세대주택)
신축공사

NAME OF DRAWING
도 면 명

2 층 평면도

NOTE
주 기

- 3 단독경보감지기(연기식)
- 3 단독경보감지기(열감지)
- 32 ABC분말소화기(2.5KG)
- 32 가스누설경보기
- 32 일산화탄소감지기

차면시설
보일러
에어컨 실외기

- * 구 조 *
- 1.콘크리트: fck = 24 MPa
 - 2. 철근 : fy = 400 MPa
 - 3.세대간벽두께:180mm(복배근
(미장마감포함 210mm이상)
 - 4.외벽두께:180mm(복배근)
 - 5.코아벽두께:180mm(복배근)
 - 6.스라브두께:210mm(복배근)

NO. REVISIONS DATE
번호 수 장 일 자

DESIGNED BY
설 계

CHECKED BY
심 사

APPROVED BY
승 인

CONSULTANTS
협 동 설 계



SCALE
축 측

DATE
일 자 2023. 04.

DWG NO.
도면 번호 A-23

SHEET NO.
일련 번호


dawoom
건축사사무소 다움건축
THE ARCHITECTS DESIGN GROUP
TEL. 02.414.6061 (代)
FAX. 02.414.6062

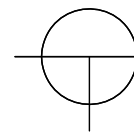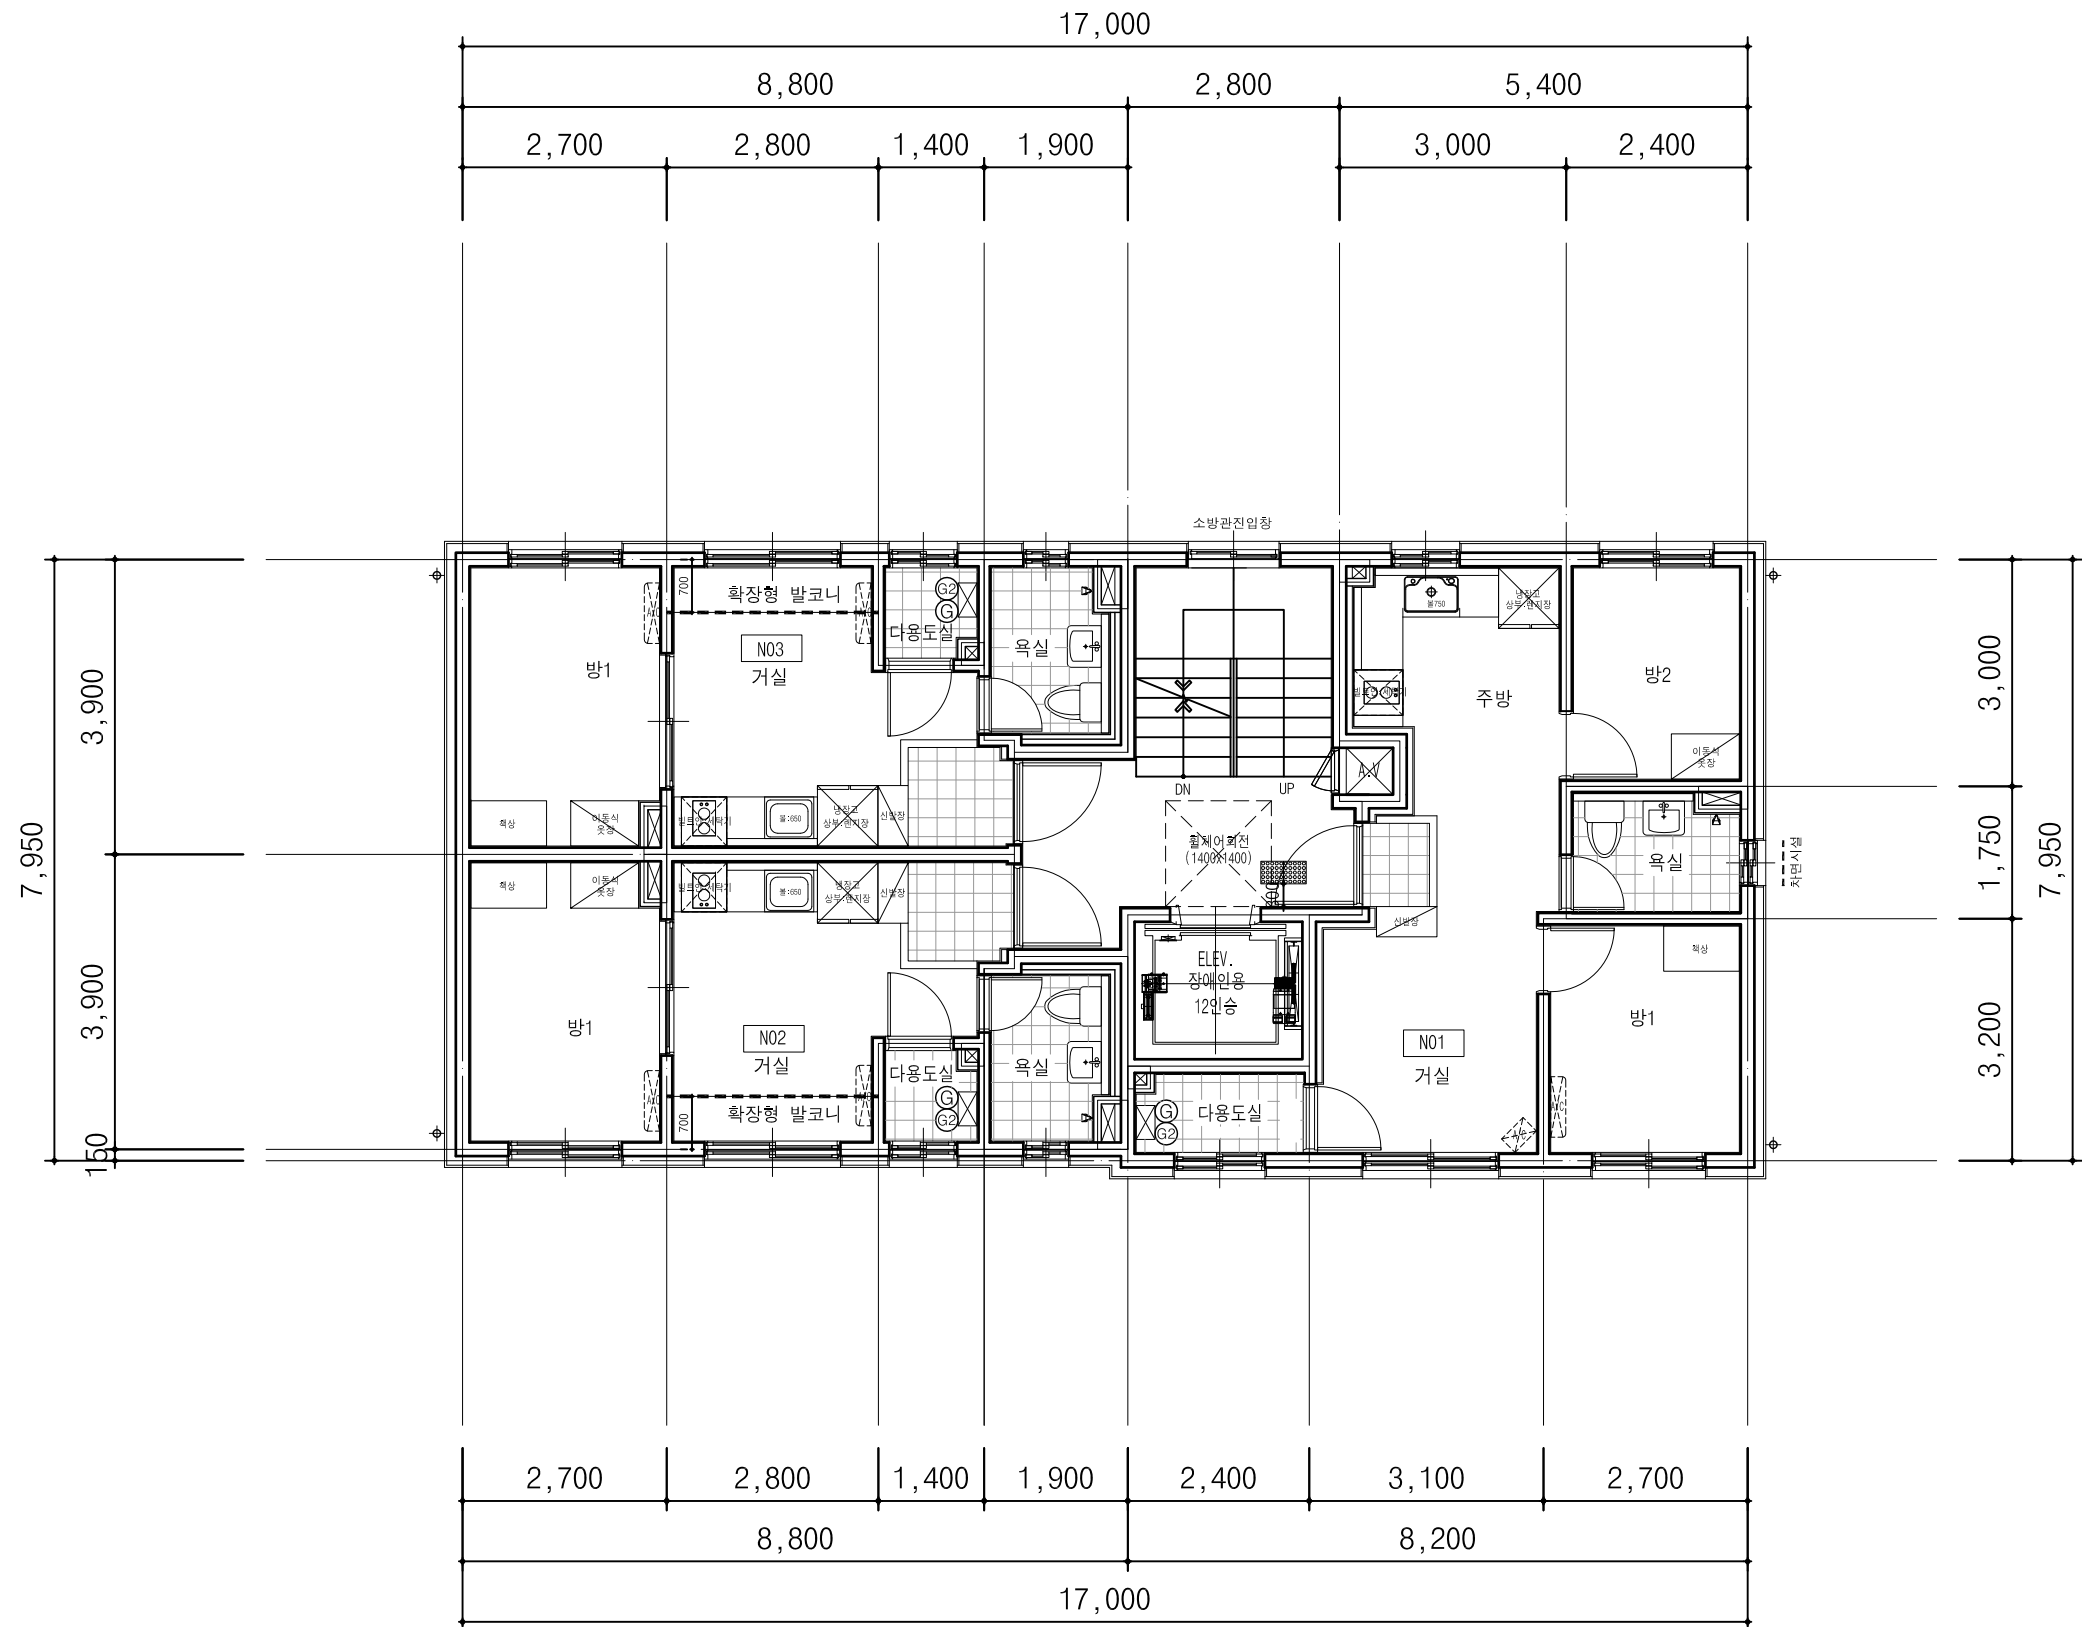

3~6 층 평면도
SCALE : A3 : 1/100

PROJECT TITLE
사 업 명 칭

관악구 신림동 1649-11호 외1필지
도시형생활주택(단지형다세대주택)
신축공사

NAME OF DRAWING
도 면 명

3-6 층 평면도

NOTE
주 기

- 3 단독경보감지기(연기식)
- 3 단독경보감지기(열감지)
- 32 ABC분말소화기(2.5KG)
- 32 가스누설경보기
- 32 일산화탄소감지기

- 차면시설
- 보일러
 - 에어컨 실외기

- * 구 조 *
- 콘크리트: fck = 24 MPa
 - 철근: fy = 400 MPa
 - 세대간벽두께: 180mm(복배근)
(미장마감포함 210mm이상)
 - 외벽두께: 180mm(복배근)
 - 코아벽두께: 180mm(복배근)
 - 스라브두께: 210mm(복배근)

NO. REVISIONS DATE
번호 수정 일자

DESIGNED BY
설 계

CHECKED BY
심 사

APPROVED BY
승 인

CONSULTANTS
협 동 설 계


SCALE
축 축

DATE
일 자 2023. 04.

DWG NO.
도면 번호 A-24



SHEET NO.
일련 번호 □-□□□

 **dawoom**
건축사사무소 다움건축
THE ARCHITECTS DESIGN GROUP
TEL. 02.414.6061 (代)
FAX. 02.414.6062

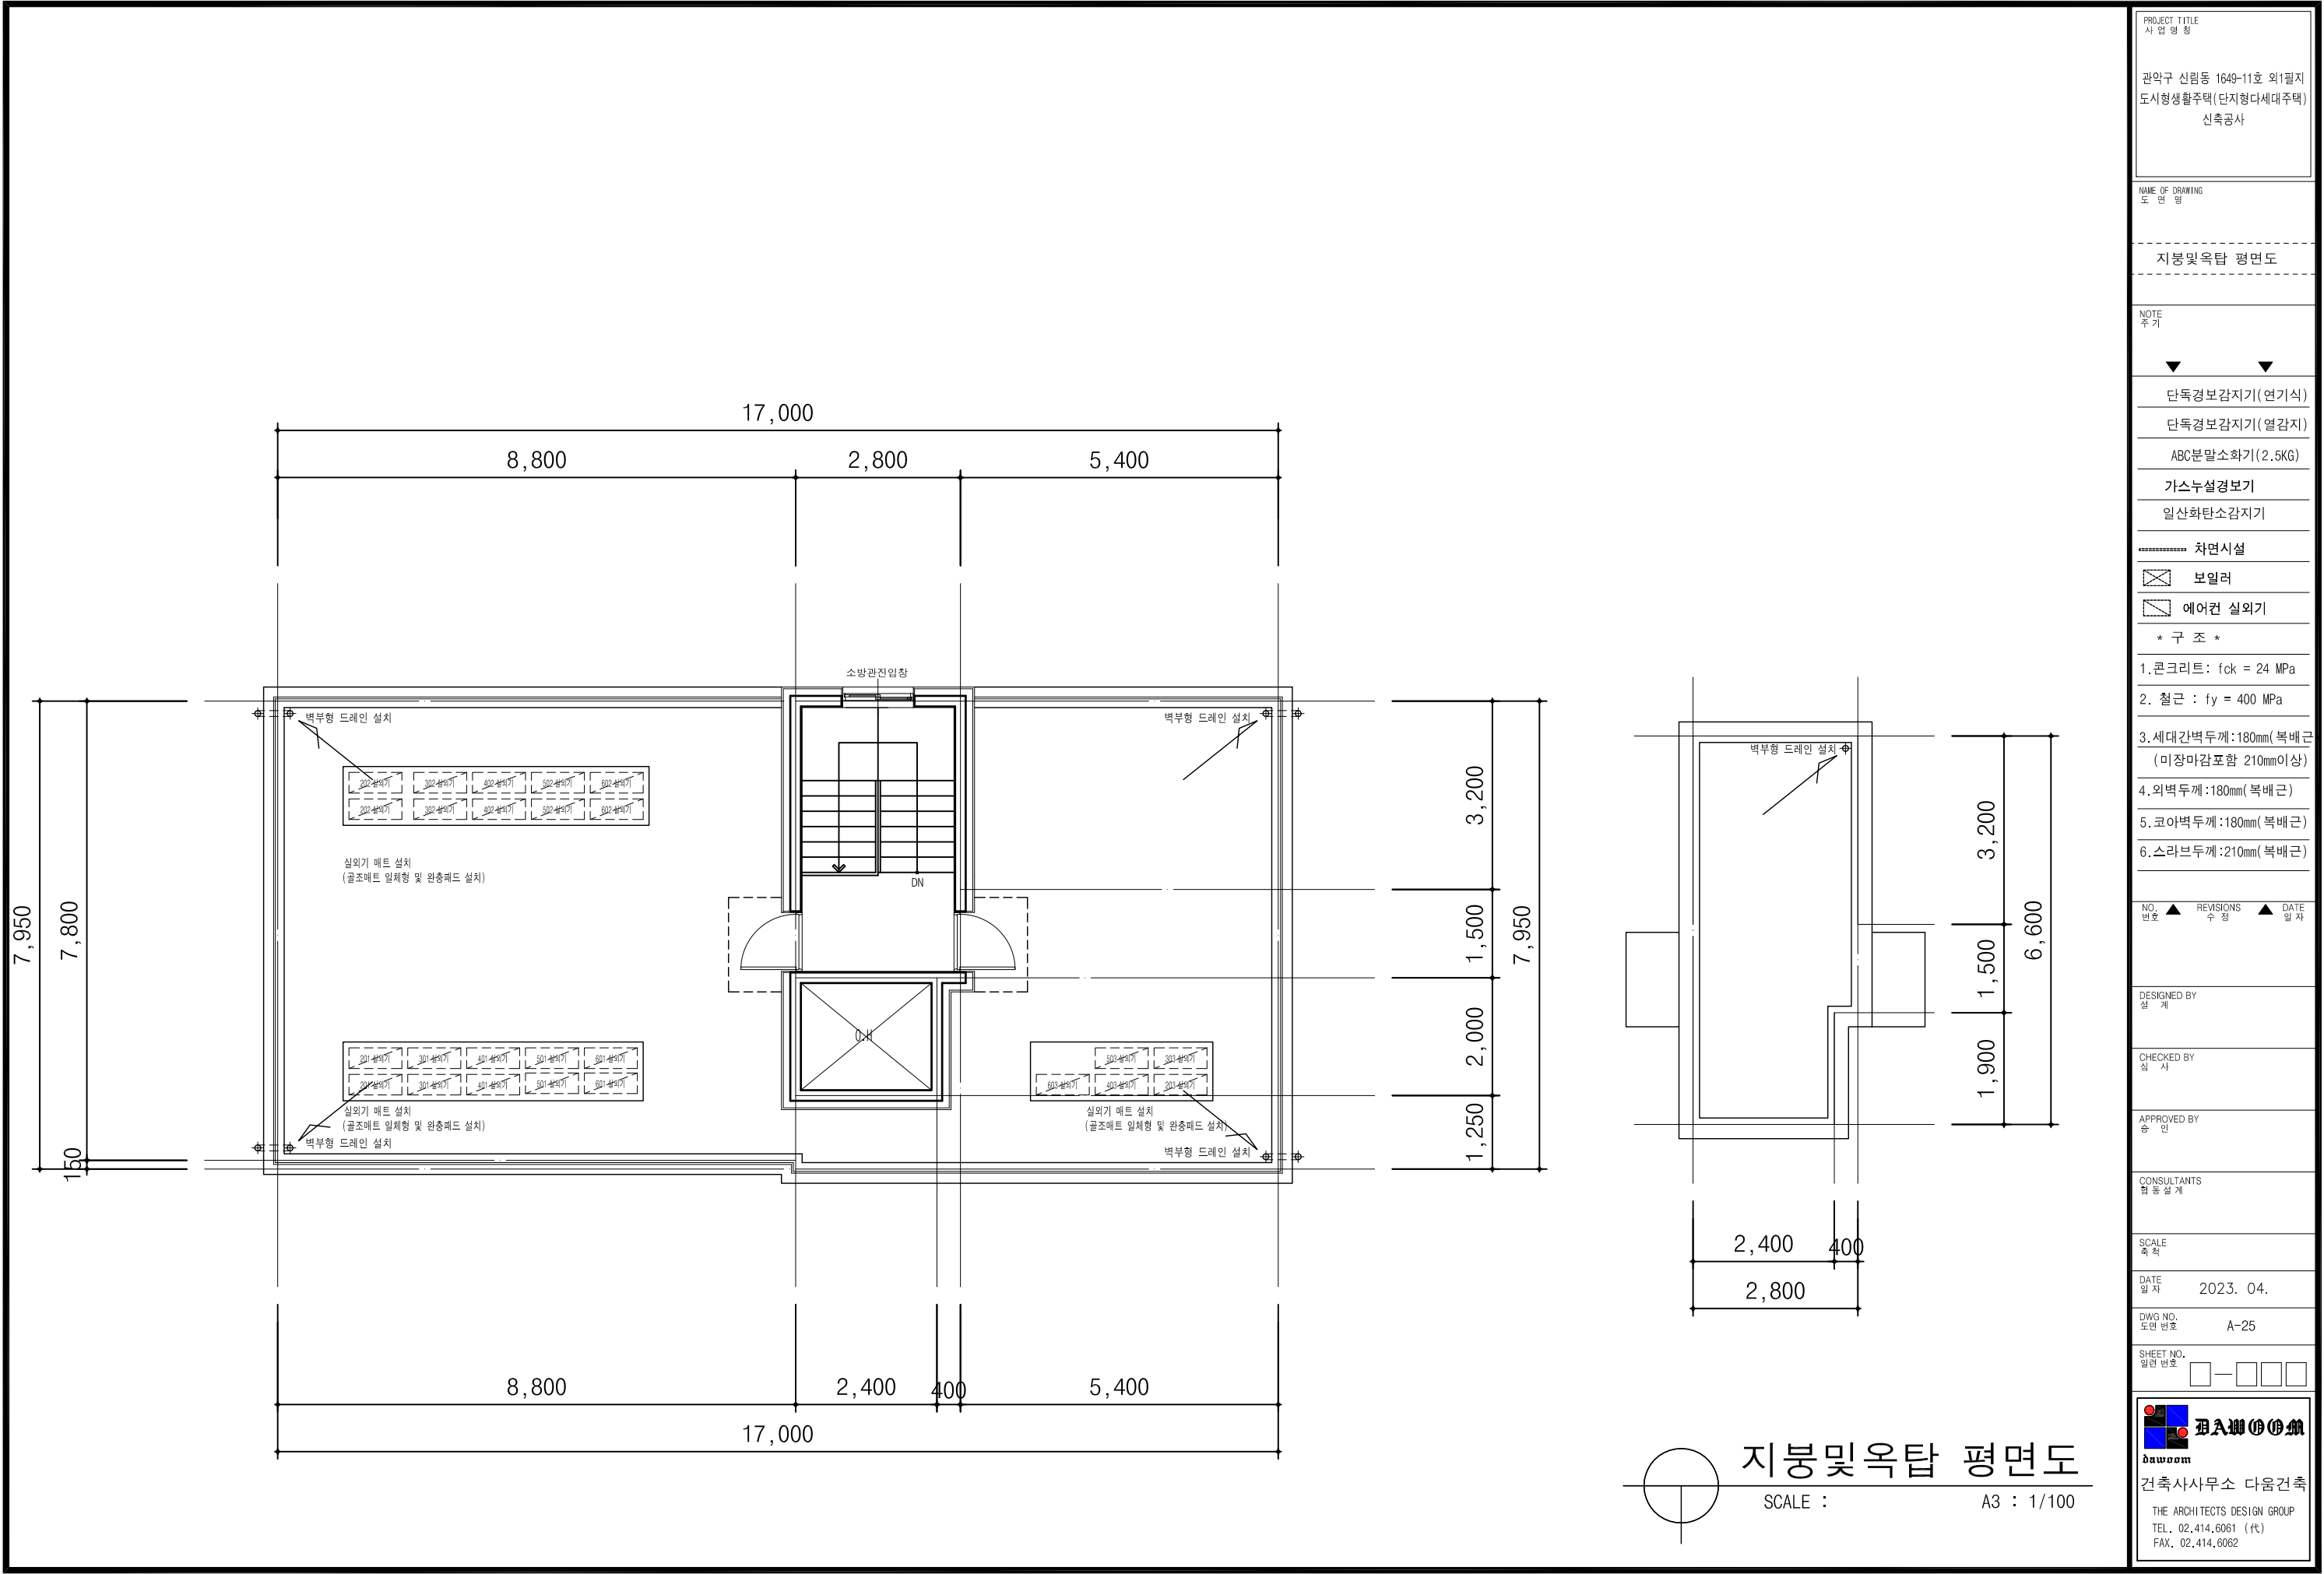


PROJECT TITLE 사업명칭	관악구 신림동 1649-11호 외1필지 도시형생활주택(단지형다세대주택) 신축공사
NAME OF DRAWING 도면명	지붕및옥탑 평면도
NOTE 주 기	
단독경보감지기(연기식)	
단독경보감지기(열감지)	
ABC분말소화기(2.5KG)	
가스누설경보기	
일산화탄소감지기	
차면시설	
보일러	
에어컨 실외기	
* 구 조 *	
1.콘크리트: fck = 24 MPa	
2. 철근 : fy = 400 MPa	
3.세대간벽두께:180mm(복배근 (미장마감포함 210mm이상)	
4.외벽두께:180mm(복배근)	
5.코아벽두께:180mm(복배근)	
6.스라브두께:210mm(복배근)	
NO. REVISIONS DATE 번호 수 장 일 자	
DESIGNED BY 설 계	
CHECKED BY 심 사	
APPROVED BY 승 인	
CONSULTANTS 협 동 설 계	
SCALE 축 측	
DATE 일 자	2023. 04.
DWG NO. 도면 번호	A-25
SHEET NO. 일련 번호	□—□□□
 dawoom 건축사사무소 다움건축	
THE ARCHITECTS DESIGN GROUP TEL. 02.414.6061 (代) FAX. 02.414.6062	

THE ARCHITECTS DESIGN GROUP
TEL. 02.414.6061 (代)
FAX. 02.414.6062

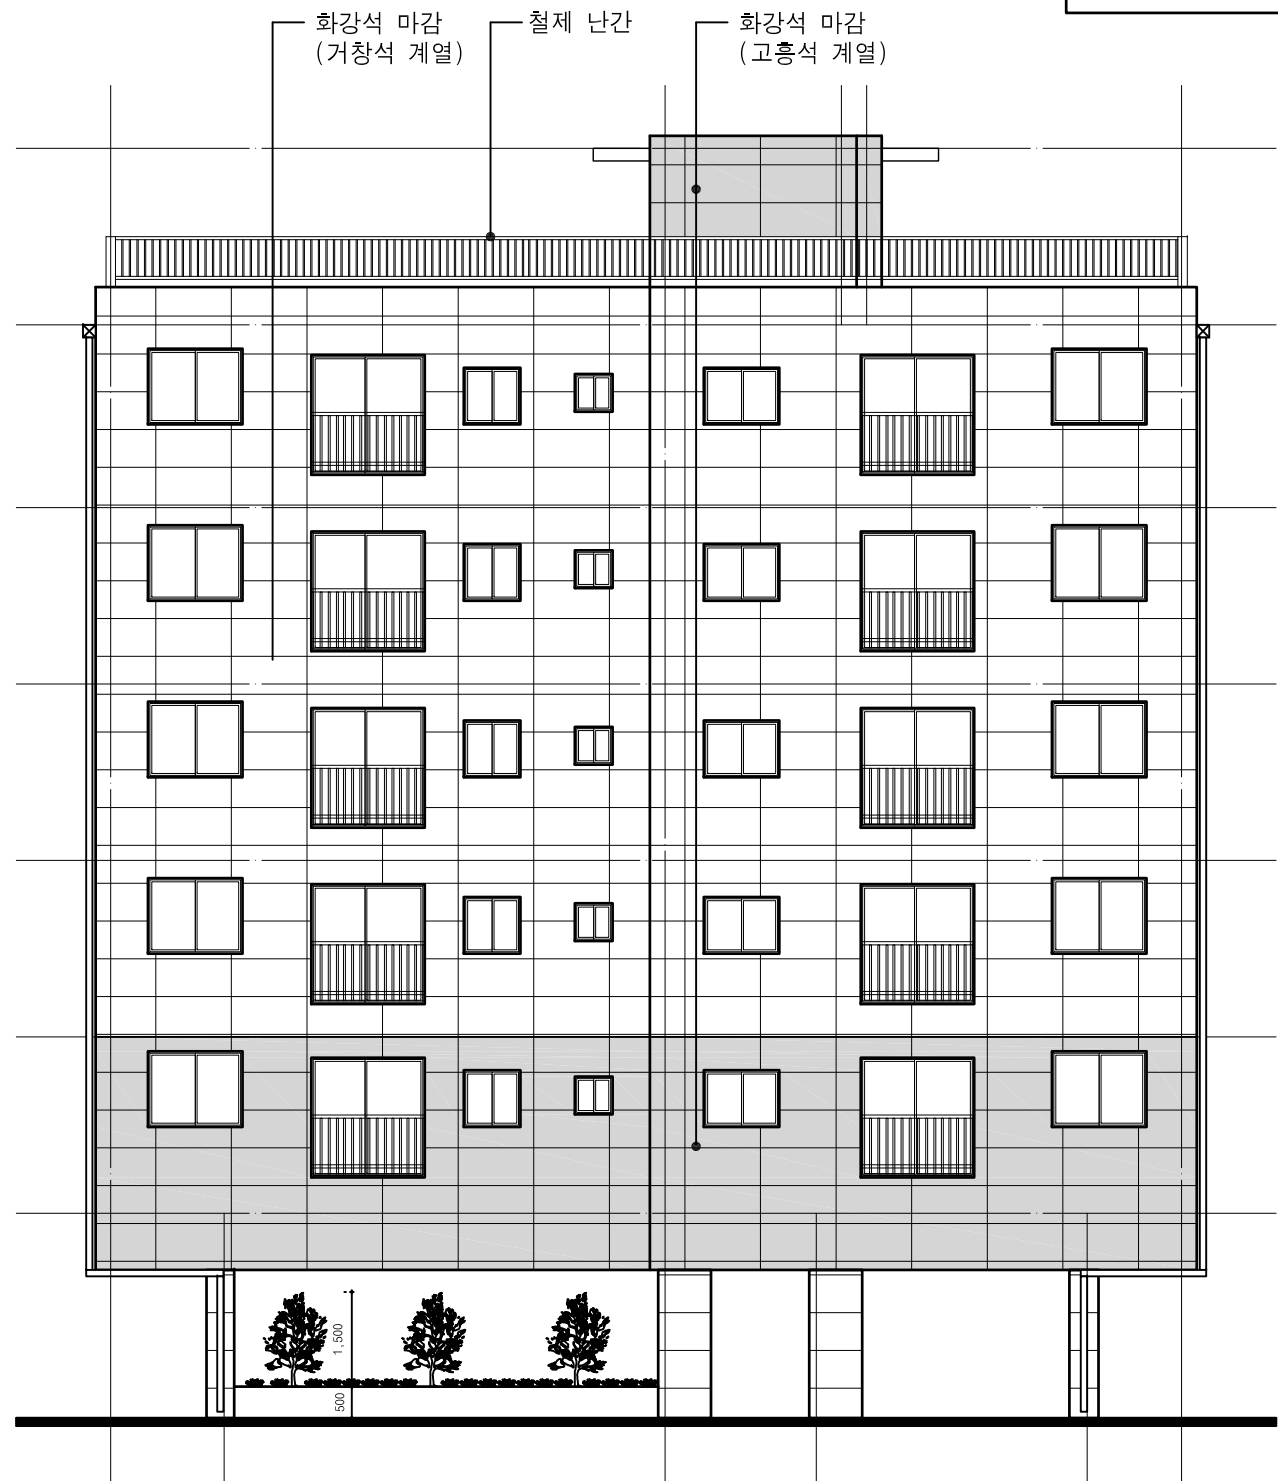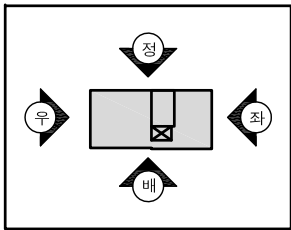

배면도
SCALE : A3 : 1/120

▽지붕층 바닥
▽6층 바닥
▽5층 바닥
▽4층 바닥
▽3층 바닥
▽2층 바닥
▽1층 바닥

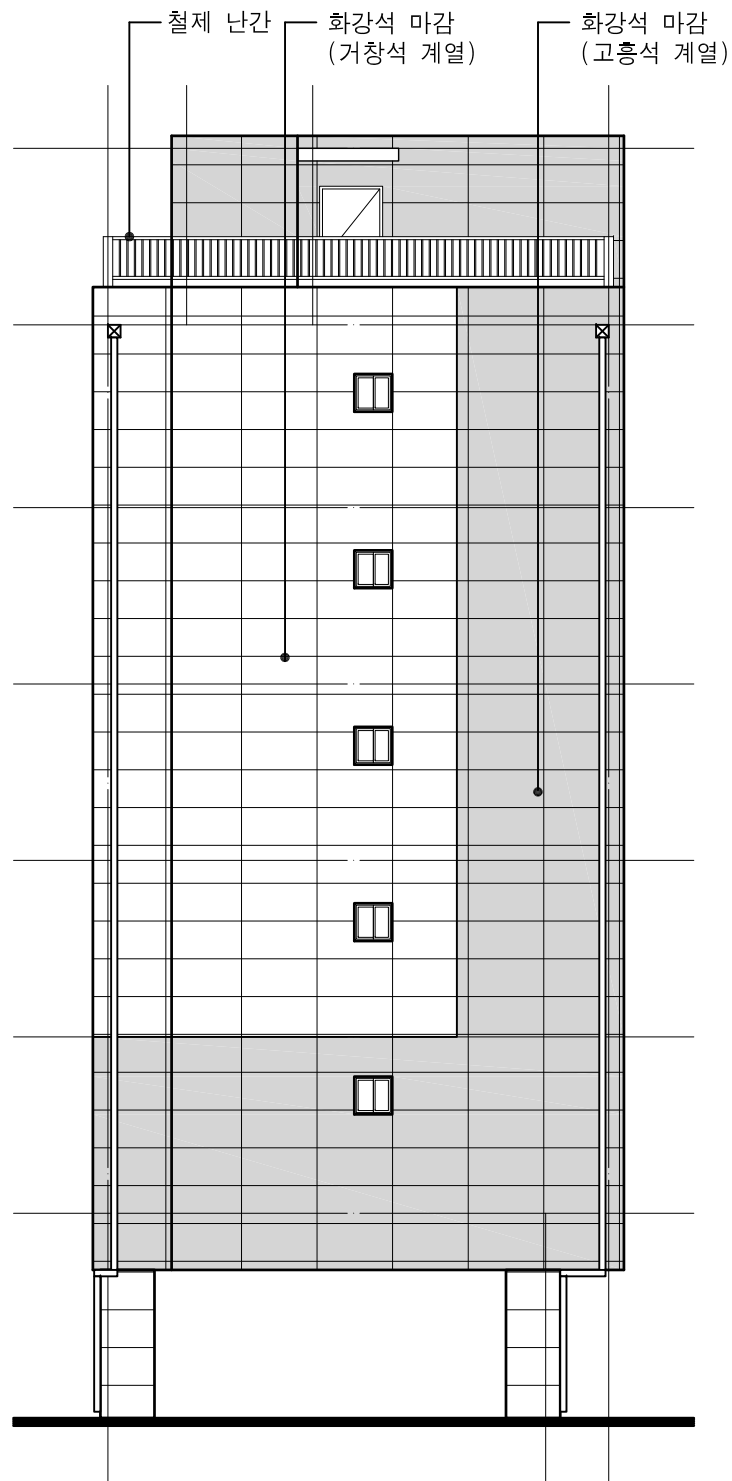

좌측면도
SCALE : A3 : 1/120

PROJECT TITLE
사업명칭
관악구 신림동 1649-11호 외1필지
도시형생활주택(단지형다세대주택)
신축공사

NAME OF DRAWING
도면명
입면도-2

NOTE
주 기
▼ ▼

NO. ▲ REVISIONS ▲ DATE
번호 수정 일자

DESIGNED BY
설계

CHECKED BY
심사

APPROVED BY
승인

CONSULTANTS
협동설계

SCALE
축척

DATE
일자 2023. 04.

DWG NO.
도면번호 A-32

SHEET NO.
일련번호 □-□□□

 **dawoom**
건축사사무소 다움건축
THE ARCHITECTS DESIGN GROUP
TEL. 02,414,6061 (代)
FAX. 02,414,6062