



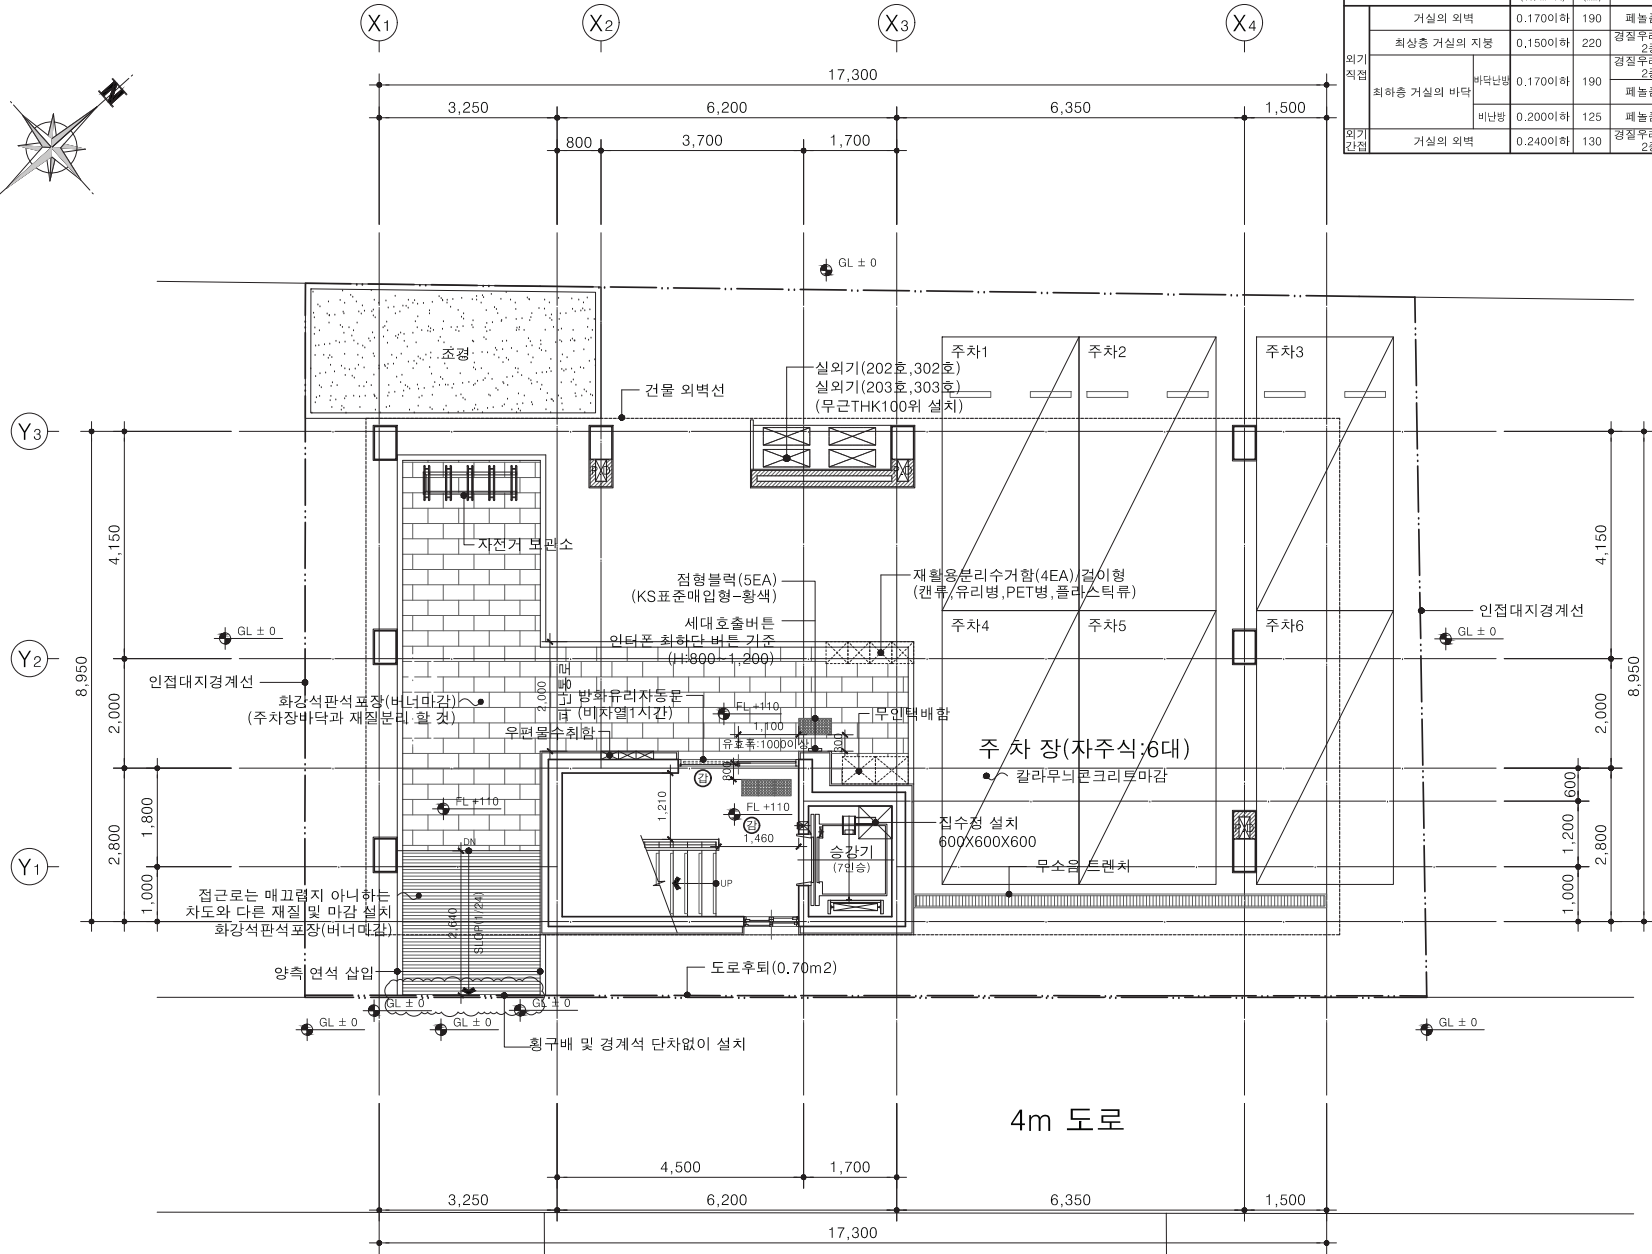

1 지상 1층 평면도
축척 - A3 : 1/100

구분	기준열전도율 (W/m ² ·K)	기준두께 (mm)	재료명	열전도율 (W/m·K)	두께 (mm)
거실의 외벽	0.170이하	190	페놀폼단열재	0.020	120
최상층 거실의 지붕	0.150이하	220	경질우레탄보온판 2층2호	0.021	190
최하층 거실의 바닥	0.170이하	190	경질우레탄보온판 2층2호	0.021	90
비난방	0.200이하	125	페놀폼단열재	0.020	100
거실의 외벽	0.240이하	130	경질우레탄보온판 2층2호	0.021	80

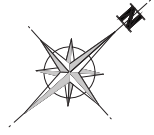

광진구 중곡동 88-20외2필지
도시형생활주택(원룸형)
신축공사

시도번호
PROJECT NO.

NOTE

- ㉔ 단독경보감지기
- ㉕ ABC분말소화기(3.3KG)
- ㉖ 60분+ 방화문, 60분 방화문
- ㉗ 보일러
- ㉘ 에어컨
- ㉙ 실외기
- 차면시설
- *기동 주위에 차량 보호대 설치
- *각세대 거실난간 국기꽃이 설치
- *승강기에 면한 침실 및 거실, 주방 방전패드 설치

* 구조 *

- 콘크리트: fck = 27 MPa
- 철근: fy = 400 MPa
- 세대벽두께: 180mm(복배근)
- 세대내벽두께: 150mm(복배근)
- 외벽두께: 180mm(복배근)
- 코아벽두께: 180mm(복배근)
- 스라브두께: 210mm(3~5층)
- 스라브두께: 180mm(2층, 지붕)
- 세대현관문 규격 (틀포함)
1,100x2,200

REVISIONS & REVISIONS		
NO.	DATE	REVISION
5		
4		
3		
2		
1		

지도
DRAWN BY 유은지, 박호연

검사
CHECKED BY 정우영

승인
APPROVED BY 김재형

도면명
NAME OF DRAWING

지상1층 평면도



제안
DATE: 2022. 09.

축척
SCALE: A3: 1/100

건축사사무소
에코플랜
Total Architecture
Engineers Group

서울특별시 송파구 삼학사로 25-1
신영빌딩 2층 (삼전동 182-4)
TEL: (02)418-7902 / FAX: (02)418-7907
E-mail: ecoplan01@hanmail.net

도면번호
DRAWING NO.

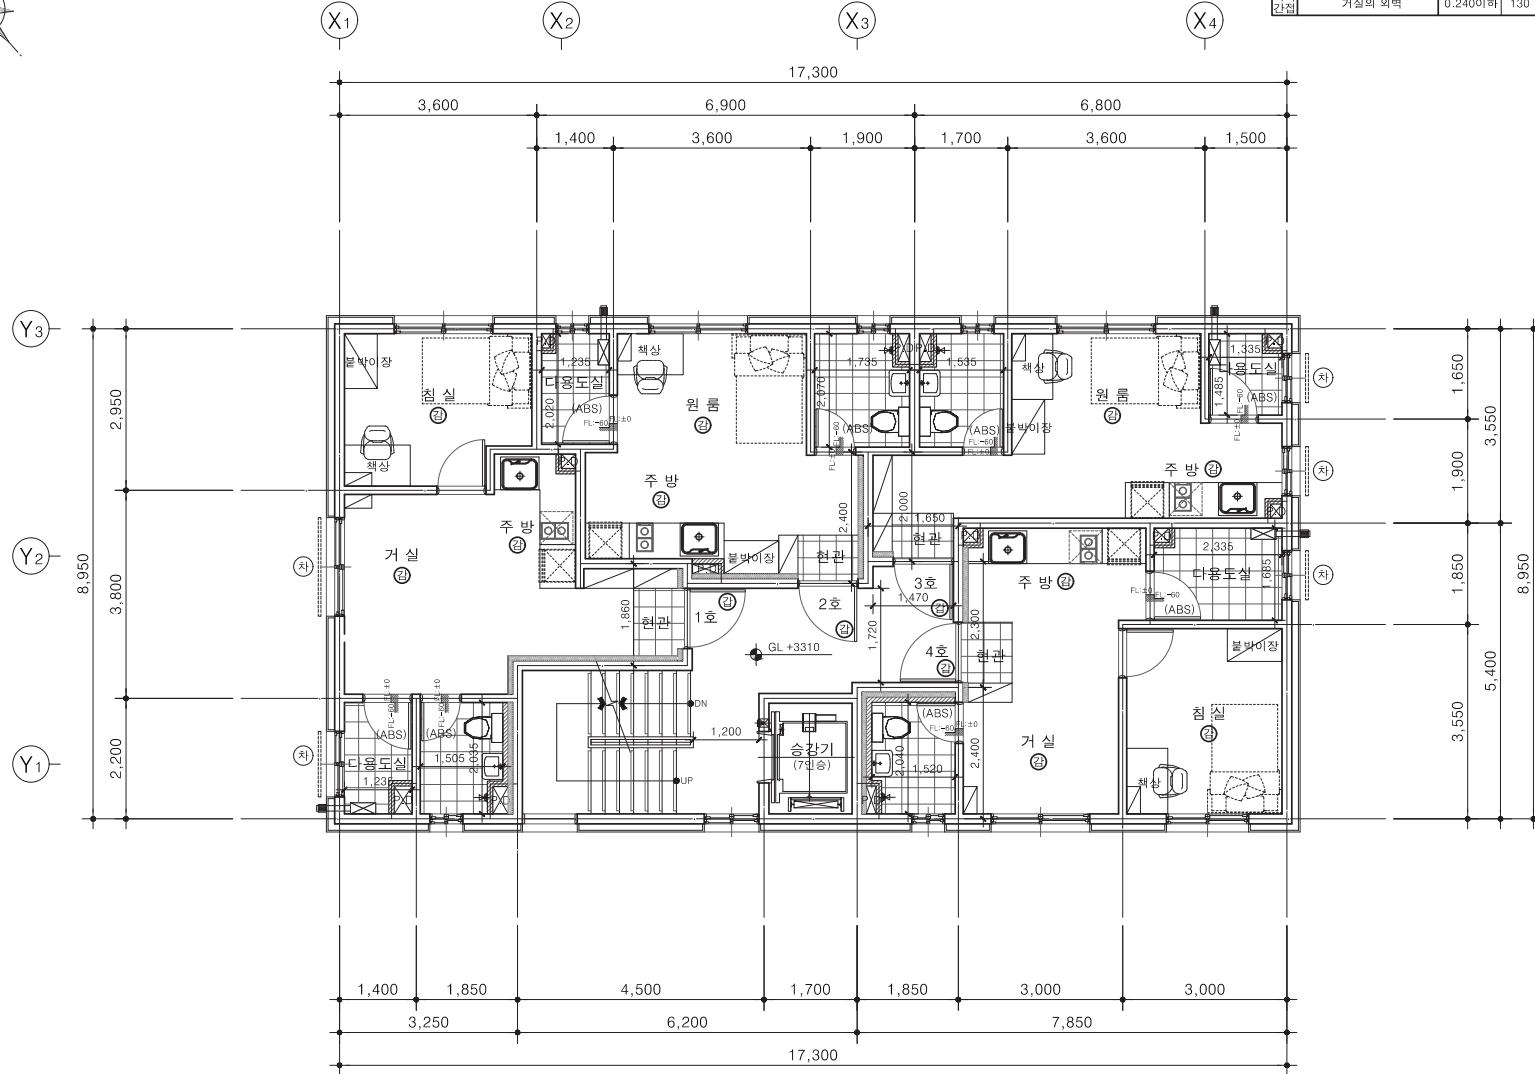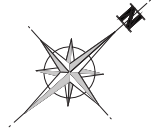

1 지상 2층 평면도
축척 - A3 : 1/100

구분	기준열전도율 (W/m ² ·K)	기준두께 (mm)	재료명	열전도율 (W/m·K)	두께 (mm)
외기 외벽	거실의 외벽	0.170이하	190	페놀폼단열재	0.020 120
	최상층 거실의 지붕	0.150이하	220	경질우레탄보온판 2층2호	0.021 190
	최하층 거실의 바닥	비단난방 0.170이하	190	경질우레탄보온판 2층2호	0.021 90
외기 기둥	비단난방	0.200이하	125	페놀폼단열재	0.020 100
	거실의 외벽	0.240이하	130	경질우레탄보온판 2층2호	0.021 80



광진구 중곡동 88-20외2필지
도시형생활주택(원룸형)
신축공사

시공명세서
PROJECT FILE

NOTE

- ㉔ 단독경보감지기
- ㉕ ABC분말소화기(3.3KG)
- ㉖ 60분+ 방화문, 60분 방화문
- 보일러
- 에어컨
- 실외기
- 차면시설
- *기동 주위에 차량 보호대 설치
- *각세대 거실난간 국기꽃이 설치
- *승강기에 면한 침실 및 거실,
주방 방전패드 설치

* 구조 *

- 콘크리트: fck = 27 MPa
- 철근: fy = 400 MPa
- 세대벽두께: 180mm(복배근)
- 세대내벽두께: 150mm(복배근)
- 외벽두께: 180mm(복배근)
- 코아벽두께: 180mm(복배근)
- 스라브두께: 210mm(3~5층)
- 스라브두께: 180mm(2층, 지붕)

9.세대현관문 규격 (틀포함)
1,100x2,200
RESULTS & REVISIONS

NO.	DATE	REVISION
5		
4		
3		
2		
1		

지도
DRAWN BY 유은지, 박호연

검사
CHECKED BY 정우영

승인
APPROVED BY 김재형

도면명
NAME OF DRAWING

지상2층 평면도

일자
DATE

2022. 09.

축척
SCALE



A3: 1/100

건축사사무소
에코플랜
Total Architecture
Engineers Group

서울특별시 송파구 삼학사로 25-1
신명빌딩 2층 (삼정동 182-4)
TEL: (02)418-7902 / FAX: (02)418-7907
E-mail: ecoplan01@hanmail.net

도면번호
DRAWING NO.

A-102

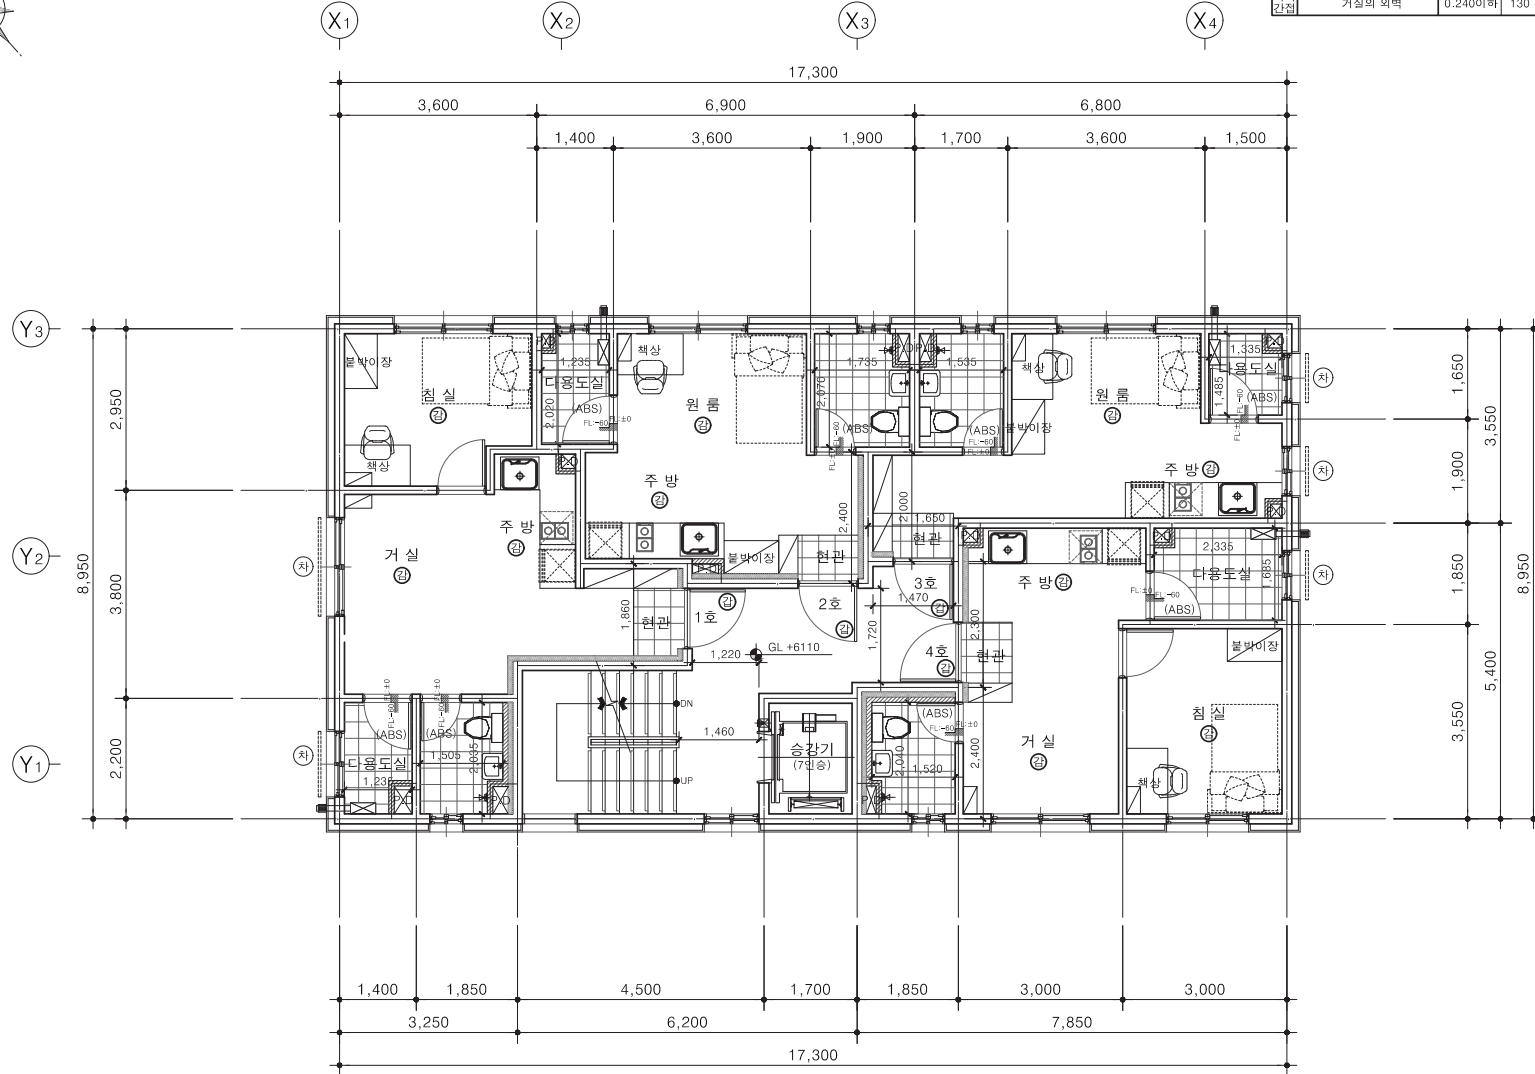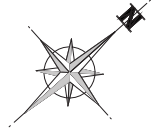

1 지상 3층 평면도
축척 - A3 : 1/100

구분	기준열전도율 (W/m ² ·K)	기준두께 (mm)	재료명	열전도율 (W/m·K)	두께 (mm)
외기 벽체	0.170이하	190	페놀폼단열재	0.020	120
외기 창문	0.150이하	220	경질우레탄보온판 2층2호	0.021	190
외기 창문	0.170이하	190	경질우레탄보온판 2층2호	0.021	90
외기 창문	0.200이하	125	페놀폼단열재	0.020	100
외기 창문	0.240이하	130	경질우레탄보온판 2층2호	0.021	80



광진구 중곡동 88-20외2필지
도시형생활주택(원룸형)
신축공사

- 시방명호
PROJECT TITLE
- NOTE
- ㉔ 단독경보감지기
 - ㉕ ABC분말소화기(3.3KG)
 - ㉖ 60분+ 방화문, 60분 방화문
 - 보일러
 - 에어컨
 - 실외기
 - 차면시설
 - *기동 주위에 차량 보호대 설치
 - *각세대 거실난간 국기꽃이 설치
 - *승강기에 면한 침실 및 거실, 주방 방진패드 설치

* 구조 *

- 콘크리트: fck = 27 MPa
- 철근: fy = 400 MPa
- 세대벽두께: 180mm(복배근)
- 세대내벽두께: 150mm(복배근)
- 외벽두께: 180mm(복배근)
- 코아벽두께: 180mm(복배근)
- 스라브두께: 210mm(3~5층)
- 스라브두께: 180mm(2층, 지붕)
- 세대현관문 규격 (틀포함)
1,100x2,200
RISUL & REVOLVING



NO.	DATE	REVISION
5		
4		
3		
2		
1		

지도 DRAWN BY	유은지, 박호연
검사 CHECKED BY	정우영
승인 APPROVED BY	김재형
도면명 NAME OF DRAWING	

지상3층 평면도	
일지 DATE	2022. 09.
축척 SCALE	A3: 1/100

건축사사무소
에코플랜
Total Architecture
Engineers Group

서울특별시 송파구 삼학사로 25-1
신명빌딩 2층 (삼정동 182-4)
TEL: (02)418-7902 / FAX: (02)418-7907
E-mail: ecoplan01@hanmail.net

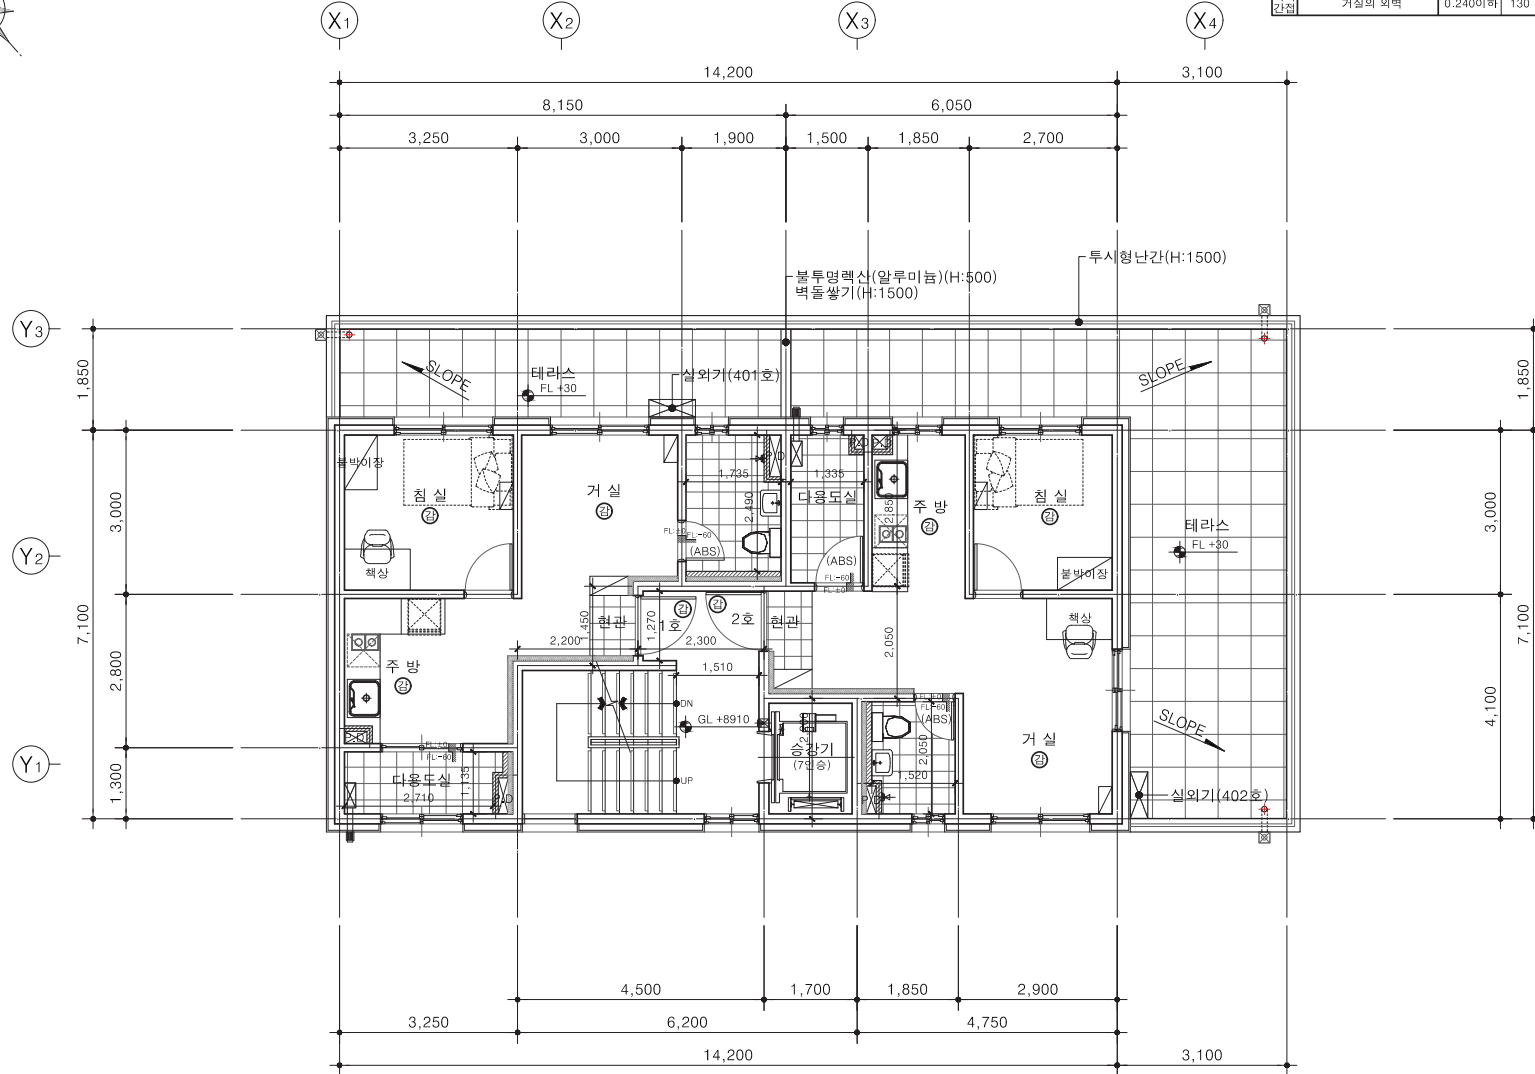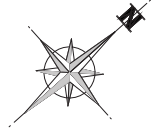

구분	기준열전도율 (W/m ² ·K)	기준두께 (mm)	재료명	열전도율 (W/m·K)	두께 (mm)
외기 적접	거실의 외벽	0.170이하	190	페놀폼단열재	0.020 120
	최상층 거실의 지붕	0.150이하	220	경질우레탄보온판 2층2호	0.021 190
	최하층 거실의 바닥	비단난방 0.170이하	190	경질우레탄보온판 2층2호	0.021 90
외기 간접	비난방	0.200이하	125	페놀폼단열재	0.020 100
	거실의 외벽	0.240이하	130	경질우레탄보온판 2층2호	0.021 80



지정명칭
PROJECT TITLE
광진구 중곡동 88-20외2필지
도시형생활주택(원룸형)
신축공사

시도번호
PROJECT NO.

NOTE

- ㉔ 단독경보감지기
- ㉕ ABC분말소화기(3.3KG)
- ㉖ 60분+ 방화문, 60분 방화문
- 보일러
- 에어컨
- 실외기

차면시설
*기동 주위에 차량 보호대 설치
*각세대 거실난간 국기꽃이 설치
*승강기에 면한 침실 및 거실,
주방 방전패드 설치

* 구조 *

- 콘크리트: fck = 27 MPa
- 철근: fy = 400 MPa
- 세대벽두께: 180mm(복배근)
- 세대내벽두께: 150mm(복배근)
- 외벽두께: 180mm(복배근)
- 코아벽두께: 180mm(복배근)
- 스라브두께: 210mm(3~5층)
- 스라브두께: 180mm(2층, 지붕)
- 세대현관문 규격 (틀포함)
1,100x2,200

REVISIONS & REVISIONS		
NO.	DATE	REVISION
5		
4		
3		
2		
1		

지도
DRAWN BY 유은지, 박호연
검사
CHECKED BY 정우영
승인
APPROVED BY 김재형
도면명
NAME OF DRAWING



지상4층 평면도

작성
DATE: 2022. 09.
중척
SCALE: A3: 1/100

건축사사무소
에코플랜
Total Architecture
Engineers Group
서울특별시 송파구 삼학사로 25-1
신영빌딩 2층 (삼전동 182-4)
TEL: (02)418-7902 / FAX: (02)418-7907
E-mail: ecoplan01@hanmail.net

도면번호
DRAWING NO.

1 지상 4층 평면도
축척 - A3 : 1/100

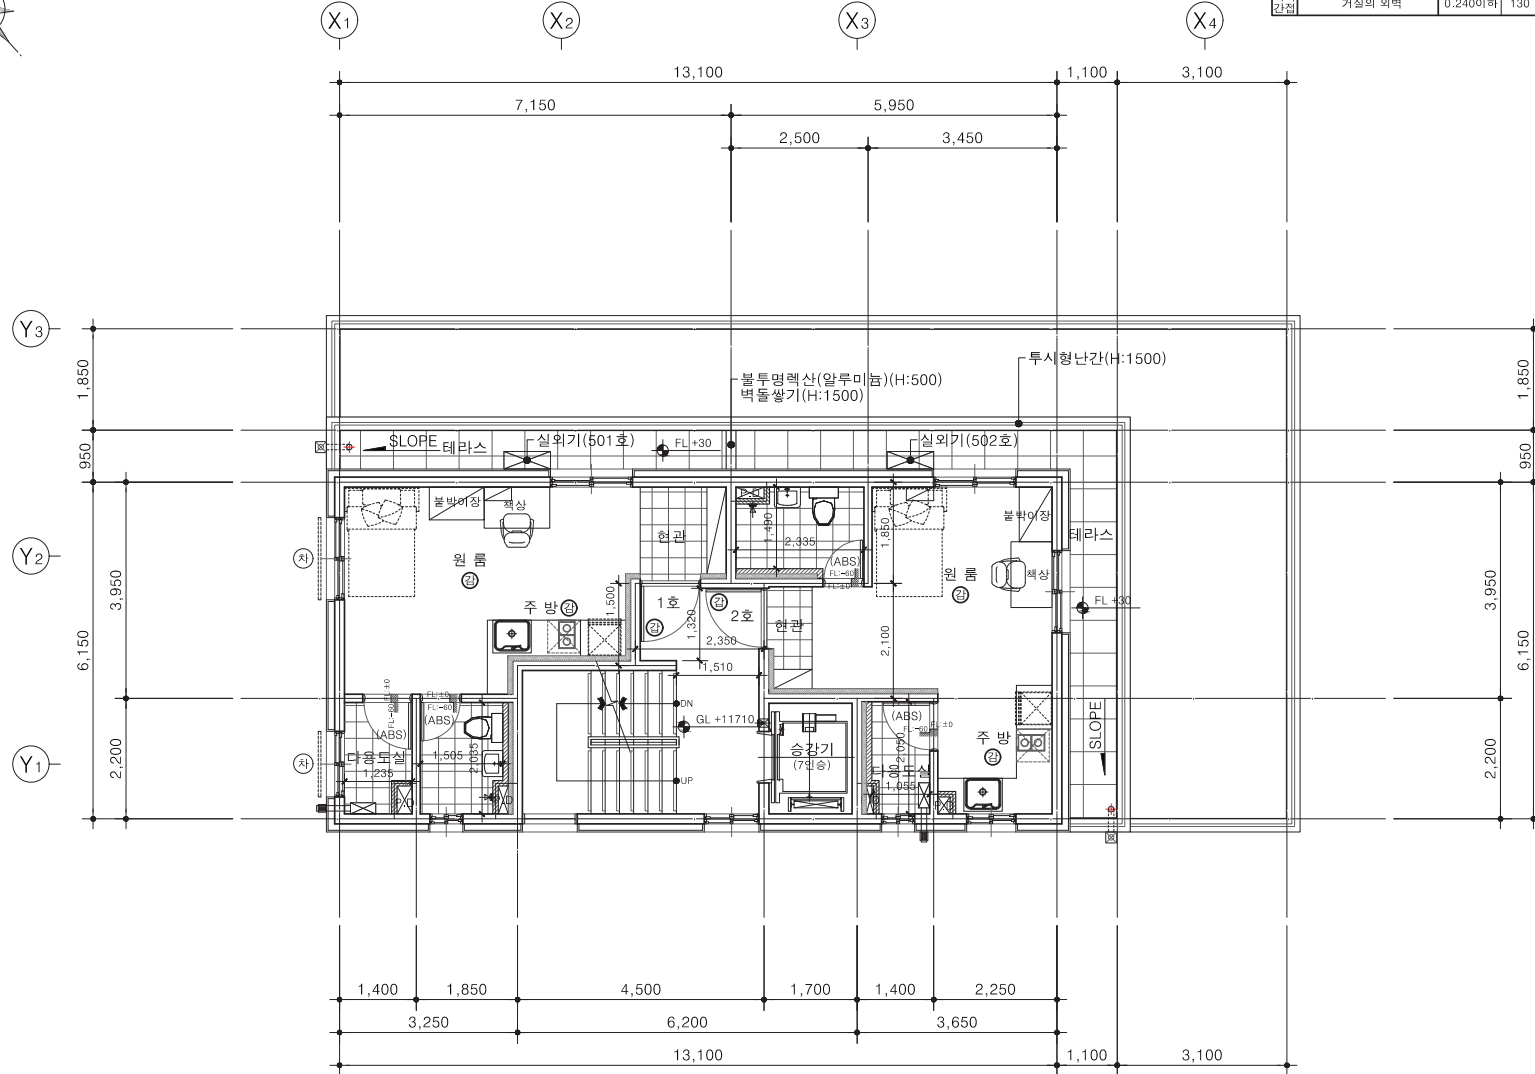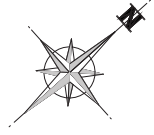

1 지상 5층 평면도
축척 - A3 : 1/100

구 분		기준열전도도 (W/m ² ·K)	기준두께 (mm)	재료명	열전도도 (W/m·K)	두께 (mm)	
외기 적층	거실의 외벽	0.170이하	190	페놀폼단열재	0.020	120	
	최상층 거실의 지붕	0.150이하	220	경질우레탄보온판 2층2호	0.021	90	
	최하층 거실의 바닥	비단난방	0.170이하	190	경질우레탄보온판 2층2호	0.021	90
		비난방	0.200이하	125	페놀폼단열재	0.020	50
				125	페놀폼단열재	0.020	100
외기 단열	거실의 외벽	0.240이하	130	경질우레탄보온판 2층2호	0.021	80	



광진구 중곡동 88-20외2필지
도시형생활주택(원룸형)
신축공사

시도번호
PROJECT NO.

NOTE

- ㉔ 단독경보감지기
- ㉕ ABC분말소화기(3.3KG)
- ㉖ 60분+ 방화문, 60분 방화문
- 보일러
- 에어컨
- 실외기

차면시설

- *기동 주위에 차량 보호대 설치
- *각세대 거실난간 국기꽃이 설치
- *승강기에 면한 침실 및 거실, 주방 방전패드 설치

* 구 조 *

- 콘크리트: fck = 27 MPa
- 철근: fy = 400 MPa
- 세대벽두께: 180mm(복배근)
- 세대내벽두께: 150mm(복배근)
- 외벽두께: 180mm(복배근)
- 코아벽두께: 180mm(복배근)
- 스라브두께: 210mm(3~5층)
- 스라브두께: 180mm(2층, 지붕)

9.세대현관문 규격 (틀포함)
1,100x2,200

REVISIONS & REVISIONS		
NO.	DATE	REVISION
5		
4		
3		
2		
1		

지도
DRAWN BY 유은지, 박호연

검사
CHECKED BY 정우영

승인
APPROVED BY 김재형

도면명
NAME OF DRAWING

지상5층 평면도



일자
DATE 2022. 09.

축척
SCALE A3: 1/100

건축사사무소
에코플랜
Total Architecture
Engineers Group


서울특별시 송파구 삼학사로 25-1
신명빌딩 2층 (삼전동 182-4)
TEL: (02)418-7902 / FAX: (02)418-7907
E-mail: ecoplan01@hanmail.net

도면번호
DRAW NO.

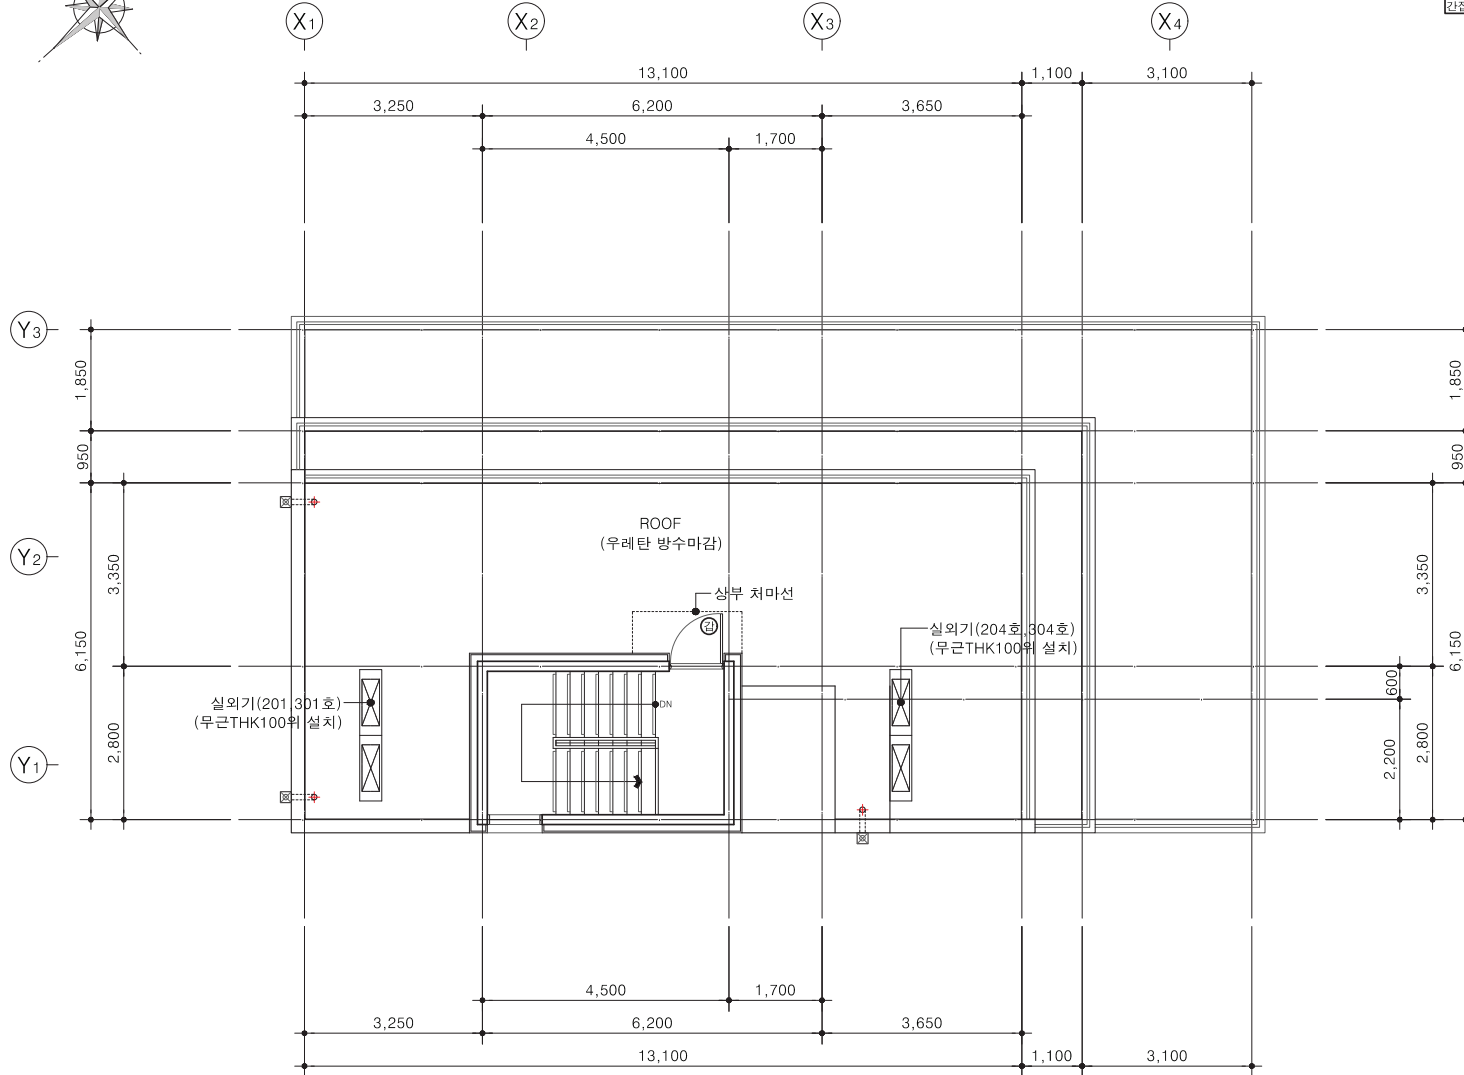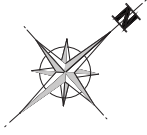


1 지붕 평면도
축척 - A3 : 1/100

구분	기준열전도율 (W/m ² ·K)	기준두께 (mm)	재료명	열전도율 (W/m·K)	두께 (mm)
외기 적접	거실의 외벽	0.170이하	190	페놀폼단열재	0.020 120
	최상층 거실의 지붕	0.1500이하	220	경질우레탄보온판 2층2호	0.021 190
	최하층 거실의 바닥	비단난방 0.170이하	190	경질우레탄보온판 2층2호	0.021 90
	비난방	0.200이하	125	페놀폼단열재	0.020 50
외기 간접	거실의 외벽	0.240이하	130	페놀폼단열재	0.020 100
				경질우레탄보온판 2층2호	0.021 80

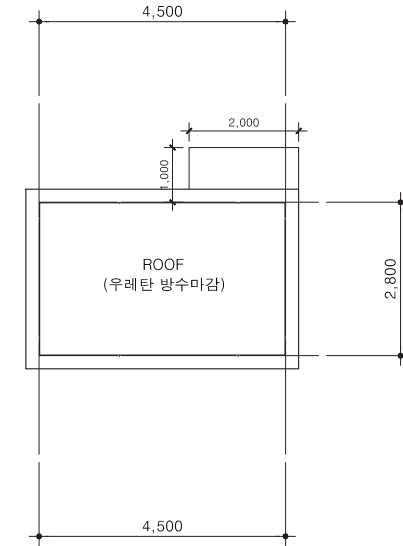

2 옥탑지붕 평면도
축척 - A3 : 1/100

* ▼ (소방관 진입창) : 창문의 가운데에 지름20cm이상의 역삼각형을 야간에도 알아볼 수 있도록 빛 반사등으로 붉은색으로 표시할 것.

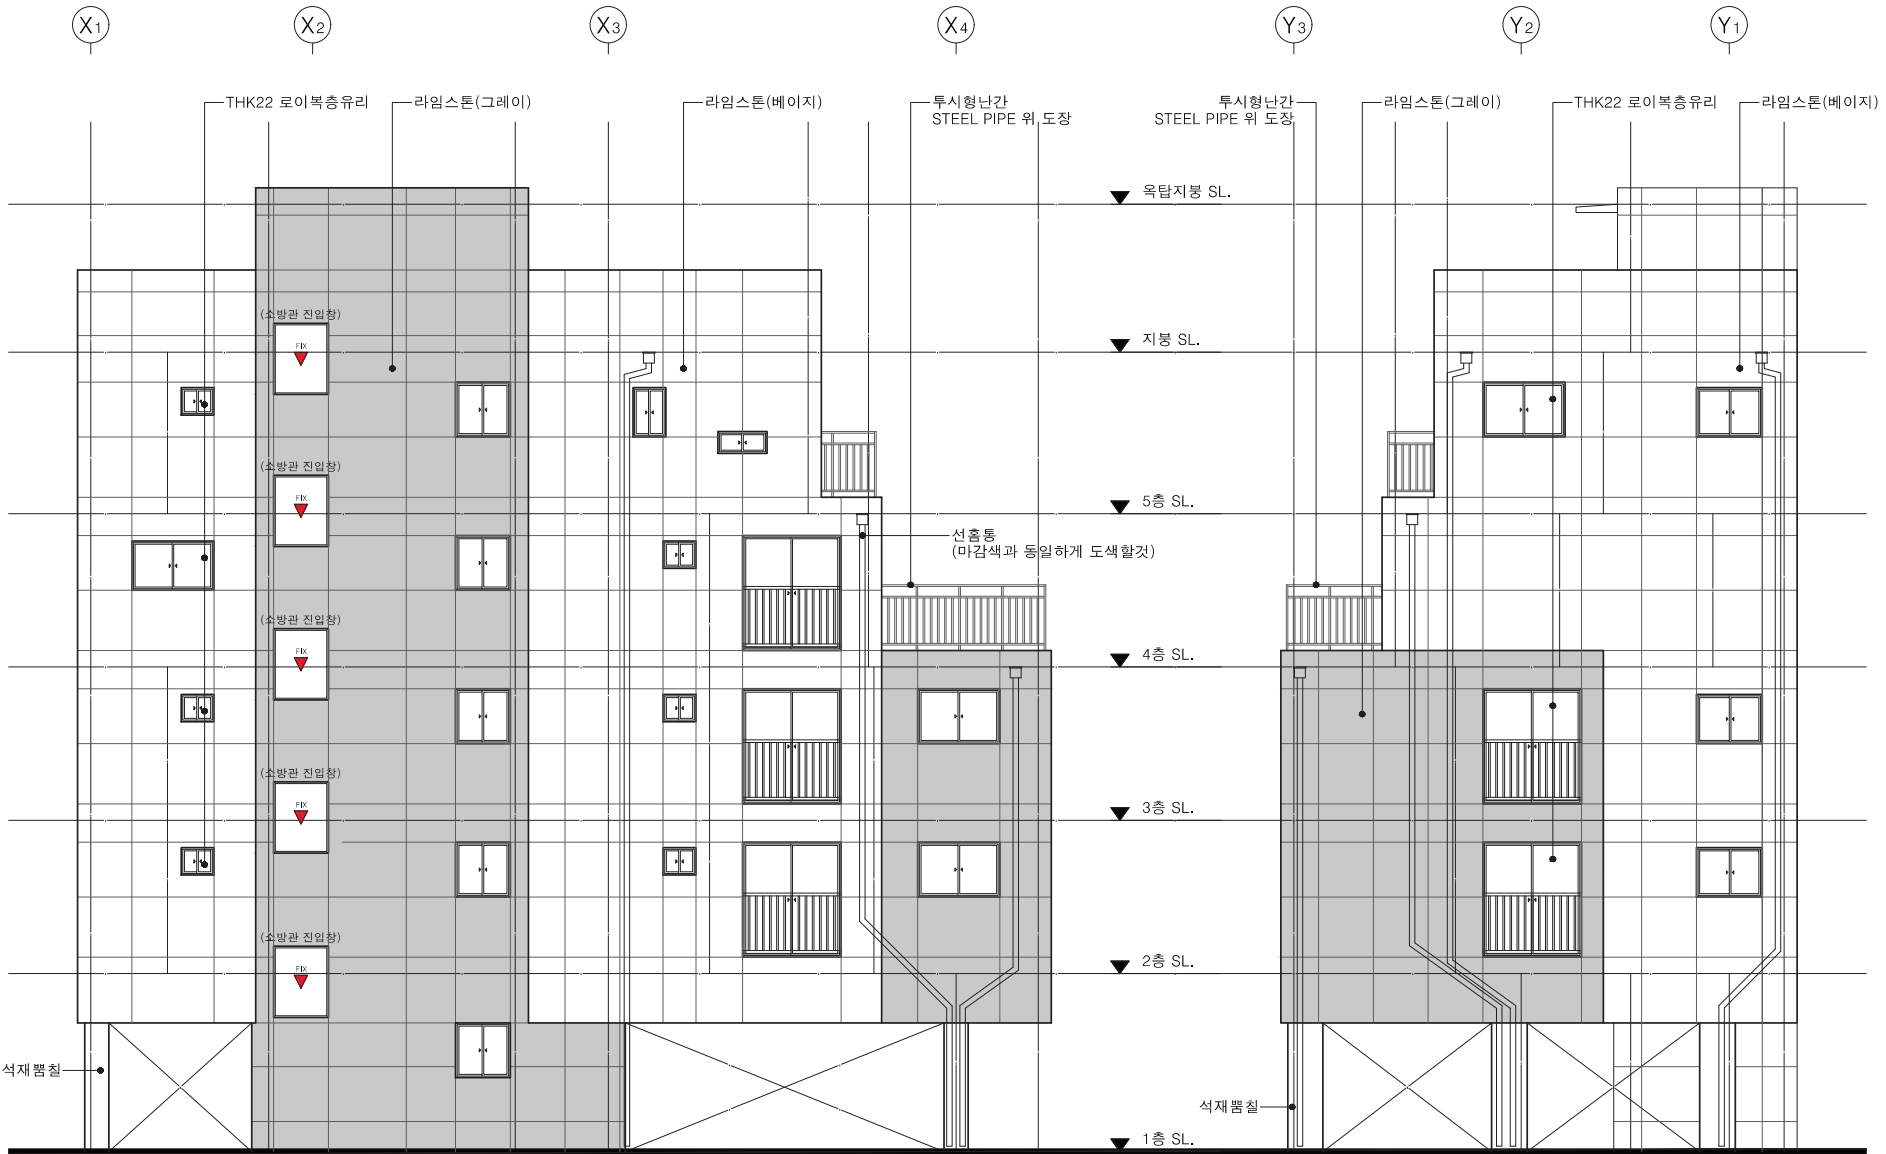

1 정 면 도
축척 - A3 : 1/100

2 우 측 면 도
축척 - A3 : 1/100


REVISIONS & REVISIONS		
NO.	DATE	REVISION
5		
4		
3		
2		
1		

지도
DRAWN BY 유은지, 박호연
검사
CHECKED BY 정우영
승인
APPROVED BY 김재형

도면명
NAME OF DRAWING
정면도, 우측면도
제차
DATE 2022. 09.
중형
SCALE A3: 1/100

건축사사무소
에코플랜
Total Architecture
Engineers Group
서울특별시 송파구 삼학사로 25-1
신명빌딩 2층 (삼전동 182-4)
TEL: (02)418-7902 / FAX: (02)418-7907
E-mail: ecoplan01@hanmail.net

* ▼ (소방관진입창) : 창문의 가운데에 지름20cm이상의 역삼각형을 야간에도 알아볼수 있도록 빛 반사등으로 붉은색으로 표시할 것.

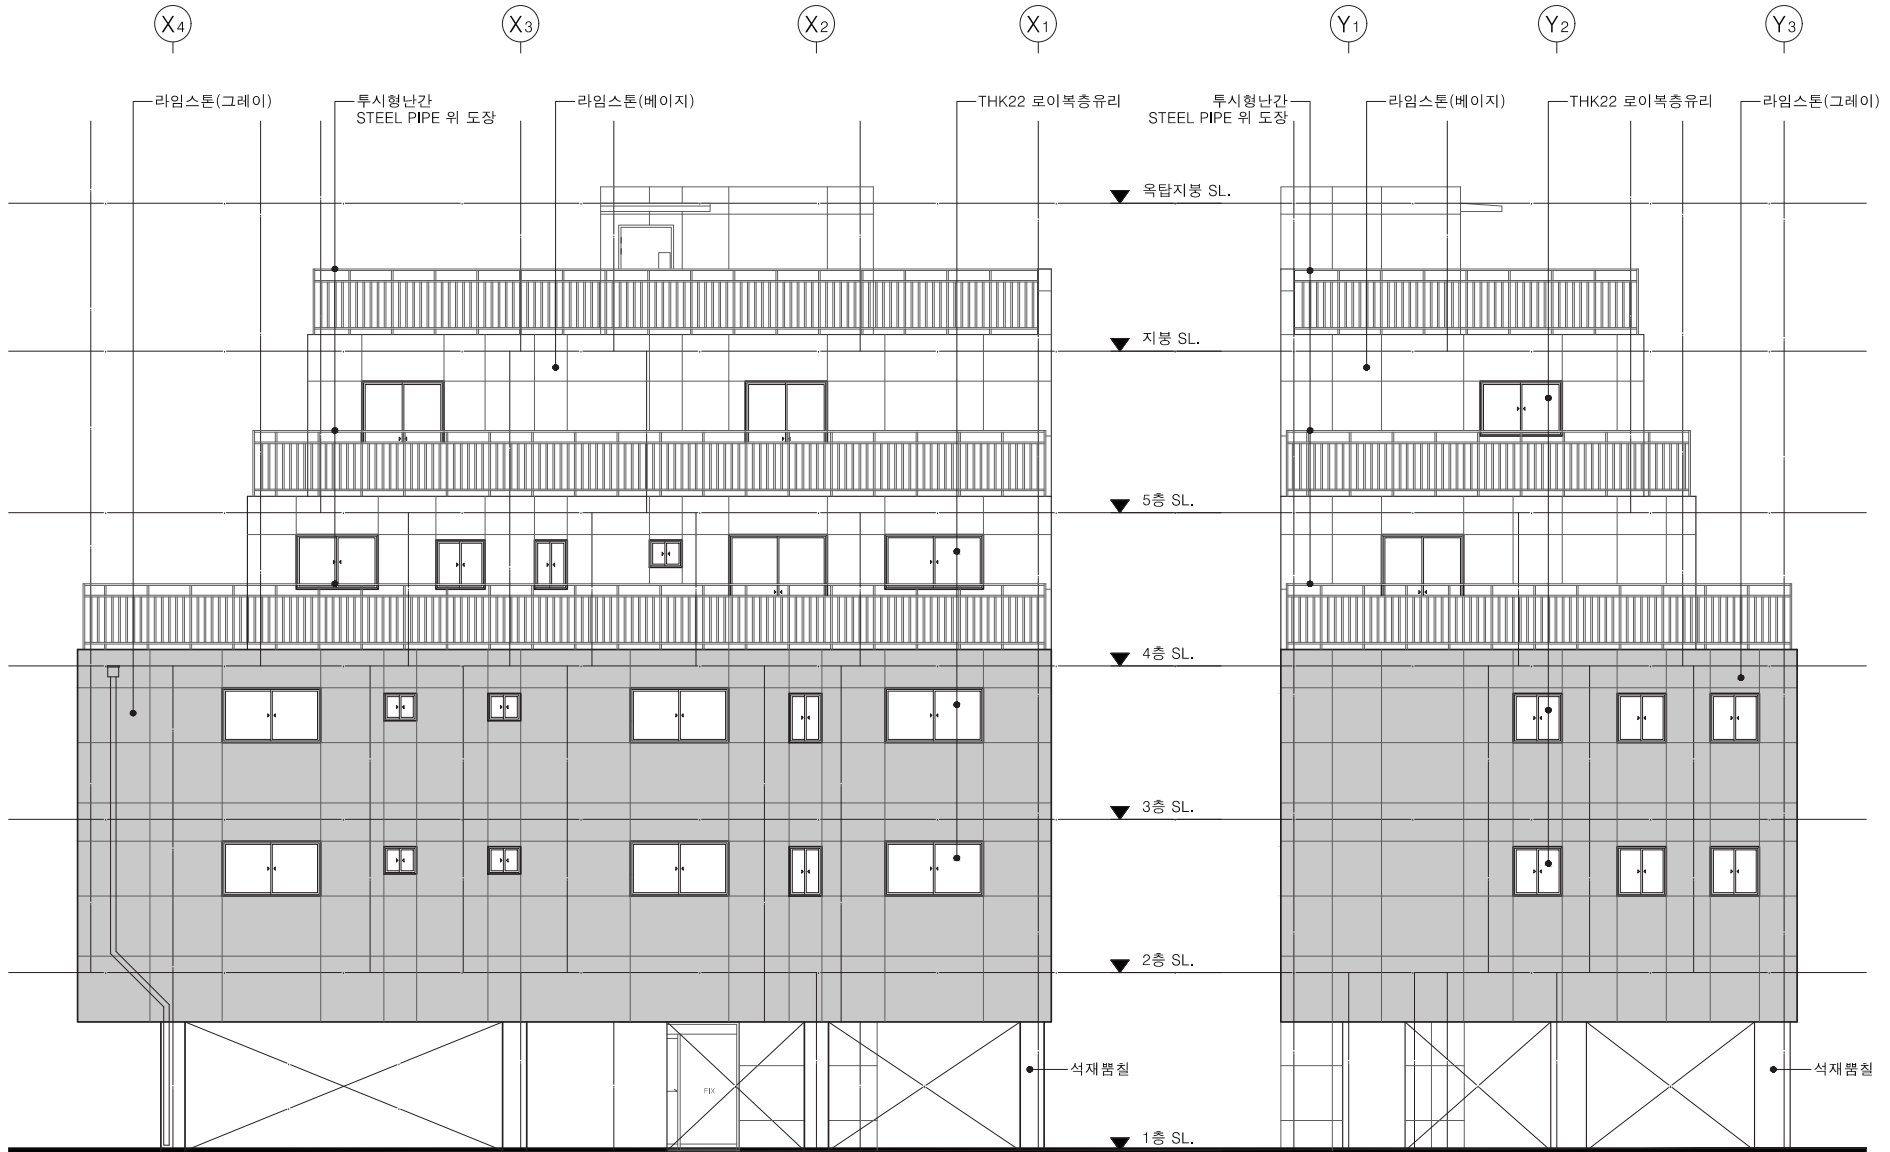

1 배 면 도
축척 - A3 : 1/100

2 좌 측 면 도
축척 - A3 : 1/100

REVISION & REVISIONS		
NO.	DATE	REVISION
5		
4		
3		
2		
1		

지도 DRAWN BY	유은지, 박호연
검사 CHECKED BY	정우영
승인 APPROVED BY	김재형
도면명 NAME OF DRAWING	

배면도, 좌측면도

일자 DATE	2022. 09.
축척 SCALE	A3: 1/100

건축사무소
에코플랜
Total Architecture
Engineers Group

서울특별시 송파구 삼학사로 25-1
신명빌딩 2층 (상전동 182-4)
TEL: (02)418-7902 / FAX: (02)418-7907
E-mail: ecoplan01@hanmail.net