


투 시 도




설계 개요 및 현황도

대지위치	서울특별시 구로구 구로동 429-254		
지역지구	제2종 일반주거지역		
대지면적	209 m ² (63.22PY)		
용 도	도시형생활주택 (원룸형 _ 9세대)		
건축면적	125.32m ²	높 이	15.75 m
건 폐 율	59.96 %	층 수	지상5층
용적률산정용 연 면 적	397.51m ²	조 경	11.65m ²
용 적 률	190.20%	정 화 조	부패정화조 30인
연 면 적	397.51m ²	주 차	5 대 설치

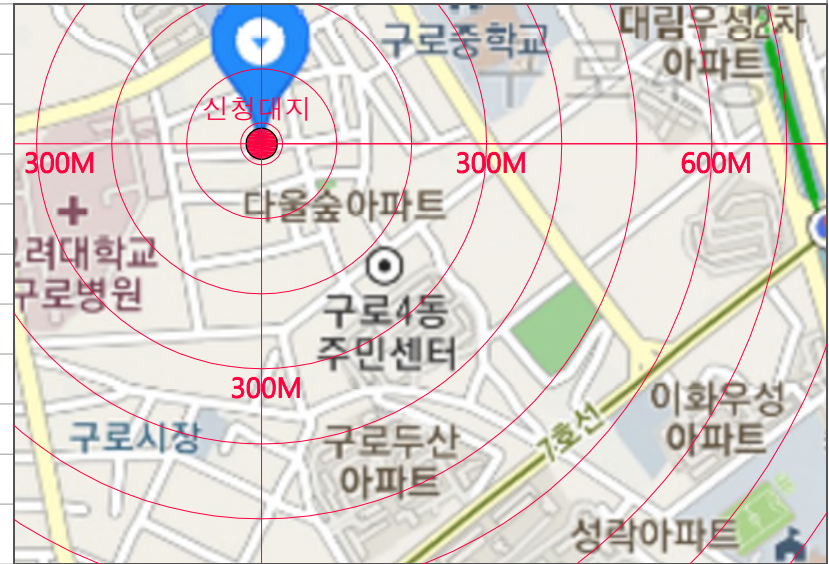

입 면 도

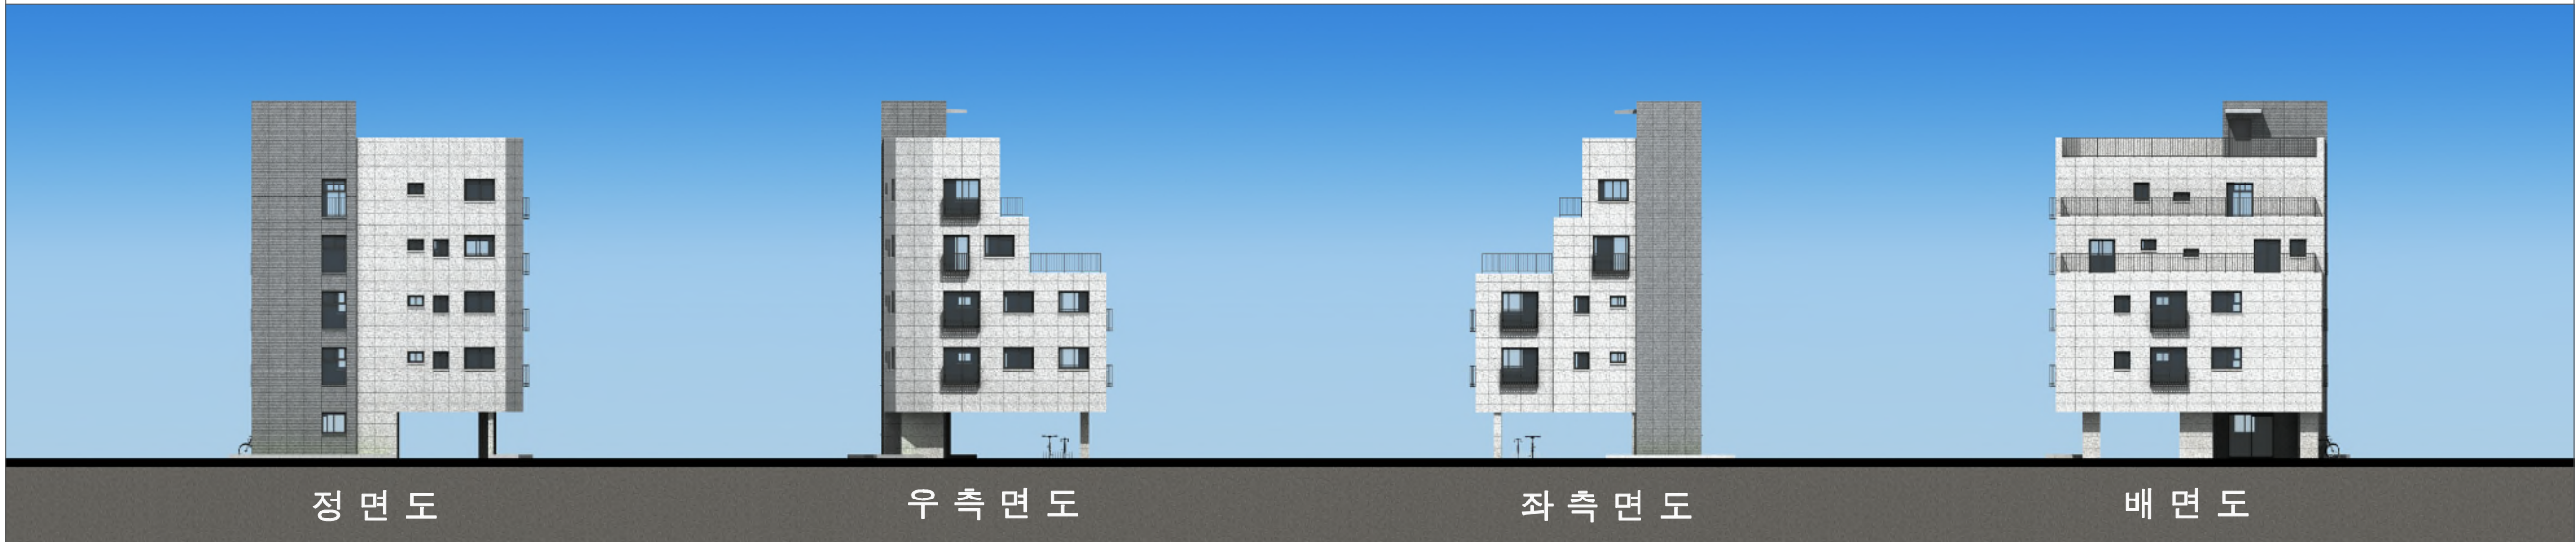

*본 상기도서 (조감도 포함)는 디자인심의회 제출된 심의도면으로서 설계도면과 일부 상이한 참조용이며 설계도면이 우선함.

PROJECT TITLE
사업명칭

구로구 구로동
429 - 254
도시형생활주택(원룸)
신축공사

사업번호 PROJCT NO.
도 면 명
2021-053(#)

NOTE

NO. ▲ REVISIONS ▲ DATE
번호 수정 일자

DESIGNED BY
설 계

CHECKED BY
심 사

APPROVED BY
승 인

CONSULTANTS
협 동 설 계

SCALE
축 척

DATE
일 자 2021. 09 .

DWG NO.
도면 번호 A-011


NAME OF DRAWING
도 면 명

디자인 개념-1

(주)에이이플러스
건축사무소
Architecture + Environment
AE+
TEL. 02-745-6511, 2057-5868
FAX. 0505-070-6511

디 자 인 의 도


- 보행자 출입구간 조경 & 사랑마당 설치-정면 & 후정설치 조경식재)
- 기능별 공간 구획의 집중화 평면 계획
- 원활한 보.차 출입 동선

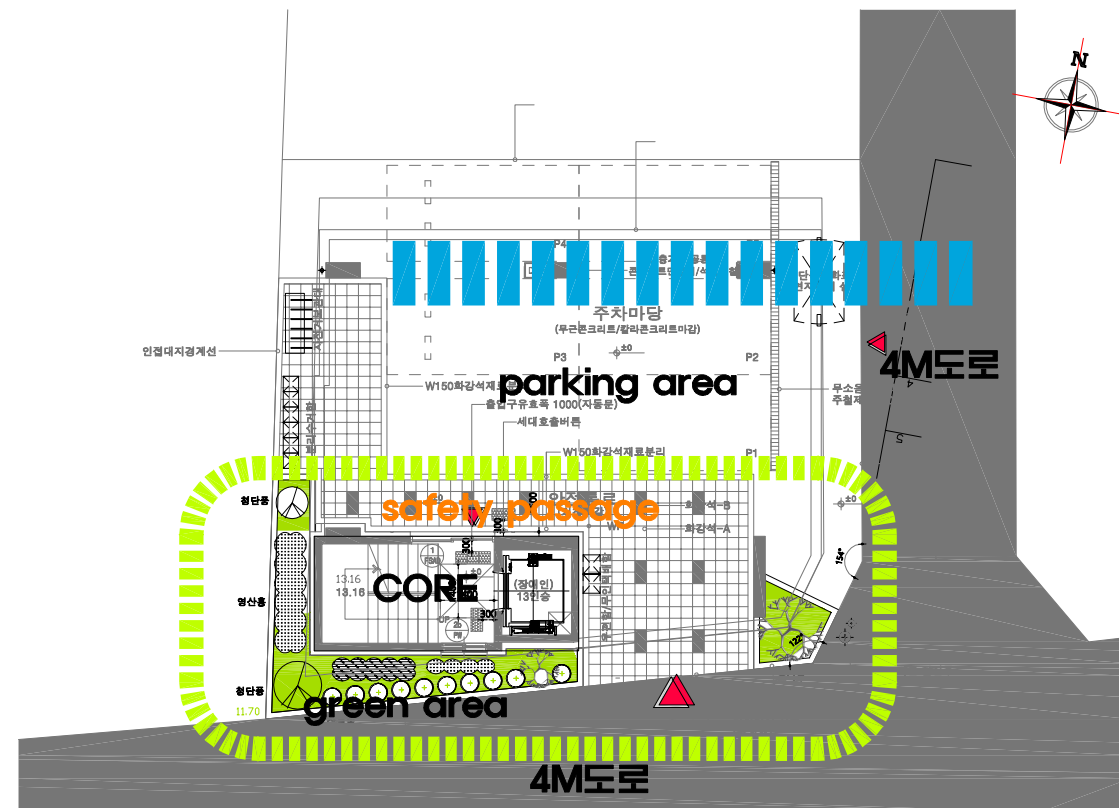

" 솿대 " < 가로 공간의 이정표.....! >



재 료 계 획

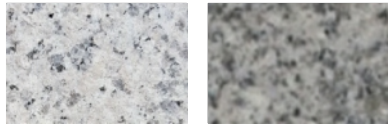외 벽	포천석(버너구이+물갈기)	
주차장바닥재	칼라무닉 콘크리트	
옥 외 난 간	주철제난간	
창호바(외부노출면)	진회색 PVC창호	

색 채 계 획

- 자연스러운 색상과 주변과의 조화
- 수직적 건물외관 및 천연재료 유지관리 고려
- 가로경관 미관성 및 친근성



진회색: 외벽주조색-1

밝은회색:외벽주조색-2

창호틀 : 짙은회색

*본 상기도서 (조감도 포함)는 디자인심의시 제출된 심의도면으로서 설계도면과 일부 상이한 참조용이며 설계도면이 우선함.

PROJECT TITLE
사업명칭

구로구 구로동
429 - 254
도시형생활주택(원룸)
신축공사

사업번호 PROJECT NO.

도면명
2021-053(#)

NOTE

NO. ▲ REVISIONS ▲ DATE
번호 수정 일자

DESIGNED BY
설계

CHECKED BY
심사

APPROVED BY
승인

CONSULTANTS
협동설계

SCALE
축척

DATE
일자 2021. 09 .

DWG NO.
도면번호 A-012

NAME OF DRAWING
도면명


디자인 개념-2

(주)에이이플러스
건축사무소

Architecture + Environment

AE+

TEL. 02-745-6511, 2057-5868
FAX. 0505-070-6511

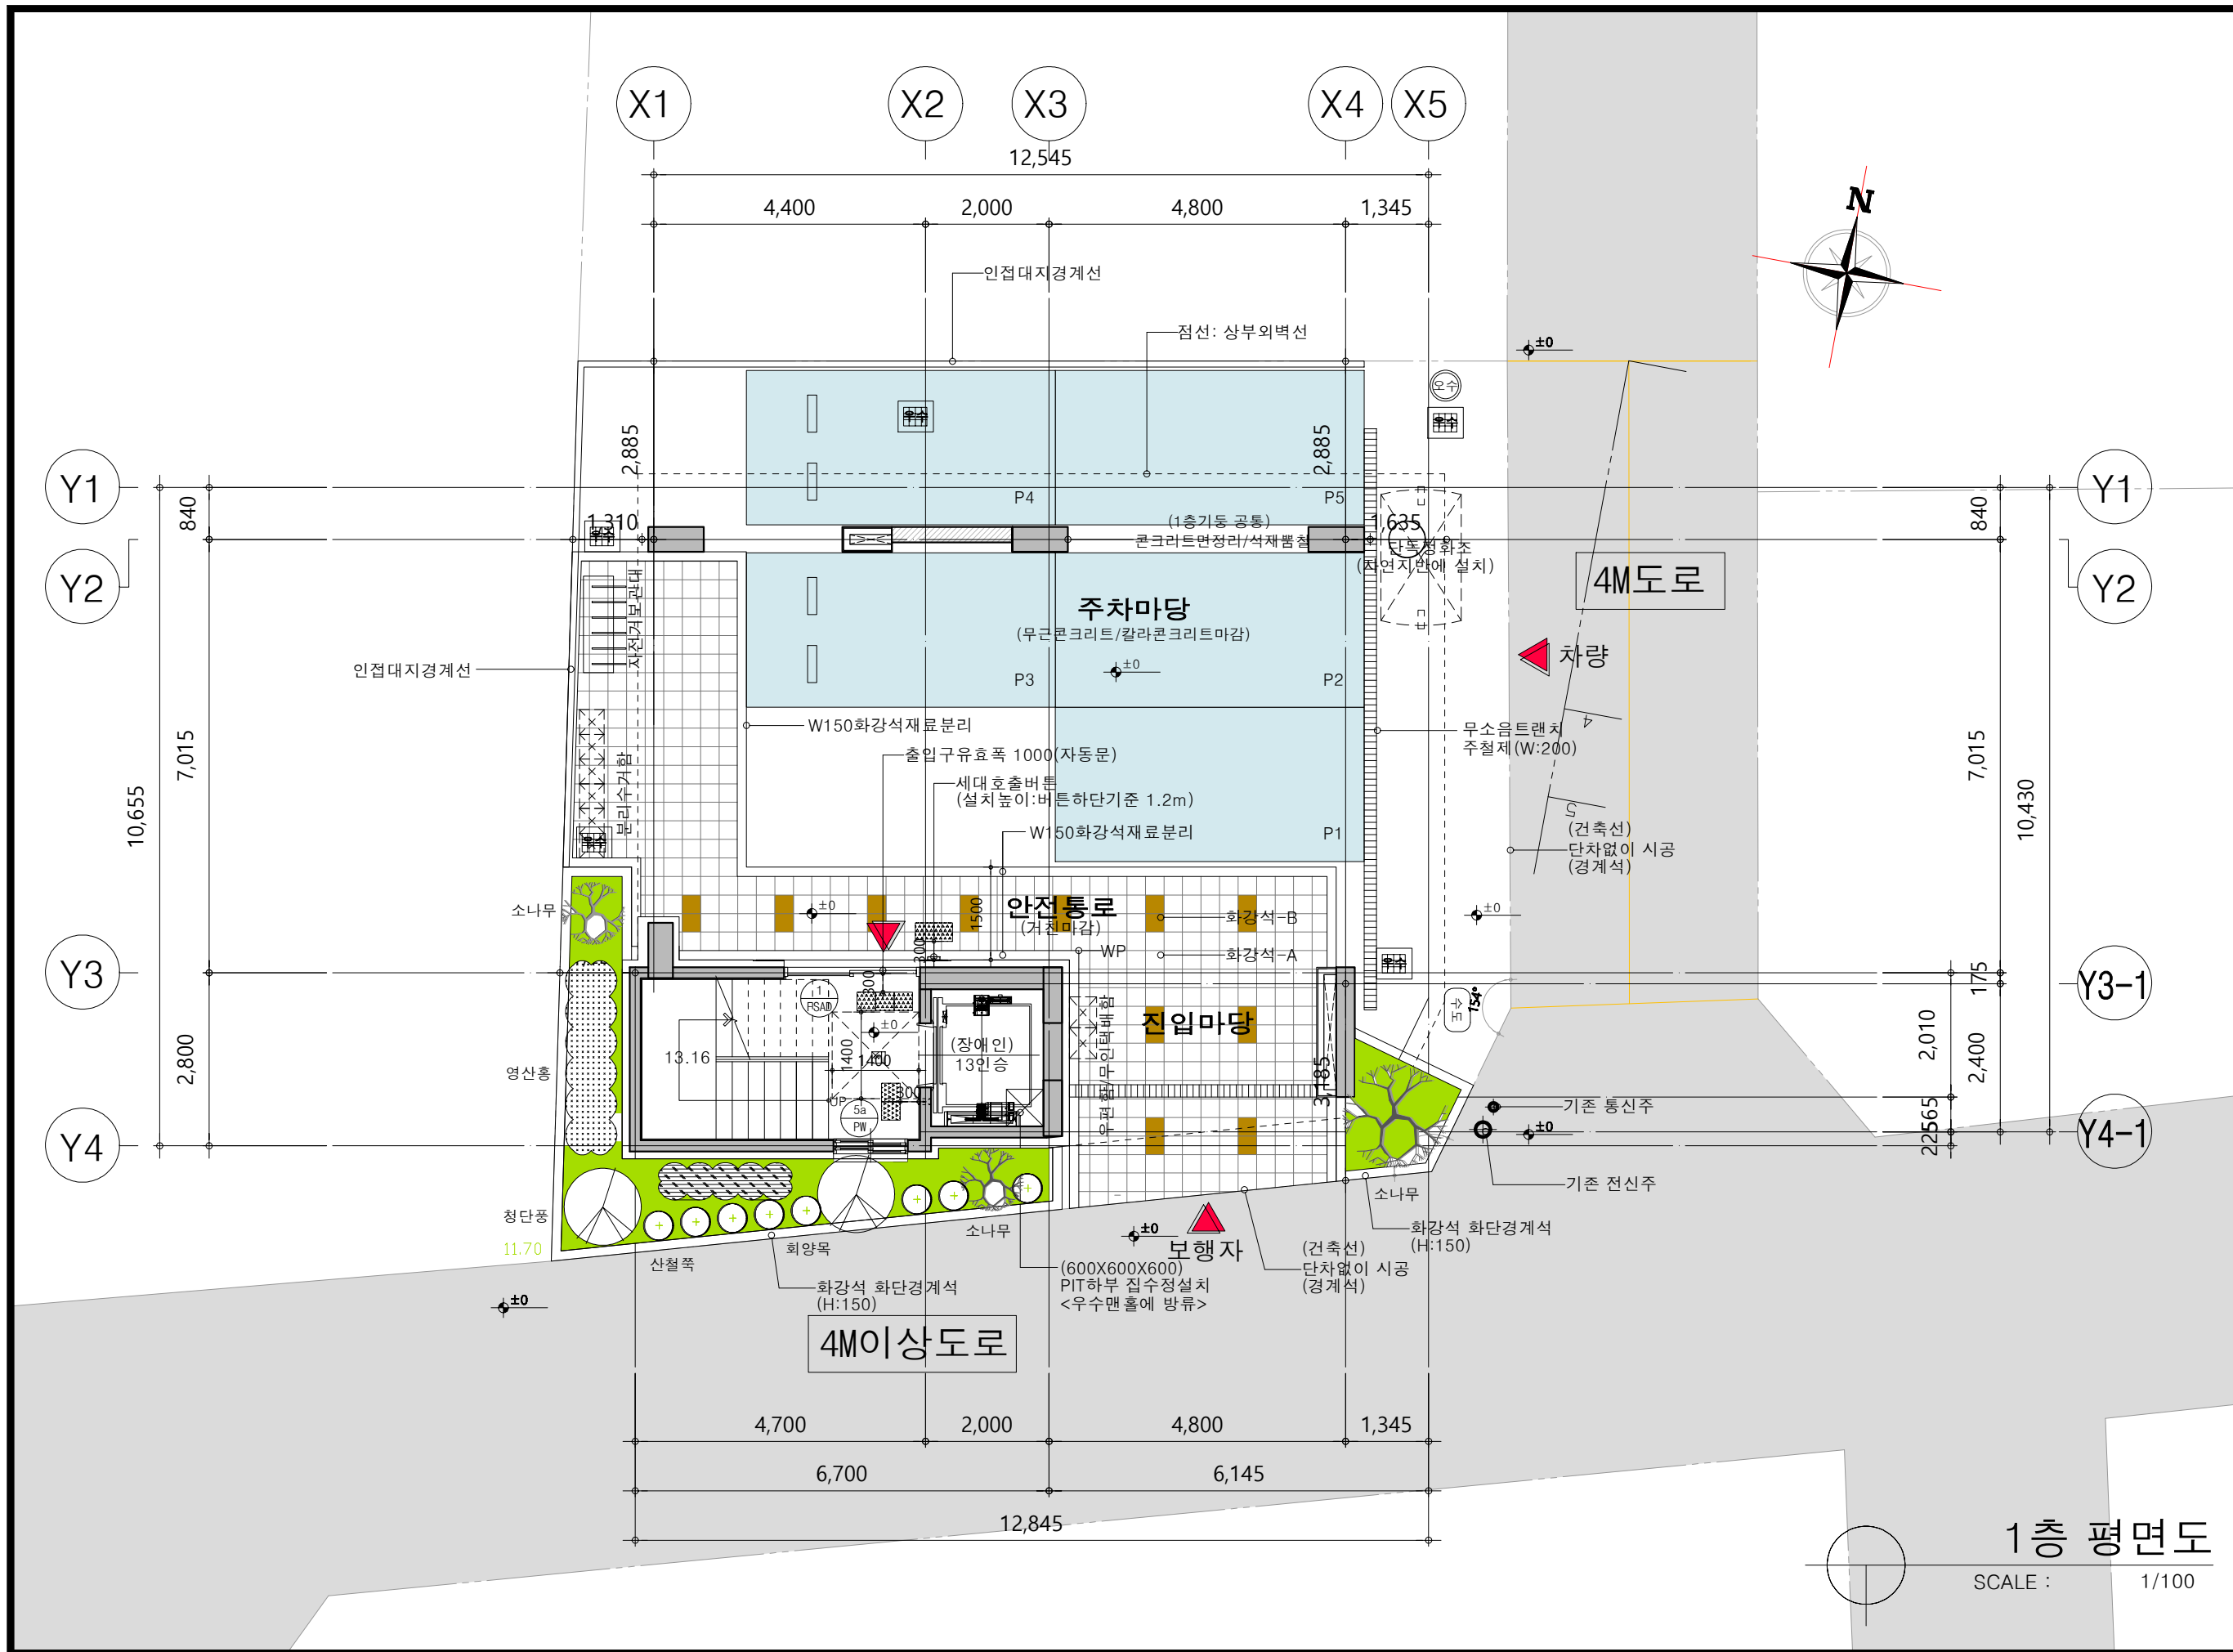

PROJECT TITLE
사업명칭

구로구 구로동
429 - 254
도시형생활주택(원룸)
신축공사

사업번호 PROJ. NO.
도면명

2021-053(#)

NOTE

NO. ▲ REVISIONS ▲ DATE
번호 수정 일자

DESIGNED BY
설계

CHECKED BY
심사

APPROVED BY
승인

CONSULTANTS
협동설계

SCALE
축척

1/100

DATE
일자

2021. 09 .

DWG NO.
도면번호


A-301

NAME OF DRAWING
도면명



1층 평면도

(주)에이이플러스
건축사무소
Architecture + Environment


TEL. 02-745-6511, 2057-5868
FAX. 0505-070-6511

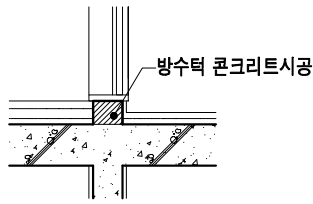

방수벽 무근콘크리트시공
(다용도실, 욕실, 옥상출입문)

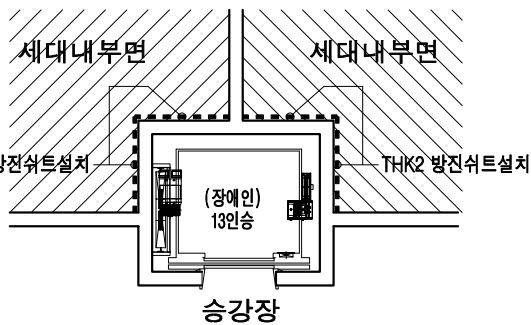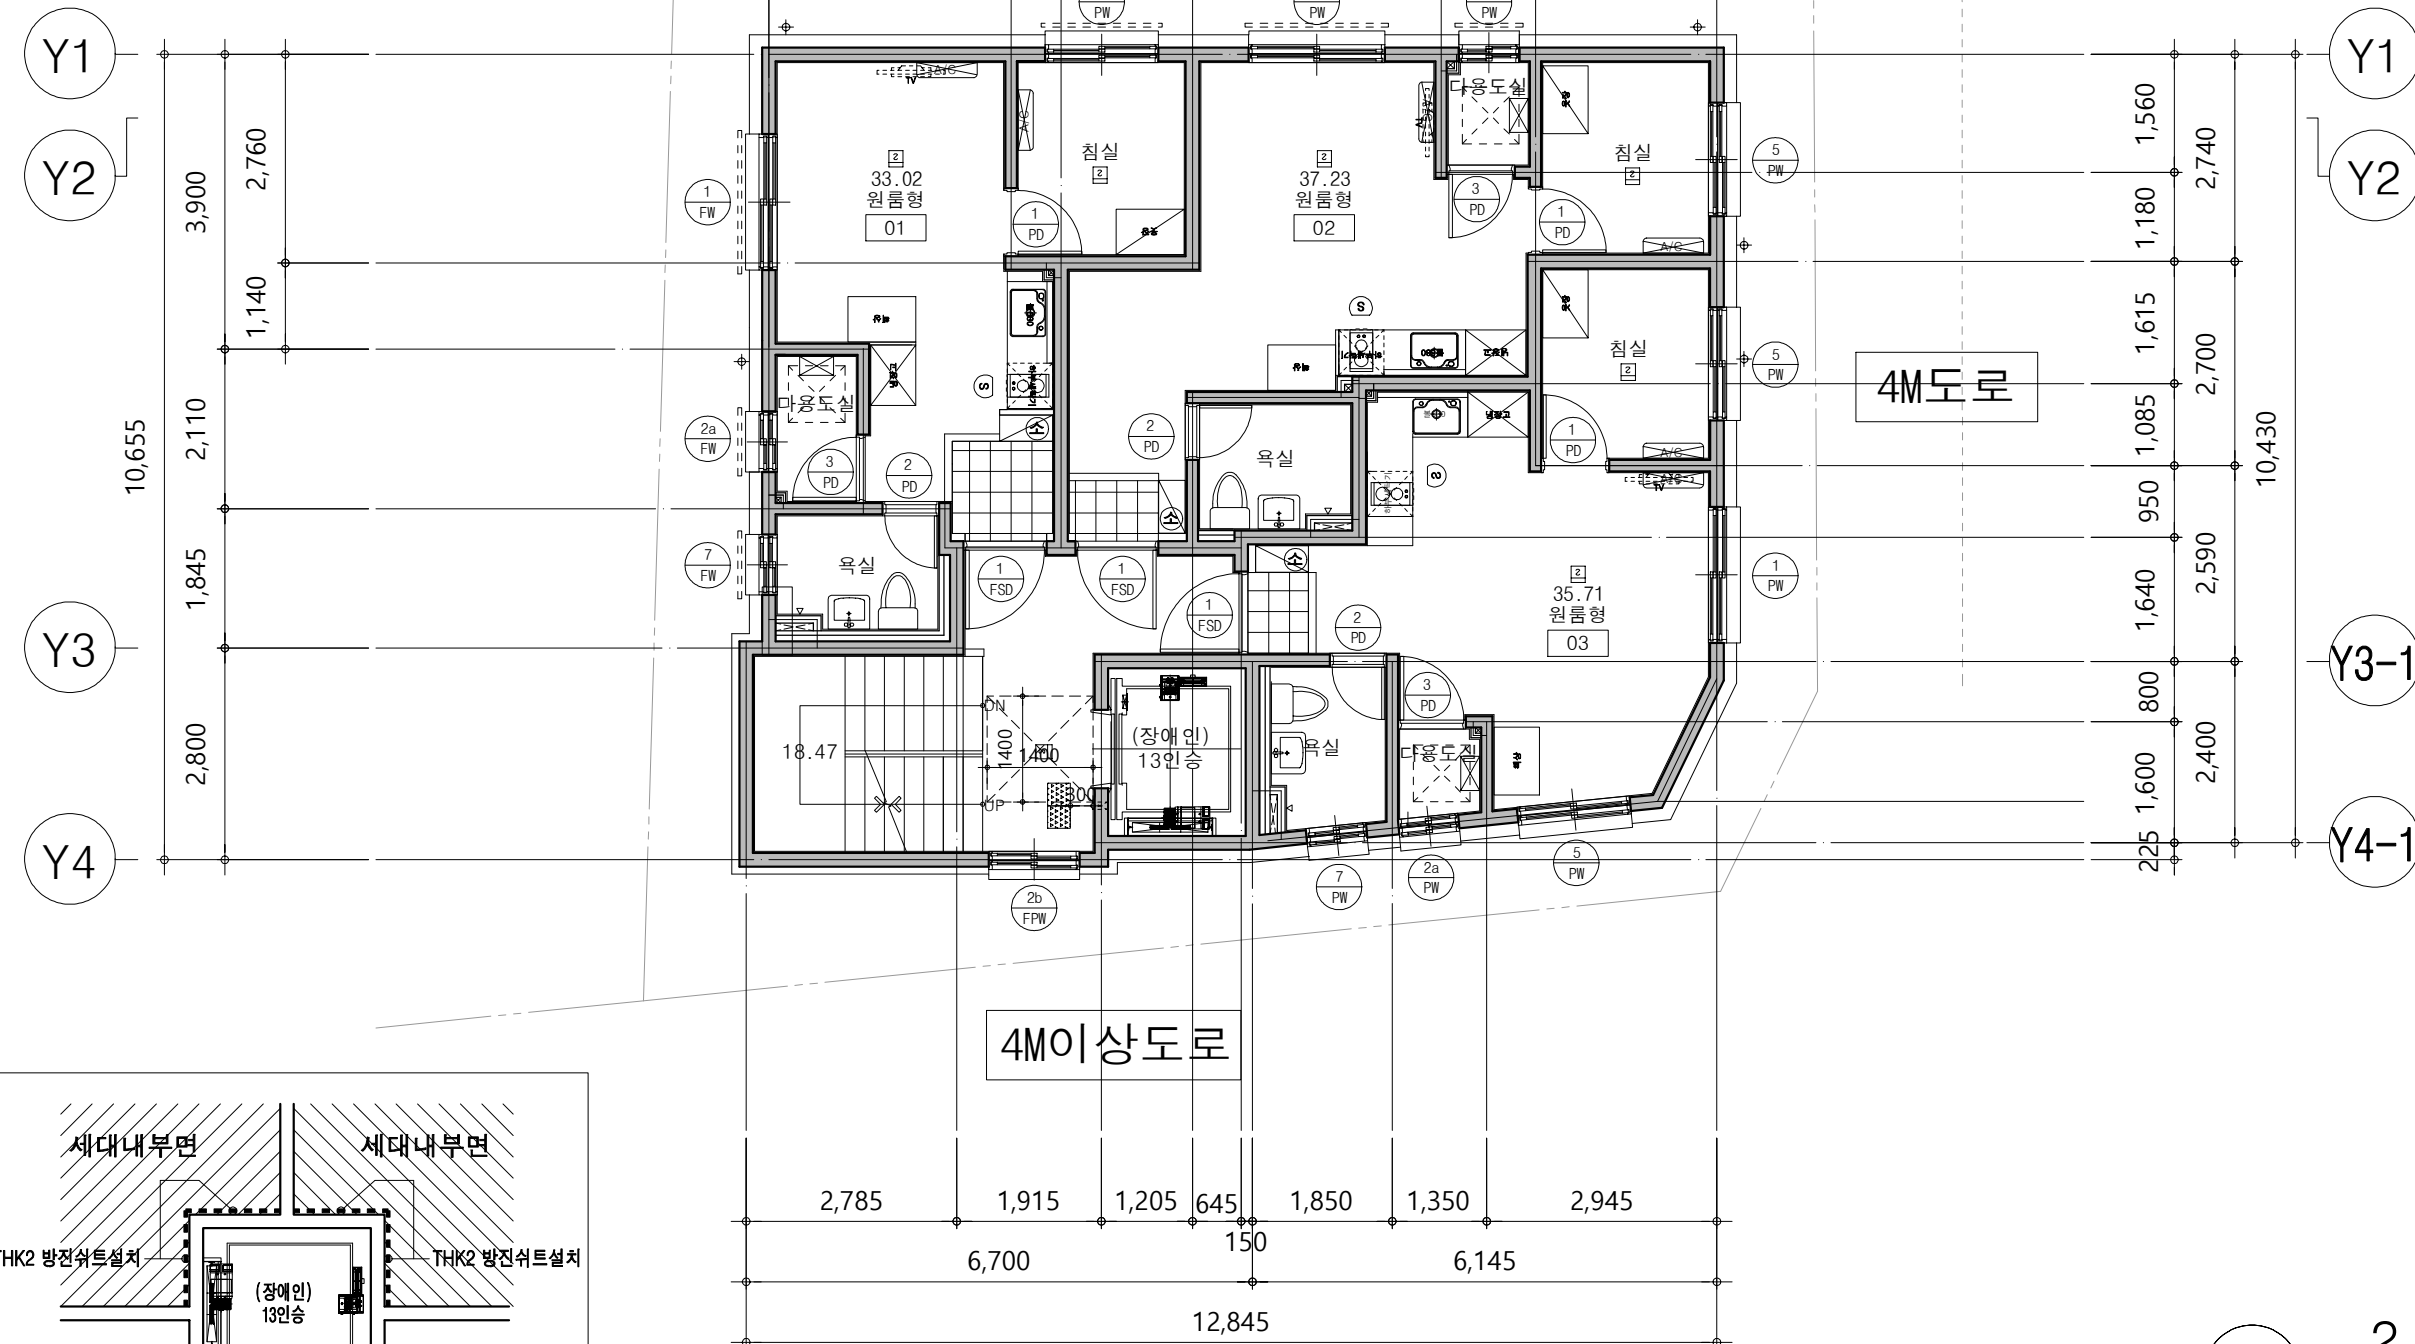

승강로에 면한 각층세대부분 방진셔틀설치도

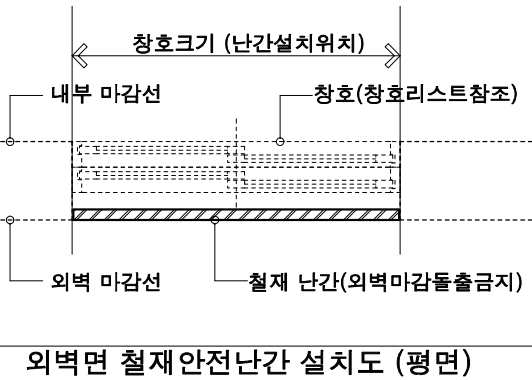

- 주방및 가구등 빌트인
- 청년주택 :
- 1.냉장고
 - 2.벽걸이 에어컨(거실&주방)
(침실 : 에어컨 배관설치)
 - 1, 2 항목 : 에너지효율 1등급
 - 3.세탁기(싱크대 하부설치)
(에너지효율 2등급)
 - 4.불박이장 또는 이동식옷장
 - 5.책상
- * 주의사항
- 매입임대주택 품질기준
도면 : A-021~034 참조할것.

PROJECT TITLE
사업명칭
구로구 구로동
429 - 254
도시형생활주택(원룸)
신축공사

사업번호 PROJ. NO.
도면번호
2021-053(#)

- NOTE
- ⑧ 단독경보감지기(연기식)
 - ⑨ 단독경보감지기(열감지)
 - ⑩ ABC분말소화기(3.3KG)
 - ⑪ 가스누설경보기
 - 차면시설
 - 보일러
 - 에어컨 실외기
 - * 구조 *

- 1.콘크리트 : fck = 24 MPa
- 2. 철근 : fy = 400 MPa
- 3. 세대간벽두께:180mm(복배근)
(미장미감포함 210mm이상)
- 4. 외벽두께:180mm(복배근)
- 5. 코아벽두께:180mm(복배근)
- 6. 스라브두께:210mm(복배근)

NO. ▲ REVISIONS ▲ DATE
번호 수정 일자

DESIGNED BY
설 계

CHECKED BY
심 사

APPROVED BY
승 인

CONSULTANTS
협동설계

SCALE
축척 1/100



DATE
일자 2021. 09 .

DWG NO.
도면번호 A-302

NAME OF DRAWING
도면명

2,3층 평면도

(주)에이이플러스
건축사무소
Architecture + Environment
AE+
TEL. 02-745-6511, 2057-5868
FAX. 0505-070-6511

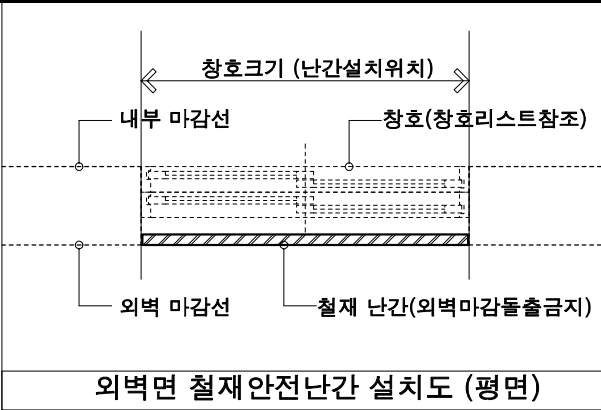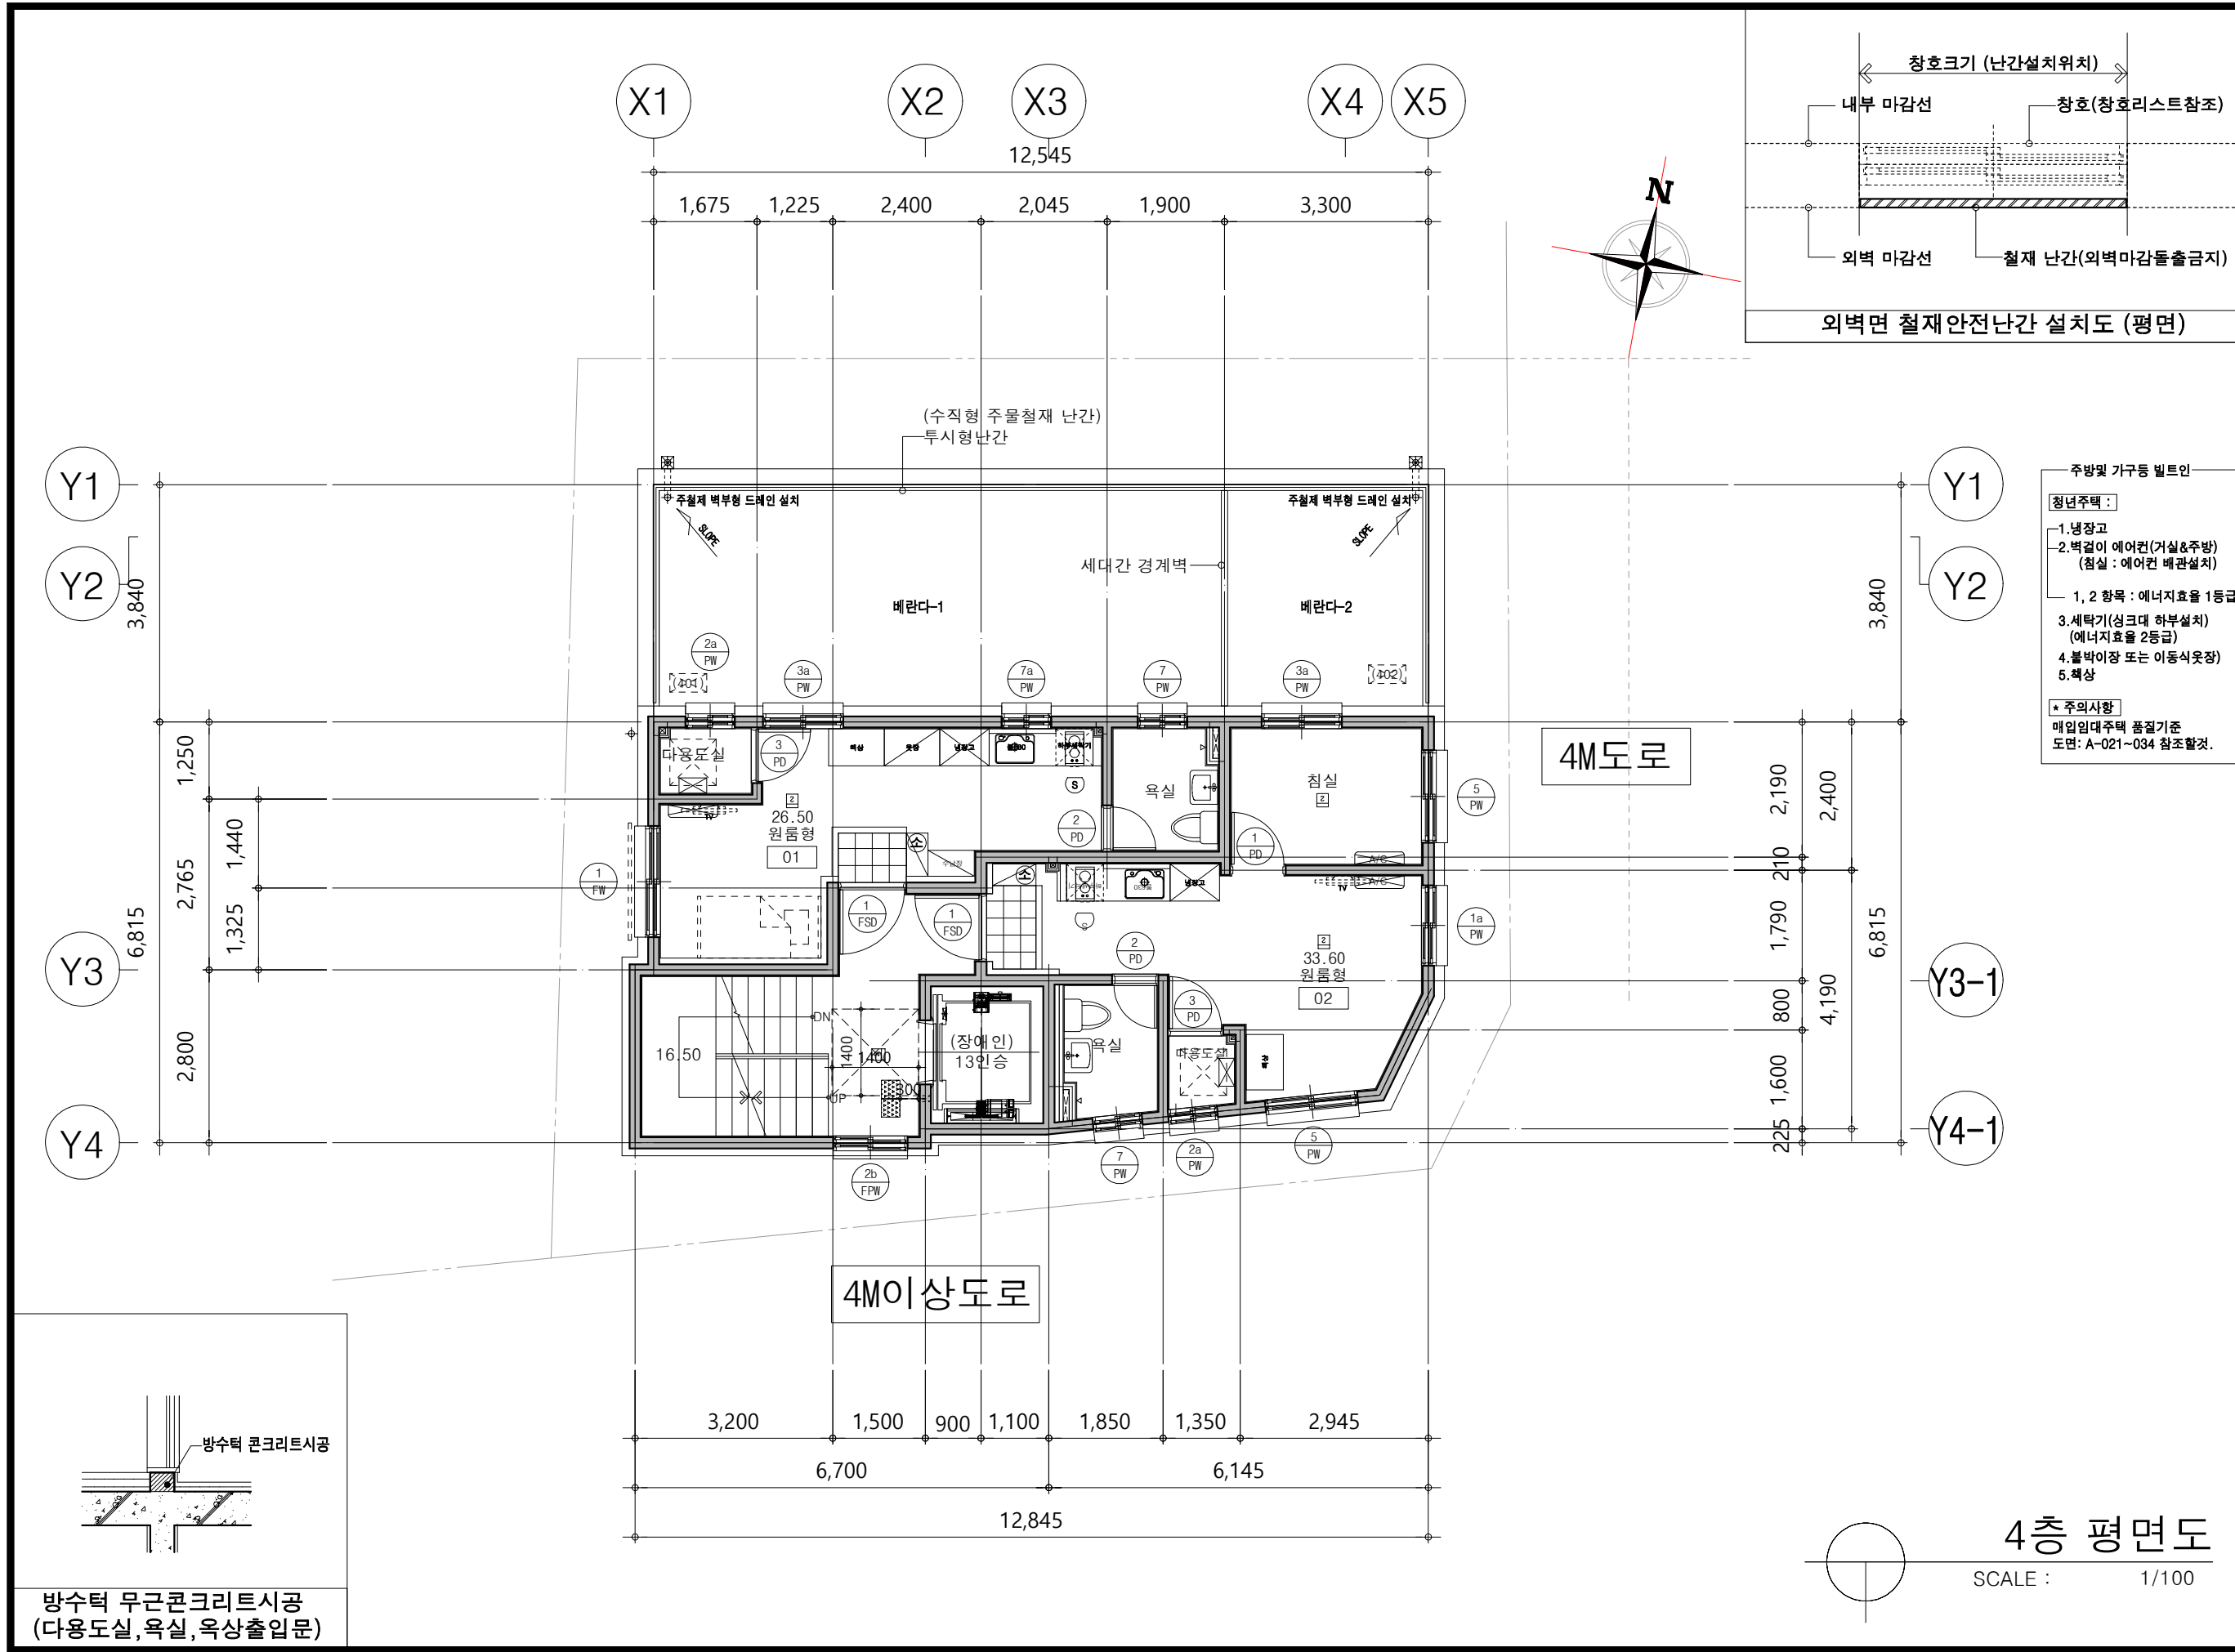

- 주방 및 가구 등 빌트인
- 창년주택 :
- 1. 냉장고
 - 2. 벽걸이 에어컨 (거실 & 주방)
(침실 : 에어컨 배관 설치)
 - 1, 2 항목 : 에너지 효율 1등급
 - 3. 세탁기 (싱크대 하부 설치)
(에너지 효율 2등급)
 - 4. 불박이장 또는 이동식 옷장
 - 5. 책상
- * 주의사항
- 매입 임대주택 품질기준
도면 : A-021~034 참조할 것.

PROJECT TITLE
사업명칭

구로구 구로동
429 - 254
도시형생활주택(원룸)
신축공사

사업번호 PROJ. NO.
도면번호

2021-053(#)

NOTE

단독경보감지기(연기식)
단독경보감지기(열감지)
ABC분말소화기(3.3KG)
가스누설경보기

차면시설

보일러
에어컨 실외기

* 구조 *

- 1. 콘크리트 : fck = 24 MPa
- 2. 철근 : fy = 400 MPa
- 3. 세대간벽두께 : 180mm (복배근)
- (미장 마감 포함 210mm 이상)
- 4. 외벽두께 : 180mm (복배근)
- 5. 코아벽두께 : 180mm (복배근)
- 6. 스라브두께 : 210mm (복배근)

NO. 번호	REVISIONS 수정	DATE 일자
-----------	-----------------	------------

DESIGNED BY
설계

CHECKED BY
심사

APPROVED BY
승인

CONSULTANTS
협동설계

SCALE
축척

1/100

DATE
일자

2021. 09 .



DWG NO.
도면번호

A-303

NAME OF DRAWING
도면명

4층 평면도

(주)에이이플러스
건축사무소
Architecture + Environment
AE+
TEL. 02-745-6511, 2057-5868
FAX. 0505-070-6511

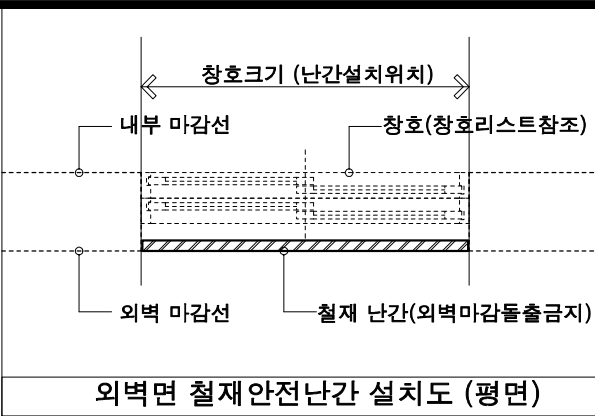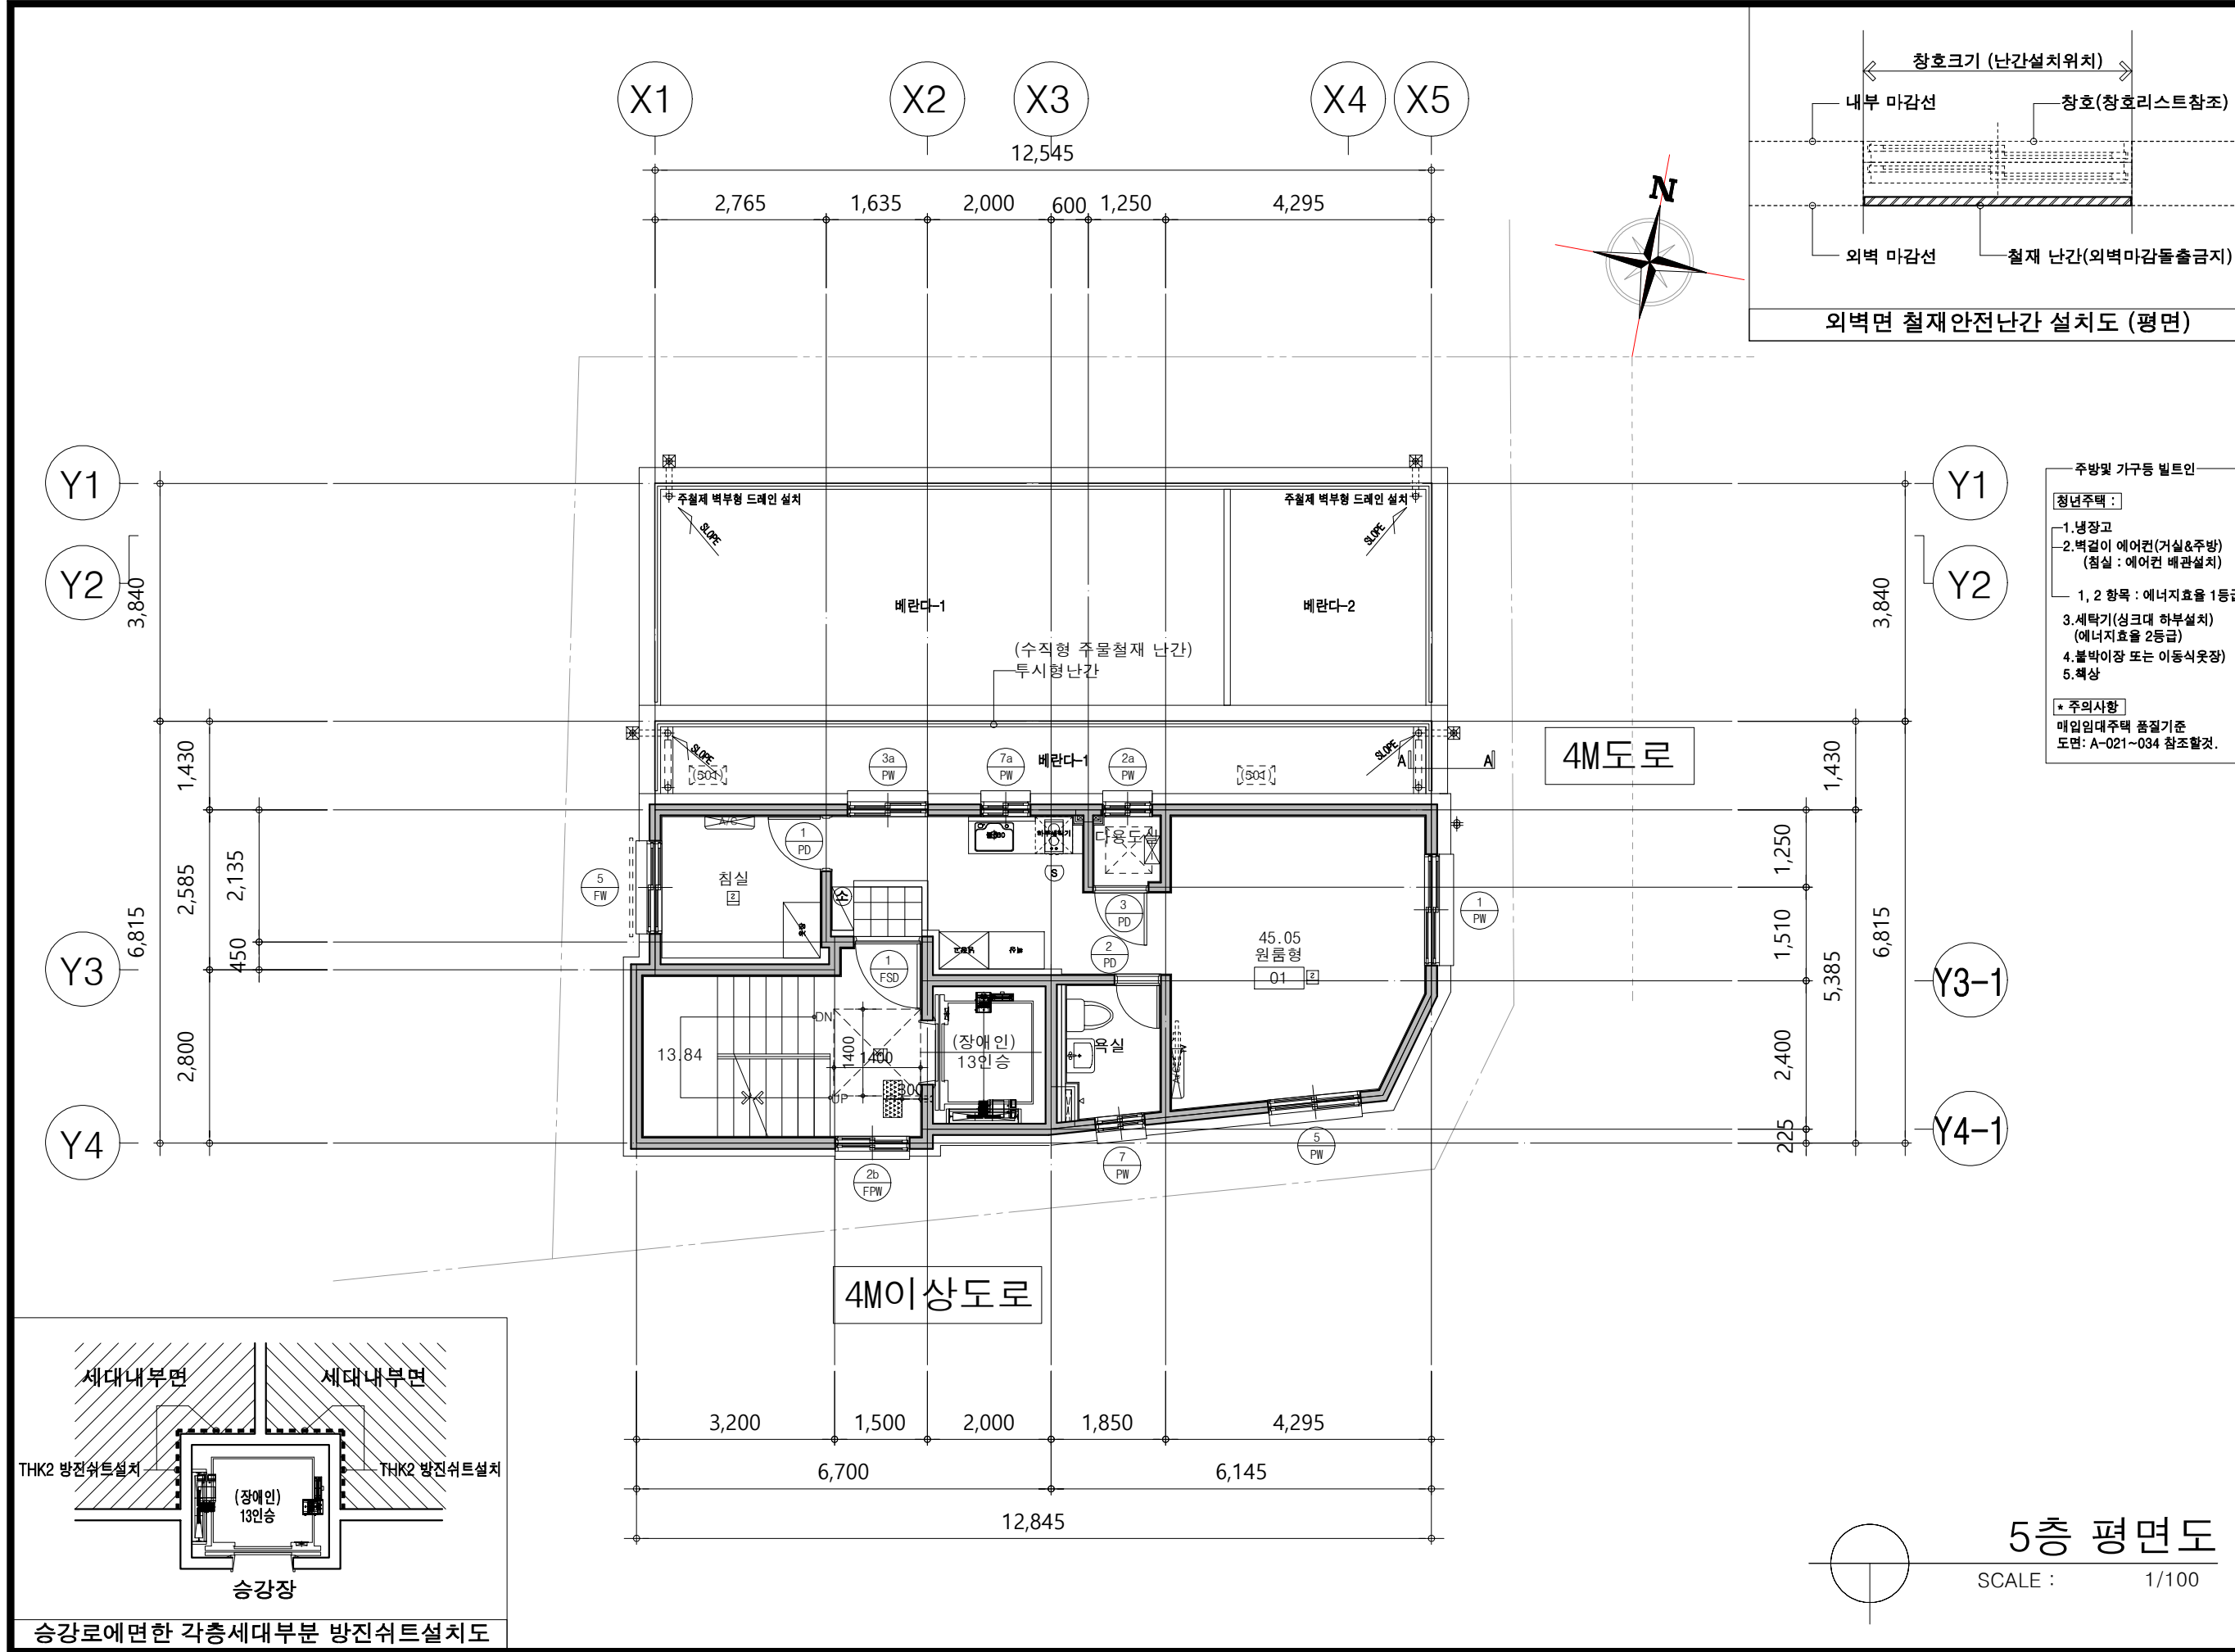

- 주방및 가구등 빌트인
- 청년주택 :
- 1.냉장고
 - 2.벽걸이 에어컨(거실&주방)
(침실 : 에어컨 배관설치)
 - 1, 2 항목 : 에너지효율 1등급
 - 3.세탁기(싱크대 하부설치)
(에너지효율 2등급)
 - 4.불박이장 또는 이동식옷장
 - 5.책상
- * 주의사항
- 매입임대주택 품질기준
도면: A-021~034 참조할것.

PROJECT TITLE
사업명칭

구로구 구로동
429 - 254
도시형생활주택(원룸)
신축공사

사업번호 PROJ. NO.
도면명

2021-053(#)

NOTE

- ⑧ 단독경보감지기(연기식)
- ⑨ 단독경보감지기(열감지)
- ③ ABC분말소화기(3.3KG)
- ⑥ 가스누설경보기

차면시설

- 보일러
- 에어컨 실외기

* 구조 *

- 1.콘크리트: fck = 24 MPa
- 2.철근: fy = 400 MPa
- 3.세대간벽두께:180mm(복배근)
- (미장마감포함 210mm이상)
- 4.외벽두께:180mm(복배근)
- 5.코아벽두께:180mm(복배근)
- 6.스라브두께:210mm(복배근)

NO.	REVISIONS	DATE
번호	수정	일자

DESIGNED BY
설계

CHECKED BY
심사

APPROVED BY
승인

CONSULTANTS
협동설계

SCALE
축척

1/100

DATE
일자

2021. 09 .


DWG NO.
도면번호

A-304

NAME OF DRAWING
도면명

5층 평면도

(주)에이이플러스
건축사무소
Architecture + Environment
AE+
TEL. 02-745-6511, 2057-5868
FAX. 0505-070-6511

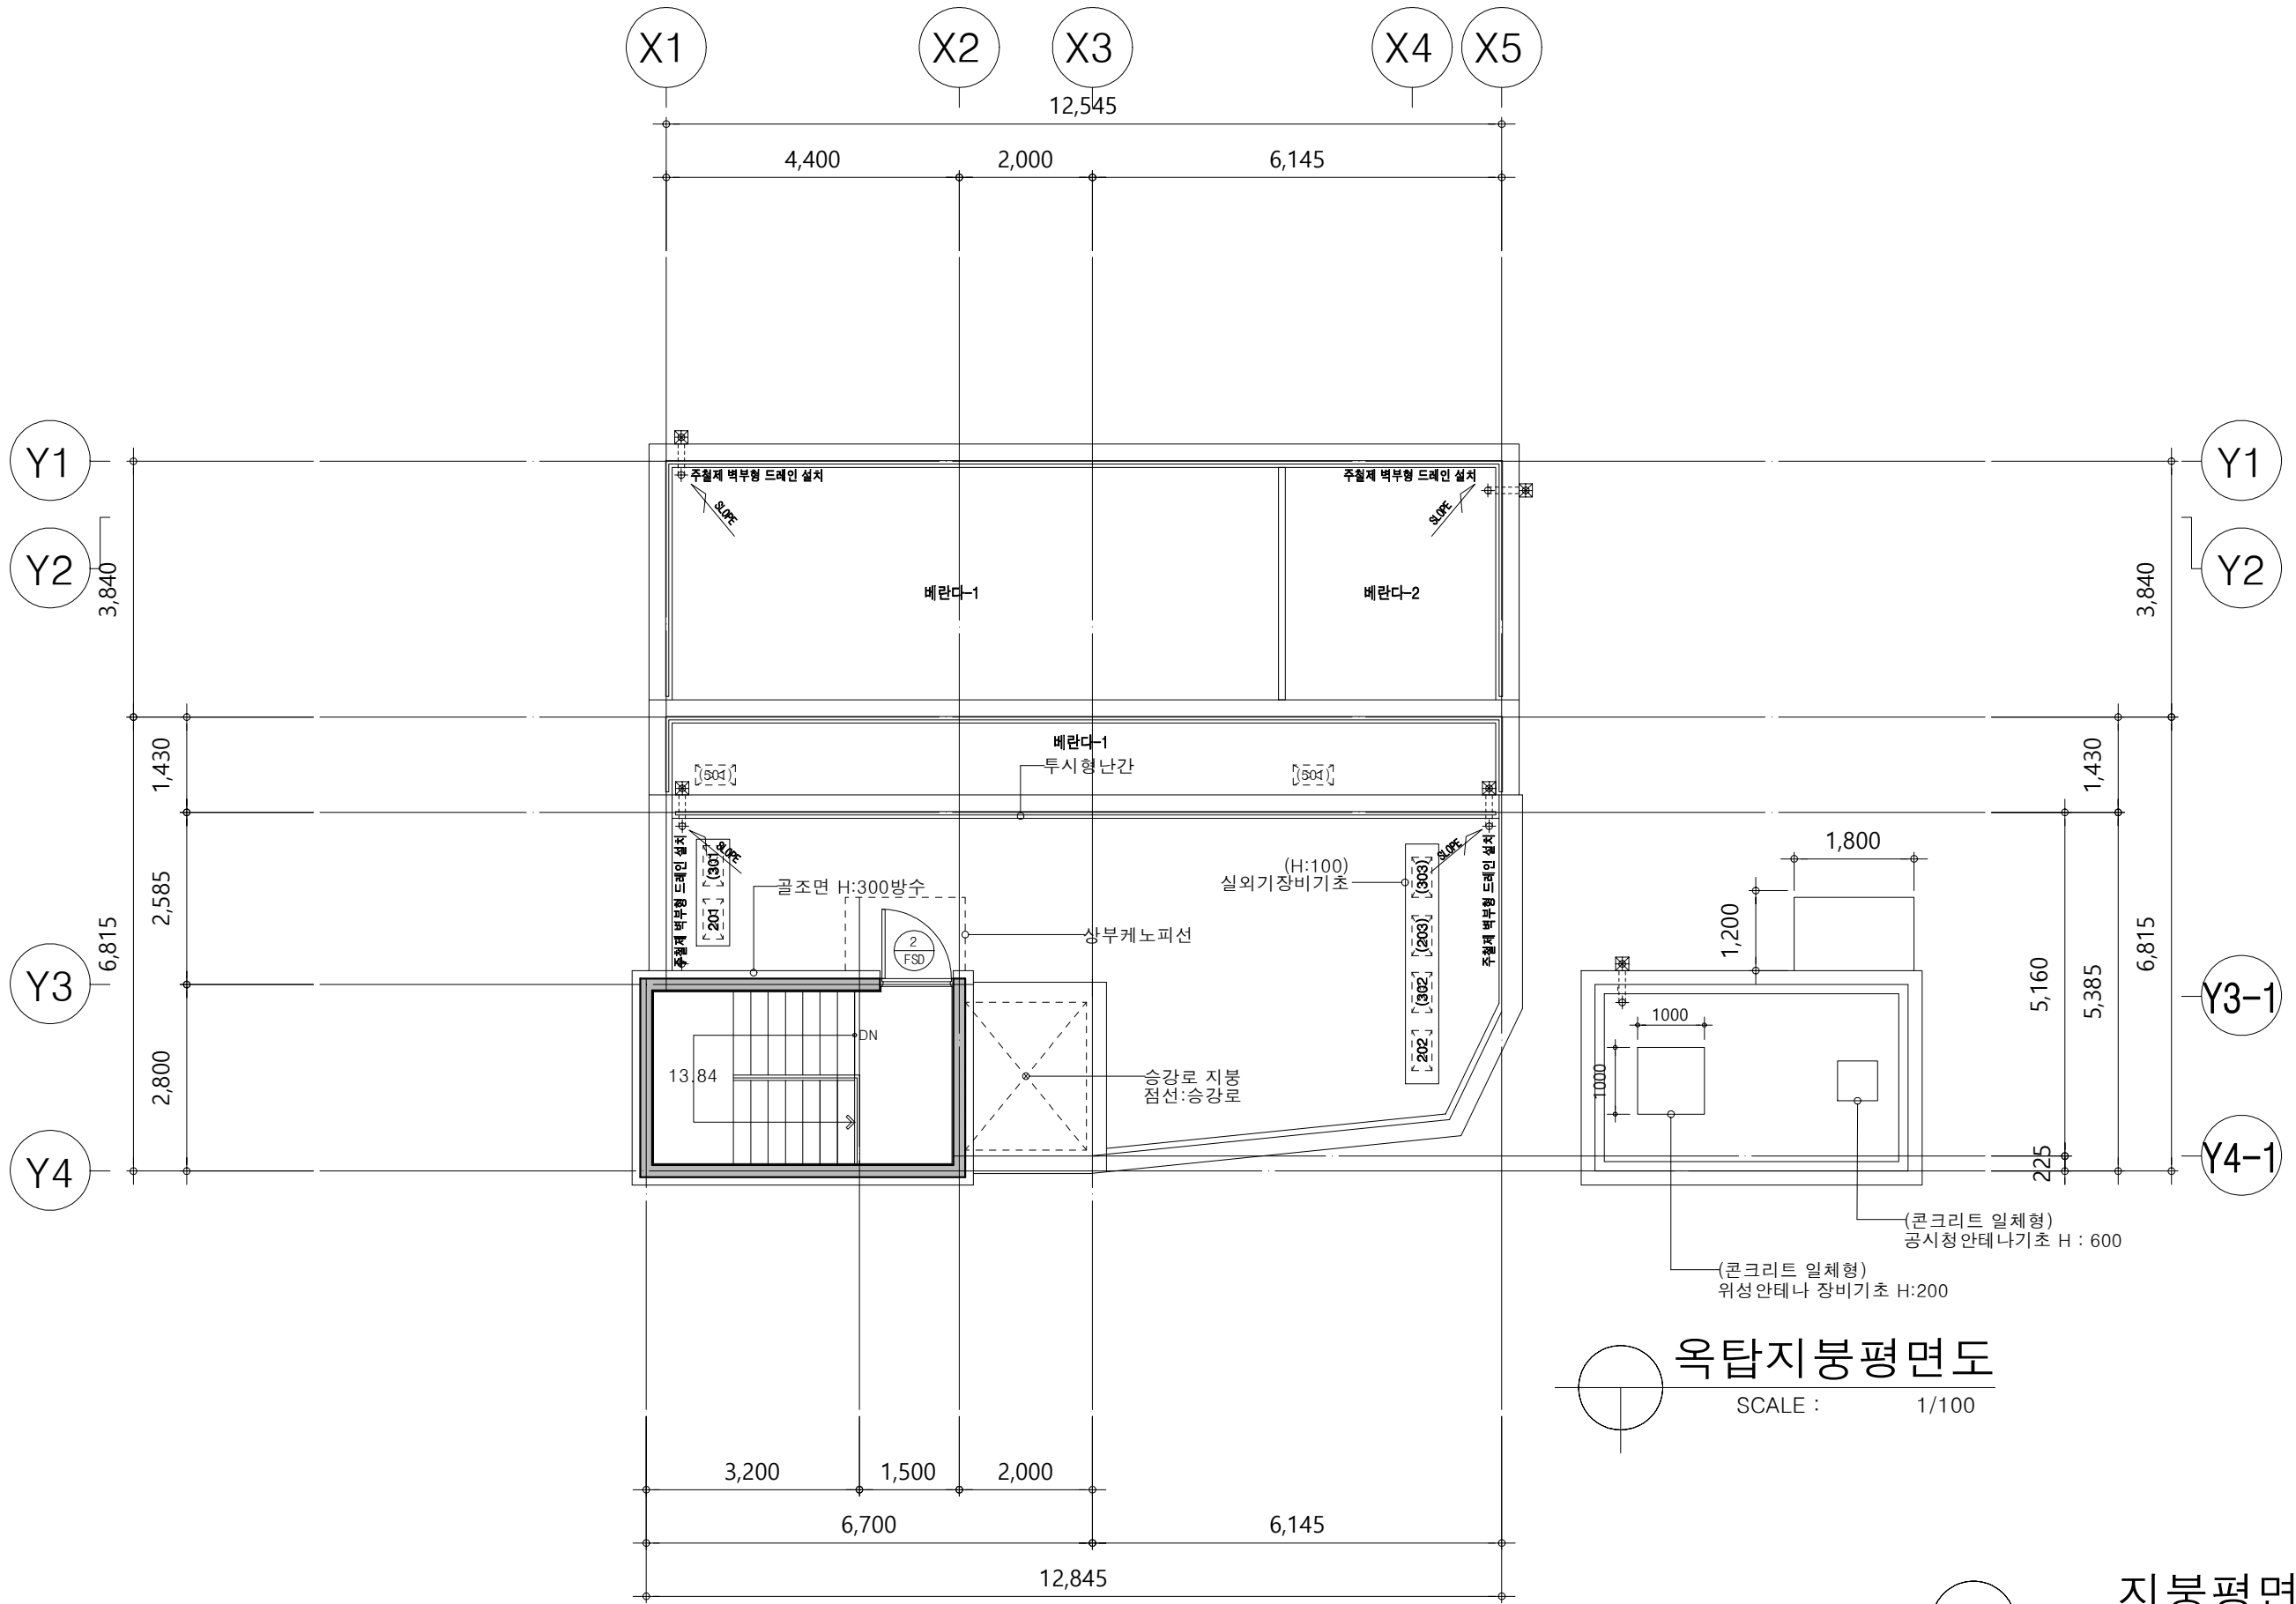

옥탑지붕평면도
SCALE : 1/100

지붕평면도
SCALE : 1/100

PROJECT TITLE
사업명칭
구로구 구로동
429 - 254
도시형생활주택(원룸)
신축공사

사업번호 PROJ. NO.
도면명
2021-053(#)

NOTE

NO. ▲ REVISIONS ▲ DATE
번호 수정 일자

DESIGNED BY
설계

CHECKED BY
심사

APPROVED BY
승인

CONSULTANTS
협동설계

SCALE
축척 1/100


DATE
일자 2021. 09 .

DWG NO.
도면번호 A-305


NAME OF DRAWING
도면명

옥탑 및
지붕 평면도

(주)에이이플러스
건축사무소
Architecture + Environment
AE+
TEL. 02-745-6511, 2057-5868
FAX. 0505-070-6511

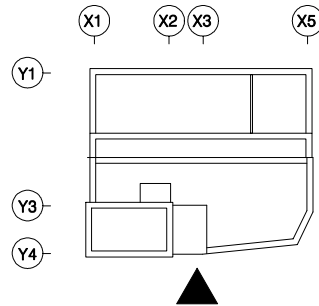


KEY PLAN

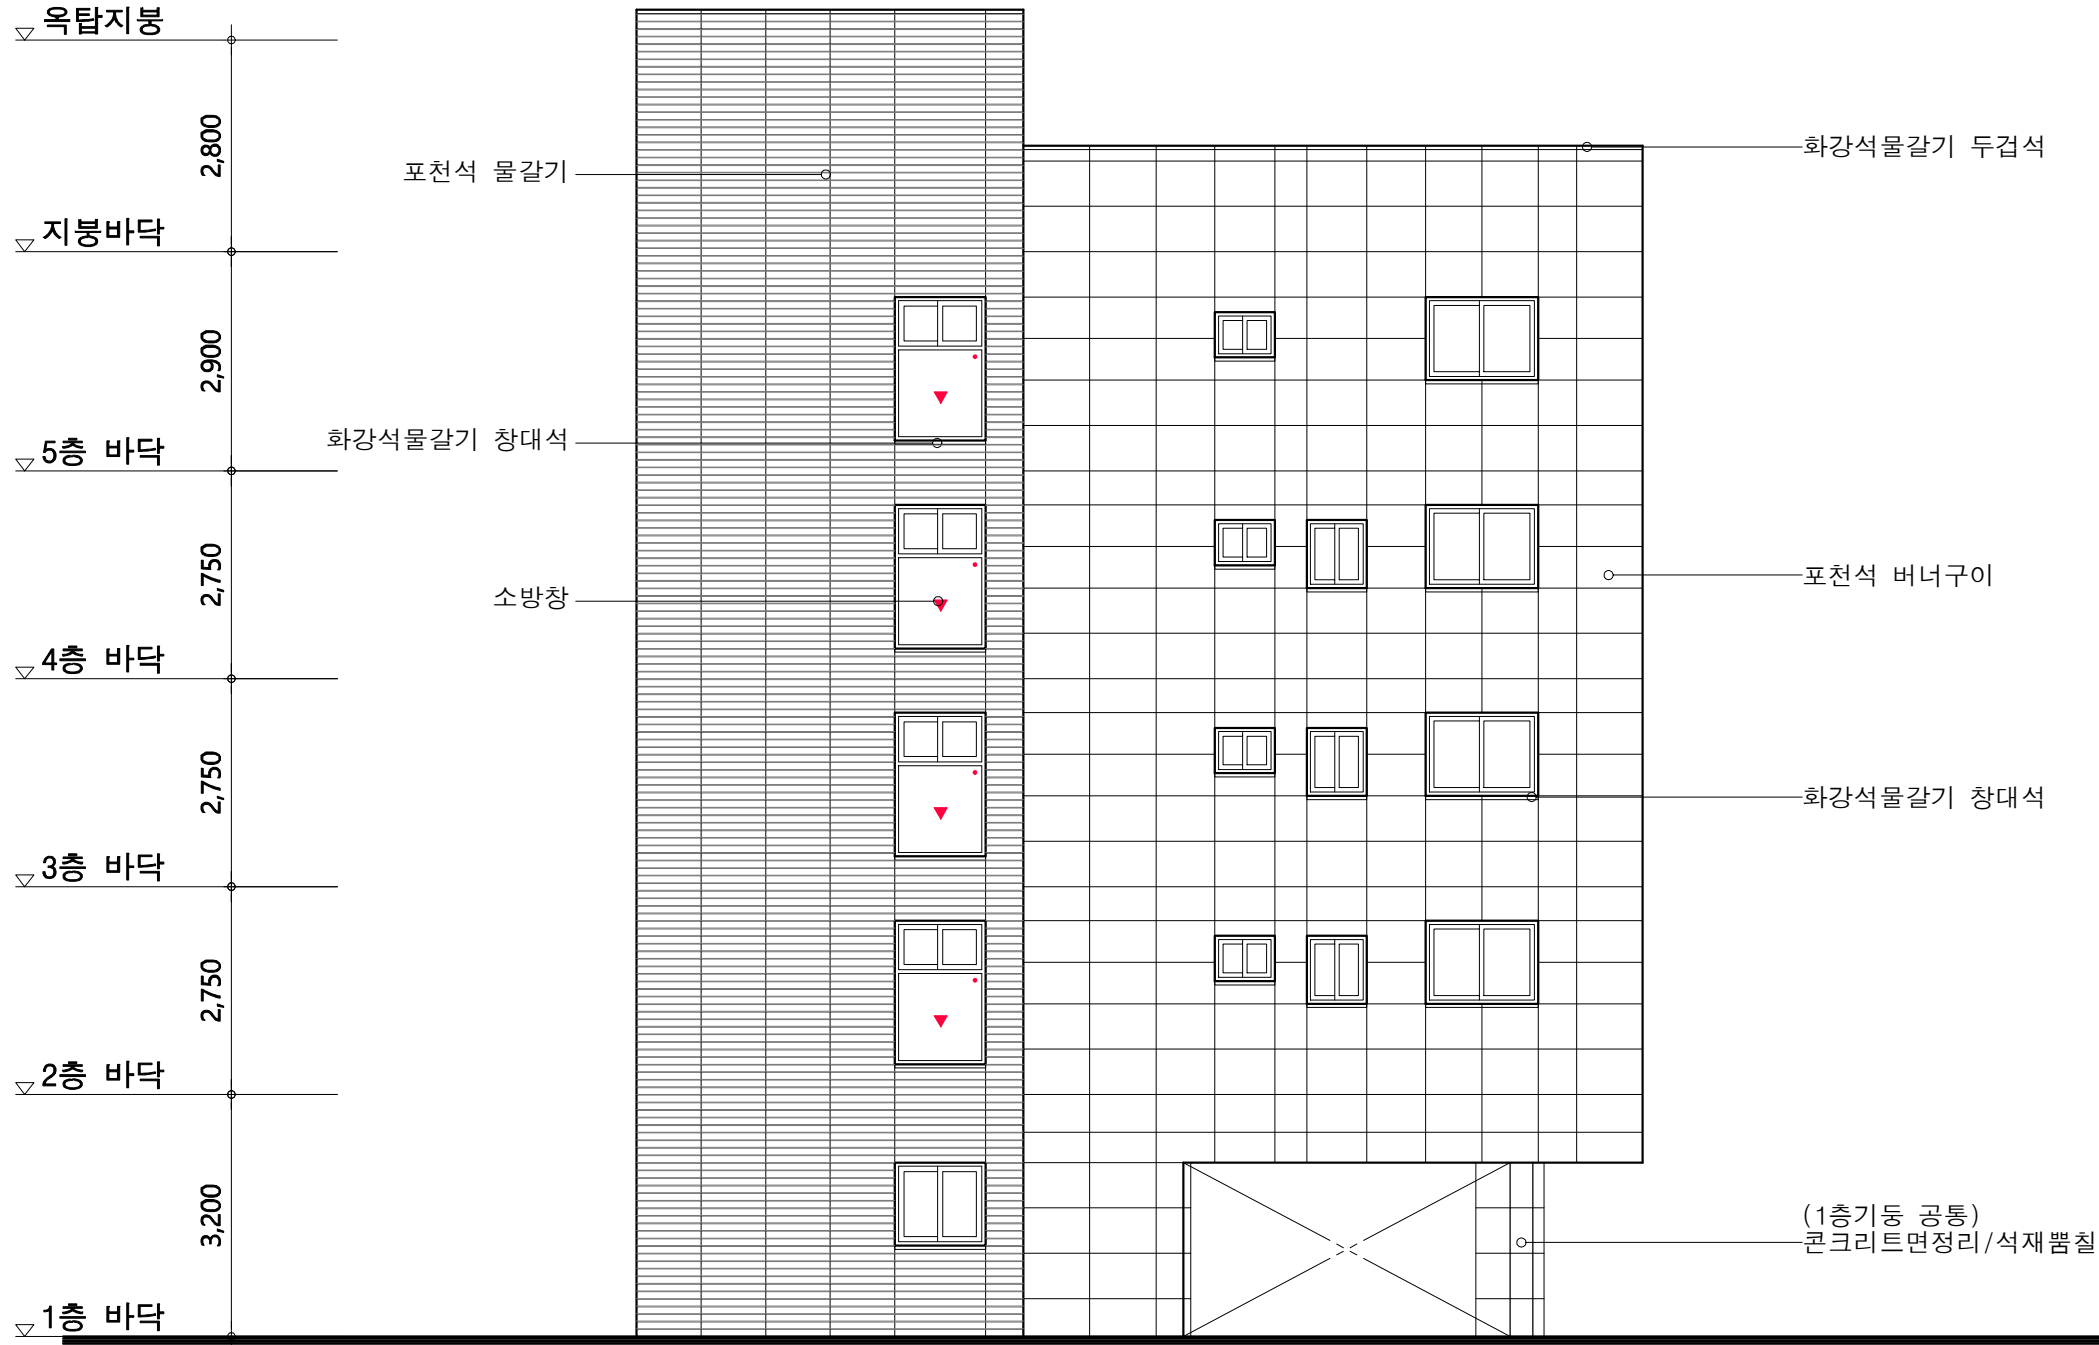

* 외부면 노출 창호프레임 칼라

건본색상
(질은회색)

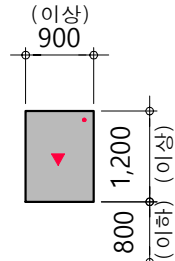

설치위치: 도로면 입면
소방관 진입창 범례

PROJECT TITLE
사업명칭
구로구 구로동
429 - 254
도시형생활주택(원룸)
신축공사

사업번호 PROJ. NO.
도면명
2021-053(#)

NOTE

NO. ▲ REVISIONS ▲ DATE
번호 수정 일자

DESIGNED BY
설계

CHECKED BY
심사

APPROVED BY
승인

CONSULTANTS
협동설계

SCALE
축척 1/100

DATE
일자 2021. 09 .


DWG NO.
도면번호 A-401

NAME OF DRAWING
도면명


정면도

정면도


SCALE : A3 : 1/100

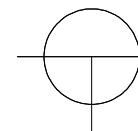

(주)에이이플러스
건축사무소
Architecture + Environment
AE+
TEL. 02-745-6511, 2057-5868
FAX. 0505-070-6511

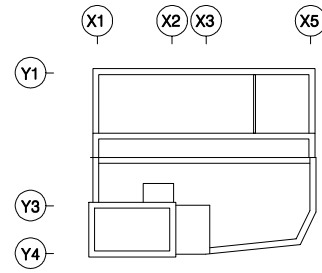

KEY PLAN

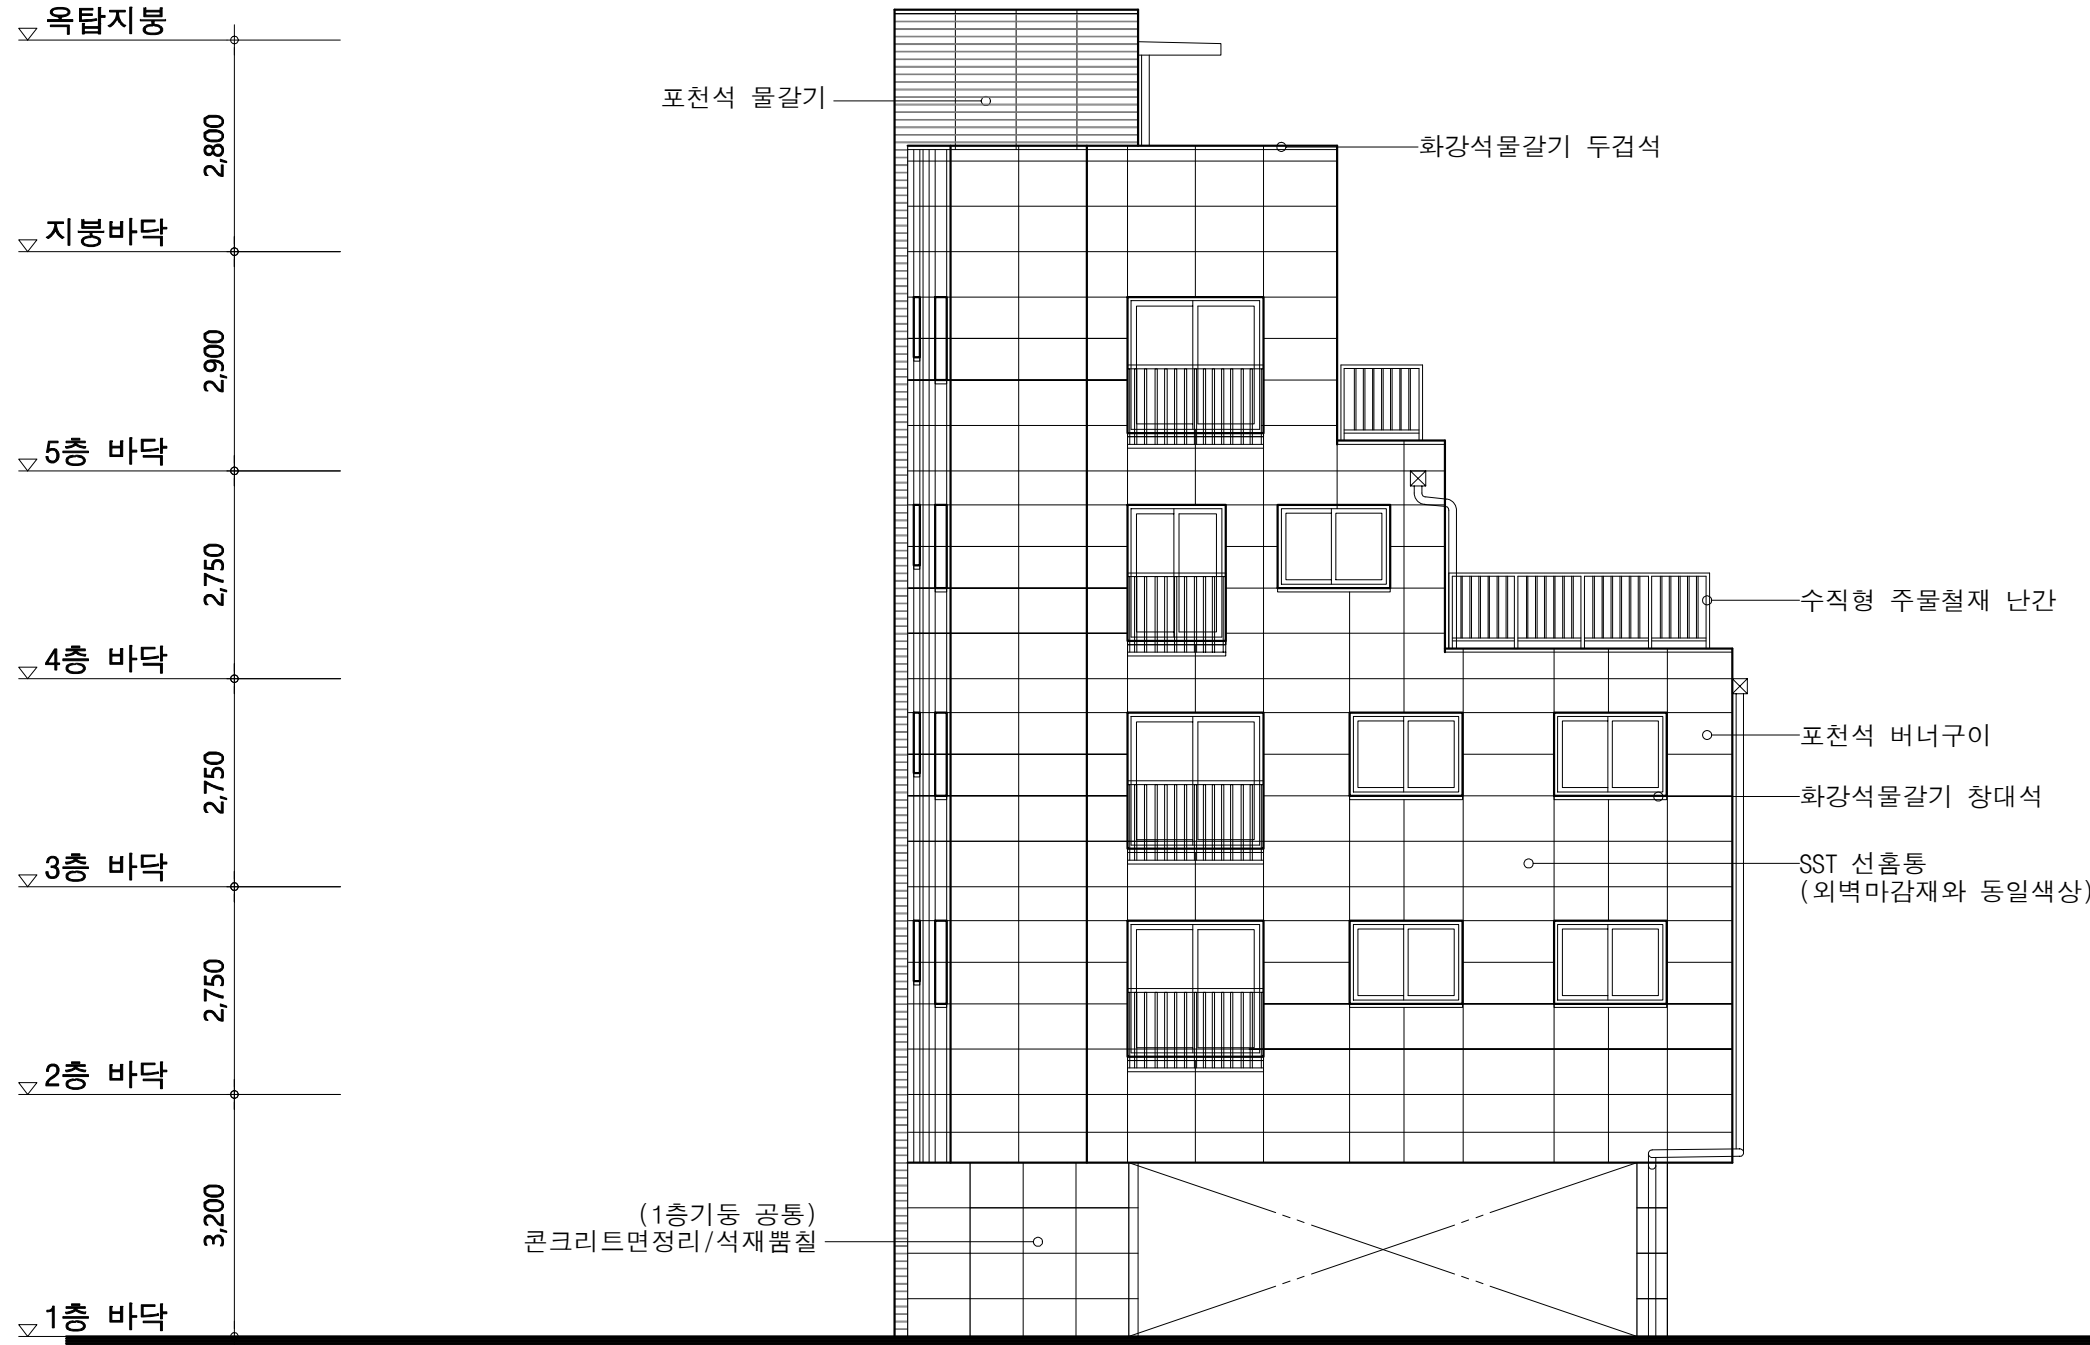

* 외부면 노출 창호프레임 칼라

건본색상
(질은회색)



PROJECT TITLE
사업명칭
구로구 구로동
429 - 254
도시형생활주택(원룸)
신축공사

사업번호 PROJ. NO.
도면명
2021-053(#)

NOTE

NO. ▲ REVISIONS ▲ DATE
번호 수정 일자

DESIGNED BY
설계

CHECKED BY
심사

APPROVED BY
승인

CONSULTANTS
협동설계

SCALE
축척 1/100


DATE
일자 2021. 09 .

DWG NO.
도면번호 A-402

NAME OF DRAWING
도면명


우측면도

(주)에이이플러스
건축사사무소
Architecture + Environment
AE+
TEL. 02-745-6511, 2057-5868
FAX. 0505-070-6511

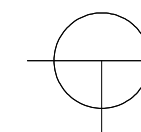


우측면도

SCALE : A3 : 1/100

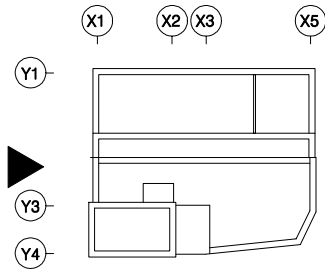

KEY PLAN

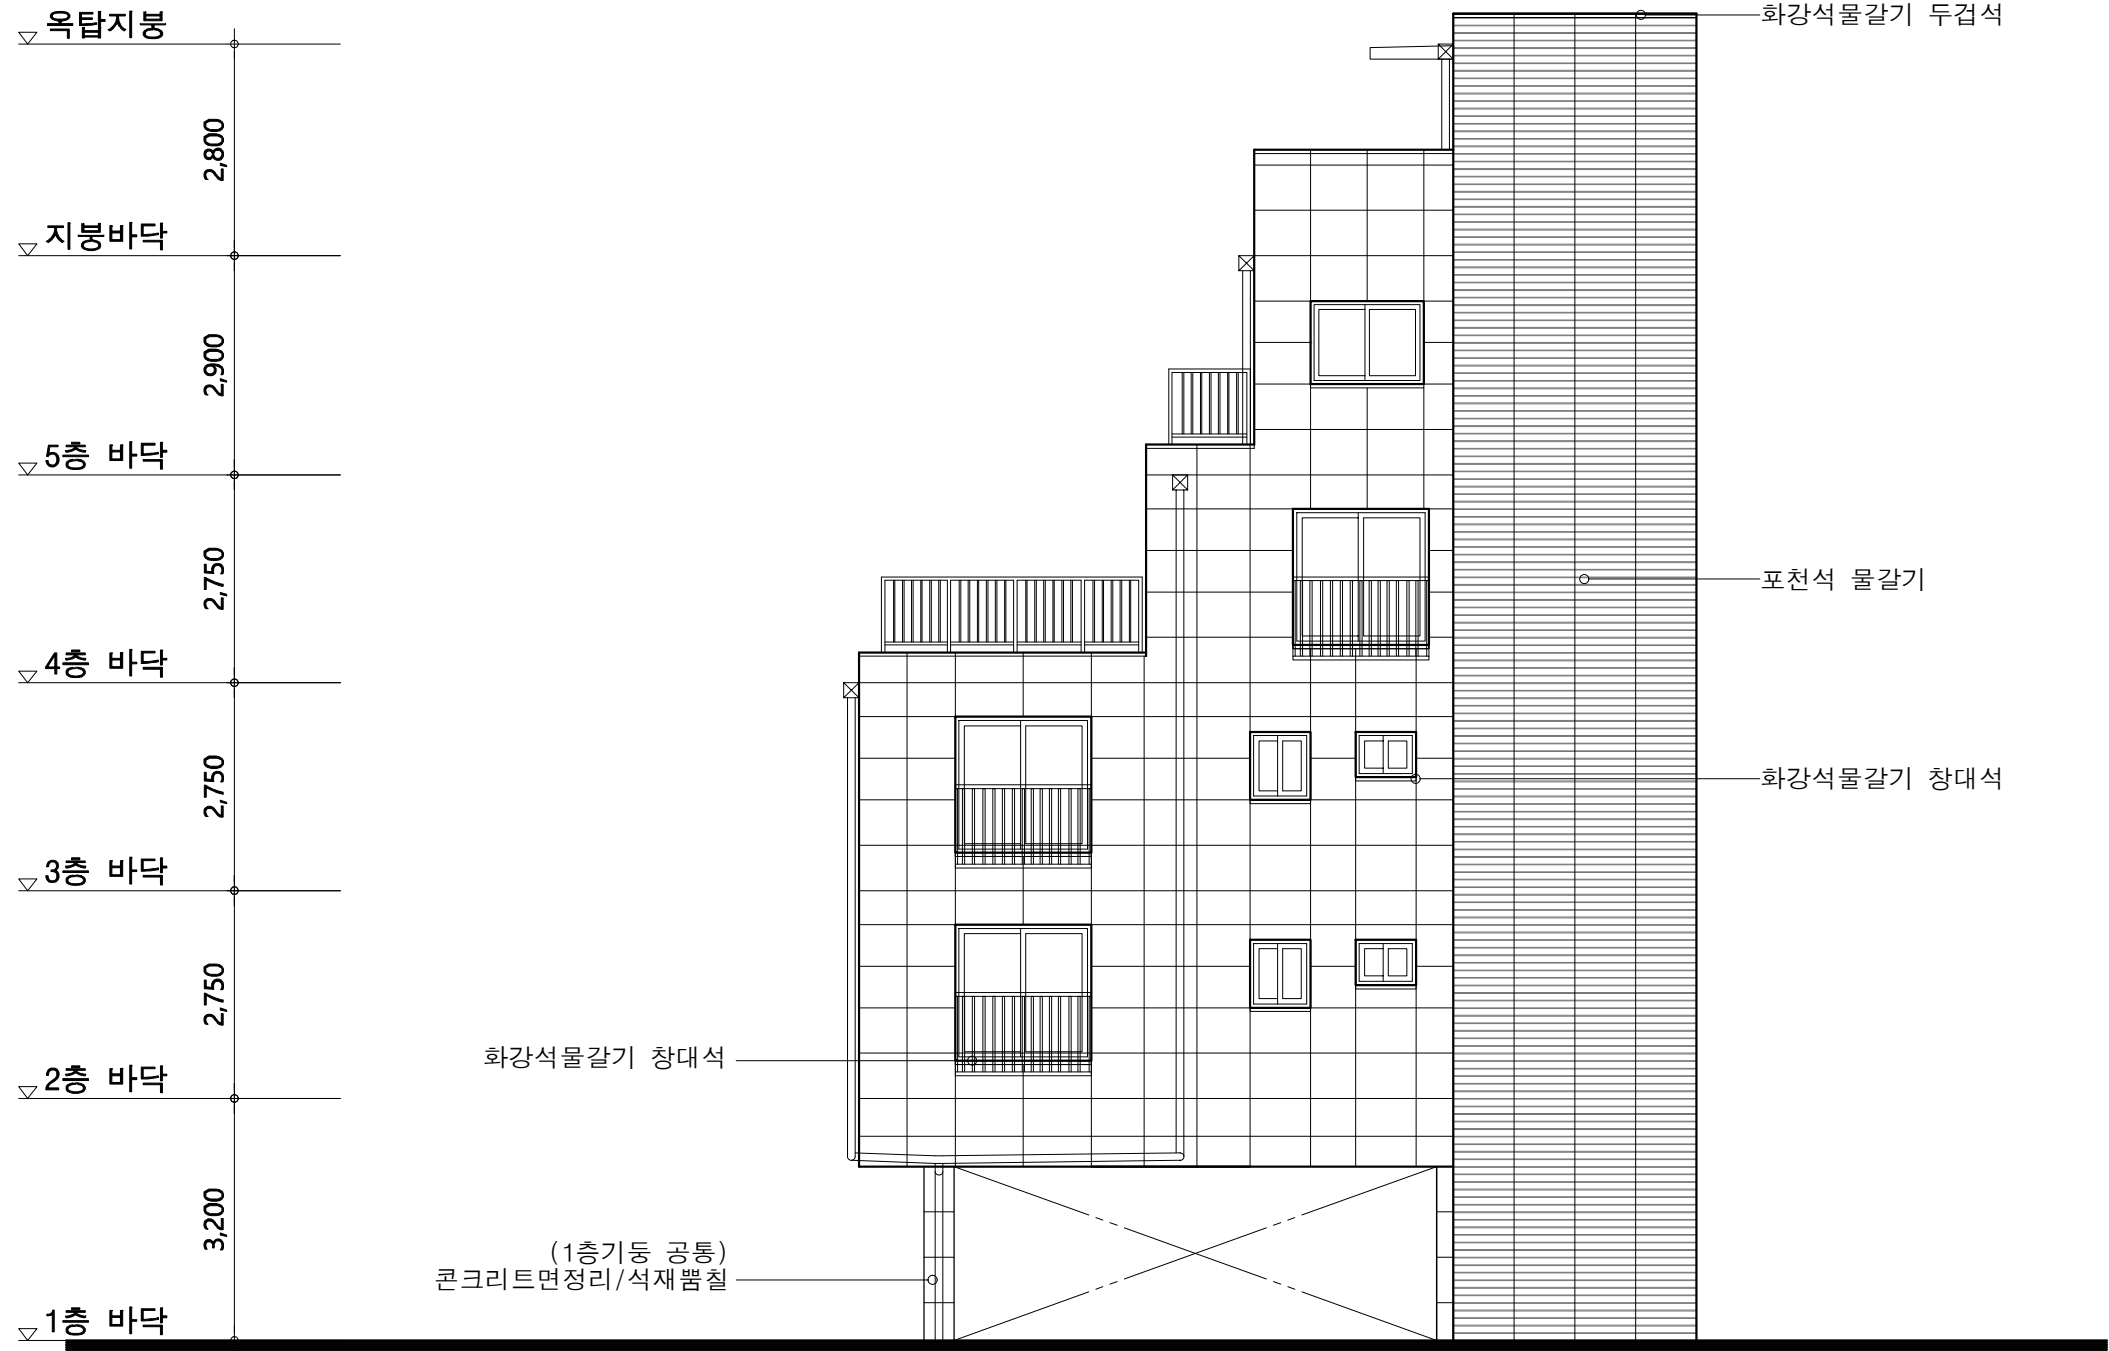

* 외부면 노출 창호프레임 칼라

건본색상
(질은회색)



PROJECT TITLE
사업명칭
구로구 구로동
429 - 254
도시형생활주택(원룸)
신축공사

사업번호 PROJ. NO.
도면명
2021-053(#)

NOTE

NO. ▲ REVISIONS ▲ DATE
번호 수정 일자

DESIGNED BY

CHECKED BY

APPROVED BY

CONSULTANTS

SCALE
축척 1/100

DATE
일자 2021. 09 .

DWG NO.
도면번호 A-403


NAME OF DRAWING
도면명

좌 측 면 도


(주)에이이플러스
건축사무소
Architecture + Environment
AE+
TEL. 02-745-6511, 2057-5868
FAX. 0505-070-6511

좌 측 면 도

SCALE : A3 : 1/100

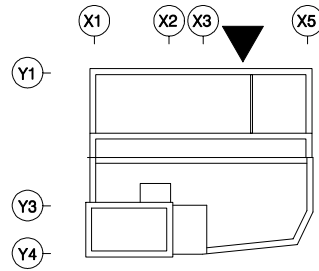

KEY PLAN

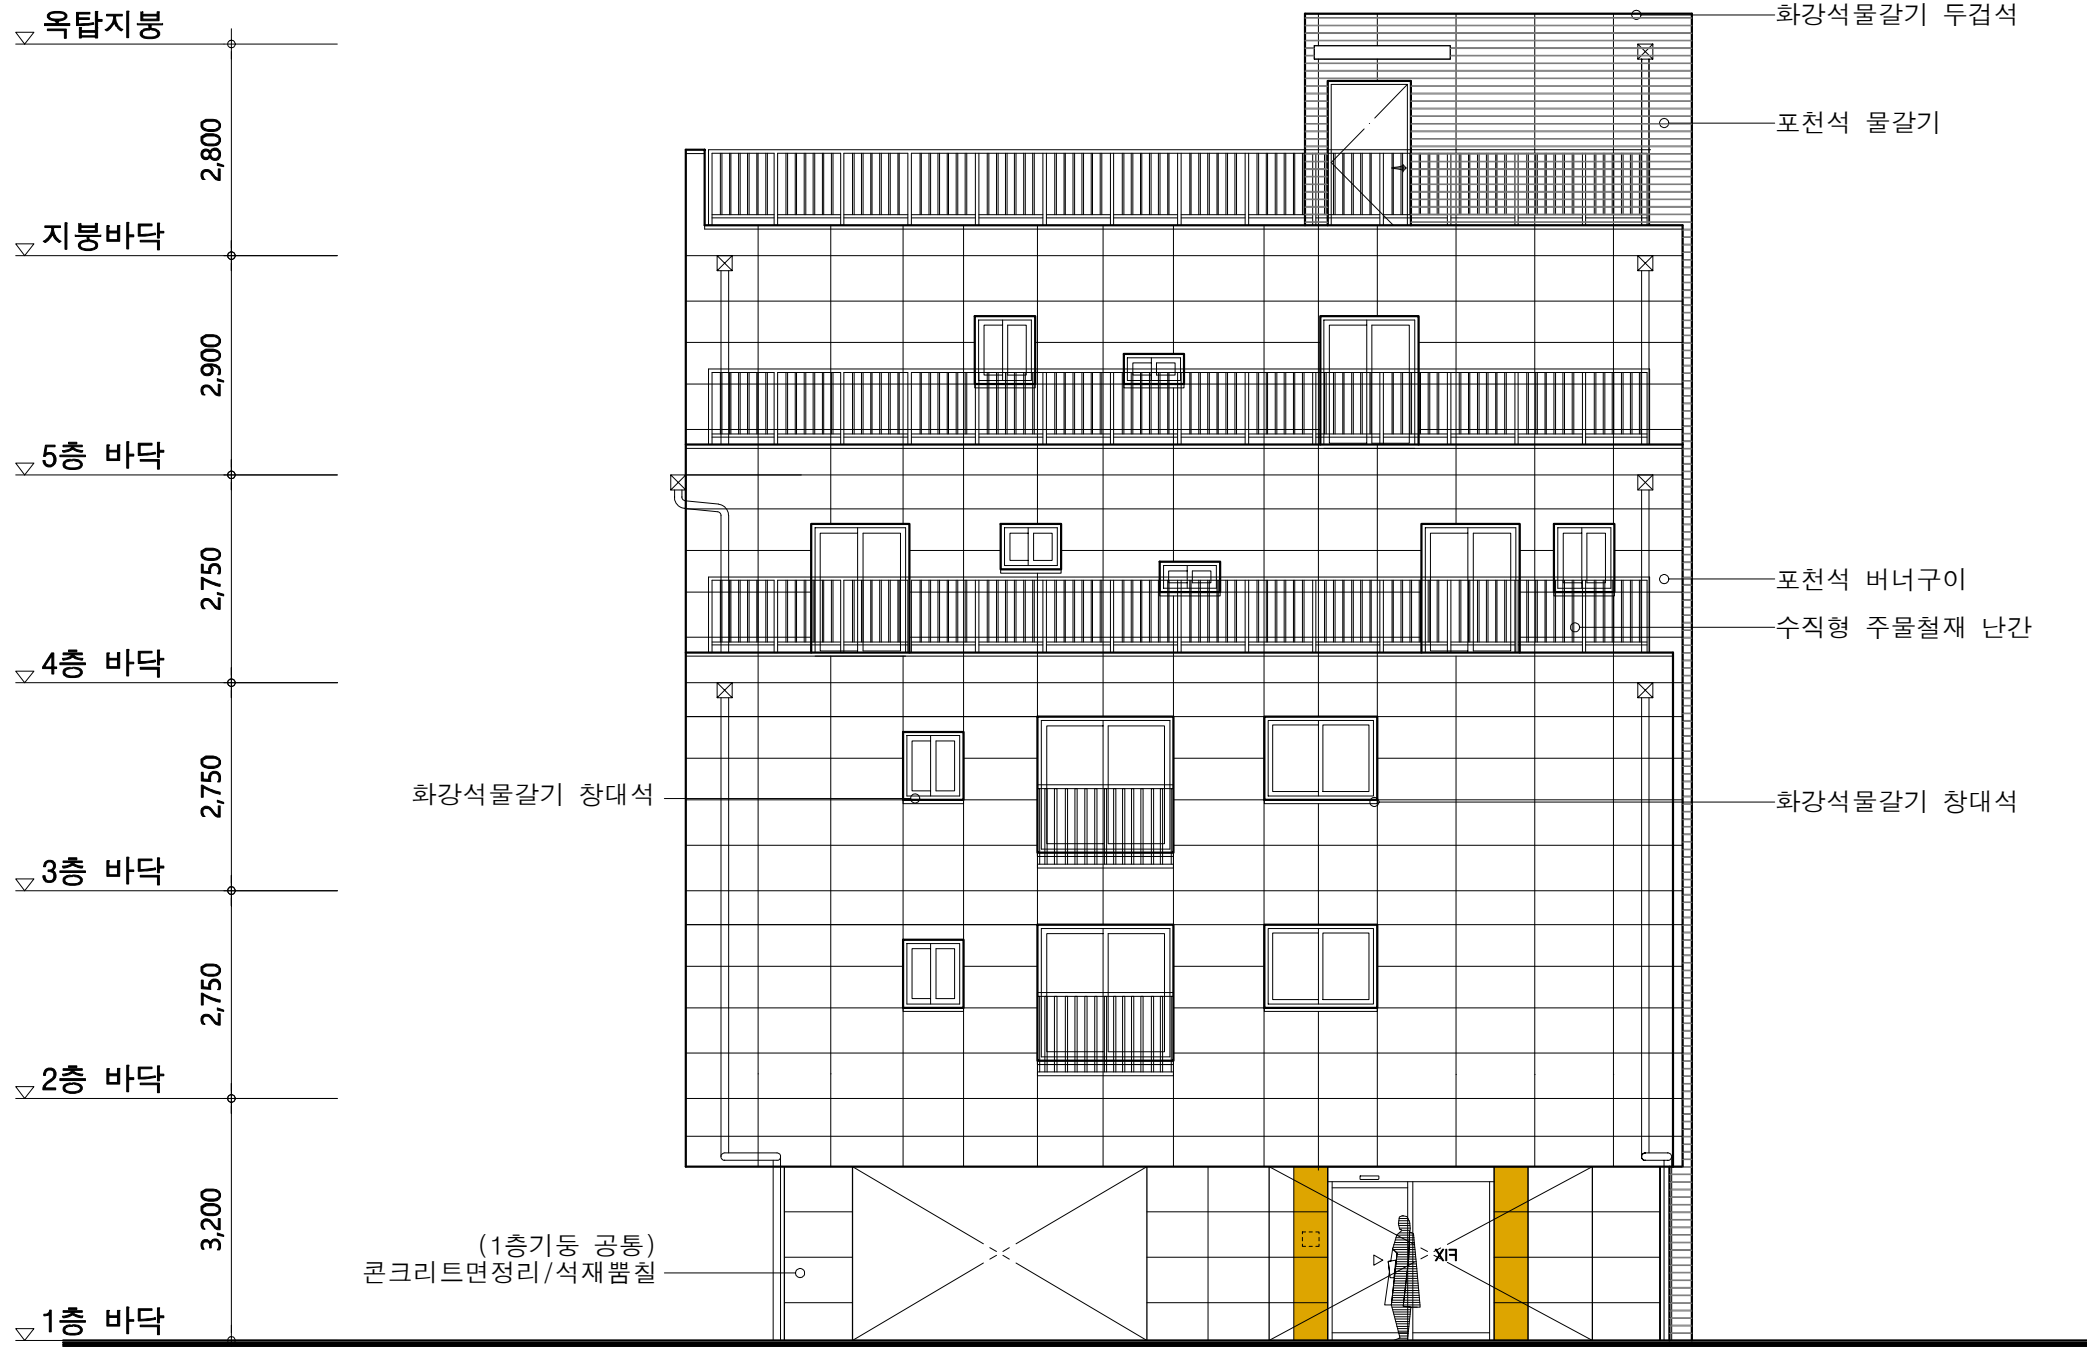

* 외부면 노출 창호프레임 칼라

건본색상
(질은회색)



PROJECT TITLE
사업명칭
구로구 구로동
429 - 254
도시형생활주택(원룸)
신축공사

사업번호 PROJ. NO.
도면명
2021-053(#)

NOTE

NO. 번호	REVISIONS 수정	DATE 일자

DESIGNED BY
설계

CHECKED BY
심사

APPROVED BY
승인

CONSULTANTS
협동설계

SCALE
축척 1/100

DATE
일자 2021. 09 .

DWG NO.
도면번호 A-404

NAME OF DRAWING
도면명

배 면 도

배 면 도

SCALE : A3 : 1/100

(주)에이이플러스
건축사사무소
Architecture + Environment
AE+
TEL. 02-745-6511, 2057-5868
FAX. 0505-070-6511