



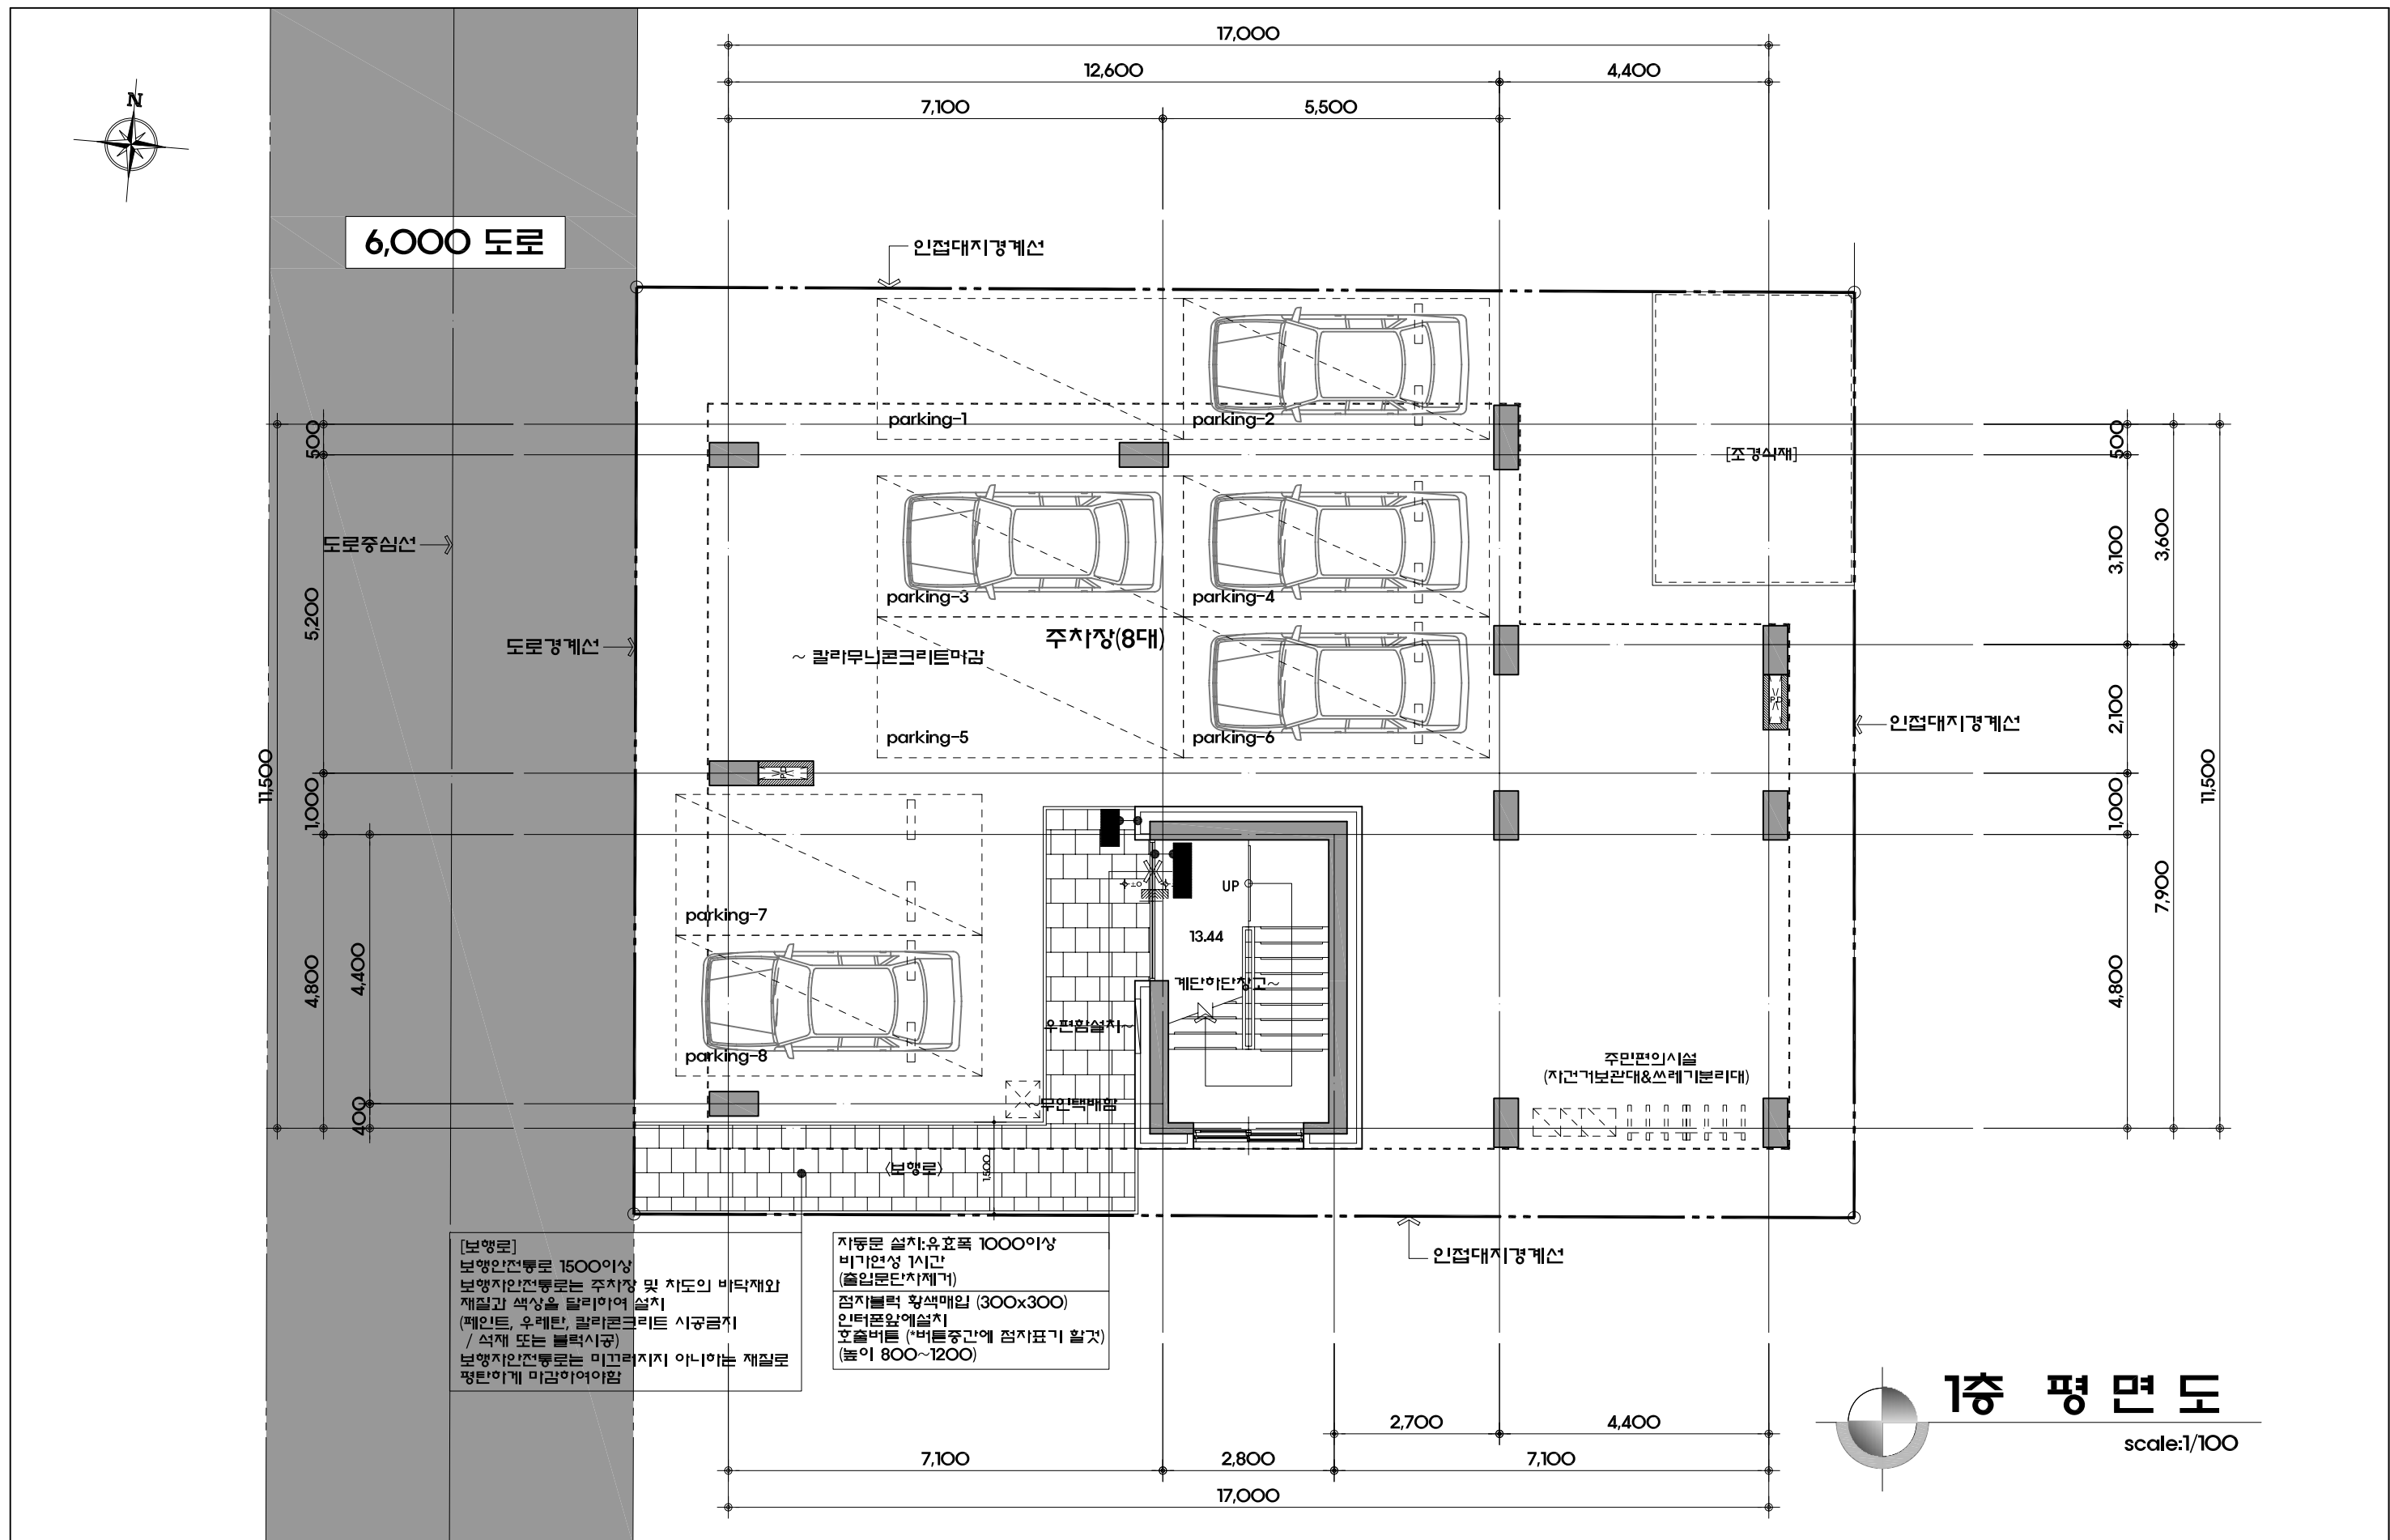


 건축사사무소 다림 Architects & Engineers Darim Tel:(02) 2066-5598, Fax:(02) 2066-5598	NO	DATE	REVISION DESCRIPTION	DRWN	CHK'D	APPD	PROJECT TITLE	CHK'D BY	SCALE	DRAWING TITLE	B.C.C NO	JOB NO	APPROVE D BY
			01. 일괄처리				개봉동 326-12호 공동주택(다세대주택) 신축공사 설계도		1/100	도면명			
									DATE	1층 평면도	DRWG NO		DESIGNED BY
									DRWN BY				

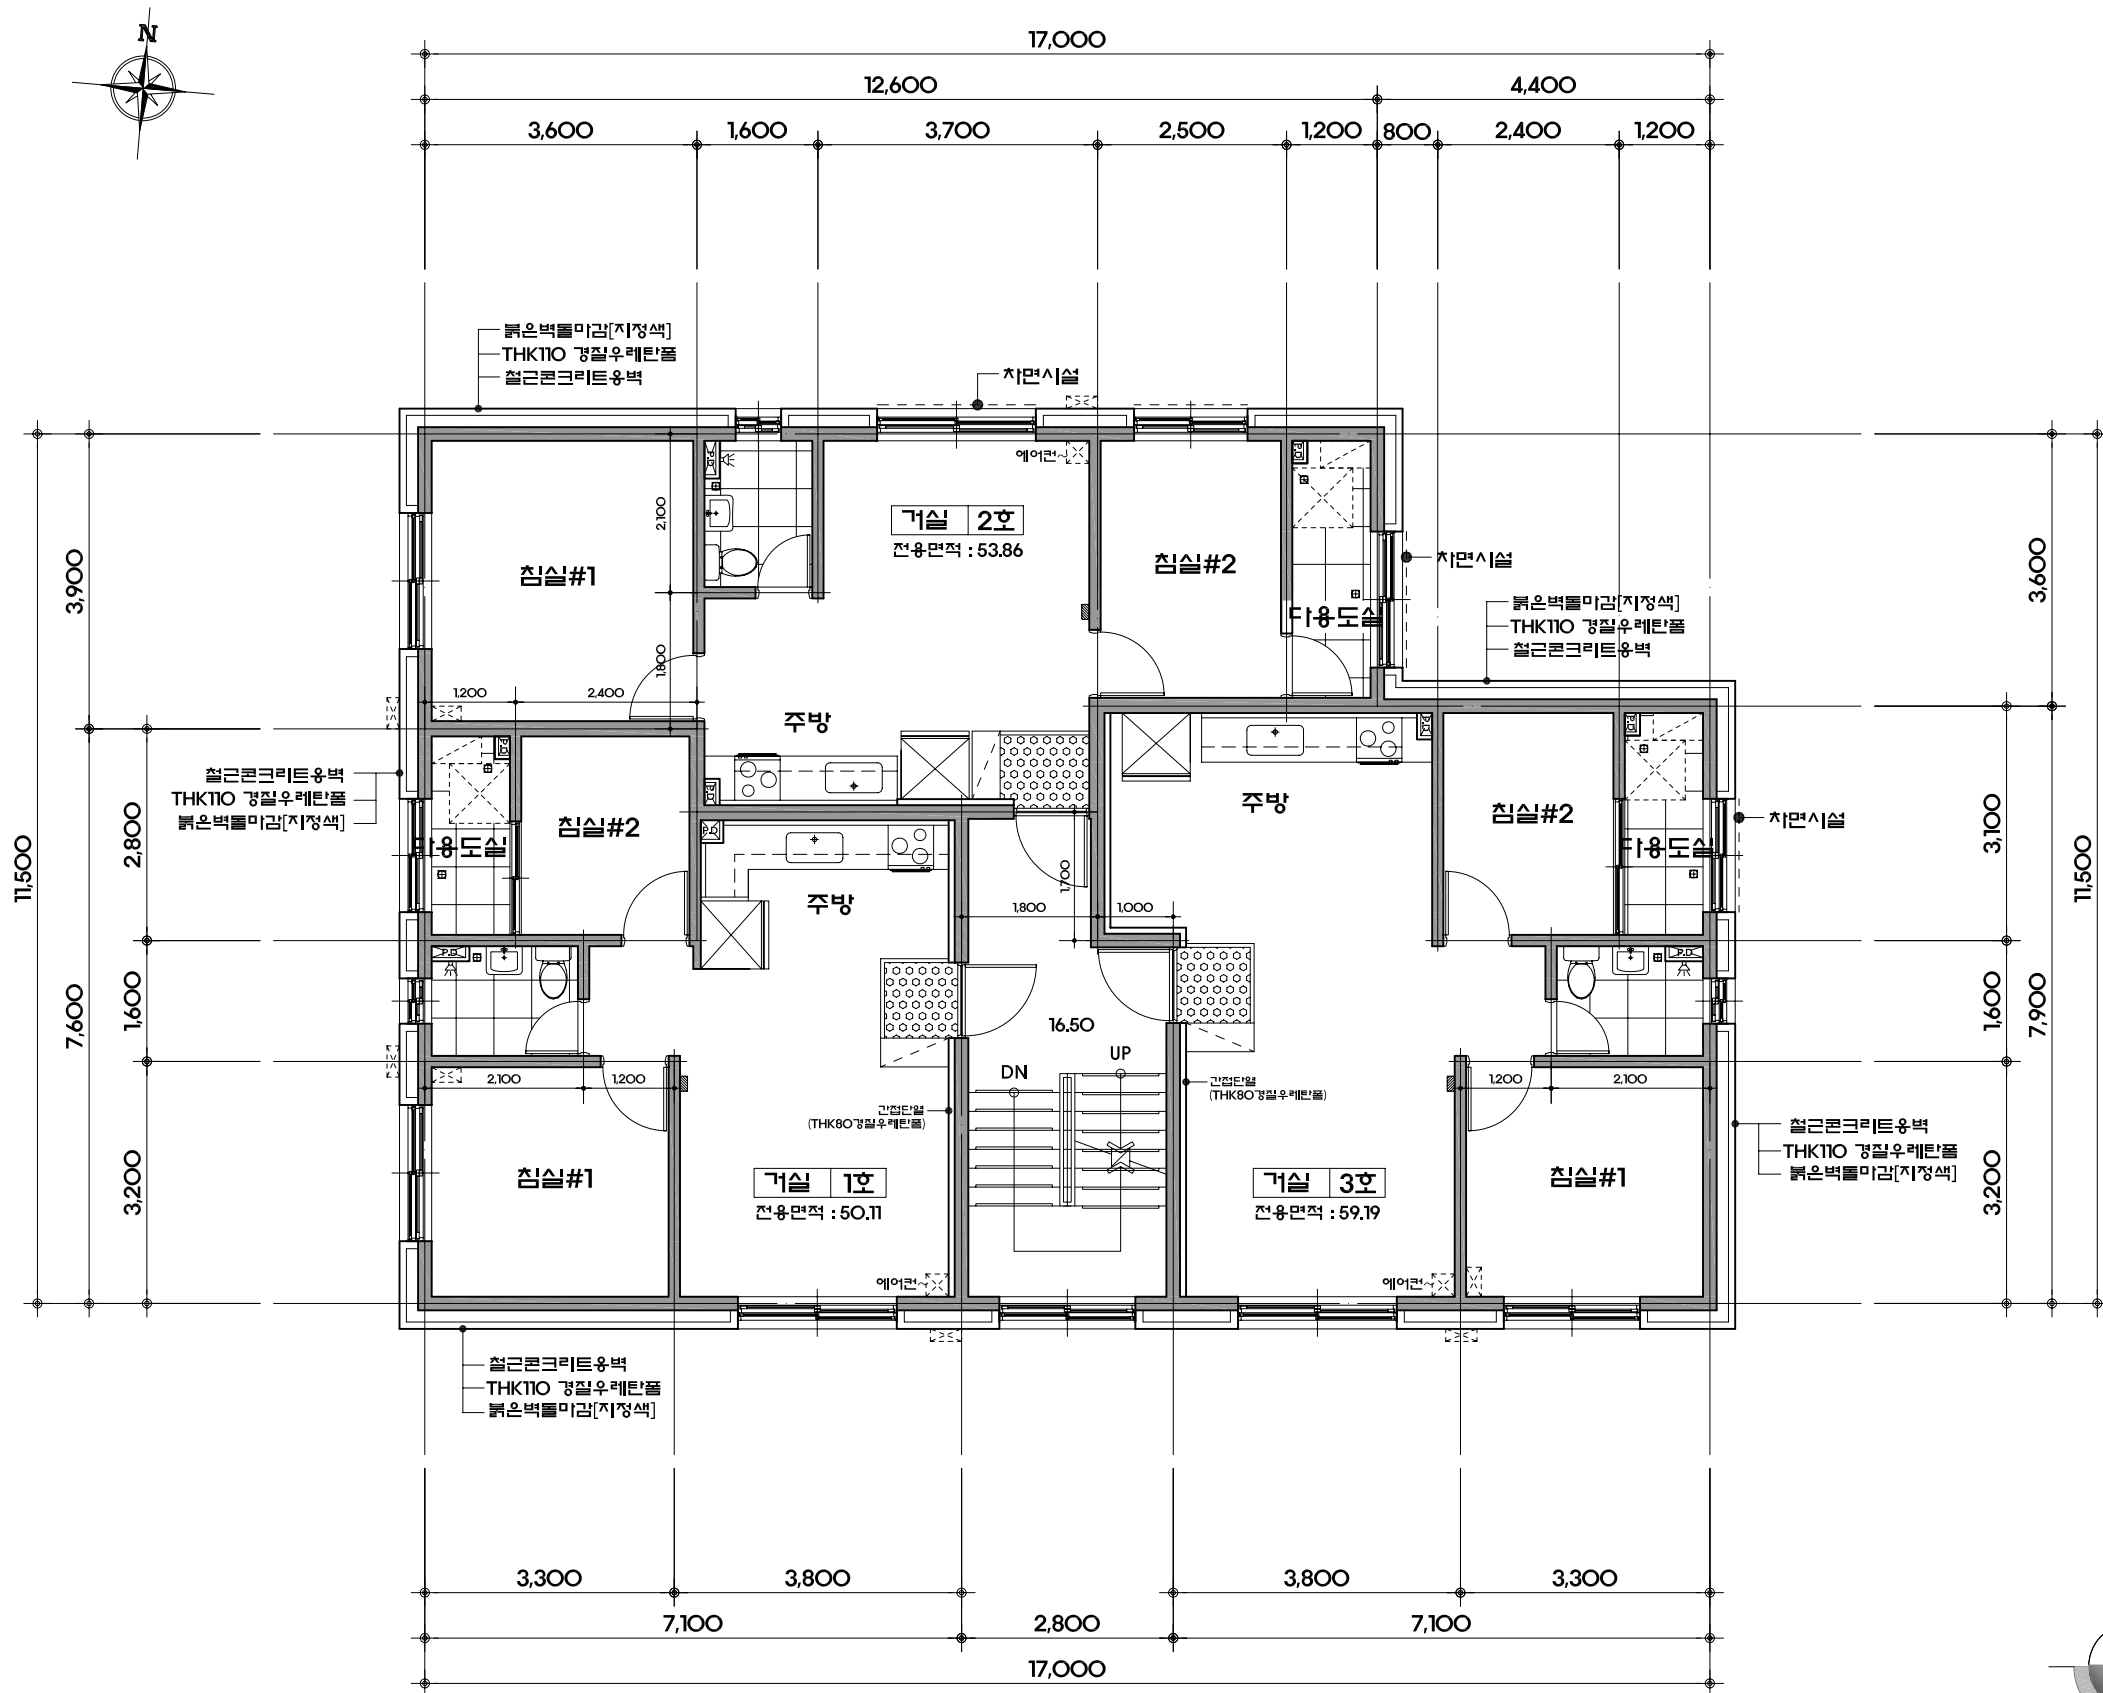

주 기		
구 조	1 (외부)	주차장내 CCTV,쓰레기분리수거,자전거보관대 설치
		우편함 설치 (세대전용, 공용, 반송용, 폐건전지함 구분 설치)
		테라스 창호 PL 이중창 설치
		세대 테라스 설치시 세대간 분리벽 계획
		세대 발코니 설치시 차양시설 설치
	2 (계단실)	세대 현관문 도어체크 설치
		계단참의 현관과 계단 이격거리 (최소600mm이상)
		세대내 욕실, 휴지걸이 매립형 설치
	3 (내부)	
	4 (시공)	콘크리트 폴타이 제거 후 마감공사 시공 (방수, 단열재 시공 등)
		욕실 & 다용도실 스위치 : 문 열리는 방향으로 시공
		주차장 차양 진출입구간 무소울트렌치 시공
		-직접외기(외벽)에 면한 실내벽면 단열재
전 기	5 (미감)	[아이소핑크(10mm) + 석고보드 마감도면 표기]
		-간접외기(계단실,복도)에 면한 실내벽면 단열재
		[경질우레탄폴(80mm) + 석고보드 마감도면 표기]
		*기타 실내 벽면 시멘트 미장 마감
	1	철근 : fy=400Mpa
		콘크리트 : fck=24Mpa
		스리브두께 : 210mm (복배근)
		외벽두께 : 180mm (복배근)
		코아벽두께 : 180mm (복배근)
	2	세대간벽두께 : 200mm (복배근)
		내벽두께 : 150mm (복배근)
	1	-콘센트 설치 (바닥 마감선 기준)
		[거실] 스탠드형 에어컨 : 350
		[안방] 벽걸이형 에어컨 : 1900
		[화장실] 양변기 옆 : 900
		[주방] 조리대 : 중앙 / 냉장고 : 350 / 후드 : 2100
	2	-비디오폰(VP),보일러온도조절기(B), 스위치(S),전열교환기스위치(E) (거실 아트홀 위치)
		에어컨 실외기
		냉매, 배수관 (배수관수직매립)
비 고	세대현관문 ## 규격"틀"포함 : 1000X2200	

2.3층 평면도
scale:1/100

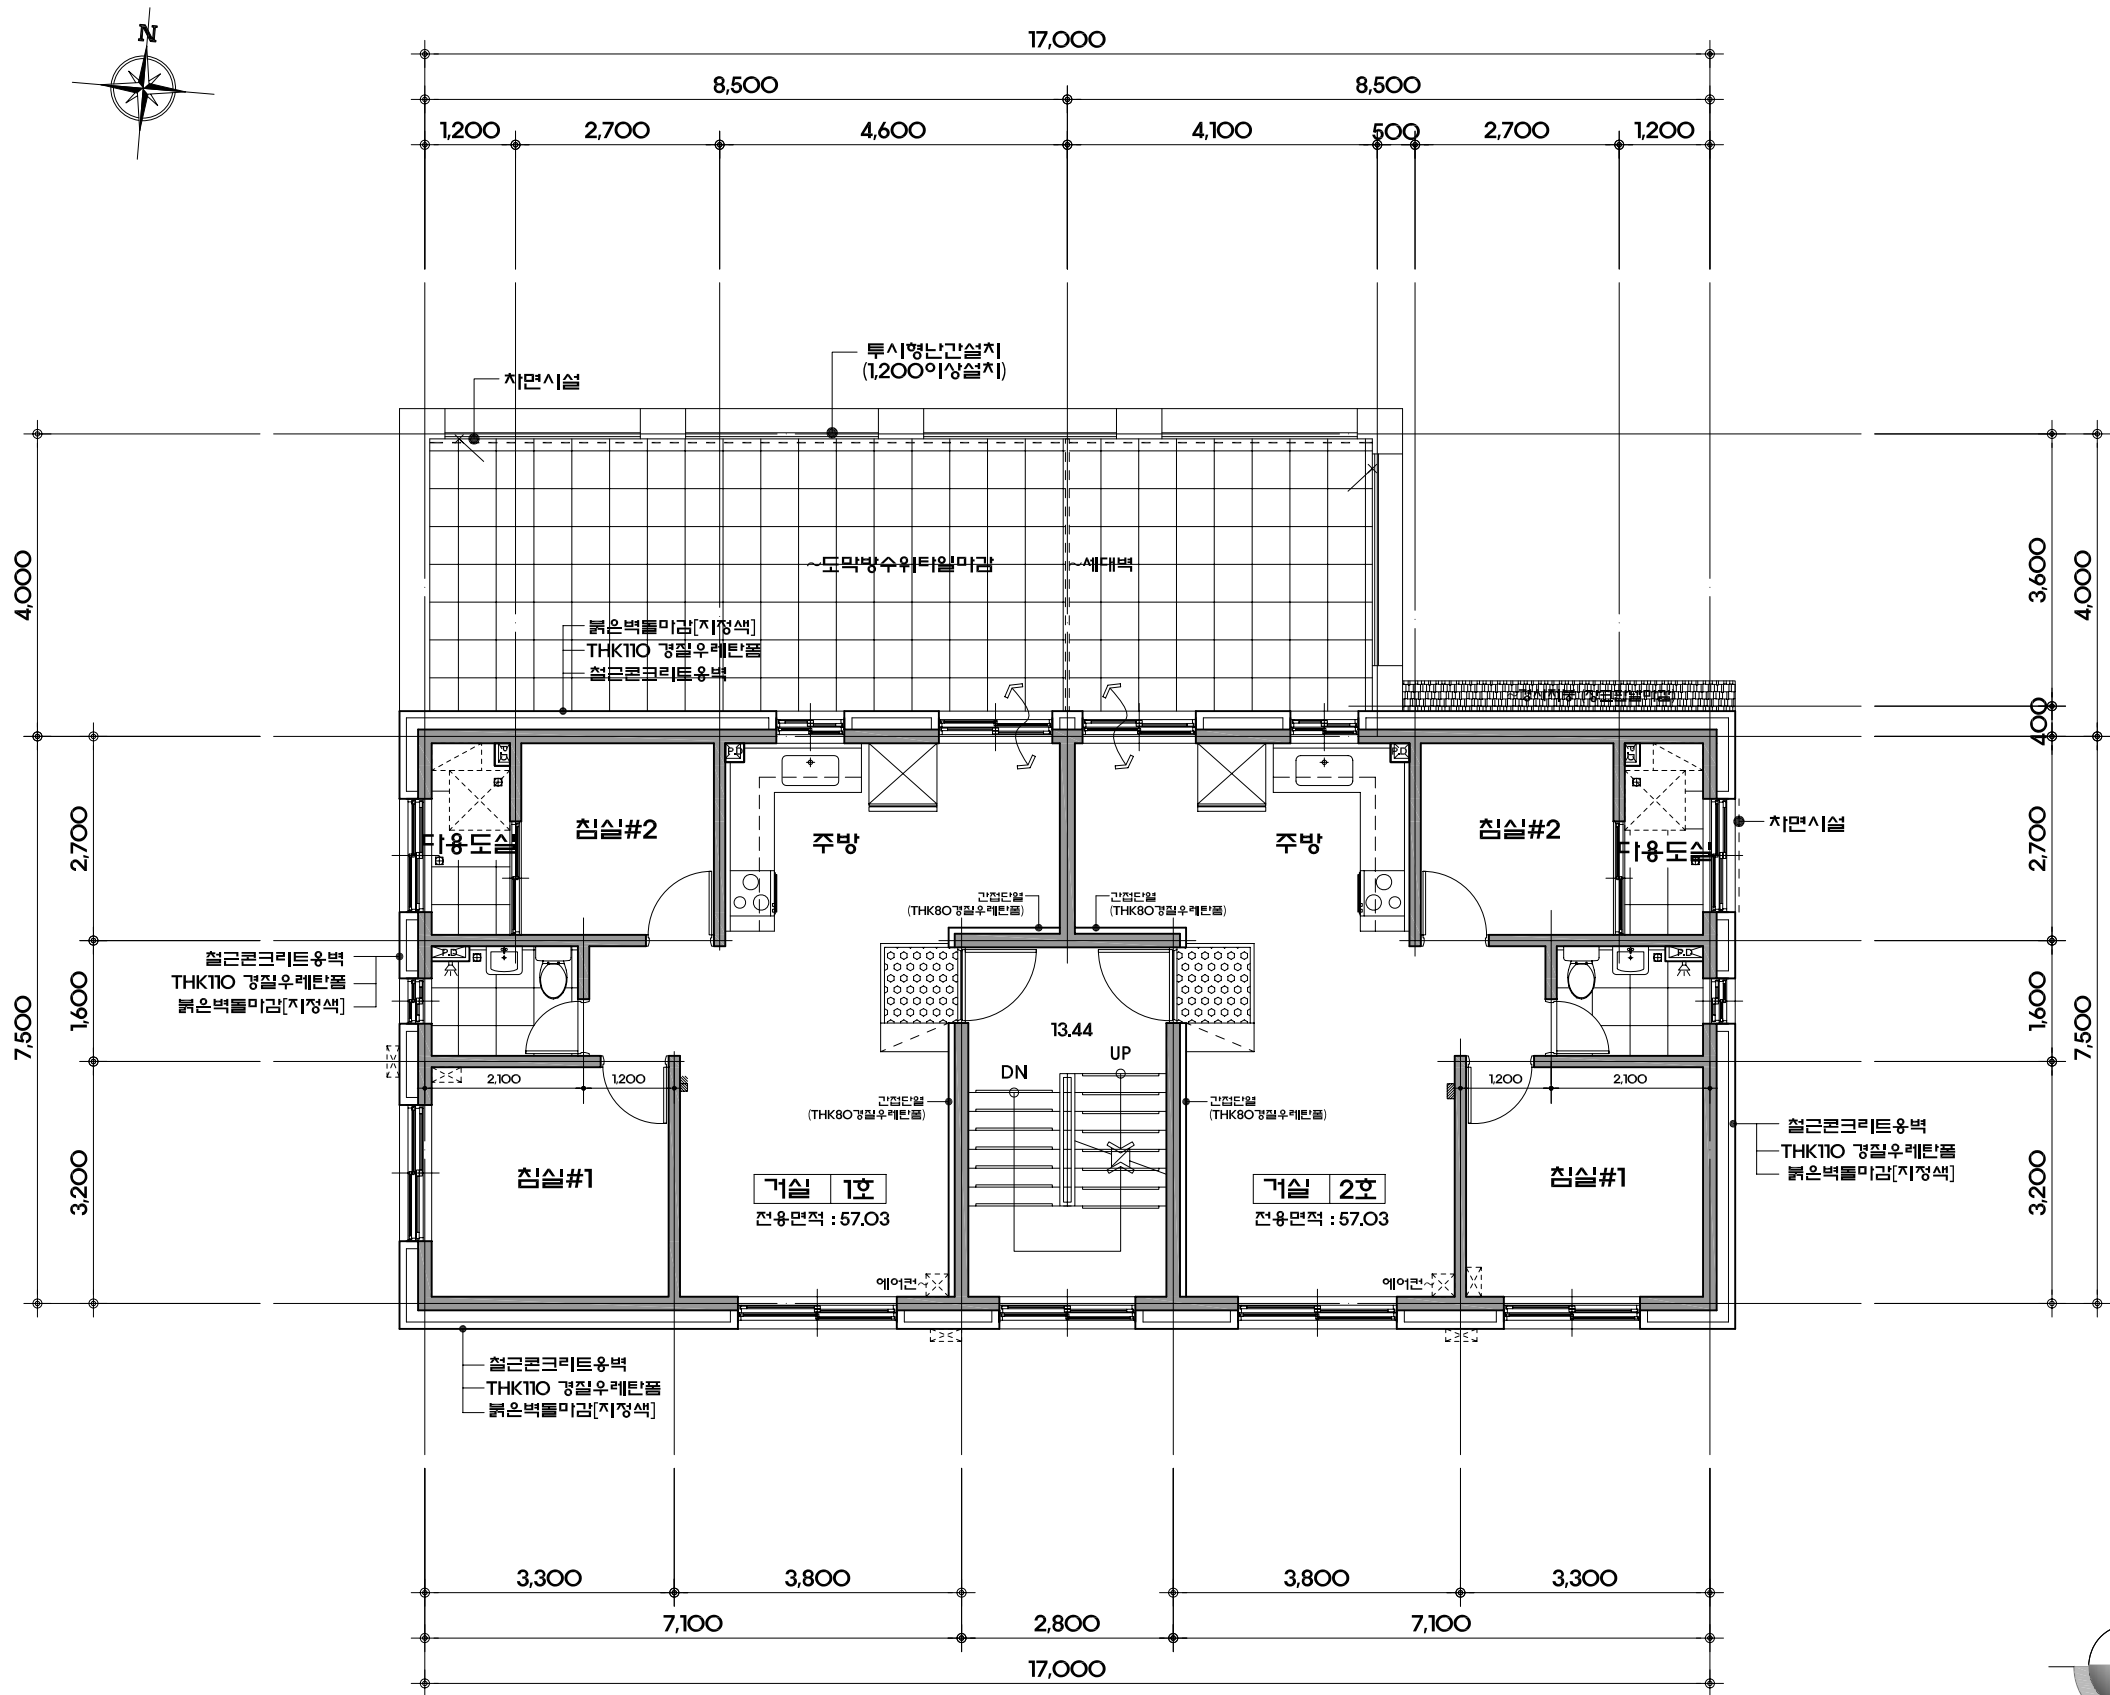


주 기		
구 조	1 (외부)	주차장내 CCTV,쓰레기분리수거,자전거보관대 설치
		우편함 설치 (세대전용, 공용, 반송용, 폐건전지함 구분 설치)
		테라스 창호 PL이중창 설치
		세대 테라스 설치시 세대간 분리벽 계획
		세대 발코니 설치시 차양시설 설치
	2 (계단실)	세대 현관문 도어체크 설치
		계단참의 현관과 계단 이격거리 (최소600mm이상)
	3 (내부)	세대내 욕실, 휴지걸이 매립형 설치
	4 (시공)	콘크리트 폴타이 제거 후 마감공사 시공 (방수, 단열재 시공 등)
		욕실 & 다용도실 스위치 : 문 열리는 방향으로 시공
		주차장 차양 진출입구간 무소울트렌치 시공
	5 (미감)	-직접외기(외벽)에 면한 실내벽면 단열재
		[아이소핑크(10mm) + 석고보드 마감도면 표기]
		-간접외기(계단실,복도)에 면한 실내벽면 단열재
		[경질우레탄폼(80mm) + 석고보드 마감도면 표기]
*기타 실내 벽면 시멘트 미장 마감		
구 조	1	철근 : fy=400Mpa
		콘크리트 : fck=24Mpa
	2	스리브두께 : 210mm (복배근)
		외벽두께 : 180mm (복배근)
		코아벽두께 : 180mm (복배근)
세대간벽두께 : 200mm (복배근)		
내벽두께 : 150mm (복배근)		
전 기	1	-콘센트 설치 (바닥 마감선 기준)
		[거실] 스탠드형 에어컨 : 350
		[안방] 벽걸이형 에어컨 : 1900
		[화장실] 양변기 옆 : 900
		[주방] 조리대 : 중앙 / 냉장고 : 350 / 후드 : 2100
	2	-비디오폰(VP),보일러온도조절기(B), 스위치(S),전열교환기스위치(E) (거실이트폴 위치)
		에어컨 실외기
	3	냉매, 배수관 (배수관수직매립)
비 고	세대현관문 ## 규격"틀"포함 : 1000X2200	

4층 평면도
scale:1/100



NO	DATE	REVISION DESCRIPTION	DRWN	CHK'D	APPD
01		일괄처리			

CHK'D BY	SCALE	1/100
	DATE	2019.01
	DRWN BY	

B.C.C NO	JOB NO	APPROVE D BY
DRWG NO		DESIGNED BY

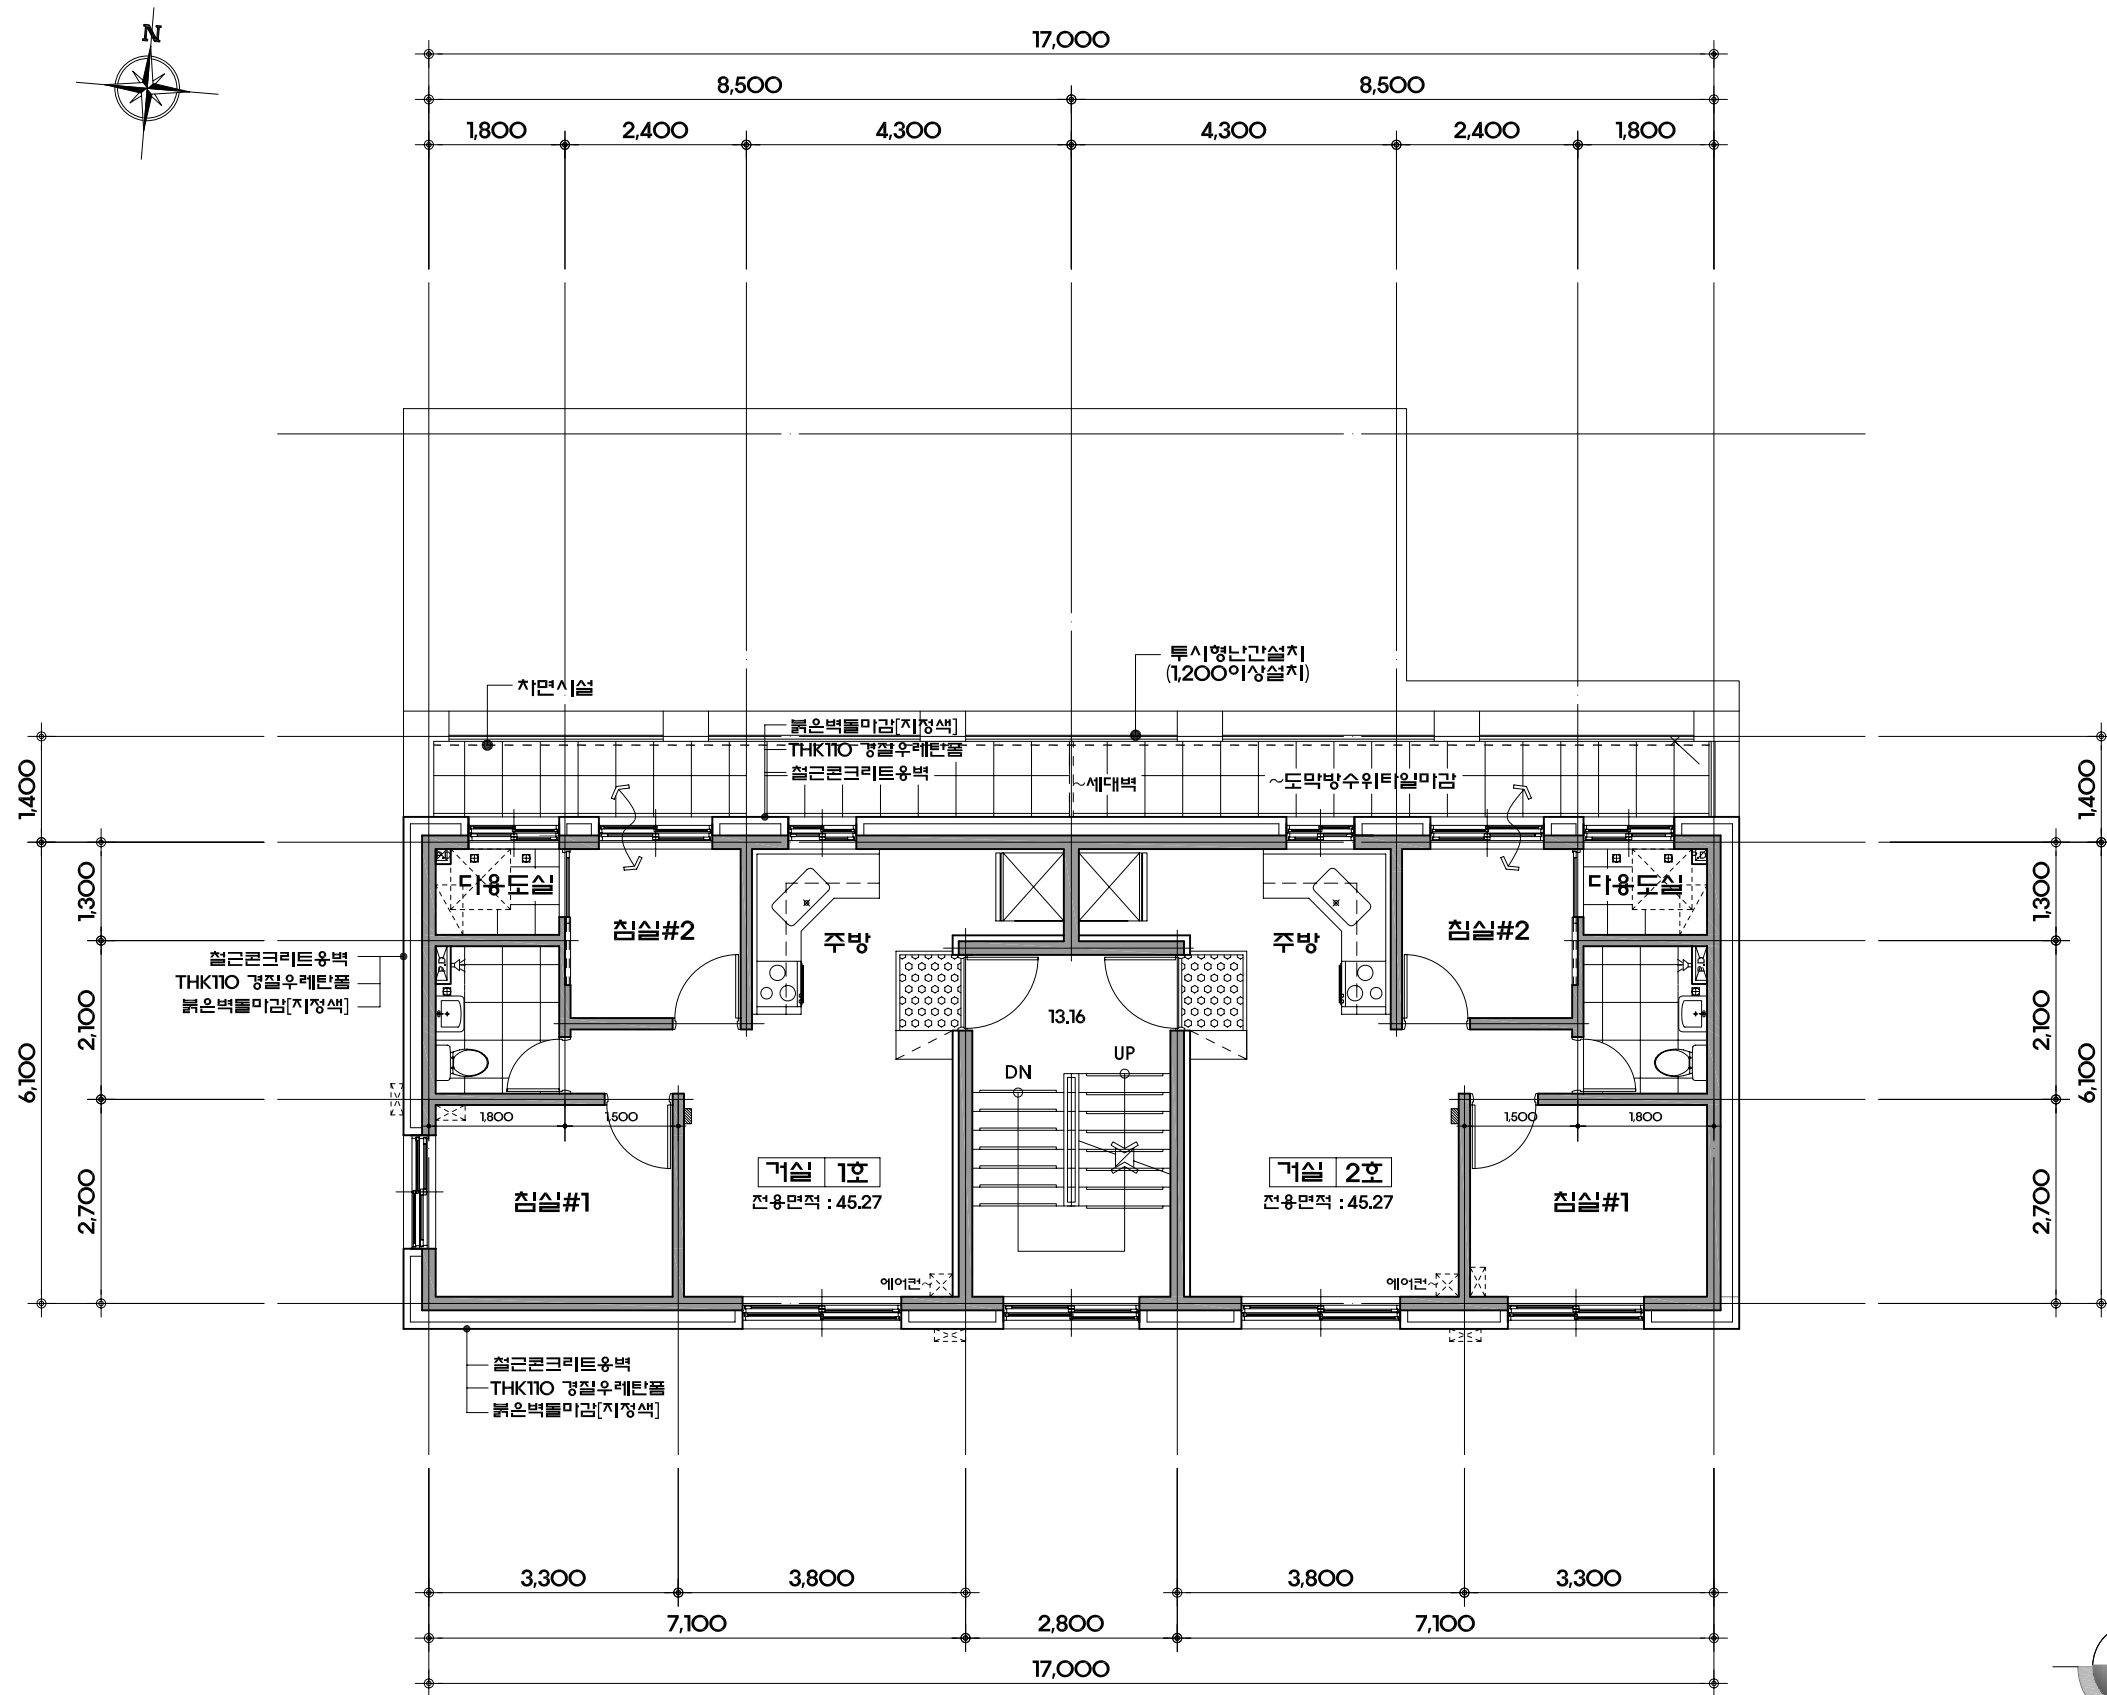

주 기		
구 조	1 (외부)	주차장내 CCTV,쓰레기분리수거,자전거보관대 설치
		우편함 설치 (세대전용, 공용, 반송용, 폐건전지함 구분 설치)
		테라스 창호 PL 이중창 설치
		세대 테라스 설치시 세대간 분리벽 계획
		세대 발코니 설치시 차양시설 설치
	2 (계단실)	세대 현관문 도어체크 설치
		계단참의 현관과 계단 이격거리 (최소600mm이상)
	3 (내부)	세대내 욕실, 휴지걸이 매립형 설치
	4 (시공)	콘크리트 폴타이 제거 후 미감공사 시공 (방수, 단열재 시공 등)
		욕실 & 다용도실 스위치 : 문 열리는 방향으로 시공
		주차장 차랑 진출입구간 무소울트렌치 시공
	5 (미감)	-직접입기(외벽)에 면한 실내벽면 단열재
		[아이소팡크(10mm) + 석고보드 미감도면 표기]
		-간접입기(계단실,복도)에 면한 실내벽면 단열재
		[경질우레탄폴(80mm) + 석고보드 미감도면 표기]
전 기	1	철근 : fy=400Mpa
		콘크리트 : fck=24Mpa
		스리브두께 : 210mm (복배근)
		외벽두께 : 180mm (복배근)
		코아벽두께 : 180mm (복배근)
	2	세대간벽두께 : 200mm (복배근)
		내벽두께 : 150mm (복배근)
		-콘센트 설치 (바닥 미감선 기준)
		[거실] 스탠드형 에어컨 : 350
		[안방] 벽걸이형 에어컨 : 1900
비 고	1	[환풍실] 양변기 옆 : 900
		[주방] 조리대 : 중앙 / 냉장고 : 350 / 후드 : 2100
		-비디오폰(VP),보일러온도조절기(B), 스위치(S),전열교환기스위치(E) (거실 아트홀 위치)
		에어컨 실외기
		냉매, 배수관 (배수관수직매립)

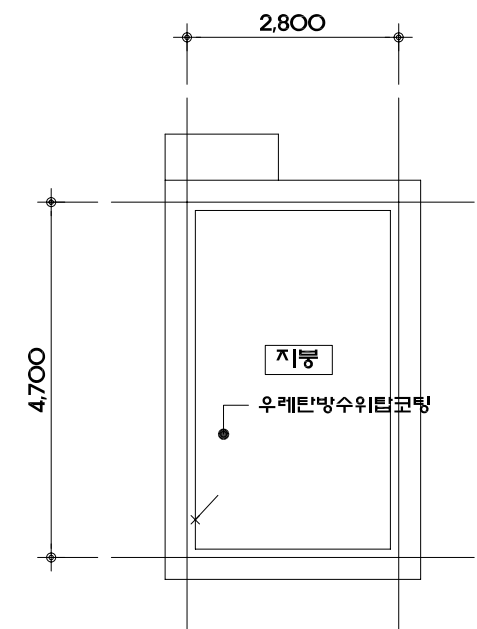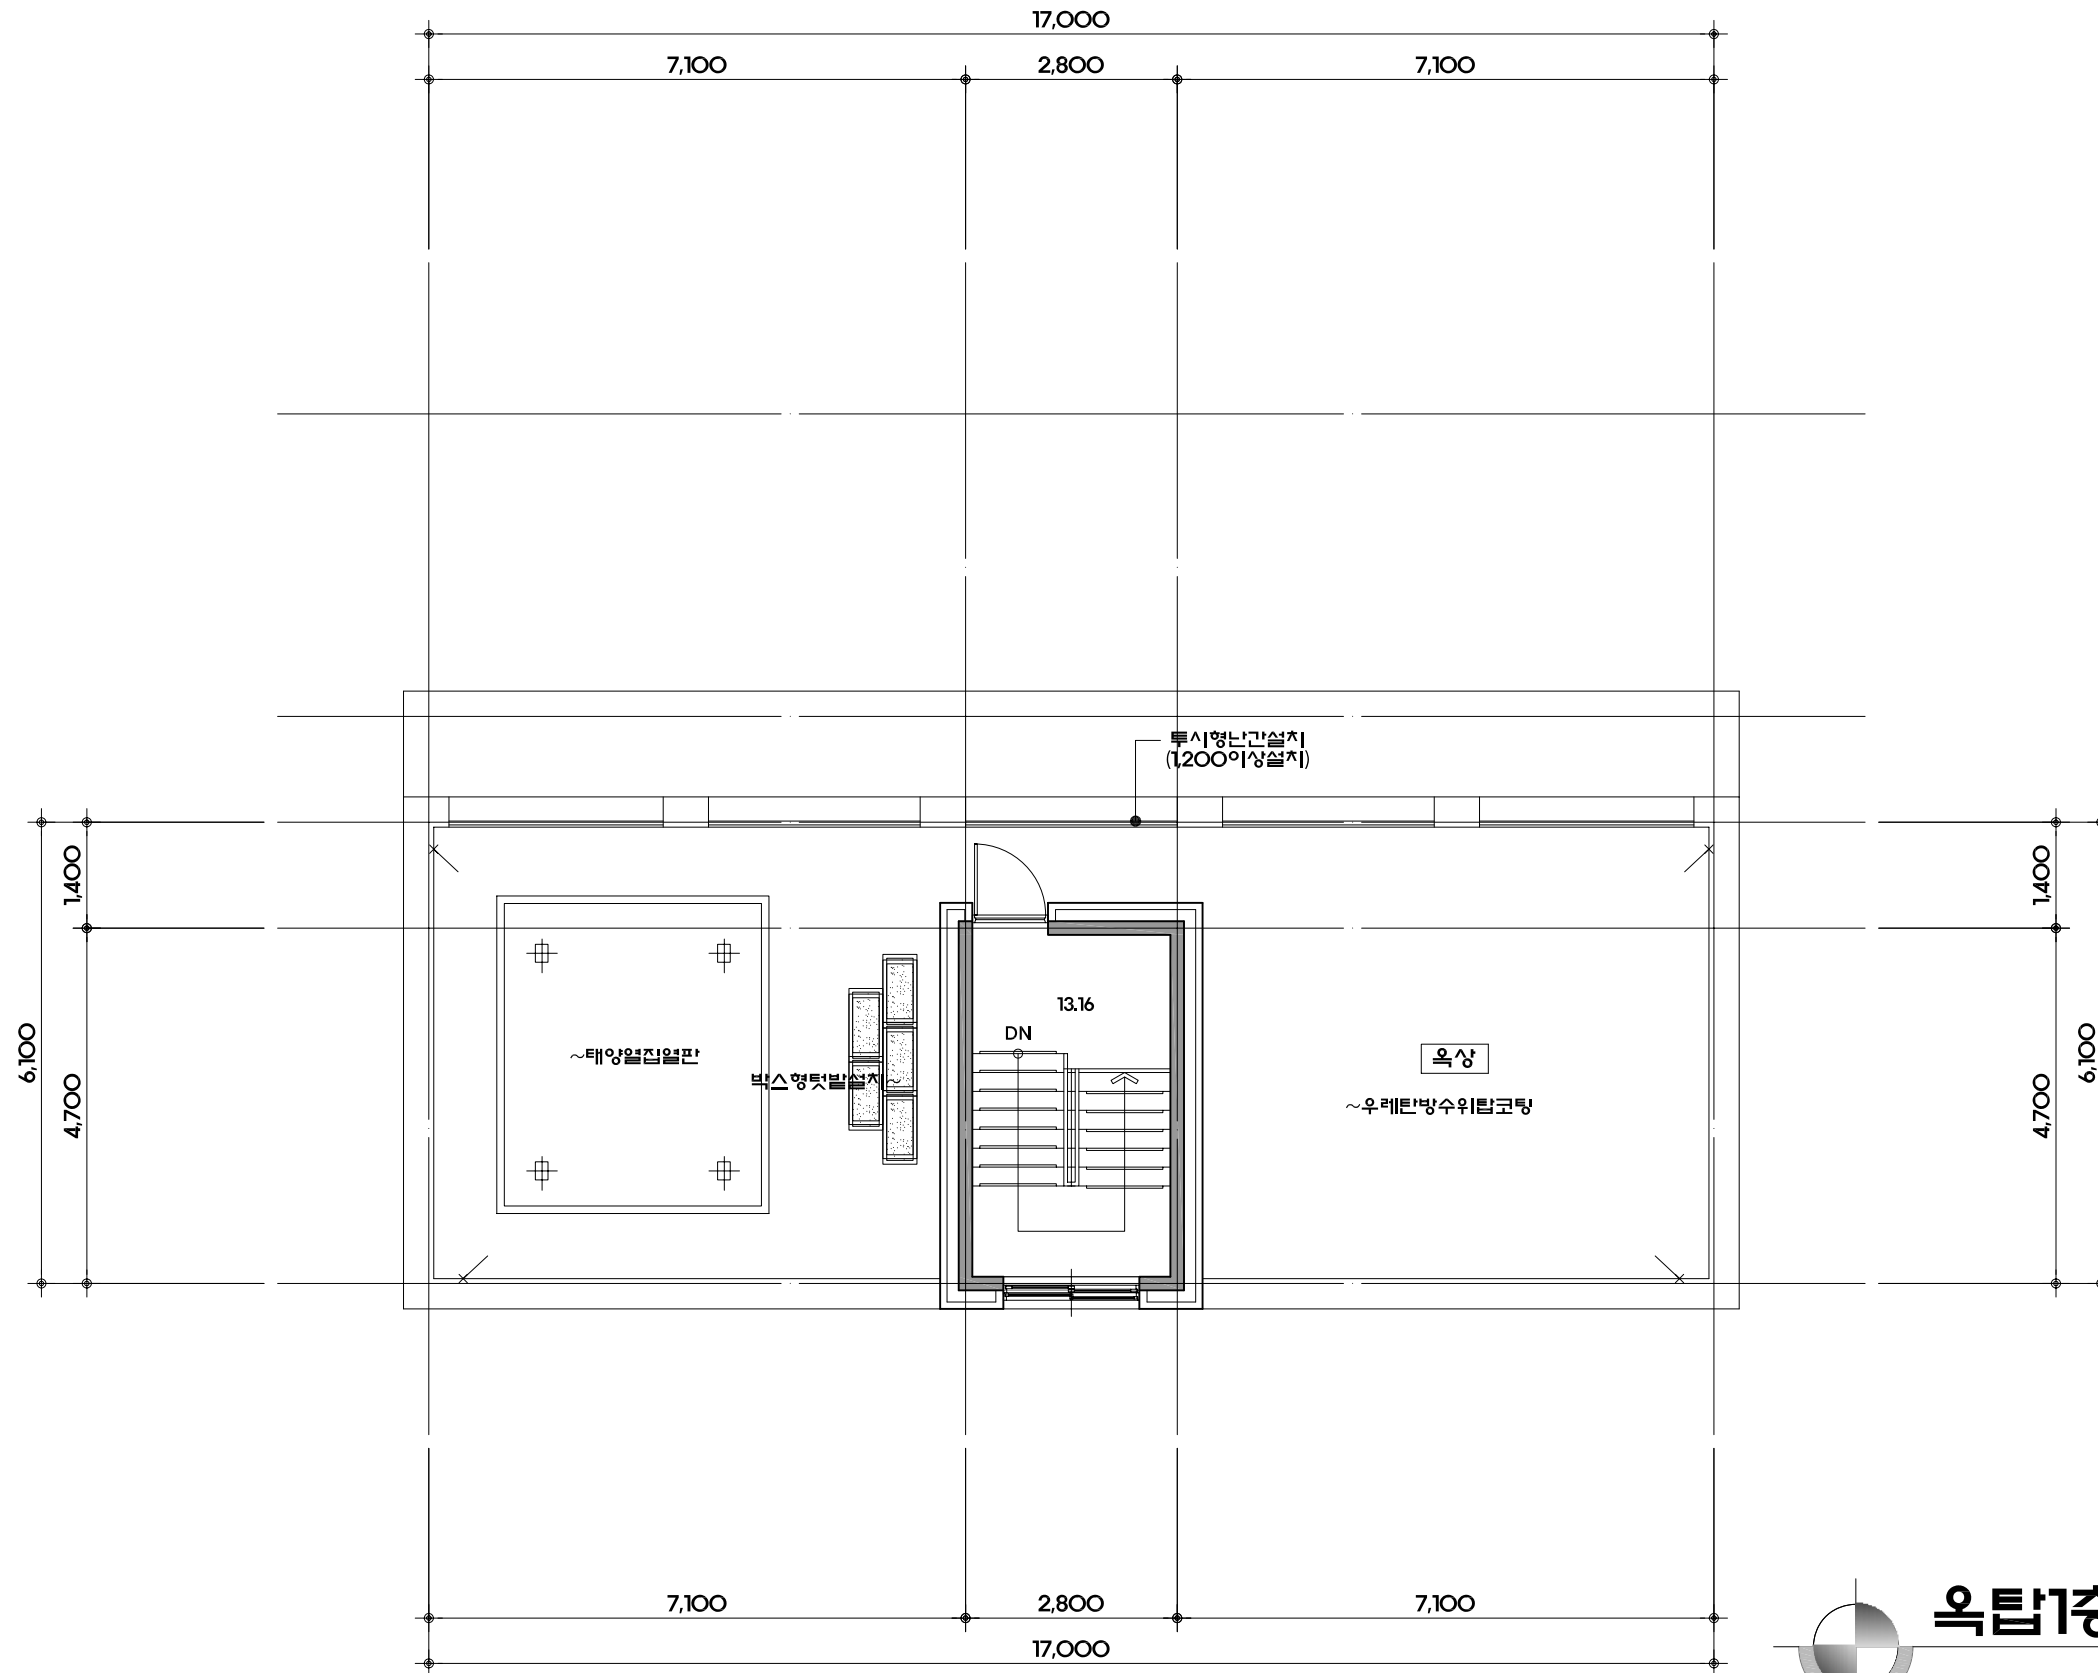



옥탑지붕 평면도
scale:1/100

옥탑1층 평면도
scale:1/100

NO	DATE	REVISION DESCRIPTION	DRWN	CHK'D	APPD
		01. 일괄처리			

CHK'D BY	SCALE 1/100
	DATE 2019.01
	DRWN BY

B.C.C NO	JOB NO	APPROVE D BY
DRWG NO		DESIGNED BY

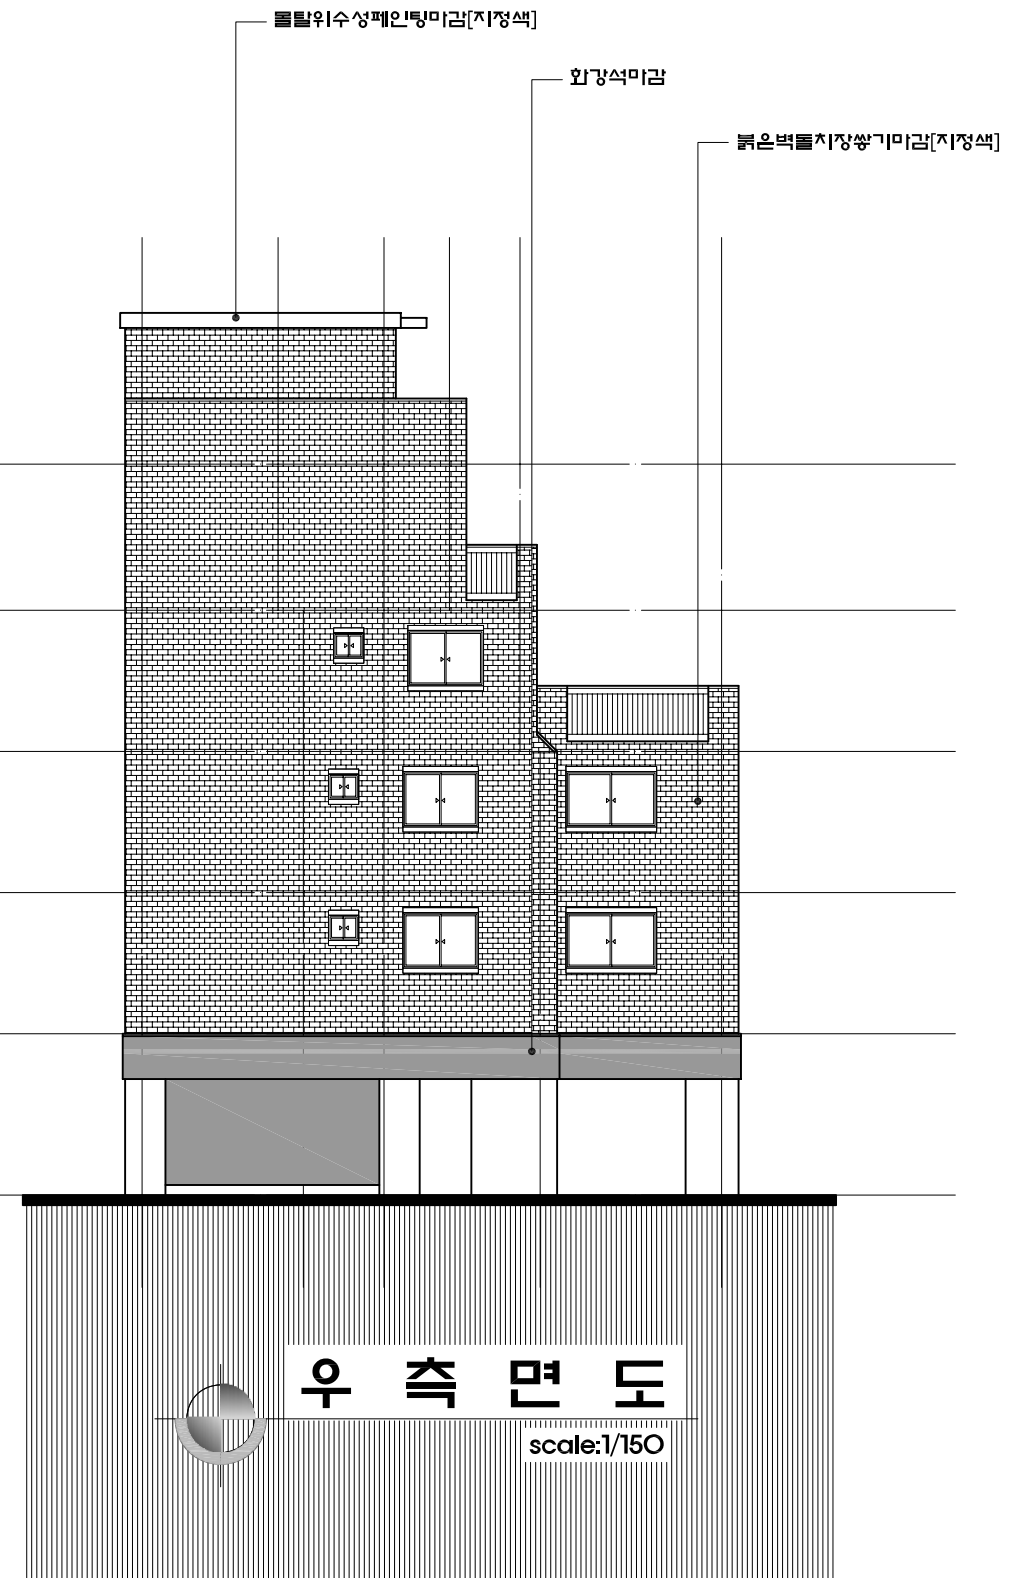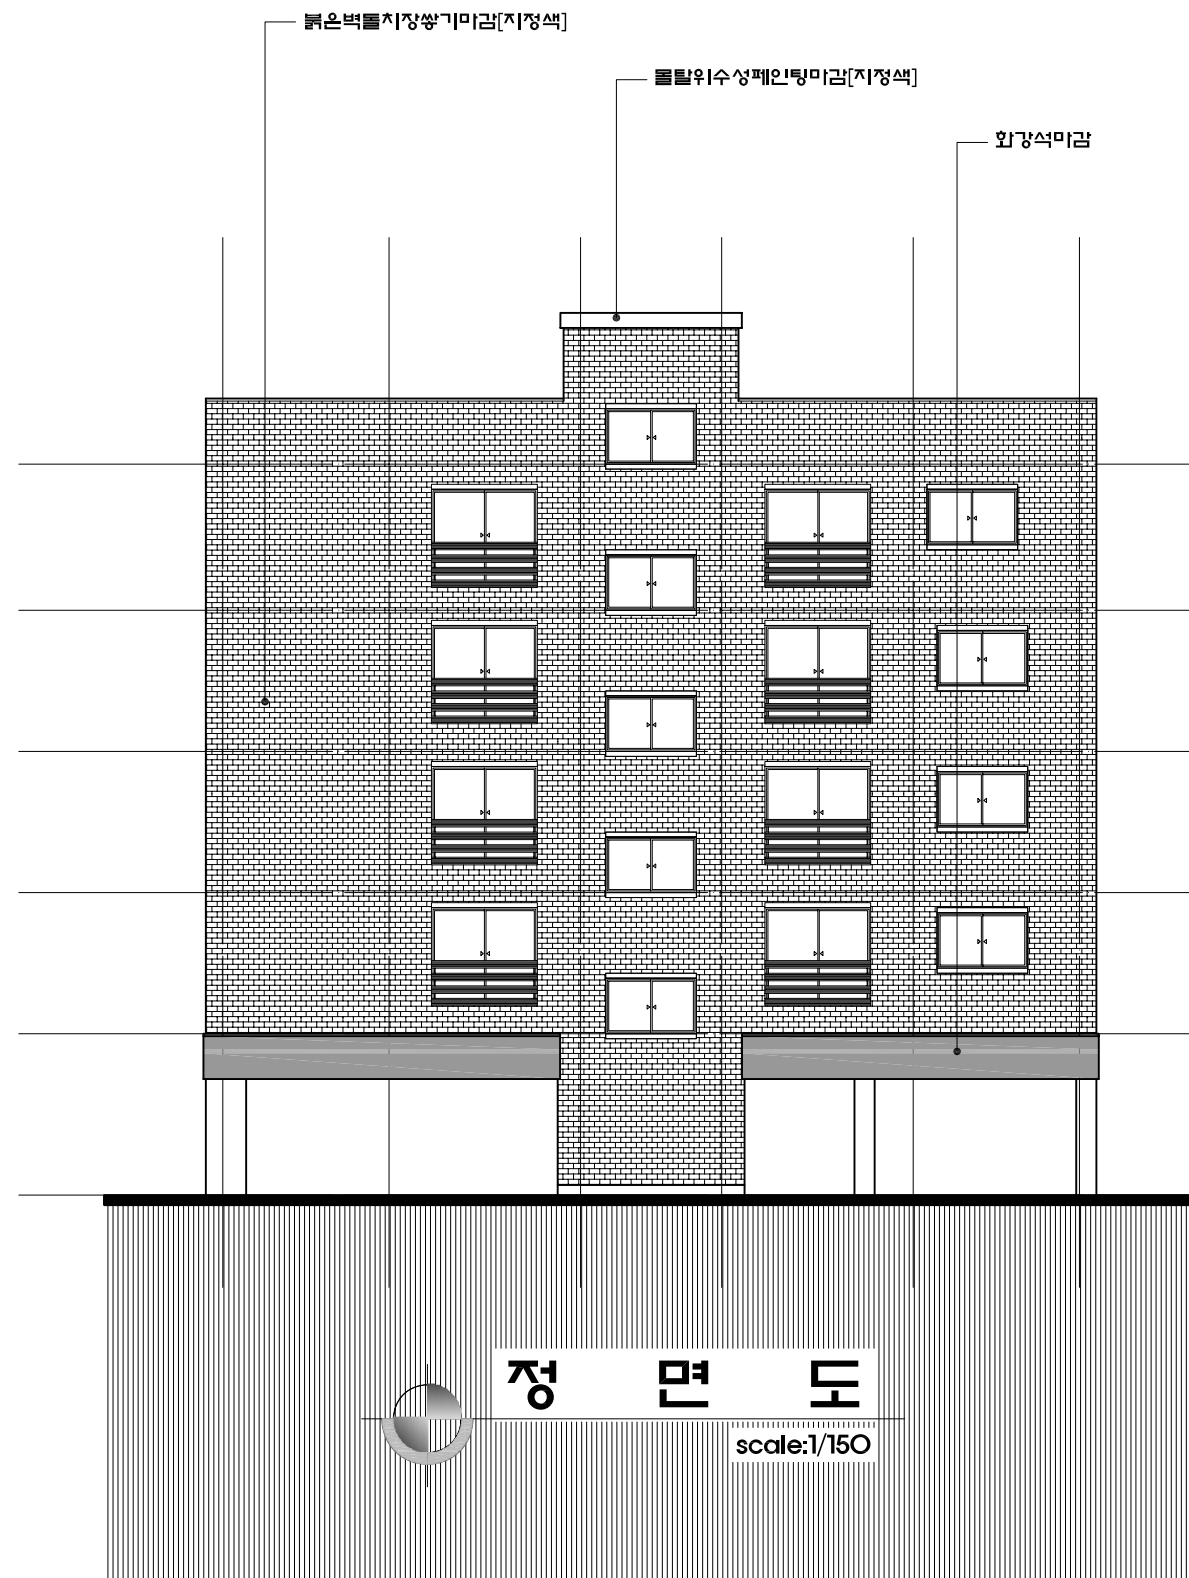



NO	DATE	REVISION DESCRIPTION	DRWN	CHK'D	APPD
		01. 일괄처리			

PROJECT TITLE
공사명
개봉동 326-12호
공동주택(다세대주택)
신축공사 설계도

CHK'D BY	SCALE
	1/150
	DATE
	2019.01
	DRWN BY

DRAWING TITLE
도면명
정면도/우측면도

B.C.C NO	JOB NO	APPROVE D BY
DRWG NO	DESIGNED BY	

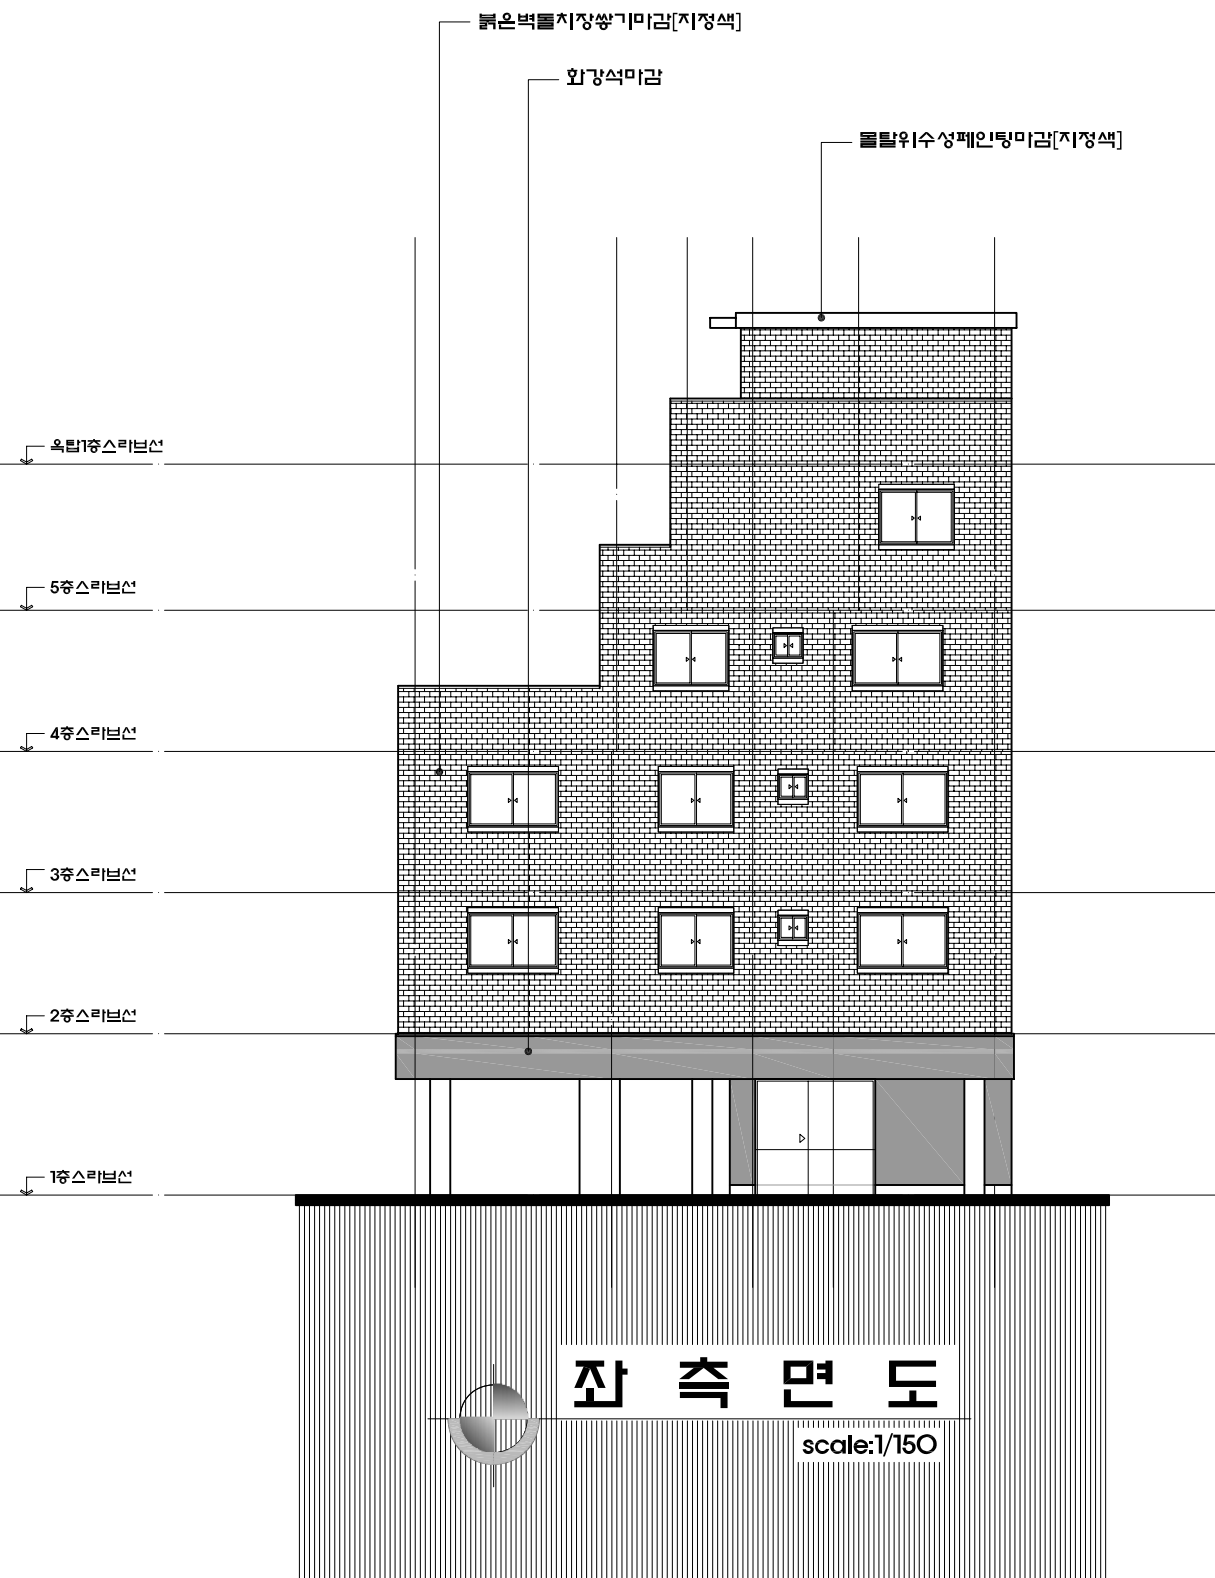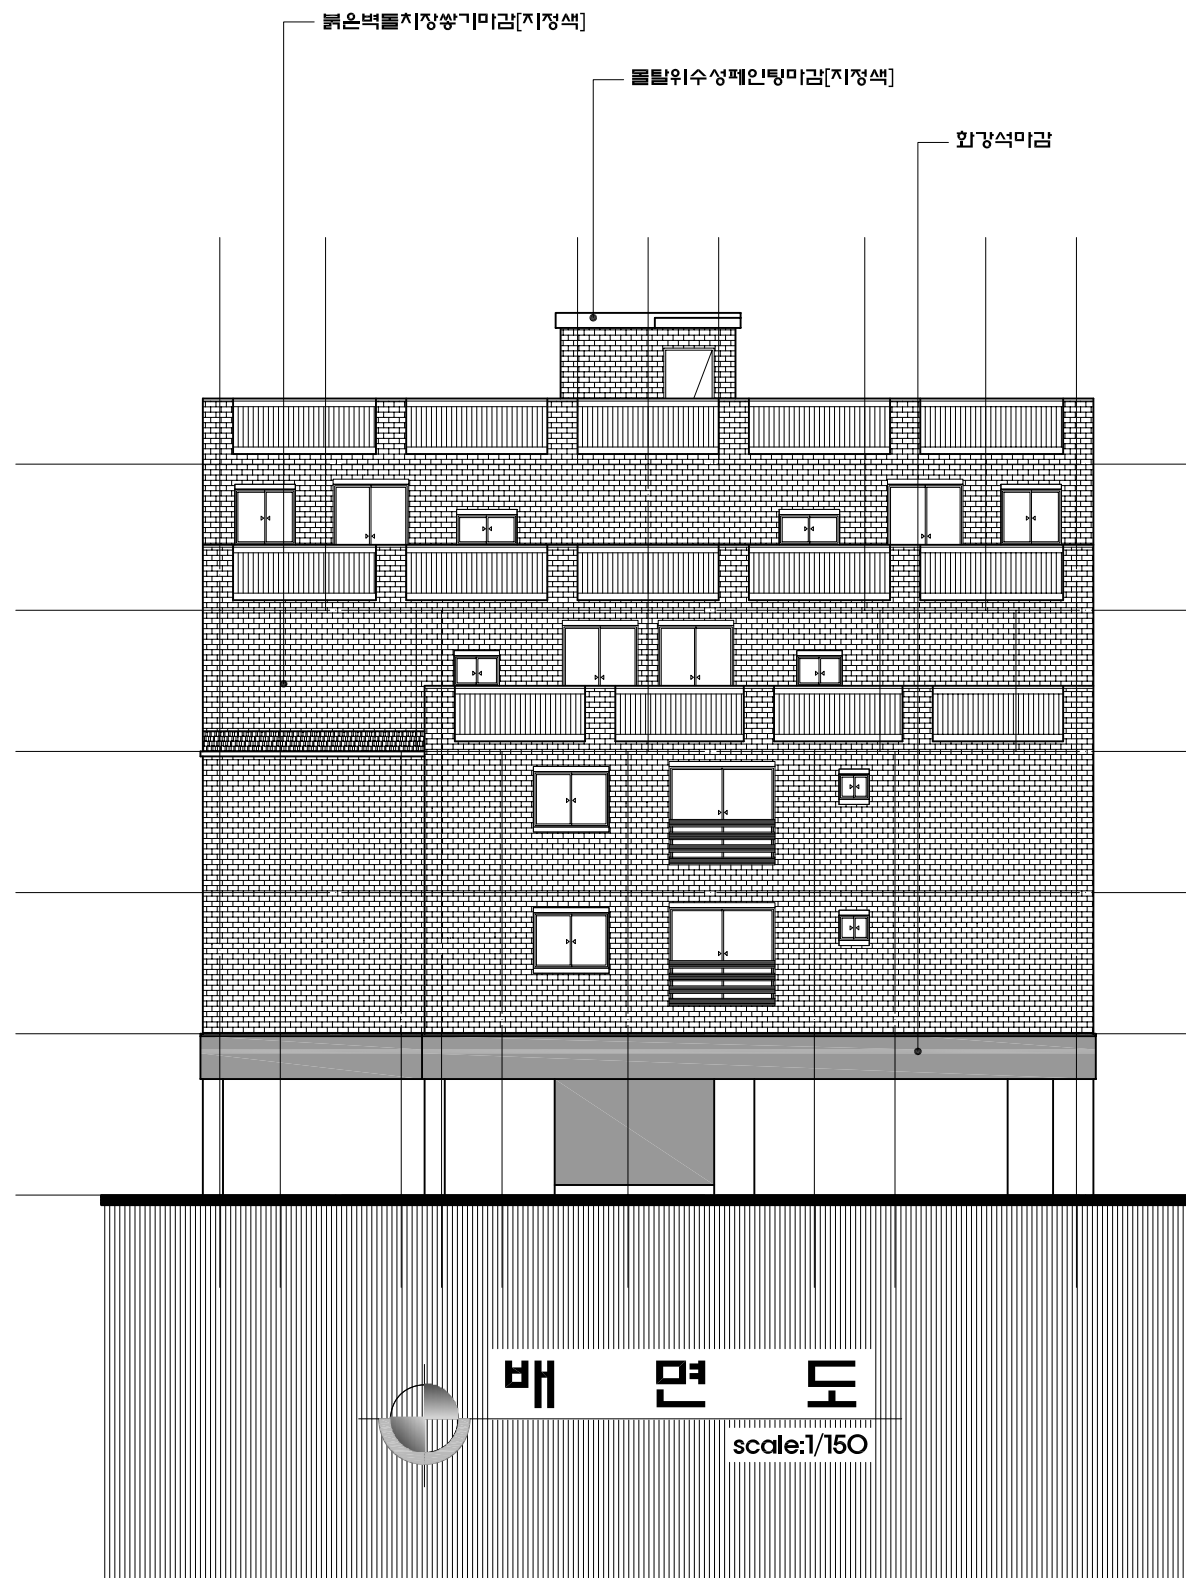


NO	DATE	REVISION DESCRIPTION	DRWN	CHK'D	APPD
		01. 일괄처리			

PROJECT TITLE
공사명
개봉동 326-12호
공동주택(다세대주택)
신축공사 설계도

CHK'D BY	SCALE 1/150
	DATE 2019.01
	DRWN BY

DRAWING TITLE
도면명
배면도/좌측면도


B.C.C NO	JOB NO	APPROVE D BY
DRWG NO		DESIGNED BY

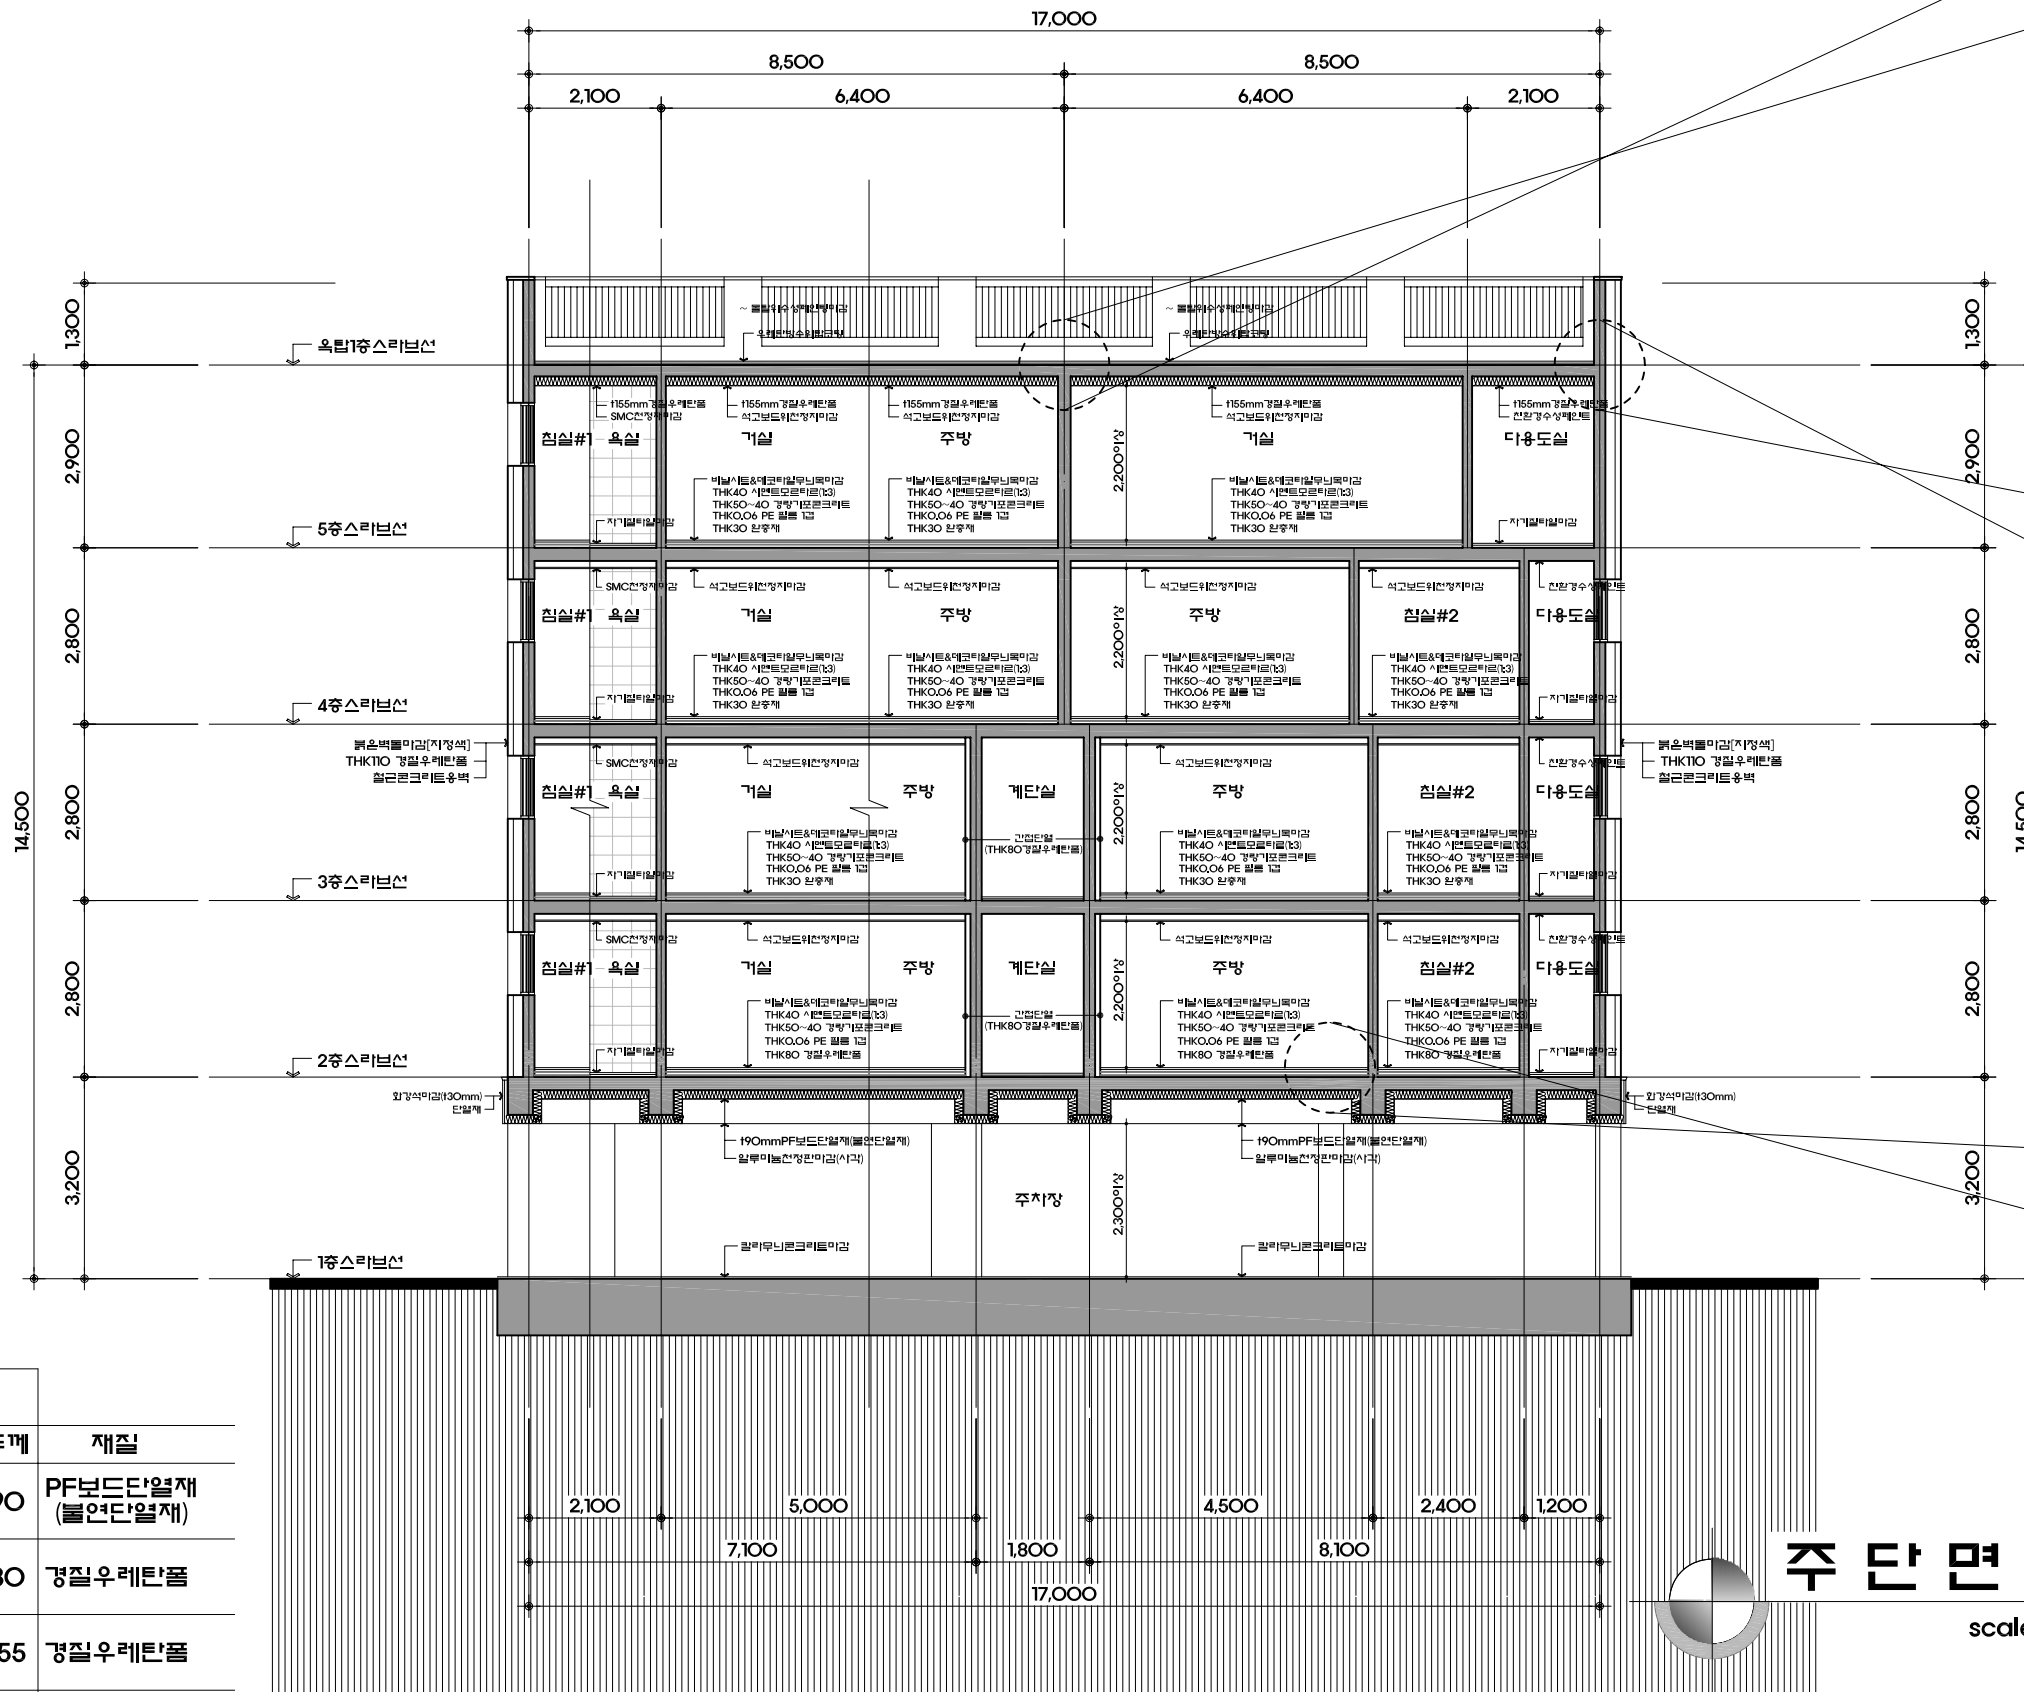


주 단 면 도

scale:1/120


〈최상층지붕 단열 단면상세〉

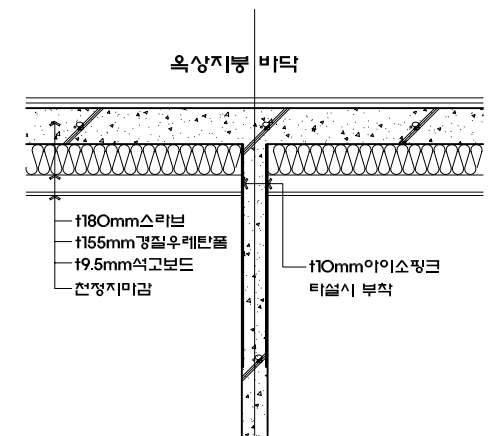

〈최상층지붕 단열 단면상세〉

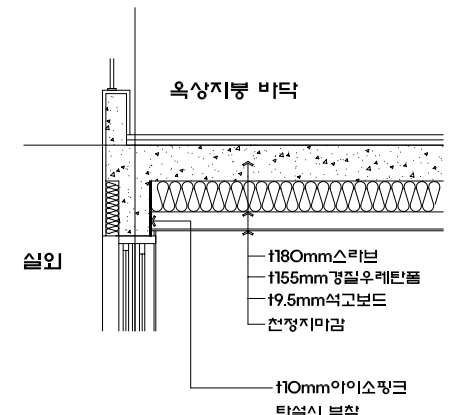

〈현관~바닥상세도(벽식구조)〉

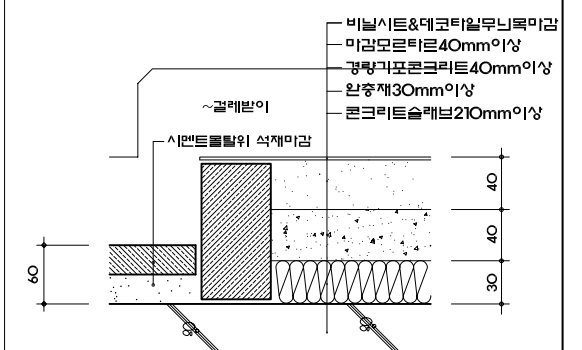

〈〈 완충재 성능 기준참조 〉〉

단열재 범위		
위치	두께	재질
주차장(천정)	90	PF보드단열재 (불연단열재)
2층 바닥	80	경질우레탄폼
지붕층	155	경질우레탄폼
외벽	110	경질우레탄폼

NO	DATE	REVISION DESCRIPTION	DRWN	CHK'D	APPD	PROJECT TITLE	CHK'D BY	SCALE	DRAWING TITLE	B.C.C NO	JOB NO	APPROVE D BY
		01. 일괄처리				개봉동 326-12호 공동주택(다세대주택) 신축공사 설계도		1/120	주단면도			
								DATE 2019.01				
								DRWN BY		DRWG NO		DESIGNED BY