

1. 조감도



2. 건축개요 및 현황도

■ 건축개요

- 설 계 명 : 개봉동 307-13 외 2필지 도시형생활주택(소형주택)
- 청년주택 -
- 대 지 위 치 : 서울특별시 구로구 개봉동 307-13 외 2필지
- 지 역 지 구 : 제3종일반주거지역
- 용 도 : 다세대주택 / 철근콘크리트구조
- 건 물 규 모 : 지상5층
- 대 지 면 적 : 348.10 m²
- 건 축 면 적 : 173.90 m²
- 연 면 적 : 659.47 m²
- 건 폐 율 : 50% (법규) / 49.96% (계획)
- 용 적 율 : 250.00% (법규) / 189.45% (계획)
- 최 고 높 이 : 14.60m
- 건 물 구 조 : 철근콘크리트구조
- 주 차 대 수 : 6.9대 (법규) / 8대 (계획)
- 조 경 면 적 : 17.41 m² (5%) (법규) / 21.35 m² (6.13%) (계획)



■ 위치도




■ 주변현황도

3. 입면도



본 상기도면은 디자인심의회 제출된 심의도면이며 설계도면과 일부 상이한 참조용이며 설계도면이 우선함

4. 설계자 의도

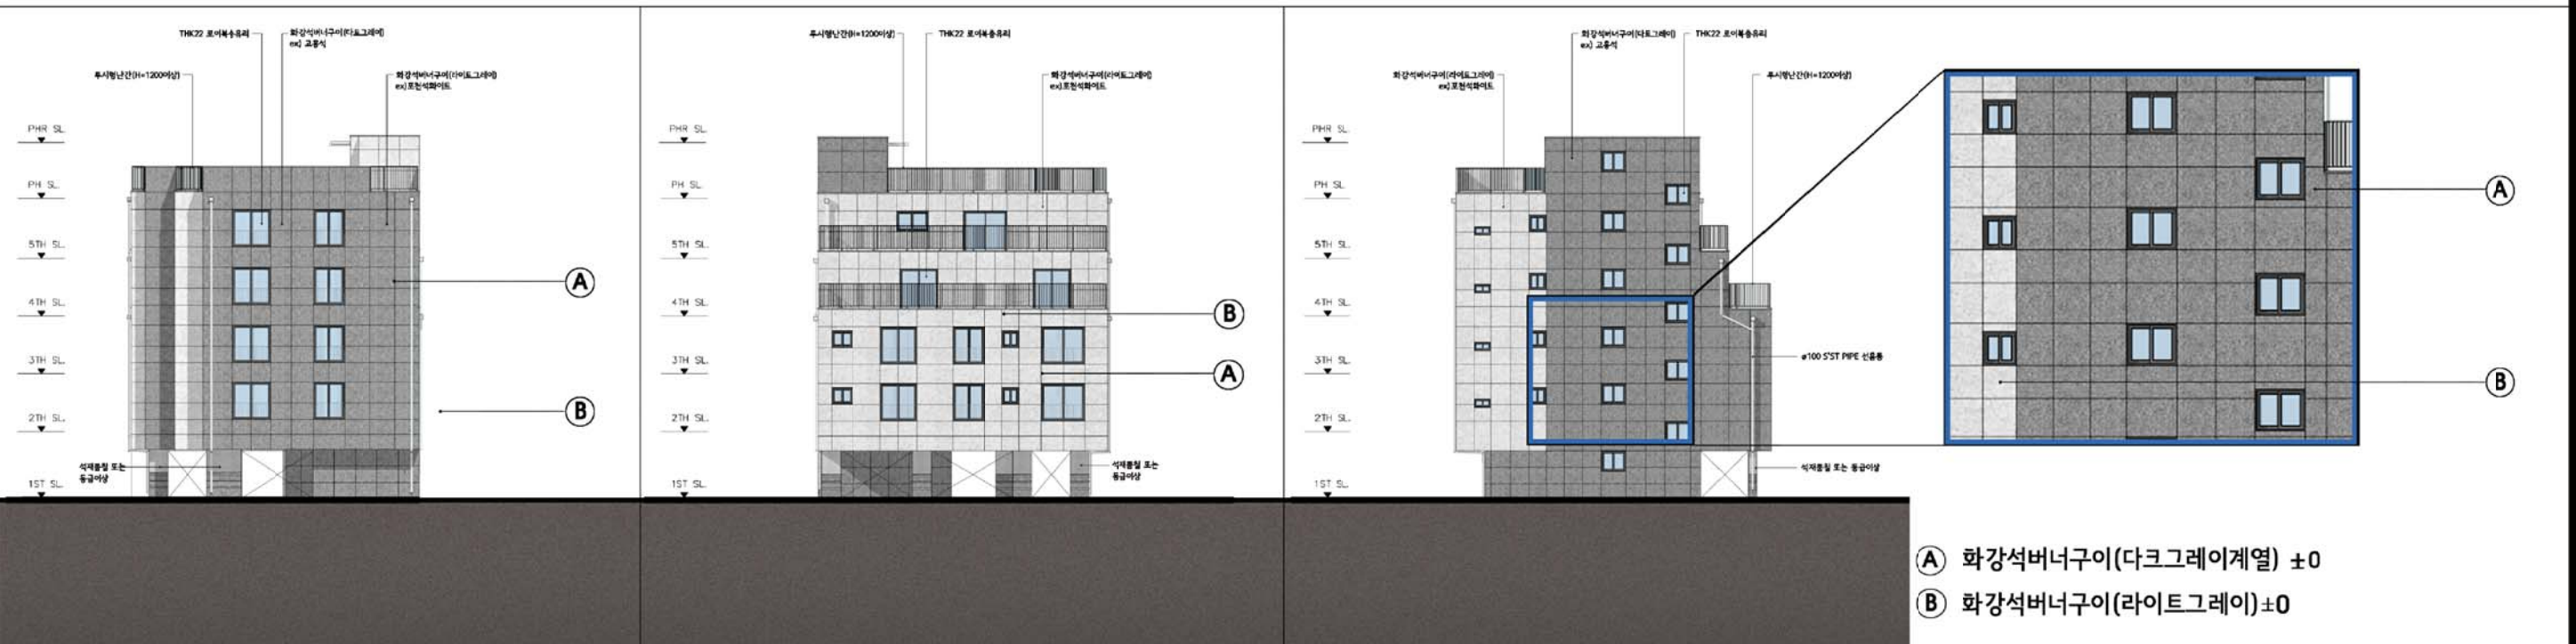


- ① 기본 외장재 화강석버너구이(다크그레이계열) 매스감을 부각시킨 디자인
- ② 외장재 화강석버너구이(라이트그레이) / 화강석 버너구이(다크그레이계열)를 강조색을 사용하여 건물의 인지성을 부여

— 기본 석재 화강석물갈기(다크그레이계열) 위주 / 화강석버너구이(라이트그레이)시공


5. 재료계획

1-1.석재 : 시선의 흐름과 인지성을 고려한 재료

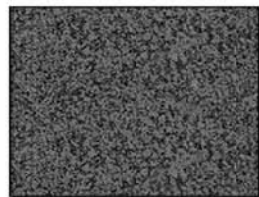

- 외장재 : 화강석버너구이(다크그레이계열) / 고흥석

1_2.석재 : 시선의 흐름과 인지성을 고려한 재료

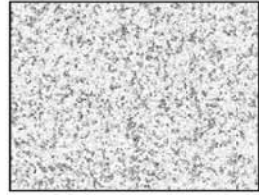

- 외장재 : 화강석버너구이(라이트그레이) / 포천석화이트

2.기둥 : 안정감이 느껴지는 색상의 재료



- 외장재 : 석재붙칠마감

■ 외장재

구분	실명	재료명
1층	피로티 주차장	바닥 : THK100칼라무늬 CON'C 천정 : AL천장재
2~5층	현관	폴리싱타일
	방	바닥 : 데코타일 무늬목 마감 벽 : 친환경실크벽지 천정 : 친환경천정기
	거실	바닥 : 데코타일 무늬목 마감 벽 : 친환경실크벽지 천정 : 친환경천정기
	계단실	바닥 : THK30 화강석 물갈기 벽 : 다채무늬도로

■ 내장재

6. 색채계획

- 주조색 / 보조색 / 강조색



WHITE



GREY




DARK GREY




- 도시이미지를 형상화한 모듈러에 흑백의 대비를 준 컨셉에 충실한 디자인 방향에 따른 대비적인 재료 및 디자인적용으로 다양성 부여

본 상기도면은 디자인심의회 제출된 심의도면이며 설계도면과 일부 상이한 참조용이며 설계도면이 우선함

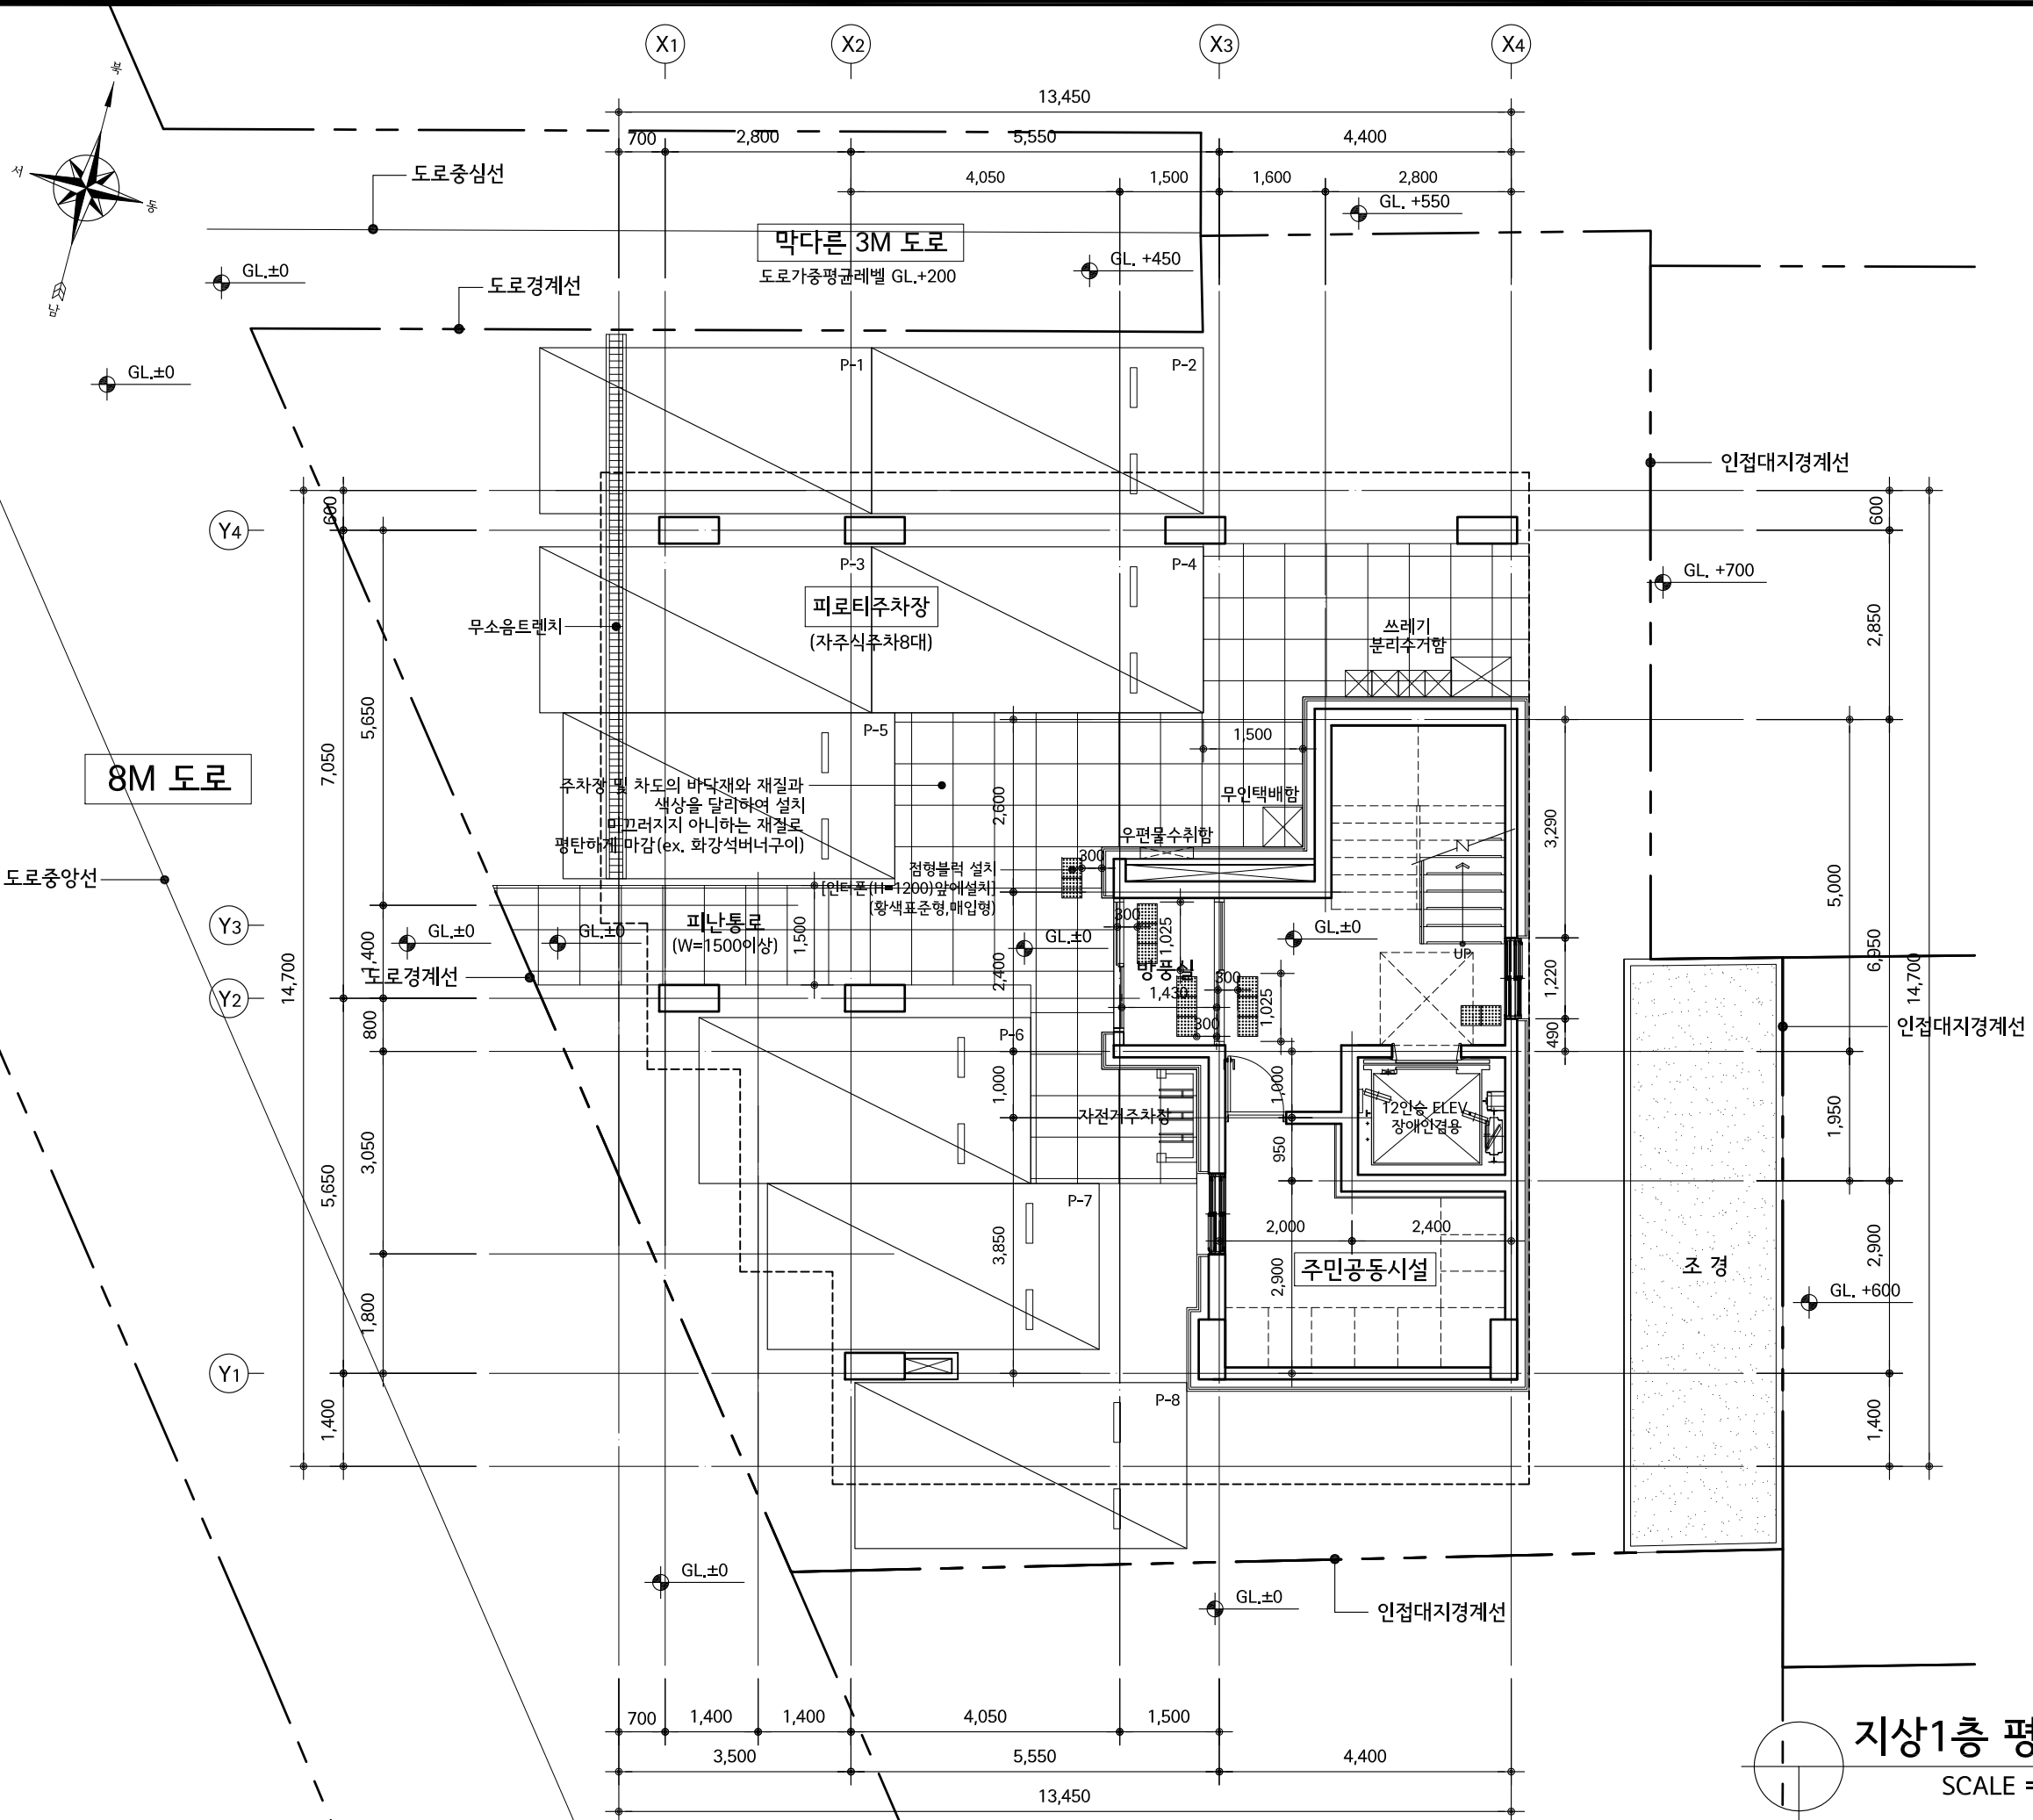


지상1층 평면도
SCALE = 1/100

사업명칭 PROJECT TITLE	
구로구 개봉동 307-13 도시형생활주택(소형주택) 신축공사-청년주택-	
사업번호 PROJECT NO.	
변경사항 ISSUER & REVISIONS	
△	
△	
△	
△	
△	
hanndas Architects & Interiors 인천광역시 연수구 남동로55번길 6-12 T_032,464,8775 F_032,881,9102	
제 도 DRAWN BY	
설 계 DESIGNED BY	
심 사 CHECKED BY	
승 인 APPROVED BY	건축사 이선영
추가사항 NOTE	
현동설계 CONSULTANTS	
일 자 DATE	
도면번호 DRAWING NO.	A - 101
축 척 SCALE	A3 : 1 / 100
도면명 NAME OF DRAWING	지상1층 평면도

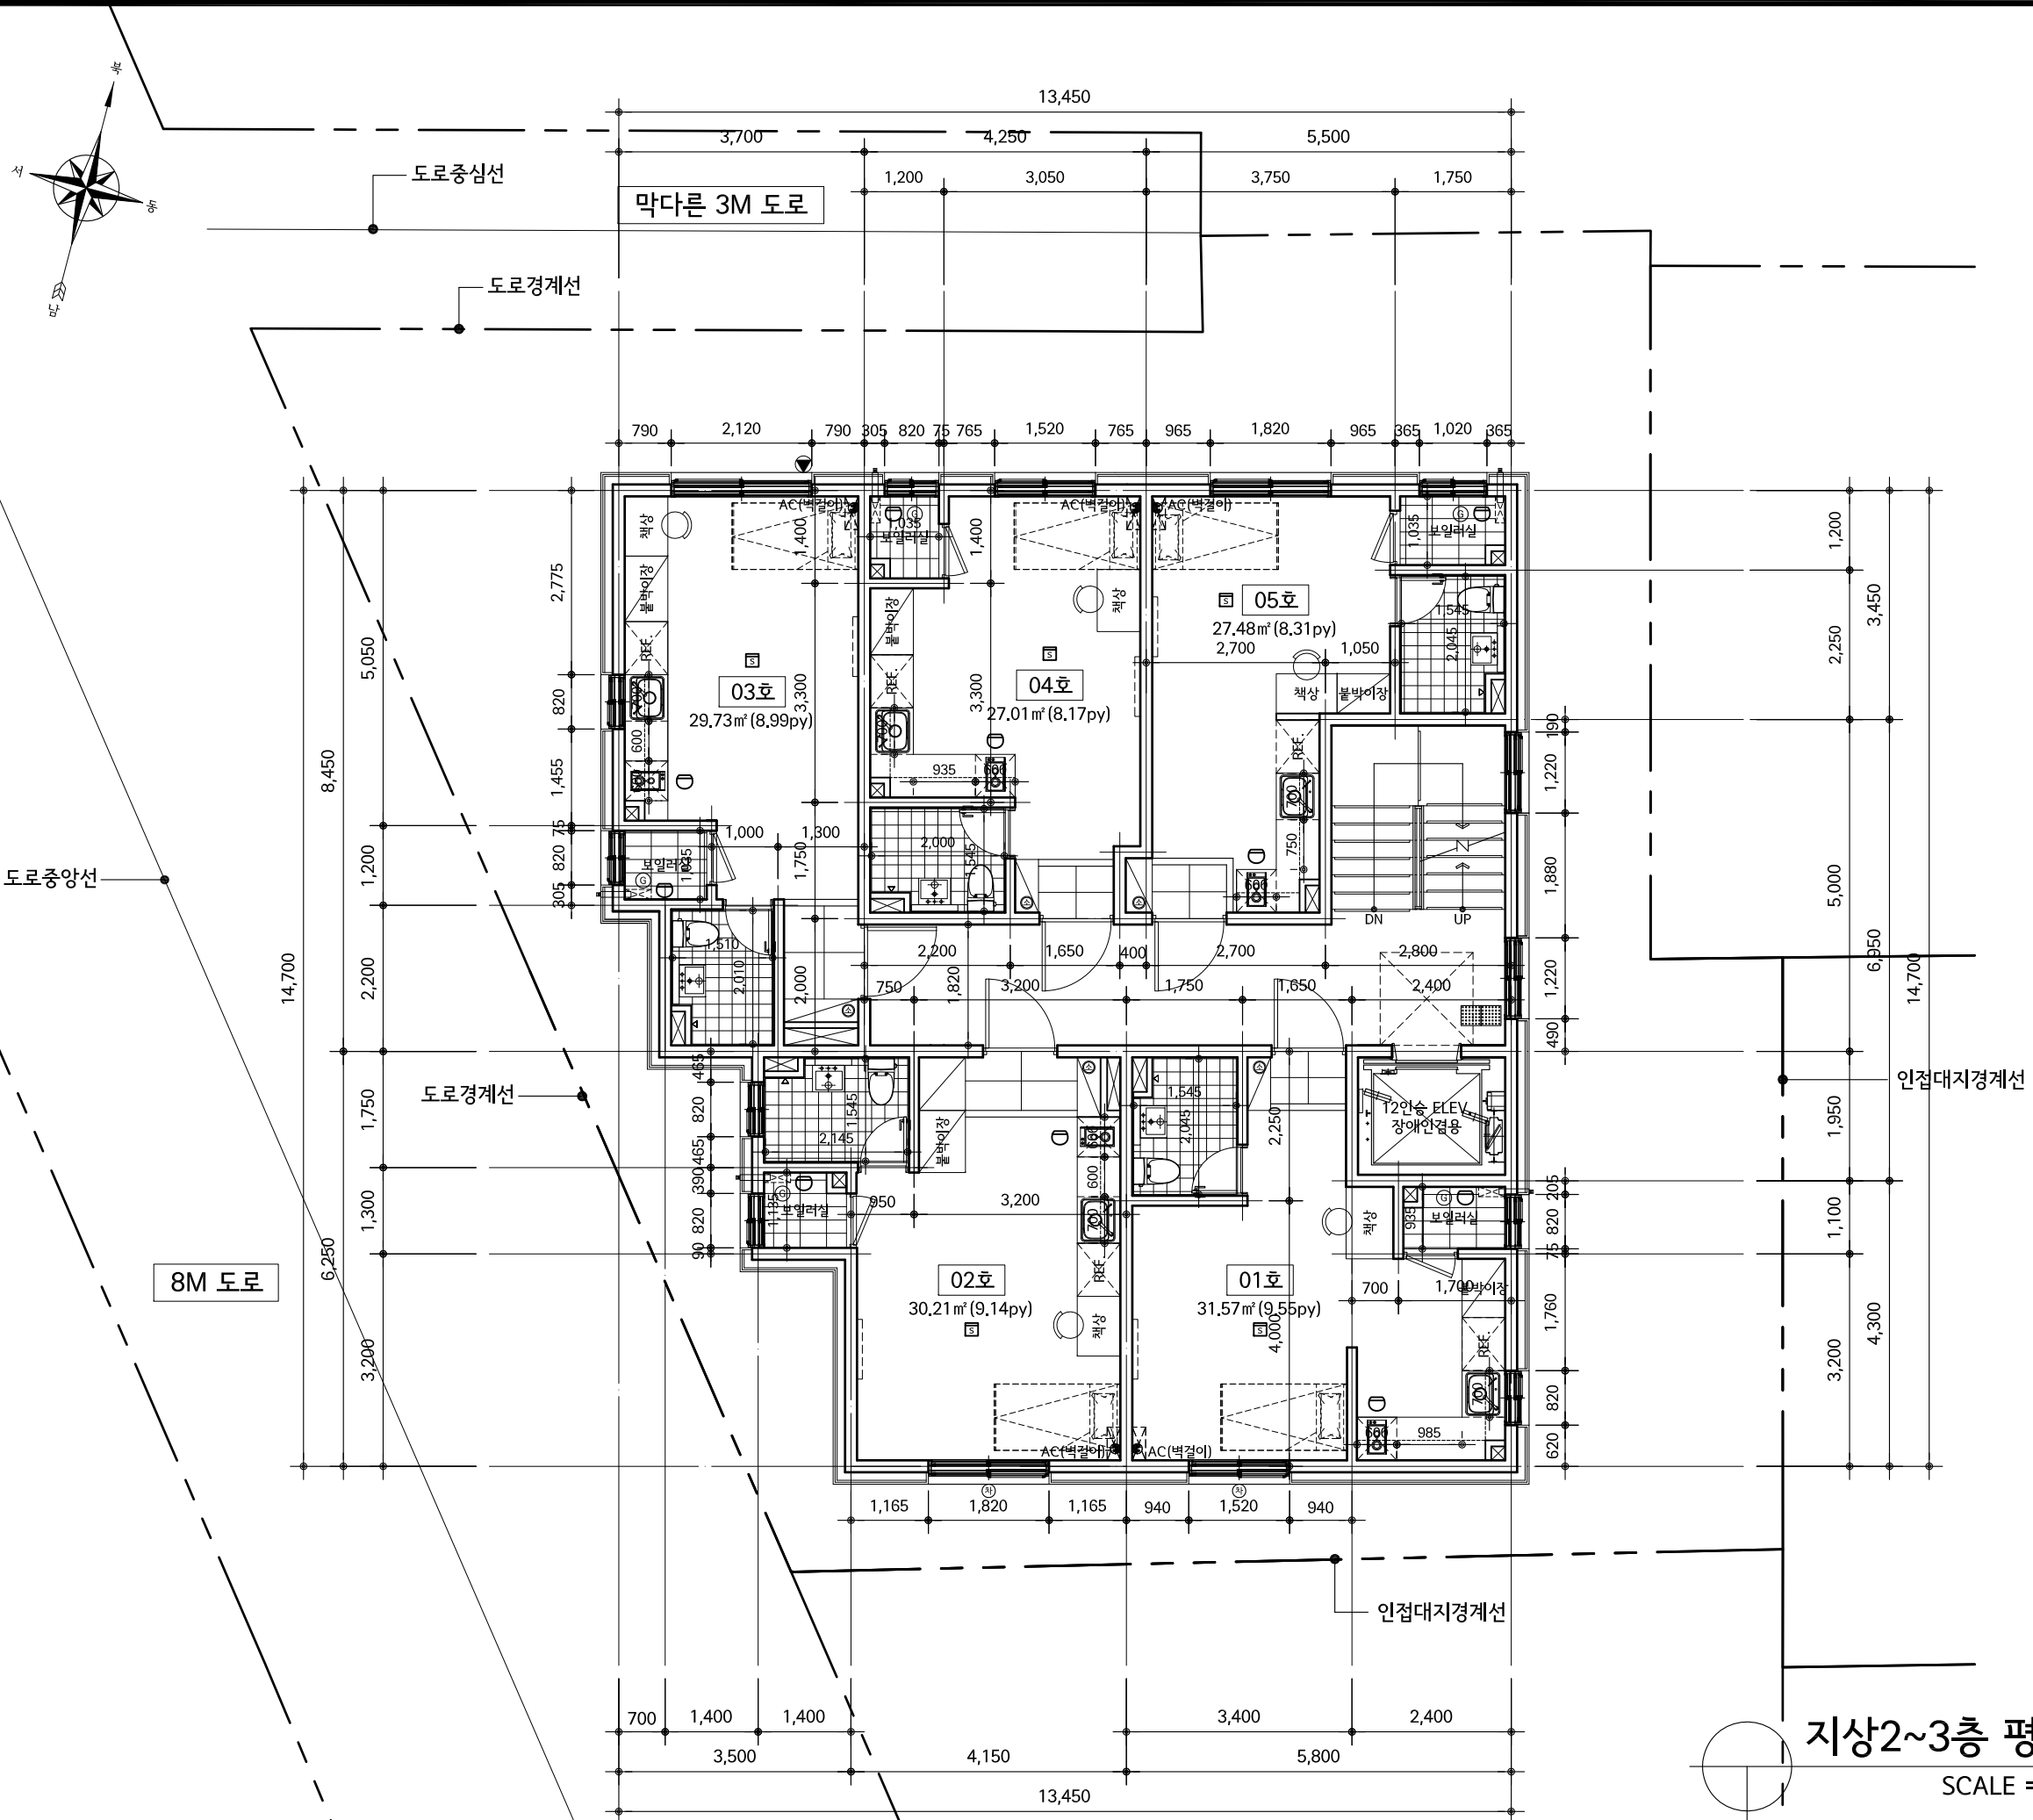


지상2~3층 평면도
SCALE = 1/100

사업명칭 PROJECT TITLE	구로구 개봉동 307-13 도시형생활주택(소형주택) 신축공사 -청년주택-
사업번호 PROJECT NO.	
변경사항 ISSUER & REVISIONS	
제 도 DRAWN BY	
설 계 DESIGNED BY	
심 사 CHECKED BY	
승 인 APPROVED BY	건축사 이선영
추가사항 NOTE	
현동설계 CONSULTANTS	
일 자 DATE	
도면번호 DRAWING NO.	A - 102
축 척 SCALE	A3 : 1 / 100
도면명 NAME OF DRAWING	지상2~3층 평면도

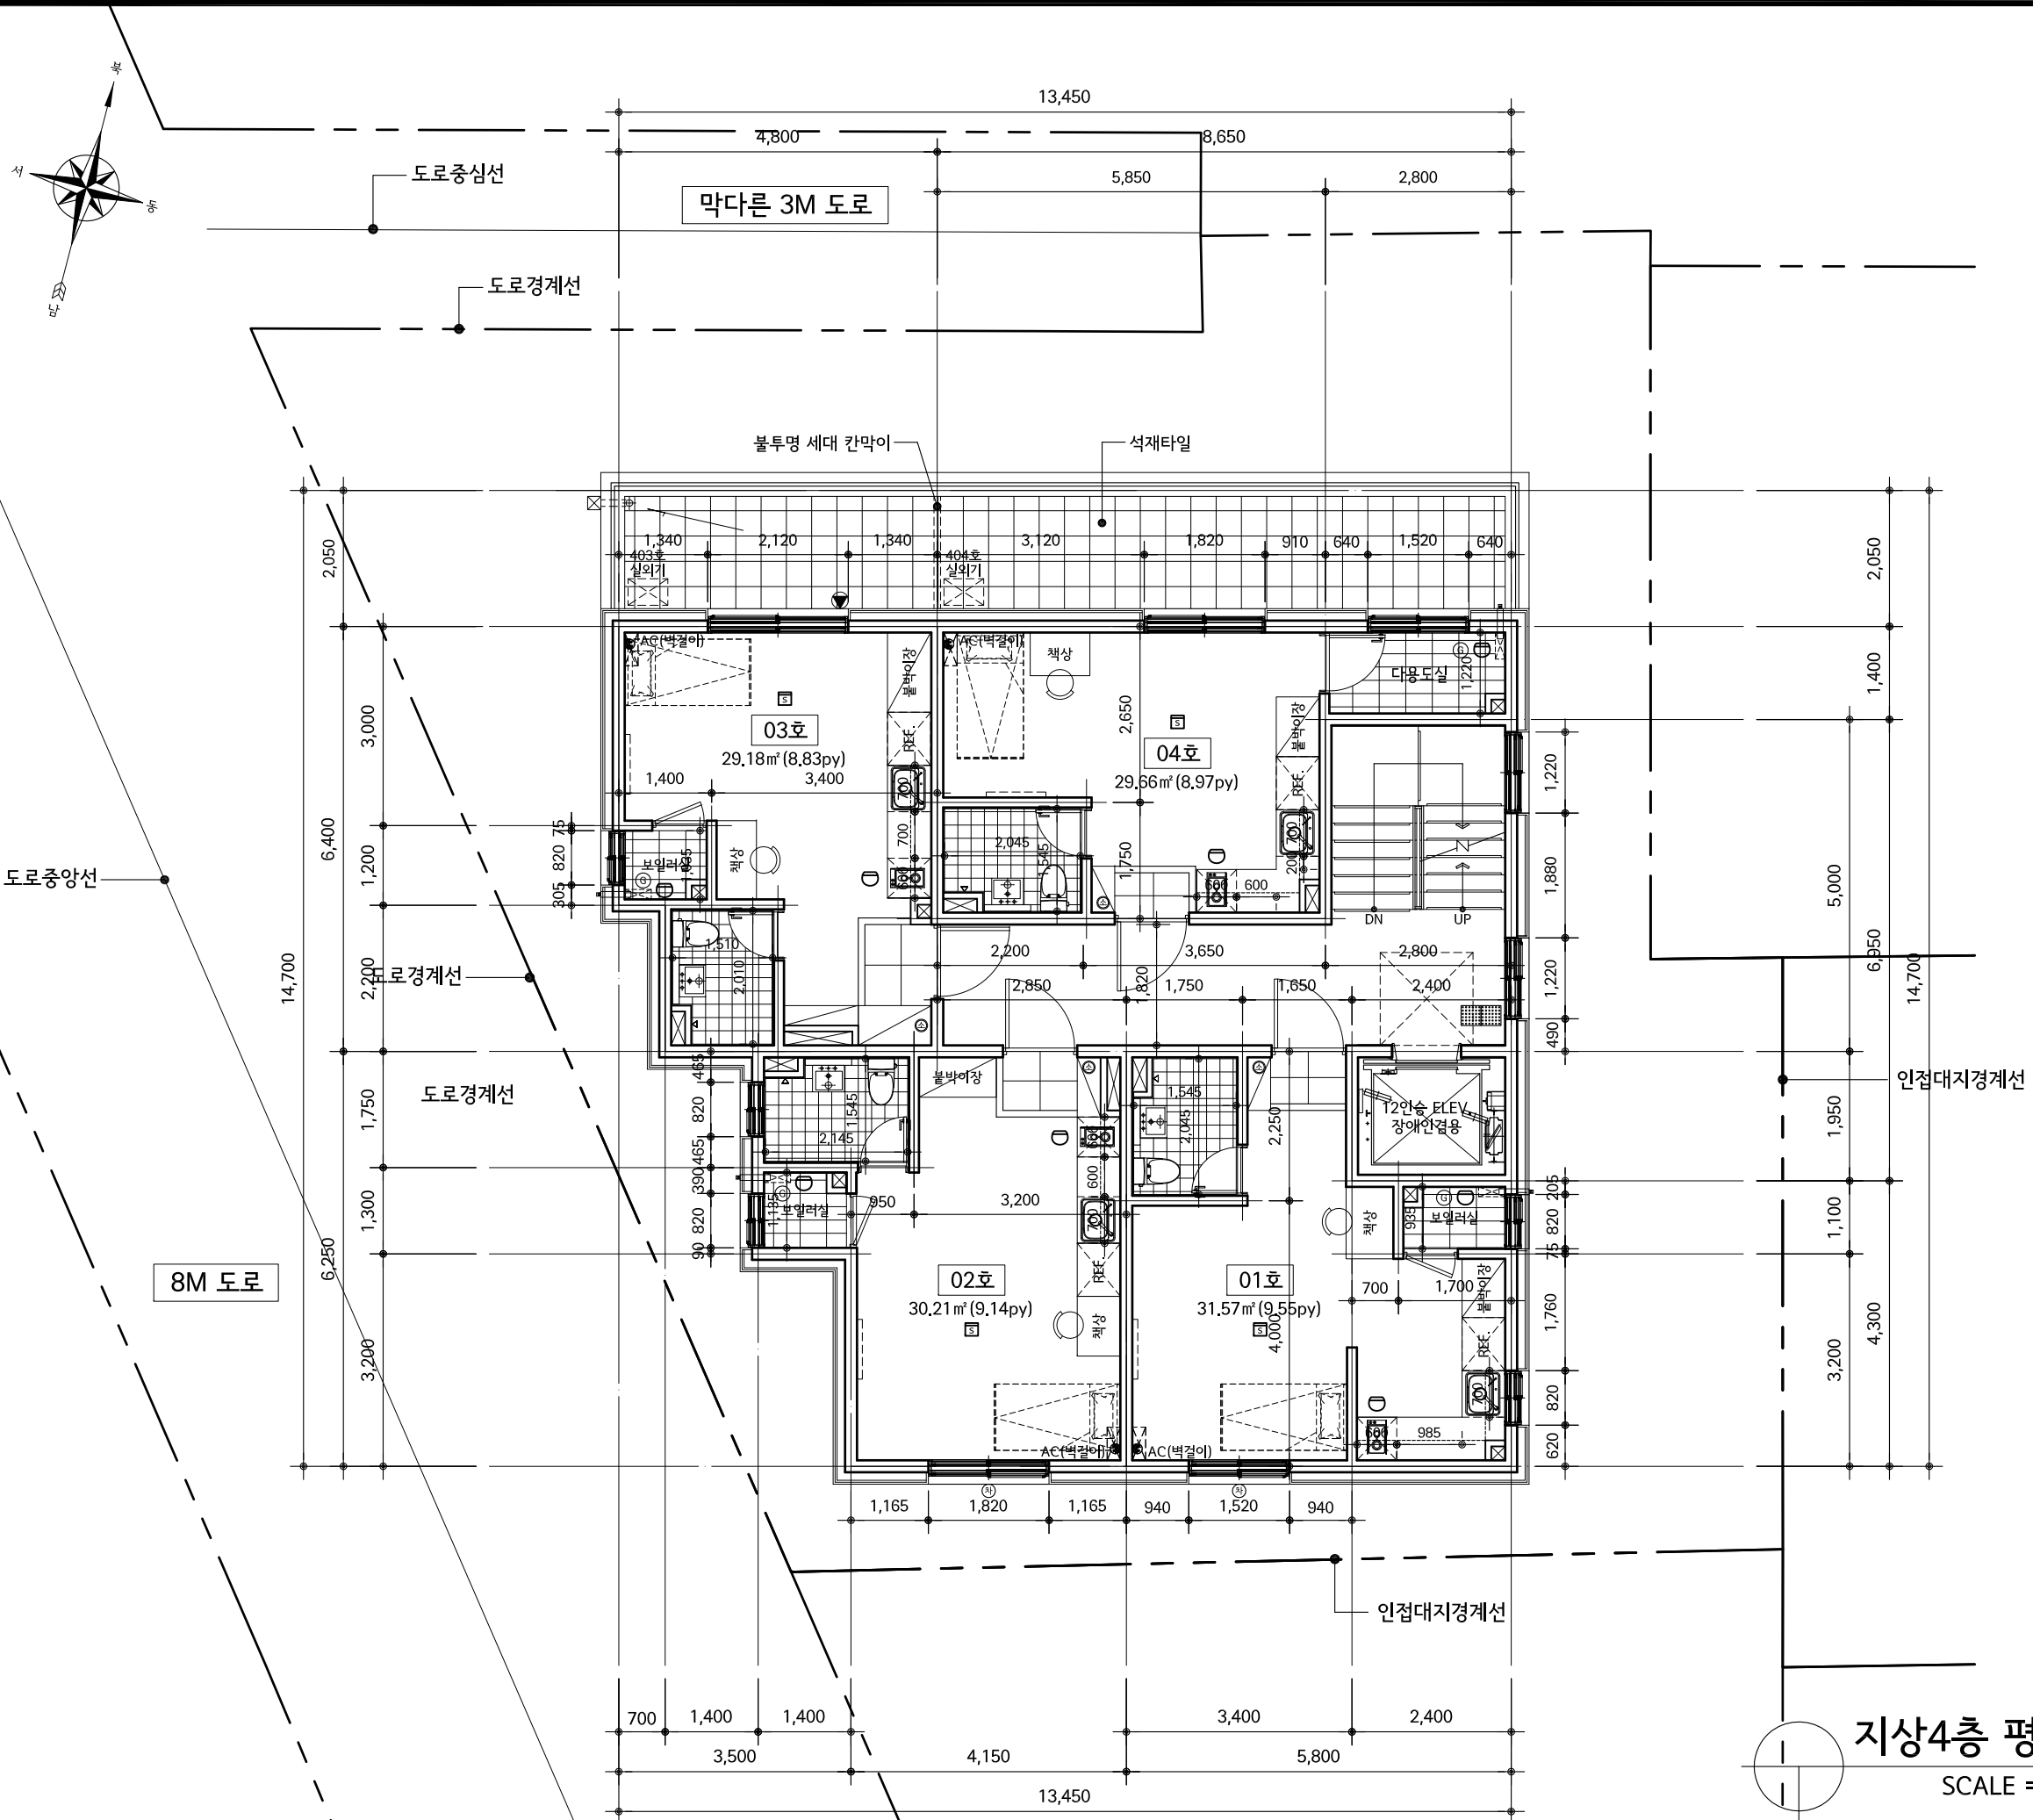




지상4층 평면도
SCALE = 1/100

사업명칭 PROJECT TITLE	
구로구 개봉동 307-13 도시형생활주택(소형주택) 신축공사 -청년주택-	
사업번호 PROJECT NO.	
변경사항 ISSUER & REVISIONS	
△	
△	
△	
△	
△	
hanndas Architects & Interiors 인천광역시 연수구 남동로55번길 6-12 T_032,464,8775 F_032,881,9102	
제 도 DRAWN BY	
설 계 DESIGNED BY	
심 사 CHECKED BY	
승 인 APPROVED BY	건축사 이선영
추가사항 NOTE	
현동설계 CONSULTANTS	
일 자 DATE	
도면번호 DRAWING NO.	A - 103
축 척 SCALE	A3 : 1 / 100
도면명 NAME OF DRAWING	지상4층 평면도

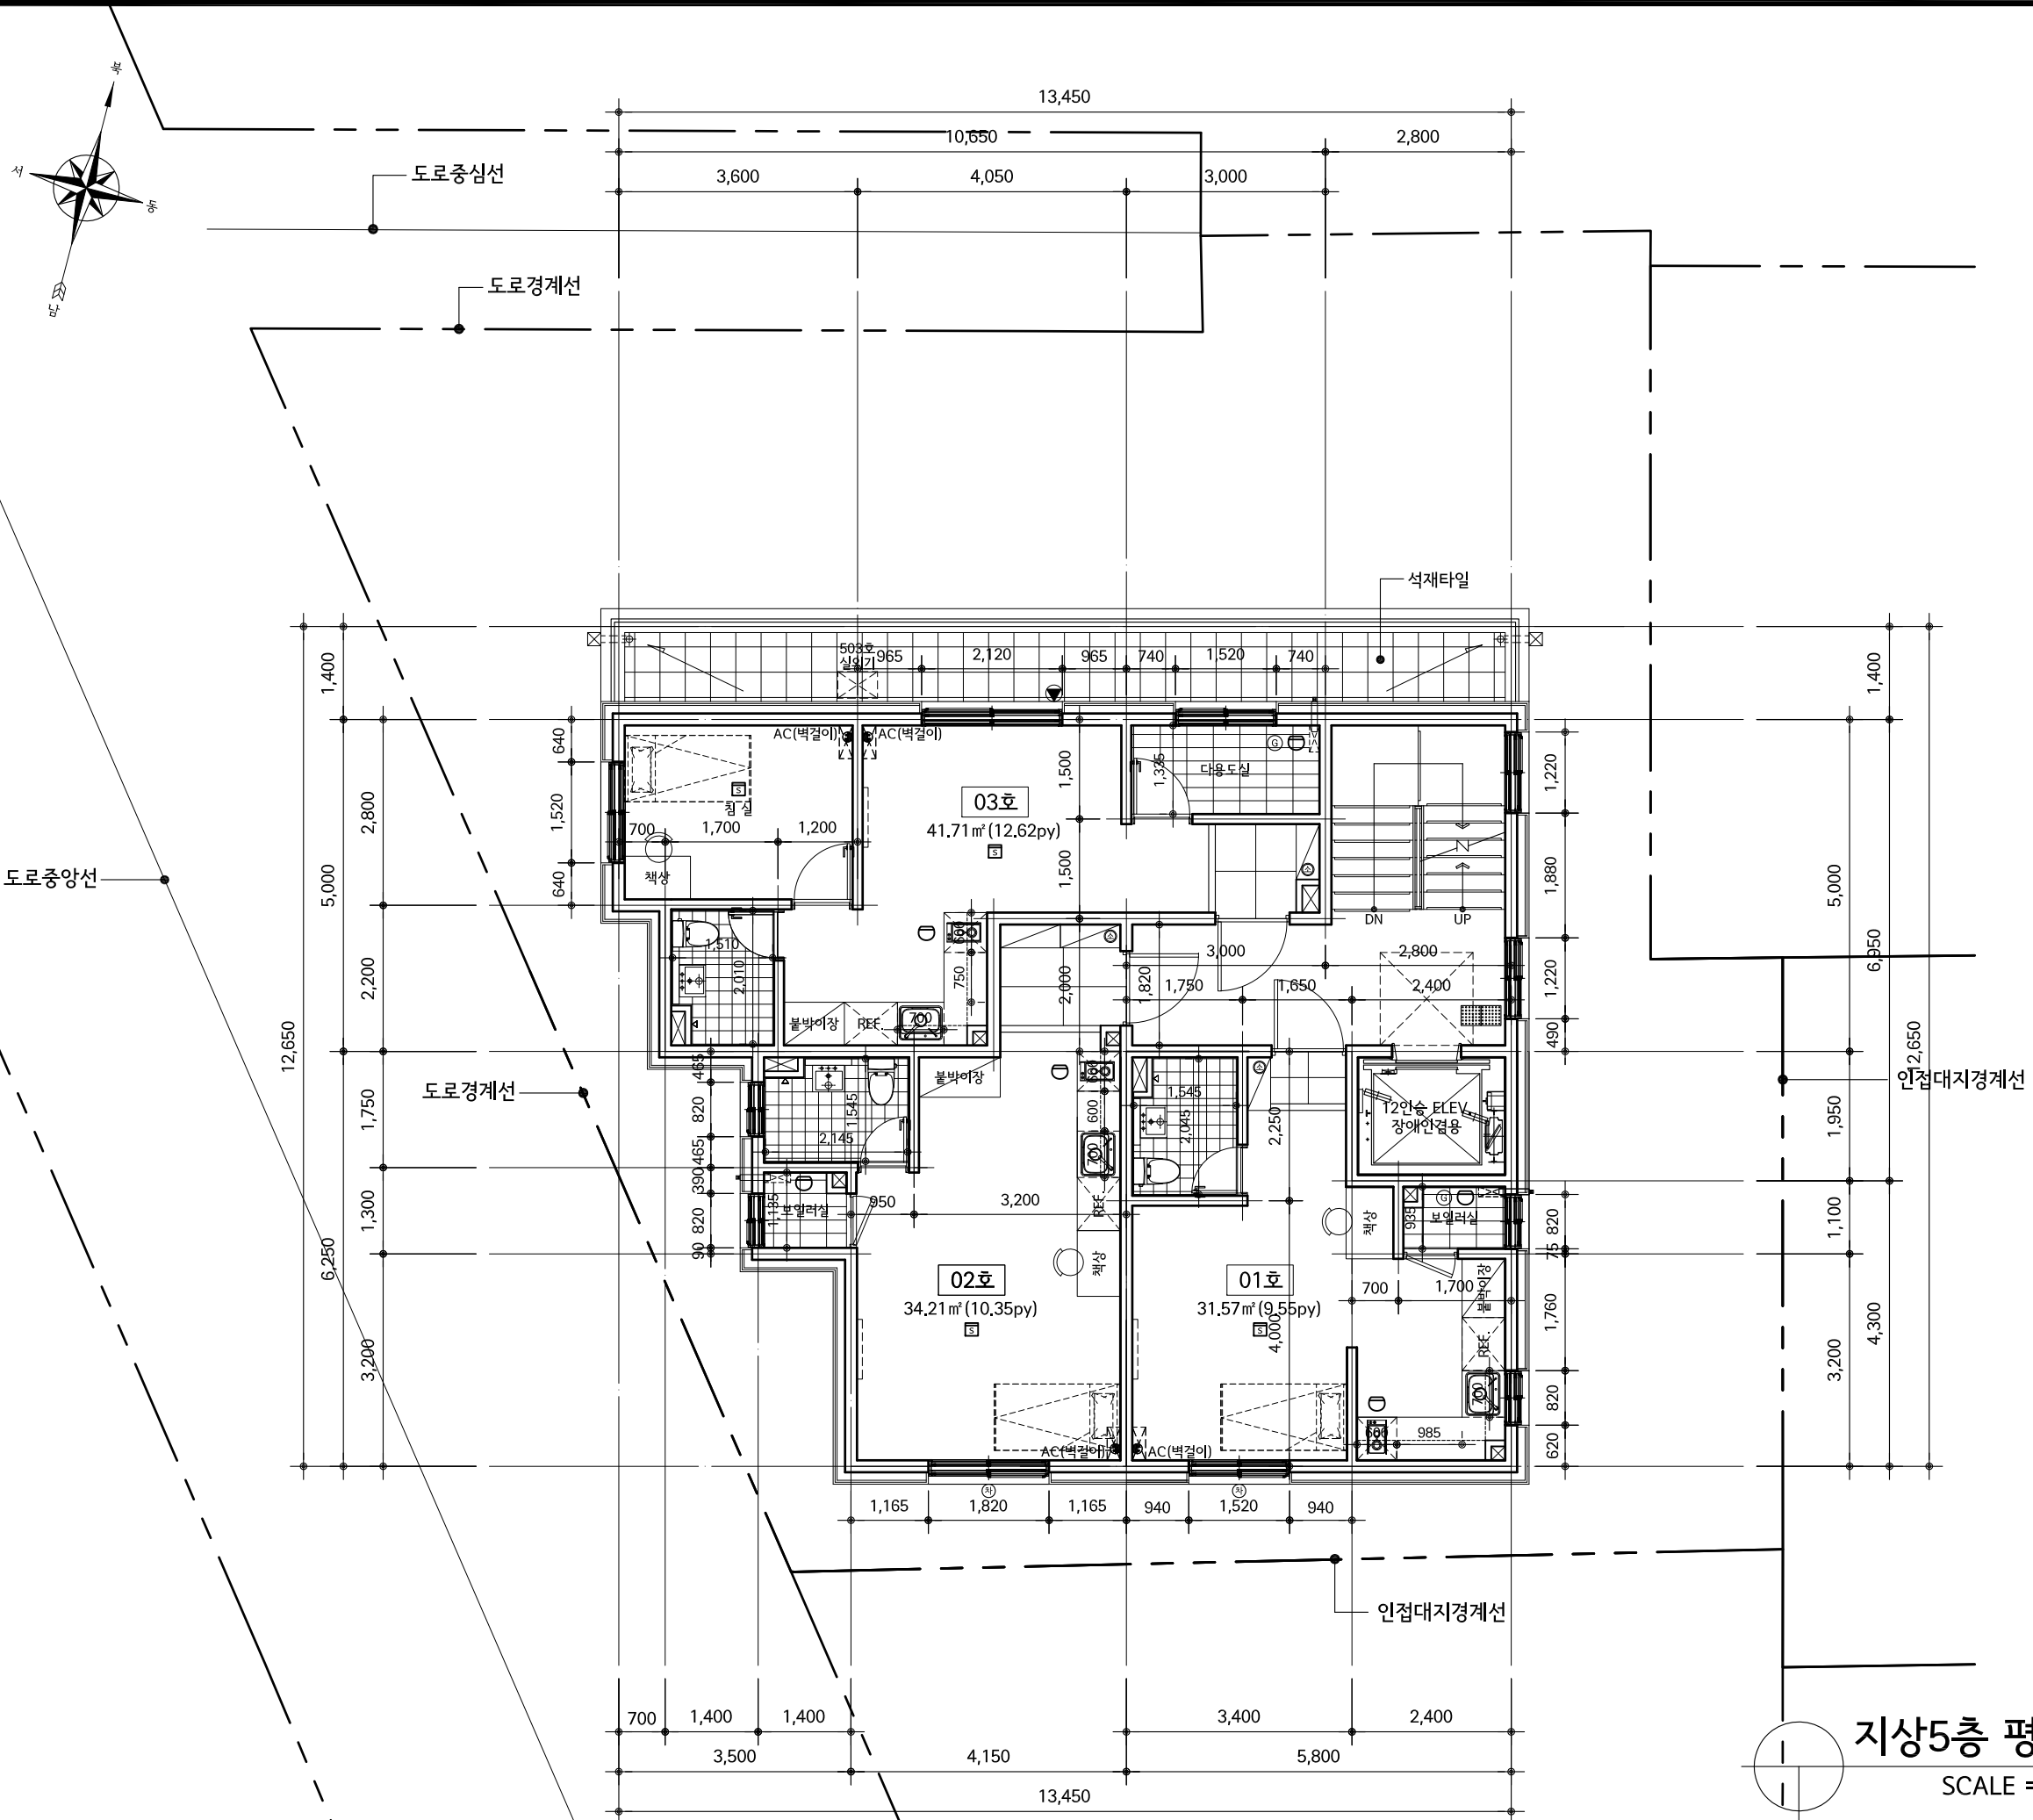

지상5층 평면도
SCALE = 1/100

사업명칭 PROJECT TITLE	
구로구 개봉동 307-13 도시형생활주택(소형주택) 신축공사 -청년주택-	
사업번호 PROJECT NO.	
변경사항 ISSUER & REVISIONS	
△	
△	
△	
△	
△	
hanndas Architects & Interiors 인천광역시 연수구 남동로55번길 6-12 T_032,464,8775 F_032,881,9102	
제 도 DRAWN BY	
설 계 DESIGNED BY	
심 사 CHECKED BY	
승 인 APPROVED BY	건축사 이선영
추가사항 NOTE	
현동설계 CONSULTANTS	
일 자 DATE	
도면번호 DRAWING NO.	A - 104
축 척 SCALE	A3 : 1 / 100
도면명 NAME OF DRAWING	지상5층 평면도

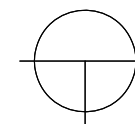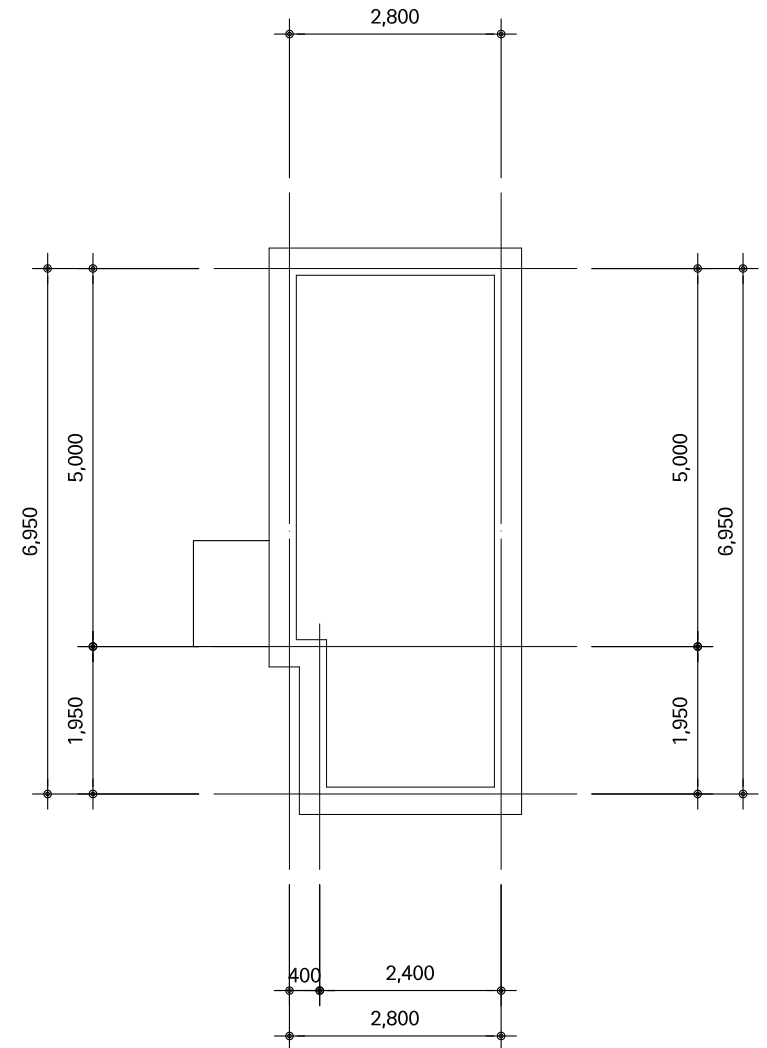
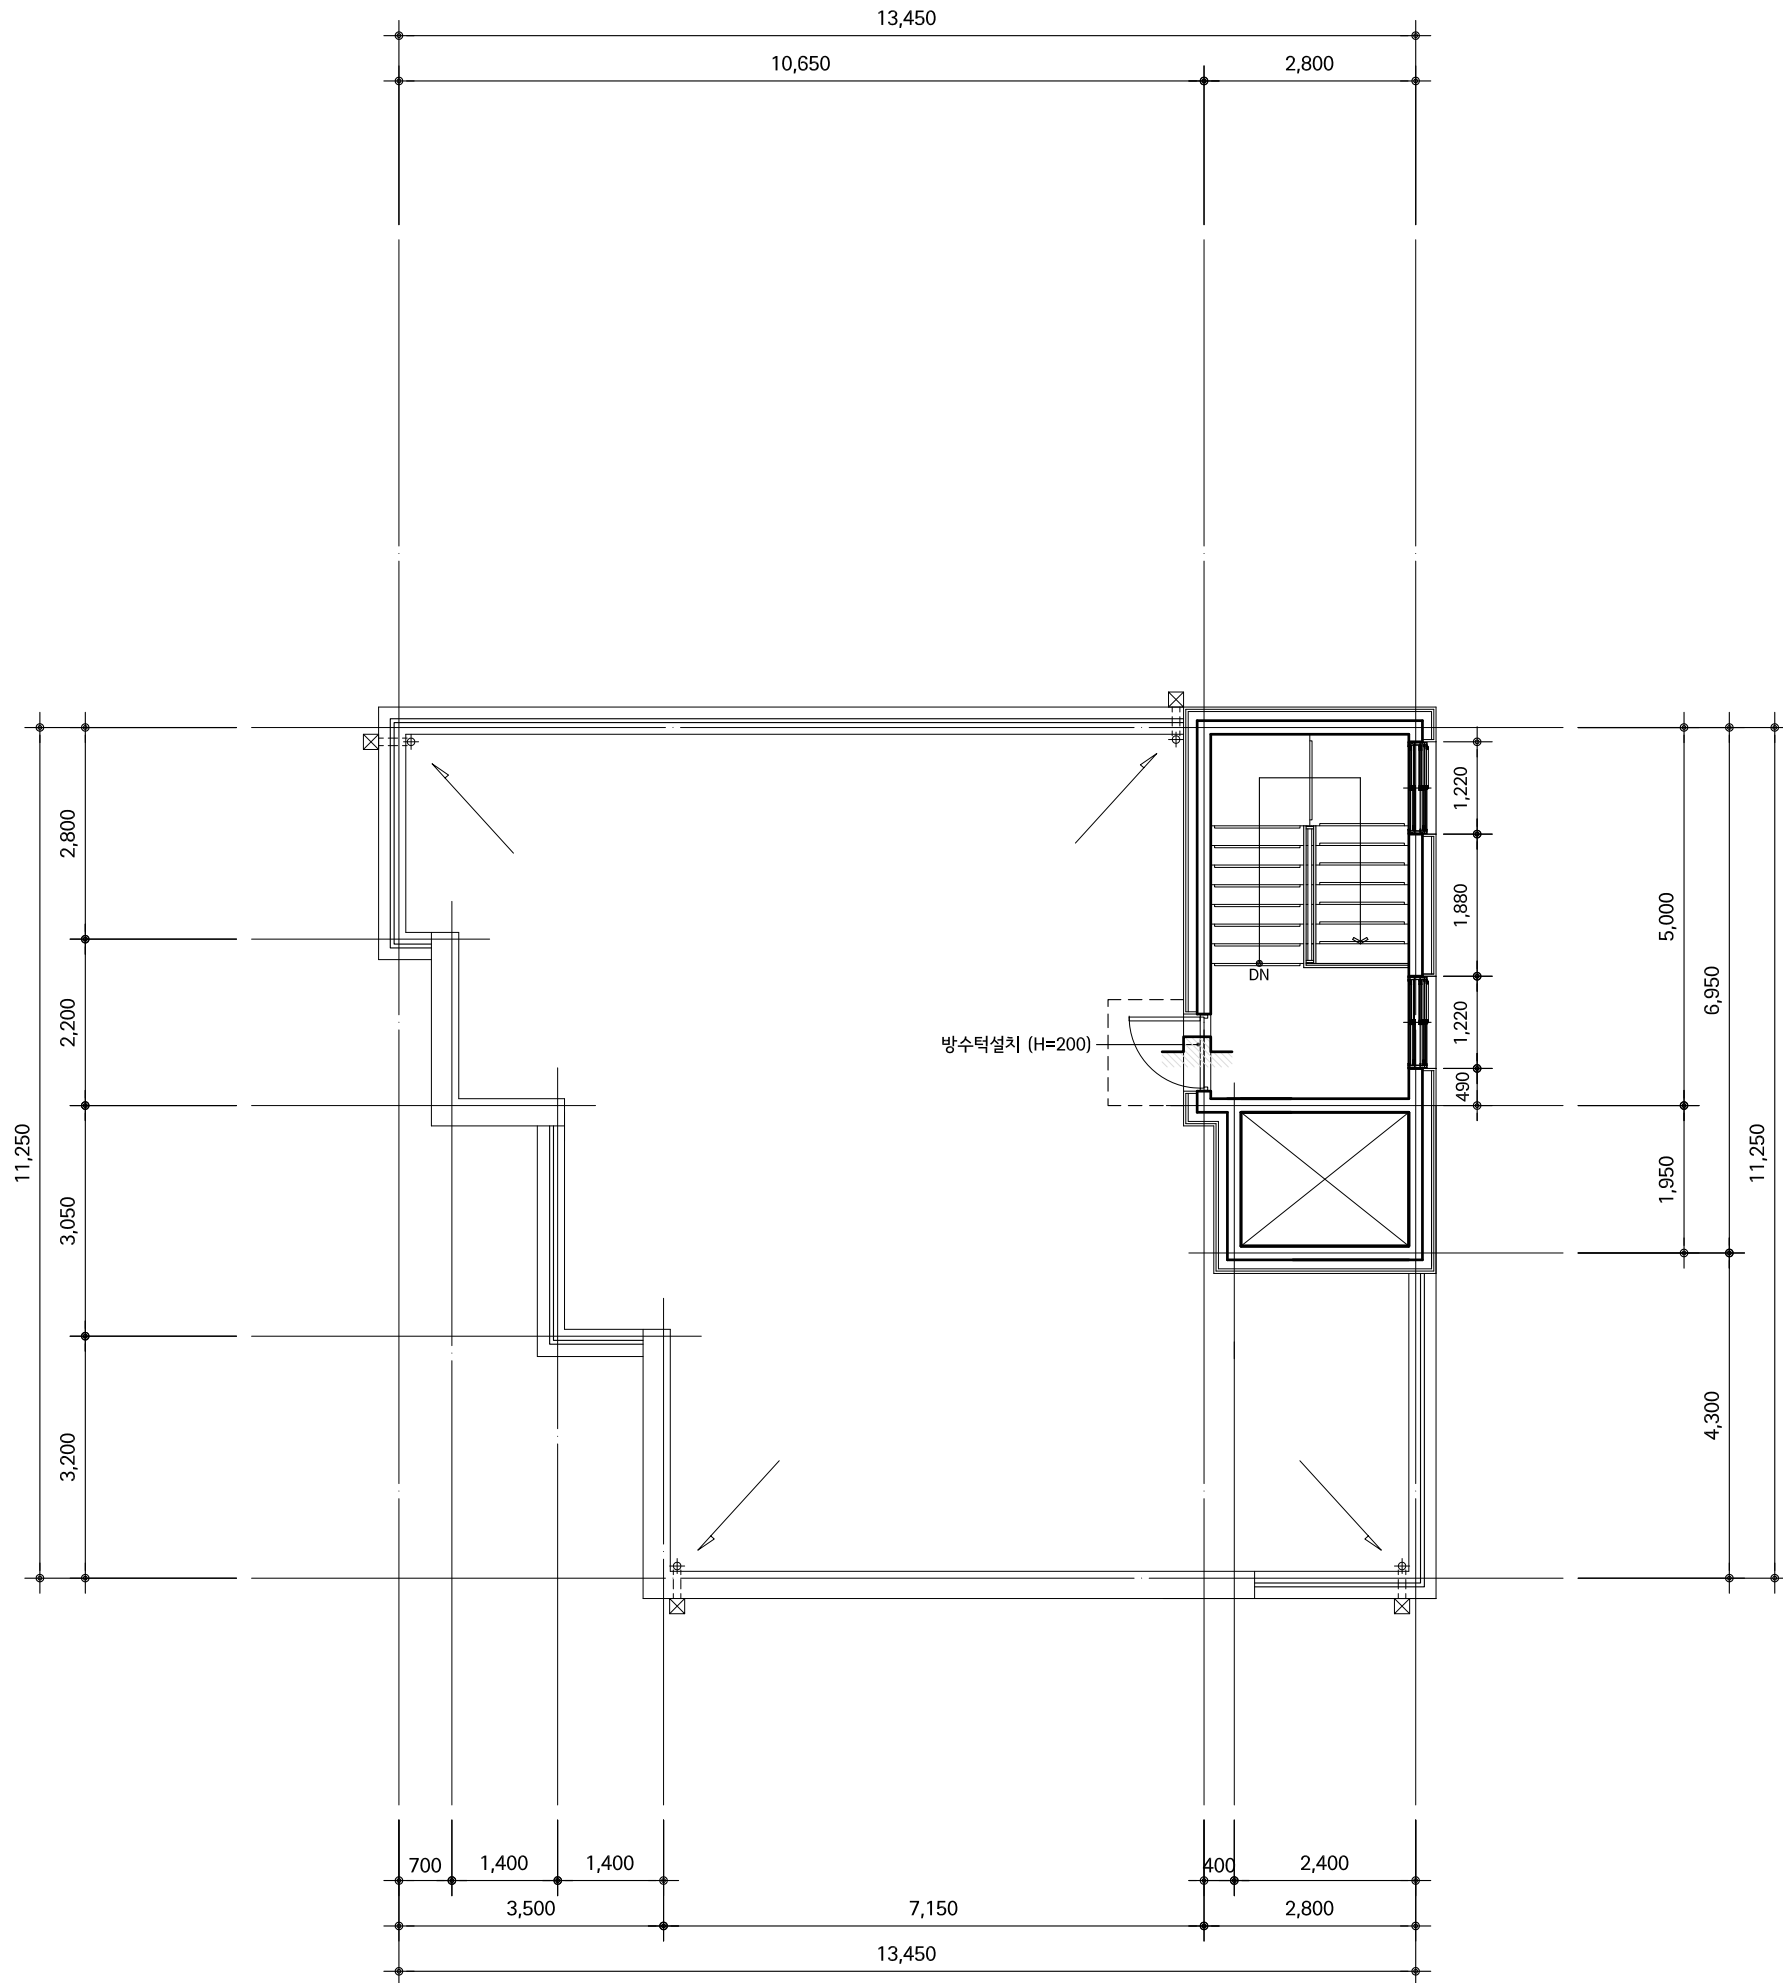


지붕층 및 옥탑지붕층 평면도

SCALE = 1/100


사업명칭 PROJECT TITLE	
구로구 개봉동 307-13 도시형생활주택(소형주택) 신축공사 -청년주택-	
사업번호 PROJECT NO.	
변경사항 ISSUER & REVISIONS	
△	
△	
△	
△	
△	
 Architects & Interiors 인천광역시 연수구 남동로55번길 6-12 T_032,464,8775 F_032,881,9102	
제 도 DRAWN BY	
설 계 DESIGNED BY	
심 사 CHECKED BY	
승 인 APPROVED BY	건축사 이선영
추가사항 NOTE	
현동설계 CONSULTANTS	
일 자 DATE	
도면번호 DRAWING NO.	
A - 105	
축 척 SCALE	
A3 : 1 / 100	
도면명 NAME OF DRAWING	
지붕층 및 옥탑지붕층 평면도	



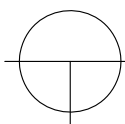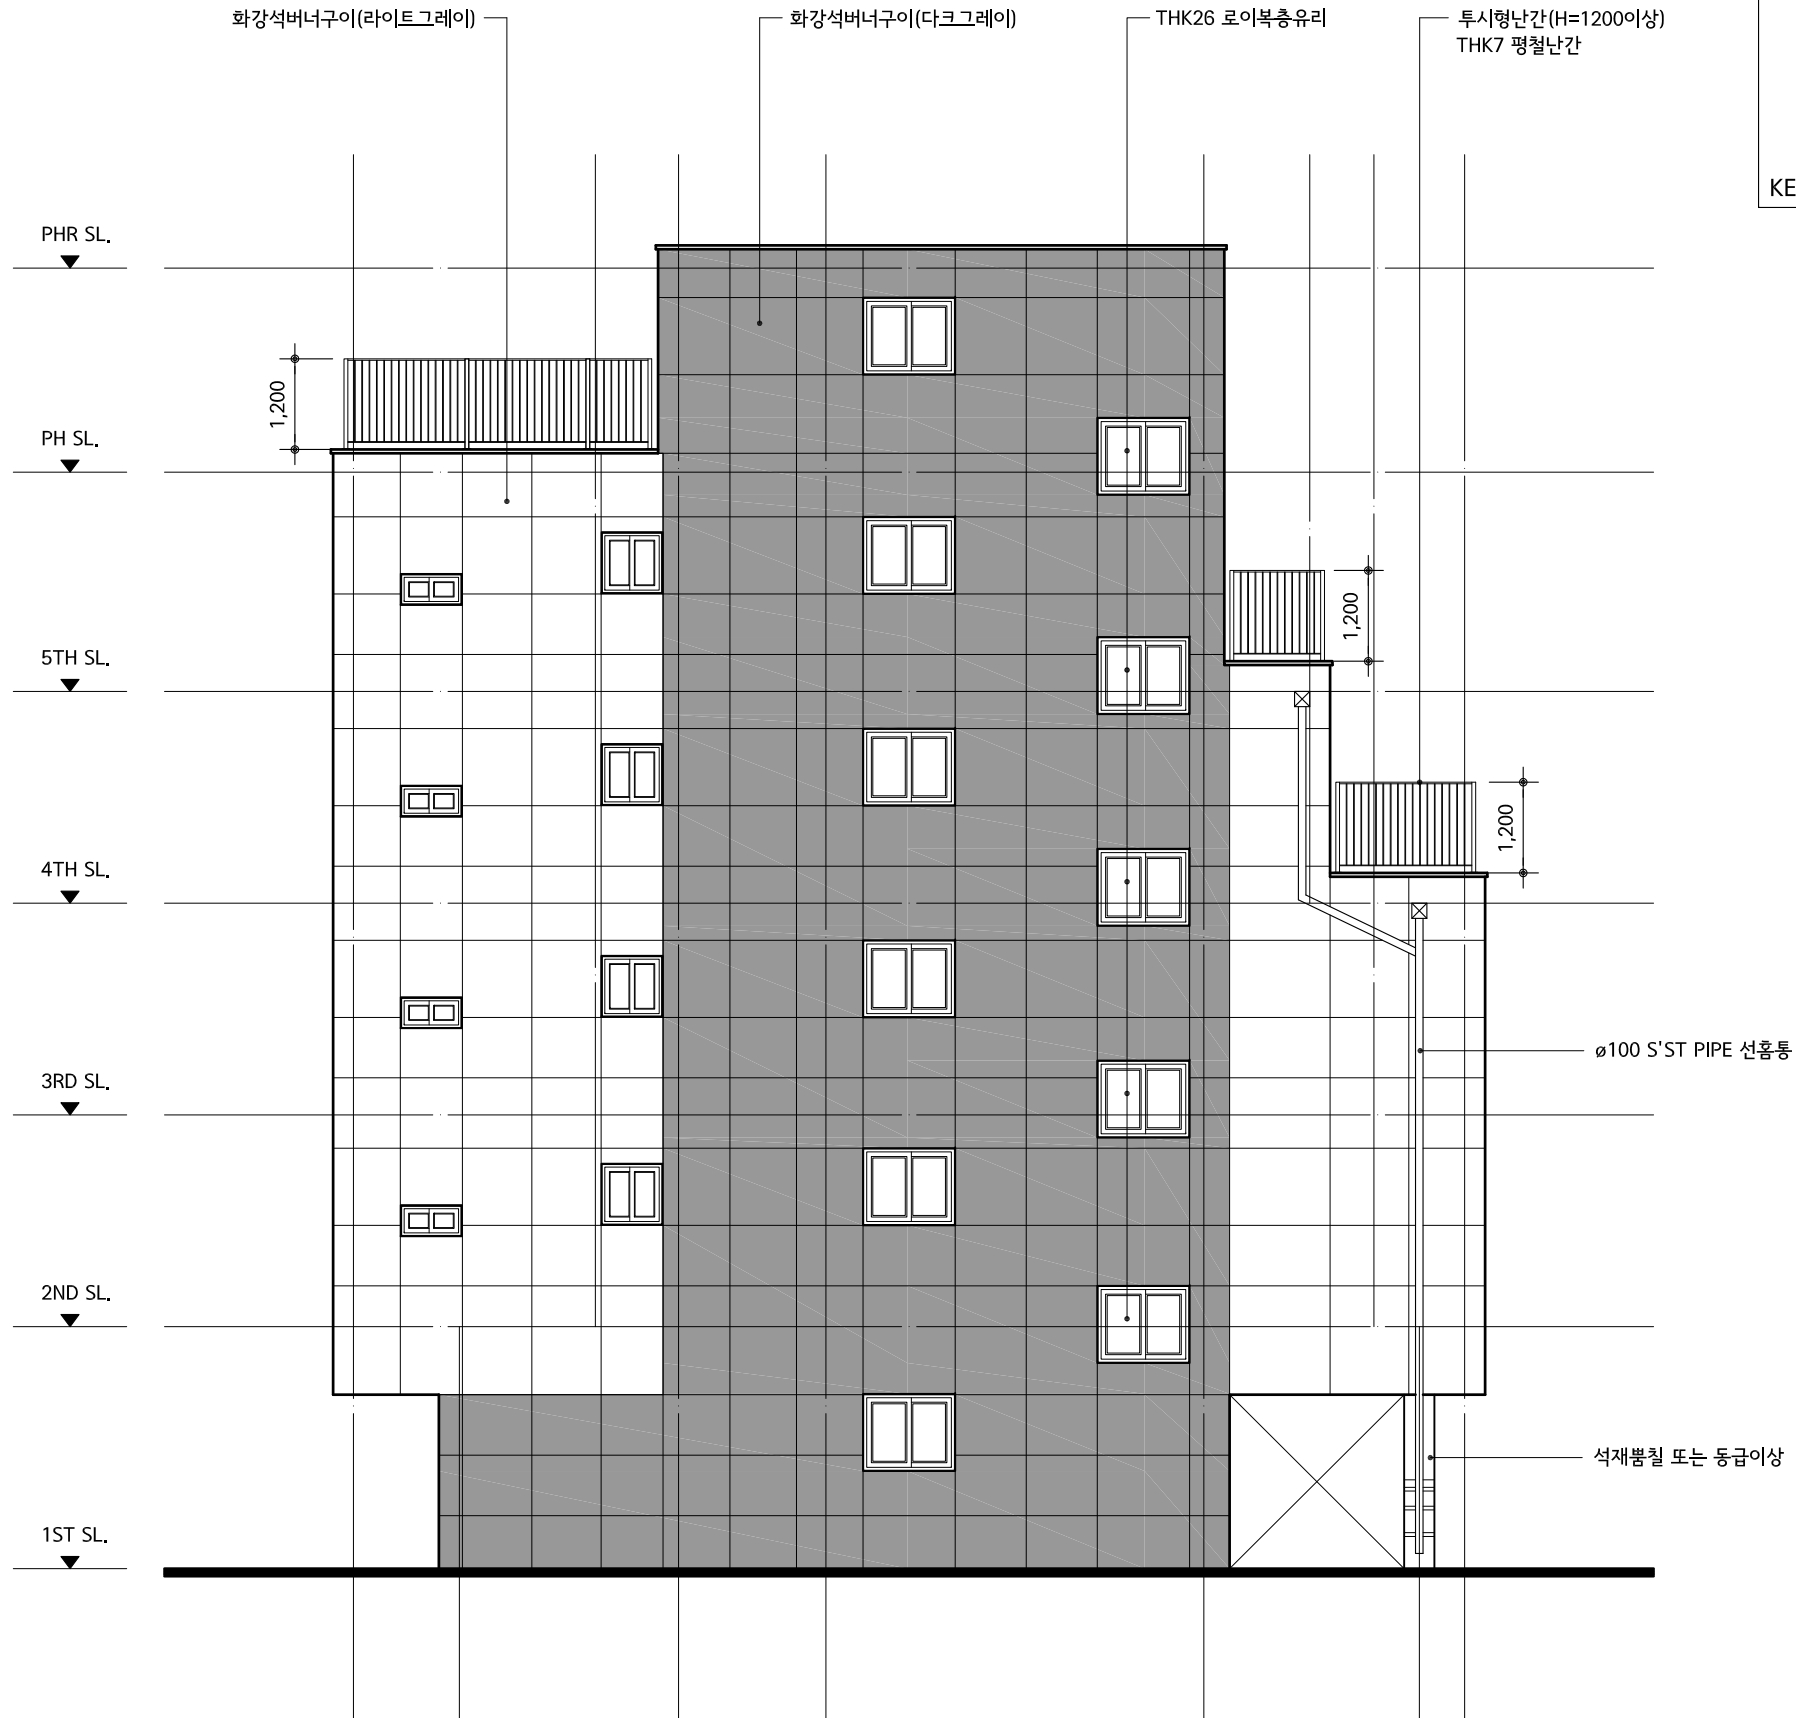

동 측 면 도

SCALE = 1/100

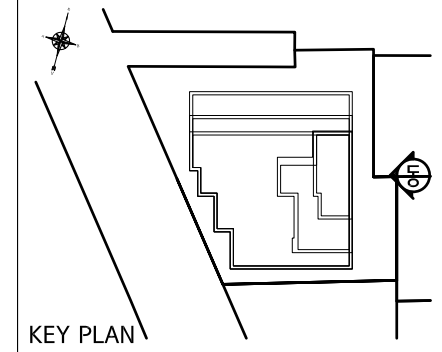

사업명칭
PROJECT TITLE

구로구 개봉동 307-13
도시형생활주택(소형주택)
신축공사 -청년주택-

사업번호
PROJECT NO.

변경사항
ISSUER & REVISIONS



제 도
DRAWN BY

설 계
DESIGNED BY

심 사
CHECKED BY

승 인
APPROVED BY

건축사 이선영

추가사항
NOTE

현동설계
CONSULTANTS

일 자
DATE

도면번호
DRAWING NO.


A - 107

축 척
SCALE

A3 : 1 / 100

도면명
NAME OF DRAWING

동측면도

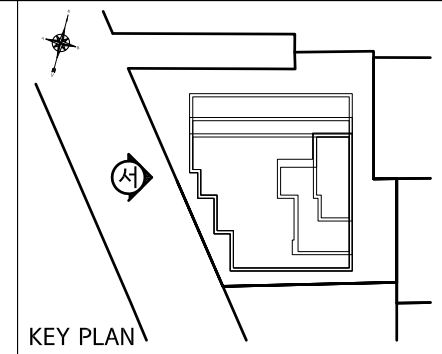

사업명칭
PROJECT TITLE

구로구 개봉동 307-13
도시형생활주택(소형주택)
신축공사 -청년주택-

사업번호
PROJECT NO.

변경사항
ISSUER & REVISIONS

△	
△	
△	
△	
△	



제 도
DRAWN BY

설 계
DESIGNED BY

심 사
CHECKED BY

승 인
APPROVED BY

건축사 이선영

추가사항
NOTE

현동설계
CONSULTANTS

일 자
DATE

도면번호
DRAWING NO.

A - 108

축 척
SCALE

A3 : 1 / 100

도면명
NAME OF DRAWING

서측면도