



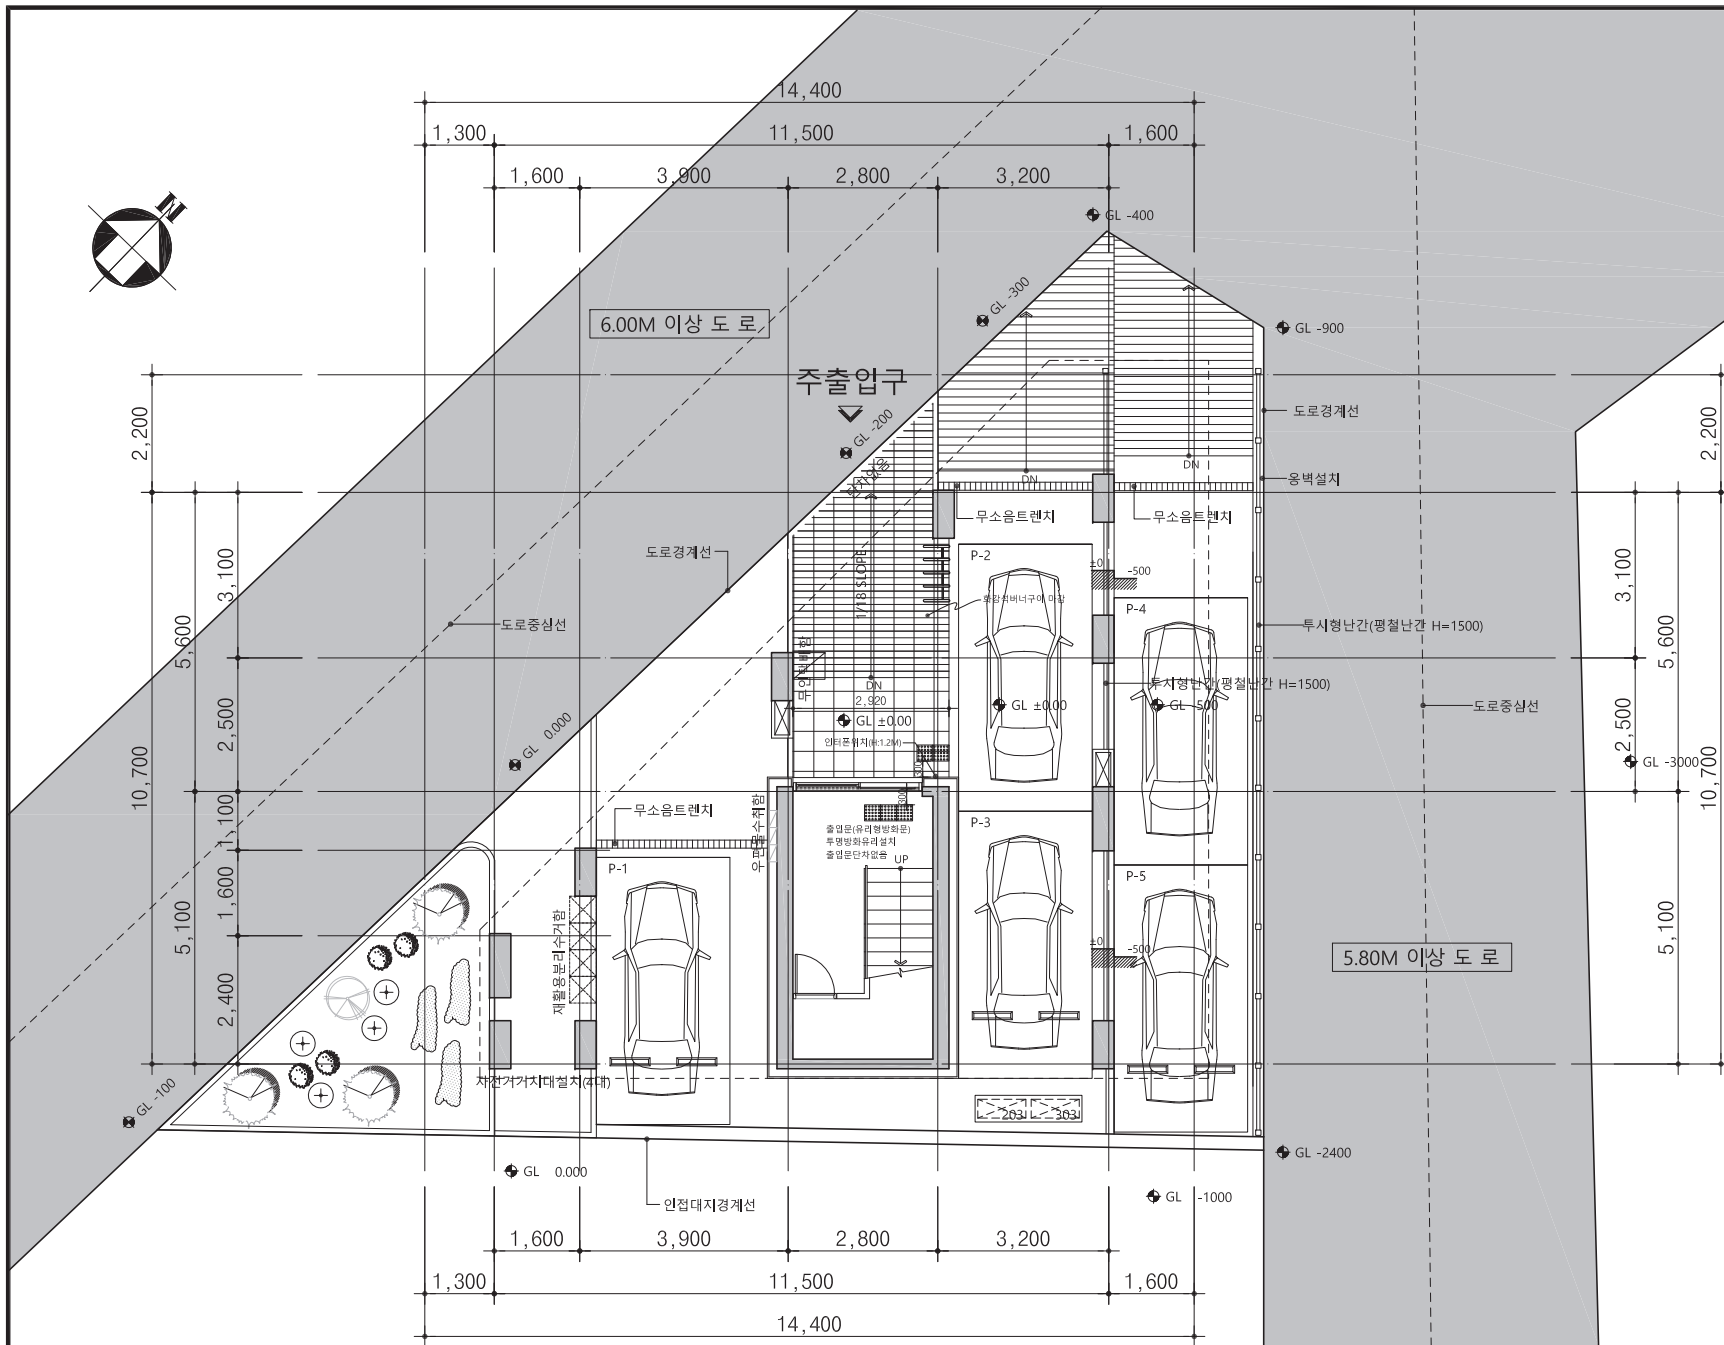


1. 접근로의 유효폭 1.2미터 이상확보
2. 접근로의 기울기는 1/18 이하로설치
3. 대지 내를 연결하는 주접근로에 단차가 있을경우 그 높이는 2cm 이하가 되도록 설치
4. 접근로는 차도와 색상과 재질을 달리하여 반드시 보차분리를 명확히 해주어야함
5. 접근로의 바닥표면은 잘미끄러지지 않는 재질로 평탄하게 마감하여야함
6. 블록 등으로 접근로를 포장하는 경우에는 이음새의 틈이 벌어지지 아니하도록 하여 면이 평탄하게 시공하여야함
7. 덩개를 설치할 경우 덩개에 격자구멍 또는 틈새의 양방향 간격이 2cm 이하가 되도록 설치
8. 점형블록은 매립형으로 설치함 (황색K.소재품)

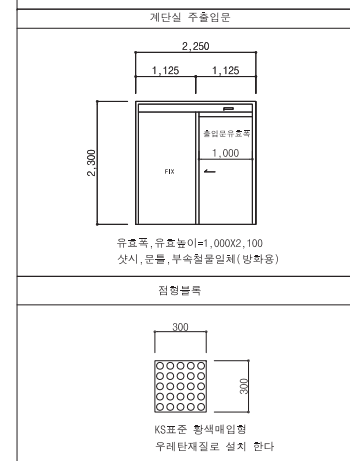

NOTE:

PROJECT	구로구 오류동 81-117번지 도시형생활주택 (원룸형) 철근콘크리트구조
APPROVED BY	건축사 구 연 욱
	건축사사무소 유일엔지니어링 서울특별시 서초구 반포대로 14길71(서초동) (5층)에클리어빌딩 1904호 TEL : 02) 540-1549, FAX : 02) 540-1576
TITLE	1층 평면도
날짜 DATE:	2022. 07. .
SCALE	1/100
DWG NO.	A - 008
REV.	

1 층 평 면 도
축척: 1/ 100

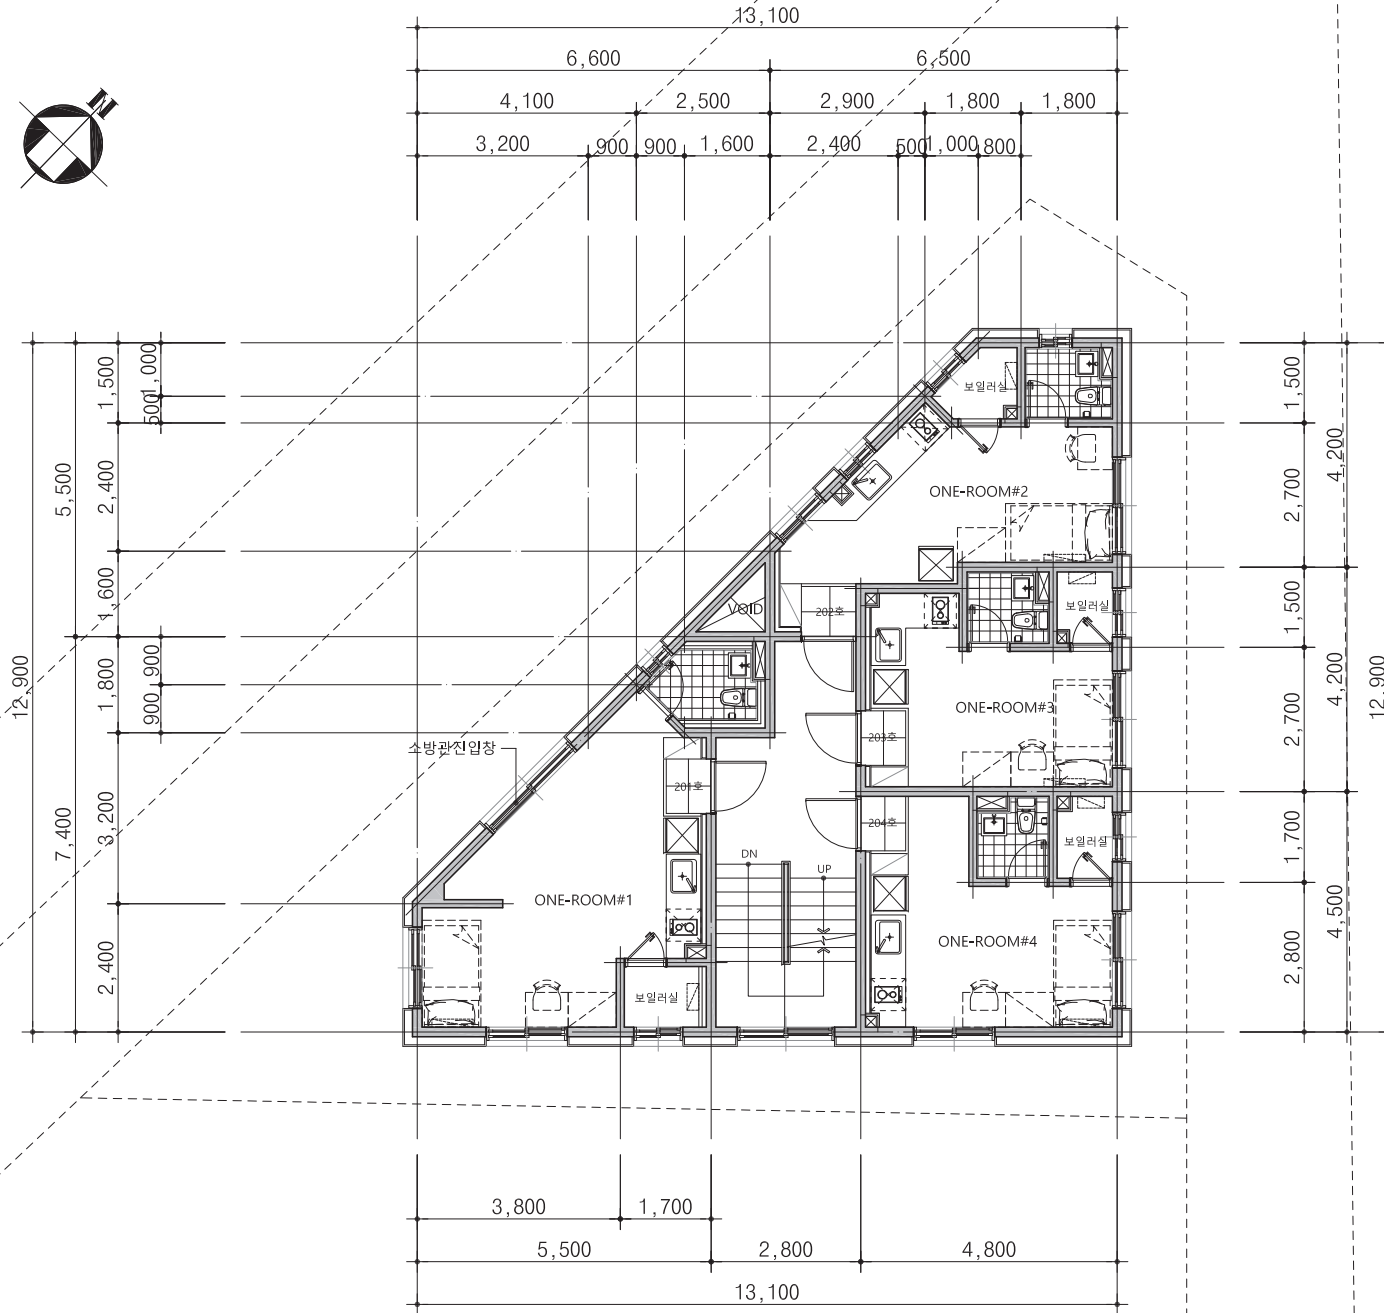

2층 평면도

축척: 1/ 100


주 기

1	세대 환관문 도어체크 및 스토퍼 계획	
2	세대 발코니 설치시 세대간 분리벽 계획	
3	세대내 비디오폰 설치	
4	주차장내 CCTV 설치	
5	벽체	직접 외기에 면한 실내벽면은 단열재 (아이소핑크10mm+석고보드 마감도면 표기) 계단실 간접 외기에 면한 실내벽면은 단열재 /복도 (경질우레탄80mm+석고보드 마감도면 표기)
6	에어콘 실외기 설치위치 및 에어콘 도면표기)	
7	불박이 가구 내부 다중도 수납기능토록 수평이동 칸막이 설치	
8	콘크리트 플러터 제거후 마감공사 시공(발수 및 단열재 시공등)	
9	구조	콘크리트 : fck=24Mpa 철근 : fy=400Mpa 세대 벽두께 : 150mm(복배근) 외벽 벽두께 : 180mm(복배근) 코아 벽두께 : 180mm(복배근) 2층 스라브 두께 : 180mm(복배근) 3-5층 스라브 두께 : 210mm(복배근)
10	기타 실내 벽면은 시멘트 미장마감	
11	욕실 & 다중도실 스위치 : 문열리는 방향으로 시공	
12	공동주택 바닥충격음 차단구조기준	
13	소방관 진입창의 기준	

NOTE:

PROJECT	구로구 오류동 81-117번지 도시형생활주택 (원룸형) 창고형주택
APPROVED BY	건축사 구 연 욱
	건축사사무소 유일엔지니어링 서울특별시 서초구 반포대로 14길71(서초동) (5층)에래빌리티 1904호 TEL : 02) 540-1546, FAX : 02) 540-1576

TITLE	2층 평면도
날짜 DATE:	2022. 07. .
SCALE	1/100
DWG NO.	A - 009
REV.	

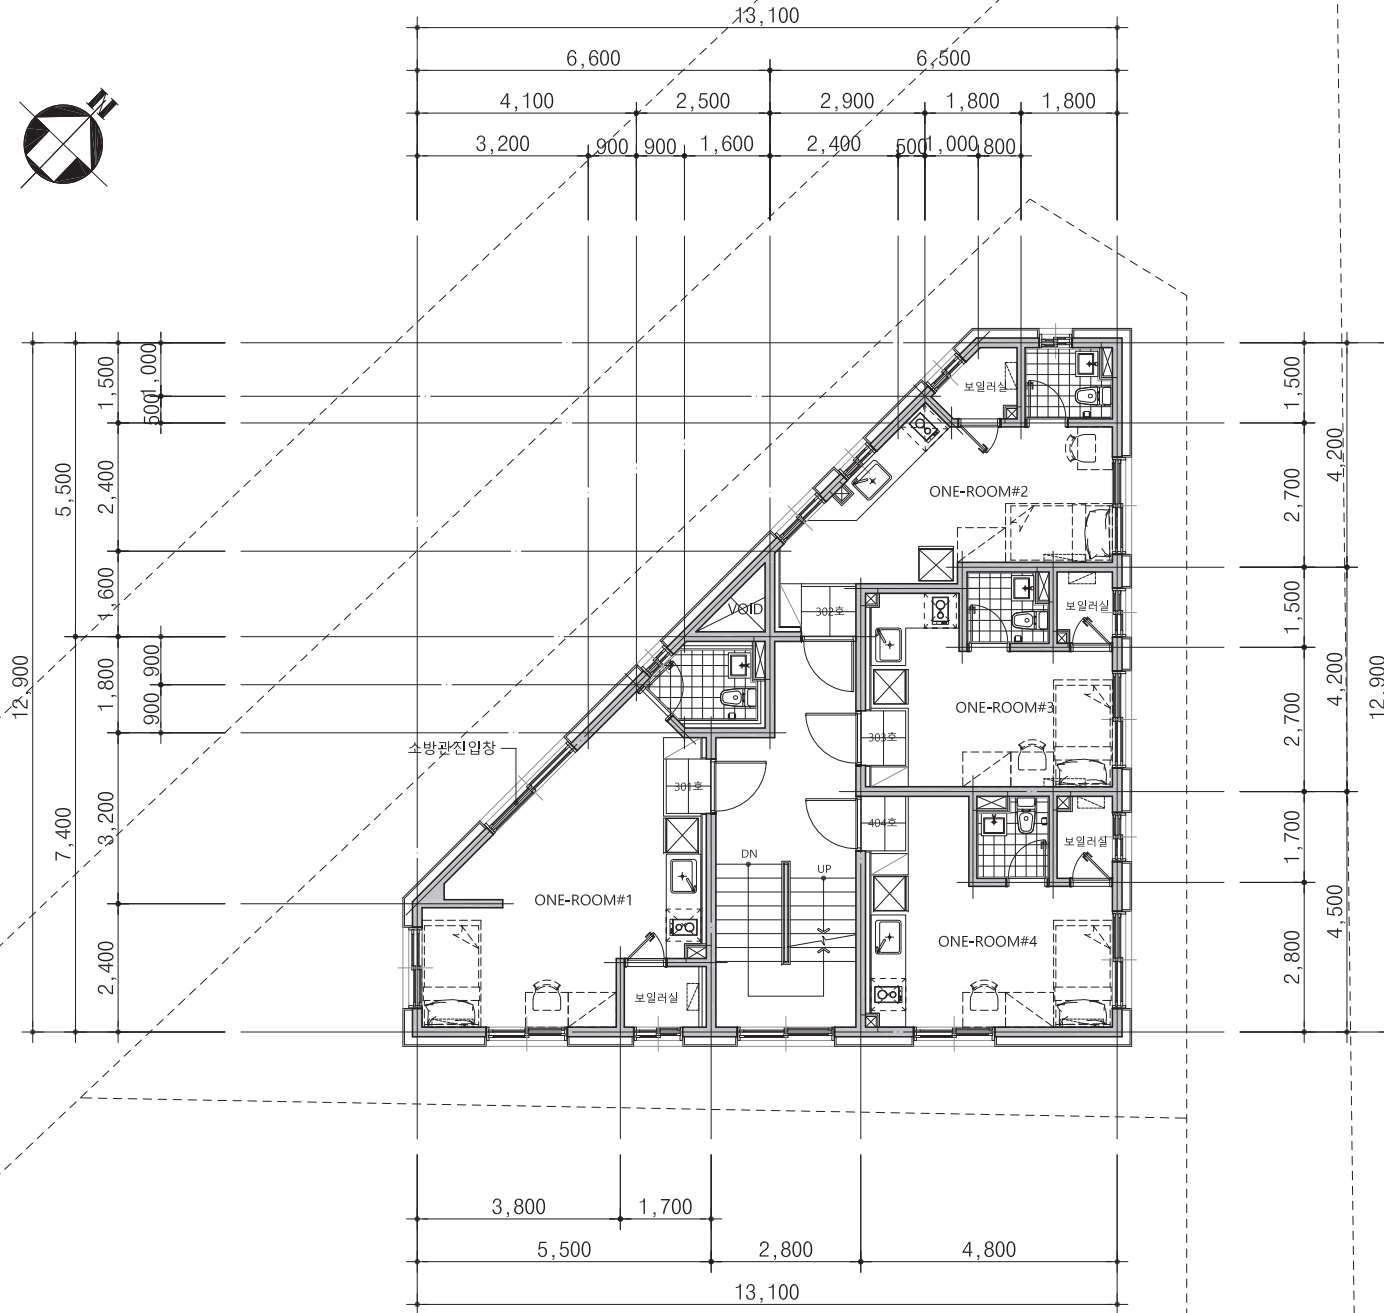


3층 평면도

축척: 1/ 100

주 기

1	세대 현관문 도어체크 및 스톱퍼 계획	
2	세대 발코니 설치시 세대간 분리벽 계획	
3	세대내 비디오존 설치	
4	주차장내 CCTV 설치	
5	벽체	직접 외기에 면한 실내벽면은 단열재 (아이소핑크10mm+석고보드 마감도면 표기) 계단실 간접 외기에 면한 실내벽면은 단열재 /복도 (경질우레탄80mm+석고보드 마감도면 표기)
6	에어콘 실외기 설치위치 및 에어콘 도면표기)	
7	불박이 가구 내부 다중도 수납가능토록 수평이동 칸막이 설치	
8	콘크리트 플러터 제거후 마감공사 시공(발수 및 단열재 시공등)	
9	구조	콘크리트 : fck=24Mpa 철근 : fy=100Mpa 세대 벽두께 : 150mm(복배근) 외벽 벽두께 : 180mm(복배근) 코아 벽두께 : 180mm(복배근) 2층 슬라브 두께 : 180mm(복배근) 3-5층 슬라브 두께 : 210mm(복배근)
10		기타 실내 벽면은 시멘트 미장마감
11		욕실 & 다중도실 스위치 : 문열리는 방향으로 시공
12		공동주택 바닥충격음 차단구조기준
13		소방관 진입창의 기준
14	외기에 간접면하는 부분은 THK80 경질우레탄폼 2중2호 설치	


3층 4층 5층	
----------------	--

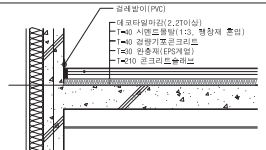

NOTE:

PROJECT : 구로구 오류동 81-117번지
도시형생활주택 (원룸형) 창고형주택
APPROVED BY : 건축사 구 연 욱
건축사사무소 유일엔지니어링
서울특별시 서초구 반포대로 14길71(서초동)
(5서초에름빌딩 1904호)
TEL : 02) 540-1546, FAX : 02) 540-1576


TITLE : 3층 평면도
날짜 : 2022. 07.
SCALE : 1/100
DWG NO. : A - 010
REV. :

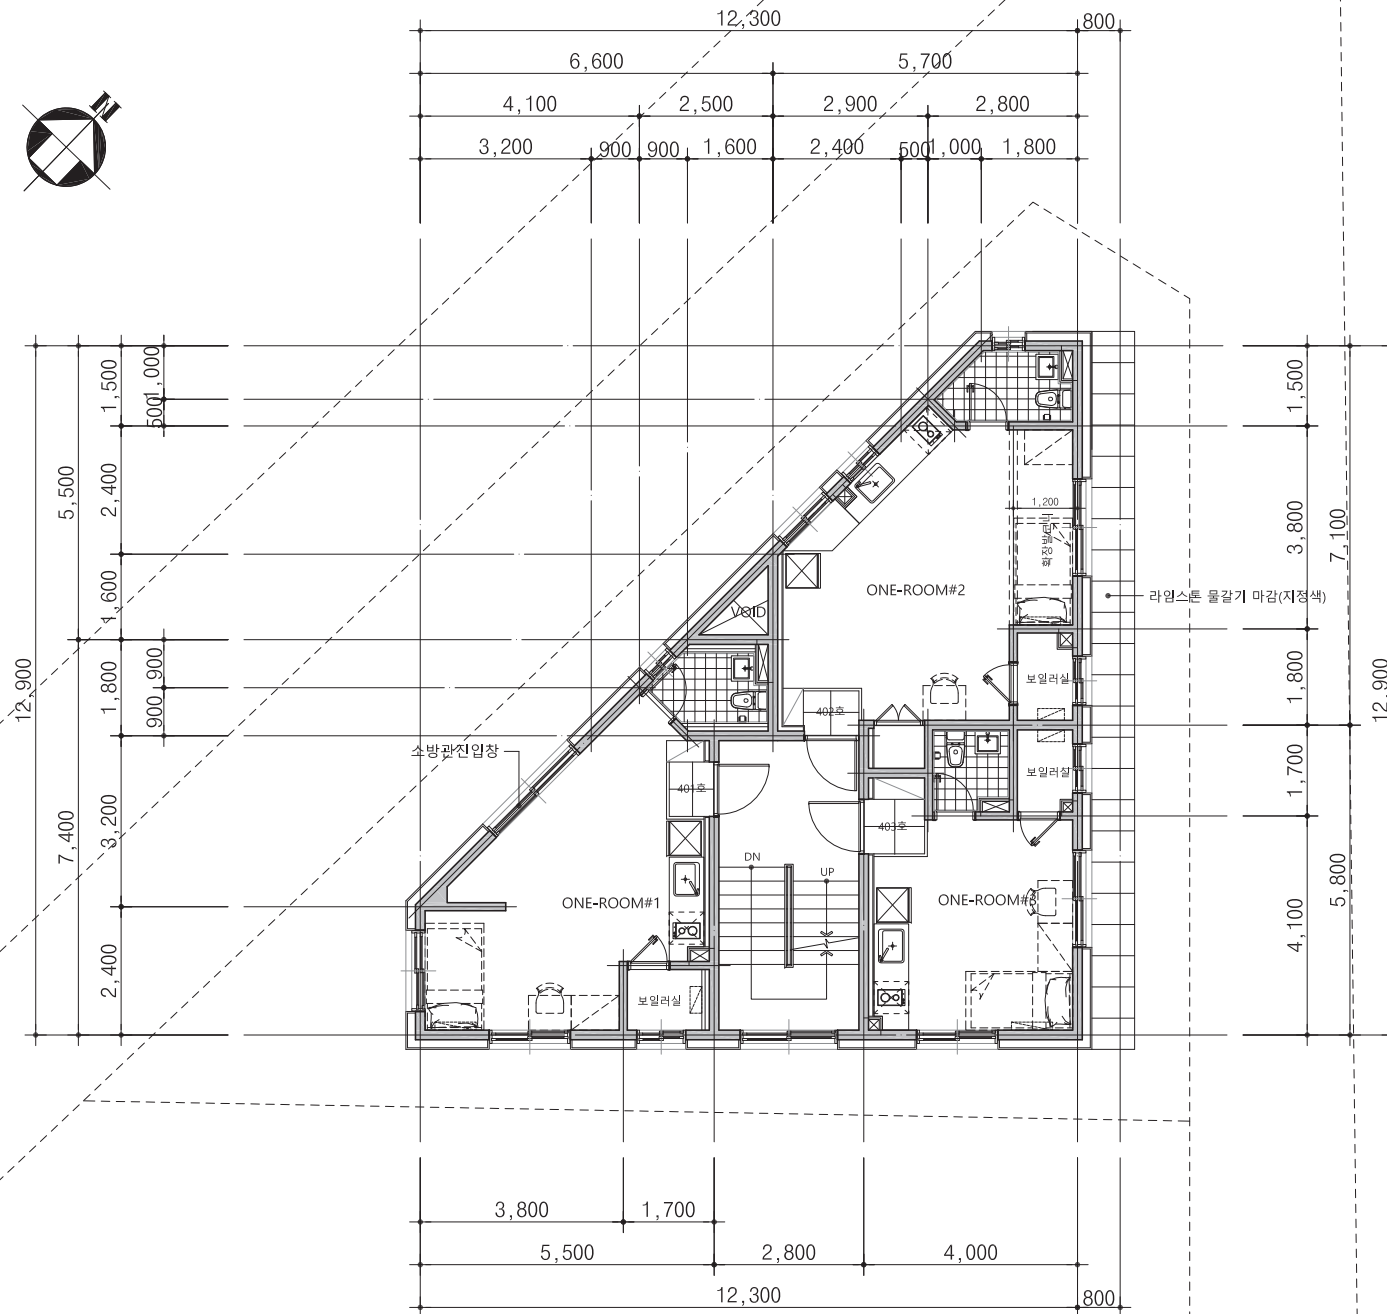

4층 평면도

축척: 1/ 100

주 기	
1	세대 현관문 도어체크 및 스톱퍼 계획
2	세대 발코니 설치시 세대간 분리벽 계획
3	세대내 비디오킷 설치
4	주차장내 CCTV 설치
5	벽체
외벽	직접 외기에 의한 실내벽면은 단열재 (아이소핑크10mm+석고보드 마감도면 표기)
계단실	간접 외기에 의한 실내벽면은 단열재 /복도 (경질우레탄80mm+석고보드 마감도면 표기)
6	에어콘 실외기 설치위치 및 에어컨 도면표기)
7	불박이 가구 내부 다중도 수납가능토록 수평이동 칸막이 설치
8	콘크리트 플러터 제거후 마감공사 시공(발수 및 단열재 시공등)
9	구조
콘크리트	: fck=24Mpa
철근	: fy=100Mpa
세대 벽두께	: 150mm(복배근)
외벽 벽두께	: 180mm(복배근)
코아 벽두께	: 180mm(복배근)
2층 슬라브 두께	: 180mm(복배근)
3-5층 슬라브 두께	: 210mm(복배근)
10	기타 실내 벽면은 시멘트 미장마감
11	욕실 & 다중도실 스위치: 문열리는 방향으로 시공
12	공동주택 바닥충격음 차단구조기준
3층	4층
5층	
13	소방관 진입창의 기준
건축물의 피난방화구조등의 기준에 관한규칙 제18조의2에 의거	
1. 2층이상 11층이하인 층에 각각 1개소 이상설치	
2. 소방차진입로또는 소방차 진입이 가능한 공터에 연결것	
3. 창문 가구에 Ø200이상의 역삼각형을 아간에 식별가능하도록 설치. (반사 등으로 붉은색으로 표시)	
4. 창문 한쪽 모서리에 타격지점 표시 (Ø30 이상의 원형)	
5. 창문크기 : 폭900 높이1,200이상 (바닥에서 찾아챌부분 높이800이내로 설치)	
6. 다음 각 목의 어느 하나에 해당하는 유리 사용할 것 가. 플로트판유리로서 두께6mm이하인것 나. 강화유리/배강도유리로서 두께5mm이하인것 다. 위의 유리로 구성된 이중유리로서 두께24mm 이하인것	
14	외기에 간접연하는 부분은 : THK80 경질우레탄폼 2중2층 설치
석고보드위벽지마감	
T80경질폴리우레탄단열재2중2층	
T180철콘크리트벽	
호 실	
계 단 실	
호 실	
석고보드위벽지마감	
T80경질폴리우레탄단열재2중2층	
T180철콘크리트벽	
NOTE:	
PROJECT	
구로구 오류동 81-117번지 도시형생활주택 (원룸형) 청진구(주) (건축사)	
APPROVED BY	
건축사 구 연 욱	
건축사사무소 유일엔지니어링	
서울특별시 서초구 반포대로 14길71(서초동) (5층지하1층) 1904호	
TEL : 02) 540-1546, FAX : 02) 540-1576	
TITLE	
4층 평면도	
날짜	
DATE: 2022. 07. .	
SCALE	1/100
DWG NO.	A - 011
REV.	

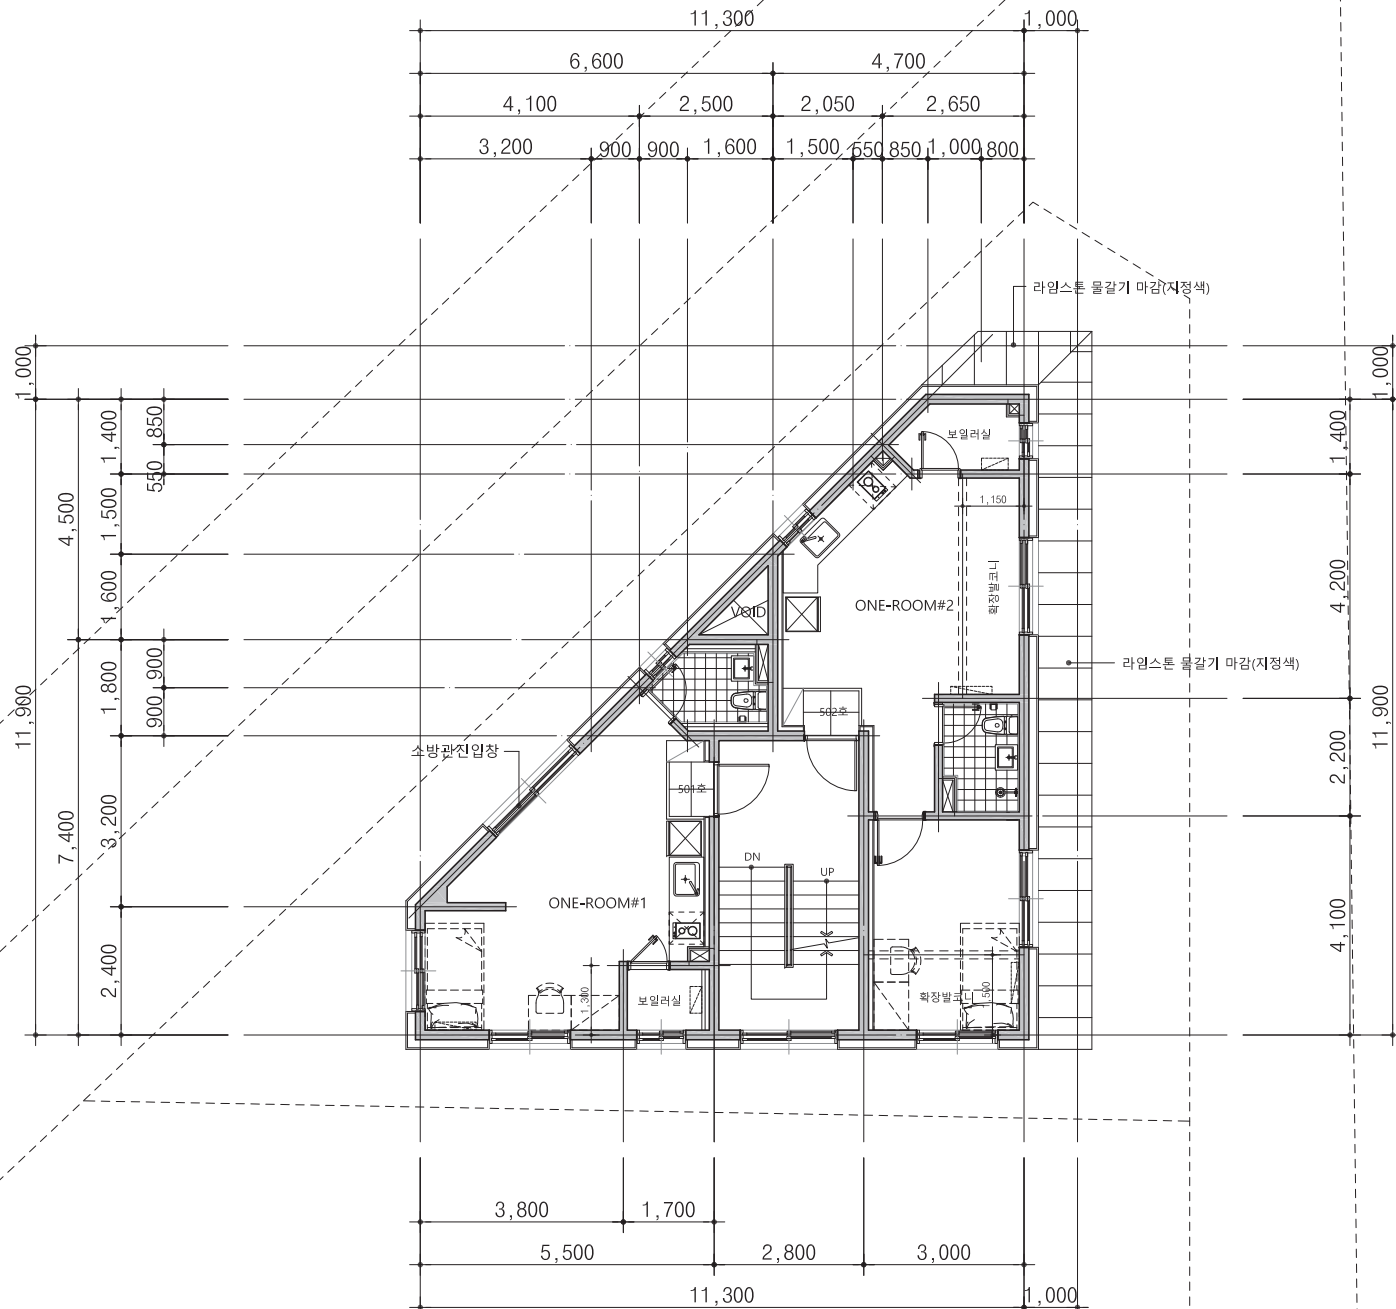

5층 평면도

축척: 1/ 100

주 기

1	세대 현관문 도어체크 및 스토퍼 계획
2	세대 발코니 설치시 세대간 분리벽 계획
3	세대내 비디오폰 설치
4	주차장내 CCTV 설치
5	벽체
외벽	직접 외기에 의한 실내벽면은 단열재 (아이소핑크10mm+석고보드 마감도면 표기)
계단실	간접 외기에 의한 실내벽면은 단열재 /복도 (경질우레탄80mm+석고보드 마감도면 표기)
6	에어콘 실외기 설치위치 및 에어콘 도면표기)
7	불박이 가구 내부 다용도 수납가능토록 수평이동 칸막이 설치
8	콘크리트 플러터 제거후 마감공사 시공(발수 및 단열재 시공등)
9	구조
콘크리트	: fck=24Mpa
철근	: fy=100Mpa
세대 벽두께	: 150mm(복배근)
외벽 벽두께	: 180mm(복배근)
코아 벽두께	: 180mm(복배근)
2층 슬라브 두께	: 180mm(복배근)
3-5층 슬라브 두께	: 210mm(복배근)
10	기타 실내 벽면은 시멘트 미장마감
11	욕실 & 다용도실 스위치: 문열리는 방향으로 시공
12	공동주택 바닥충격음 차단구조기준
3층	교체방이(PVC)
4층	대포타일마감(2,21이상)
5층	100 시멘트도배(1.5, 2.0, 3.0, 4.0,99.0, 100.0)
13	소방관 전입창의 기준
건축물의 피난방화구조등의 기준에 관한규칙 제18조의2에 의거	
1. 2층이상 11층이하인 층에 각각 1개소 이상설치	
2. 소방차전입로또는 소방차 전입이 가능한 공터에 면할것	
3. 창문 가운데 Ø200이상의 역삼각형을 아간에 식별가능하도록 설치. (반사 등으로 붉은색으로 표시)	
4. 창문 한쪽 모서리에 타격지점 표시 (Ø30 이상의 원형)	
5. 창문크기: 폭900 높이1,200이상 (바닥에서 창아랫부분 높이800이내로 설치)	
6. 다음 각 목의 어느 하나에 해당하는 유리 사용할 것 가. 플로트판유리로서 두께6mm이하인것 나. 강화유리/배강도유리로서 두께5mm이하인것 다. 위의 유리로 구성된 이중유리로서 두께24mm 이하인것	
14	외기에 간접면하는 부분: THK80 경질우레탄폼 2중2호 설치
석고보드위벽지마감	
T80경질폴리우레탄폼단열재2중2호	
T180절콘크리트벽	
호 실	
계 단 실	
호 실	
석고보드위벽지마감	
T80경질폴리우레탄폼단열재2중2호	
T180절콘크리트벽	

NOTE:

PROJECT

구로구 오류동 81-117번지
도시형생활주택 (원룸형) 청담구로역(신도림)역

APPROVED BY

건축사 구 연 욱



건축사사무소 유일엔지니어링

서울특별시 서초구 반포대로 14길71(서초동)

(5층)에 설립(1994년)

TEL : 02) 540-1546, FAX : 02) 540-1576

TITLE

5층 평면도

날짜

DATE: 2022. 07. .


SCALE

1/100

DWG NO.

A - 012

REV.

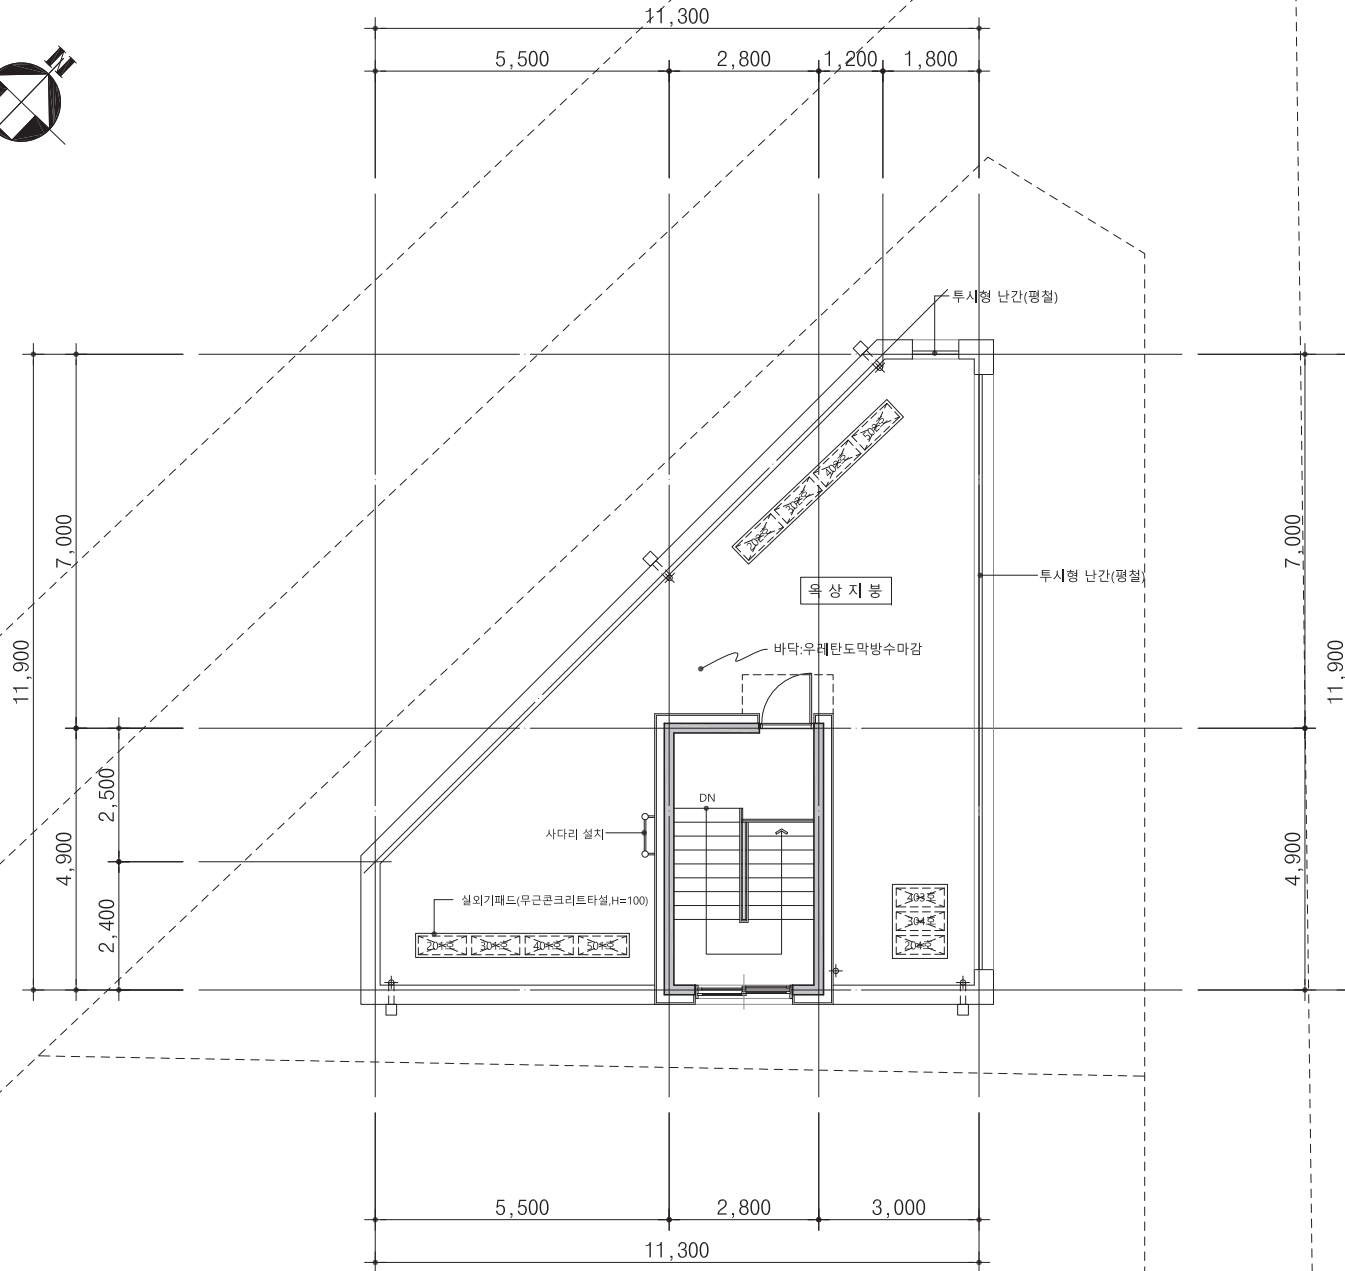


1
A 00

옥탑층 평면도

축척: 1/100

NOTE:

PROJECT	구로구 오류동 81-117번지 도시형생활주택 (원룸형) 창고형주택공급사업		
APPROVED BY	건축사 구연복		
			
	건축사무소 유일엔지니어링 서울특별시 서초구 반포대로 14길 71 (서초동) (8서초에듀빌딩 1904호) TEL : 02) 540-1546, FAX : 02) 540-1576		
TITLE	옥탑층 평면도		
날짜 DATE	2022. 07. .		
SCALE	1/100	DWG NO.	A - 013
			REV.

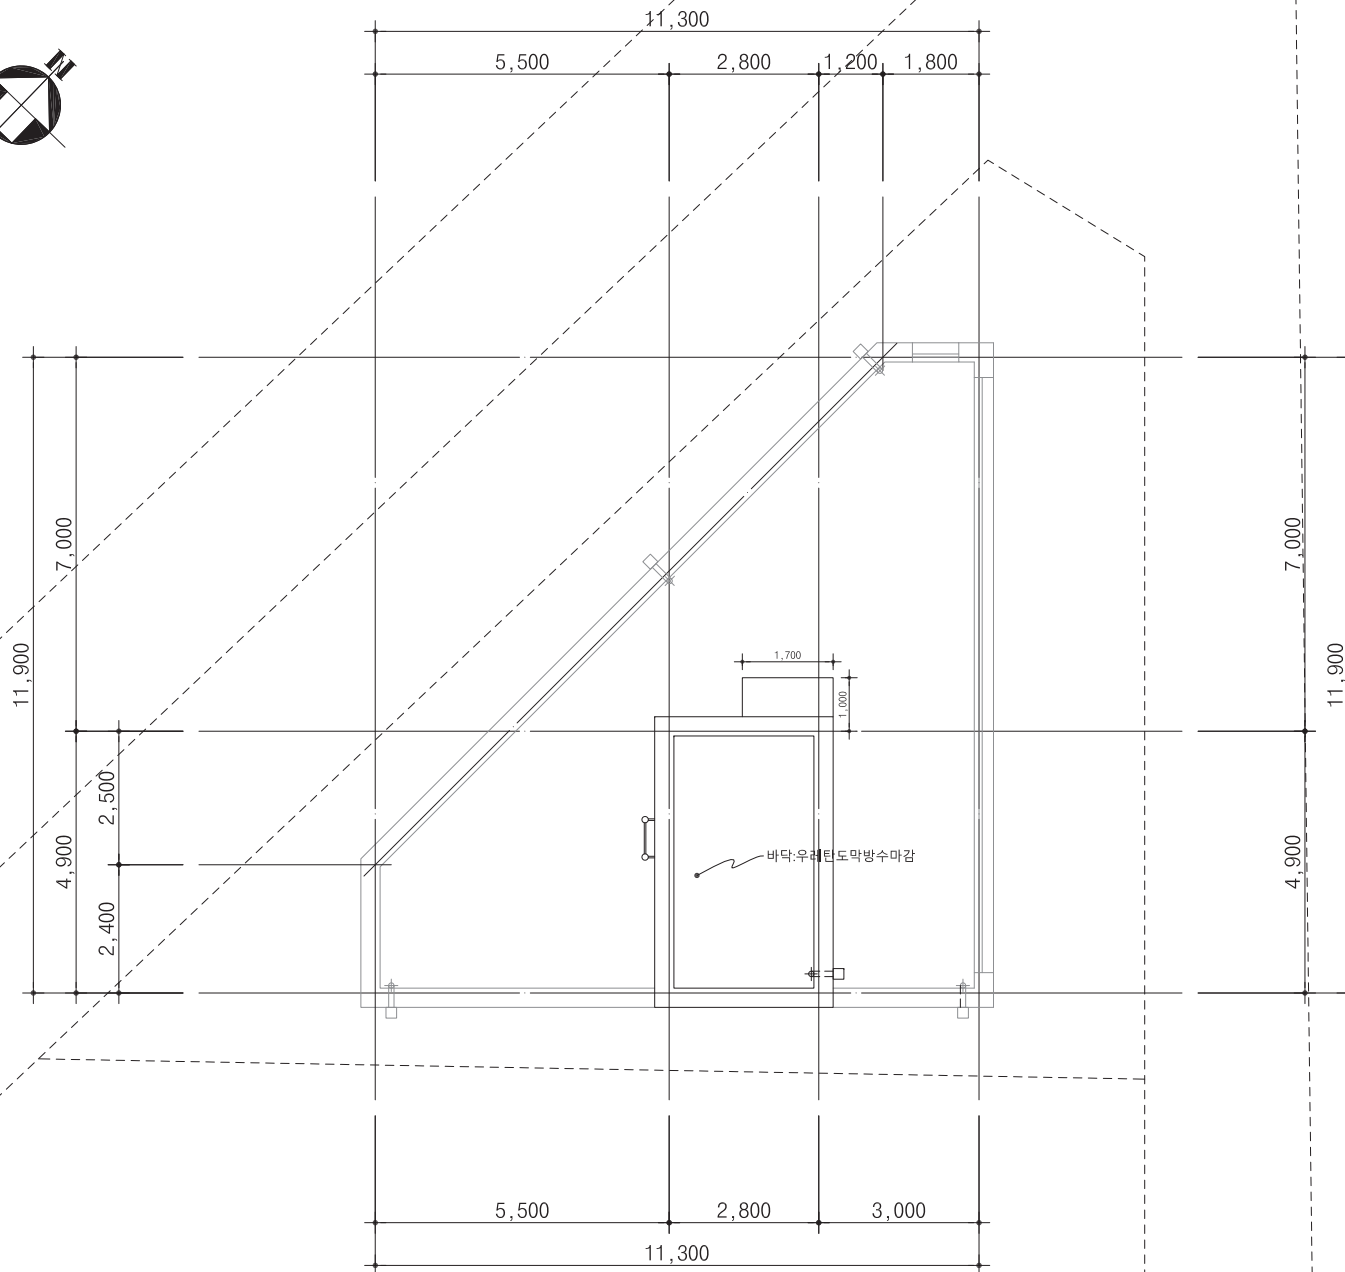


옥탑지붕 평면도

축척: 1/ 100

NOTE:


PROJECT		구로구 오류동 81-117번지 도시형생활주택 (원룸형) 창고형주택(공동주택)	
APPROVED BY		건축사 구연복	
ARCHITECT & ENGINEER		건축사사무소 유일엔지니어링 서울특별시 서초구 반포대로 14길 71 (서초동) (8서초에 글라피드 1904호) TEL : 02) 540-1540, FAX : 02) 540-1576	
TITLE		옥탑지붕 평면도	
날짜 DATE:		2022. 07. .	
SCALE	1/100	DWG NO.	A - 014
		REV.	

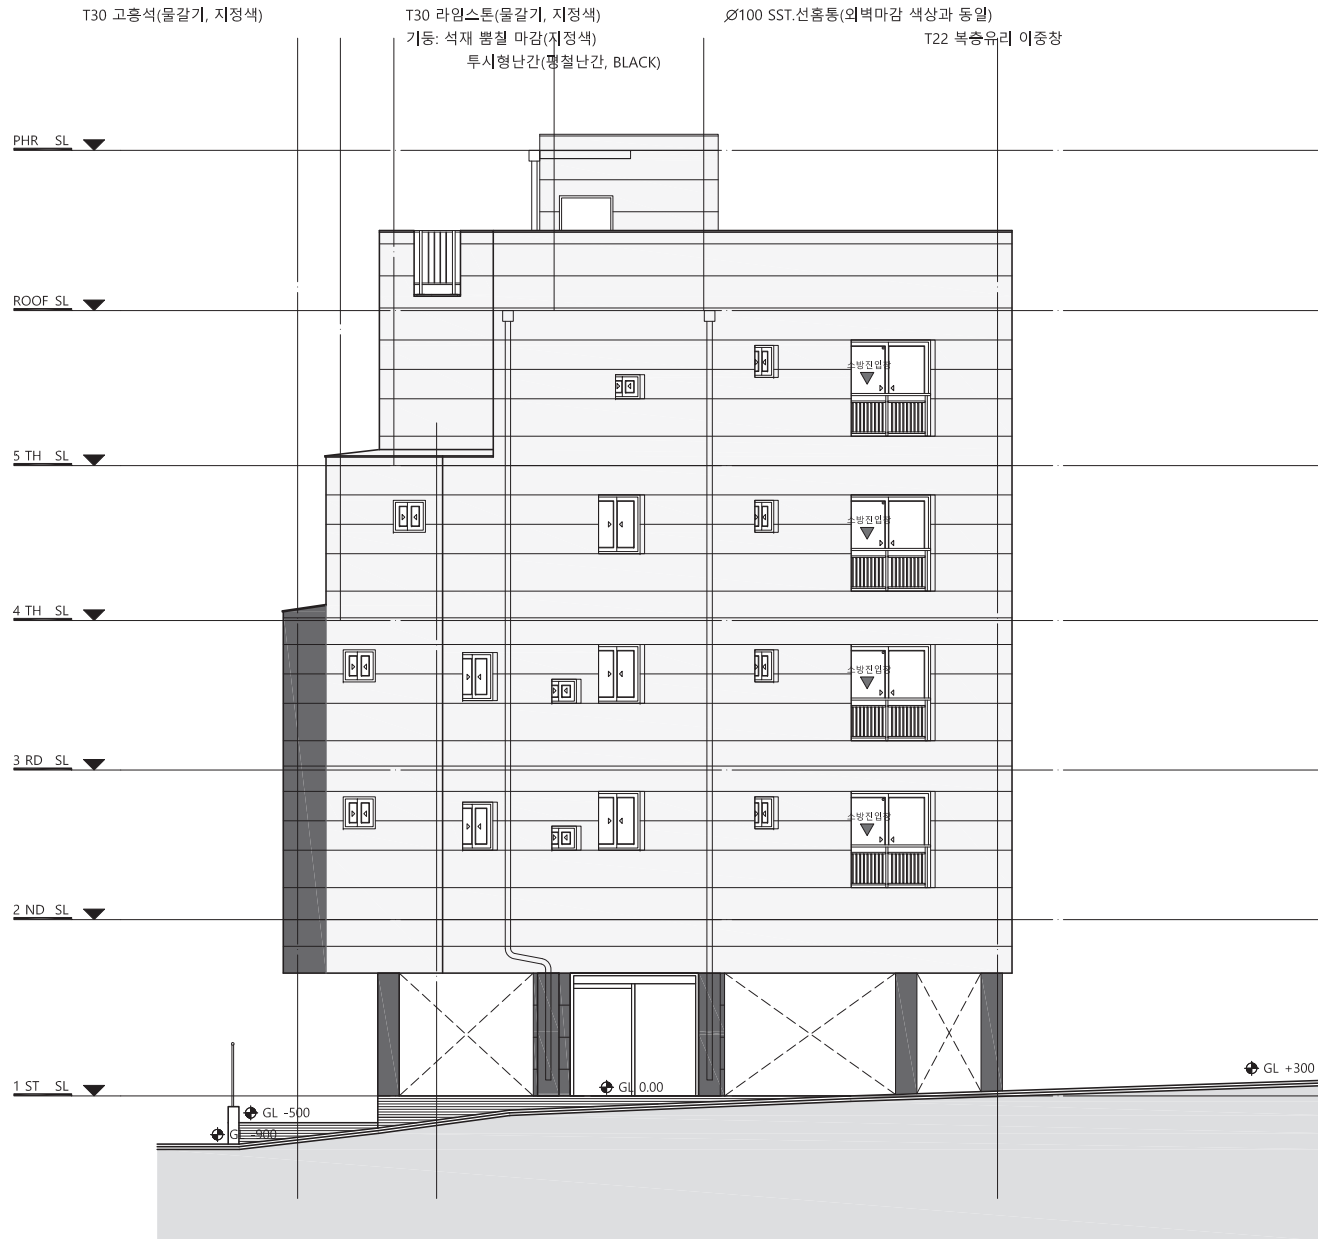

정면도

축척 : 1/ 100

KEY PLAN

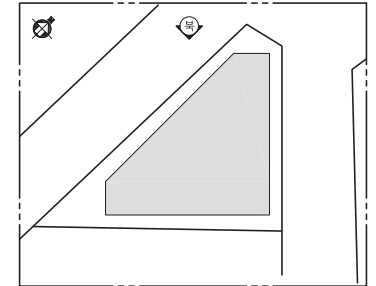

NOTE:



PROJECT
구로구 오류동 81-117번지
도시형생활주택 (원룸형) 창고형주택(공동주택)
APPROVED BY
건축사 구연복
건축사사무소 유일엔지니어링
서울특별시 서초구 반포대로 14길71(서초동)
(5서초에 글라피드 1904호)
TEL : 02) 540-1546, FAX : 02) 540-1576

TITLE
정면도

날짜
DATE
2022. 07.

SCALE
1/100
DWG NO.
A - 015
REV.

KEY PLAN

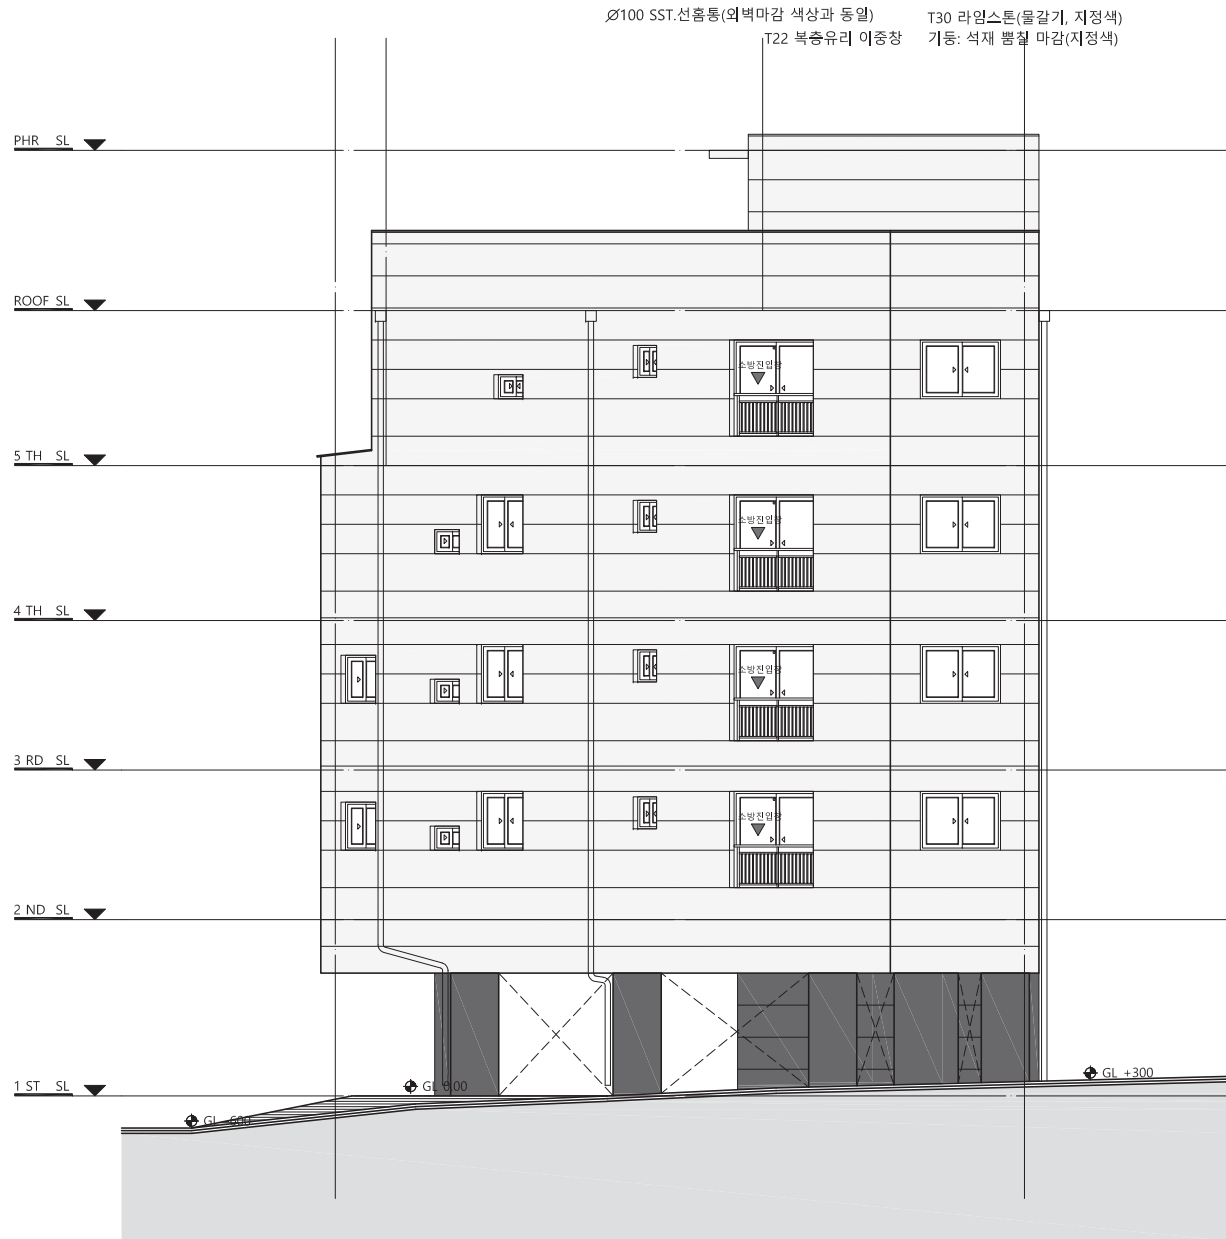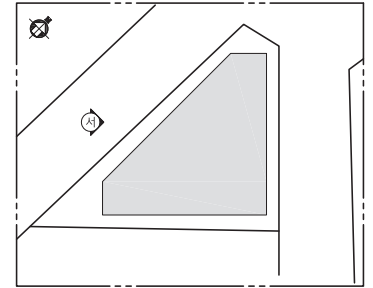


우측면도

축척 : 1/ 100

NOTE:

PROJECT		구로구 오류동 81-117번지 도시형생활주택 (원룸형) 창고형주택	
APPROVED BY		건축사 구연복	
ARCHITECT & ENGINEER		건축사사무소 유일엔지니어링 서울특별시 서초구 반포대로 14길 71 (서초동) (8서초에 글라피드 1904호) TEL : 02) 540-1546, FAX : 02) 540-1576	
TITLE		우측면도	
DATE		2022. 07.	
SCALE	1/100	DWG NO.	A - 016
		REV.	

KEY PLAN

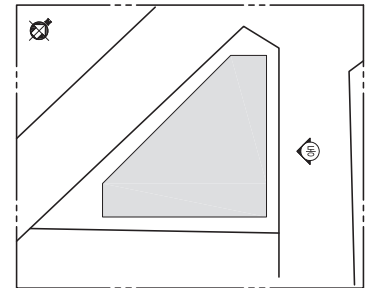

좌측면도

축척: 1/ 100

NOTE:

PROJECT	구로구 오류동 81-117번지 도시형생활주택 (원룸형) 용적률 300%		
APPROVED BY	건축사 구연복		
			
	 건축사무소 유일엔지니어링 서울특별시 서초구 반포대로 14길 71(서초동) (5서초에 글라피드 1904호) TEL : 02) 540-1546, FAX : 02) 540-1576		
TITLE	좌측면도		
날짜 DATE	2022. 07. .		
SCALE	1/100	DWG NO.	A - 017
		REV.	