


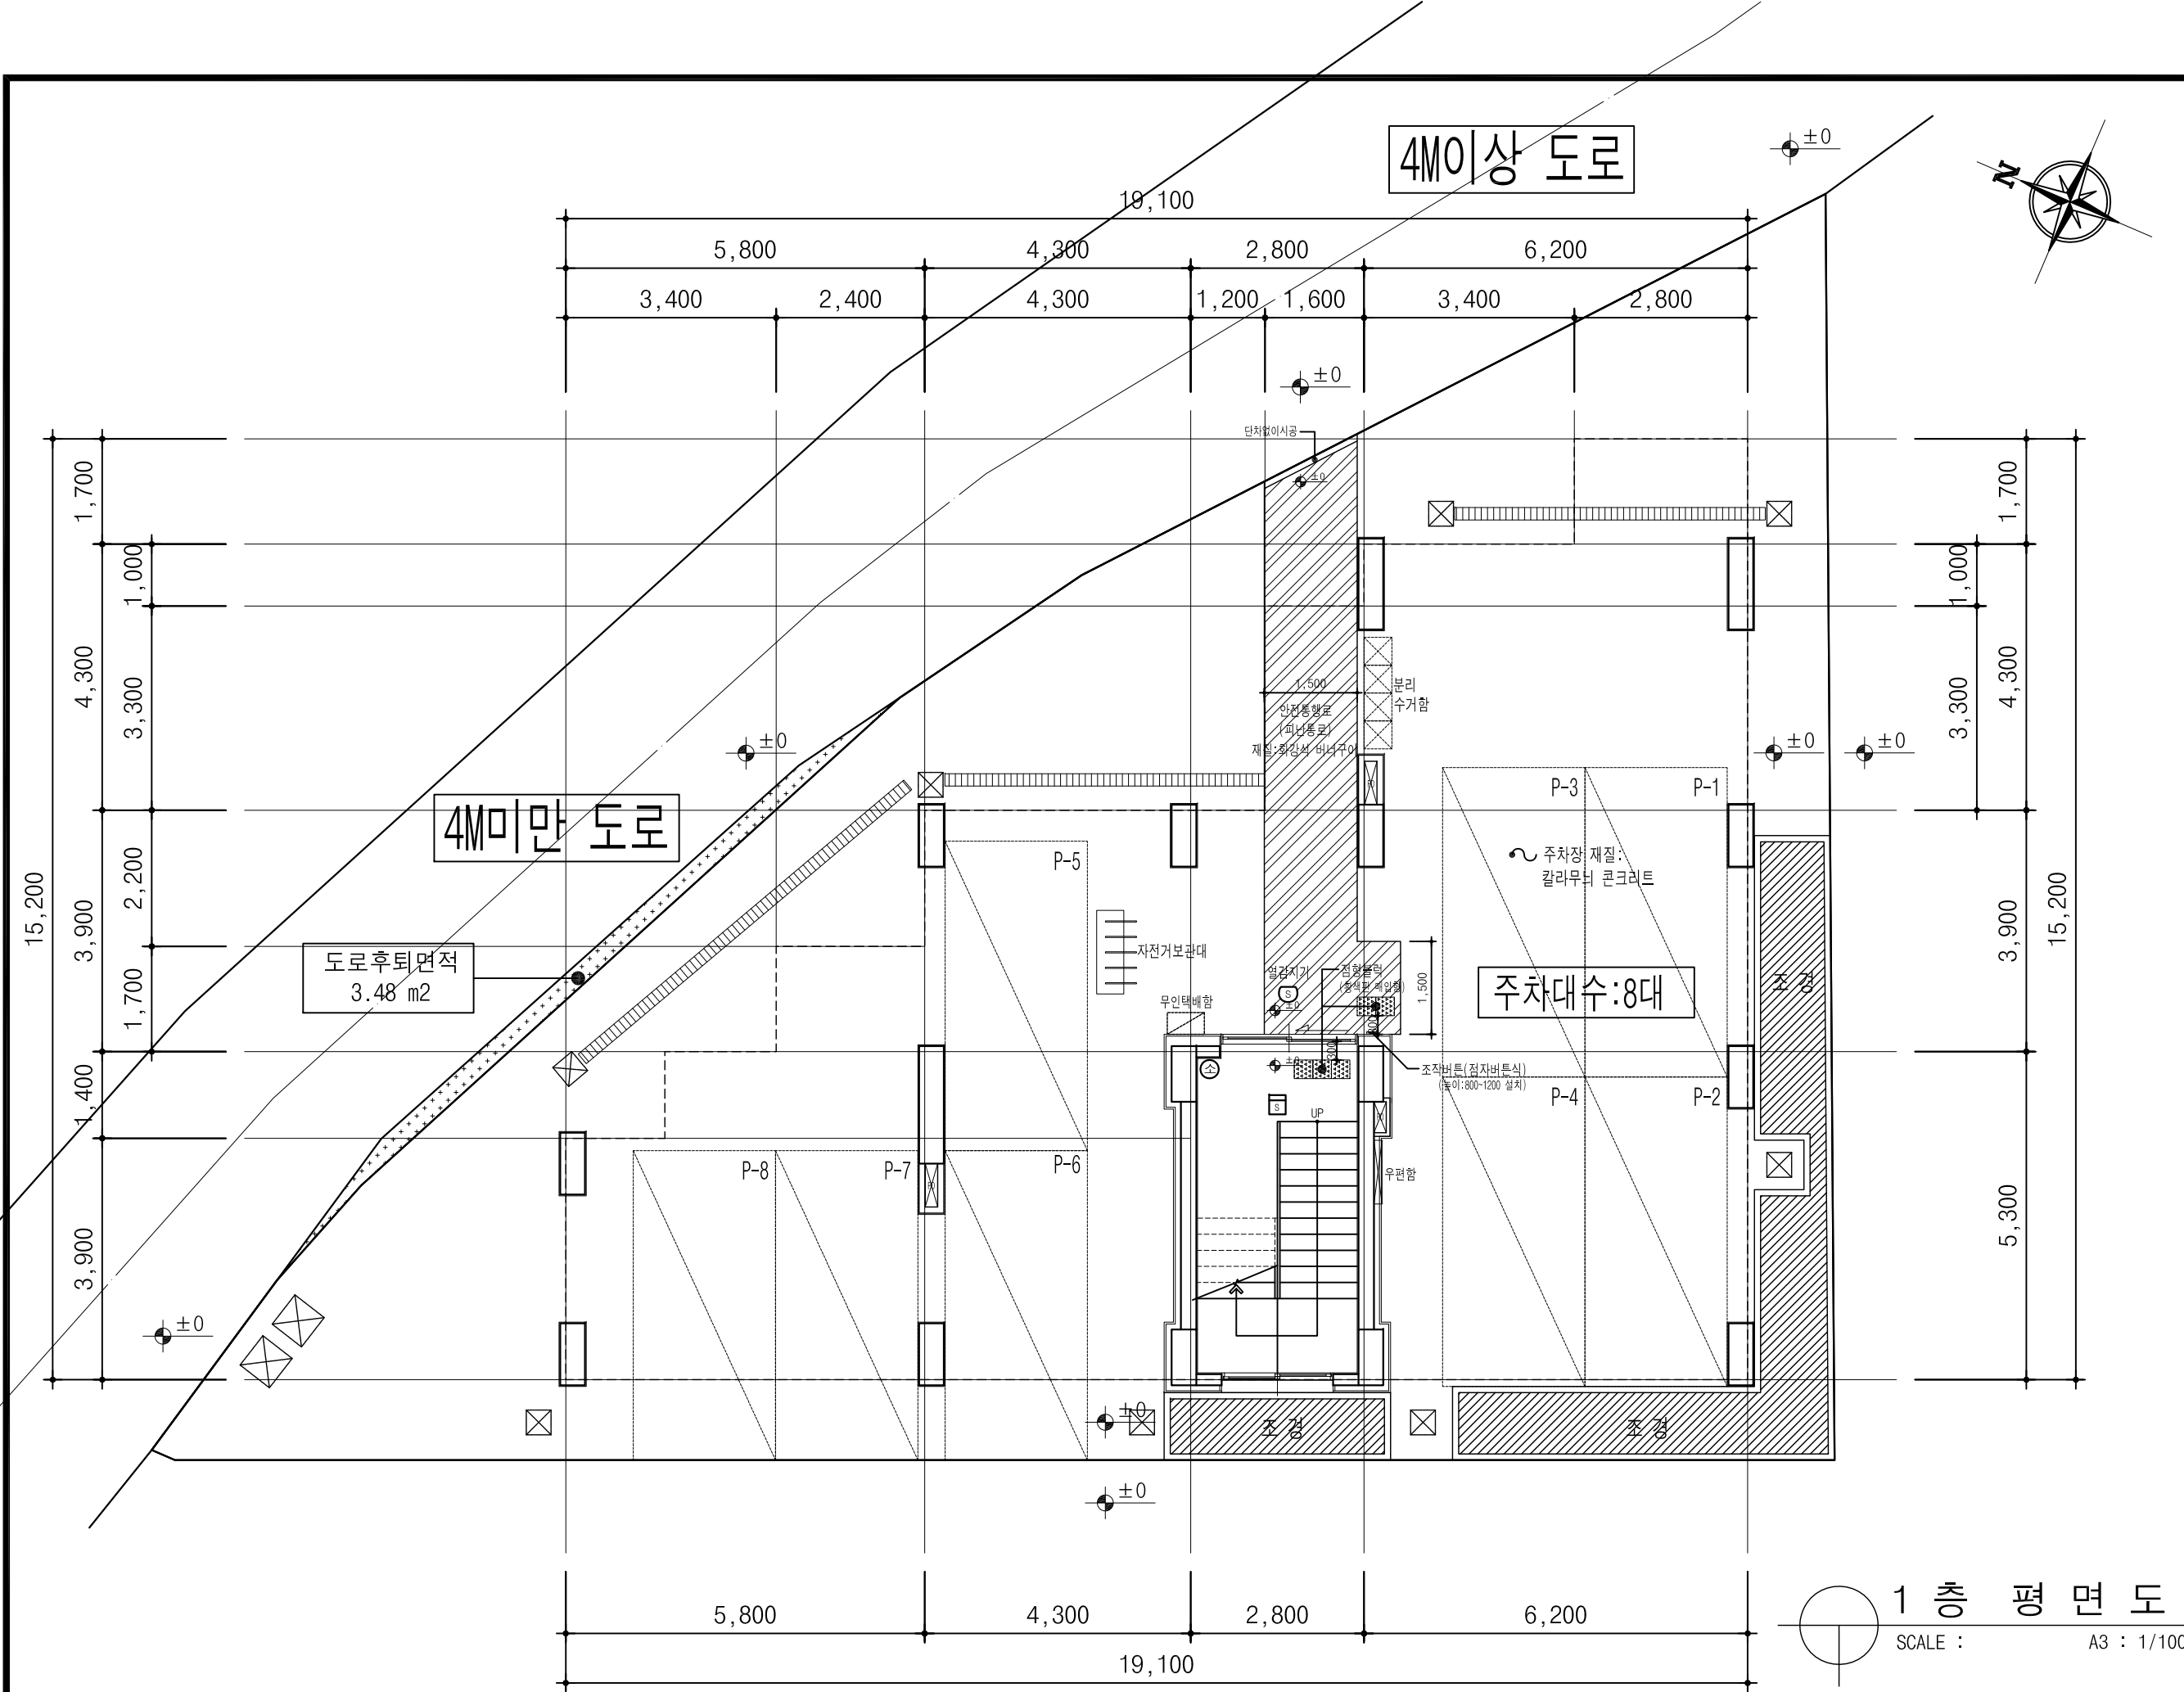

PROJECT TITLE
사업명칭

구로구 개봉동 131-5호 외 2필지
도시형생활주택(원룸형) 신축공사

NAME OF DRAWING
도면명

1층 평면도

NOTE
주 기

단독경보감지기

ABC분말소화기(3.3KG)

보일러

에어컨 실외기

* 구조 *

1.콘크리트: fck = 24 MPa

2. 철근 : fy = 400 MPa

3. 세대간벽두께:180mm(복배근)

4. 외벽두께:180mm(복배근)

5. 코아벽두께:180mm(복배근)

6. 스라브두께:210mm(복배근)

NO. ▲ REVISIONS ▲ DATE
번호 수 영 일 자

DESIGNED BY
설 계

CHECKED BY
심 사

APPROVED BY
승 인

CONSULTANTS
합 동 설 계

SCALE
축 척 1/100

DATE
일 자 2019. 02.

DWG NO.
도면번호

SHEET NO.
일련번호

□-□□□

THE ARCHITECTS DESIGN GROUP
건축사사무소 다움건축

TEL. 02.414.6061 (代)
FAX. 02.414.6062

1층 평면도

SCALE : A3 : 1/100

PROJECT TITLE
사 업 명 칭

구로구 개봉동 131-5호 외 2필지
도시형생활주택(원룸형) 신축공사

NAME OF DRAWING
도 면 명

2~3 층 평 면 도

NOTE
주 기

- 단독경보감지기
- ABC분말소화기(3.3KG)
- 보일러
- 에어컨 실외기

- * 구 조 *
- 콘크리트: fck = 24 MPa
 - 철근: fy = 400 MPa
 - 세대간벽두께: 180mm(복배근)
 - 외벽두께: 180mm(복배근)
 - 코아벽두께: 180mm(복배근)
 - 스라브두께: 210mm(복배근)

NO. ▲ REVISIONS 수 ▲ DATE
번호 장 일 자

DESIGNED BY
설 계

CHECKED BY
심 사

APPROVED BY
승 인

CONSULTANTS
합 동 설 계

SCALE
축尺 1/100

DATE
일 자 2019. 02.

DWG NO.
도면 번호

SHEET NO.
일련 번호

DAWOO
dawoom
건축사사무소 다움건축
THE ARCHITECTS DESIGN GROUP
TEL. 02.414.6061 (代)
FAX. 02.414.6062



2~3 층 평 면 도
SCALE : A3 : 1/100



4 층 평면도
SCALE : A3 : 1/100

PROJECT TITLE
사업명칭

구로구 개봉동 131-5호 외 2필지
도시형생활주택(원룸형) 신축공사

NAME OF DRAWING
도면명

4 층 평면도

- NOTE
주 기
- 단독경보감지기
 - ABC분말소화기(3.3KG)
 - 보일러
 - 에어컨 실외기

- * 구 조 *
- 콘크리트: fck = 24 MPa
 - 철근: fy = 400 MPa
 - 세대간벽두께: 180mm(복배근)
 - 외벽두께: 180mm(복배근)
 - 코아벽두께: 180mm(복배근)
 - 스라브두께: 210mm(복배근)

NO. 번호	REVISIONS 수정	DATE 일
-----------	-----------------	-----------

DESIGNED BY
설계

CHECKED BY
심사

APPROVED BY
승인

CONSULTANTS
합동설계

SCALE
축척 1/100

DATE
일자 2019. 02.

DWG NO.
도면번호

SHEET NO.
일련번호 □-□□□

DAWOO
dawoom
건축사사무소 다움건축
THE ARCHITECTS DESIGN GROUP
TEL. 02.414.6061 (代)
FAX. 02.414.6062

PROJECT TITLE
사업명칭

구로구 개봉동 131-5호 외 2필지
도시형생활주택(원룸형) 신축공사

NAME OF DRAWING
도면명

5층 평면도

NOTE
주 기

- 단독경보감지기
ABC분말소화기(3.3KG)
보일러
에어컨 실외기

* 구조 *

1. 콘크리트: fck = 24 MPa
2. 철근: fy = 400 MPa
3. 세대간벽두께: 180mm(복배근)
4. 외벽두께: 180mm(복배근)
5. 코아벽두께: 180mm(복배근)
6. 스라브두께: 210mm(복배근)

NO. REVISIONS DATE
번호 수정 일자

DESIGNED BY
설계

CHECKED BY
심사

APPROVED BY
승인

CONSULTANTS
합동설계


SCALE
축척 1/100

DATE
일자 2019. 02.





DWG NO.
도면번호

SHEET NO.
일련번호


DAWOO
dawoom
건축사사무소 다움건축
THE ARCHITECTS DESIGN GROUP
TEL. 02.414.6061 (代)
FAX. 02.414.6062

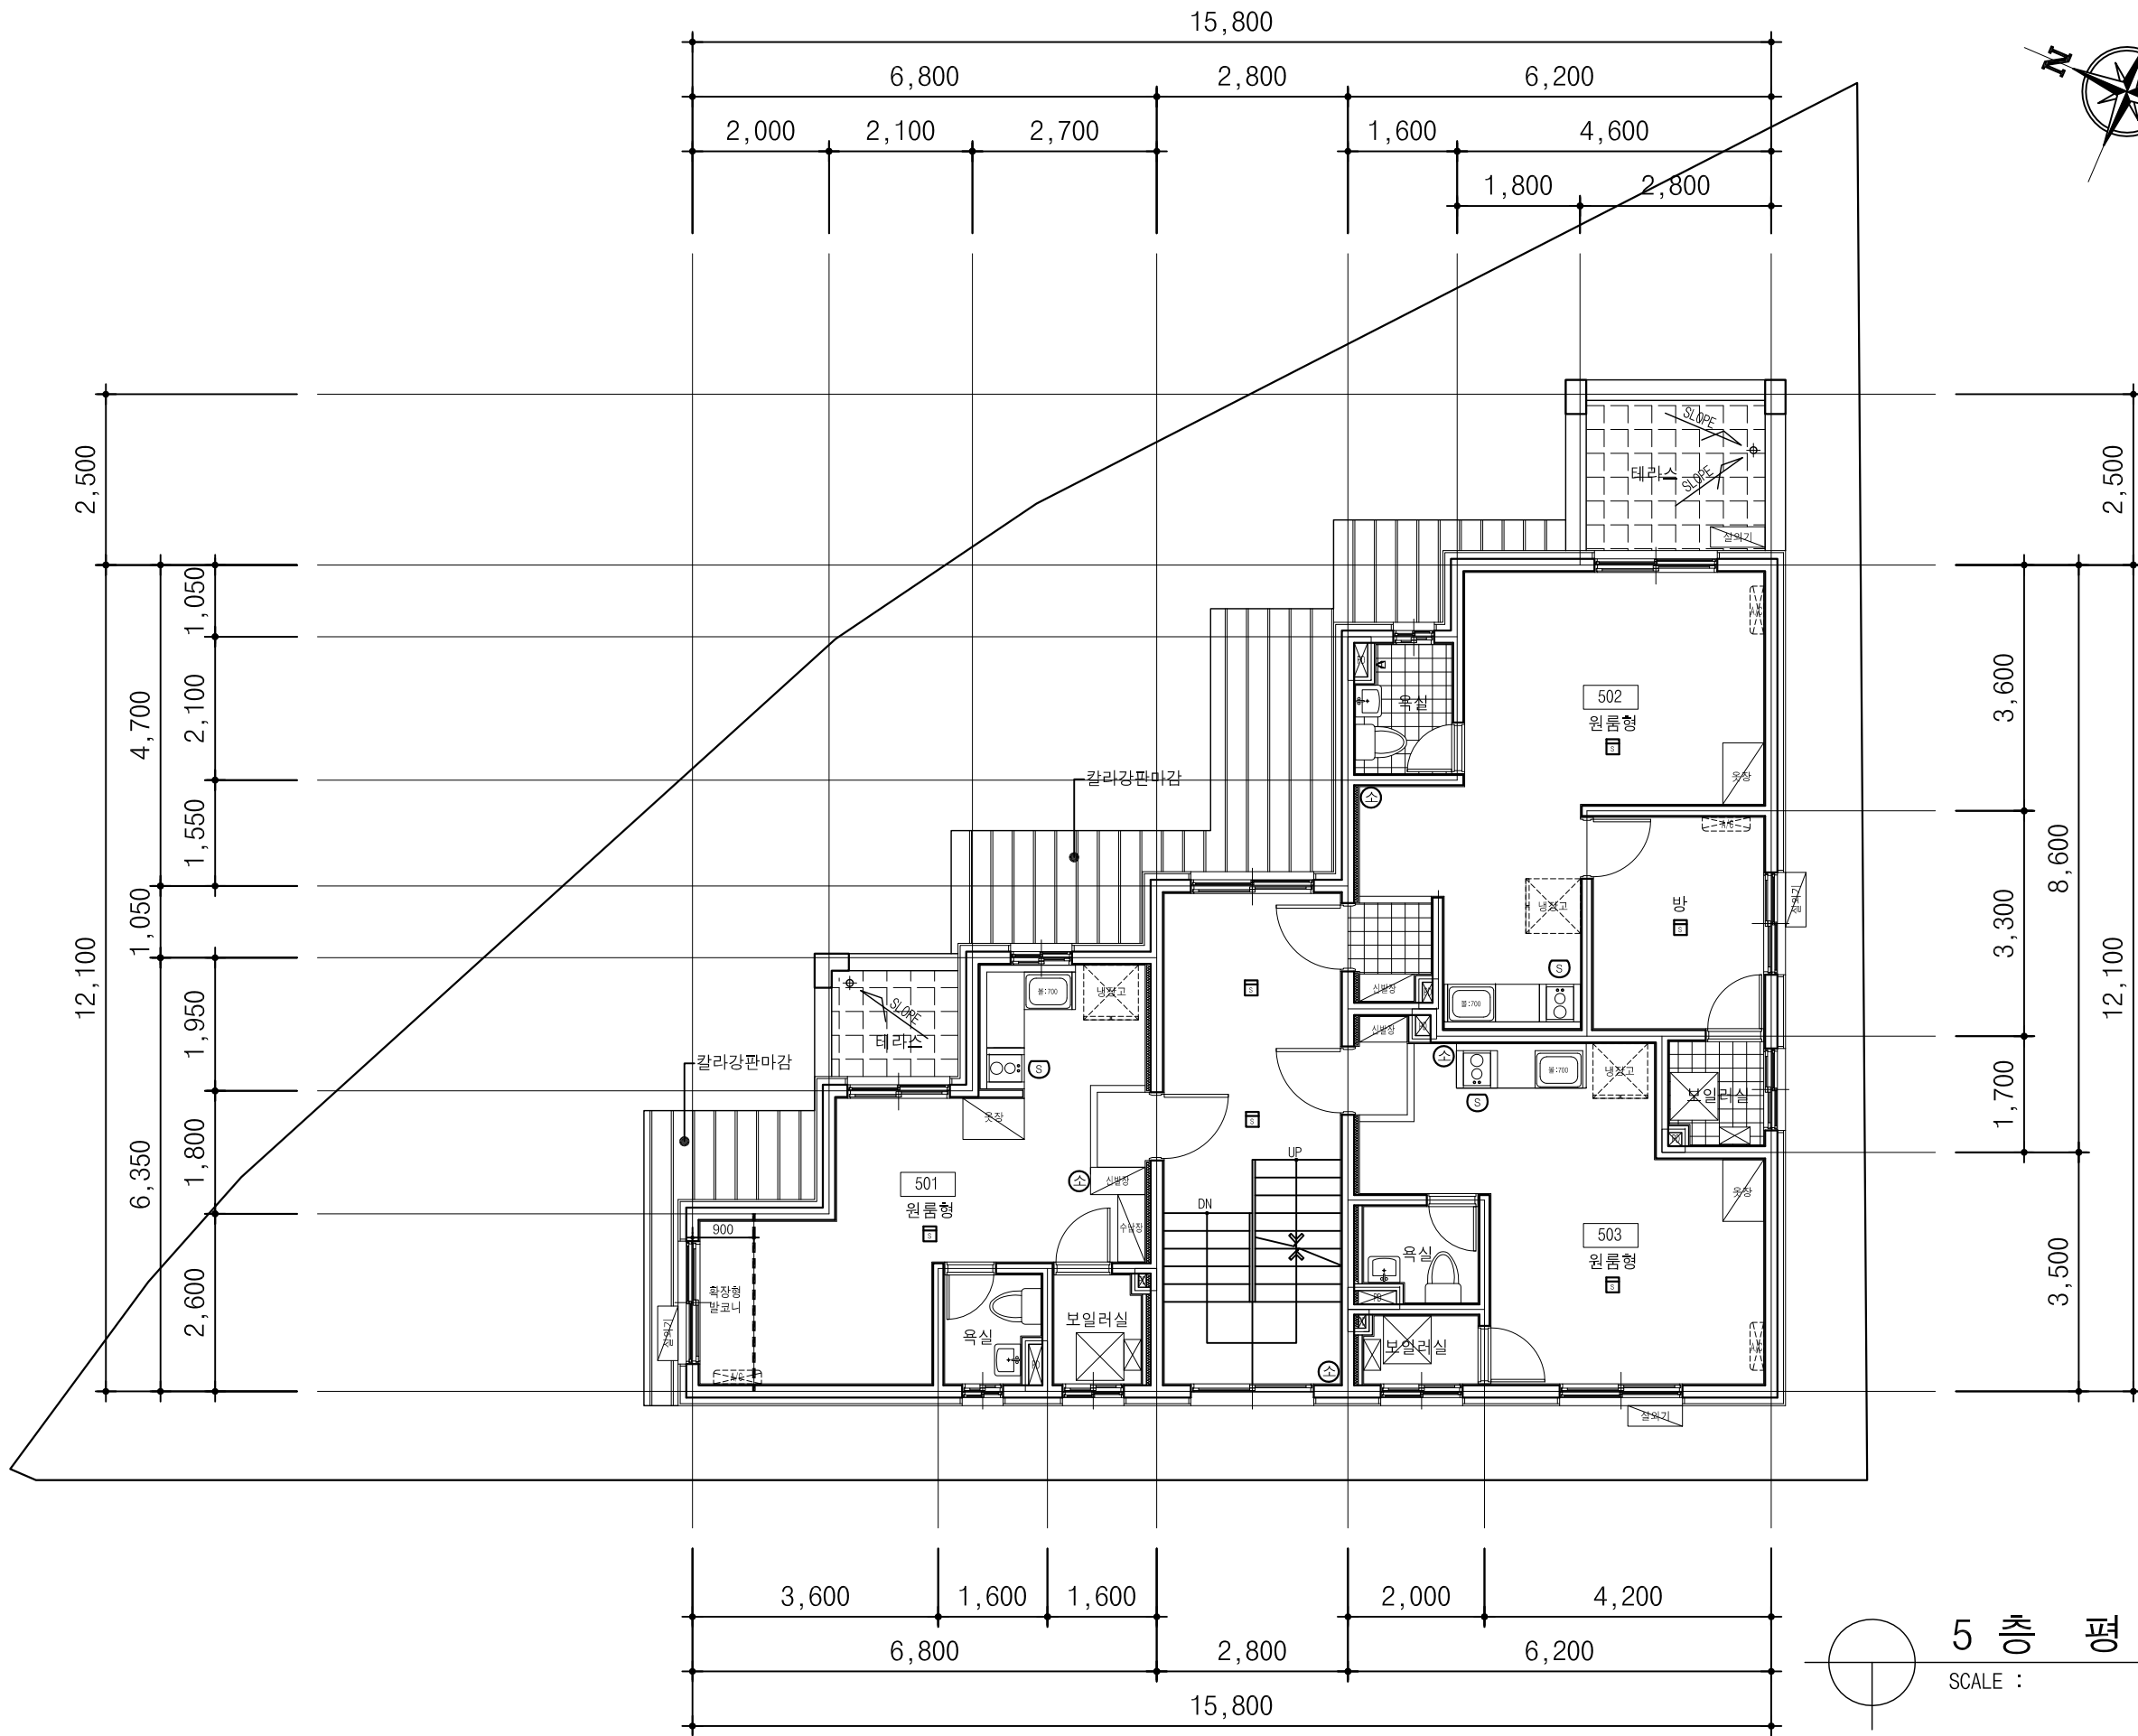

5층 평면도
SCALE : A3 : 1/100

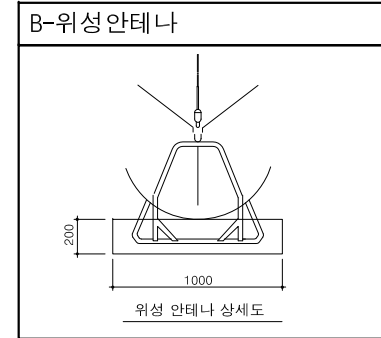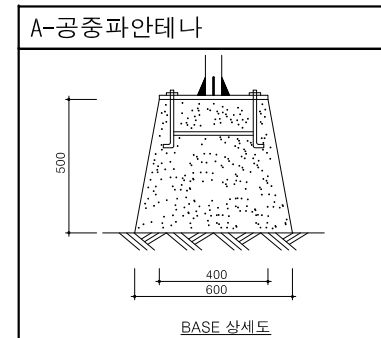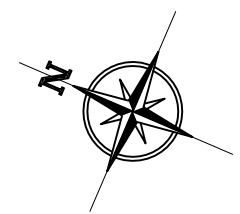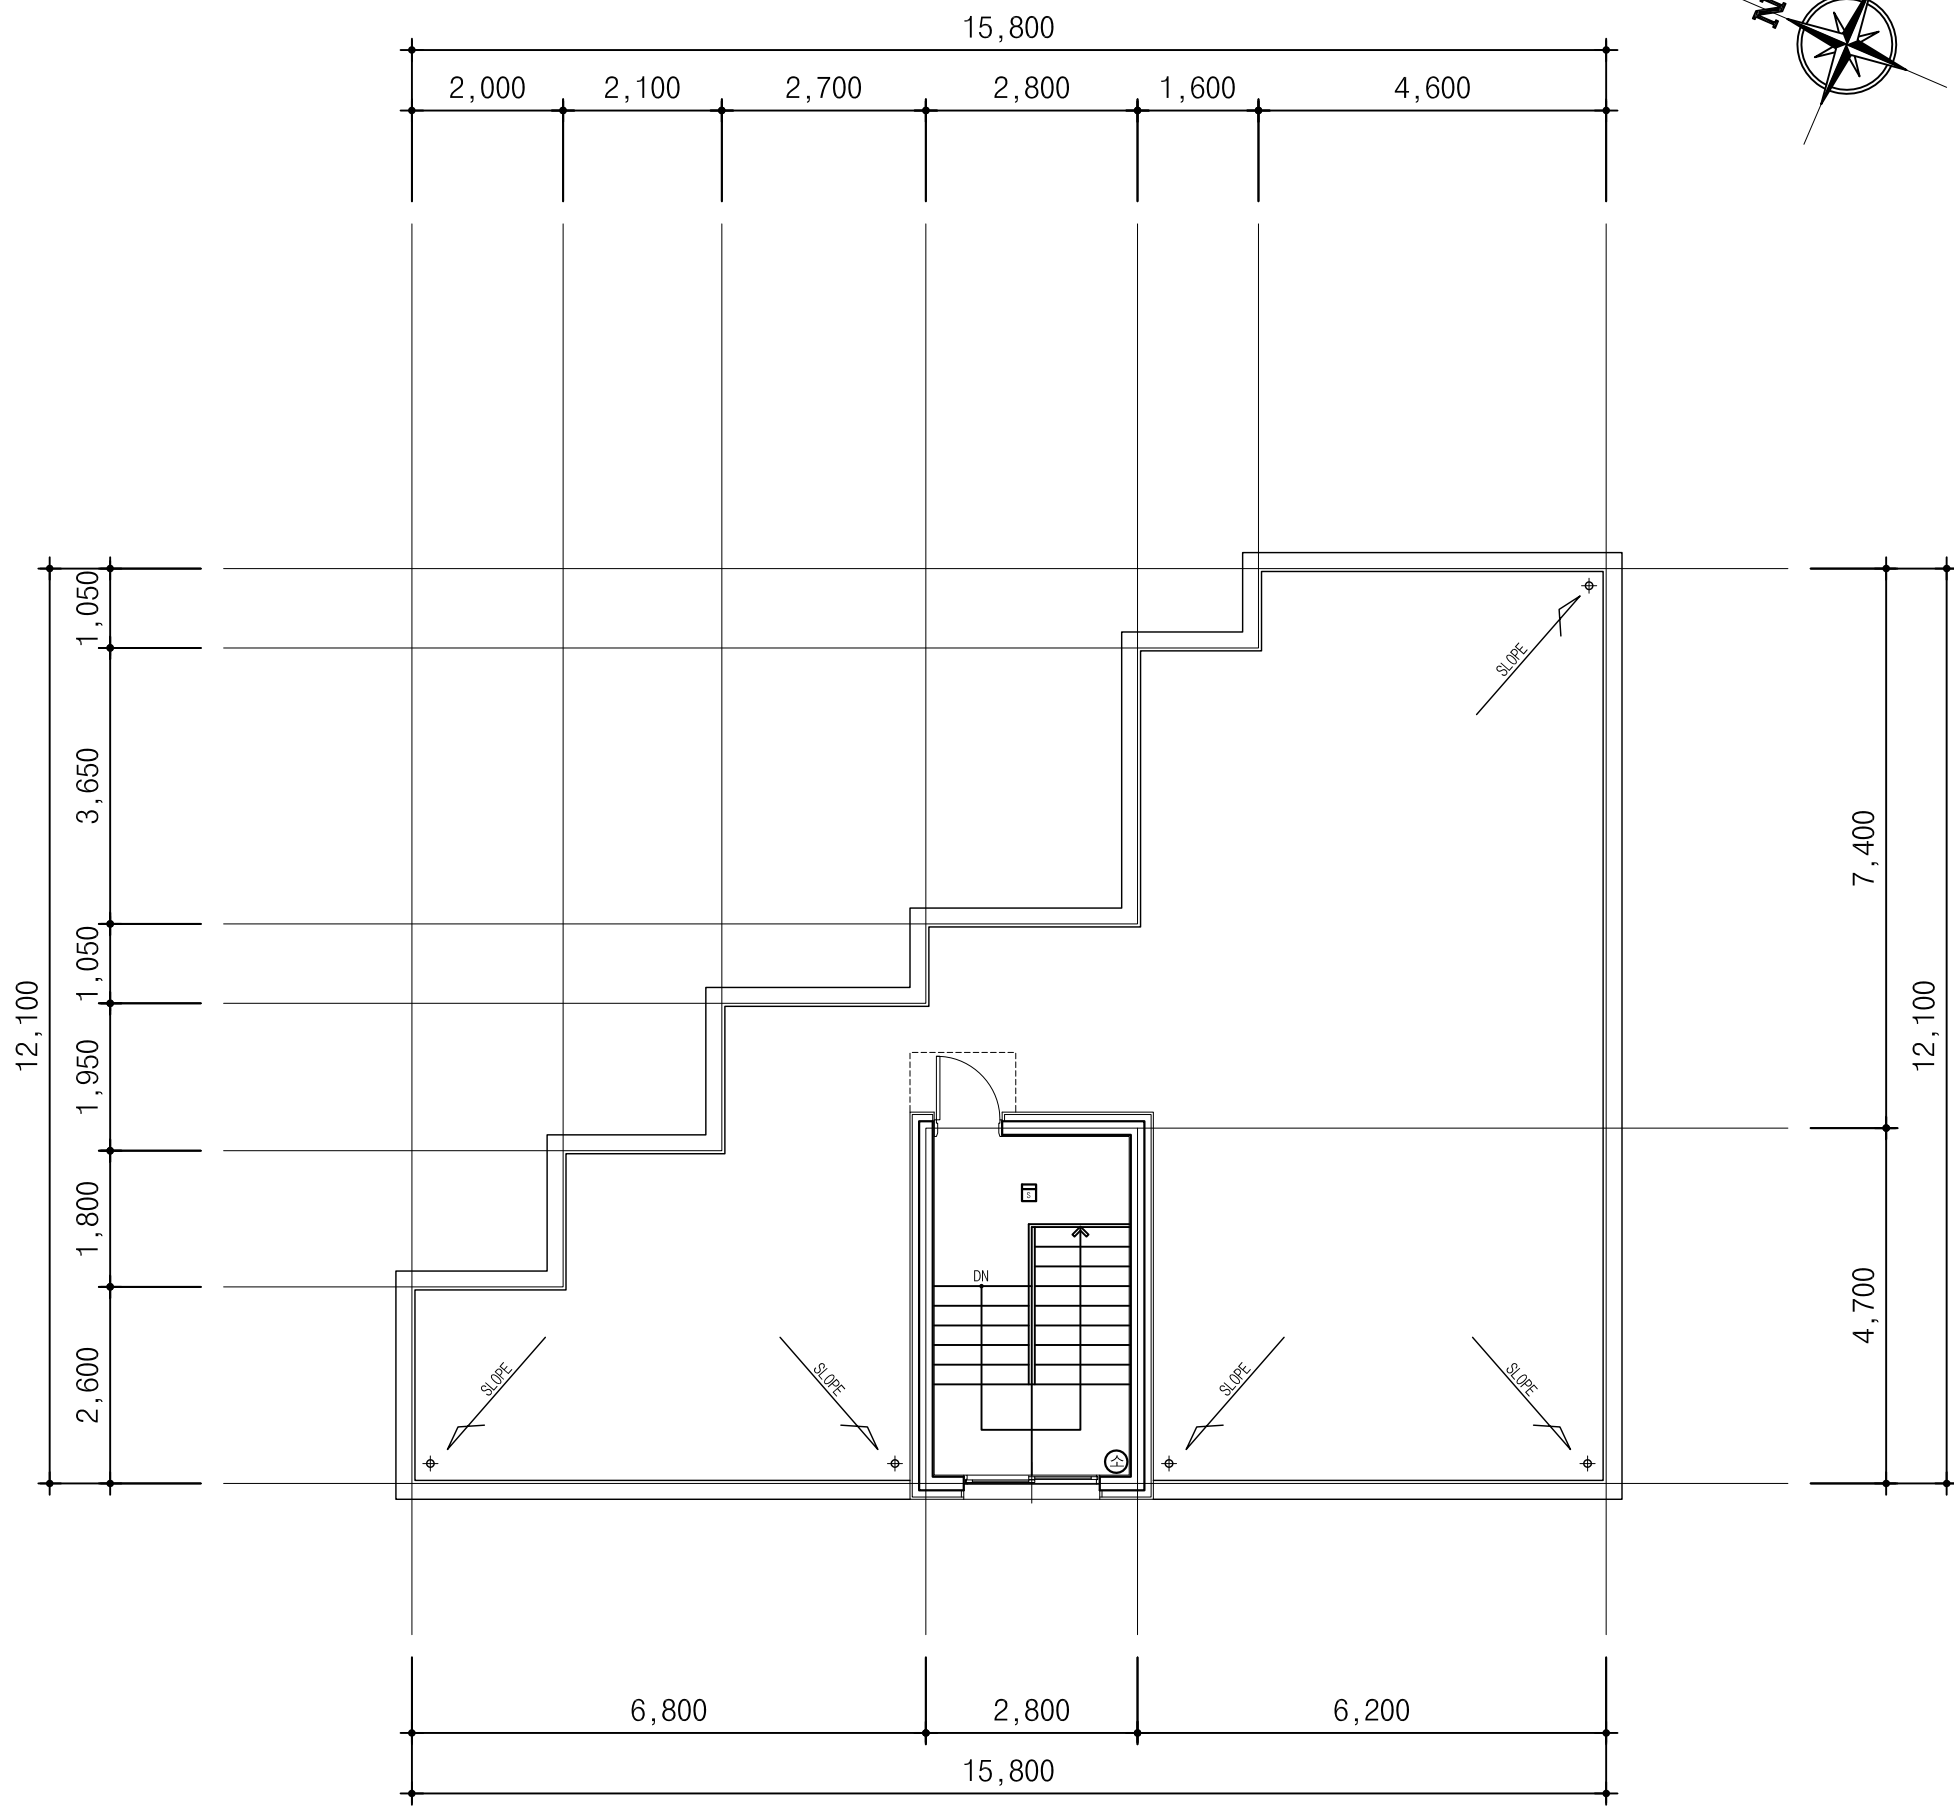

*통신도면-정보통신상세도 참고

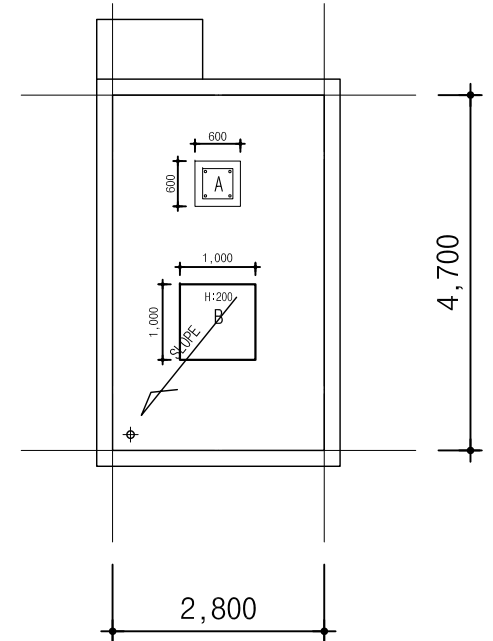

지붕 및 옥탑 평면도
SCALE : A3 : 1/100

PROJECT TITLE
사 업 명 칭
구로구 개봉동 131-5호 외 2필지
도시형생활주택(원룸형) 신축공사

NAME OF DRAWING
도 면 명
지붕 및 옥탑 평면도

NOTE
주 기
단독경보감지기
ABC분말소화기(3.3KG)

- * 구 조 *
1. 콘크리트: fck = 24 MPa
 2. 철근 : fy = 400 MPa
 3. 세대간벽두께: 180mm(복배근)
 4. 외벽두께: 180mm(복배근)
 5. 코아벽두께: 180mm(복배근)
 6. 스라브두께: 210mm(복배근)

NO. ▲ REVISIONS ▲ DATE
번호 수정 일자

DESIGNED BY
설 계

CHECKED BY
심 사

APPROVED BY
승 인

CONSULTANTS
합 동 설 계



SCALE
축 척 1/100

DATE
일 자 2019. 02.

DWG NO.
도면 번호




SHEET NO.
일련 번호 □-□□□


dawoom
건축사사무소 다웁건축
THE ARCHITECTS DESIGN GROUP
TEL. 02,414,6061 (代)
FAX. 02,414,6062

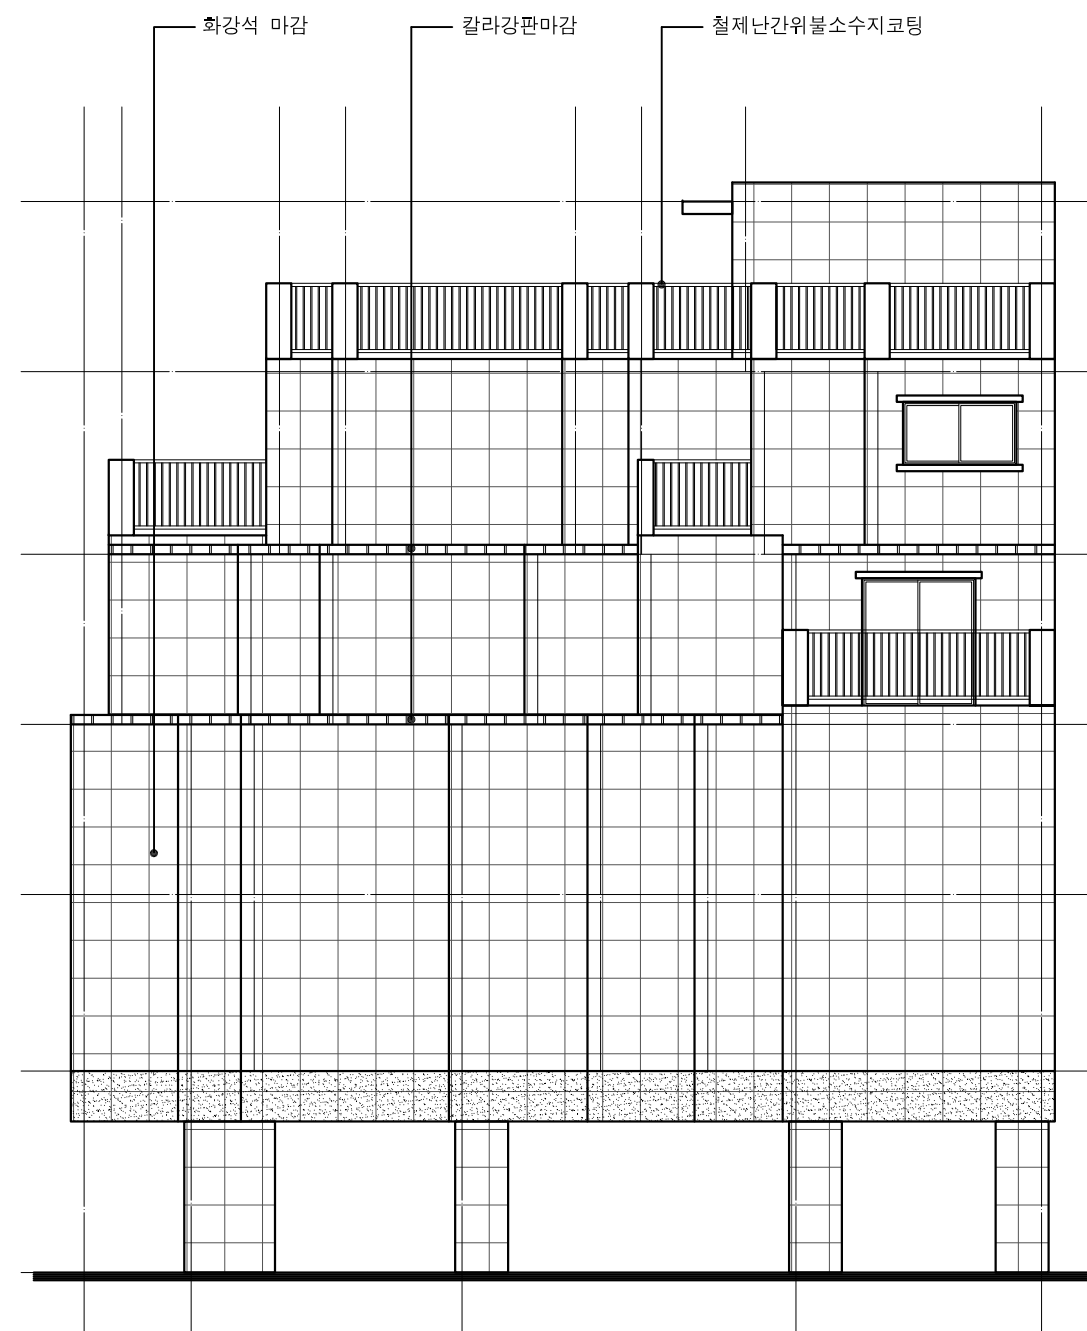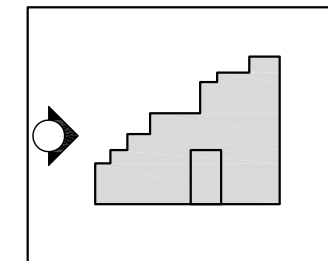


우 측 면 도
SCALE : A3 : 1/120

 **다움건축**
dawoom
건축사사무소 다움건축
THE ARCHITECTS DESIGN GROUP
TEL. 02.414.6061 (代)
FAX. 02.414.6062

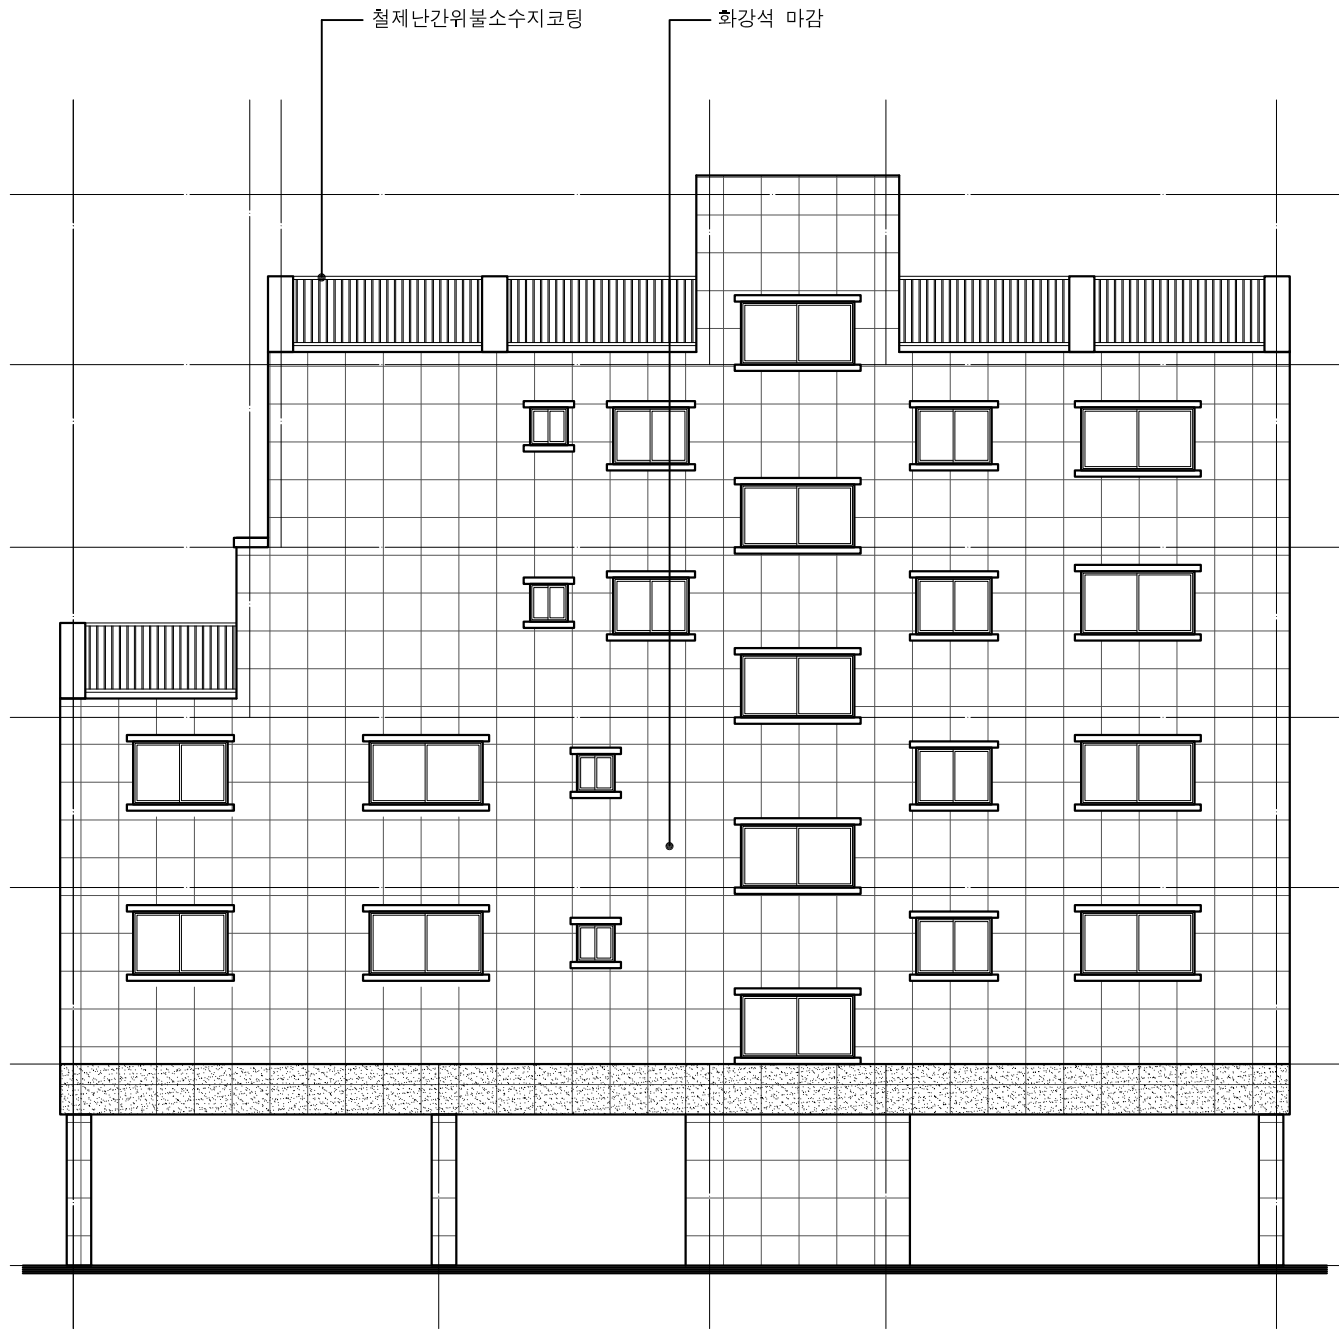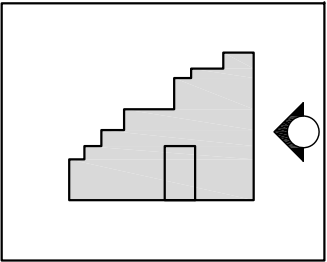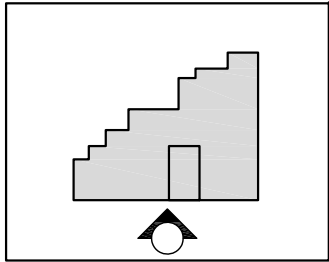

배 면 도
SCALE : A3 : 1/120

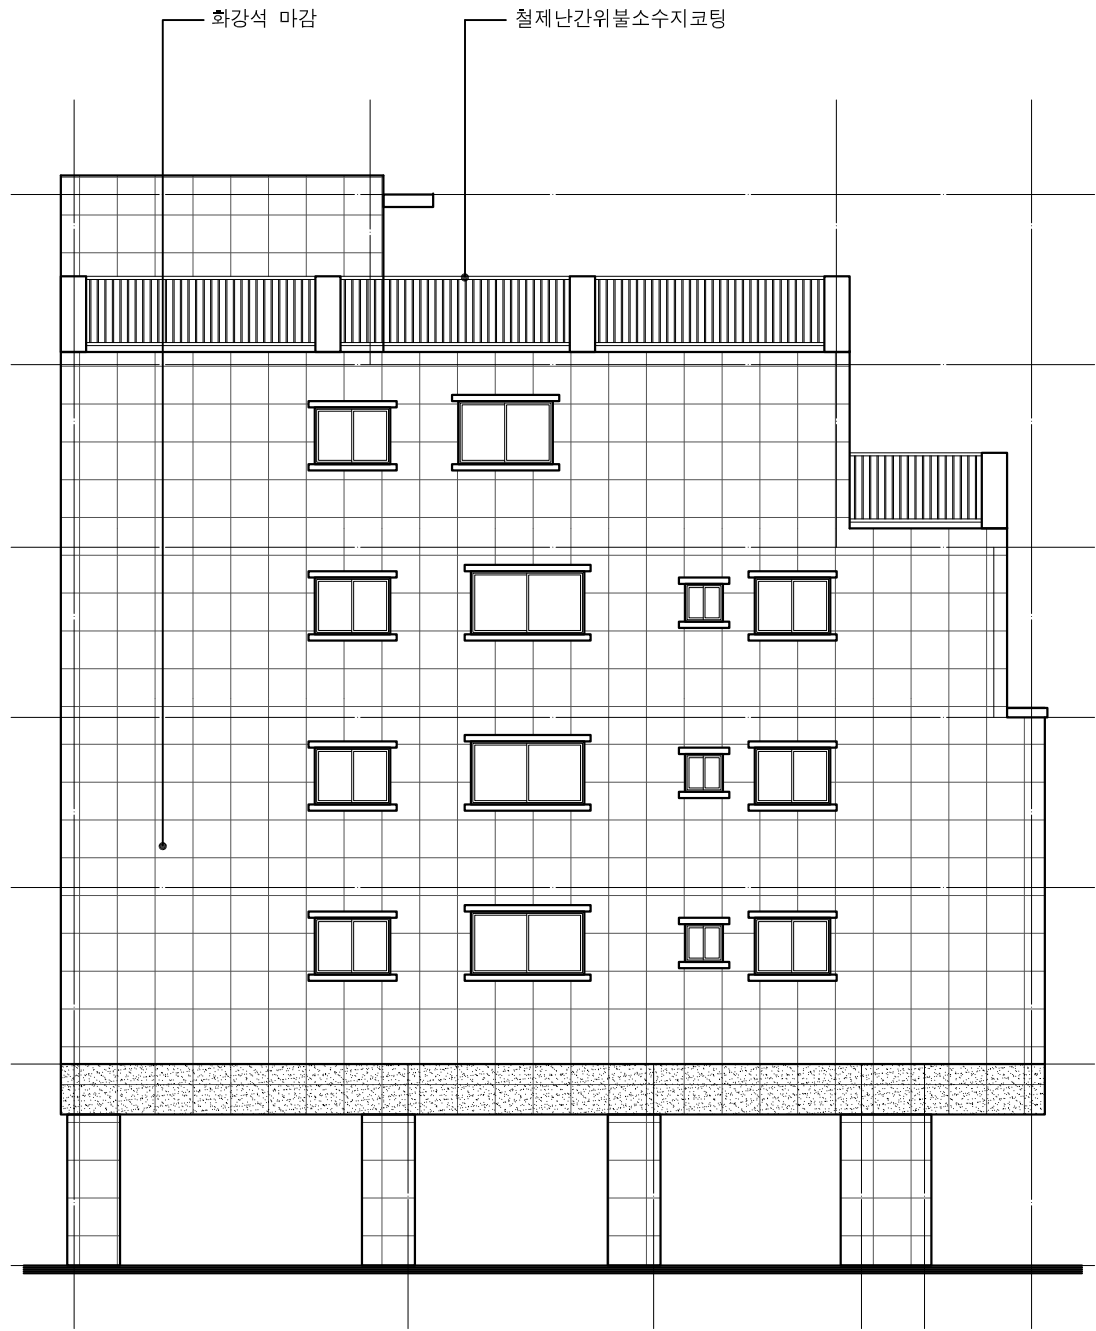

좌 측 면 도
SCALE : A3 : 1/120

PROJECT TITLE

사 업 명 칭

구로구 개봉동 131-5호 외 2필지
도시형생활주택(원룸형) 신축공사

NAME OF DRAWING

도 면 명

입면도-2

NOTE

주 기

NO. ▲ REVISIONS ▲ DATE

번호 수정 일자

DESIGNED BY

설 계

CHECKED BY

심 사

APPROVED BY

승 인

CONSULTANTS

합 동 설 계

SCALE

1/120

DATE

2019. 02.

DWG NO.

도면 번호

SHEET NO.

일련 번호

□-□□□





da

건축사사무소 다움건축

THE ARCHITECTS DESIGN GROUP

TEL. 02.414.6061 (代)

FAX. 02.414.6062

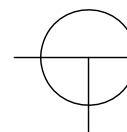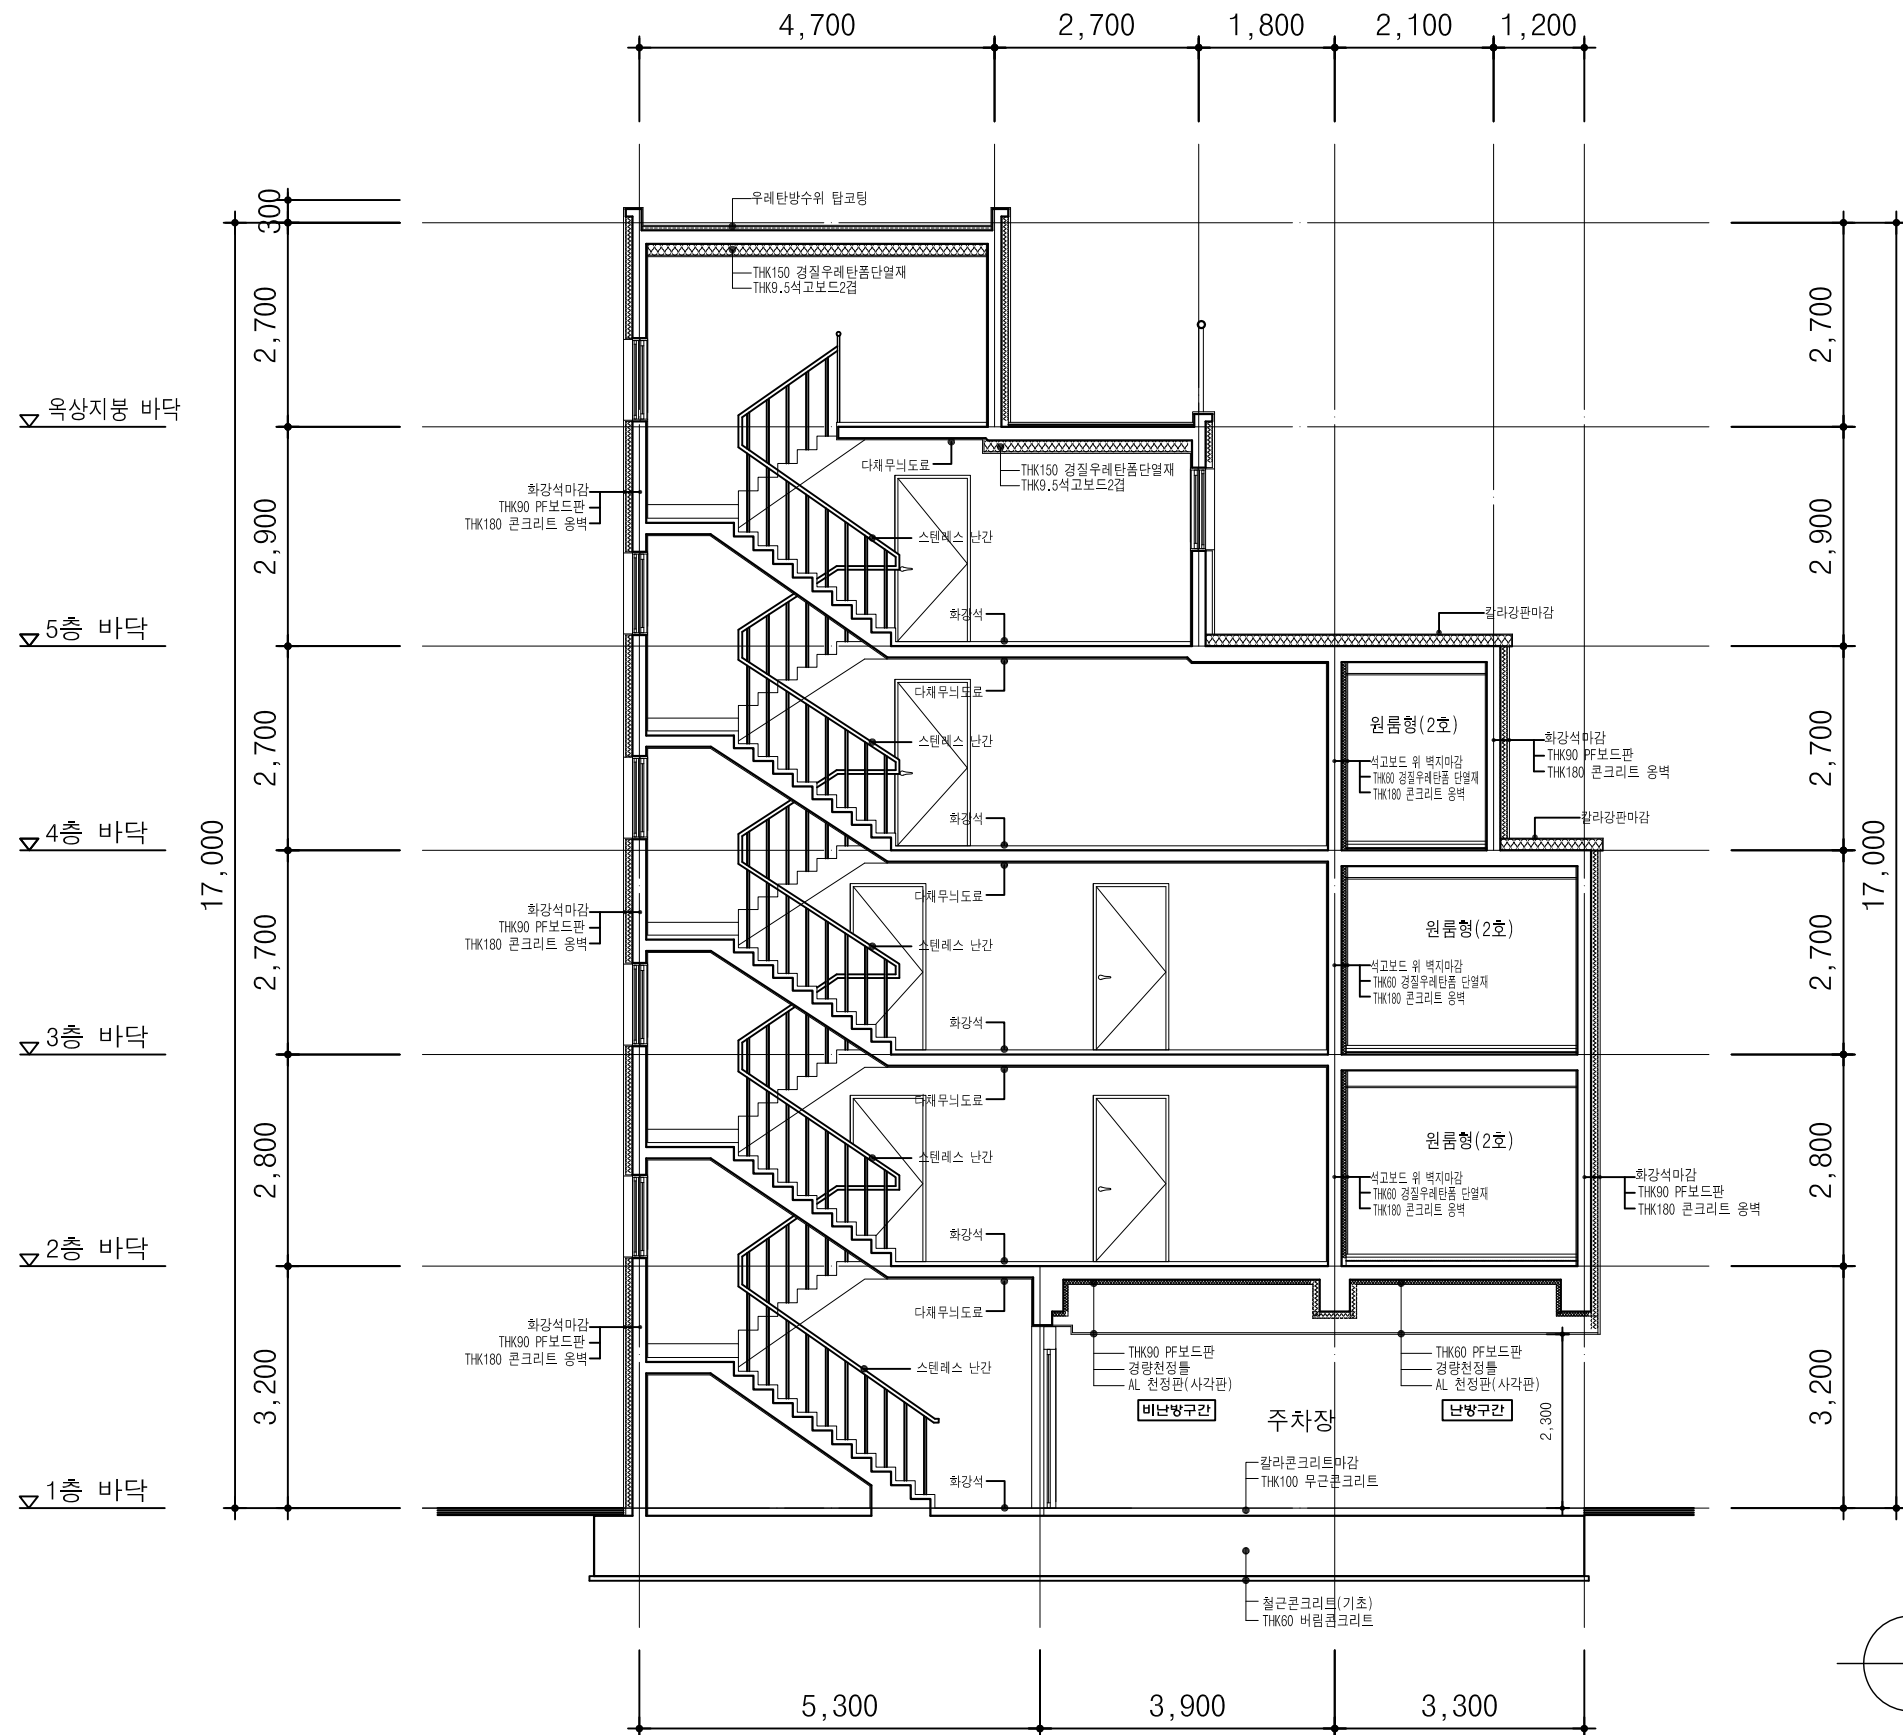

계단 단면도

SCALE : A3 : 1/100

PROJECT TITLE
사업명

구로구 개봉동 131-5호 외 2필지
도시형생활주택(원룸형) 신축공사

NAME OF DRAWING
도면명

계단 단면도

NOTE
주 기

NO. ▲ REVISIONS ▲ DATE
번호 수정 일자

DESIGNED BY
설 계

CHECKED BY
심 사

APPROVED BY
승 인

CONSULTANTS
합 동 설 계

SCALE
축 척 1/100

DATE
일 자 2019. 02.

DWG NO.
도면 번호

SHEET NO.
일련 번호

DAWOOOM
dawoom
건축사사무소 다움건축

THE ARCHITECTS DESIGN GROUP
TEL. 02.414.6061 (代)
FAX. 02.414.6062