

1. 조 감 도




1. 투 시 도



2. 건축개요 및 현황도

건축개요

설 계 명 : 구로구 고척동 253-40번지 외 1필지
도시형 생활주택 (원룸형) 청년주택 신축공사
대지위치 : 서울특별시 구로구 고척동 253-40번지 외 1필지
지역지구 : 제2종 일반주거지역
건물용도 : 도시형생활주택(원룸형)18세대
건물규모 : 지하 0층, 지상 5층
대지면적 : 264.50 m²
건축면적 : 157.88 m²
연 면 적 : 528.37 m²
건 폐 율 : 56.69 %
용 적 륜 : 199.76 %
최고높이 : 16.80 M
구 조 철근콘크리트조
주차대수 : 법정 6대, 계획 8대
조경면적 : 14.82 m²

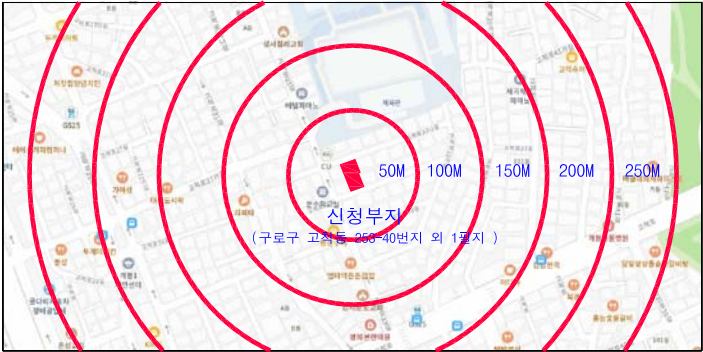

위 치 도



주변현황도

3. 입 면 도



정 면 도






좌 측 면 도



우 측 면 도





배 면 도

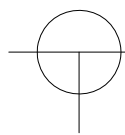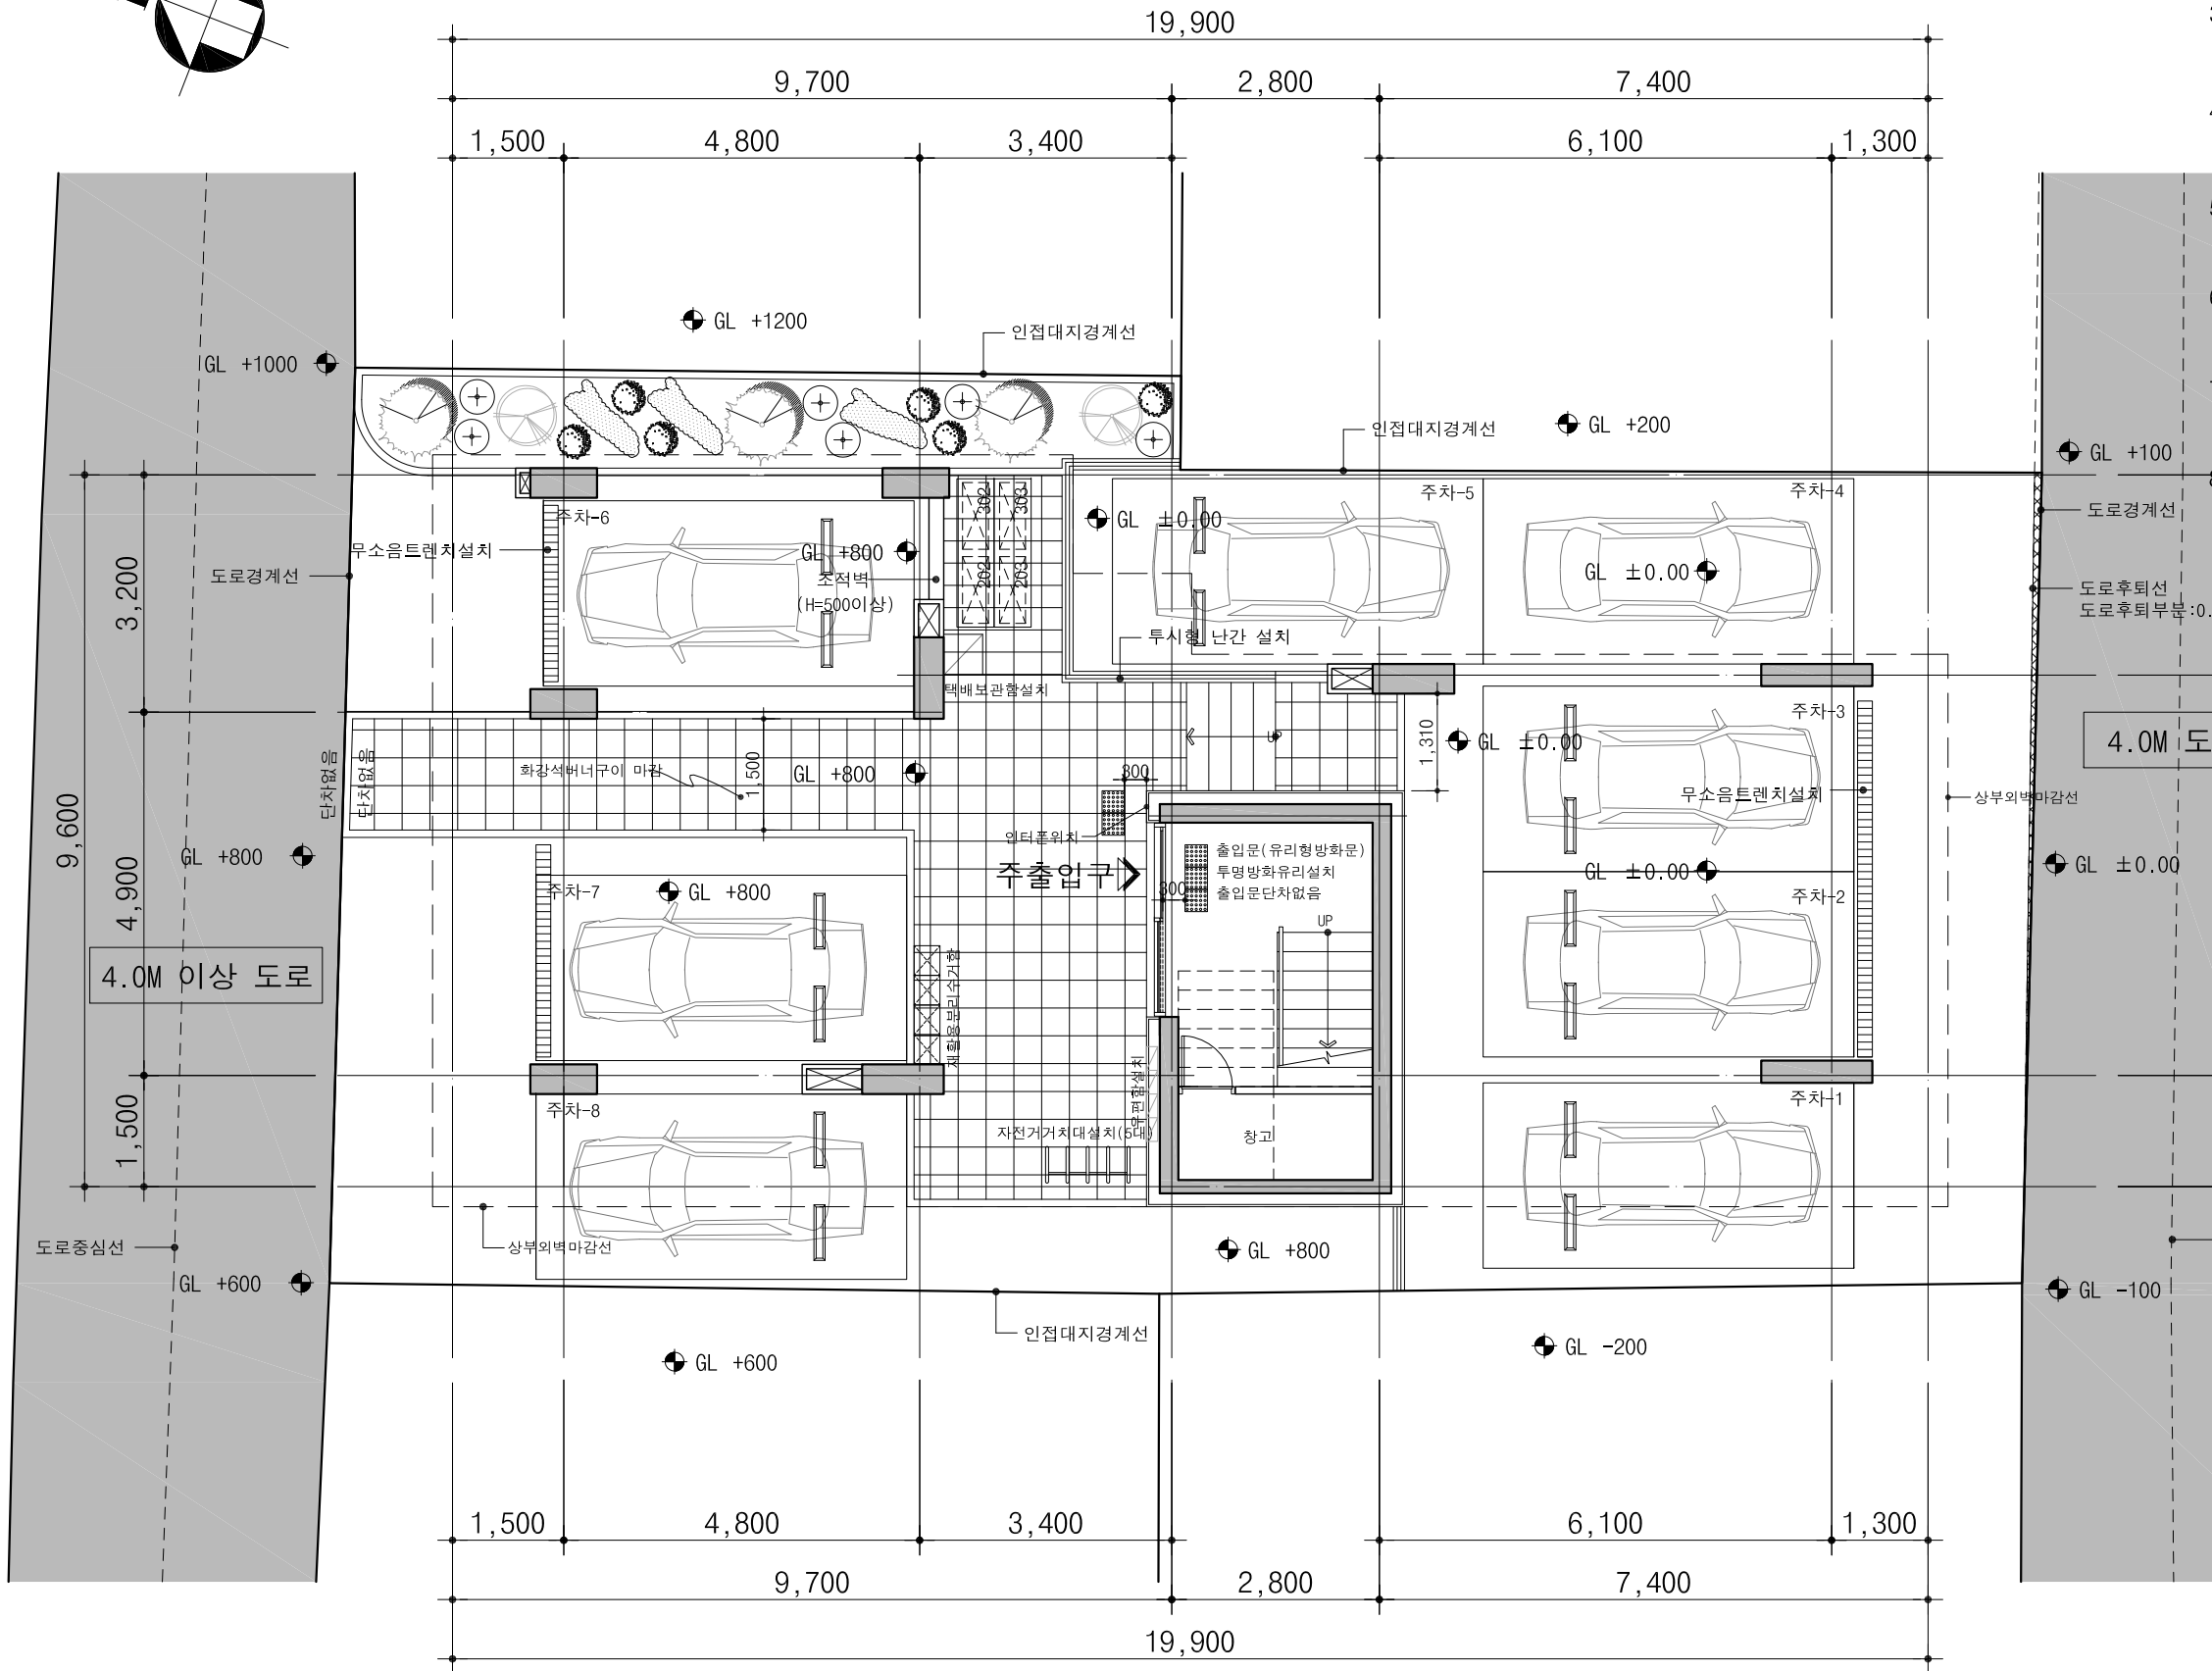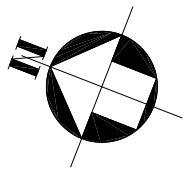

1 층 평 면 도

SCALE: 1/100

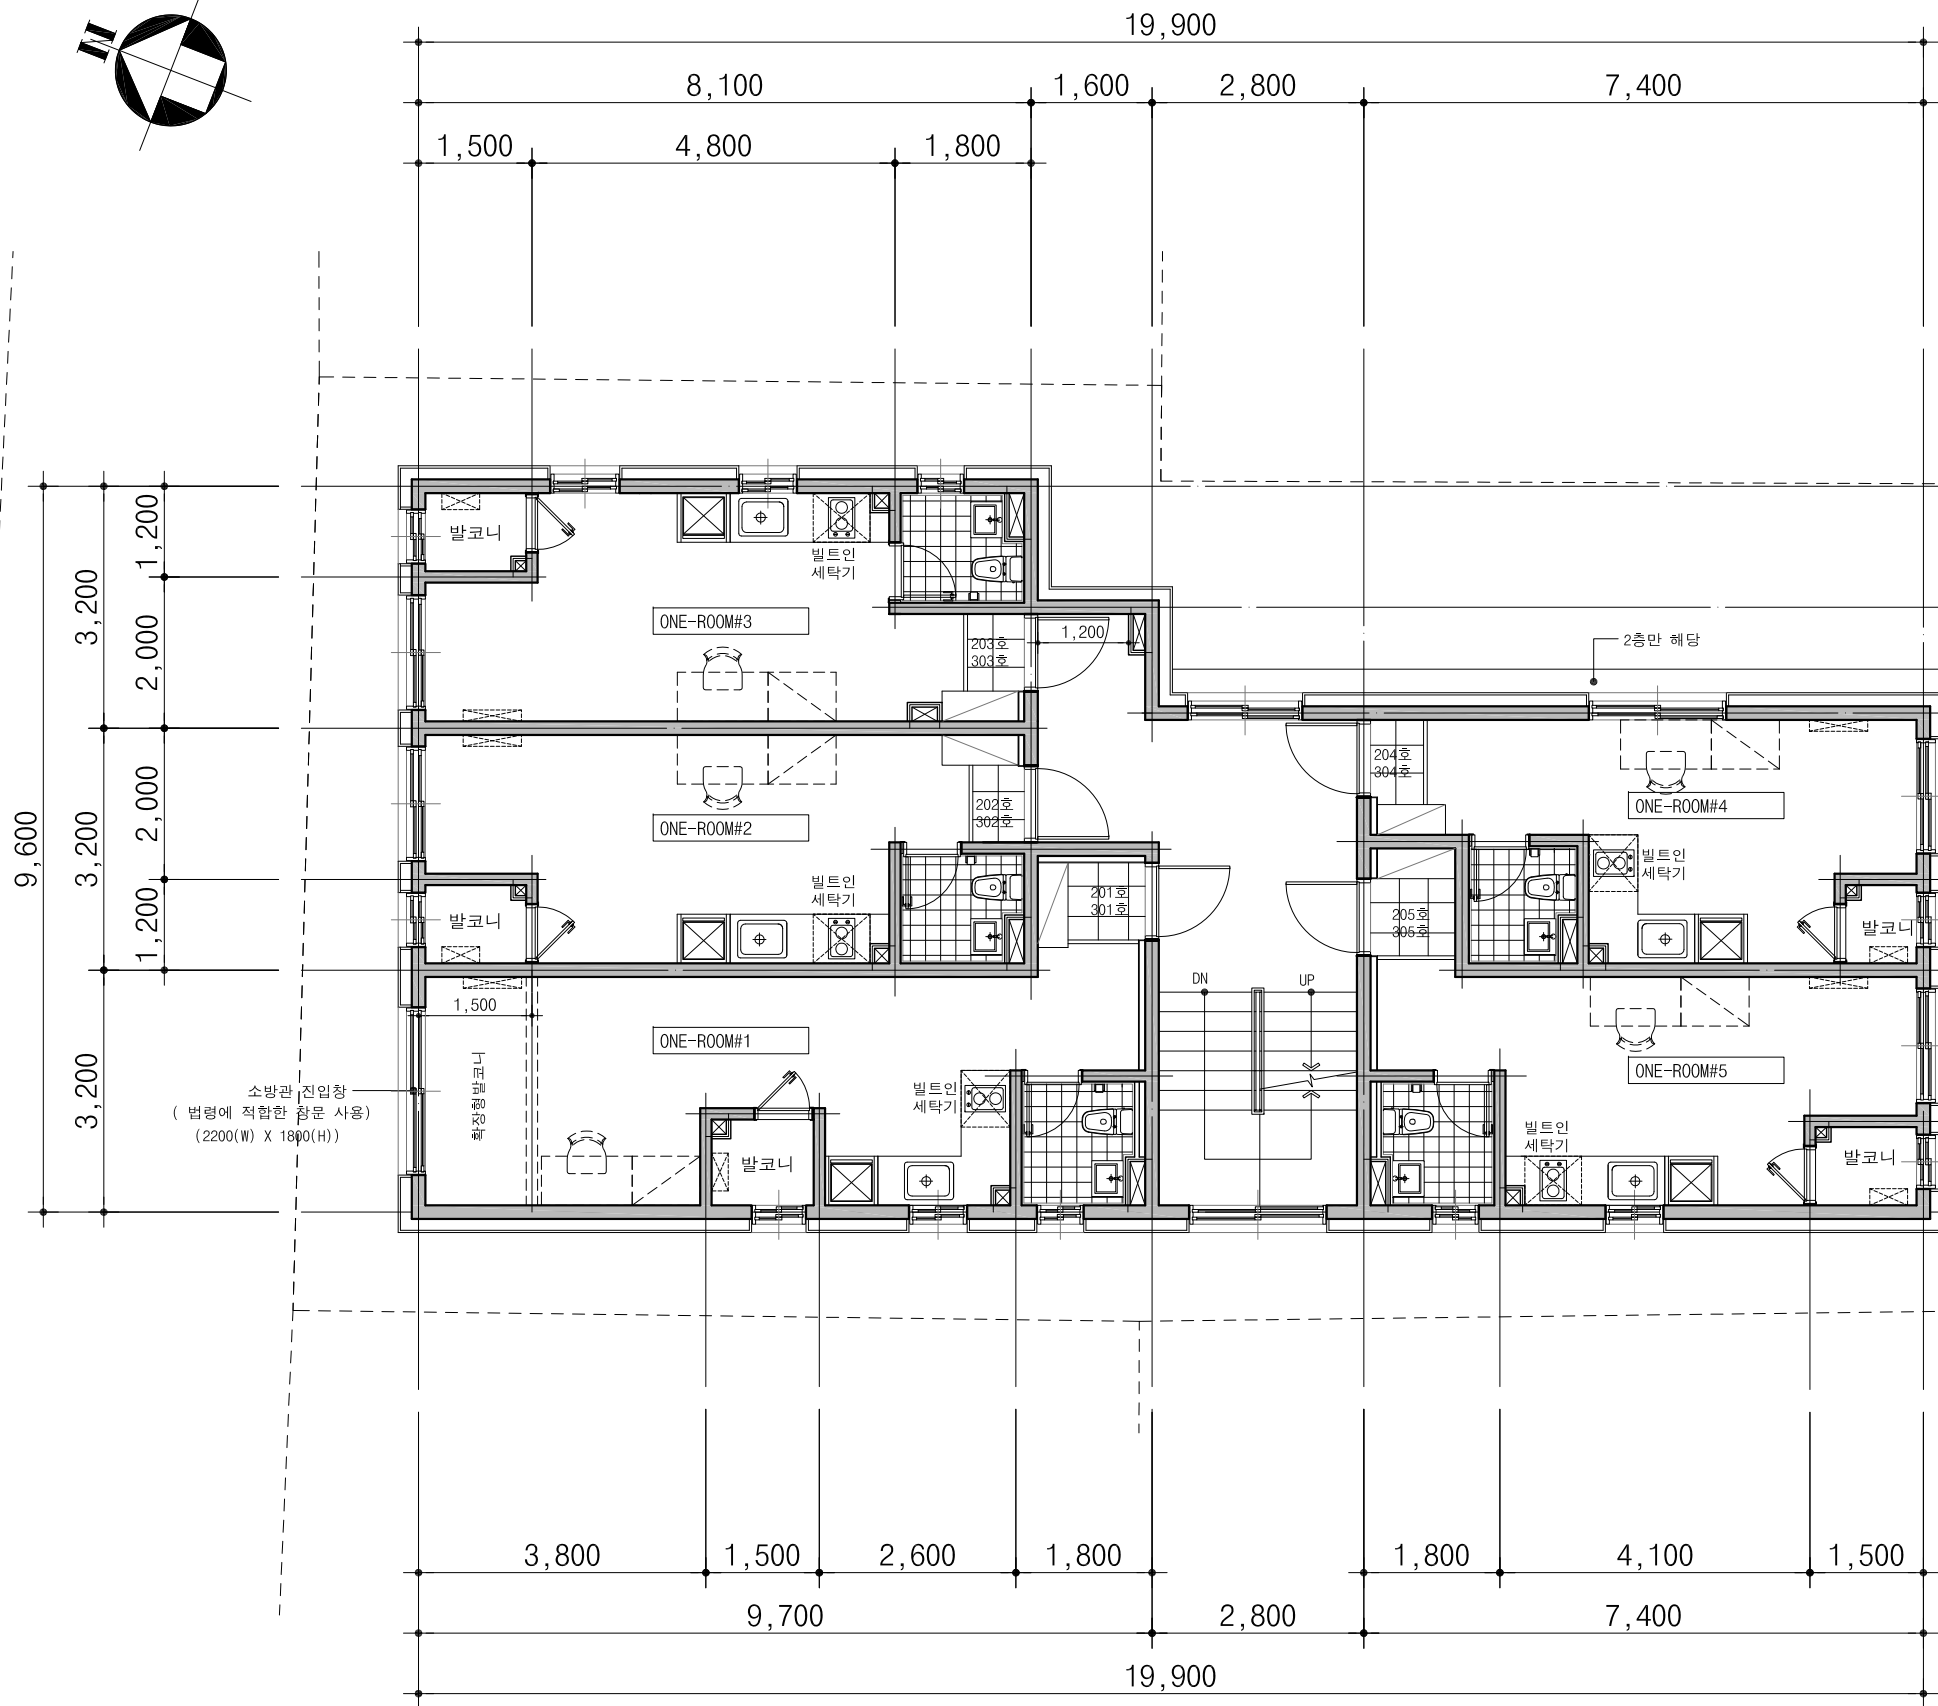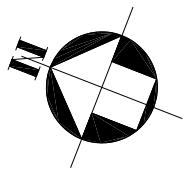



2 ~ 3 층 평 면 도
SCALE: 1/100

석고보드위벽지마감
T80경질우레탄폼2층2호
T180철근콘크리트벽

계단실

석고보드위벽지마감
T80경질우레탄폼2층2호
T180철근콘크리트벽

외기공간
경질우레탄폼

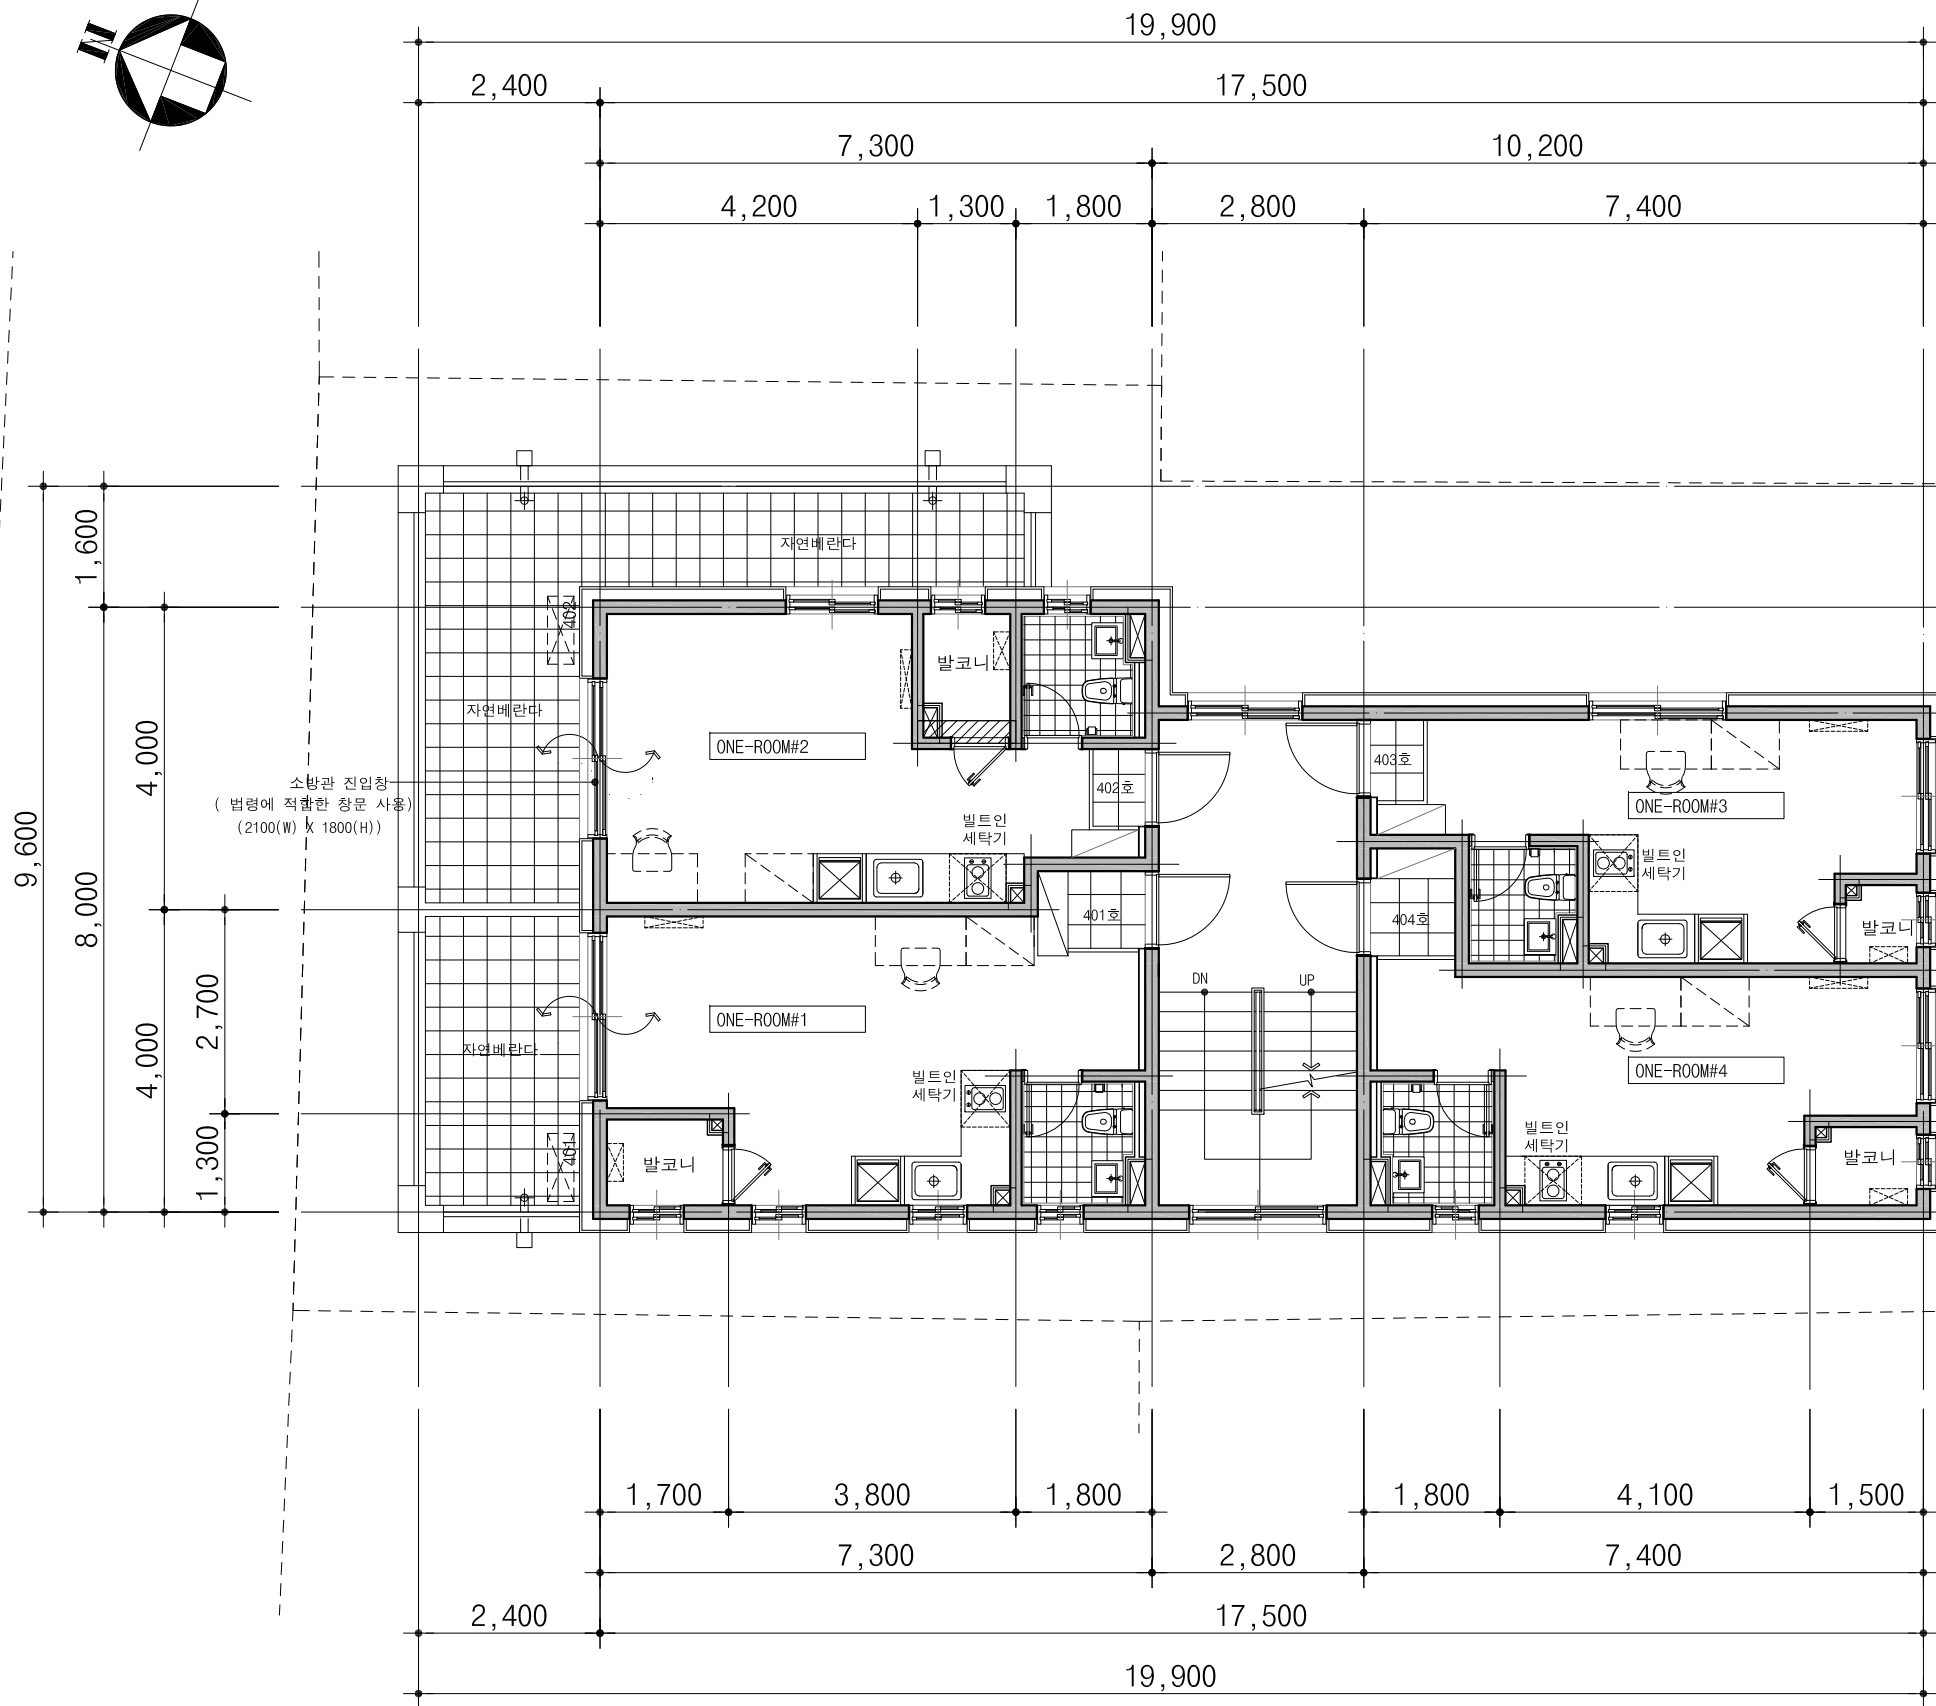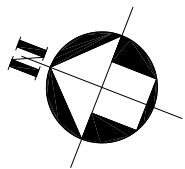



4 층 평 면 도
SCALE: 1/100

석고보드위벽지마감
T80경질우레탄폼2층2호
T180철근콘크리트벽

계단실

석고보드위벽지마감
T80경질우레탄폼2층2호
T180철근콘크리트벽

외기예간
경질우레탄폼

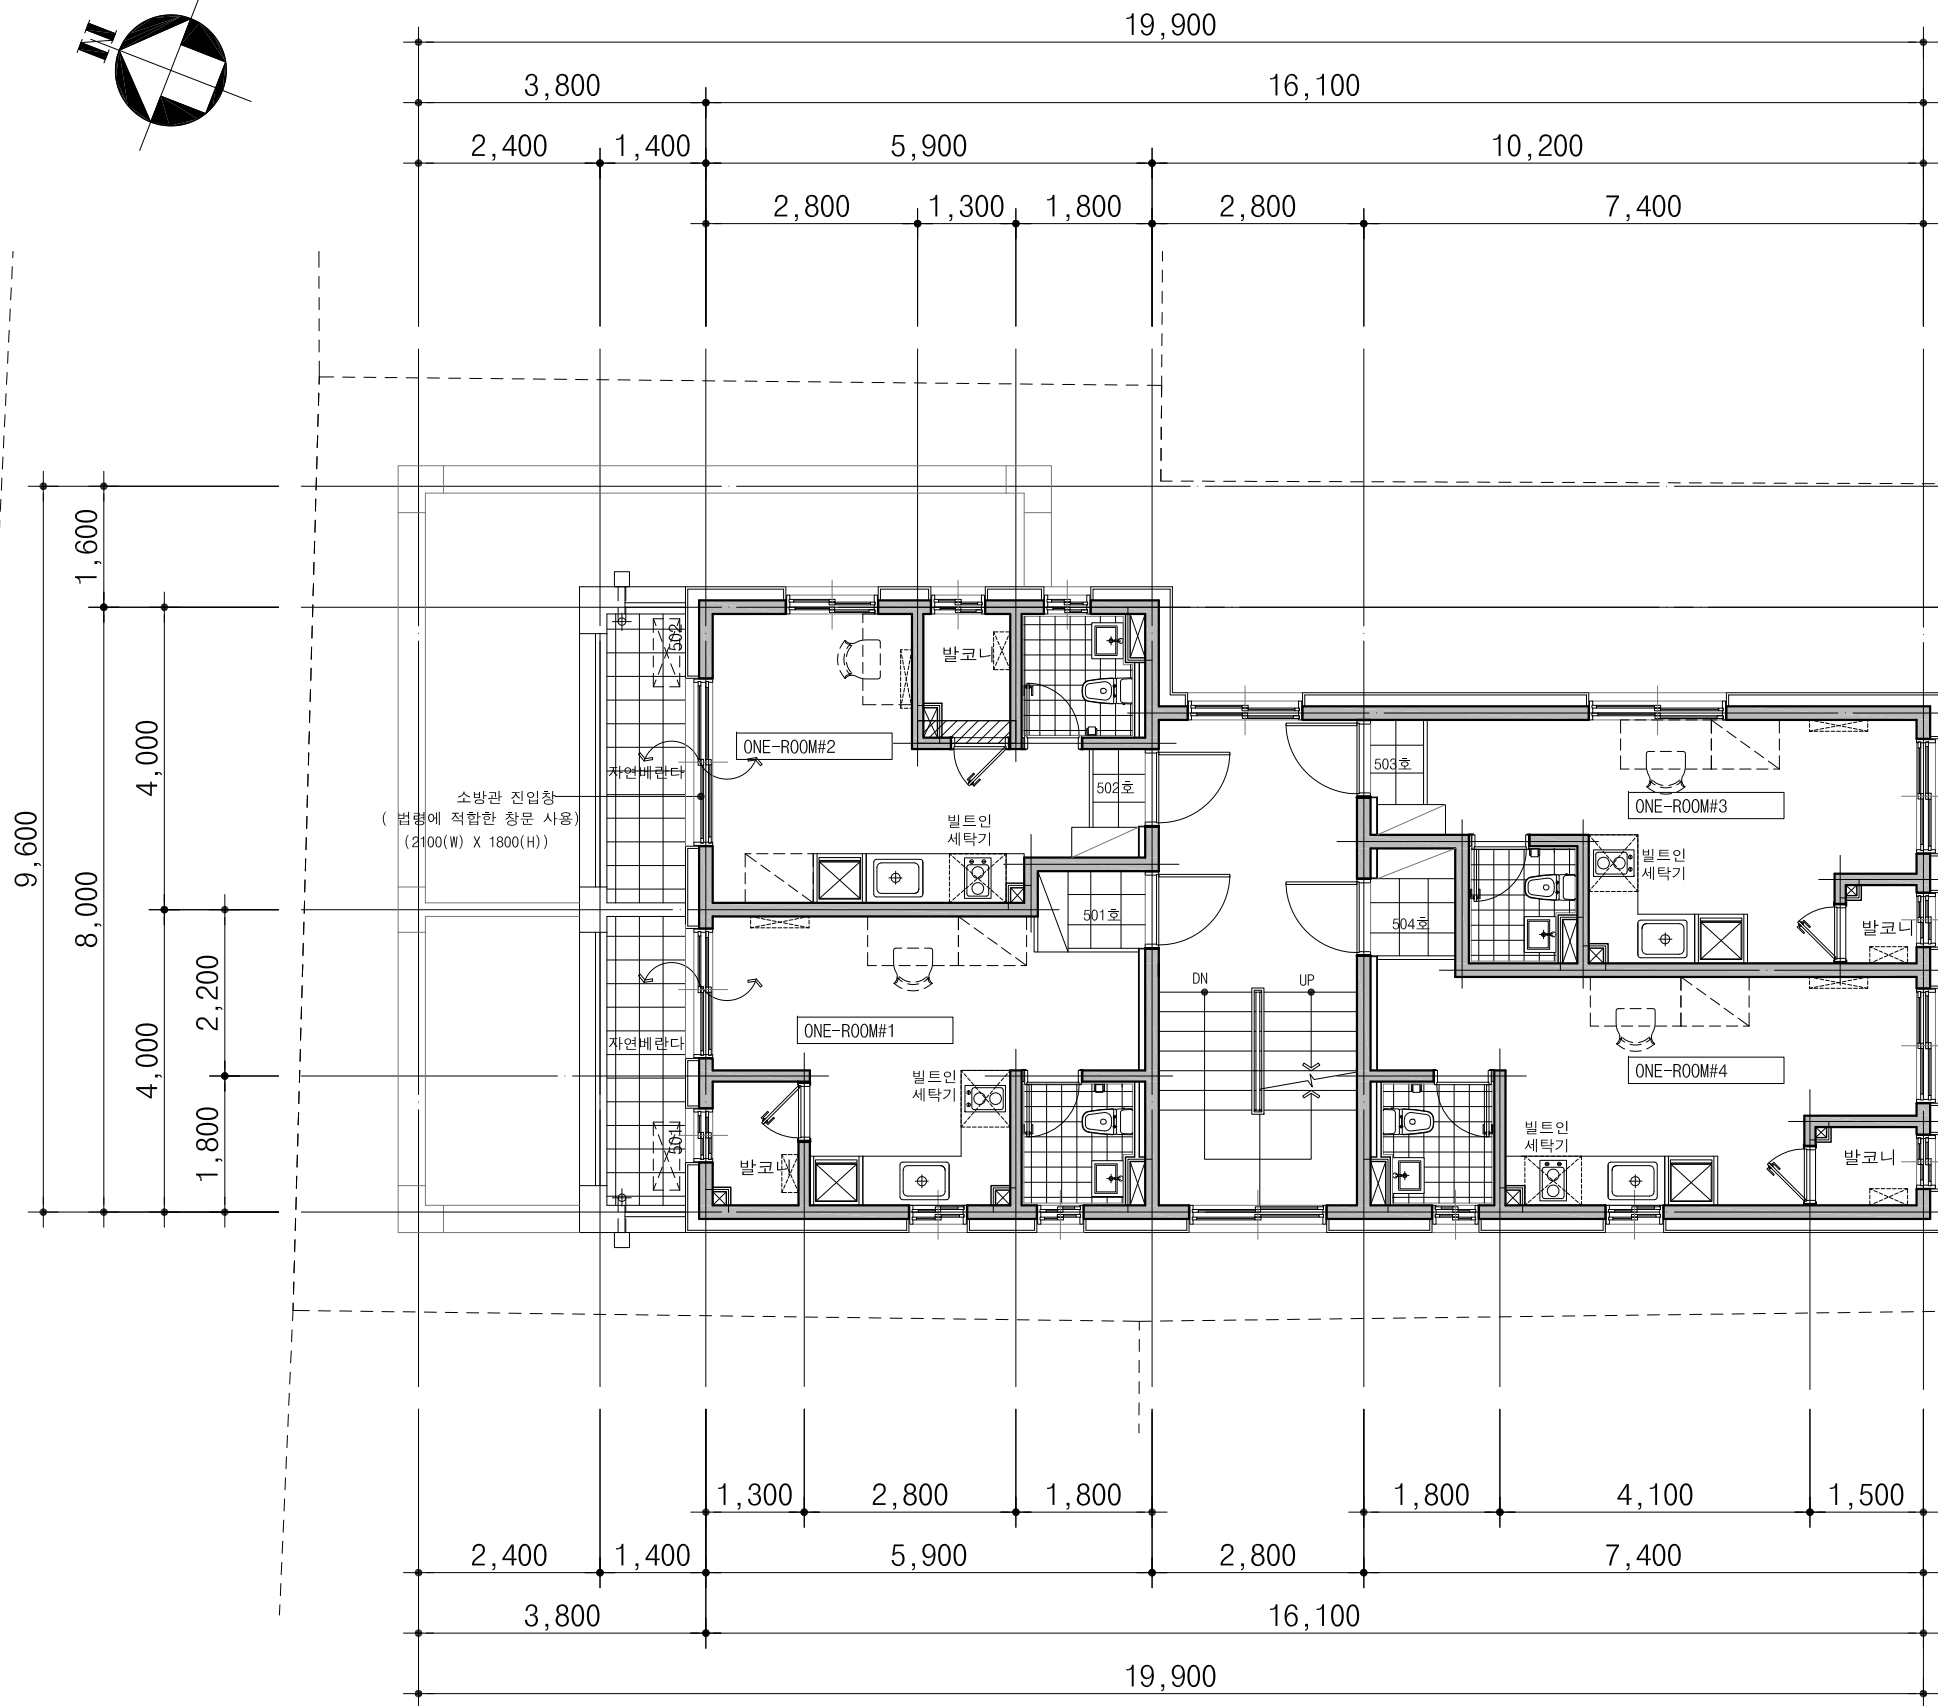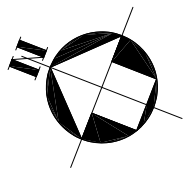


5 층 평 면 도
SCALE: 1/100

석고보드위벽지마감
T80경질우레탄폼2층2호
T180철근콘크리트벽

계단실


석고보드위벽지마감
T80경질우레탄폼2층2호
T180철근콘크리트벽

외기에간
경질우레탄폼

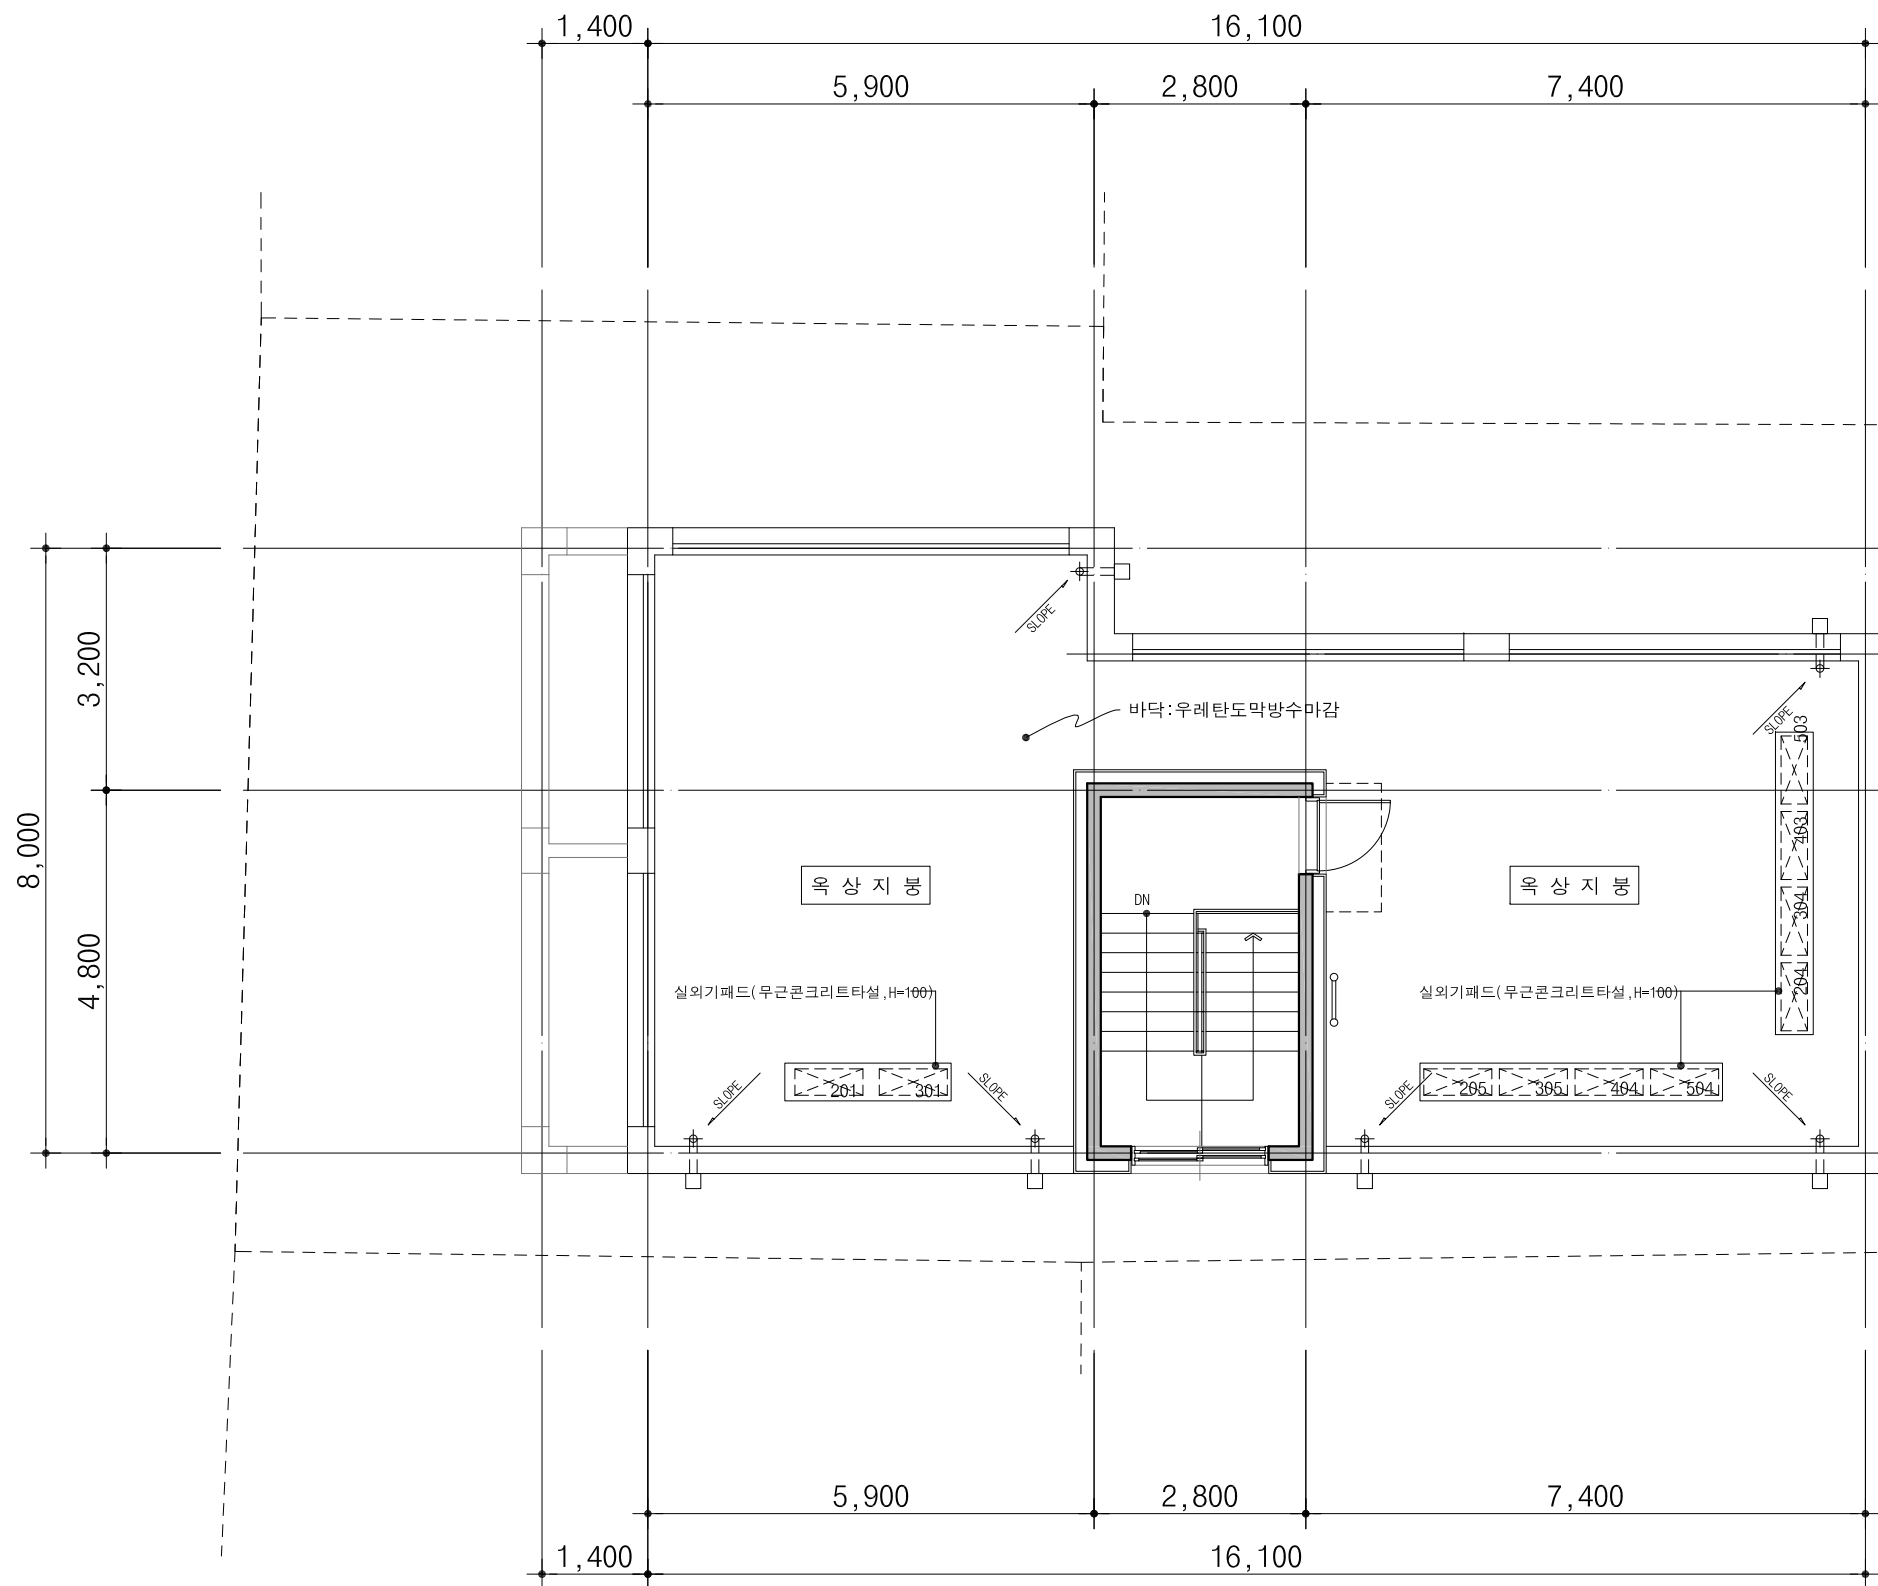


옥탑층 평면도

SCALE: 1/100

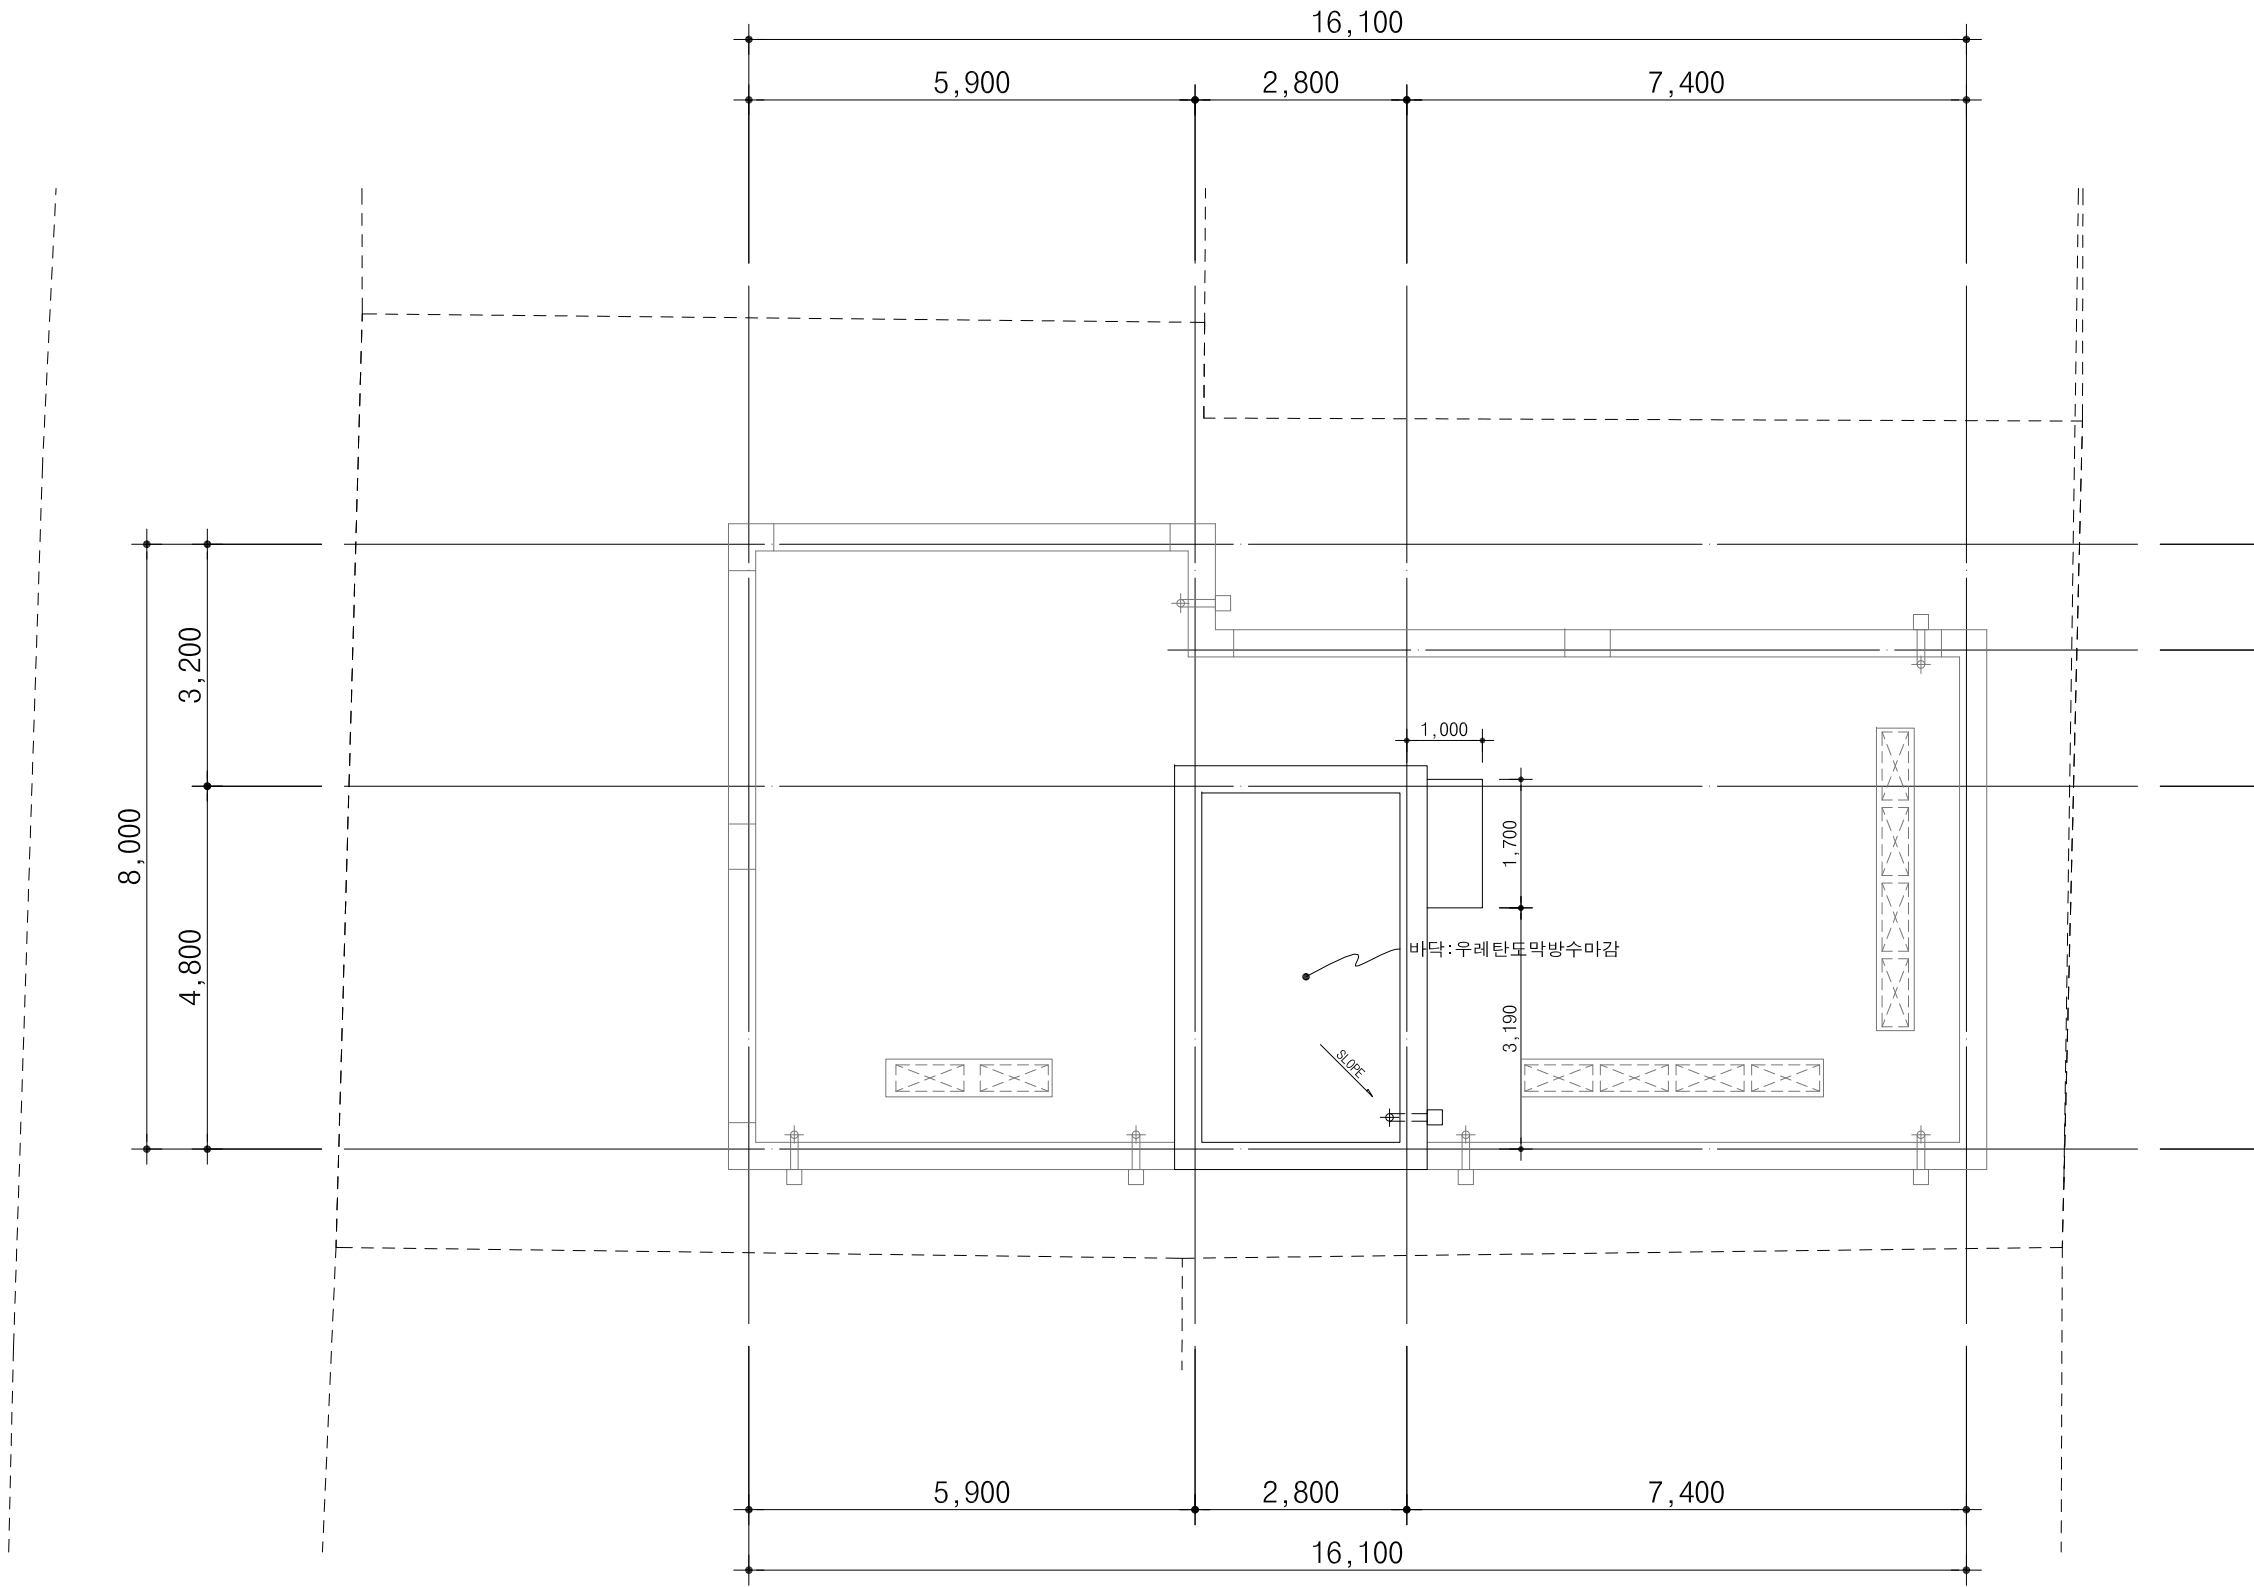

옥 탑 지 붕 평 면 도

SCALE: 1/100


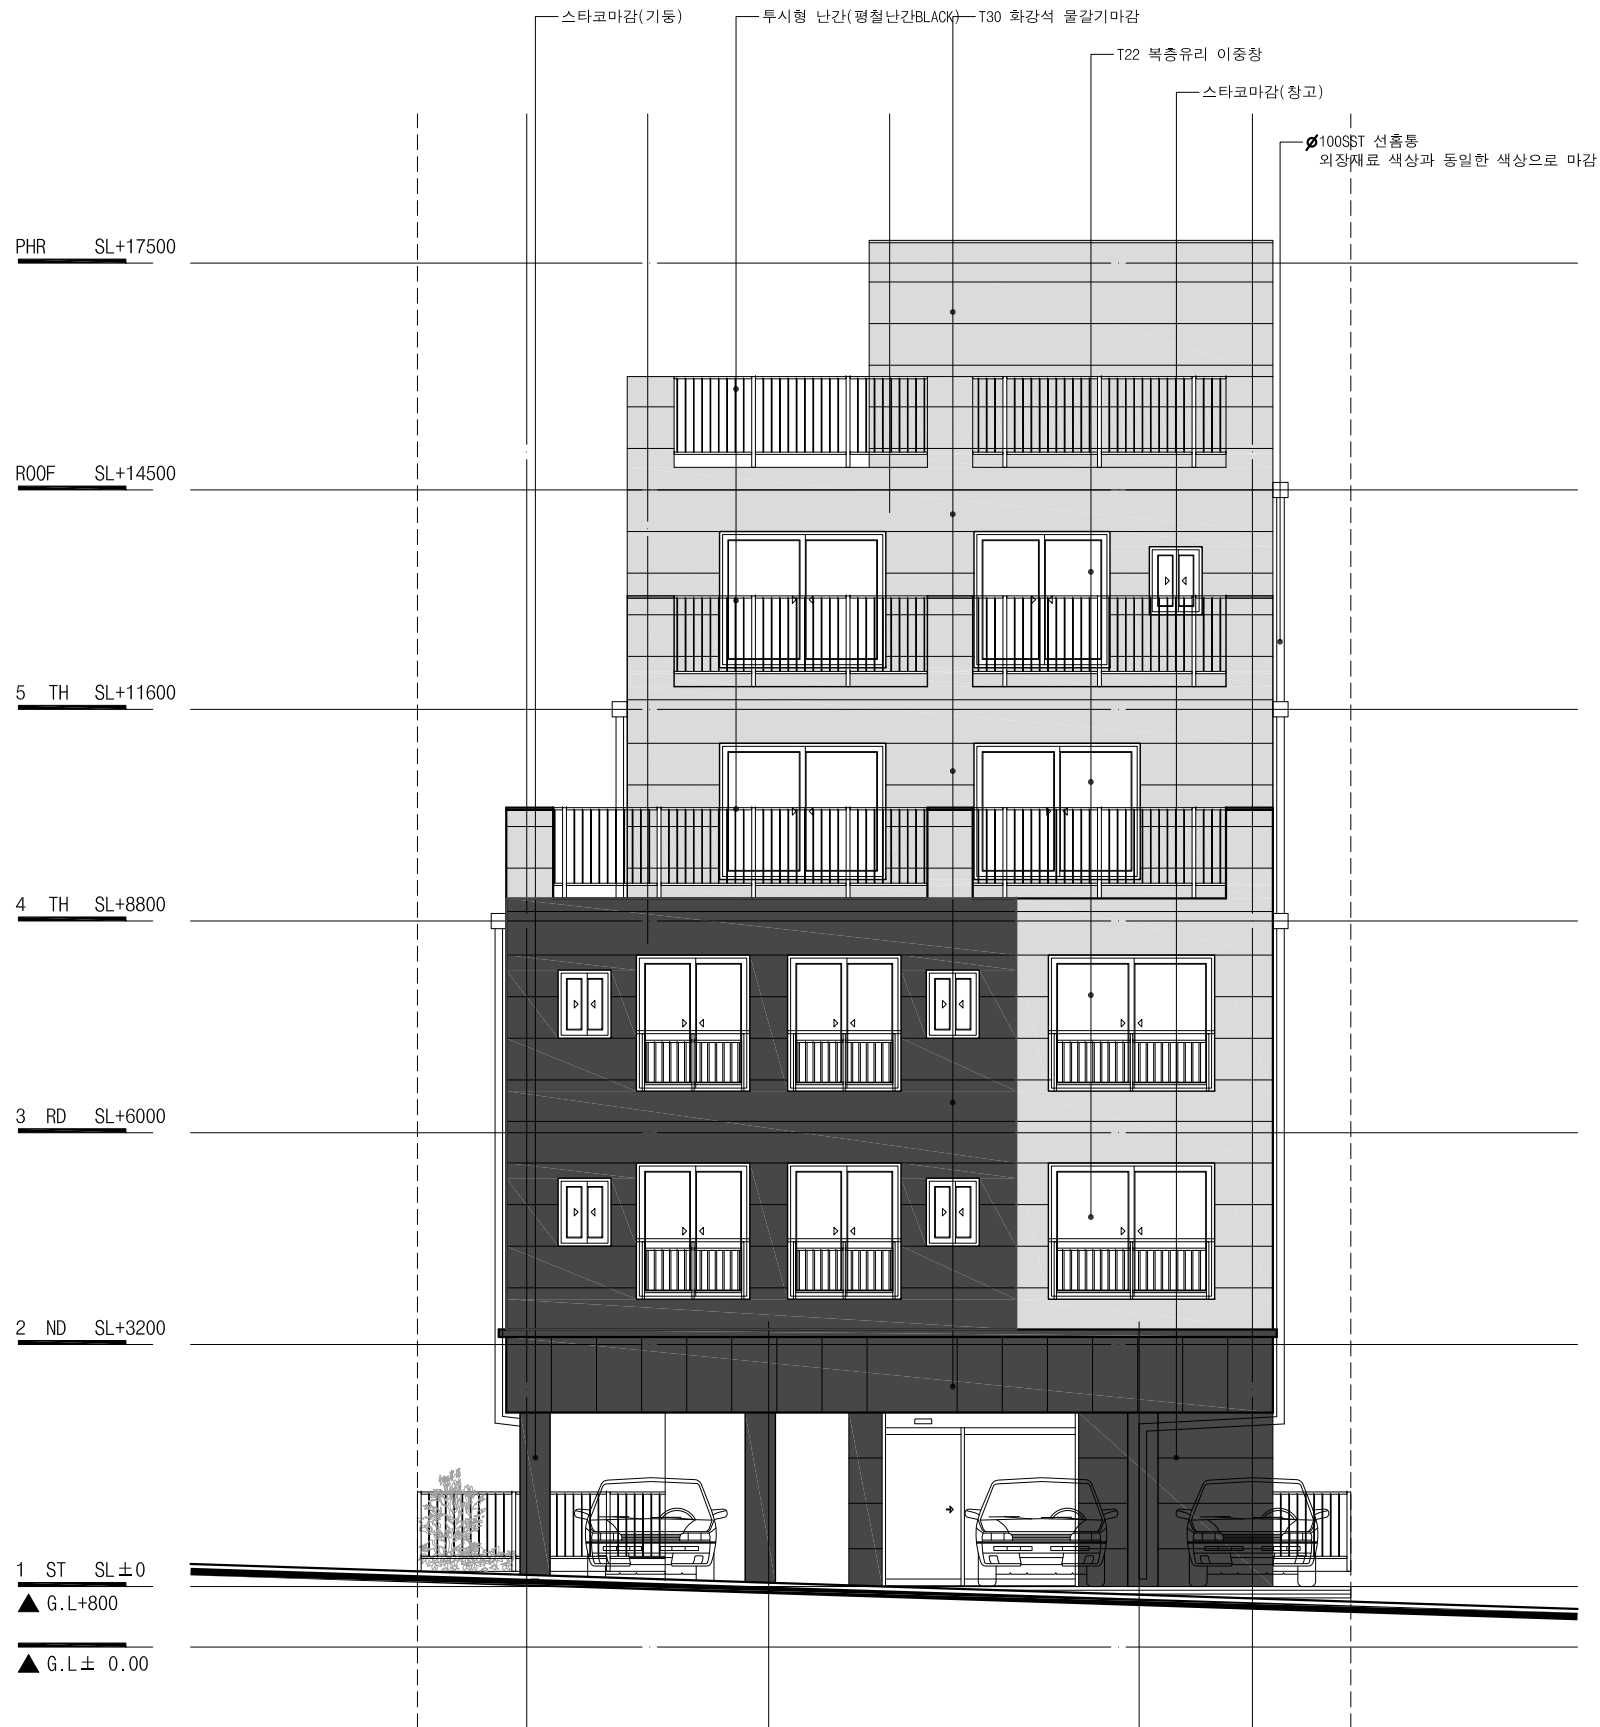


정 면 도
SCALE: 1/100



좌 측 면 도

SCALE: 1/100

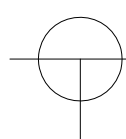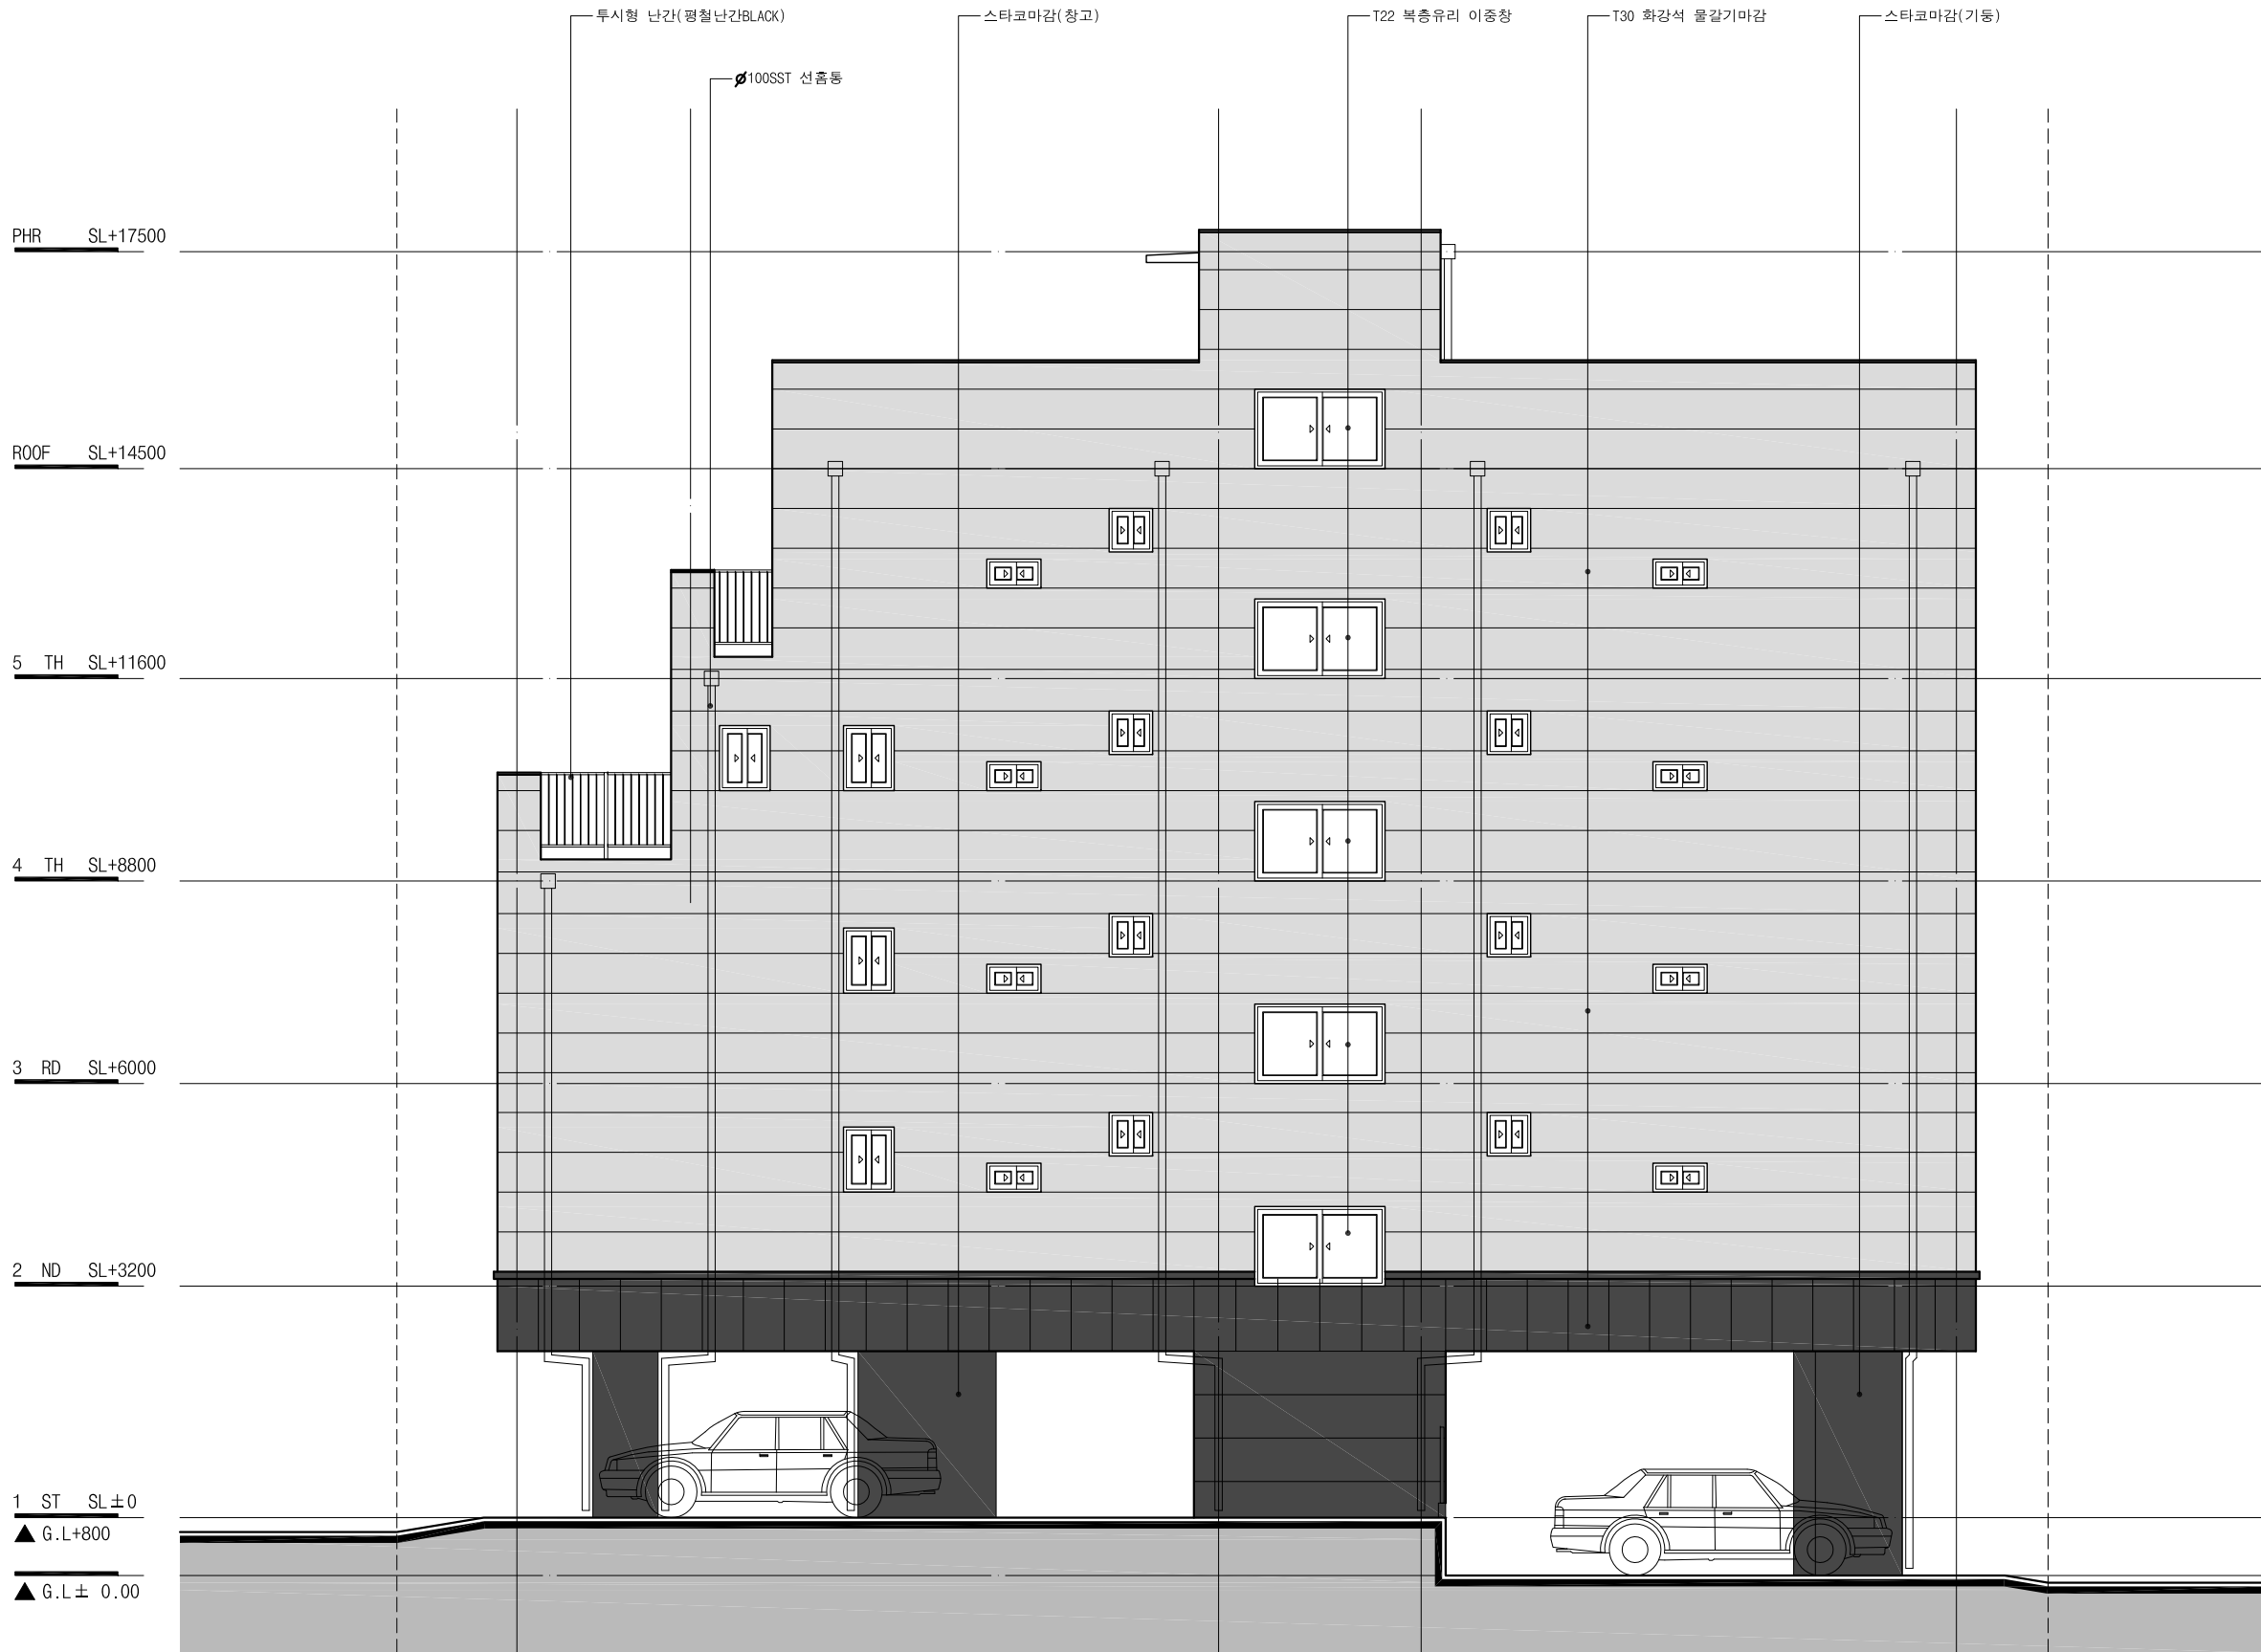

우 측 면 도

SCALE:1/100





【 본 건 전 경 】



【 주 변 전 경 】