

1. 조감도




1. 투 시 도



2. 건축개요 및 현황도

건축개요

설 계 명 : 구로구 공동 190-84번지 외 1필지
도시형생활주택 (원룸형) 청년주택 신축공사
대지위치 : 서울특별시 구로구 공동 190 - 84 번지 외 1 필지
지역지구 : 제2종 일반주거지역 (7층이하)
건물용도 : 도시형 생활 주택(원룸형)
건물규모 : 지하 0층, 지상 5층
대지면적 : 294.80 m²
건축면적 : 172.87 m²
연 면 적 : 588.86 m²
건 폐 율 : 58.64 %
용 적 륜 : 199.75 %
최고높이 : 16.10 M
구 조 : 철근콘크리트조
주차대수 : 법정 6대, 계획 7대
조경면적 : 16.57 m²

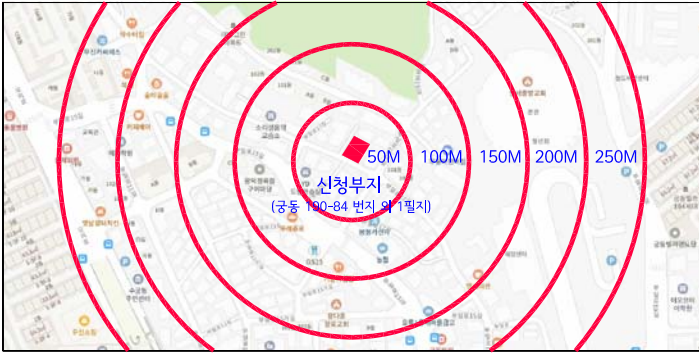

위 치 도



주변현황도

3. 입 면 도



정 면 도



좌 측 면 도




우 측 면 도



배 면 도

4. 설계자 의도

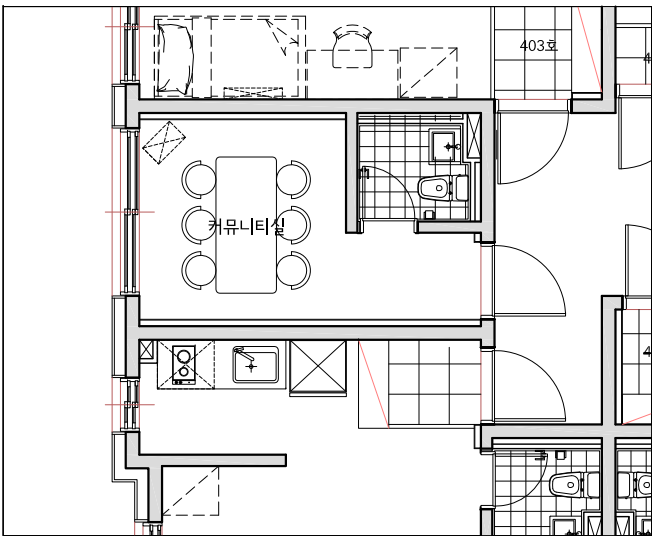


- 주민편의시설로 커뮤니티실을 설치
1인가족이 많은 원룸형주택에 소외받는 주민이 없도록
이웃간 소통할수 있는 공간을 제공



- 공간 예상 이미지

- 화강석 (상부외벽)
웅장하고 고급스러운 외관에
열은색으로 깨끗함을 더함
- 화강석 (하부외벽)
웅장하고 고급스러운 외관에
짙은색으로 무게감을 더함
- 화강석 (포인트외벽)
웅장하고 고급스러운 외관에
열은색과 짙은색 사이에 강조되어
고급스러움을 더함
- 금속 (난간,창틀,갈바룸)
깔끔한 색채와 소재로 건물의
모던함을 강조함

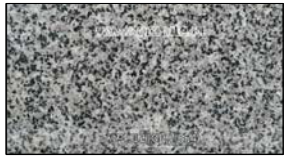


- 거실, 방(바닥)
데코타일



- 거실, 방(벽)
벽지



- 화장실, 욕실
Tile(Non-slip)

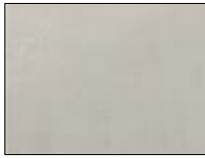


- 계단실
수성페인트/타일
/무늬텍스



5. 재료계획



- 바닥 : 데코타일 마감
벽 : 천연실크 벽지마감

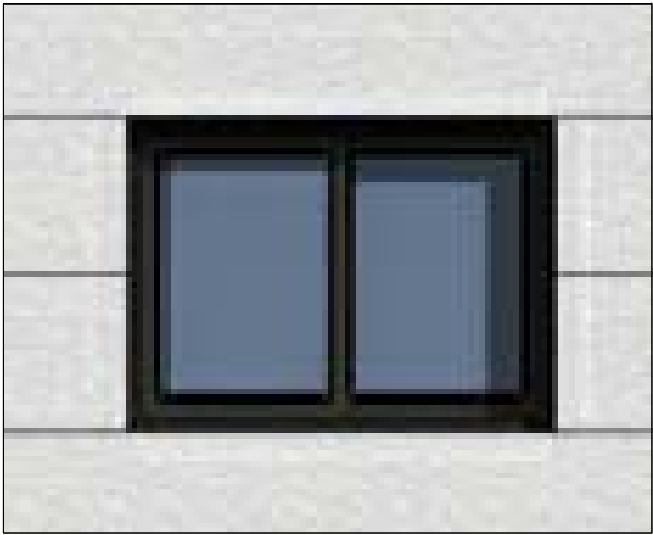

- 화강석 : 진 주 회

■ 내장재

■ 외장재

6. 색채계획

. 구조색 / 보조색

진 주 회




샤먼그레이



버터플라이화이트



- 주변과 조화를 이루는 고명도의 무채색 및 저채도 계열색상으로 도시적이면서 모던한 색채를 연출

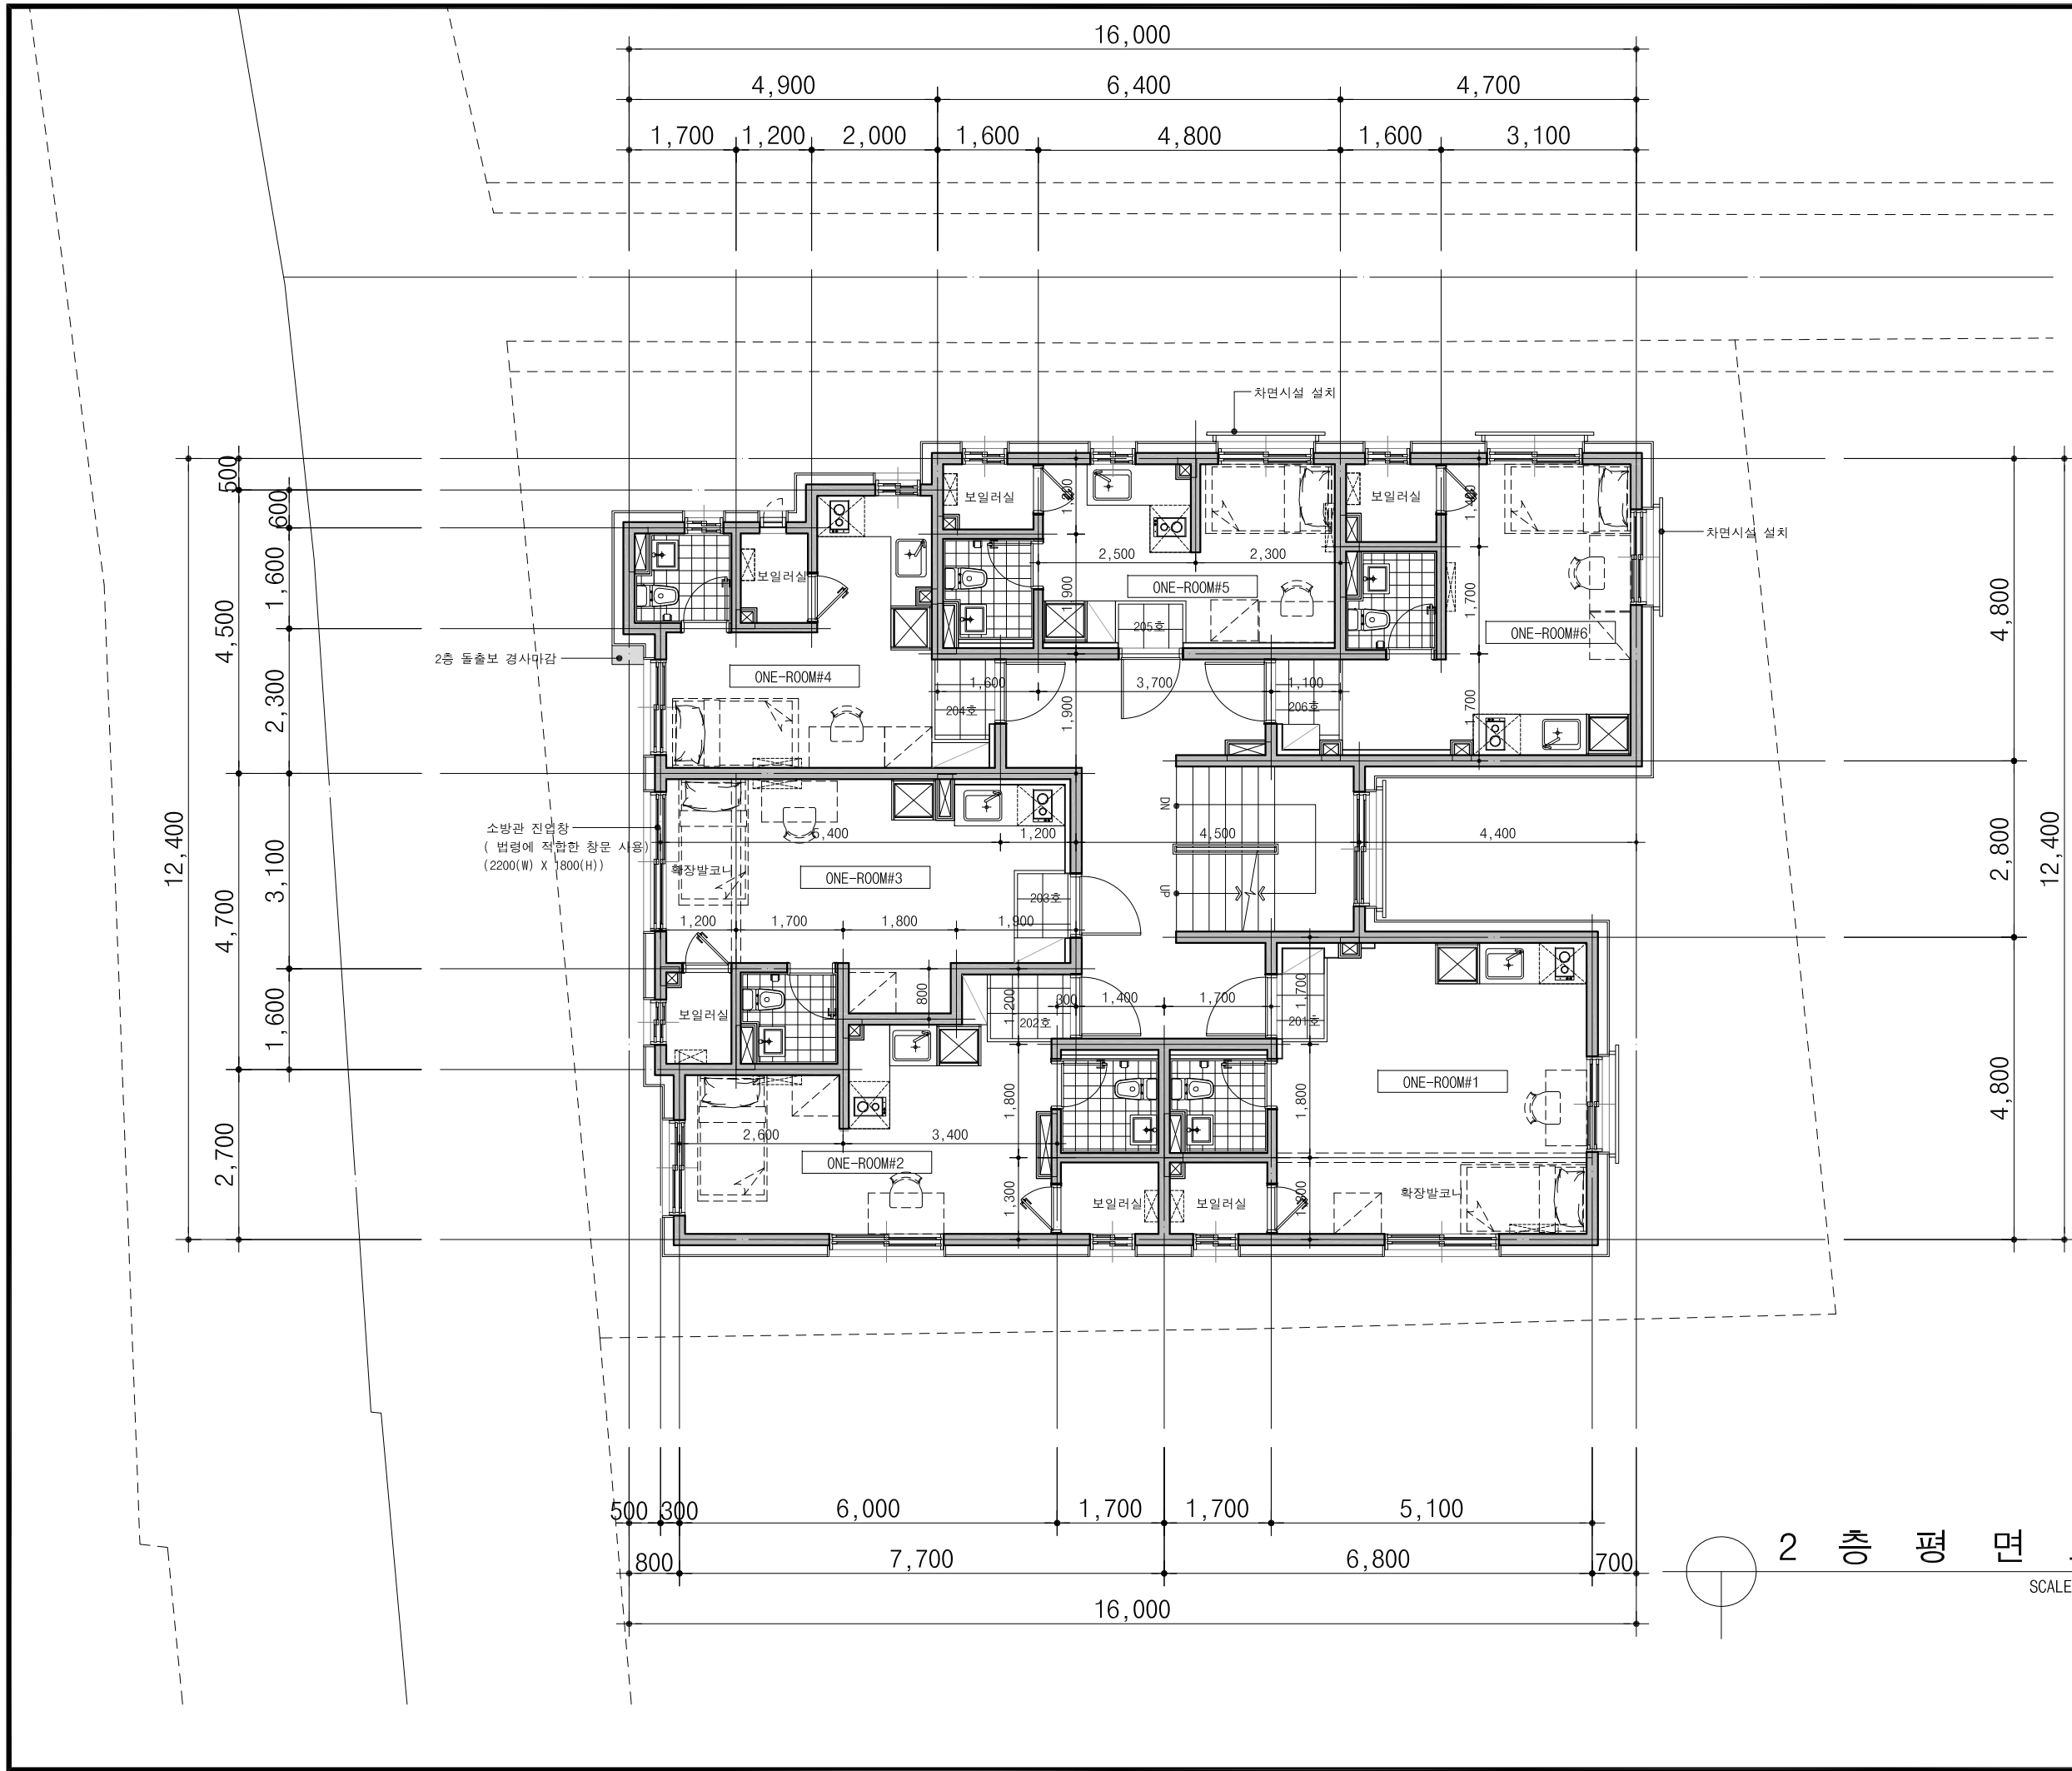


2 층 평 면 도
SCALE: 1/100

주 기		
1	세대	현관문 도어체크 및 스토퍼 계획
2	세대	발코니 설치시 세대간 분리벽 계획
3	세대내	비디오폰 설치
4	주차장내	CCTV 설치
5	벽체	외벽 직접 외기에 면한 실내벽면은 단열재 (아이소핑크10mm+석고보드 마감도면 표기) 계단실 간접 외기에 면한 실내벽면은 단열재 /복도 (경질우레탄80mm+석고보드 마감도면 표기)
6	에어콘	실외기 설치위치 및 에어컨 도면표기)
7	불박이	가구 내부 다용도 수납가능토록 수평이동 칸막이 설치
8	콘크리트	폼타이 제거후 마감공사 시공(방수 및 단열재 시공등)
9	구조	콘크리트 : fck=24Mpa 철근 : fy=400Mpa 세대 벽두께 : 150mm(복배근) 외벽 벽두께 : 180mm(복배근) 코아 벽두께 : 180mm(복배근) 2층 슬라브 두께 : 180mm(복배근) 3-5층 슬라브 두께 : 210mm(복배근)
10	기타	실내 벽면은 시멘트 미장마감
11	욕실 & 다용도실	스위치 : 문열리는 방향으로 시공
12	공동주택	바닥충격을 차단구조기준
2층		
13	소방관	진입창의 기준 건축물의 피난방화구조등의 기준에 관한규칙 제18조의2에 의거 1. 2층이상 11층이하인 층에 각각 1개소 이상설치 2. 소방차진입로또는 소방차 진입이 가능한 공터에 면할것 3. 창문 가운데 Ø200이상의 역삼각형을 아간에 식별가능하도록 설치.(반사 등으로 붉은색으로 표시) 4. 창문 한쪽 모서리에 타격지점 표시 (Ø30 이상의 원형) 5. 창문크기 : 폭900 높이1,200이상 (바닥에서 창아랫부분 높이800이내로 설치) 6. 다음 각 목의 어느 하나에 해당하는 유리 사용할 것 가. 플로트판유리로서 두께6mm이하인것 나. 강화유리/배강도유리로서 두께5mm이하인것 다. 위의 유리로 구성된 이중유리로서 두께24mm 이하인것
14	외기에	간접면하는 부분 : THK80 경질우레탄폼 2중2호 설치

NOTE:

PROJECT 구로구 공동 190-84번지 외1필지 도시형 생활주택 (원룸형)신축공사			
APPROVED BY 건축사 구 연 목			
건축사사무소 유일엔지니어링 서울특별시 서초구 반포대로 14길 71(서초동) LG서초에클리트(1904호) TEL : 02) 540-1546, FAX : 02)540-1576			
TITLE 2 층 평 면 도			
날짜 DATE: 2021. 08. .			
SCALE	1 / 100	DWG NO.	A - 009
		REV.	

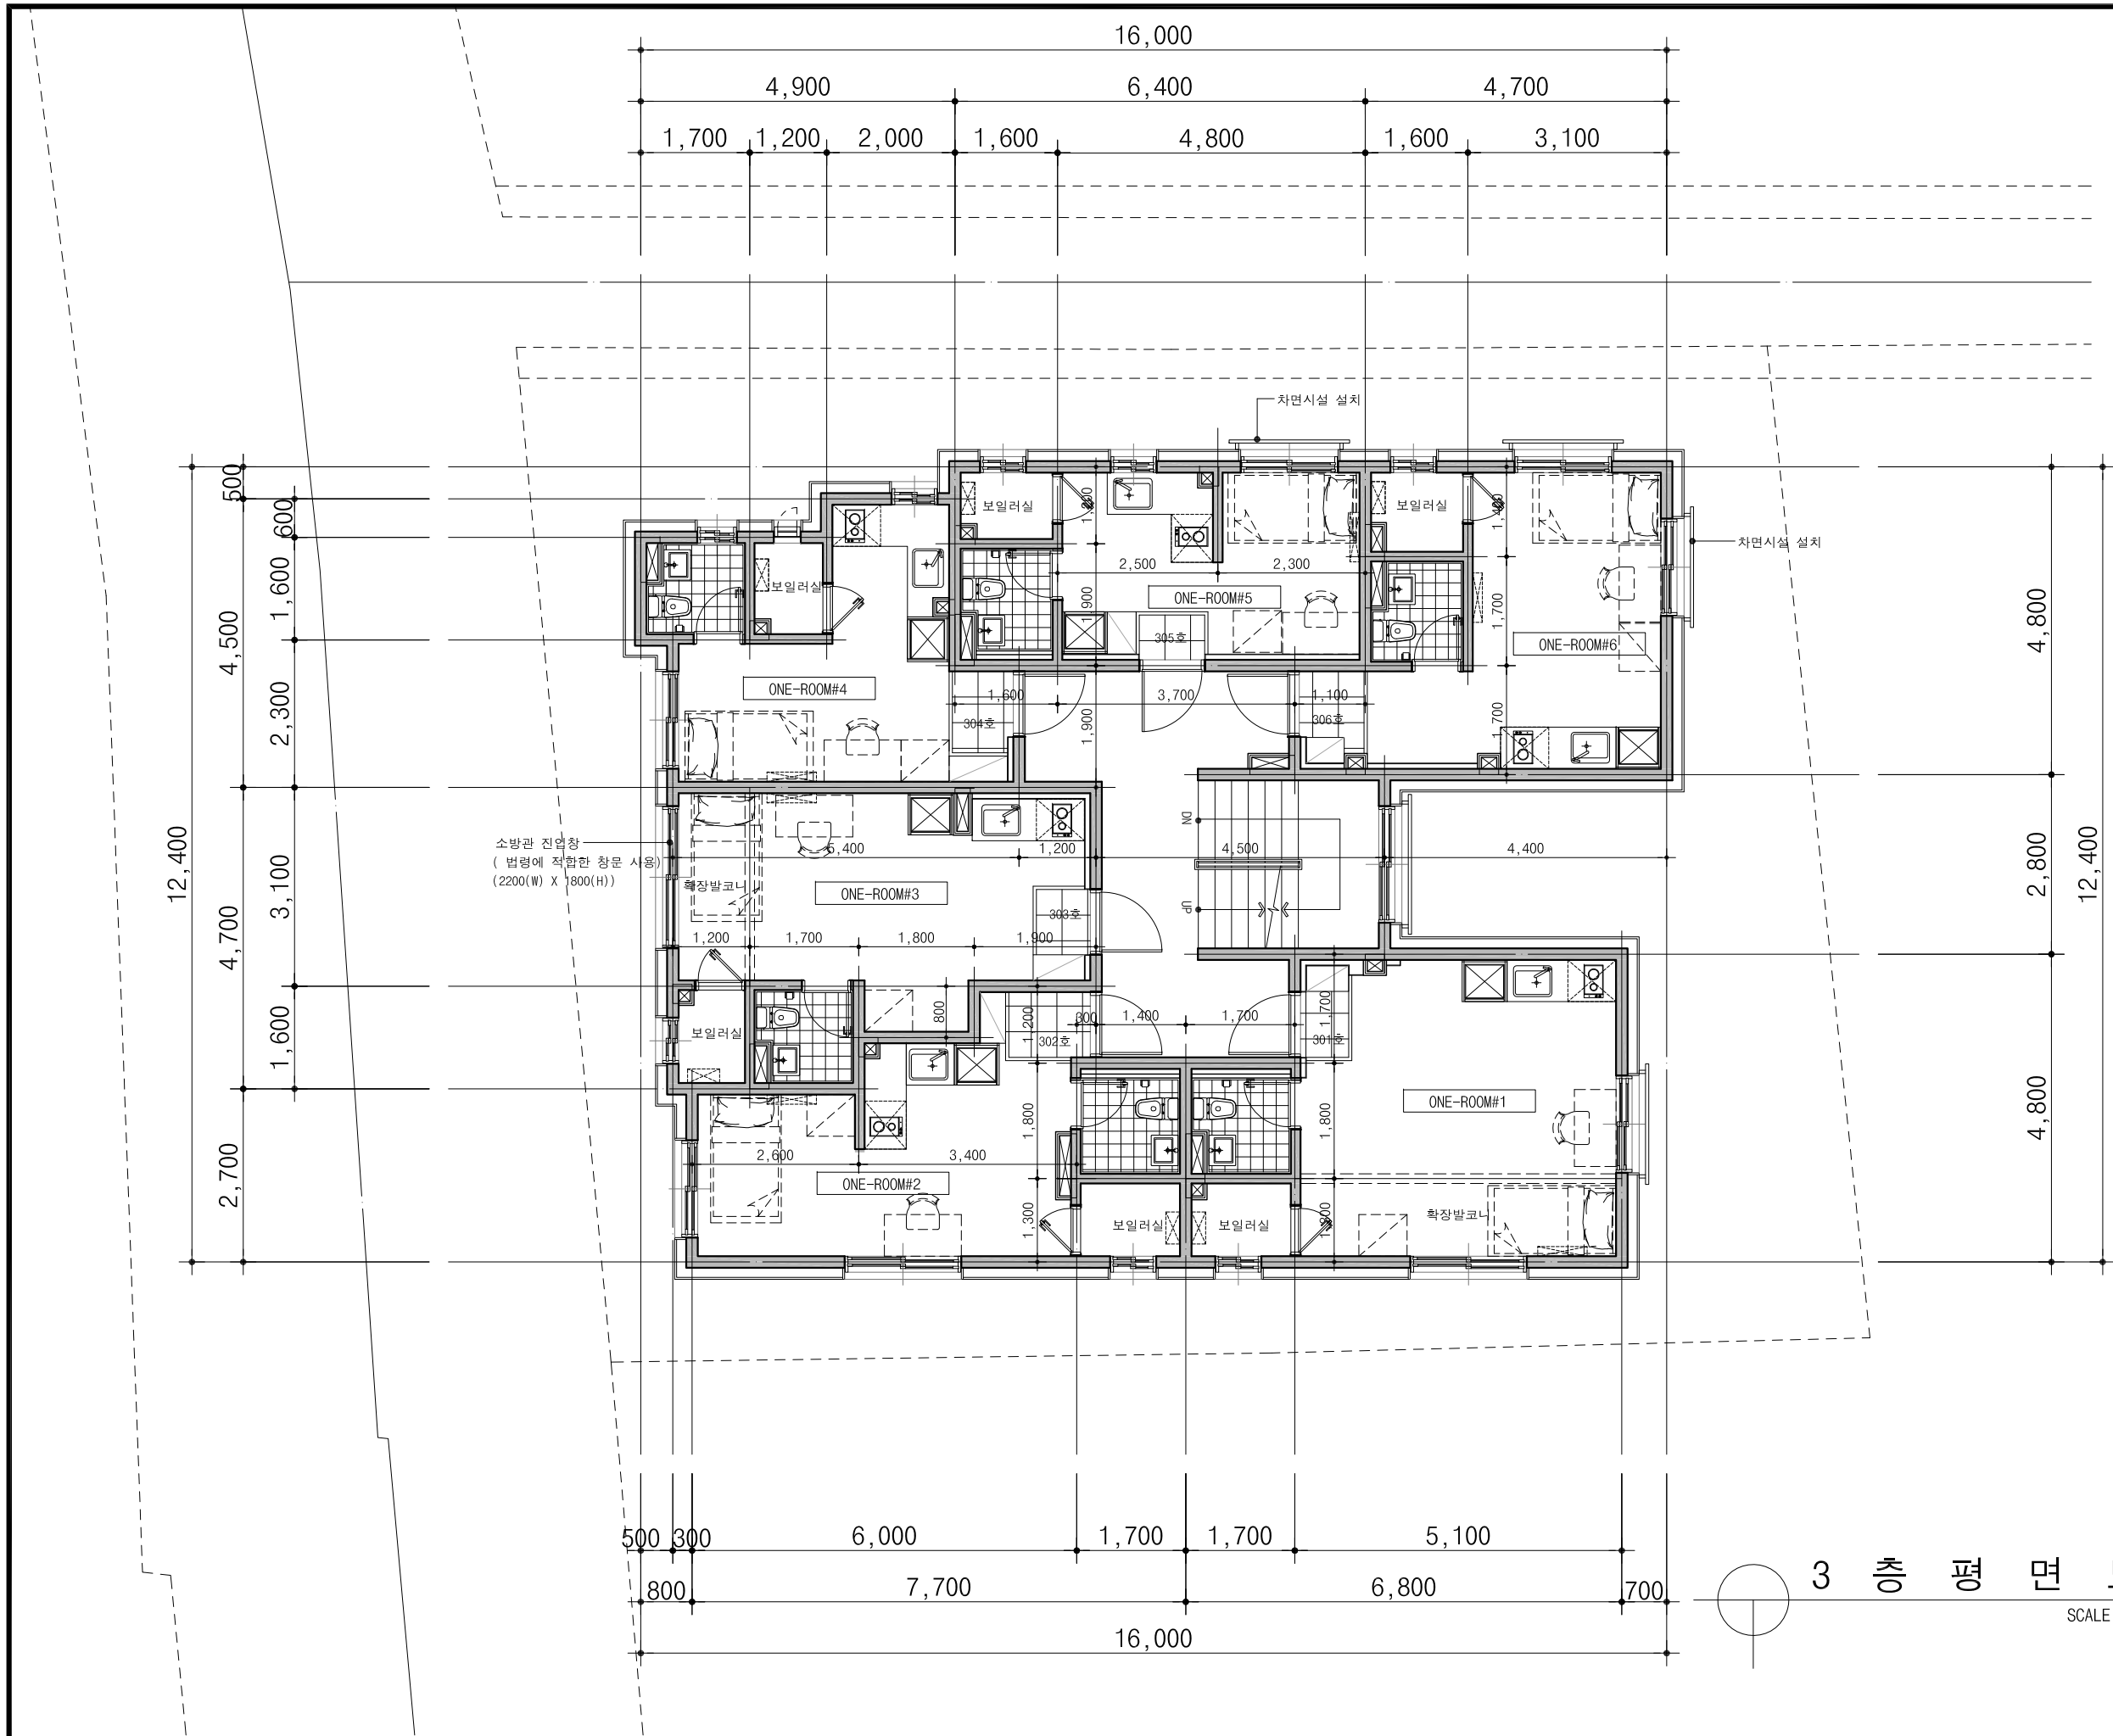

3 층 평 면 도
SCALE: 1/100

주 기		
1	세대 현관문 도어체크 및 스토퍼 계획	
2	세대 발코니 설치시 세대간 분리벽 계획	
3	세대내 비디오폰 설치	
4	주차장내 CCTV 설치	
5	벽체	외벽 직접 외기에 면한 실내벽면은 단열재 (아이소핑크10mm+석고보드 마감도면 표기) 계단실 간접 외기에 면한 실내벽면은 단열재 /복도 (경질우레탄80mm+석고보드 마감도면 표기)
6	에어콘 실외기 설치위치 및 에어콘 도면표기)	
7	불박이 가구 내부 다용도 수납가능토록 수평이동 칸막이 설치	
8	콘크리트 폼타이 제거후 마감공사 시공(방수 및 단열재 시공등)	
9	구조	콘크리트 : fck=24Mpa 철근 : fy=400Mpa 세대 벽두께 : 150mm(복배근) 외벽 벽두께 : 180mm(복배근) 코아 벽두께 : 180mm(복배근) 2층 슬라브 두께 : 180mm(복배근) 3-5층 슬라브 두께 : 210mm(복배근)
10	기타 실내 벽면은 시멘트 미장마감	
11	욕실 & 다용도실 스위치 : 문열리는 방향으로 시공	
12	공동주택 바닥충격음 차단구조기준	
3층, 4층, 5층	결재말이(PVC) 데크타일마감(2.2T이상) T=40 시멘트몰탈(1:3, 평창채 혼입) T=40 경질우레탄폼콘크리트 T≤30 완충재(EPS게셀) T≤10 콘크리트슬라브	
13	소방관 진입창의 기준 건축물의 피난방화구조등의 기준에 관한규칙 제18조의2에 의거 1. 2층이상 11층이하인 층에 각각 1개소 이상설치 2. 소방차진입로또는 소방차 진입이 가능한 공터에 면할것 3. 창문 가운데 Ø200이상의 역삼각형을 아간에 식별가능하도록 설치.(반사 등으로 붉은색으로 표시) 4. 창문 한쪽 모서리에 타격지점 표시 (Ø30 이상의 원형) 5. 창문크기 : 폭900 높이1,200이상 (바닥에서 창아랫부분 높이800이내로 설치) 6. 다음 각 목의 어느 하나에 해당하는 유리 사용할 것 가. 플로트판유리로서 두께6mm이하인것 나. 강화유리/배강도유리로서 두께5mm이하인것 다. 위의 유리로 구성된 이중유리로서 두께24mm 이하인것	
14	외기에 간접면하는 부분 : THK80 경질우레탄폼 2중2호 설치 석고보드워벽지마감 T80경질폴리우레탄폼단열재2중2호 T180철콘크리트벽 호 실 계단실 호 실	

NOTE:


PROJECT
구로구 공동 190-84번지 외1필지
도시형 생활주택 (원룸형)신축공사
APPROVED BY
건축사 구 연 목

ARCHITECTURE & ENGINEERING
건축사사무소 유일엔지니어링
서울특별시 서초구 반포대로 14길 71(서초동)
LG서호에클리트(1904호)
TEL : 02) 540-1546, FAX : 02)540-1576

TITLE
3 층 평 면 도

날짜
DATE: 2021. 08. .

SCALE	1 / 100	DWG NO.	A - 010	REV.
-------	---------	---------	---------	------

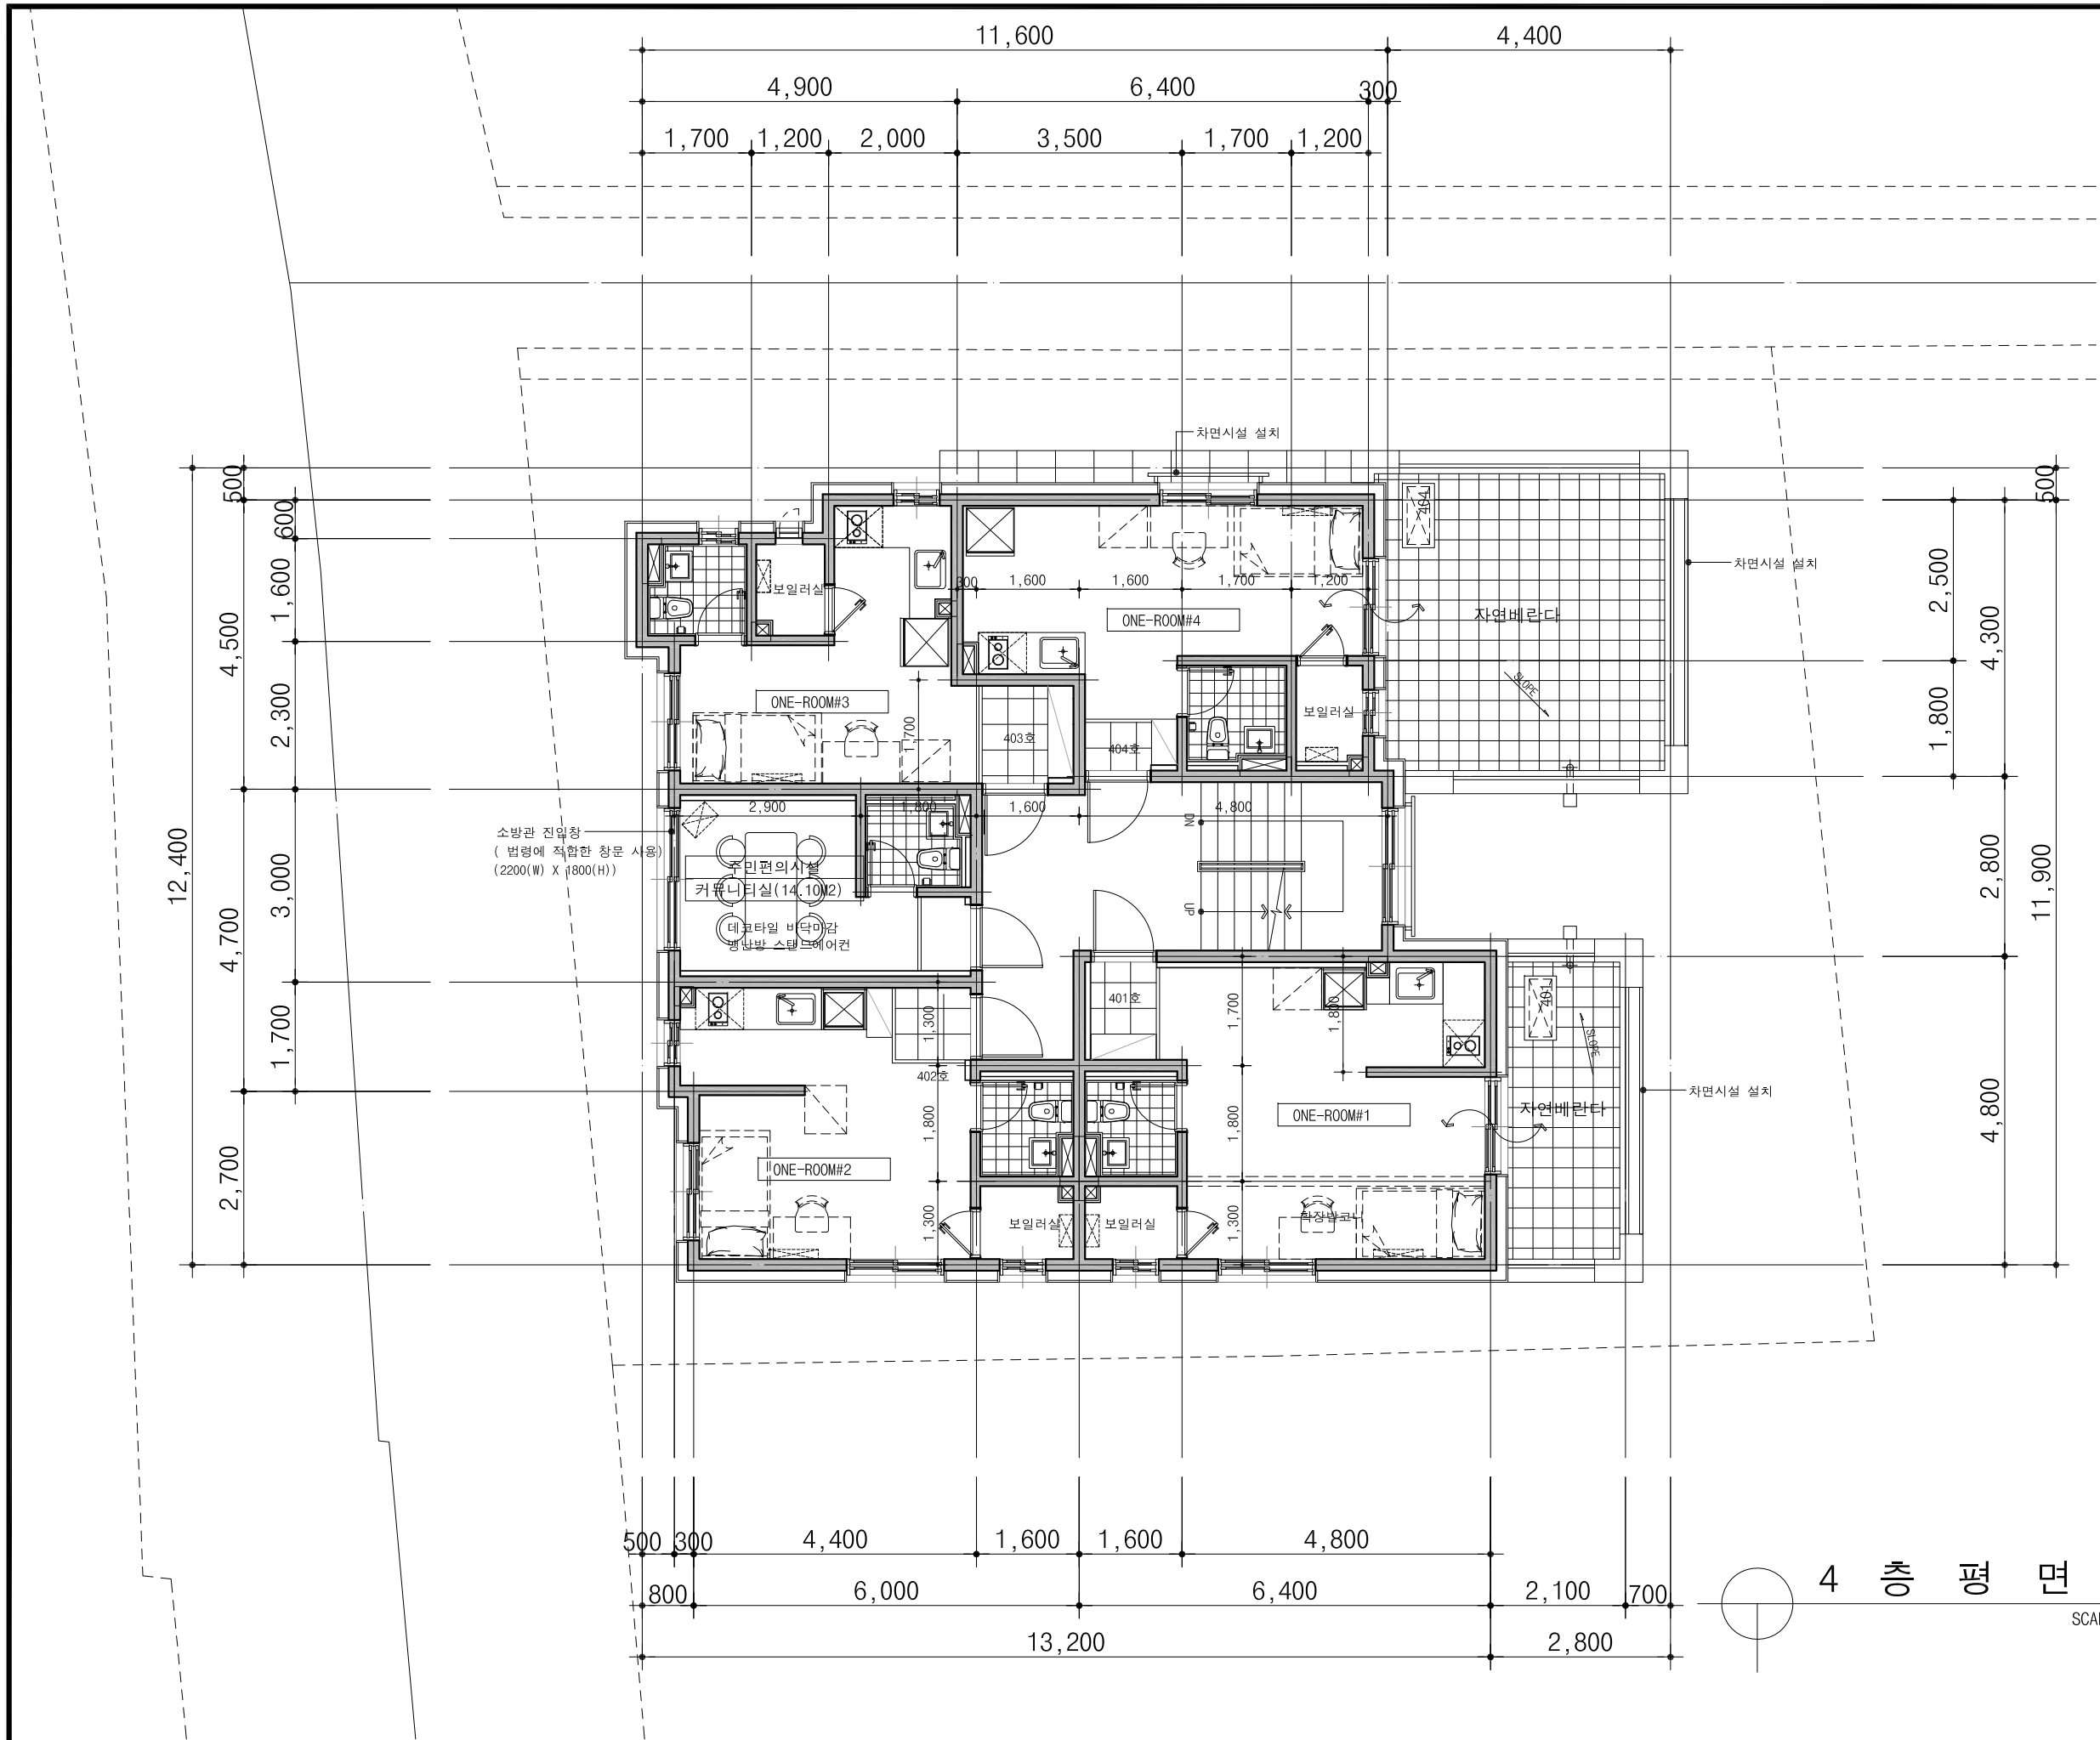

4 층 평 면 도
SCALE: 1/100

주 기		
1	세대 현관문 도어체크 및 스토퍼 계획	
2	세대 발코니 설치시 세대간 분리벽 계획	
3	세대내 비디오폰 설치	
4	주차장내 CCTV 설치	
5	벽체	직접 외기에 면한 실내벽면은 단열재 (아이소핑크10mm+석고보드 마감도면 표기) 계단실 간접 외기에 면한 실내벽면은 단열재 /복도 (경질우레탄80mm+석고보드 마감도면 표기)
6	에어콘 실외기 설치위치 및 에어컨 도면표기)	
7	불박이 가구 내부 다용도 수납가능토록 수평이동 칸막이 설치	
8	콘크리트 폼타이 제거후 마감공사 시공(방수 및 단열재 시공등)	
9	구조	콘크리트 : fck=24Mpa 철근 : fy=400Mpa 세대 벽두께 : 150mm(복배근) 외벽 벽두께 : 180mm(복배근) 코아 벽두께 : 180mm(복배근) 2층 슬라브 두께 : 180mm(복배근) 3-5층 슬라브 두께 : 210mm(복배근)
10	기타 실내 벽면은 시멘트 미장마감	
11	욕실 & 다용도실 스위치 : 문열리는 방향으로 시공	
12	공동주택 바닥충격음 차단구조기준	
3층, 4층, 5층		
13	소방관 진입창의 기준	건축물의 피난방화구조등의 기준에 관한규칙 제18조의2에 의거 1. 2층이상 11층이하인 층에 각각 1개소 이상설치 2. 소방차진입로또는 소방차 진입이 가능한 공터에 면할것 3. 창문 가운데 Ø200이상의 역삼각형을 야간에 식별가능하도록 설치.(반사 등으로 붉은색으로 표시) 4. 창문 한쪽 모서리에 타격지점 표시 (Ø30 이상의 원형) 5. 창문크기 : 폭900 높이1,200이상 (바닥에서 창아랫부분 높이800이내로 설치) 6. 다음 각 목의 어느 하나에 해당하는 유리 사용할 것 가. 플로트판유리로서 두께6mm이하인것 나. 강화유리/배강도유리로서 두께5mm이하인것 다. 위의 유리로 구성된 이중유리로서 두께24mm 이하인것
14	외기에 간접면하는 부분 : THK80 경질우레탄폼 2중2호 설치	

NOTE:

PROJECT

구로구 공동 190-84번지 외1필지
도시형 생활주택 (원룸형)신축공사

APPROVED BY

건축사 구 연 목

호실

호실

호실

호실

건축사사무소 유일엔지니어링

서울특별시 서초구 반포대로 14길 71(서초동)
LG서호에클리트(1904호)
TEL : 02) 540-1546, FAX : 02)540-1576

TITLE

4 층 평 면 도

날짜

DATE: 2021. 08. .


SCALE

1 / 100

DWG NO.

A - 011

REV.

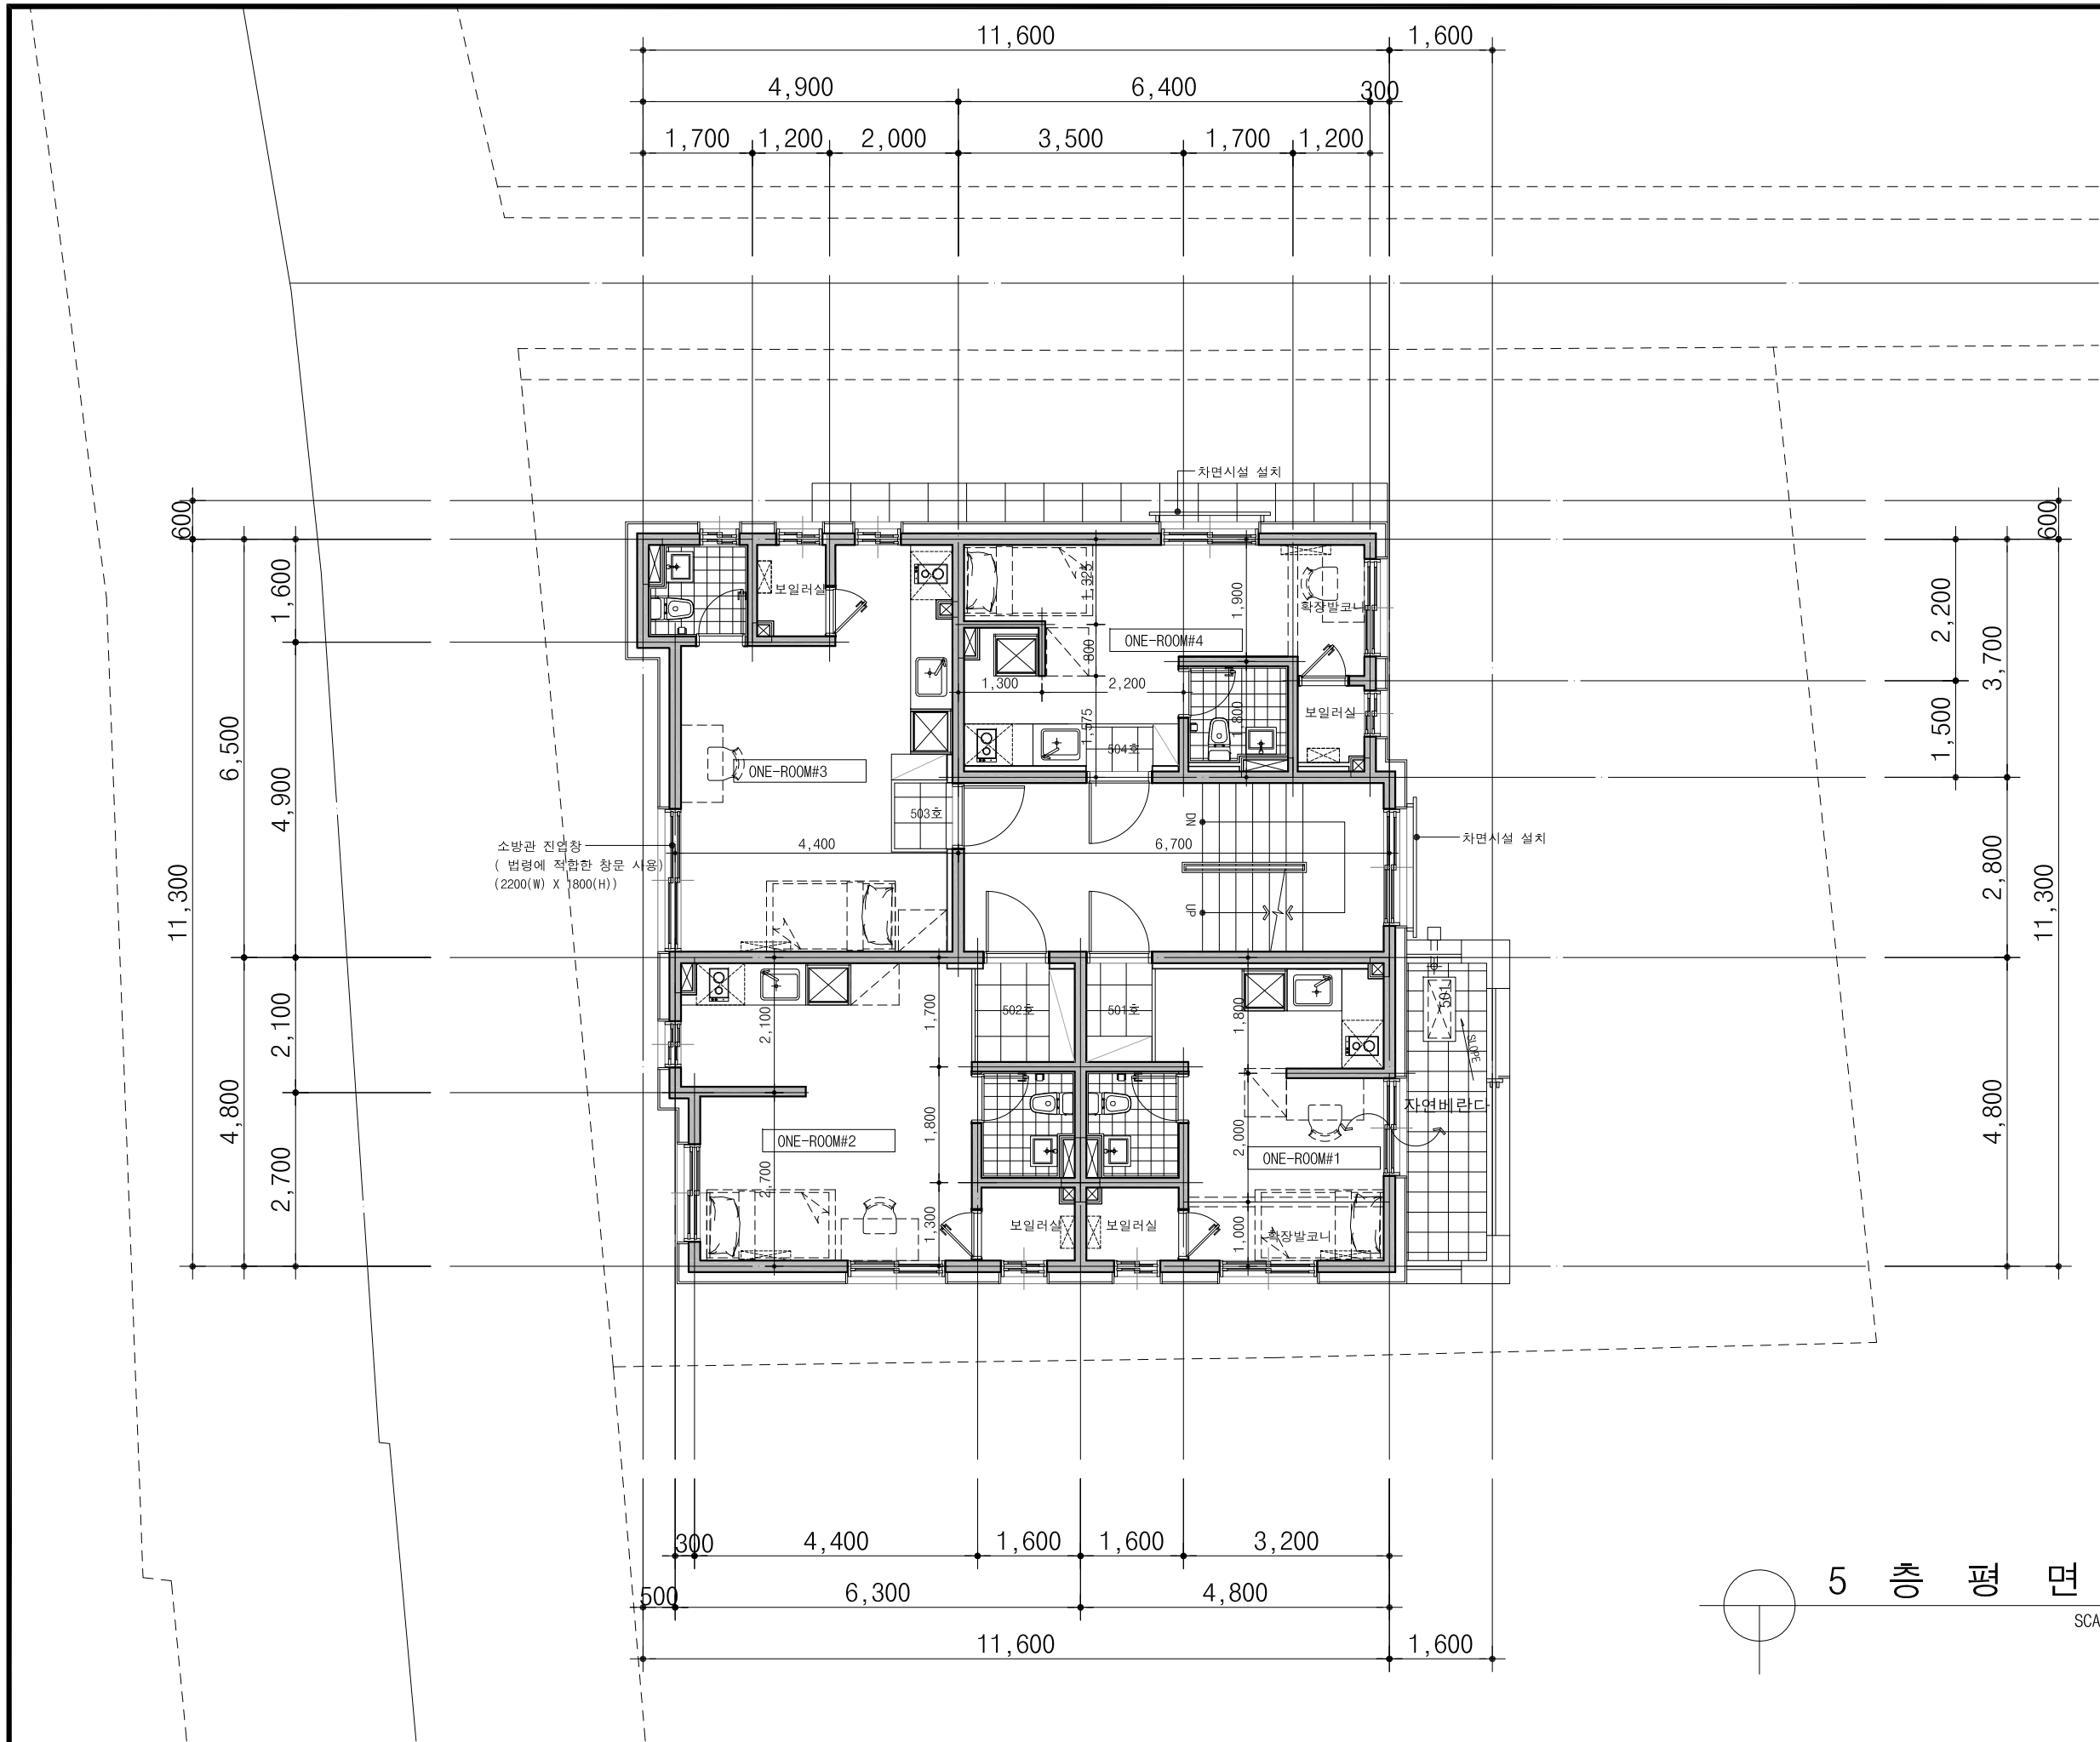


5 층 평 면 도
SCALE: 1/100

주 기		
1	세대 현관문 도어체크 및 스토퍼 계획	
2	세대 발코니 설치시 세대간 분리벽 계획	
3	세대내 비디오폰 설치	
4	주차장내 CCTV 설치	
5	벽체	외벽 직접 외기에 면한 실내벽면은 단열재 (아이소핑크10mm+석고보드 마감도면 표기) 계단실 간접 외기에 면한 실내벽면은 단열재 /복도 (경질우레탄80mm+석고보드 마감도면 표기)
6	에어콘 실외기 설치위치 및 에어컨 도면표기)	
7	불박이 가구 내부 다용도 수납가능토록 수평이동 칸막이 설치	
8	콘크리트 폼타이 제거후 마감공사 시공(방수 및 단열재 시공등)	
9	구조	콘크리트 : fck=24Mpa 철근 : fy=400Mpa 세대 벽두께 : 150mm(복배근) 외벽 벽두께 : 180mm(복배근) 코아 벽두께 : 180mm(복배근) 2층 슬라브 두께 : 180mm(복배근) 3-5층 슬라브 두께 : 210mm(복배근)
10	기타 실내 벽면은 시멘트 미장마감	
11	욕실 & 다용도실 스위치 : 문열리는 방향으로 시공	
12	공동주택 바닥충격음 차단구조기준	
3층, 4층, 5층		결재필요(PVC) 데크타일마감(2.2T이상) T=40 시멘트충진(1:3, 평상재 혼입) T=40 경질우레탄크리드 T=30 완충재(EPS계열) T=210 콘크리트슬라브
13	소방관 진입창의 기준	건축물의 피난방화구조등의 기준에 관한규칙 제18조의2에 의거 1. 2층이상 11층이하인 층에 각각 1개소 이상설치 2. 소방차진입로또는 소방차 진입이 가능한 공터에 면할것 3. 창문 가운데 Ø200이상의 역삼각형을 아간에 식별가능하도록 설치.(반사 등으로 붉은색으로 표시) 4. 창문 한쪽 모서리에 타격지점 표시 (Ø30 이상의 원형) 5. 창문크기 : 폭900 높이1,200이상 (바닥에서 창아랫부분 높이800이내로 설치) 6. 다음 각 목의 어느 하나에 해당하는 유리 사용할 것 가. 플로트판유리로서 두께6mm이하인것 나. 강화유리/배강도유리로서 두께5mm이하인것 다. 위의 유리로 구성된 이중유리로서 두께24mm 이하인것
14	외기에 간접면하는 부분 : THK80 경질우레탄폼 2중2호 설치	
호실 계단실 호실 석고보드워벽지마감 T80경질폴리우레탄폼단열재2중2호 T180철콘크리트벽		

NOTE:

PROJECT		구로구 공동 190-84번지 외1필지 도시형 생활주택 (원룸형)신축공사	
APPROVED BY		건축사 구 연 목	
ARCHITECTURE & ENGINEERING		건축사사무소 유일엔지니어링	
서울특별시 서초구 반포대로 14길 71(서초동) LG서초에클리트(1904호) TEL : 02) 540-1546, FAX : 02)540-1576			
TITLE		5 층 평 면 도	
날짜 DATE:		2021. 08. .	
SCALE	1 / 100	DWG NO.	A - 012
		REV.	

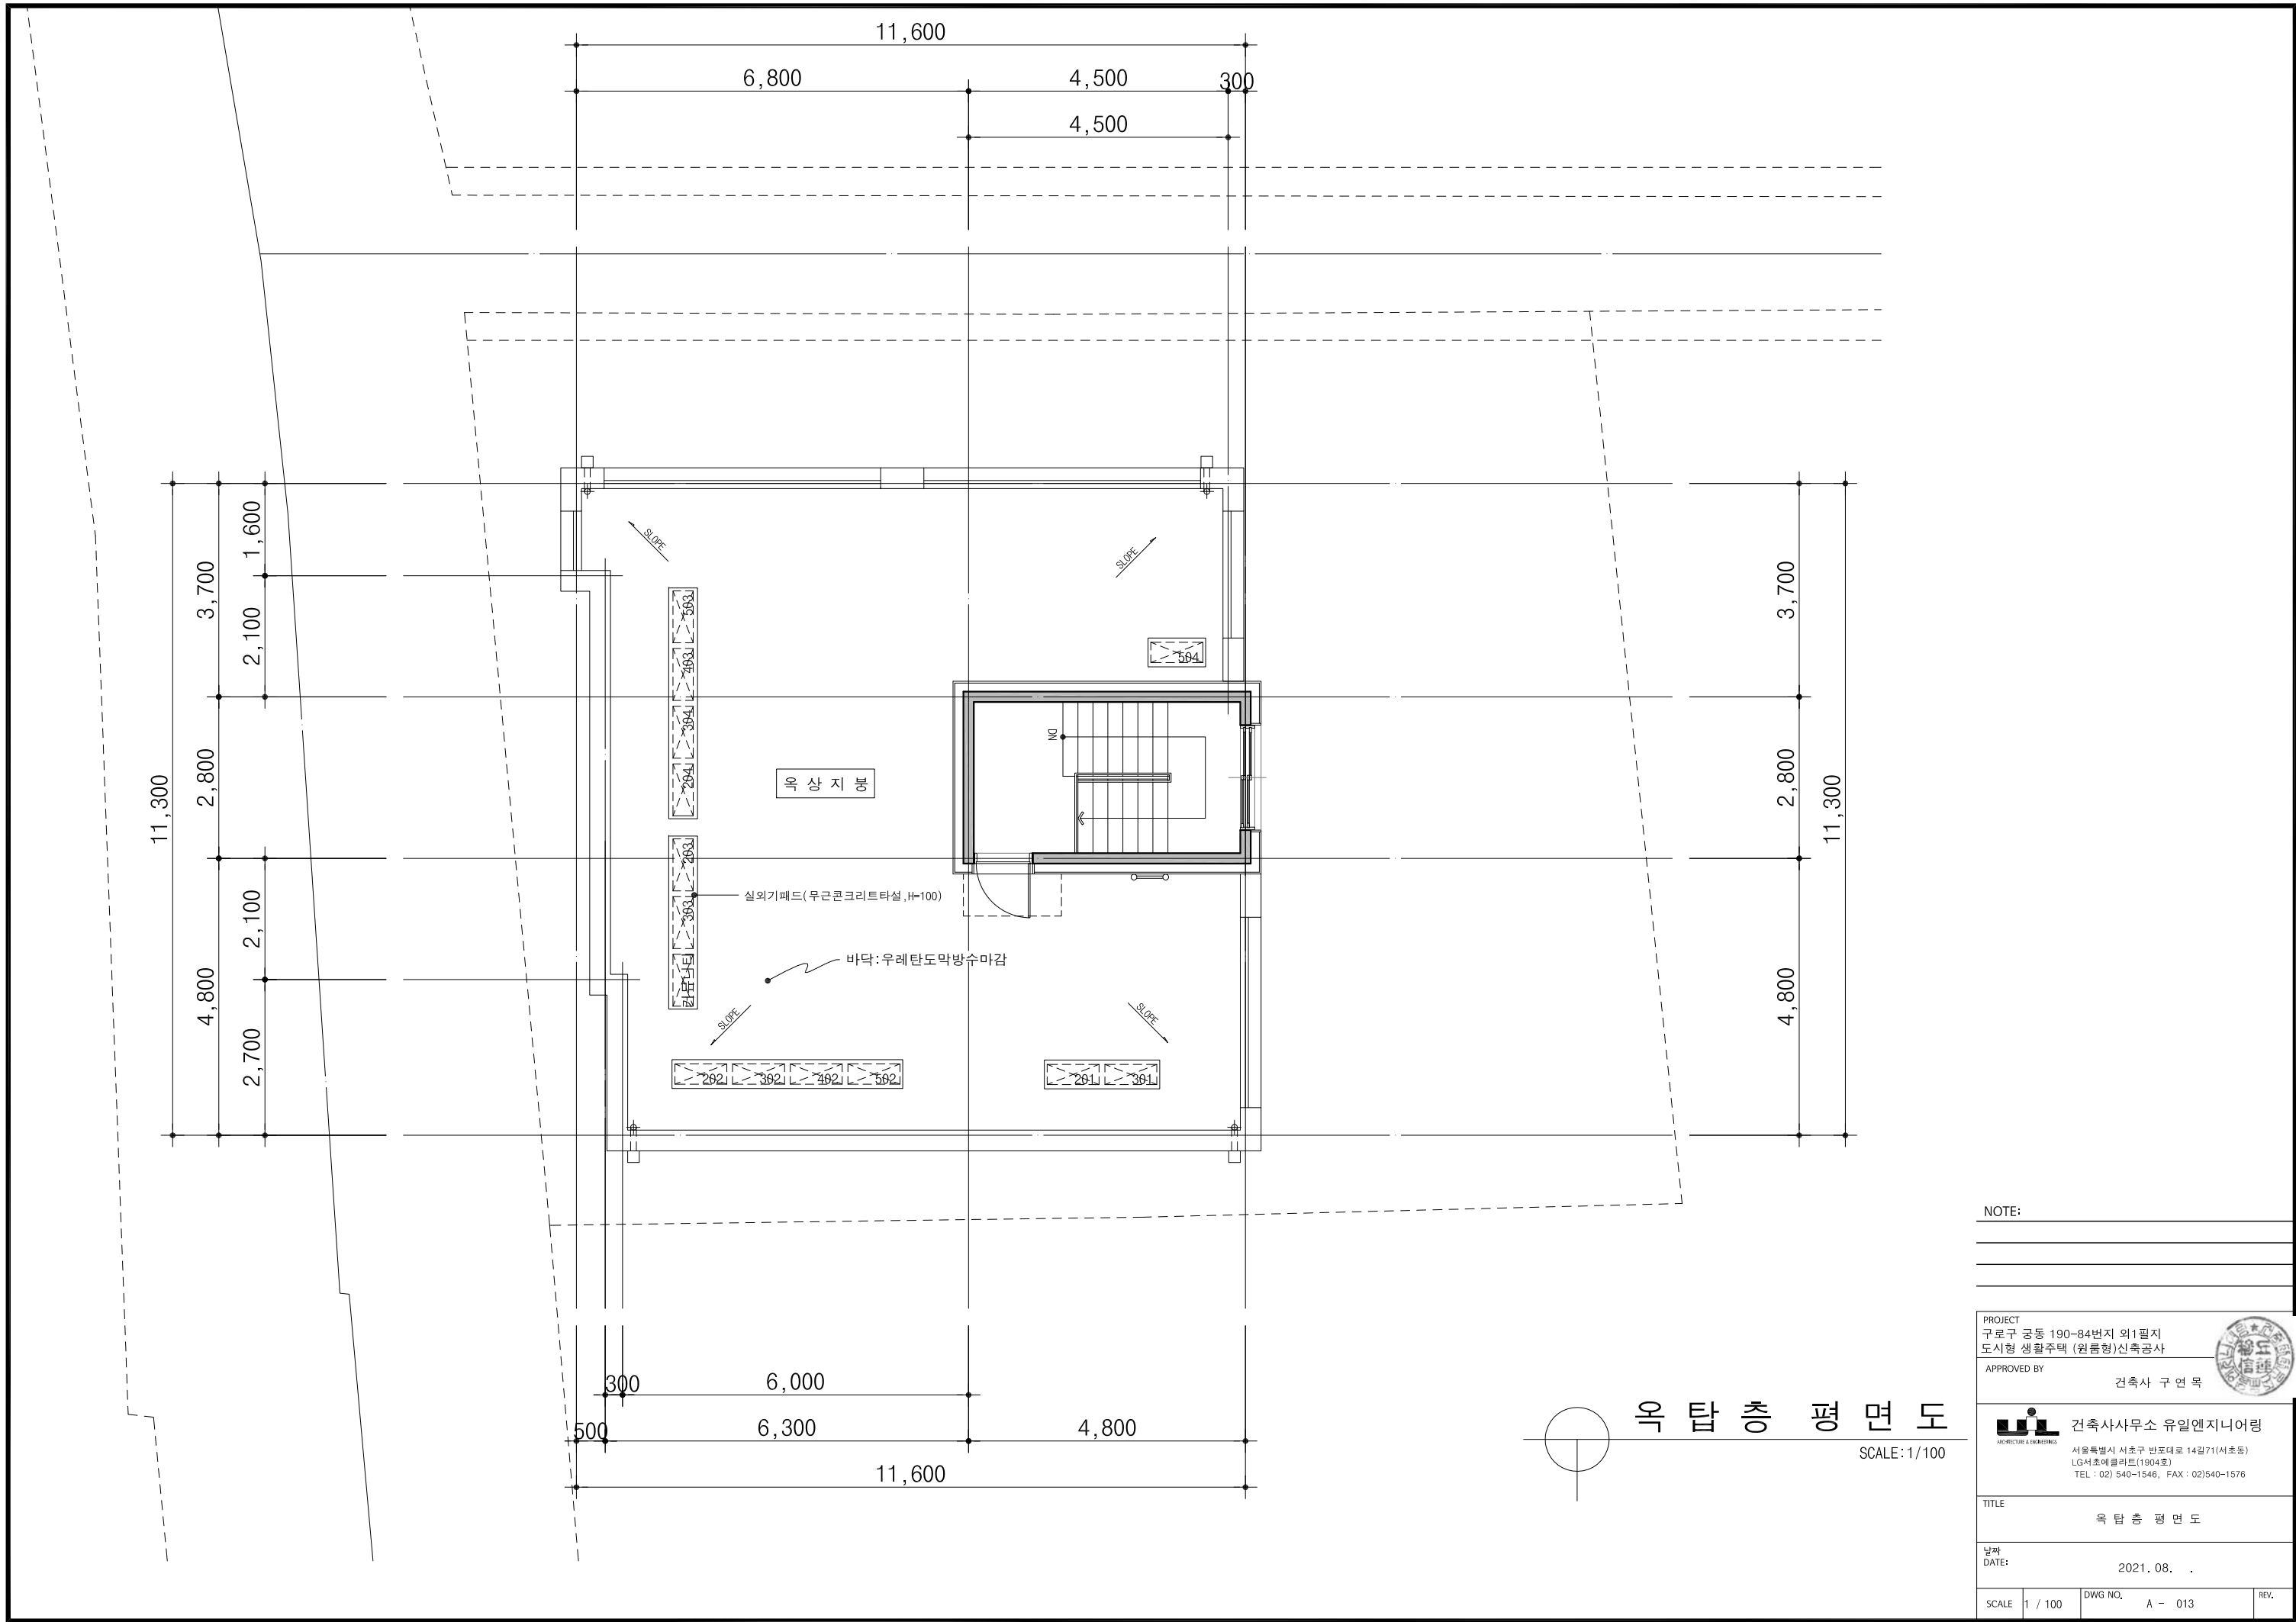

NOTE:

PROJECT
구로구 공동 190-84번지 외1필지
도시형 생활주택 (원룸형)신축공사


APPROVED BY
건축사 구 연 목


ARCHITECTURE & ENGINEERING
서울특별시 서초구 반포대로 14길 71 (서초동)
LG서초예클리어트(1904호)
TEL : 02) 540-1546, FAX : 02) 540-1576

TITLE
옥 탑 층 평 면 도



날짜
DATE: 2021. 08. .

SCALE 1 / 100 DWG NO. A - 013 REV.

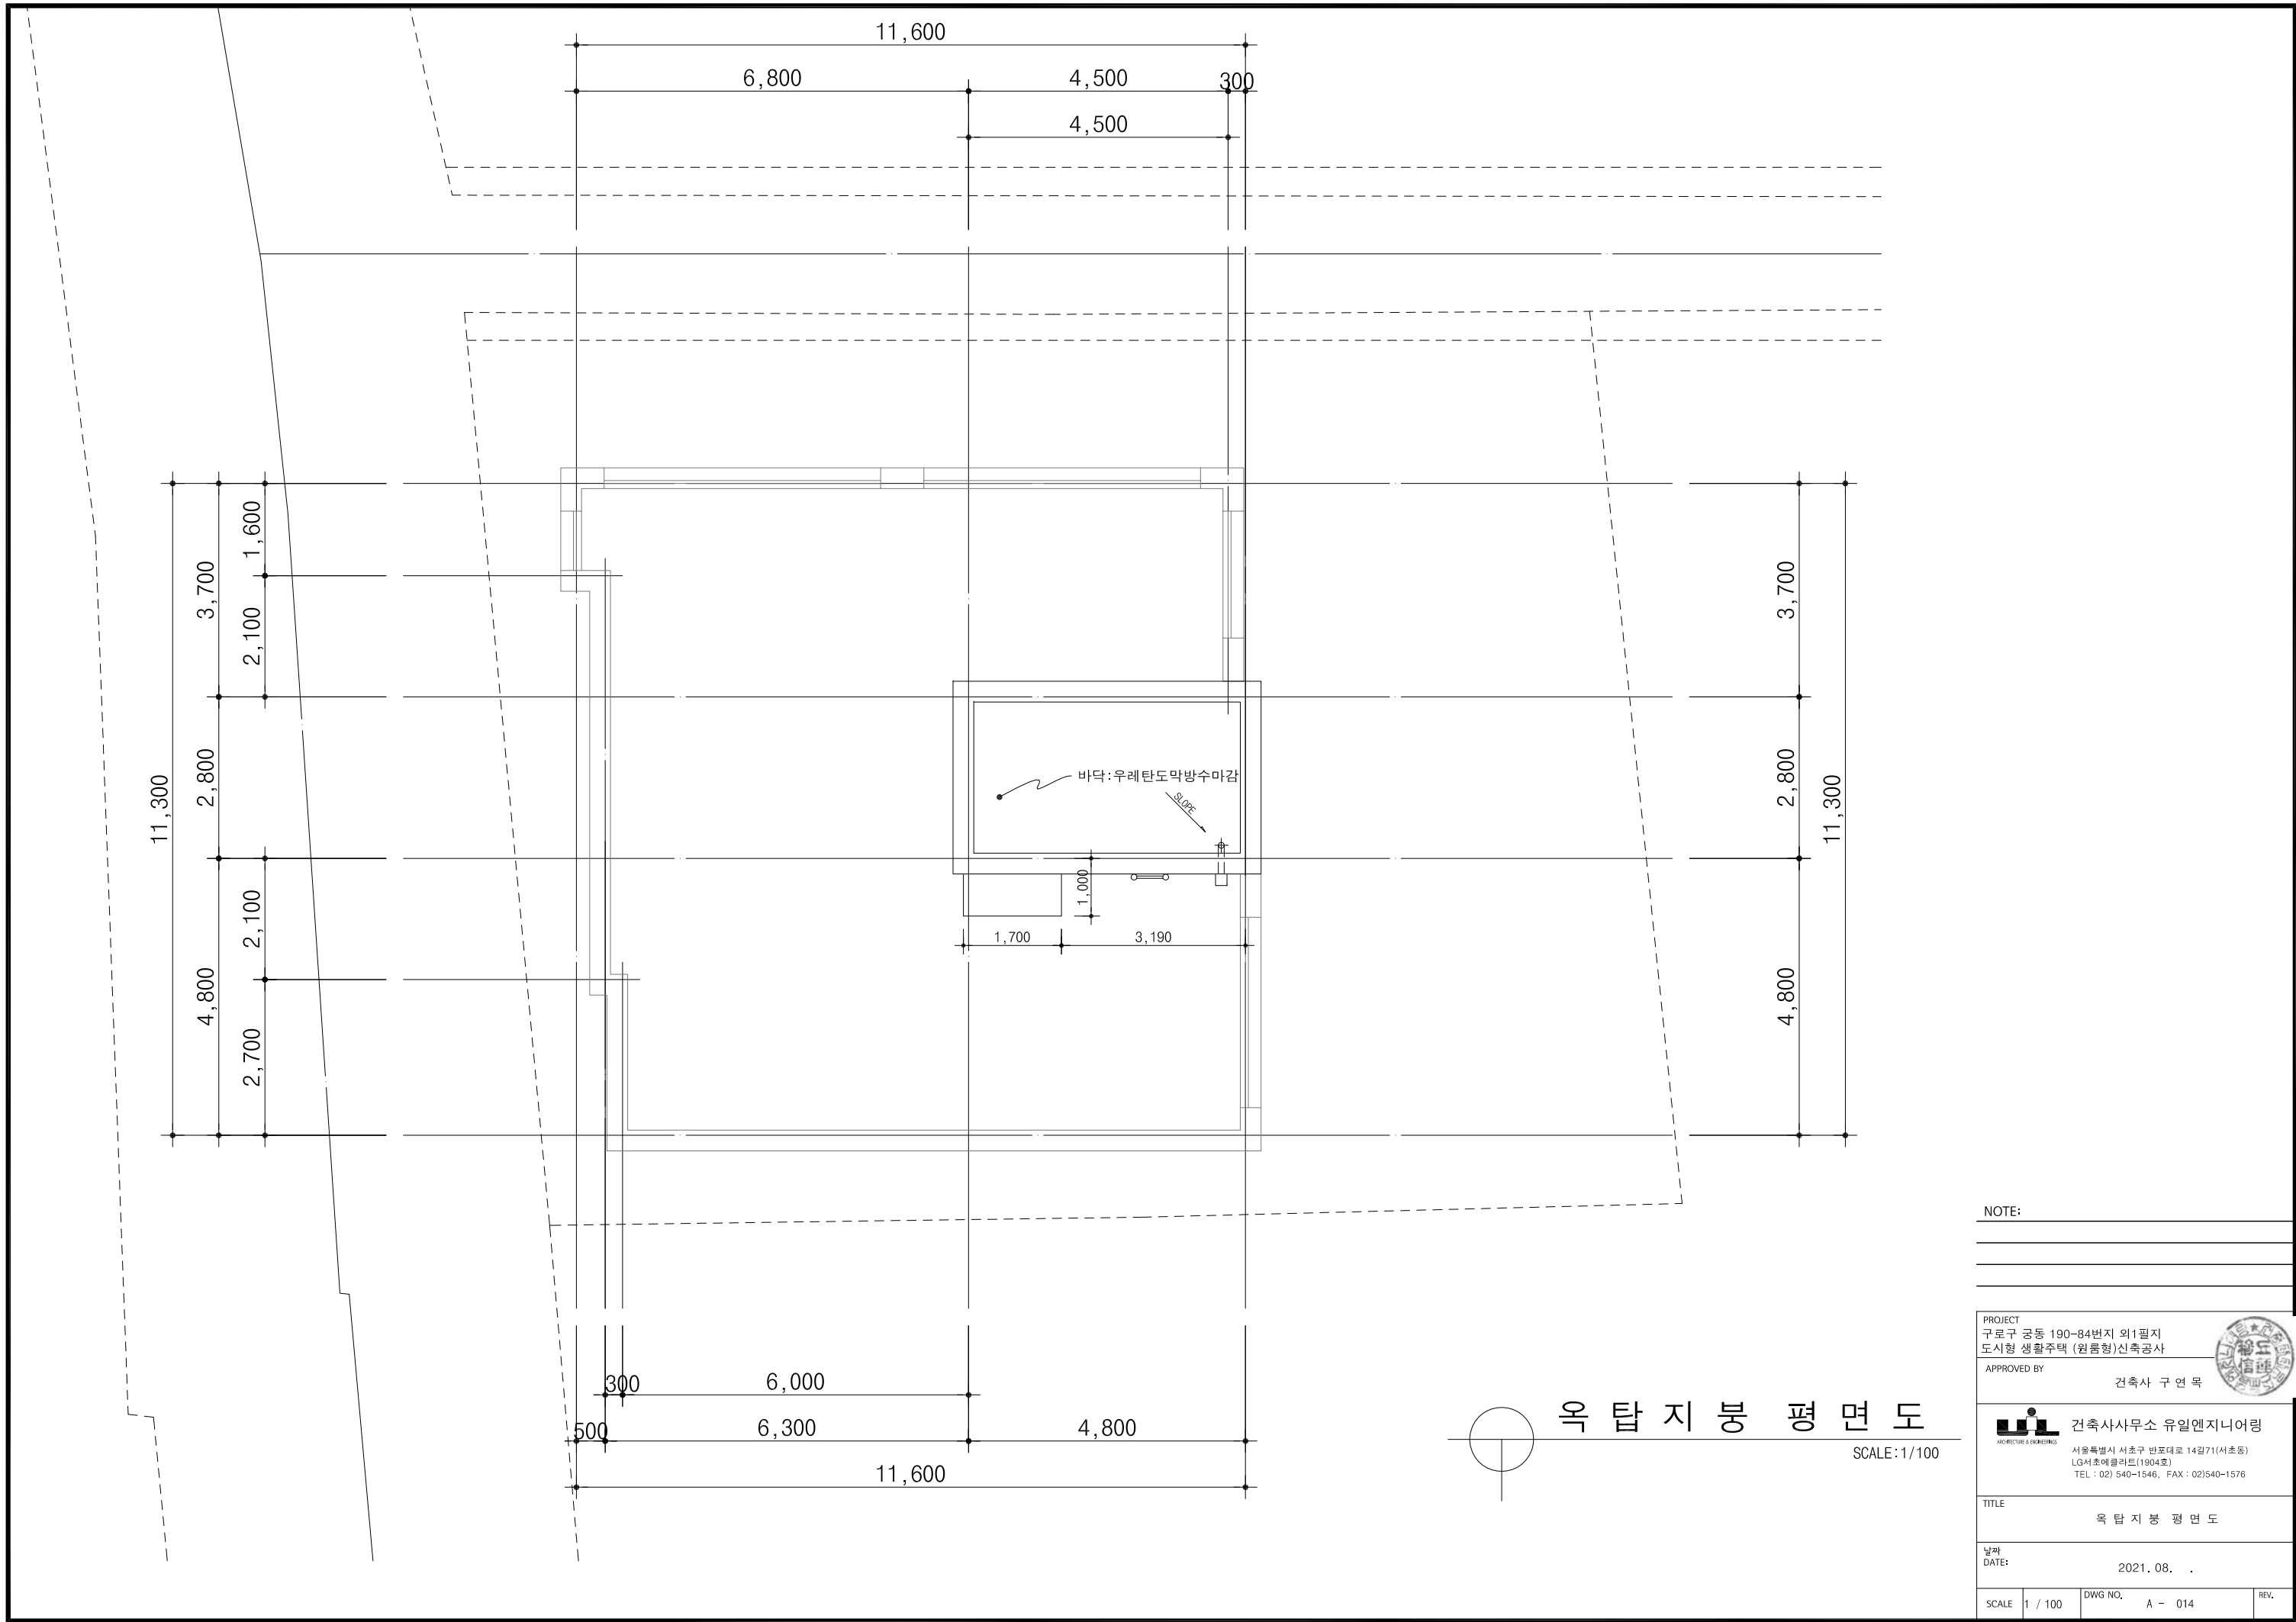

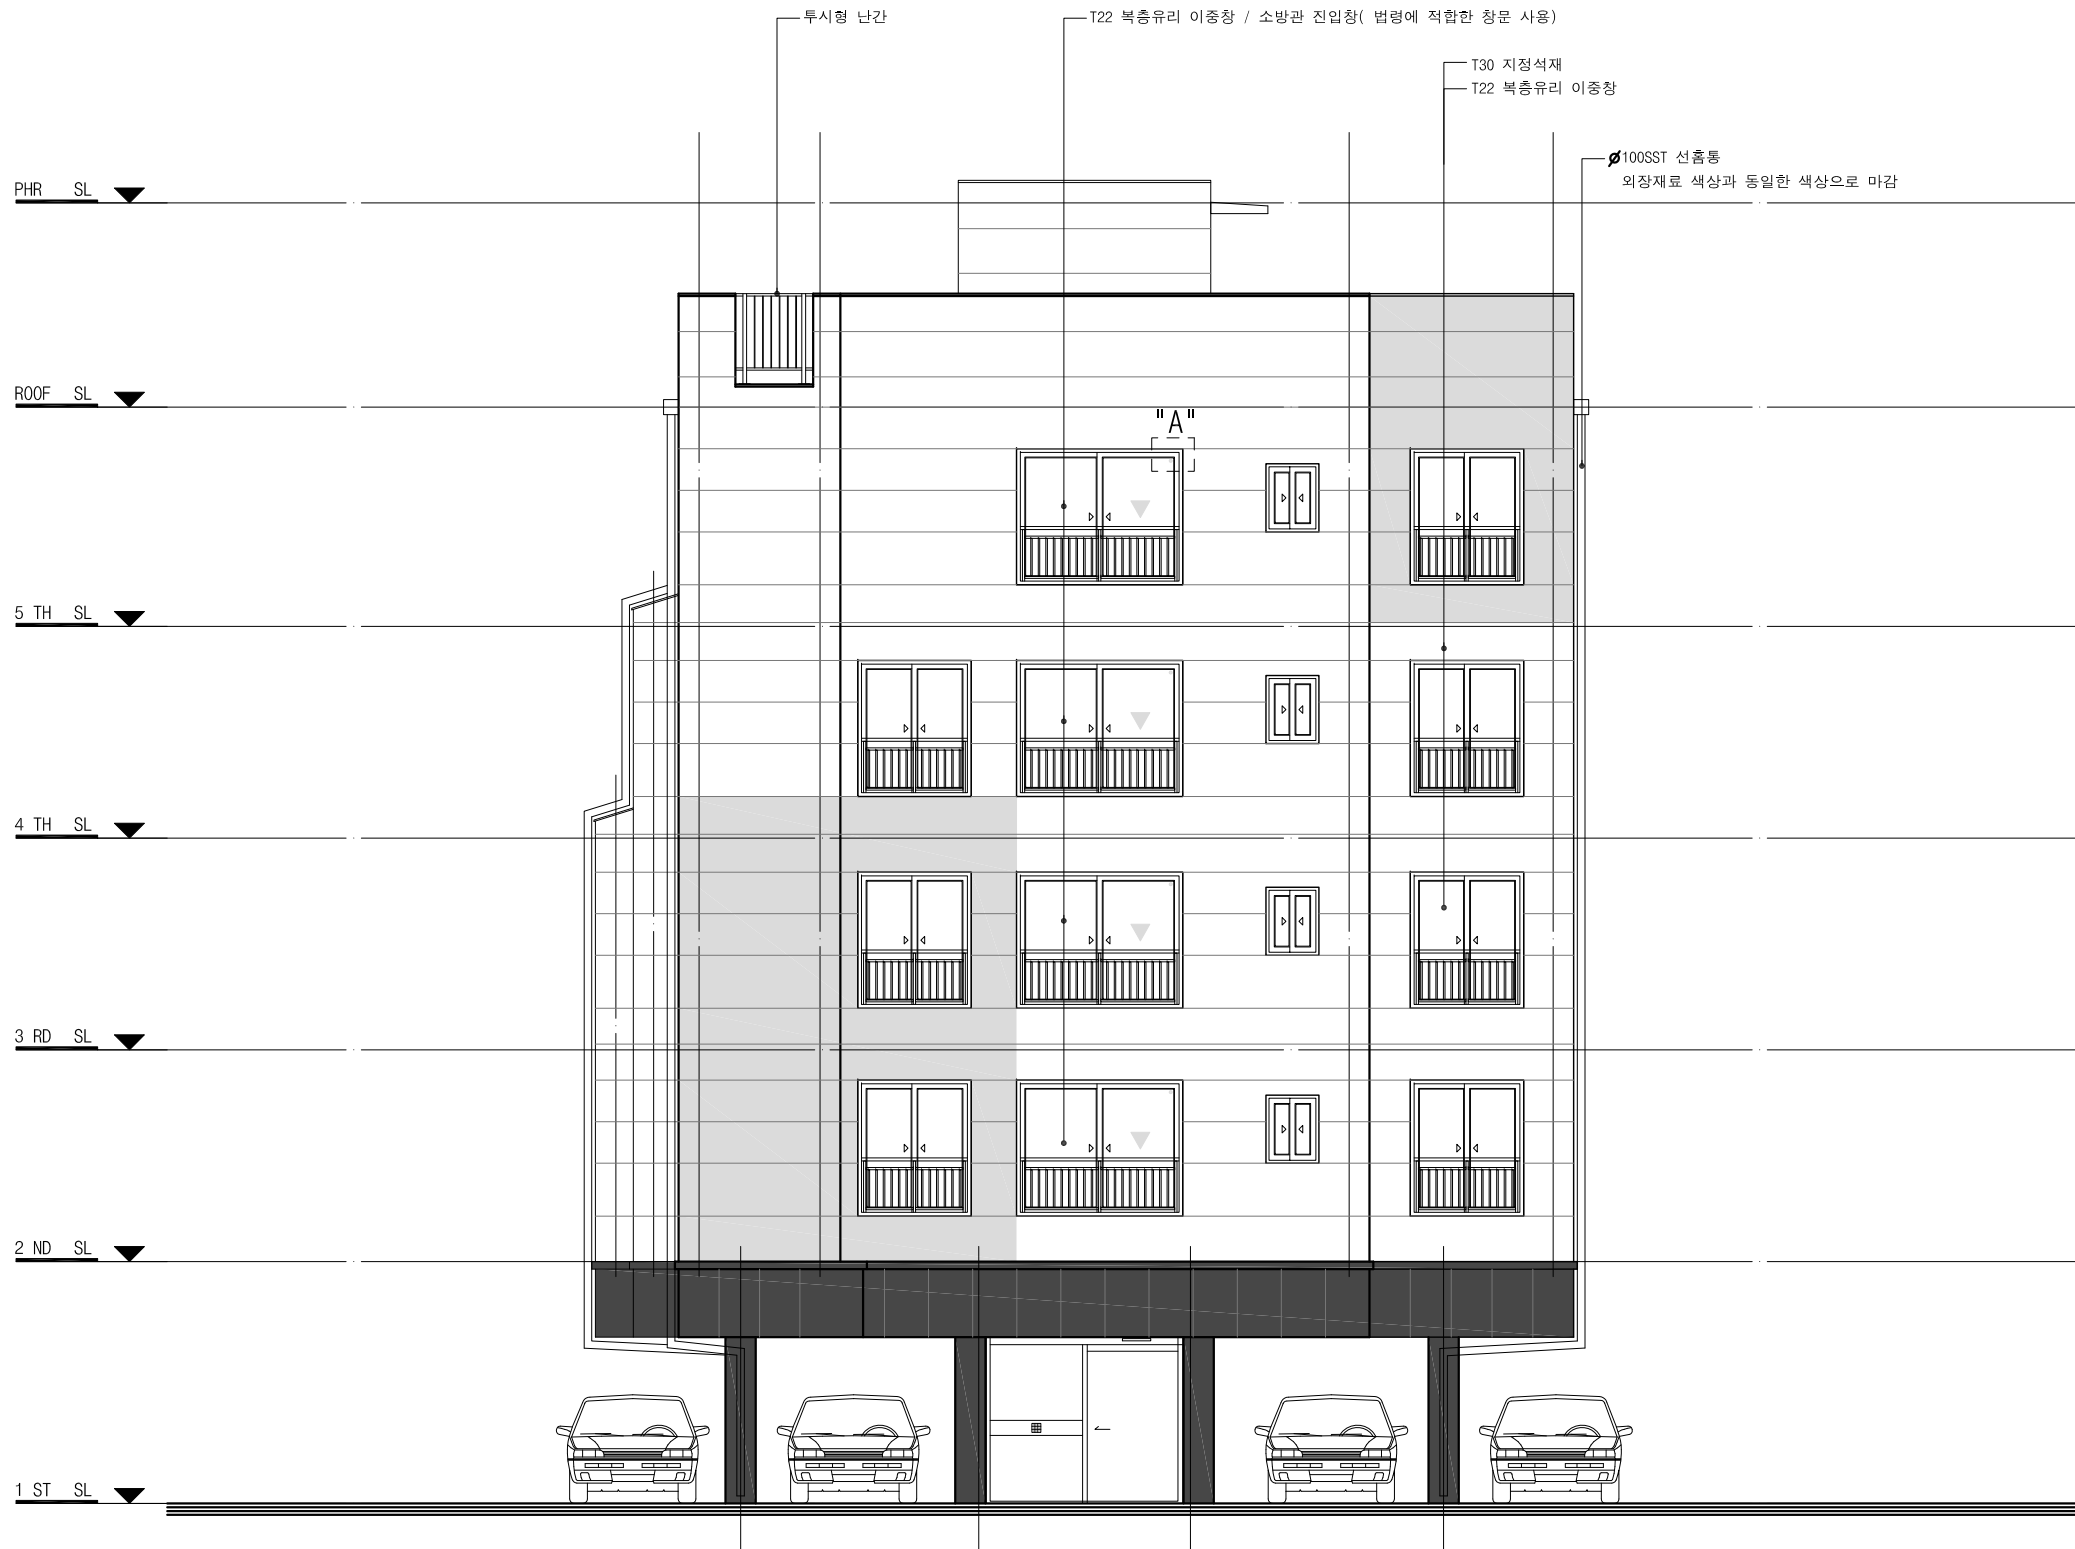



정 면 도
SCALE:1/100

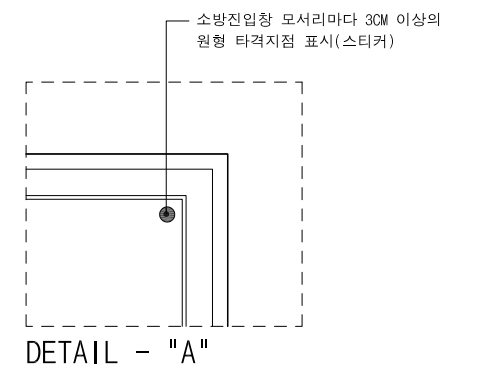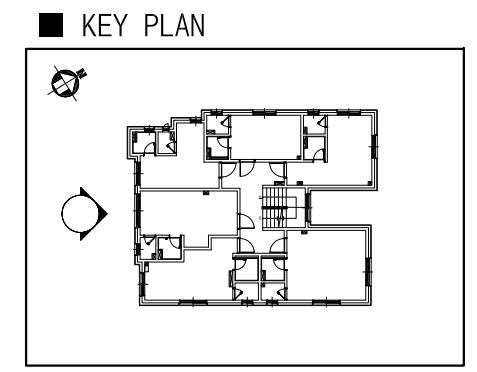

NOTE:

PROJECT 구로구 공동 190-84번지 외1필지 도시형 생활주택 (원룸형)신축공사			
APPROVED BY		건축사 구 연 목	
 건축사사무소 유일엔지니어링 서울특별시 서초구 반포대로 14길 71(서초동) LG서호에클리트(1904호) TEL : 02) 540-1546, FAX : 02)540-1576			
TITLE 정 면 도			
날짜 DATE: 2021. 08. .			
SCALE	1 / 100	DWG NO. A - 015	REV.

KEY PLAN

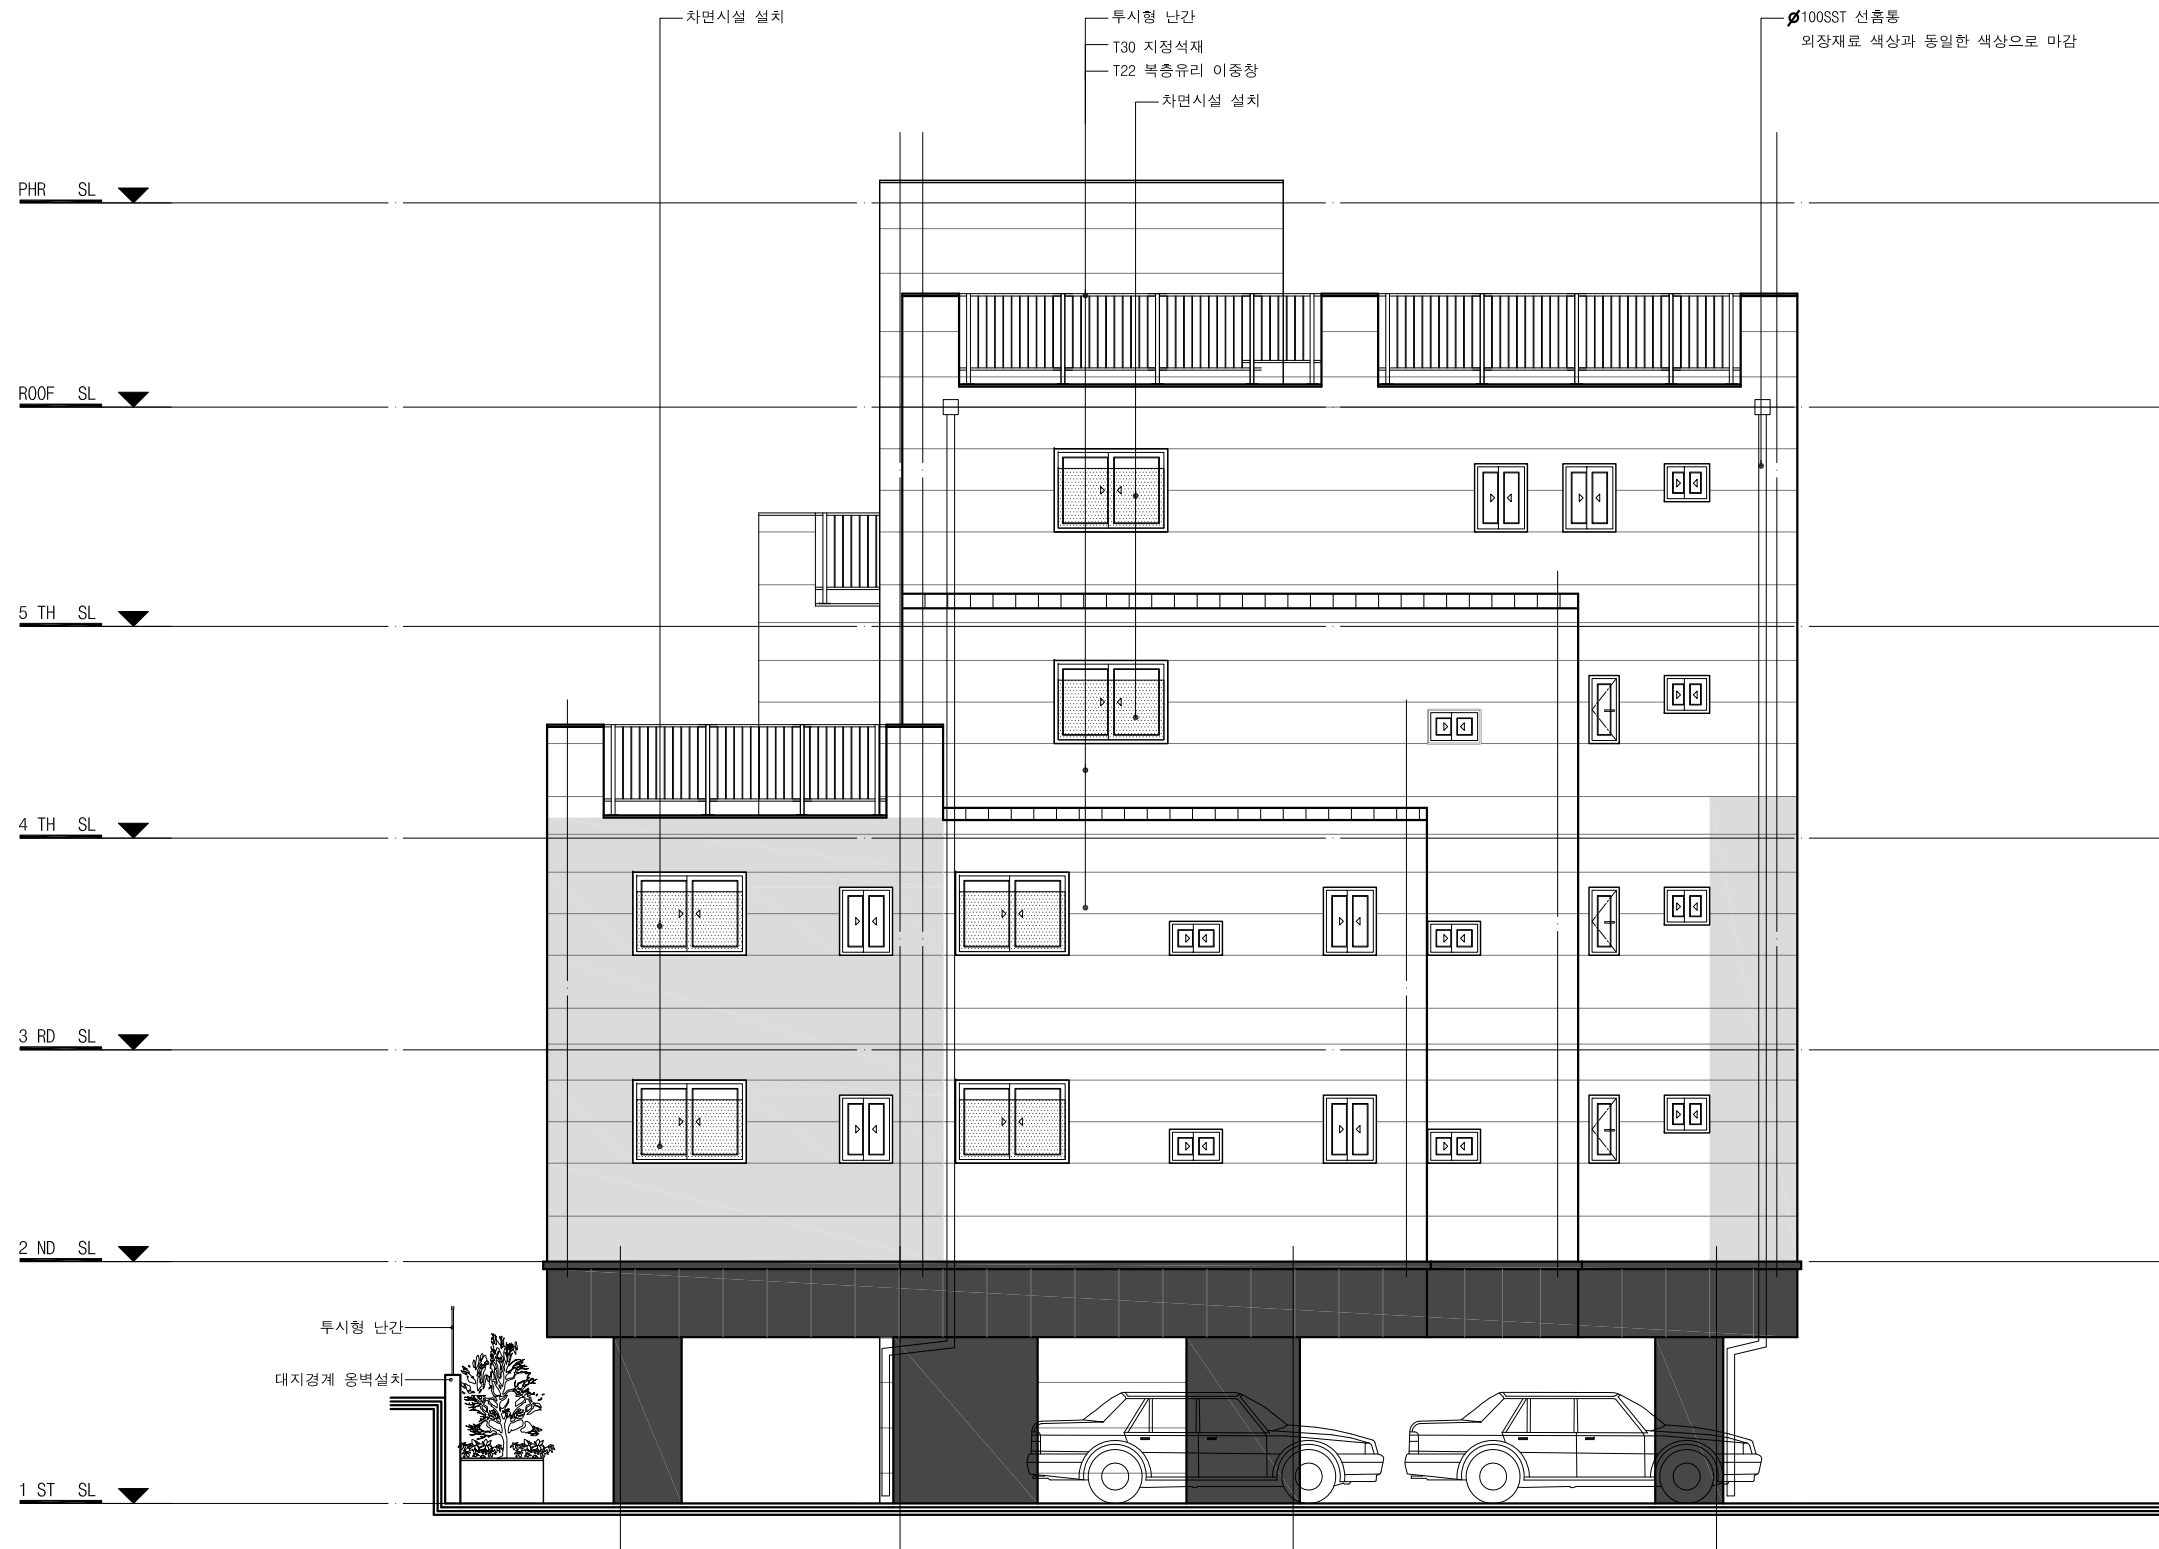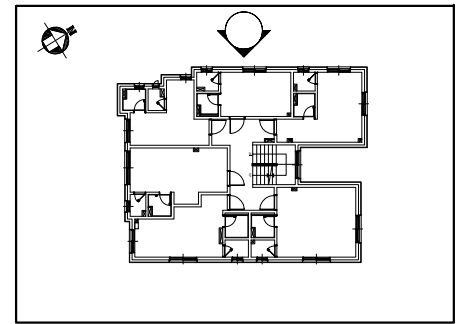

좌측면도

SCALE: 1/100

NOTE:

PROJECT
구로구 공동 190-84번지 외1필지
도시형 생활주택 (원룸형) 신축공사

APPROVED BY

건축사 구연목



건축사사무소 유일엔지니어링

서울특별시 서초구 반포대로 14길 71 (서초동)
LG서호에클라트(1904호)
TEL : 02) 540-1546, FAX : 02) 540-1576

TITLE

좌측면도

날짜

DATE:

2021. 08. .

SCALE



1 / 100

DWG NO.

A - 016

REV.

KEY PLAN

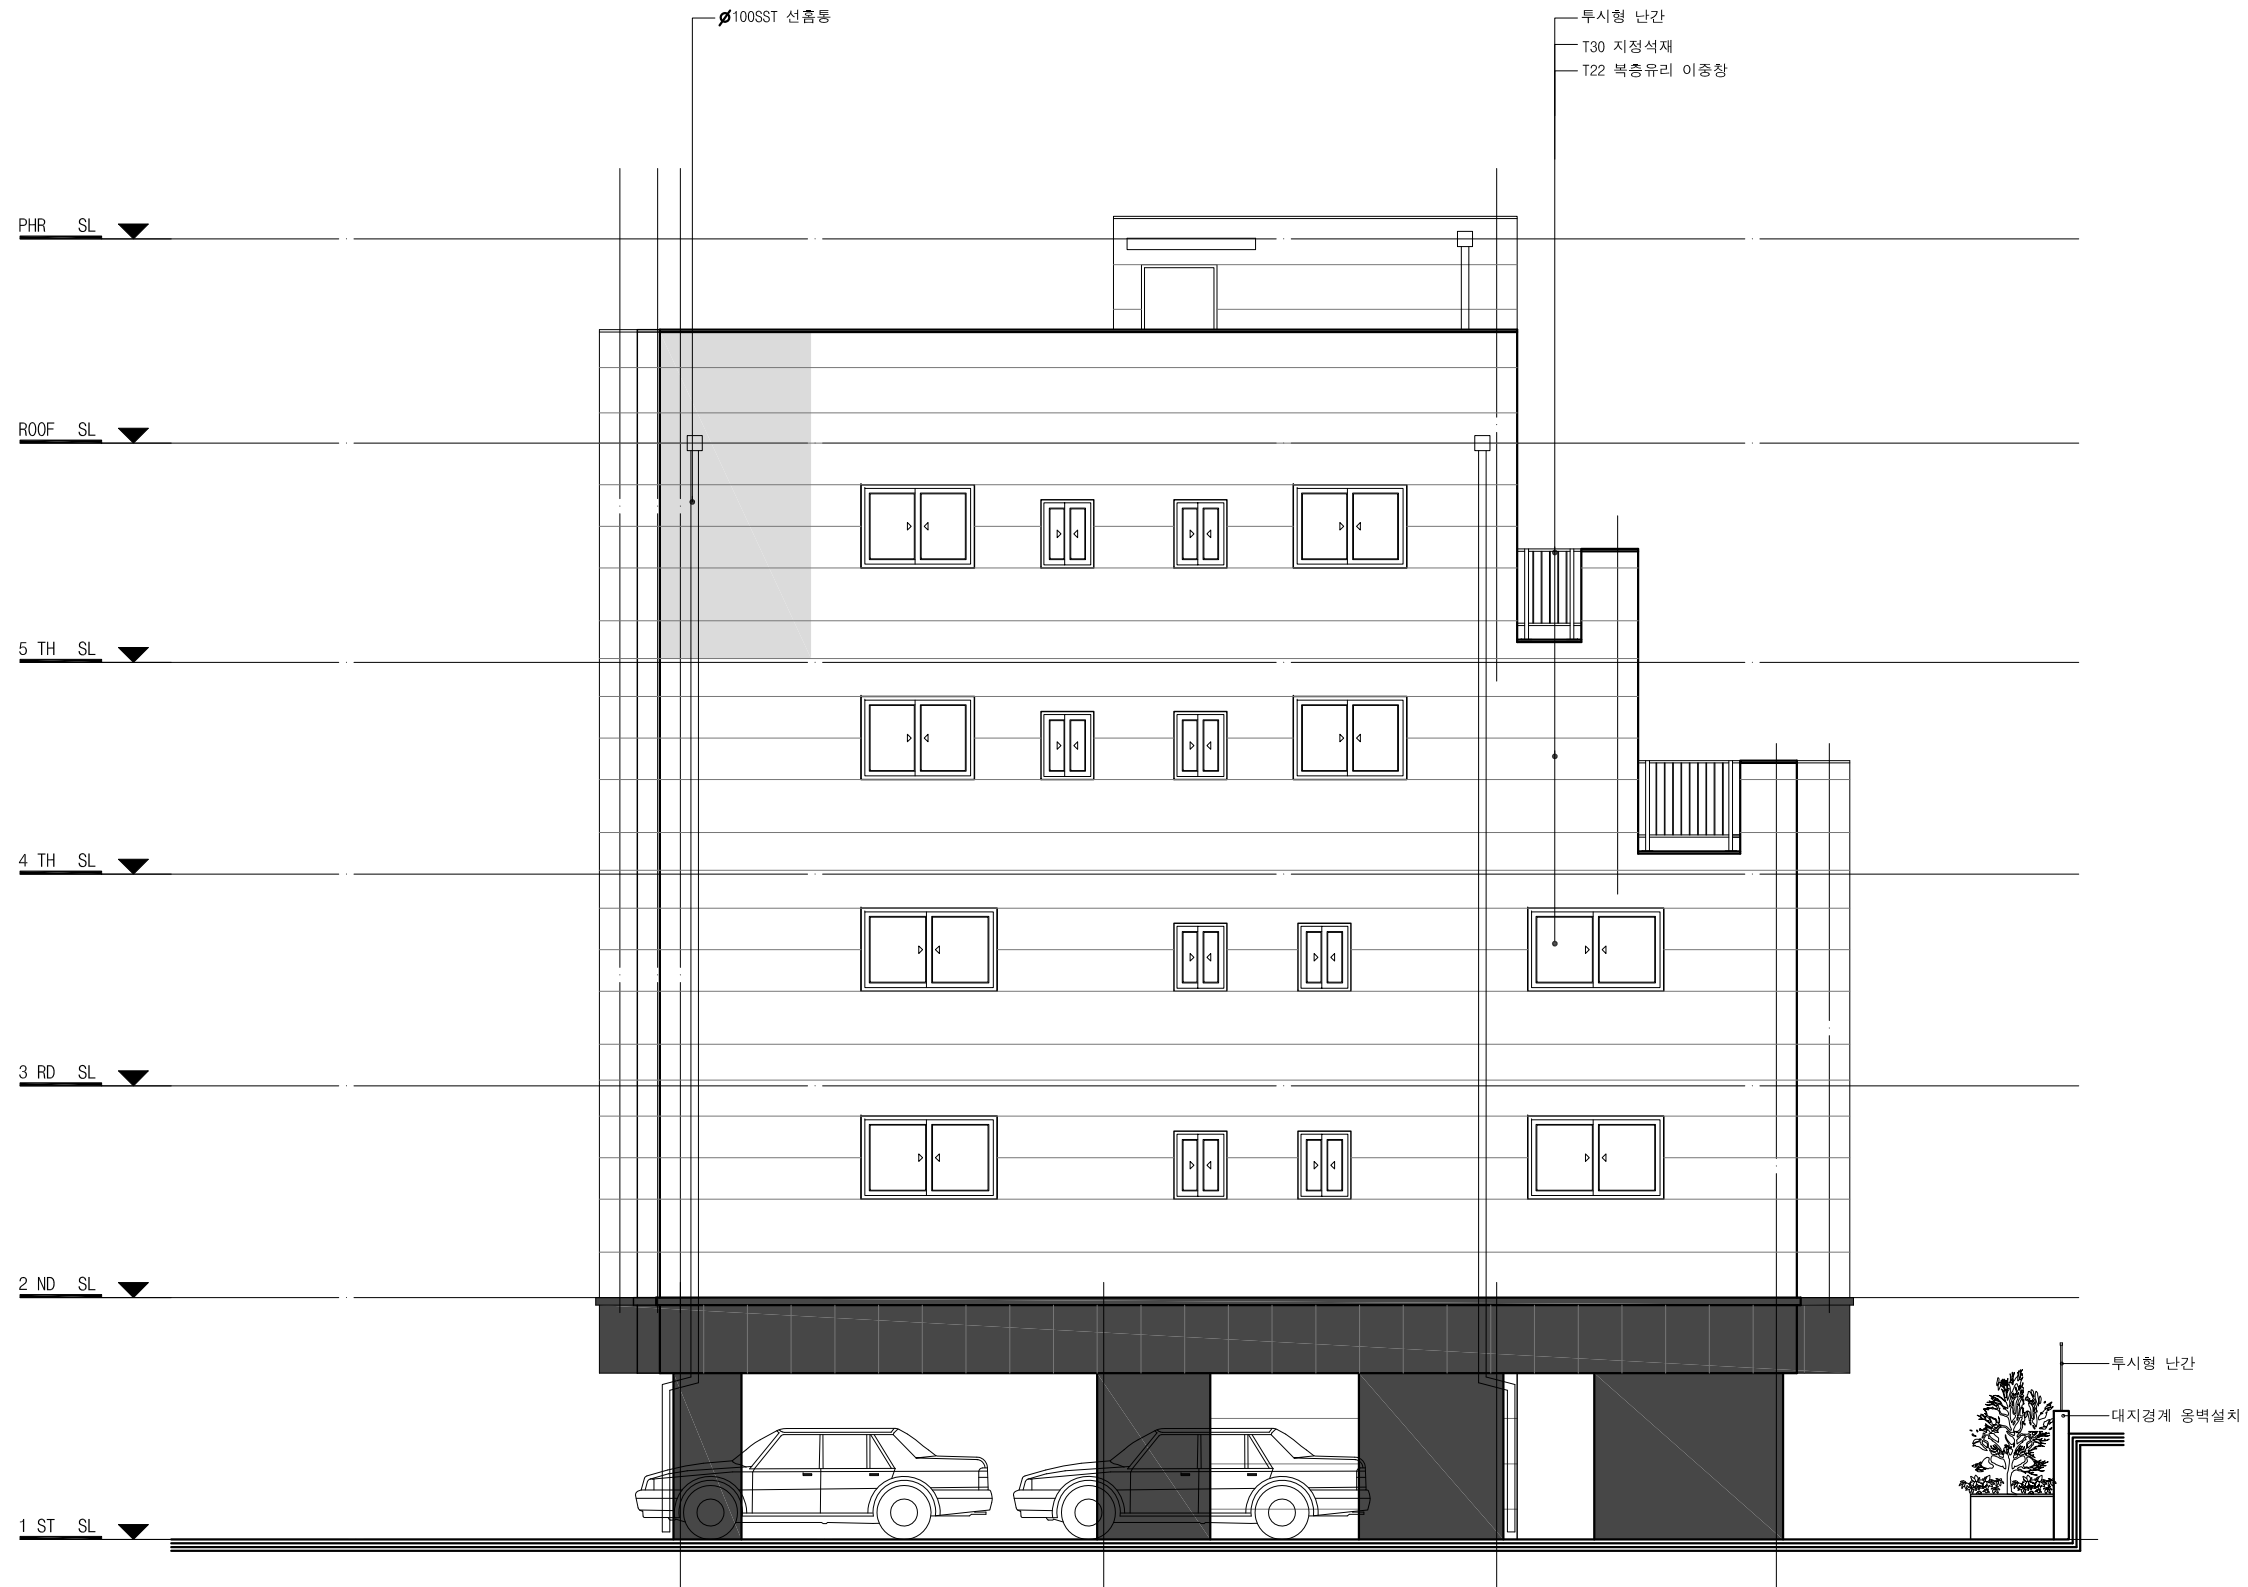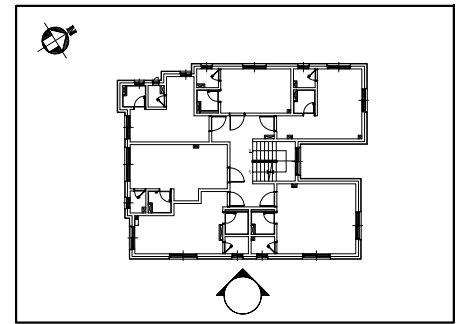

NOTE:

PROJECT
구로구 공동 190-84번지 외1필지
도시형 생활주택 (원룸형)신축공사

APPROVED BY

건축사 구 연 목



건축사사무소 유일엔지니어링

서울특별시 서초구 반포대로 14길 71(서초동)
LG서초에클라트(1904호)
TEL : 02) 540-1546, FAX : 02)540-1576

TITLE

우 측 면 도

날짜

DATE:

2021. 08. .

SCALE



1 / 100

DWG NO.

A - 017

REV.

KEY PLAN

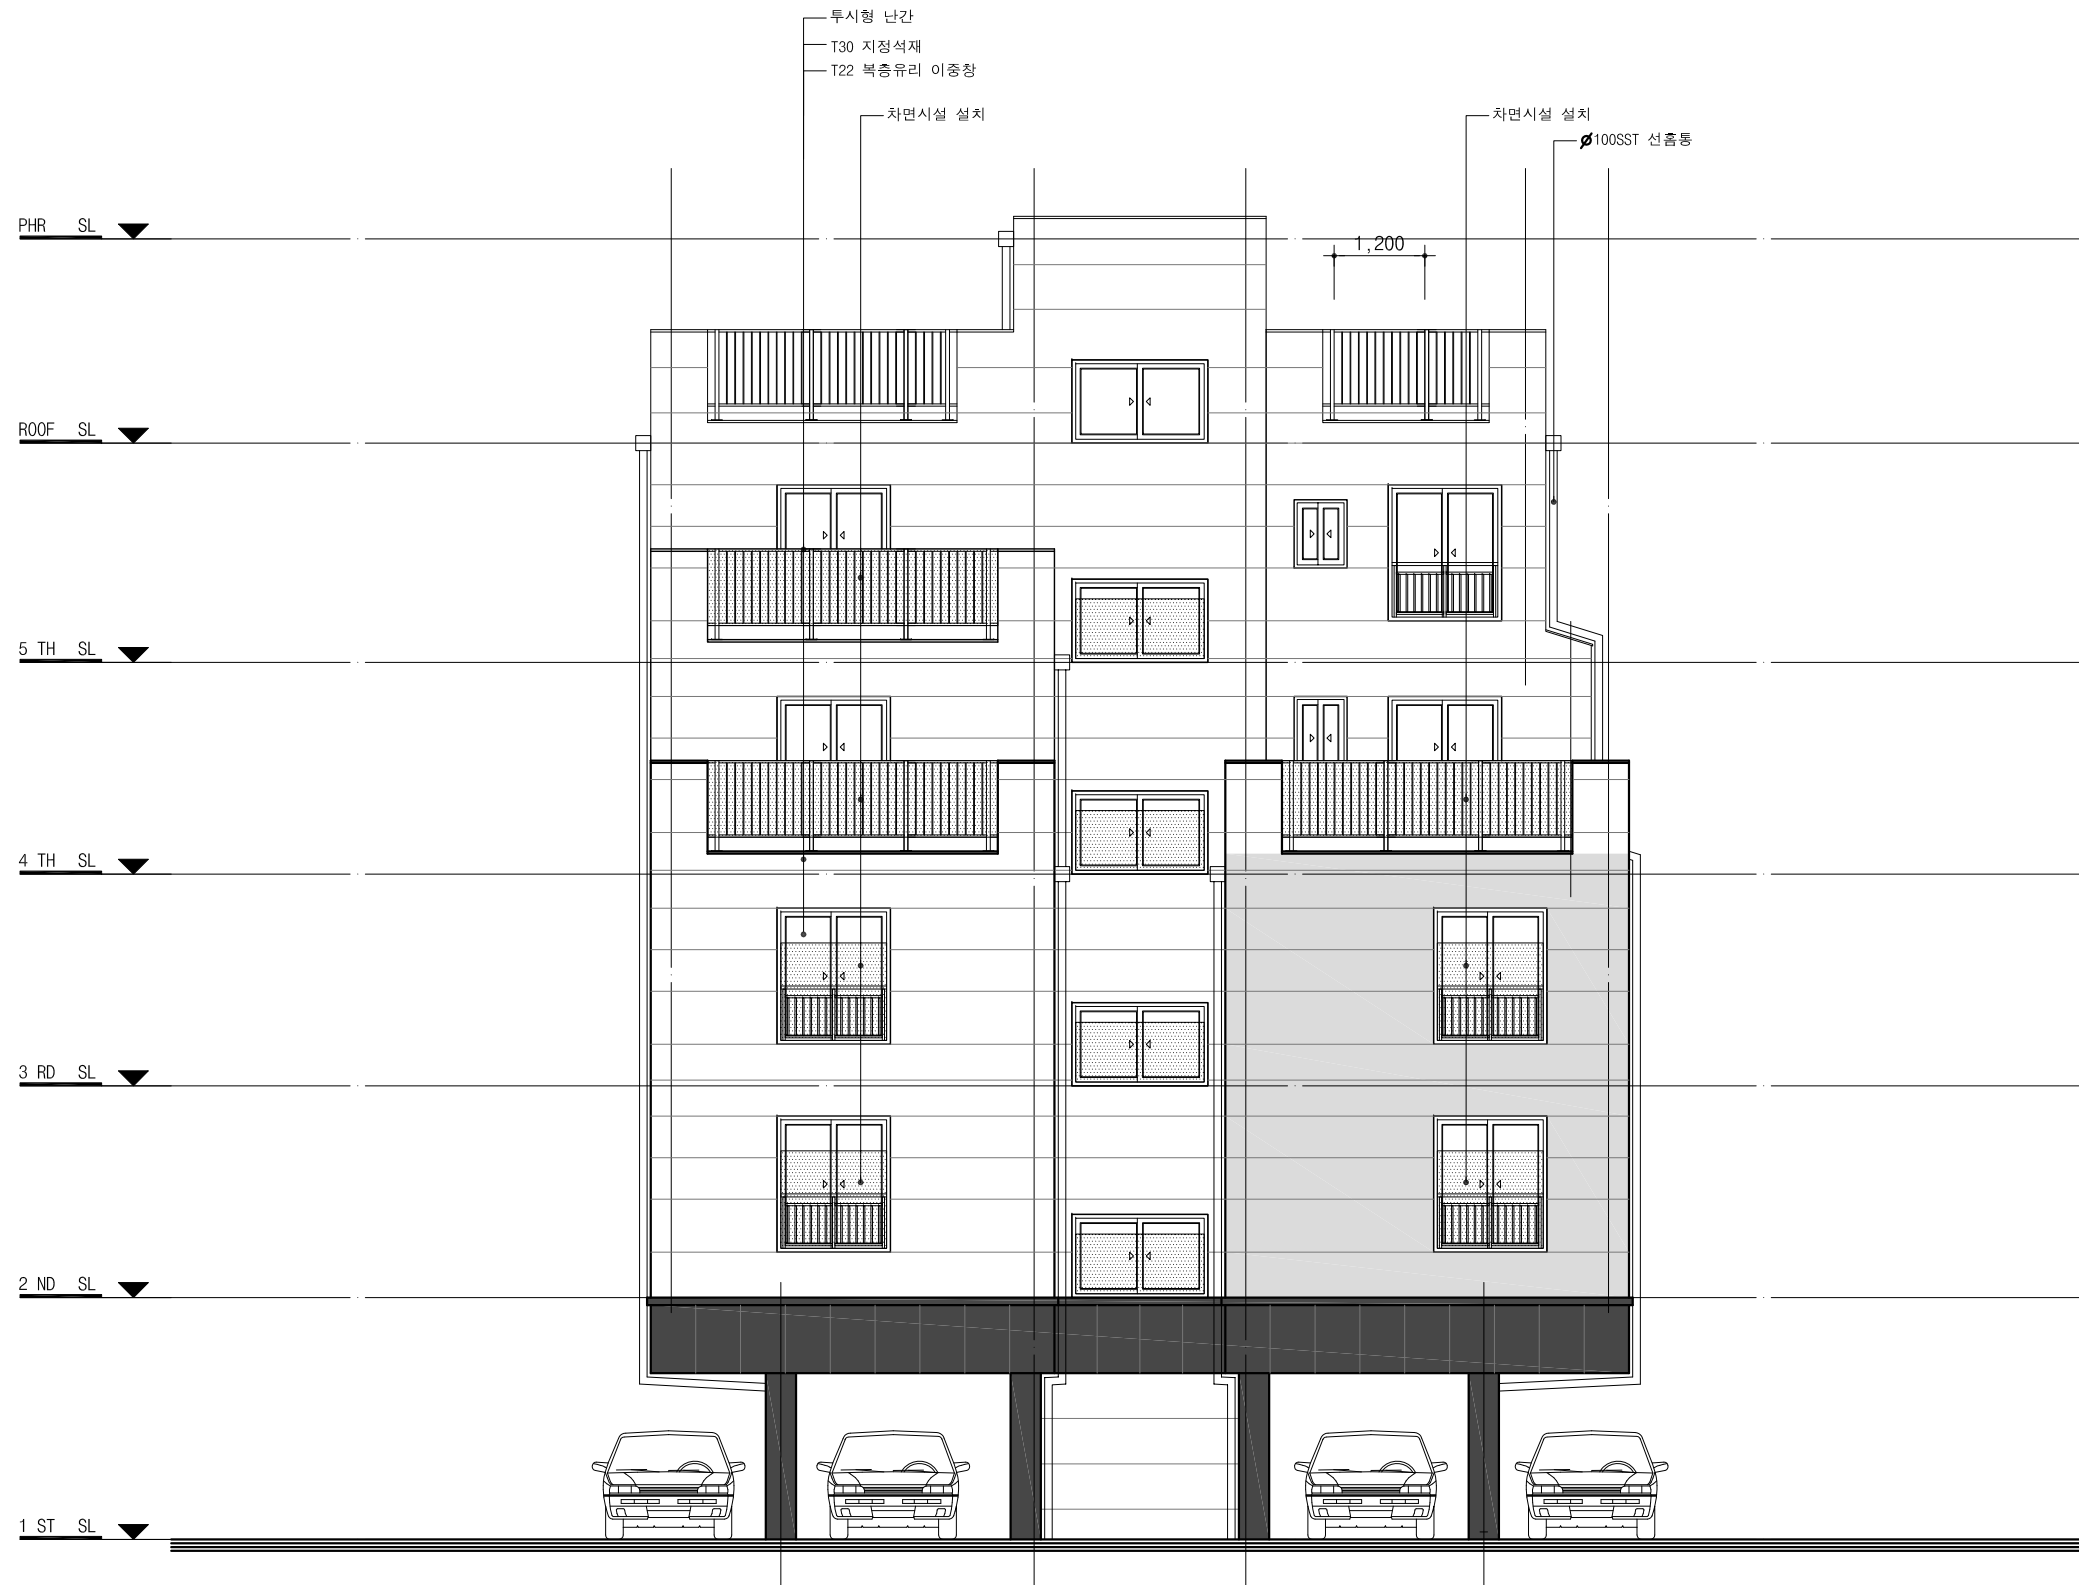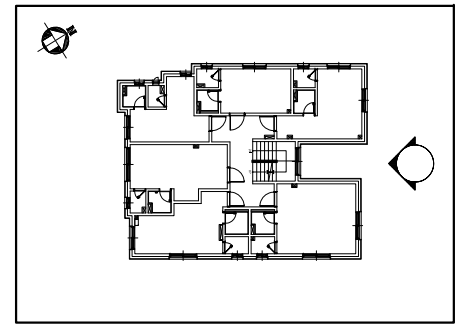

배 면 도
SCALE: 1/100

NOTE:

PROJECT
구로구 공동 190-84번지 외1필지
도시형 생활주택 (원룸형) 신축공사
APPROVED BY
건축사 구 연 목

ARCHITECTURE & ENGINEERING
건축사사무소 유일엔지니어링
서울특별시 서초구 반포대로 14길 71 (서초동)
LG서호에클라트(1904호)
TEL : 02) 540-1546, FAX : 02) 540-1576

TITLE
배 면 도

날짜
DATE: 2021. 08. .

SCALE	1 / 100	DWG NO.	A - 018	REV.
-------	---------	---------	---------	------