

1. 조 감 도




1. 투 시 도



2. 건축개요 및 현황도

건축개요

설 계 명 : 구로구 공동 190-84번지 외 1필지
도시형생활주택 (원룸형) 청년주택 신축공사
대지위치 : 서울특별시 구로구 공동 190 - 84 번지 외 1 필지
지역지구 : 제2종 일반주거지역 (7층이하)
건물용도 : 도시형 생활 주택(원룸형)
건물규모 : 지하 0층, 지상 5층
대지면적 : 294.80 m²
건축면적 : 172.87 m²
연 면 적 : 588.86 m²
건 폐 율 : 58.64 %
용 적 륜 : 199.75 %
최고높이 : 16.10 M
구 조 : 철근콘크리트조
주차대수 : 법정 6대, 계획 7대
조경면적 : 16.57 m²

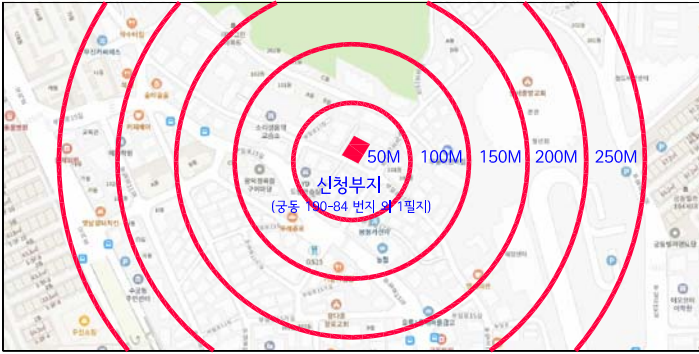

위 치 도



주변현황도

3. 입 면 도



정 면 도




좌 측 면 도




우 측 면 도



배 면 도

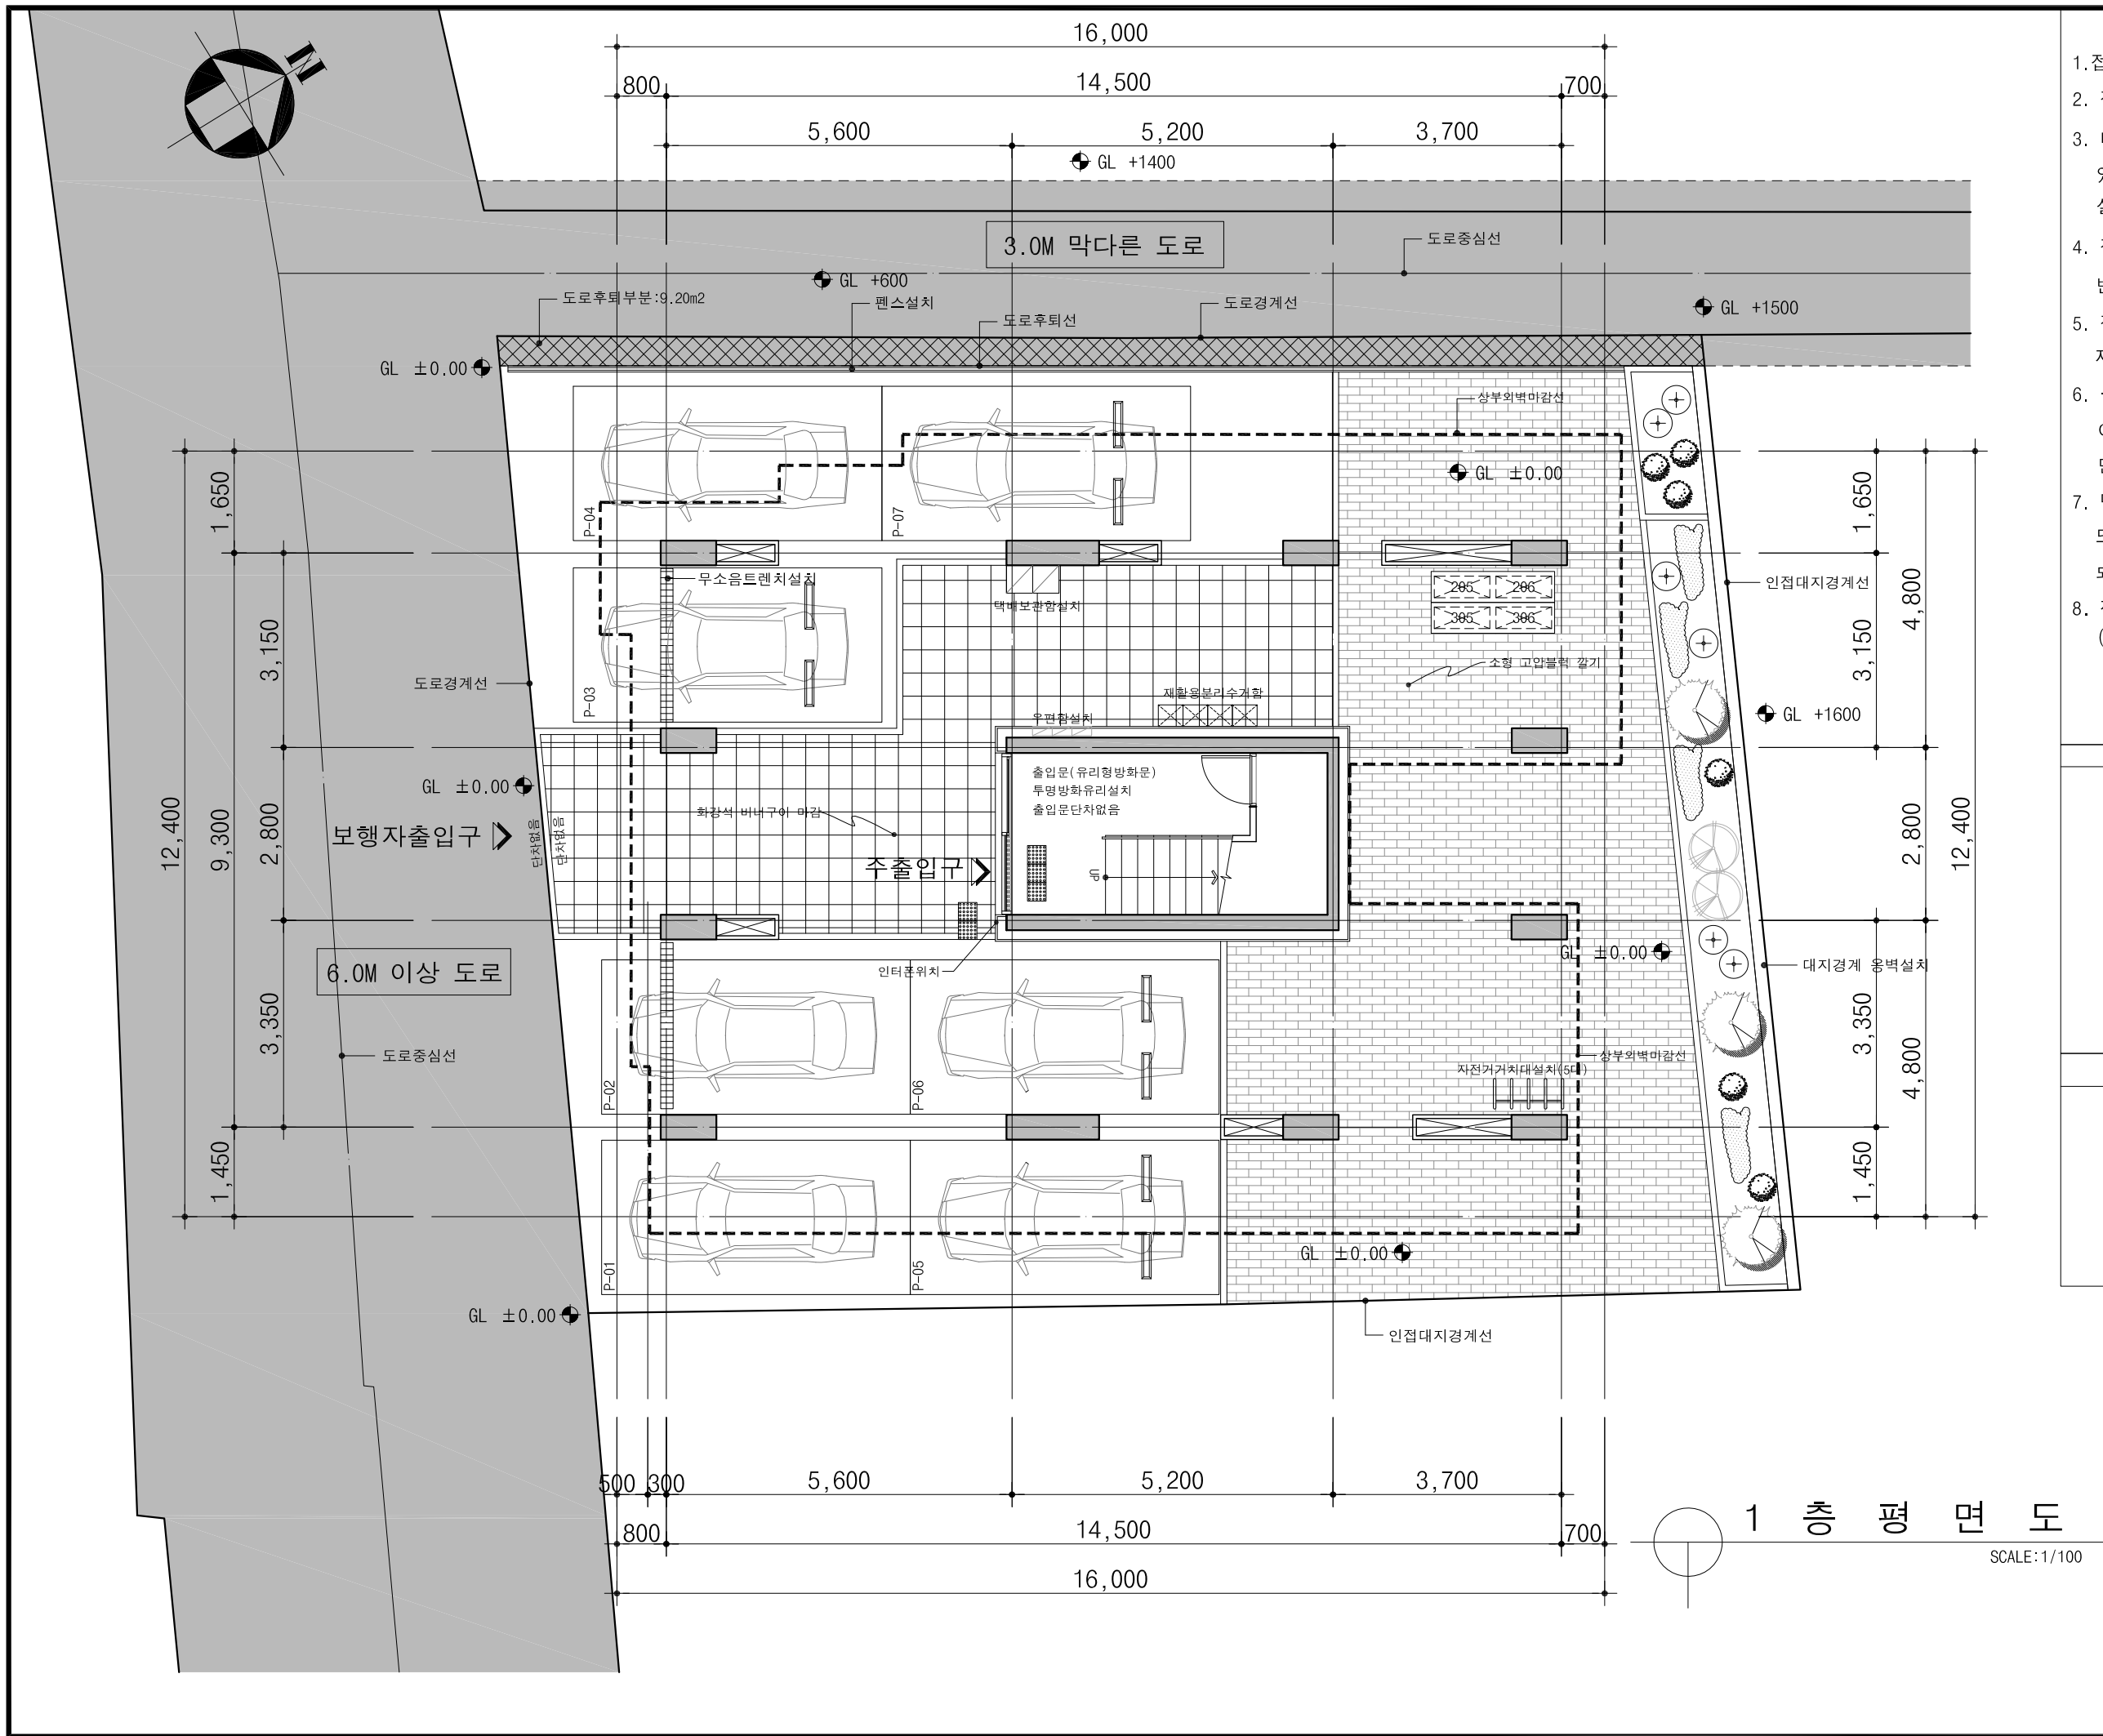

1. 접근로의 유효폭 1.2미터 이상 확보
2. 접근로의 기울기는 1/18 이하로 설치
3. 대지 내를 연결하는 주 접근로에 단차가 있을 경우 그 높이차는 2cm 이하가 되도록 설치
4. 접근로는 차도와 색상과 재질을 달리하여 반드시 보차분리를 명확히 해주어야 함
5. 접근로의 바닥 표면은 잘 미끄러지지 않는 재료로 평탄하게 마감하여야 함
6. 블록 등으로 접근로를 포장하는 경우에는 이음새의 틈이 벌어지지 아니하도록 하여 면이 평탄하게 시공하여야 함
7. 덮개를 설치할 경우 덮개에 격자구멍 또는 틈새의 양방향 간격이 2cm 이하가 되도록 설치
8. 점형블록은 매립형으로 설치함 (황색 K.S 제품)

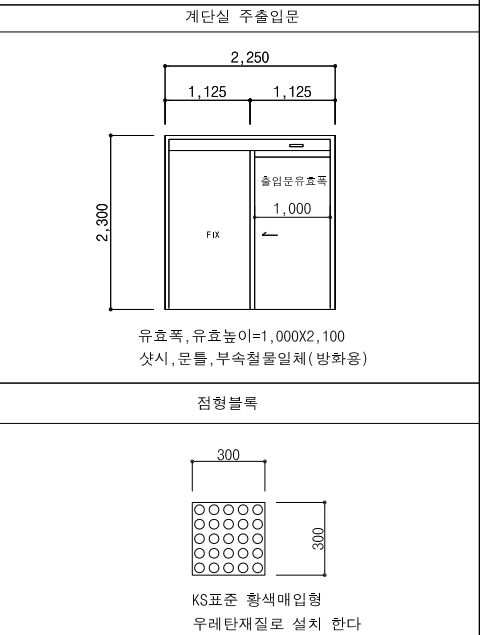

NOTE:

PROJECT
구로구 공동 190-84번지 외1필지
도시형 생활주택 (원룸형) 신축공사
APPROVED BY
건축사 구 연 목


ARCHITECTURE & ENGINEERING
건축사사무소 유일엔지니어링
서울특별시 서초구 반포대로 14길 71 (서초동)
LG서호에클리트(1904호)
TEL : 02) 540-1546, FAX : 02) 540-1576

TITLE
1 층 평 면 도

날짜
DATE: 2021. 08. .

SCALE 1 / 100 DWG NO. A - 008 REV.

1 층 평 면 도
SCALE: 1/100

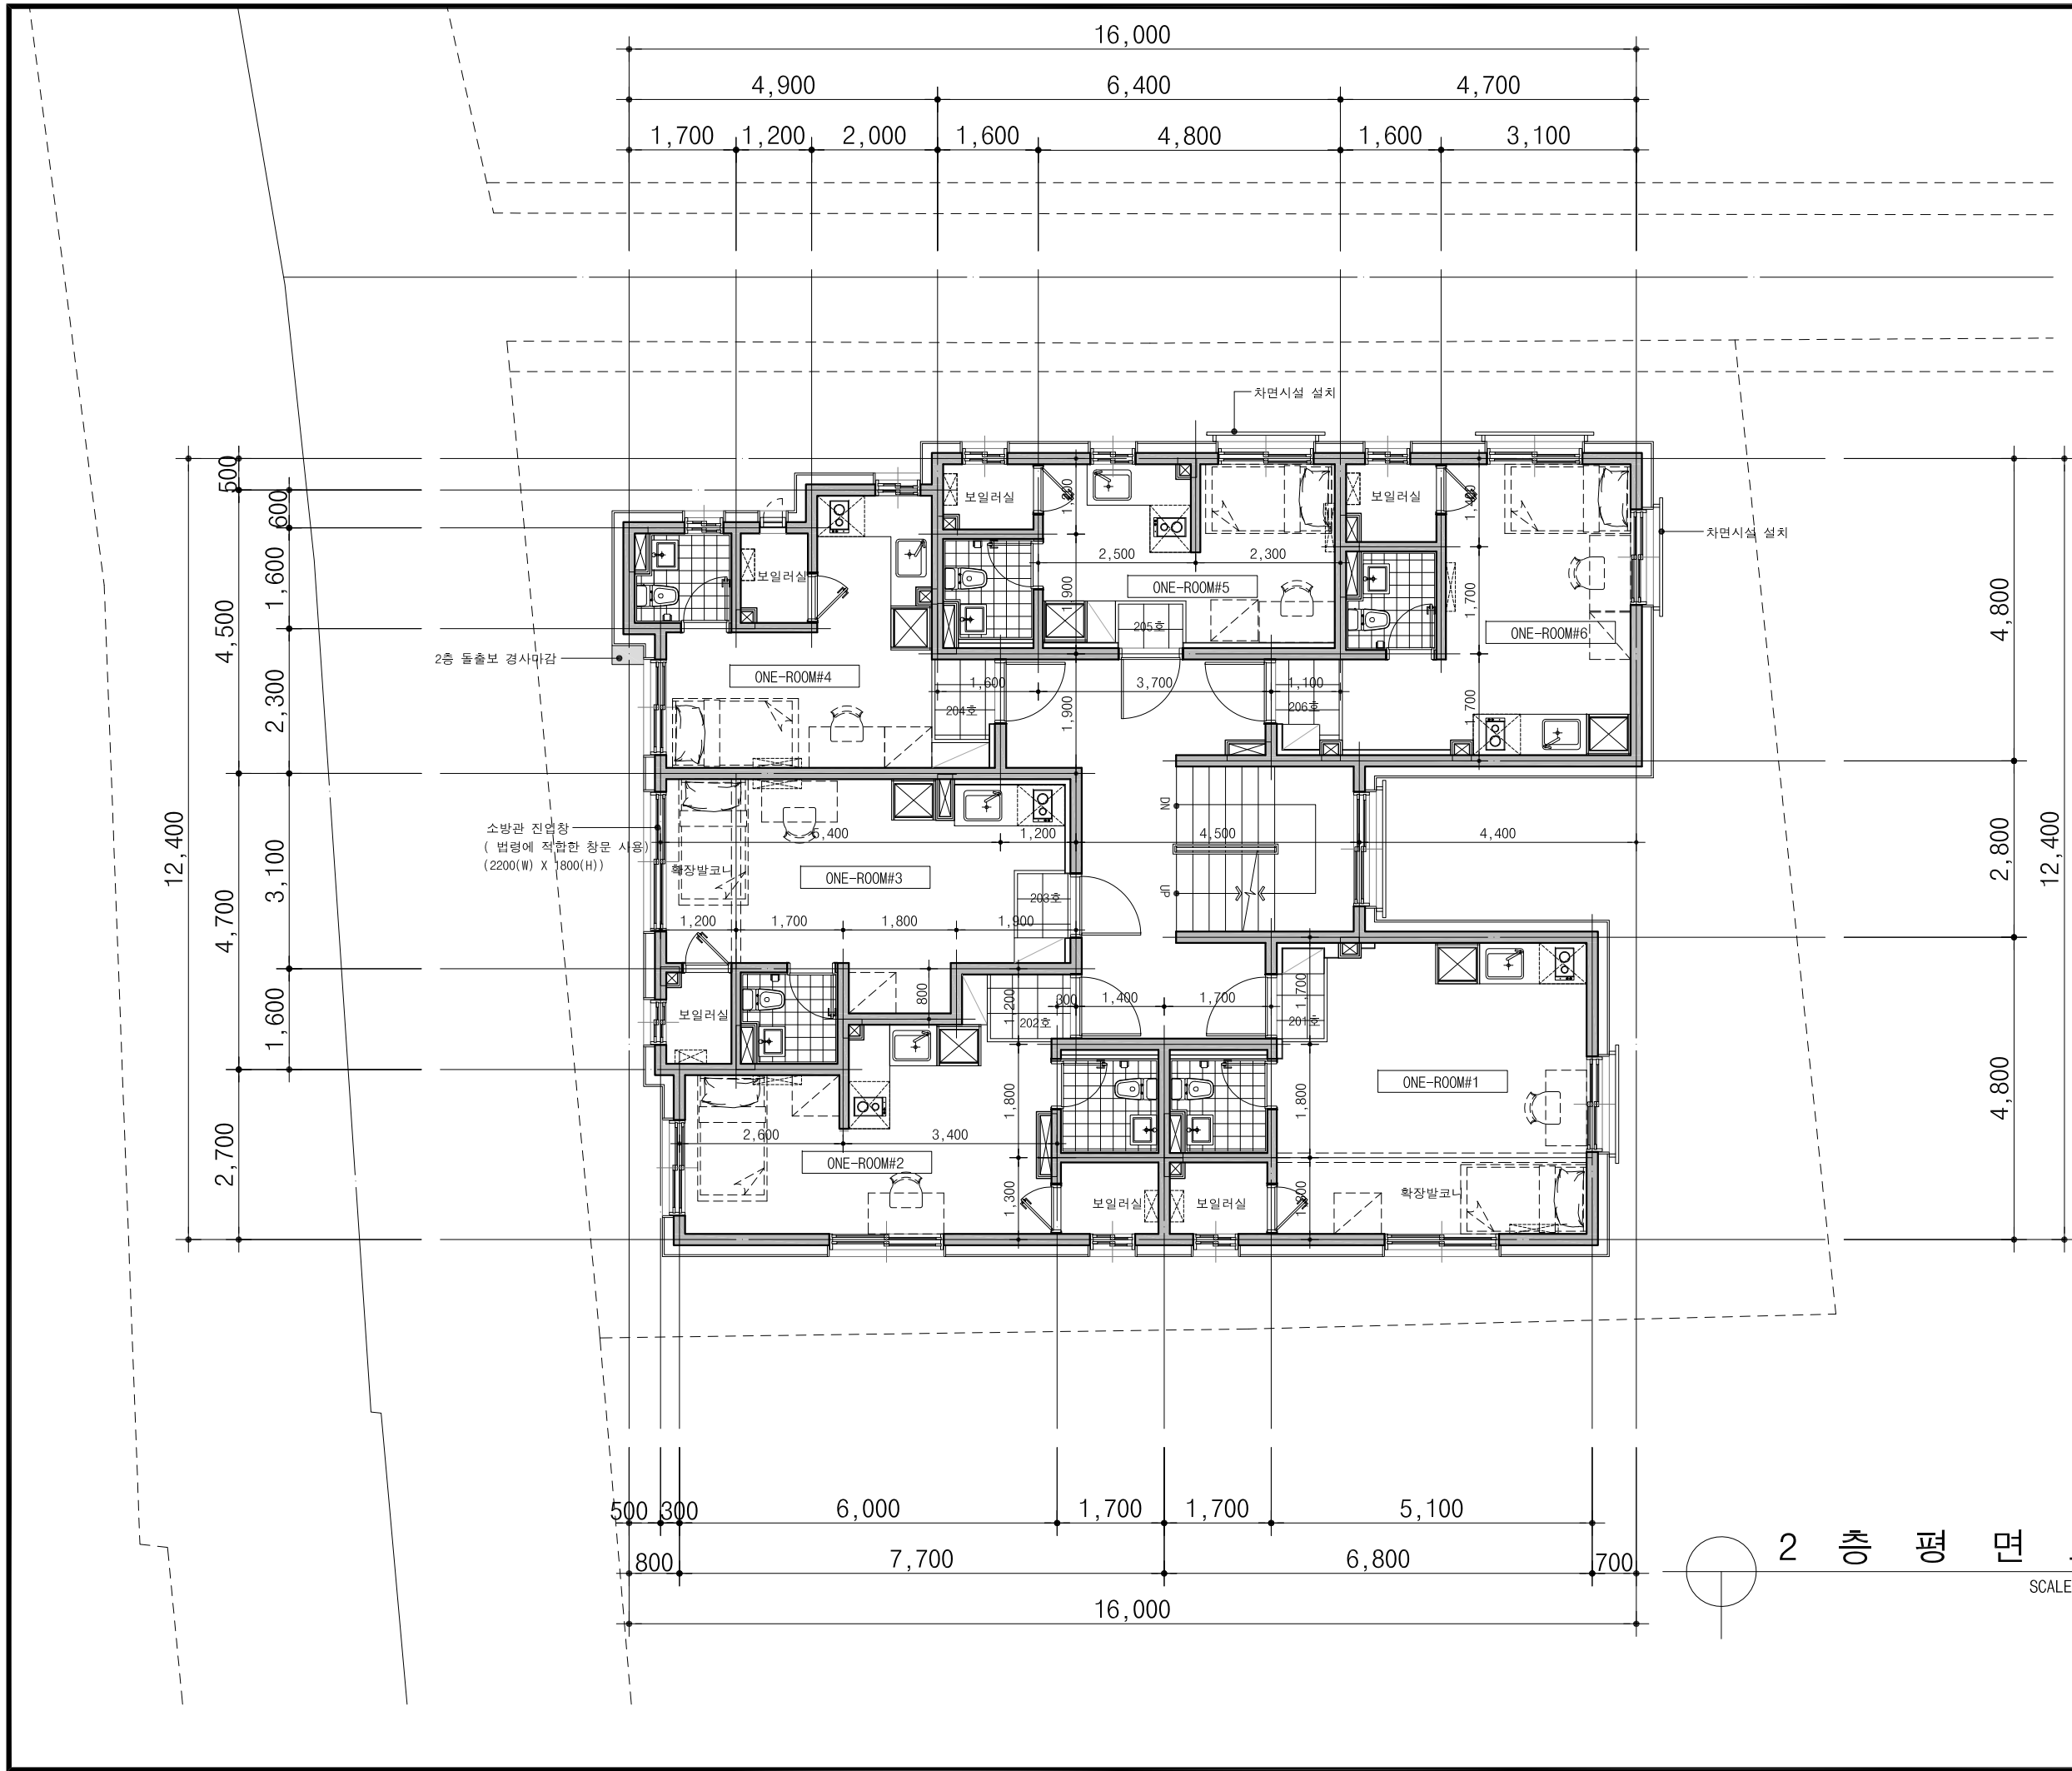

2 층 평 면 도
SCALE: 1/100

주 기		
1	세대 현관문 도어체크 및 스토퍼 계획	
2	세대 발코니 설치시 세대간 분리벽 계획	
3	세대내 비디오폰 설치	
4	주차장내 CCTV 설치	
5	벽체	외벽 직접 외기에 면한 실내벽면은 단열재 (아이소핑크10mm+석고보드 마감도면 표기) 계단실 간접 외기에 면한 실내벽면은 단열재 /복도 (경질우레탄80mm+석고보드 마감도면 표기)
6	에어콘 실외기 설치위치 및 에어컨 도면표기)	
7	불박이 가구 내부 다용도 수납가능토록 수평이동 칸막이 설치	
8	콘크리트 폼타이 제거후 마감공사 시공(방수 및 단열재 시공등)	
9	구조	콘크리트 : fck=24Mpa 철근 : fy=400Mpa 세대 벽두께 : 150mm(복배근) 외벽 벽두께 : 180mm(복배근) 코아 벽두께 : 180mm(복배근) 2층 슬라브 두께 : 180mm(복배근) 3-5층 슬라브 두께 : 210mm(복배근)
10	기타 실내 벽면은 시멘트 미장마감	
11	욕실 & 다용도실 스위치 : 문열리는 방향으로 시공	
12	공동주택 바닥충격음 차단구조기준	
2층		
13	소방관 진입창의 기준	건축물의 피난방화구조등의 기준에 관한규칙 제18조의2에 의거 1. 2층이상 11층이하인 층에 각각 1개소 이상설치 2. 소방차진입로또는 소방차 진입이 가능한 공터에 면할것 3. 창문 가운데 Ø200이상의 역삼각형을 아간에 식별가능하도록 설치.(반사 등으로 붉은색으로 표시) 4. 창문 한쪽 모서리에 타격지점 표시 (Ø30 이상의 원형) 5. 창문크기 : 폭900 높이1,200이상 (바닥에서 창아랫부분 높이800이내로 설치) 6. 다음 각 목의 어느 하나에 해당하는 유리 사용할 것 가. 플로트판유리로서 두께6mm이하인것 나. 강화유리/배강도유리로서 두께5mm이하인것 다. 위의 유리로 구성된 이중유리로서 두께24mm 이하인것
14	외기에 간접면하는 부분 : THK80 경질우레탄폼 2중2호 설치	
호실 계단실 호실		

NOTE:


PROJECT 구로구 공동 190-84번지 외1필지 도시형 생활주택 (원룸형)신축공사			
APPROVED BY 건축사 구 연 목			
ARCHITECTURE & ENGINEERING 건축사사무소 유일엔지니어링 서울특별시 서초구 반포대로 14길 71(서초동) LG서초에클리트(1904호) TEL : 02) 540-1546, FAX : 02)540-1576			
TITLE 2 층 평 면 도			
날짜 DATE: 2021. 08. .			
SCALE	1 / 100	DWG NO.	A - 009
			REV.



주 기	
1	세대 현관문 도어체크 및 스톱퍼 계획
2	세대 발코니 설치시 세대간 분리벽 계획
3	세대내 비디오폰 설치
4	주차장내 CCTV 설치
5	벽체
	외벽 직접 외기에 면한 실내벽면은 단열재 (아소스프크10mm+석고보드 마감도면 표기) 계단실/복도 간접 외기에 면한 실내벽면은 단열재 (경질우레탄80mm+석고보드 마감도면 표기)
6	에어콘 실외기 설치위치 및 에어컨 도면표기)
7	불박이 가구 내부 다용도 수납기능토록 수평이동 칸막이 설치
8	콘크리트 폼라이 제거후 마감공사 시공(방수 및 단열재 시공등)
9	구조
	콘크리트 : $f_{ck}=24\text{Mpa}$ 철근 : $f_y=400\text{Mpa}$ 세대 벽두께 : 150mm (복배근) 외벽 벽두께 : 180mm (복배근) 코아 벽두께 : 180mm (복배근) 2층 슬라브 두께 : 180mm (복배근) 3~5층 슬라브 두께 : 210mm (복배근)
10	기타 실내 벽면은 시멘트 미장마감
11	욕실 & 다용도실 스위치 : 문열리는 방향으로 시공
12	공동주택 바닥충격률 차단구조기준
3층, 4층, 5층	
13	소방관 진입창의 기준
	건축물의 피난방화구조등의 기준에 관한규칙 제18조의2에 의거 1. 2층이상 11층이하인 층에 각각 1개소 이상설치 2. 소방차진입로되는 소방차 진입이 가능한 공터에 면할것 3. 창문 가우에 $\varnothing 200$이상의 역삼각형틀 아간에 식별가능하도록 설치. (반사 등으로 붉은색으로 표시) 4. 창문 한쪽 모서리에 타격지점 표시 ($\varnothing 30$ 이상의 원형) 5. 창문크기 : 폭900 높이1,200이상 (바닥에서 창아랫부분 높이800이내로 설치) 6. 다음 각 목의 어느 하나에 해당하는 유리 사용할 것 가. 플리트판유리로서 두께6mm이하인것 나. 강화유리/배강도유리로서 두께5mm이하인것 다. 위의 유리로 구성된 이중유리로서 두께24mm 이하인것
14	외기에 간접연하는 부분 : THK80 경질우레탄폼 2중2호 설치
	석고보드위벽지마감 T80경질폴리우레탄폼단열재2중2호 T180철콘크리트벽 계단실 호실 석고보드위벽지마감 T80경질폴리우레탄폼단열재2중2호 T180철콘크리트벽 호실

NOTE:

PROJECT 구로구 공동 190-84번지 외1필지 도시형 생활주택 (원룸형)신축공사			
APPROVED BY		건축사 구 연 목	
		건축사사무소 유일엔지니어링	
서울특별시 서초구 반포대로 14길71(서초동) LG서초에클라트(1904호) TEL : 02) 540-1546, FAX : 02)540-1576			
TITLE		3 층 평 면 도	
날짜 DATE:		2021. 08. .	
SCALE	1 / 100	DWG NO.	A - 010
		REV.	

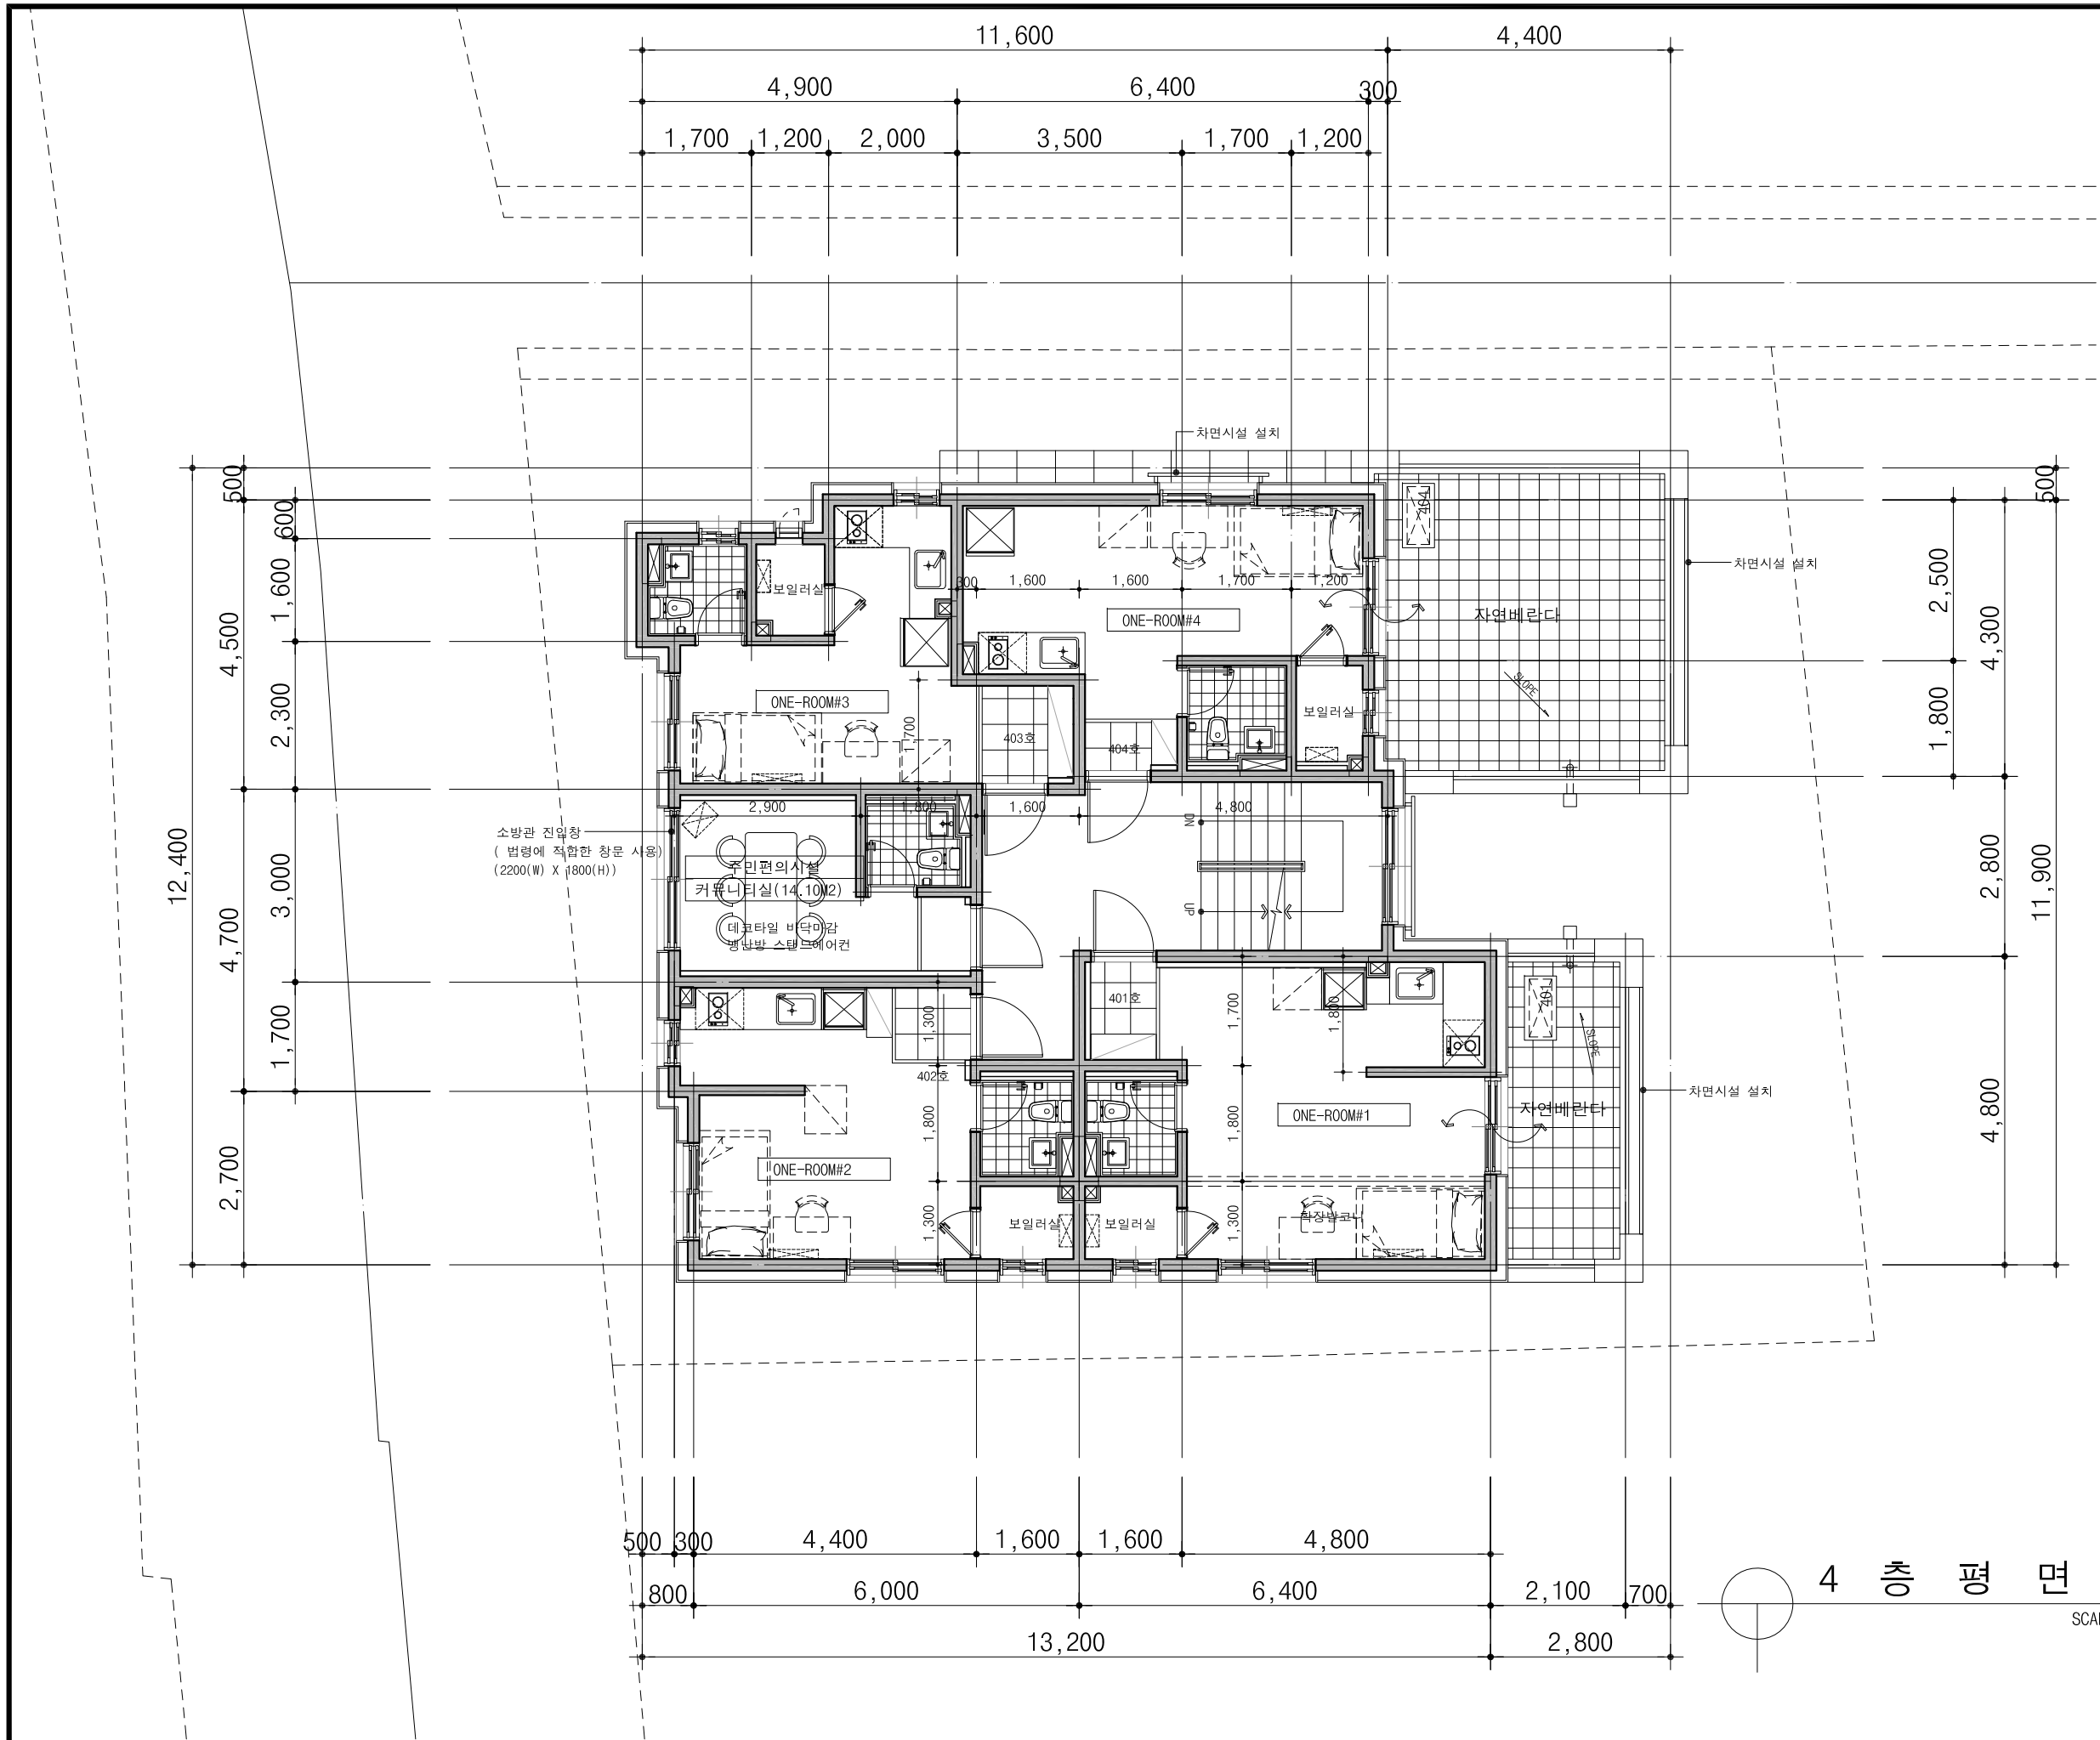

주 기		
1	세대 현관문 도어체크 및 스토퍼 계획	
2	세대 발코니 설치시 세대간 분리벽 계획	
3	세대내 비디오폰 설치	
4	주차장내 CCTV 설치	
5	벽체	외벽 직접 외기에 면한 실내벽면은 단열재 (아이소핑크10mm+석고보드 마감도면 표기) 계단실 간접 외기에 면한 실내벽면은 단열재 /복도 (경질우레탄80mm+석고보드 마감도면 표기)
6	에어콘 실외기 설치위치 및 에어컨 도면표기)	
7	불박이 가구 내부 다용도 수납가능토록 수평이동 칸막이 설치	
8	콘크리트 폼타이 제거후 마감공사 시공(방수 및 단열재 시공등)	
9	구조	콘크리트 : fck=24Mpa 철근 : fy=400Mpa 세대 벽두께 : 150mm(복배근) 외벽 벽두께 : 180mm(복배근) 코아 벽두께 : 180mm(복배근) 2층 슬라브 두께 : 180mm(복배근) 3-5층 슬라브 두께 : 210mm(복배근)
10	기타 실내 벽면은 시멘트 미장마감	
11	욕실 & 다용도실 스위치 : 문열리는 방향으로 시공	
12	공동주택 바닥충격음 차단구조기준	
3층, 4층, 5층		절緣材(PVC) 데크타일마감(2.2T이상) T=40 시멘트충진(1:3, 평창채 혼입) T=40 경질우레탄콘크리트 T≤30 완충재(EPS계열) T≤210 콘크리트슬라브
13	소방관 진입창의 기준	건축물의 피난방화구조등의 기준에 관한규칙 제18조의2에 의거 1. 2층이상 11층이하인 층에 각각 1개소 이상설치 2. 소방차진입로또는 소방차 진입이 가능한 공터에 면할것 3. 창문 가운데 Ø200이상의 역삼각형을 야간에 식별가능하도록 설치.(반사 등으로 붉은색으로 표시) 4. 창문 한쪽 모서리에 타격지점 표시 (Ø30 이상의 원형) 5. 창문크기 : 폭900 높이1,200이상 (바닥에서 창아랫부분 높이800이내로 설치) 6. 다음 각 목의 어느 하나에 해당하는 유리 사용할 것 가. 플로트판유리로서 두께6mm이하인것 나. 강화유리/배강도유리로서 두께5mm이하인것 다. 위의 유리로 구성된 이중유리로서 두께24mm 이하인것
14	외기에 간접면하는 부분 : THK80 경질우레탄폼 2중2호 설치	
호실 계단실 호실		

NOTE:

PROJECT
구로구 공동 190-84번지 외1필지
도시형 생활주택 (원룸형)신축공사

APPROVED BY
건축사 구 연 목


건축사사무소 유일엔지니어링
서울특별시 서초구 반포대로 14길 71(서초동)
LG서호에클리트(1904호)
TEL : 02) 540-1546, FAX : 02)540-1576

TITLE
4 층 평 면 도

날짜
DATE: 2021. 08. .

SCALE 1 / 100 DWG NO. A - 011 REV.

4 층 평 면 도
SCALE: 1/100

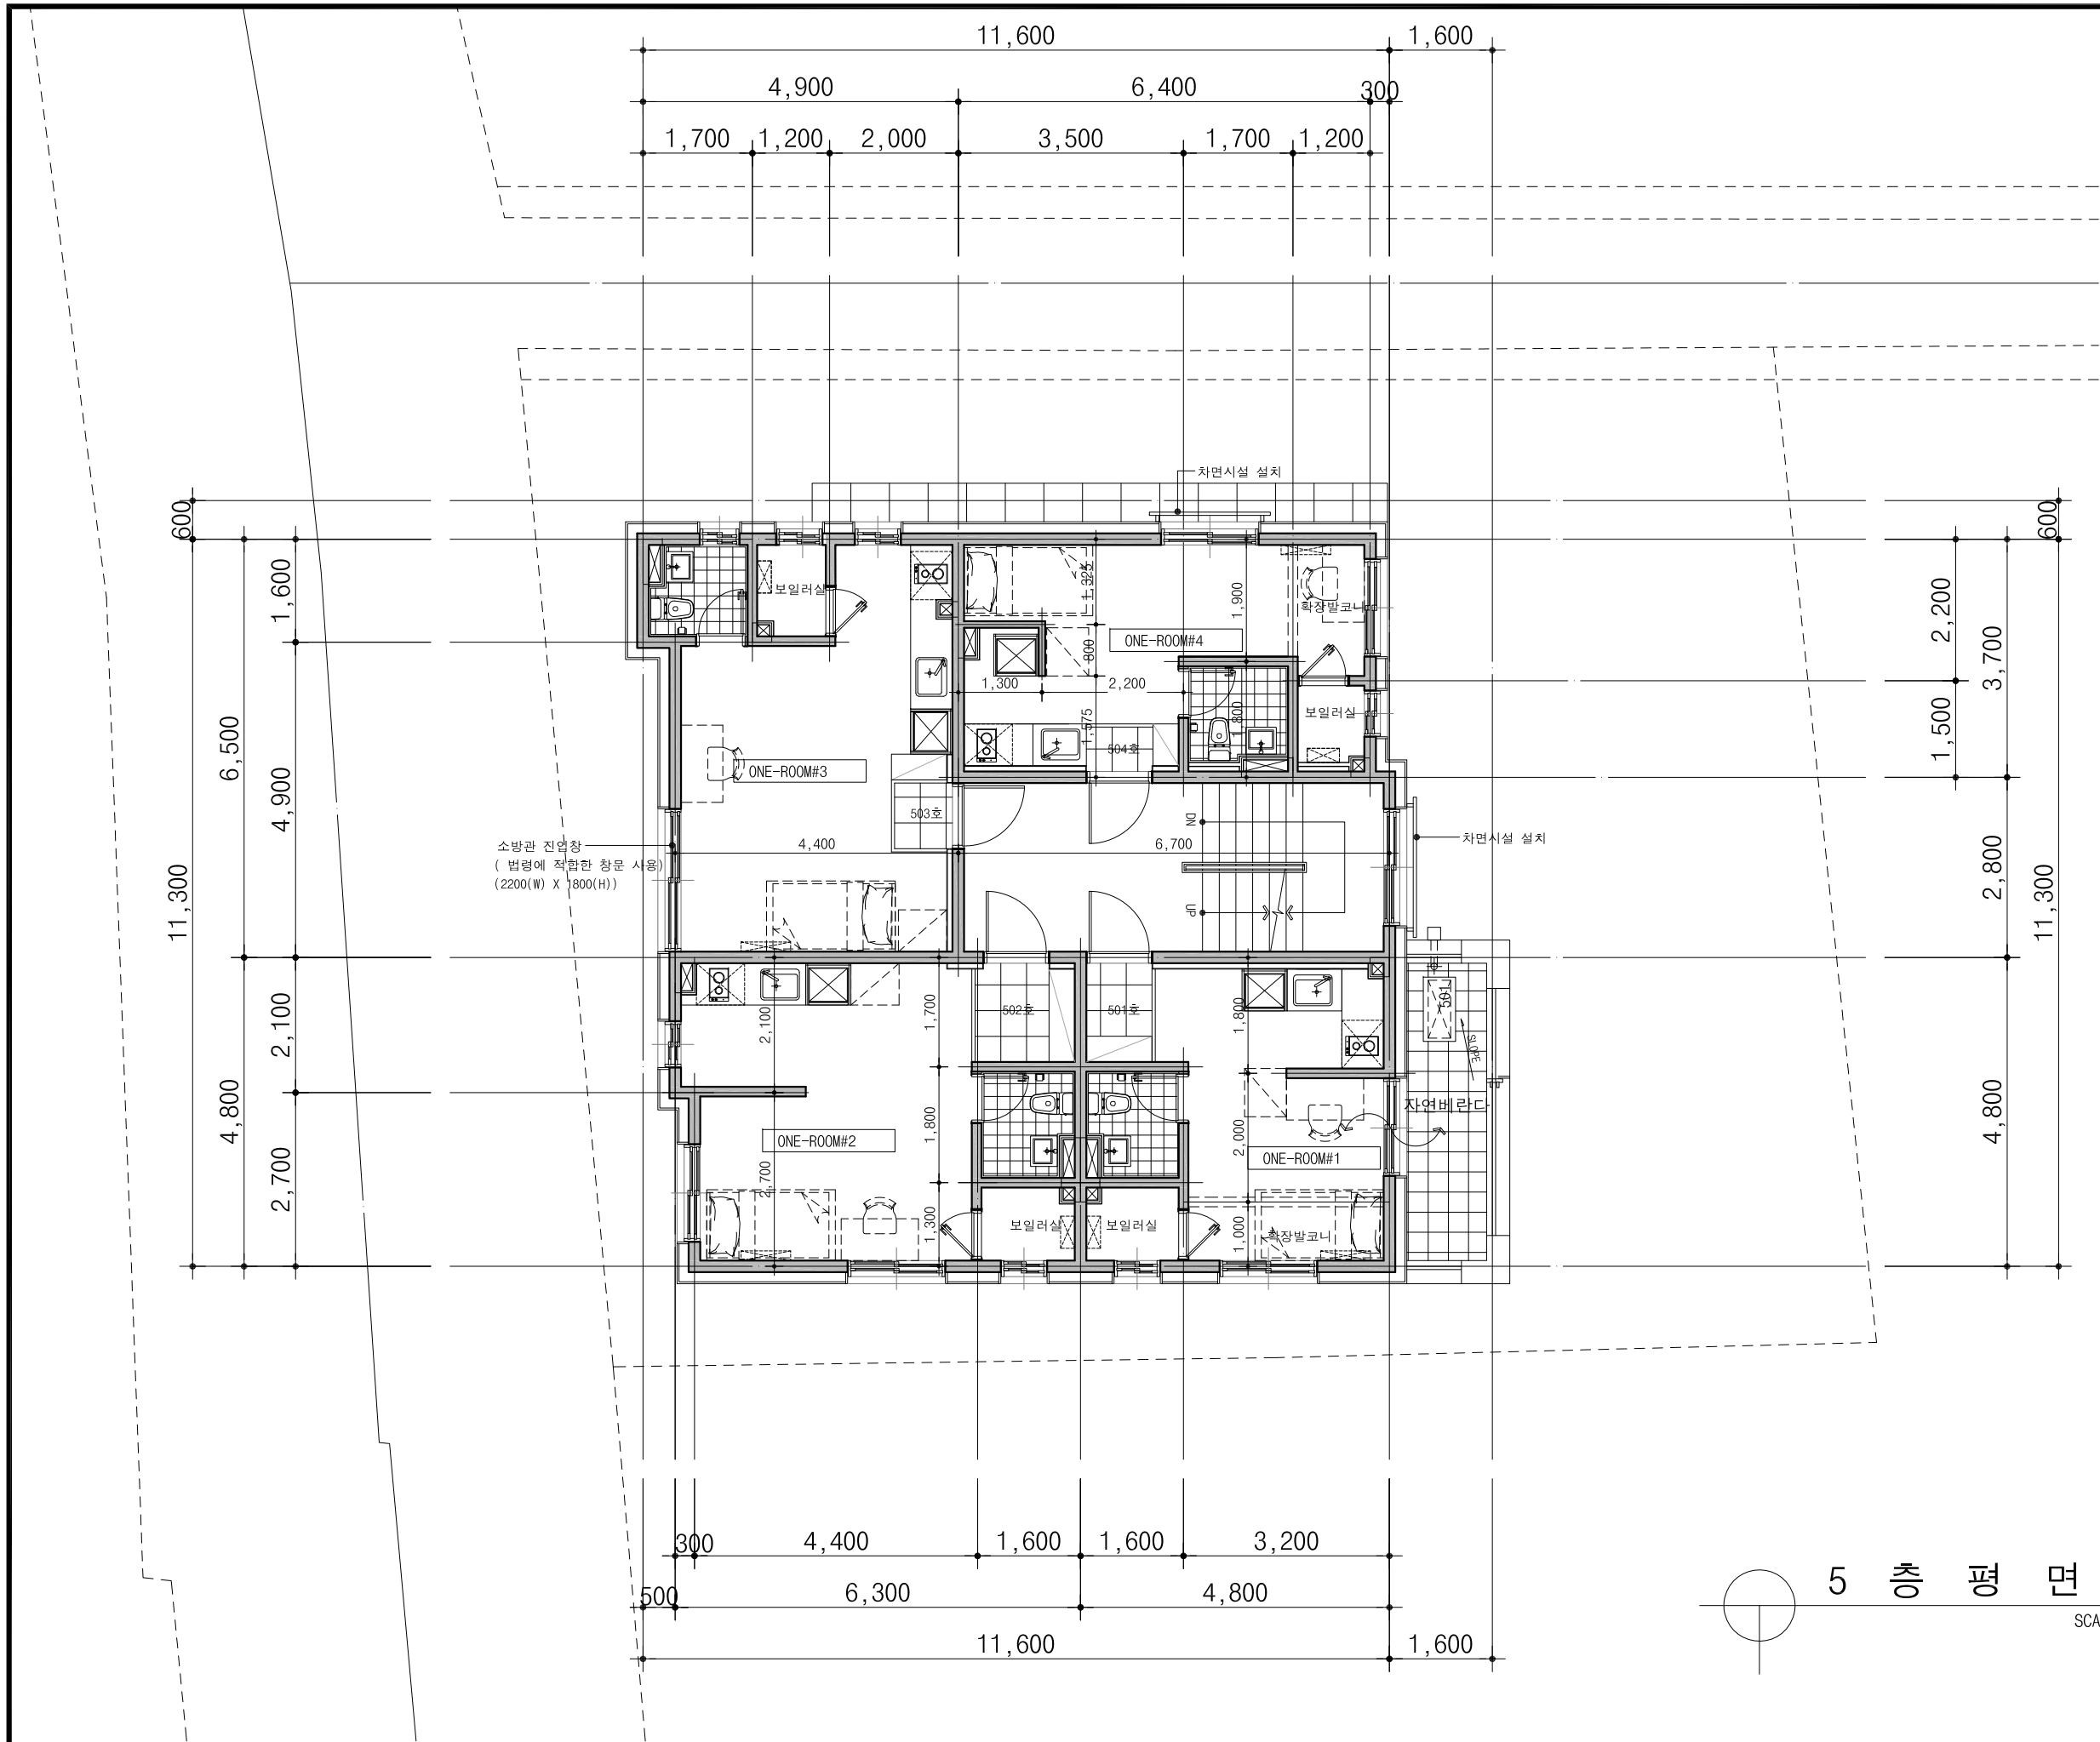

5 층 평 면 도
SCALE: 1/100

주 기		
1	세대 현관문 도어체크 및 스토퍼 계획	
2	세대 발코니 설치시 세대간 분리벽 계획	
3	세대내 비디오폰 설치	
4	주차장내 CCTV 설치	
5	벽체	외벽 직접 외기에 면한 실내벽면은 단열재 (아이소핑크10mm+석고보드 마감도면 표기) 계단실 간접 외기에 면한 실내벽면은 단열재 /복도 (경질우레탄80mm+석고보드 마감도면 표기)
6	에어콘 실외기 설치위치 및 에어컨 도면표기)	
7	불박이 가구 내부 다용도 수납가능토록 수평이동 칸막이 설치	
8	콘크리트 폼타이 제거후 마감공사 시공(방수 및 단열재 시공등)	
9	구조	콘크리트 : fck=24Mpa 철근 : fy=400Mpa 세대 벽두께 : 150mm(복배근) 외벽 벽두께 : 180mm(복배근) 코아 벽두께 : 180mm(복배근) 2층 슬라브 두께 : 180mm(복배근) 3-5층 슬라브 두께 : 210mm(복배근)
10	기타 실내 벽면은 시멘트 미장마감	
11	욕실 & 다용도실 스위치 : 문열리는 방향으로 시공	
12	공동주택 바닥충격음 차단구조기준	
3층, 4층, 5층		
13	소방관 진입창의 기준	건축물의 피난방화구조등의 기준에 관한규칙 제18조의2에 의거 1. 2층이상 11층이하인 층에 각각 1개소 이상설치 2. 소방차진입로또는 소방차 진입이 가능한 공터에 면할것 3. 창문 가운데 Ø200이상의 역삼각형을 아간에 식별가능하도록 설치.(반사 등으로 붉은색으로 표시) 4. 창문 한쪽 모서리에 타격지점 표시 (Ø30 이상의 원형) 5. 창문크기 : 폭900 높이1,200이상 (바닥에서 창아랫부분 높이800이내로 설치) 6. 다음 각 목의 어느 하나에 해당하는 유리 사용할 것 가. 플로트판유리로서 두께6mm이하인것 나. 강화유리/배강도유리로서 두께5mm이하인것 다. 위의 유리로 구성된 이중유리로서 두께24mm 이하인것
14	외기에 간접면하는 부분 : THK80 경질우레탄폼 2중2호 설치	

NOTE:

PROJECT
구로구 공동 190-84번지 외1필지
도시형 생활주택 (원룸형)신축공사


APPROVED BY
건축사 구 연 목


건축사사무소 유일엔지니어링
서울특별시 서초구 반포대로 14길 71(서초동)
LG서호에클리트(1904호)
TEL : 02) 540-1546, FAX : 02)540-1576

TITLE
5 층 평 면 도

날짜
DATE: 2021. 08. .


SCALE 1 / 100 DWG NO. A - 012 REV.

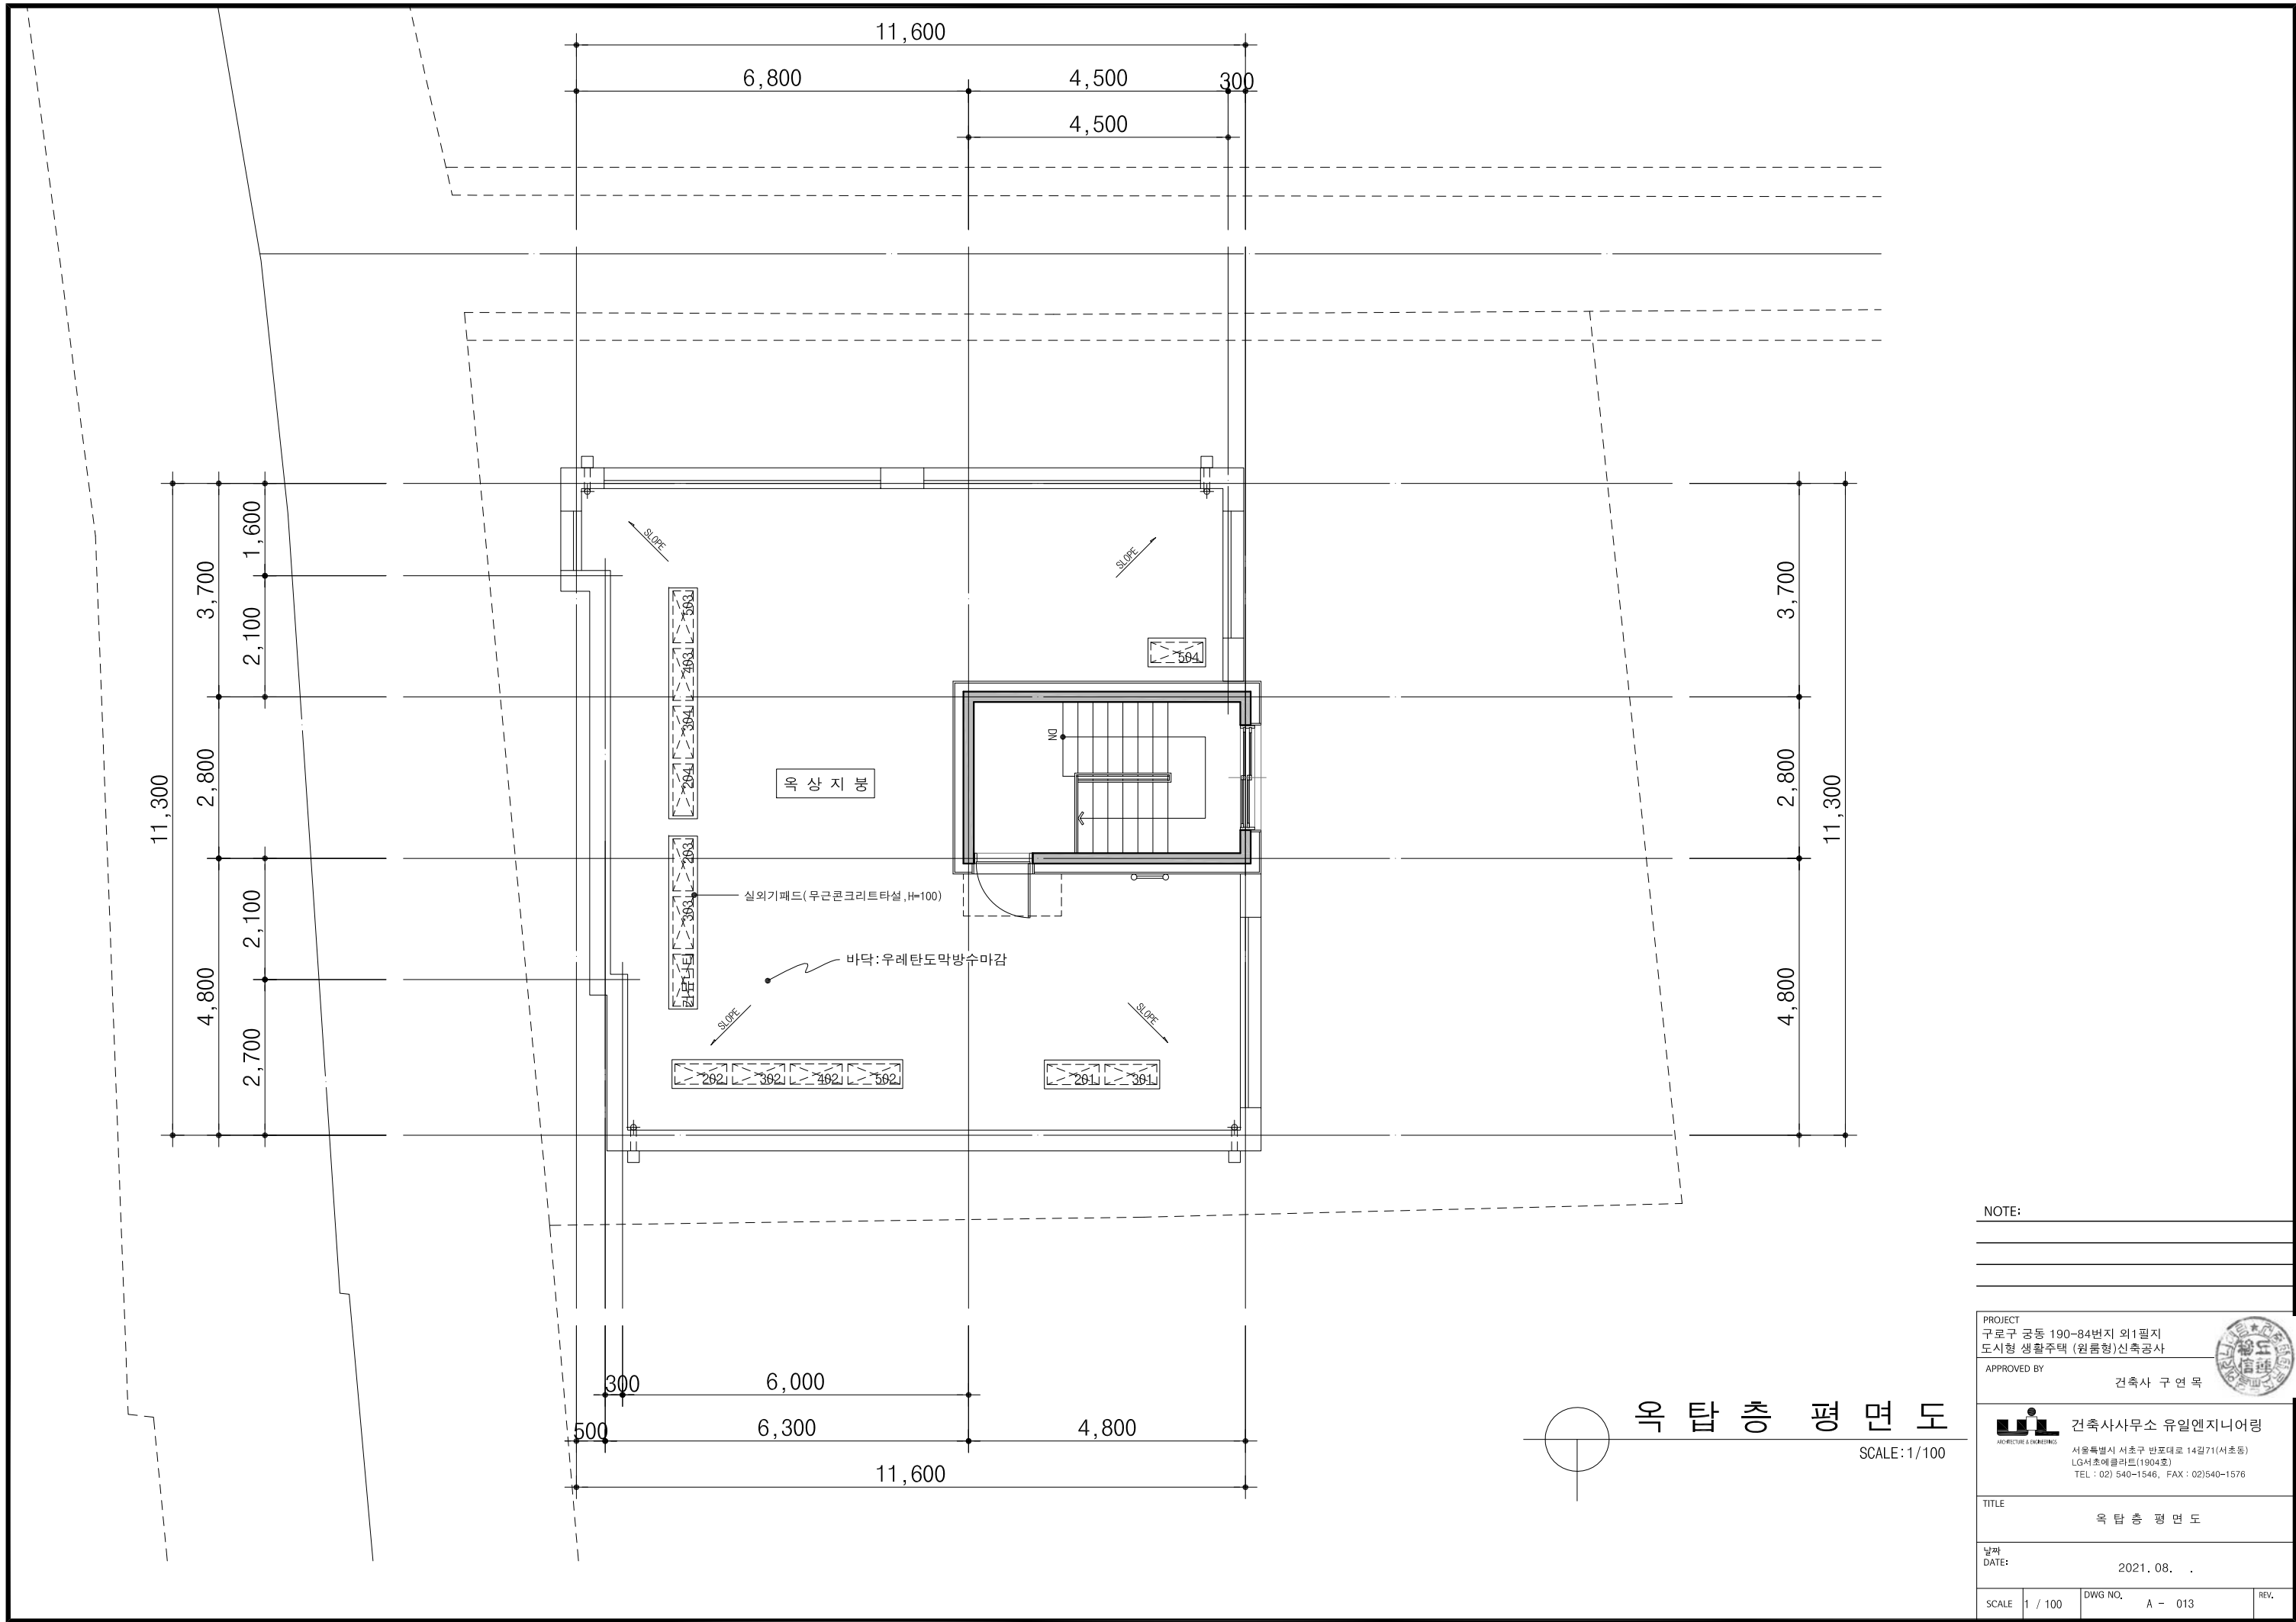

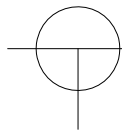


SCALE:1/100

SCALE	1 / 100	DWG NO.	A - 014	REV.
-------	---------	---------	---------	------

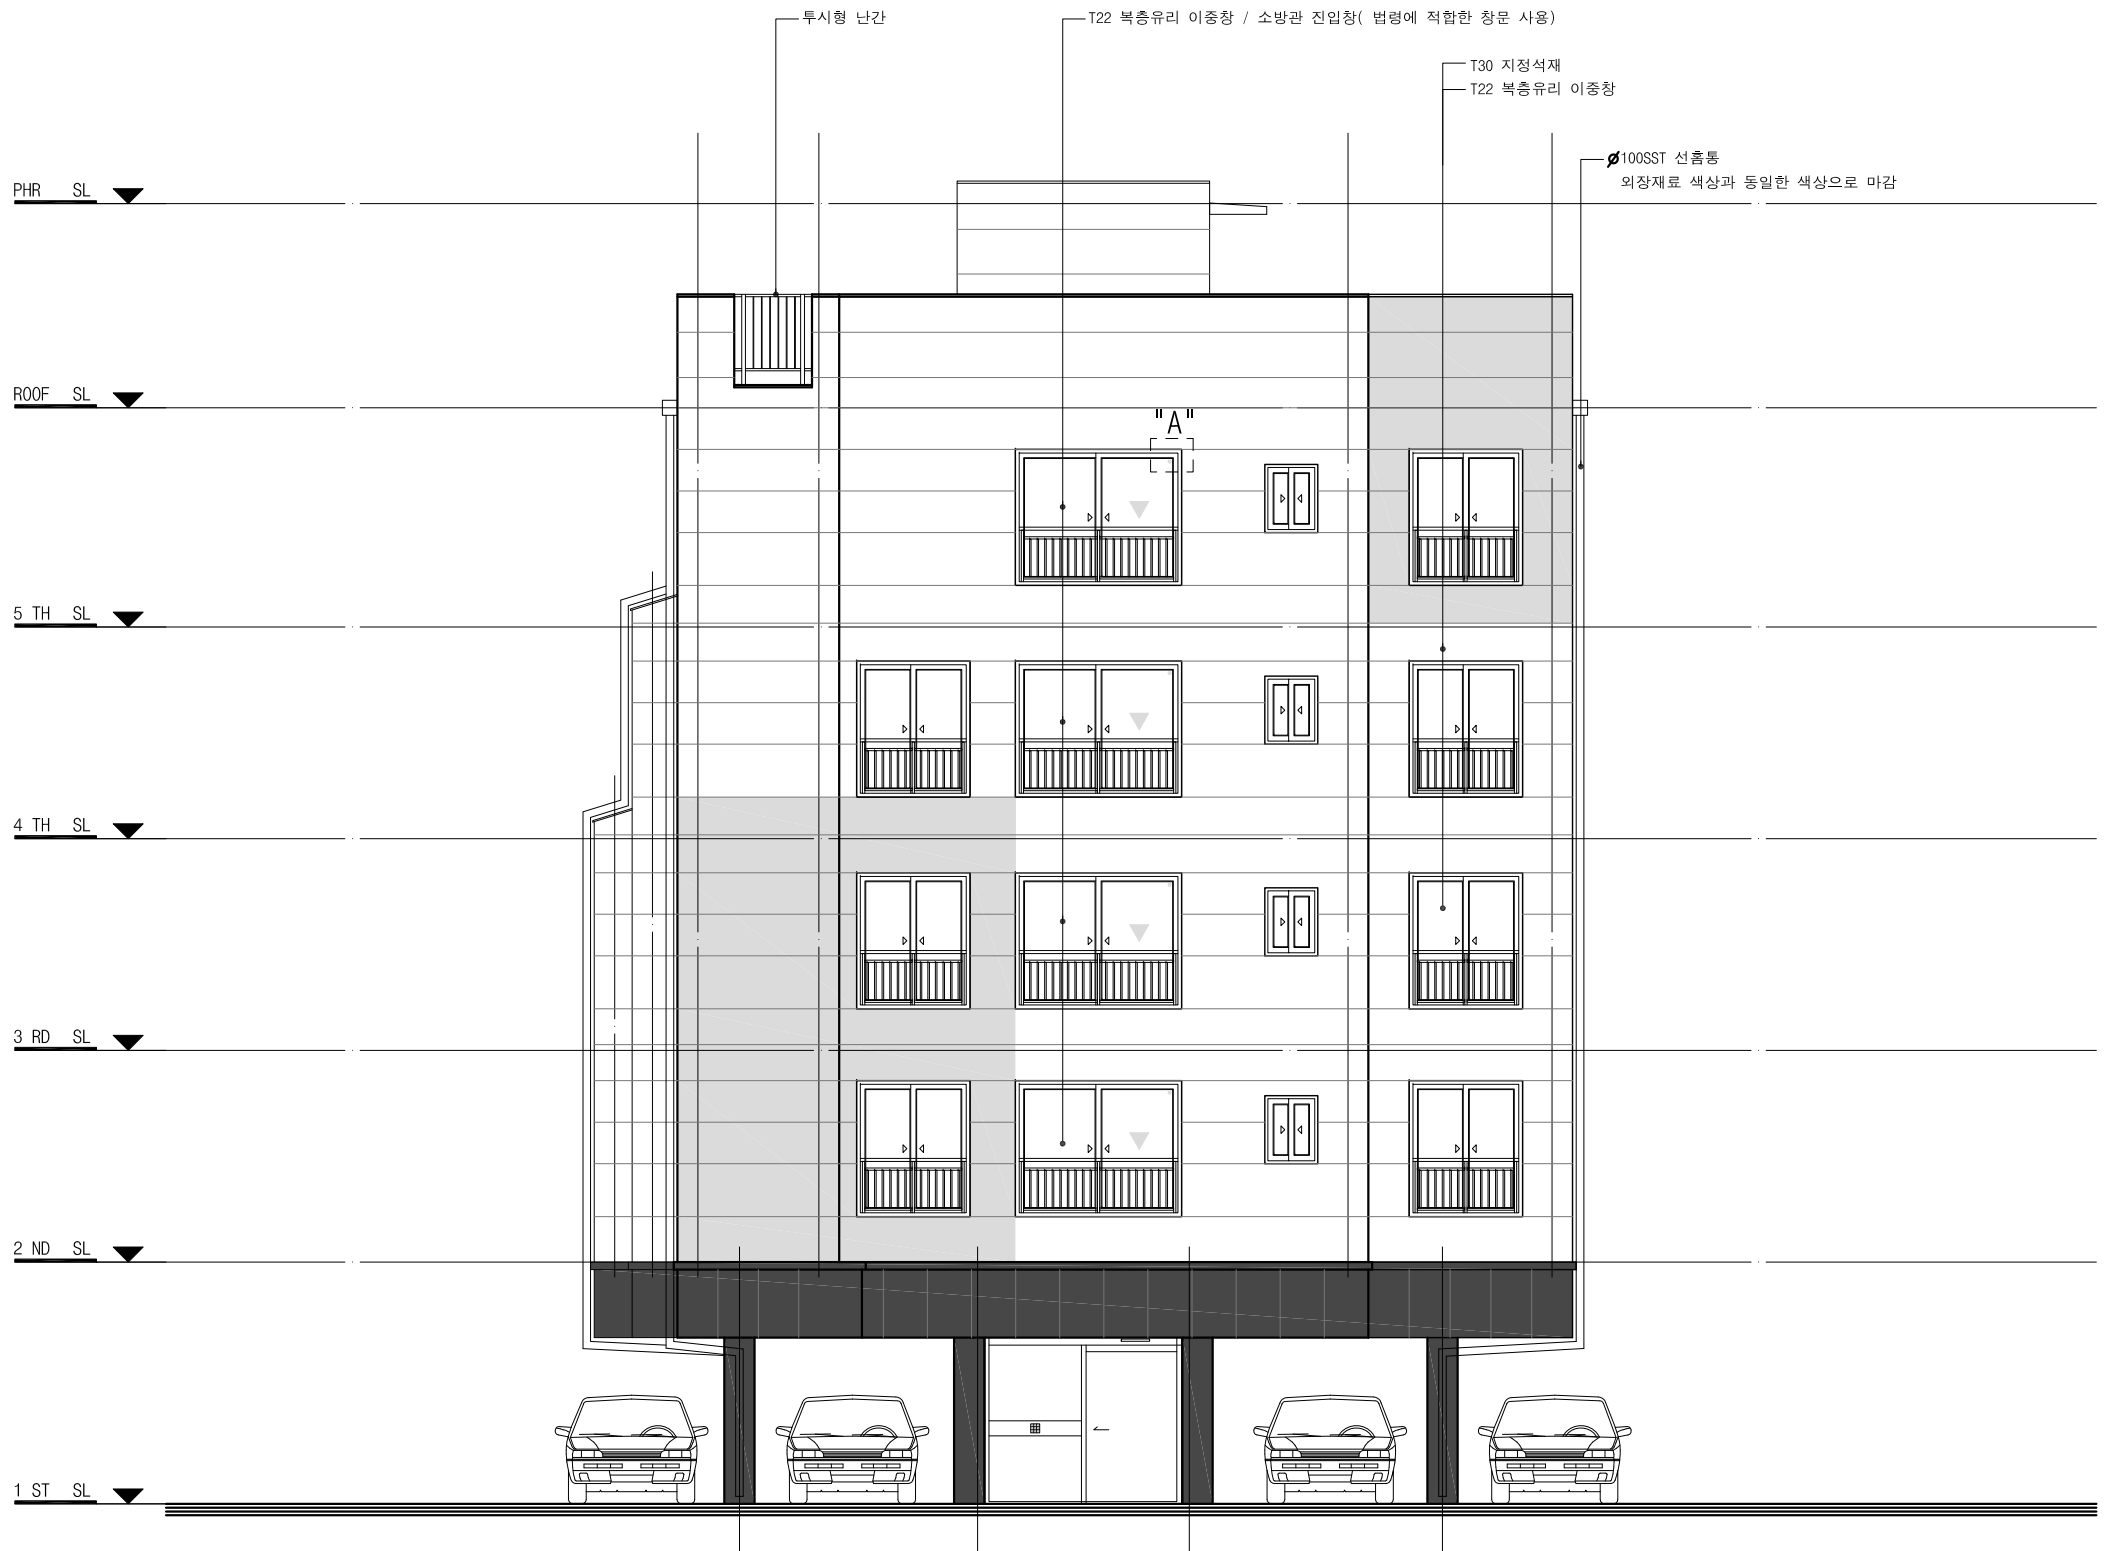


정 면 도
SCALE: 1/100

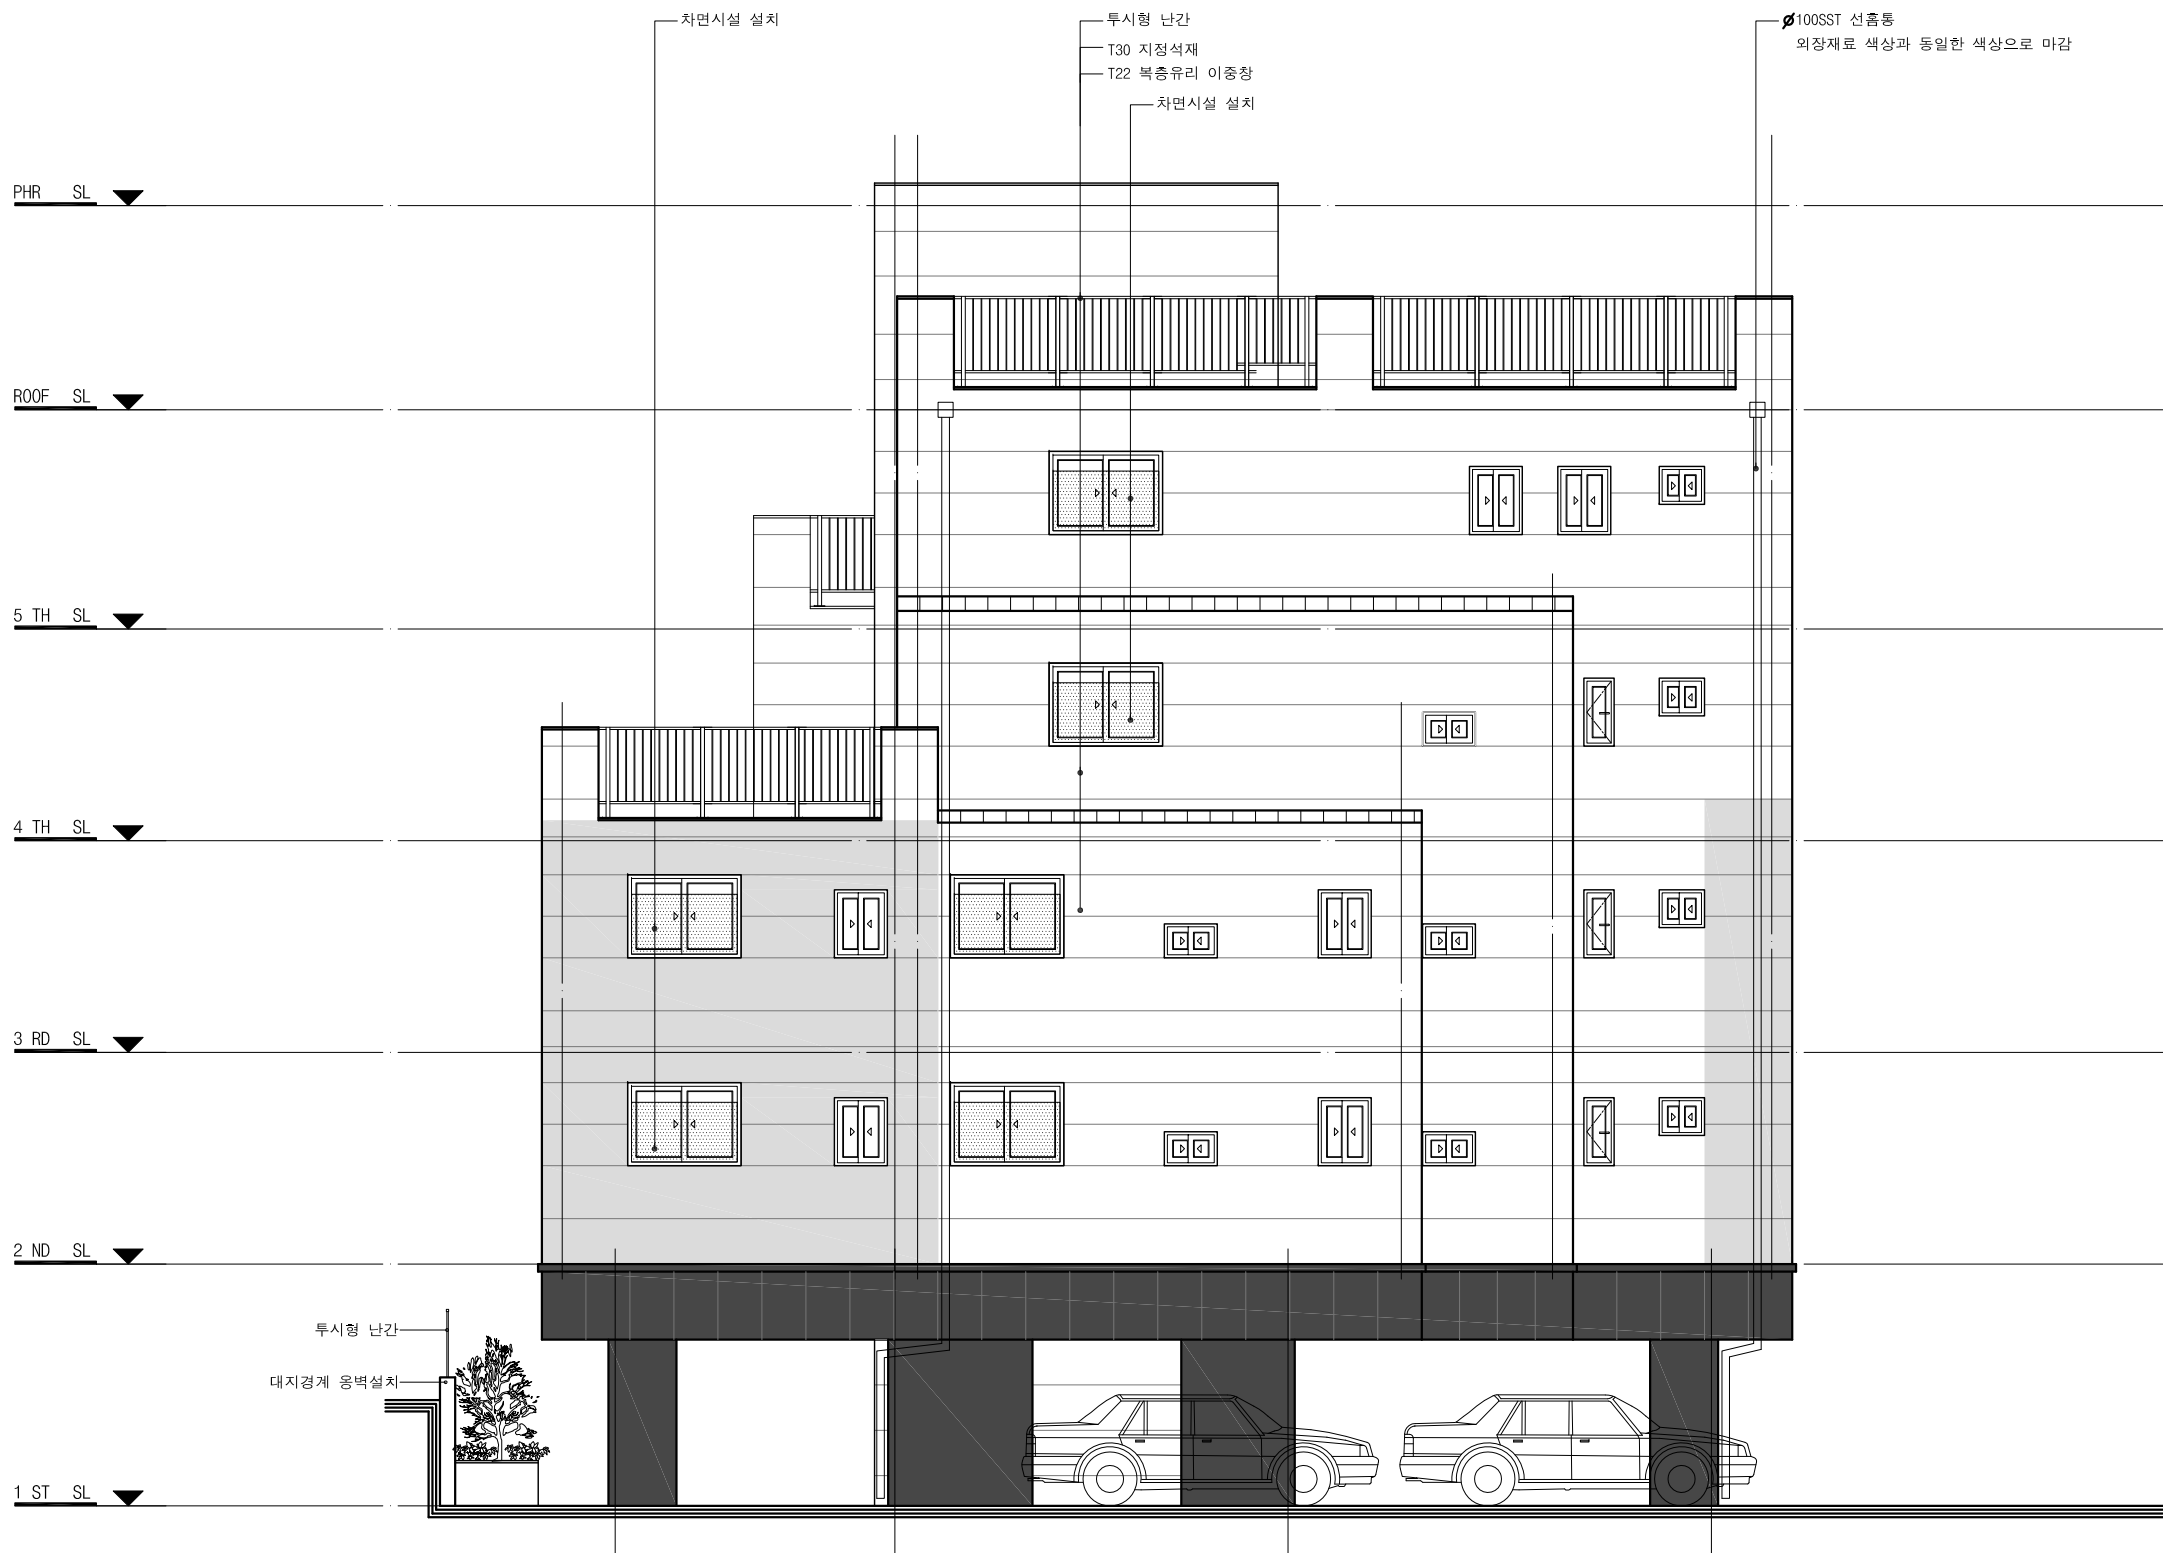



좌 측 면 도

SCALE: 1/100

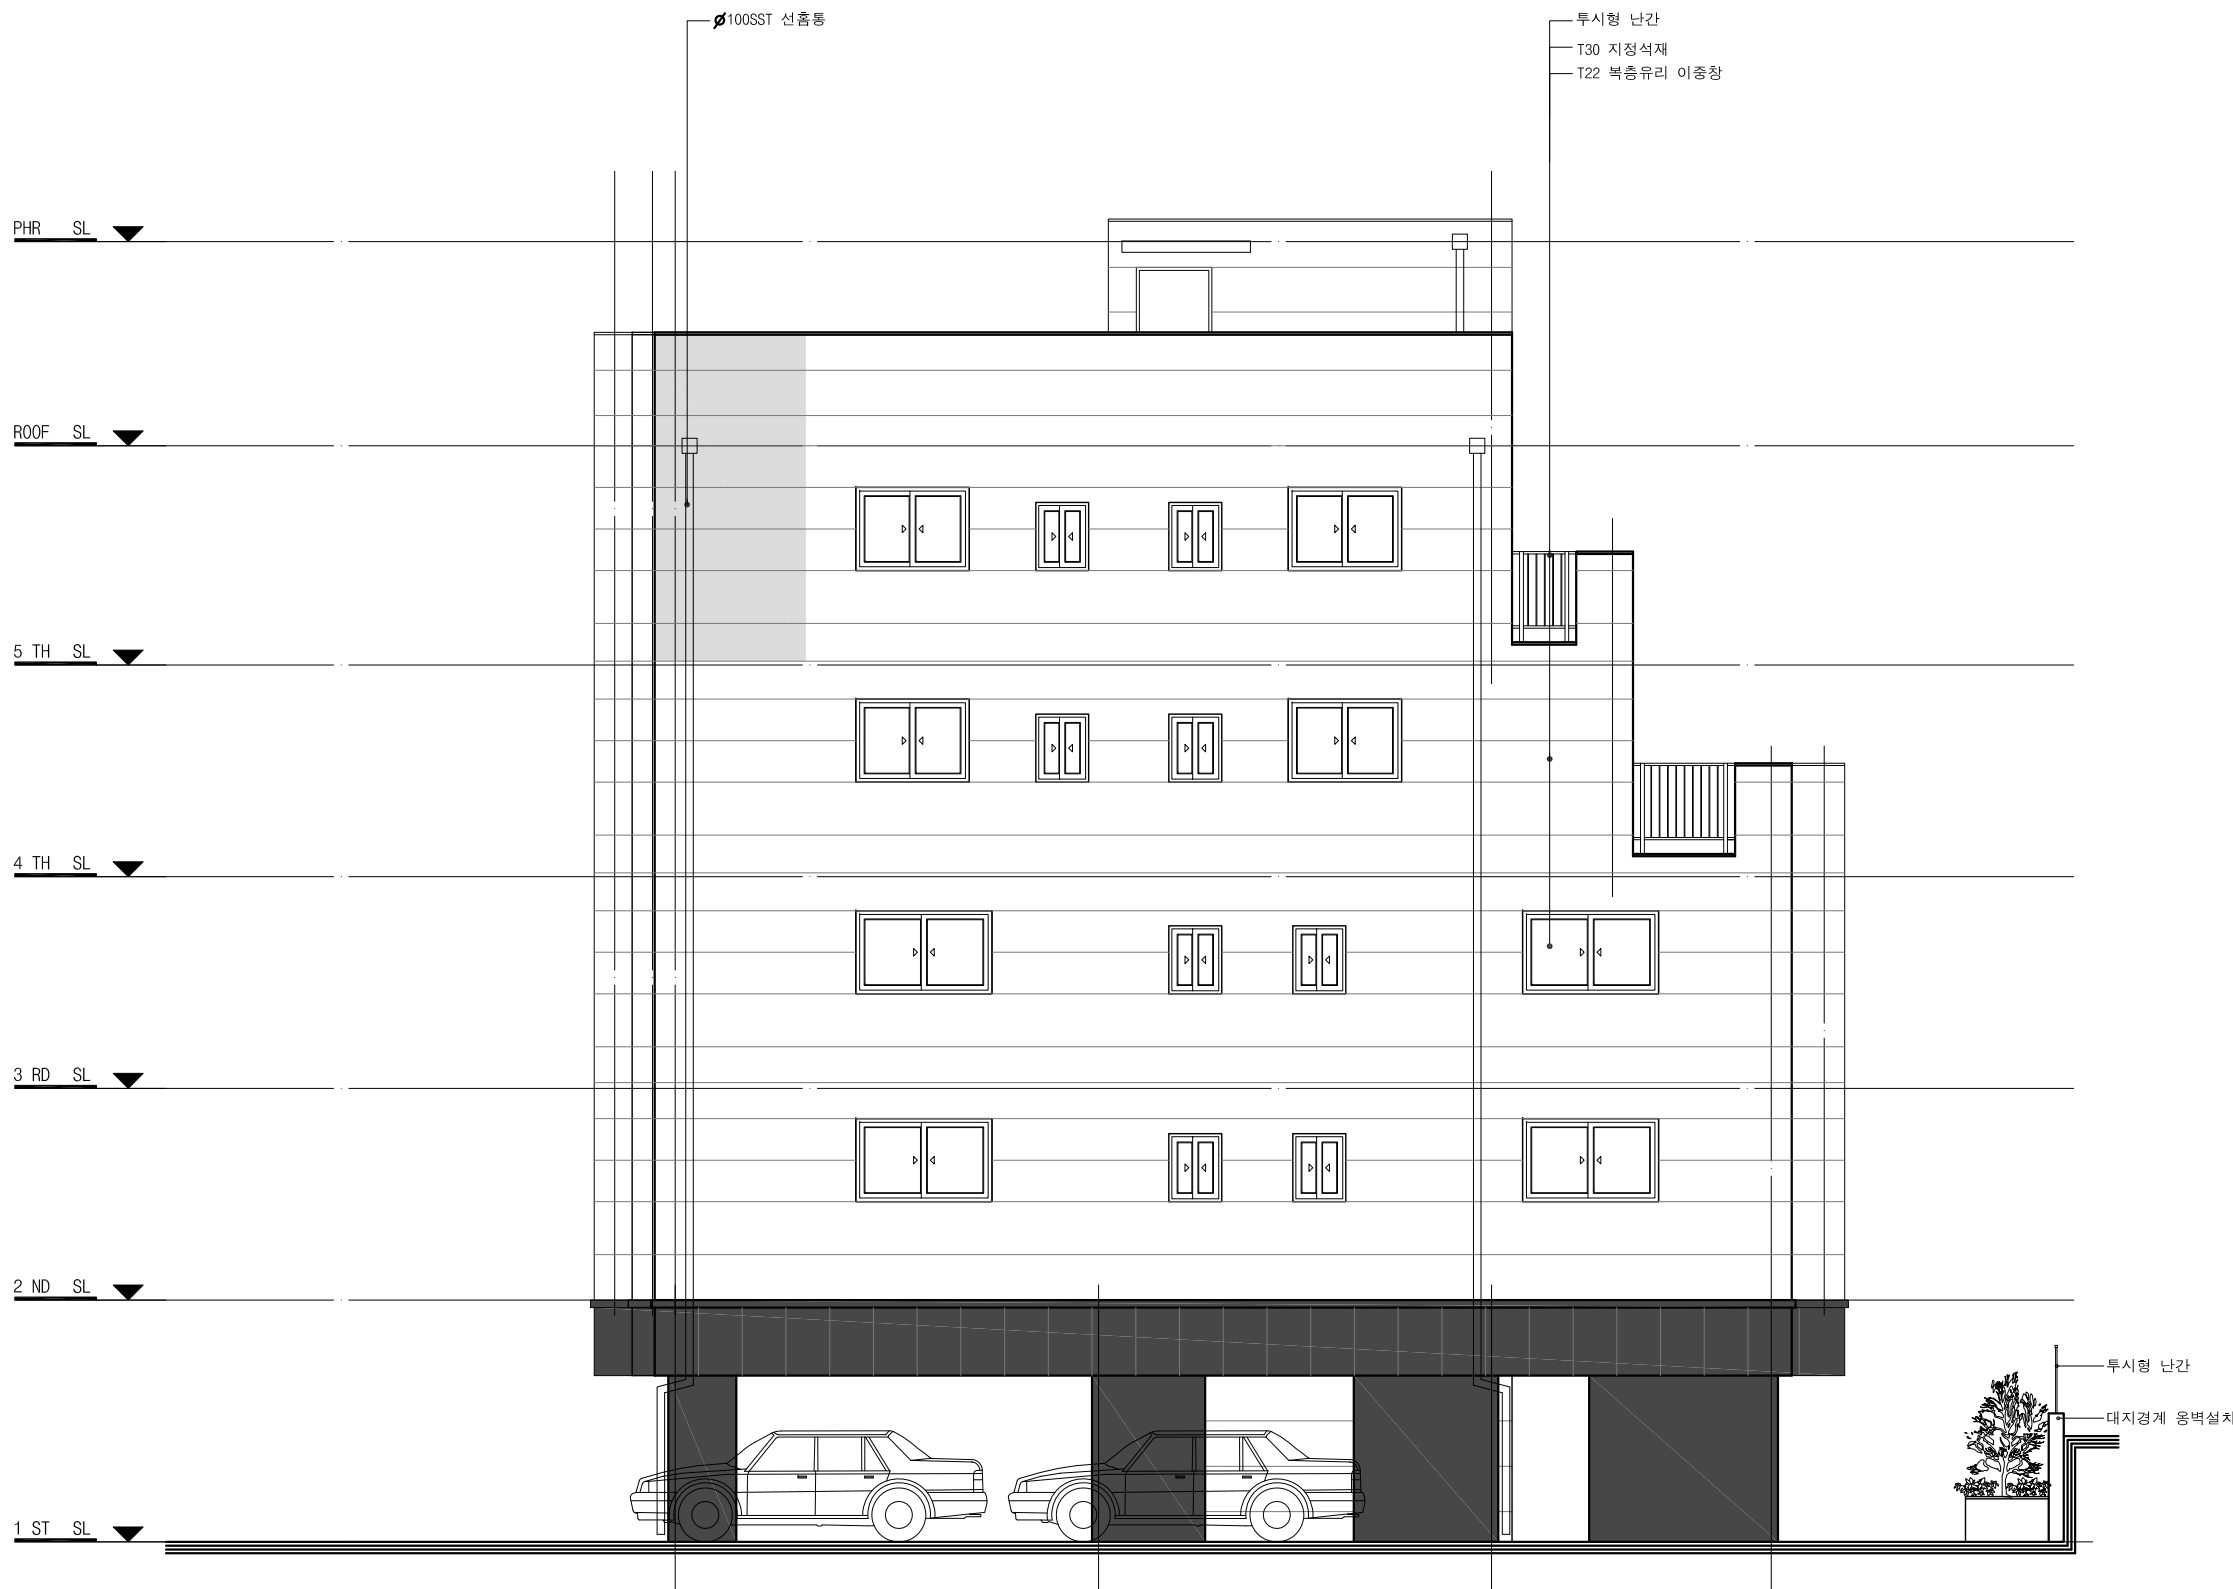

우 측 면 도

SCALE: 1/100

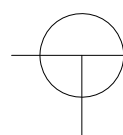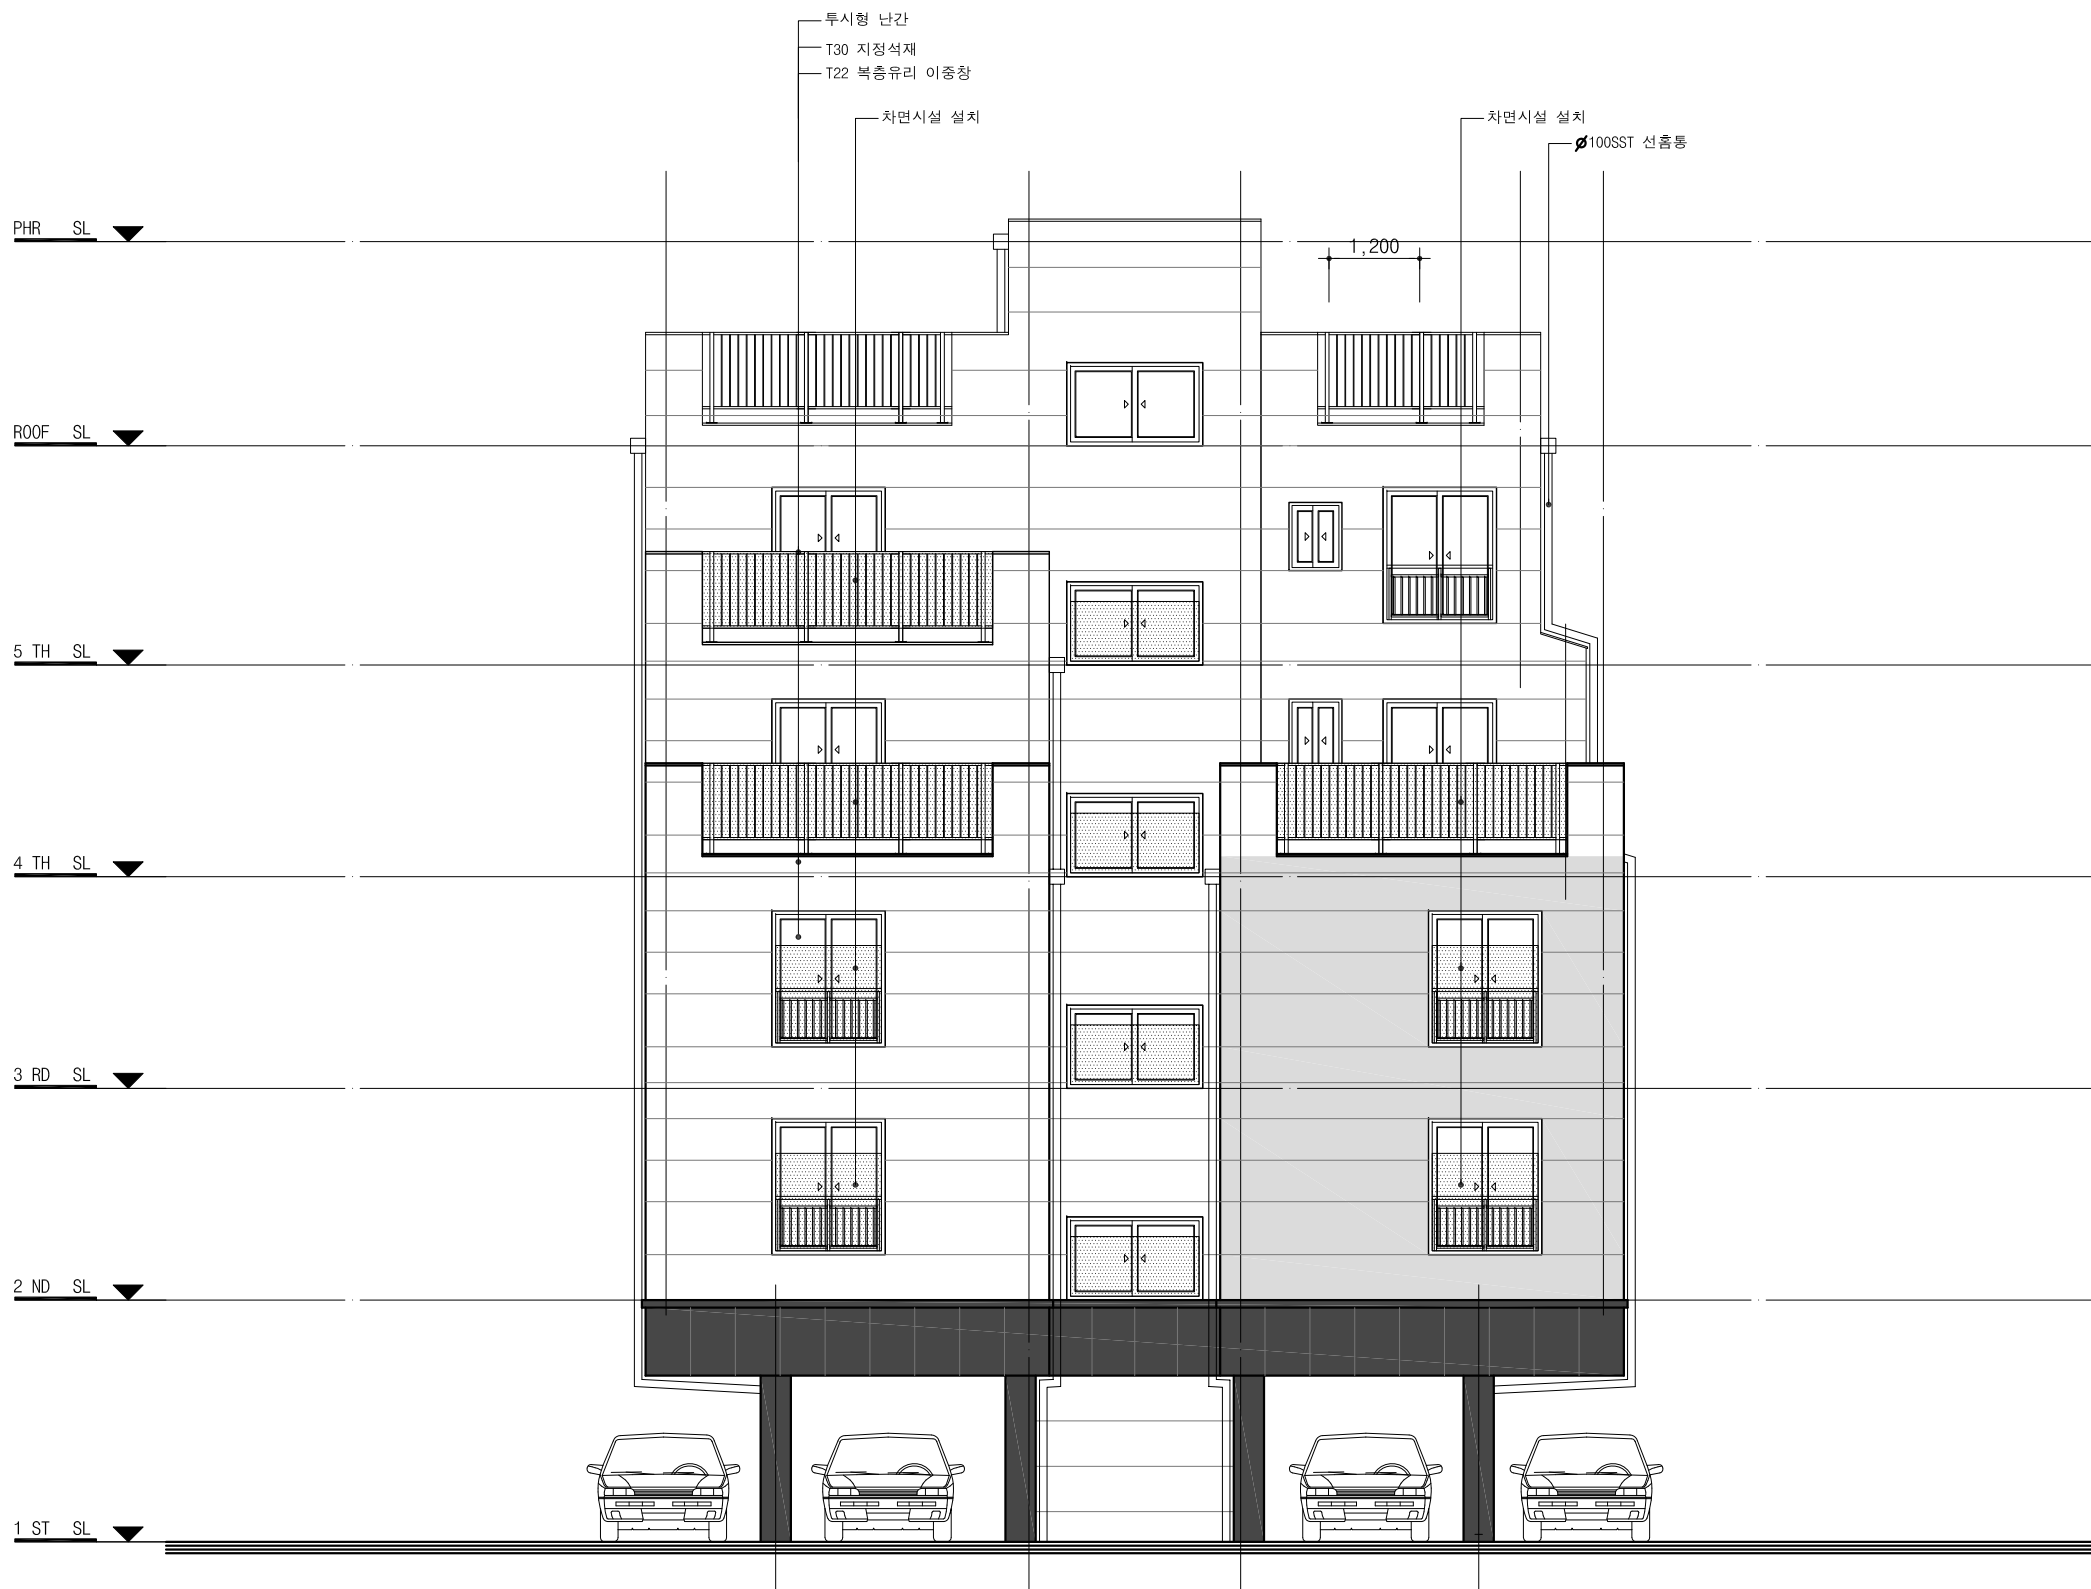

배 면 도

SCALE: 1/100



【 본 건 전 경 】



【 주 변 전 경 】