





남 측 면



북 측 면



동 남 측 면



서 남 측 면

6M 도로

4M 도로

1 층 평 면 도


SCALE: 1 / 100

우편물취급함

960		
320	320	320




201	202	203
301	302	303
401	402	반송함
501	502	전선지함

SCALE:1/50
규 격 : 320 X 250 X 160

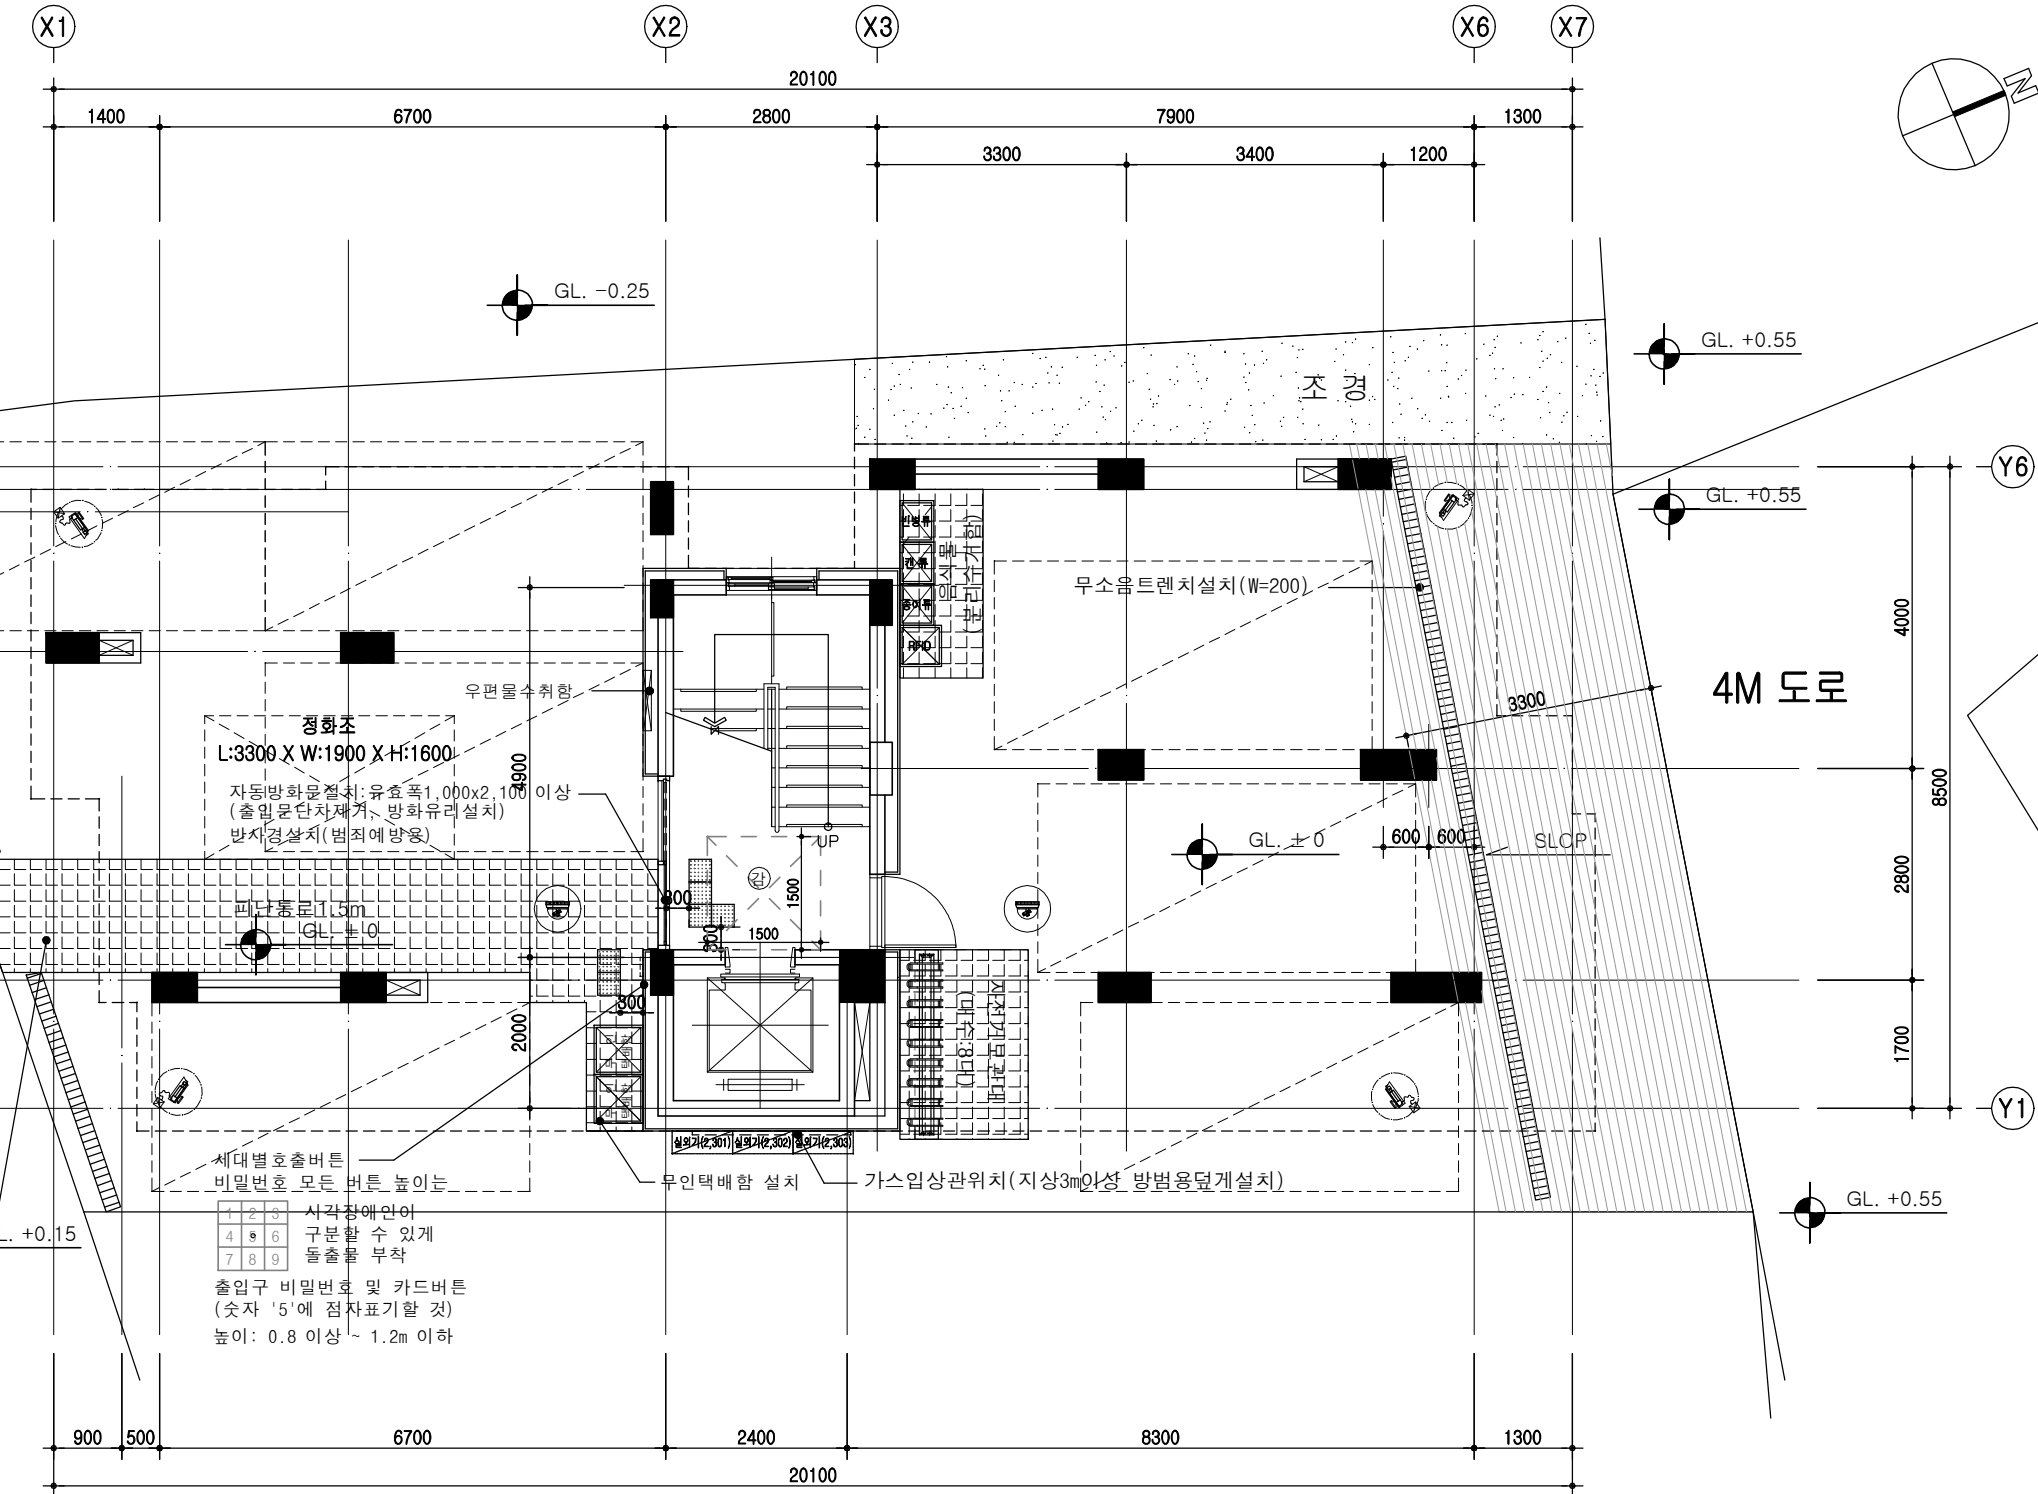

보행안전통로는 미끄러지지 아니하는 재질로 평탄하게 마감하여야 함.
(페인트, 우레탄, 칼라무늬콘크리트 시공금지/석재 Type시공)
보행안전통행로는 주차장 및 차도의 바닥재와 재질과 색상을달리하여 설치

* 무인택배함, 재활용분리수거함. 자전거보관대 바닥마감은 보행안전통로와 같은 마감으로 할것.

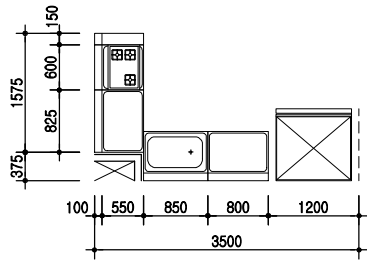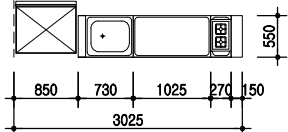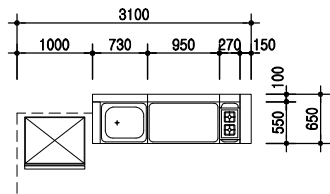

N01호

N02호

N03호

<범례>

▨ : 조적벽
— : CON' 벽

① : 인터폰
② : 소화기(설비도면 참조)
③ : 감지기(설비도면 참조)

▤ : 점자블럭 (0.3m 이격거리 확보)


▧ : 커튼박스

동측, 서측 창문(차면시설설치)
(임면도 참조)

*외기에 접한 거실 벽면은 반드시
THK10결로방지 단열재를 시공할것.

Material	fck = 24MPa-Con'c
	fck = 400MPa(SD400)-D220이하
SLAB	THK = 210mm
	THK = 150mm(계단실)
WALL	THK = 200mm
	(외부벽체 및 세대간 벽체, 코어벽체) THK = 150mm(내부벽체)

*싱크대 상판은 인조대리석(12T, MMA급 이상)
*싱크대 끝단부는 반드시 물코와 물턱을 설치 할것.

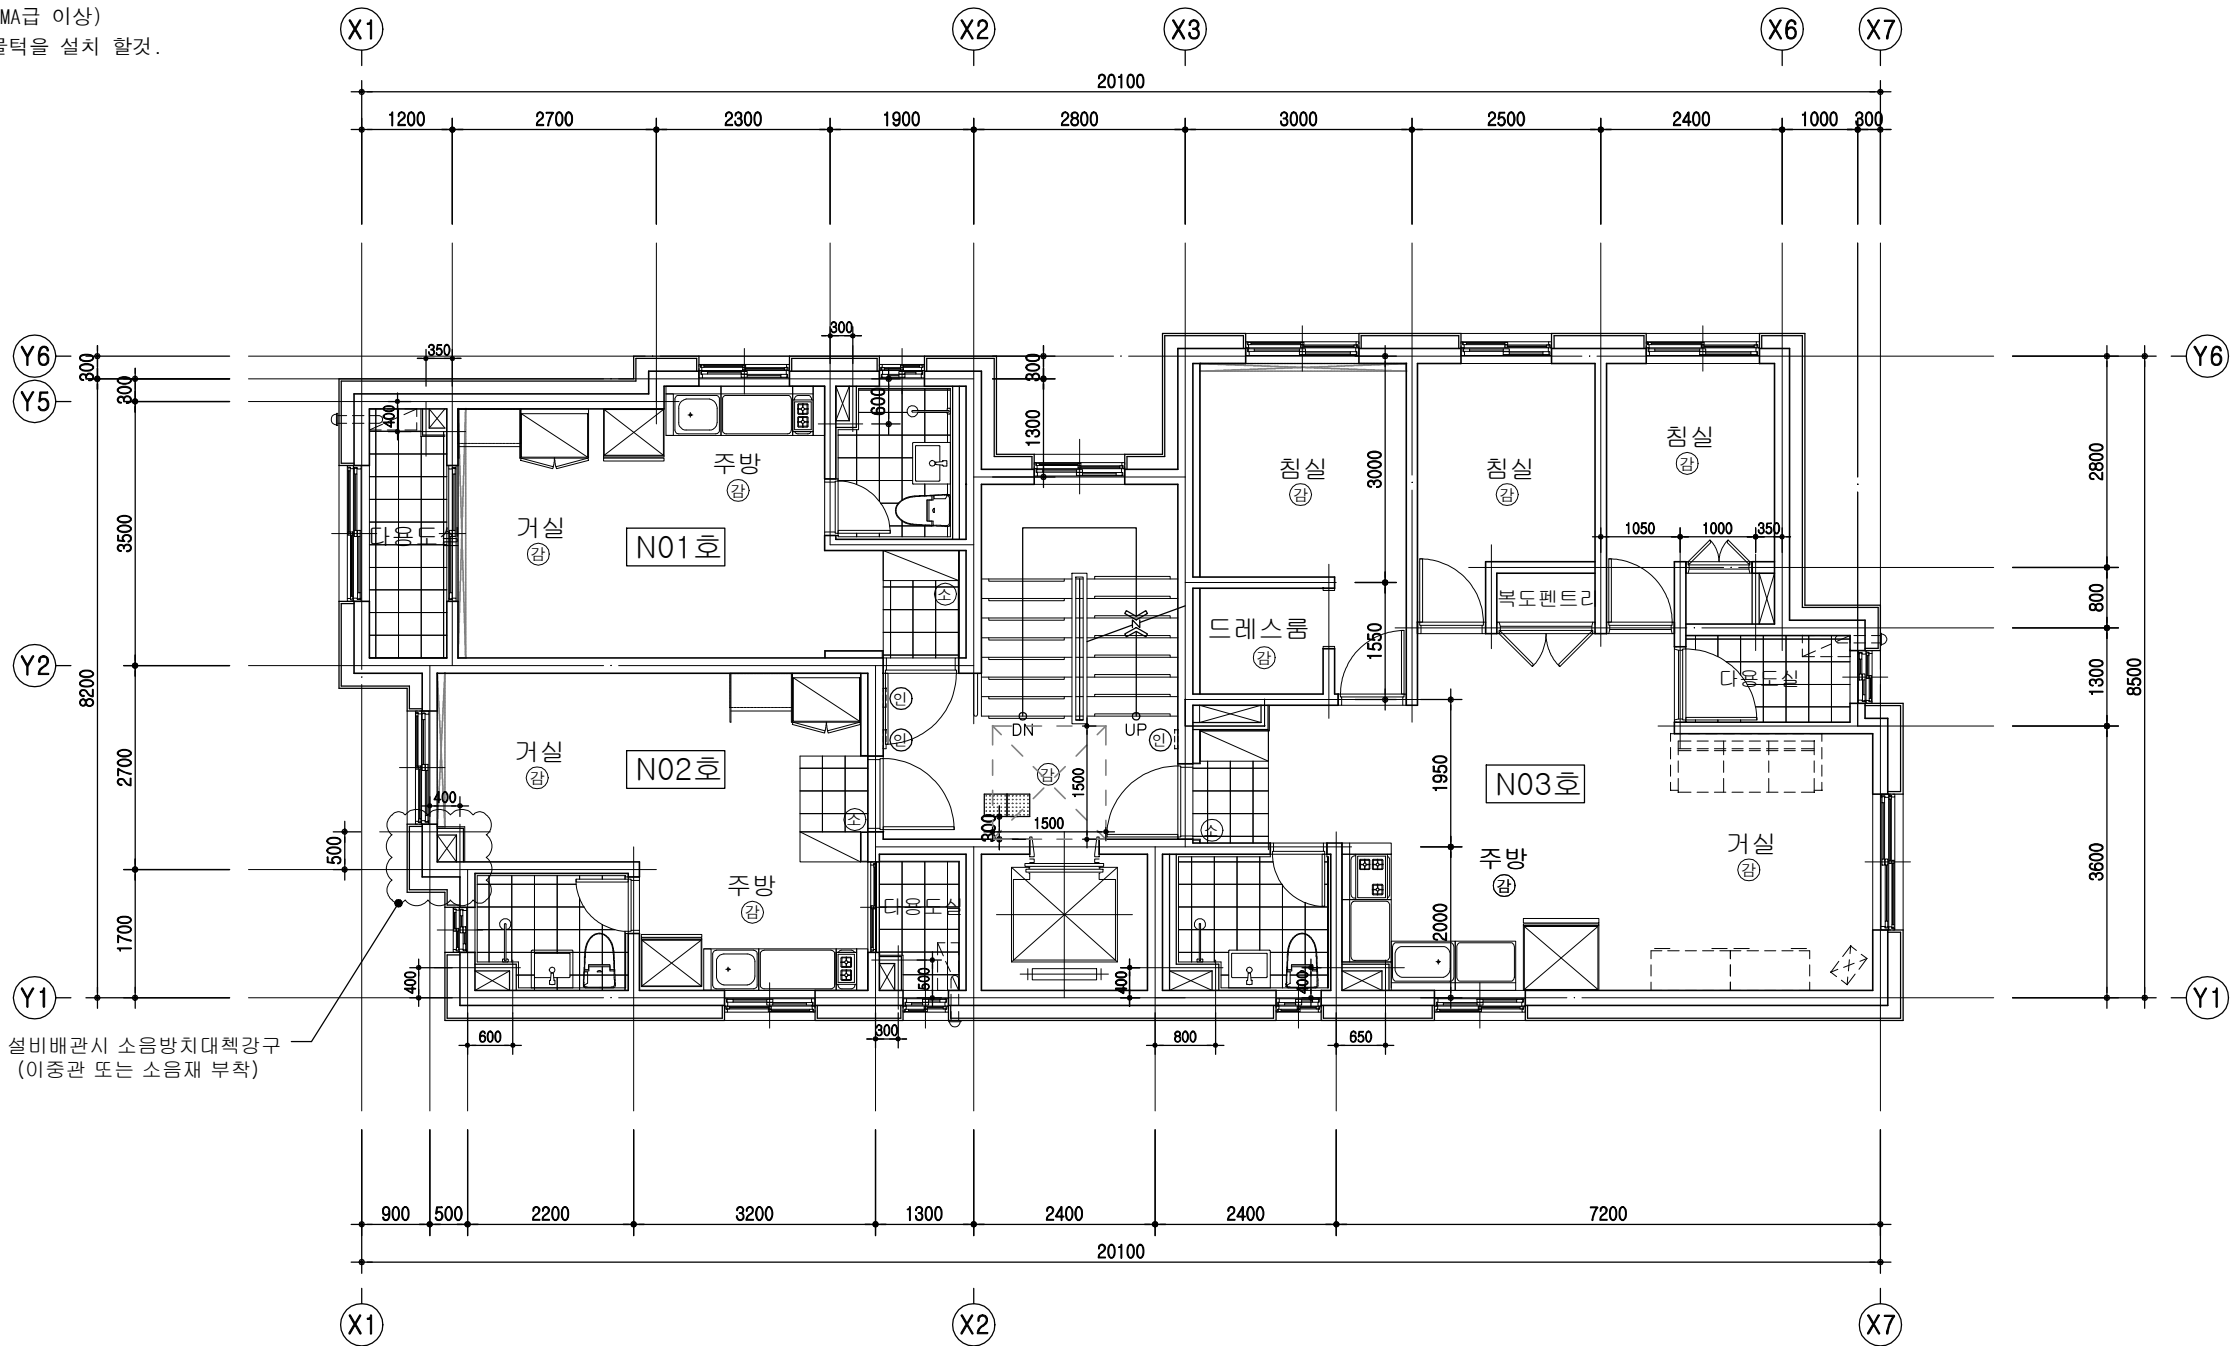


설비배관시 소음방지대책강구
(이중관 또는 소음재 부착)

2, 3 층 평 면 도


SCALE: 1 / 100

■ 범례

연면적제외	▨
발코니확장	▧

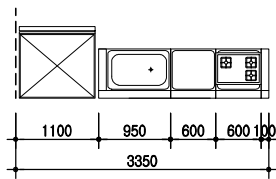

401호

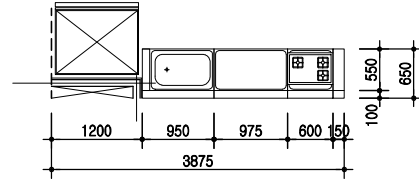

402호

<범례>


▨ : 조적벽
— : CON' 벽

(인) : 인터폰
(소) : 소화기(설비도면 참조)
(감) : 감지기(설비도면 참조)

▤ : 점자블럭 (0.3m 이격거리확보)
▧ : 커튼박스
동측, 서측 창문(차면시설설치)
(임면도 참조)
*외기에 접한 거실 벽면은 반드시
THK10결로방지 단열재를 시공할것.

Material	fck = 24MPa-Con'c
	fck = 400MPa(SD400)-D220이하
SLAB	THK = 210mm
	THK = 150mm(계단실)
WALL	THK = 200mm
	(외부벽체 및 세대간 벽체, 코어벽체) THK = 150mm(내부벽체)

*싱크대 상판은 인조대리석(12T, MMA급 이상)
*싱크대 끝단부는 반드시 물코와 물턱을 설치 할것.


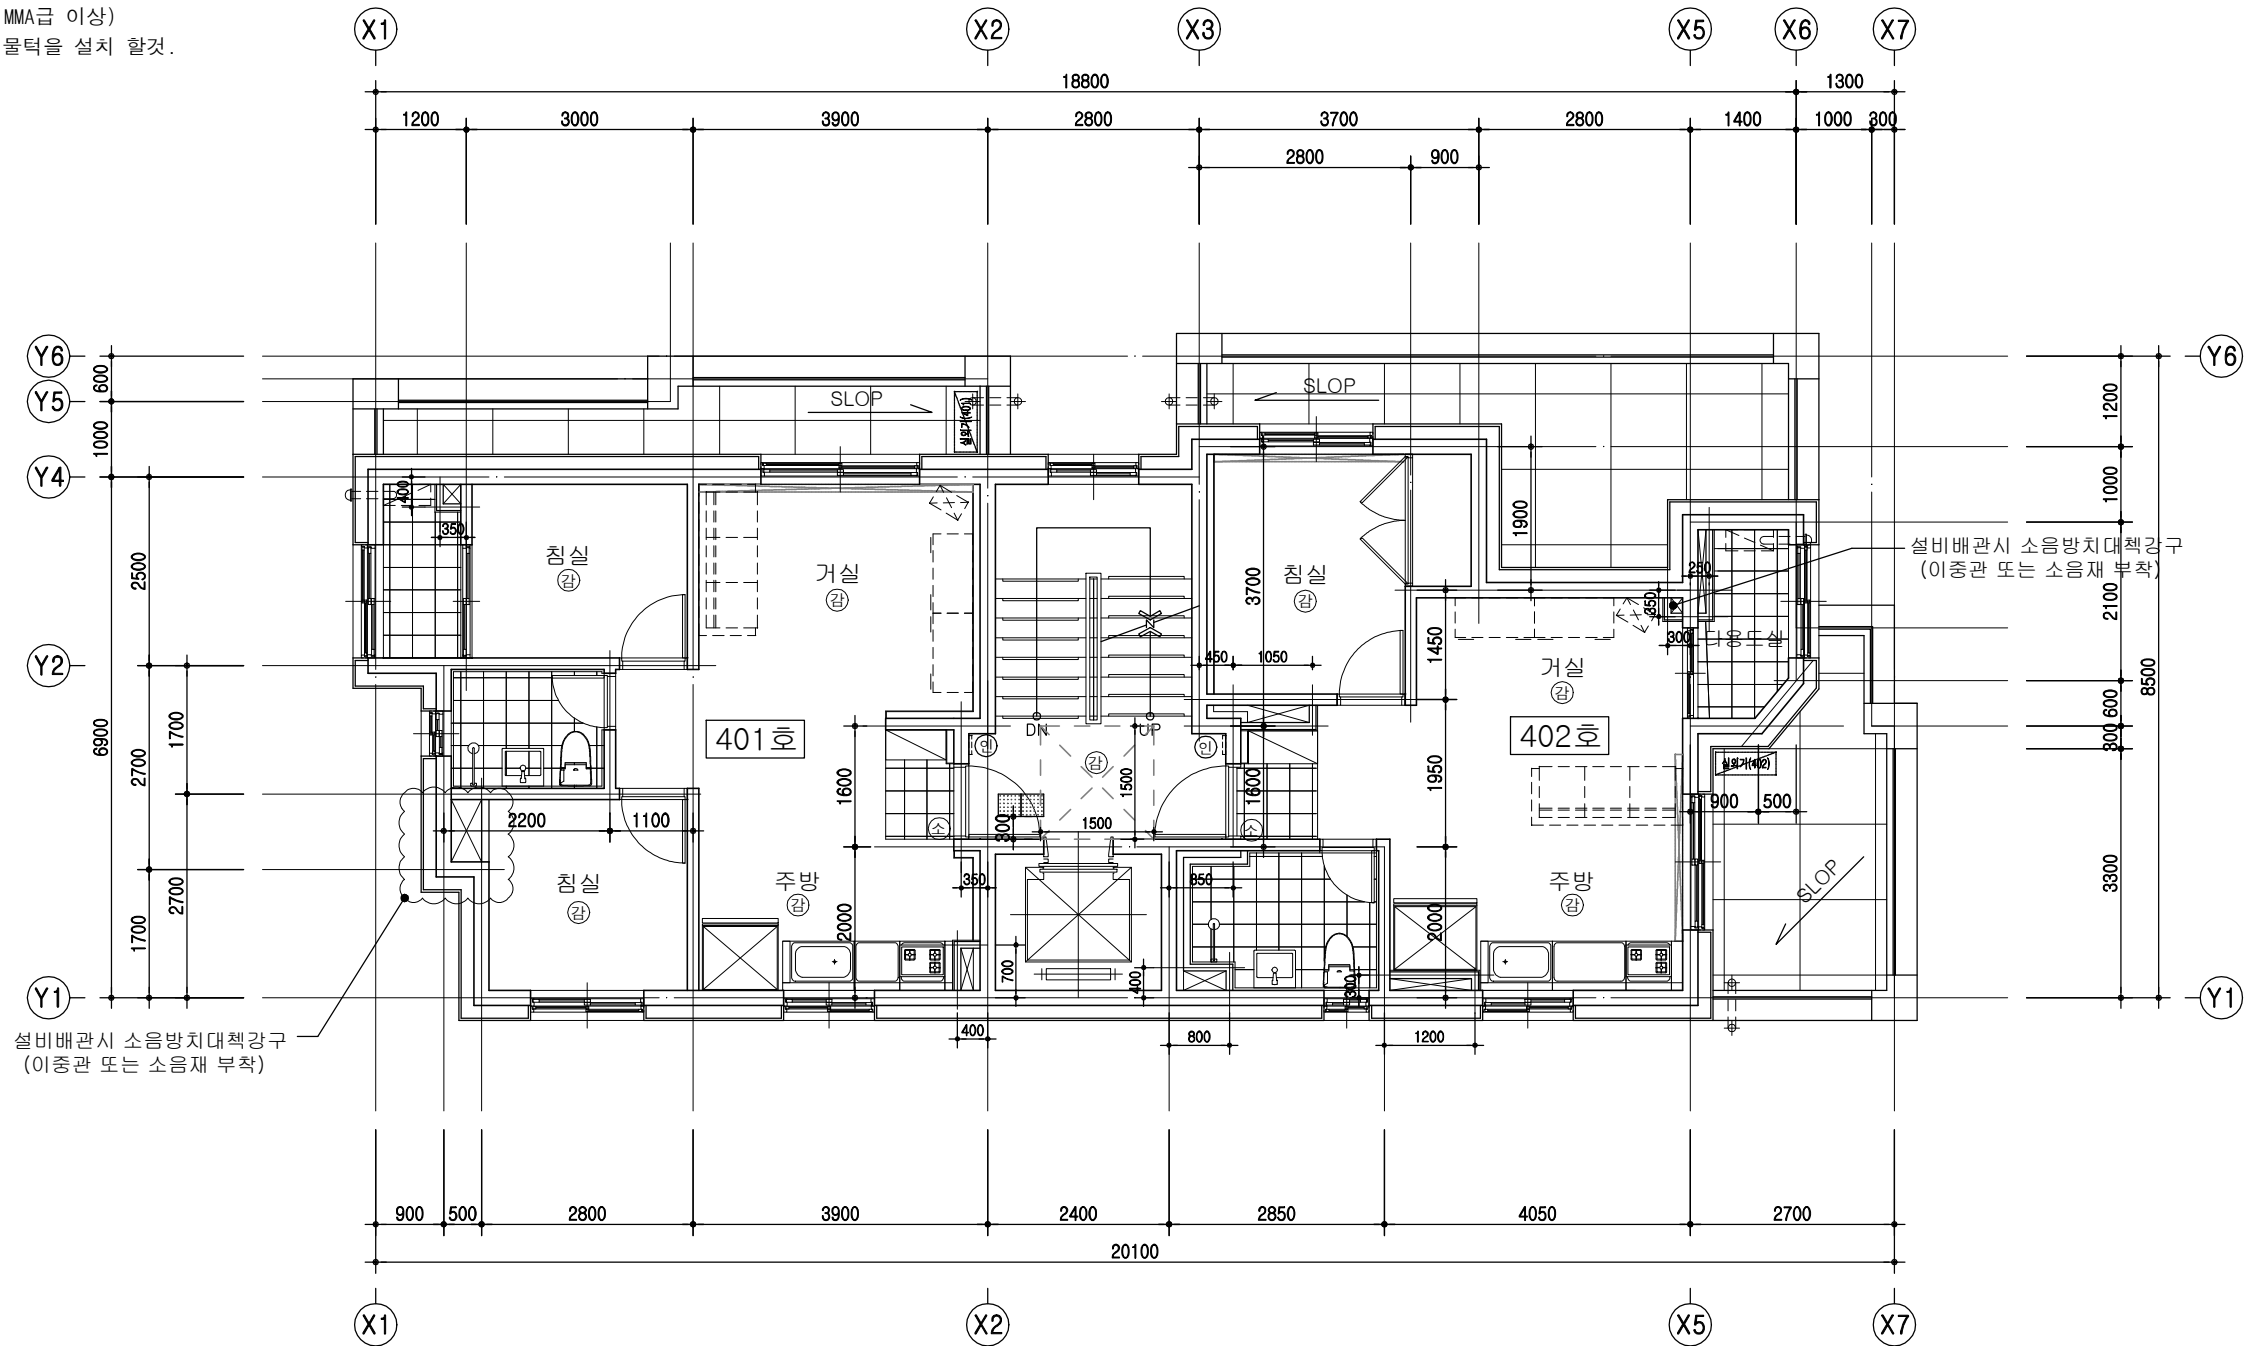


4 층 평 면 도

SCALE: 1 / 100

■ 범례

연면적제외	▨
발코니확장	▧

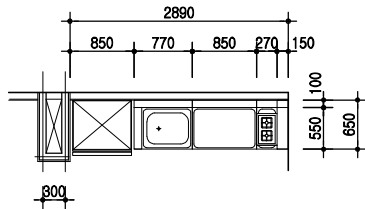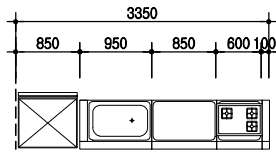

501호

502호

<범례>


조적벽
CON' 벽

인 : 인터폰
소 : 소화기(설비도면 참조)
감 : 감지기(설비도면 참조)

점자블럭 (0.3m 이격거리 확보)
커튼박스
동측, 서측 창문(차면시설설치)
(임면도 참조)
*외기에 접한 거실 벽면은 반드시
THK10결로방지 단열재를 시공할것.

Material	fck = 24MPa-Con'c
	fck = 400MPa(SD400)-D220이하
SLAB	THK = 210mm
	THK = 150mm(계단실)
WALL	THK = 200mm
	(외부벽체 및 세대간 벽체, 코어벽체) THK = 150mm(내부벽체)

*싱크대 상판은 인조대리석(12T, MMA급 이상)
*싱크대 끝단부는 반드시 물코와 물턱을 설치 할것.

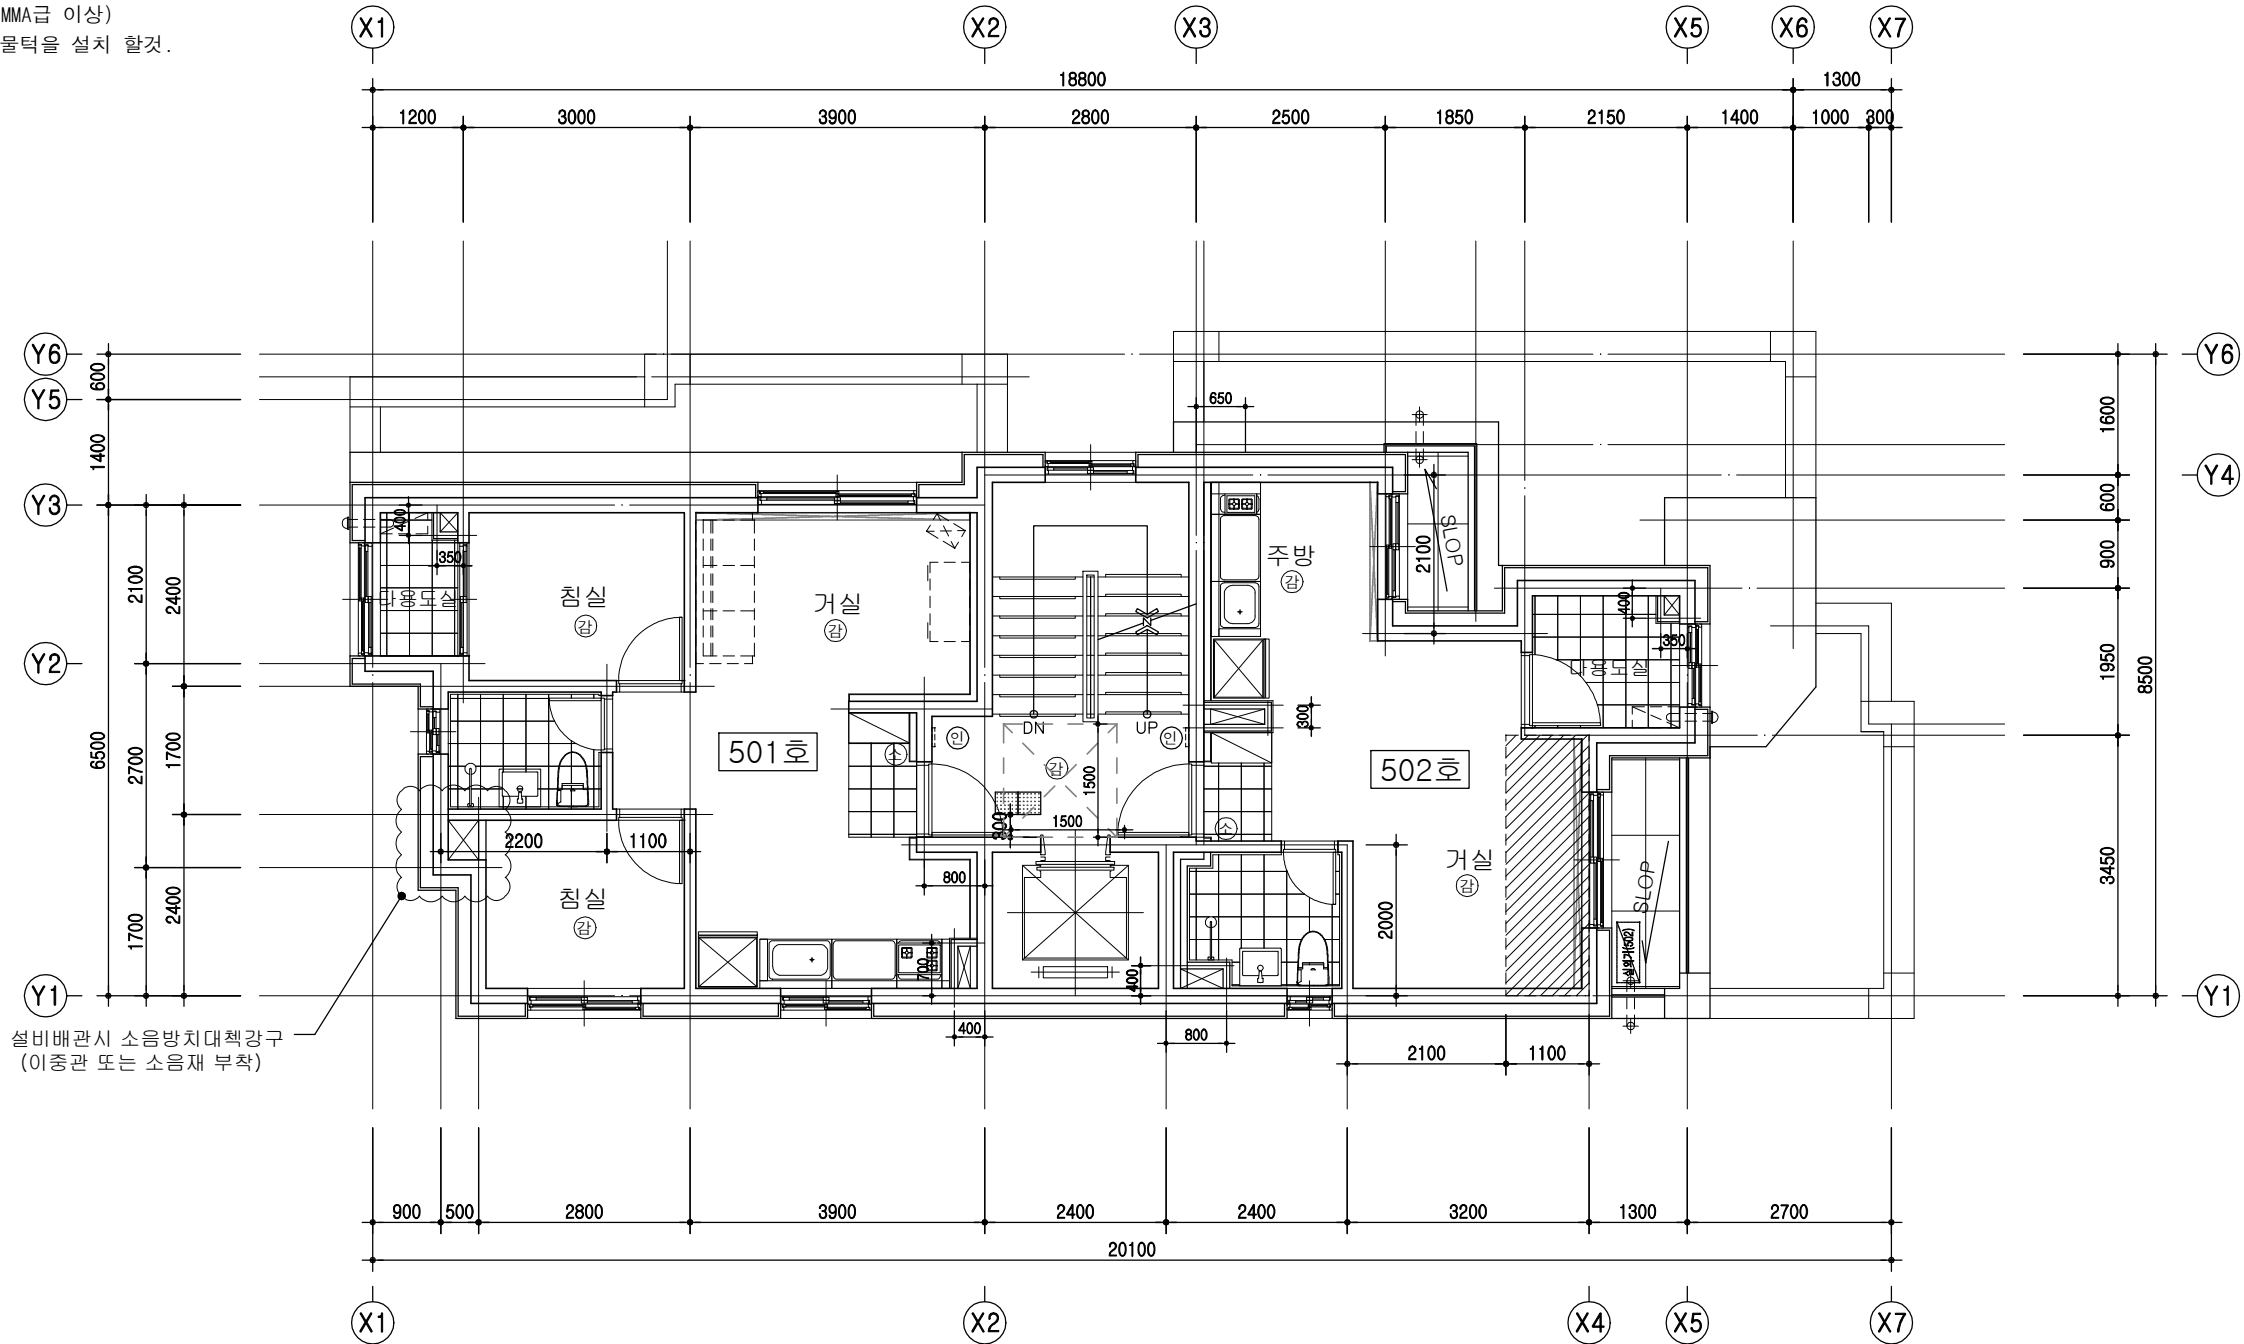

5 층 평 면 도
SCALE: 1 / 100

범례	
연면적제외	
발코니확장	

<범례>

▨ : 조적벽
—— : CON' 벽

①인 : 인터폰
①소 : 소화기(설비도면 참조)
①감 : 감지기(설비도면 참조)


▤ : 점자블럭 (0.3m 이격거리 확보)

▤ : 커튼박스


동측, 서측 창문(차면시설 설치)
(입면도 참조)

*외기에 접한 거실 벽면은 반드시
THK10결로방지 단열재를 시공할것.



Material	fck = 24MPa-Con'c
	fck = 400MPa(SD400)-D220이하
SLAB	THK = 210mm
	THK = 150mm(계단실)
WALL	THK = 200mm
	(외부벽체 및 세대간 벽체, 코어벽체) THK = 150mm(내부벽체)

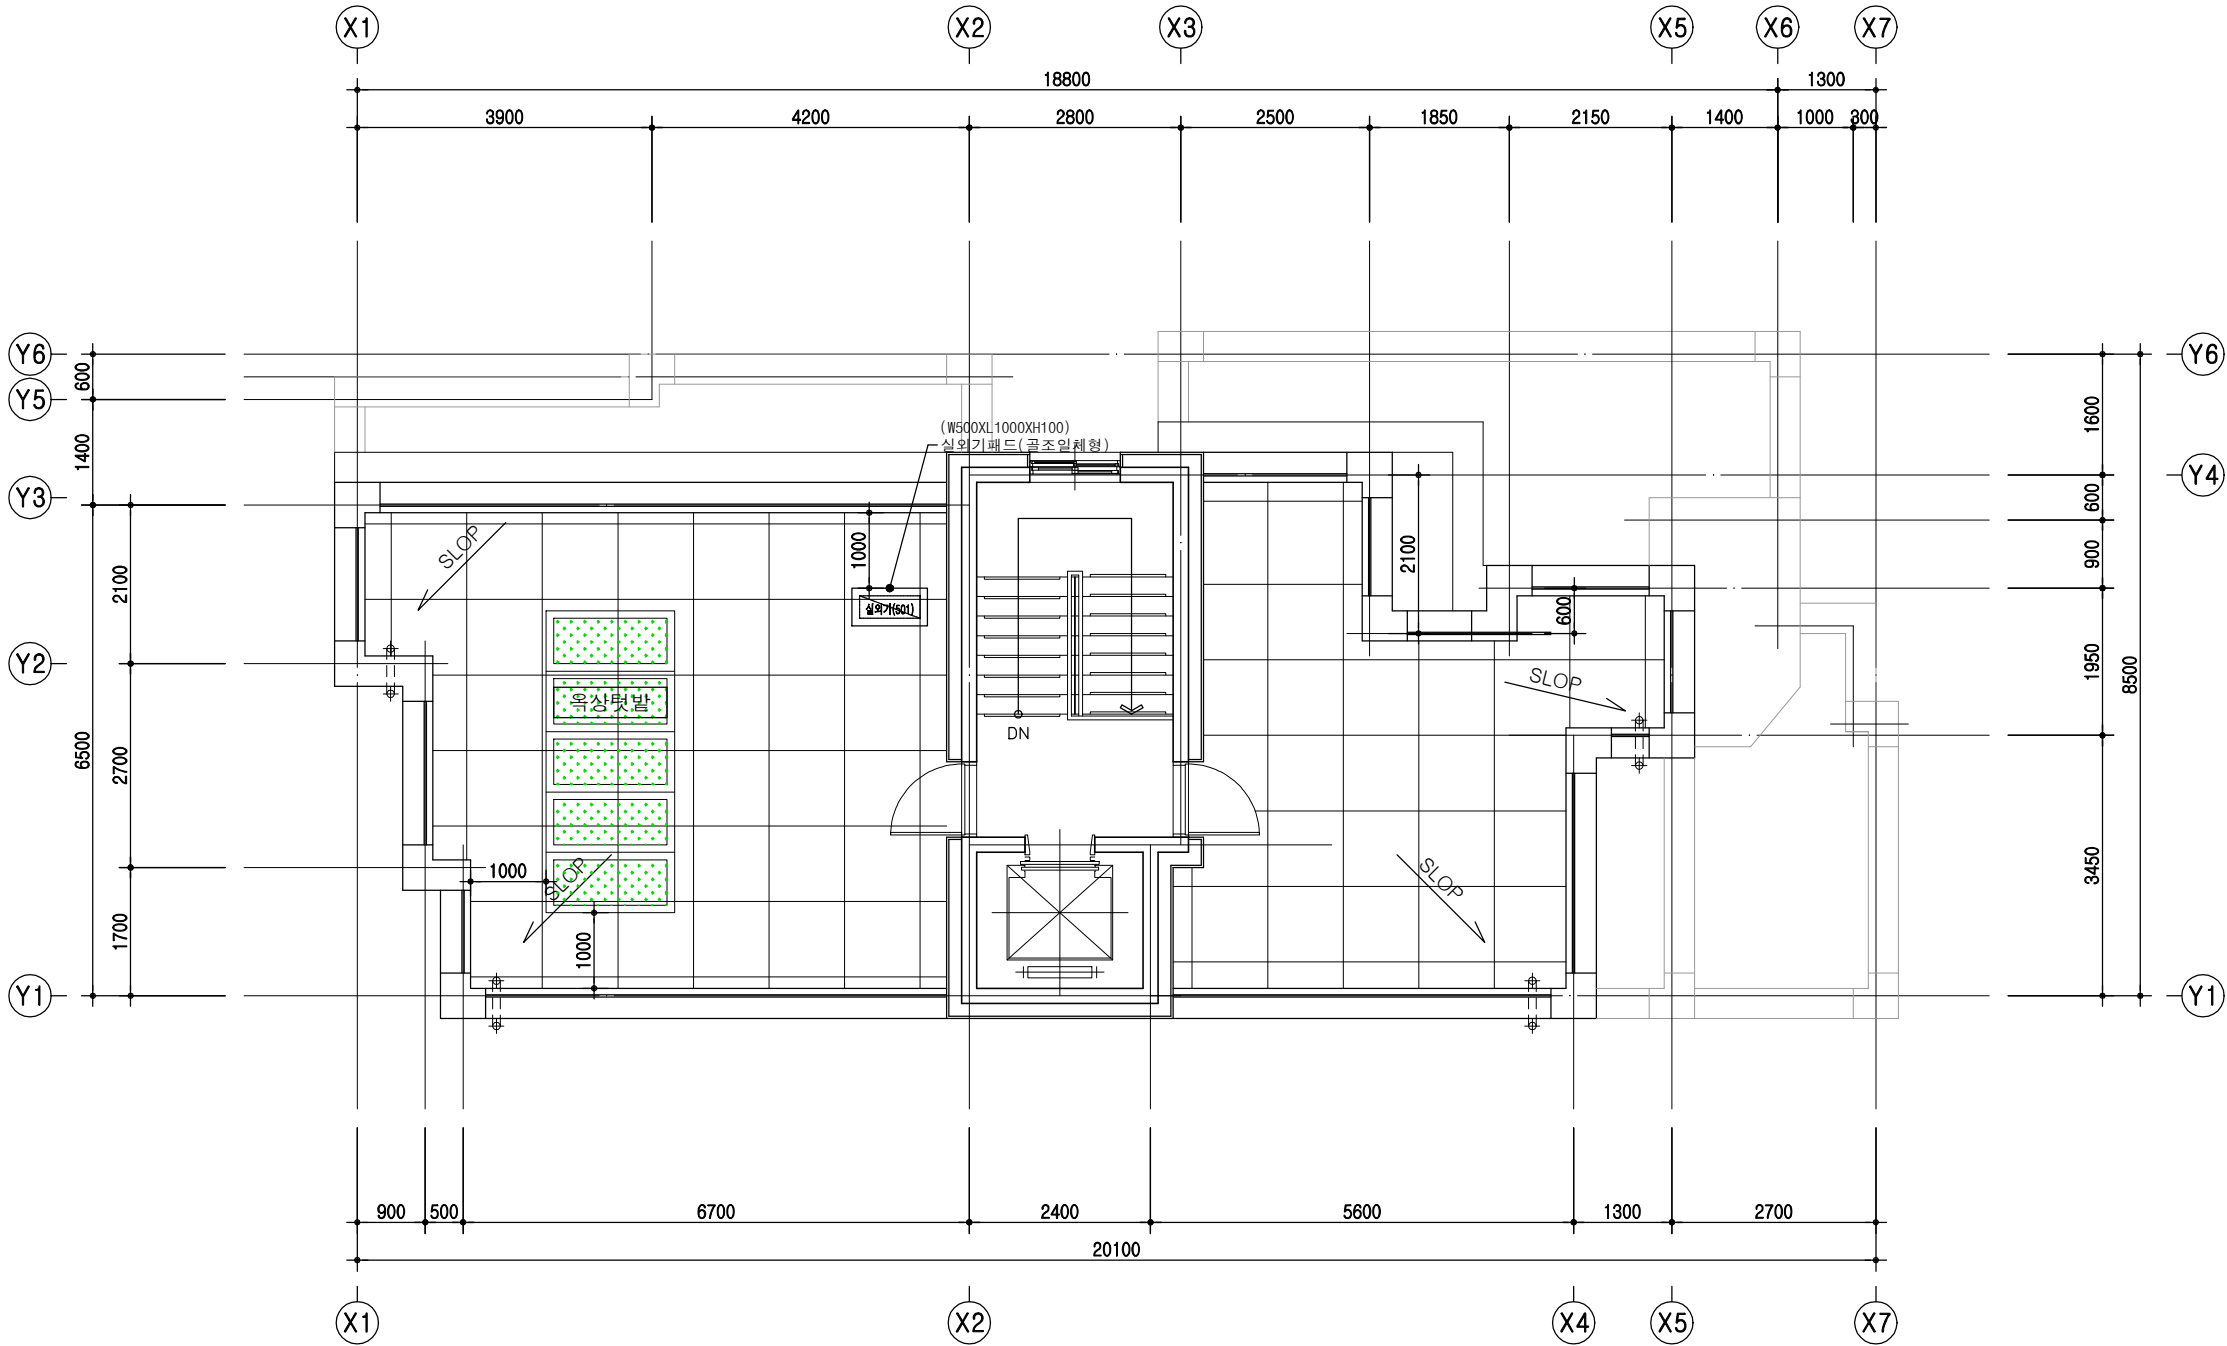

지붕층 평면도
SCALE: 1 / 100

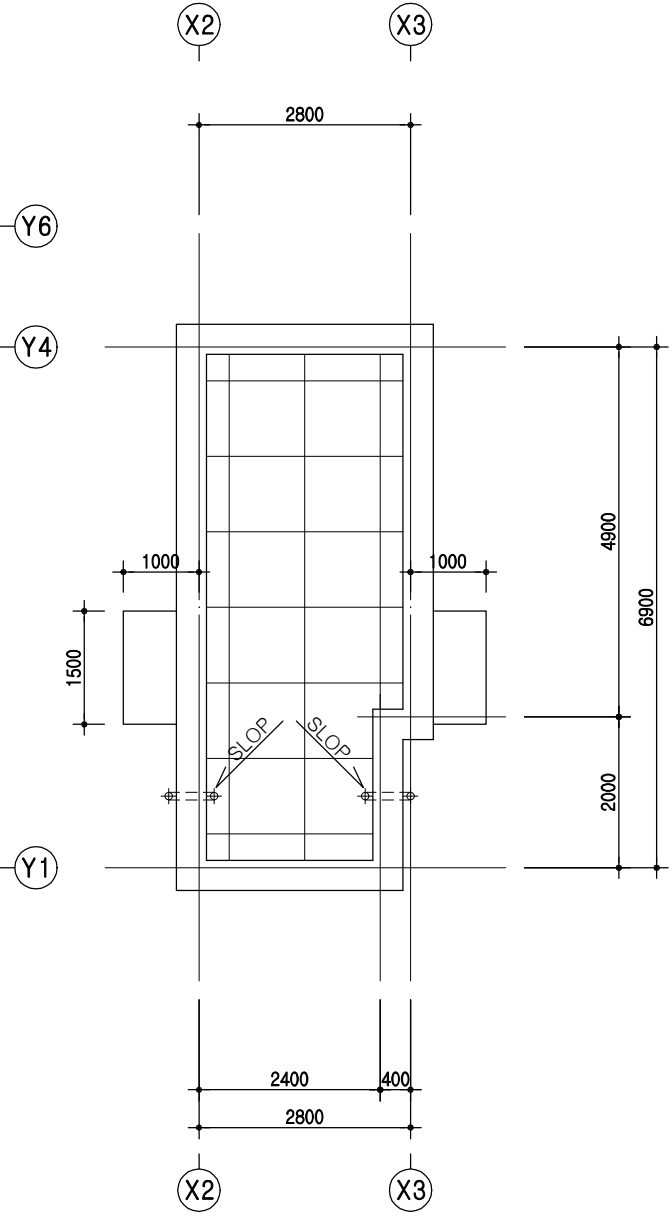


옥탑지붕 평면도
SCALE: 1 / 100

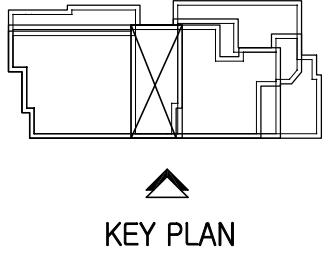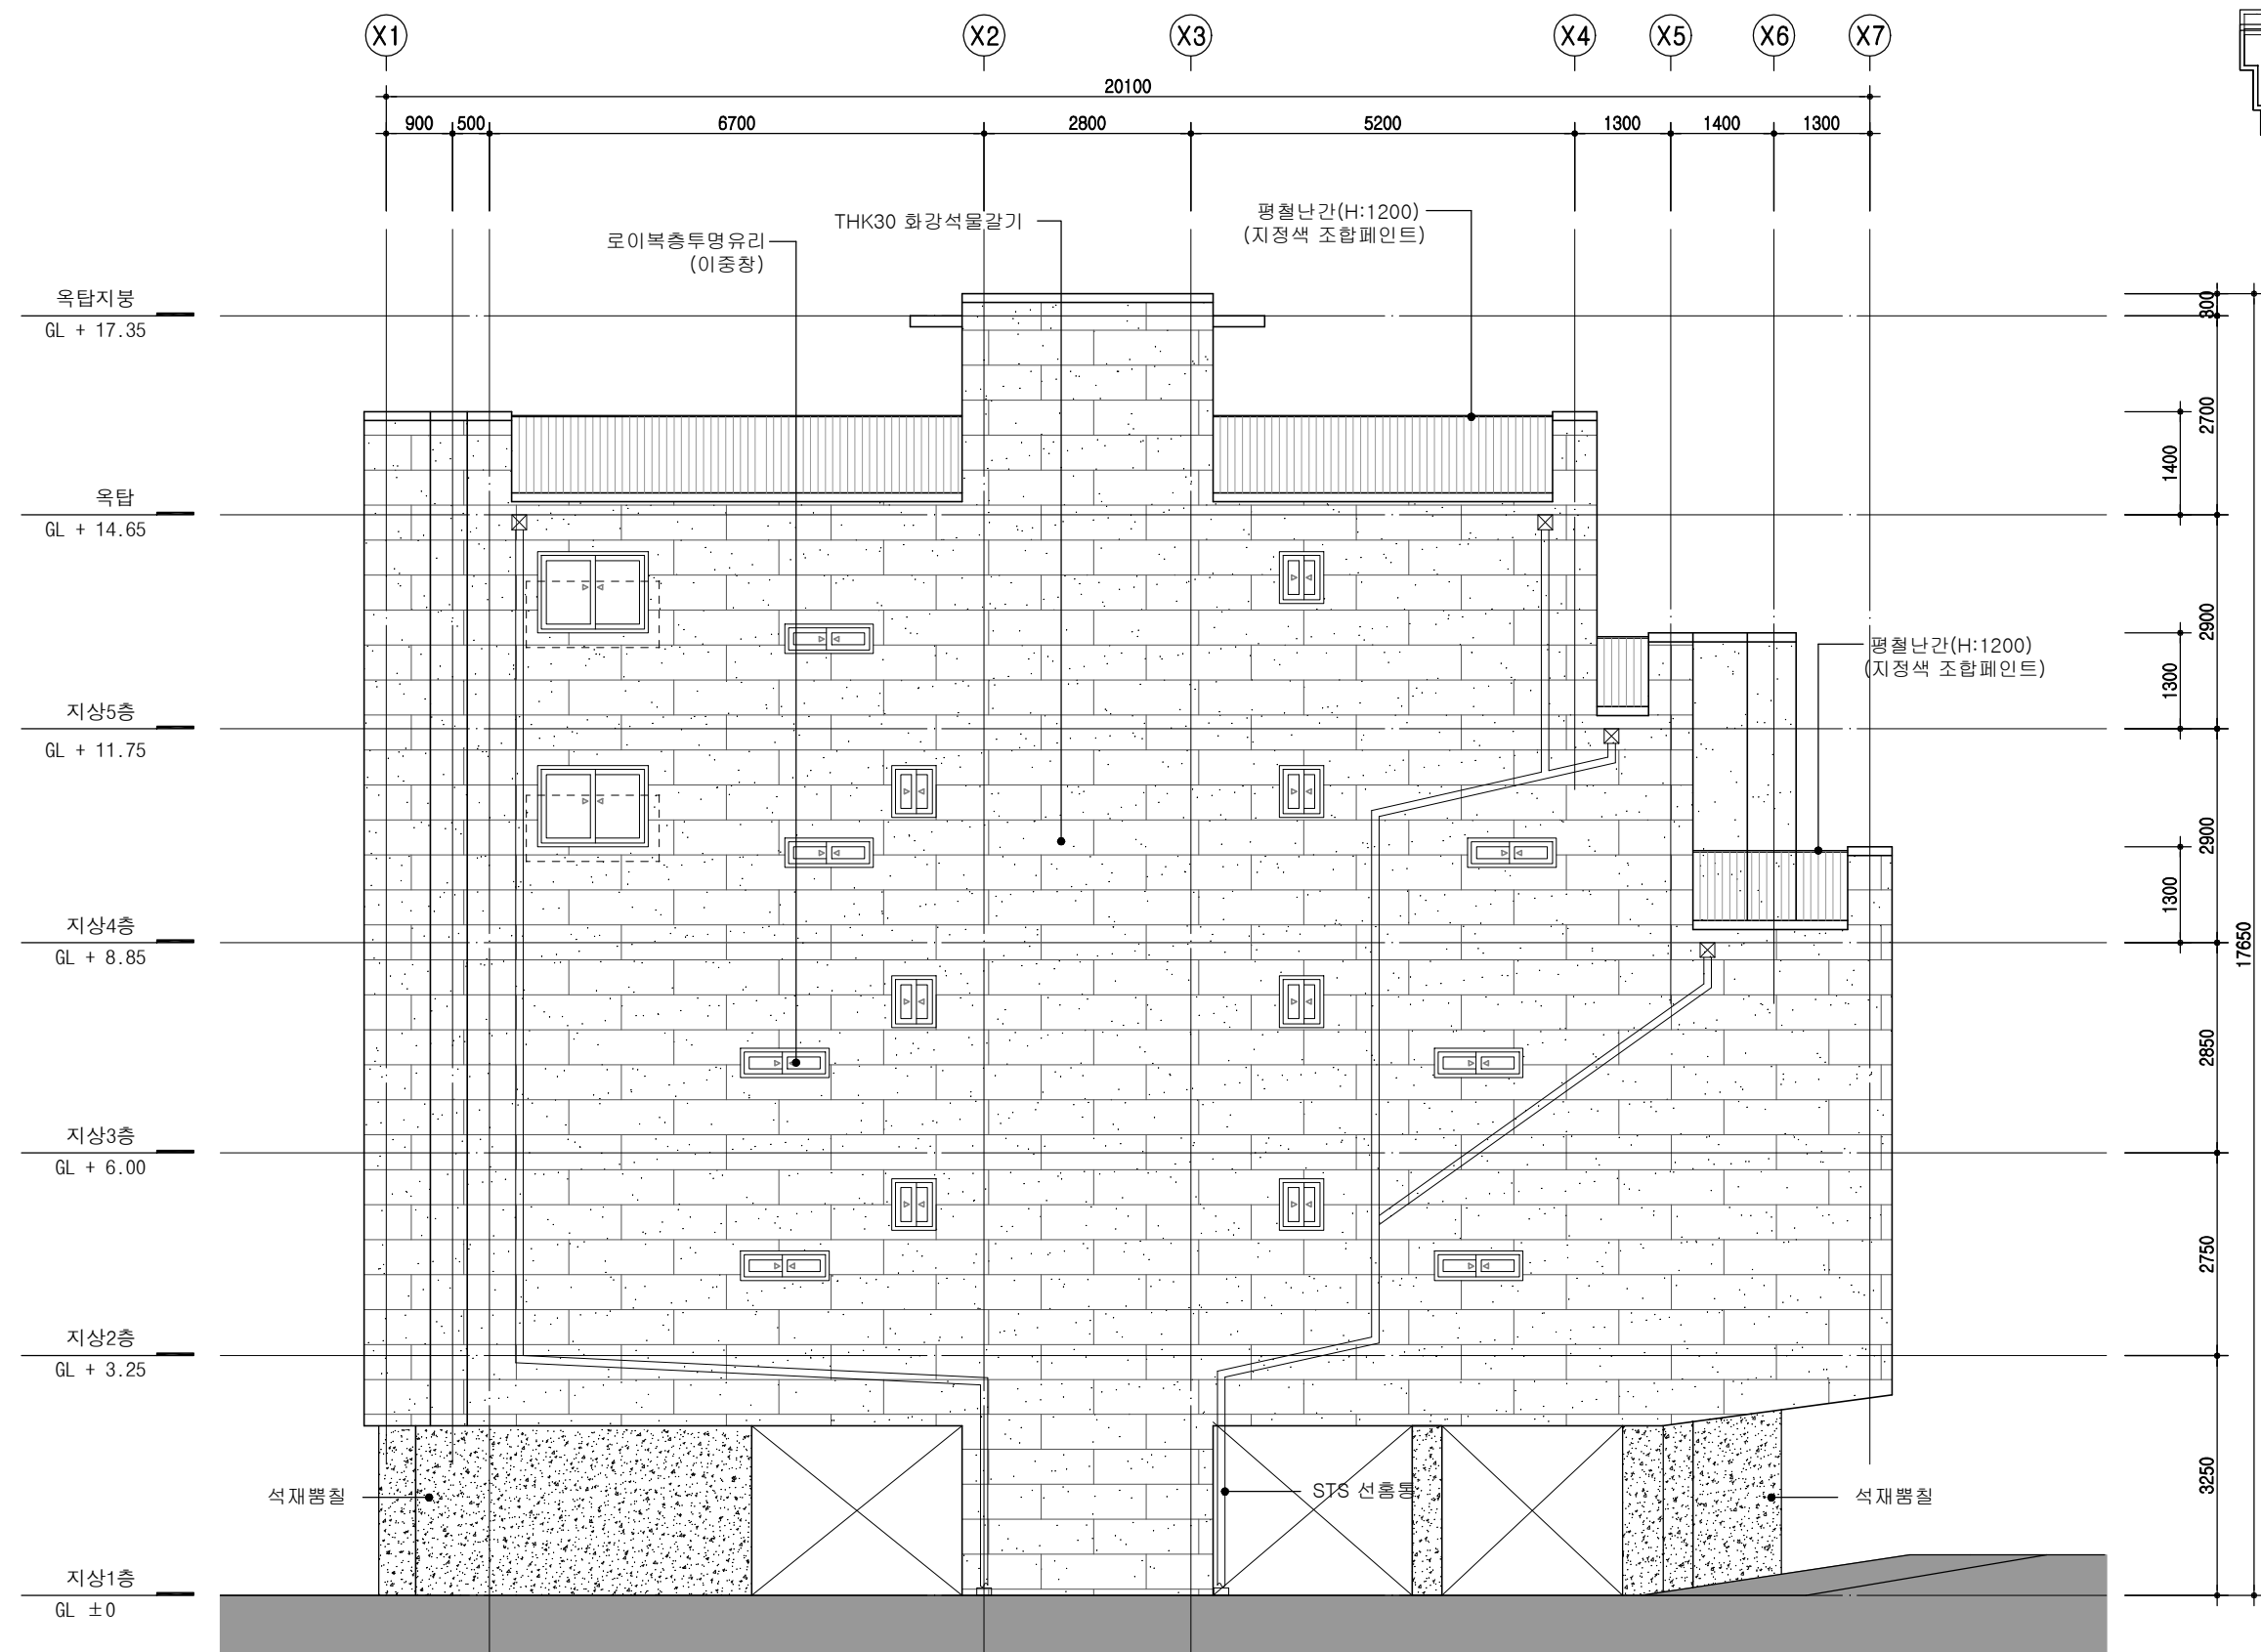


동측면도
SCALE: 1 / 100

*NOTE
 [---] 차면시설설치
 - 입면의 색상은 외관디자인계획(입면도) 참조
 - 외벽배관(흡통, 냉난방설비 등) 침입방지시설할것
 (지표면에서 지상2층, 옥상에서 최상층 배관)

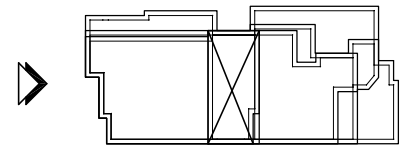

KEY PLAN

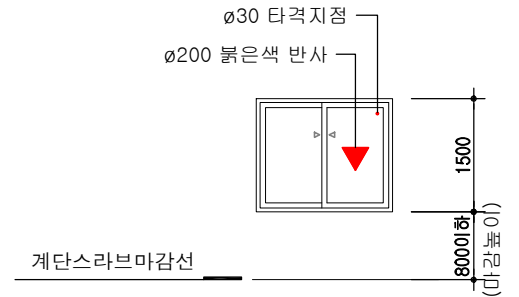

소방관 진입창



남측면도
SCALE: 1 / 100

*NOTE

[] 차면시설설치

- 입면의 색상은 외관디자인계획(입면도) 참조

- 외벽배관(흡통, 냉난방설비 등) 침입방지시설할것
(지표면에서 지상2층, 옥상에서 최상층 배관)

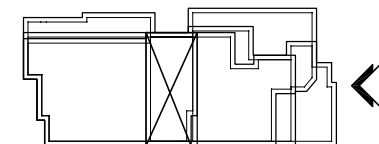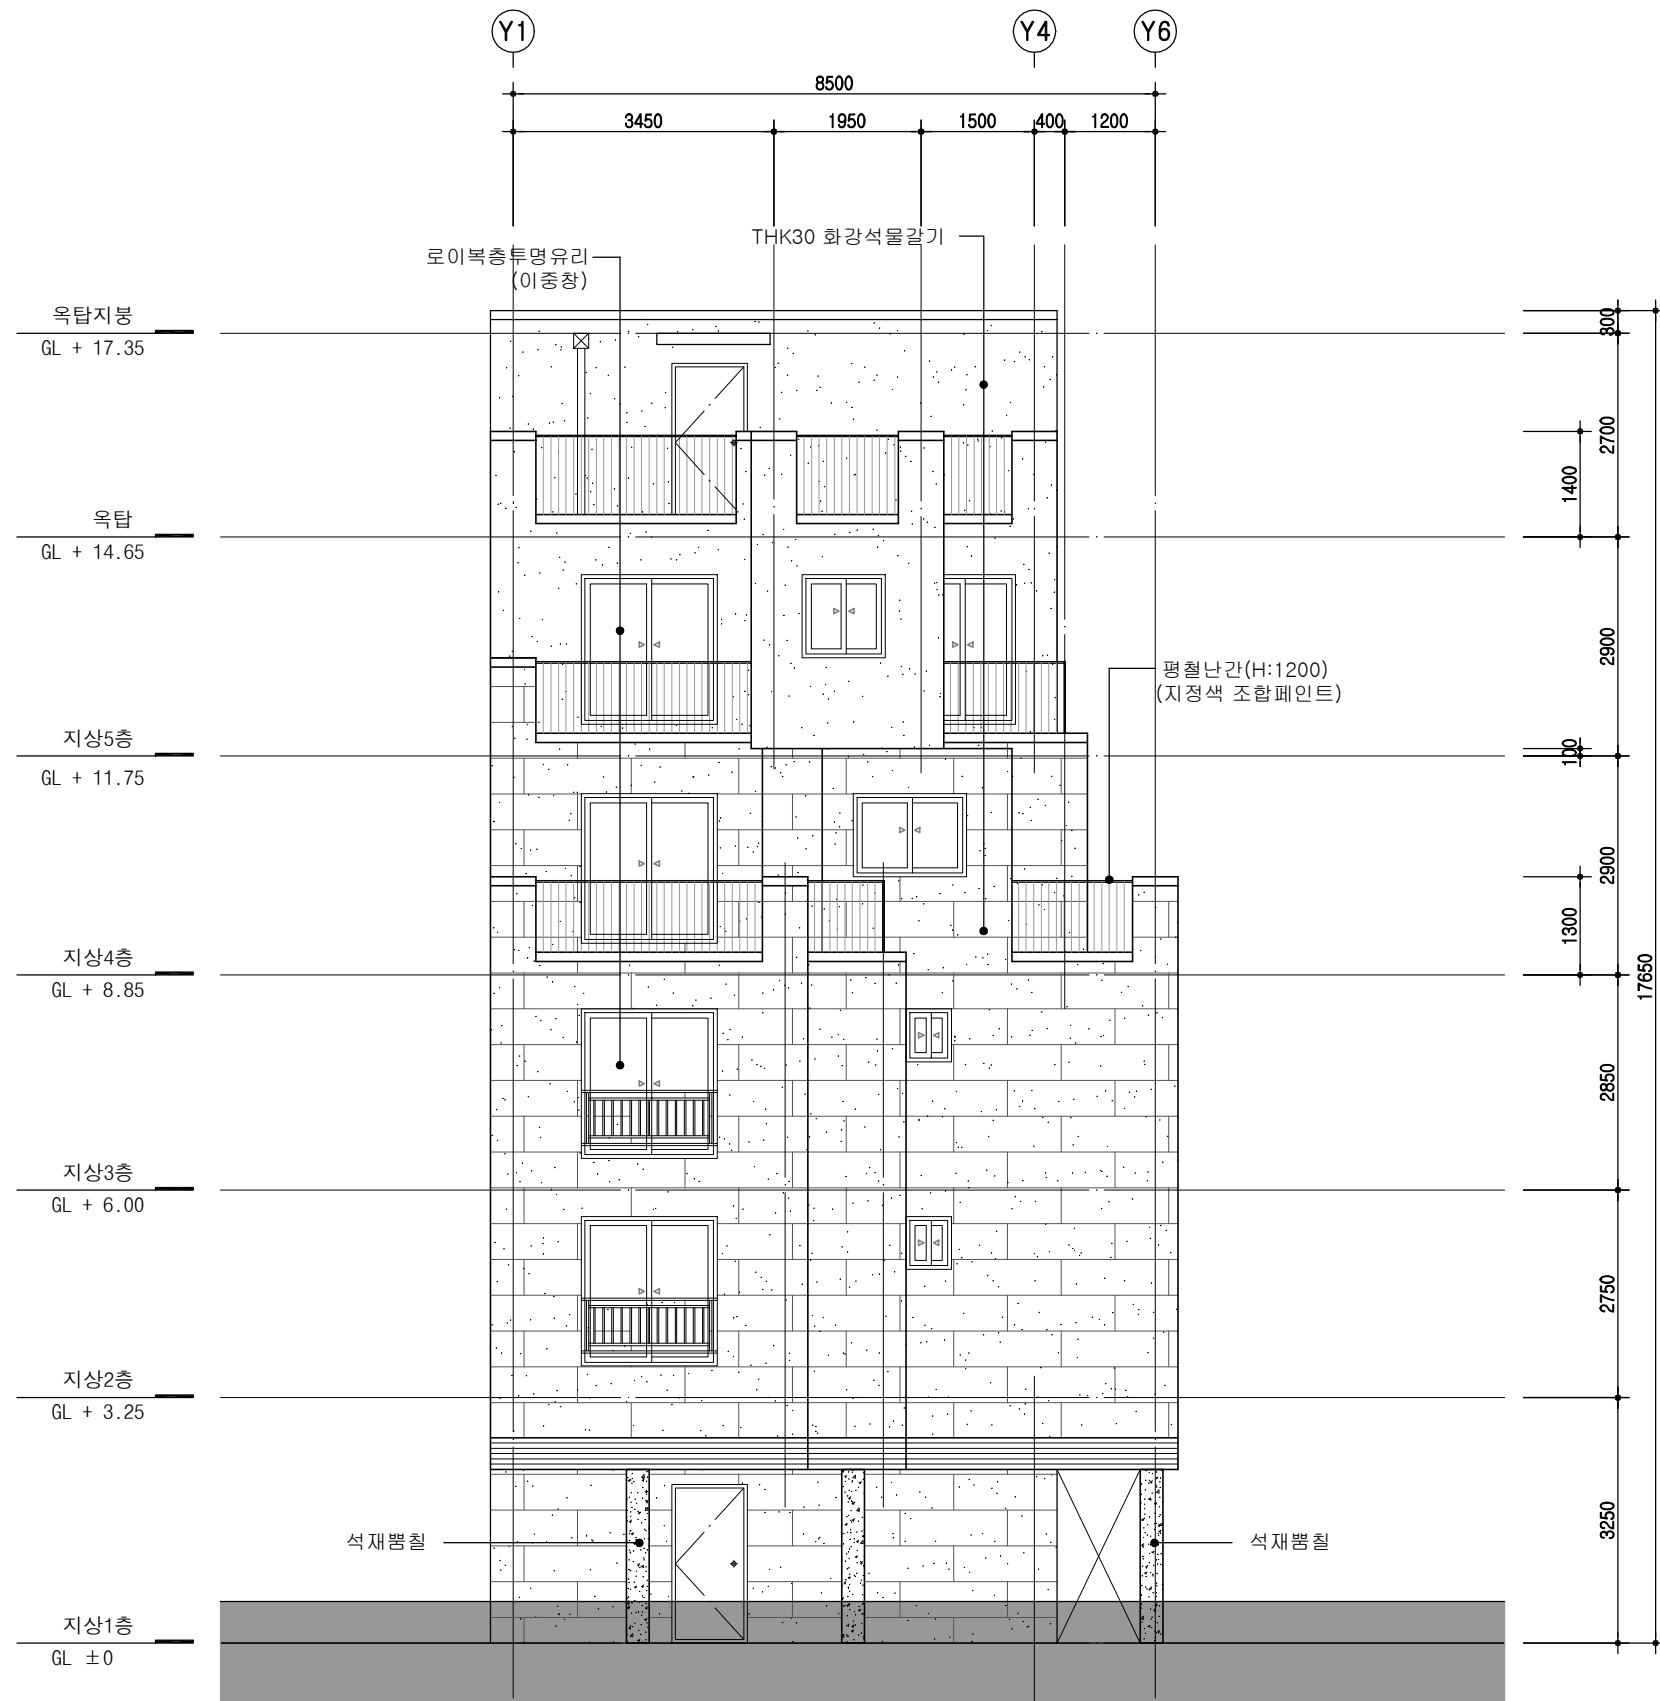

KEY PLAN



북쪽면도
SCALE: 1 / 100

*NOTE

[] 차면시설설치

- 입면의 색상은 외관디자인계획(입면도) 참조

- 외벽배관(흡통, 냉난방설비 등) 침입방지시설할것
(지표면에서 지상2층, 옥상에서 최상층 배관)

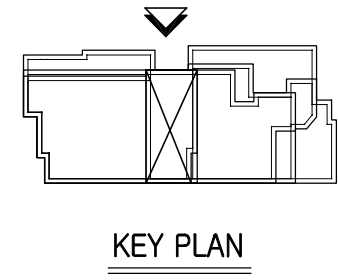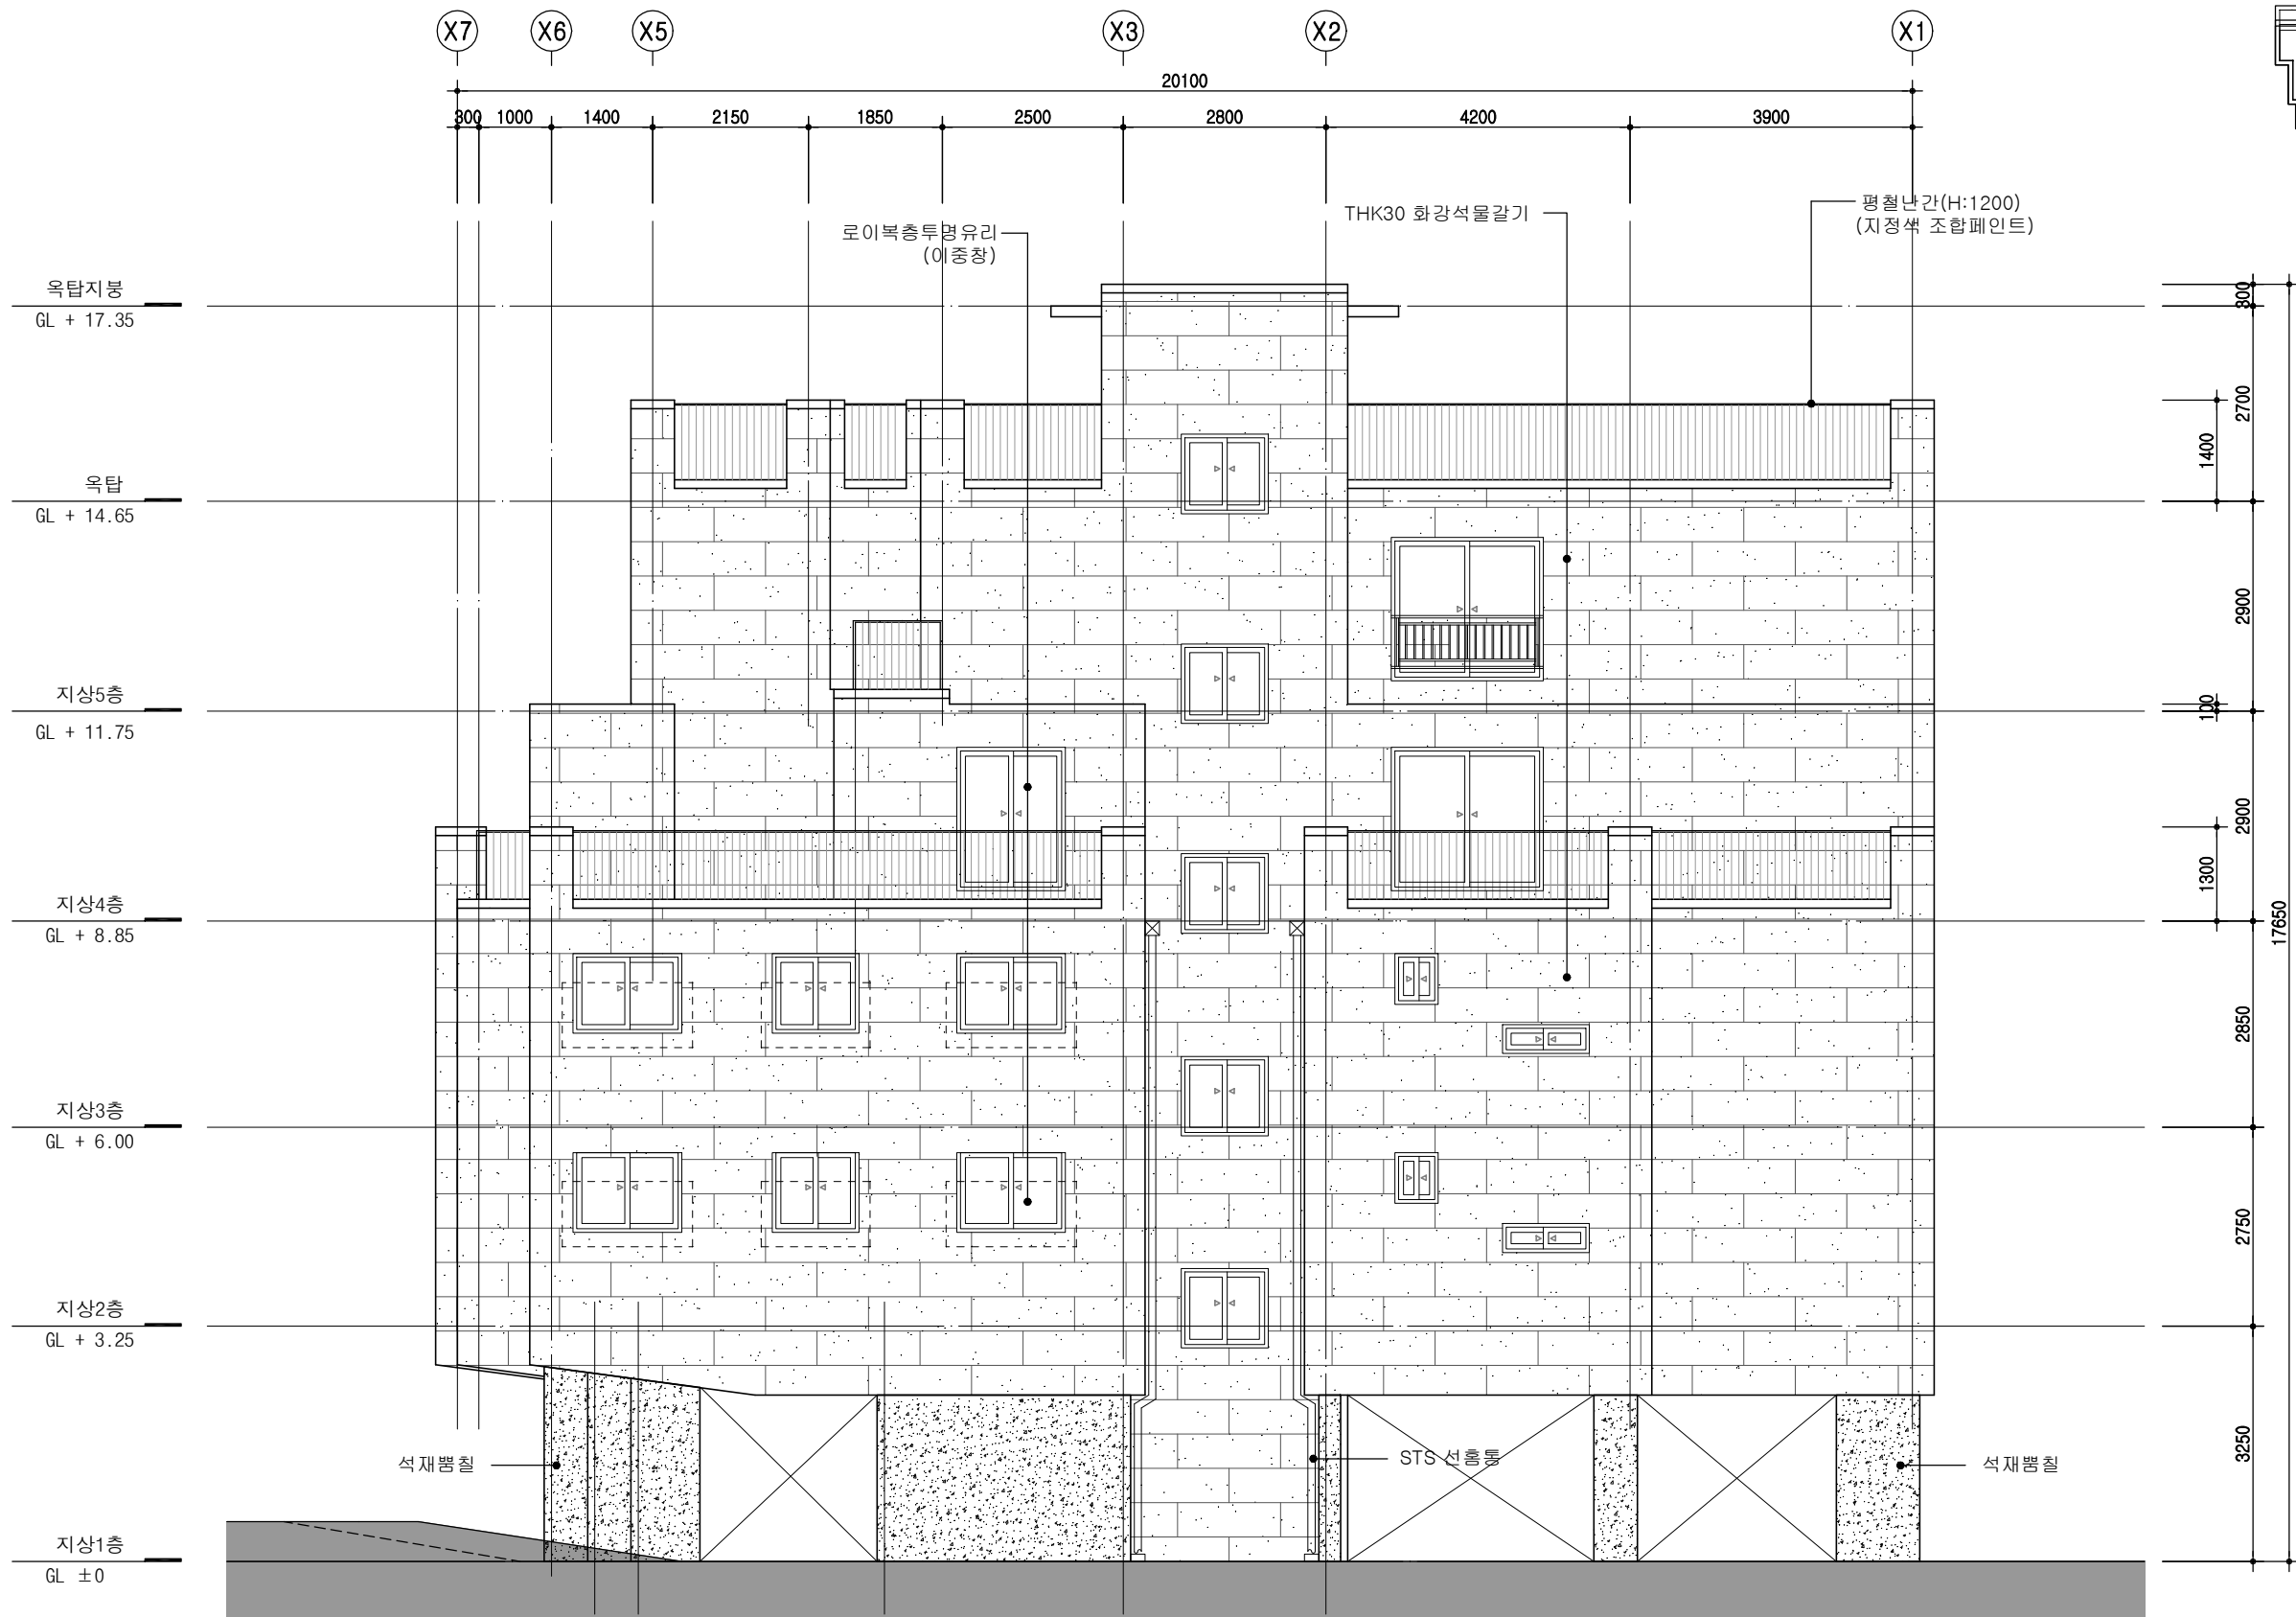

서 측 면 도
SCALE: 1 / 100

*NOTE
 [---] 차면시설설치
 - 입면의 색상은 외관디자인계획(입면도) 참조
 - 외벽배관(흡통, 냉난방설비 등) 침입방지시설할것 (지표면에서 지상2층, 옥상에서 최상층 배관)



본건 전경



주변 환경



공용현관



공용현관



주차장



주차장



201,301호



202,302호



203,303호



401호



402호



501호



502호



계단실