



바다건축

BADA ARCHITECTS & ENGINEERS
TEL: 031) 523-3363 FAX: 031) 571-3348

NOTE

DATE	REV	DESCRIPTION	DRW	CHE	APP
일지	번	명	내	용	

APPROVED BY
승 인

CHECKED BY
리 통

DRAWN BY
제 도


DATE
일 지 2018.09.


PROJECT NAME
사 업 명
시흥동 849-1, 32, 33번지
도시명생활주택(원룸형)
신축공사 (A 단지)

DRAWING TITLE
도 면 명
1층 평면도
(A 단지)

SCALE
축 적
1 / 100


DRAWING NO.
도 면 번 호
A-

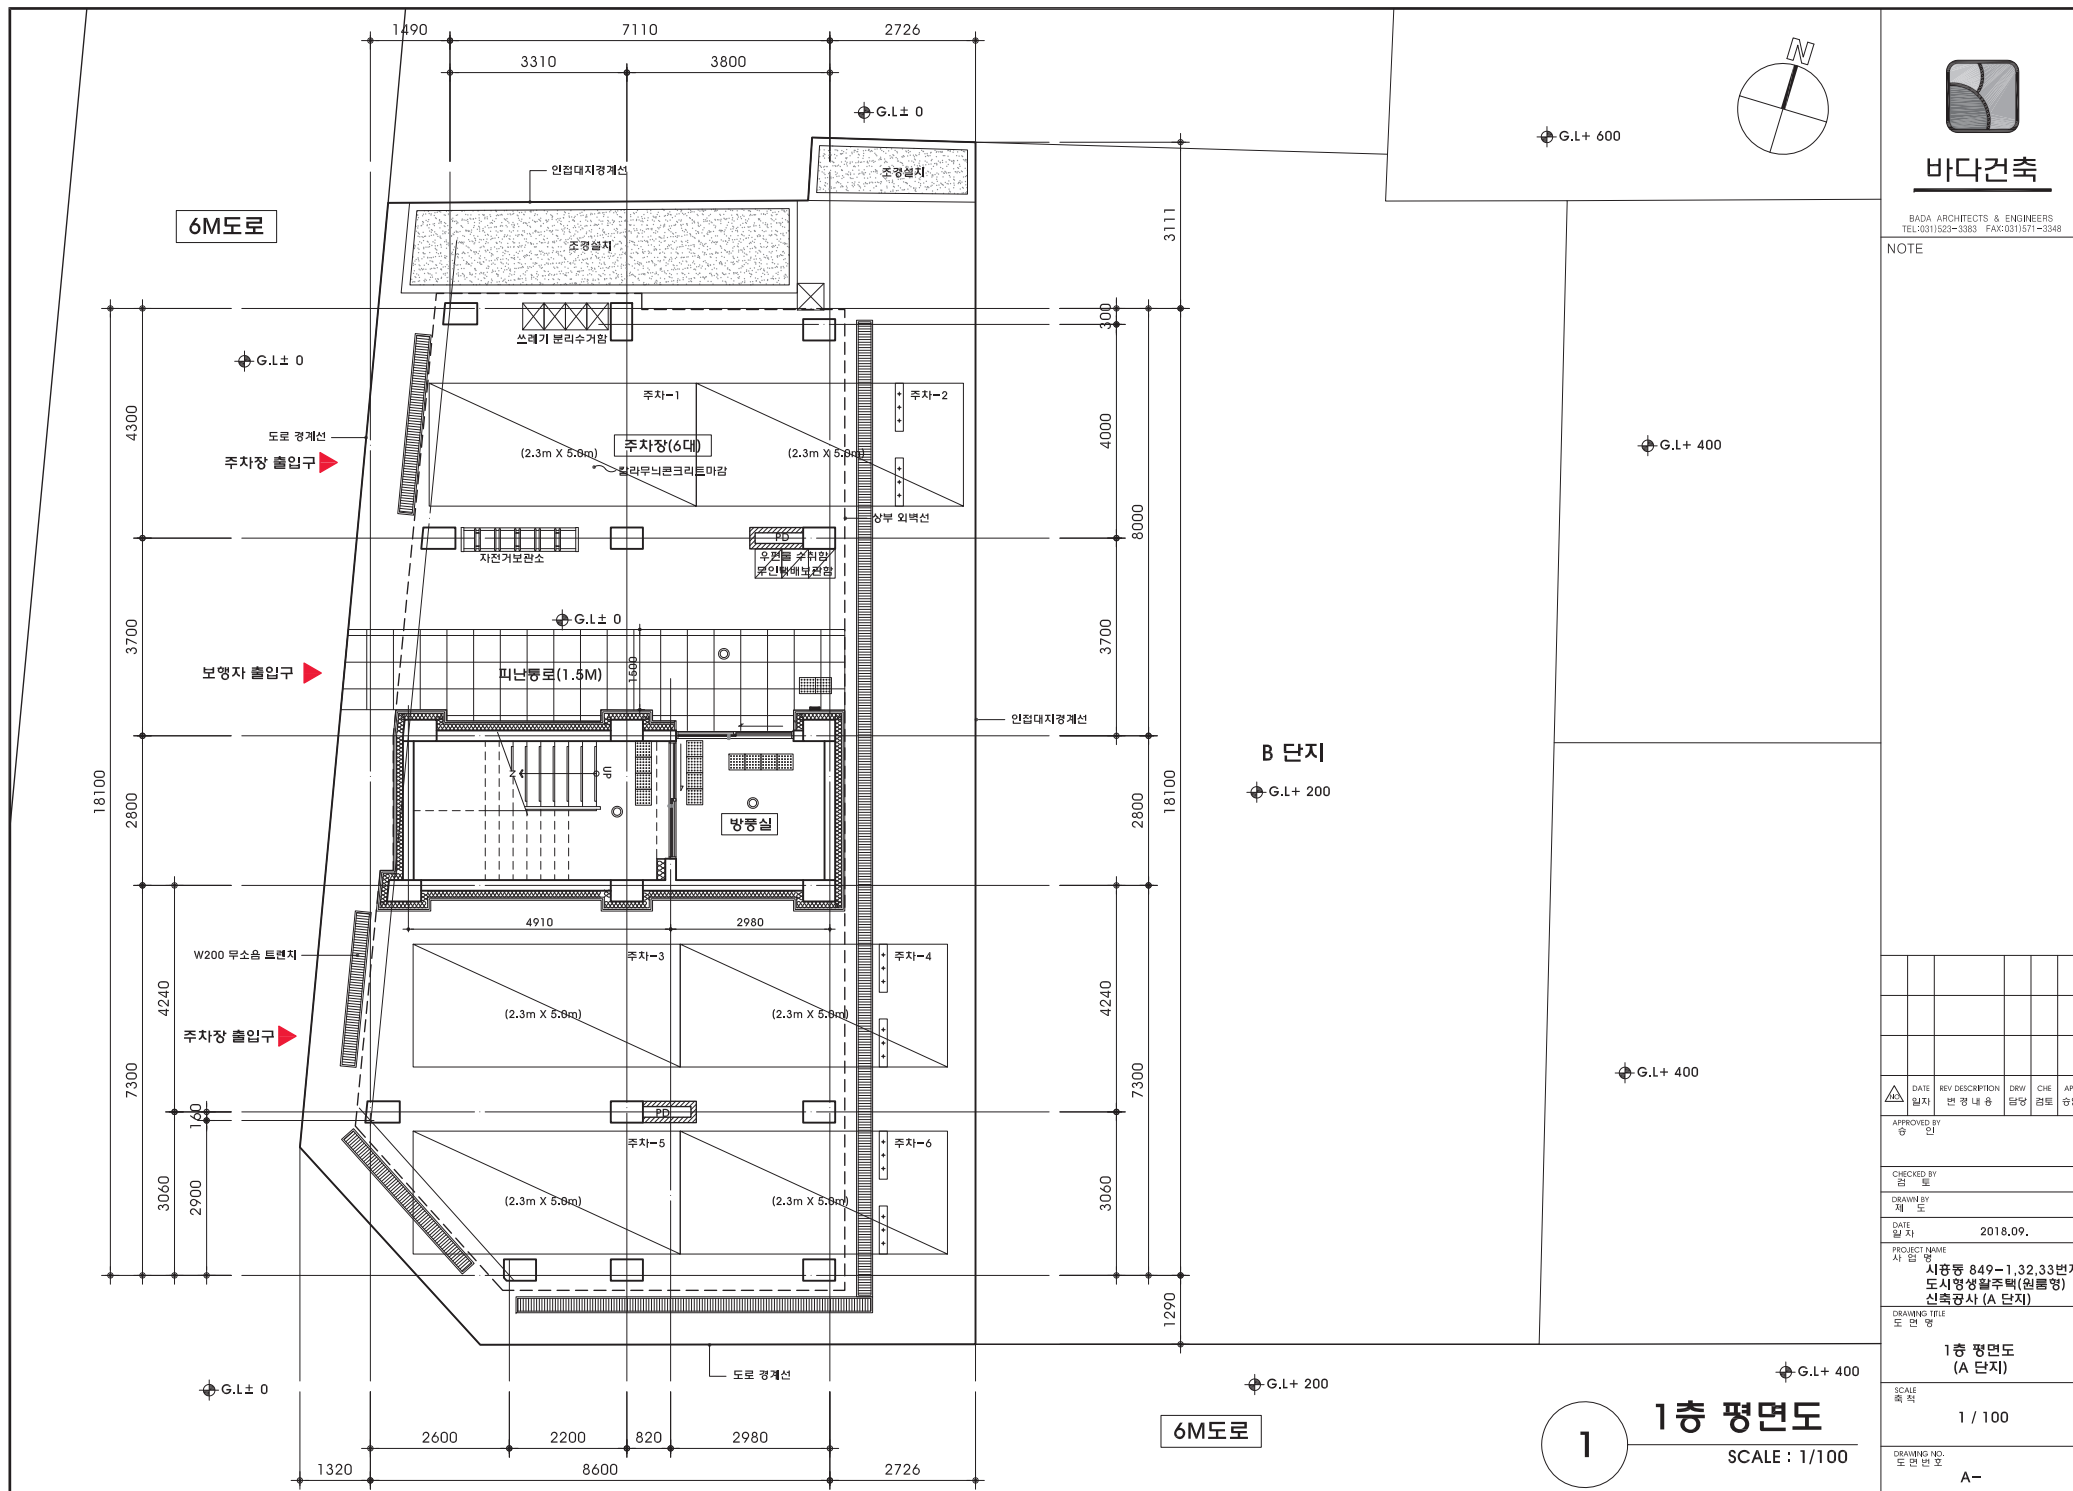

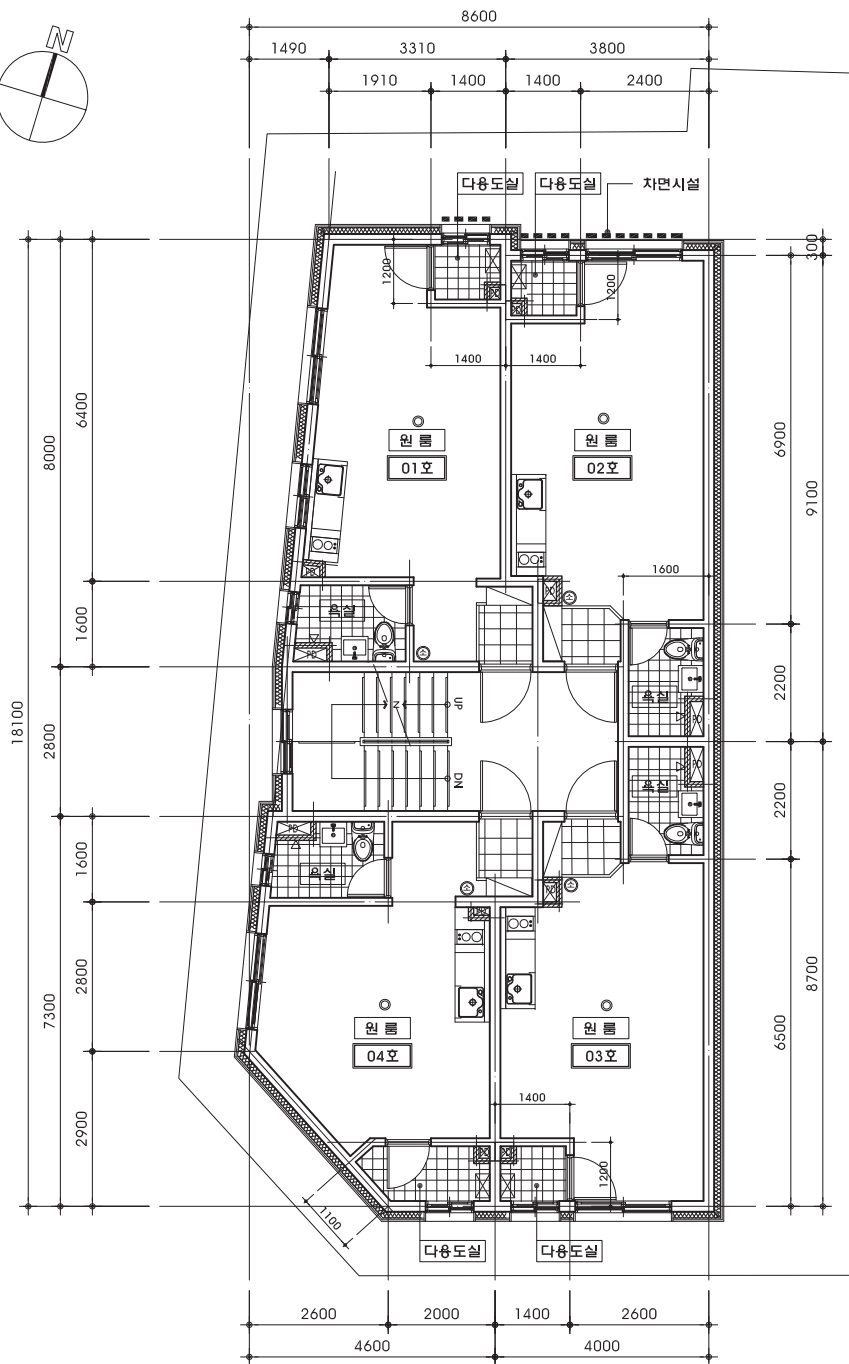


2층,3층 평면도

SCALE : 1/100

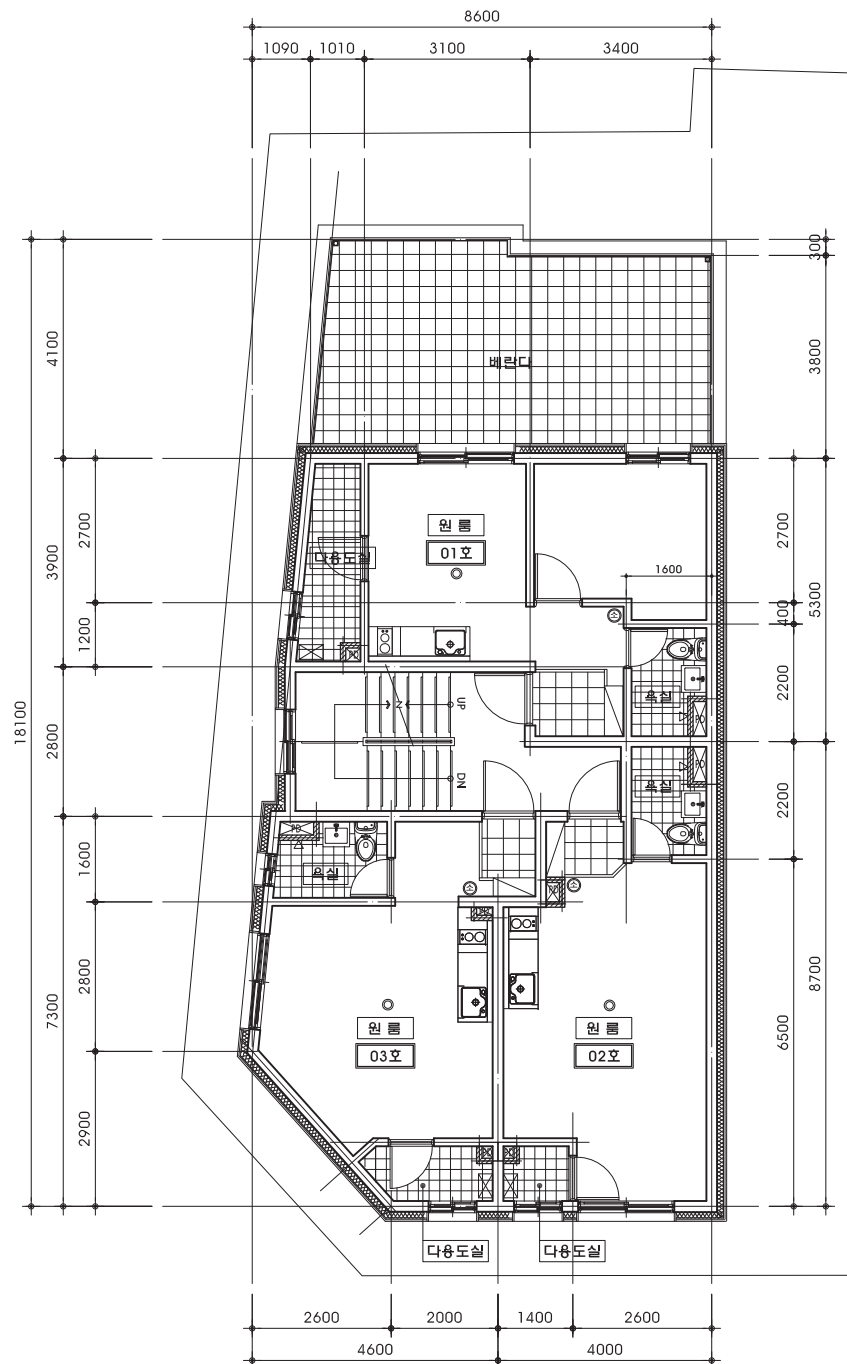

4층 평면도


SCALE : 1/100

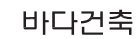

BADA ARCHITECTS & ENGINEERS
TEL:031)523-3383 FAX:031)571-3348

NOTE


[illegible]

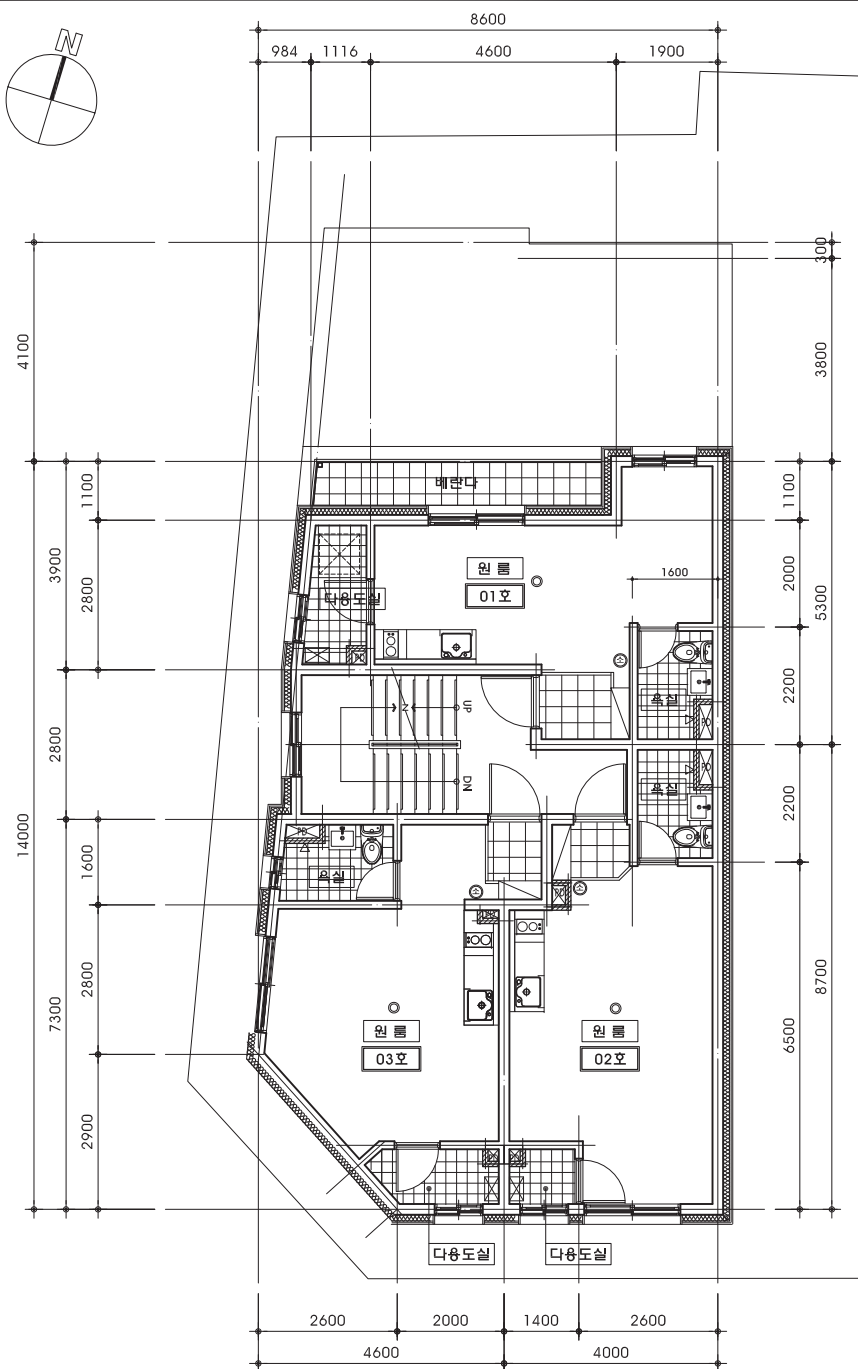

Architectural floor plan showing dimensions in millimeters. The plan includes a central staircase labeled 'D.C.' and a rectangular area labeled '뒤편벽' (Back Wall). Dimensions are provided for various sections:

- Overall width: 8600mm
- Overall depth: 18100mm
- Top horizontal dimensions: 710mm, 4490mm, 3400mm, 1500mm, 1900mm
- Left vertical dimensions: 4100mm, 3900mm, 2800mm, 2800mm, 7300mm, 2900mm
- Right vertical dimensions: 3800mm, 1100mm, 3900mm, 2800mm, 7300mm
- Bottom horizontal dimensions: 2600mm, 2600mm, 3400mm
- Internal vertical dimensions: 1100mm, 2800mm, 2800mm


2 옥탑 평면도
SCALE : 1/100

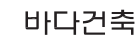

BADA ARCHITECTS & ENGINEERS
TEL:031)523-3383 FAX:031)571-3348


NOTE

A	DATE 일지	REV DESCRIPTION 변경 내역	DRAW 도면명	CHE 검토자	
APPROVED BY 승인					
CHECKED BY 확인					
DRAWN BY 제 도					
DATE 발주 일자 2018.09.					
PROJECT NAME 시공품 명 : 사 일 방 동 849-1,32,33번 도시양생빌주택(원룸형 신축공사(A 단지))					
DRAWINGS TITLE 도 면 명 : 5층 옥상 평면도 (A 단지)					
SCALE 축척 : 1 / 100					
DRAWING NO. 도 면 번호 : A-					

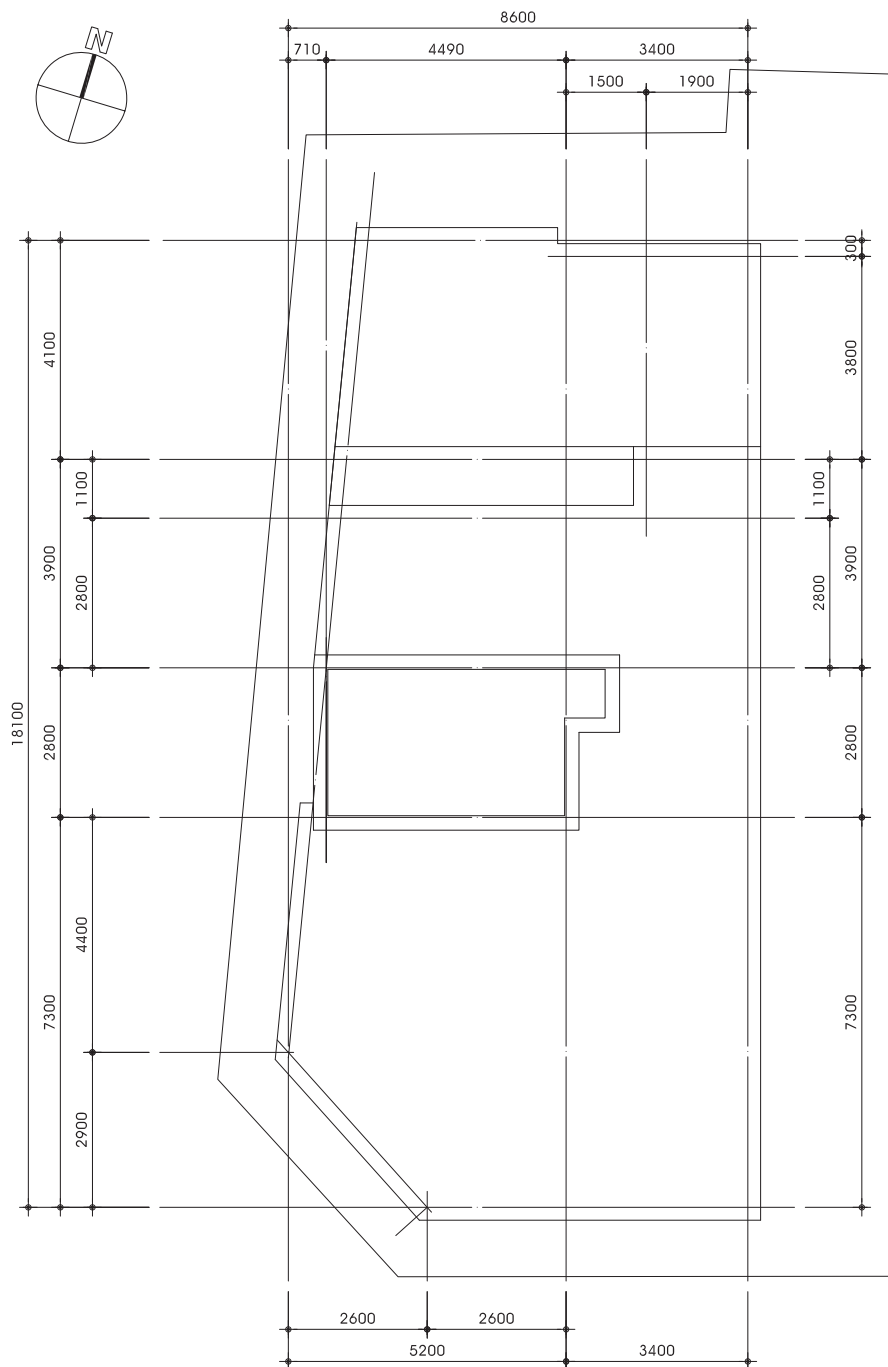


옥탑지붕 평면도

SCALE : 1/100

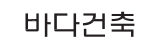


NOTE

	DATE 일차	REV DESCRIPTION 번 경 내 용	DRW 일차	CHE 검토	APP 승인
APPROVED BY 승 인					
CHECKED BY 검 토					
DRAWN BY 제 도					
DATE 일차		2018.09.			
PROJECT NAME 사 명					
시공동 849-1,32,33번지 도시형생활주택(원룸형) 신축공사 (A 단지)					
DRAWING TITLE 도 명					
옥탑지동 평면도 (A 단지)					
SCALE 축 척		1 / 100			
DRAWING NO. 도 면 번호					

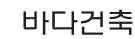


BADA ARCHITECTS & ENGINEERS
TEL:031)523-3383 FAX:031)571-3348

NOTE

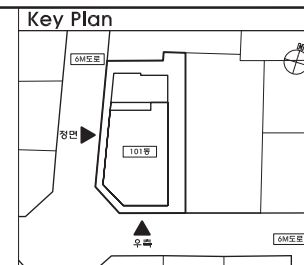


	DATE 일치	REV DESCRIPTION 변 경 내 용	DRAW 일당	CHE 검토	AP 승인
APPROVED BY 승 인					
CHECKED BY 검 토					
DRAWN BY 제 도					
DATE 일 치		2018.09.			
PROJECT NAME 사 업 명					
시공품 849-1,32,33번 도시정생활주책(원룸형) 신관공사 (A 단지)					
DRAWING TITLE 도 면 명					
정면도, 후측면도 (A 단지)					
SCALE 축 적		1 / 150			
DRAWING NO. 도 면 번 호					
A-					

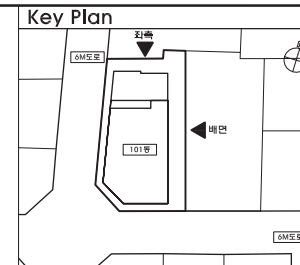


바다건축

BADA ARCHITECTS & ENGINEERS
TEL: 031-523-3363 FAX: 031-571-3348

NOTE

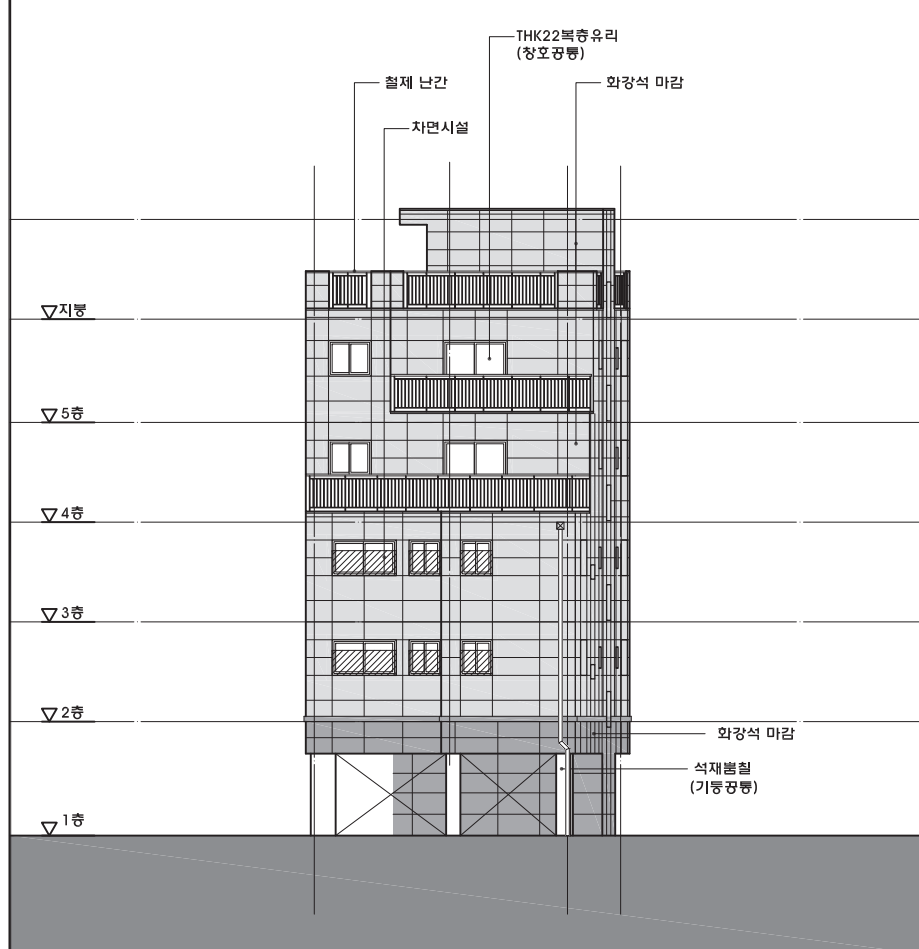

1 **좌측면도**
SCALE : 1/150

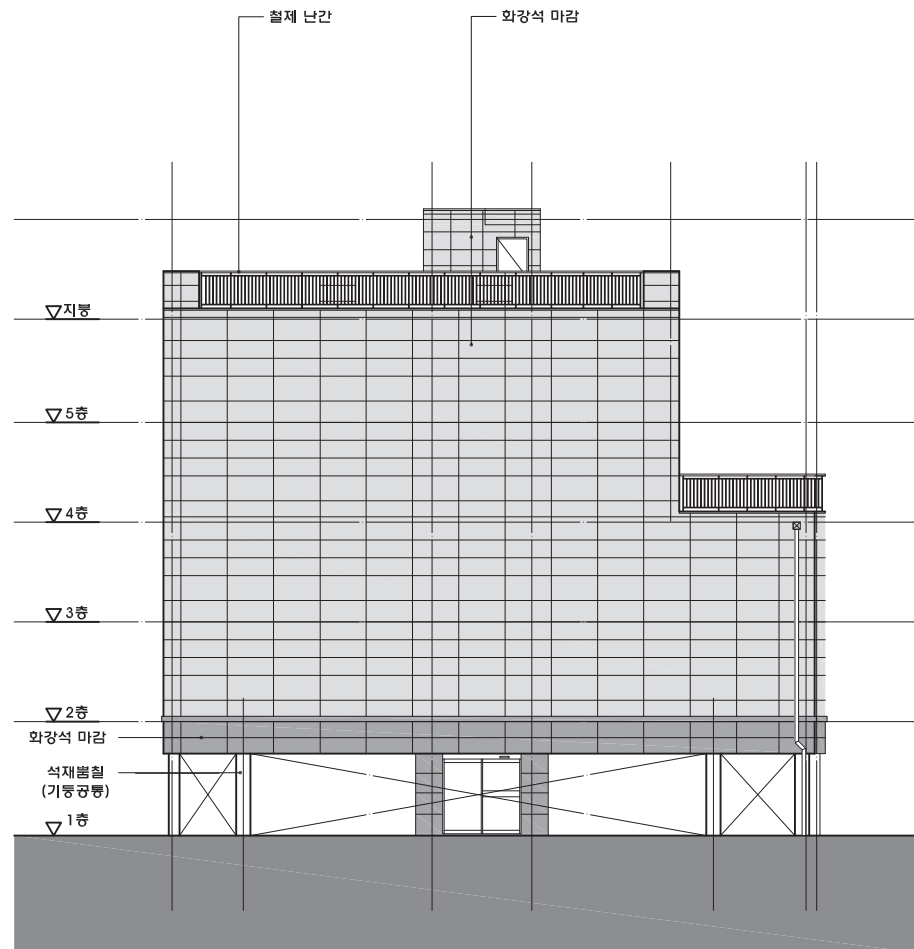

2 **배면도**
SCALE : 1/150

DATE	REV DESCRIPTION	DRW	CHE	APP
일지	변경내용	필명	검토	승인
APPROVED BY 승인				
CHECKED BY 리토				
DRAWN BY 재도				
DATE 일지 2018.09.				
PROJECT NAME 사업명 시흥동 849-1, 32, 33번지 도시명생원주택(원룸형) 신축공사 (A 단지)				
DRAWING TITLE 도면명 좌측면도, 배면도 (A 단지)				
SCALE 축척 1 / 150				
DRAWING NO. 도면번호 A-				