

독산동 234-22.24
단지형 다세대 주택 신축공사

[illegible]

== 차면시설

 보일러

 에어컨 실외기

1. 콘크리트: $f_{ck} = 24 \text{ MPa}$

2. 철근 : $f_y = 400 \text{ MPa}$

5. 제14조 제4항제2호(2007년(국회))
(미장마감포함210)

세대내벽두께:150mm(복배근)

5. 코아벽두께: 180mm(북배근)

6. 스라브두께:210mm(북배근)


Structure

Structure

Mechanical

Electrical

Fire Protection

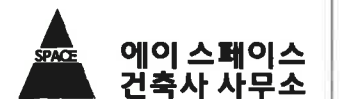

서울시 송파구 방아동 151-1 부곡빌딩 2층
(백계고분로 48가길30)
TEL 02) 417-8606 FAX 02) 516-1852

Drawing Title

1층 평면도

Scale 1/150


Date 2017

Approved By 건축사 백남권

Checked By _____


In Charge

Drawn By _____ A- 13-1

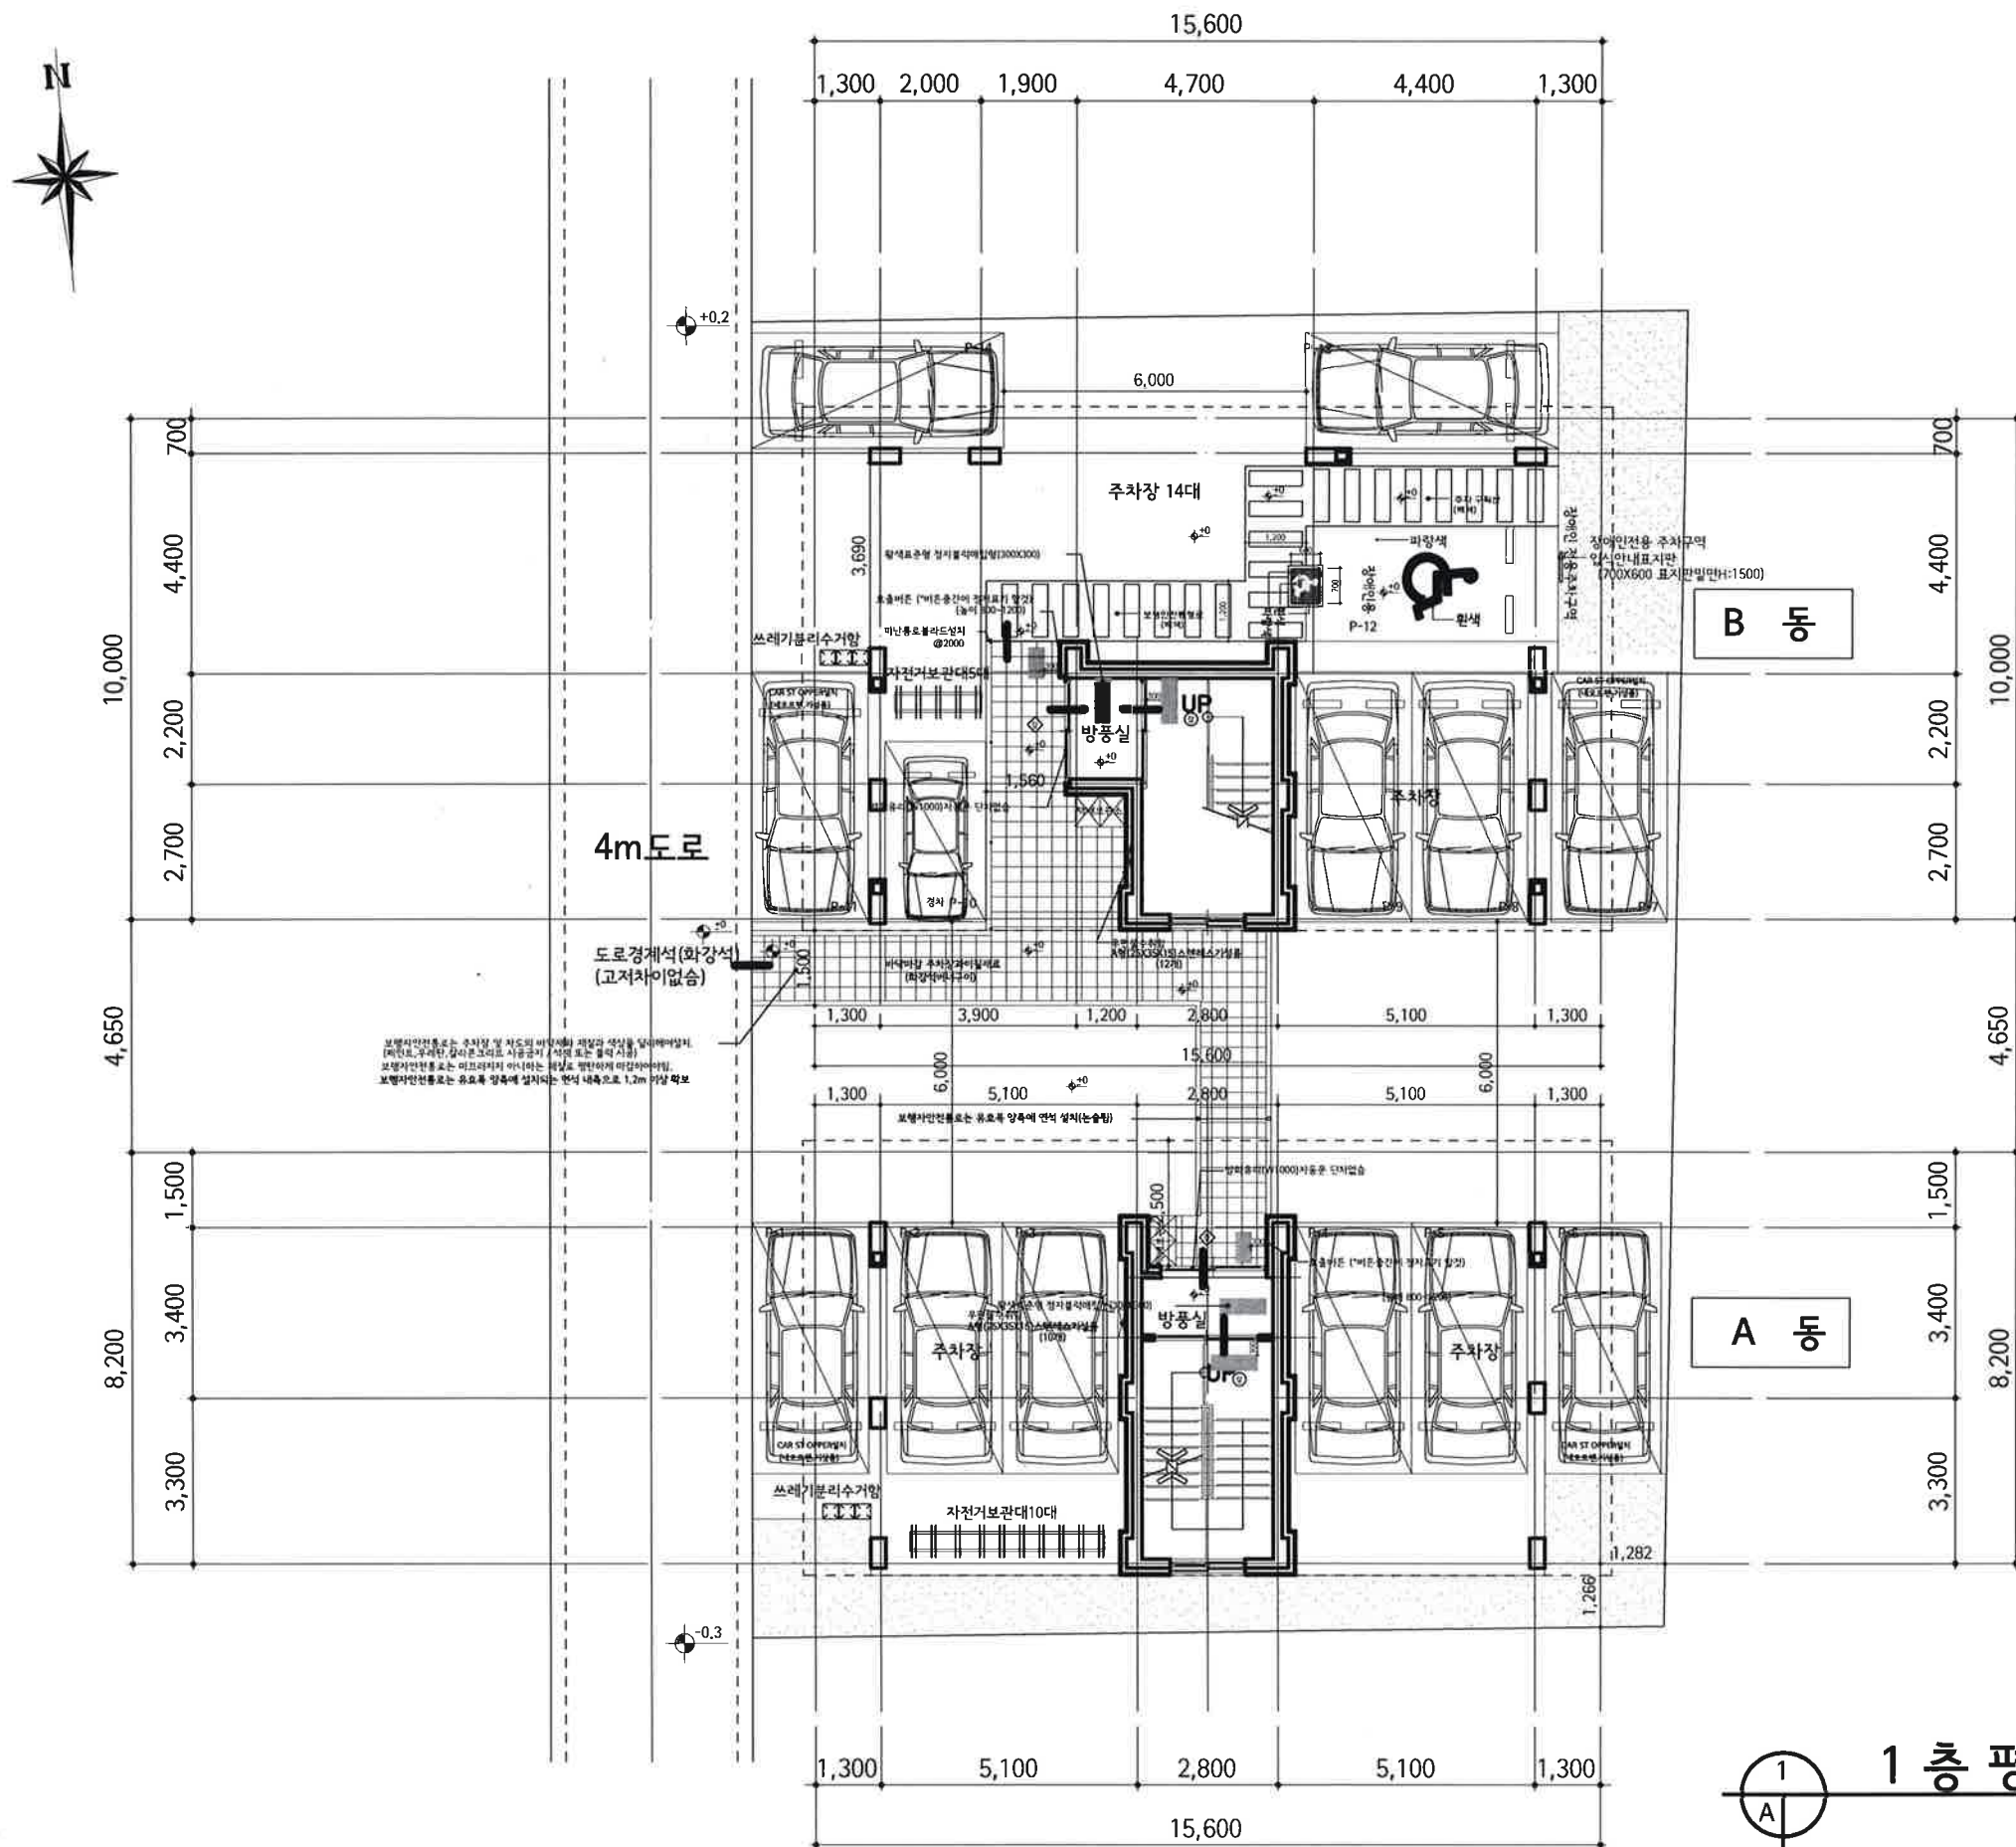

1층 평면도

축척 : 1/ 150

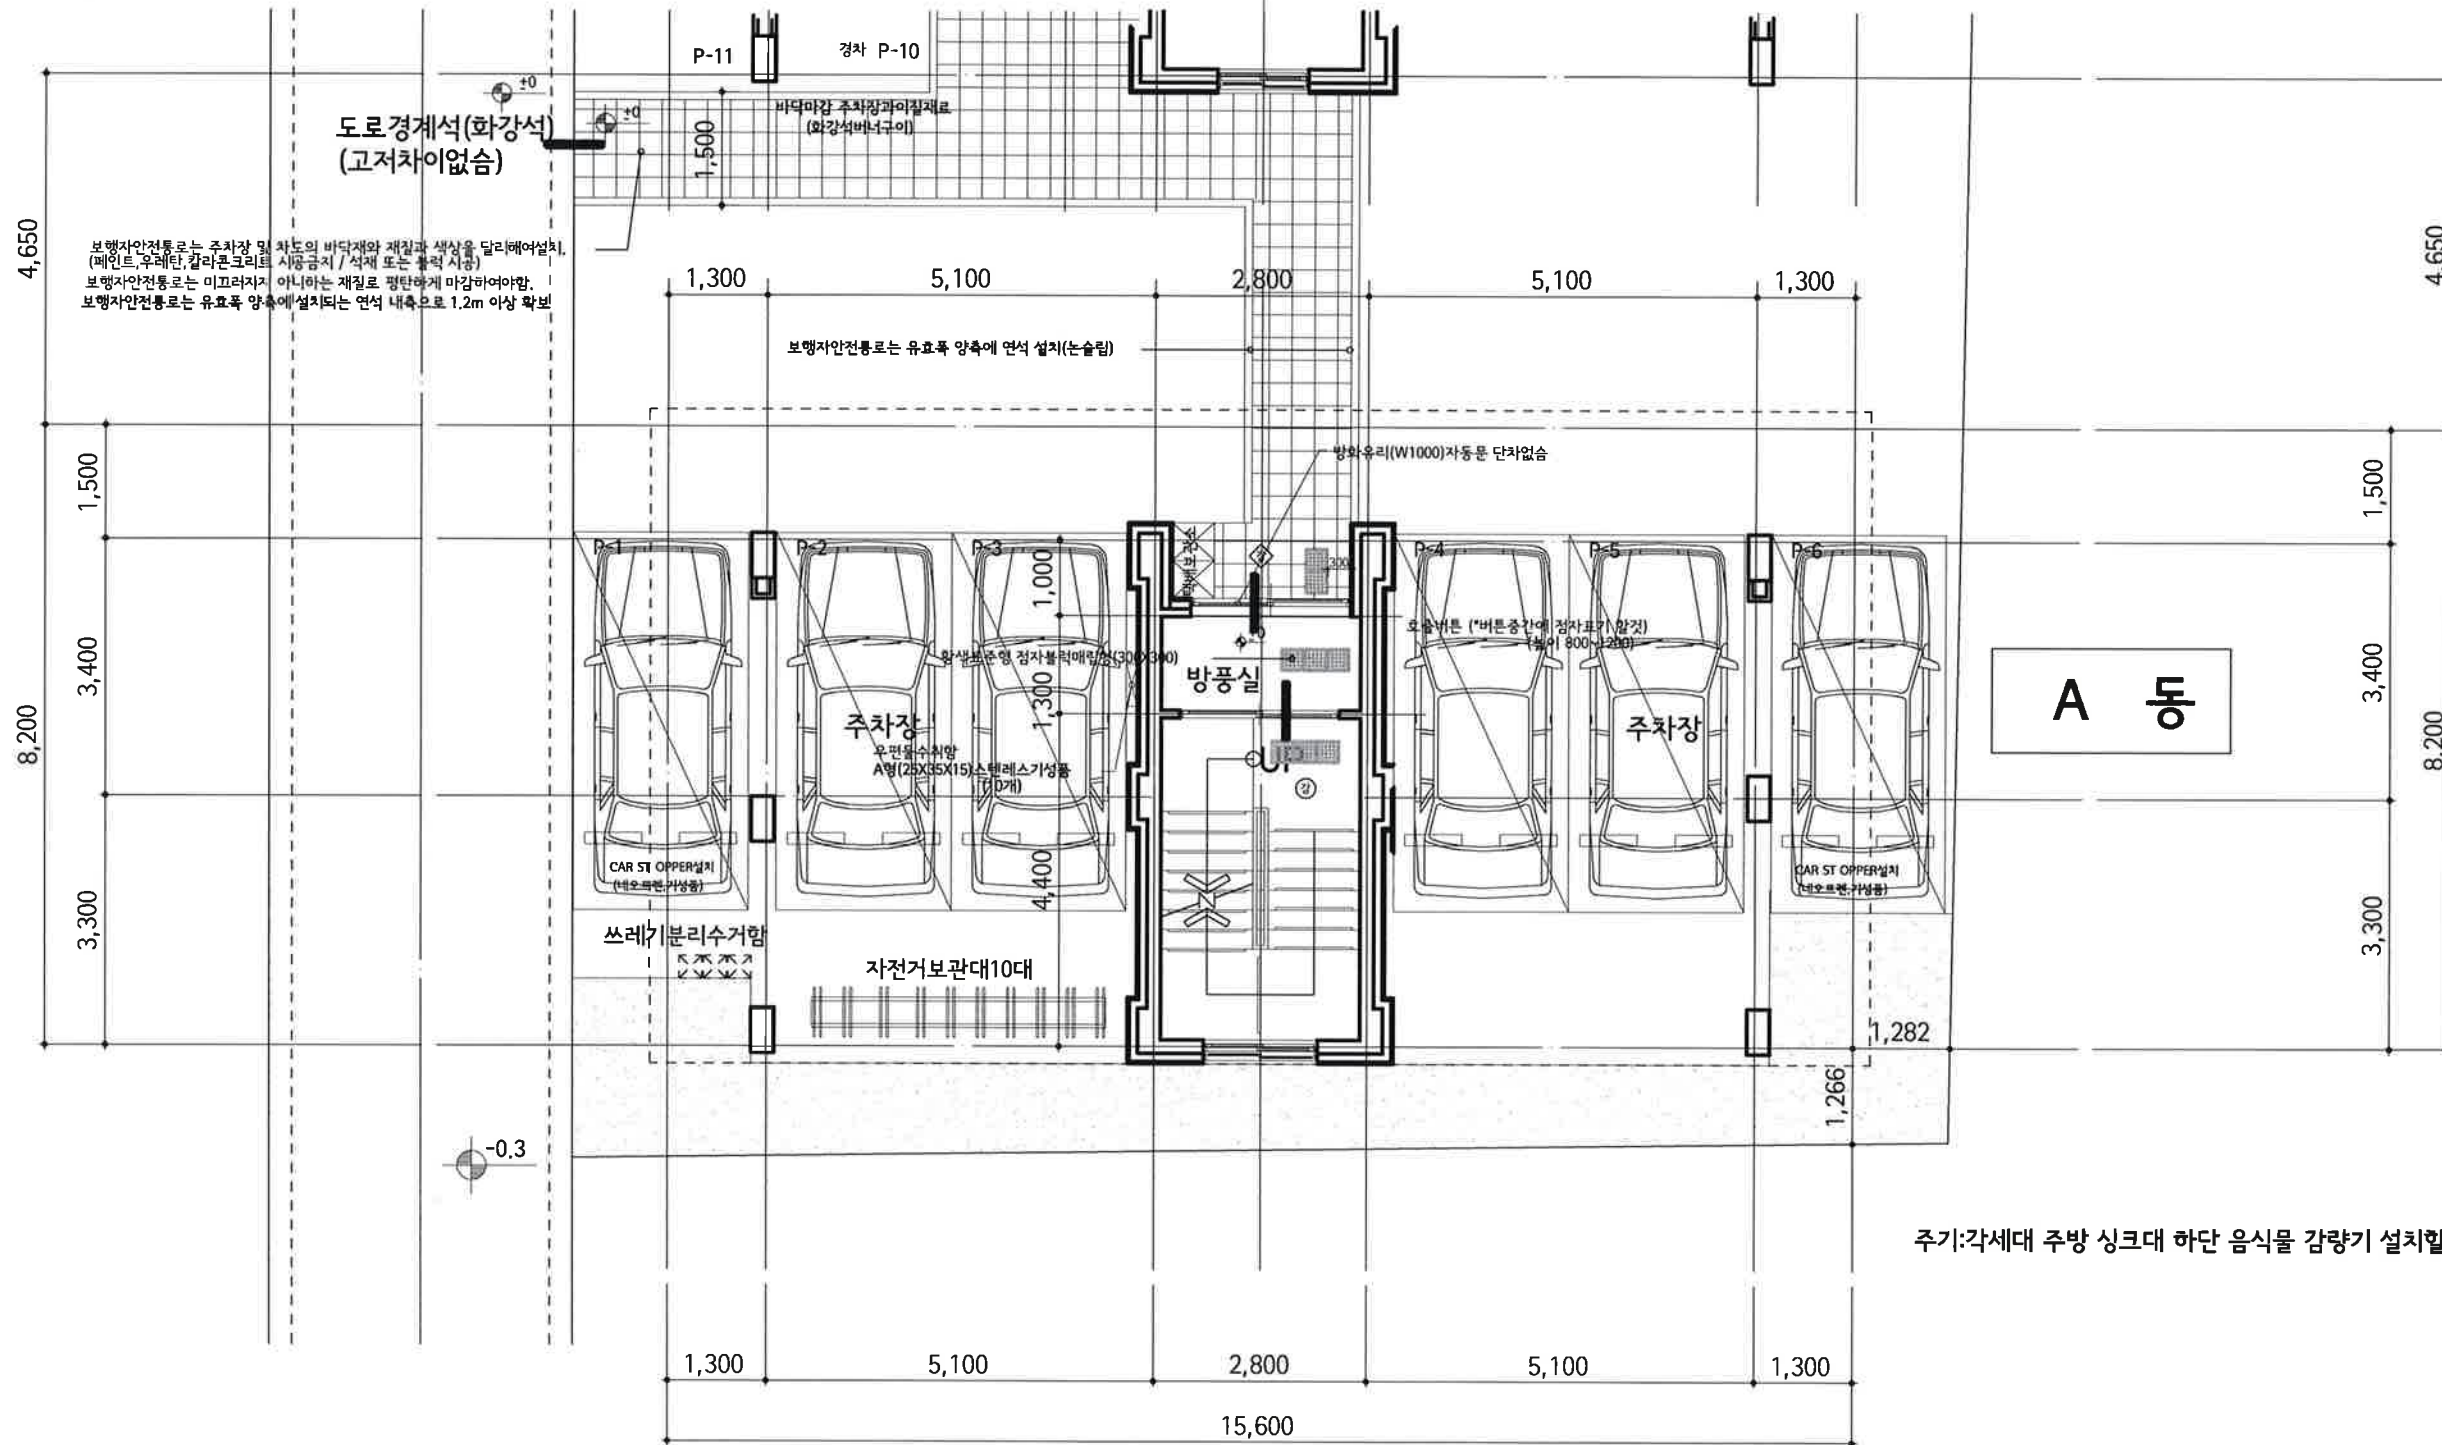

주기:각세대 주방 싱크대 하단 음식물 감량기 설치할것

1 층 평면도 (A동)
축척: 1/100

Project Title.

독산동 234-22.24

단지형 다세대 주택 신축공사

Date.
No. Revision

NOTE

Structure

Mechanical

Electrical

Fire Protection

에이 스페이스
건축사 사무소

서울시 송파구 방이동 151-1 부평빌딩 2층
(특정고분포 48가정30)
TEL 02) 417-8606 FAX 02) 516-1852

Drawing Title

1 층 평면도 (A동)

Scale 1/100 A4:150

Date

Approved By 건축사 백남권

Checked By

In Charge

Drawn By A- 14

Project Title.

독산동 234-22.24

단지형 다세대 주택 신축공사

Date.

No. Revision

NOTE

- ② 단독경보감지기(연기)
- ③ 단독경보감지기(열)
- ④ ABC분말소화기(3.3KG)
- ⑤ 자동확산소화기설치

- - - 차면시설

보일러

에어컨 실외기

* 구조 *

1. 콘크리트: $f_{ck} = 24 \text{ MPa}$

2. 철근: $f_y = 400 \text{ MPa}$

3. 세대간벽두께: 200mm (복배근)
(미장마감포함210)

세대내벽두께: 150mm (복배근)

4. 외벽두께: 180mm (복배근)

5. 코아벽두께: 180mm (복배근)

6. 스라브두께: 210mm (복배근)

Structure

Mechanical

Electrical

Fire Protection



에이 스페이스
건축사 사무소

서울시 송파구 방아동 151-1 부평빌딩 2층

(등록번호 48가설30)

TEL 02) 417-8606 FAX 02) 516-1852

Drawing Title

지붕 & 옥탑 평면도
(A동)

Scale 1/100, A4:150



Date

Approved By 건축사 박남영

Checked By

In Charge

Drawn By A- 16

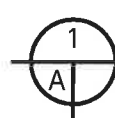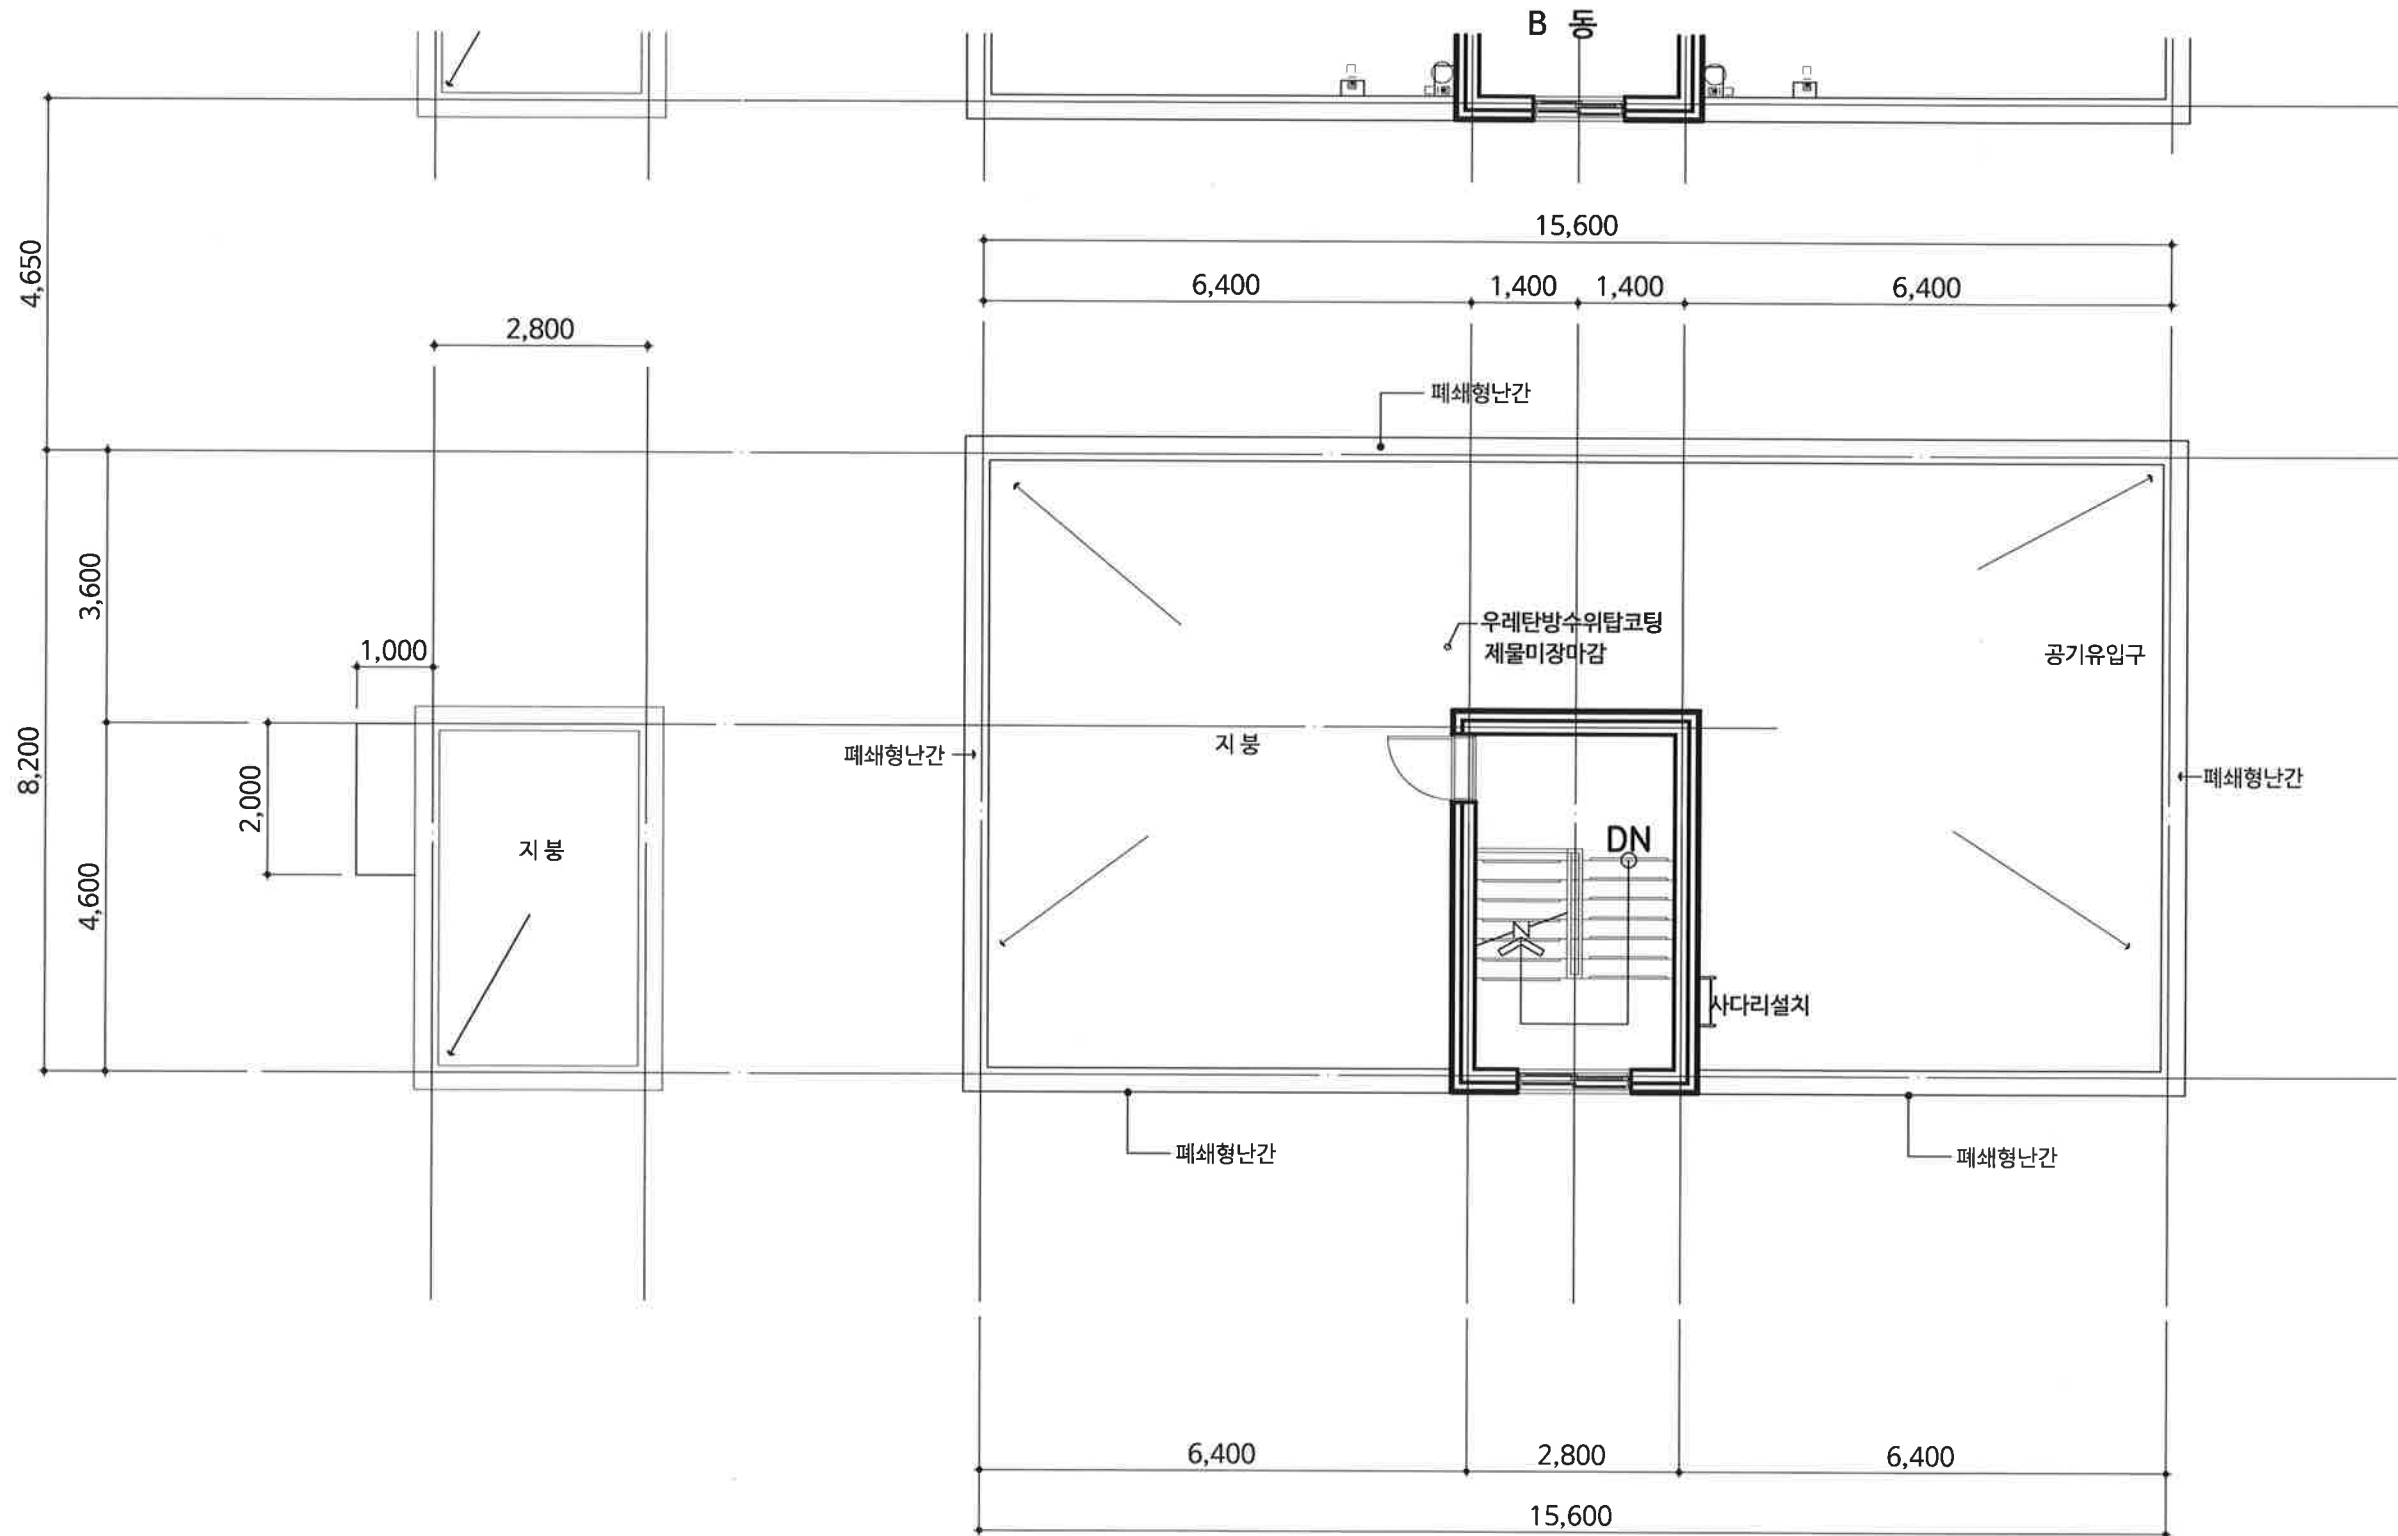

지붕 & 옥탑 평면도(A동)

축척: 1/100

Project Title.

독산동 234-22.24

단지형 다세대 주택 신축공사

Date.

No. Revision

NOTE

- ② 단독경보감지기(연기)
- ③ 단독경보감지기(열)
- ④ ABC분말소화기(3.3KG)
- ⑤ 자동확산소화기설치

--- 차면시설

☒ 보일러

☒ 에어컨 실외기

1. 콘크리트: fck = 24 MPa

2. 철근: fy = 400 MPa

3. 세대간벽두께: 200mm(복배근)

(미장 마감 포함 210)

세대내벽두께: 150mm(복배근)

4. 외벽두께: 180mm(복배근)

5. 코아벽두께: 180mm(복배근)

6. 스라브두께: 210mm(복배근)

Structure

Mechanical

Electrical

Fire Protection

에이 스페이스
건축사 사무소

서울시 송파구 방이동 151-1 부광빌딩 2층
(우편번호 04530)
TEL 02) 417-8606 FAX 02) 516-1852

Drawing Title

1 층 평면도 (B동)

Scale 1/100 A4:150

Date


Approved By 건축사 백남권

Checked By

In Charge

Drawn By

A- 17

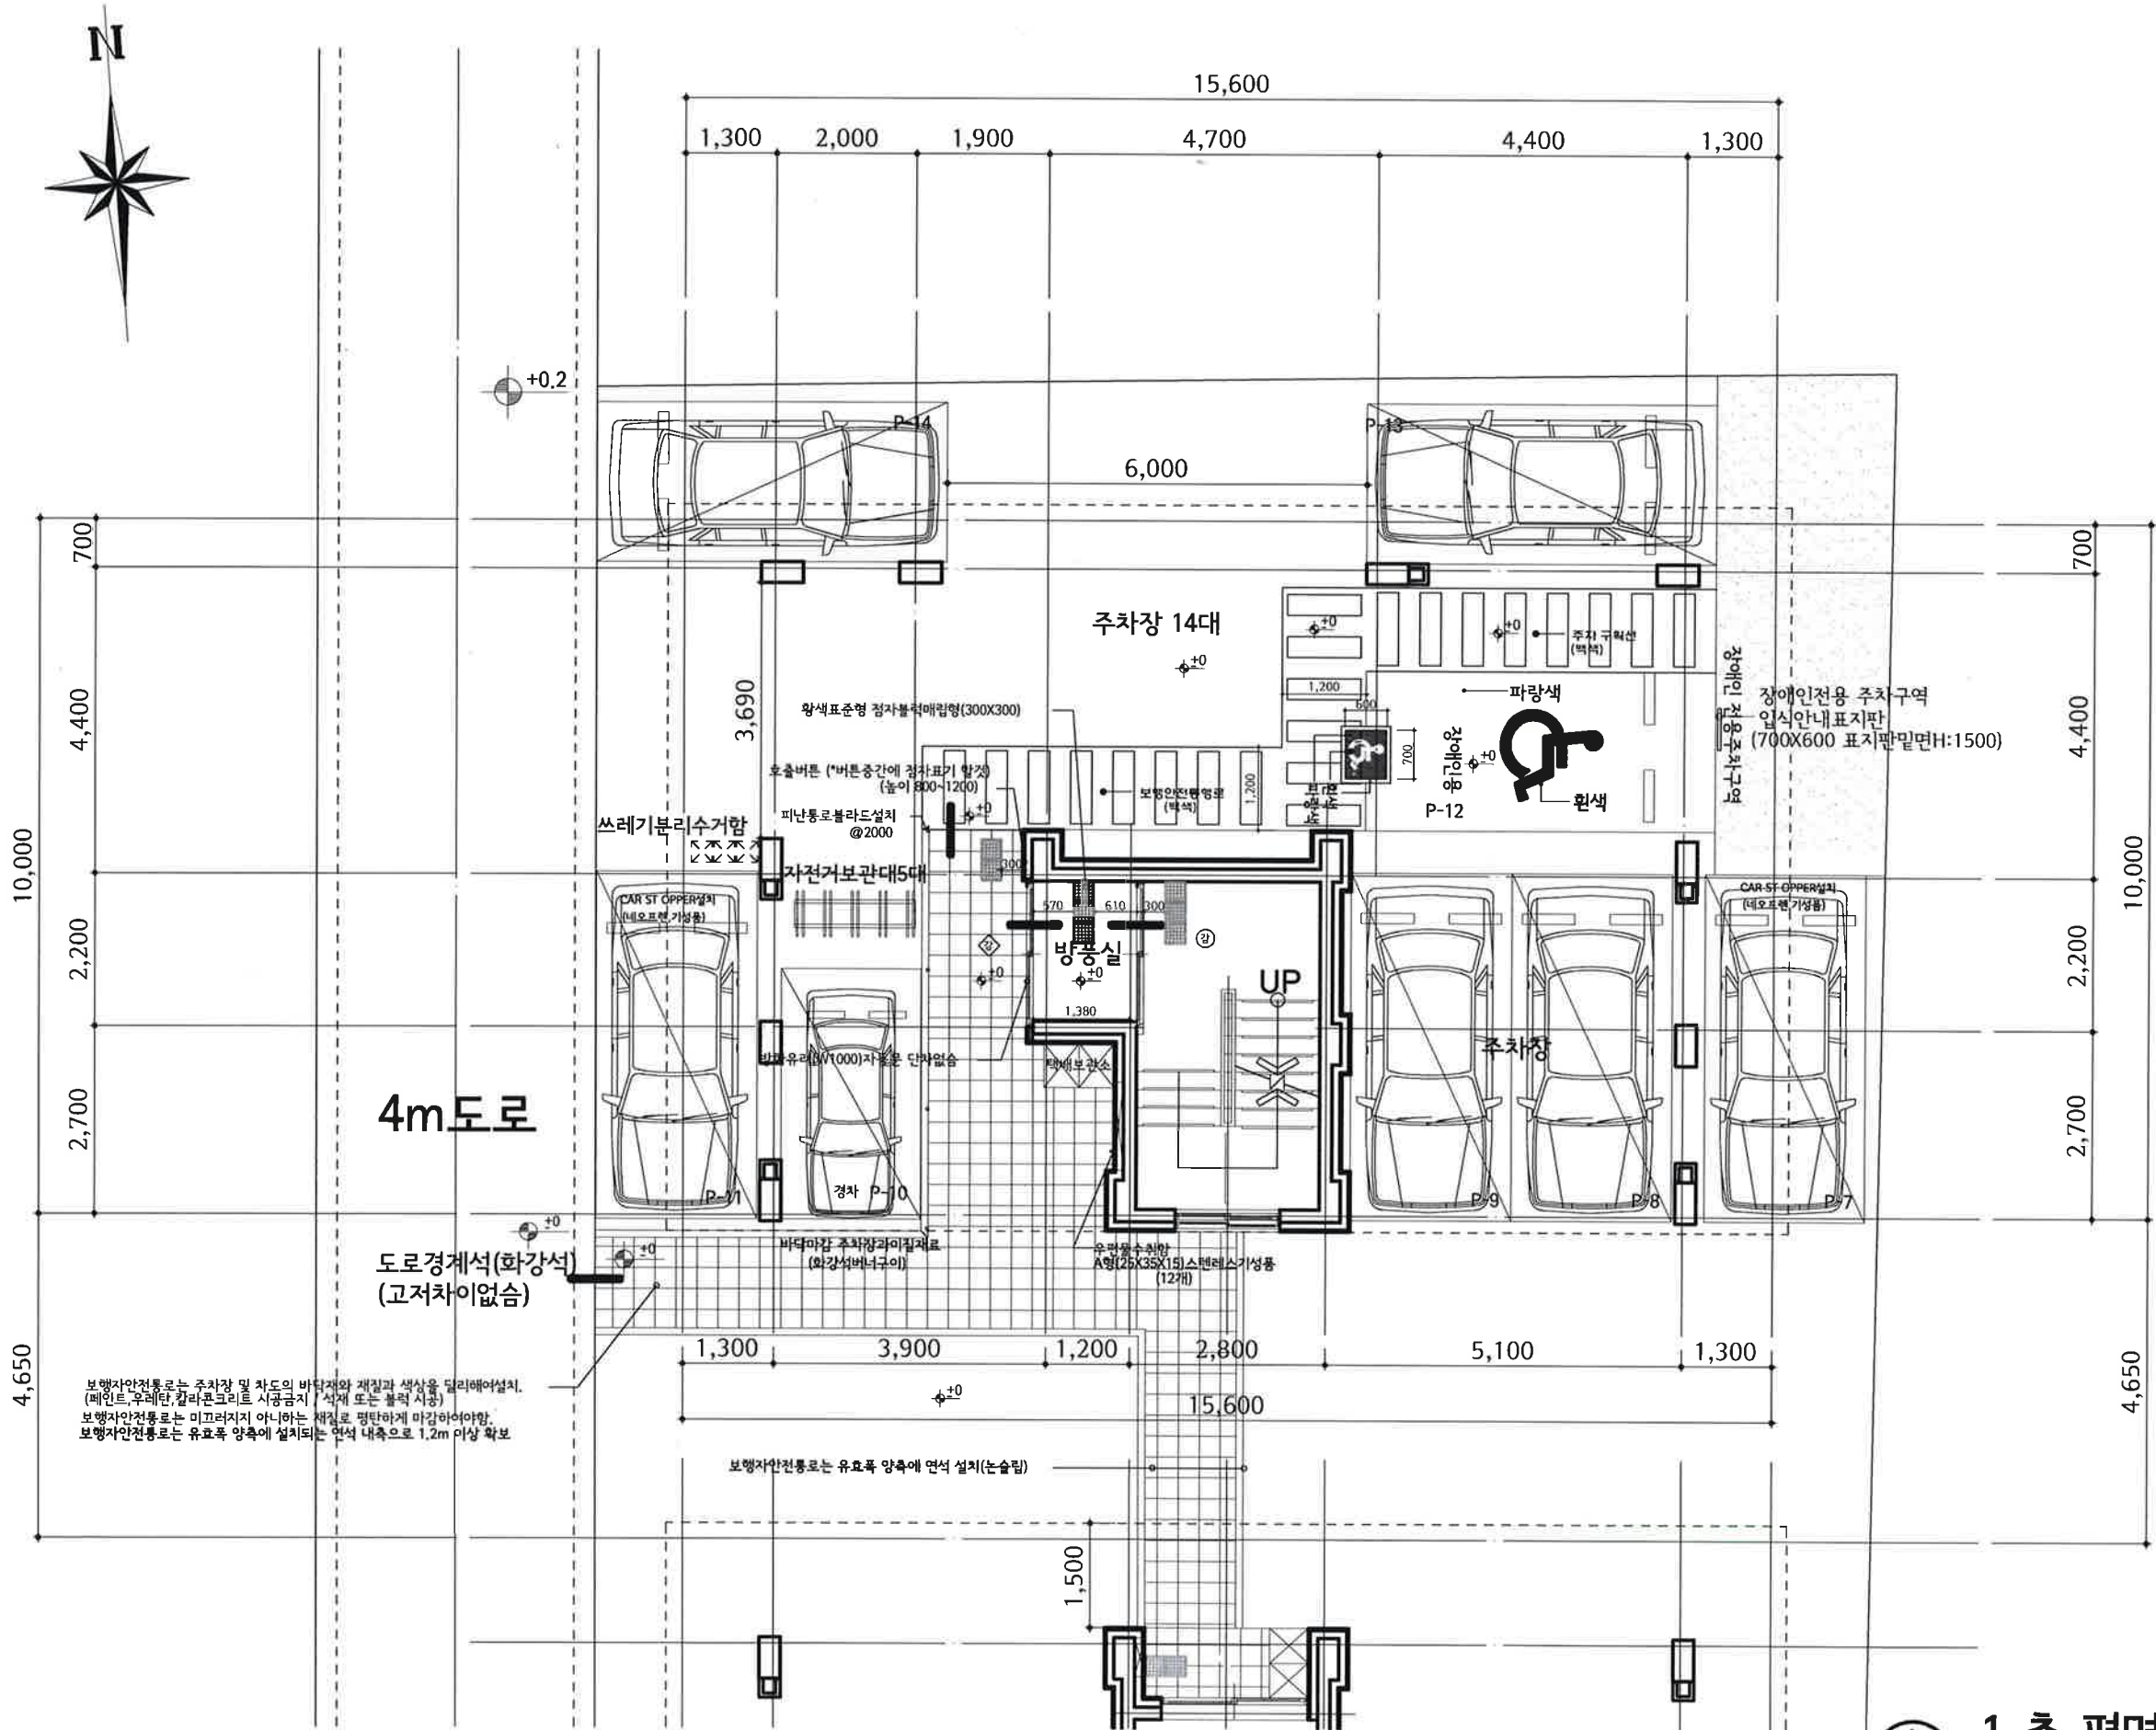

1 층 평면도 (B동)

축척: 1/100

Project Title.

독산동 234-22.24

단지형 다세대 주택 신축공사

Date.	
No.	Revision
-	-
-	-
-	-
-	-
-	-
-	-
-	-
-	-
-	-
-	-
-	-

NOTE
① 단독경보감지기(연기)
② 단독경보감지기(열)
③ ABC분말소화기(3.3KG)
④ 자동확산소화기설치

--- 차면시설

☒ 보일러

☒ 에어컨 실외기

* 구조 *

1. 콘크리트: fck = 24 MPa

2. 철근: fy = 400 MPa

3. 세대간벽두께: 200mm (복배근)

(미장 마감 포함 210)

세대내벽두께: 150mm (복배근)

4. 외벽두께: 180mm (복배근)

5. 코아벽두께: 180mm (복배근)

6. 스라브두께: 210mm (복배근)

Structure

Mechanical

Electrical

Fire Protection

SPACE
에이 스페이스
건축사 사무소

서울시 송파구 방이동 151-1 부경빌딩 2층
(여제고로 45가길30)
TEL 02) 417-8606 FAX 02) 516-1852

Drawing Title

2~3 층 평면도 (B동)

Scale 1/100 A4:150


Date

Approved By 건축사 백남권

Checked By

In Charge

Drawn By A- 18

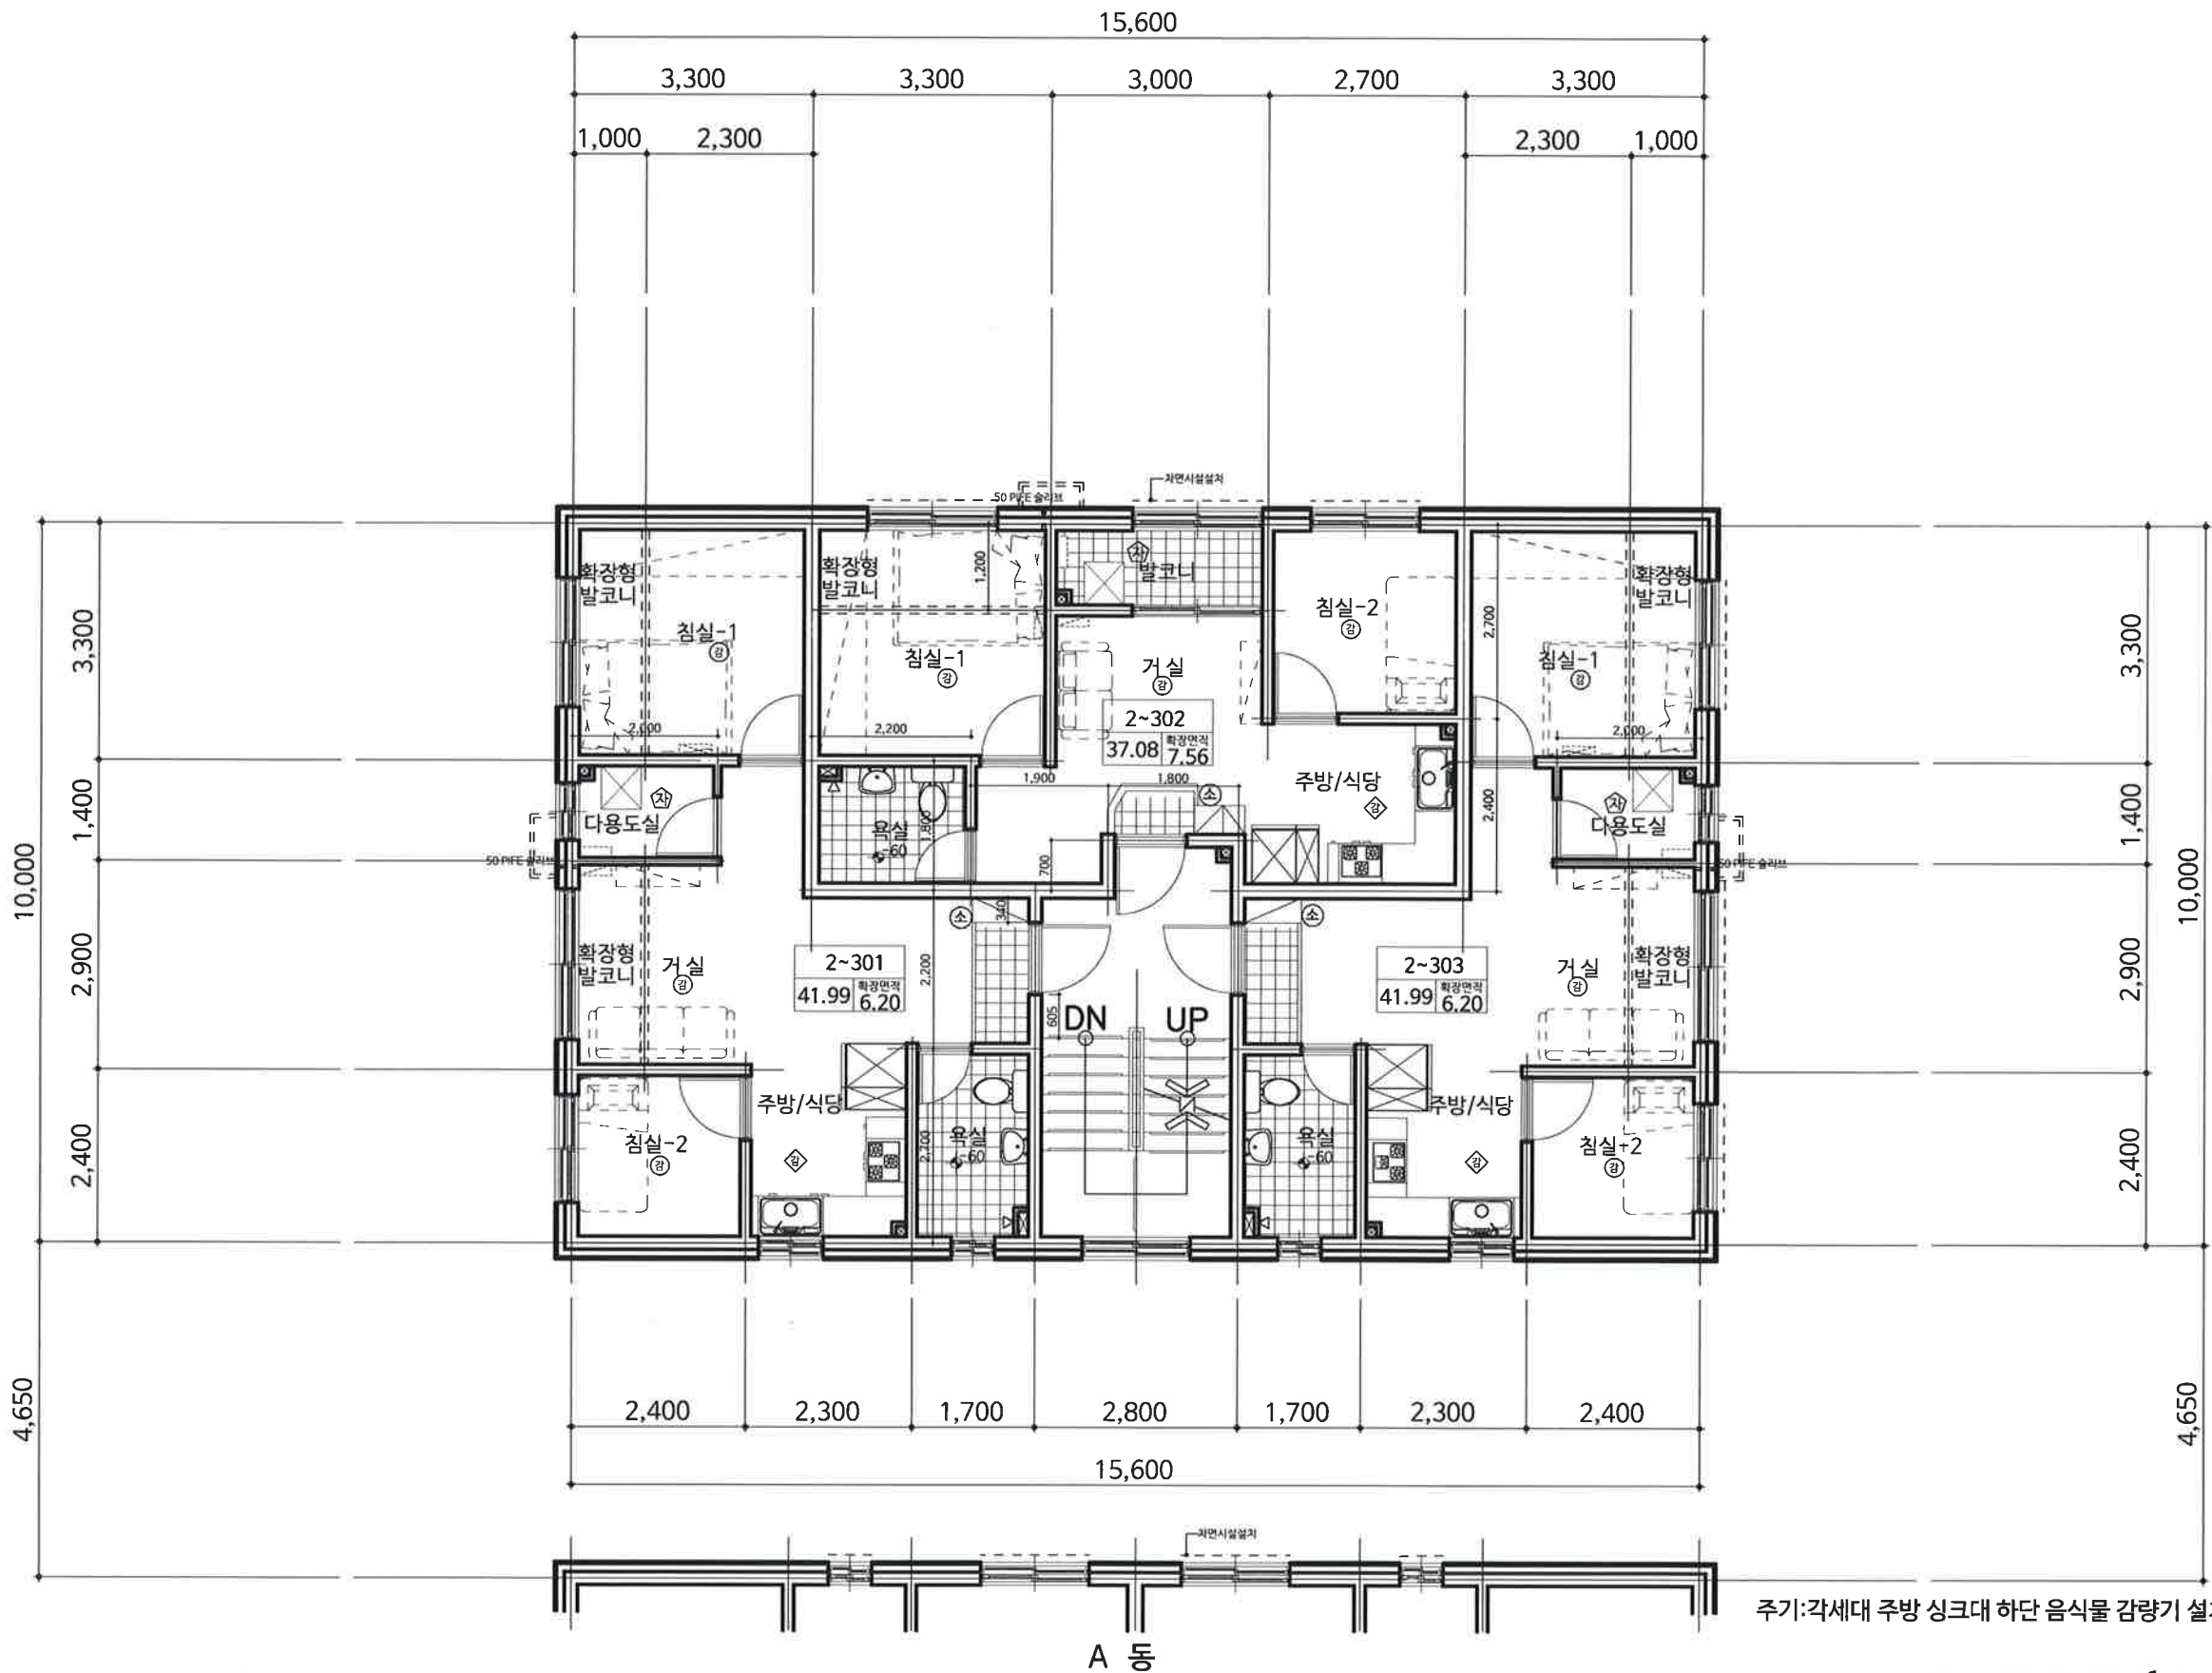


추가: 각세대 주방 싱크대 하단 음식물 감량기 설치할것



2~3 층 평면도 (B동)

축척: 1/100

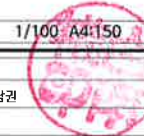

Project Title.

독산동 234-22.24

단지형 다세대 주택 신축공사

Date.

No. Revision

NOTE

- ② 단독경보감지기 (연기)
- ③ 단독경보감지기 (열)
- ④ ABC분말소화기 (3.3KG)
- ⑤ 자동확산소화기설치

- - - 차면시설

☒ 보일러

☒ 에어컨 실외기

* 구조 *

1. 콘크리트: fck = 24 MPa

2. 철근: fy = 400 MPa

3. 세대간벽두께: 200mm (복배근)
(미장마감포함 210)

세대내벽두께: 150mm (복배근)

4. 외벽두께: 180mm (복배근)

5. 코아벽두께: 180mm (복배근)

6. 스라브두께: 210mm (복배근)

Structure

Mechanical

Electrical

Fire Protection



에이 스페이스
건축사 사무소

서울시 송파구 방이동 151-1 부평빌딩 2층

(등록번호 487430)

TEL 02) 417-8606 FAX 02) 516-1852

Drawing Title

5 층 평면도 (B동)

Scale 1/100 A4:150

Date


Approved By 건축사 박남권

Checked By


In Charge

Drawn By

A- 20

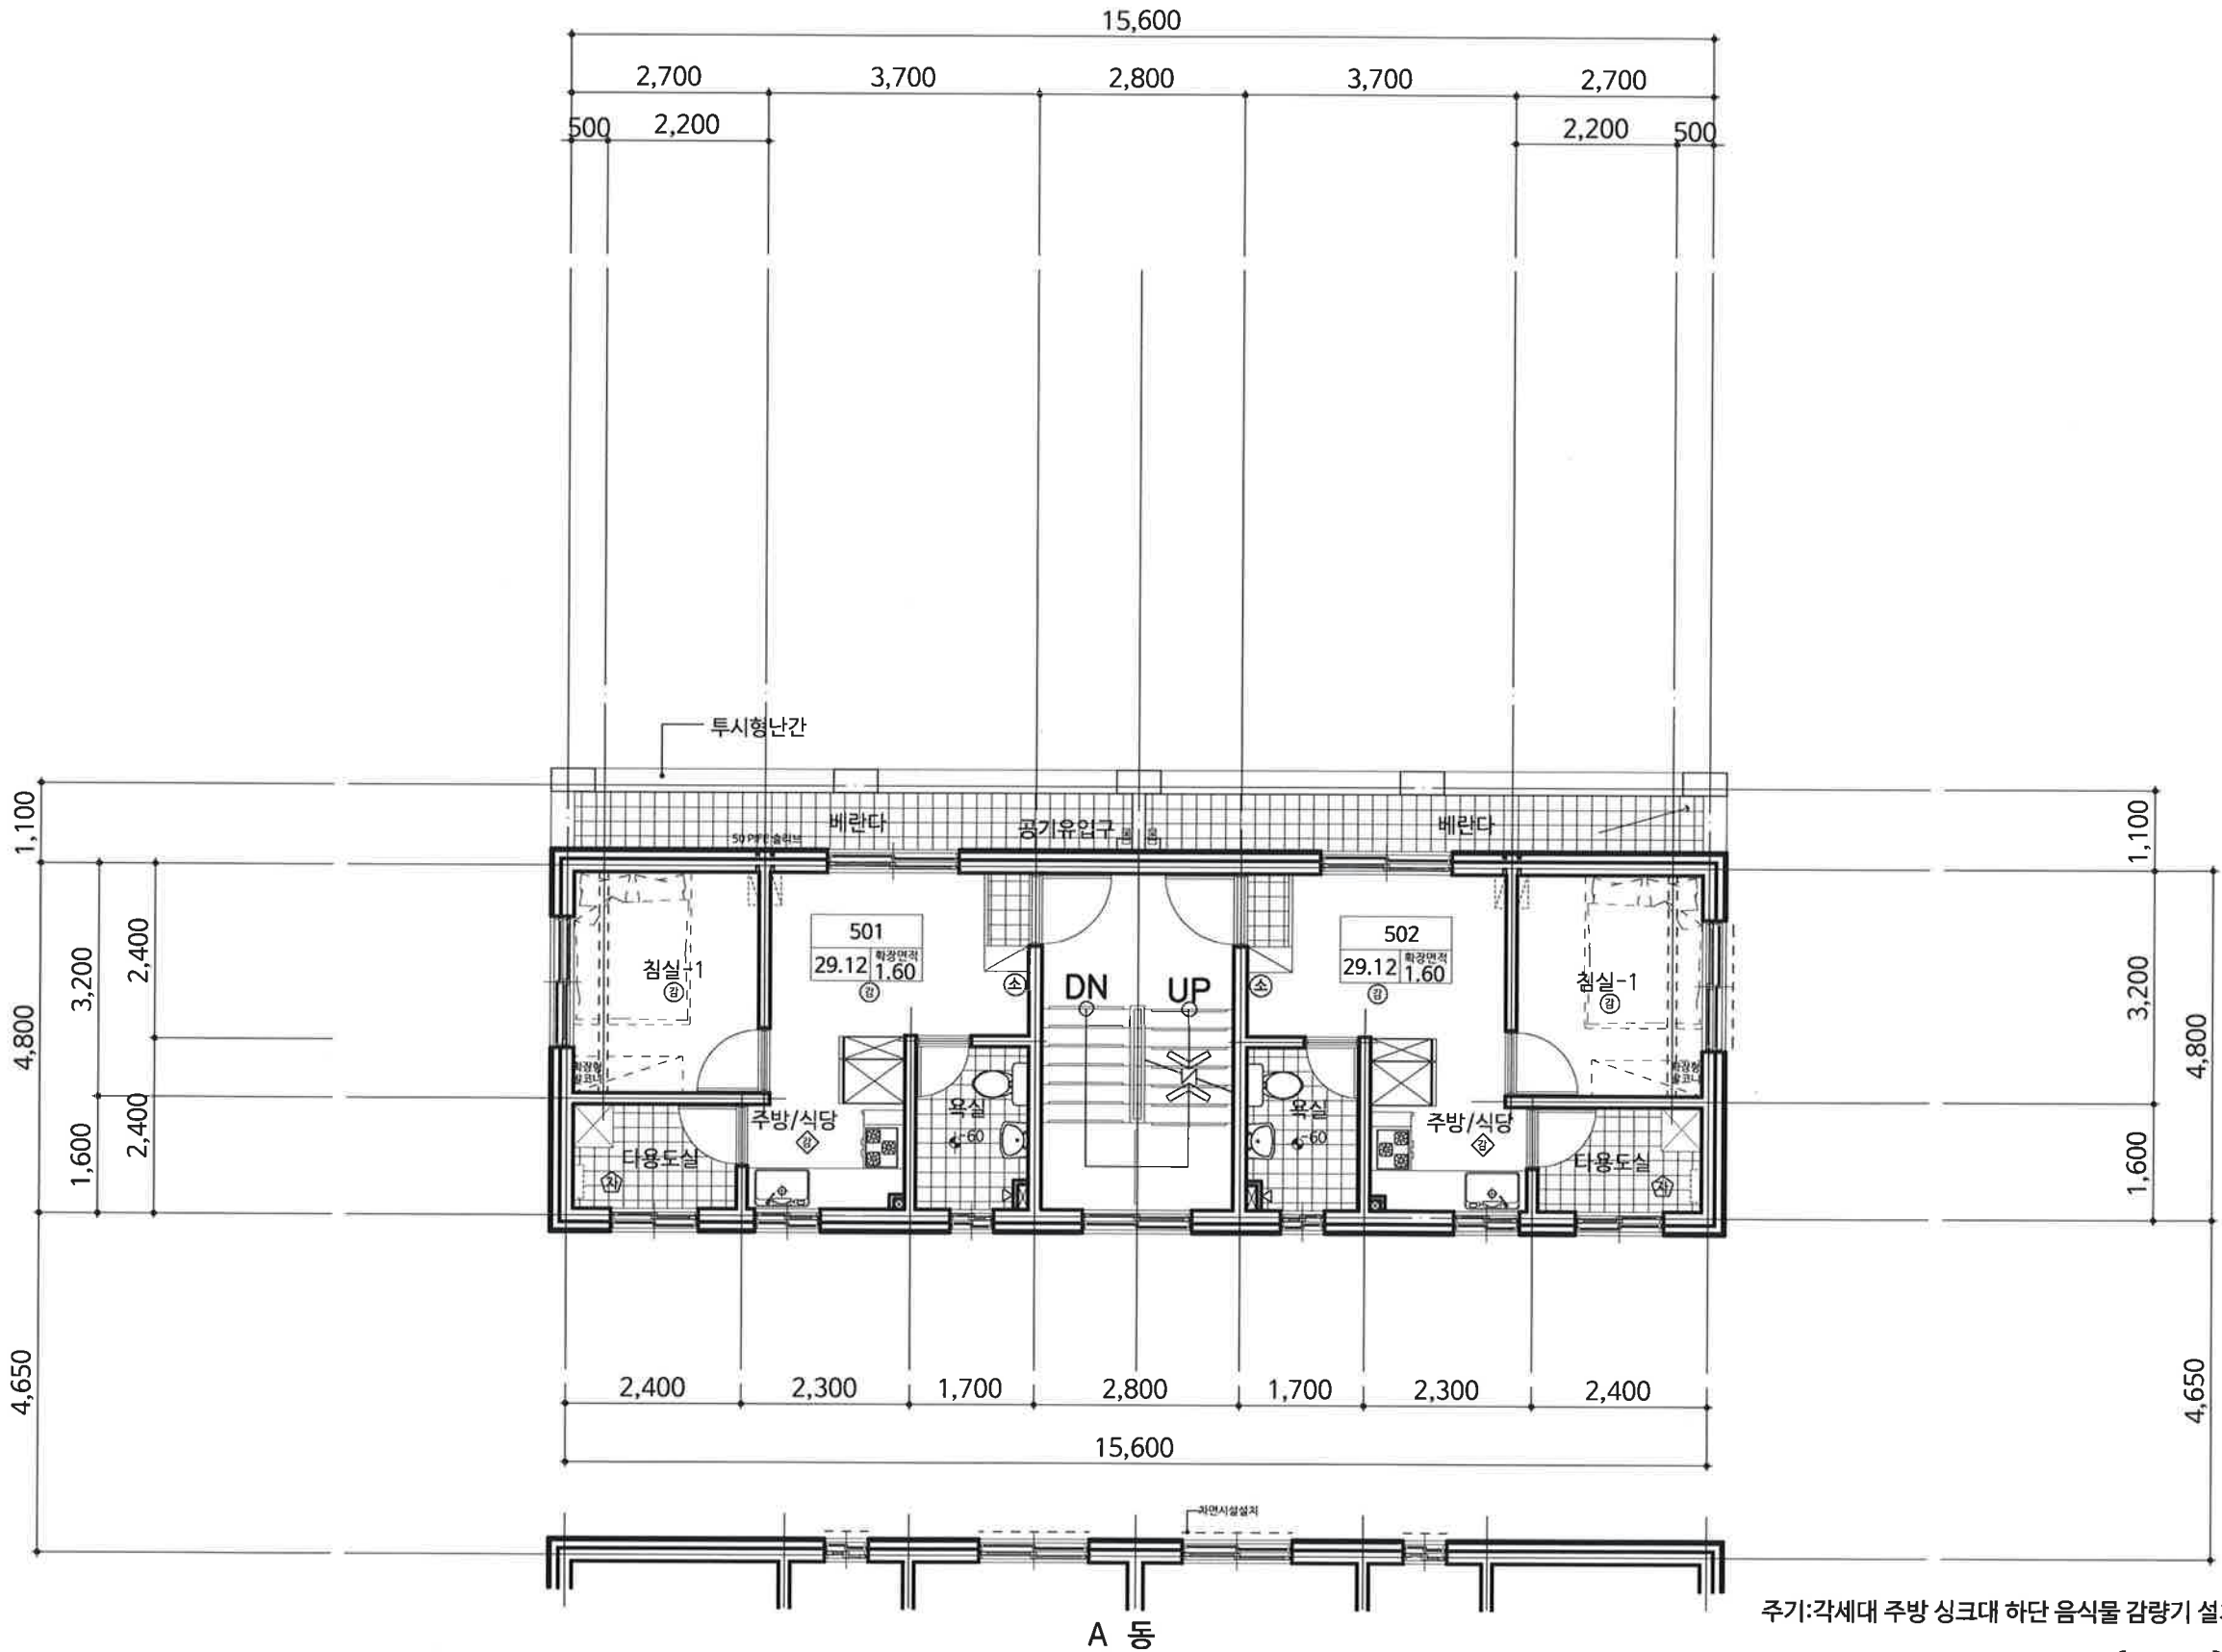

주거: 각세대 주방 싱크대 하단 음식물 감량기 설치할것

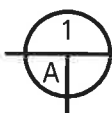

5 층 평면도 (B동)

축척: 1/100


Project Title.

독산동 234-22.24

단지형 다세대 주택 신축공사

Date.	
No.	Revision

NOTE

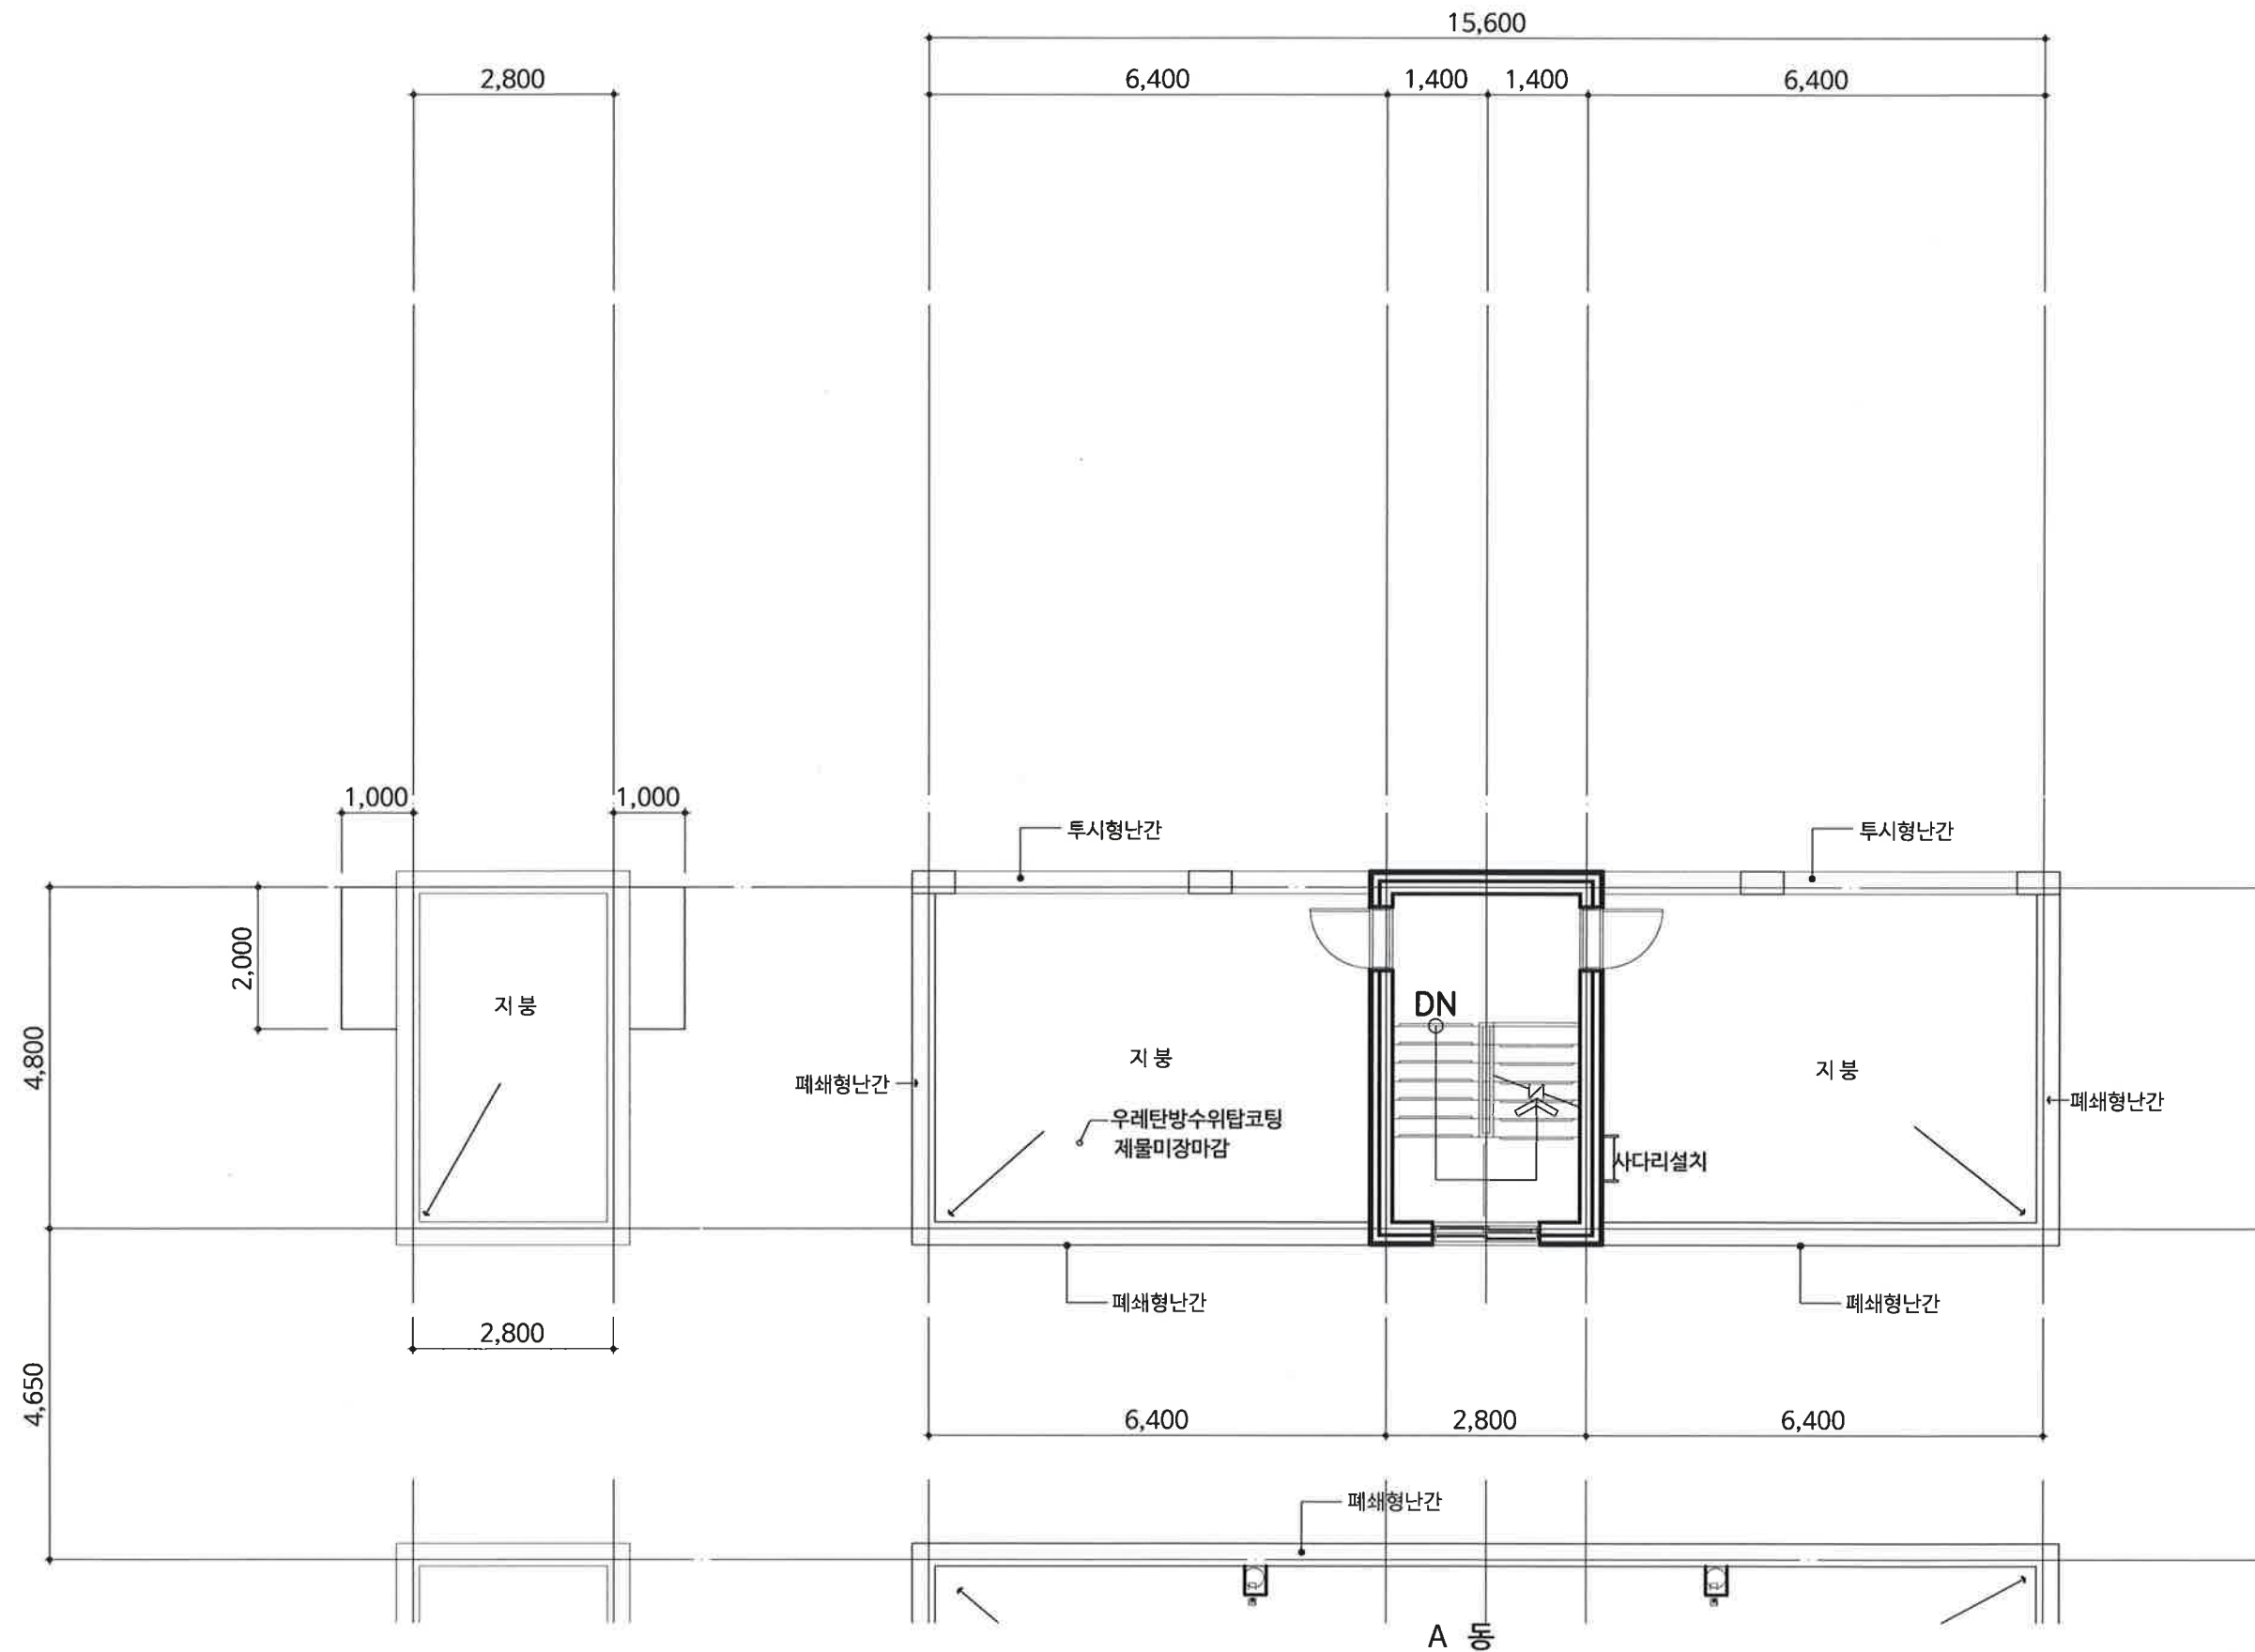

Structure

Mechanical

Electrical

Fire Protection

에이 스페이스
건축사 사무소

서울시 송파구 방아동 151-1 부광빌딩 2층
(북계고분로 48가길30)
TEL 02) 417-8606 FAX 02) 516-1852

Drawing Title

지붕 & 옥탑 평면도 (B동)

Scale 1/100 A4:150

Date
Approved By 건축사 백남권
Checked By
In Charge
Drawn By A- 21

지붕 & 옥탑 평면도(B동)
축척 : 1/100

독산동 234-22.24
단지형 다세대 주택 신축공사

[illegible]

Structure

Mechanical

Electrical

Fire Protection



서울시 송파구 방이동 151-1 부광빌딩 2층
(백제고분로 48가길30)
TEL 02) 417-8606 FAX 02) 516-1852

Drawing Title

정 면 도(A동)
좌 측 면 도(A동)


Scale 1/100 A4:150

Date 2017. . .

Approved by 건축사 백남권

In Charge _____

Drawn By A- 22

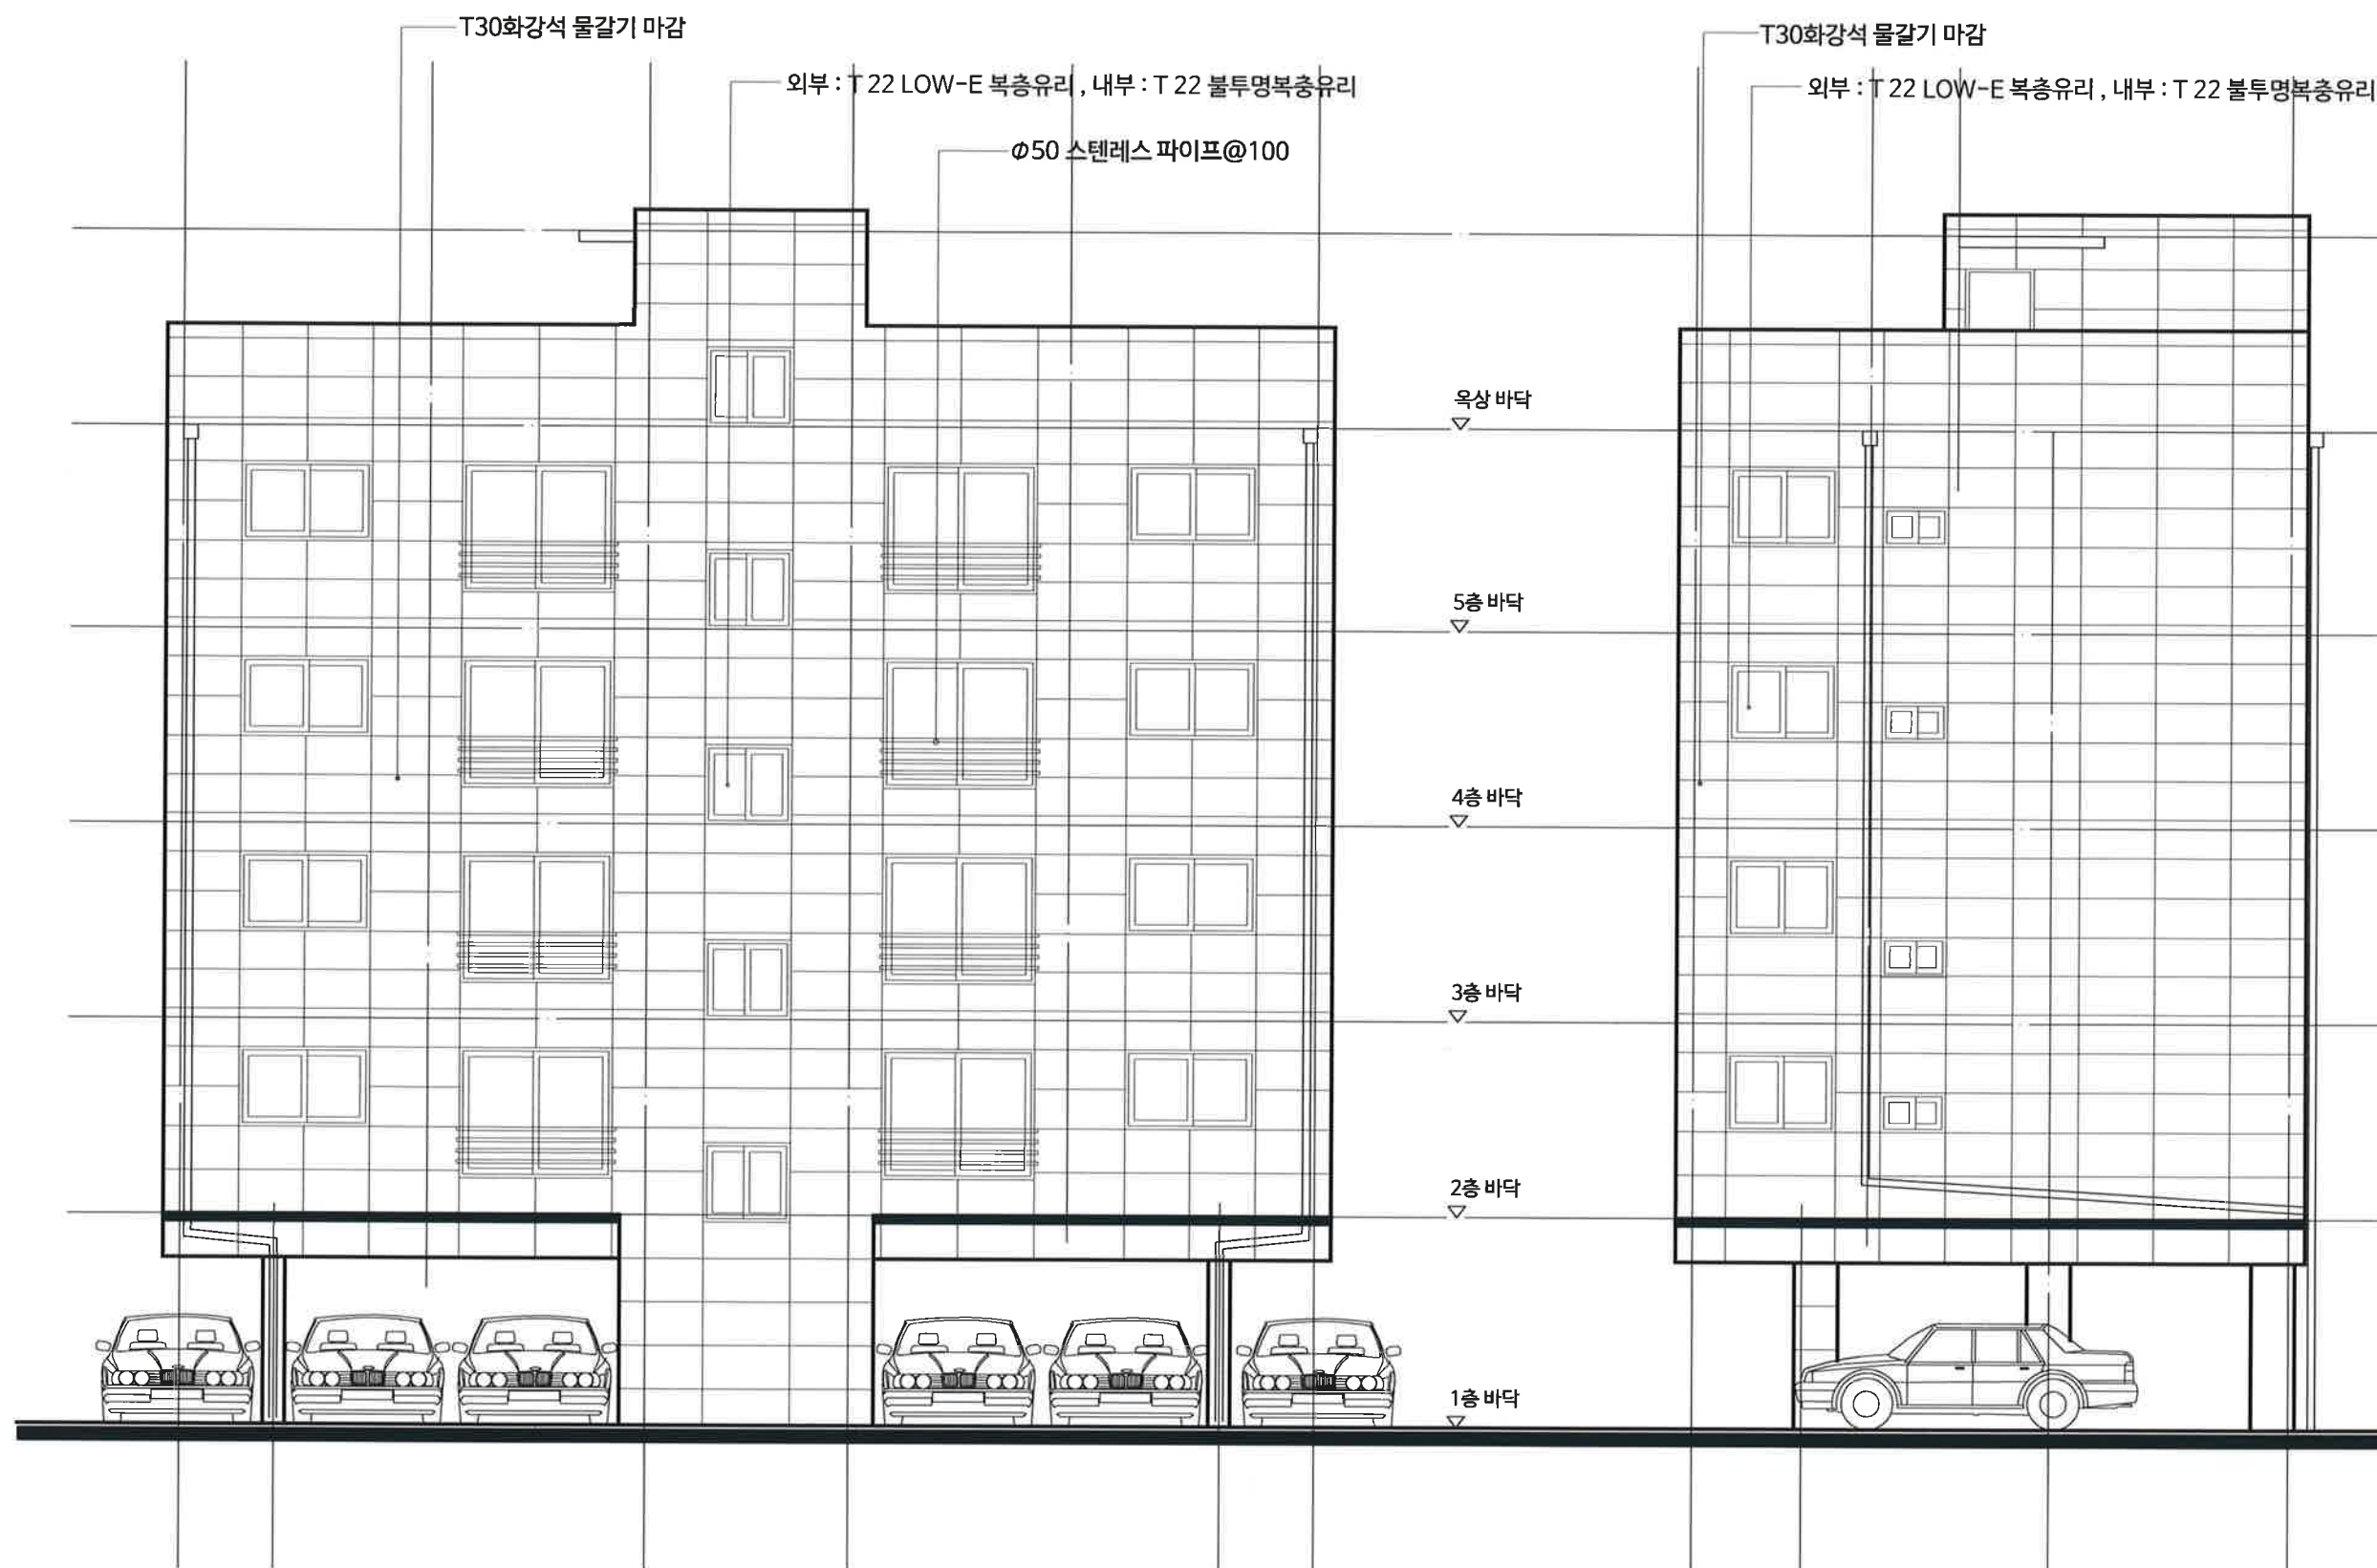

Drawn By A- 22

Project Title.

독산동 234-22.24
단지형 다세대 주택 신축공사

Date.	No.	Revision

NOTE

Structure
Mechanical
Electrical
Fire Protection

에이 스페이스
건축사 사무소


서울시 송파구 방이동 151-1 부경빌딩 2층
(역삼로 48가길30)
TEL 02) 417-8606 FAX 02) 516-1852

Drawing Title

우 측 면 도(A동)
배 면 도(A동)

Scale 1/100 A4:150

Date 2017 . . .
Approved By 건축사 백남권
Checked By
In Charge
Drawn By A- 23

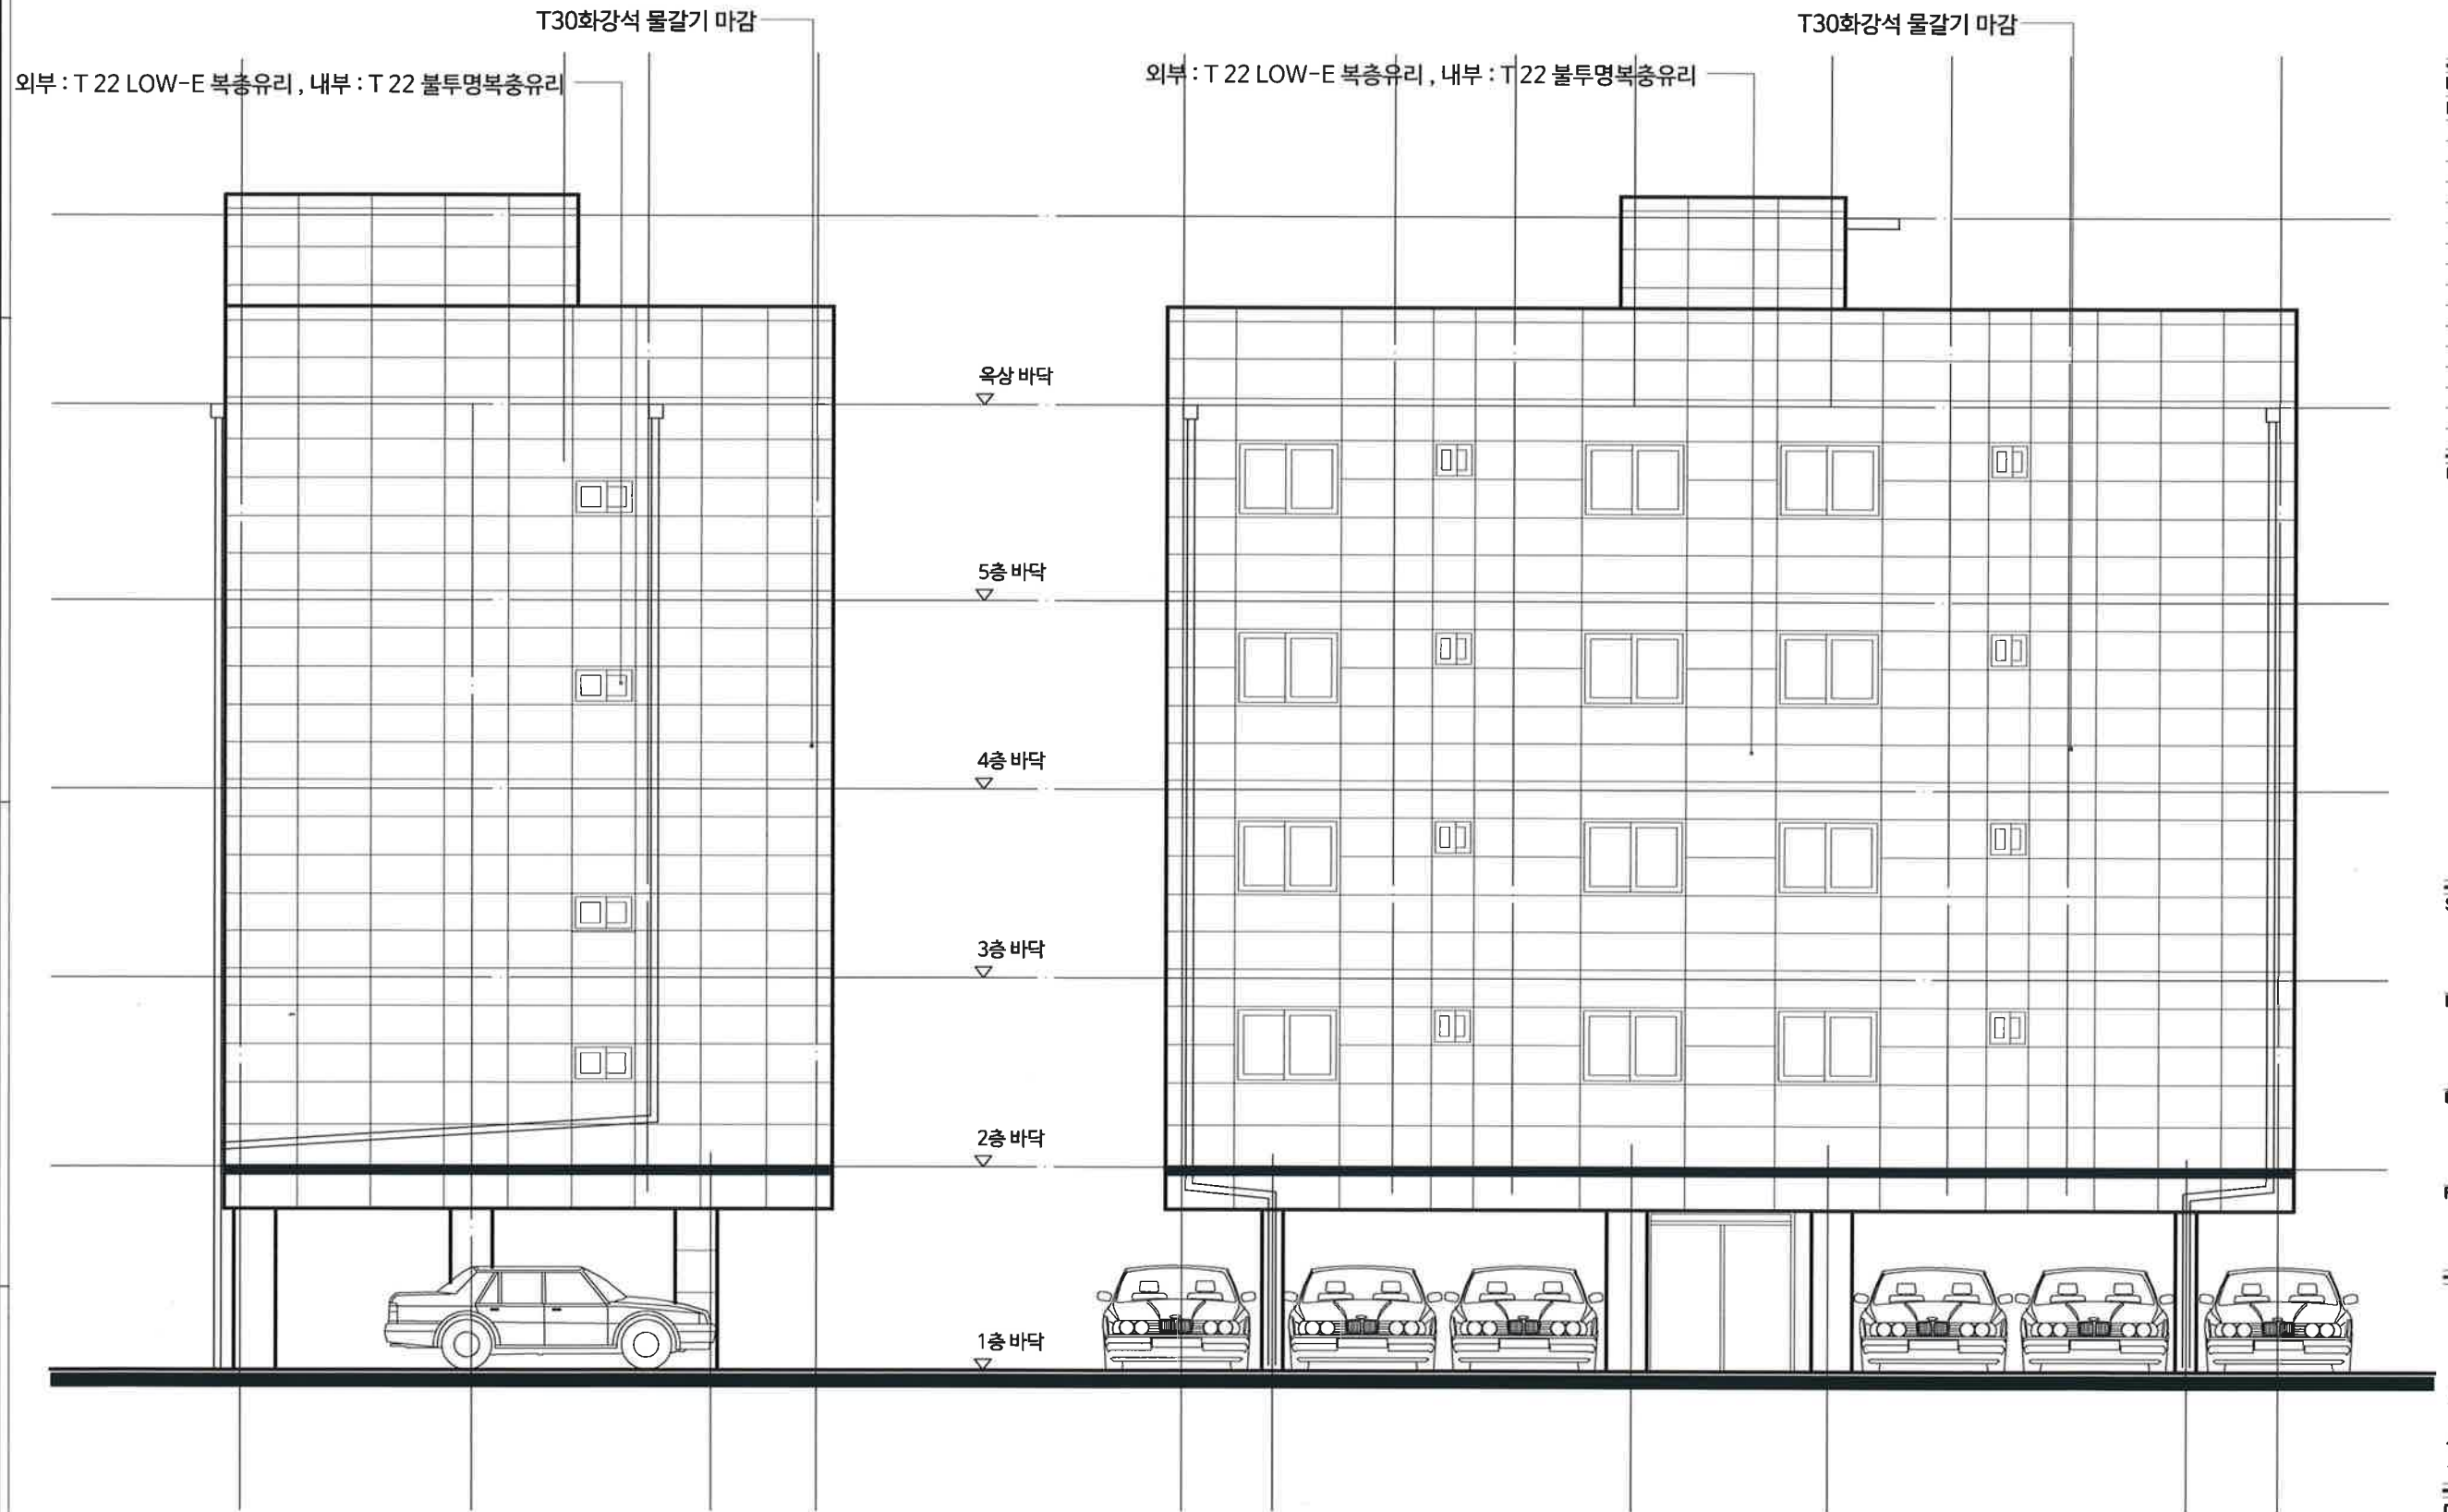

1
A
우 측 면 도 (A동)
축척: 1/100

1
A
배 면 도 (A동)
축척: 1/100

독산동 234-22.24
단지형 다세대 주택 신축공사

[illegible]

Fire Protection


에이 스페이스
건축사 사무소

서울시 송파구 방아동 151-1 부경빌딩 2층
(백제고분로 48가길30)
TEL 02) 417-8606 FAX 02) 516-1852

정 면 도 (B동)
좌 측 면 도 (B동)

Drawn By

A- 24

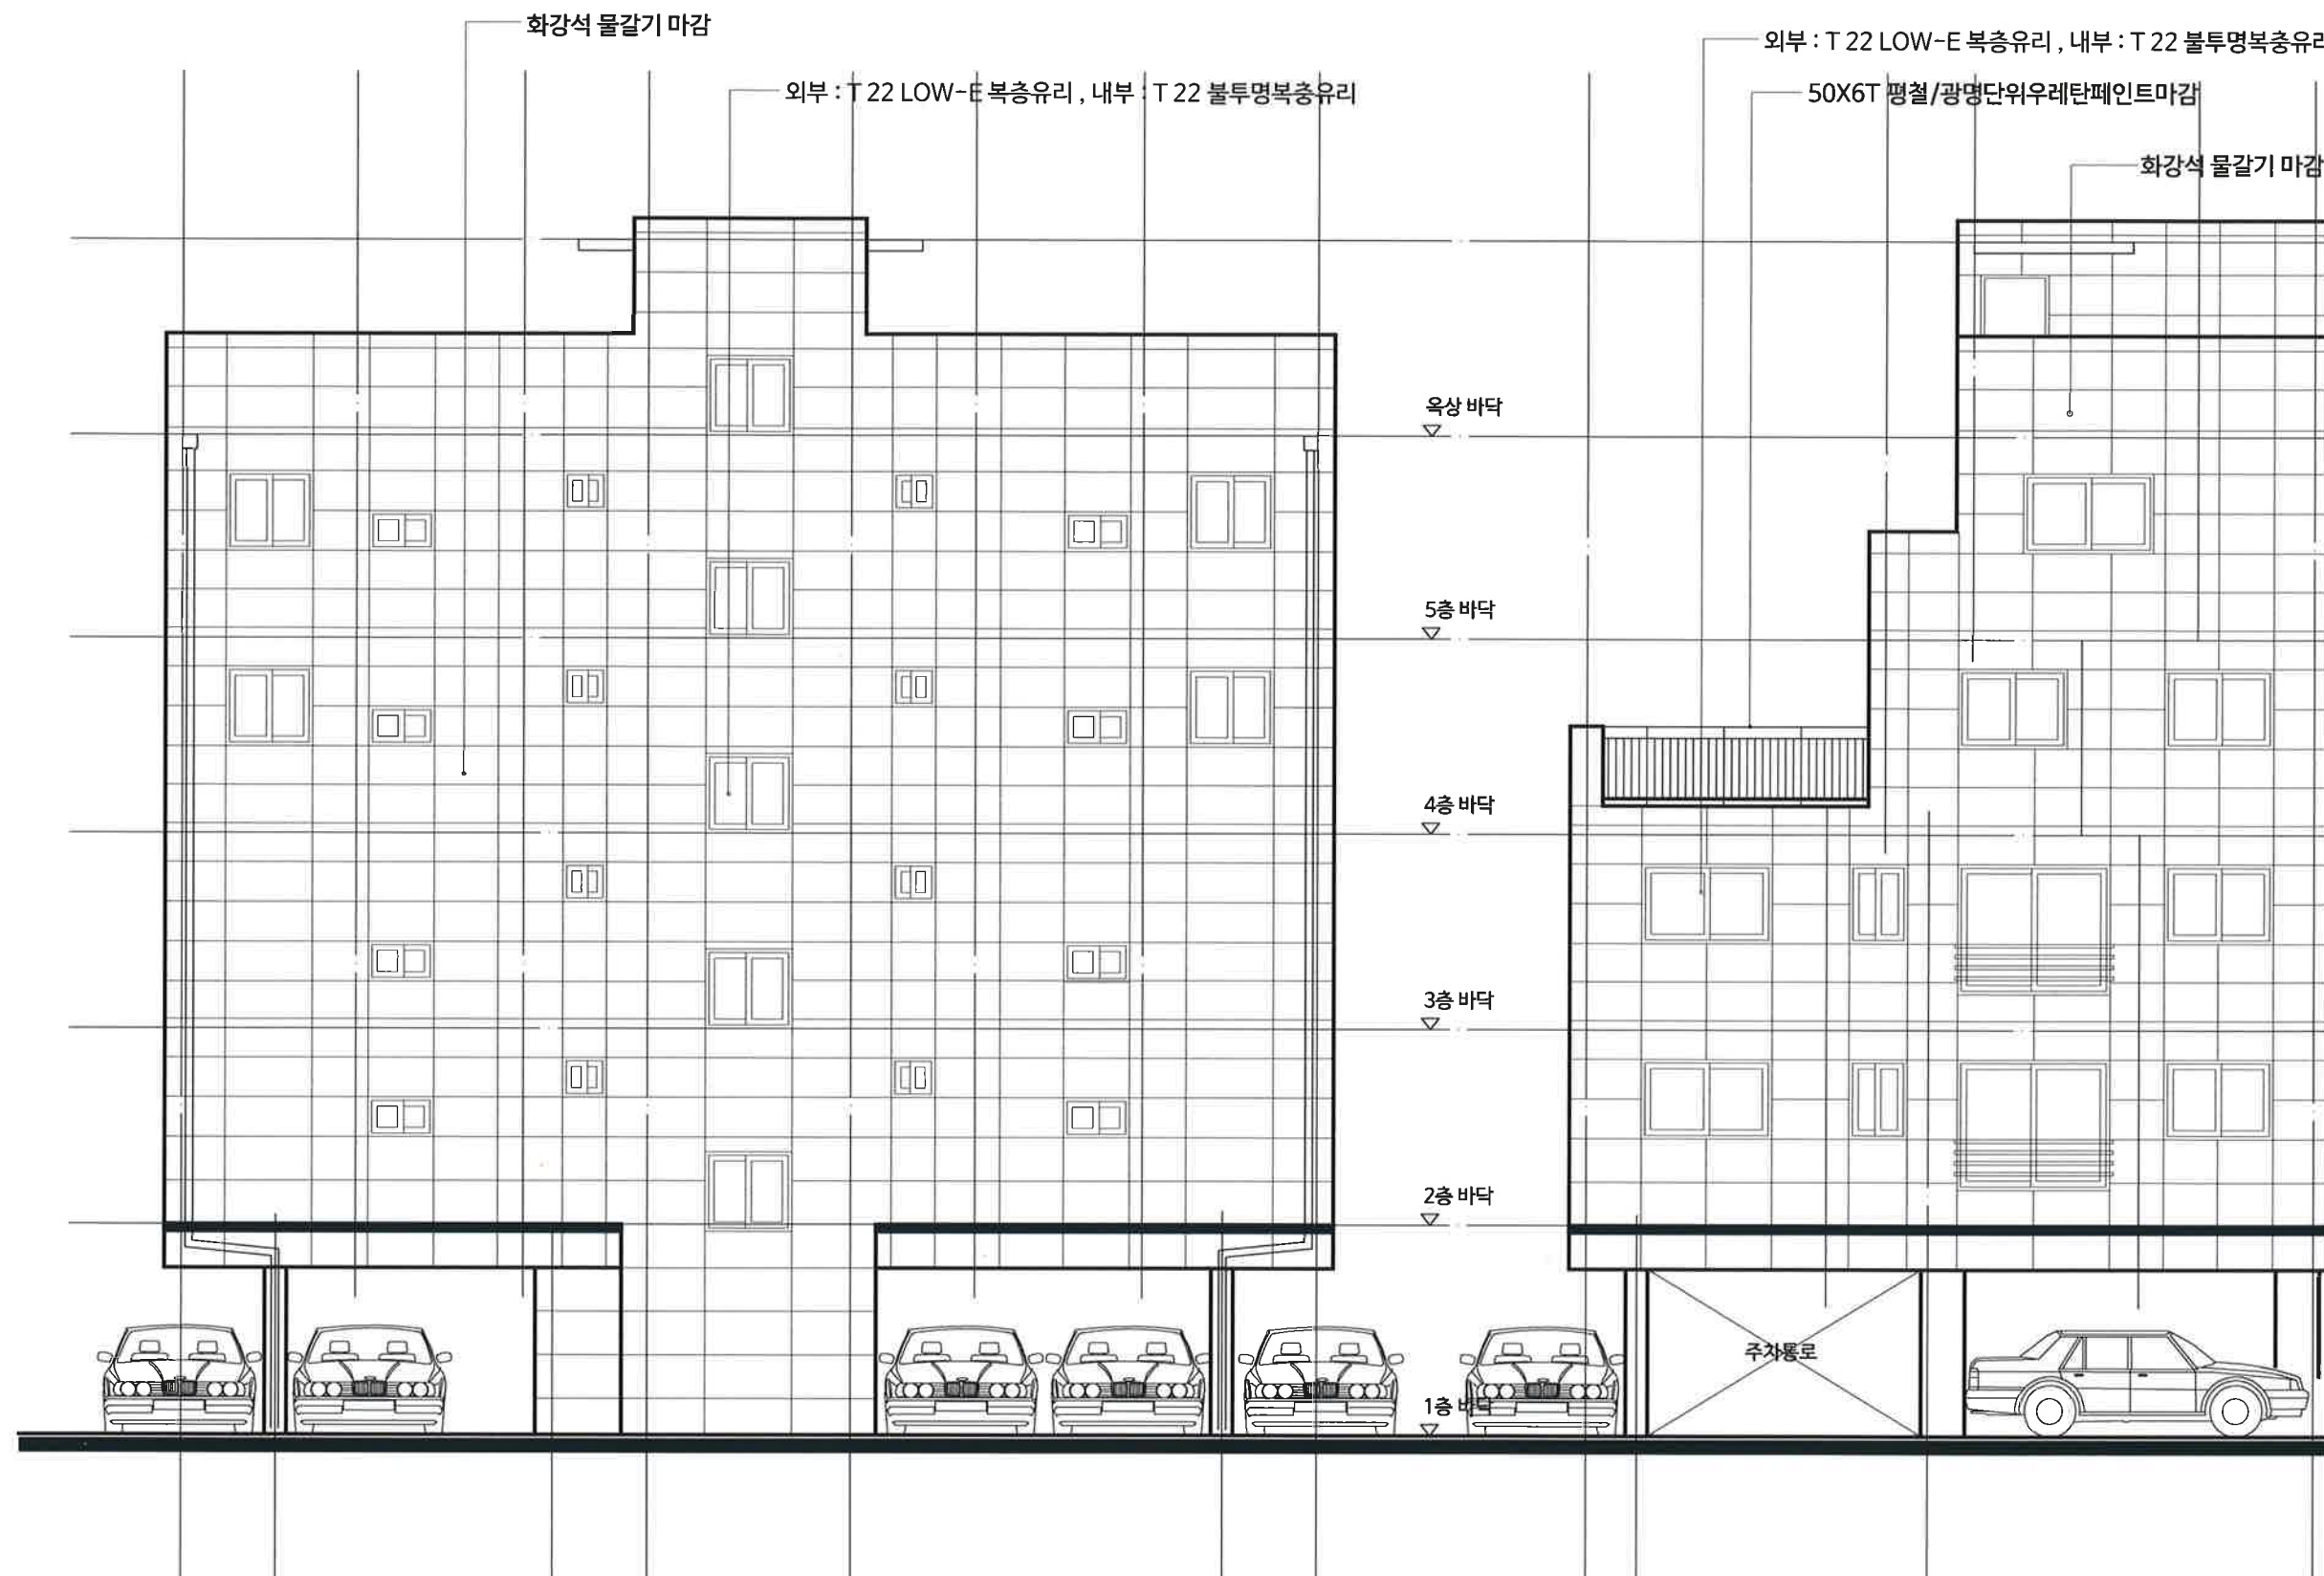

정 면 도 (B동)

축척: 1/100


좌 측 면 도 (B동)
 축척: 1/100

Project Title.

독산동 234-22.24
단지형 다세대 주택 신축공사

Date.	
No.	Revision
-	-
-	-
-	-
-	-
-	-
-	-
-	-
-	-
-	-
-	-

NOTE

Structure	
Mechanical	
Electrical	
Fire Protection	

SPACE
에이 스페이스
건축사 사무소

서울시 송파구 방이동 151-1 부곡빌딩 2층
(백제고분로 48가길30)
TEL 02) 417-8606 FAX 02) 516-1852

Drawing Title

우 측 면 도 (B동)
배 면 도 (B동)

Scale 1/100 A4:150

Date 2017.
Approved By 건축사 백남권
Checked By
In Charge
Drawn By A-25

외부 : T 22 LOW-E 복층유리, 내부 : T 22 불투명복층유리

50X6T 평철/광명단위우레탄페인트마감

T30화강석 물갈기 마감

50X6T 평철/광명단위우레탄페인트마감

외부 : T 22 LOW-E 복층유리, 내부 : T 22 불투명복층유리

T30화강석 물갈기 마감

옥상 바닥

5층 바닥

4층 바닥

3층 바닥

2층 바닥

주차통로

바닥

1
A
우 측 면 도 (B동)
축척 : 1/100