



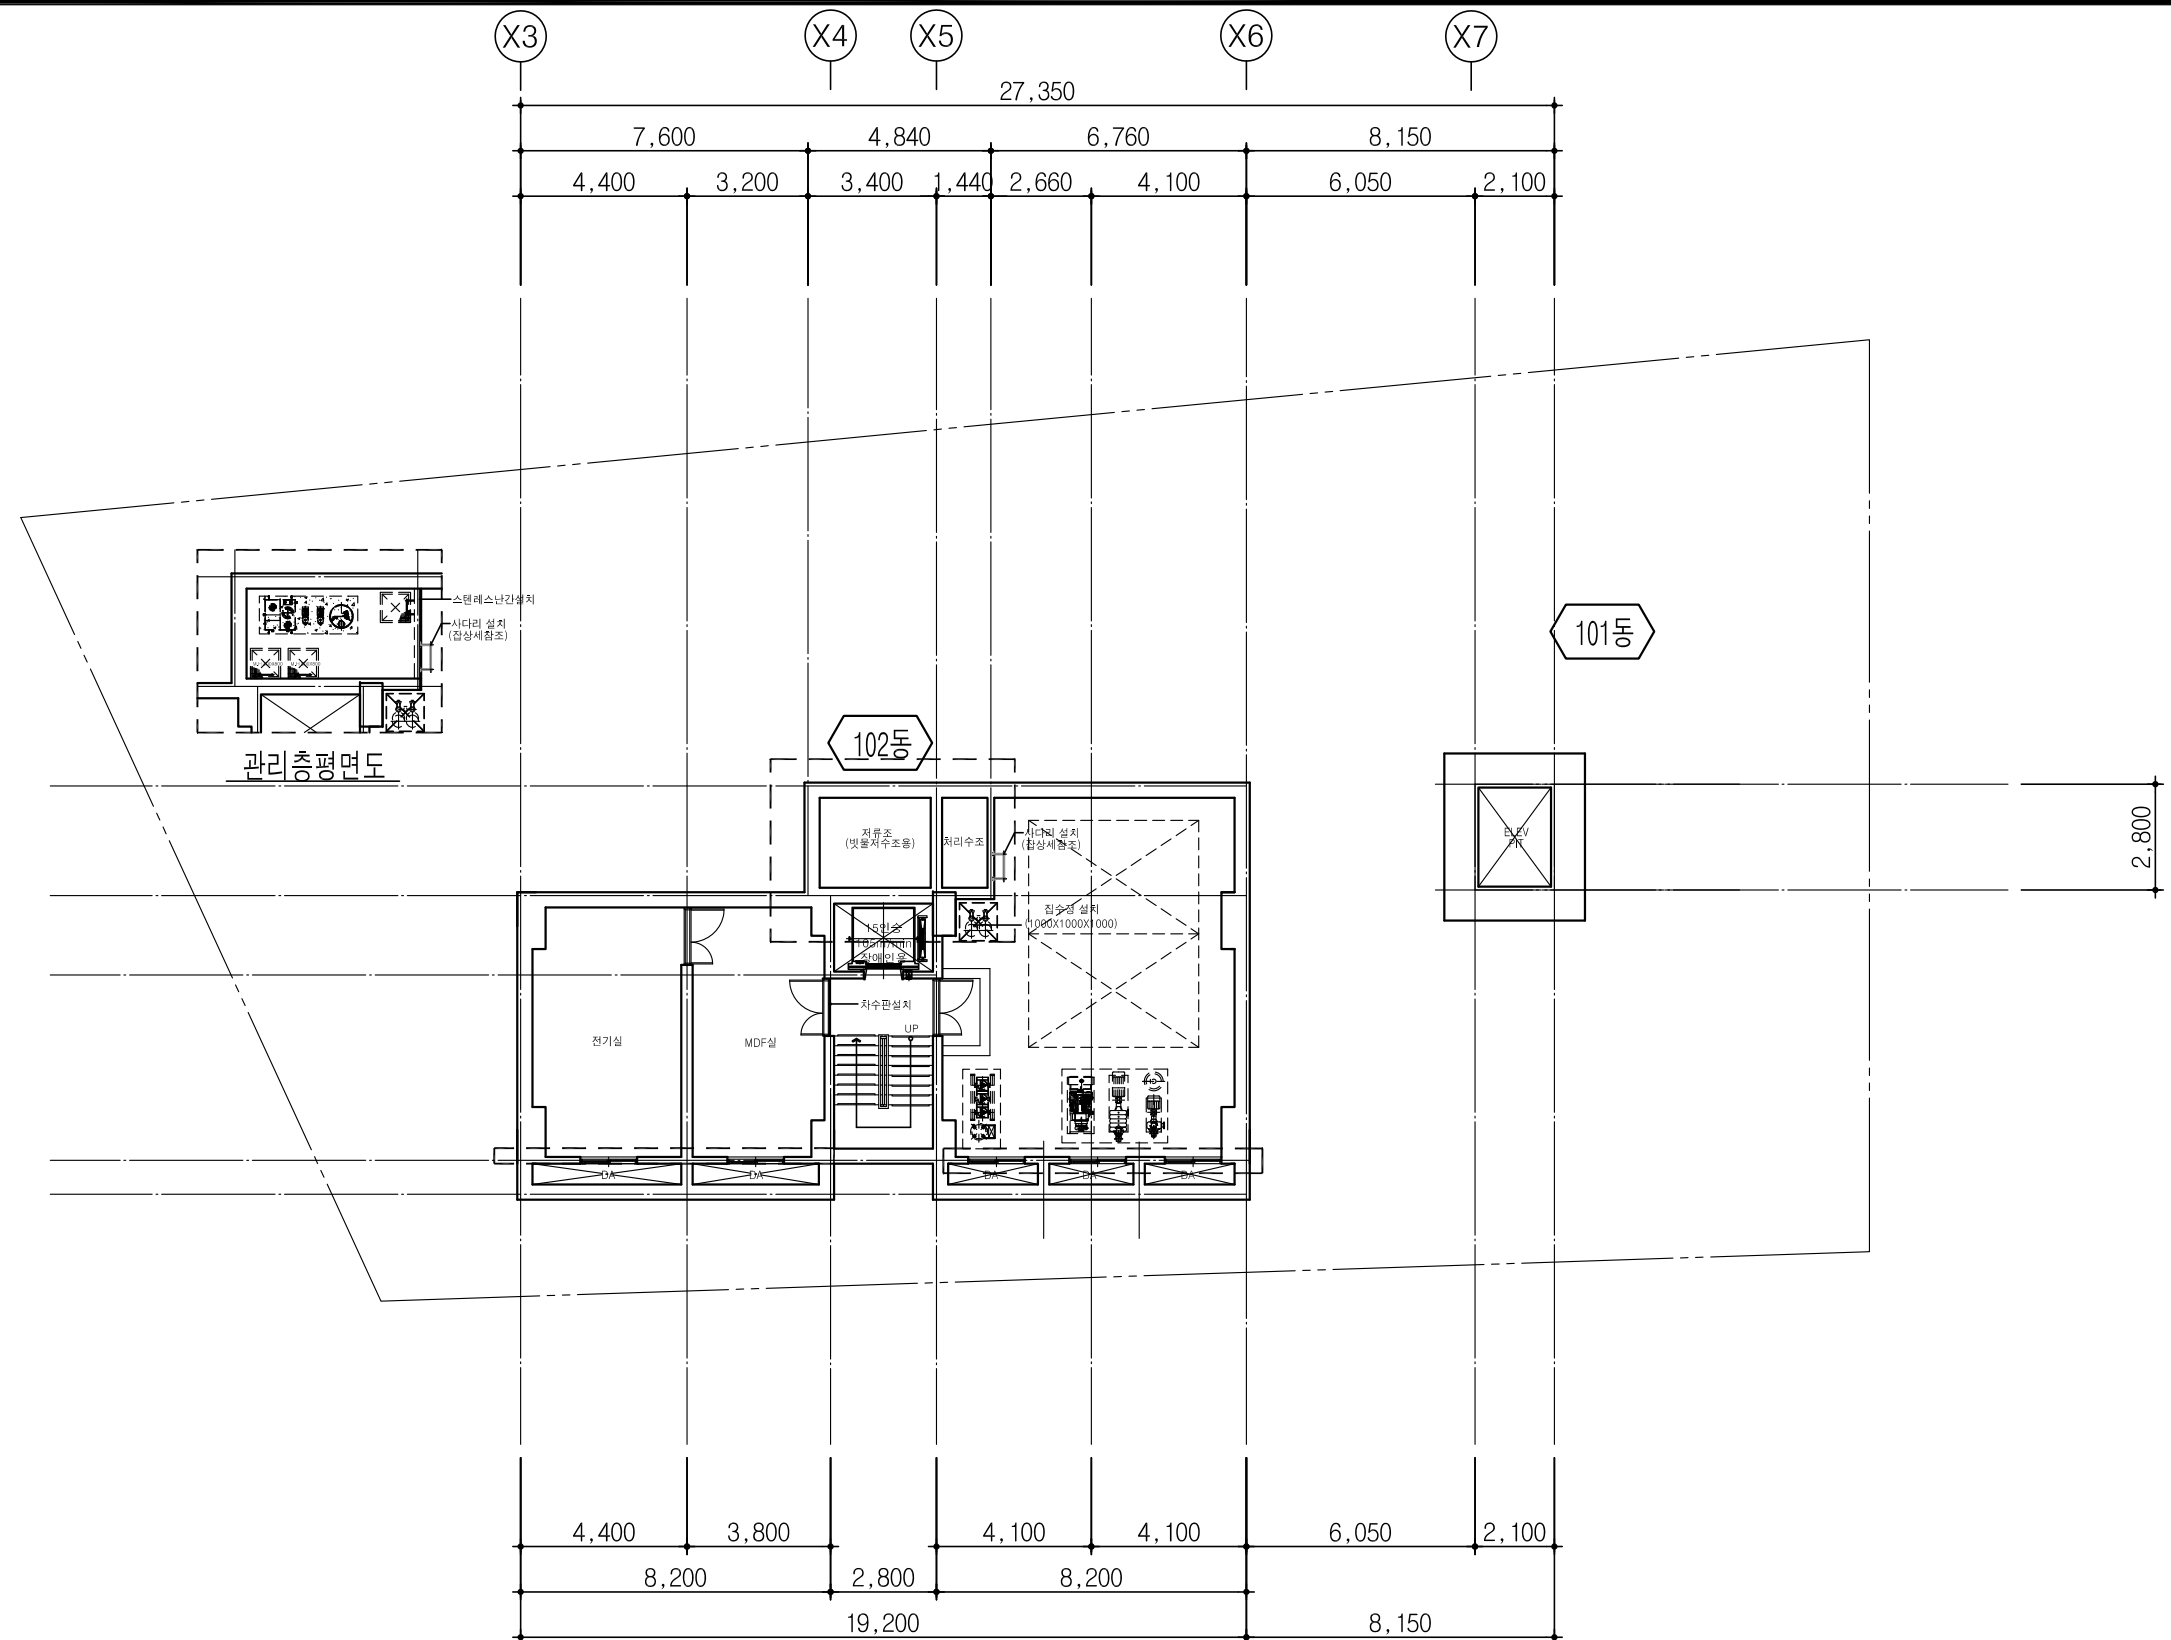


1

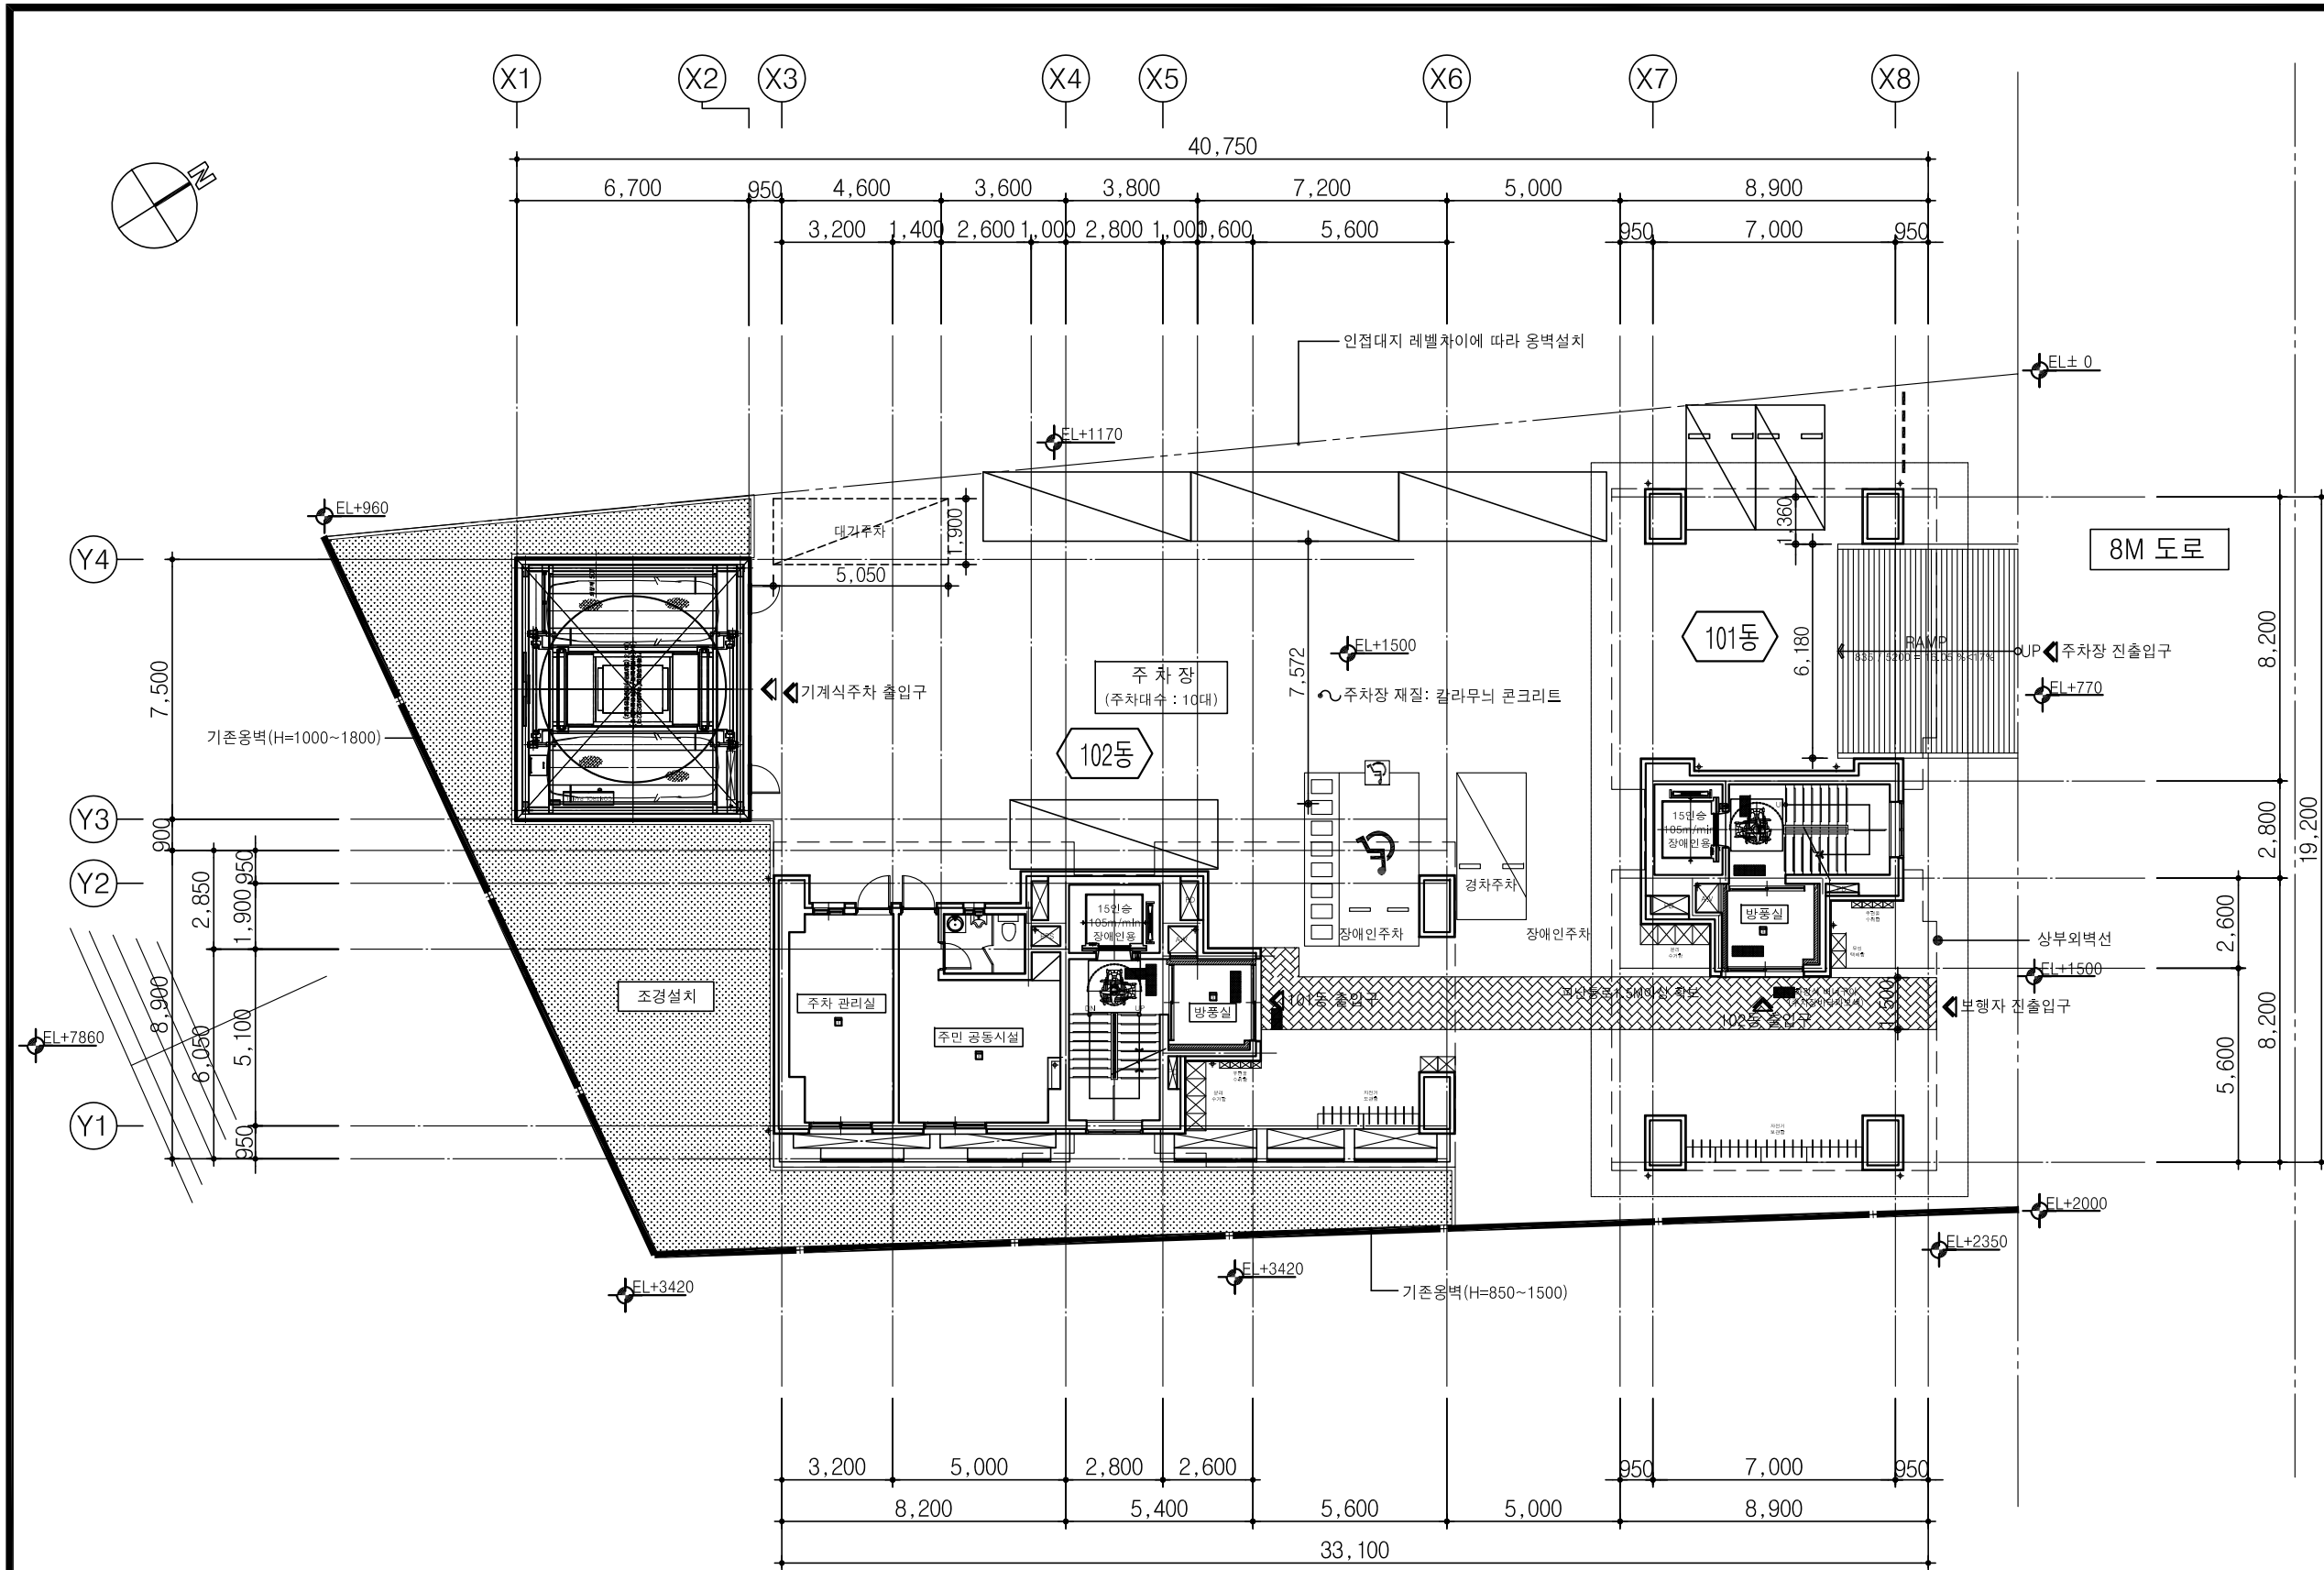

1 지상 1층 평면도
축척 : A3:1/200

PROJECT TITLE 사업명칭		
독산동 1005-3 오피스텔 신축공사		
NAME OF DRAWING 도면명		
지상 1층 평면도		
NOTE 주 기		
* 각동 주 출입문은 방화유리 적용		
NO. ▲ REVISIONS ▲ DATE 번호 수정 일자		
DESIGNED BY 설 계		
CHECKED BY 심 사		
APPROVED BY 승 인		
CONSULTANTS 협동설계		
SCALE 축척		
DATE 일 자 2019. 10		
DWG. NO. 도면 번호		
SHEET NO. 일련 번호 A-13		
 건축사사무소 시그에이 THE ARCHITECTS GROUP TEL. 02.541.5516 FAX. 02.512.2882		

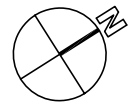

1 지상 2~8층 평면도
축척 : A3:1/200


PROJECT TITLE 사업명칭 독산동 1005-3 오피스텔 신축공사		
NAME OF DRAWING 도면명 지상 2~8층 평면도		
NOTE 주 기 ▼ ▼		
NO. ▲ REVISIONS ▲ DATE 번호 수정 일자		
DESIGNED BY 설 계		
CHECKED BY 심 사		
APPROVED BY 승 인		
CONSULTANTS 협 동 설 계		
SCALE 축 척		
DATE 일 자 2019. 10		
DWG NO. 도면 번호		
SHEET NO. 일련 번호 A-14		
sig.A 건축사사무소 시그에이 THE ARCHITECTS GROUP TEL. 02.541.5516 FAX. 02.512.2882		

PROJECT TITLE
사업명칭

NAME OF DRAWING
도면명

NOTE
주 기

NO. 번호	▲	REVISIONS 수 정	▲	DATE 일 자
-----------	---	------------------	---	-------------

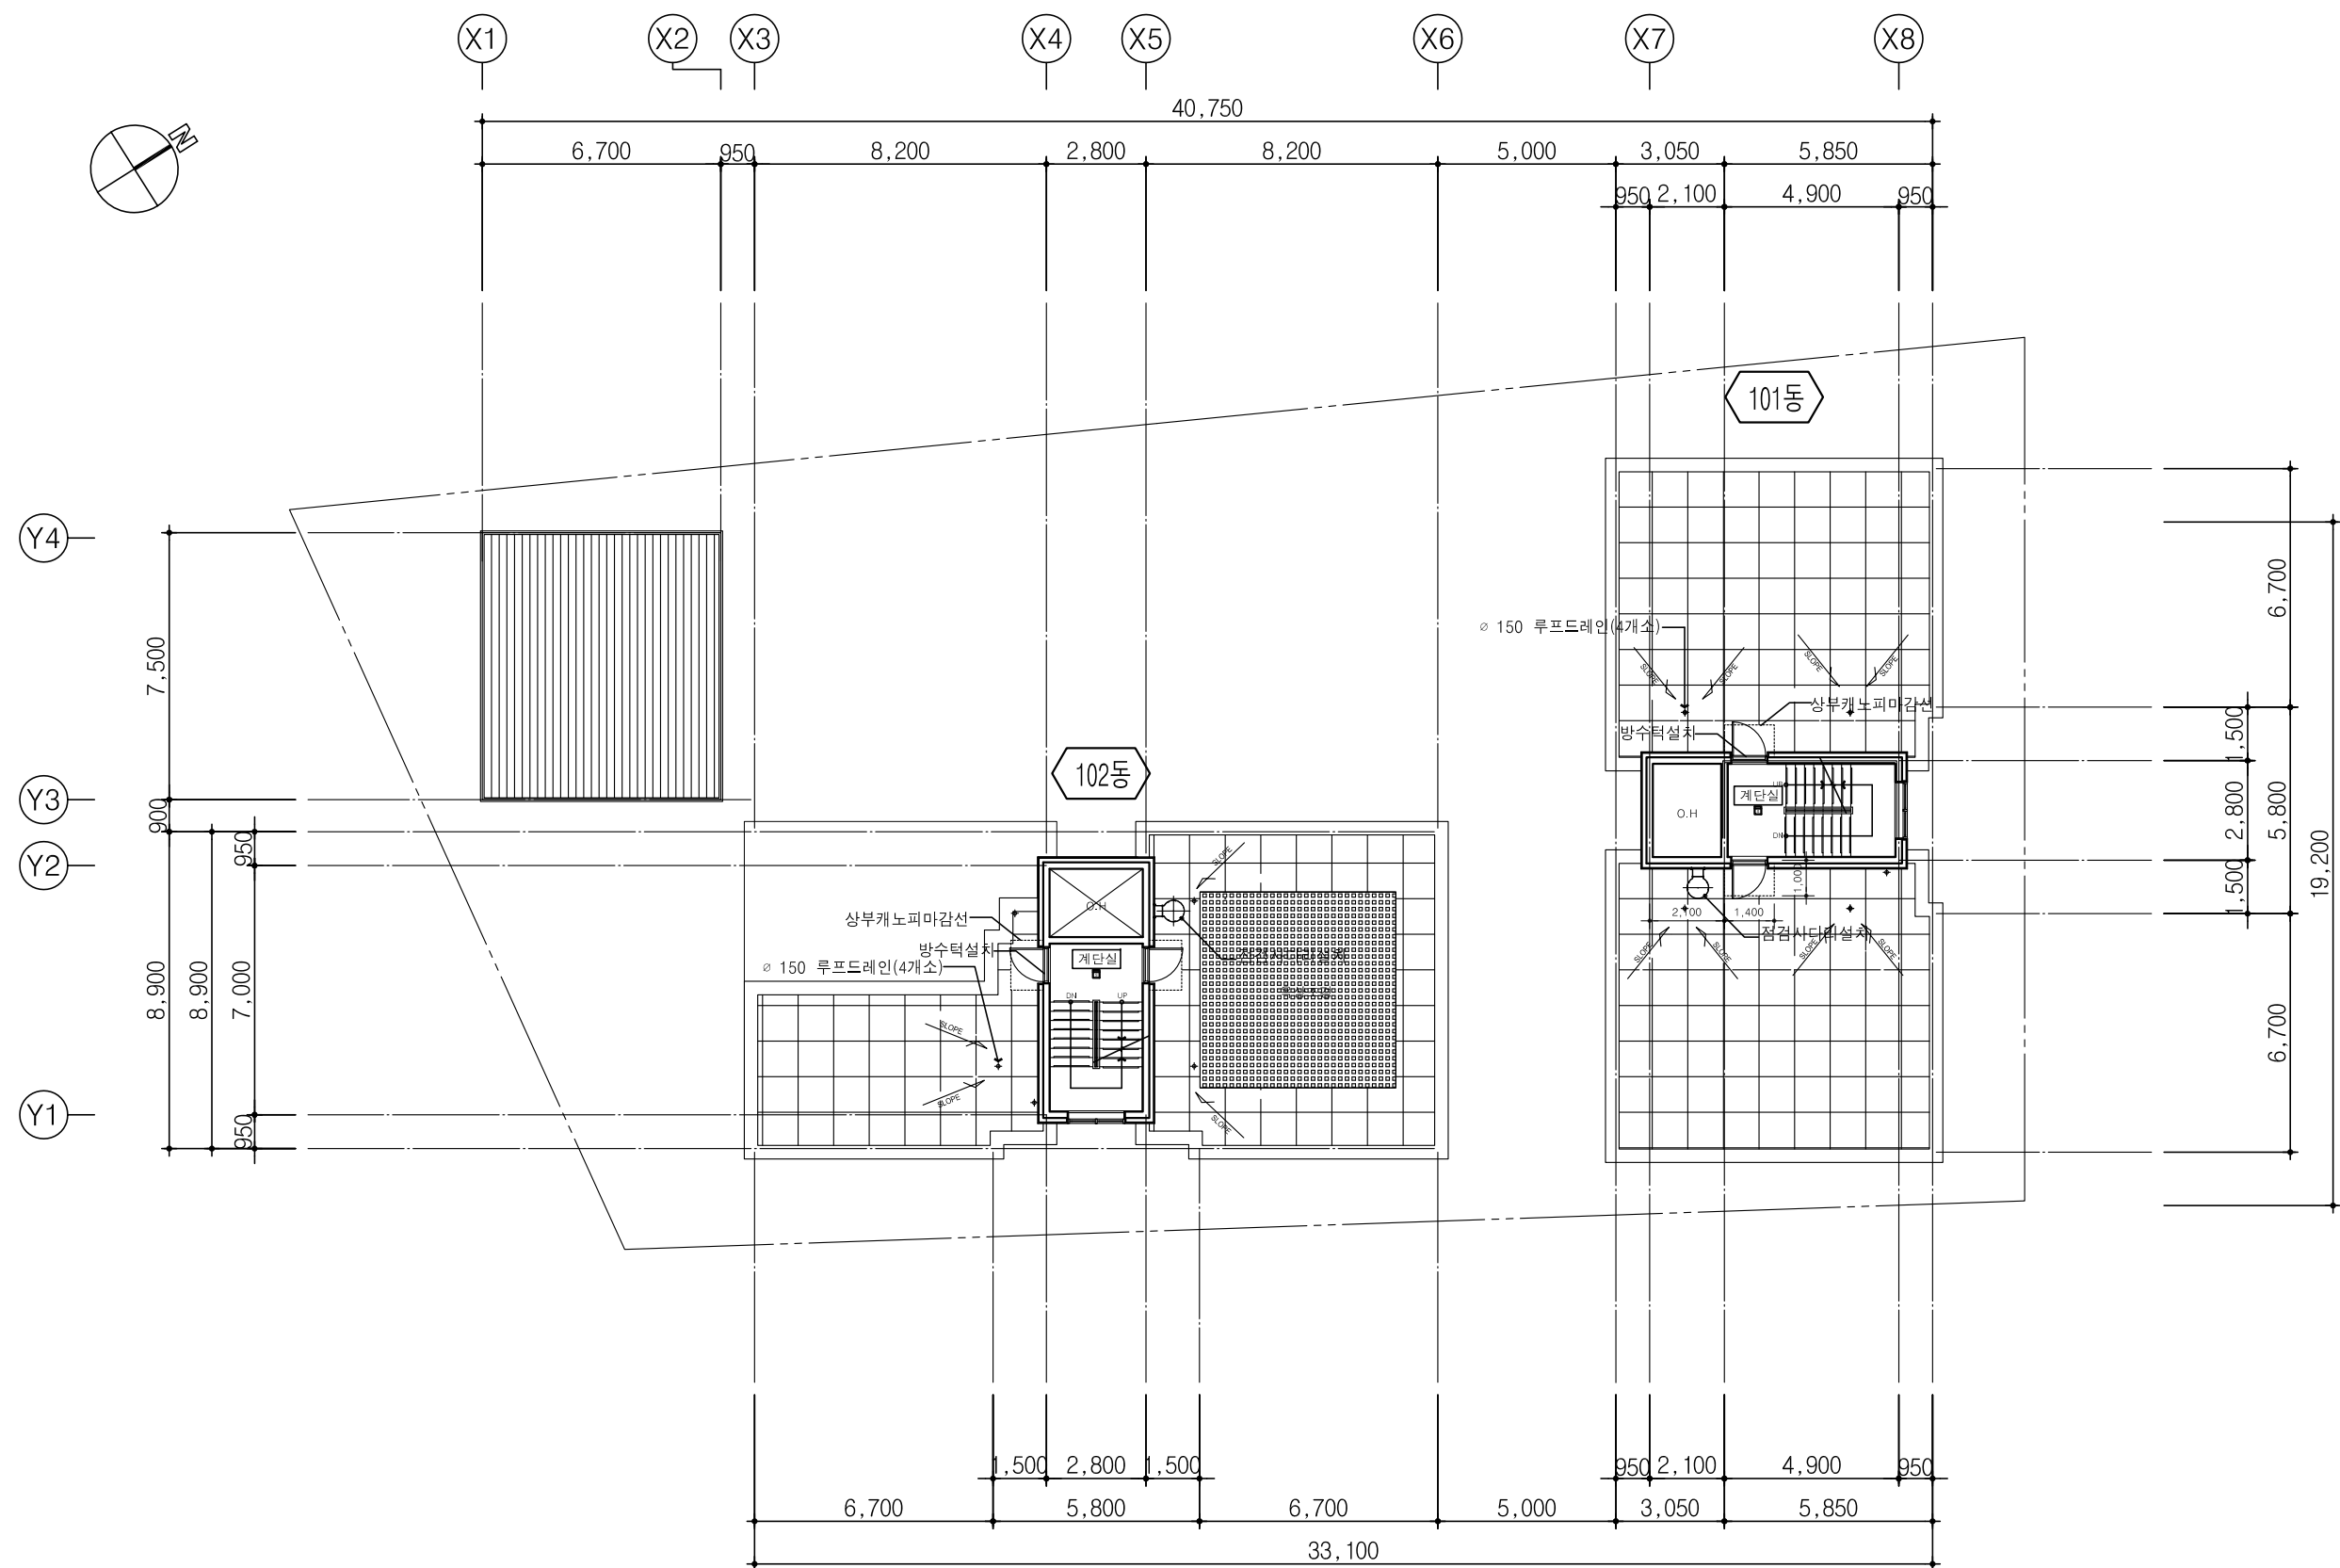PROJECT TITLE
사업명칭

NAME OF DRAWING
도면명


NOTE
주 기

NO. 번호	▲	REVISIONS 수 정	▲	DATE 일 자
-----------	---	------------------	---	-------------



1


지붕 및 옥탑지붕층 평면도

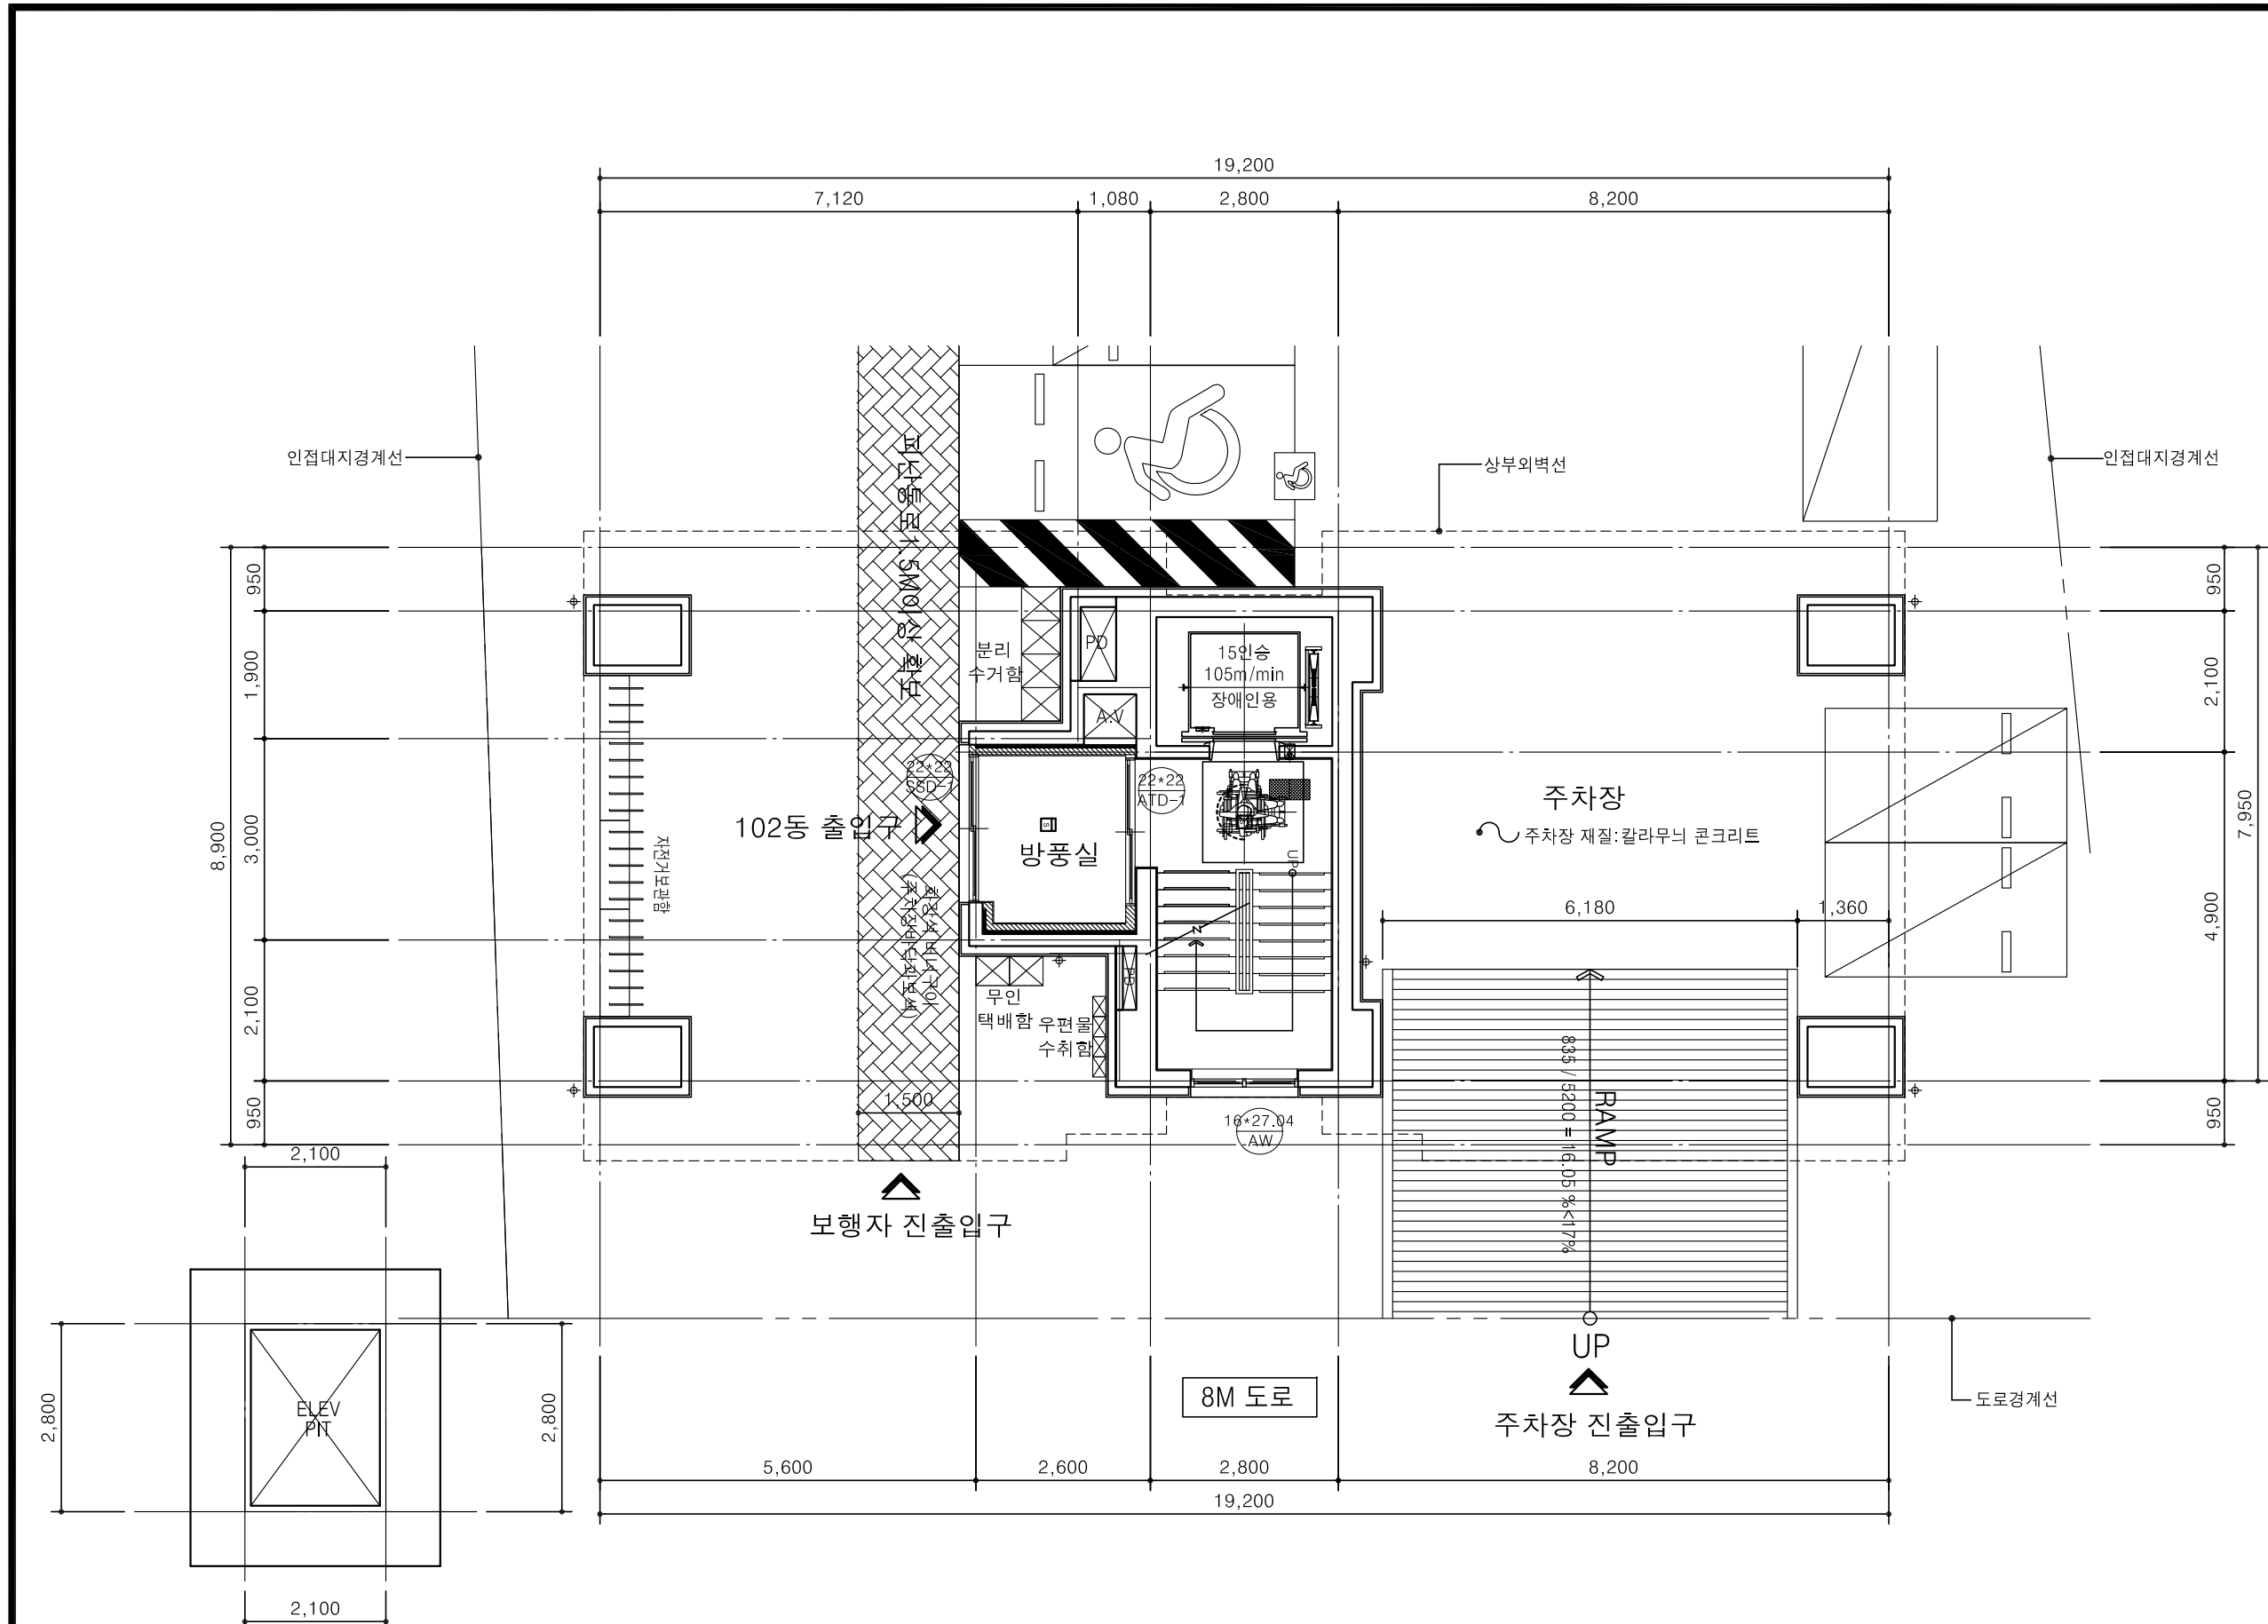

1 101동 ELEV. PIT 평면도
축척: A3:1/100

1 101동 1층 동 평면도
축척: A3:1/100

PROJECT TITLE 사업명칭		
독산동 1005-3 오피스텔 신축공사		
NAME OF DRAWING 도면명		
101동 1층 동 평면도		
NOTE 주 기		
NO. 번호 REVISIONS 수정 DATE 일자		
DESIGNED BY 설계		
CHECKED BY 심사		
APPROVED BY 승인		
CONSULTANTS 협동설계		
SCALE 축척		
DATE 일자 2019. 10		
DWG. NO. 도면번호		
SHEET NO. 일련번호		
A-17		
건축사사무소 시그에이 THE ARCHITECTS GROUP TEL. 02.541.5516 FAX. 02.512.2882		

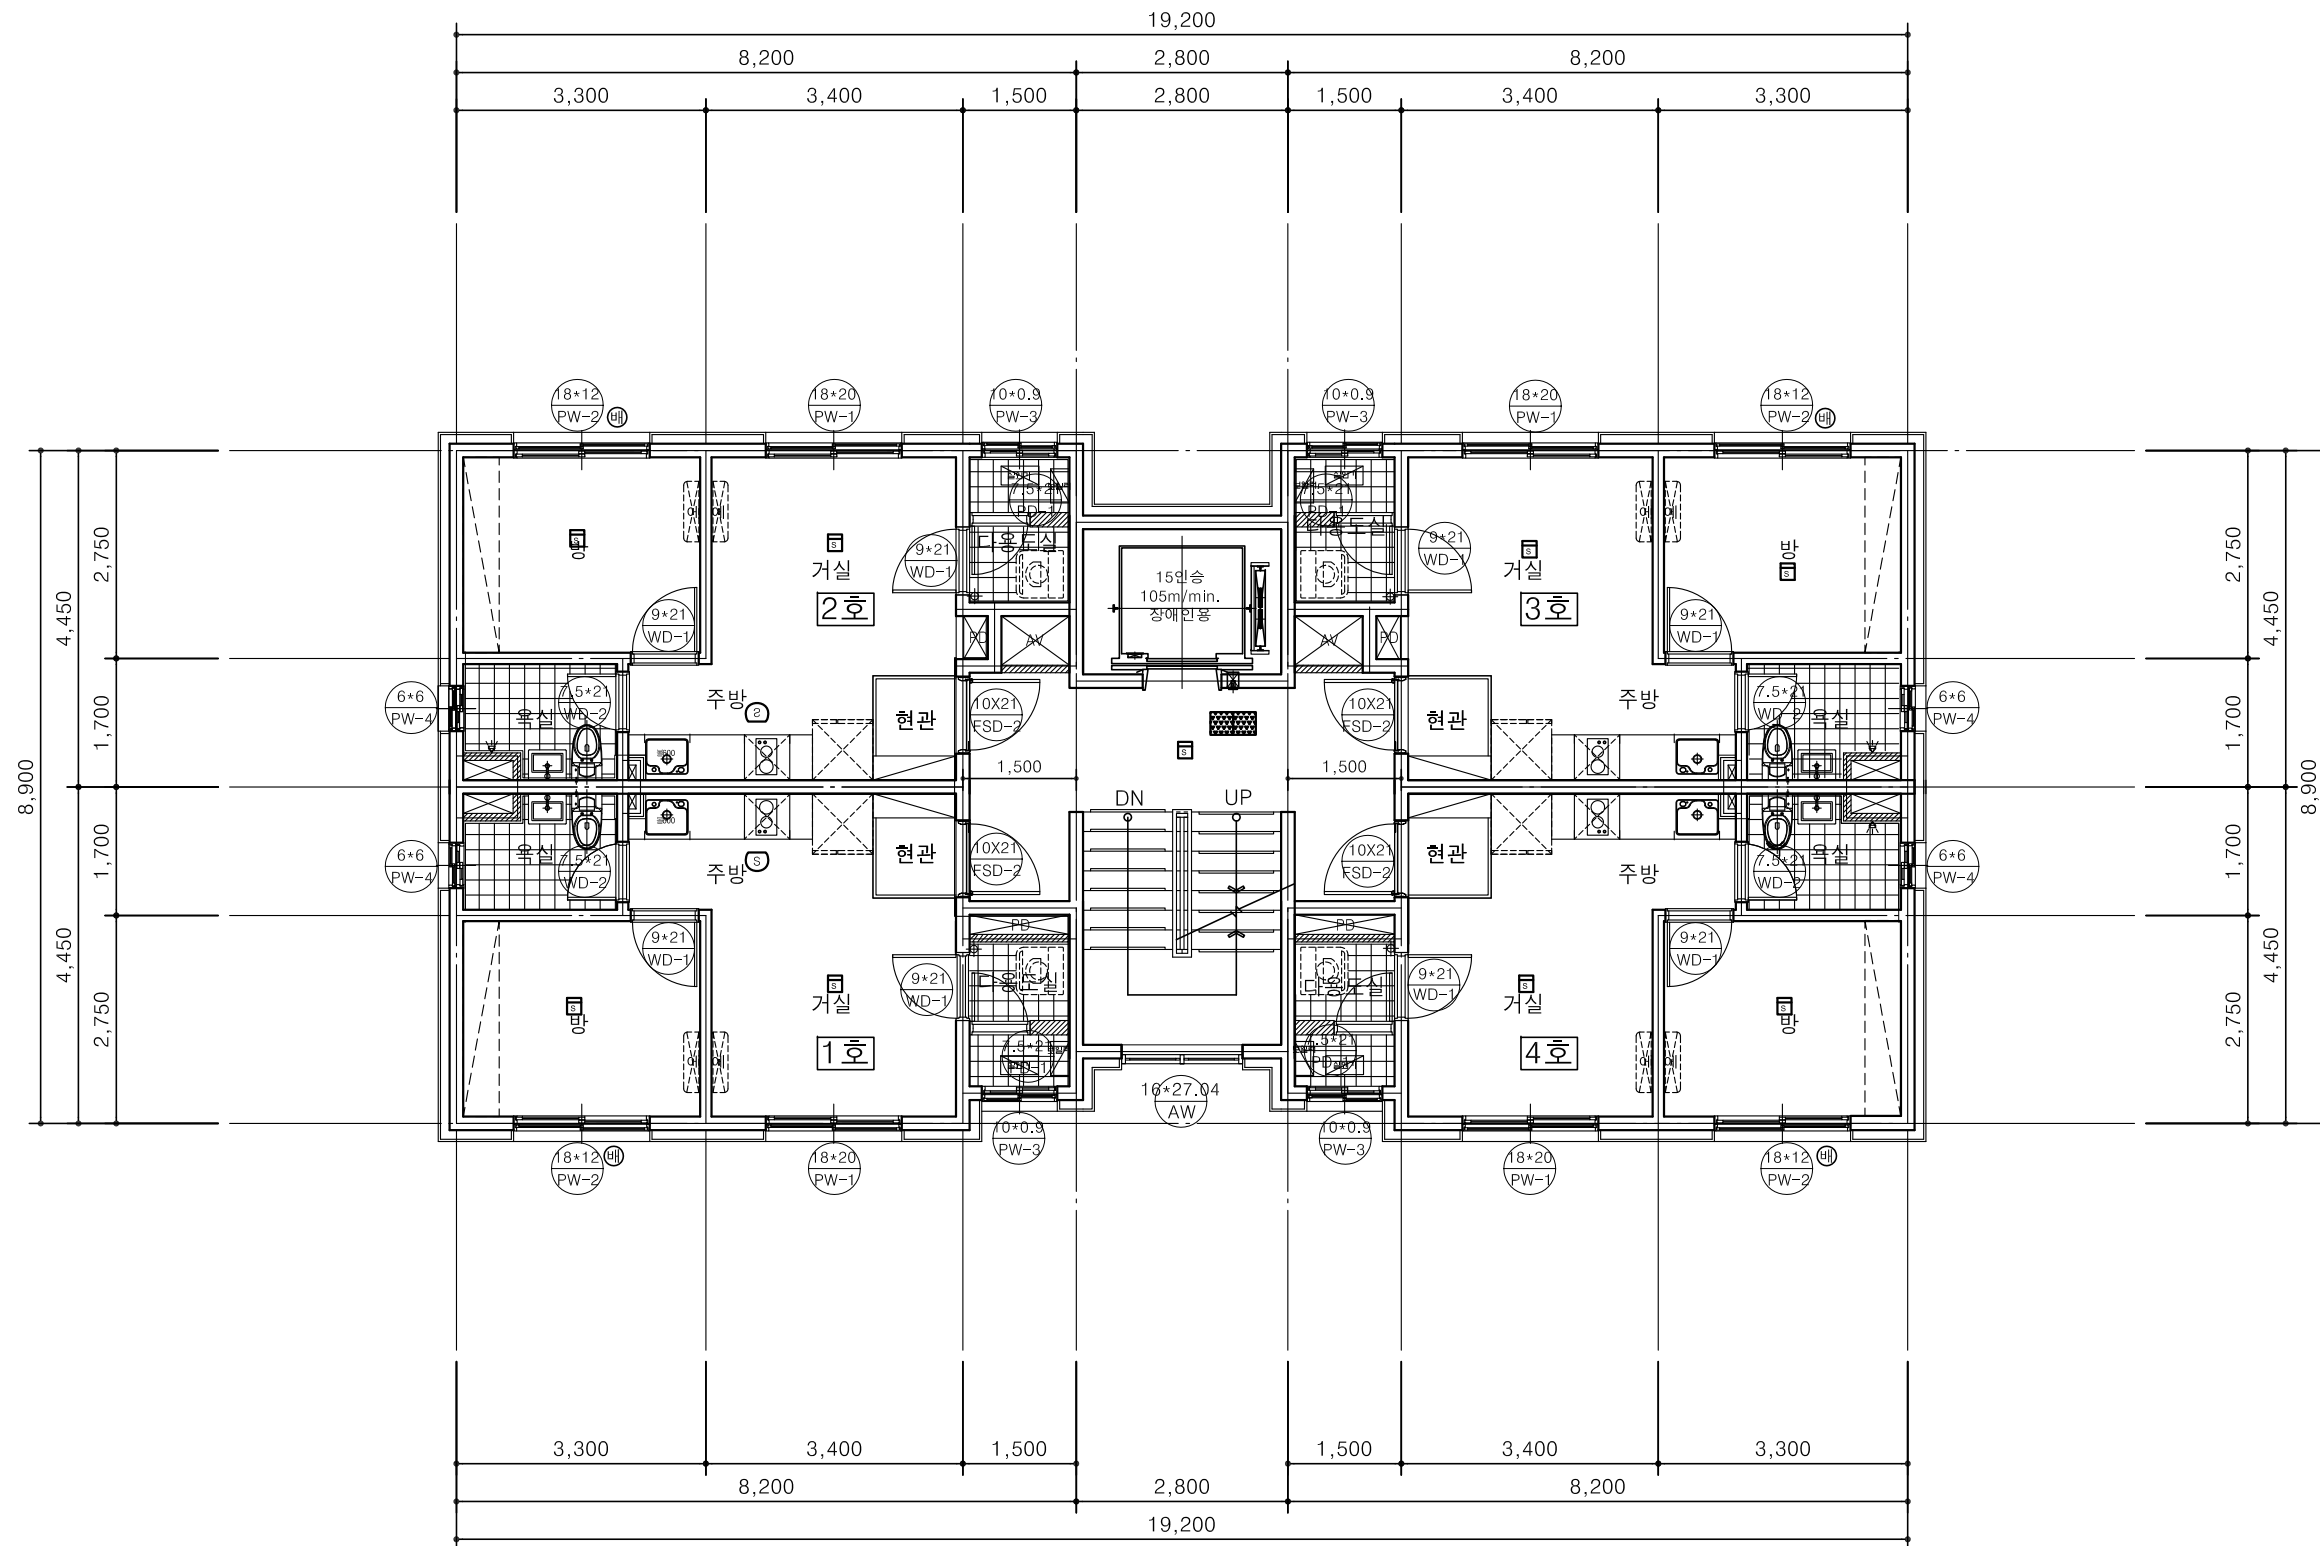

1 101동 2-9층 동 평 면 도
축척 : A3:1/100

PROJECT TITLE
사업명칭

독산동 1005-3 오피스텔
신축공사

NAME OF DRAWING
도면명

101동 2-9층 동 평 면 도

NOTE
주 기

NO. REVISIONS DATE
번호 수정 일자

DESIGNED BY
설 계

CHECKED BY
심 사

APPROVED BY
승 인

CONSULTANTS
협 동 설 계

SCALE
축 척

DATE
일 자 2019. 10

DWG. NO.
도면 번호

SHEET NO.
일련 번호


A-18

sig.A

건축사사무소 시그에이
THE ARCHITECTS GROUP
TEL. 02.541.5516
FAX. 02.512.2882



건축사사무소 시그에이
THE ARCHITECTS GROUP
TEL. 02.541.5516
FAX. 02.512.2882

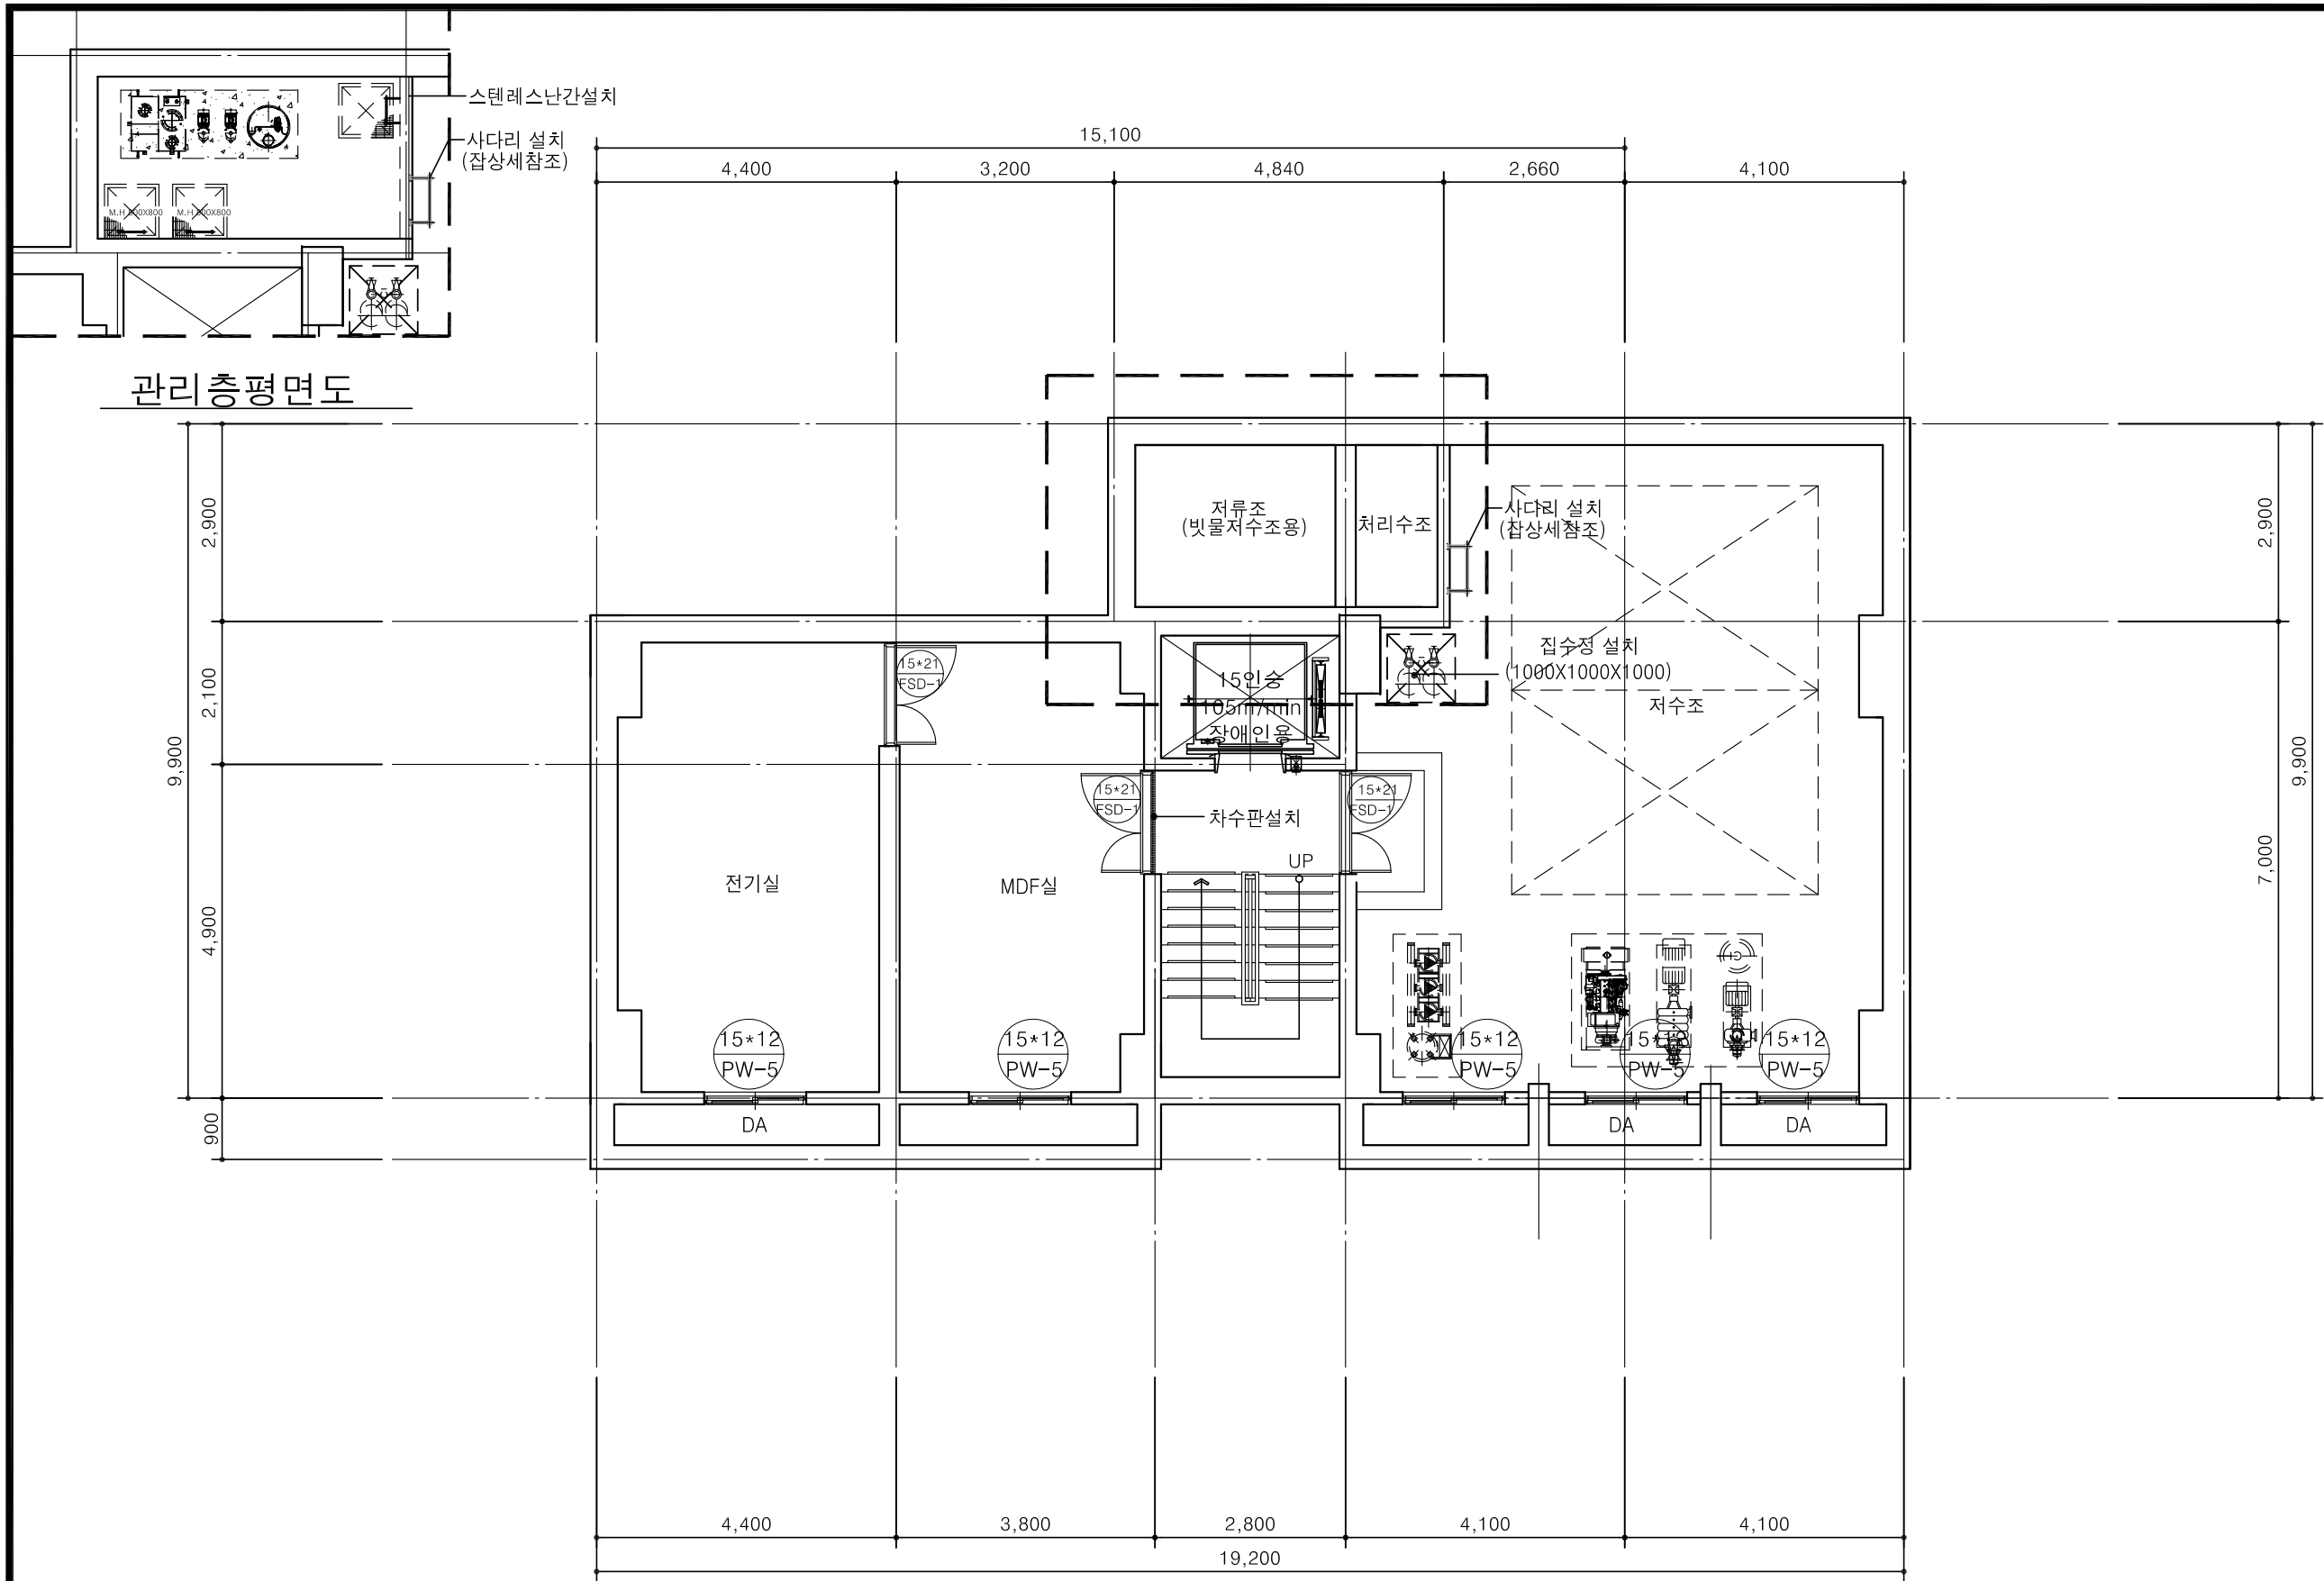

PROJECT TITLE
사업명칭

독산동 1005-3 오피스텔
신축공사

NAME OF DRAWING
도면명

102동 지하1층 동 평면도

NOTE
주 기

▼ ▼

NO. ▲ REVISIONS ▲ DATE
번호 수정 일자

DESIGNED BY
설 계

CHECKED BY
심 사

APPROVED BY
승 인

CONSULTANTS
협 동 설 계

SCALE
축 척

DATE
일 자

2019. 10

DWG. NO.
도면 번호

SHEET NO.
일련 번호

A-□2□0

sig.A

건축사사무소 시그에이

THE ARCHITECTS GROUP
TEL. 02.541.5516
FAX. 02.512.2882

1 102동 지하1층 동 평면도
축척: A3:1/100

PROJECT TITLE
사업명칭

독산동 1005-3 오피스텔
신축공사

NAME OF DRAWING
도면명

102동 1층 동 평면도

NOTE
주 기

▼ ▼

NO. ▲ REVISIONS ▲ DATE
번호 수정 일자

DESIGNED BY
설 계

CHECKED BY
심 사

APPROVED BY
승 인

CONSULTANTS
협 동 설 계

SCALE
축 척

DATE
일 자

2019. 10

DWG. NO.
도면 번호


SHEET NO.
일련 번호

A-□□21

sig.A


건축사사무소 시그에이

THE ARCHITECTS GROUP
TEL. 02.541.5516
FAX. 02.512.2882

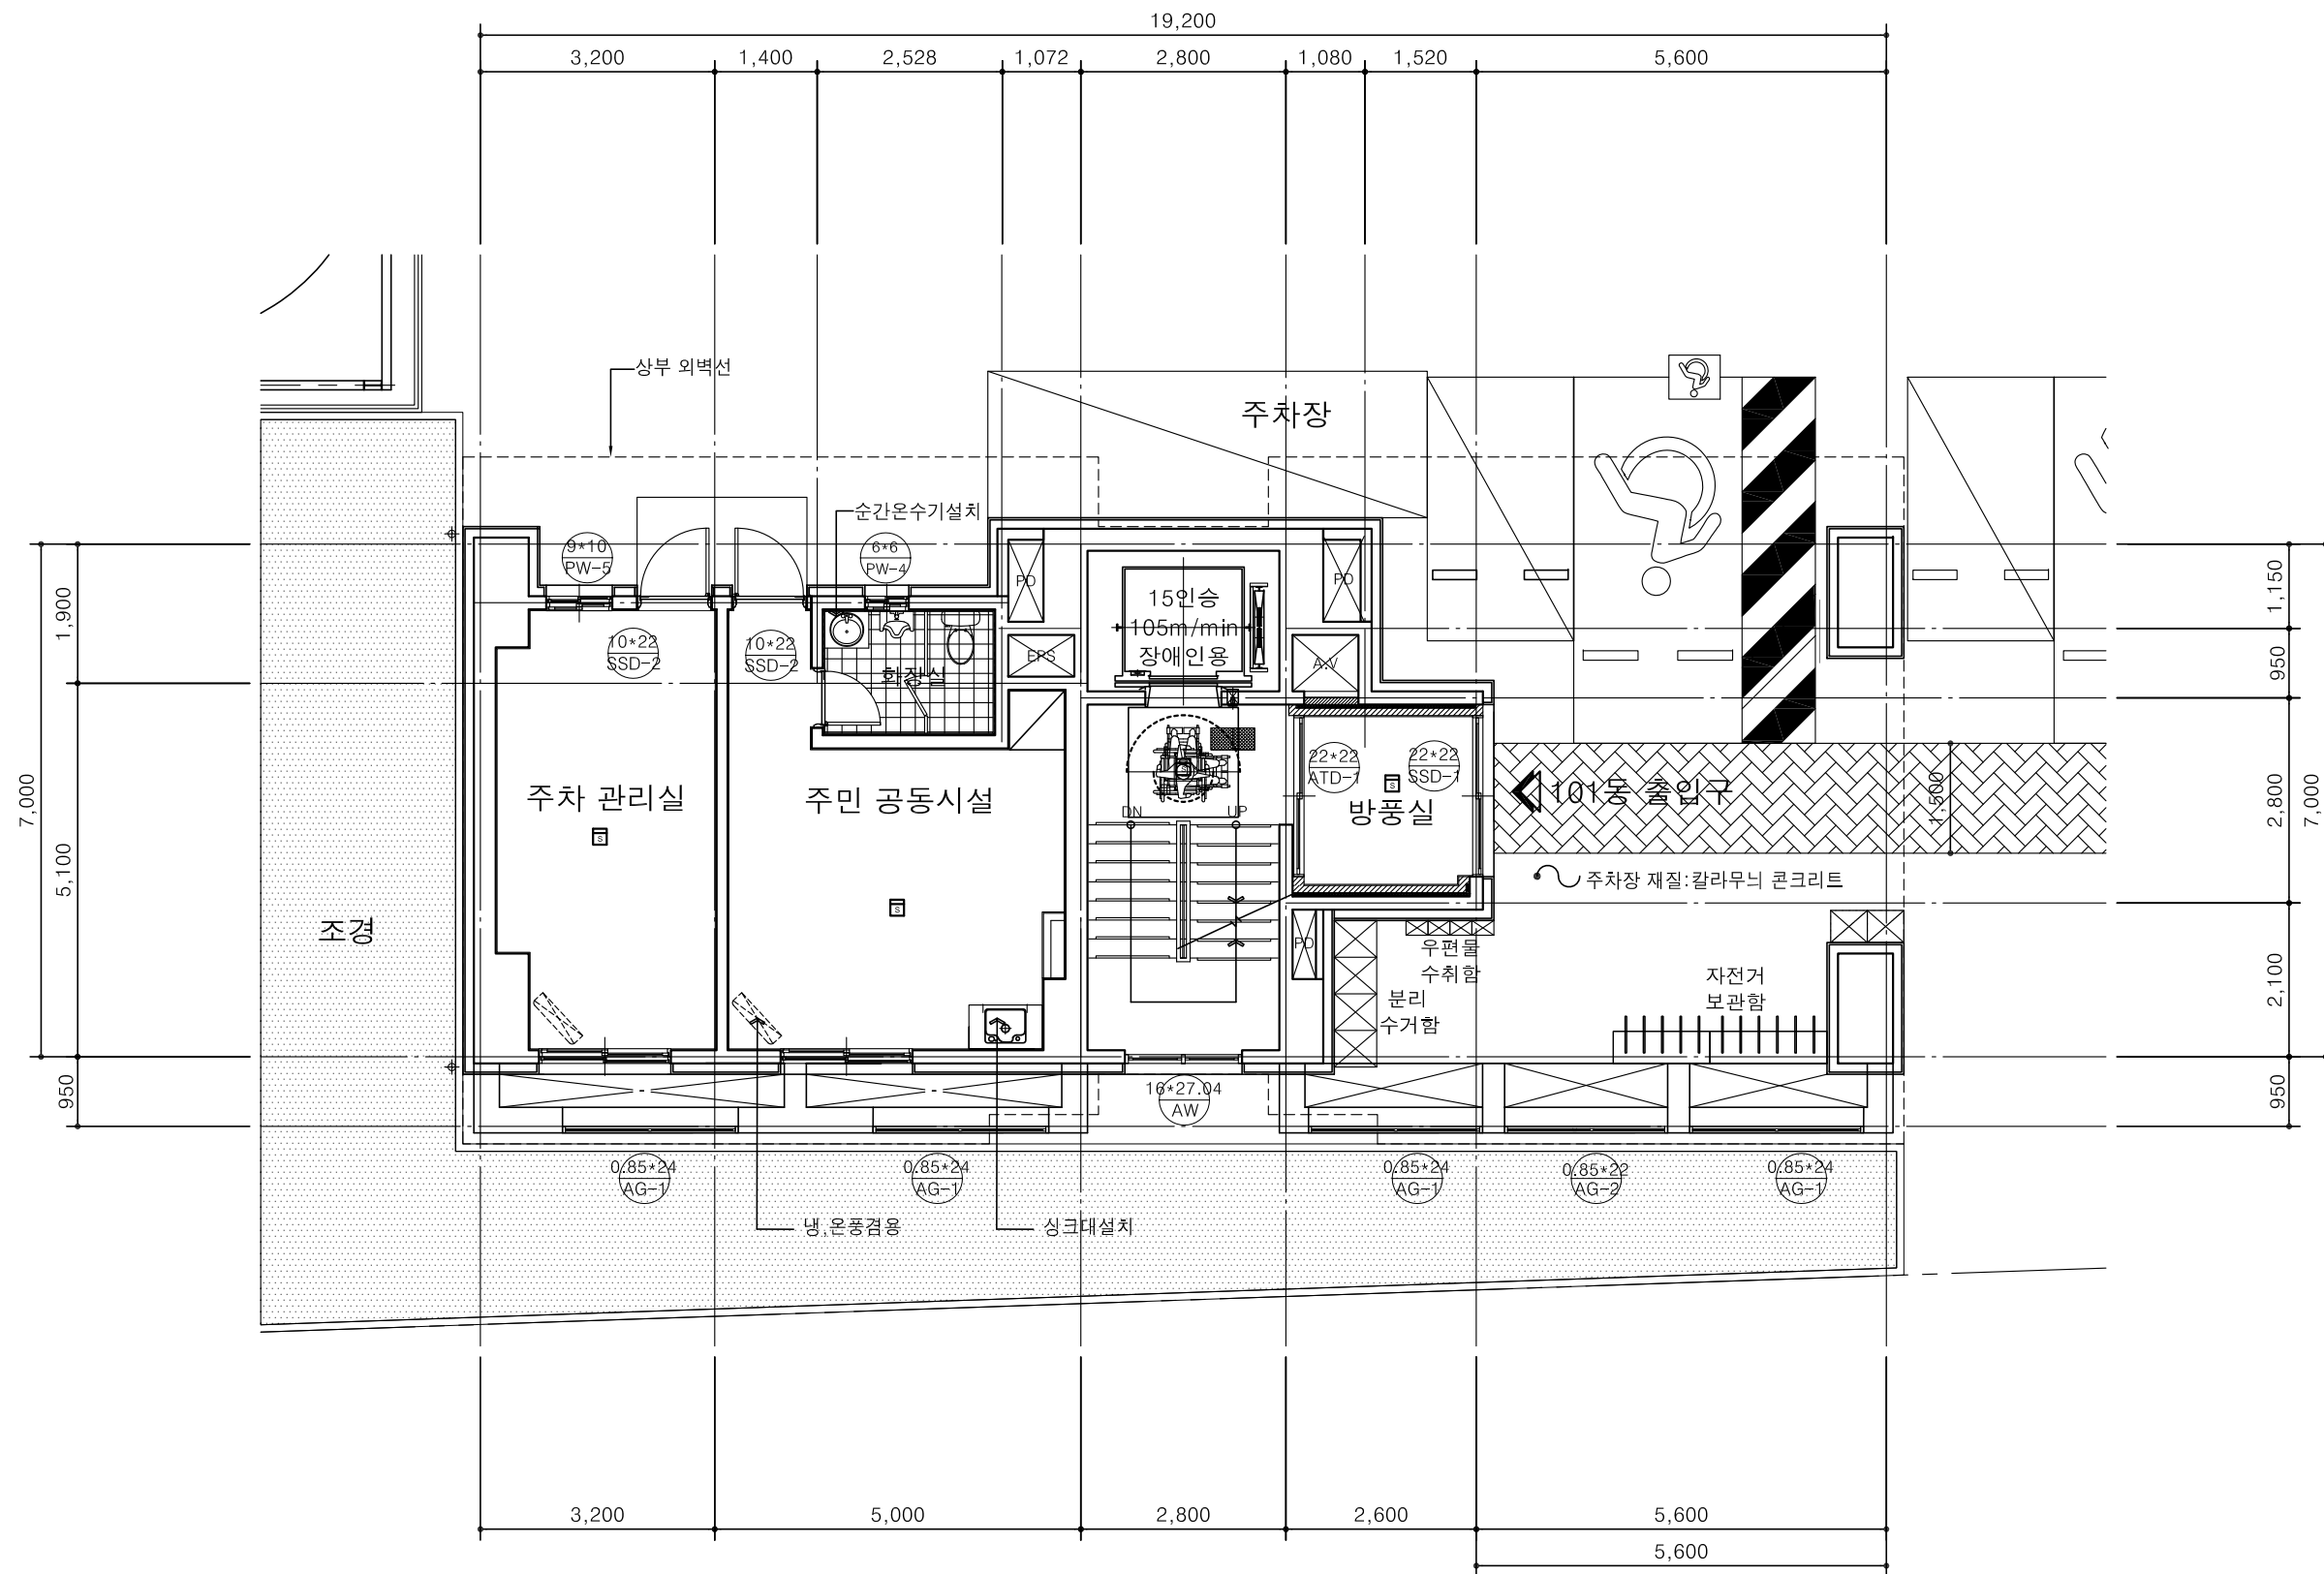


1 102동 1층 동 평면도

축척: A3:1/100

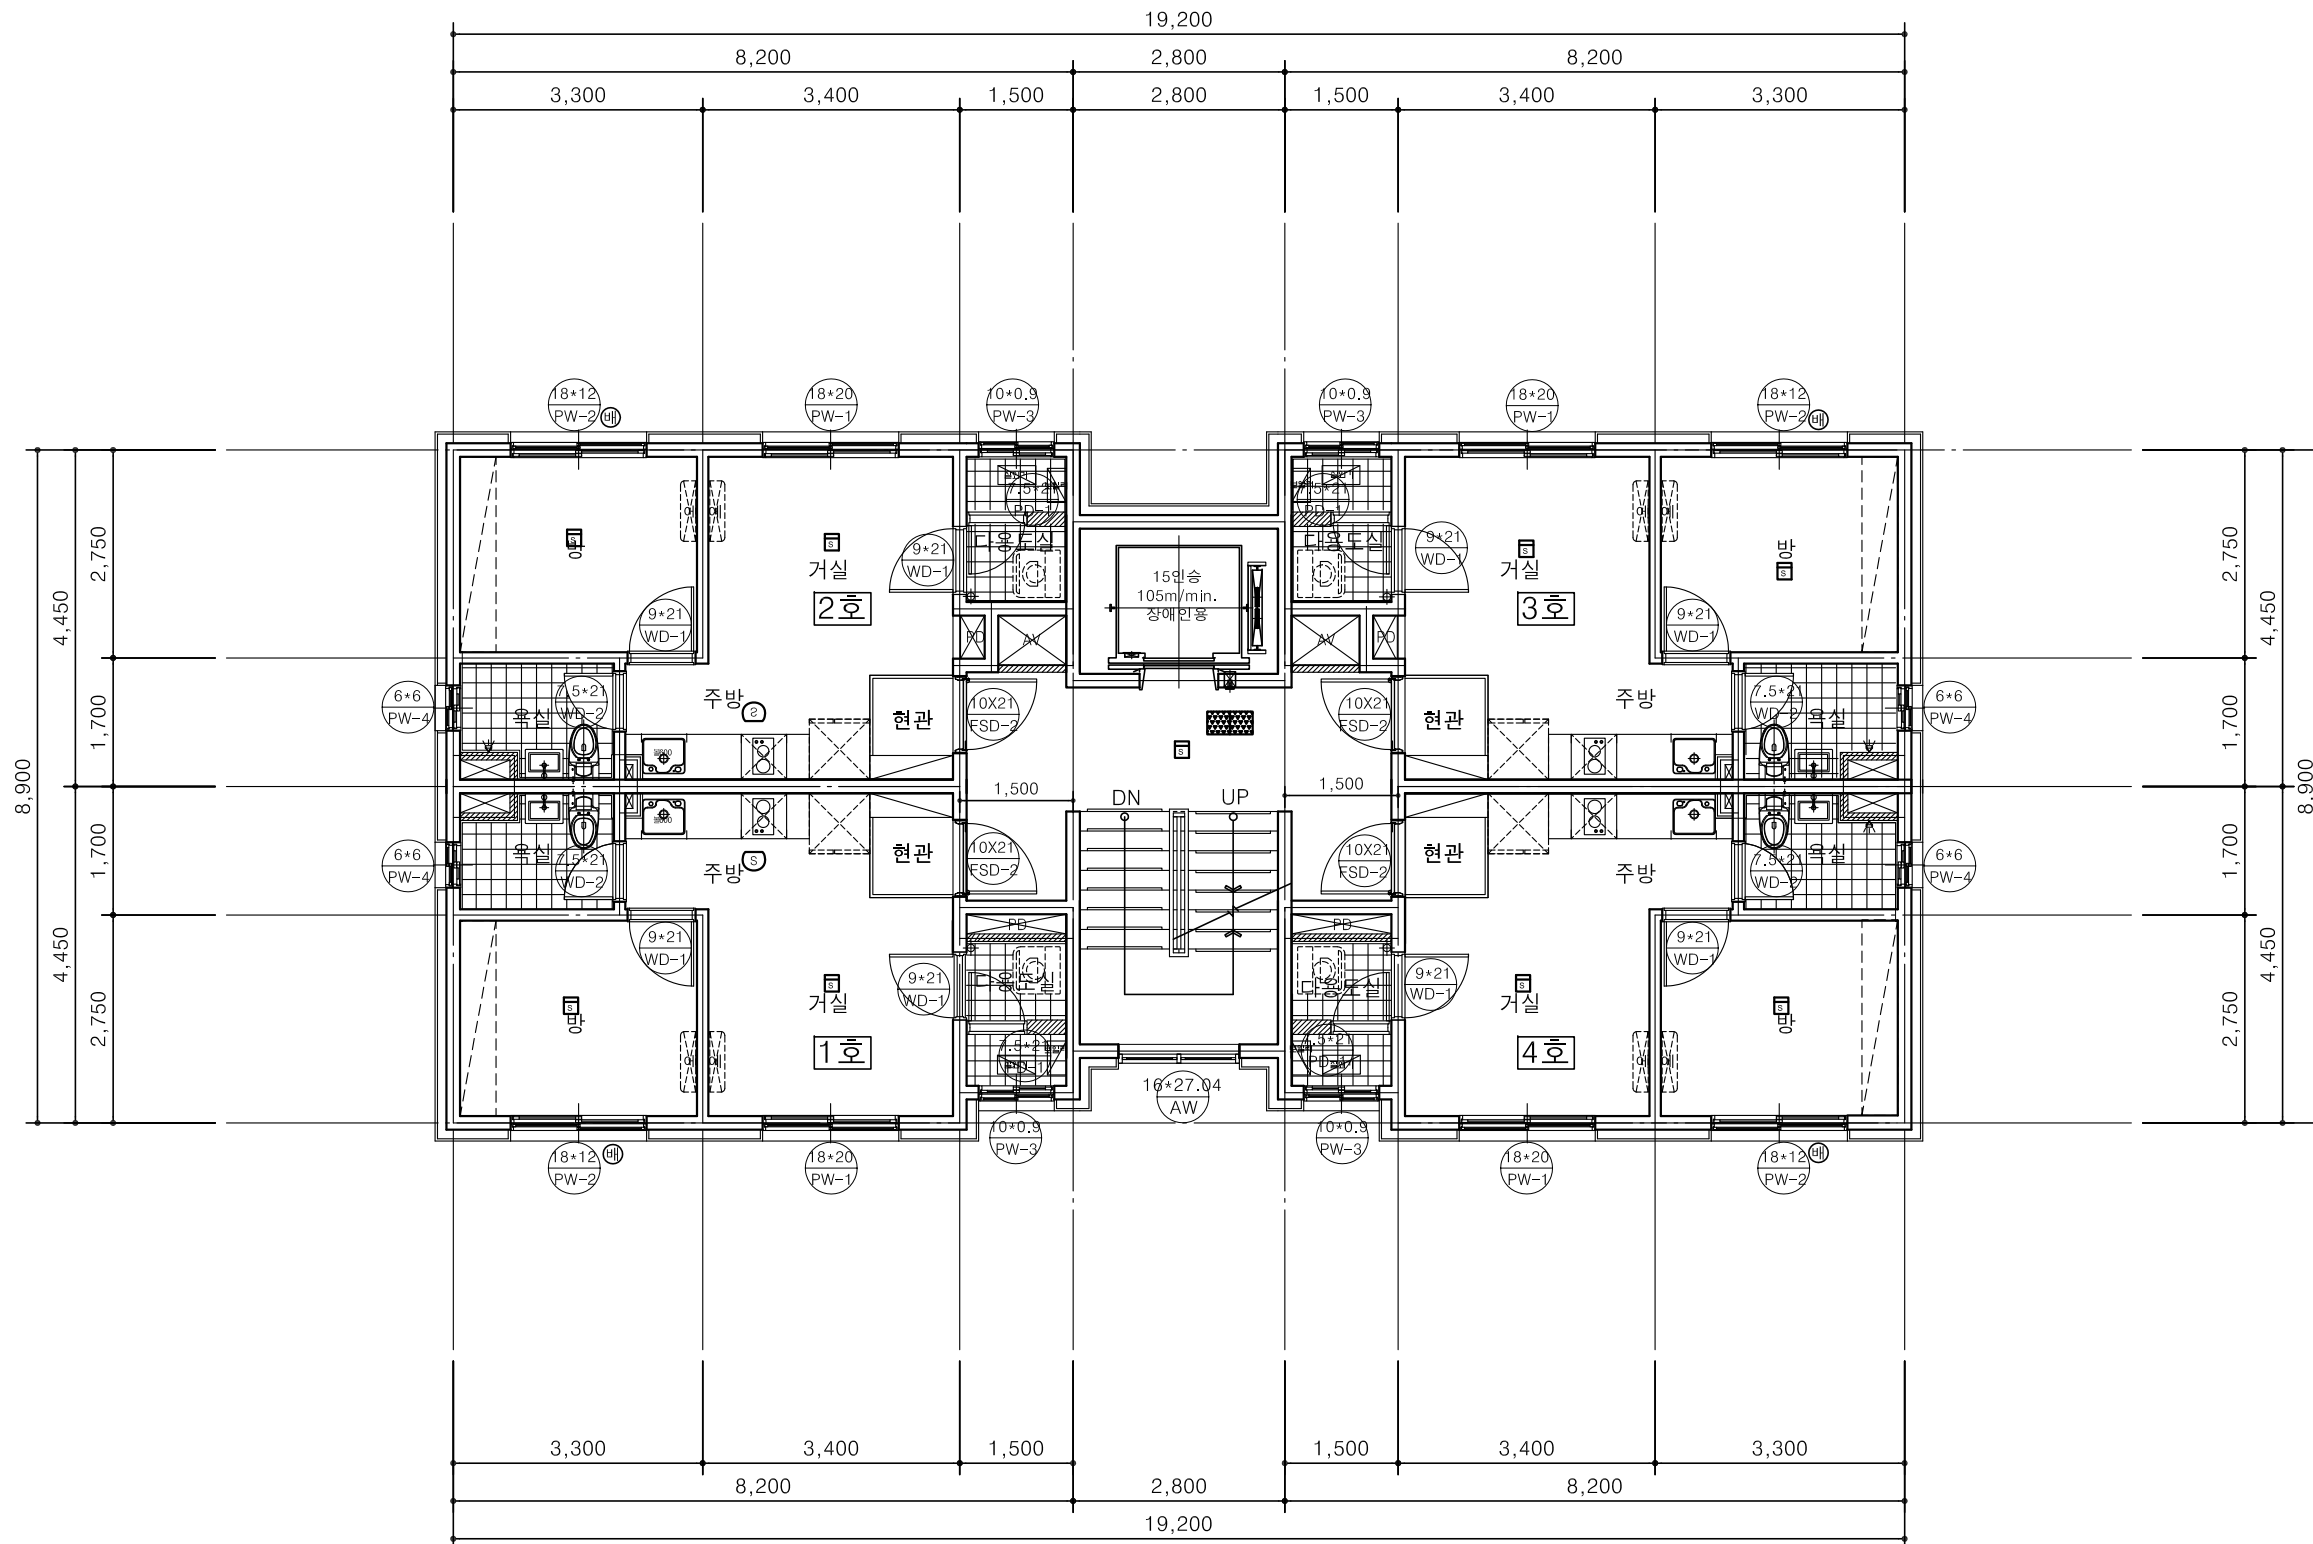


1 102동 2-8층 동 평 면 도
축척 : A3:1/100

PROJECT TITLE 사업명칭		
독산동 1005-3 오피스텔 신축공사		
NAME OF DRAWING 도면명		
102동 2-8층 동 평 면 도		
NOTE 주 기		
▼ ▼		
NO. ▲ REVISIONS ▲ DATE 번호 수정 일자		
DESIGNED BY 설 계		
CHECKED BY 심 사		
APPROVED BY 승 인		
CONSULTANTS 협 동 설 계		
SCALE 축 척		
DATE 일 자 2019. 10		
DWG. NO. 도면 번호		
SHEET NO. 일련 번호 A-□22		
건축사사무소 시그에이		
THE ARCHITECTS GROUP		
TEL. 02.541.5516		
FAX. 02.512.2882		

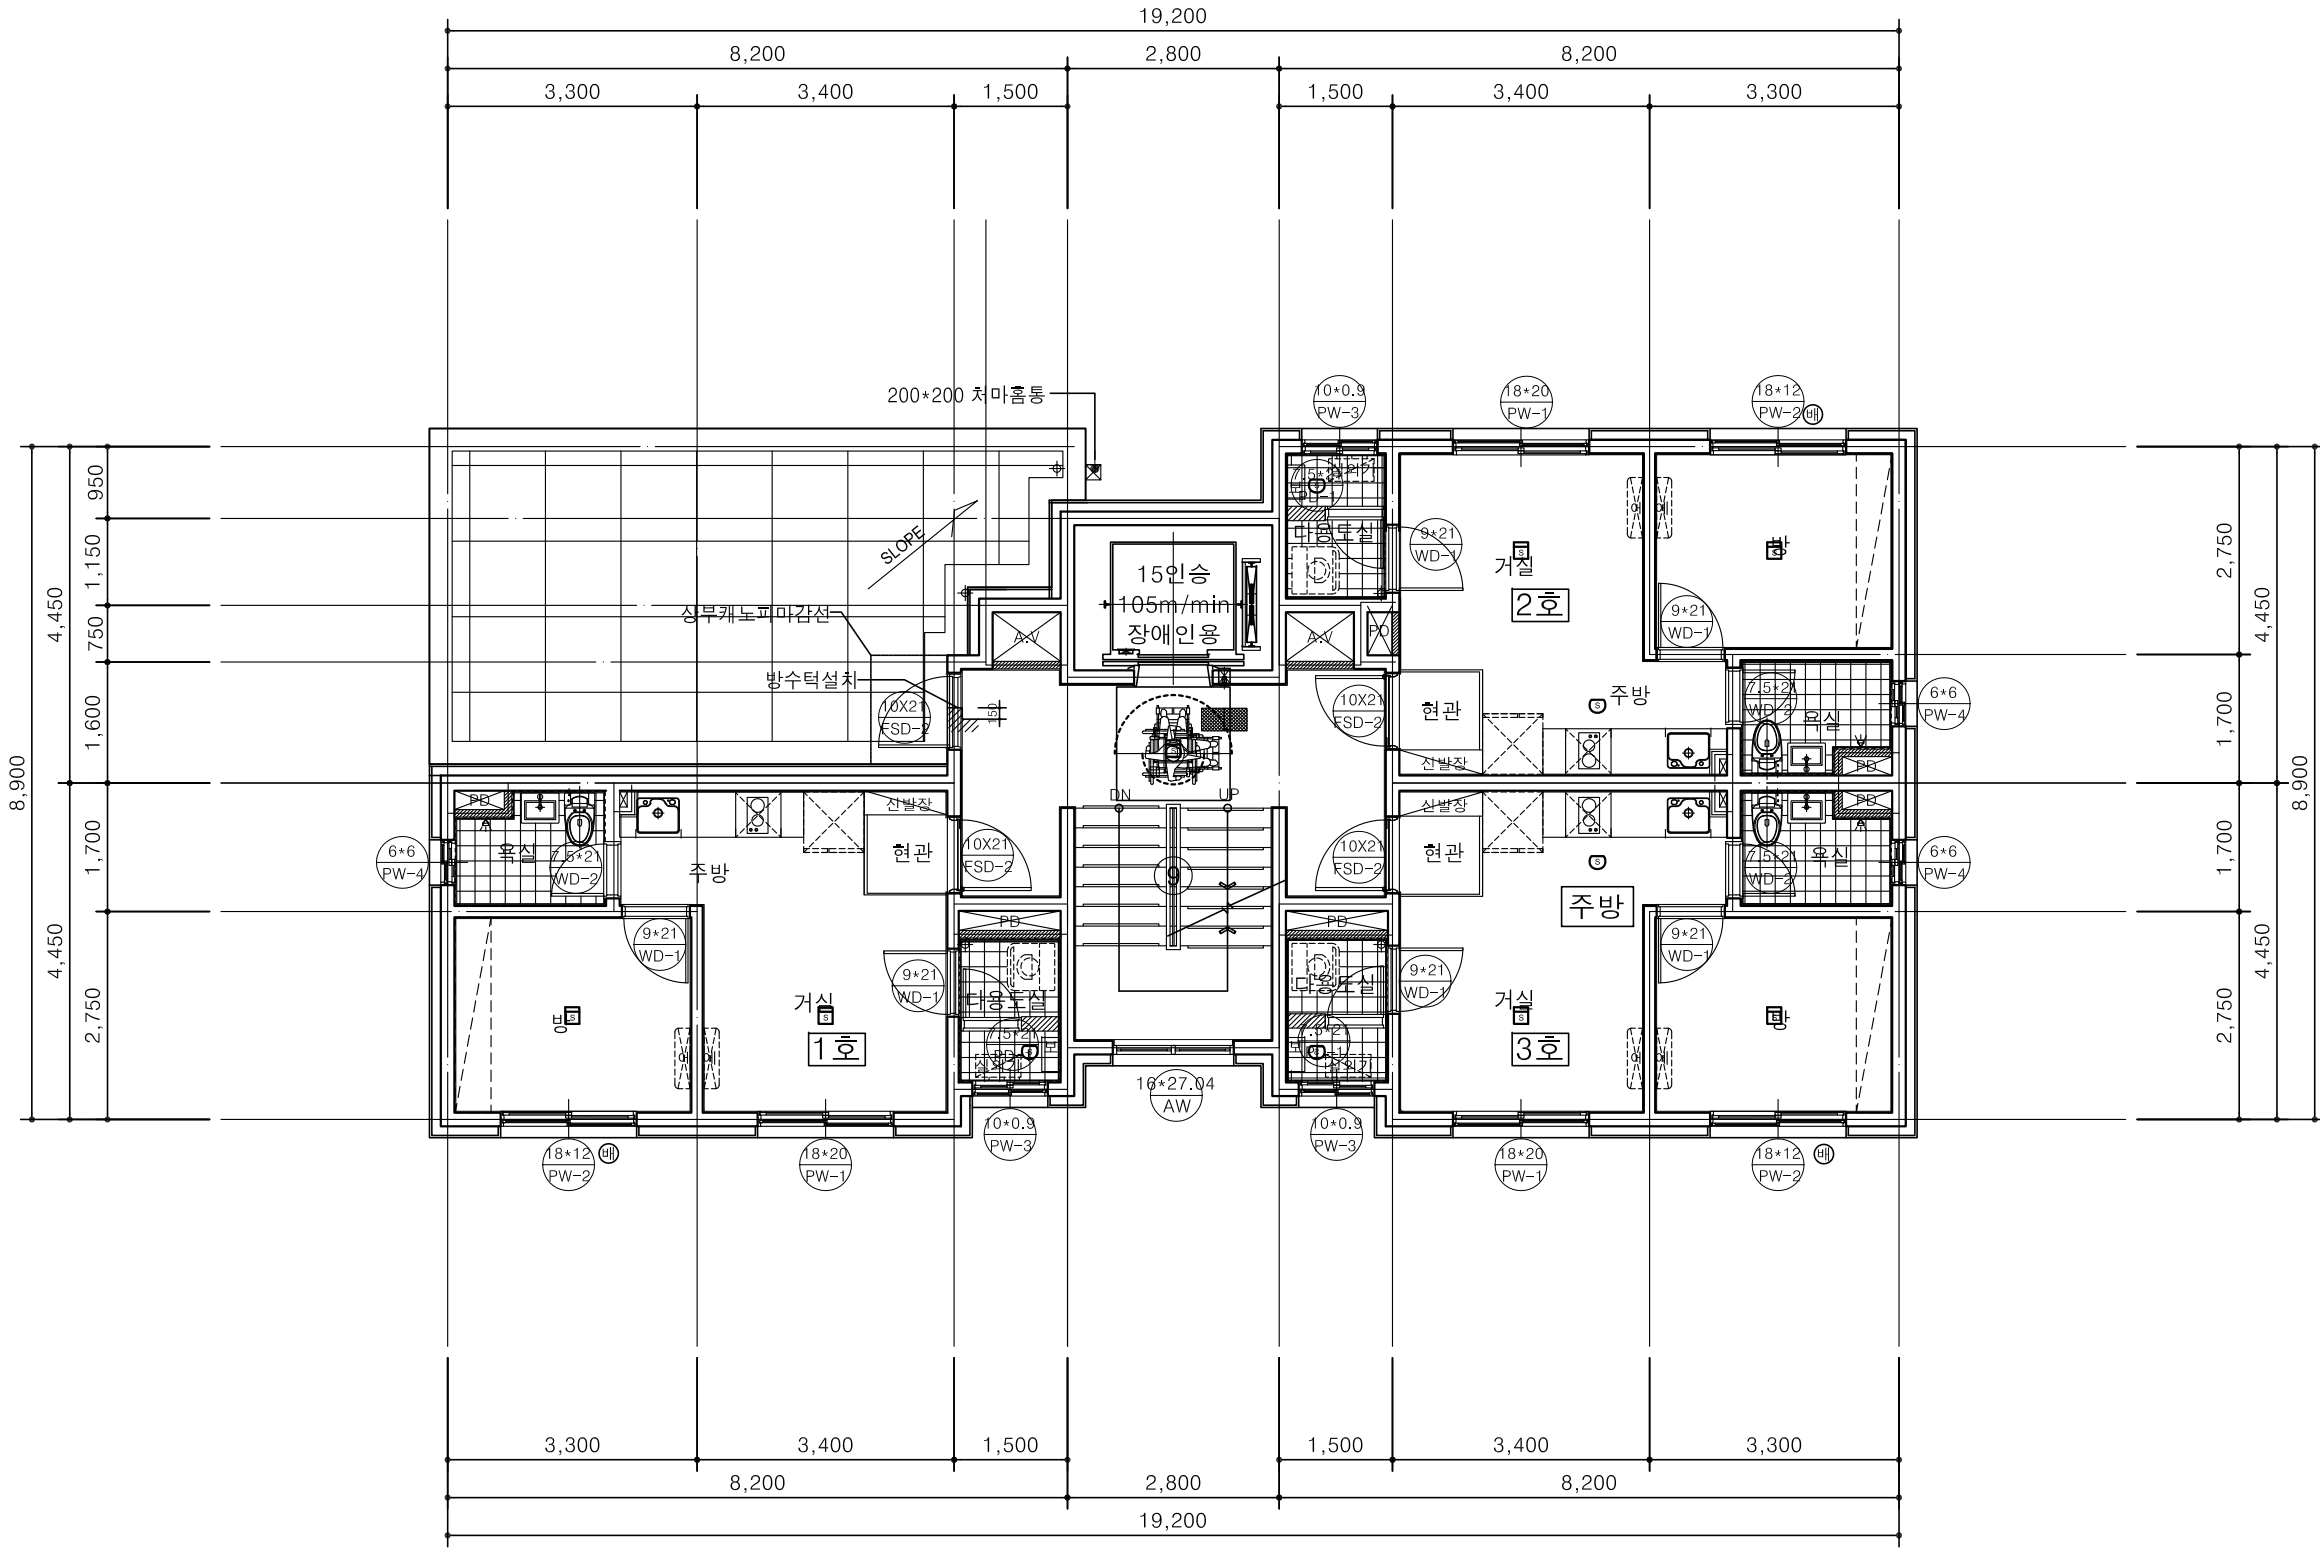

1 102동 9층 동 평 면 도
축척: A3:1/100

PROJECT TITLE 사업명칭	
독산동 1005-3 오피스텔 신축공사	
NAME OF DRAWING 도면명	
102동 9층 동 평 면 도	
NOTE 주 기	
NO. 번호 REVISIONS 수정 DATE 일자	
DESIGNED BY 설계	
CHECKED BY 심사	
APPROVED BY 승인	
CONSULTANTS 협동설계	
SCALE 축척	
DATE 일자	2019. 10
DWG. NO. 도면번호	
SHEET NO. 일련번호	
A-□23	
	
건축사사무소 시그에이 THE ARCHITECTS GROUP TEL. 02.541.5516 FAX. 02.512.2882	

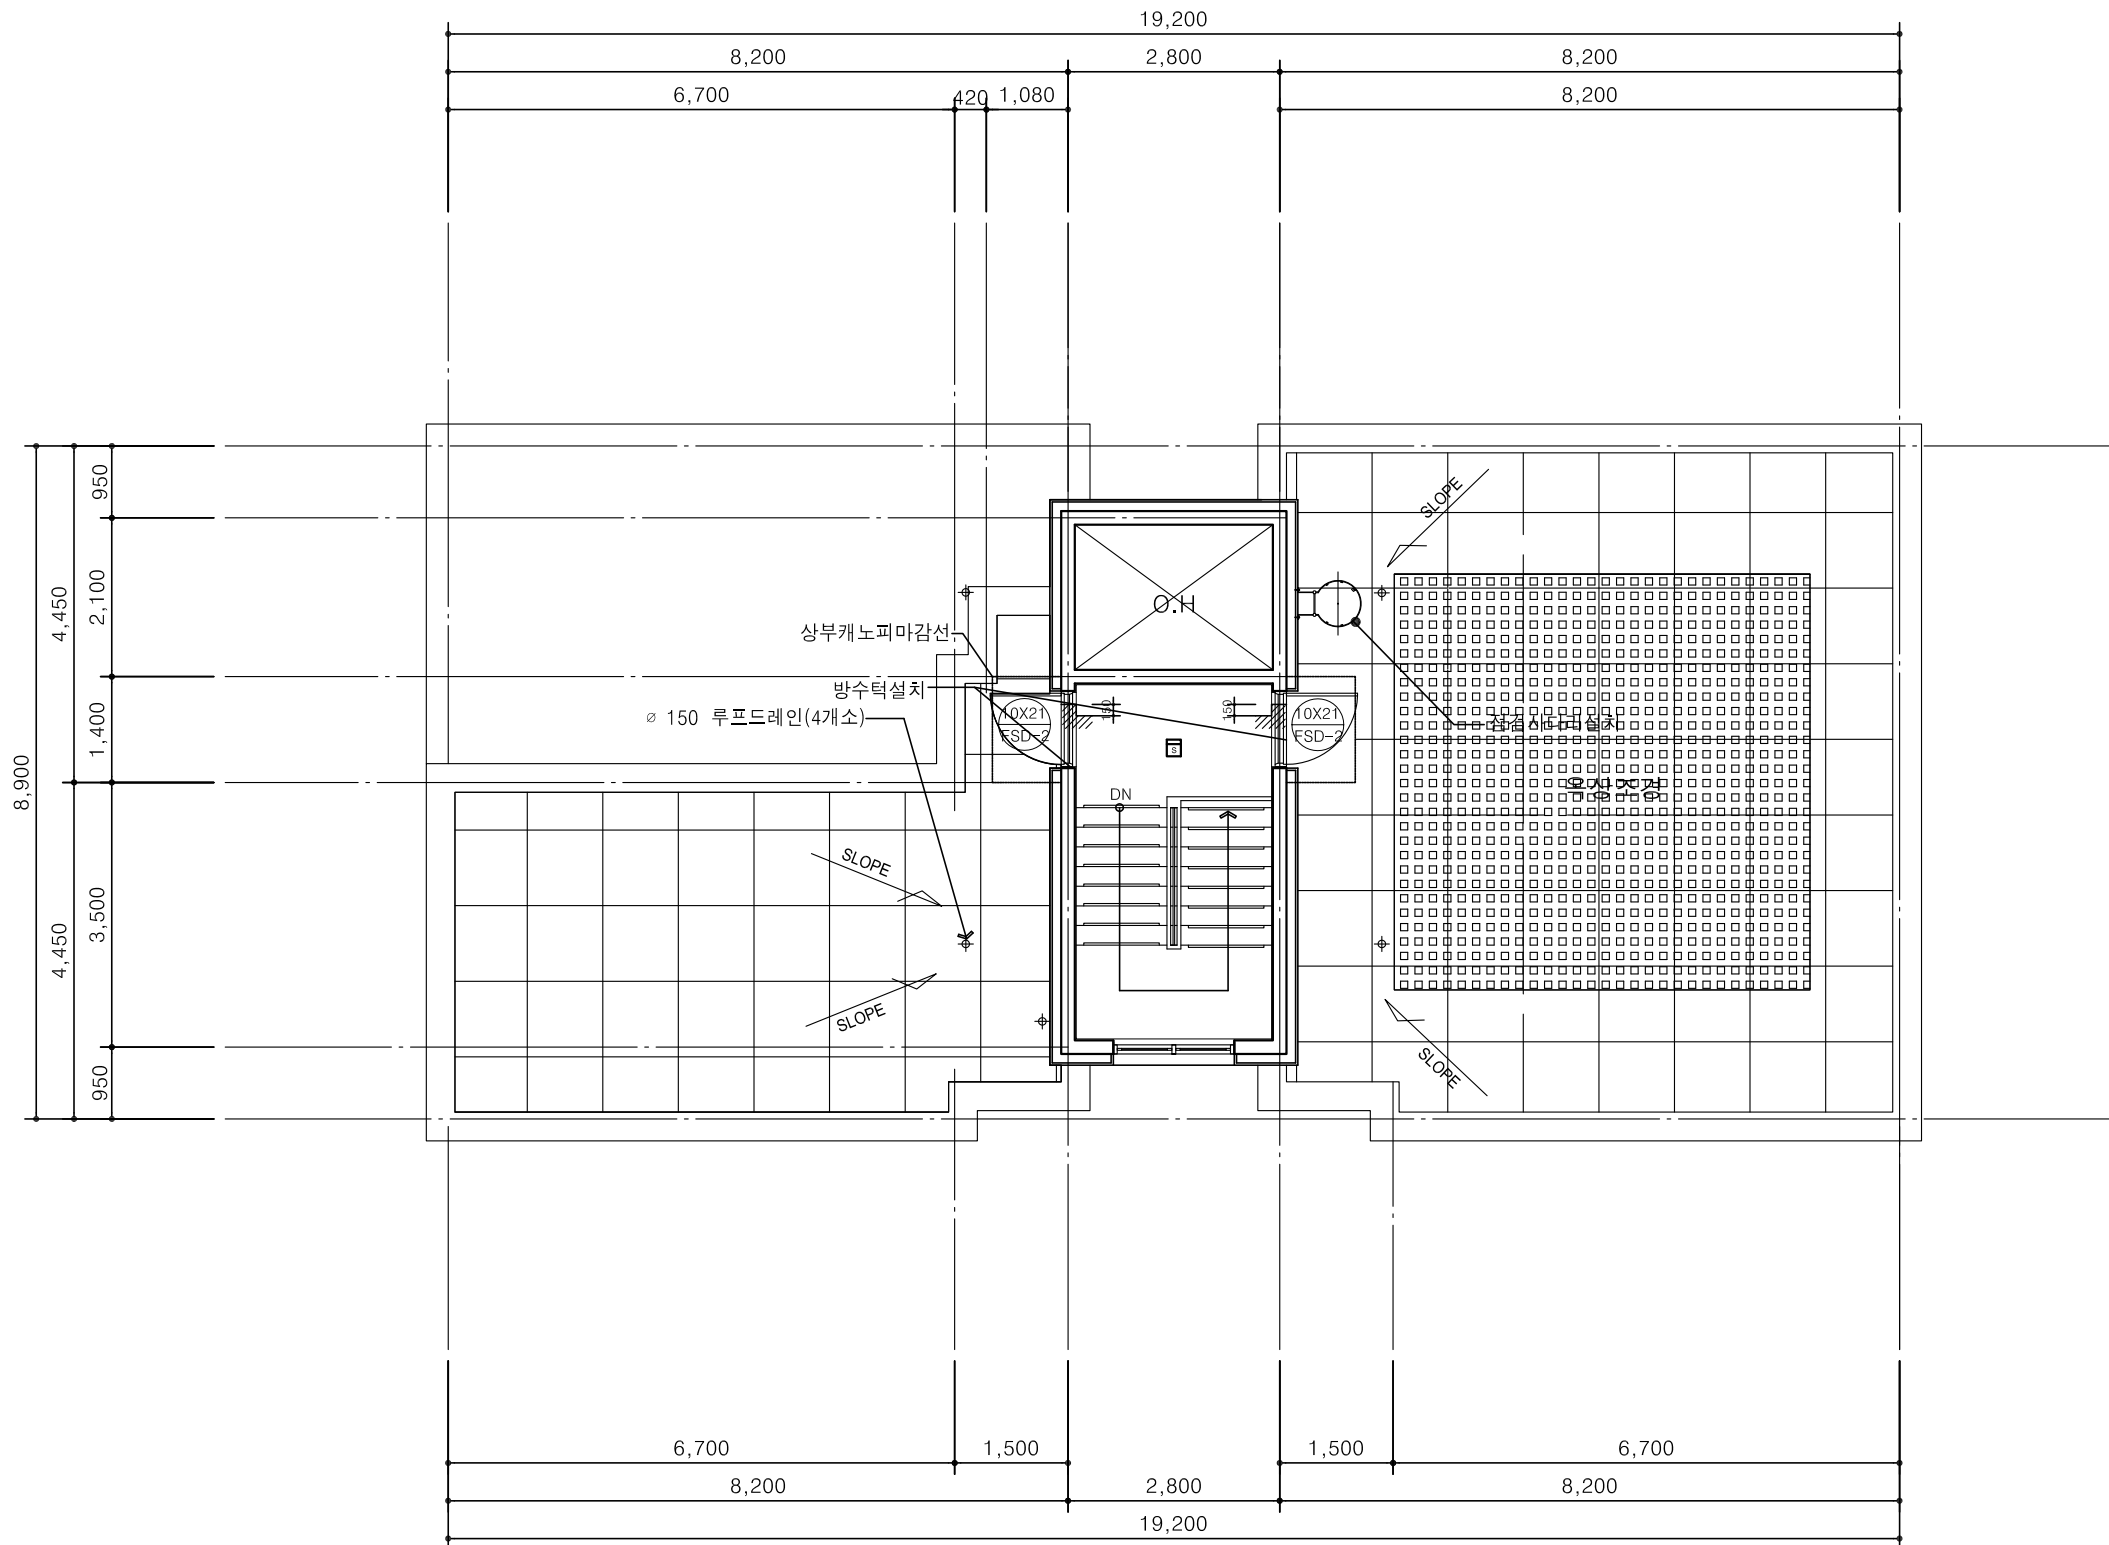

1 102동 옥탑층 동 평 면 도
축척: A3:1/100

PROJECT TITLE
사업명칭

독산동 1005-3 오피스텔
신축공사

NAME OF DRAWING
도면명

102동 옥탑층 동 평 면 도

NOTE
주 기

NO. ▲ REVISIONS ▲ DATE
번호 수정 일자

DESIGNED BY
설 계

CHECKED BY
심 사

APPROVED BY
승 인

CONSULTANTS
협 동 설 계

SCALE
축 척

DATE
일 자 2019. 10


DWG. NO.
도면 번호

SHEET NO.
일련 번호

A-24

sig.A

건축사사무소 시그에이
THE ARCHITECTS GROUP
TEL. 02.541.5516
FAX. 02.512.2882

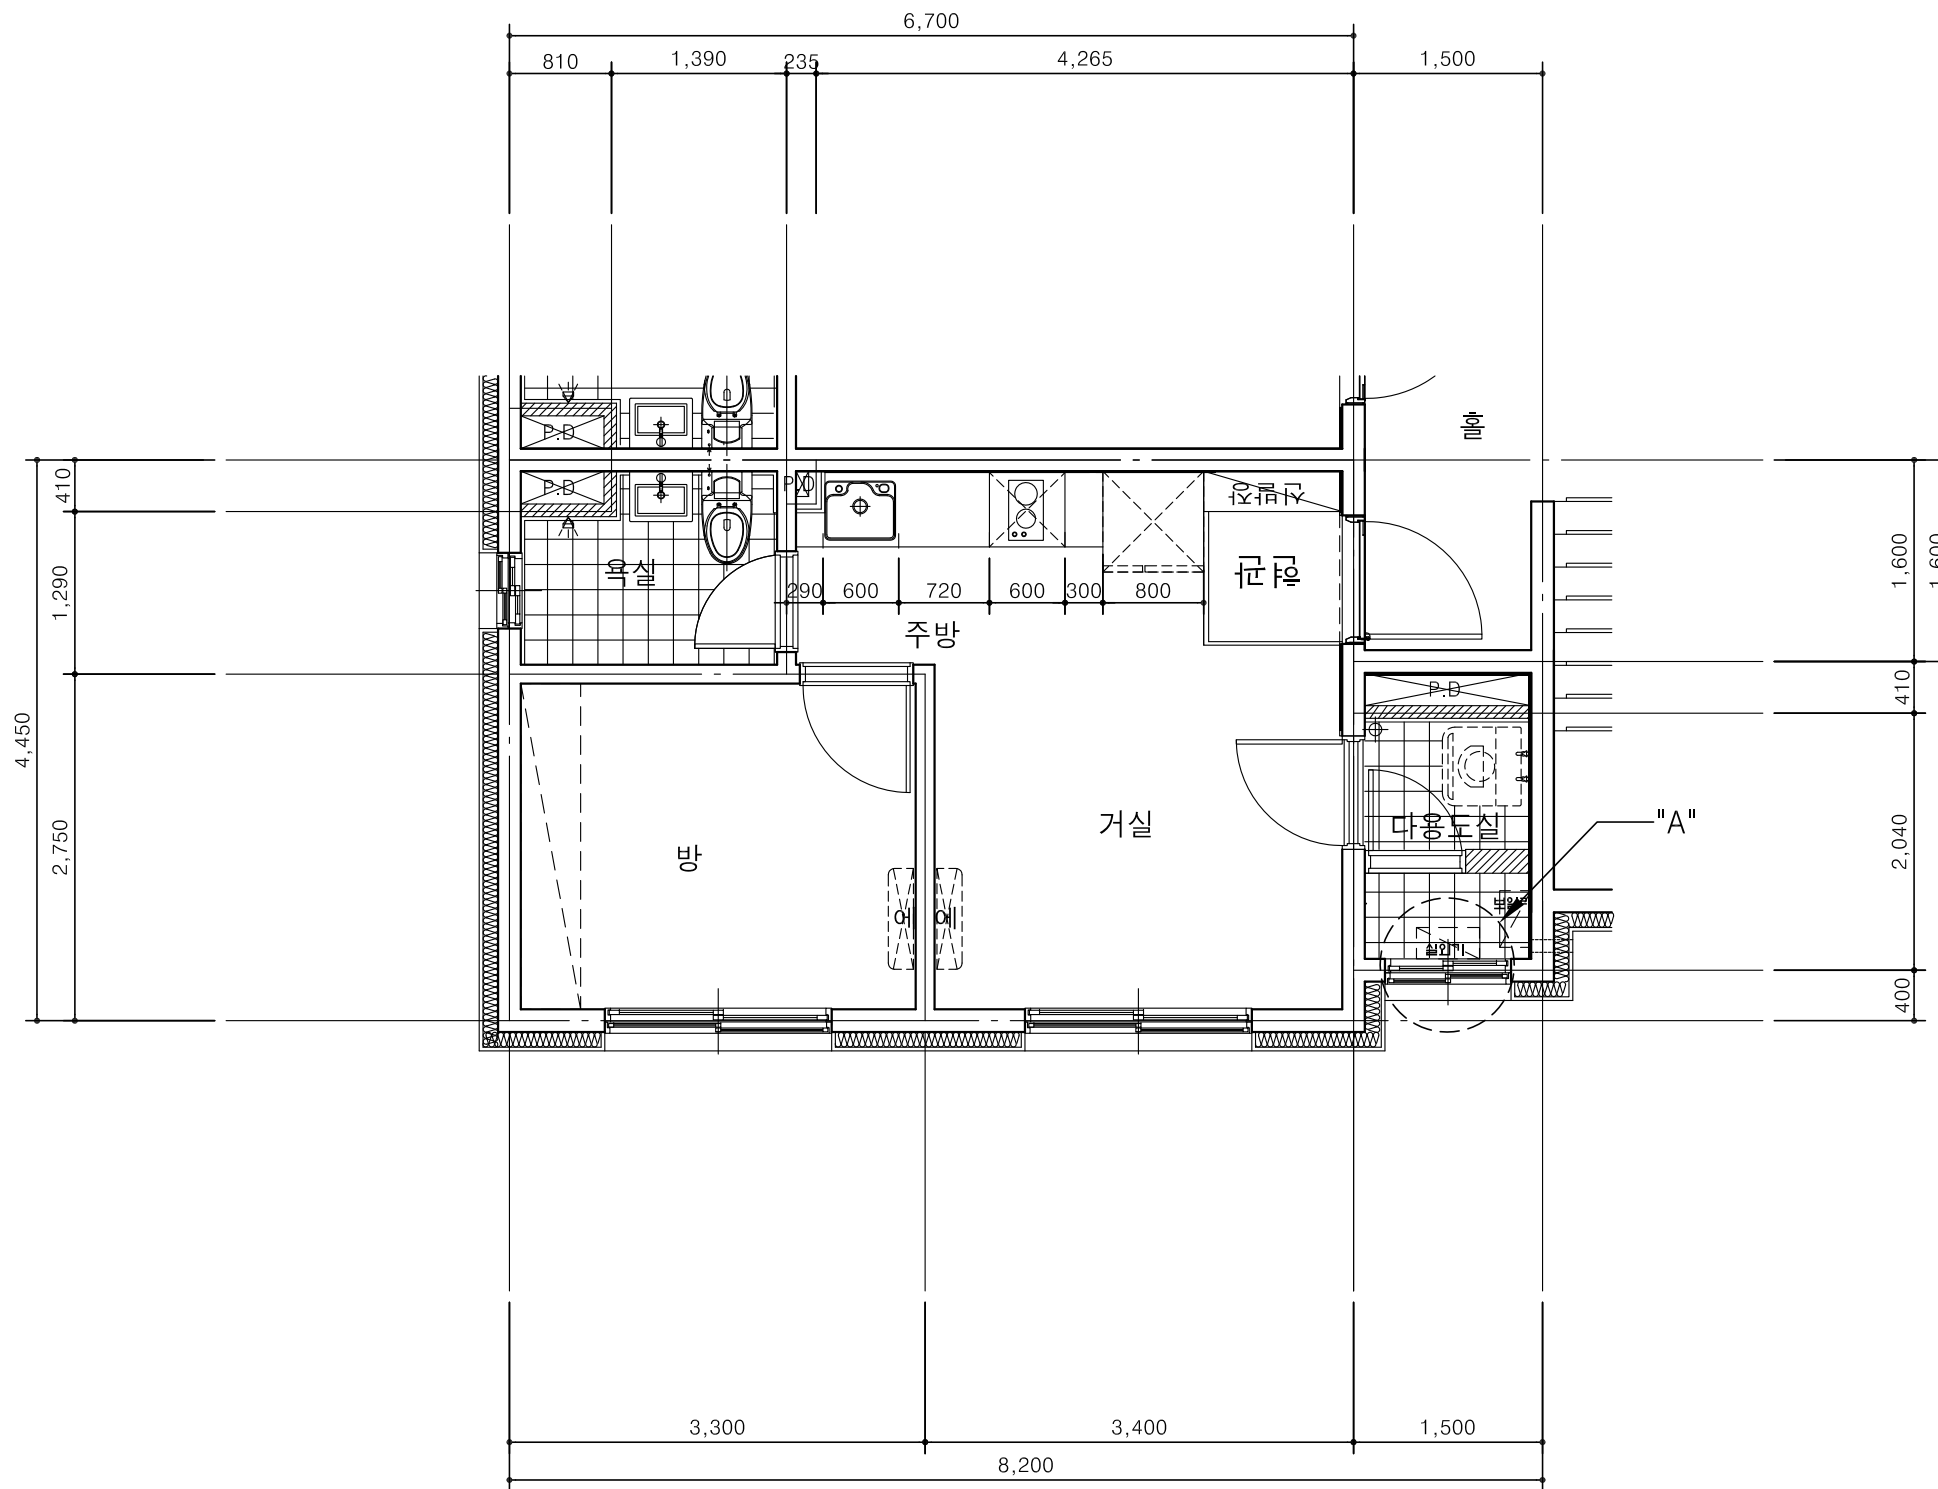


■ "A"상세도


<다용도실내부설외기설치상세>
(전동 적용)

PROJECT TITLE 사업명칭	
독산동 1005-3 오피스텔 신축공사	
NAME OF DRAWING 도면명	
A-TYPE 단위세대 평면도	
NOTE 주 기	
▼ ▼	
NO. ▲ REVISIONS ▲ DATE 번호 수정 일자	
DESIGNED BY 설 계	
CHECKED BY 심 사	
APPROVED BY 승 인	
CONSULTANTS 협 동 설 계	
SCALE 축 척	
DATE 일 자 2019. 10	
DWG NO. 도면 번호	
SHEET NO. 일련 번호 A-□25	
건축사사무소 시그에이 THE ARCHITECTS GROUP TEL. 02.541.5516 FAX. 02.512.2882	

1 A-TYPE 단위세대 평면도
축척: A3:1/60

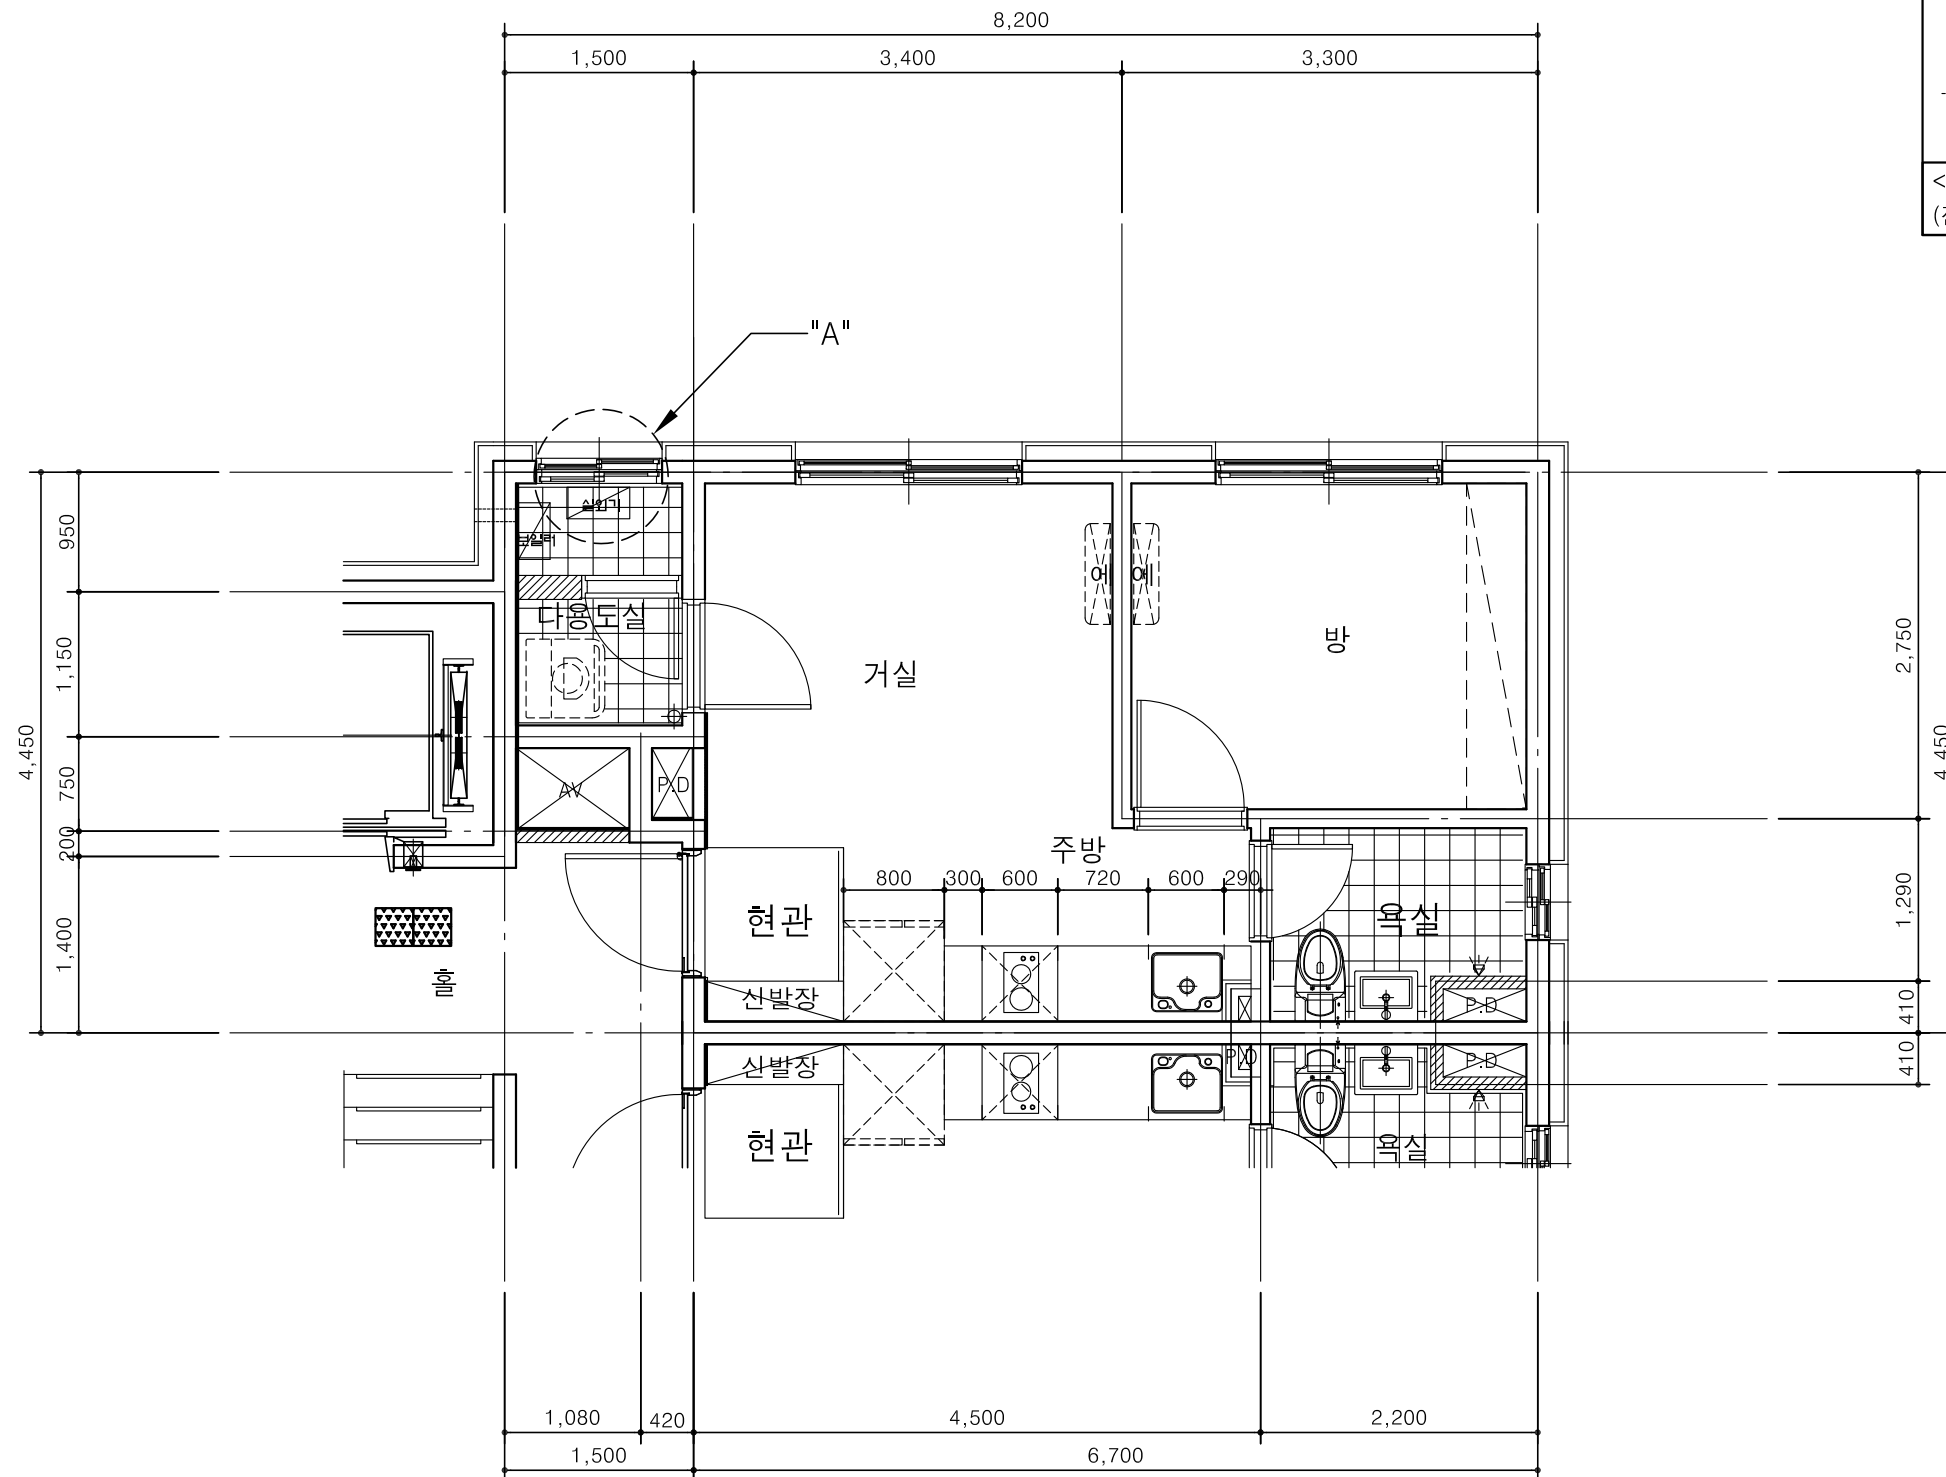

■ "A"상세도

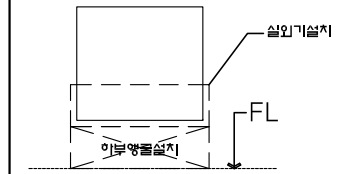

<다용도실내부설외기설치상세>
(전동 적용)

PROJECT TITLE
사업명칭

독산동 1005-3 오피스텔
신축공사

NAME OF DRAWING
도면명

B-TYPE 단위세대 평면도

NOTE
주 기

NO. ▲ REVISIONS ▲ DATE
번호 수정 일자

DESIGNED BY
설 계

CHECKED BY
심 사

APPROVED BY
승 인

CONSULTANTS
협 동 설 계

SCALE
축 척

DATE
일 차 2019. 10

DWG. NO.
도면 번호

SHEET NO.
일련 번호

A-□2□6


sig.A

건축사사무소 시그에이
THE ARCHITECTS GROUP
TEL. 02.541.5516
FAX. 02.512.2882


1

B-TYPE 단위세대 평면도

축척: A3:1/60

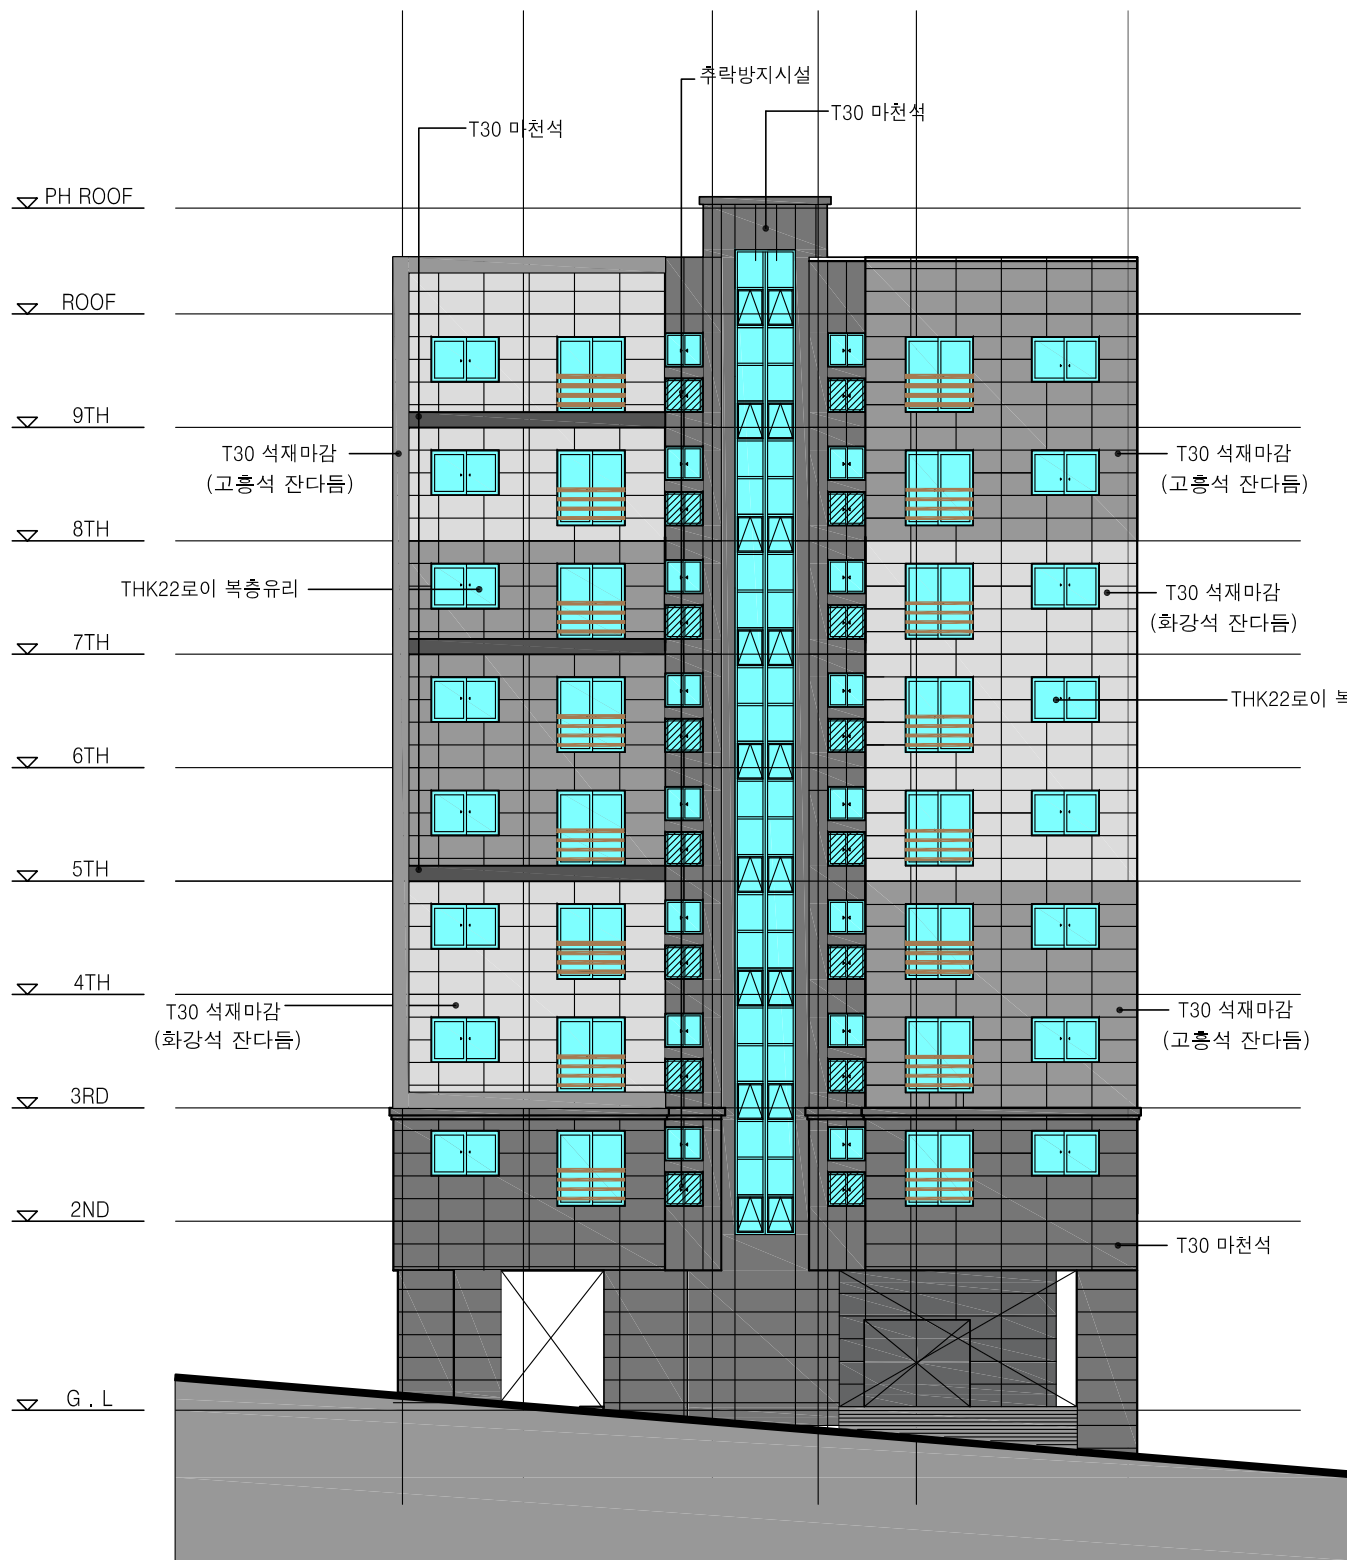

① 정 면 도
축척 : A3:1/200

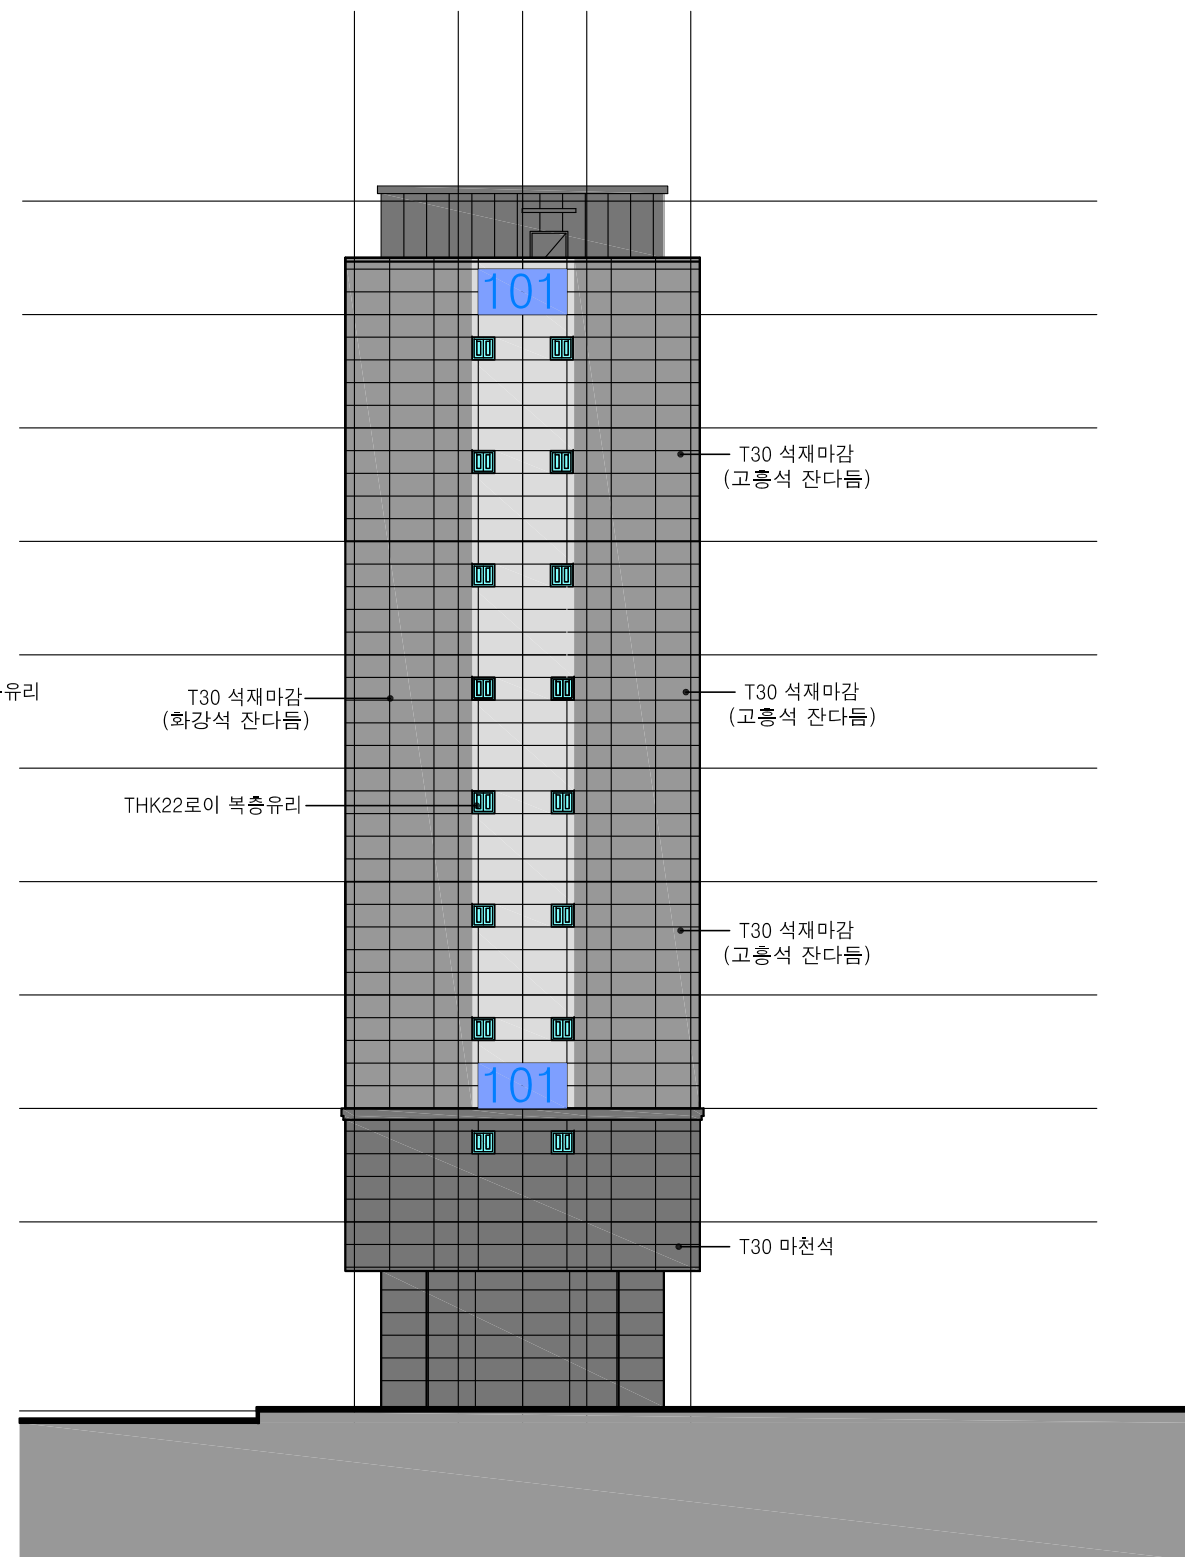

① 우 측 면 도
축척 : A3:1/200

PROJECT TITLE
사업명칭

독산동 1005-3 오피스텔
신축공사

NAME OF DRAWING
도면명

101동 정,우측면도

NOTE
주 기

NO. ▲ REVISIONS ▲ DATE
번호 수정 일자

DESIGNED BY
설 계

CHECKED BY
심 사

APPROVED BY
승 인

CONSULTANTS
협동설계

SCALE 축척 60

DATE 일자 2019. 10


DWG. NO.
도면번호

SHEET NO.
일련번호

A-□27

sig.A

건축사사무소 시그에이
THE ARCHITECTS GROUP
TEL. 02.541.5516
FAX. 02.512.2882

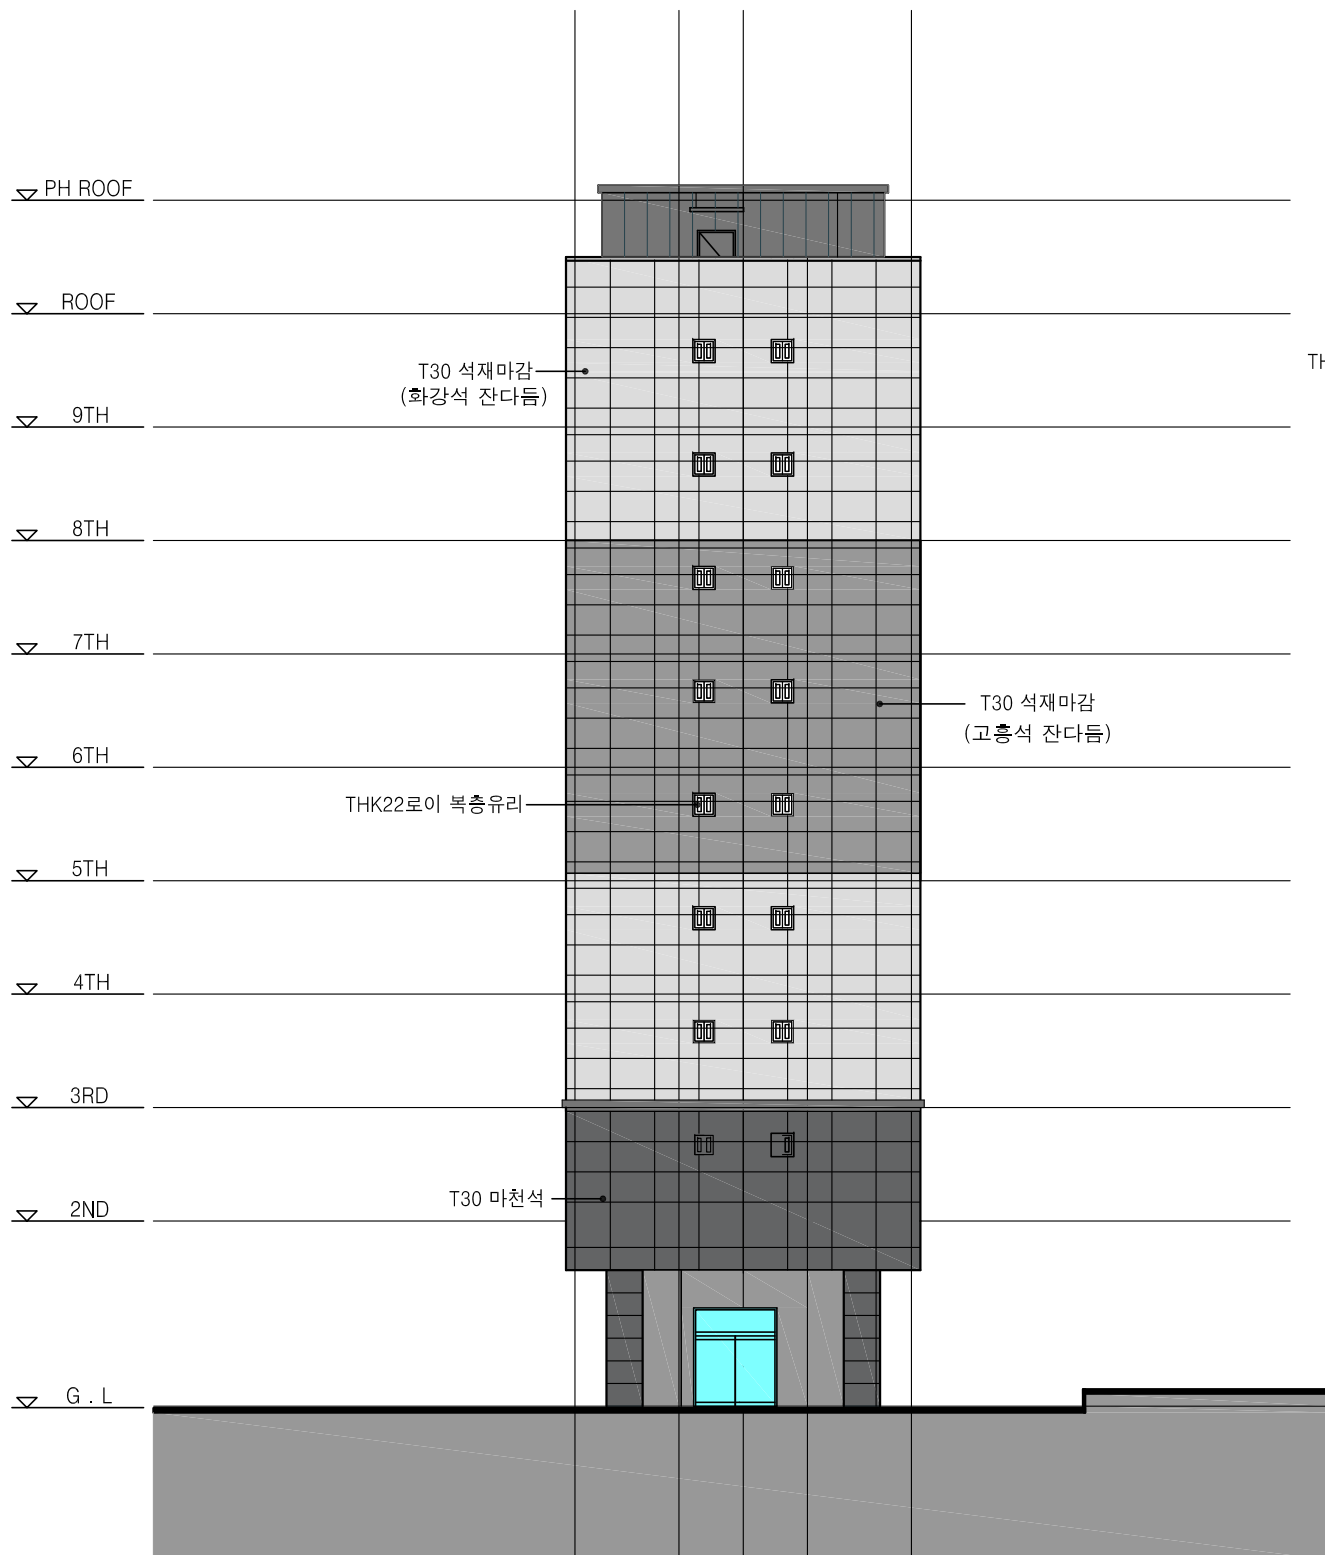

① 좌측면도
축척 : A3:1/200



② 배면도
축척 : A3:1/200

PROJECT TITLE
사업명칭
독산동 1005-3 오피스텔
신축공사

NAME OF DRAWING
도면명
101동 배,좌측면도

NOTE
주 기
▼ ▼

NO. ▲ REVISIONS ▲ DATE
번호 수정 일자

DESIGNED BY
설 계

CHECKED BY
심 사

APPROVED BY
승 인

CONSULTANTS
협 동 설 계

SCALE
축 척 60

DATE
일 자 2019. 10

DWG. NO.
도면 번호


SHEET NO.
일련 번호 A-□28

sig.A

건축사사무소 시그에이
THE ARCHITECTS GROUP
TEL. 02.541.5516
FAX. 02.512.2882



① 정 면 도
축척 : A3:1/200

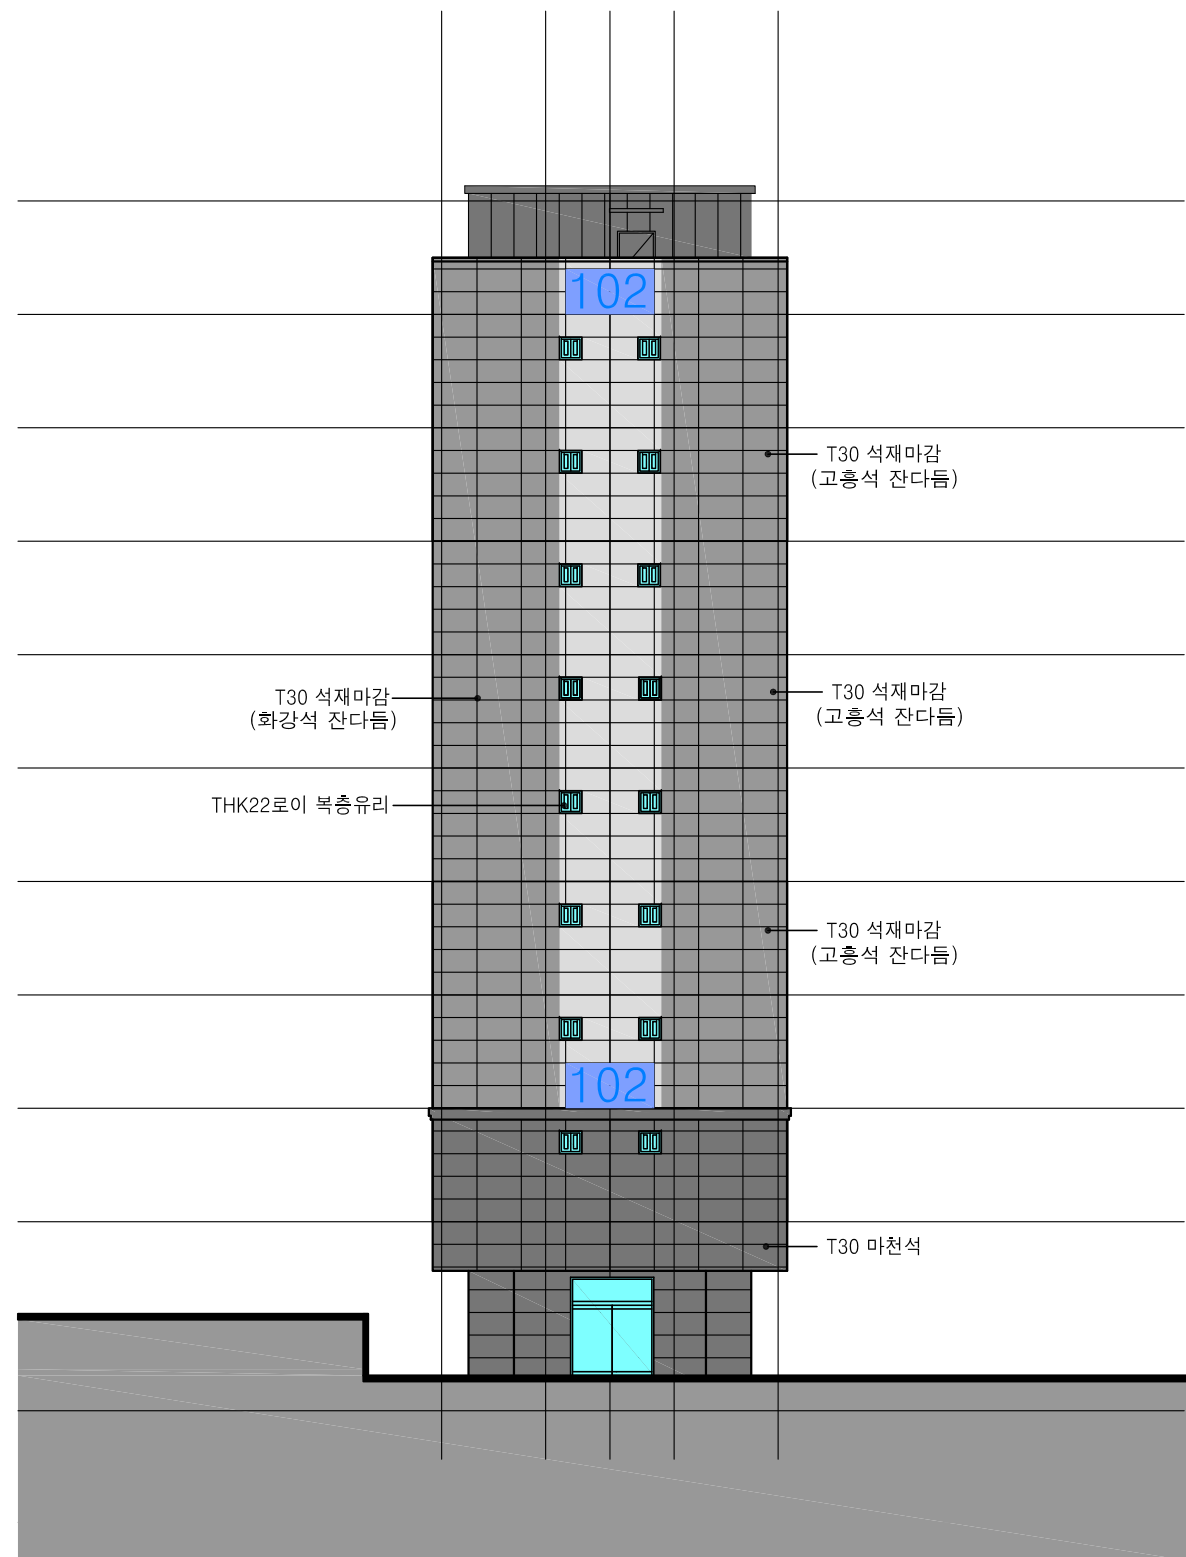

① 우 측 면 도
축척 : A3:1/200

PROJECT TITLE
사업명칭

독산동 1005-3 오피스텔
신축공사

NAME OF DRAWING
도면명

102동 정,우측면도

NOTE
주 기

NO. ▲ REVISIONS 수 정 DATE
번호 ▲ 일자

DESIGNED BY
설 계

CHECKED BY
심 사

APPROVED BY
승 인

CONSULTANTS
협동설계

SCALE 축척 60


DATE 일자 2019. 10

DWG. NO.
도면번호

SHEET NO.
일련번호 A-□29

sig.A

건축사사무소 시그에이
THE ARCHITECTS GROUP
TEL. 02.541.5516
FAX. 02.512.2882

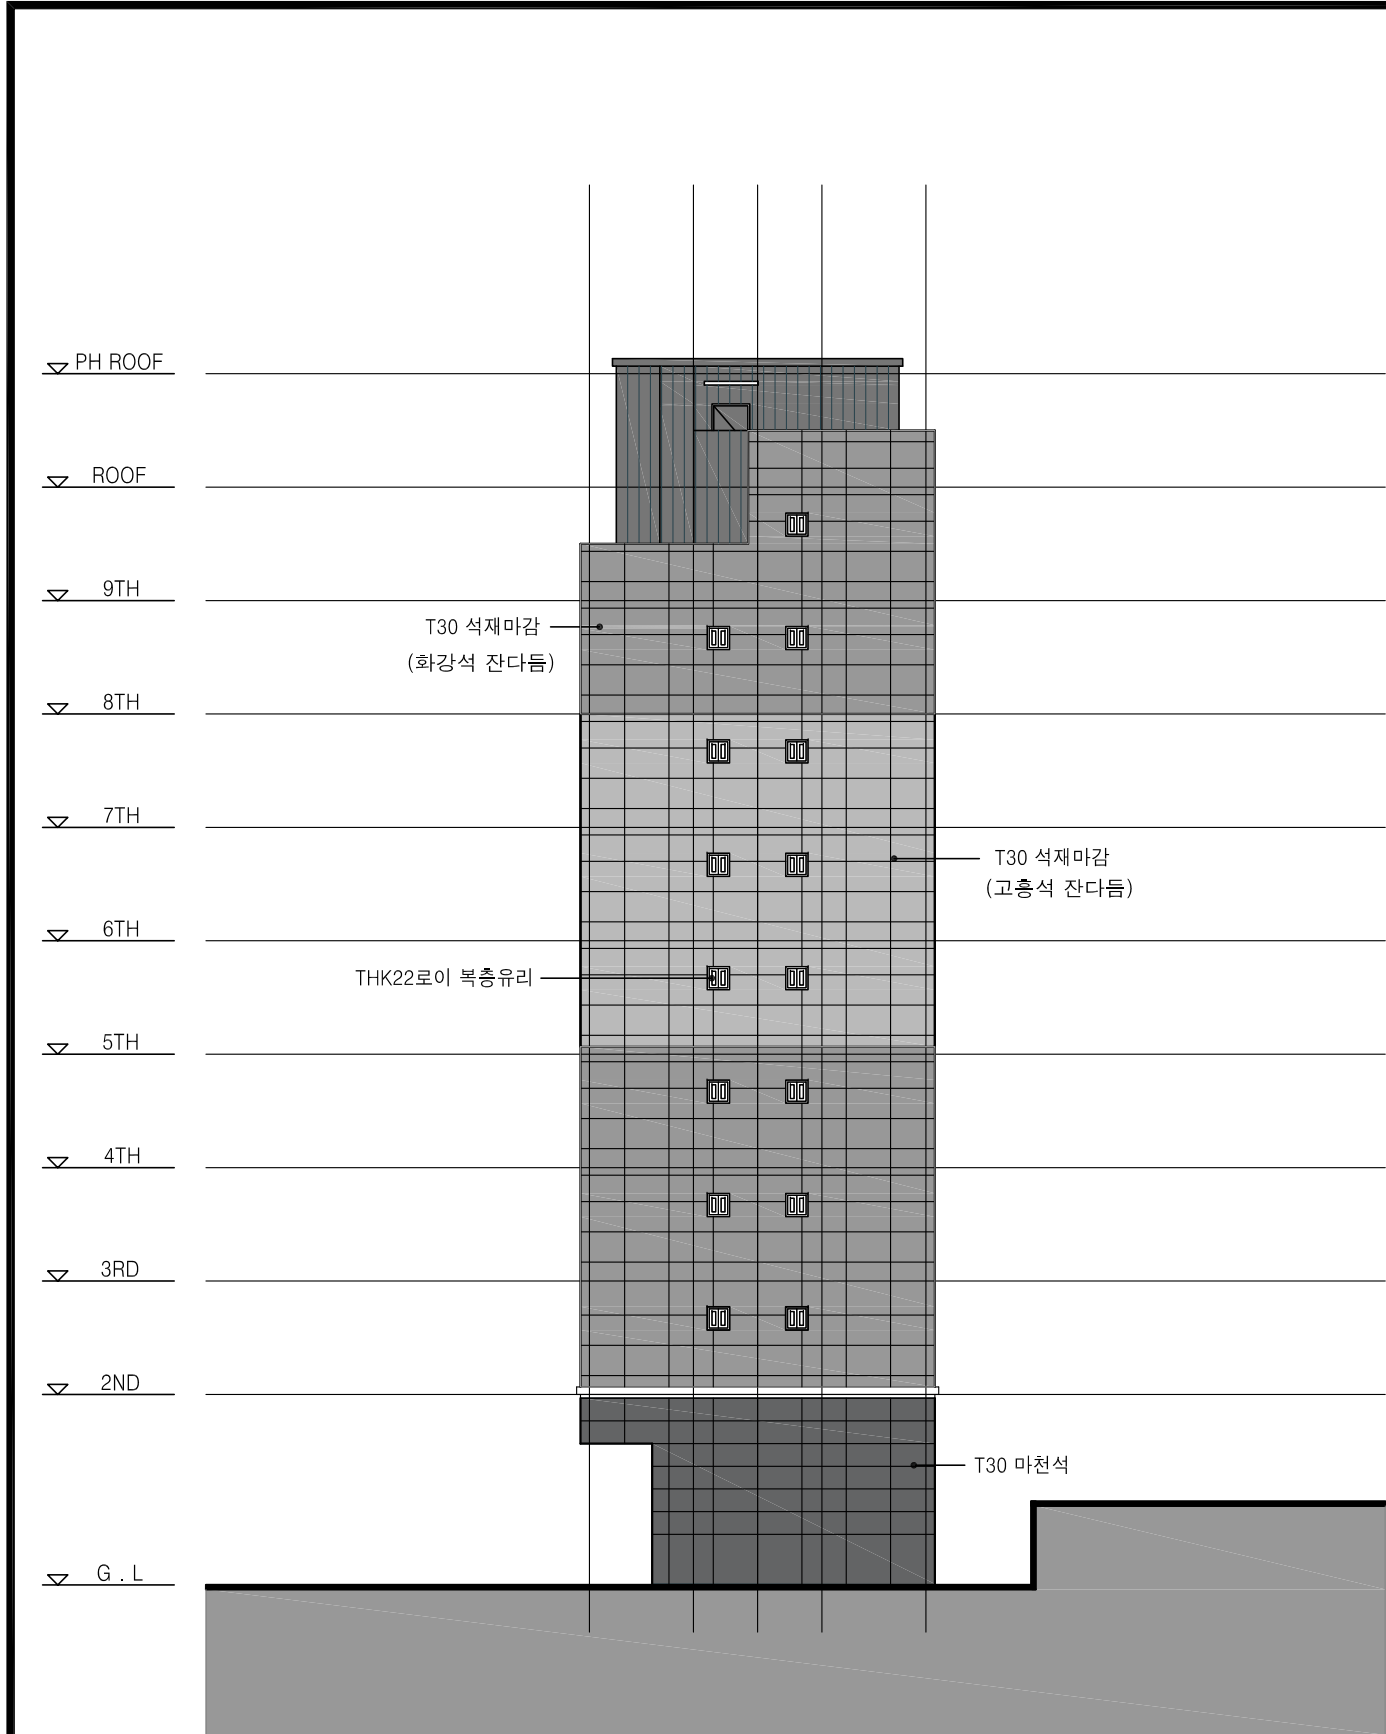

① 좌측면도
축척 : A3:1/200



② 배면도
축척 : A3:1/200

PROJECT TITLE
사업명칭

독산동 1005-3 오피스텔
신축공사

NAME OF DRAWING
도면명

102동 배,좌측면도

NOTE
주 기

▼ ▼

NO. ▲ REVISIONS ▲ DATE
번호 수정 일자

DESIGNED BY
설 계

CHECKED BY
심 사

APPROVED BY
승 인

CONSULTANTS
협동설계

SCALE
축척 60

DATE
일자 2019. 10

DWG. NO.
도면번호

SHEET NO.
일련번호

A-30

sig.A
건축사사무소 시그에이
THE ARCHITECTS GROUP
TEL. 02.541.5516
FAX. 02.512.2882