


1. 투 시 도 	2. 건 축 개 요 건 축 개 요 - 설 계 명 : 시흥동 공동주택(다세대주택) 신축공사 - 대 지 위 치 : 서울특별시 금천구 시흥동 220-116번지 외 2필지 - 지 역 · 지 구 : 제2종일반주거지역 - 건 물 용 도 : 공동주택 (다세대주택 - 원룸형) - 건 물 규 모 : 지상 5층 4.0M이상 도로에 약 17.25M 접합 - 대 지 면 적 : 377.16 m² - 건 축 면 적 : 220.73 m² - 연 면 적 : 658.74 m² - 건 폐 율 : 58.52 % - 용 적 륜 : 174.66 % - 최 고 높 이 : 14.80 M - 건 물 구 조 : 철근콘크리트구조 - 주 차 대 수 : 8대 설치 - 조 경 면 적 : 29.47 m² (7.81%)
---	---

3. 입 면 도  동측면도	 서측면도	 남측면도	 북측면도
■ 동측면도	■ 서측면도	■ 남측면도	■ 북측면도

 (株)明珍플러스 建築士事務所 ARCHITECTS & ENGINEERS TEL:2667-2588 FAX:866-5068	NO	DATE	REVISION DESCRIPTION	DRWN	CHK'D	APPR	PROJECT TITLE 공사명 금천구 시흥동 220-32번지 외1필지 다세대주택 신축공사	APPROVE D 	CHK'D BY	SCALE 1 / NONE	DRAWING TITLE 도면명 외관디자인계획도 - 1	S-C-C NO
								DESIGNED BY	DATE 2021. 02.	DRAWN BY		DRAWING NO A-106

※ 본 설계도면은(초상권) 디자인십리시 제출한 심의도면으로서 설계도면과 일부 상이한 합중물이며 설계도면이 우선함.

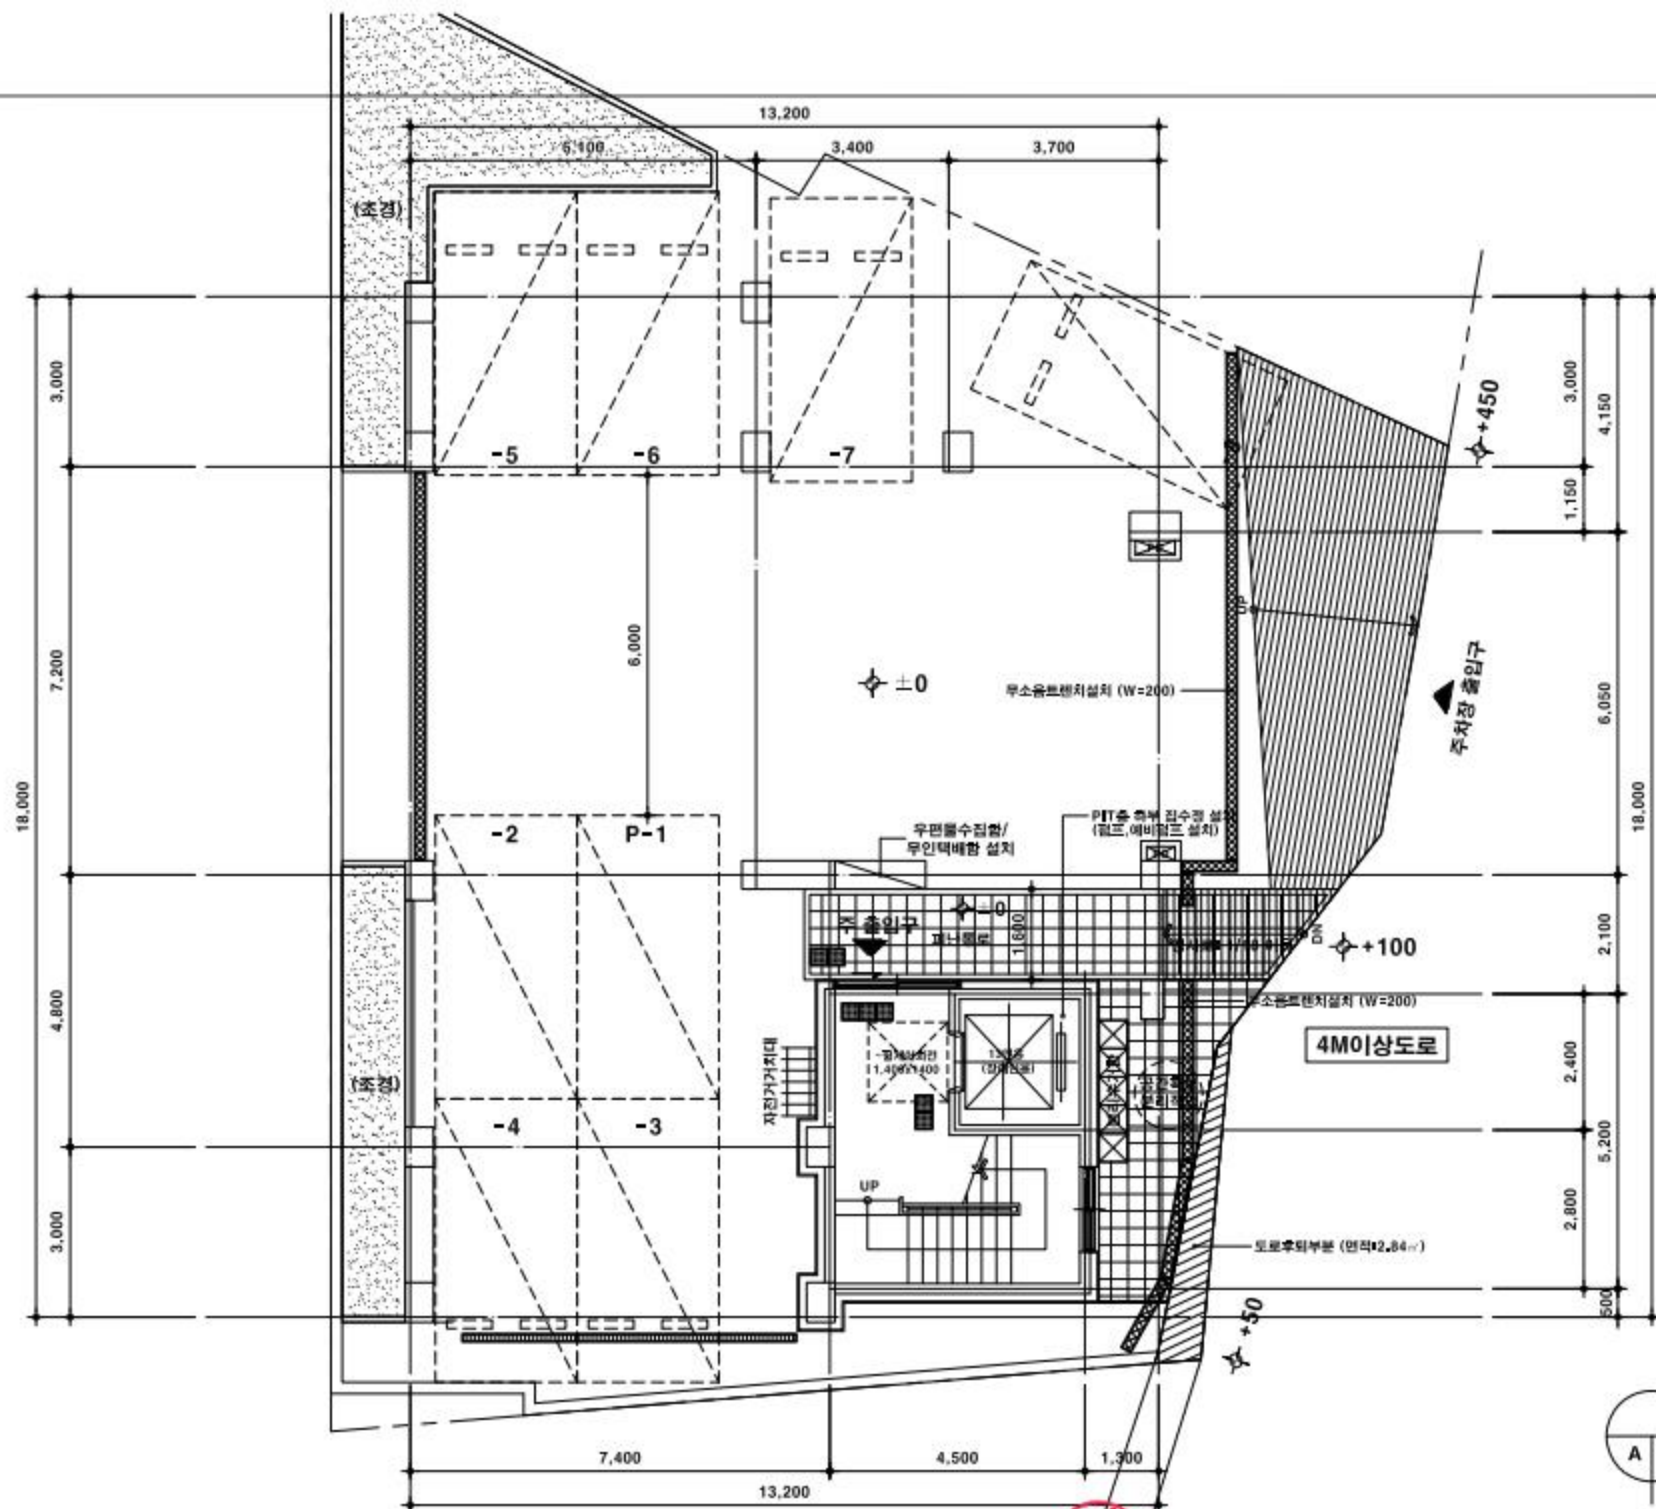

1층 평면도

SCALE: 1 / 100



(株)明珍플러스

TEL:2667-2598
FAX:866-9068

建築士事務所
ARCHITECTS & ENGINEERS

NO	DATE	REVISION DESCRIPTION	DRWN	CHK'D	APPD

PROJECT TITLE
공사명
금천구 시흥동 220-116번지 외 2필지
다세대주택 (원룸) 신축공사

APPROVE
DESIGNED BY

CHK'D BY

SCALE 1 / 100

DATE 2023. 03


DRWN BY

DRAWING TITLE
도면명

1층 평면도

S.C.C NO

DWG NO
A-203

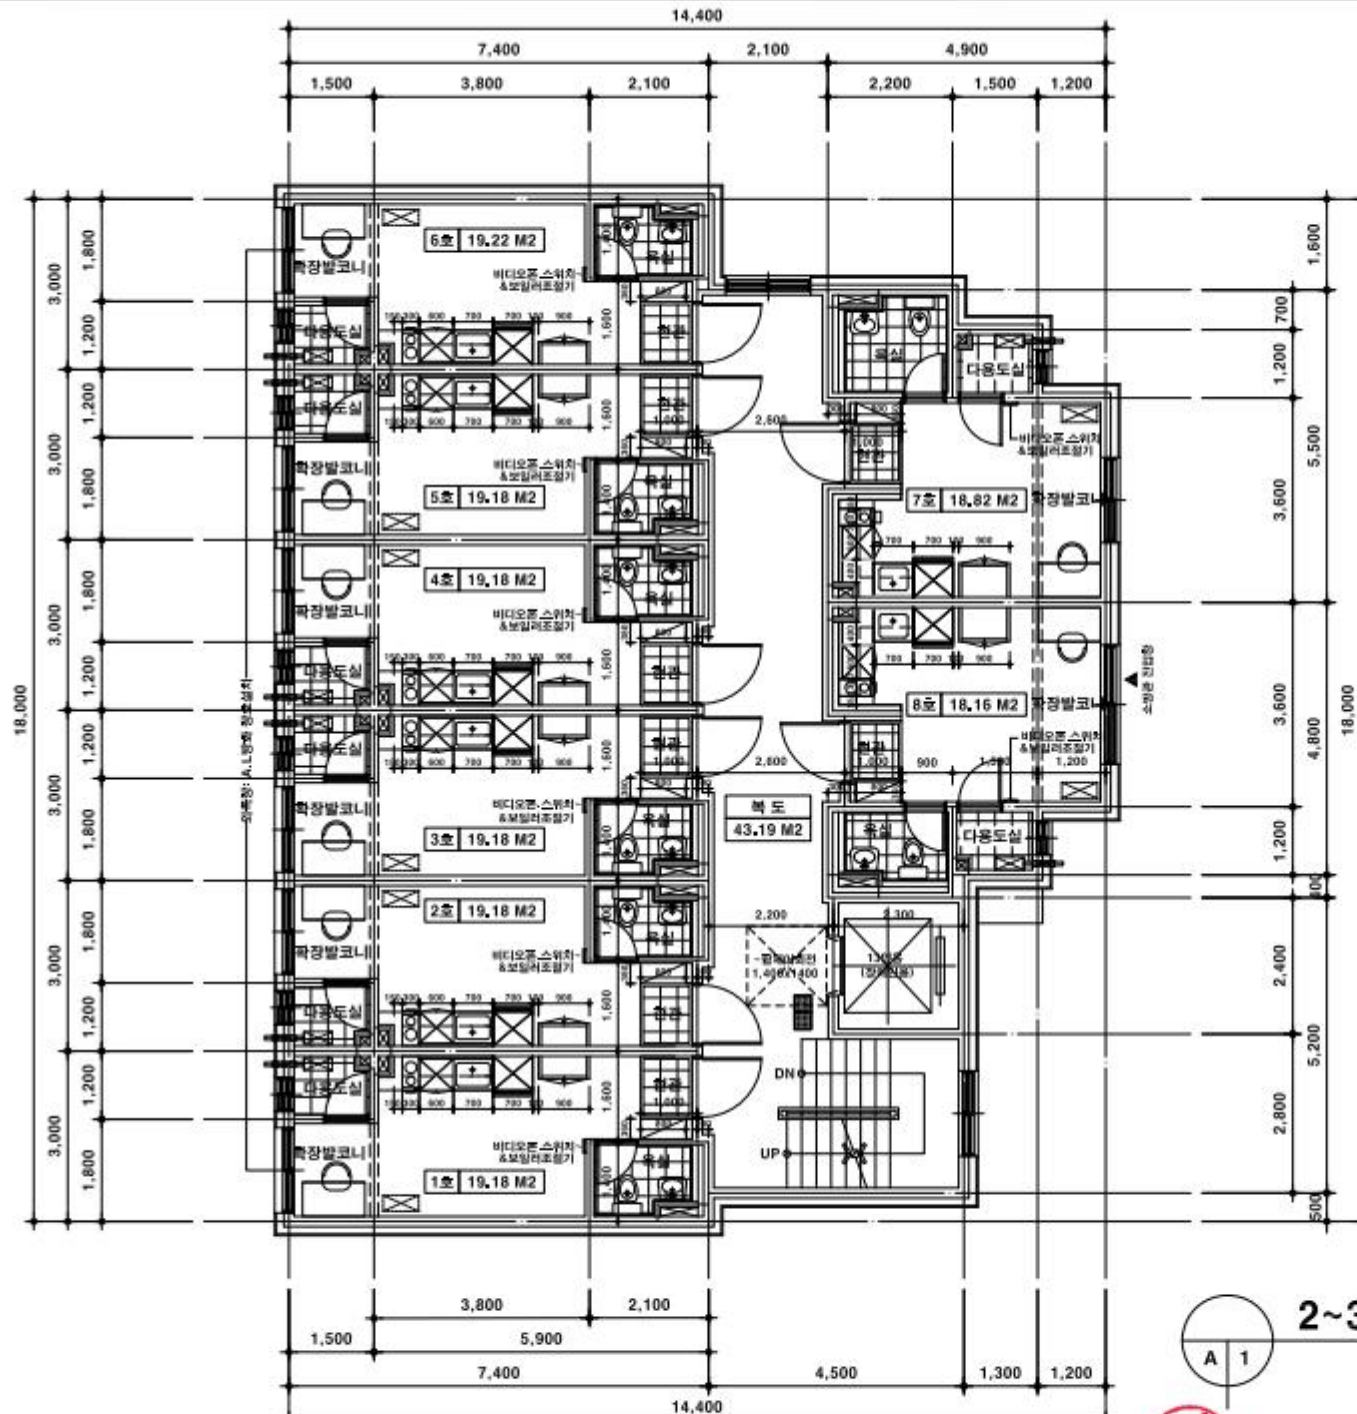

2~3층 평면도

SCALE : 1 / 100

주 기

1 (외부)	주차장내 CCTV, 쓰레기분리수거, 자전거보관대 설치
	우편함 설치 (세대전용, 공용, 반송용, 폐건진지함 구분 설치)
	테라스 창호 PL이중창 설치
	세대 테라스 설치시 세대간 분리벽 계획
	세대 발코니 설치시 차양시설 설치
2 (계단실)	세대 현관문 도어체크 설치
	계단실의 현관과 계단 이격거리 (최소600mm이상)
3 (내부)	세대내 욕실, 휴지걸이 매립형 설치
	콘크리트 골타이 제거 후 마감공사 시공 (방수, 단열재 시공 등)
4 (시공)	욕실 & 다용도실 스위치 : 문 열리는 방향으로 시공
	주차장 차양 진출입구간 무소음트랜치 시공
5 (마감)	-직접외기(외벽)에 면한 실내벽면 단열재
	[아이소핑크(10mm) + 석고보드 마감도면 표기]
	-간접외기(계단실, 복도)에 면한 실내벽면 단열재
	[경질우레탄폼(100mm) + 석고보드 마감도면 표기]
구 분	*기타 실내 벽면 시멘트 마감 마감
	철근 : fy=400Mpa
	콘크리트 : fck=24Mpa
	스라브두께 : 210mm (복배근)
	외벽두께 : 180mm (복배근)
전 기	코아벽두께 : 180mm (복배근)
	세대간벽두께 : 180mm (복배근)
	내벽두께 : 150mm (복배근)
	-콘센트 설치 (바닥 마감선 기준)
	[거실] 스탠드형 에어컨 : 350
비 고	[안방] 벽걸이형 에어컨 : 1900
	[화장실] 양변기 높 : 900
	[주방] 조리대 : 중앙 / 냉장고 : 350 / 후드 : 2100
	-비디오폰(VP), 보일러온도조절기(B), 스위치(S) 설치 (거실 아르를 위치)
	-위치 표기
비 고	에어컨 설치기
	에어컨 콘센트
	냉매, 배수관 (배수관수직매립)
	세대현관문
	## 규격"를"포함 : 1100X2200



(株)明珍플러스

TEL:2667-2588 FAX:266-9058
建築士事務所
ARCHITECTS & ENGINEERS

NO	DATE	REVISION DESCRIPTION	DRWN	CHK'D	APP'D

PROJECT TITLE
공 사 명
금천구 시흥동 220-116번지 외 2필지
다세대주택 (원룸) 신축공사


APPROVE	CHK'D BY
DESIGNED BY	

SCALE	1 / 100
DATE	2023. 03
DRWN BY	

DRAWING TITLE
도 면 명
2~3층 평면도

S.C.D NO

DSNG NO
A-204

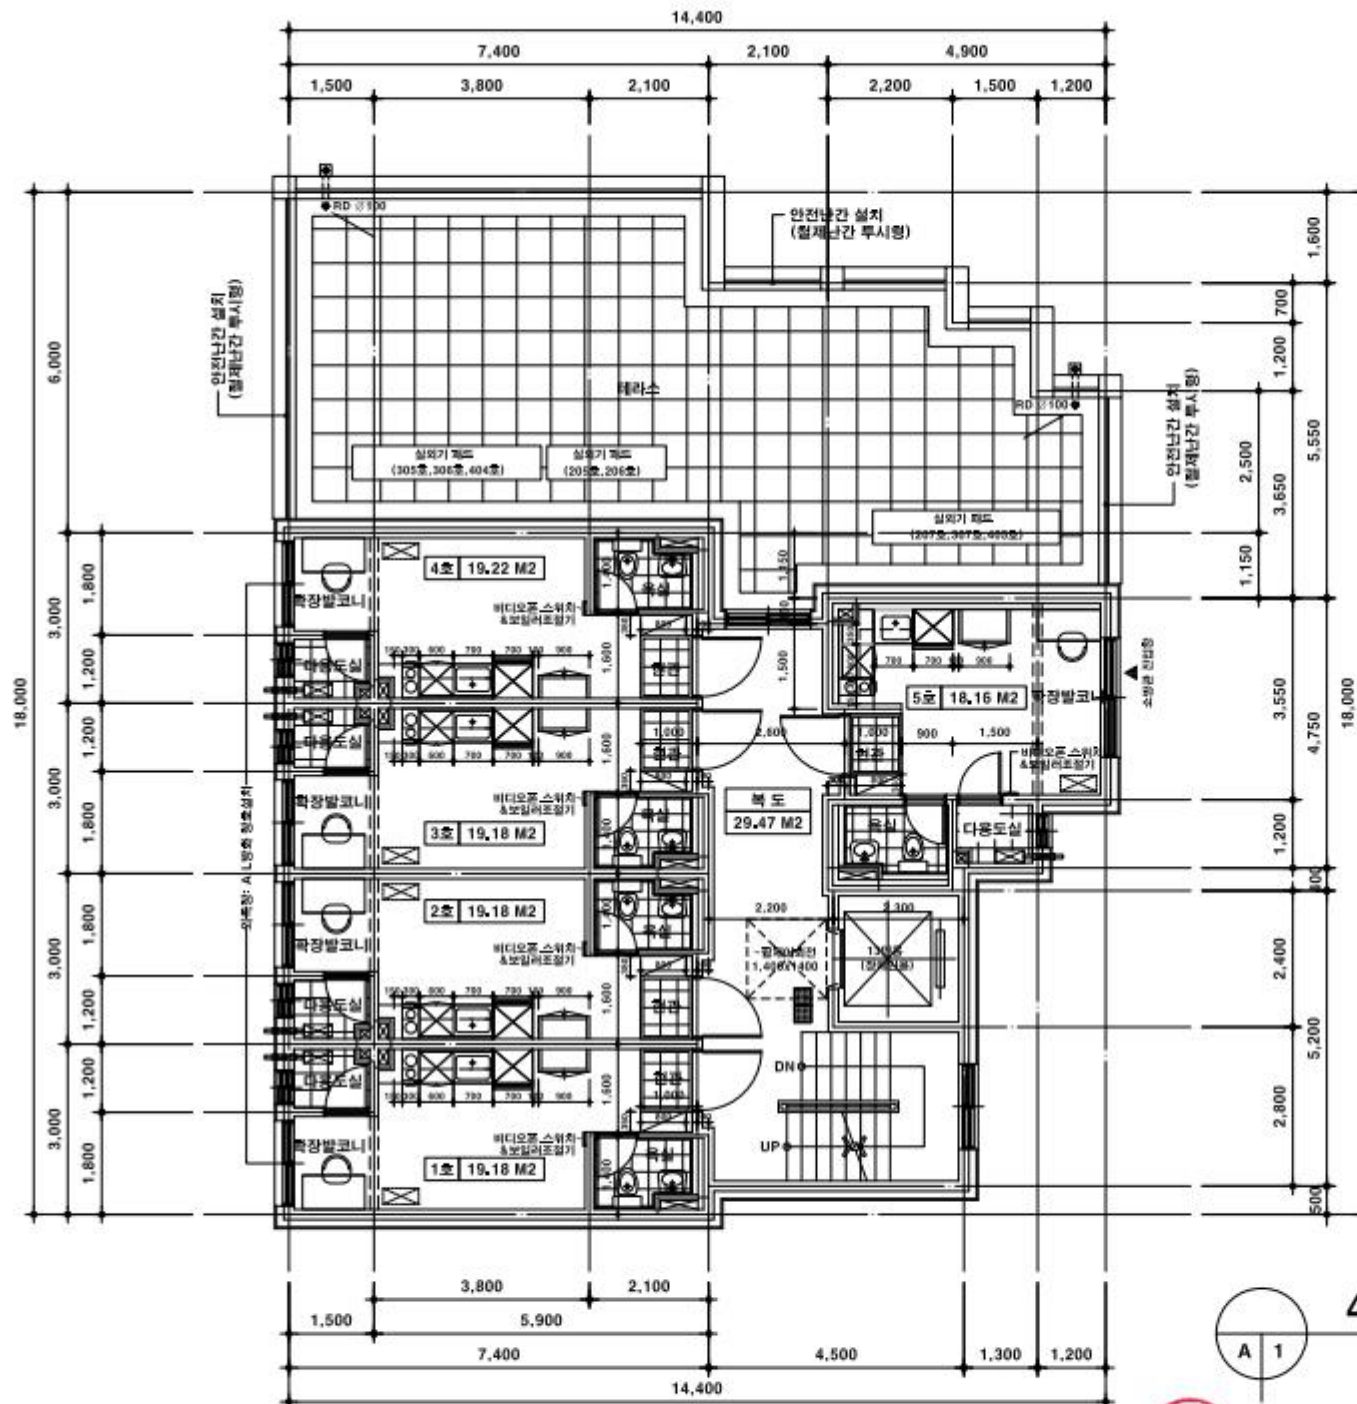

4층 평면도

SCALE : 1 / 100



주 기

1 (외부)	주차장내 CCTV, 쓰레기분리수거, 자진거보관대 설치
	우편함 설치 (세대전용, 공용, 반송용, 폐건전지함 구분 설치)
	테라스 창호 PL이중창 설치
	세대 테라스 설치시 세대간 분리벽 계획
	세대 발코니 설치시 차양시설 설치
2 (계단실)	세대 현관문 도어체크 설치
	계단실의 현관과 계단 이격거리 (최소600mm이상)
3 (내부)	세대내 욕실, 휴지걸이 배립형 설치
	콘크리트 폴타이 제거 후 마감공사 시공 (방수, 단열재 시공 등)
4 (시공)	욕실 & 다용도실 스위치 : 문 열리는 방향으로 시공
	주차장 차량 진출입구간 무소음트렌치 시공
5 (마감)	-직접외기(외벽)에 면한 실내벽면 단열재
	[아이소핑크(10mm) + 석고보드 마감도면 표기]
	-간접외기(계단실, 복도)에 면한 실내벽면 단열재
	[경질우레탄폼(100mm) + 석고보드 마감도면 표기]
	*기타 실내 벽면 시연트 미장 마감
구 번	철근 : fy=400Mpa
	콘크리트 : fck=24Mpa
	스라브두께 : 210mm (복배근)
	외벽두께 : 180mm (복배근)
	코아벽두께 : 180mm (복배근)
전 기	세대간벽두께 : 180mm (복배근)
	내벽두께 : 150mm (복배근)
	-콘센트 설치 (바닥 마감선 기준)
	[거실] 스탠드형 에어컨 : 350
	[안방] 벽걸이형 에어컨 : 1900
기	[화장실] 양변기 옆 : 900
	[주방] 조리대 : 중앙 / 냉장고 : 350 / 후드 : 2100
	-비디오콘(VP), 보일러온도조절기(B), 스위치(S) 설치 (거실 아트를 위치)
	-위치 표기
	에어컨 실외기
비 고	에어컨 콘센트
	냉매, 배수관 (배수관수직배관)

세대현관문
규격"틀"포함 : 1100X2200



(株)明珍플러스

TEL:2687-2588
FAX:866-9068

建築士事務所
ARCHITECTS & ENGINEERS

RD	DATE	REVISION DESCRIPTION	DRWN	CHK'D	APP'D

PROJECT TITLE
공 사 명
금천구 시흥동 220-116번지 외 2필지
다세대주택 (원룸) 신축공사

APPROVE
DESIGNED BY

CHK'D BY

SCALE
1 / 100

DATE
2023. 03

DRWN BY


DRAWING TITLE
도 면 명

4층 평면도


S.C.C NO

DRWG NO


A-205

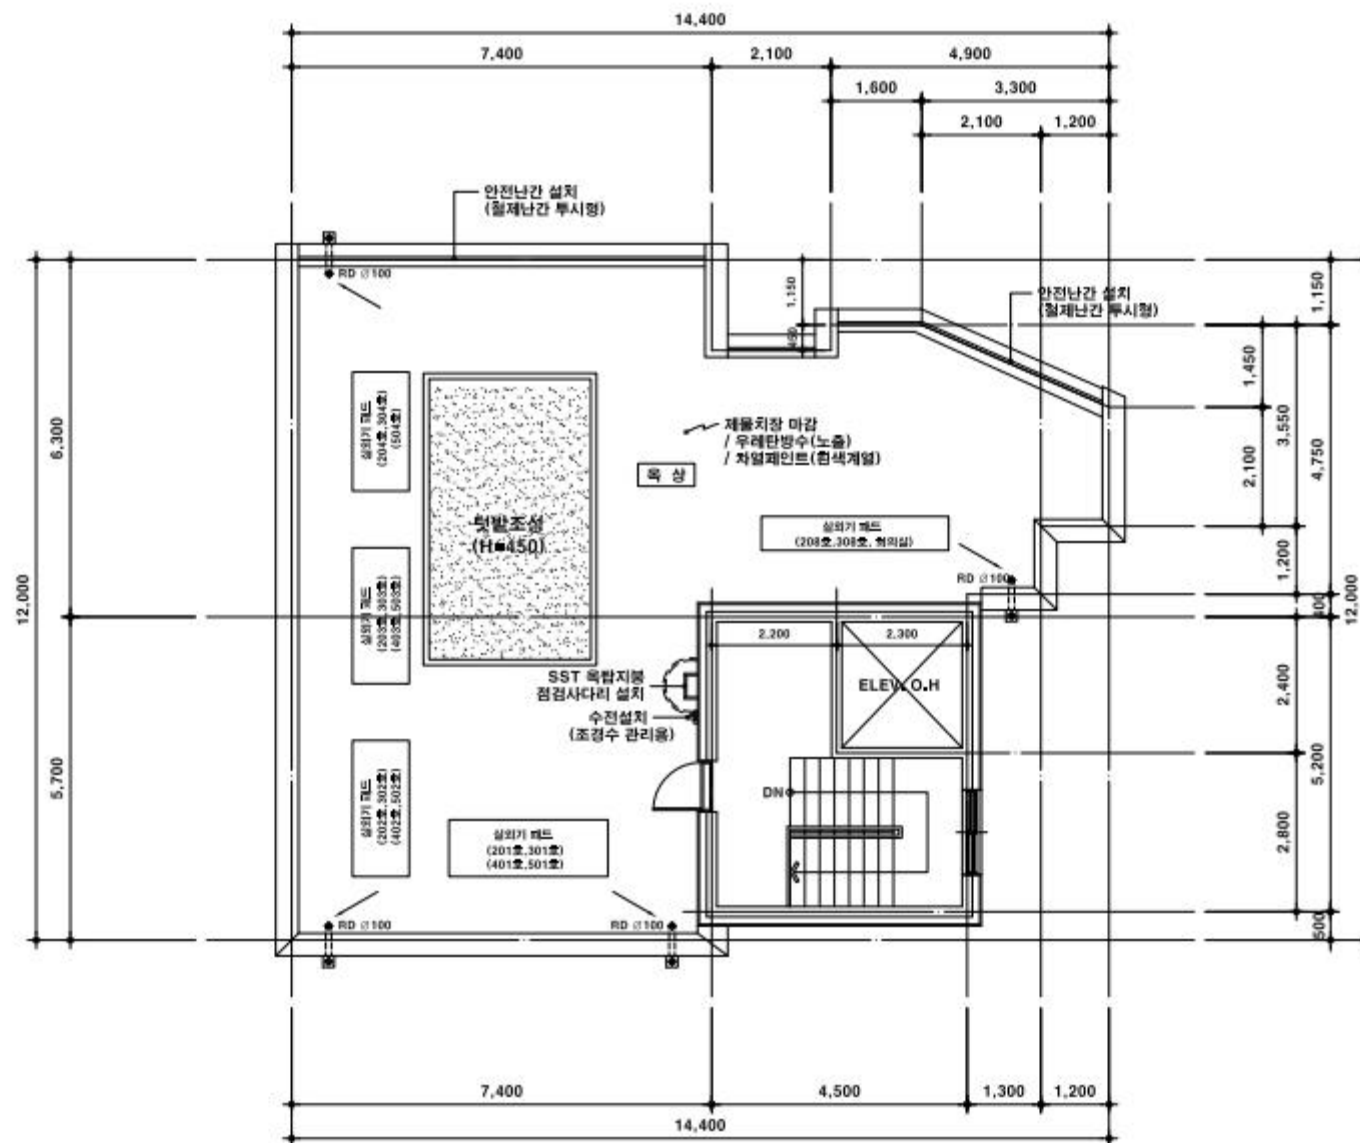

지붕 평면도
SCALE : 1 / 100

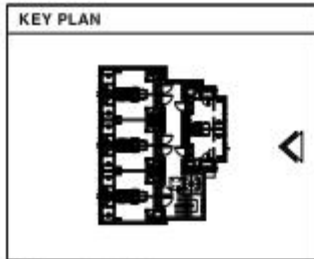

▼ 소방관 진입장

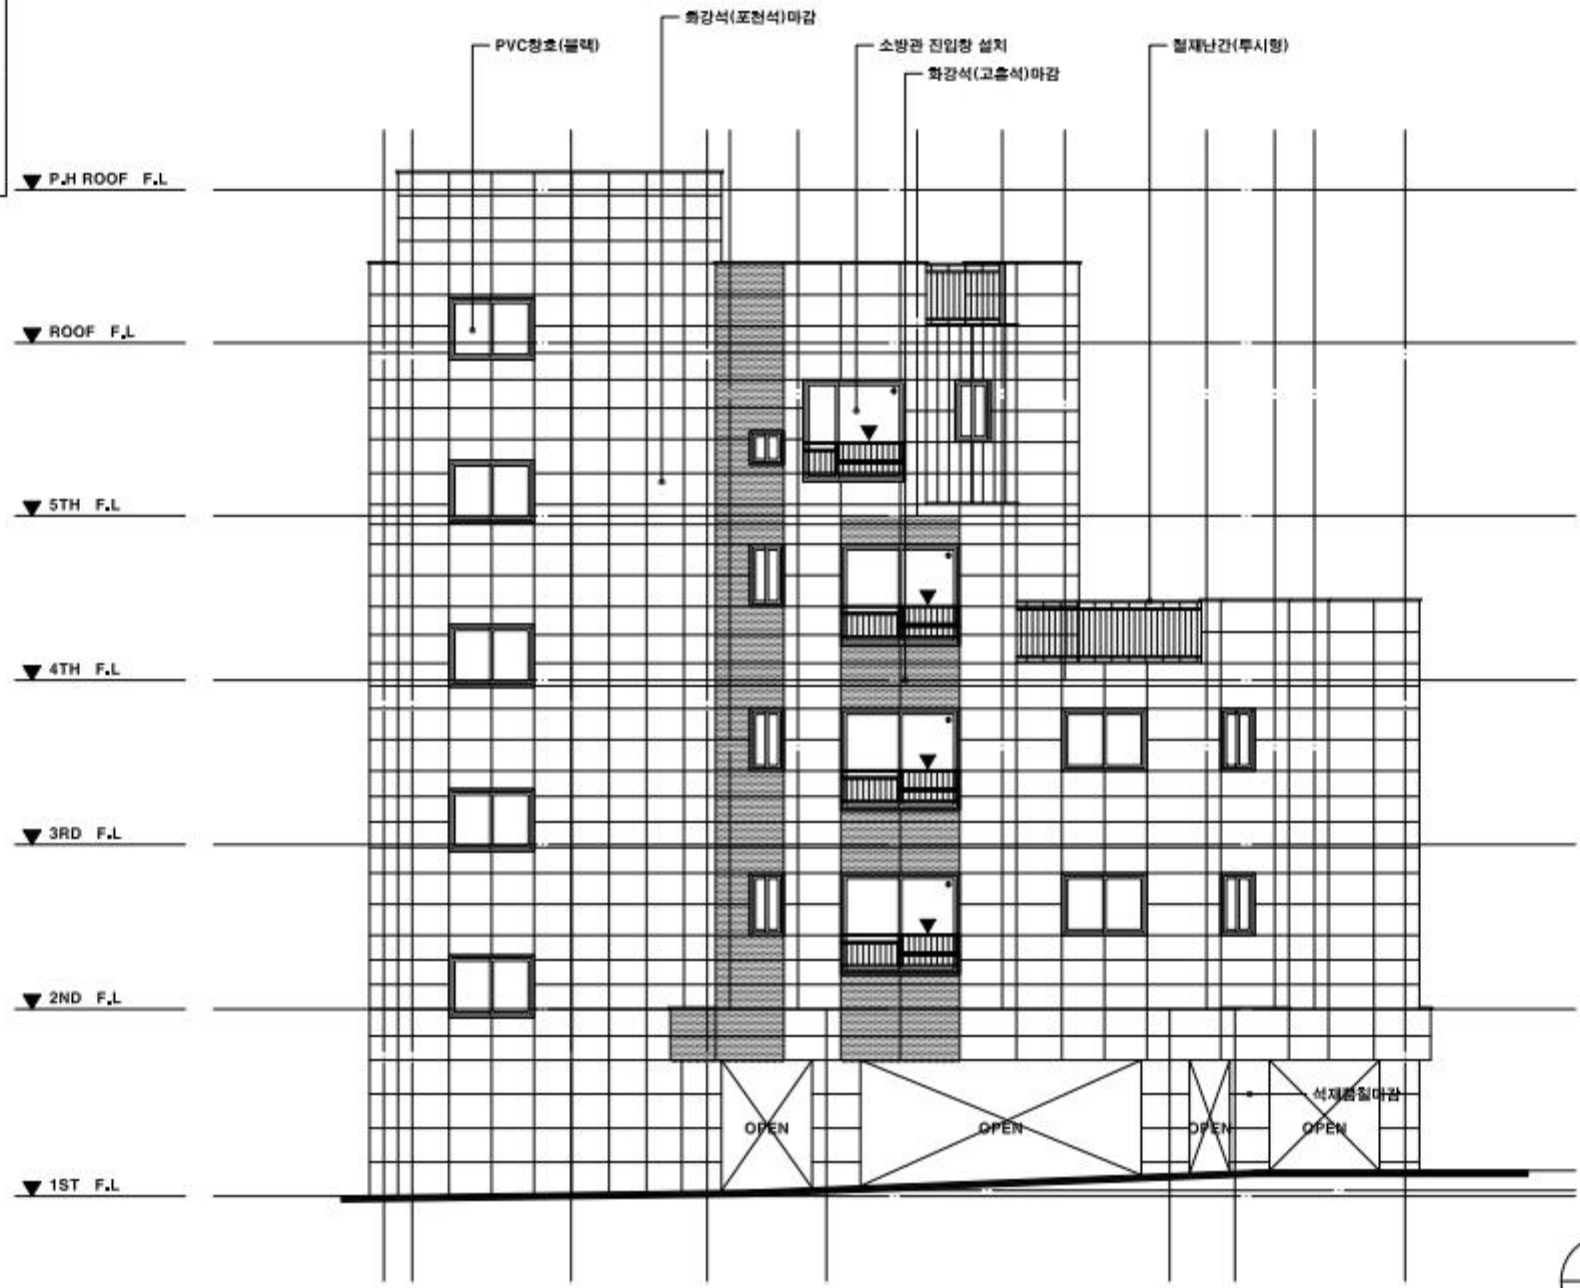


동측면도
SCALE : 1 / 100

 (株)明珍플러스 建築士事務所 ARCHITECTS & ENGINEERS TEL:2667-2588 FAX:866-9068	NO	DATE	REVISION DESCRIPTION	DRAWN	CHECKED	APPRO	PROJECT TITLE	APPROVED BY	CHECKED BY	SCALE	DRAWING TITLE	S.C.C NO
							공사명			1 / 100	도면명	
							금천구 시흥동 220-116번지 외 2필지 다세대주택 (임플) 신축공사			DATE 2023. 03	동측면도	DRAWING NO A-208
								DESIGNED BY		DRAWN BY		



KEY PLAN

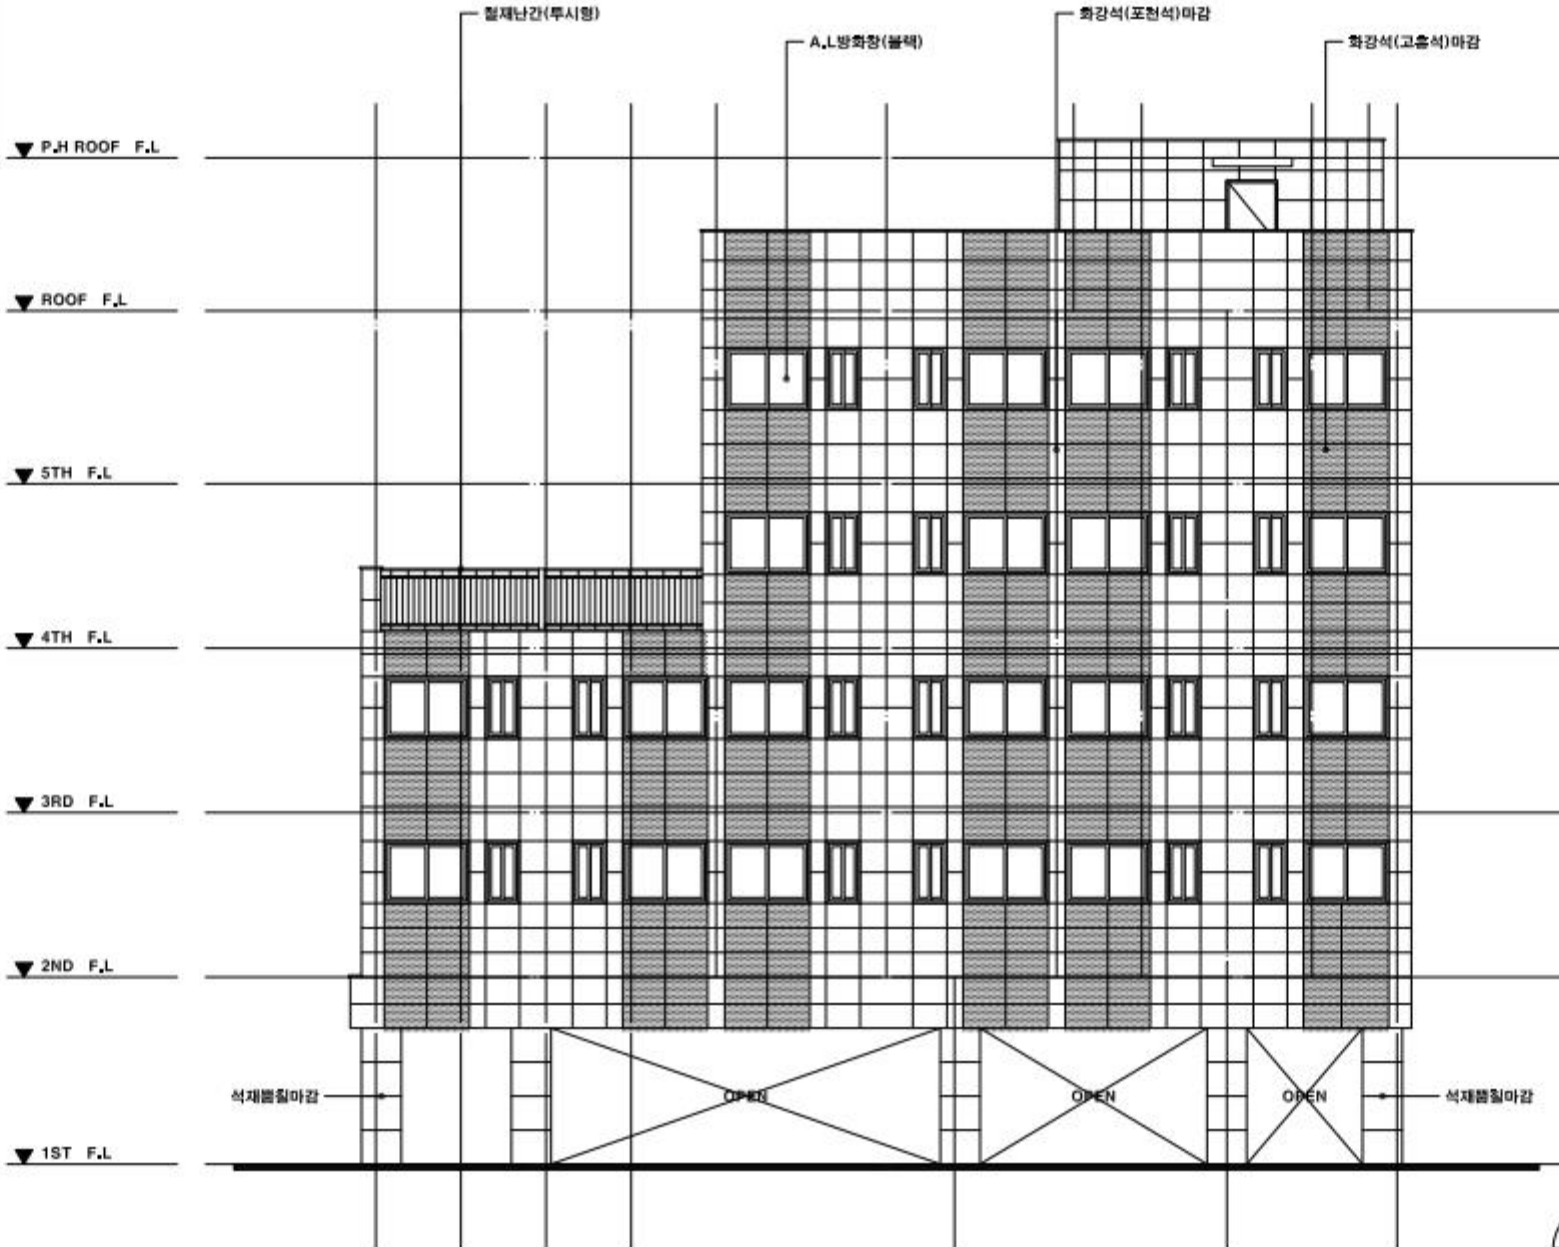

서측면도

SCALE : 1 / 100



(株)明珍플러스

TEL:2687-2588
FAX:866-9068建築士事務所
ARCHITECTS & ENGINEERS

NO	DATE	REVISION DESCRIPTION	DRWN	CHK'D	APP'D

PROJECT TITLE

공사명

금천구 시흥동 220-116번지 외 2필지
다세대주택 (임물) 신축공사

APPROVE

DESIGNED BY

CHK'D BY

SCALE 1 / 100

DATE 2023. 03

DRAWN BY

DRAWING TITLE

도면명

서측면도

S.C.O NO

DRWG NO

A-209

KEY PLAN



▼ P.H ROOF F.L

▼ ROOF F.L

▼ 5TH F.L

▼ 4TH F.L

▼ 3RD F.L

▼ 2ND F.L

마천석 물받기

보재틀림마감

OPEN

OPEN

OPEN

보재틀림마감

철재난간(투시형)

PVC창호(블랙)

화강석(포천석)마감

서측면도

SCALE : 1 / 100

A 1



(株)明珍플러스
建築士事務所
ARCHITECTS & ENGINEERS

NO	DATE	REVISION DESCRIPTION	DRWN	CHK'D	APPR

PROJECT TITLE
공사명
공천구 시흥동 220-116번지 외 2필지
다세대주택 (임플) 신축공사



APPROVE D	CHK'D BY
DESIGNED BY	

SCALE 1 / 100
DATE 2021. 08
DRAWN BY

DRAWING TITLE
도면명
서측면도

S.C.C NO
DRAW NO
A-209

KEY PLAN

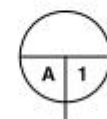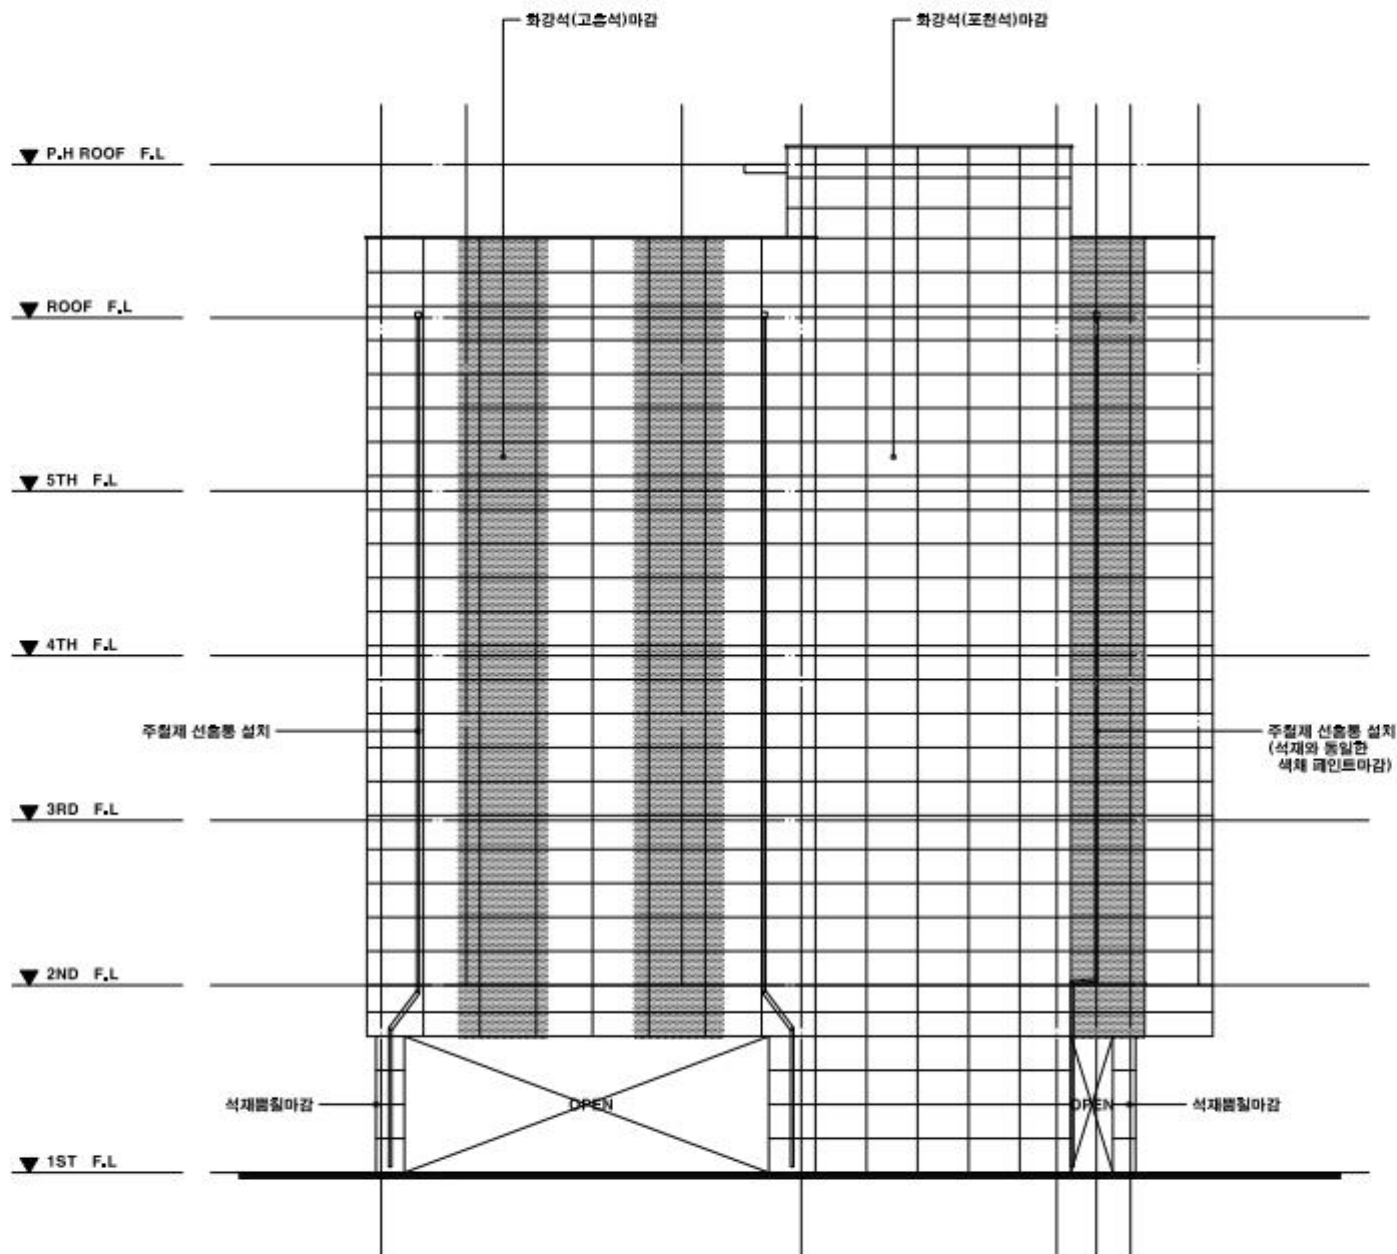

남측면도

SCALE : 1 / 100



(株)明珍플러스
建築士事務所
ARCHITECTS & ENGINEERS

NO	DATE	REVISION DESCRIPTION	DRWN	CHK'D	APP'D


PROJECT TITLE
공사명
금천구 시흥동 220-116번지 외 2필지
다세대주택 (원룸) 신축공사





APPROVE & DATE	CHK'D BY	SCALE
		1 / 100
DESIGNED BY		DATE
		2023. 03
		DRAWN BY

DRAWING TITLE
도면명
남측면도

S.C.C NO	
DRAWING NO	A-210

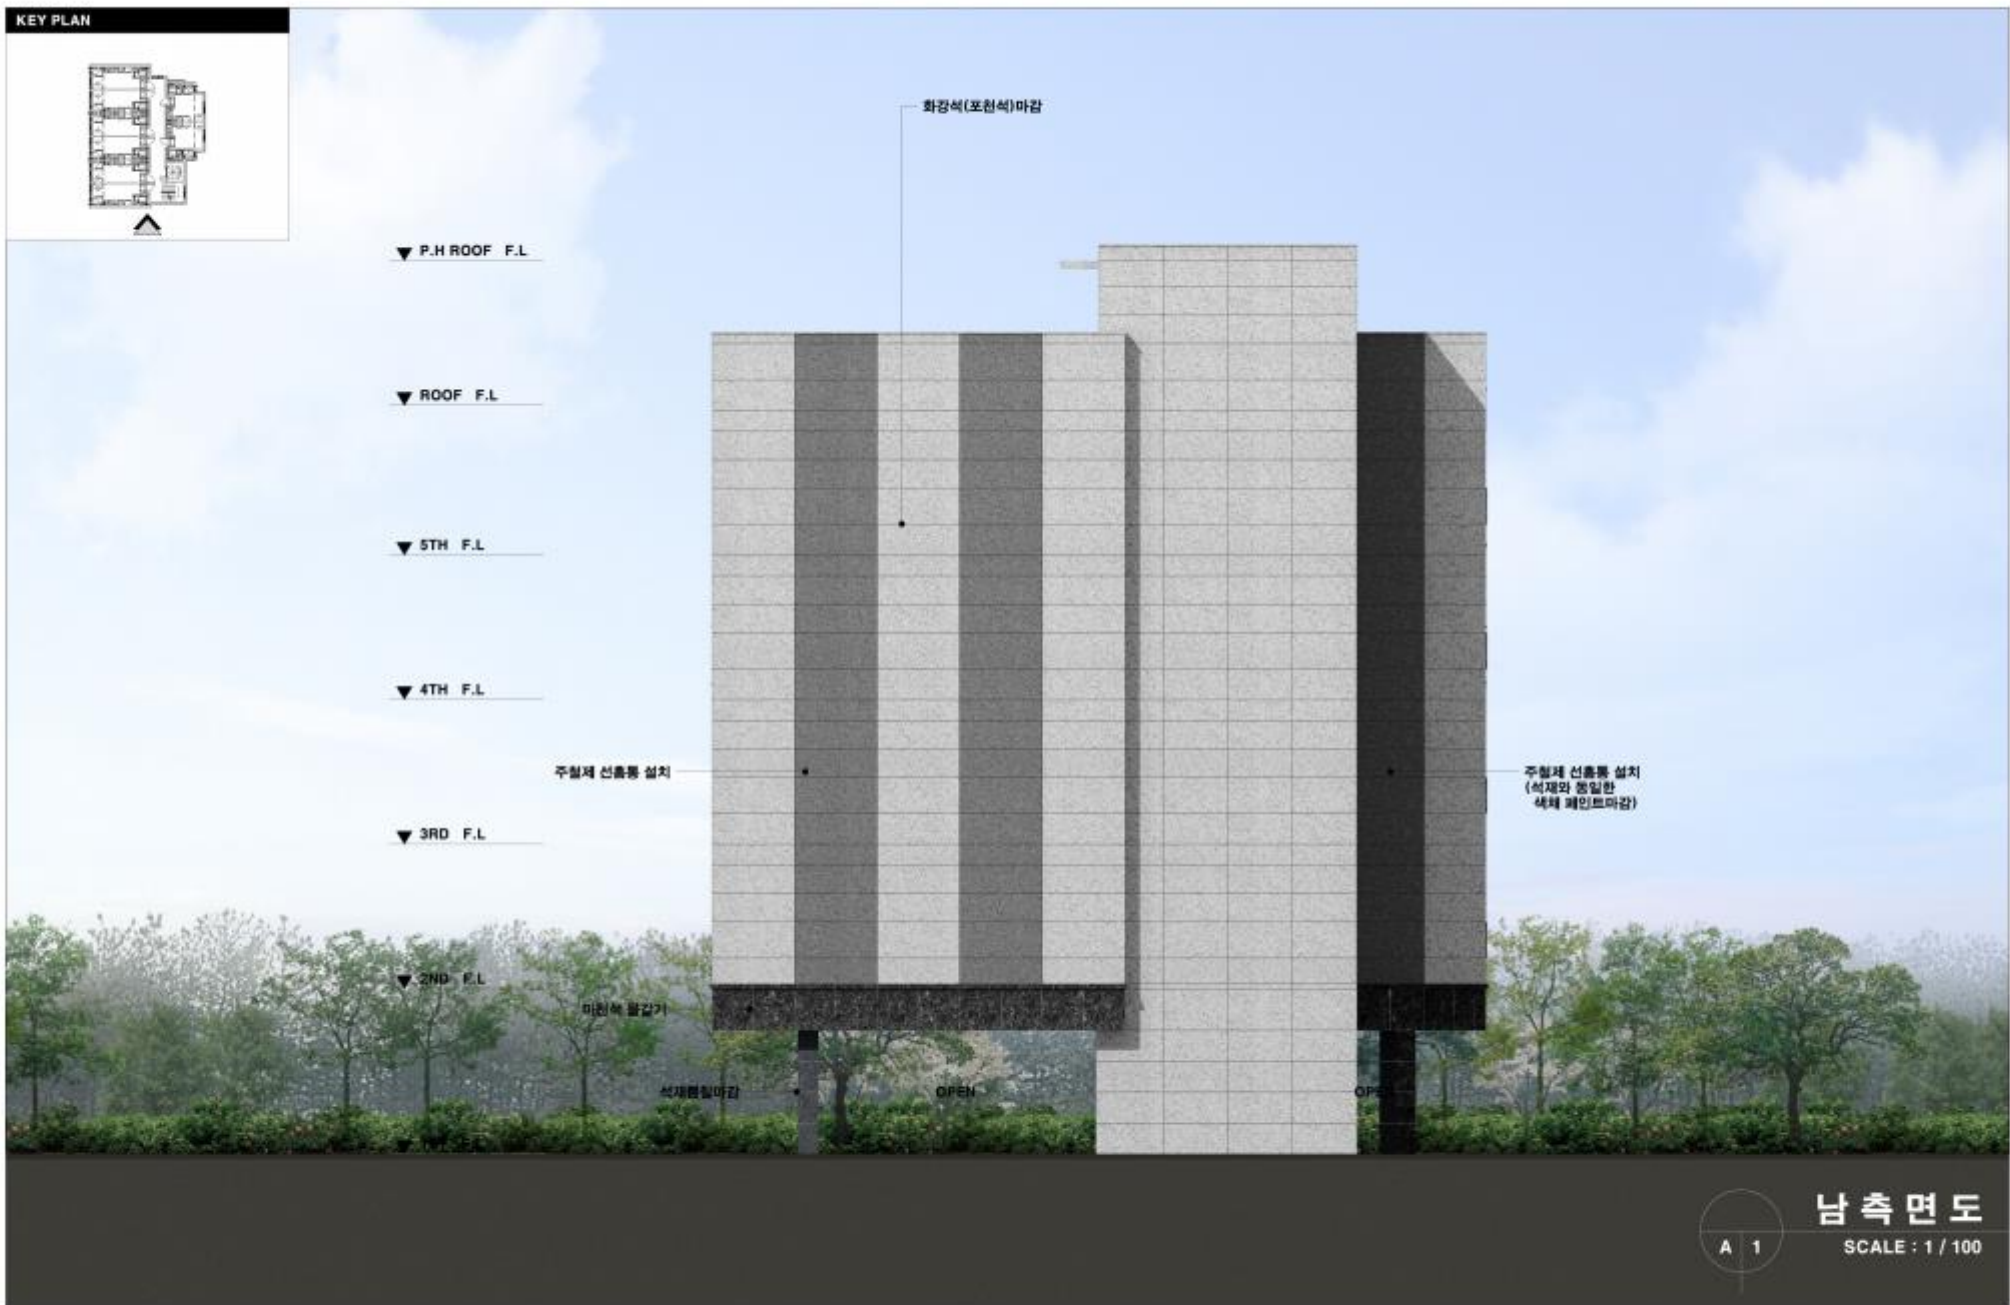

KEY PLAN

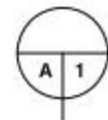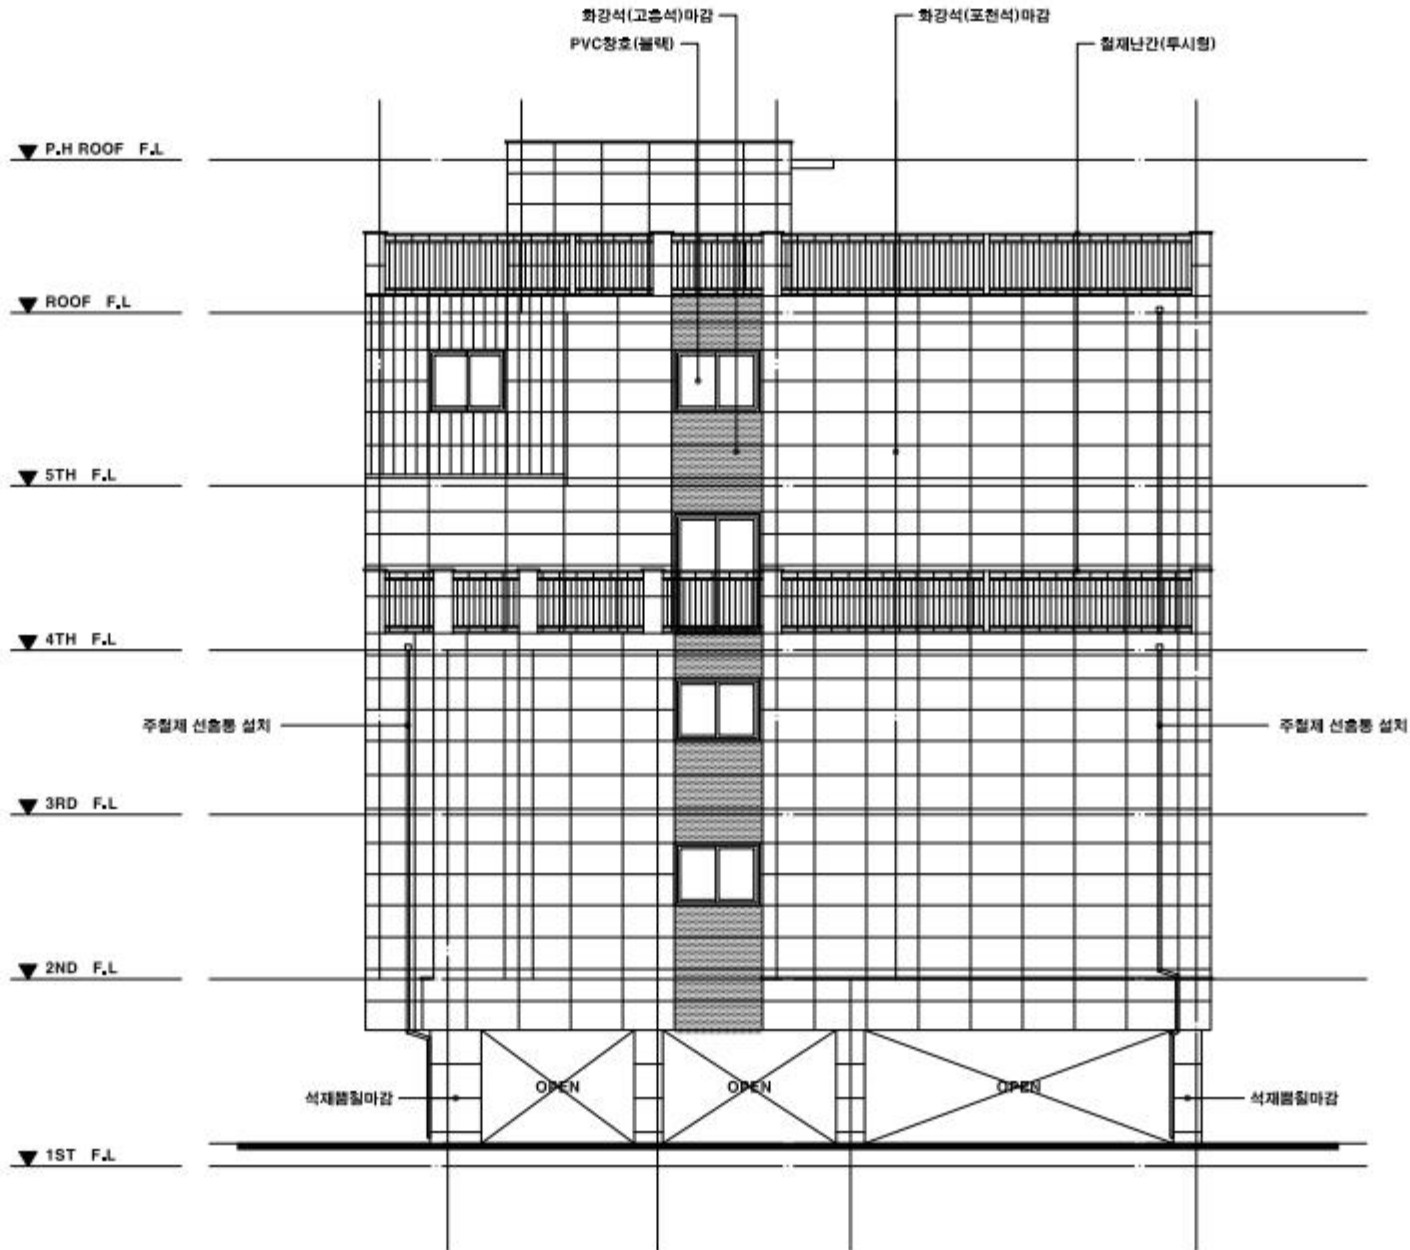

북측면도

SCALE : 1 / 100



(株)明珍플러스

 建築士事務所
 ARCHITECTS & ENGINEERS
 TEL:2667-2588
 FAX:866-9068

NO	DATE	REVISION DESCRIPTION	DRWN	CHK'D	APP'D

PROJECT TITLE
공사명
금천구 시흥동 220-116번지 외 2필지
다세대주택 (임플) 신축공사

APPROVE
DESIGNED BY
CHK'D BY

SCALE
1 / 100
DATE
2023. 03
DRAWN BY

DRAWING TITLE
도면명
북측면도

S.C.C NO
DRAWING NO
A-211



(株)明珍플러스
建築士事務所
ARCHITECTS & ENGINEERS

NO	DATE	REVISION DESCRIPTION	DRWN	CHK'D	APPR

PROJECT TITLE
공사명
금천구 시흥동 220-116번지 외 2필지
다세대주택 (임플) 신축공사

APPROVE	CHK'D BY
DESIGNED BY	

SCALE 1 / 100
DATE 2021. 08
DRWN BY

DRAWING TITLE
도면명
북측면도

SHEET NO
DWG NO

A-211