


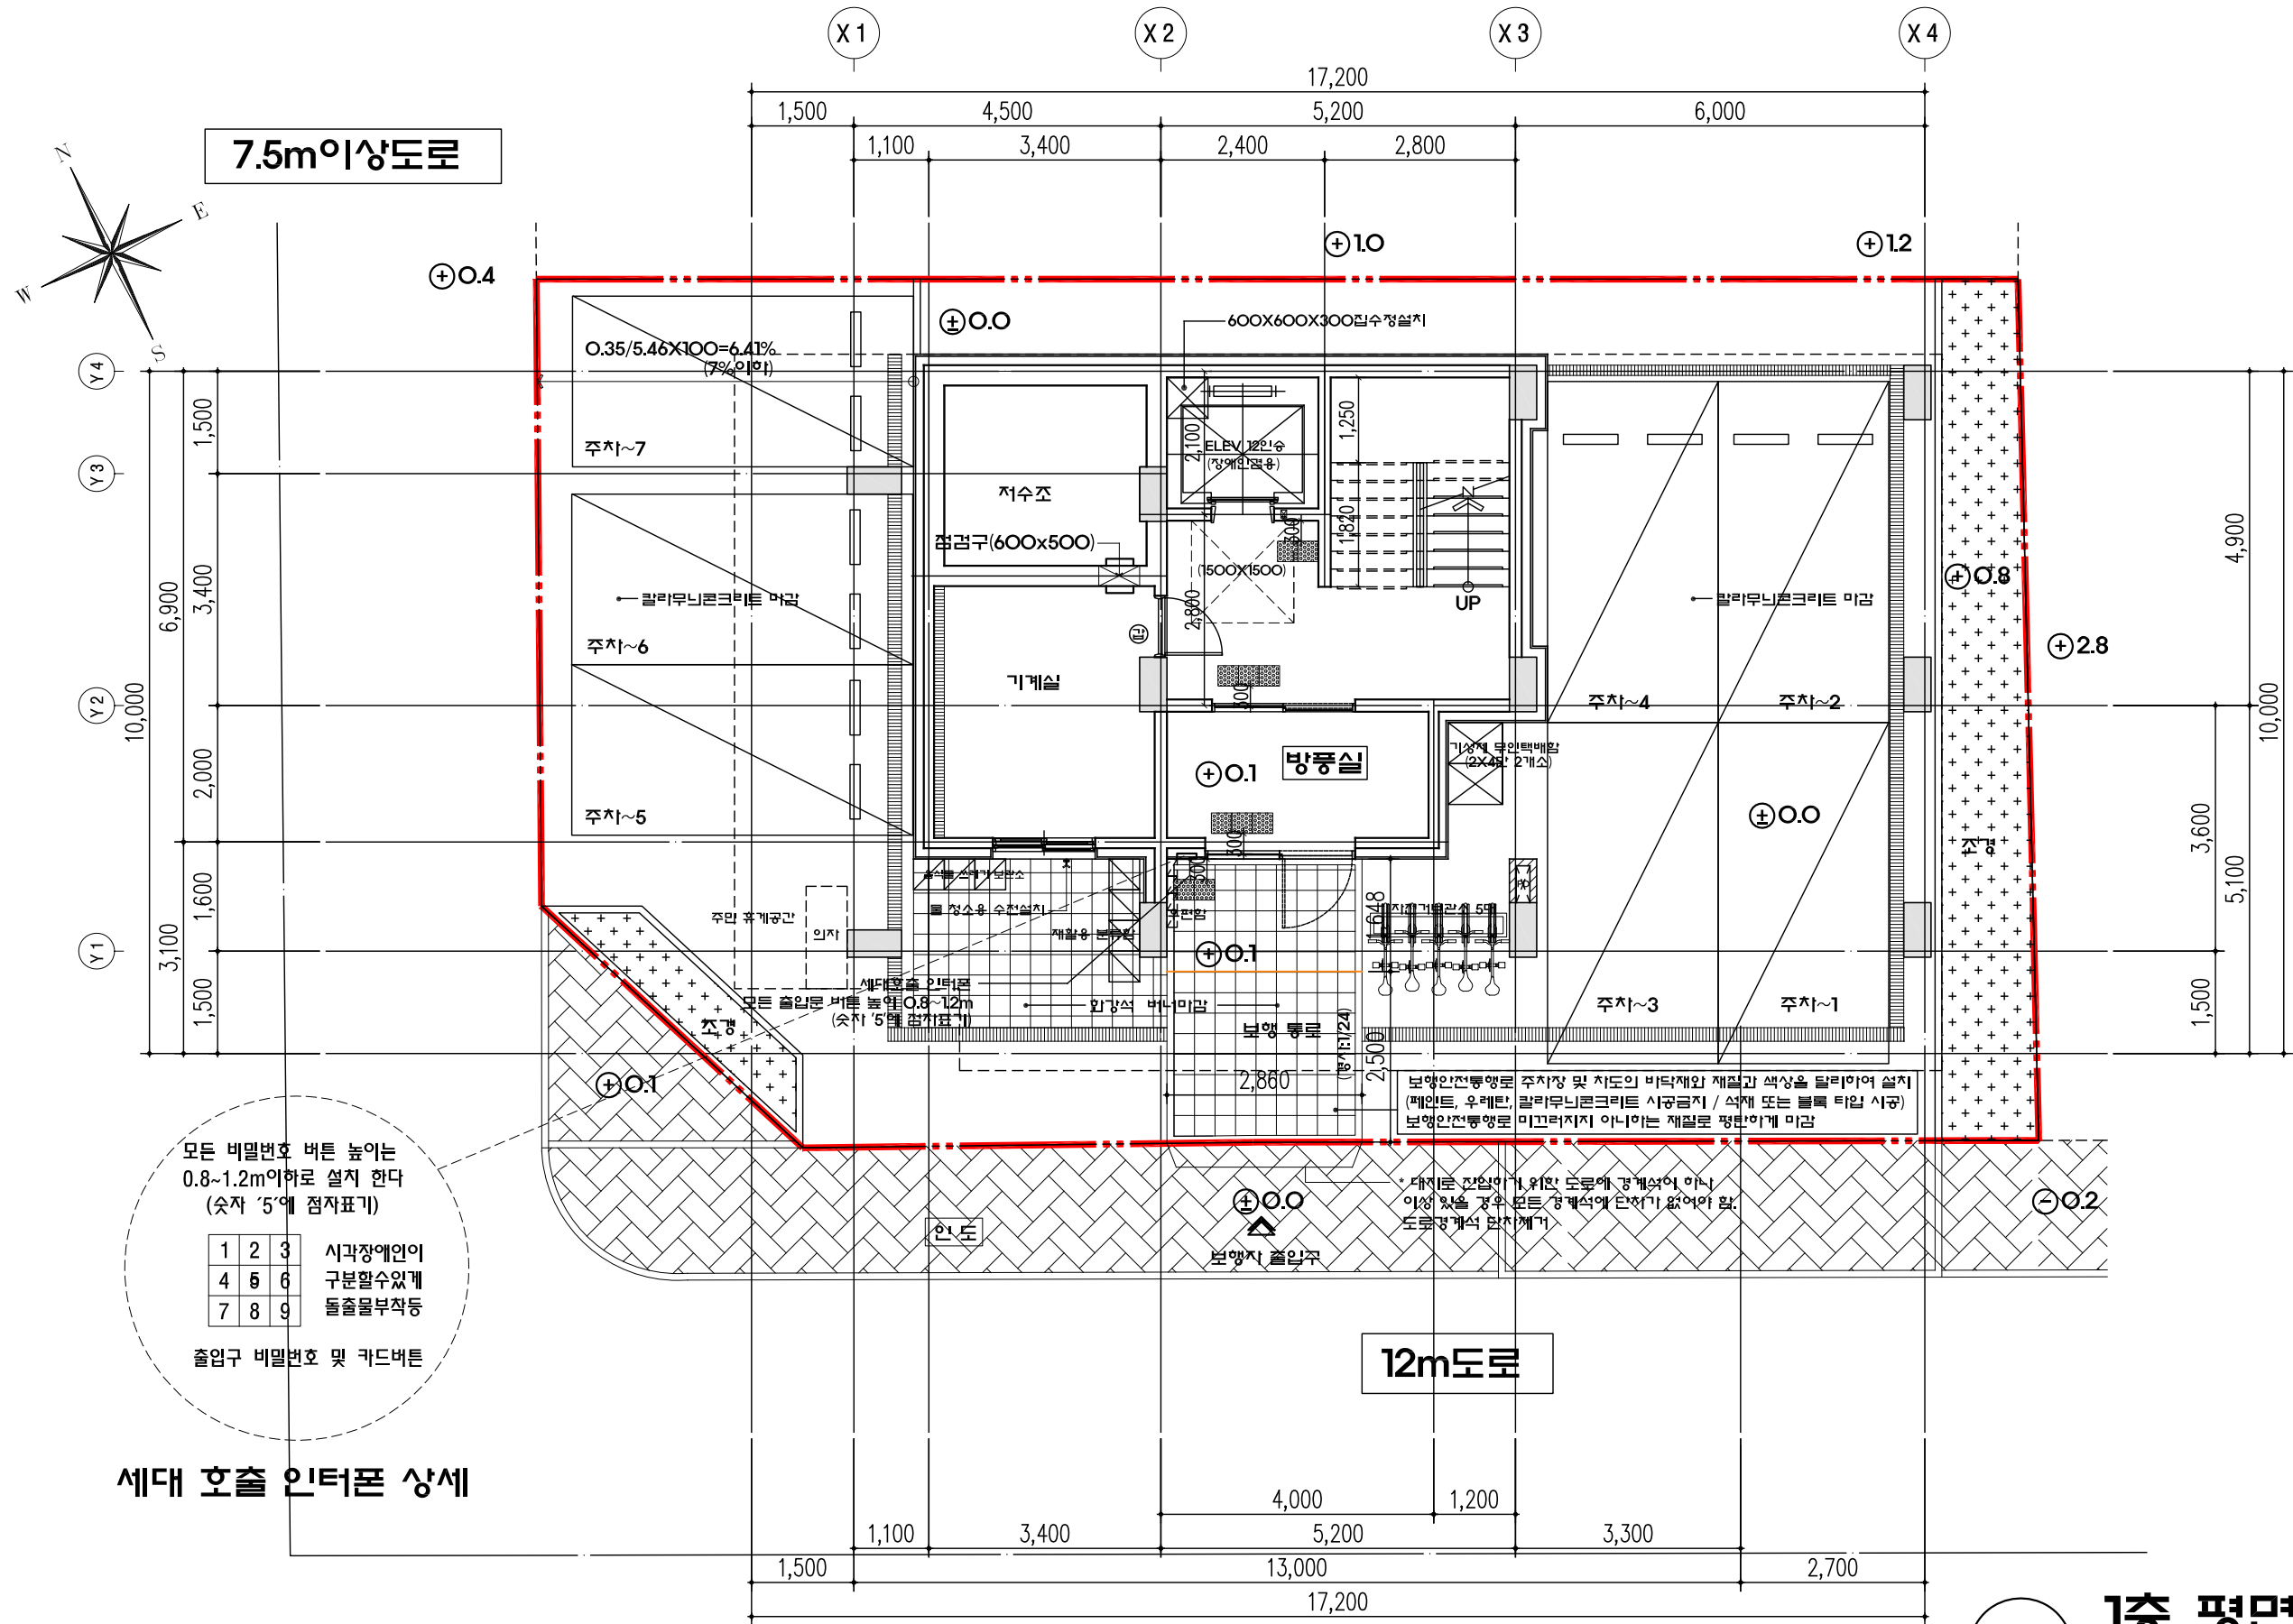

1층 평면도
축척: 1/100



백이건축사사무소
서울특별시 강북구 삼양로 361, 2층
TEL.(대표)02-908-8894, FAX:02-908-8896

NO.	DATE	REVISION DESCRIPTION	DRWN.	CHKD.	APPD.

공사명 PROJECT TITLE
서울특별시 도봉구 창2동 621-43번지
도시형생활주택 단지형 다세대주택 신축공사

승인 APPROVED BY
설계 DESIGNED BY

검토 3
CHKD BY
검토 2
CHKD BY
검토 1
CHKD BY

축척 SCALE
설치 DATE
담당 DRWN. BY

입력명 ACAD#
DRWG NO.
A-401

작업번호 JOB NO.
REV NO.
SHEET NO.

도면명 DRAWING TITLE
1층 평면도



2~5층 평면도
축척: 1/100



백이건축사사무소
서울특별시 강북구 삼양로 361, 2층
TEL.(대표)02-908-8894, FAX:02-908-8896

NO.	DATE	REVISION DESCRIPTION	DRWN.	CHK'D	APPD.

공사명 PROJECT TITLE
서울특별시 도봉구 창2동 621-43번지
도시형생활주택 단지형 다세대주택 신축공사

승인 APPROVED BY
설계 DESIGNED BY

검토 3
CHK'D BY
검토 2
CHK'D BY
검토 1
CHK'D BY

축척 SCALE
2025.12
일 자 DATE
필 당
DRWN. BY

입력명 ACAD#
A-402
DRWG NO.

작업번호 JOB NO.
REV NO.
도면명 DRAWING TITLE
2~5층 평면도



6층 평면도

축척: 1/ 100



백이건축사사무소

서울특별시 강북구 삼양로 361. 2층

TEL.(대표)02-908-8894, FAX:02-908-8896

NO.	DATE	REVISION DESCRIPTION	DRWN.	CHK'D	APP'D

공사명 PROJECT TITLE
서울특별시 도봉구 창2동 621-43번지
도시형생활주택 단지형 다세대주택 신축공사

승인 APPROVED BY
설계 DESIGNED BY



검토 3
CHK'D BY
검토 2
CHK'D BY
검토 1
CHK'D BY

축척
SCALE
날자
DATE
2025.12
담당
DRWN. BY

입찰명 ACAD#
DRWG NO.
A-403

작업번호 JOB NO.
REV NO.
SHEET NO.

도면명 DRAWING TITLE
6층 평면도

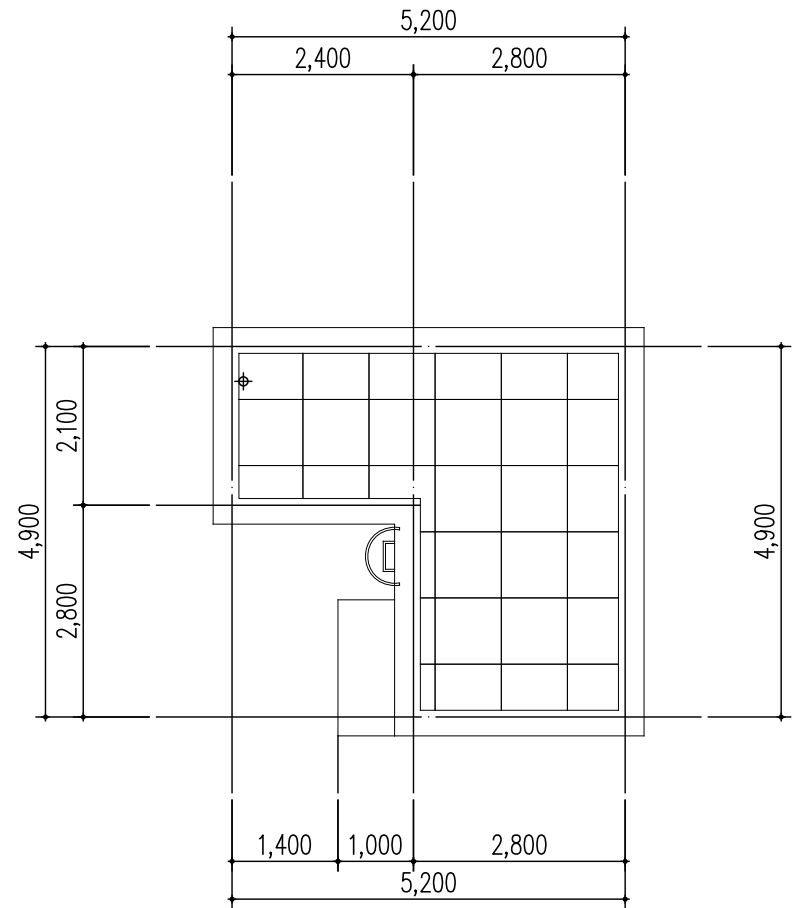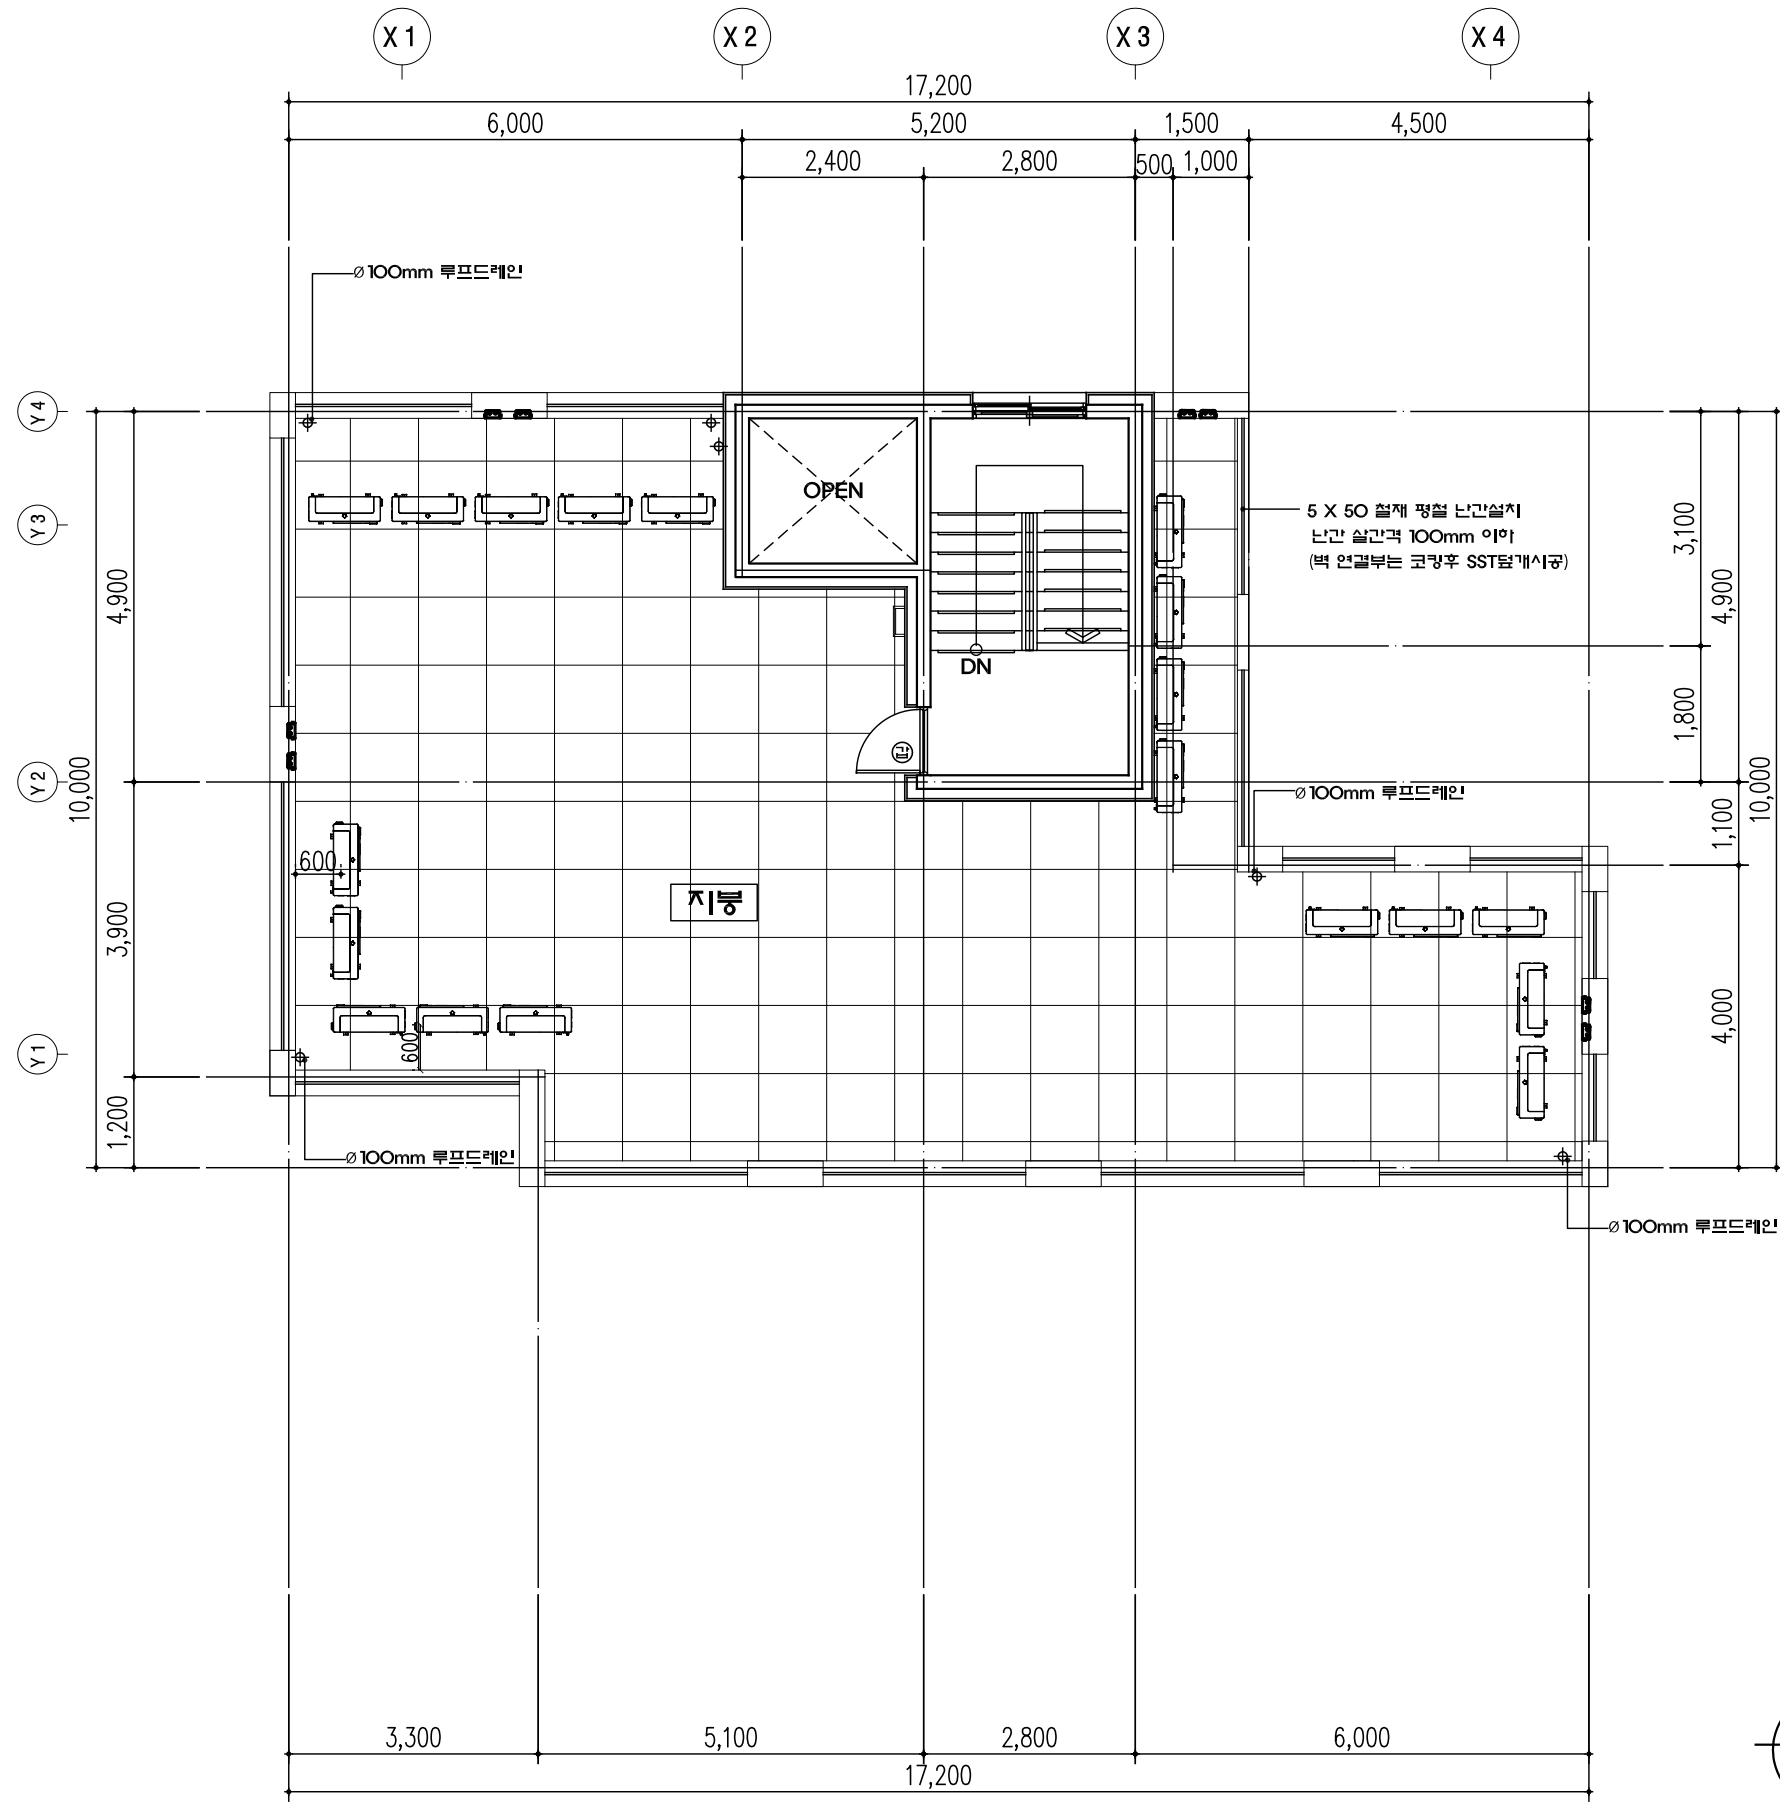

지붕밋옥탑 지붕평면도
축척:1/ 100



백이건축사사무소
서울특별시 강북구 삼양로 361. 2층
TEL.(대표)02-908-8894, FAX:02-908-8896

NO.	DATE	REVISION DESCRIPTION	DRWN.	CHK'D	APPD.

공사명 PROJECT TITLE
서울특별시 도봉구 창2동 621-43번지
도시형생활주택 단지형 다세대주택 신축공사


승인 APPROVED BY
설계 DESIGNED BY

검토 3
CHK'D BY
검토 2
CHK'D BY
검토 1
CHK'D BY
축척 SCALE
2025.12
일 자 DATE
필 당
DRWN. BY


입력명 ACAD#
DRWG NO.
A-404

작업번호 JOB NO.
REV NO.
SHEET NO.

도면명 DRAWING TITLE
지붕밋옥탑 지붕평면도

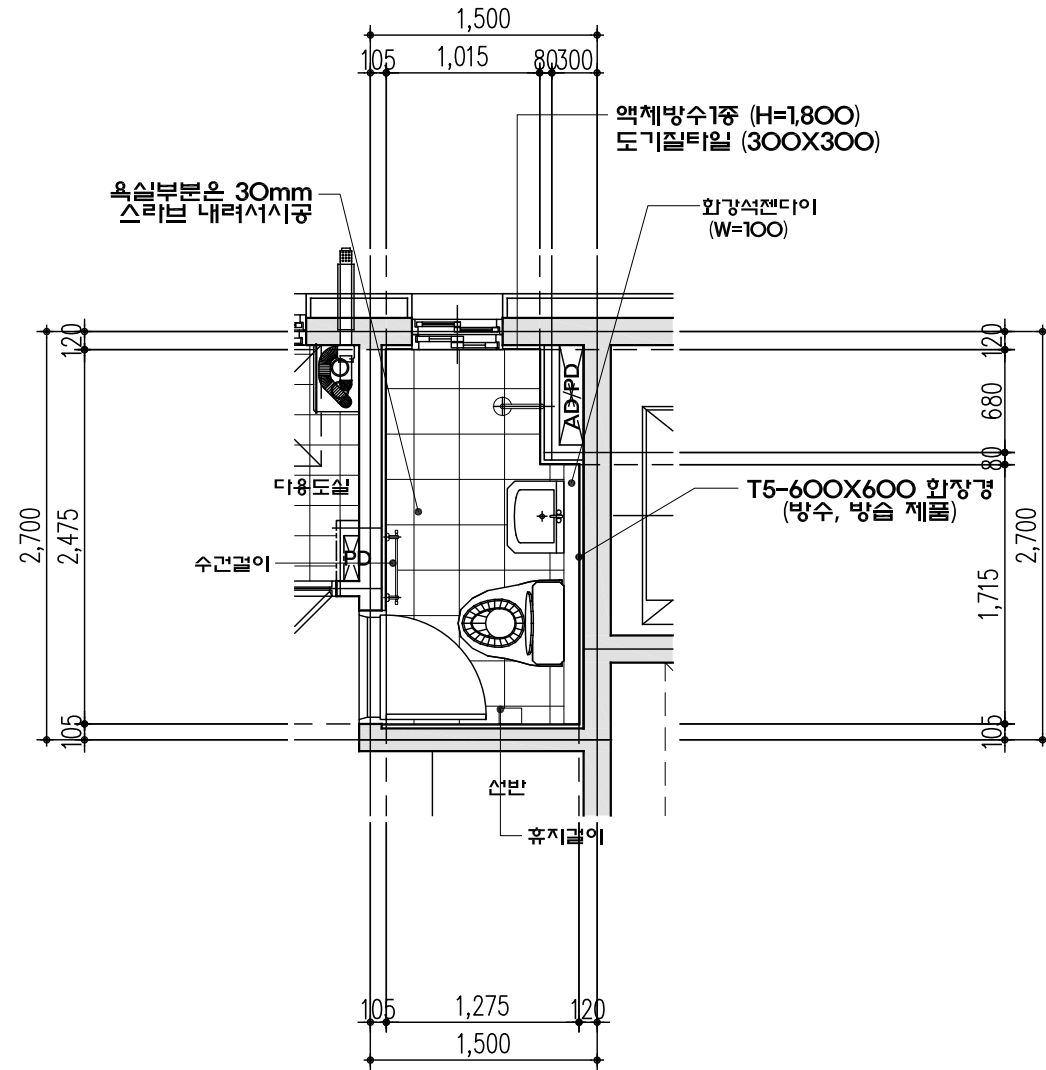

2~601호 화장실 확대 평면도
축척:1/ 50

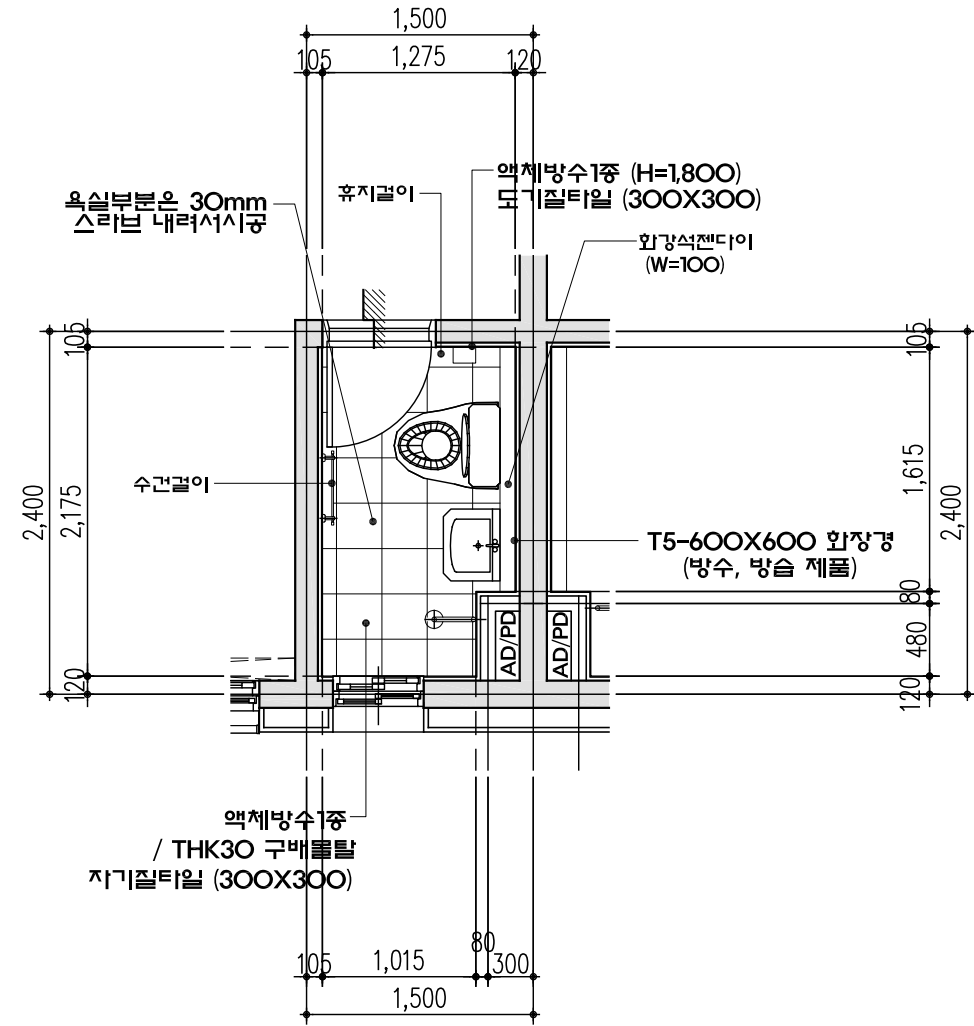

2~602호 화장실 확대 평면도
축척:1/ 50



백이건축사사무소
서울특별시 강북구 삼양로 361. 2층
TEL.(대표)02-908-8894, FAX:02-908-8896

NO.	DATE	REVISION DESCRIPTION	DRWN.	CHK'D	APPD.

공사명 PROJECT TITLE
서울특별시 도봉구 창2동 621-43번지
도시형생활주택 단지형 다세대주택 신축공사


승인 APPROVED BY
설계 DESIGNED BY

검토 3 CHK'D BY	축척 SCALE
검토 2 CHK'D BY	날자 DATE
검토 1 CHK'D BY	담당 DRWN. BY


입찰명 ACAD#
DRWG NO.

작업번호 JOB NO.
SHEET NO.
A-405

도면명 DRAWING TITLE
2~501호 화장실 확대 평면도
2~502호,601호 화장실 확대 평면도

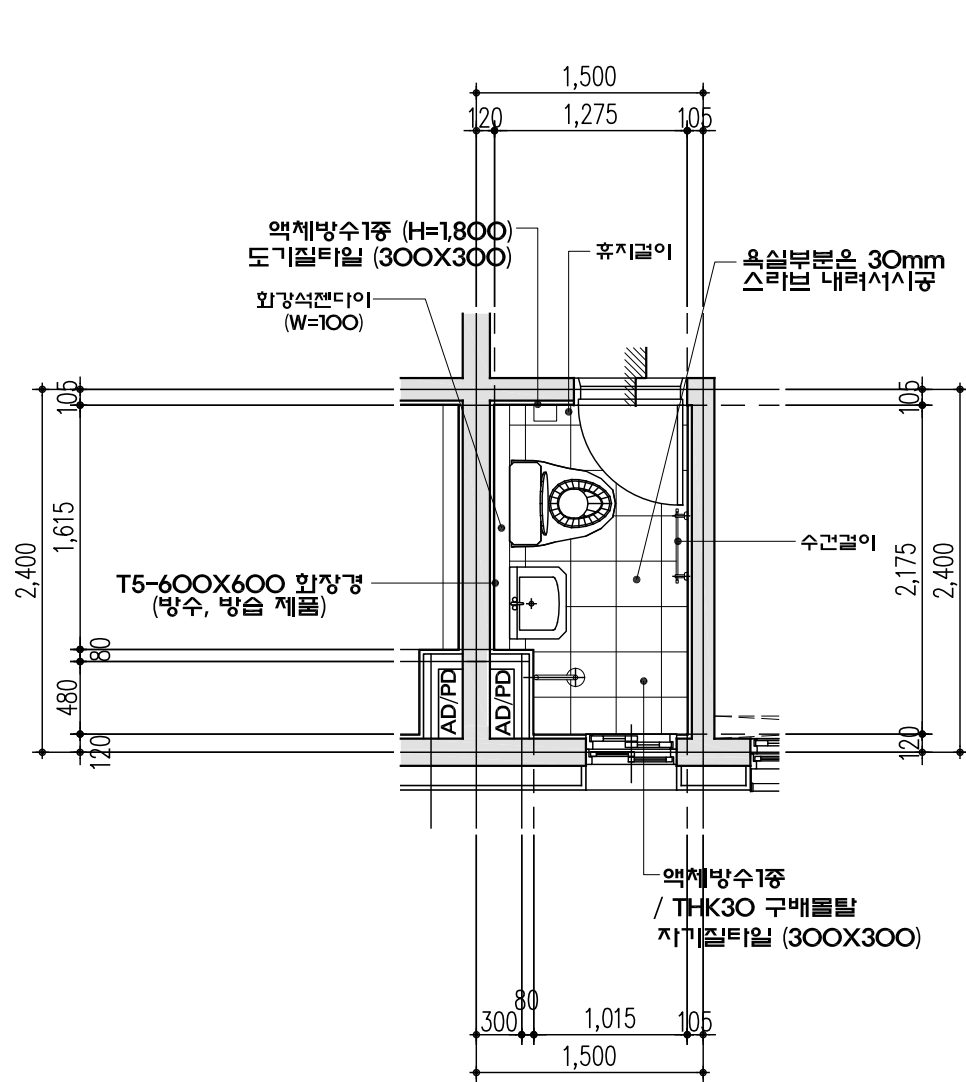

2~603호 화장실 확대 평면도
축척:1/ 50

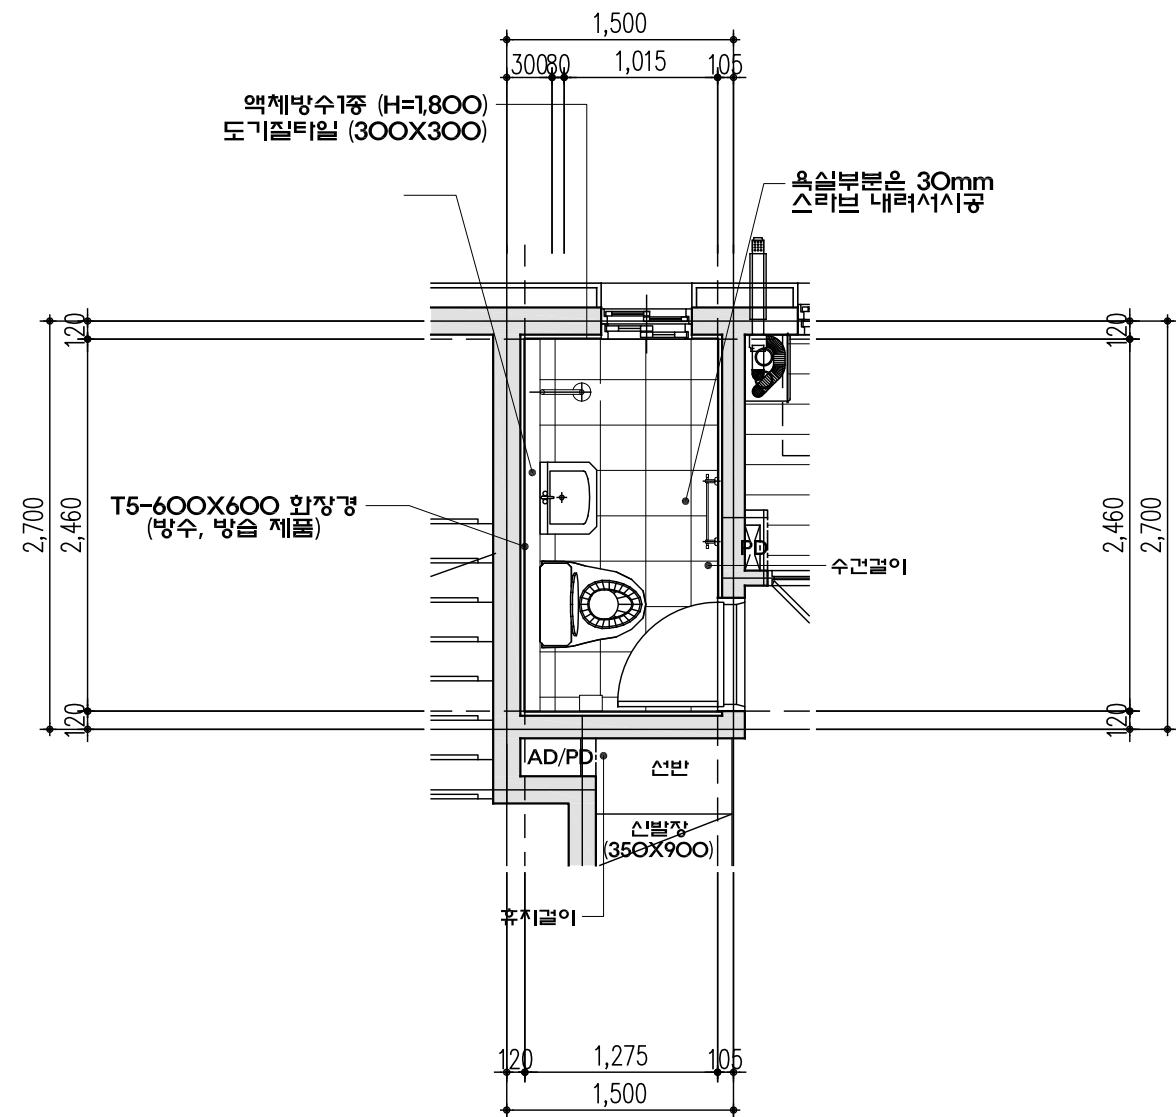

2~504호 화장실 확대 평면도
축척:1/ 50



백이건축사사무소
서울특별시 강북구 삼양로 361. 2층
TEL.(대표)02-908-8894, FAX:02-908-8896

NO.	DATE	REVISION DESCRIPTION	DRWN.	CHK'D	APPD.

공사명 PROJECT TITLE
서울특별시 도봉구 창2동 621-43번지
도시형생활주택 단지형 다세대주택 신축공사

승인 APPROVED BY
설계 DESIGNED BY

검토 3 CHK'D BY	축척 SCALE
검토 2 CHK'D BY	날자 DATE
검토 1 CHK'D BY	담당 DRWN. BY

입력명 ACAD#
DRWG NO.

작업번호 JOB NO.
SHEET NO.
A-406

도면명 DRAWING TITLE
2~503호,602 화장실 확대 평면도
2~504호,603호 화장실 확대 평면도



정 면 도
축척:1/100



백이건축사사무소
서울특별시 강북구 삼양로 361. 2층
TEL.(대표)02-908-8894, FAX:02-908-8896

NO.	DATE	REVISION DESCRIPTION	DRWN.	CHK'D	APP'D

공사명 PROJECT TITLE
서울특별시 도봉구 창2동 621-43번지
도시형생활주택 단지형 다세대주택 신축공사

승인 APPROVED BY
설계 DESIGNED BY

공도 3
CHK'D BY
공도 2
CHK'D BY
공도 1
CHK'D BY

축척 SCALE
날자 DATE
2025.12
담당 DRWN. BY

입찰명 ACAD#
DRWG NO.
A-501

작업번호 JOB NO.
REV NO.
SHEET NO.

도면명 DRAWING TITLE
정 면 도



배면도
축척: 1/100



백이건축사사무소
서울특별시 강북구 삼양로 361. 2층
TEL.(대표)02-908-8894, FAX:02-908-8896

NO.	DATE	REVISION DESCRIPTION	DRWN.	CHK'D	APPD.

공사명 PROJECT TITLE
서울특별시 도봉구 창2동 621-43번지
도시형생활주택 단지형 다세대주택 신축공사

승인 APPROVED BY
설계 DESIGNED BY

공도 3
CHK'D BY
공도 2
CHK'D BY
공도 1
CHK'D BY

축척 SCALE
날자 DATE
2025.12
담당 DRWN. BY

입찰명 ACAD#
DRWG NO.
A-502

작업번호 JOB NO.
REV NO.
SHEET NO.

도면명 DRAWING TITLE
배면도



* ▼표시 - 소방관 진입창 설치
(지름20cm이상의 역삼각형 표시
- 붉은색, 반사처리 등)

우측면도
축척:1/100

좌측면도
축척:1/100



백이건축사사무소
서울특별시 강북구 삼양로 361. 2층
TEL.(대표)02-908-8894, FAX:02-908-8896

NO.	DATE	REVISION DESCRIPTION	DRWN.	CHK'D	APP'D

공사명 PROJECT TITLE
서울특별시 도봉구 창2동 621-43번지
도시형생활주택 단지형 다세대주택 신축공사

승인 APPROVED BY
설계 DESIGNED BY

규모 3
CHK'D BY
규모 2
CHK'D BY
규모 1
CHK'D BY
축척 SCALE
날자 DATE
2025.12
담당 DRWN. BY

입찰명 ACAD#
DRWG NO.
A-503

작업번호 JOB NO.
REV NO.
SHEET NO.

도면명 DRAWING TITLE
우측면도
좌측면도