


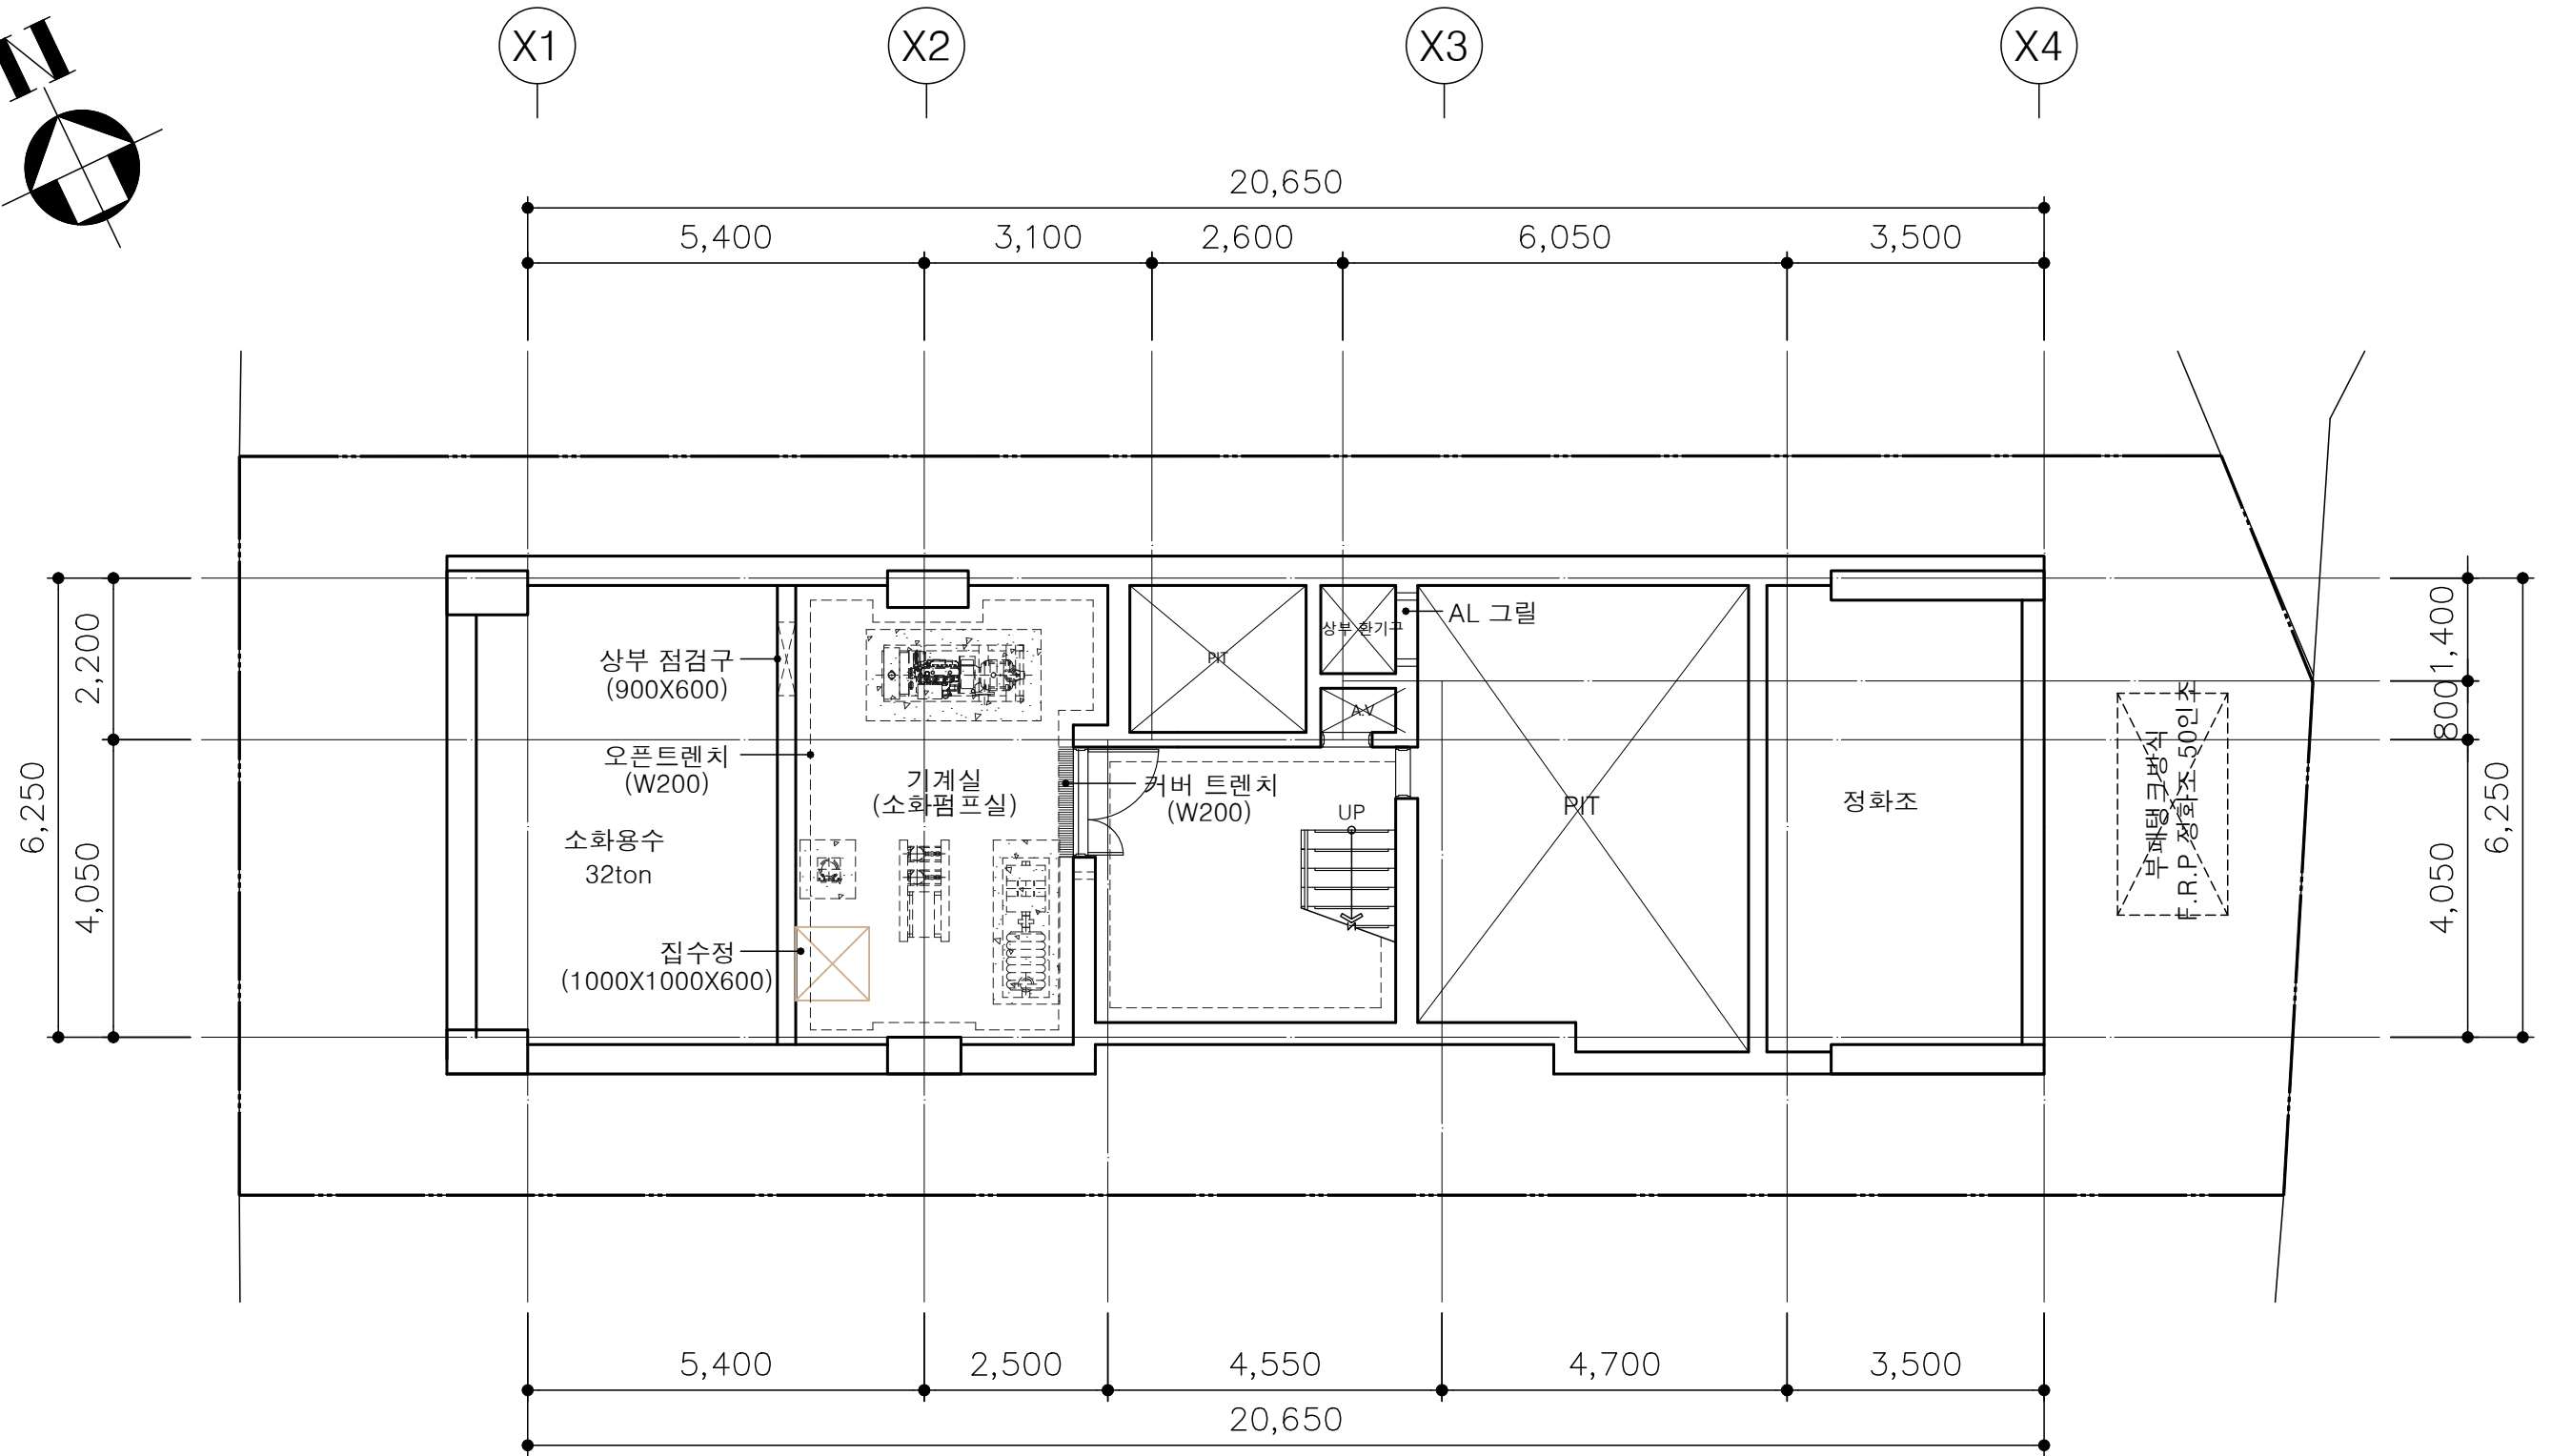
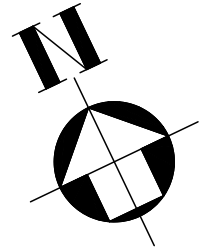


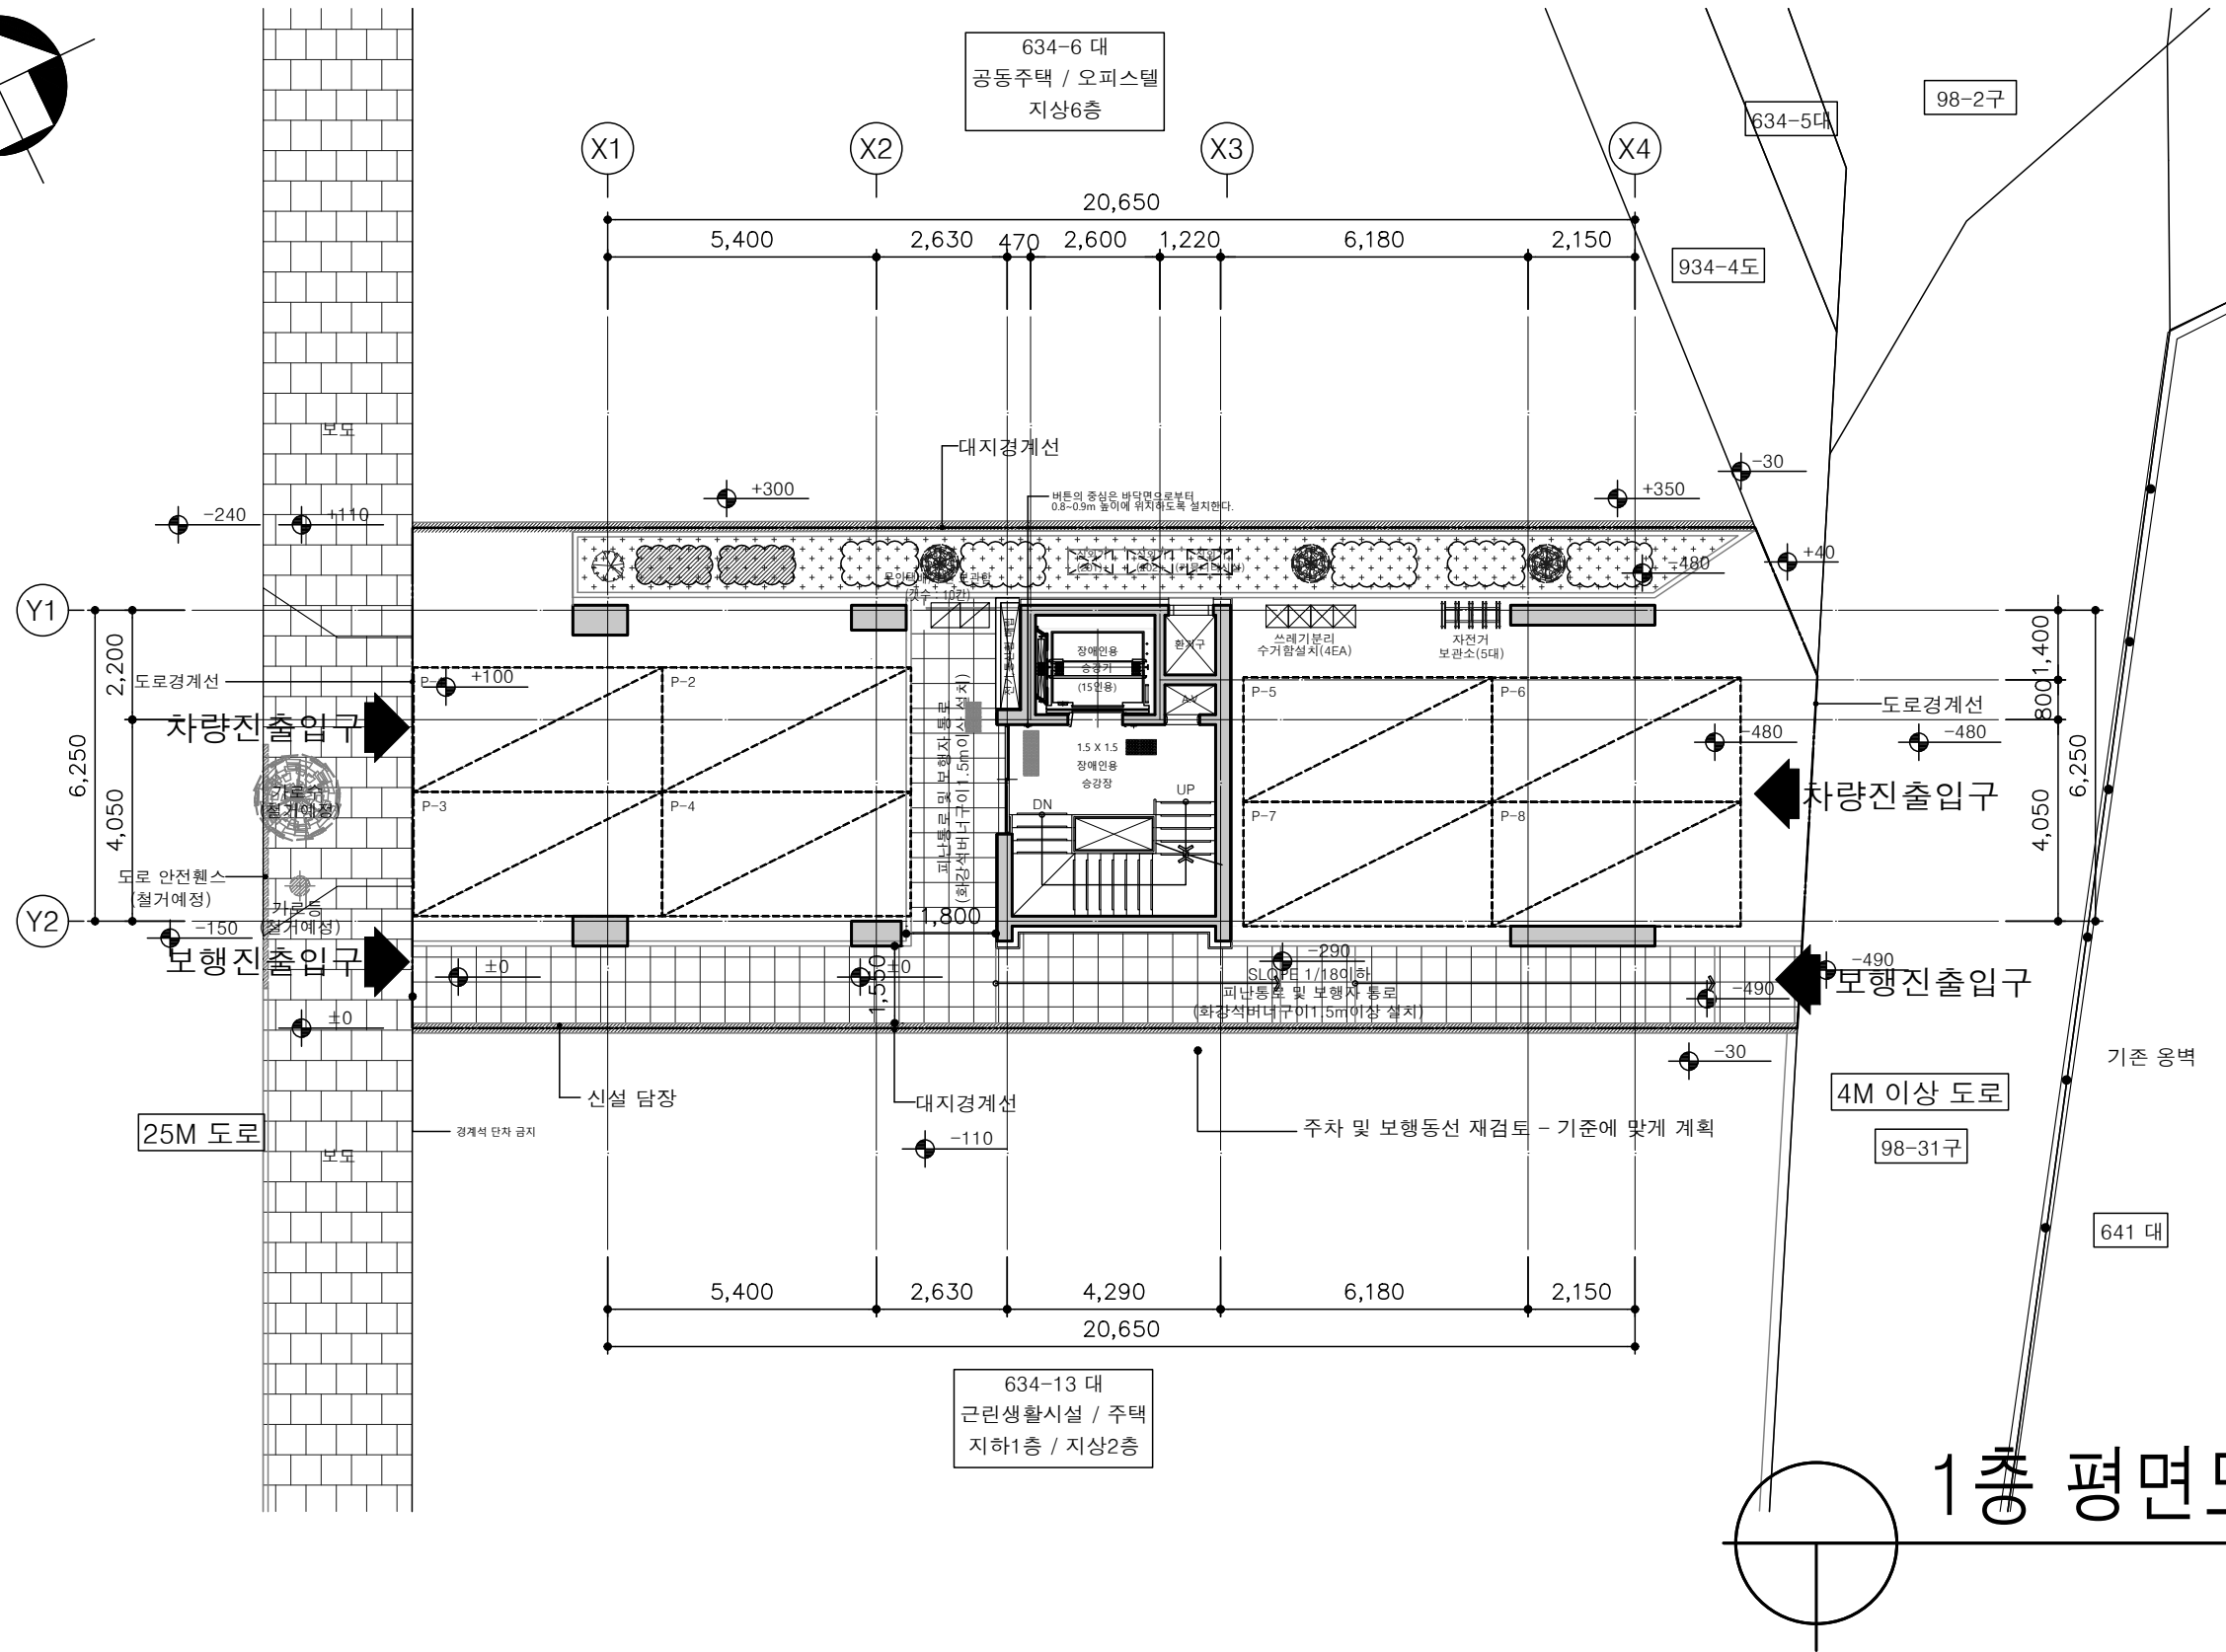

지하1층 평면도
축척:1/100

비밀 생활 건축 사무소 서울특별시 도봉구 마들로 684-9 T. 02 - 725 - 3491 상가동 311호 (도봉동, 서원아파트) F. 070 - 4337 - 0902	설계명 PROJECT TITLE 도봉구 도봉동 634-21 신축공사	노트 NOTE -장애인 편의시설 관련 사항 : 장애인, 노인, 임산부 등의 편의증진보장에 관한 법률/시행령/시행규칙에 준하여 설치 기준 및 계획도를 참고하여, 담당자와 협의 후 시공할 것. - 공용으로 사용되는 모든 출입구(문) (근생, 계단실, 일반화장실 등.) * 유효폭 0.9m 이상 설치 * 손잡이 높이 0.8~0.9m 설치 형태는 레버형, 수평 또는 수직 막대형으로 설치. * 출입구(문) 단차 없이 설치. * 출입구(문) 측면 1.5m 높이에 실명점자표지판을 설치. * 자동문이 아닐 경우 출입구(문) 옆에 0.6m 이상의 활동공간을 확보.(신축) * 주출입구 높이차이 없이 평탄하게 설치. * 안내표지판 및 촉지도식안내표지판등의 설치 위치는 준공전 반드시 점검자와 협의하여 설치 할 것. * 방화문 SILL TYPE -디테일추가-(참고도서에 있음)	설계구분 PROJECT KINDS	담당 DRAWN BY :	축척 SCALE 1/100	도면명칭 DRAWING TITLE
			설계번호 PROJECT NO.	검토 CHECKED BY : PIC APPROVED BY :	날짜 DATE 2023.12.	지하1층 평면도 도면번호 SHEET NO. A-028

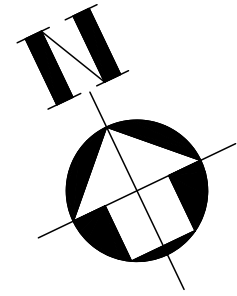


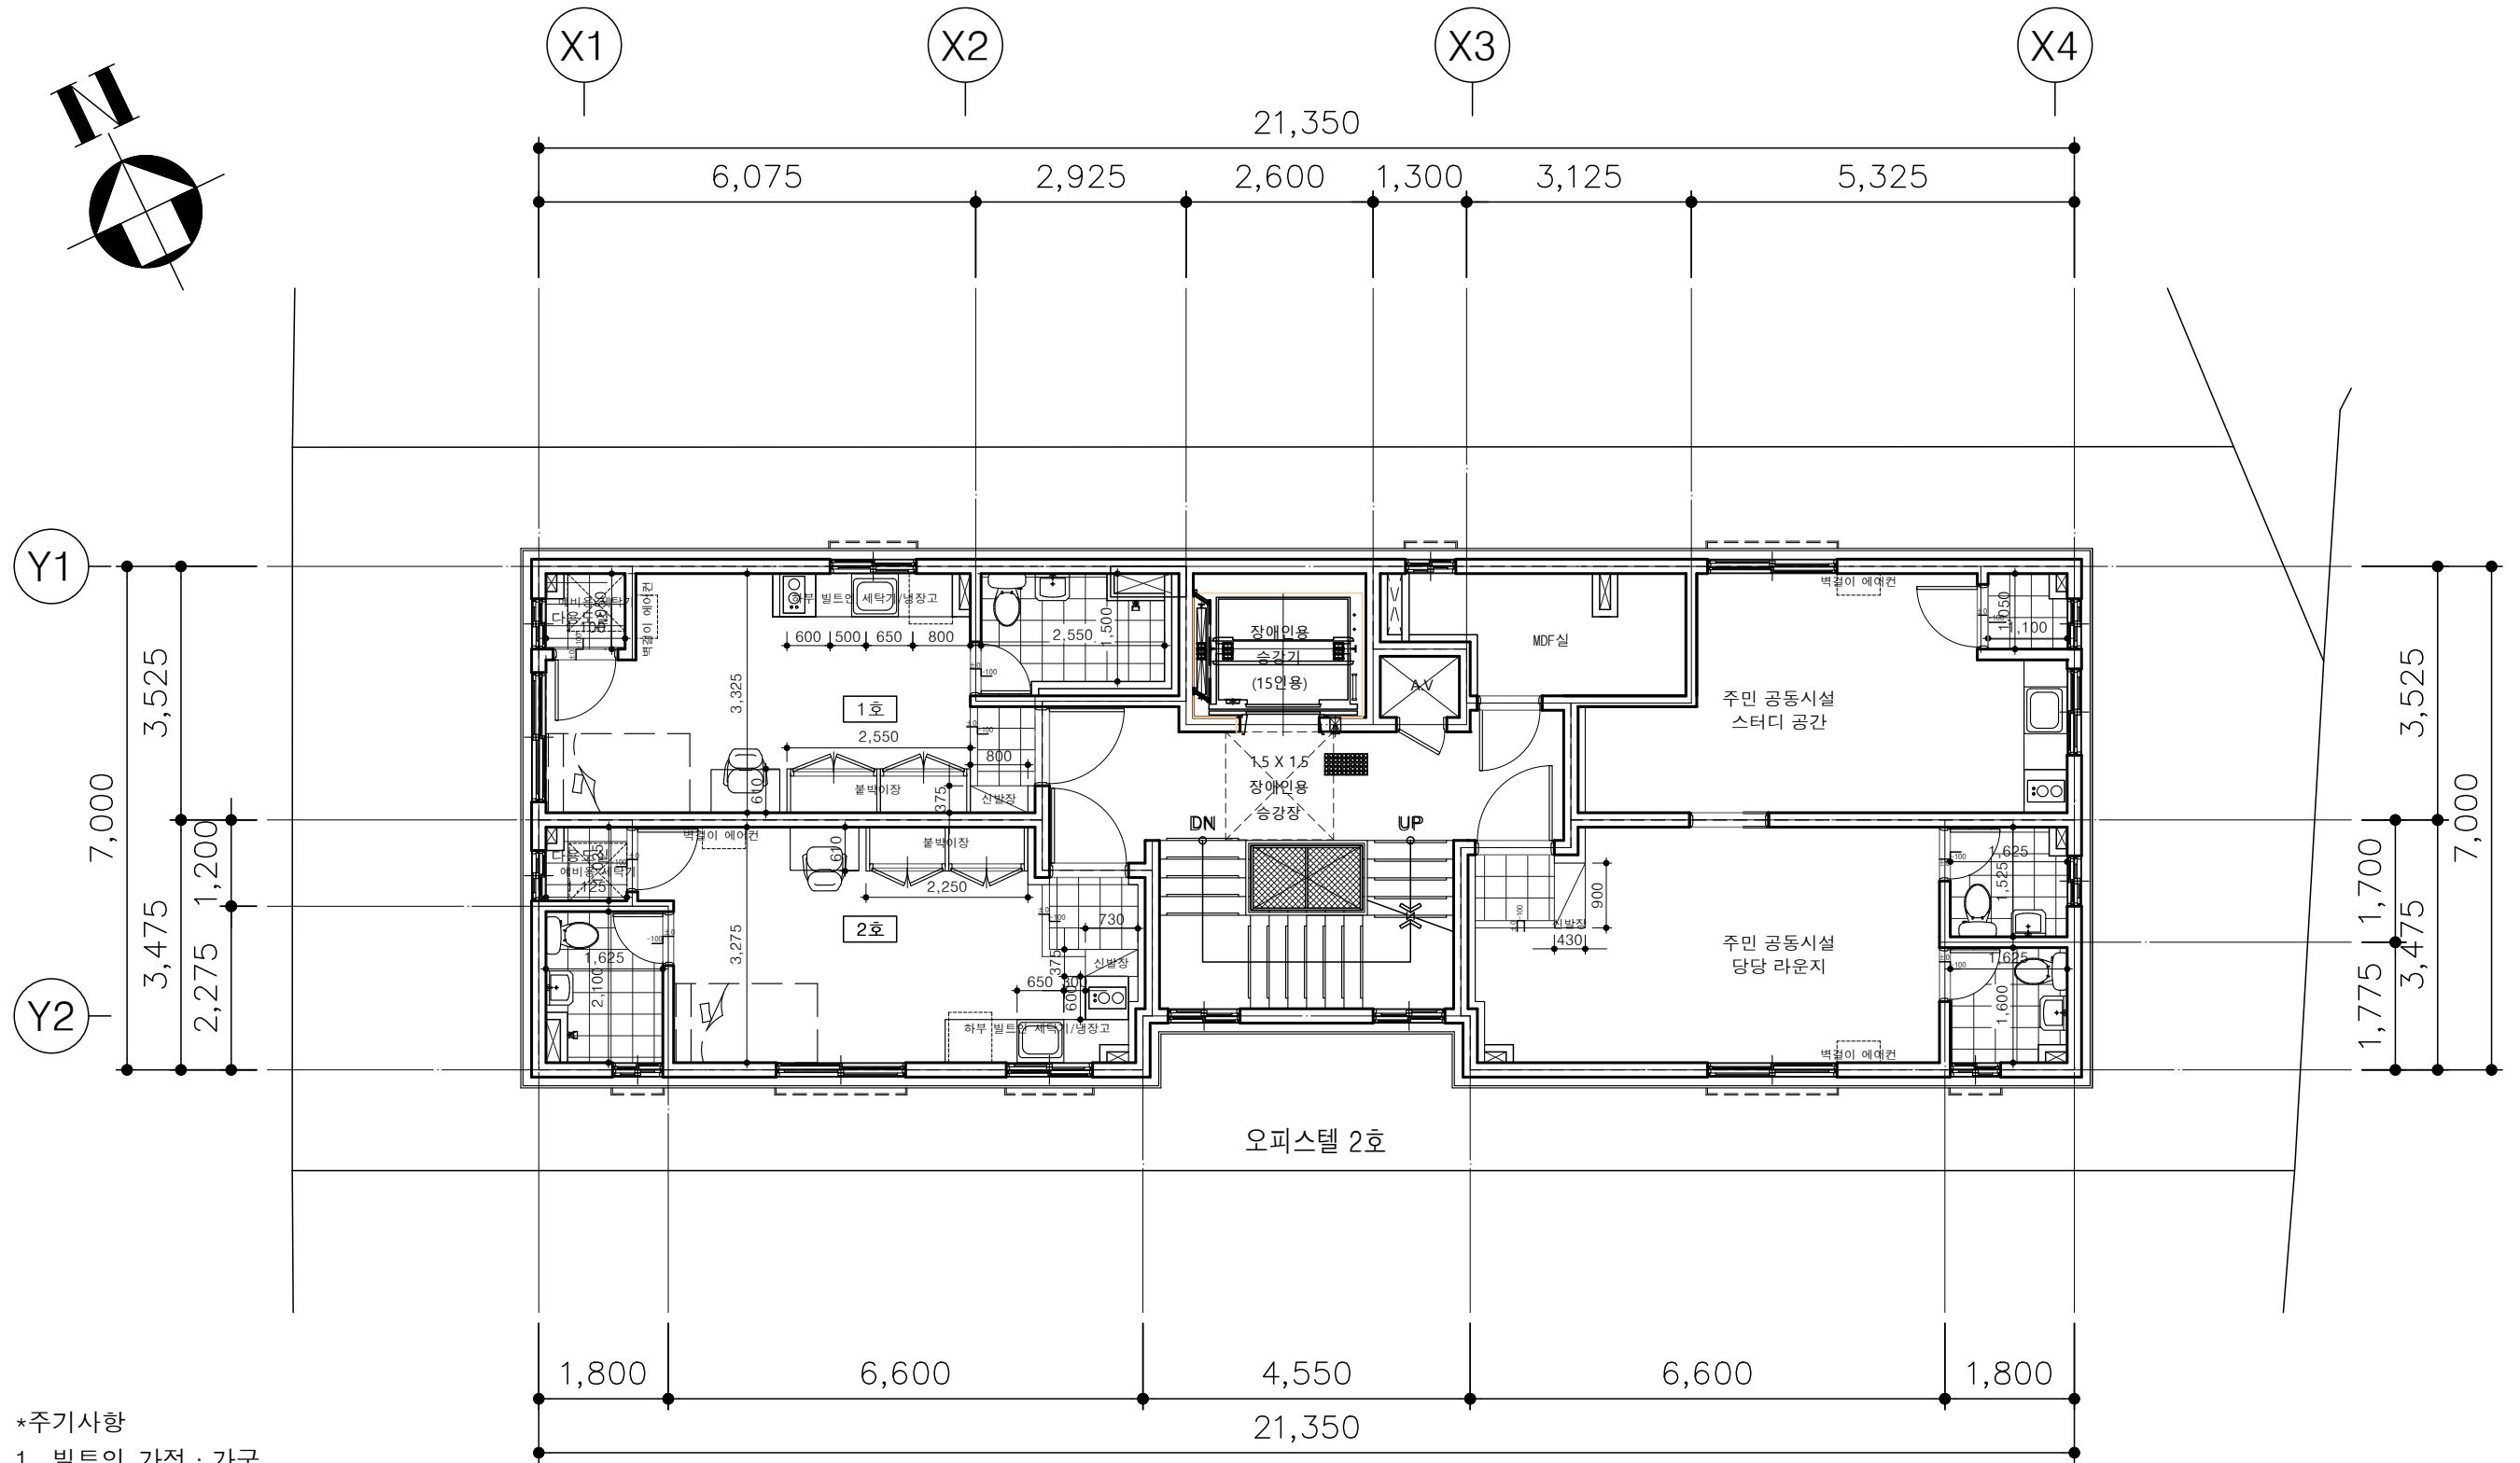

- *주기사항
1. 빌트인 가전 · 가구
냉장고, 세탁기, 벽걸이에어컨, 불박이장 또는 이동식 옷장, 책상 전부 설치
 2. 거실 단변 폭 최소 2,700mm 이상 계획
 3. 욕실 최소크기 적용 및 세면대와 샤워공간 분리 (외벽에 면할 경우 : 환기창 600X400 이상 설치 적용)
 4. 주방가구 크기
냉장고 : 1,000mm이상(청년800mm) , 가열대 : 2구 전기형 쿡탑(벽면 및 가구·가전으로부터 최소 100mm이격)
조리대 : 500mm 이상 , 개수대 : 630 싱크 이상, 상부 SST 건조선반 설치
 5. 그 외 우리공사 계획설계기준 및 디자인가이드라인 준수하여 시공

2층 평면도
축척:1/100

비밀 생활 건축사무소 서울특별시 도봉구 도당로 122 T. 02 - 725 - 3491 (방학동, 2층) F. 070 - 4015 - 2227	설계명 PROJECT TITLE 도봉구 도봉동 634-21 신축공사	노트 NOTE -장애인 편의시설 관련 사항 : 장애인, 노인, 임산부 등의 편의증진보장에 관한 법률/시행령/시행규칙에 준하여 설치 기준 및 계획도를 참고하여, 담당자와 협의 후 시공할 것. - 공용으로 사용되는 모든 출입구(문) (근생, 계단실, 일반화장실 등.) * 유효폭0.9m이상설치 * 손잡이 높이 0.8~0.9m 설치 형태는 레버형, 수평 또는 수직 막대형으로 설치. * 출입구(문)단차 없이 설치. * 출입구(문) 측면 1.5m 높이에 설명점자표지판을 설치. * 자동문이 아닐 경우 출입구(문) 옆에 0.6m 이상의 활동공간을 확보.(신축) * 주출입구 높이가차 없이 평탄하게 설치. * 안내표지판 및 촉지도식안내표지판등의 설치 위치는 준공전 반드시 점검자와 협의하여 설치 할 것. * 방화문 SILL TYPE -디테일추가-(참고도서에 있음)	설계구분 PROJECT KINDS	담당 DRAWN BY :	축척 SCALE 1/100	도면명칭 DRAWING TITLE
			설계번호 PROJECT NO.	검토 CHECKED BY : PIC APPROVED BY :	날짜 DATE 2023.12.	지상2층 평면도 도면번호 SHEET NO. A-030

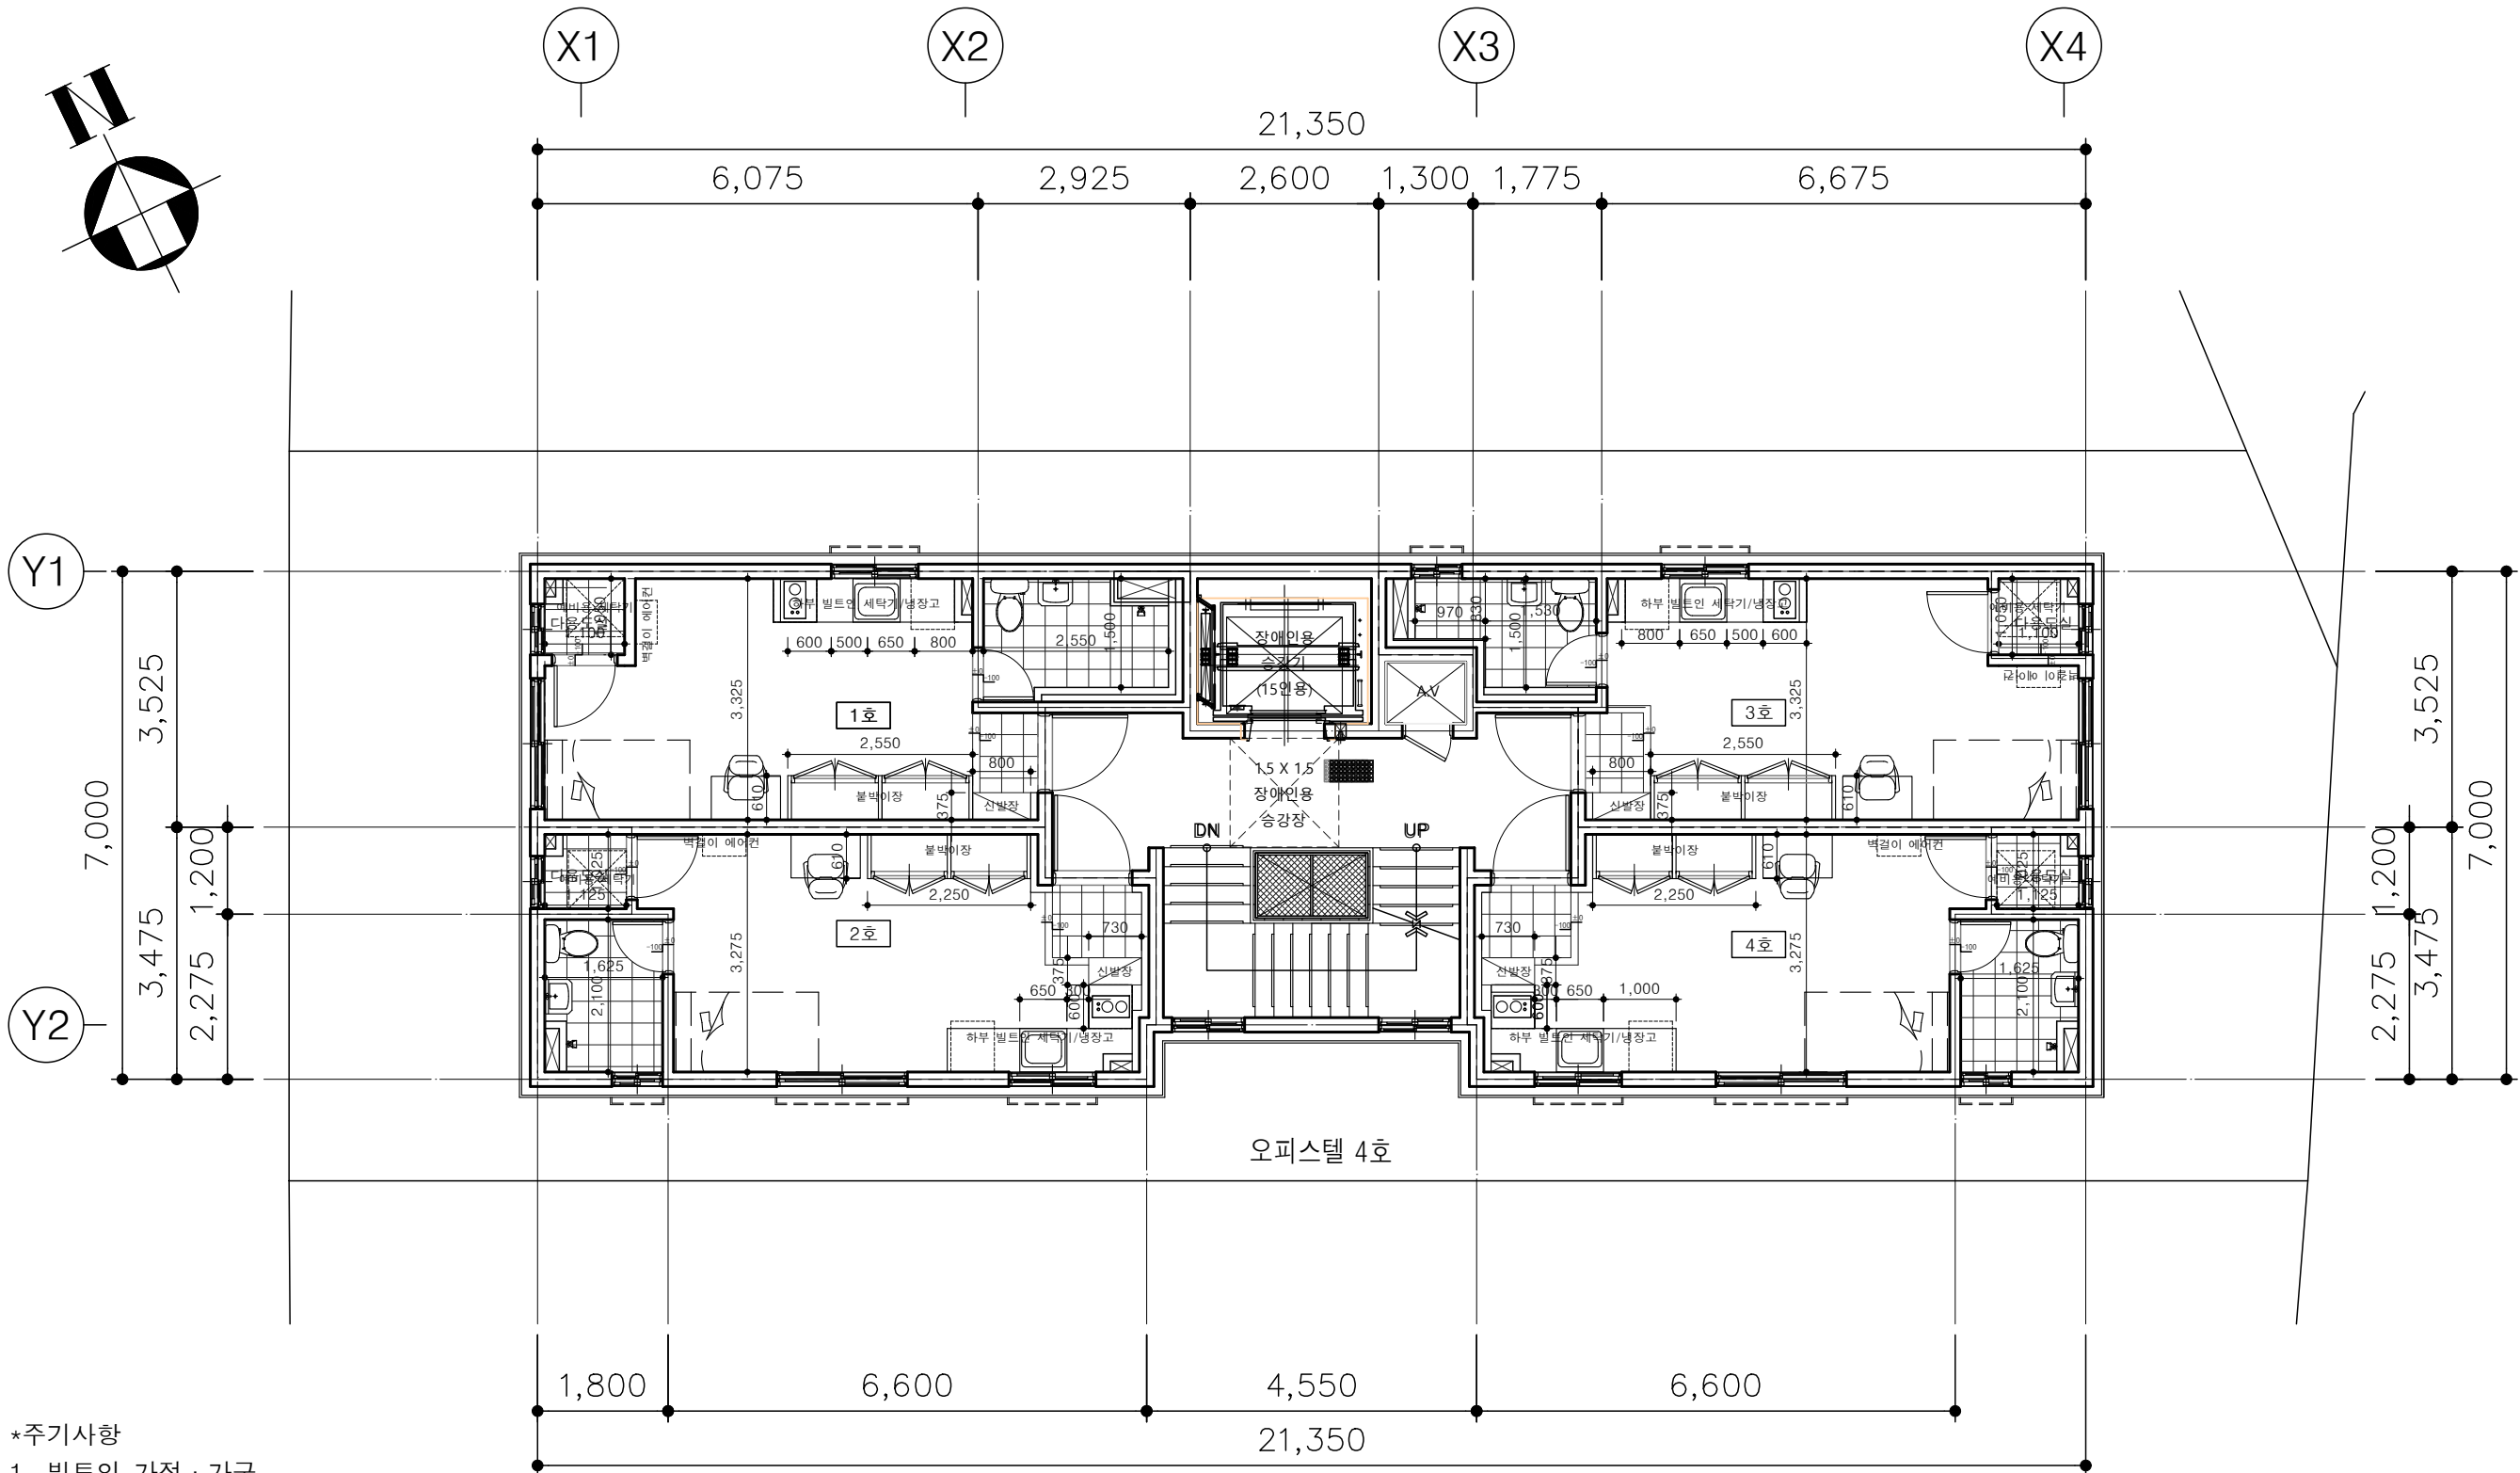

*주기사항

1. 빌트인 가전 · 가구

냉장고, 세탁기, 벽걸이에어컨, 불박이장 또는 이동식 옷장, 책상 전부 설치

2. 거실 단변 폭 최소 2,700mm 이상 계획

3. 욕실 최소크기 적용 및 세면대와 샤워공간 분리 (외벽에 면할 경우 : 환기창 600X400 이상 설치 적용)

4. 주방가구 크기

냉장고 : 1,000mm이상(청년800mm) , 가열대 : 2구 전기형 쿡탑(벽면 및 가구·가전으로부터 최소 100mm이격)

조리대 : 500mm 이상 , 개수대 : 630 싱크 이상, 상부 SST 건조선반 설치

5. 그 외 우리공사 계획설계기준 및 디자인가이드라인 준수하여 시공

3층 평면도

축척:1/100

비밀 생활 건축사사무소
서울특별시 도봉구 도당로 122 T. 02 - 725 - 3491
(방학동, 2층) F. 070 - 4015 - 2227

설계명 PROJECT TITLE

도봉구 도봉동 634-21 신축공사

노트 NOTE -장애인 편의시설 관련 사항

: 장애인, 노인, 임산부등의 편의증진보장에 관한 법률/시행령/시행규칙에 준하여 설치 기준 및 계획도를 참고하여, 담당자와 협의 후 시공할 것.
- 공용으로 사용되는 모든 출입구(문) (근생, 계단실, 일반화장실 등.) * 유요폭0.9m이상설치 * 손잡이 높이 0.8~0.9m 설치
형태는 레버형, 수평 또는 수직 막대형으로 설치. * 출입구(문)단차 없이 설치. * 출입구(문) 측면 1.5m 높이에 실명점자표지판을 설치.
* 자동문이 아닐 경우 출입구(문) 옆에 0.6m 이상의 활동공간을 확보.(신축) * 주출입구 높이가차이 없이 평탄하게 설치.
* 안내표지판 및 촉지도식안내표지판등의 설치 위치는 준공전 반드시 점검자와 협의하여 설치 할 것. * 방화문 SILL TYPE -디테일추가-(참고도서에 있음)

설계구분 PROJECT KINDS

설계번호 PROJECT NO.

담당 DRAWN BY :

담당 DRAWN BY :

검토 CHECKED BY :

PIC APPROVED BY :

축척
SCALE 1/100


날짜
DATE 2023.12.

도면명칭 DRAWING TITLE

지상3층 평면도

도면번호 SHEET NO.

A-031

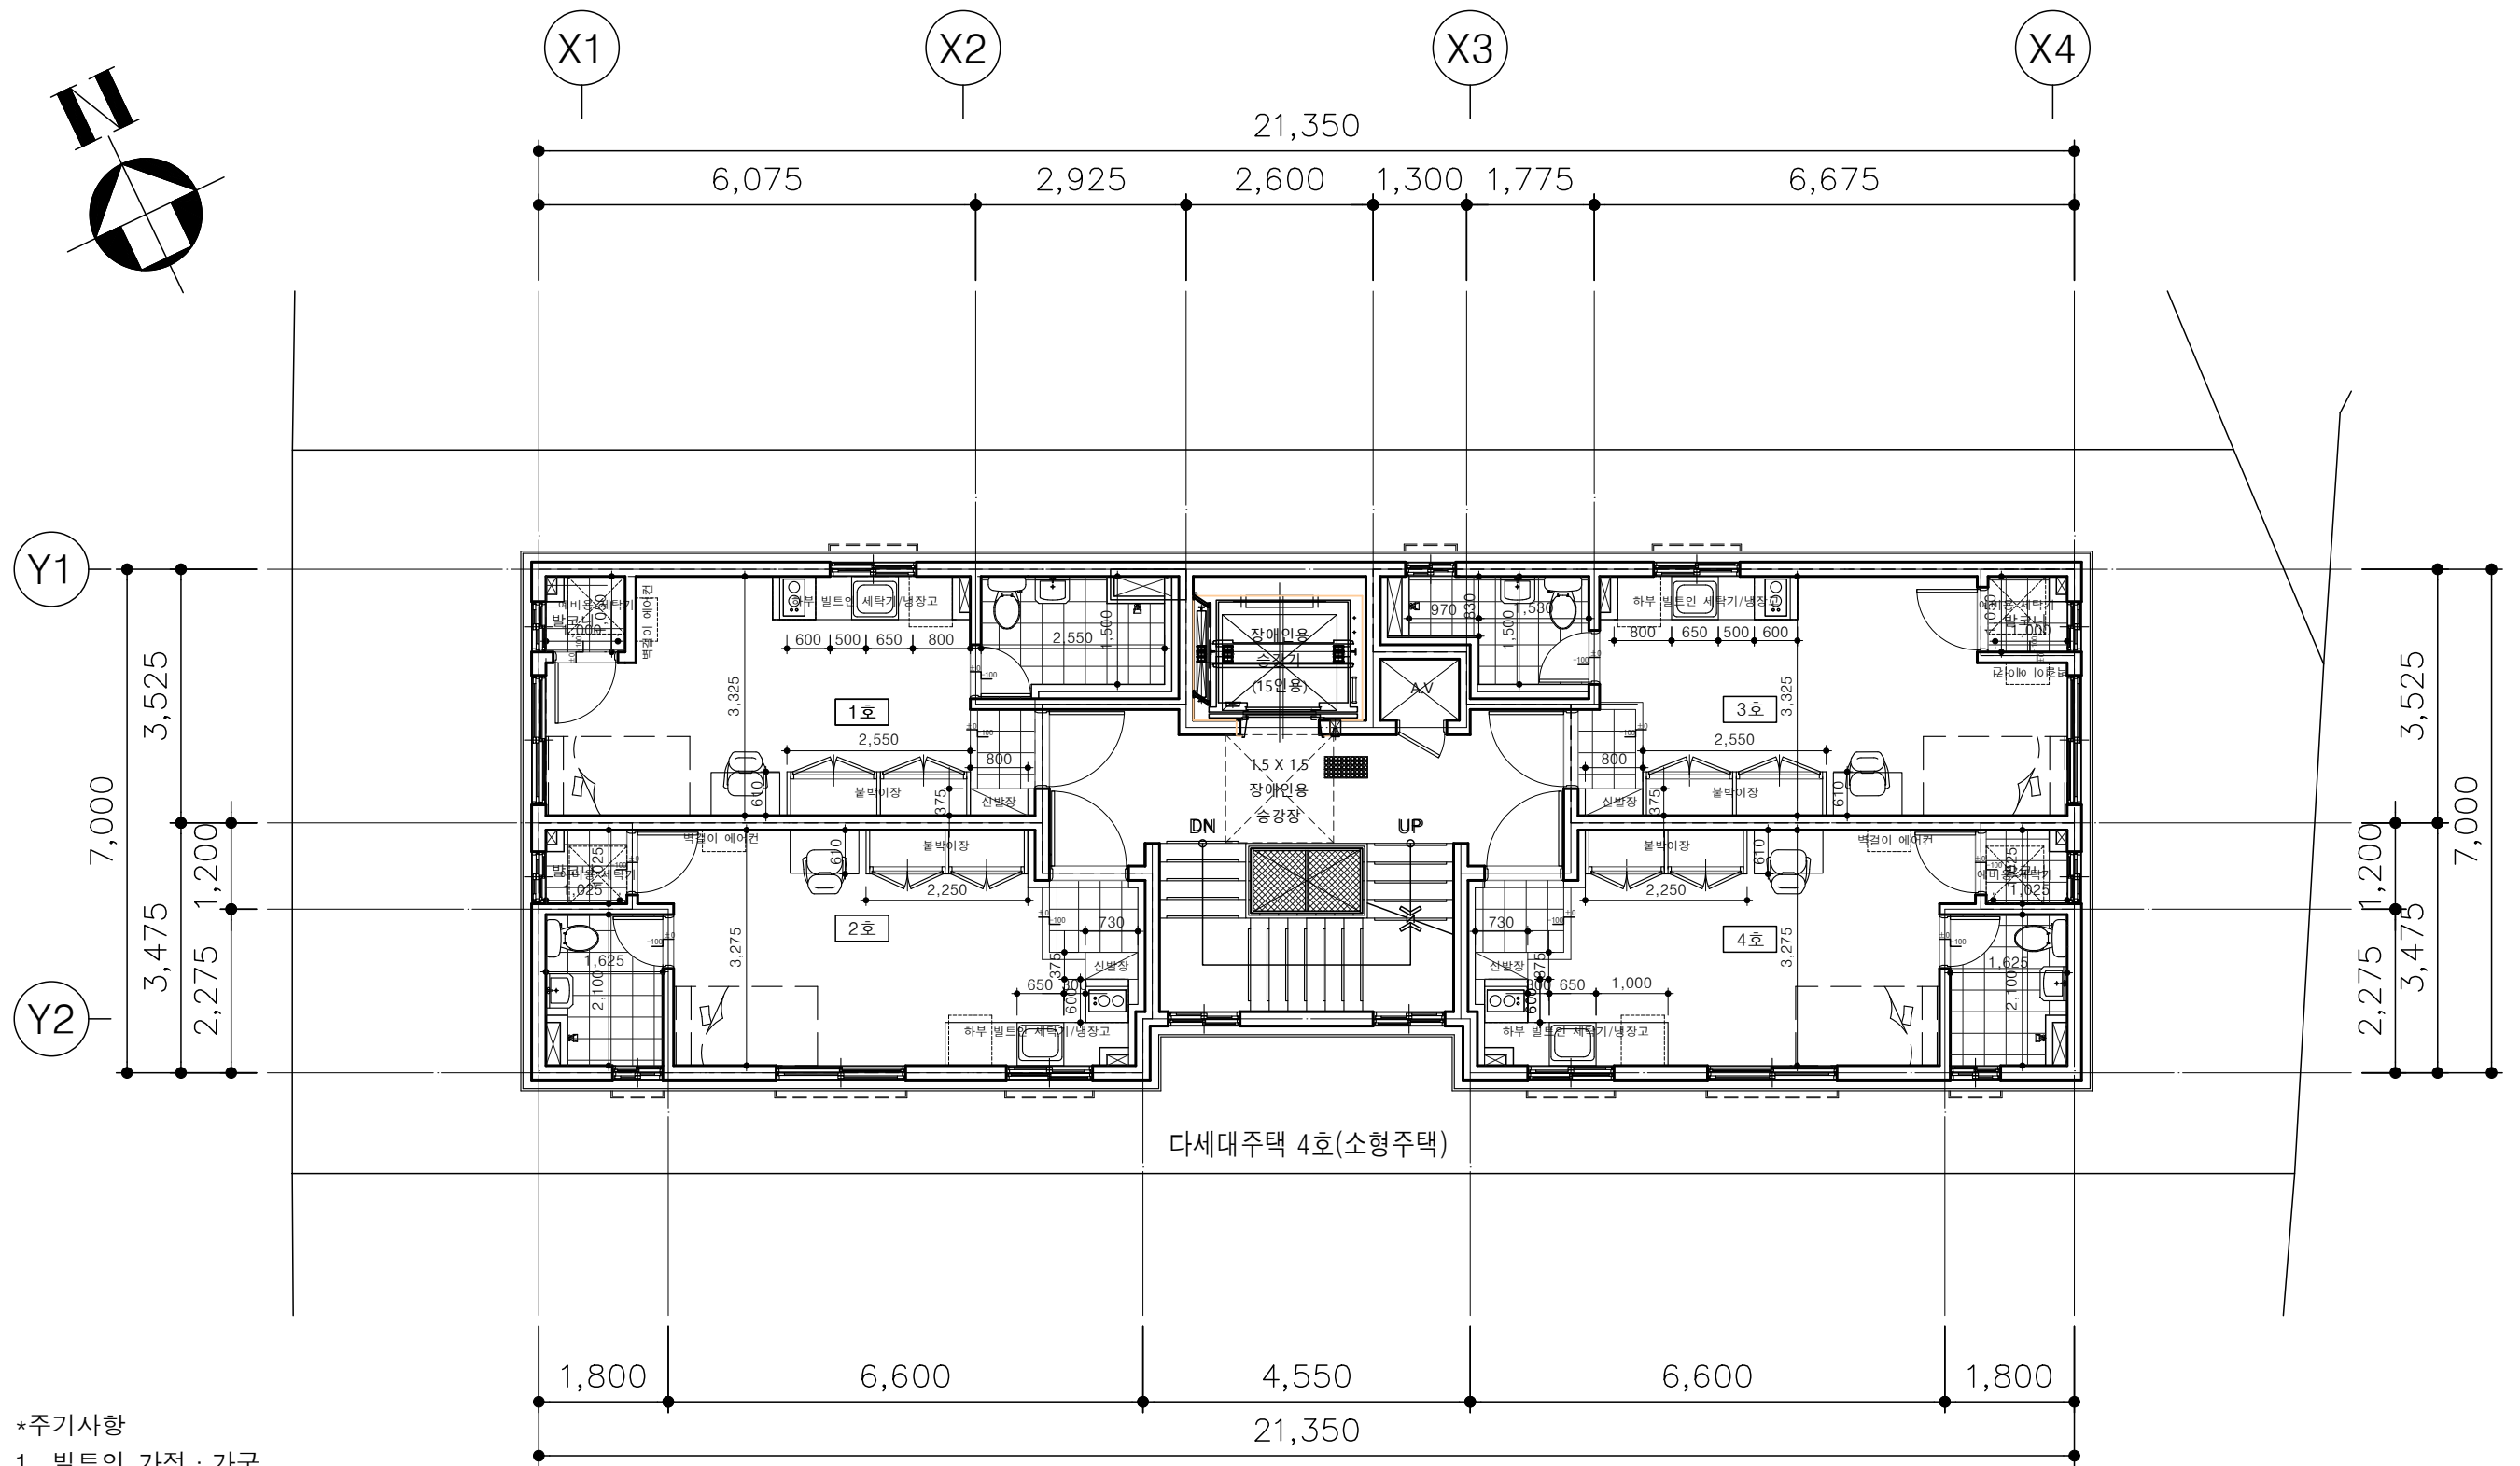



*주기사항

1. 빌트인 가전 · 가구
냉장고, 세탁기, 벽걸이에어컨, 불박이장 또는 이동식 옷장, 책상 전부 설치
2. 거실 단변 폭 최소 2,700mm 이상 계획
3. 욕실 최소크기 적용 및 세면대와 샤워공간 분리 (외벽에 면할 경우 : 환기창 600X400 이상 설치 적용)
4. 주방가구 크기
냉장고 : 1,000mm이상(청년800mm) , 가열대 : 2구 전기형 쿡탑(벽면 및 가구·가전으로부터 최소 100mm이격)
조리대 : 500mm 이상 , 개수대 : 630 싱크 이상, 상부 SST 건조선반 설치
5. 그 외 우리공사 계획설계기준 및 디자인가이드라인 준수하여 시공

4~7층 평면도

축척:1/100

미필생활건축사무소 서울특별시 도봉구 도당로 122 T. 02 - 725 - 3491 (방학동, 2층) F. 070 - 4015 - 2227	설계명 PROJECT TITLE 도봉구 도봉동 634-21 신축공사	노트 NOTE -장애인 편의시설 관련 사항 : 장애인, 노인, 임산부 등의 편의증진보장에 관한 법률/시행령/시행규칙에 준하여 설치 기준 및 계획도를 참고하여, 담당자와 협의 후 시공할 것. - 공용으로 사용되는 모든 출입구(문) (근생, 계단실, 일반화장실 등.) * 유요폭0.9m이상설치 * 손잡이 높이 0.8~0.9m 설치 형태는 레버형, 수평 또는 수직 막대형으로 설치. * 출입구(문)단차 없이 설치. * 출입구(문) 측면 1.5m 높이에 실명점자표지판을 설치. * 자동문이 아닐 경우 출입구(문) 옆에 0.6m 이상의 활동공간을 확보.(신축) * 주출입구 높이차이 없이 평탄하게 설치. * 안내표지판 및 촉지도식안내표지판등의 설치 위치는 준공전 반드시 점검자와 협의하여 설치 할 것. * 방화문 SILL TYPE -디테일추가-(참고도서에 있음)	설계구분 PROJECT KINDS	담당 DRAWN BY :	축척 SCALE 1/100	도면명칭 DRAWING TITLE
			설계번호 PROJECT NO.	검토 CHECKED BY : PIC APPROVED BY :	날짜 DATE 2023.12.	지상4~7층 평면도 도면번호 SHEET NO. A-032

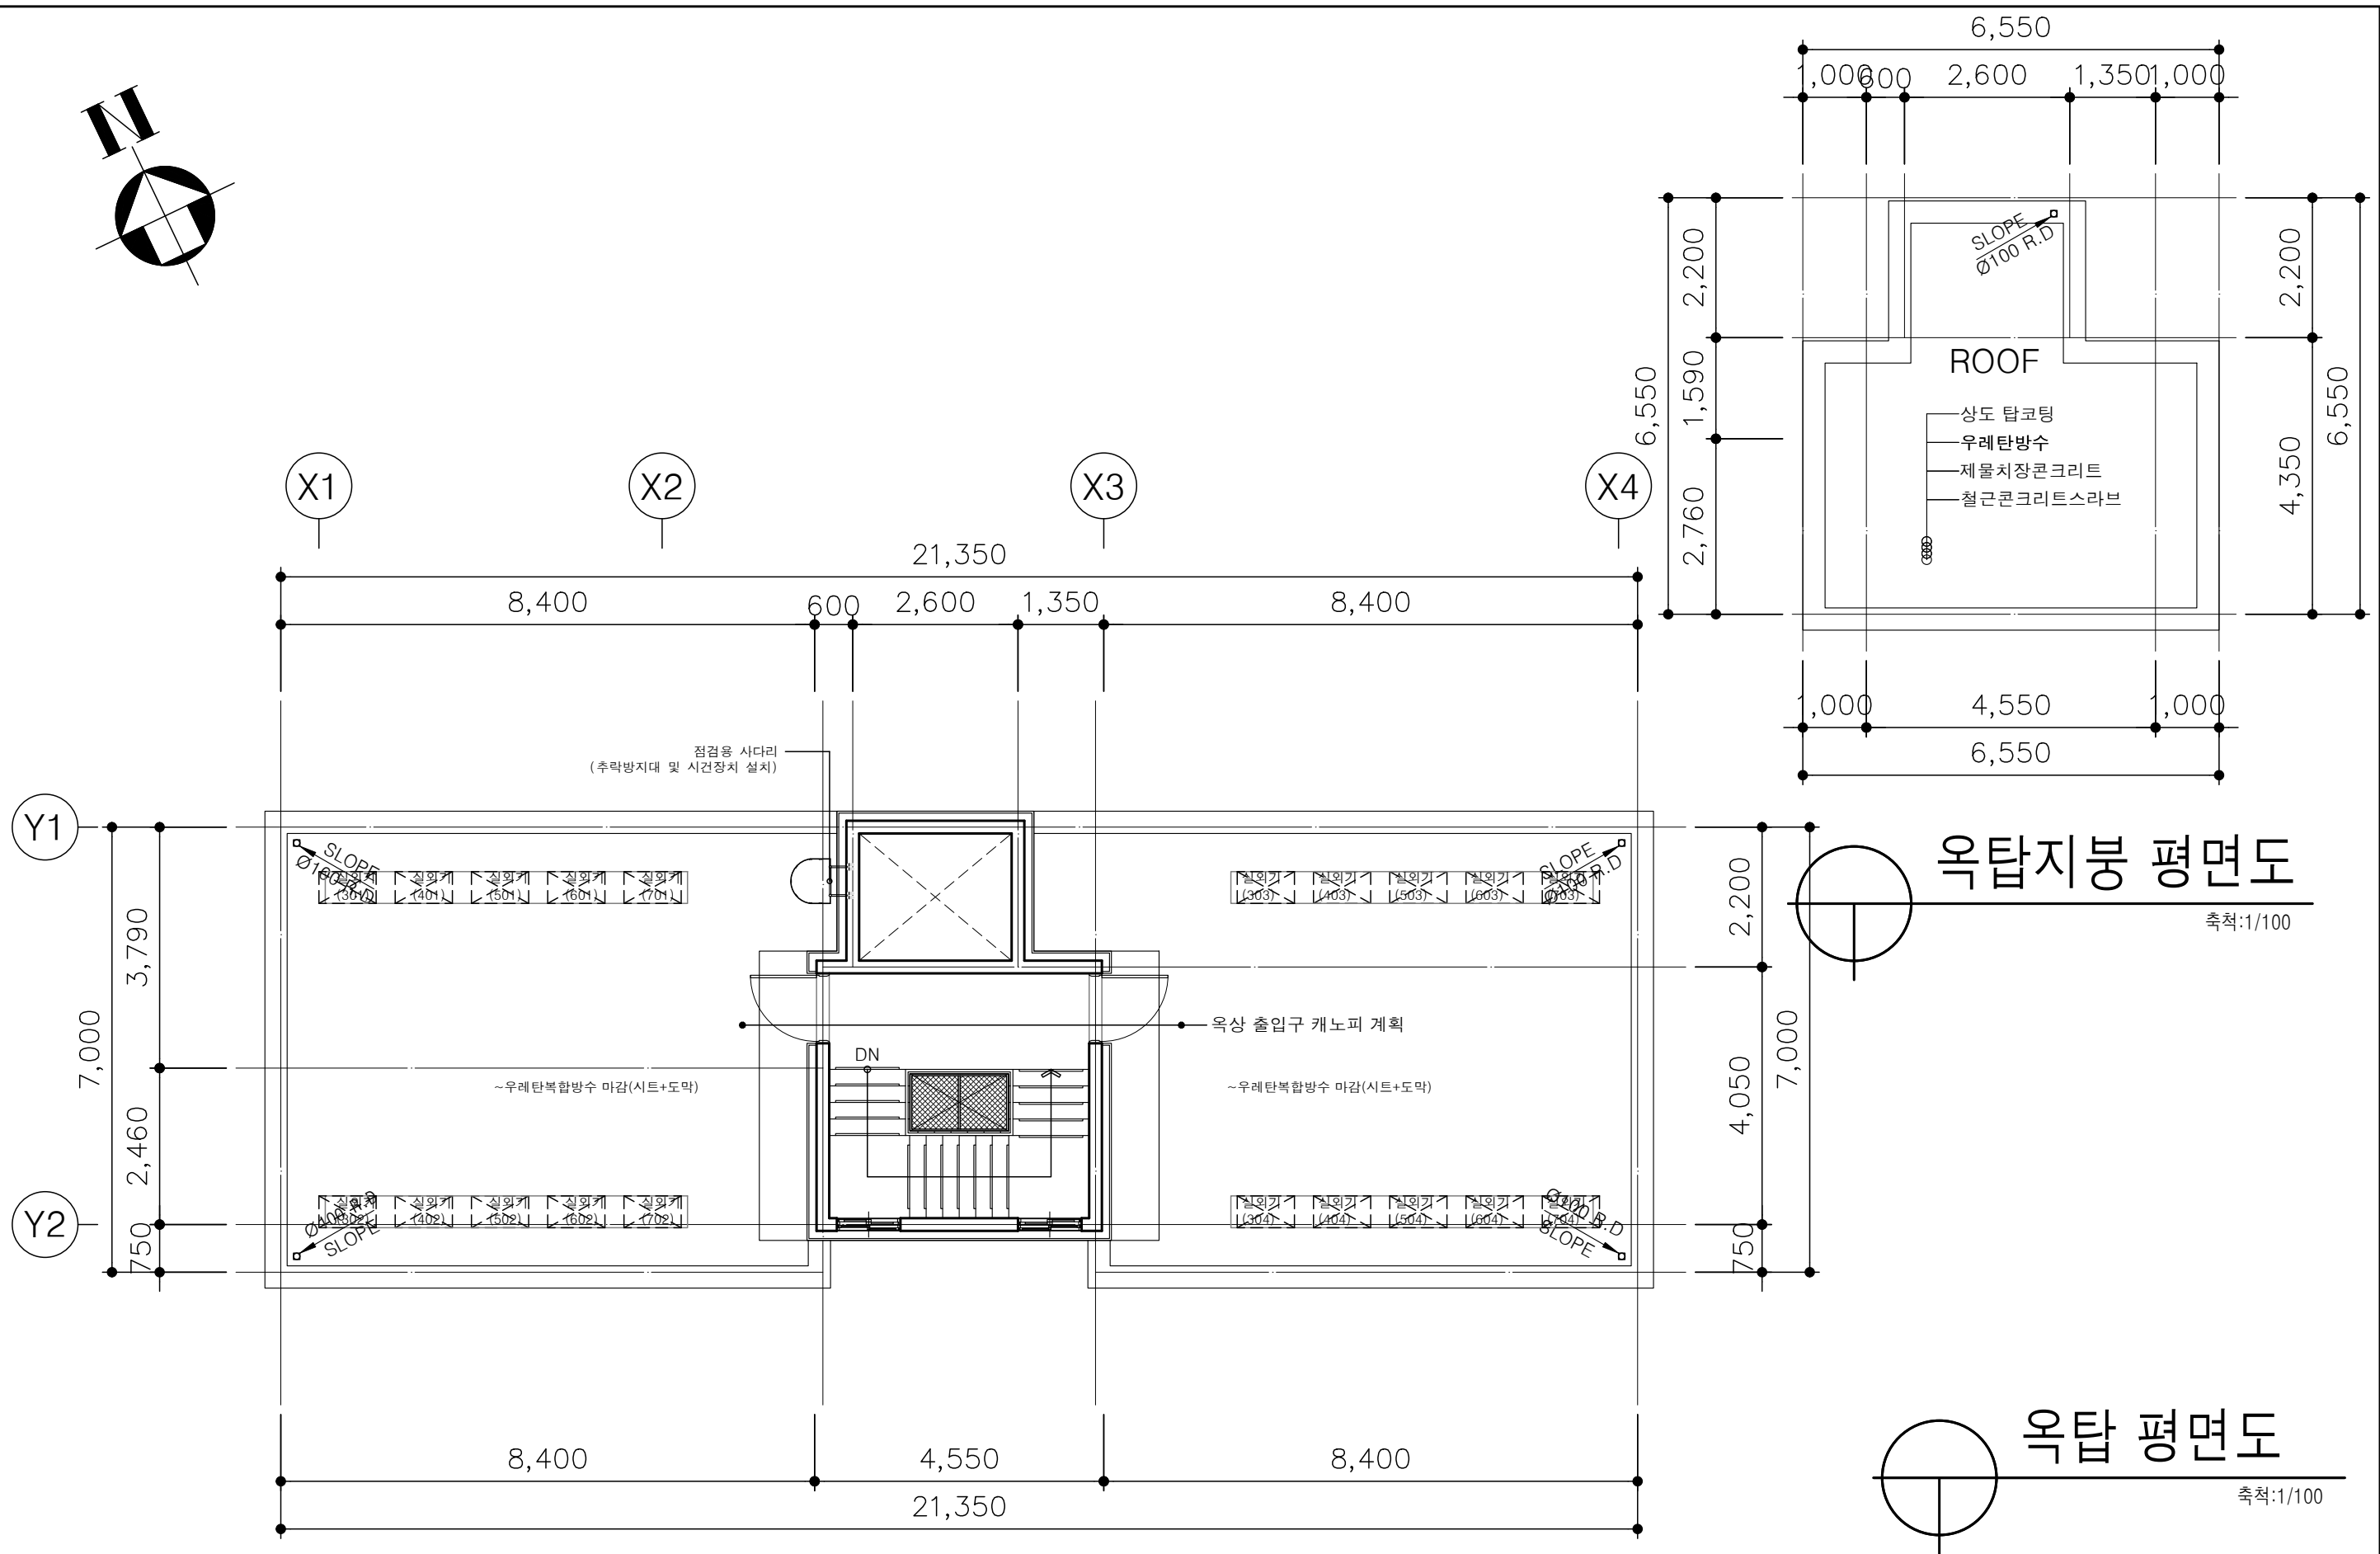
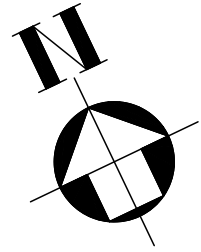




옥탑지붕 평면도


축척:1/100

옥탑 평면도


축척:1/100

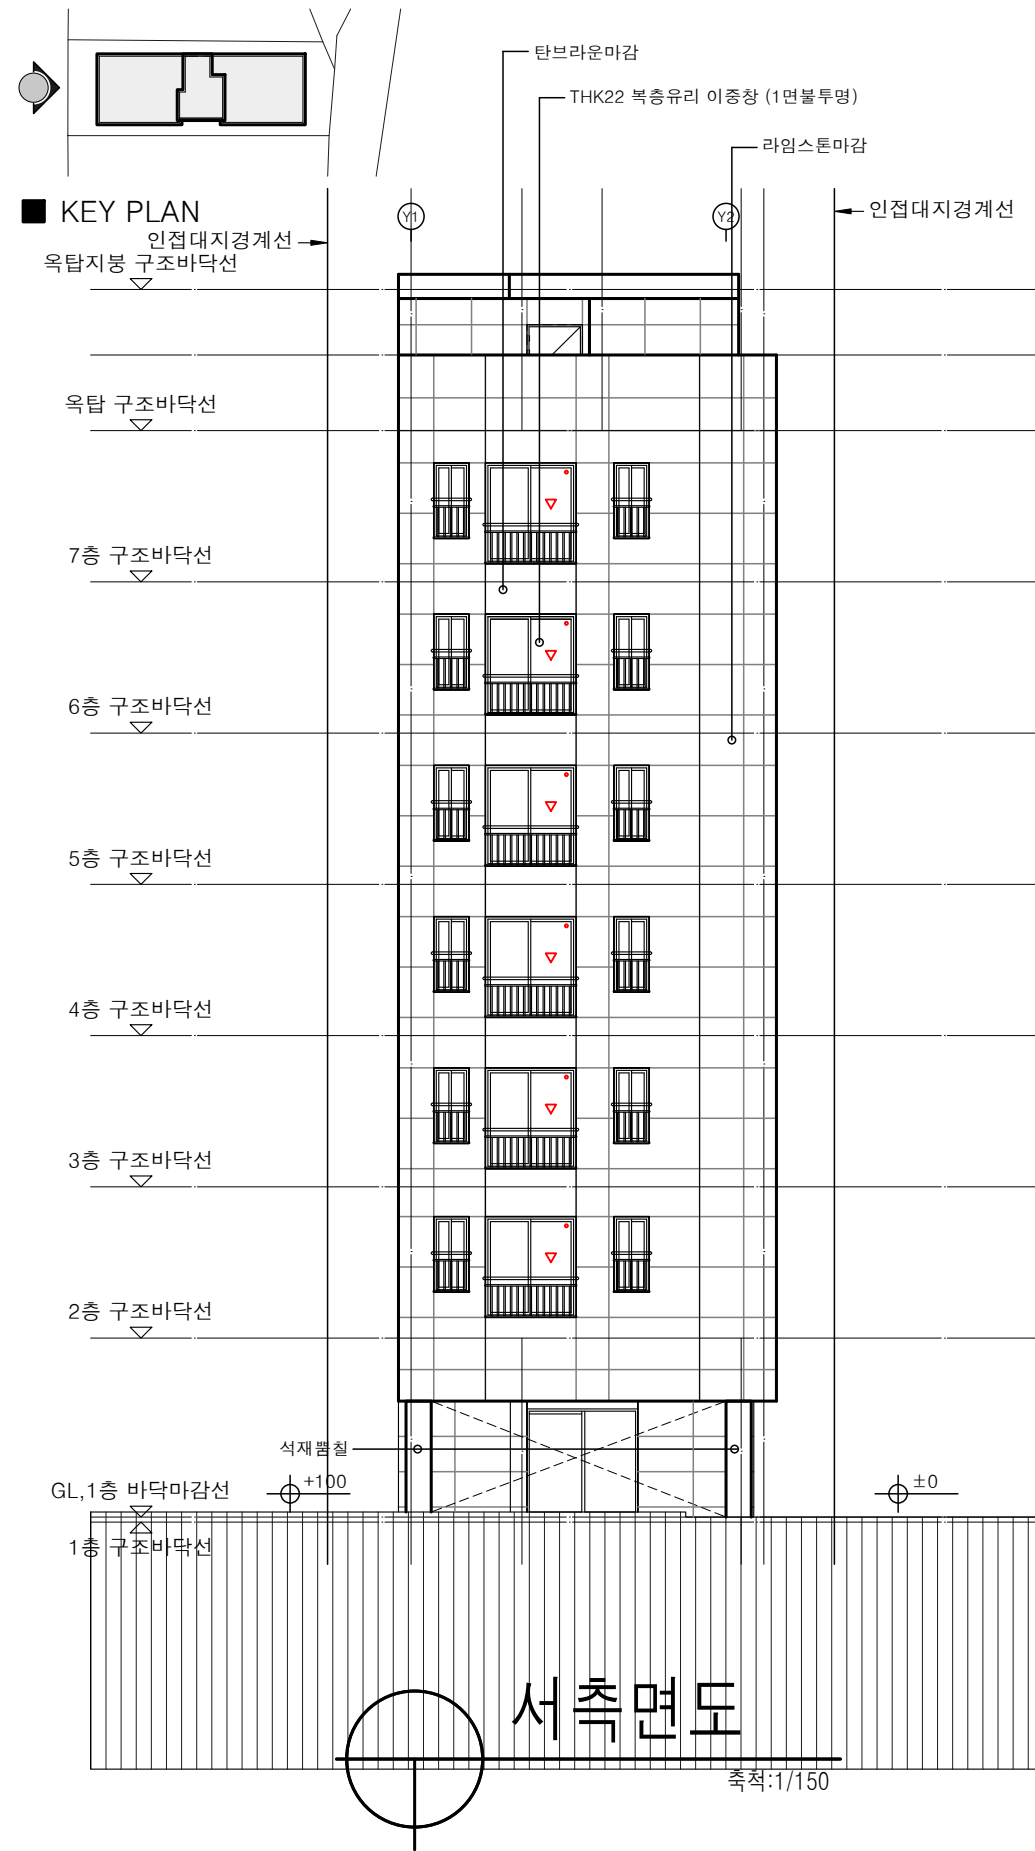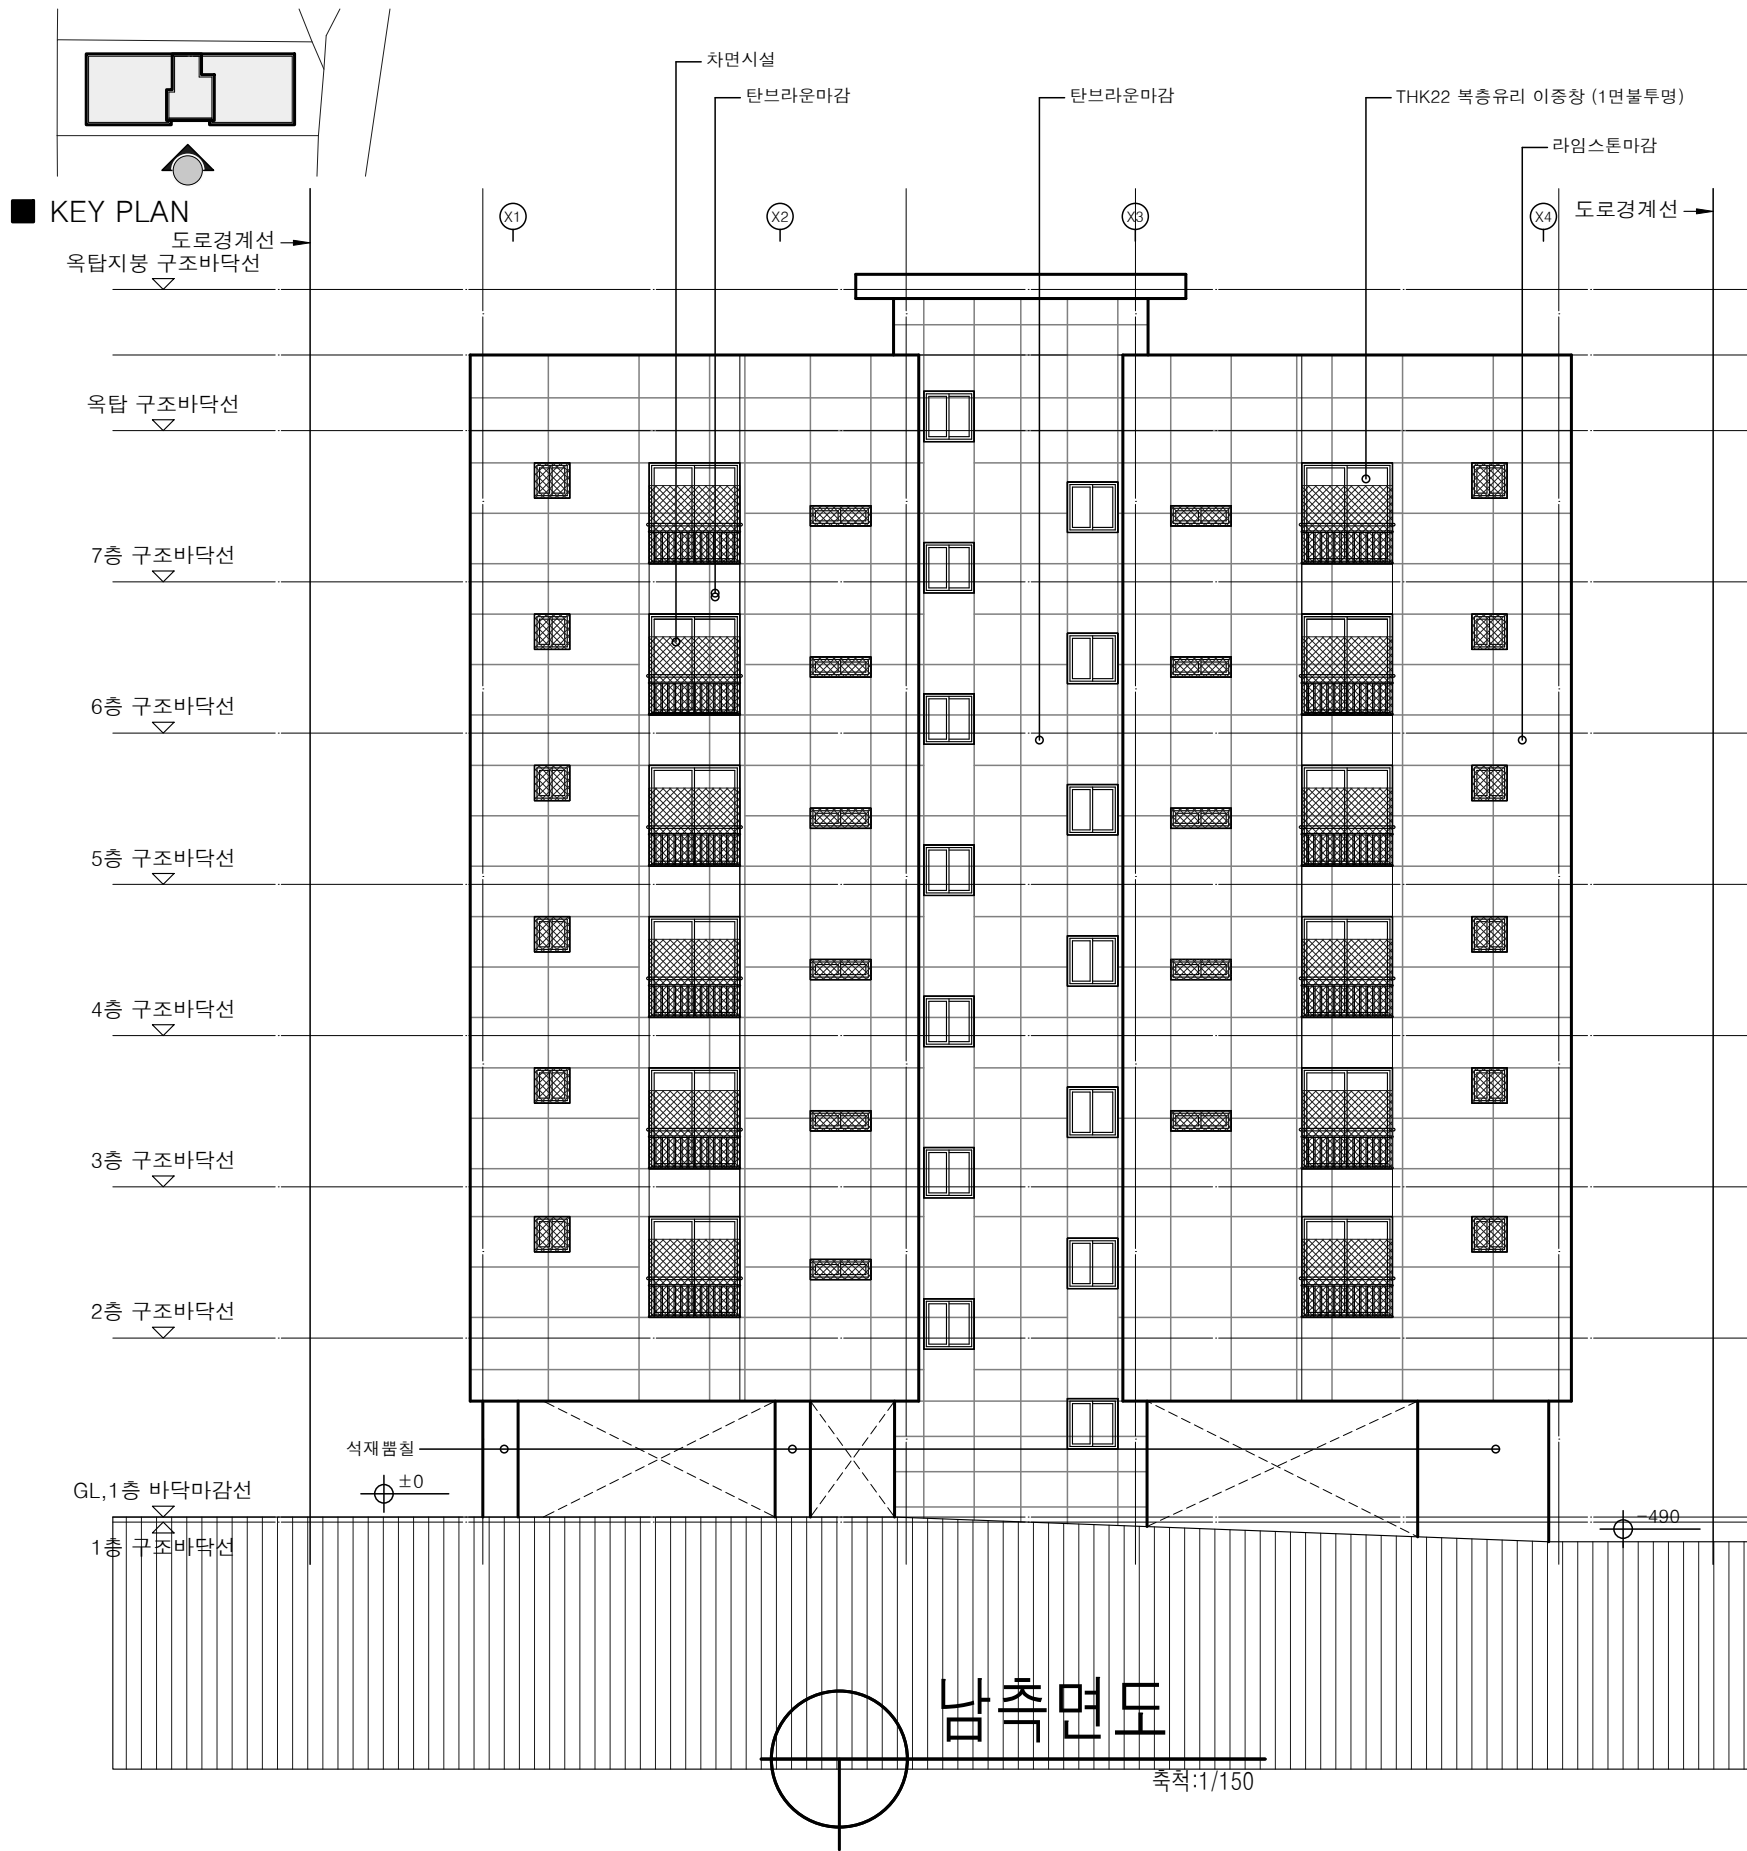

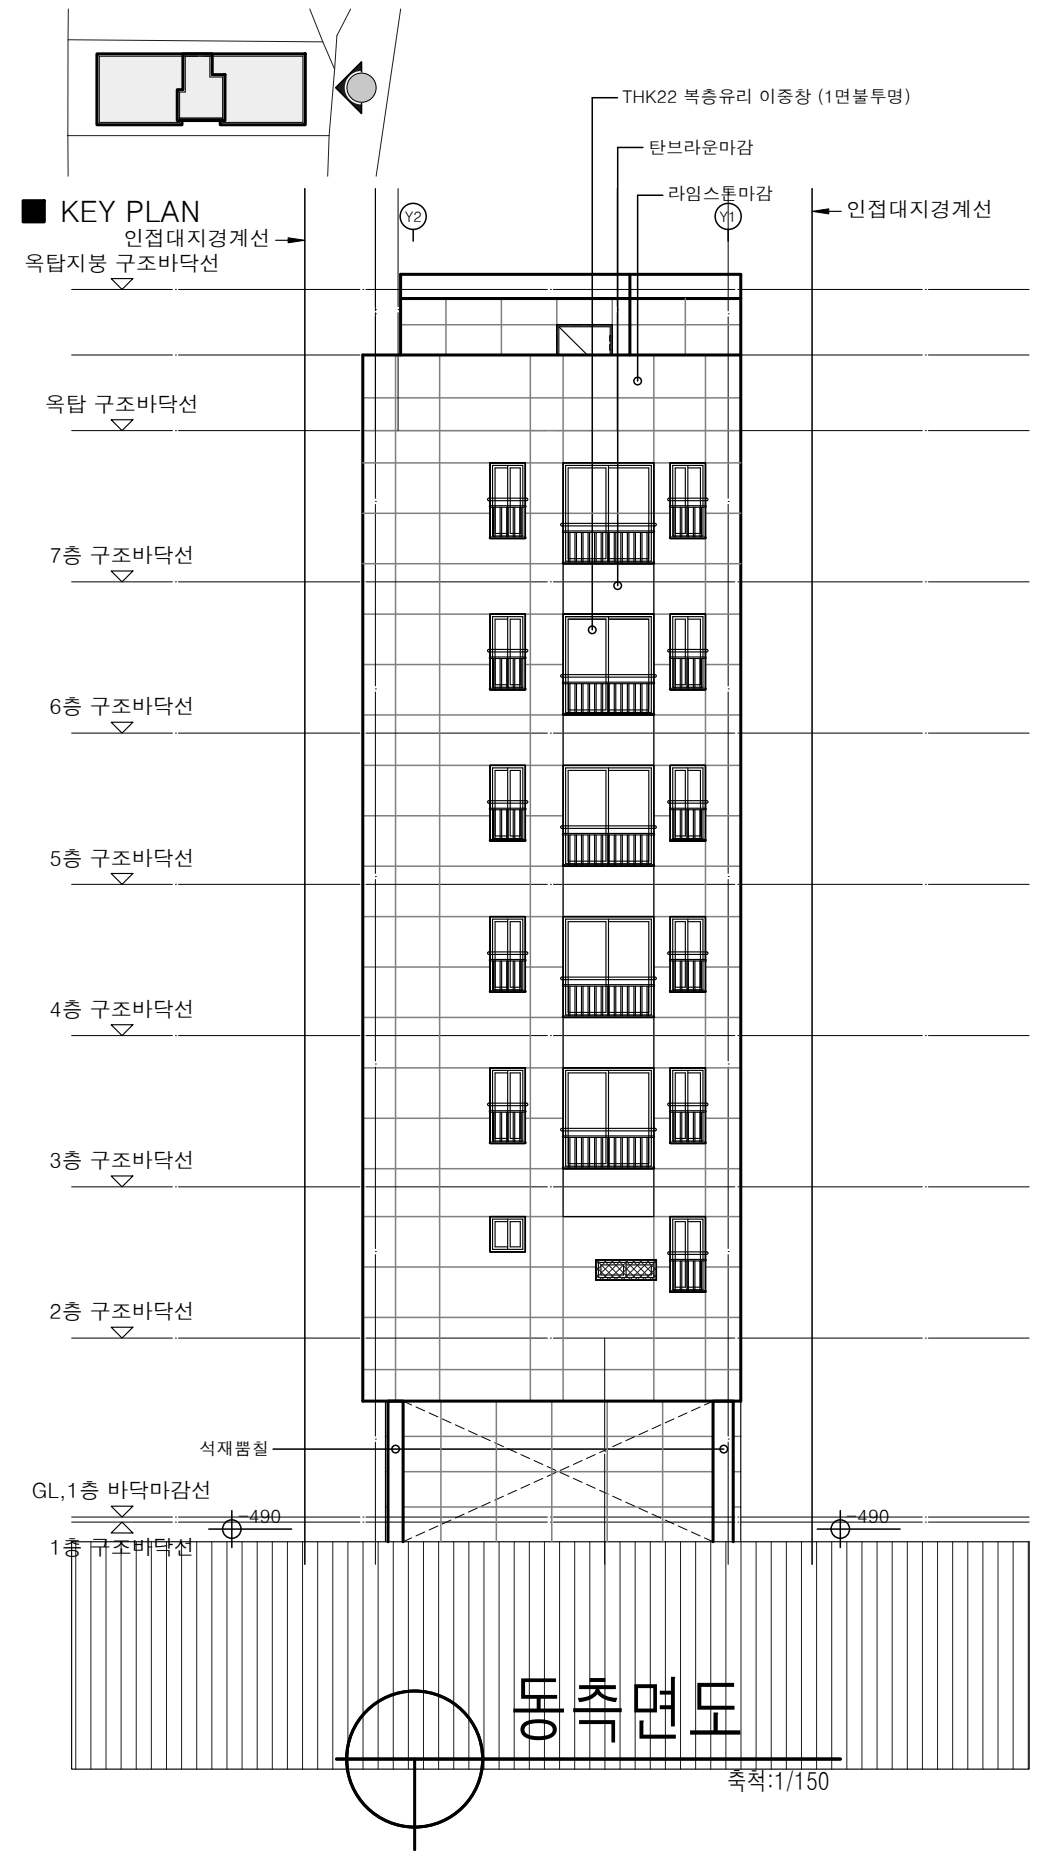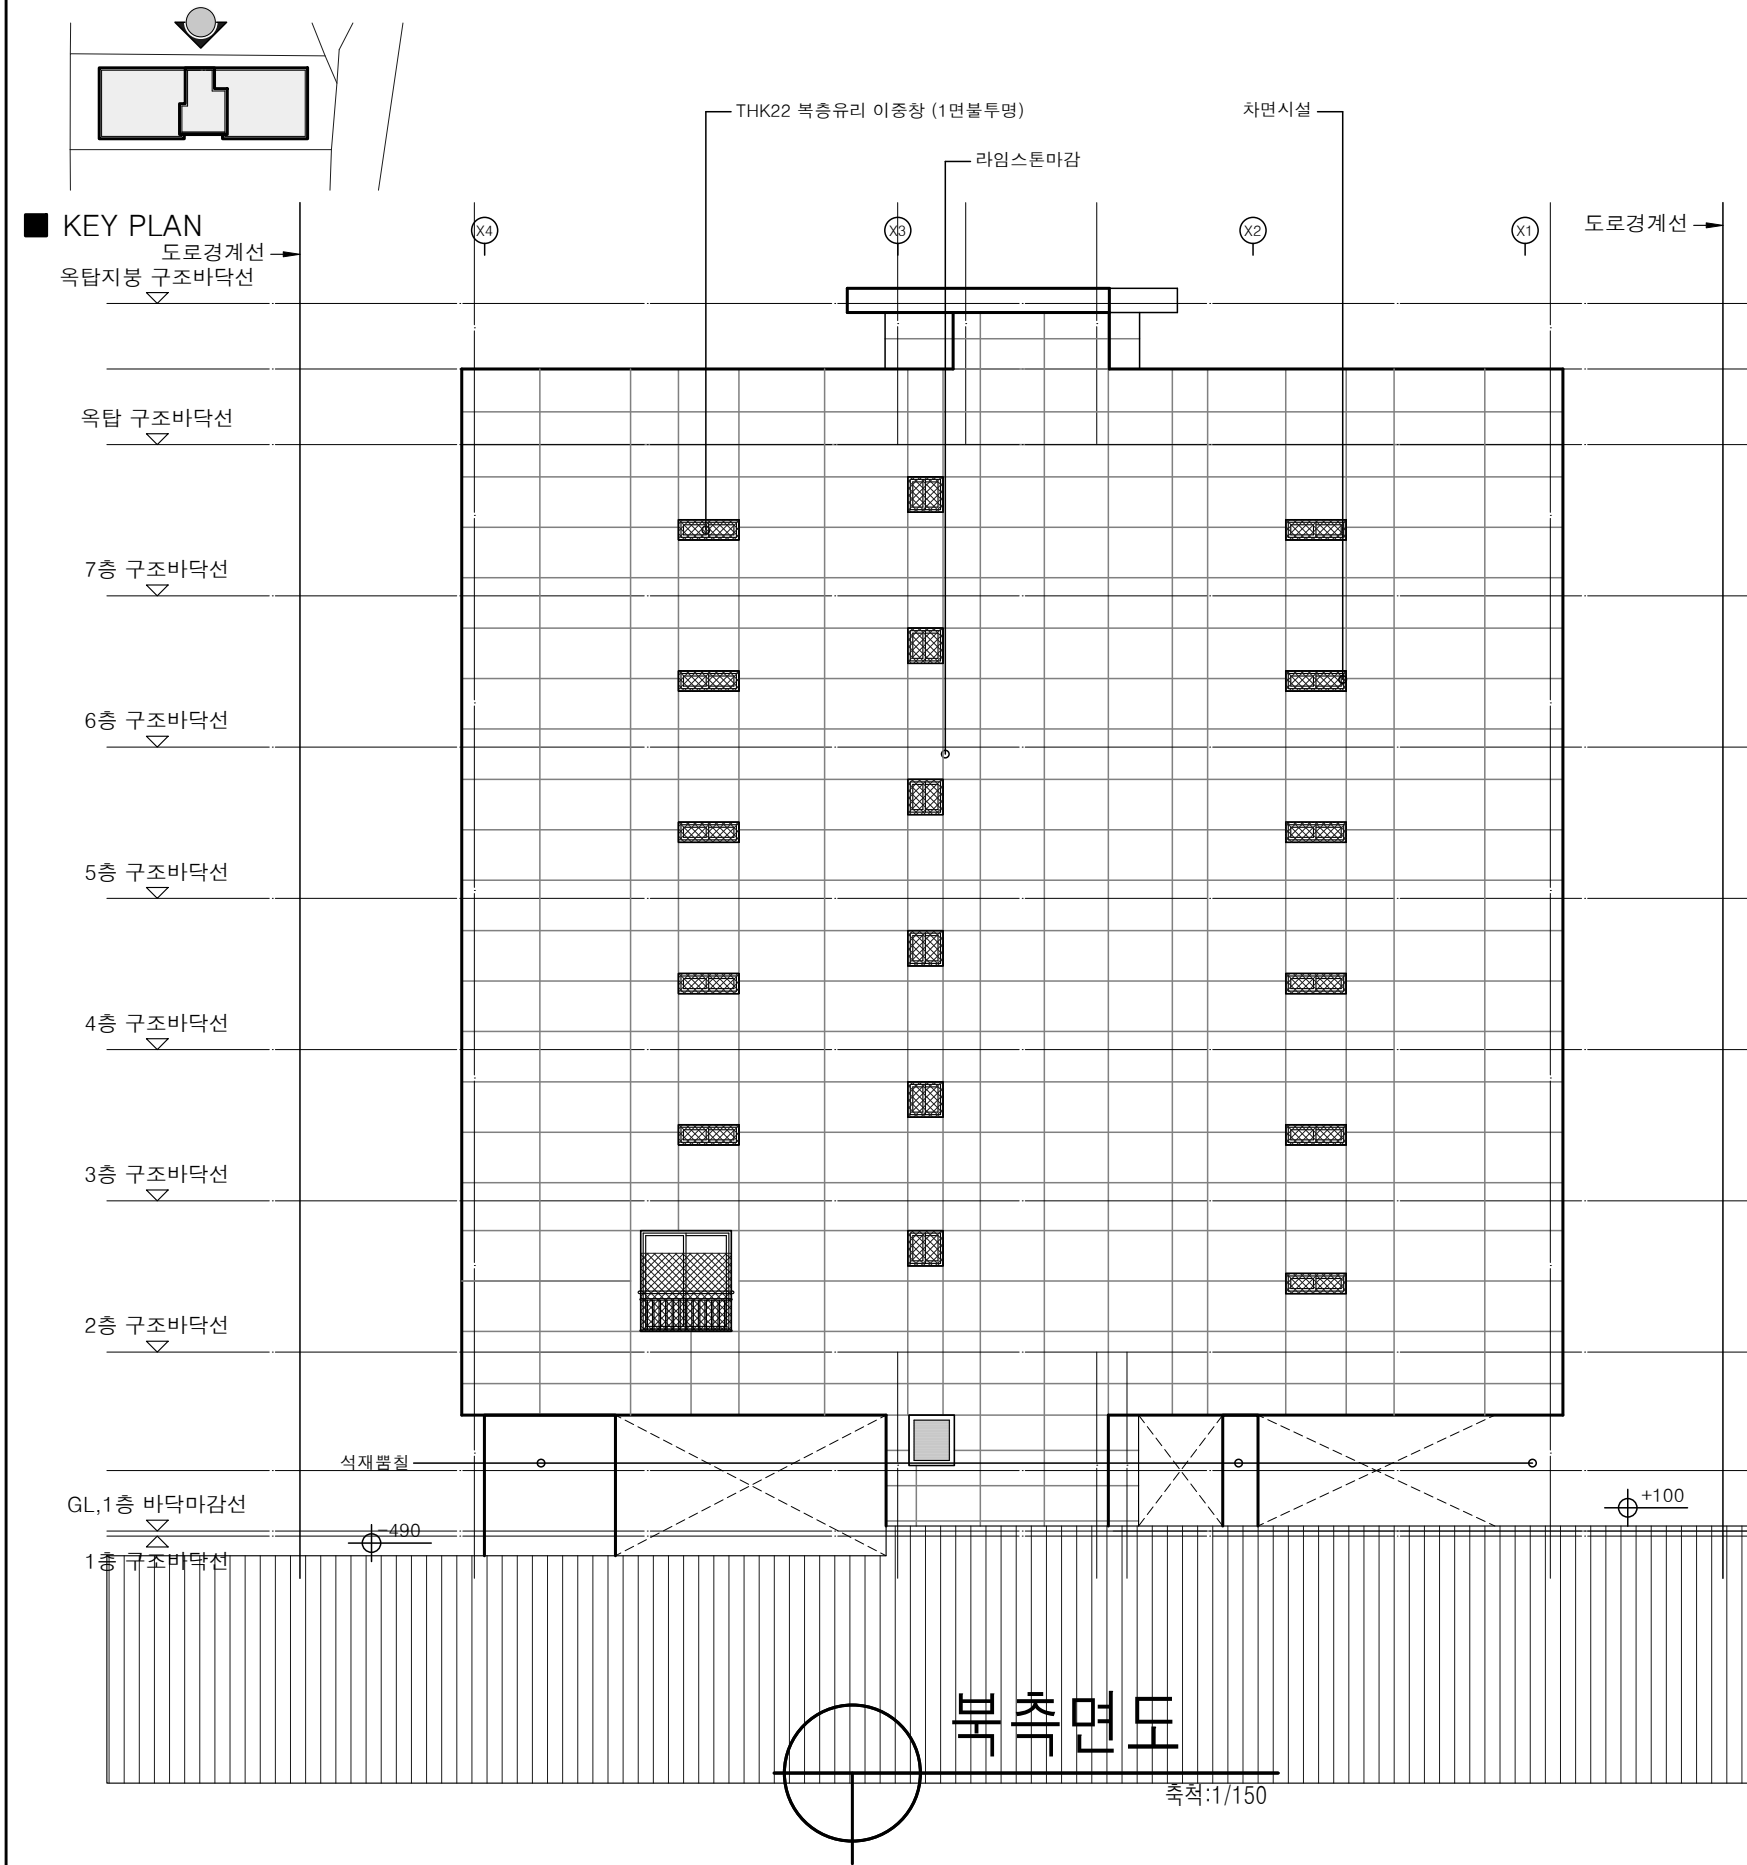

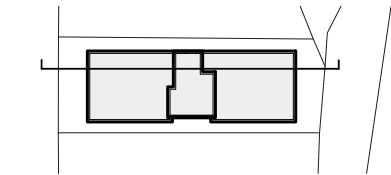


KEY PLAN

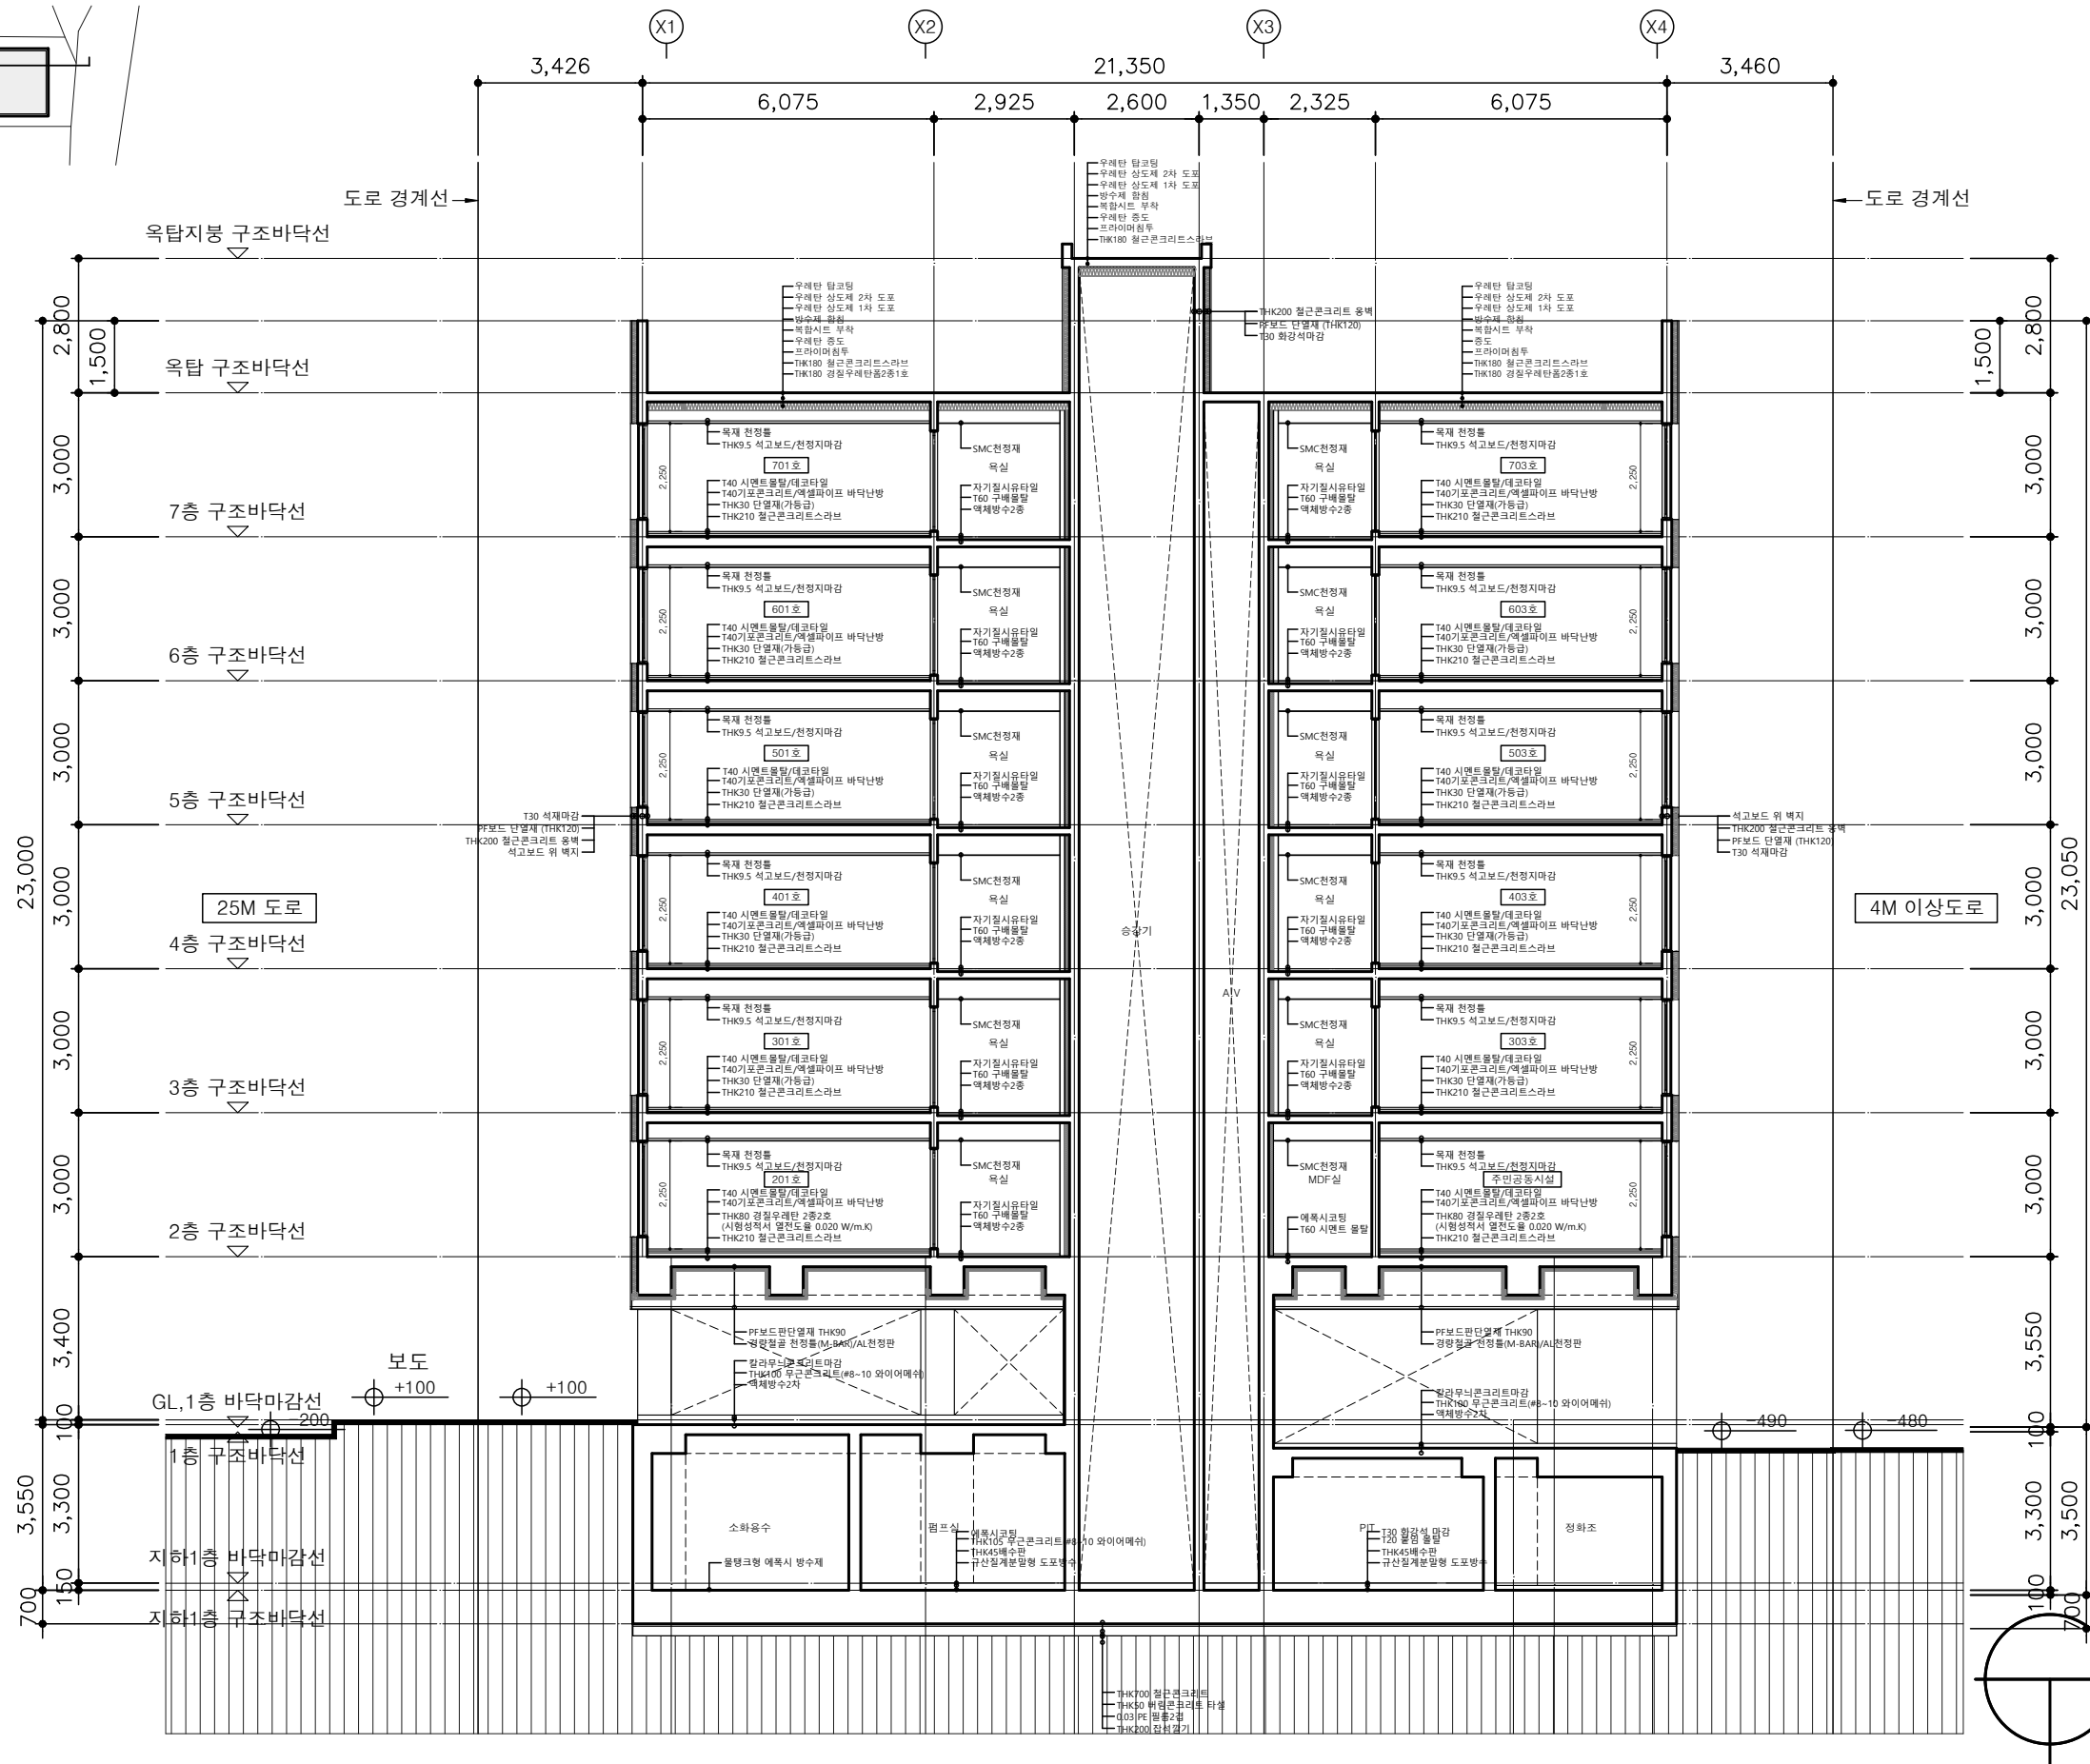


주 단면도

축척:1/150

비밀 생활 건축사사무소 서울특별시 도봉구 도당로 122 T. 02 - 725 - 3491 (방학동, 2층) F. 070 - 4015 - 2227	설계명 PROJECT TITLE 도봉구 도봉동 634-21 신축공사	노트 NOTE	설계구분 PROJECT KINDS	담당 DRAWN BY :	축척 SCALE 1/150	도면명칭 DRAWING TITLE 주 단면도
				담당 DRAWN BY :		
			설계번호 PROJECT NO.	검토 CHECKED BY :	날짜 DATE 2023.12.	도면번호 SHEET NO. A-036
				PIC APPROVED BY :		

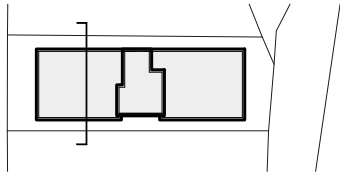

KEY PLAN

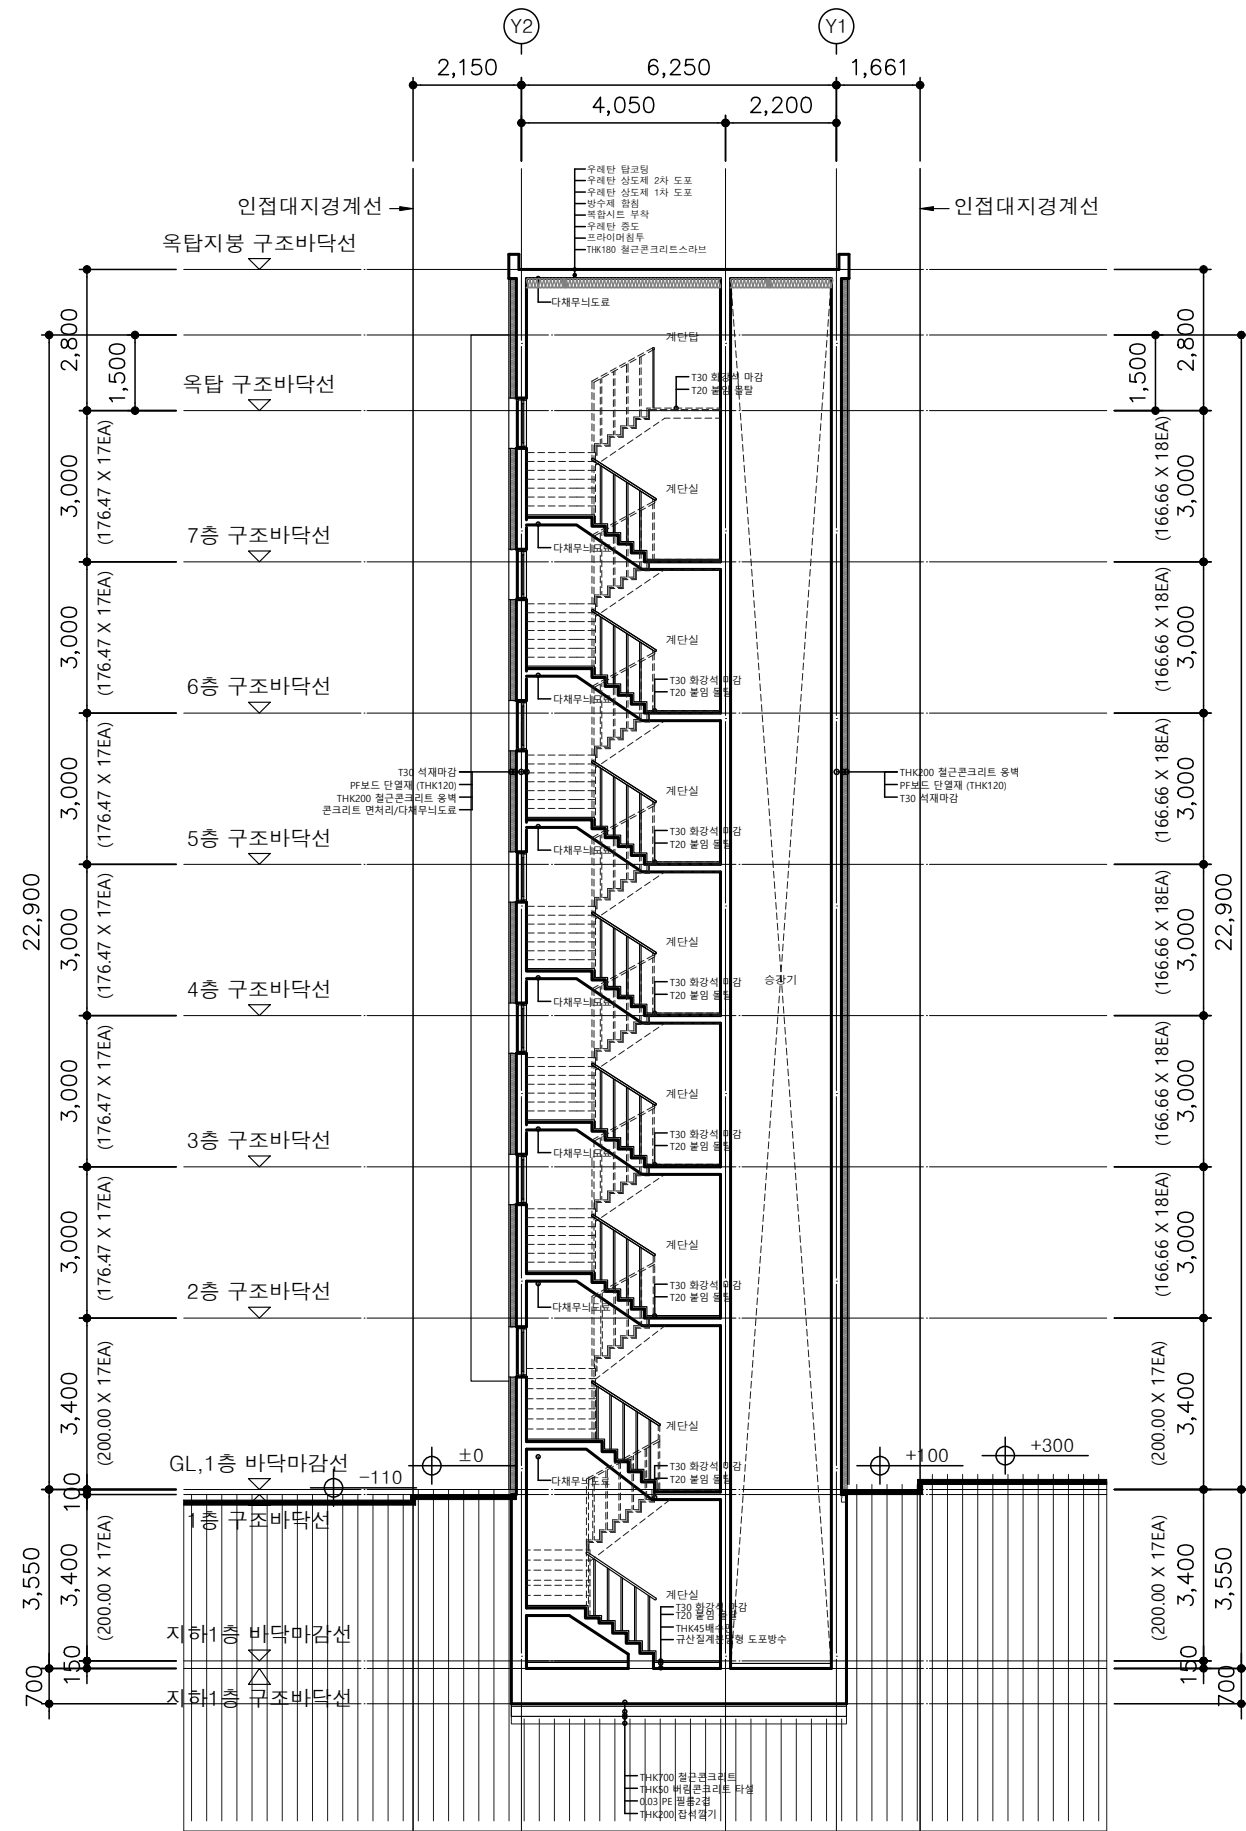

계단 단면도
축척:1/150

미필 생활 건축사 사무소
서울특별시 도봉구 도당로 122 T. 02 - 725 - 3491
(방학동, 2층) F. 070 - 4015 - 2227

설계명 PROJECT TITLE
도봉구 도봉동 634-21 신축공사

노트 NOTE

설계구분 PROJECT KINDS	담당 DRAWN BY :	축척 SCALE 1/150	도면명칭 DRAWING TITLE 계단 단면도
	검토 CHECKED BY :		
설계번호 PROJECT NO.	PIC APPROVED BY :	날짜 DATE 2023.12.	도면번호 SHEET NO. A-037