

수정 및 제출내용
ISSUES & REVISION

번호 NO.	내 DESCRIPTION	일자 DATE	승인 APPR
△			
△			
△			
△			
△			

설 계 DRAWN BY	
검 토 1 CHECKED-1 BY	박 동 국
검 토 2 CHECKED-2 BY	박 동 국
승 인 APPROVED BY	박 경 진
기 관 분 류 ORGAN CLASS	

도 면 명 DRAWING TITLE	지상1층 평면도
------------------------------	----------

축 척 SCALE	A1 : 50 A3 : 100	날 짜 DATE	2022.11.
-----------------	---------------------	----------------	----------

도 면 번 호 DWG NO.	A - 102
-----------------------------	---------


설 계 용 역 PROJECT OFFICE	
------------------------------------	--

HYUN
[주]종합건축사사무소 현

서울특별시 강남구 테헤란로81길 유림빌딩 9층
TEL (02)2135-8087, FAX (02)2135-8085

협력업체-1
CONSULTS

협력업체-2
CONSULTS

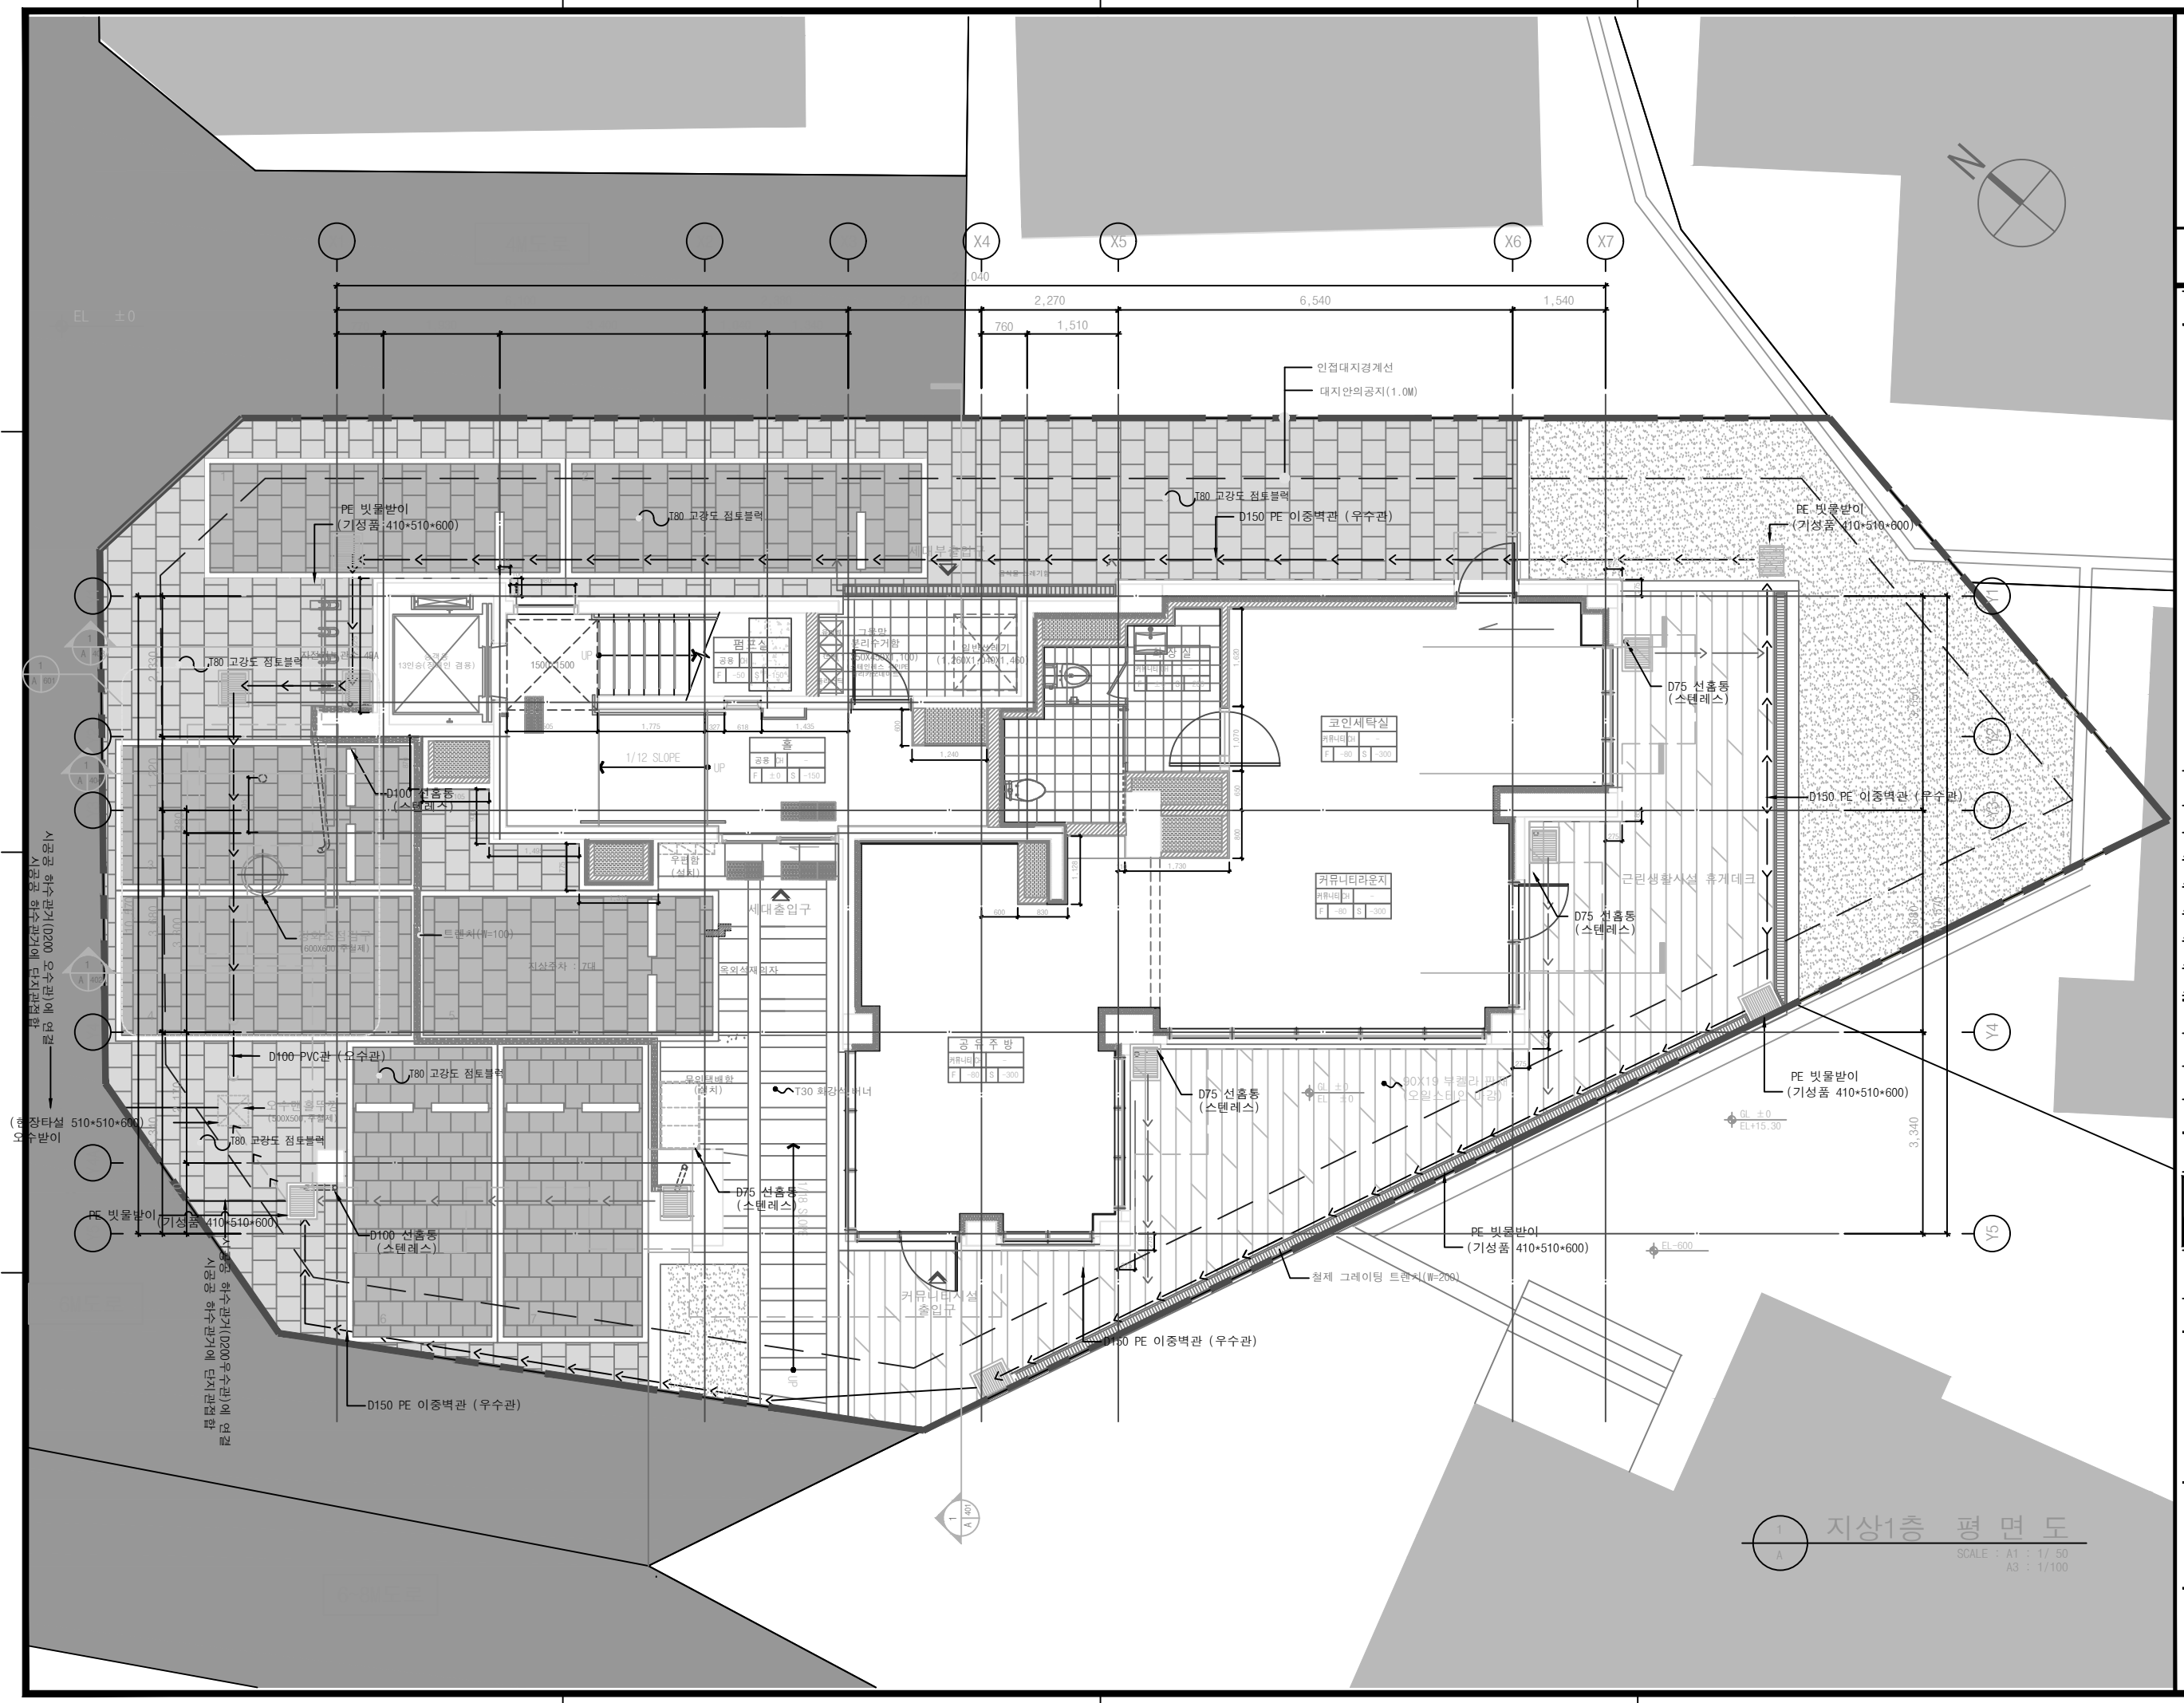

지상1층 평면도
SCALE : A1 : 1/50
A3 : 1/100

수정 및 제출내용
ISSUES & REVISION

번호 NO.	내용 DESCRIPTION	일자 DATE	승인 APPR.

설 계 DRAWN BY	
검 토 1 CHECKED-1 BY	박 동 국
검 토 2 CHECKED-2 BY	박 동 국
승 인 APPROVED BY	박 경 진
기 관 분 류 ORGAN CLASS	

도 면 명 DRAWING TITLE	지상2층 평면도
------------------------------	----------

축 척 SCALE	A1 : 50 A3 : 100	날 짜 DATE	2022. 11.
-----------------	---------------------	----------------	-----------

도면번호 DWG NO.	A - 103
-----------------	---------


설 계 용 역 PROJECT OFFICE	
------------------------------------	--

HYUN
[주]종합건축사사무소 현 [주]

서울특별시 강남구 테헤란로81길 유림빌딩 9층
TEL (02)2135-8087, FAX (02)2135-8085

협력업체-1
CONSULTS

협력업체-2
CONSULTS

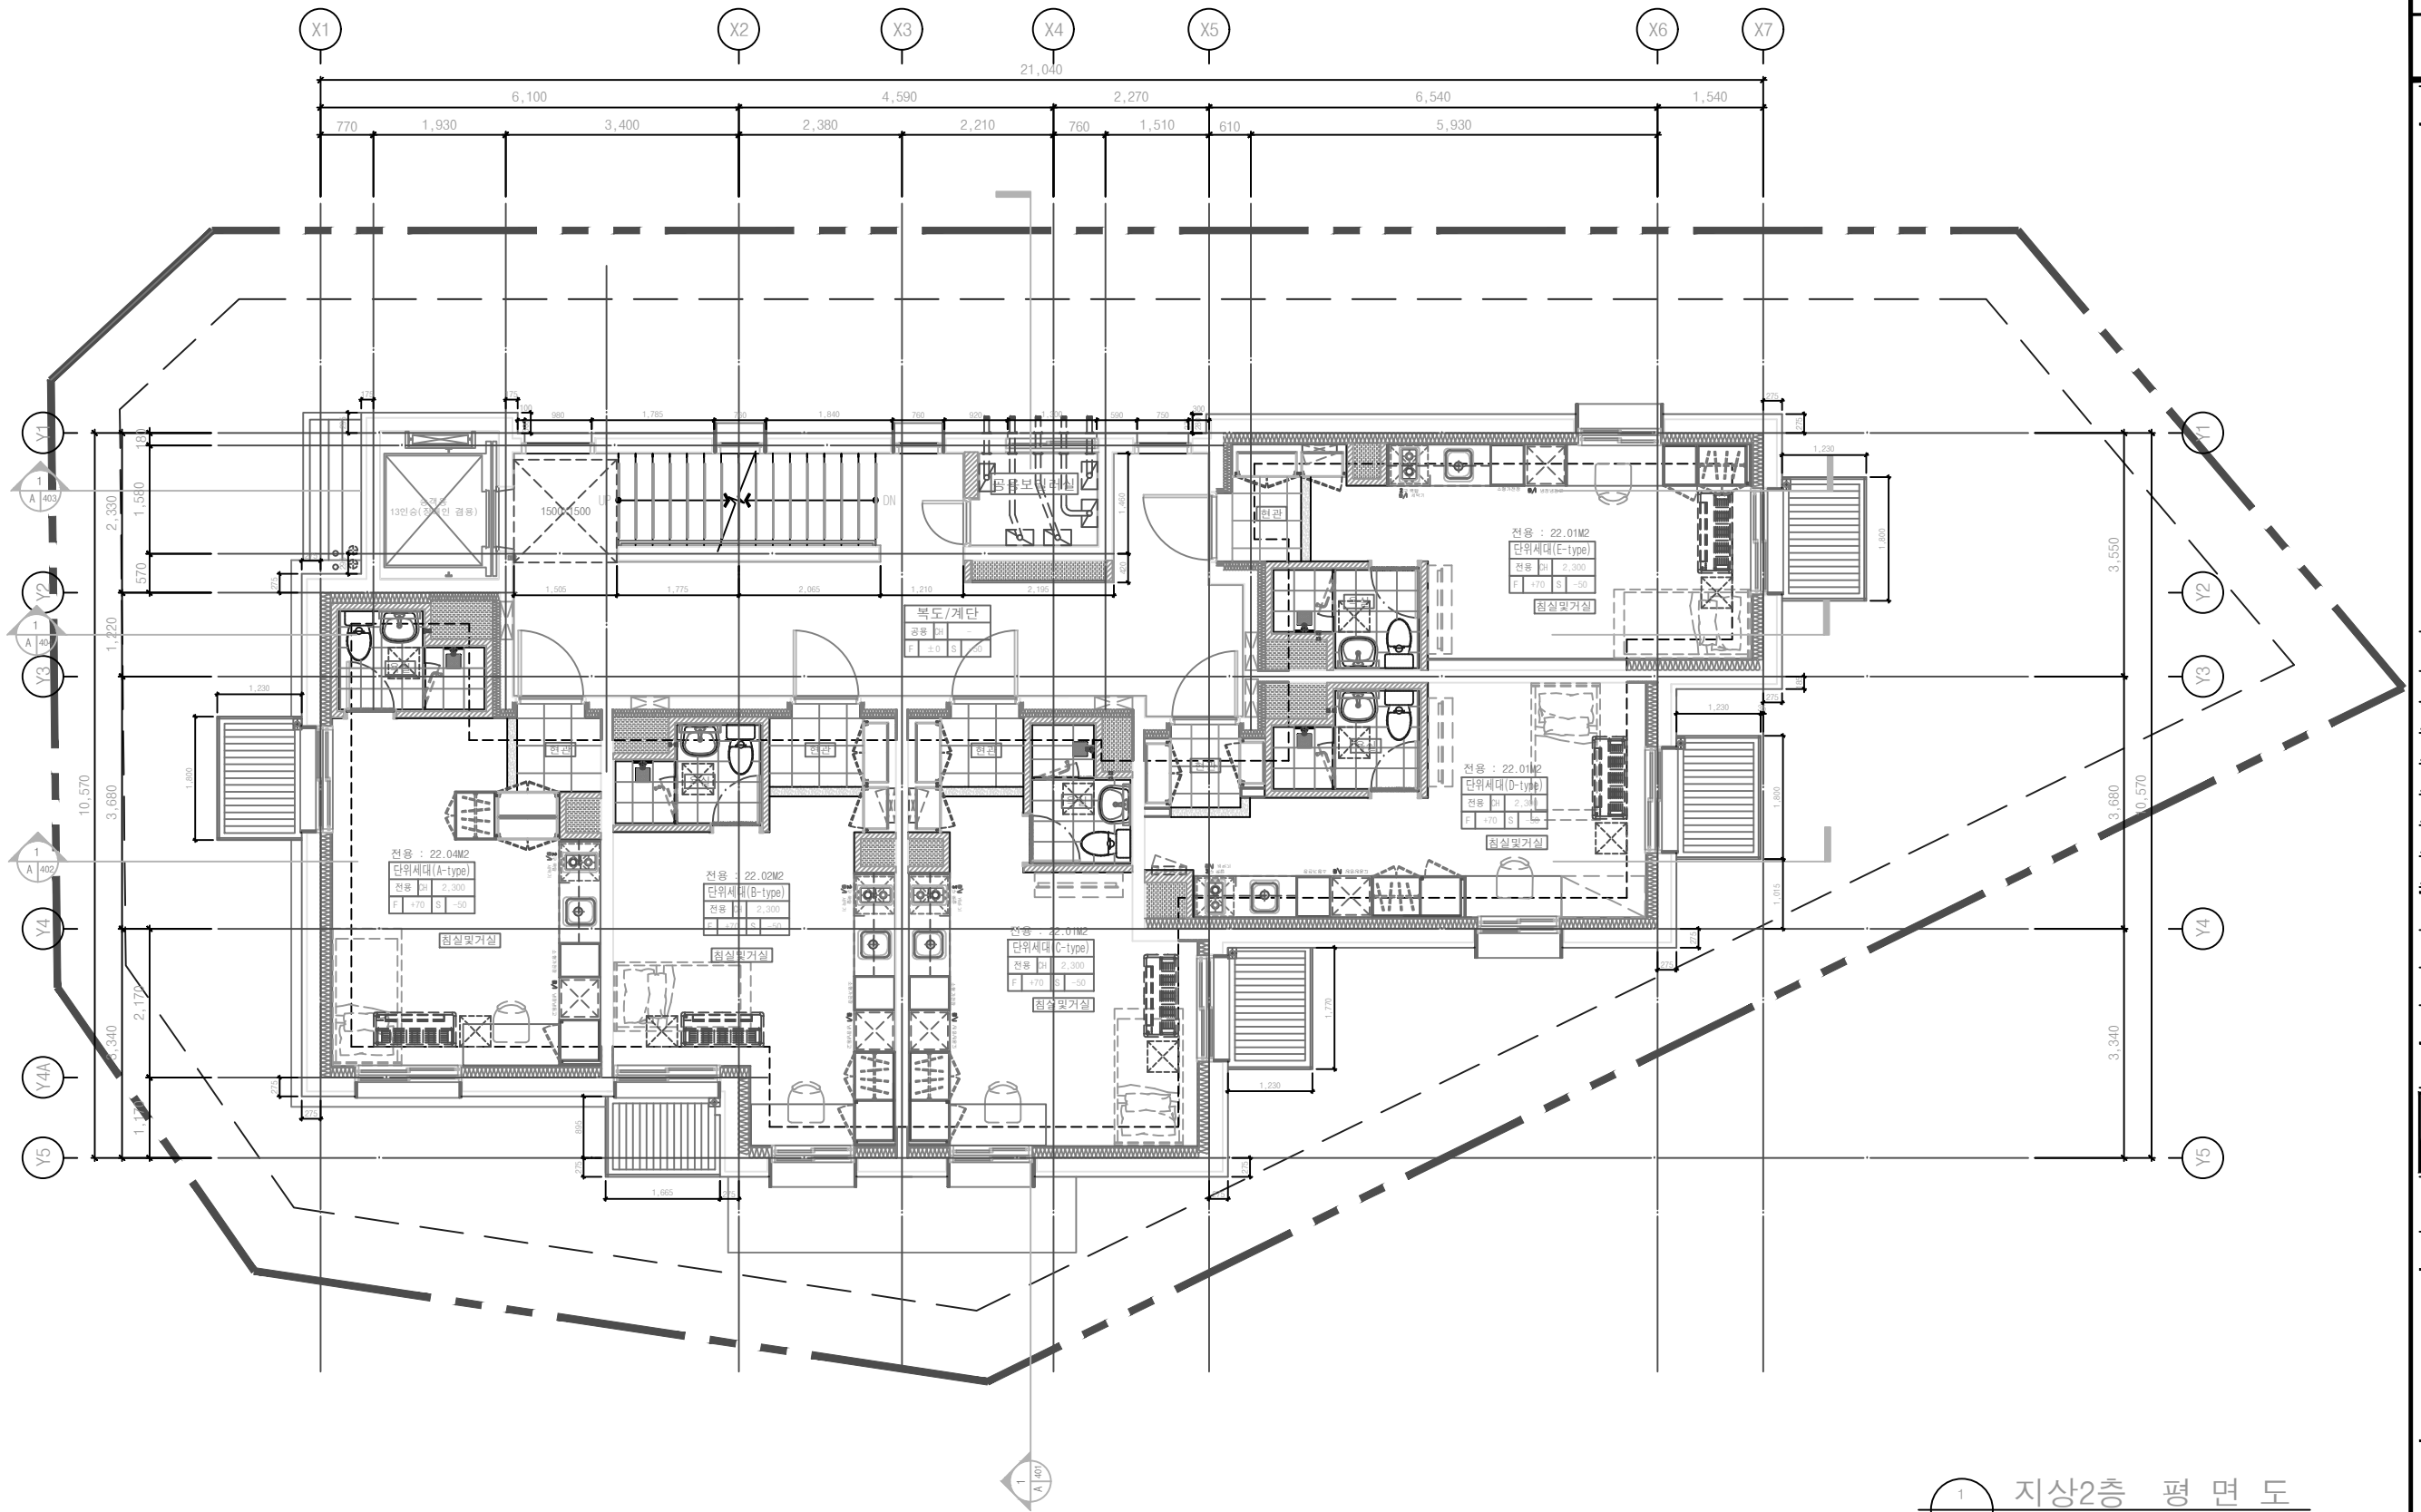

1 지상2층 평면도
A SCALE : A1 : 1/ 50
A3 : 1/100

수정 및 제출내용
ISSUES & REVISION

번호 NO.	내용 DESCRIPTION	일자 DATE	승인 APPR

설 계 DRAWN BY	
검 토 1 CHECKED-1 BY	박 동 국
검 토 2 CHECKED-2 BY	박 동 국
승 인 APPROVED BY	박 경 진
기 관분류 ORGAN CLASS	

도 면 명 DRAWING TITLE	지상3층 평면도
------------------------	----------

축척 SCALE	A1 : 50 A3 : 100	날 짜 DATE	2022. 11.
-------------	---------------------	-------------	-----------

도면번호 DWG NO.	A - 104
-----------------	---------


설 계 용 역 PROJECT OFFICE	
---------------------------	--

HYUN
[주]종합건축사사무소 현 [주]

서울특별시 강남구 테헤란로81길 유림빌딩 9층
TEL (02)2135-8087, FAX (02)2135-8085

협력업체-1
CONSULTS

협력업체-2
CONSULTS

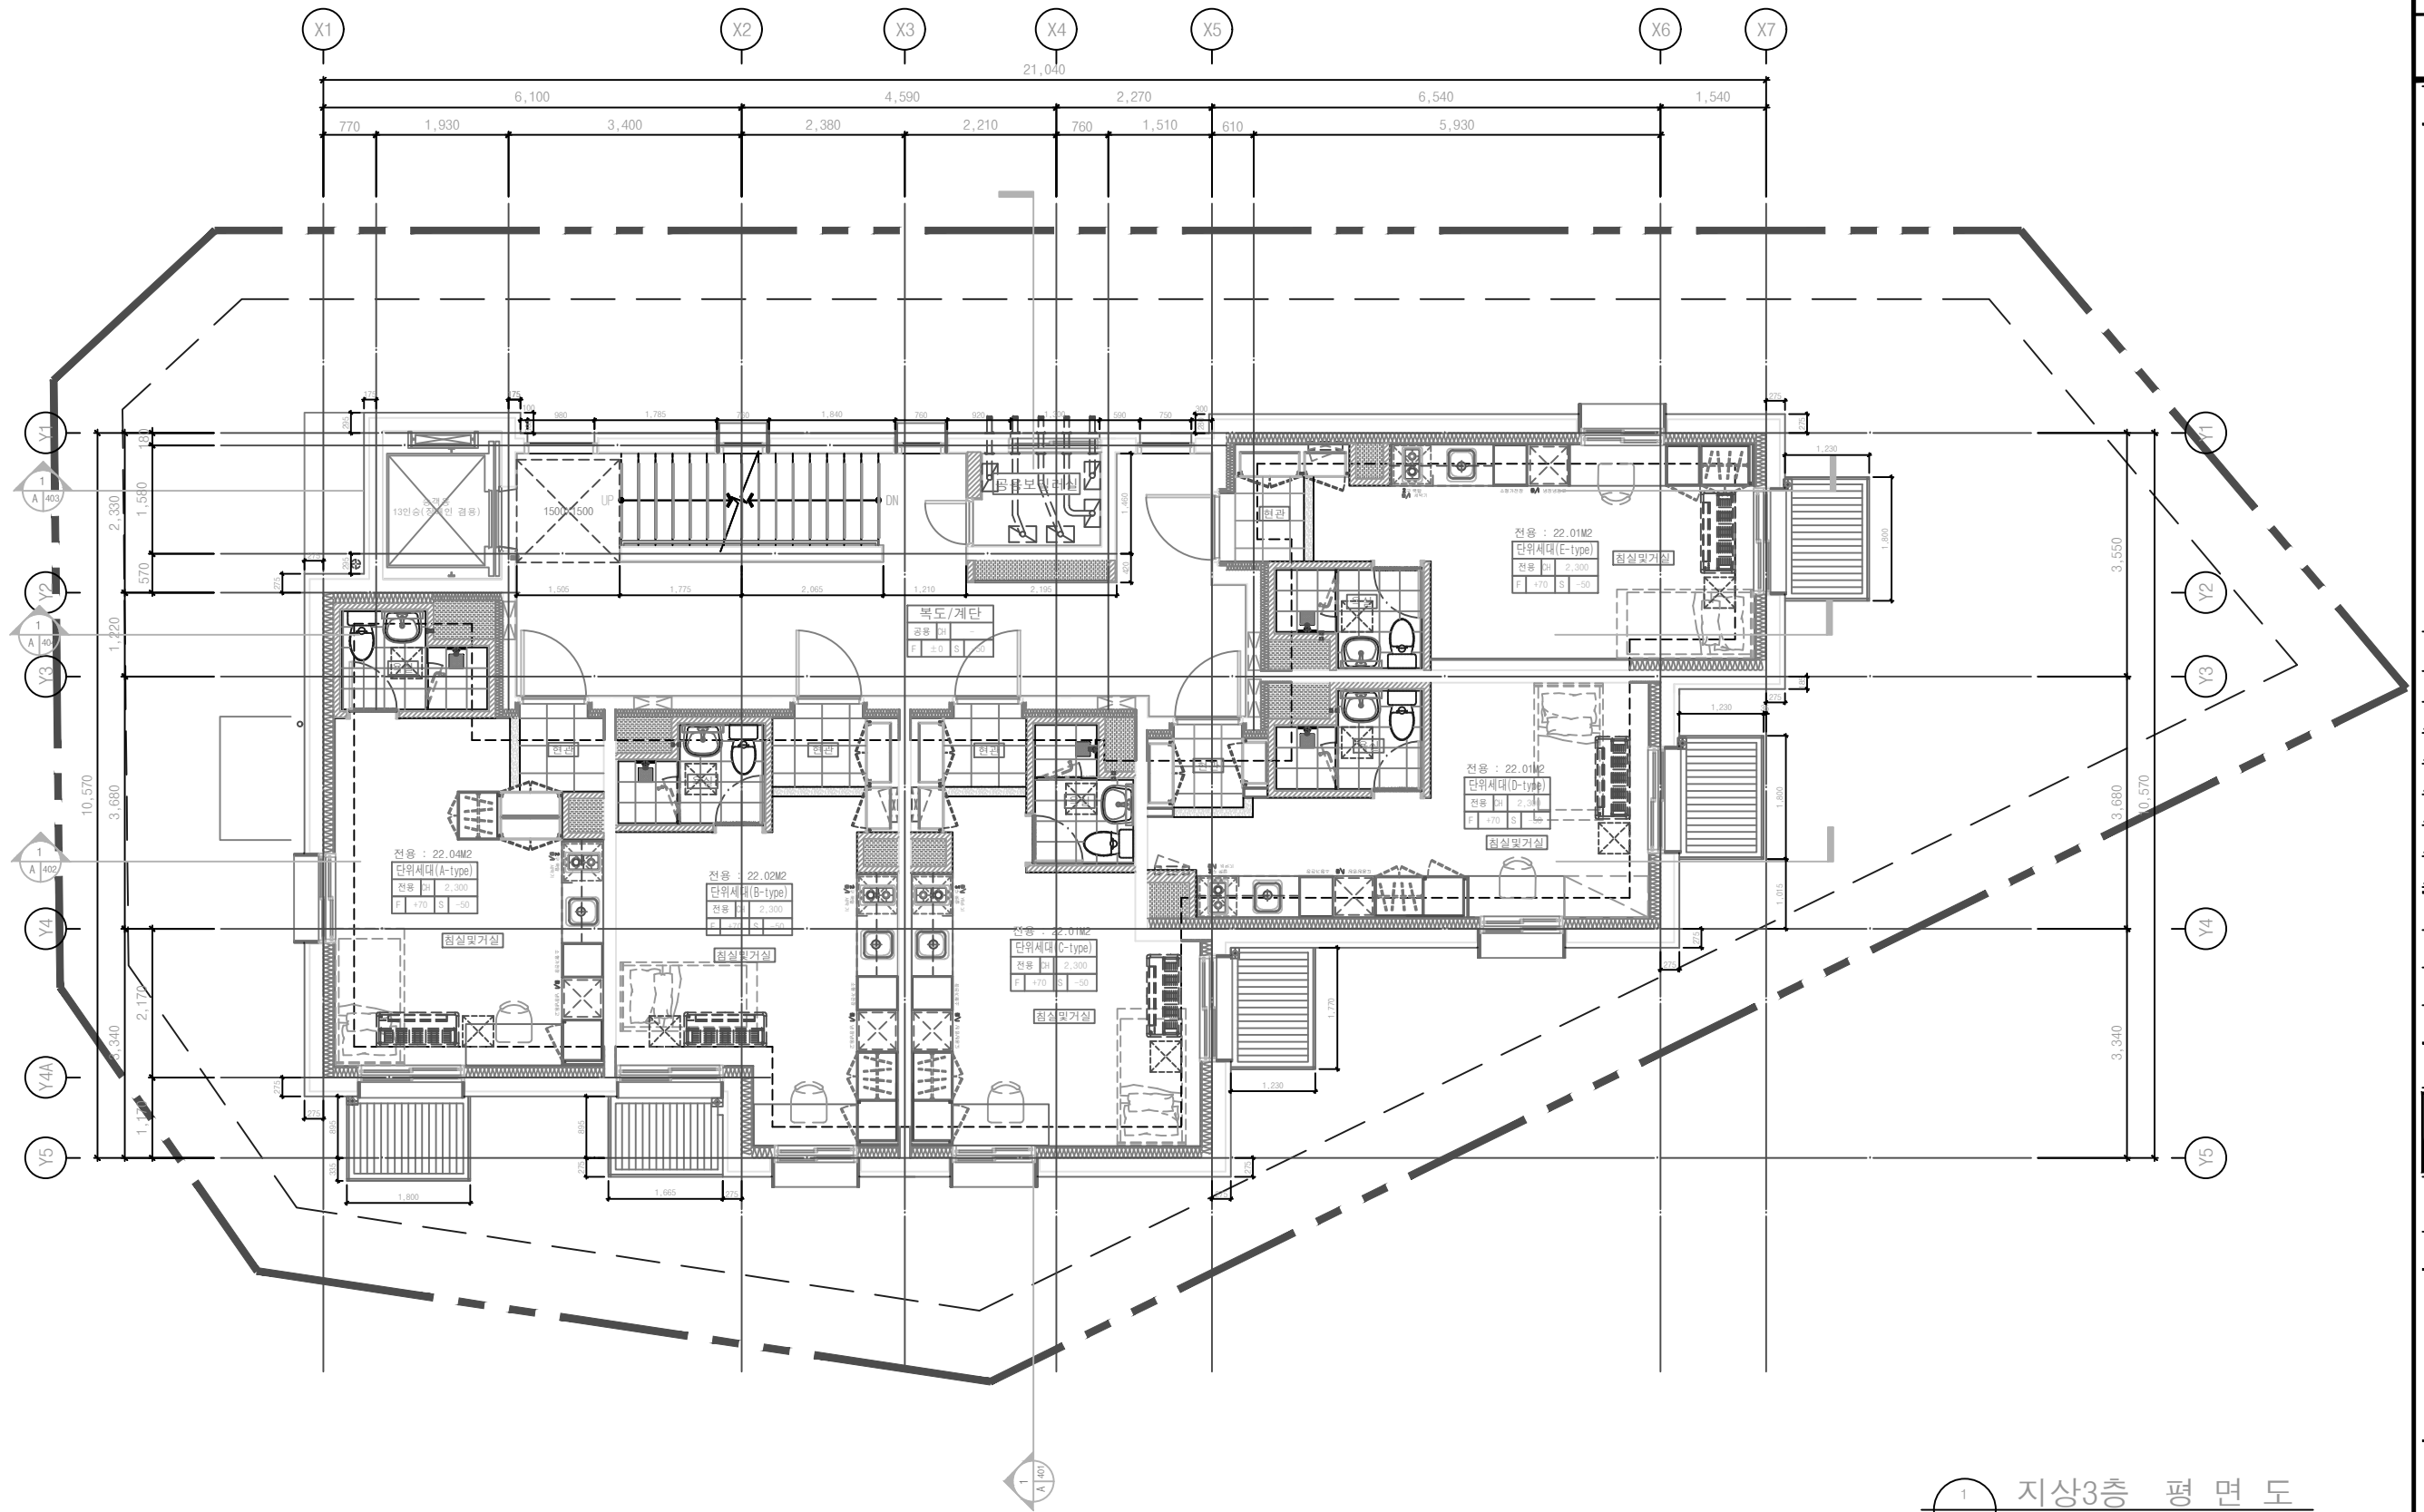

1 지상3층 평면도
A SCALE : A1 : 1/ 50
A3 : 1/100

수정 및 제출내용
ISSUES & REVISION

번호 NO.	내용 DESCRIPTION	일자 DATE	승인 APPR

설 계 DRAWN BY	
검 토 1 CHECKED-1 BY	박 동 국
검 토 2 CHECKED-2 BY	박 동 국
승 인 APPROVED BY	박 경 진
기관분류 ORGAN CLASS	

도 면 명 DRAWING TITLE	지상4층 평면도
------------------------	----------

축척 SCALE	A1 : 50 A3 : 100	날 짜 DATE	2022. 11.
-------------	---------------------	-------------	-----------

도면번호 DWG NO.	A - 105
-----------------	---------


설 계 용 역 PROJECT OFFICE	
---------------------------	--

HYUN
[주]종합건축사사무소 한 Hyun

서울특별시 강남구 테헤란로81길 유림빌딩 9층
TEL (02)2135-8087, FAX (02)2135-8085

협력업체-1
CONSULTS

협력업체-2
CONSULTS

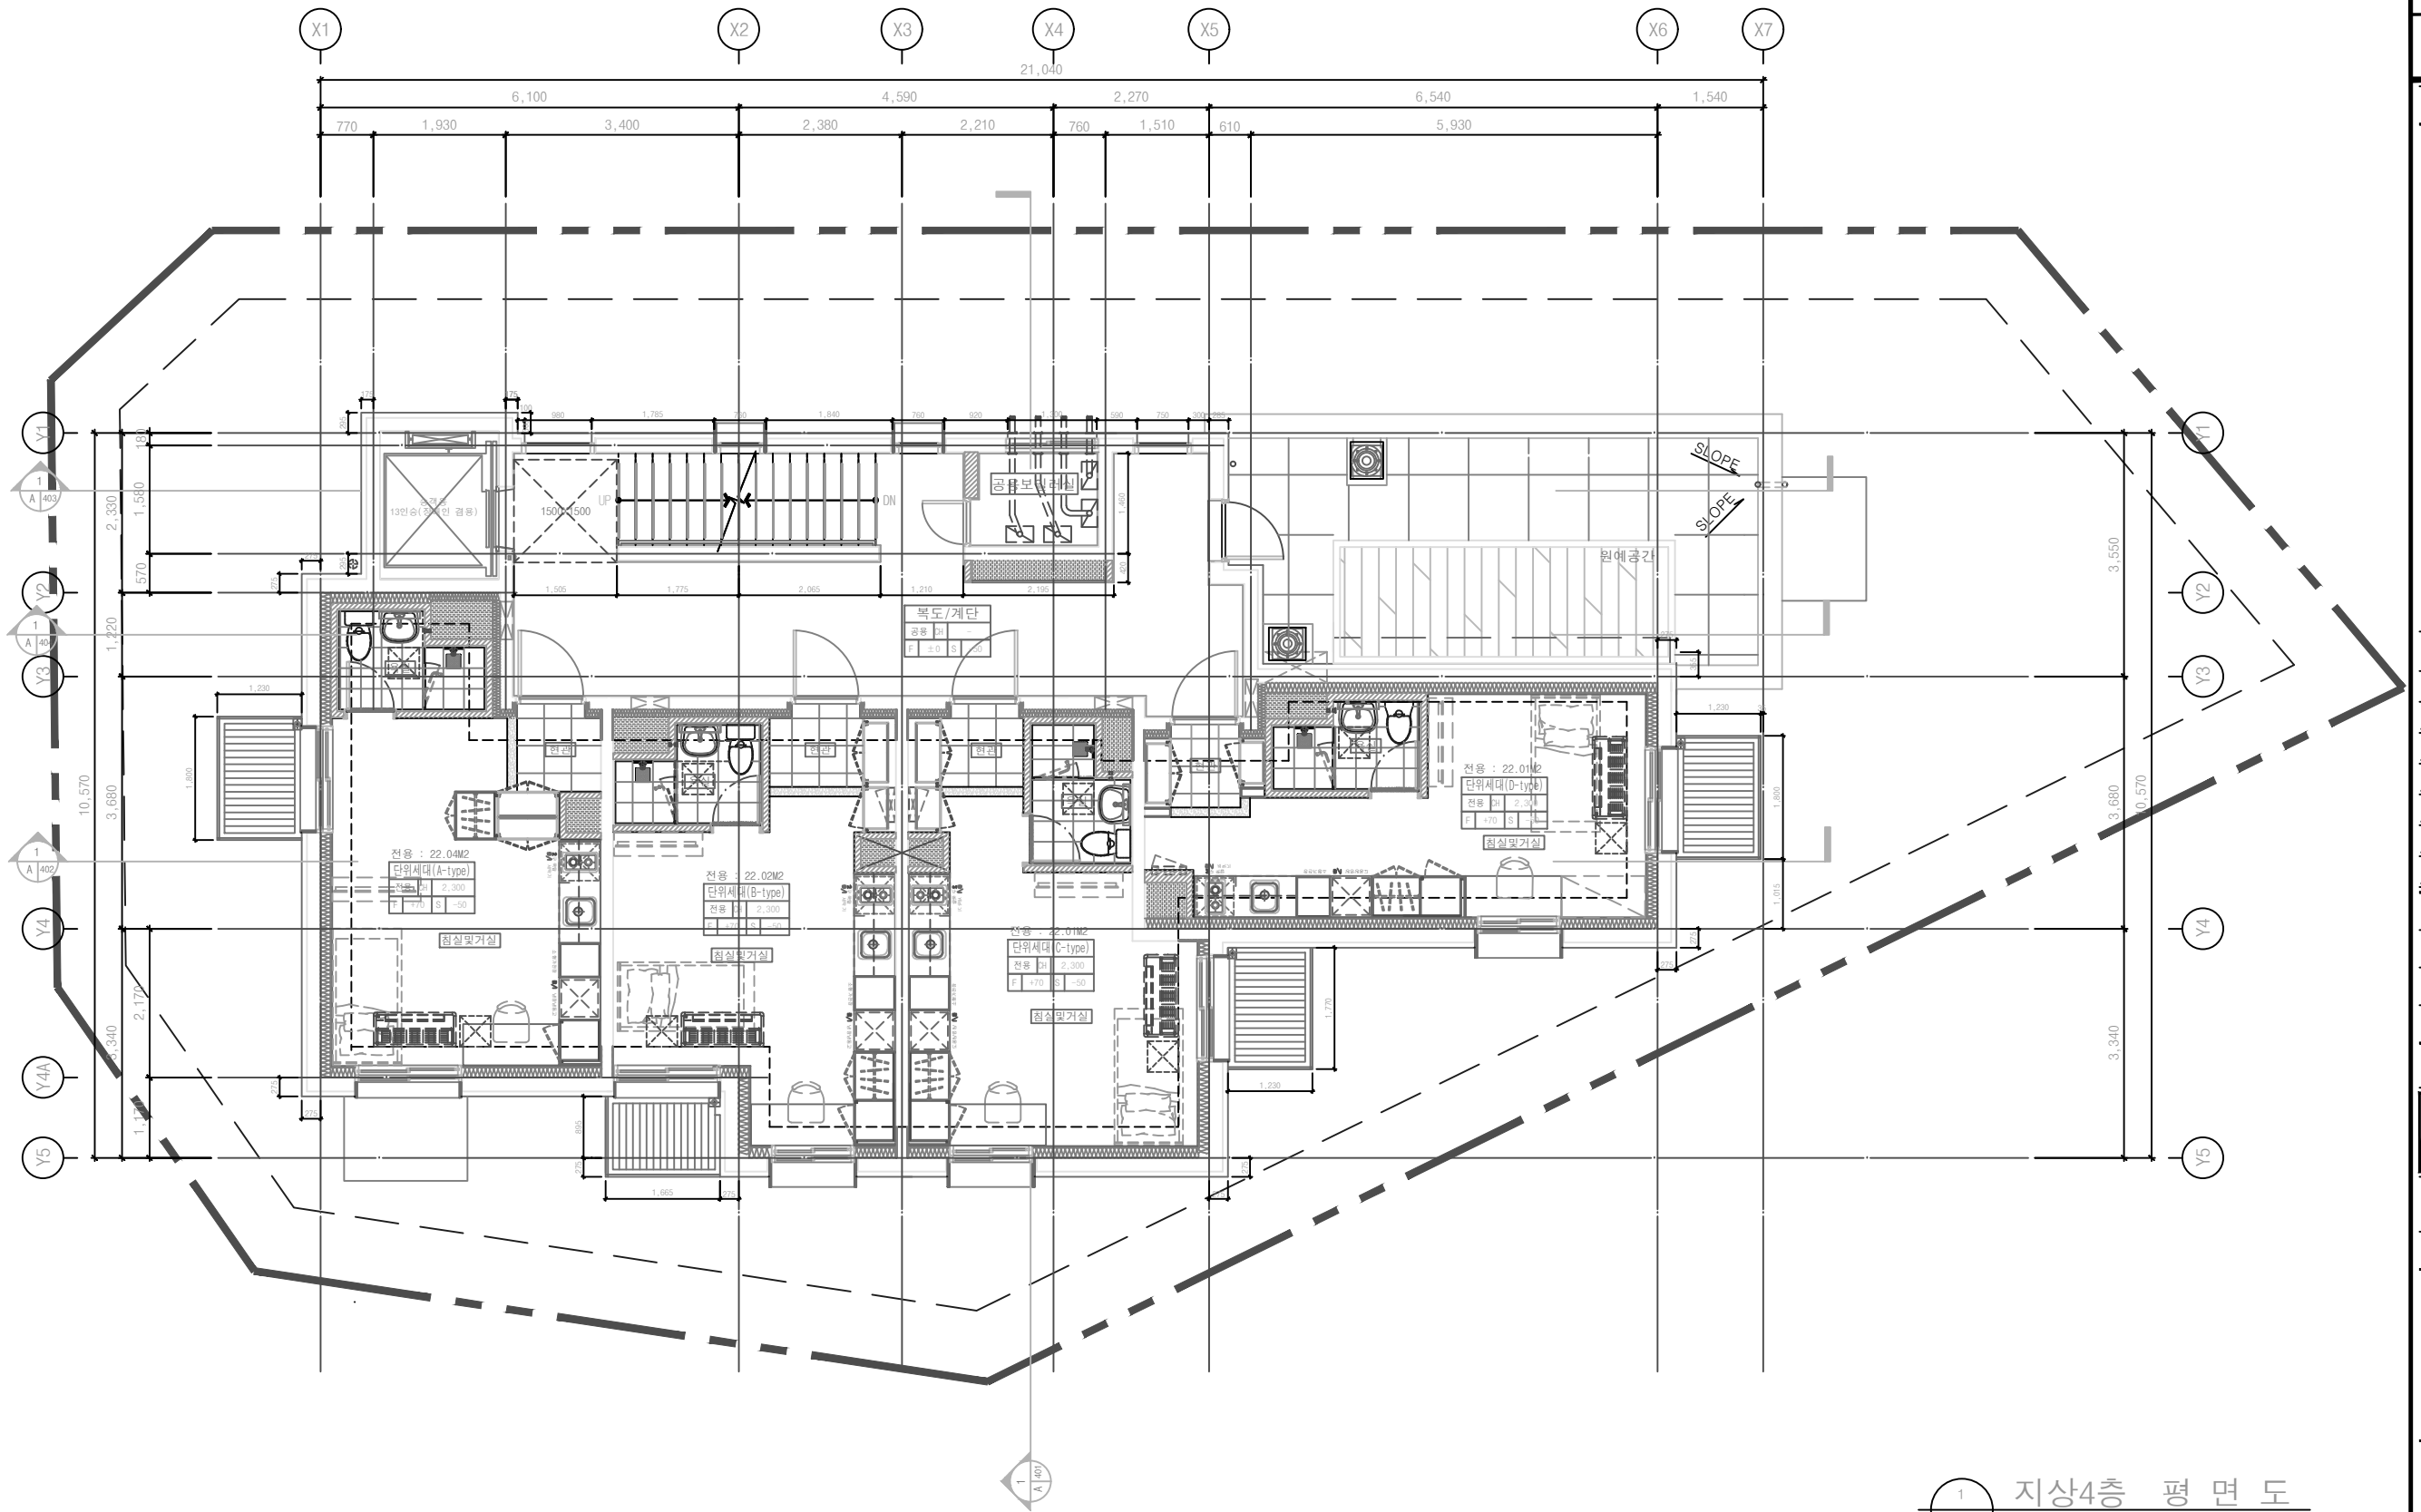

1 지상4층 평면도
A SCALE : A1 : 1/ 50
A3 : 1/100

수정 및 제출내용
ISSUES & REVISION

번호 NO.	내용 DESCRIPTION	일자 DATE	승인 APPR

설 계 DRAWN BY	
검 토 1 CHECKED-1 BY	박 동 국
검 토 2 CHECKED-2 BY	박 동 국
승 인 APPROVED BY	박 경 진
기관분류 ORGAN CLASS	

도 면 명 DRAWING TITLE	지상5층 평면도
------------------------	----------

축척 SCALE	A1 : 50 A3 : 100	날 짜 DATE	2022. 11.
-------------	---------------------	-------------	-----------

도면번호 DWG NO.	A - 106
-----------------	---------


설 계 용 역 PROJECT OFFICE	
---------------------------	--

HYUN
[주]종합건축사사무소 한 [주]

서울특별시 강남구 테헤란로81길 유림빌딩 9층
TEL (02)2135-8087, FAX (02)2135-8085

협력업체-1
CONSULTS

협력업체-2
CONSULTS

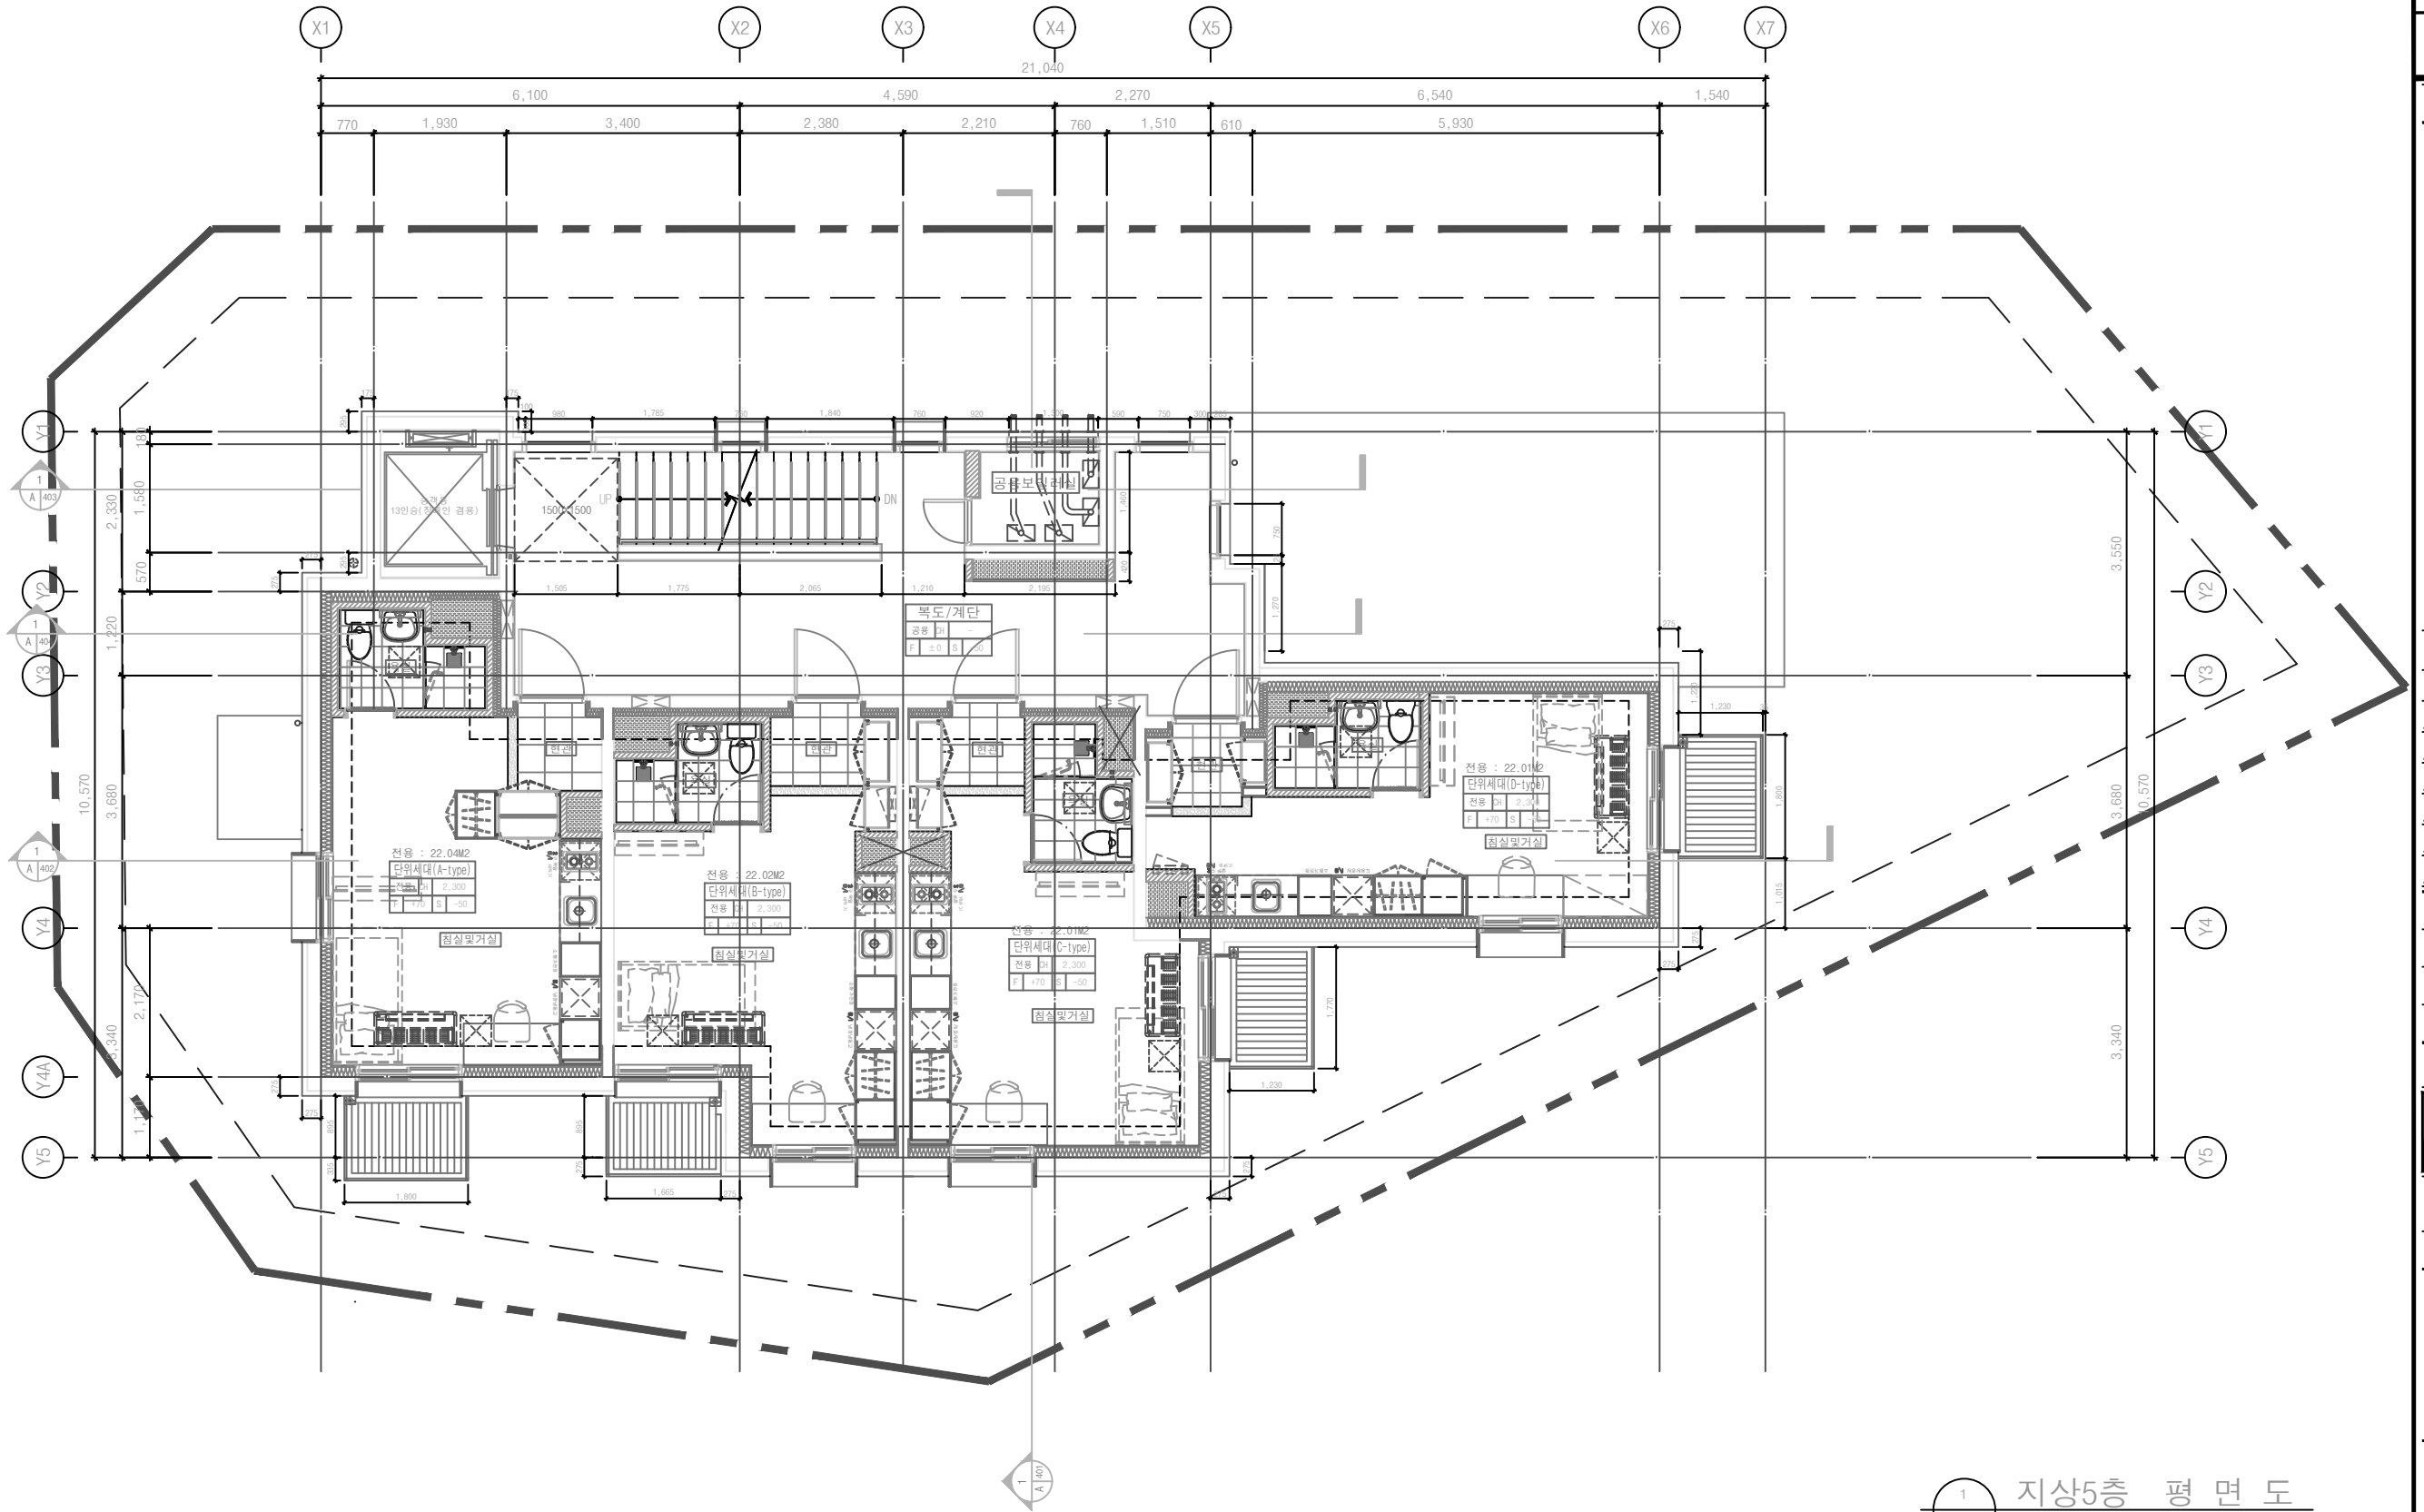

1 지상5층 평면도
A SCALE : A1 : 1/ 50
A3 : 1/100



방학동 313-7, 38번지
공공리모델링 공사

프로젝트코드
PROJECT CODE
N O T E

수정 및 제출내용
ISSUES & REVISION

번호 NO.	내용 DESCRIPTION	일자 DATE	승인 APPR
△			
△			
△			
△			
△			

설 계 DRAWN BY	
검 토 1 CHECKED-1 BY	박 동 국
검 토 2 CHECKED-2 BY	박 동 국
승 인 APPROVED BY	박 경 진
기 관 분 류 ORGAN CLASS	

도 면 명 DRAWING TITLE	옥탑층 평면도
------------------------------	---------

축 척 SCALE	A1: 50 A3: 100	날 짜 DATE	2022. 11.
-----------------	-------------------	----------------	-----------

도면번호 DWG NO.	A - 107
-----------------	---------


설 계 용 역 PROJECT OFFICE	
------------------------------------	--

HYUN
[주]종합건축사사무소 한 [주]

서울특별시 강남구 테헤란로81길 유림빌딩 9층
TEL (02)2135-8087, FAX (02)2135-8085

협력업체-1
CONSULTS

협력업체-2
CONSULTS

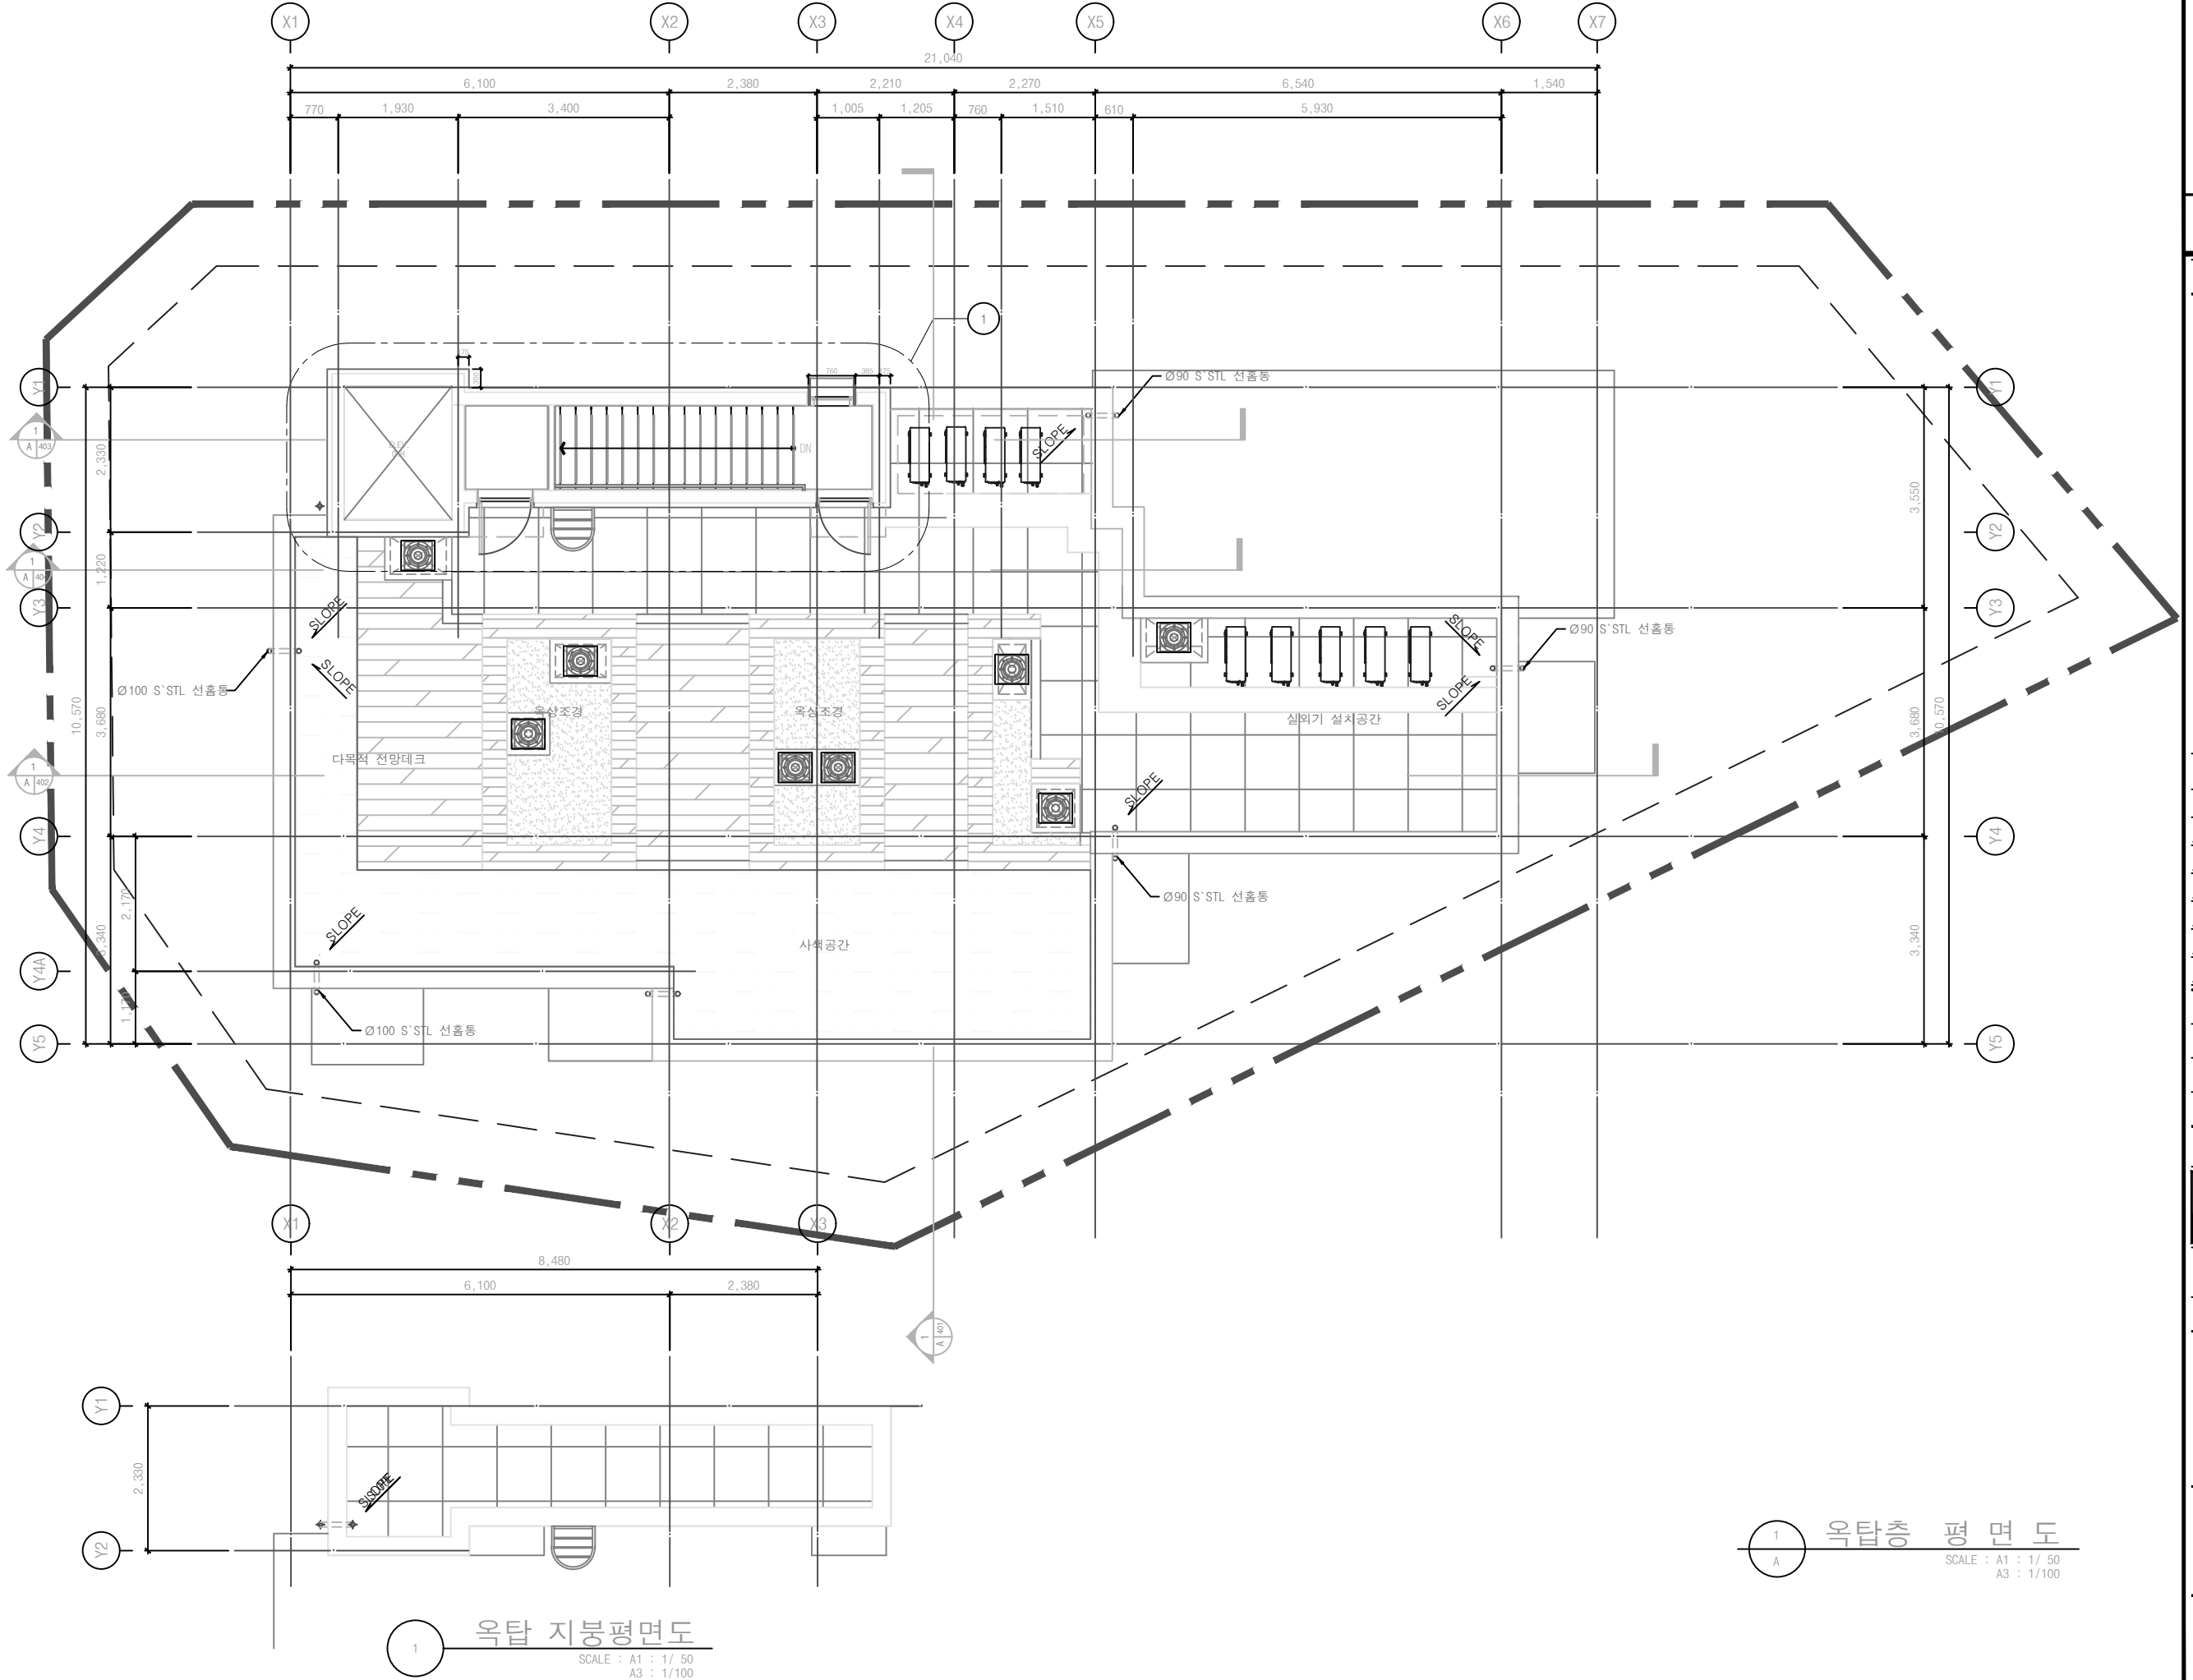

1. 코아부분은 동별 코아 평, 단면도 참조
2. 피로티상부 옥실레벨은 구조도면 참조
3.  부분은 설비담당과 협의후
슬리브 설치(기계)
4. 세대분전반 설치시 신발장 상세에
대해 언급할 것
5. 발코니 외부창호는 현장실측후
제작설치
7. 우수 및 배수드레인은 기계공중시설
설치도 참조하되 반드시 건축감독과
위치를 협의할 것.
8. 세대간벽은 차음1등급(58dB) 이상
만족하도록 밀실하게 시공할 것.

수정 및 제출내용
ISSUES & REVISION

번호 NO.	내 DESCRIPTION	용 DATE	일자 DATE	승인 APPR
△				
△				
△				
△				
△				



설 계 DRAWN BY	
검 토 1 CHECKED-1 BY	박 동 국
검 토 2 CHECKED-2 BY	박 동 국
승 인 APPROVED BY	박 경 진
기 관 분 류 ORGAN CLASS	

도 면 명 DRAWING TITLE	단위세대 평면도-1
------------------------------	------------

축 척 SCALE	A1: 40 A3: 80	날 짜 DATE	2022. 11.
-----------------	------------------	----------------	-----------

도면번호 DWG NO.	A - 201
-----------------	---------


설 계 용 역 PROJECT OFFICE	
------------------------------------	--

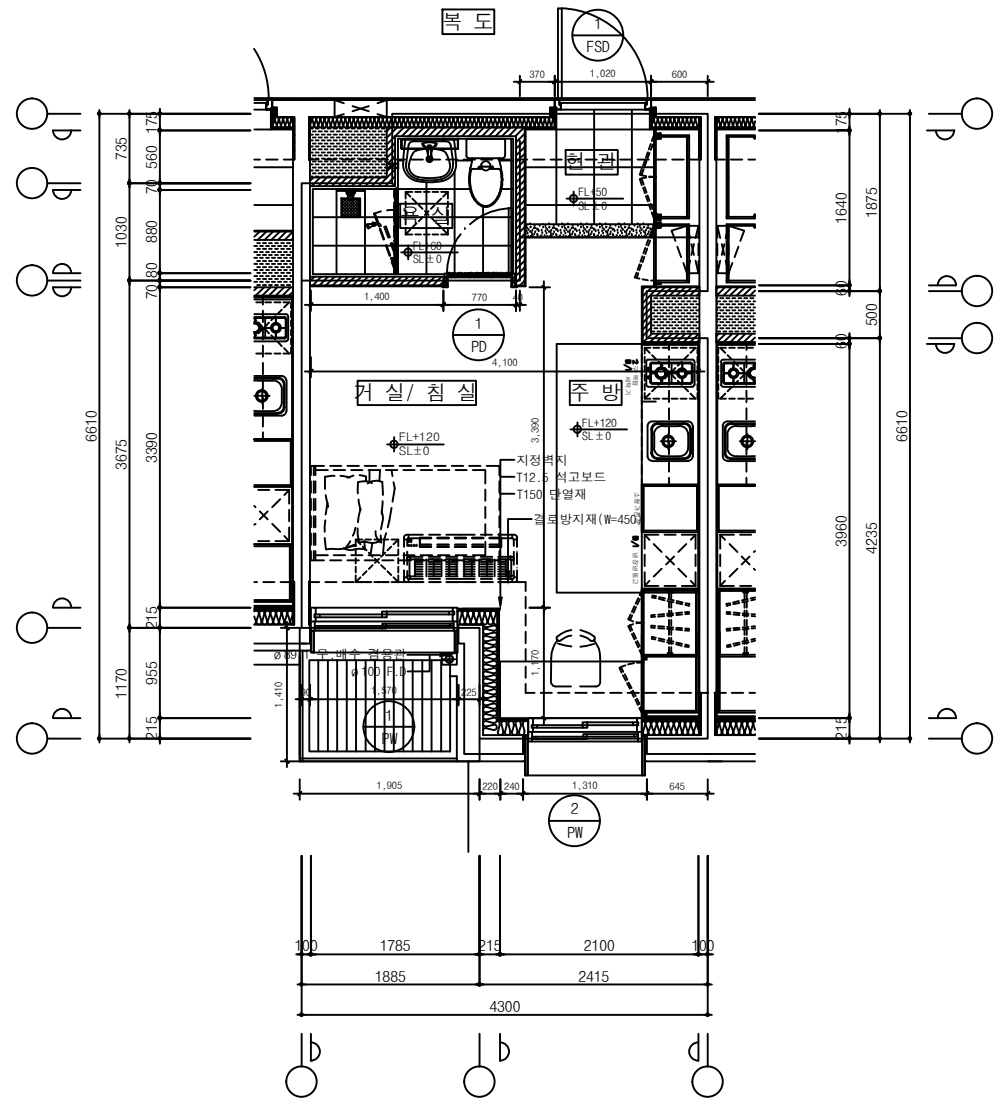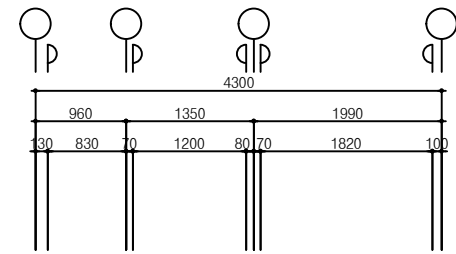

2 22m² 형 단위세대 평면도(B-type)
SCALE : A1 : 1/40
A3 : 1/80

■22m² 단위세대(B-type) 실별 면적표


구분	실 별	면 적(m²)	구분		면 적(m²)
전용	거실/침실	13.18	주거 공용 면적	벽체 중심 면적	3.17
	주방/식당	3.95			
	현관	2.13			
	욕실	2.76	서비스 면적	발코니	2.69
전용면적계		22.02	주거공용면적계		3.17
계(전용+주거공용)		25.19			

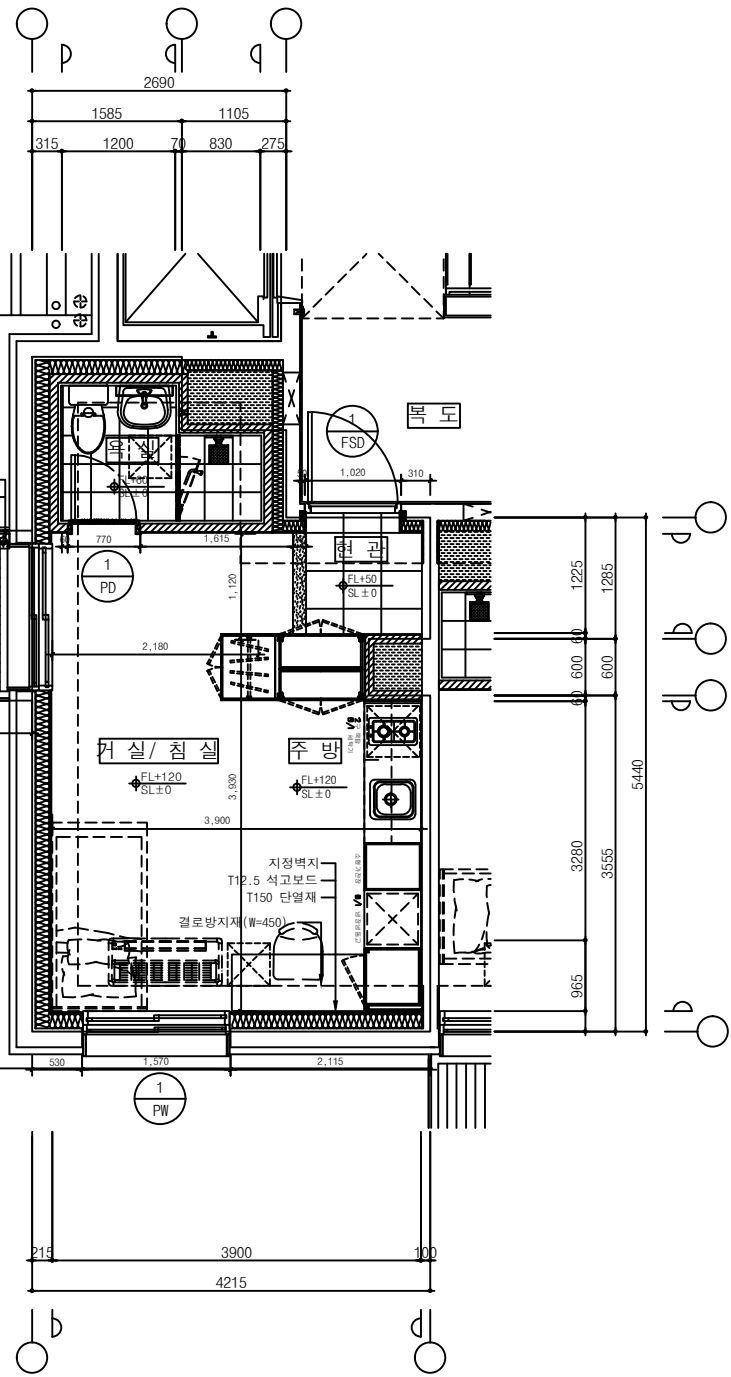

1 22m² 형 단위세대 평면도(A-type)
SCALE : A1 : 1/40
A3 : 1/80

■22m² 단위세대(A-type) 실별 면적표


구분	실 별	면 적(㎡)	구분		면 적(㎡)
전용	거실/침실	14.16	주거 공용 면적	벽체 중심 면적	4.21
	주방/식당	3.77			
	현관	1.47			
	욕실	2.64	서비스 면적	발코니	2.65
전용면적계		22.04	주거공용면적계		4.21
계(전용+주거공용)		26.25			

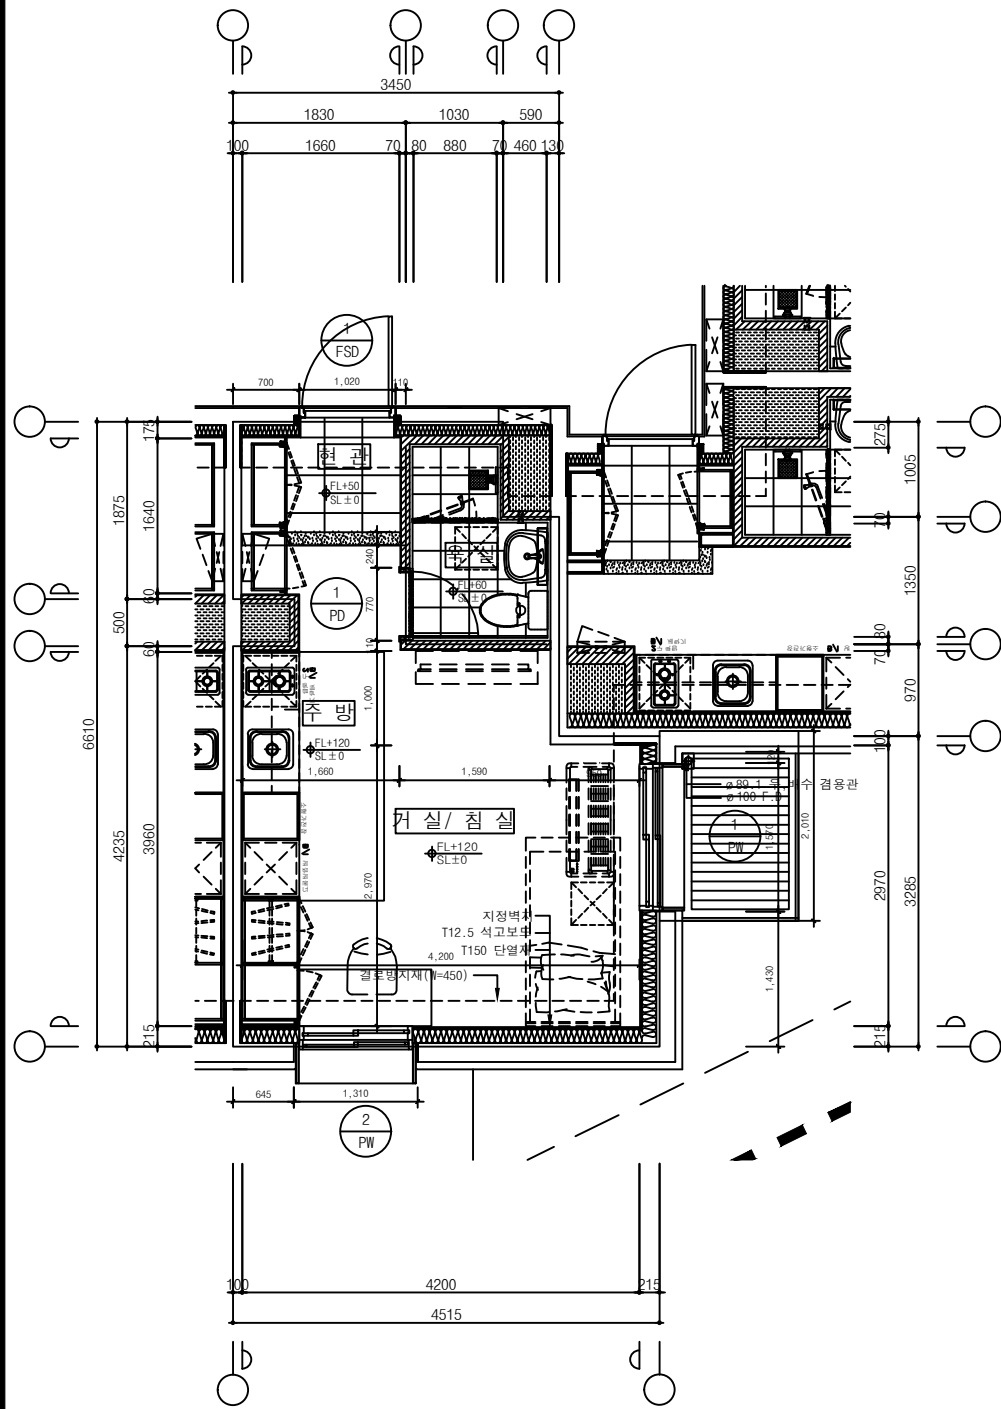

3 22m² 형 단위세대 평면도(C-type)
SCALE : A1 : 1/40
A3 : 1/80

■22m² 단위세대(C-type) 실별 면적표


구분	실 별	면 적(㎡)	구분	면 적(㎡)	
전용	거실/침실	13.44	주거 공용 면적	벽체 중심 면적	3.37
	주방/식당	3.94			
	현관	1.95			
	욕실	2.68	서비스 면적	발코니	2.95
전용면적계		22.01	주거공용면적계		3.37
계(전용+주거공용)		25.38			

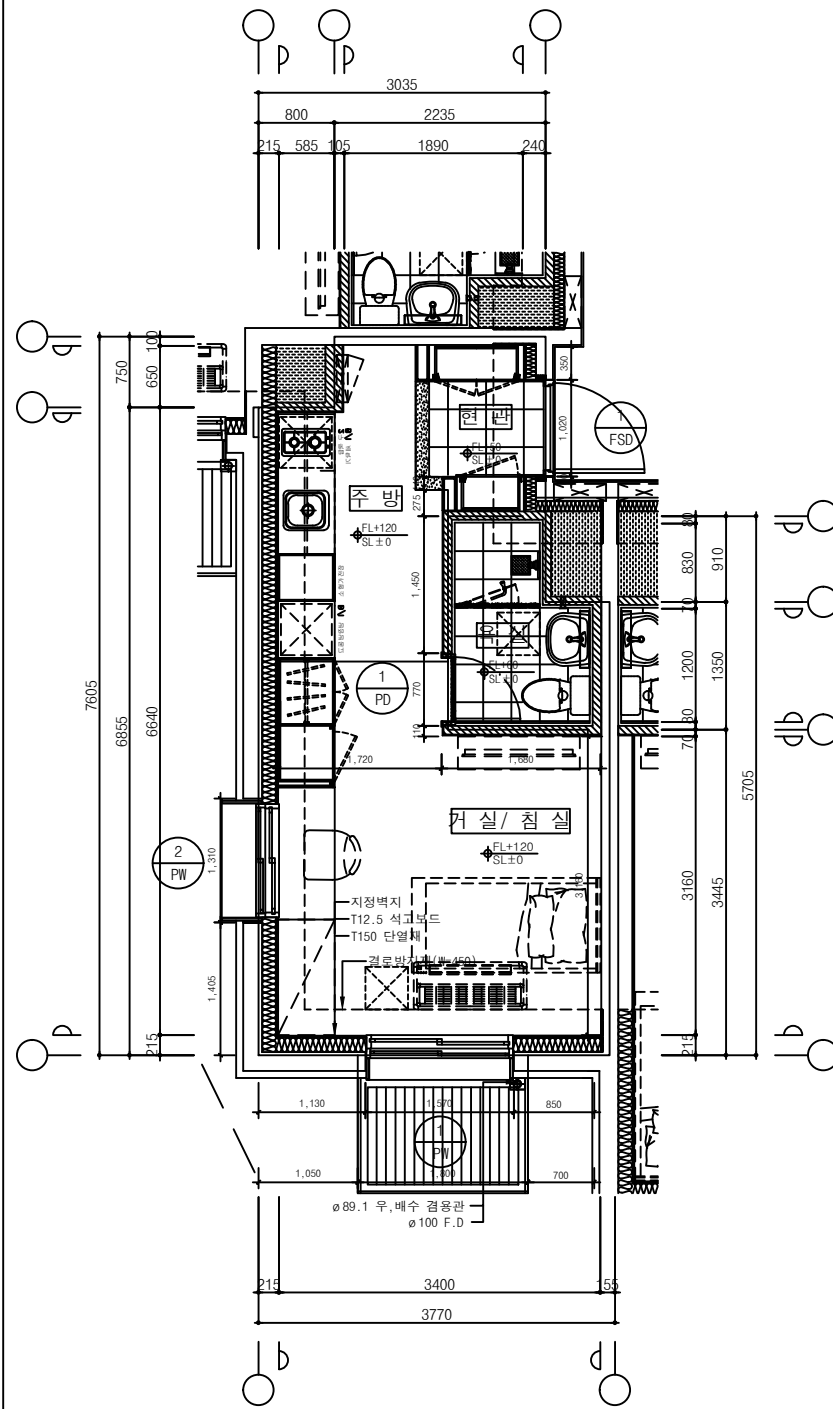

4 22m² 형 단위세대 평면도(D-type)
SCALE : A1 : 1/40
A3 : 1/80

■22m² 단위세대(D-type) 실별 면적표

구분	실 별	면 적(m²)	구분	면 적(m²)	
전용	거실/침실	12.26	주거 공용 면적	벽체 중심 면적	3.75
	주방/식당	4.97			
	현관	1.94			
	욕실	2.84	서비스 면적	발코니	2.63
전용면적계		22.01	주거공용면적계		3.75
계(전용+주거공용)		25.76			

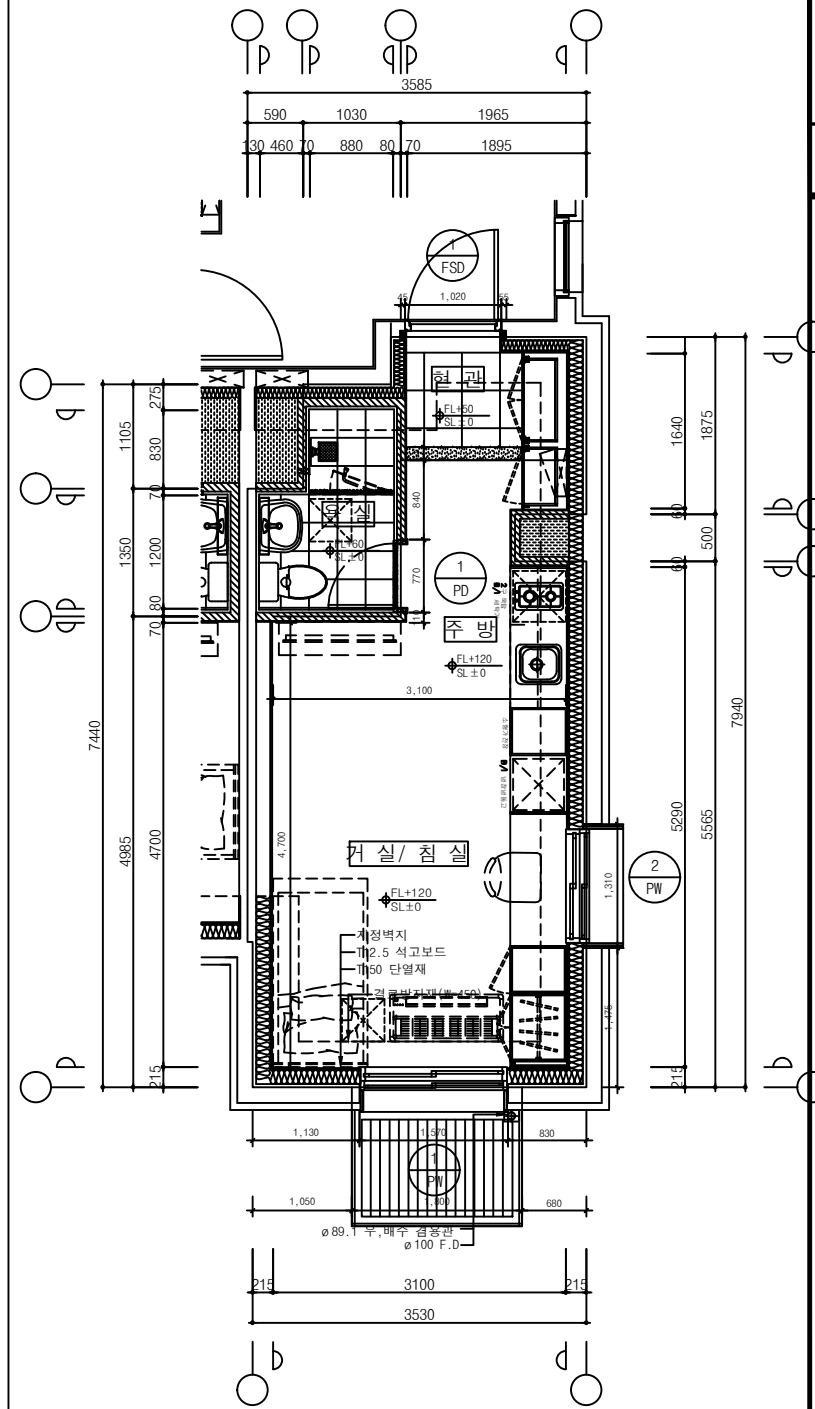

5 22m² 형 단위세대 평면도(E-type)
SCALE : A1 : 1/40
A3 : 1/80

■22m² 단위세대(E-type) 실별 면적표

구분	실 별	면 적(㎡)	구분	면 적(㎡)	
전용	거실/침실	13.36	주거 공용 면적	벽체 중심 면적	4.59
	주방/식당	3.94			
	현관	1.94			
	욕실	2.77	서비스 면적	발코니	2.65
전용면적계		22.01	주거공용면적계		4.59
계(전용+주거공용)		26.60			

SH
에스이이치 공사

방향동 313-7, 38번지
공공리모델링 공사

프로젝트 코드
PROJECT CODE
N O T E

1. 코아부분은 동별 코아 평. 단면도 참조
2. 피로티상부 옥실레벨은 구조도면 참조
3. 부분은 설비담당과 협의후 슬리브 설치(기계)
4. 세대분전반 설치시 신발장 상세에 대해 언급할 것
5. 발코니 외부창호는 현장실측후 제작설치
7. 우수 및 배수드레인은 기계공중시설 설치도 참조하되 반드시 건축감독과 위치를 협의할 것.
8. 세대간벽은 차음1등급(58dB) 이상 만족하도록 밀실하게 시공할 것.

수정 및 제출내용
ISSUES & REVISION

번호 NO.	내 DESCRIPTION	용 DATE	일자 DATE	승인 APPR
1				
2				
3				
4				
5				

설 계 DRAWN BY	
검 토 1 CHECKED-1 BY	박 동 국
검 토 2 CHECKED-2 BY	박 동 국
승 인 APPROVED BY	박 경 진
기 관 분 류 ORGAN CLASS	

도 면 명
DRAWING TITLE
단위세대 평면도-2

축
척
SCALE A1:40
A3:80
날
짜
DATE 2022. 11.

도면번호
DWG NO. A - 202

설
계
용
역
PROJECT OFFICE

HYUN
[주]종합건축사사무소 한
서울특별시 강남구 테헤란로81길 유림빌딩 9층
TEL (02)2135-8087, FAX (02)2135-8085

협력업체-1
CONSULTS

협력업체-2
CONSULTS

수정 및 제출내용
ISSUES & REVISION

번호 NO.	내용 DESCRIPTION	일자 DATE	승인 APPR
△			
△			
△			
△			
△			


설계 DRAWN BY	
검토 1 CHECKED-1 BY	박 동 국
검토 2 CHECKED-2 BY	박 동 국
승인 APPROVED BY	박 경 진
기관분류 ORGAN CLASS	

도면명 DRAWING TITLE
단위세대 평면도-3

축척 SCALE	A1: A3:	날짜 DATE	2022. 11.
-------------	------------	------------	-----------

도면번호 DWG NO.	A - 203
-----------------	---------

설계용역 PROJECT OFFICE

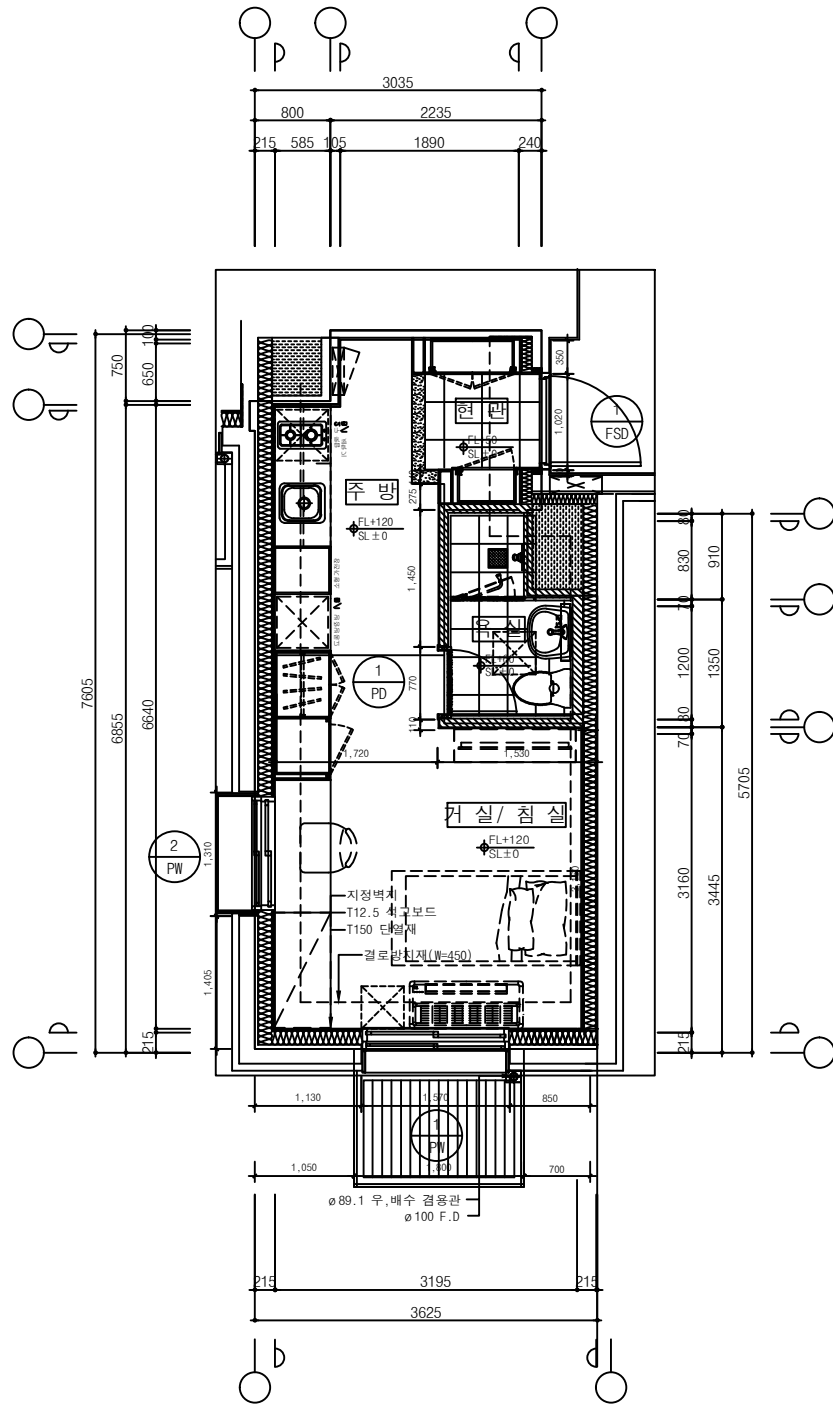

4
A 21㎡형 단위세대 평면도(D-1type)4,5 층
SCALE : A1 : 1/40
A3 : 1/80

■ 21㎡ 단위세대(D-1type) 실별 면적표

구분	실 별	면 적(㎡)	구분	면 적(㎡)
전용	거실/침실	11.60	주거 공용 면적	벽체 중심 면적
	주방/식당	4.97		
	현관	1.94		
	욕실	2.51	서비스 면적	발코니
전용면적계		21,02	주거공용면적계	4,17
계(전용+주거공용)				25,19

수정 및 제출내용
ISSUES & REVISION

번호 NO.	내용 DESCRIPTION	일자 DATE	승인 APPR
△			
△			
△			
△			
△			


설계 DRAWN BY	
검토 1 CHECKED-1 BY	박 동 국
검토 2 CHECKED-2 BY	박 동 국
승인 APPROVED BY	박 경 진
기관분류 ORGAN CLASS	

도면명 DRAWING TITLE	단위세대 MC 중심선도-1
----------------------	-------------------



축척 SCALE	A1 : 40 A3 : 80	날짜 DATE	2022. 11.
-------------	--------------------	------------	-----------

도면번호 DWG NO.	A - 211
-----------------	---------

설계용역 PROJECT OFFICE	
------------------------	--

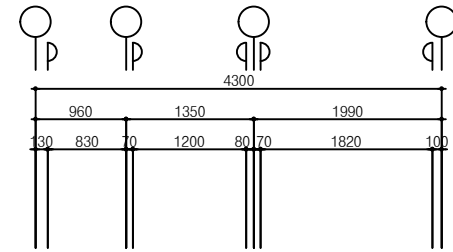

평면도

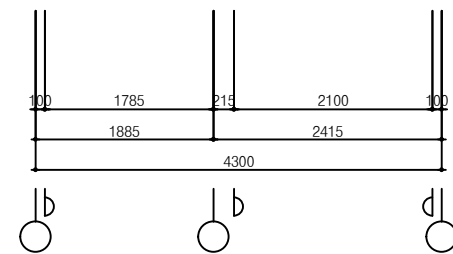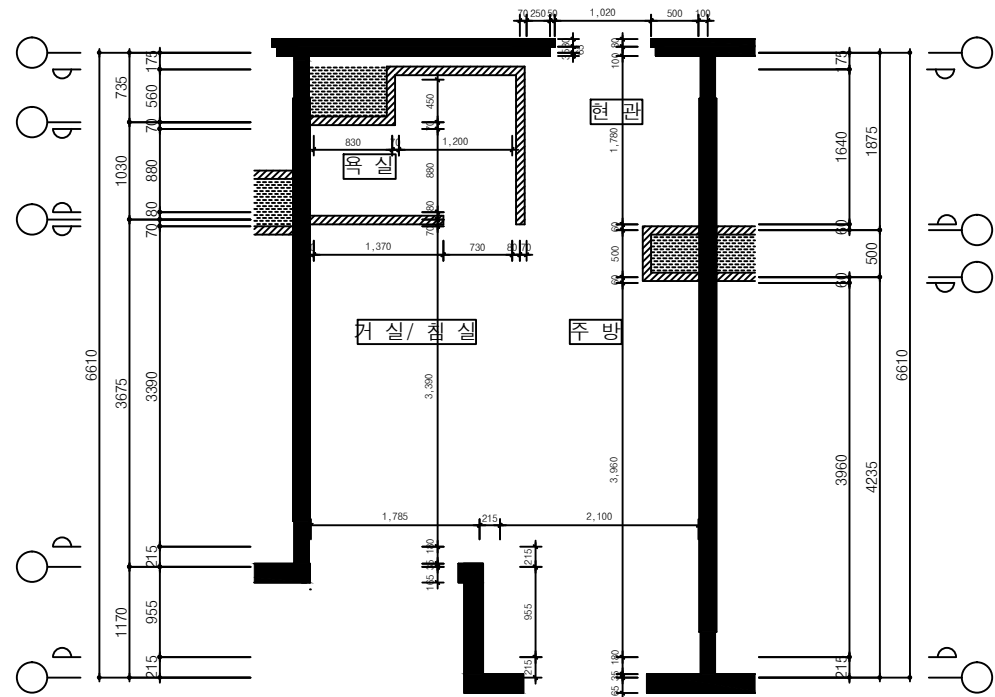


2 22m² 형 단위세대 평면도(B-type)

SCALE : A1 : 1/40
A3 : 1/80

22m² 단위세대(B-type) 실별 면적표

구분	실 별	면 적(㎡)	구분	면 적(㎡)	
전용	거실/침실	13.18	주거 공용 면적	벽체 중심 면적	3.17
	주방/식당	3.95			
	현관	2.13			
	욕실	2.76	서비스 면적	발코니	2.60
전용면적계		22.02	주거공용면적계		3.17
계(전용+주거공용)		25.19			

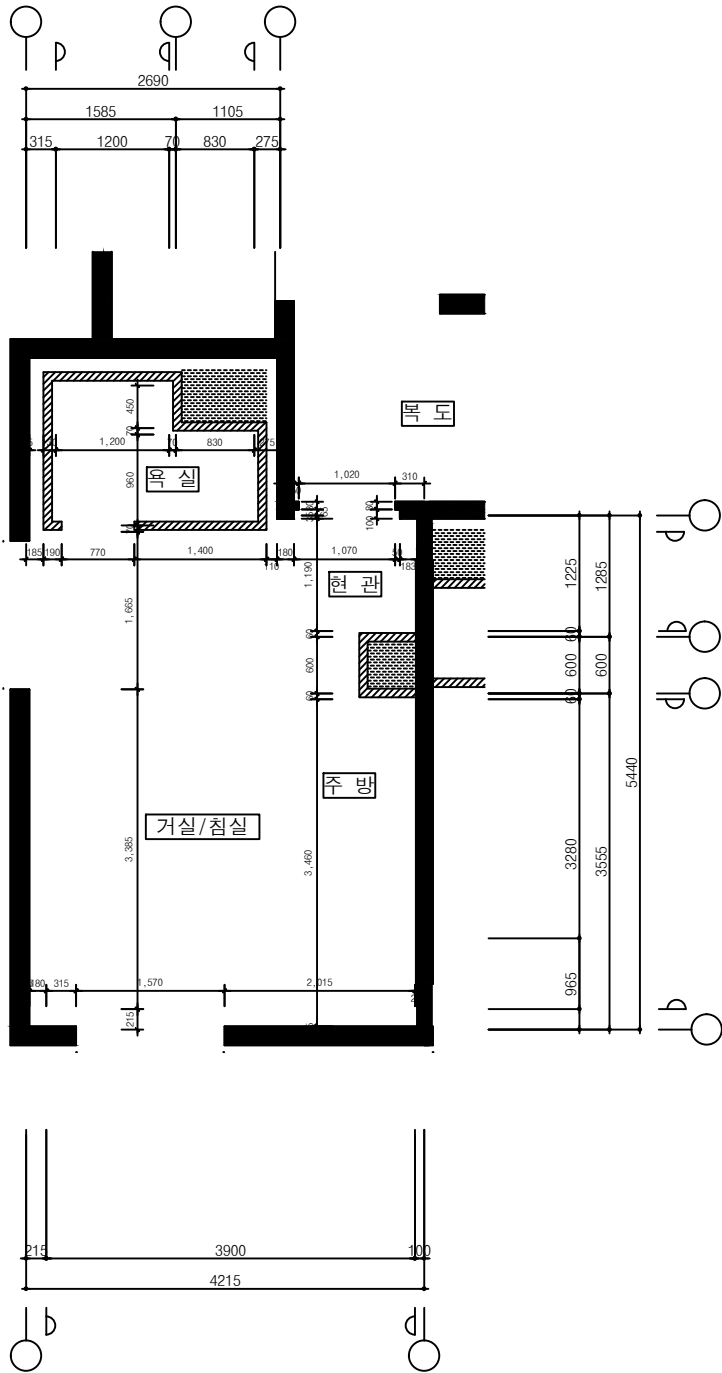


1 22m² 형 단위세대 평면도(A-type)

SCALE : A1 : 1/40
A3 : 1/80

22m² 단위세대(A-type) 실별 면적표


구분	실 별	면 적(㎡)	구분	면 적(㎡)		
전용	거실/침실	14.27	주거 공용 면적	벽체 중심 면적	4.21	
	주방/식당	3.24				
	현관	1.89				
	욕실	2.64	서비스 면적	발코니	2.61	
전용면적계		22.04	주거공용면적계		4.21	
계(전용+주거공용)						26.25

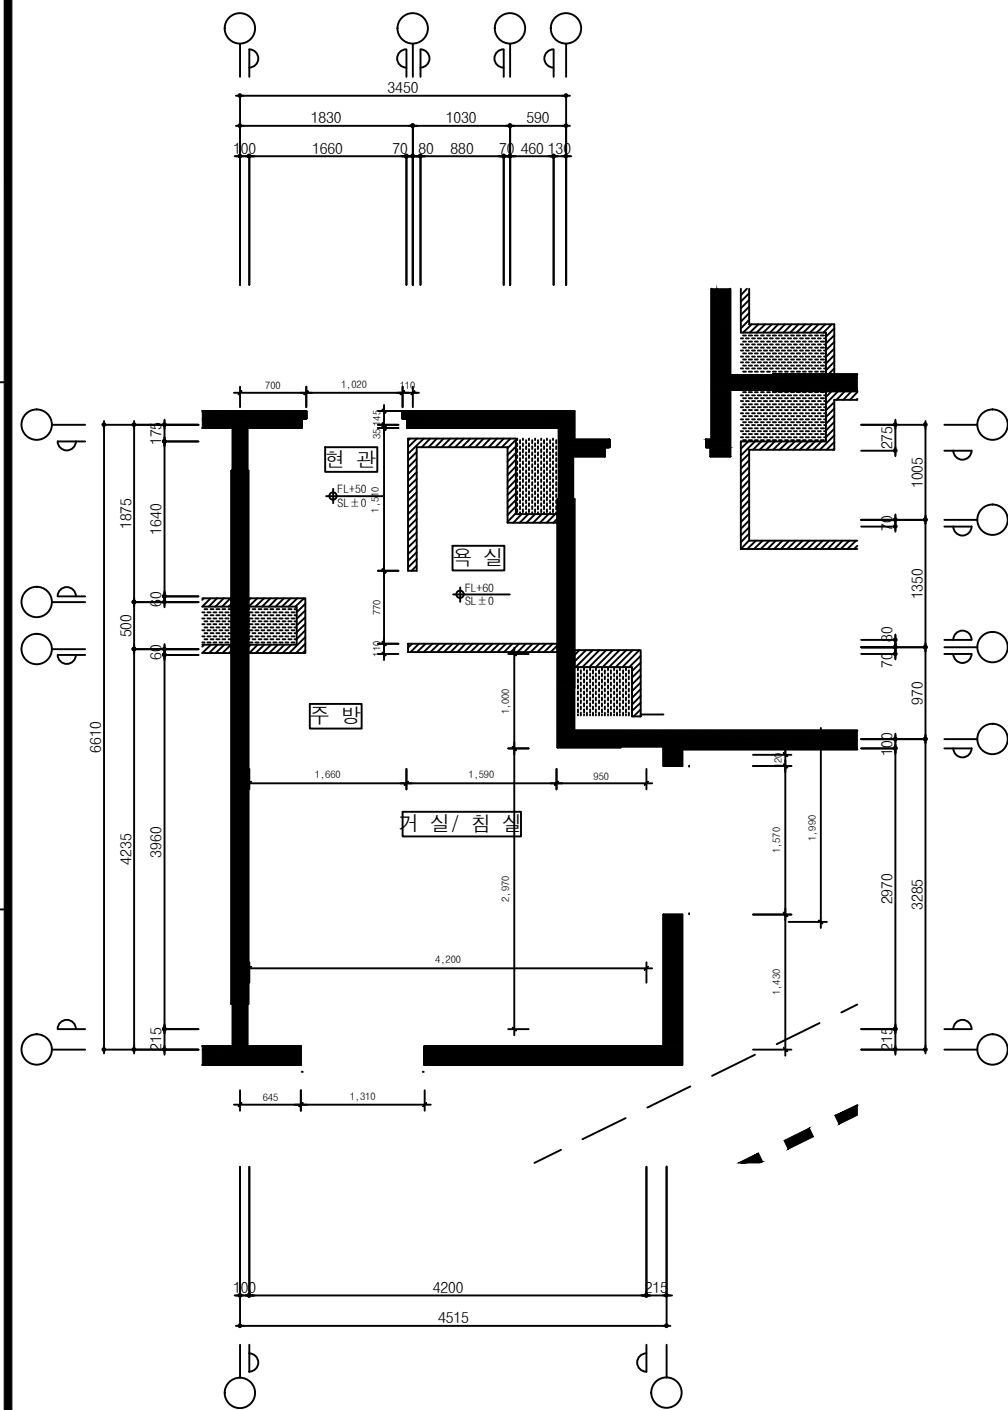

3 22m² 형 단위세대 평면도(C-type)
SCALE : A1 : 1/40
A3 : 1/80

■22m² 단위세대(C-type) 실별 면적표


구분	실 별	면 적(m ²)	구분	면 적(m ²)	
전용	거실/침실	13.44	주거 공용 면적	벽체 중심 면적	3.37
	주방/식당	3.94			
	현관	1.95			
	욕실	2.68	서비스 면적	발코니	2.89
전용면적계		22.01	주거공용면적계		3.37
계(전용+주거공용)		25.38			

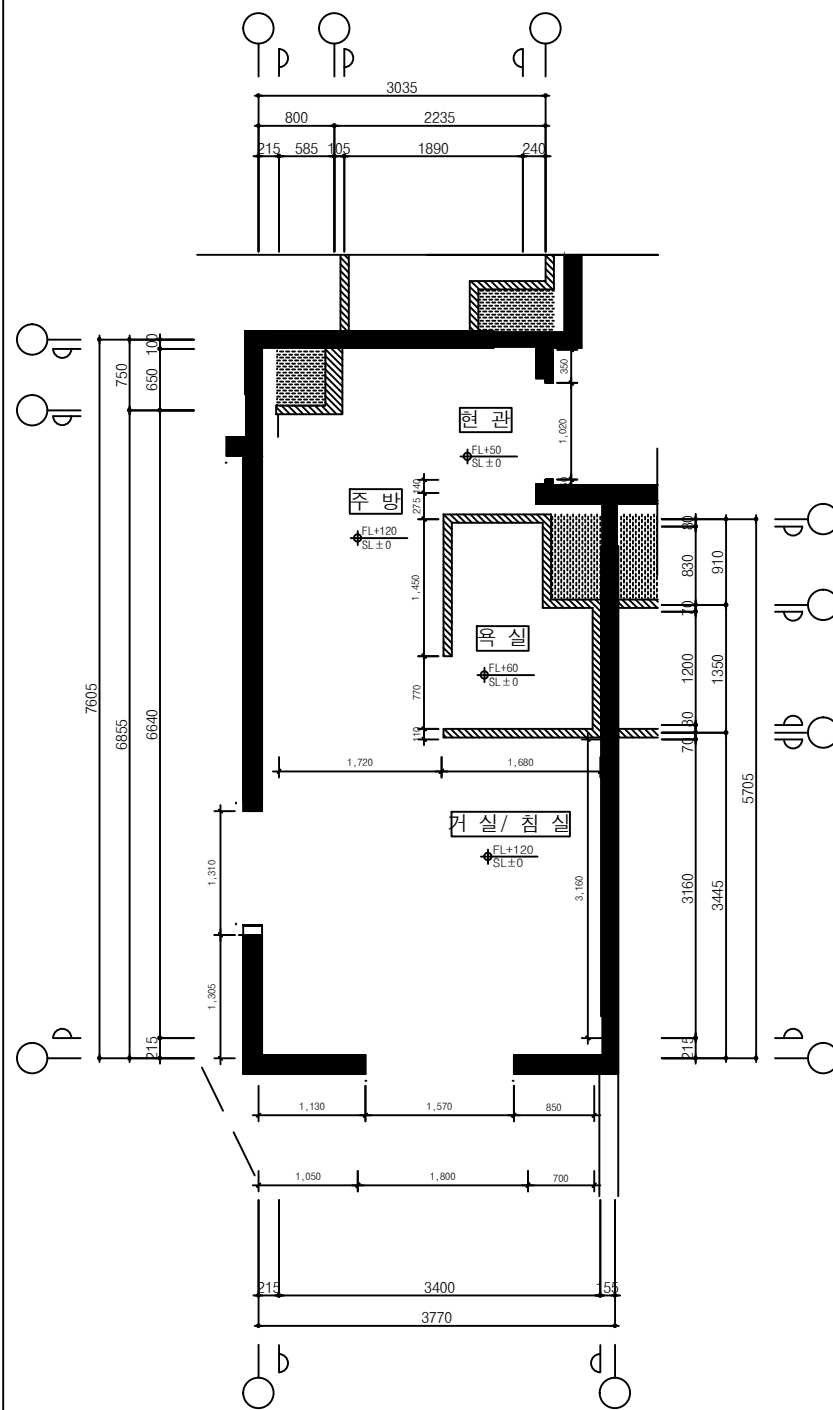

4 22m² 형 단위세대 평면도(D-type)
SCALE : A1 : 1/40
A3 : 1/80

■22m² 단위세대(D-type) 실별 면적표

구분	실 별	면 적(m²)	구분	면 적(m²)	
전용	거실/침실	12.26	주거 공용 면적	벽체 중심 면적	3.75
	주방/식당	4.97			
	현관	1.94			
	욕실	2.84	서비스 면적	발코니	2.61
전용면적계		22.01	주거공용면적계		3.75
계(전용+주거공용)		25.76			

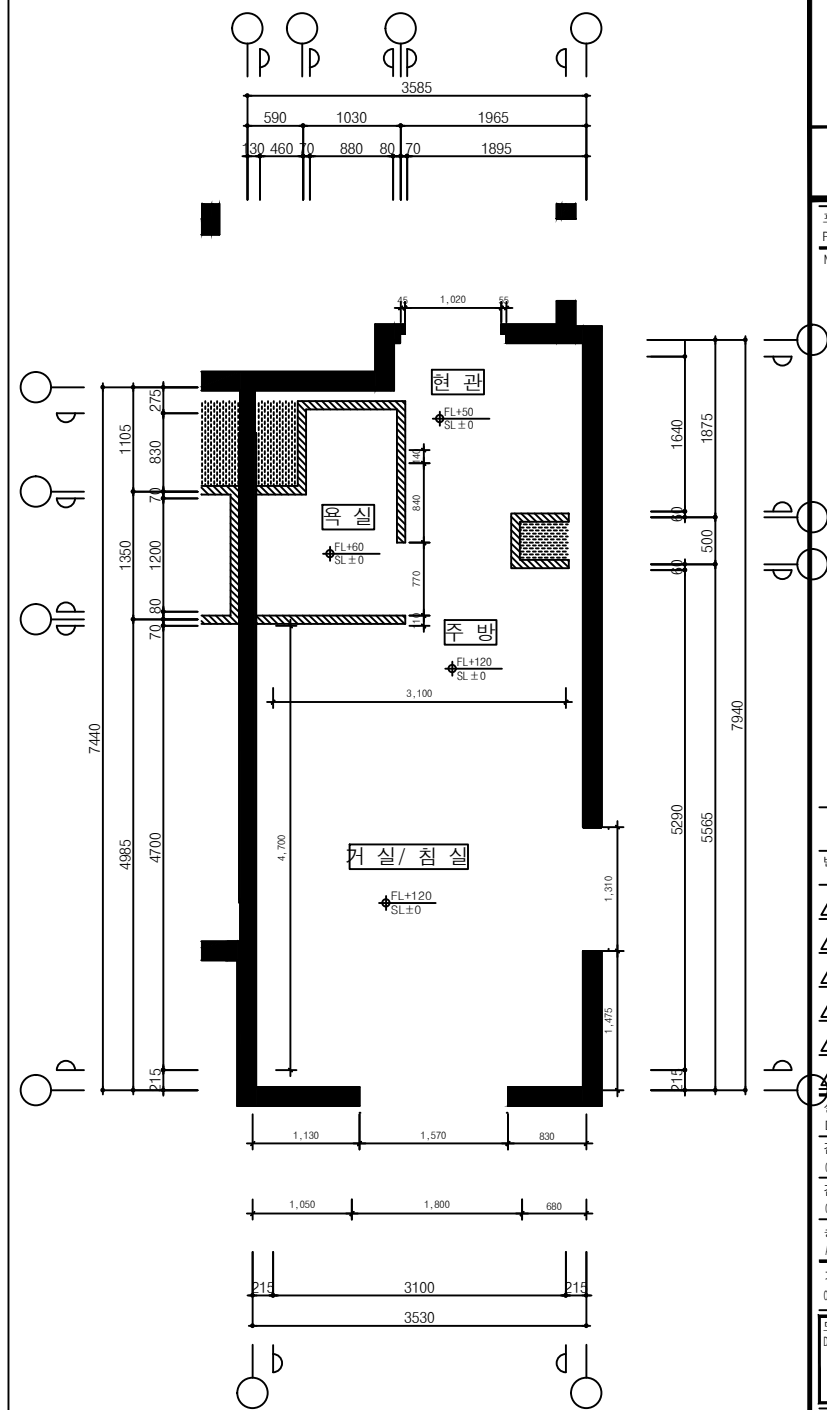

5 22m² 형 단위세대 평면도(E-type)
SCALE : A1 : 1/40
A3 : 1/80

■22m² 단위세대(E-type) 실별 면적표

구분	실 별	면 적(m²)	구분	면 적(m²)	
전용	거실/침실	13.36	주거 공용 면적	벽체 중심 면적	4.59
	주방/식당	3.94			
	현관	1.94			
	욕실	2.77	서비스 면적	발코니	2.61
전용면적계		22.01	주거공용면적계		4.59
계(전용+주거공용)		26.60			



방학동 313-7, 38번지
공공리모델링 공사

프로젝트코드
PROJECT CODE
N O T E

수정 및 제출내용
ISSUES & REVISION

번호 NO.	내 DESCRIPTION	용 DATE	일자 DATE	승인 APPR
△				
△				
△				
△				
△				

설 계 DRAWN BY	
검 토 1 CHECKED-1 BY	박 동 국
검 토 2 CHECKED-2 BY	박 동 국
승 인 APPROVED BY	박 경 진
기 관 분 류 ORGAN CLASS	

도 면 명 DRAWING TITLE	단위세대 MC 중심선도-2
------------------------------	-------------------

축 척 SCALE	A1: 40 A3: 80	날 짜 DATE	2022. 11.
-----------------	------------------	----------------	-----------

도면번호
DWG NO. A - 212

설
계
용
역
PROJECT OFFICE



서울특별시 강남구 테헤란로81길 유림빌딩 9층
TEL (02)2135-8087, FAX (02)2135-8085

협력업체-1
CONSULTS

협력업체-2
CONSULTS



방학동 313-7, 38번지
공공리모델링 공사

프로젝트코드
PROJECT CODE
N O T E

수정 및 제출내용
ISSUES & REVISION

번호 NO.	내 容 DESCRIPTION	일자 DATE	승인 APPR
△			
△			
△			
△			
△			

설 계 DRAWN BY	
검 토 1 CHECKED-1 BY	박 동 국
검 토 2 CHECKED-2 BY	박 동 국
승 인 APPROVED BY	박 경 진
기 관 분 류 ORGAN CLASS	

도 면 명 DRAWING TITLE	단위세대 MC 중심선도-3
------------------------------	-------------------

축 척 SCALE	A1 : 40 A3 : 80	날 짜 DATE	2022. 11.
-----------------	--------------------	----------------	-----------

도면번호 DWG NO.	A - 213
-----------------	---------


설 계 용 역 PROJECT OFFICE	
------------------------------------	--



서울특별시 강남구 테헤란로81길 유림빌딩 9층
TEL (02)2135-8087, FAX (02)2135-8085

협력업체-1
CONSULTS





협력업체-2
CONSULTS

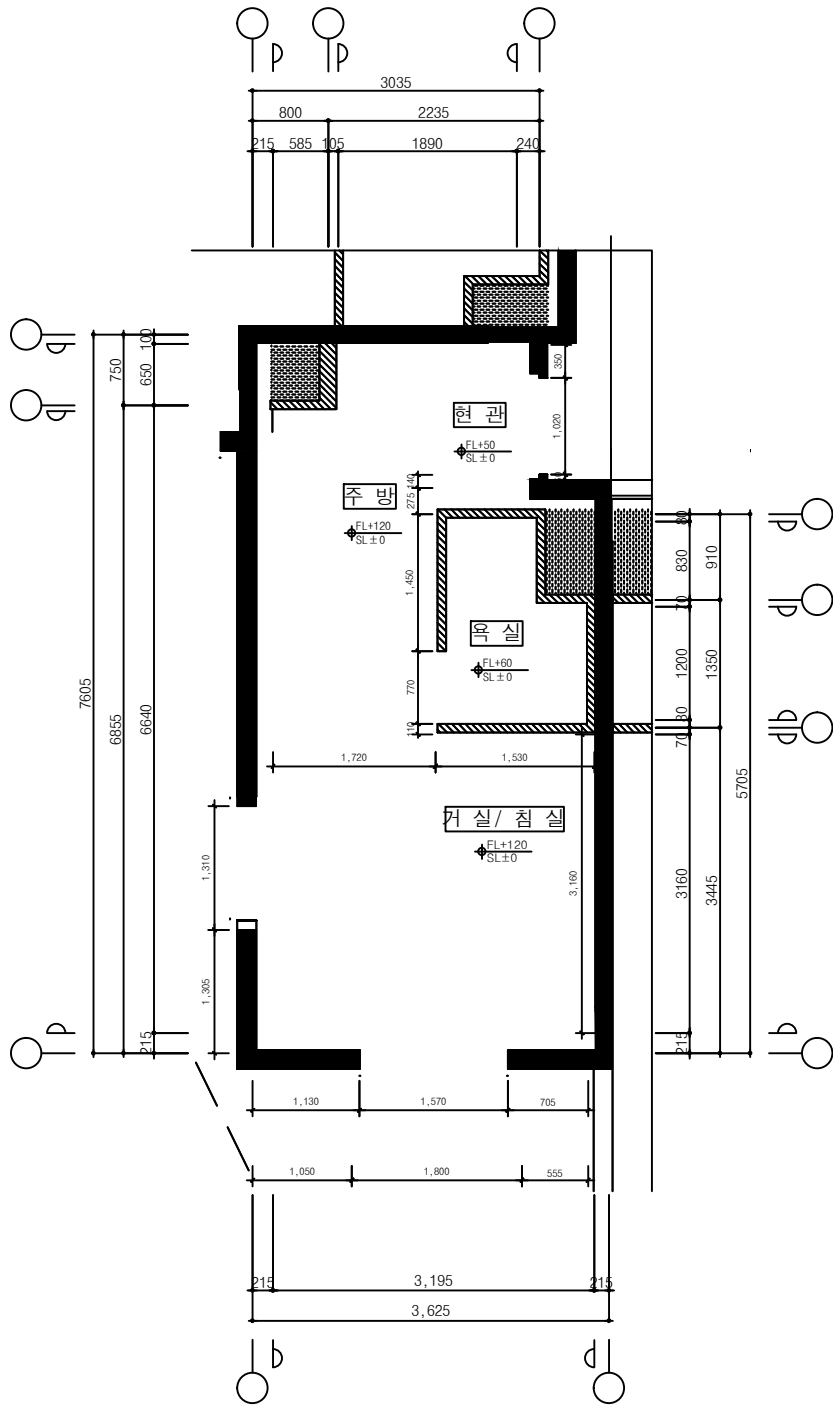

4 21㎡형 단위세대 평면도(D-1type)4,5층
A SCALE : A1 : 1/40
A3 : 1/80

구분	실 별	면 적(㎡)	구분	면 적(㎡)	
전용	거실/침실	11.60	주거 공용 면적	벽체 중심 면적	4.17
	주방/식당	4.97			
	현관	1.94	서비스 면적	발코니	
	욕실	2.51			
전용면적계		21.02	주거공용면적계		4.17
계(전용+주거공용)		25.19			

KEY MAP

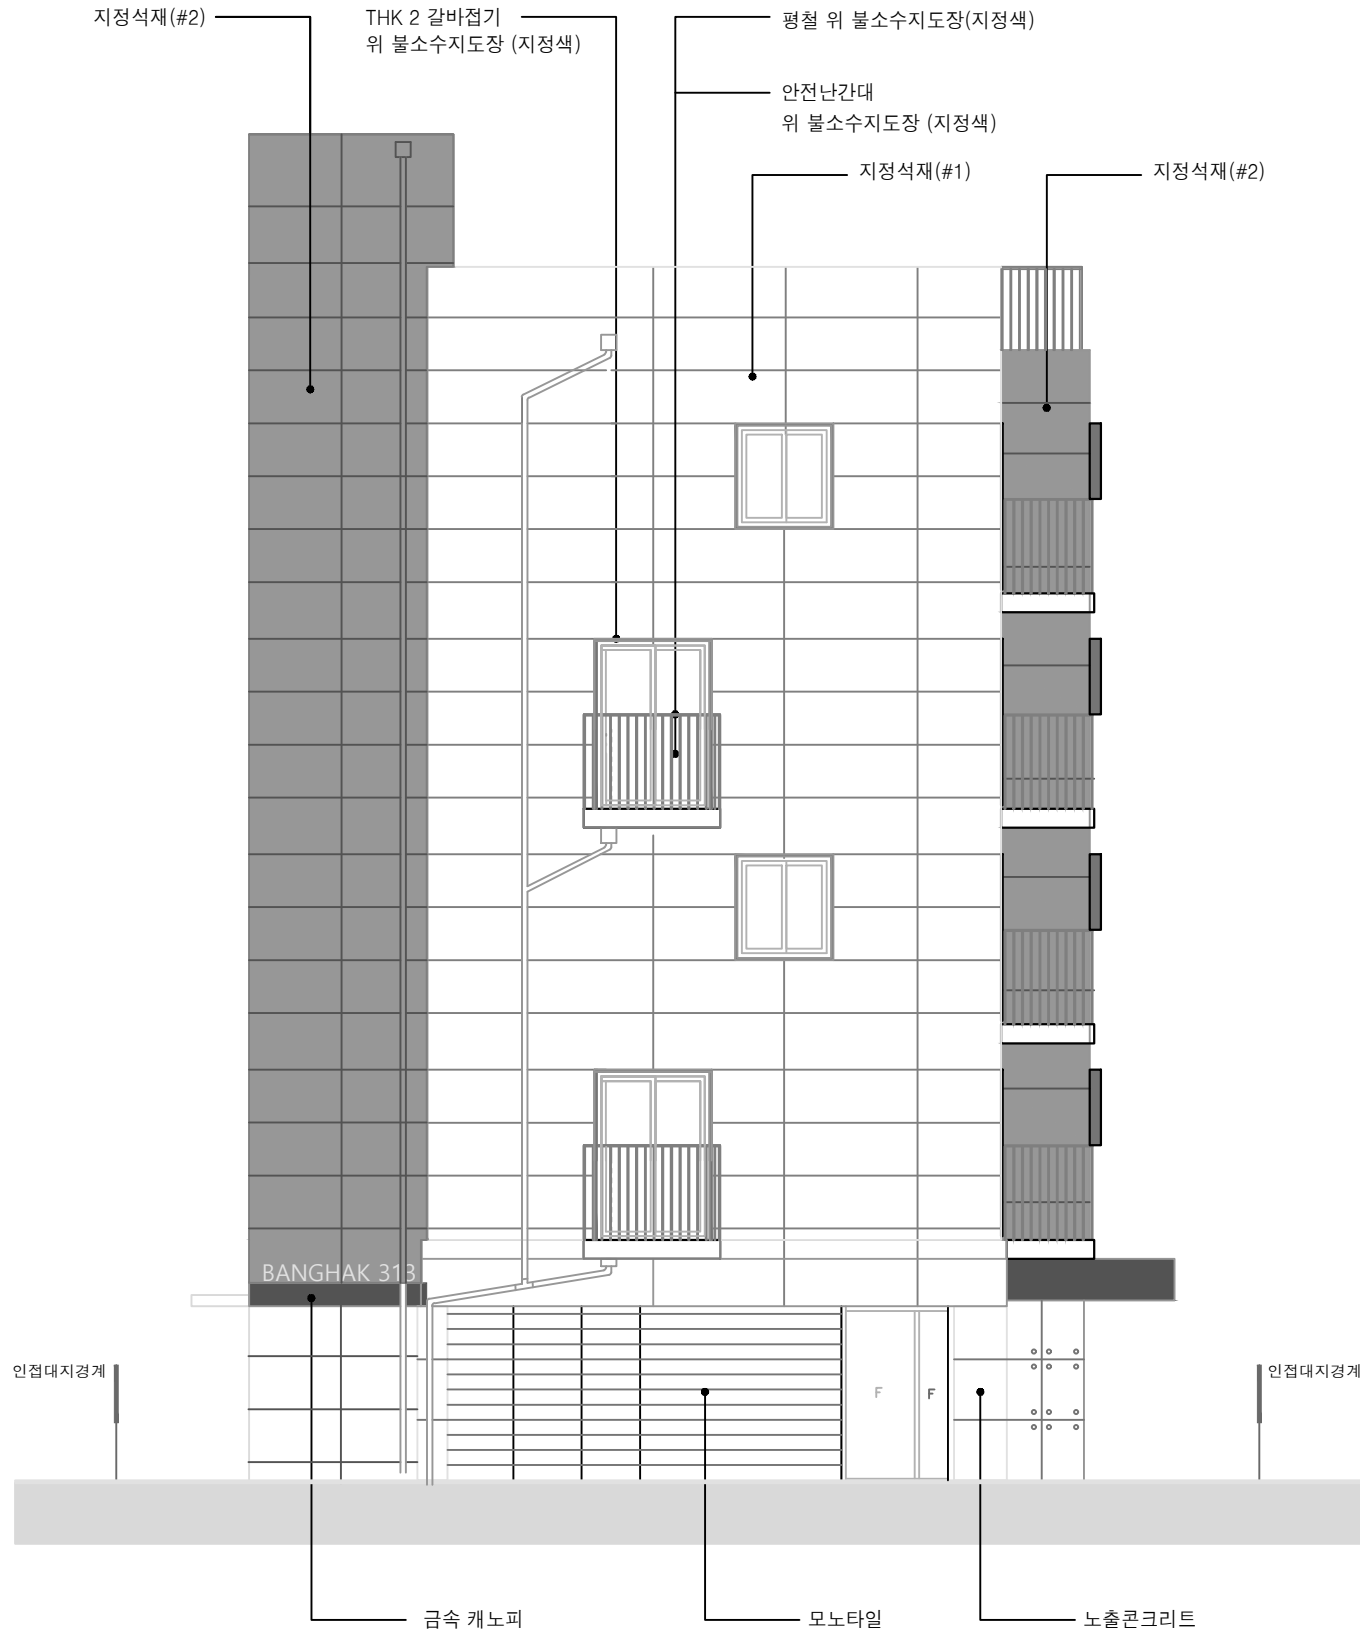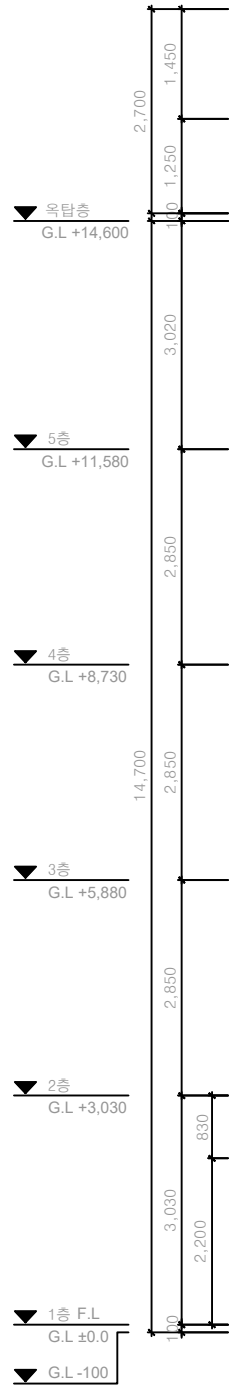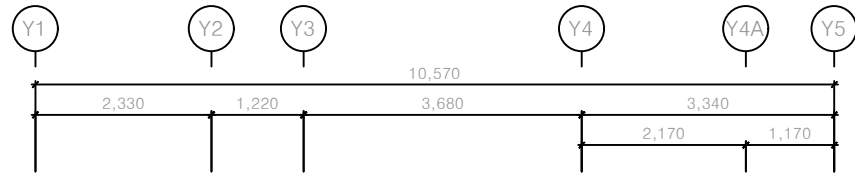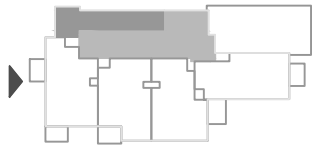

북측면도
SCALE : A1 : 1/ 50
A3 : 1/100



방학동 313-7, 38번지
공공리모델링 공사

프로젝트코드
PROJECT CODE
N O T E

수정 및 제출내용
ISSUES & REVISION

번호 NO.	내 DESCRIPTION	용 DATE	일자 DATE	승인 APPR
△				
△				
△				
△				
△				

설 계 DRAWN BY	
검 토 1 CHECKED-1 BY	박 동 국
검 토 2 CHECKED-2 BY	박 동 국
승 인 APPROVED BY	박 경 진
기 관 분 류 ORGAN CLASS	

도 면 명 DRAWING TITLE	북측면도
------------------------------	------

축 척 SCALE	A1 : 50 A3 : 100	날 짜 DATE	2022. 11.
-----------------	---------------------	----------------	-----------

도면번호 DWG NO.	A - 301
-----------------	---------

설 계 용 역 PROJECT OFFICE	
------------------------------------	--





서울특별시 강남구 테헤란로81길 유림빌딩 9층
TEL (02)2135-8087, FAX (02)2135-8085

협력업체-1 CONSULTS	
--------------------	--

협력업체-2 CONSULTS	
--------------------	--

KEY MAP

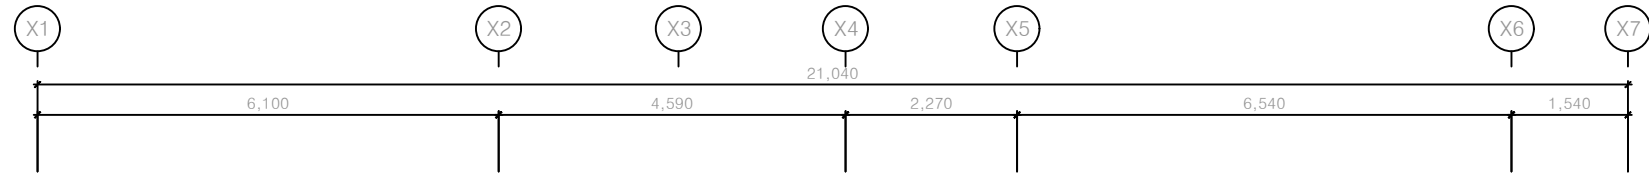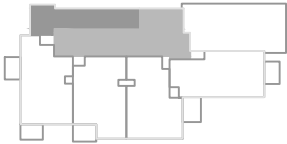

방학동 313-7,38번지
공공리모델링 공사

프로젝트코드
PROJECT CODE
N O T E

수정 및 제출내용
ISSUES & REVISION

번호 NO.	내용 DESCRIPTION	일자 DATE	승인 APPR
△			
△			
△			
△			
△			

설 계 DRAWN BY	
검 토 1 CHECKED-1 BY	박 동 국
검 토 2 CHECKED-2 BY	박 동 국
승 인 APPROVED BY	박 경 진
기관분류 ORGAN CLASS	

도 면 명 DRAWING TITLE	서 측 면 도
------------------------	---------

축 척 SCALE	A1: 50 A3: 100	날 짜 DATE	2022. 11.
--------------	-------------------	-------------	-----------

도면번호 DWG NO.	A - 302
-----------------	---------

설 계 용 역 PROJECT OFFICE	
---------------------------	--



서울특별시 강남구 테헤란로81길 유림빌딩 9층
TEL (02)2135-8087, FAX (02)2135-8085

협력업체-1
CONSULTS





협력업체-2
CONSULTS



서 측 면 도

SCALE : A1 : 1/ 50
A3 : 1/100

KEY MAP

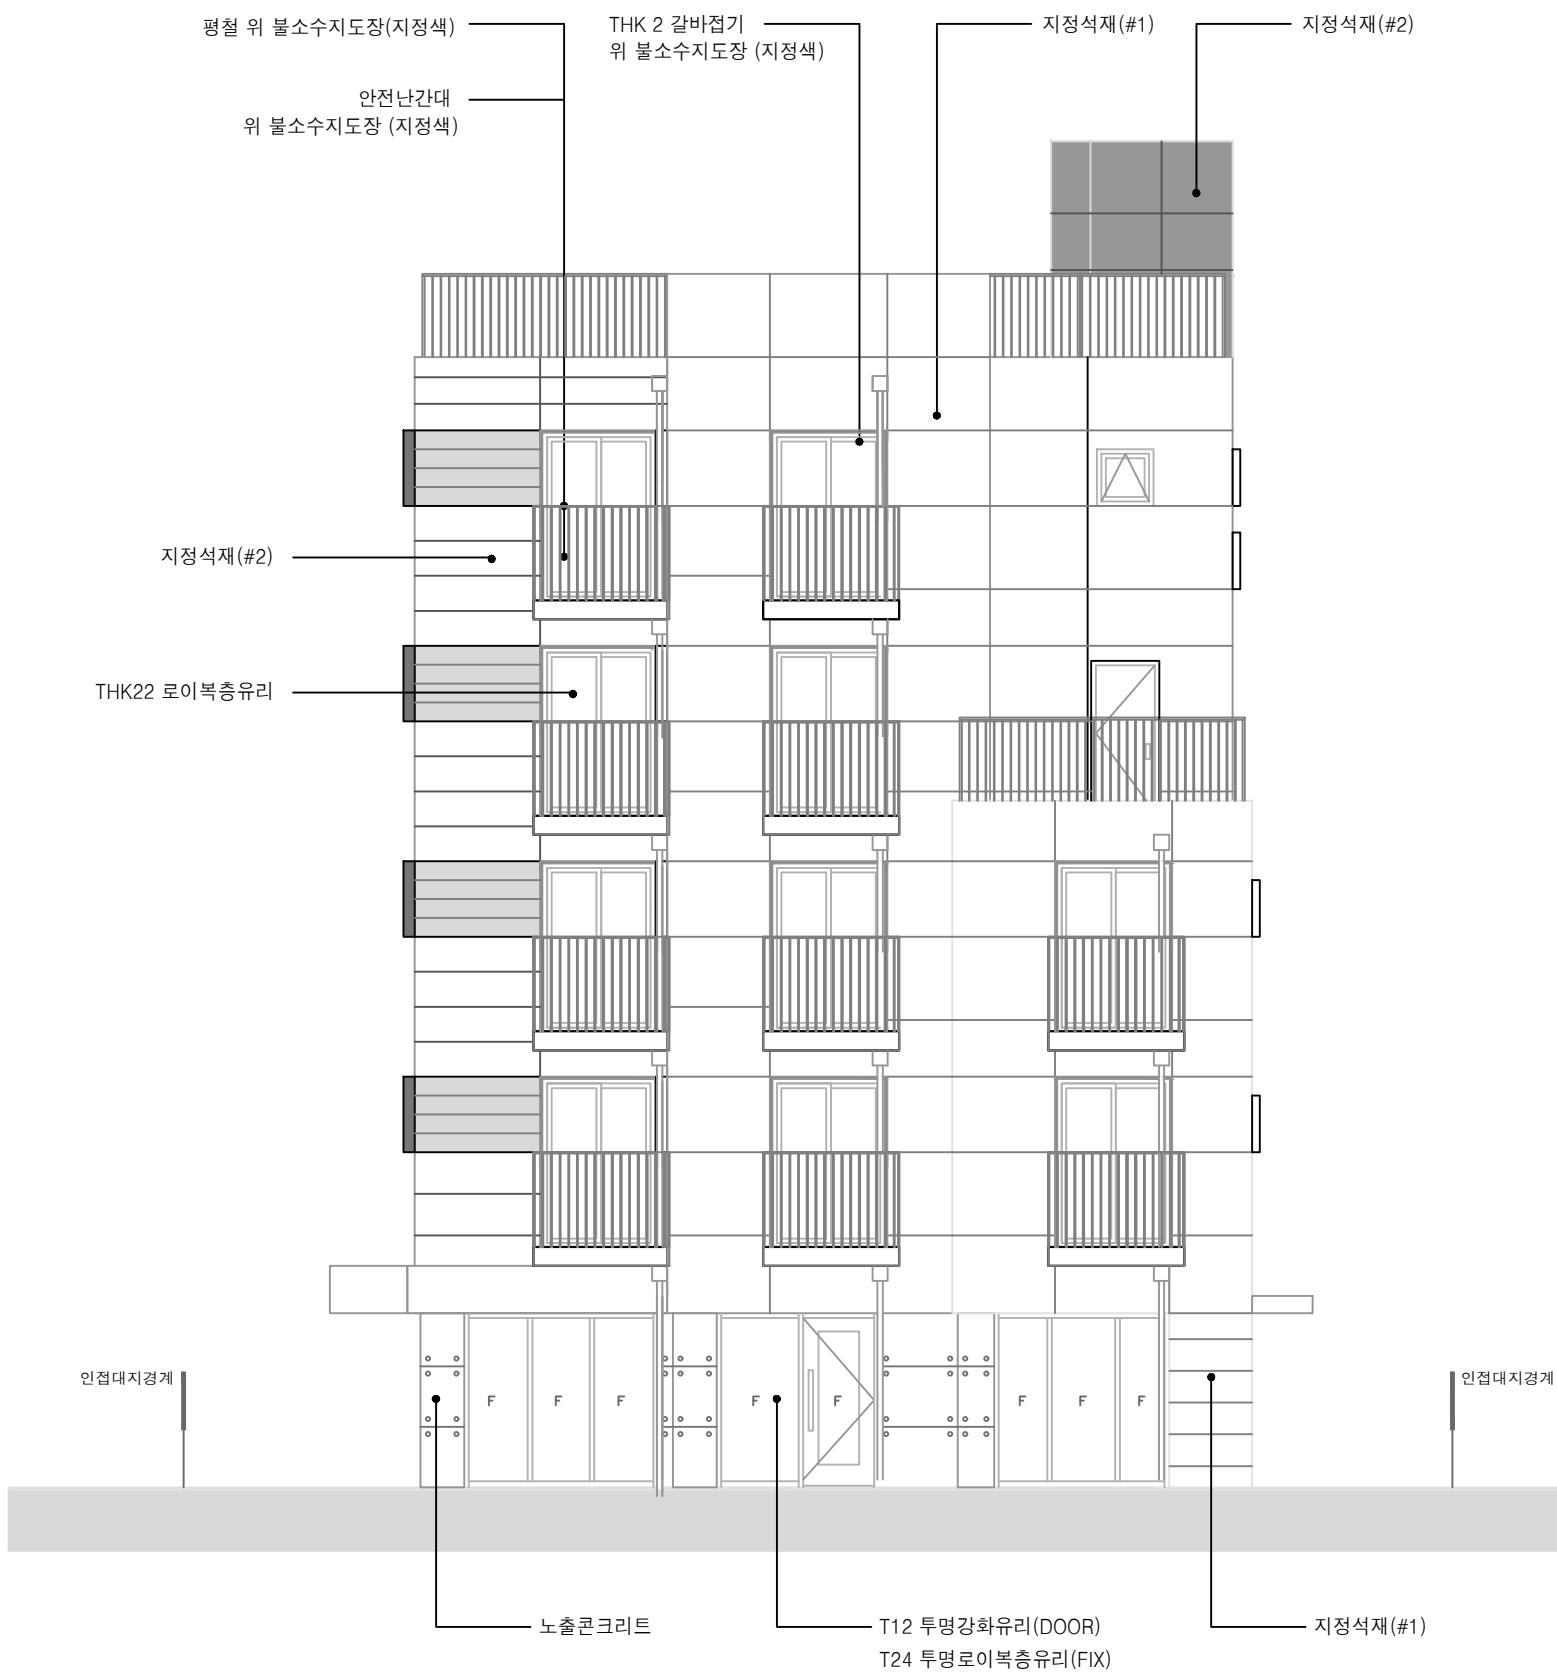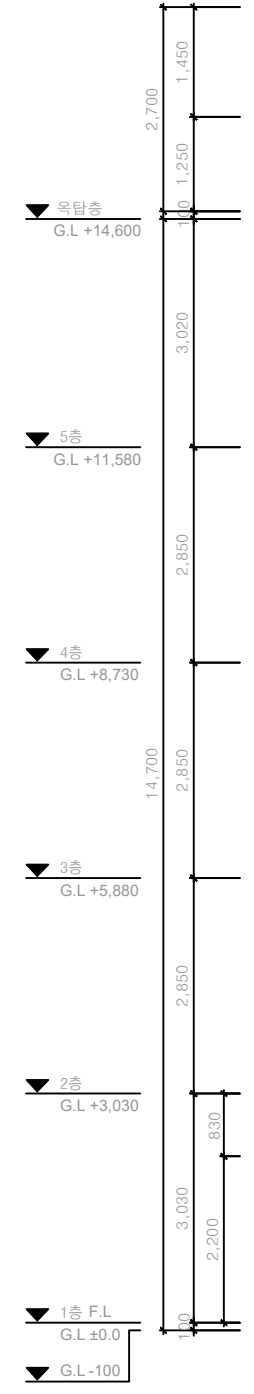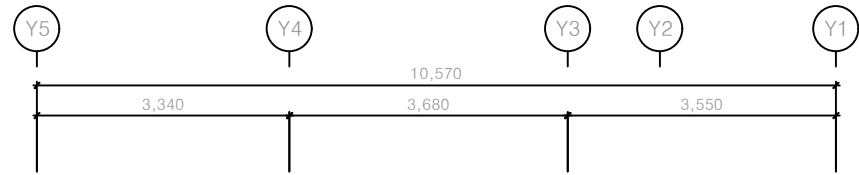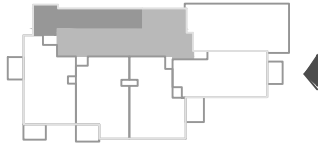

남측면도
SCALE : A1 : 1/ 50
A3 : 1/100



방학동 313-7, 38번지
공공리모델링 공사

프로젝트코드
PROJECT CODE
N O T E

수정 및 제출내용
ISSUES & REVISION

번호 NO.	내용 DESCRIPTION	일자 DATE	승인 APPR
△			
△			
△			
△			
△			

설계 DRAWN BY	
검토 1 CHECKED-1 BY	박 동 국
검토 2 CHECKED-2 BY	박 동 국
승인 APPROVED BY	박 경 진
기관분류 ORGAN CLASS	

도면명
DRAWING TITLE
남측면도

축척 SCALE	A1 : 50 A3 : 100	날짜 DATE	2022. 11.
-------------	---------------------	------------	-----------

도면번호
DWG NO. A - 303

설계용역
PROJECT OFFICE






서울특별시 강남구 테헤란로81길 유림빌딩 9층
TEL (02)2135-8087, FAX (02)2135-8085

협력업체-1
CONSULTS

협력업체-2
CONSULTS

KEY MAP

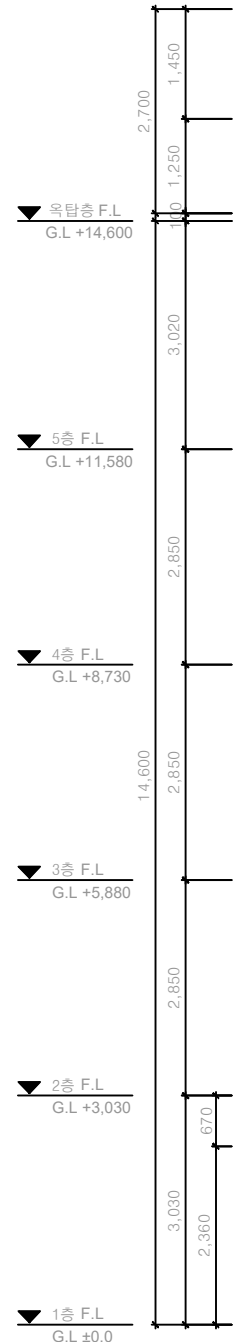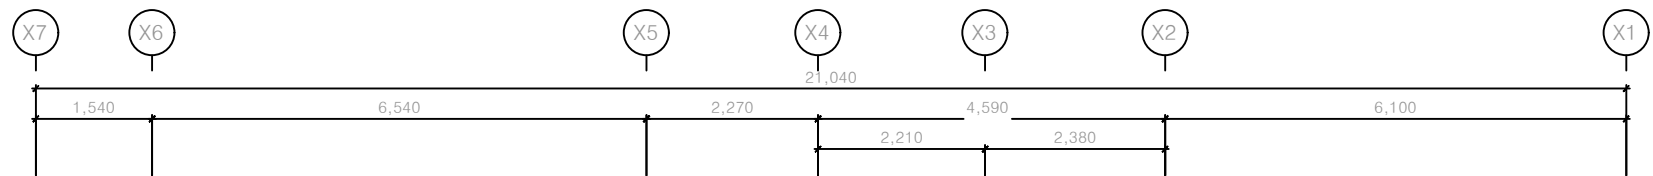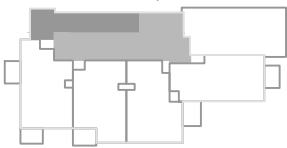

동측면도
SCALE : A1 : 1/ 50
A3 : 1/100



방학동 313-7,38번지
공공리모델링 공사

프로젝트코드
PROJECT CODE
N O T E

수정 및 제출내용
ISSUES & REVISION

번호 NO.	내 DESCRIPTION	용 DATE	승인 APPR
△			
△			
△			
△			
△			

설 DRAWN BY	
검 토 1 CHECKED-1 BY	박 동 국
검 토 2 CHECKED-2 BY	박 동 국
승 인 APPROVED BY	박 경 진
기 관분류 ORGAN CLASS	

도 면 명 DRAWING TITLE	동 측 면 도
------------------------	---------

축척 SCALE	A1: 50 A3: 100	날 짜 DATE	2022. 11.
-------------	-------------------	-------------	-----------

도면번호
DWG NO. A - 304

설 계 용 역
PROJECT OFFICE

HYUN
[주]종합건축사사무소 현 (株)
서울특별시 강남구 테헤란로81길 유림빌딩 9층
TEL (02)2135-8087, FAX (02)2135-8085

협력업체-1
CONSULTS

협력업체-2
CONSULTS