


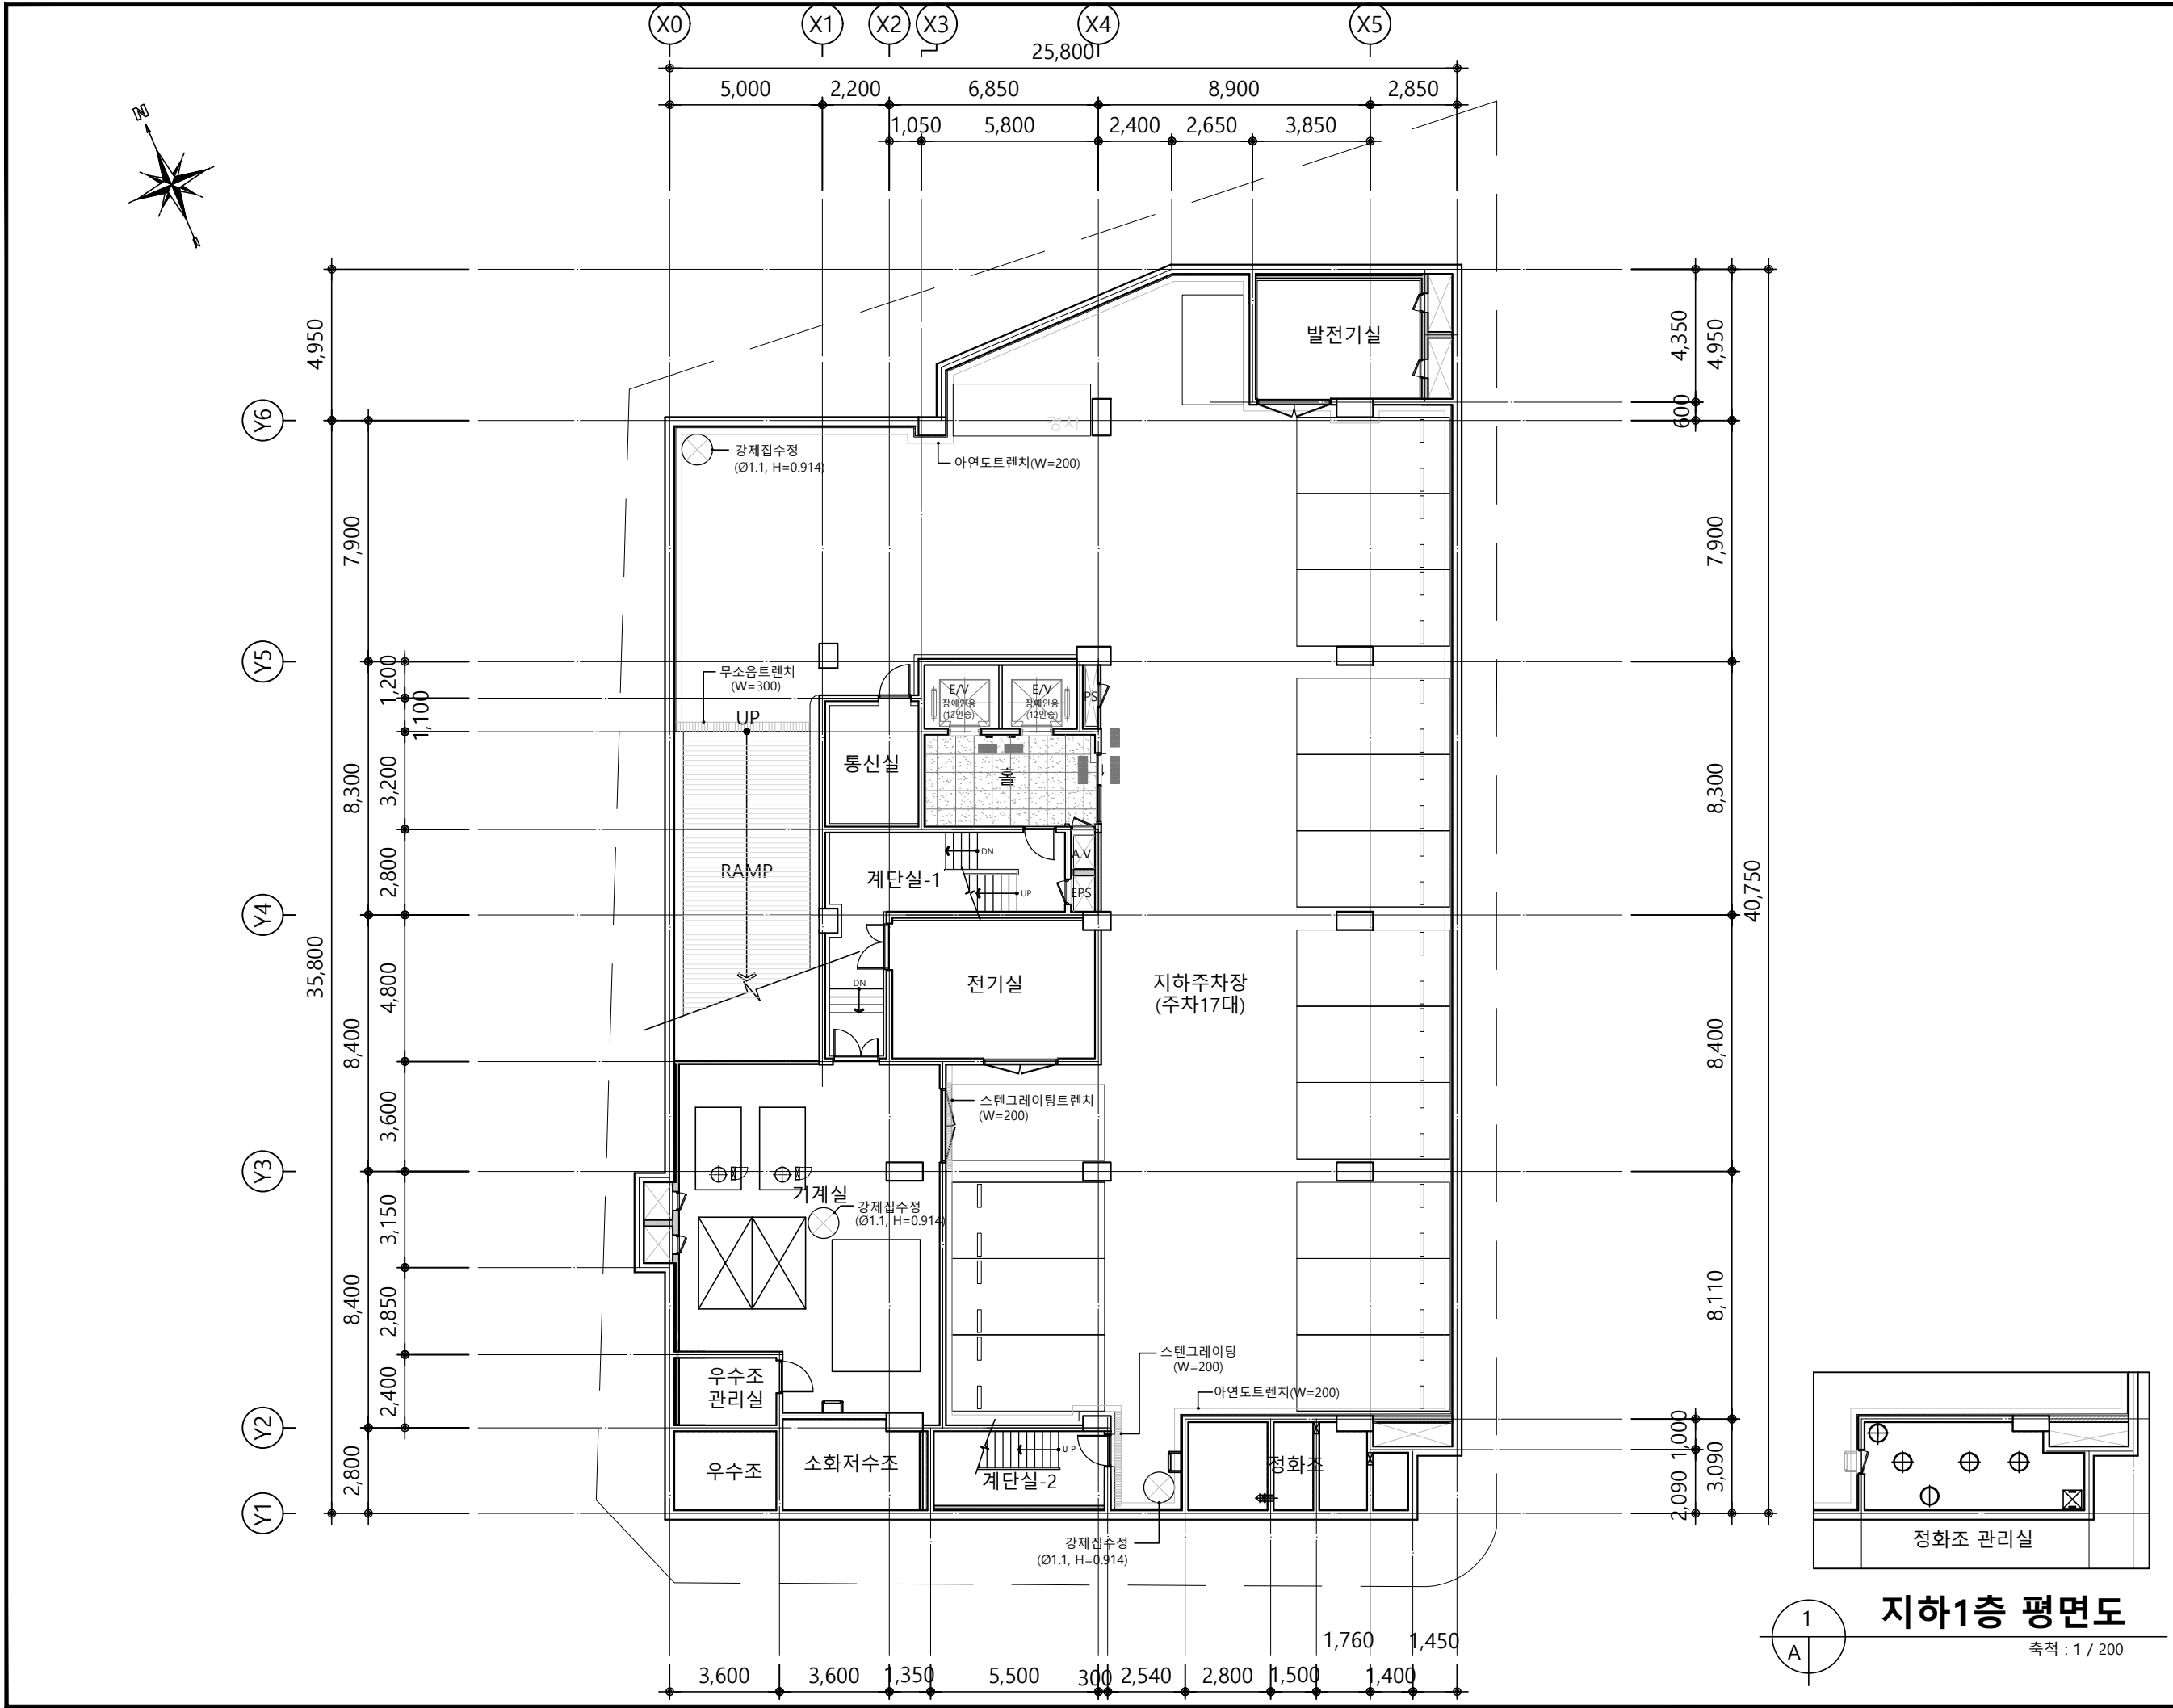

PROJECT TITLE


장안동 591
주거복합시설
신축공사

제이케이건축사사무소(주)
Architects & Planners

TEL : 02-533-9431 FAX : 02-532-9431

NOTE

설 계 변 경 DESCRIPTION OF REVISION					
번 호		내 용			
일 자	설 계	검 토	심 사	승 인	
	2024.06				
승인 APPROVED BY					
축 척 SCALE	A1	1 / 100			
	A3	1 / 200			
도면명 DRAWING TITLE					
지하1층 평면도					
도면번호 DRAWING NO.					
A - 301					


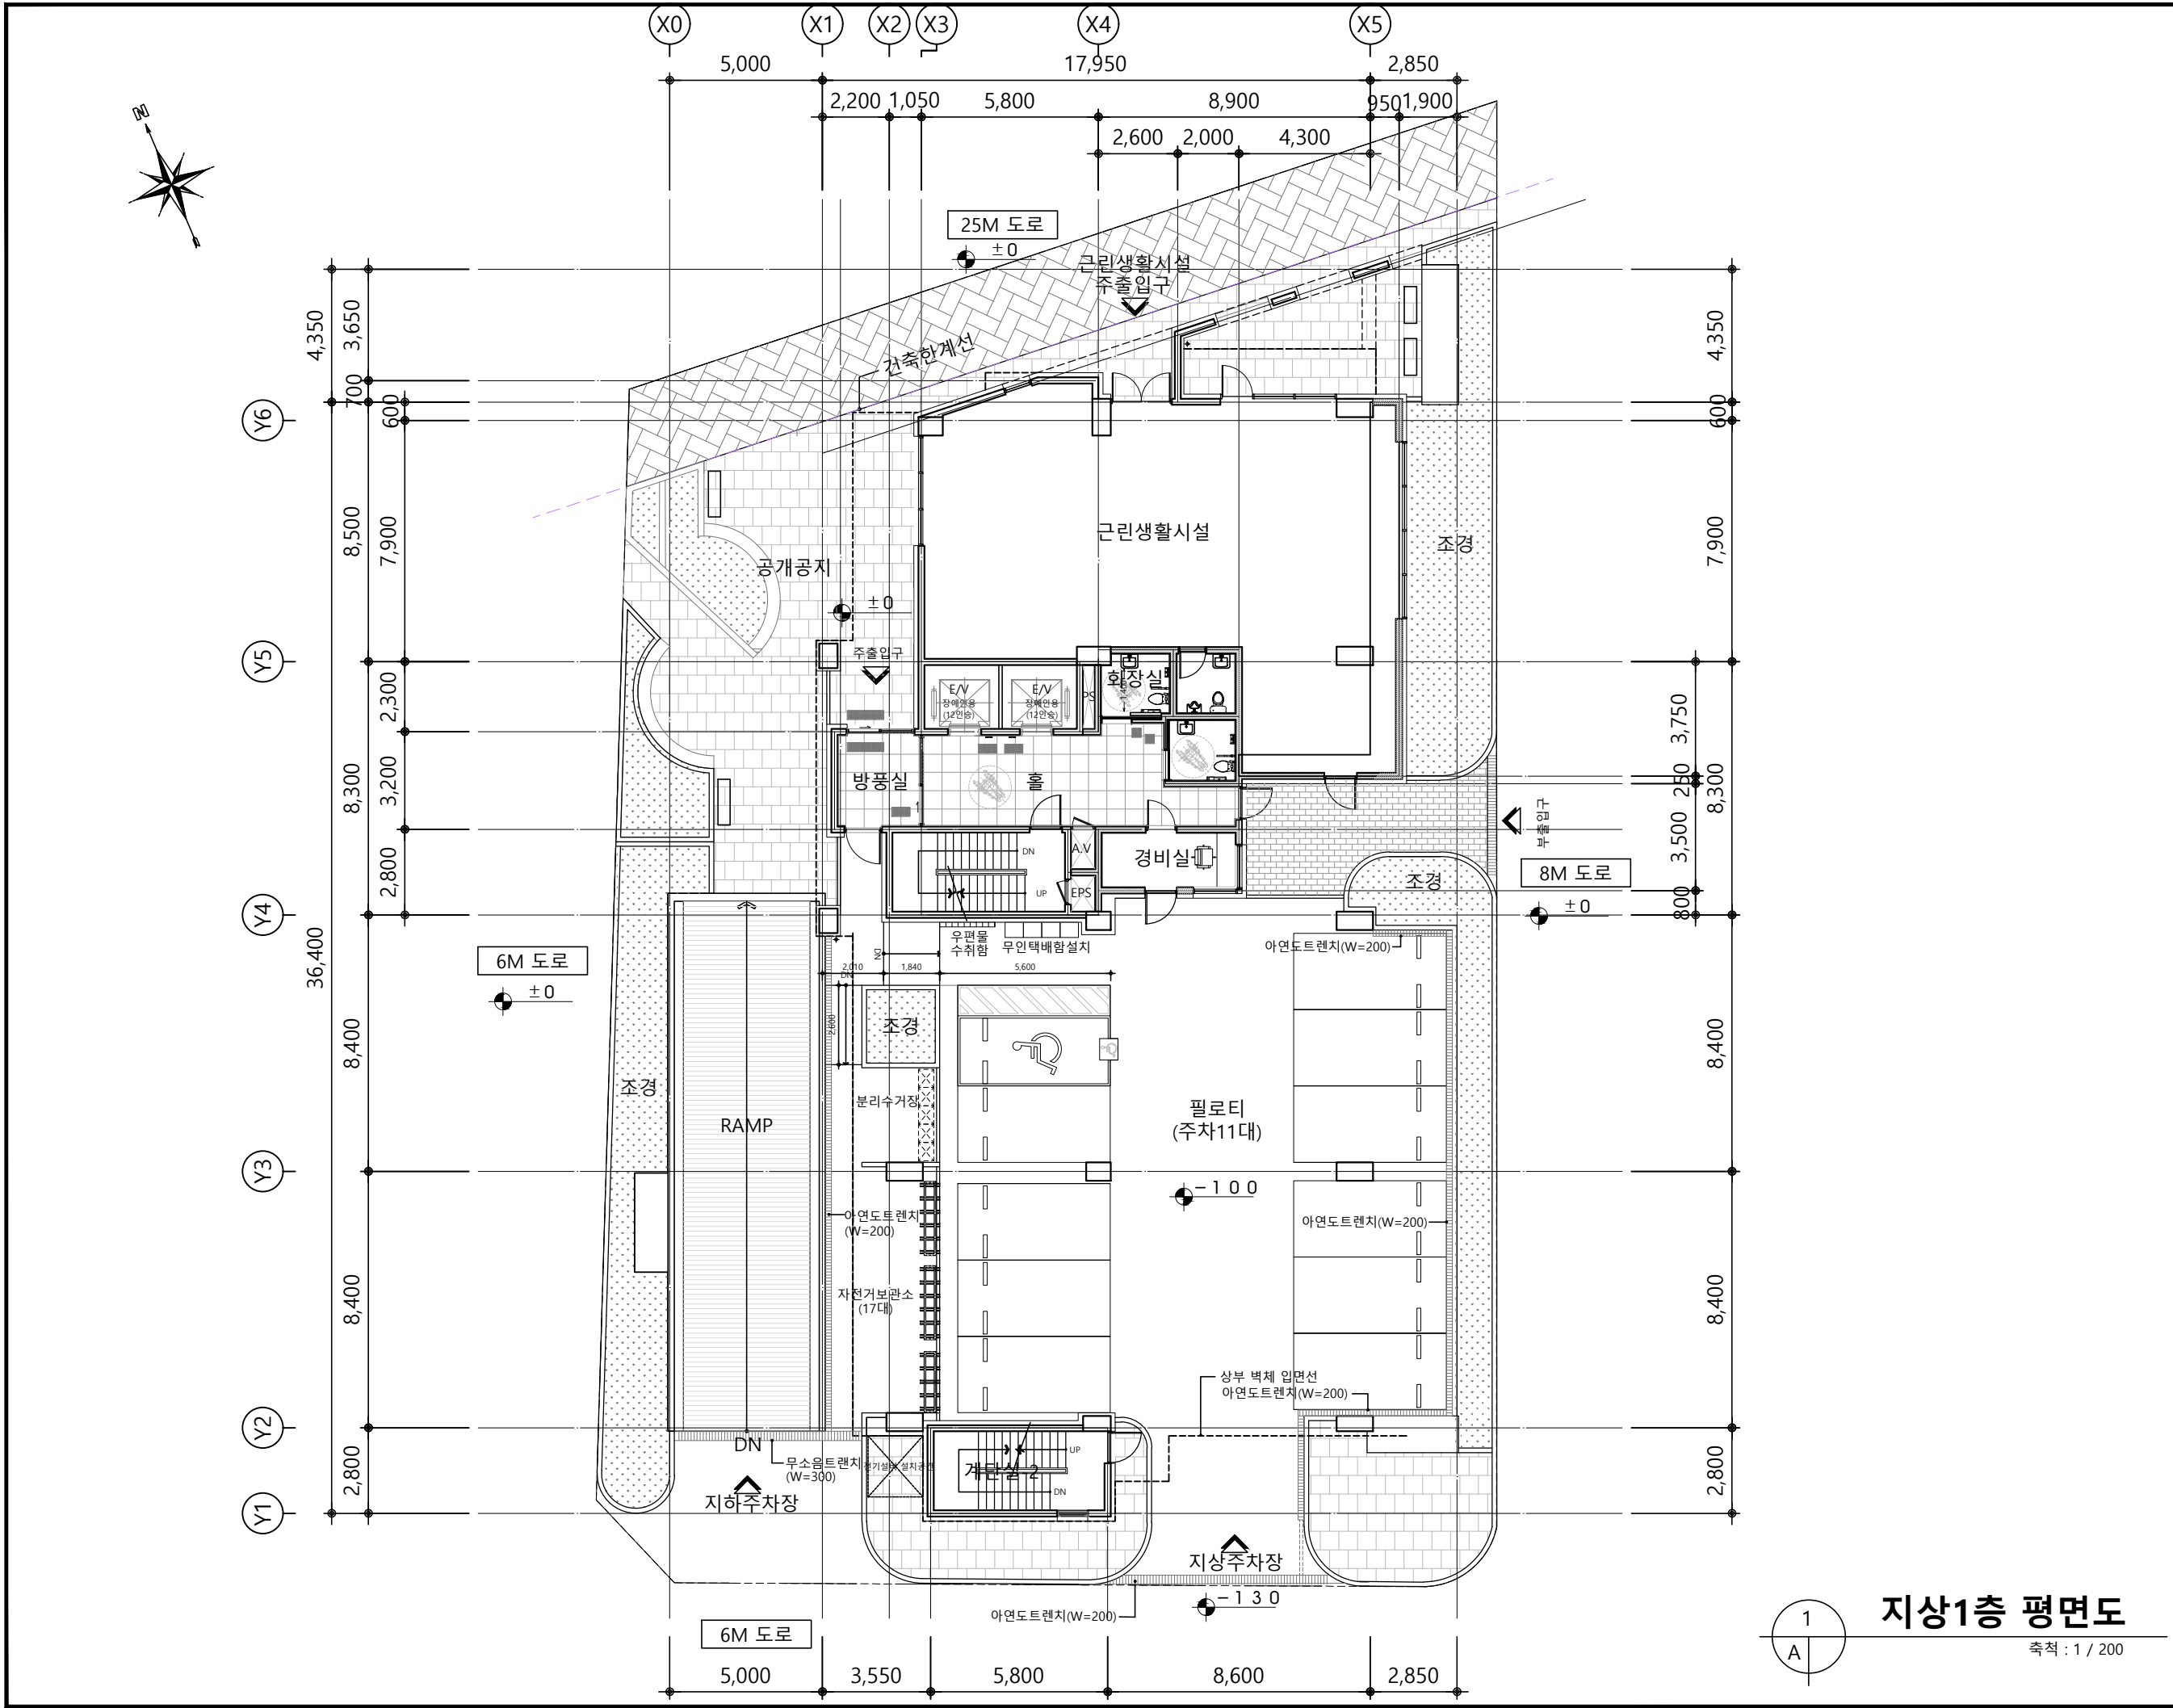


PROJECT TITLE
장안동 591
주거복합시설
신축공사

jk
제이케이건축사사무소(주)
Architects & Planners
TEL : 02-533-9431 FAX : 02-532-9431

NOTE

설 계 변 경 DESCRIPTION OF REVISION				
번 호		내 용		
일 자	설 계	검 토	심 사	승 인
	2024.06			
승인 APPROVED BY				
축척 SCALE	A1	1 / 100		
	A3	1 / 200		
도면명 DRAWING TITLE				
지상1층 평면도				
도면번호 DRAWING NO.				
A - 302				

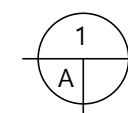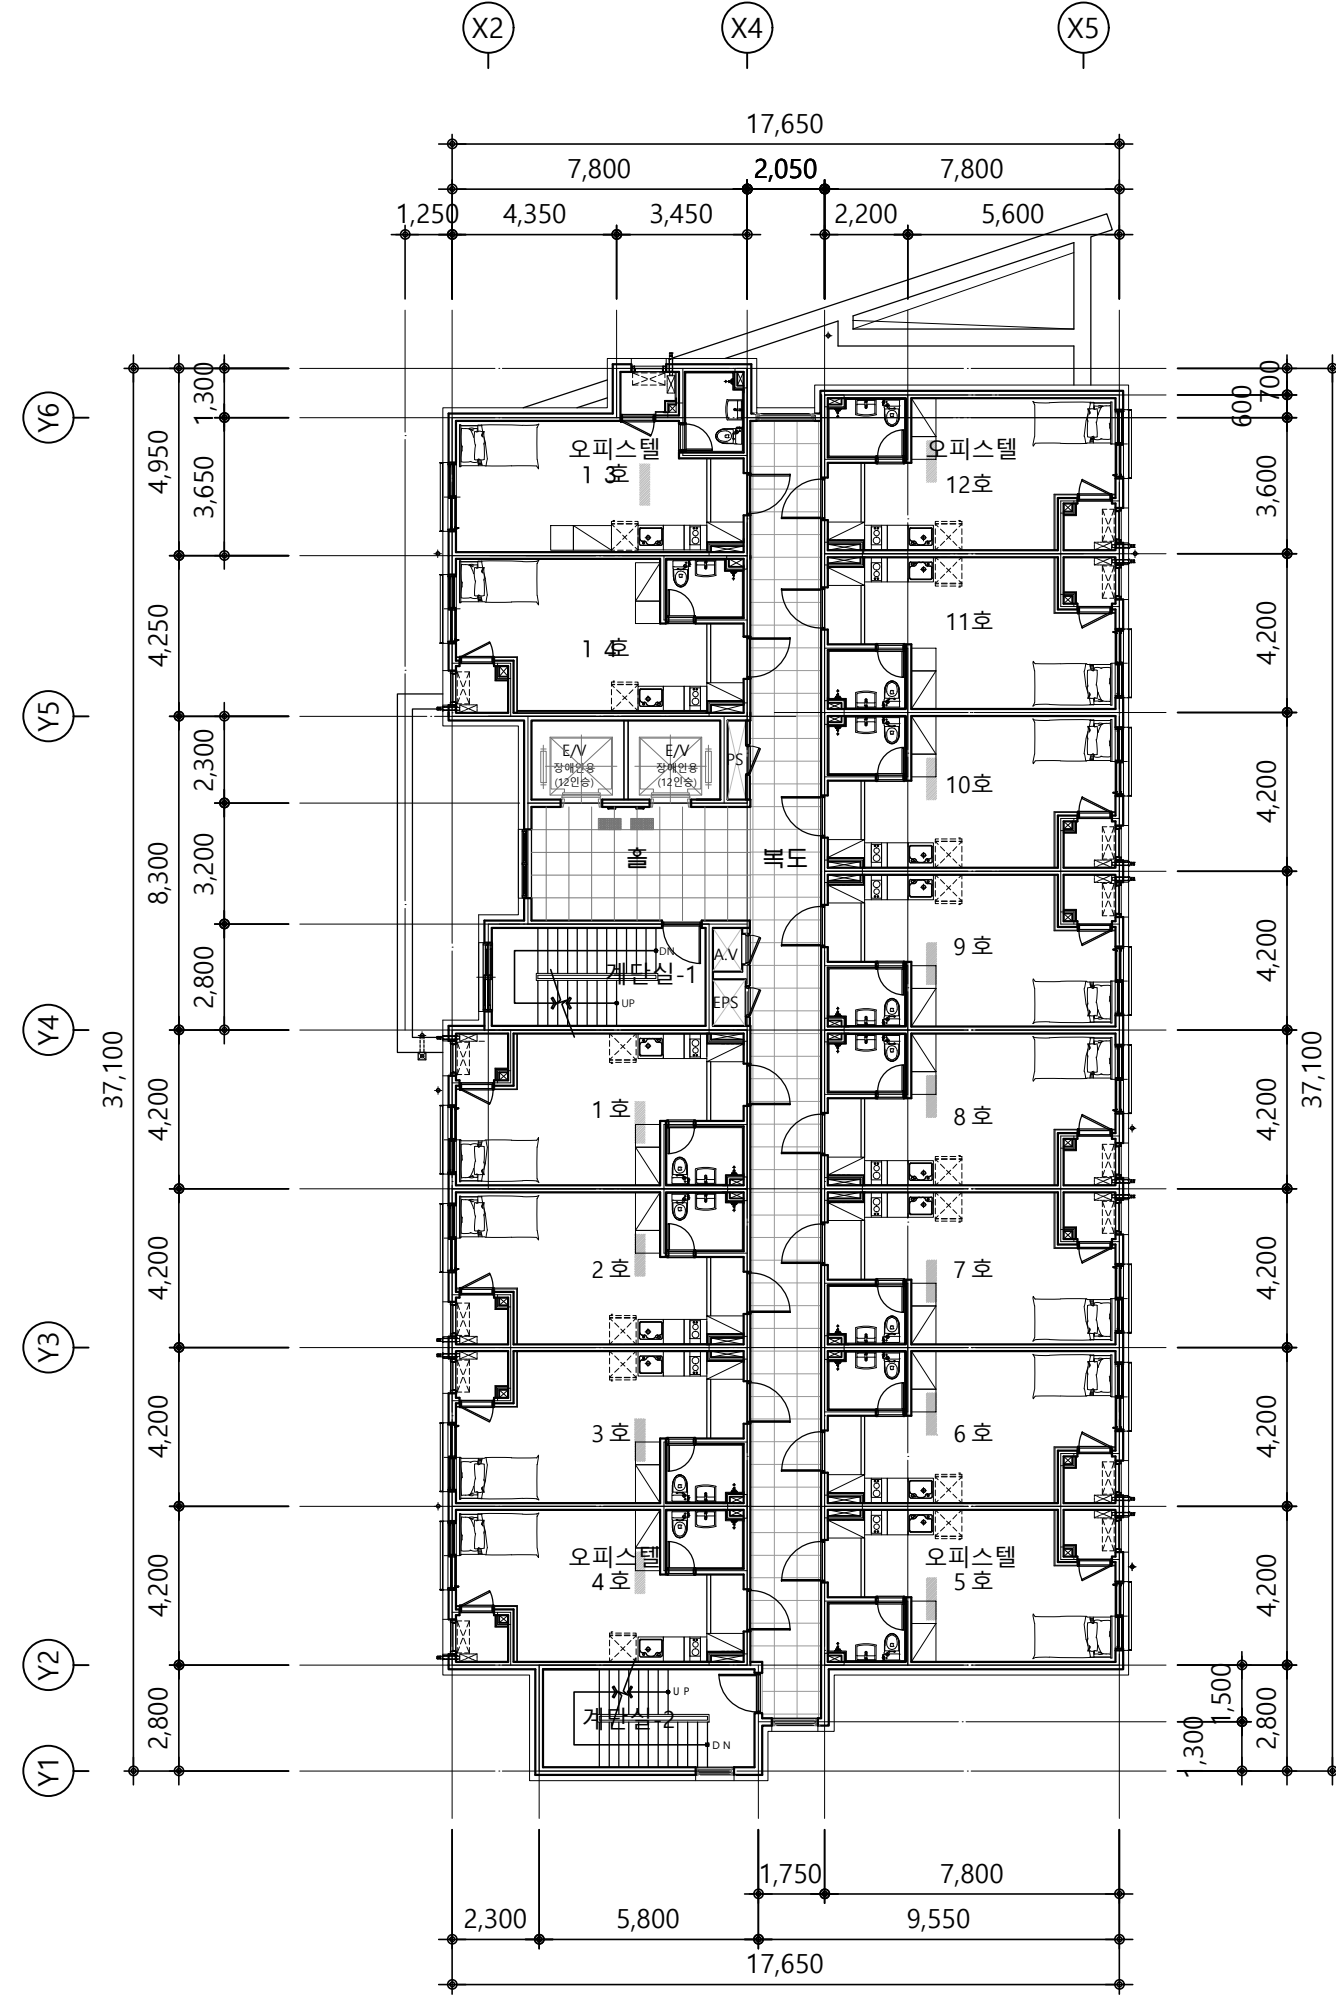

지상2층 평면도
축척 : 1 / 200

PROJECT TITLE
장안동 591
주거복합시설
신축공사


jk
제이케이건축사사무소(주)
Architects & Planners
TEL : 02-533-9431 FAX : 02-532-9431

NOTE

설 계 변 경 DESCRIPTION OF REVISION					
번 호	내 용				
일 자	설 계	검 토	심 사	승 인	
△	2024.06				
승인 APPROVED BY					



축 척 SCALE	A1	1 / 100
	A3	1 / 200

도면명 DRAWING TITLE	
지상2층 평면도	
도면번호 DRAWING NO.	
A - 303	

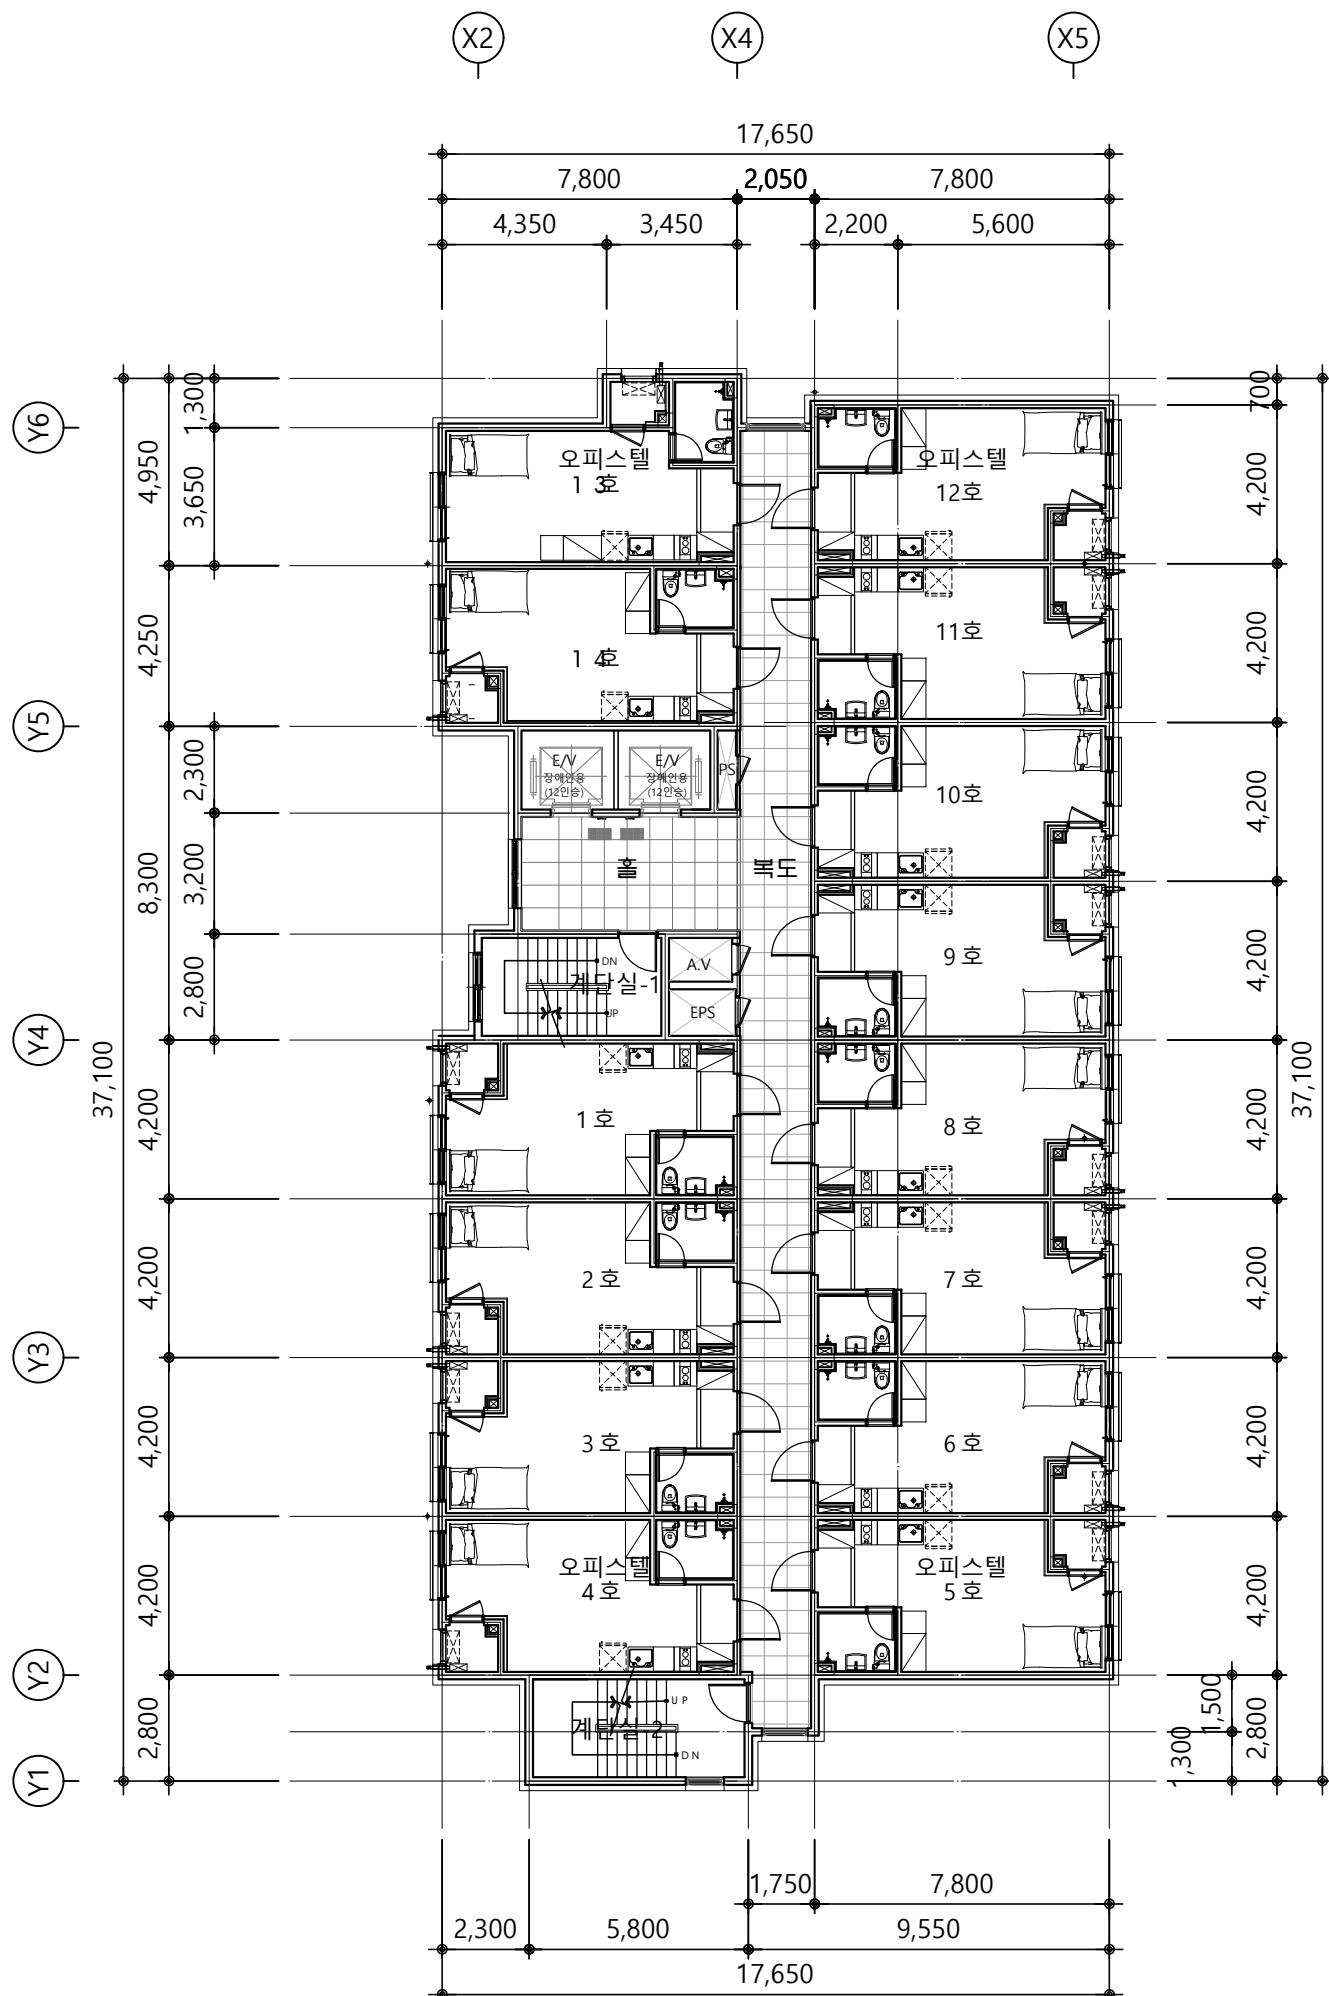

지상3~4층 평면도

A - 304

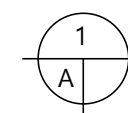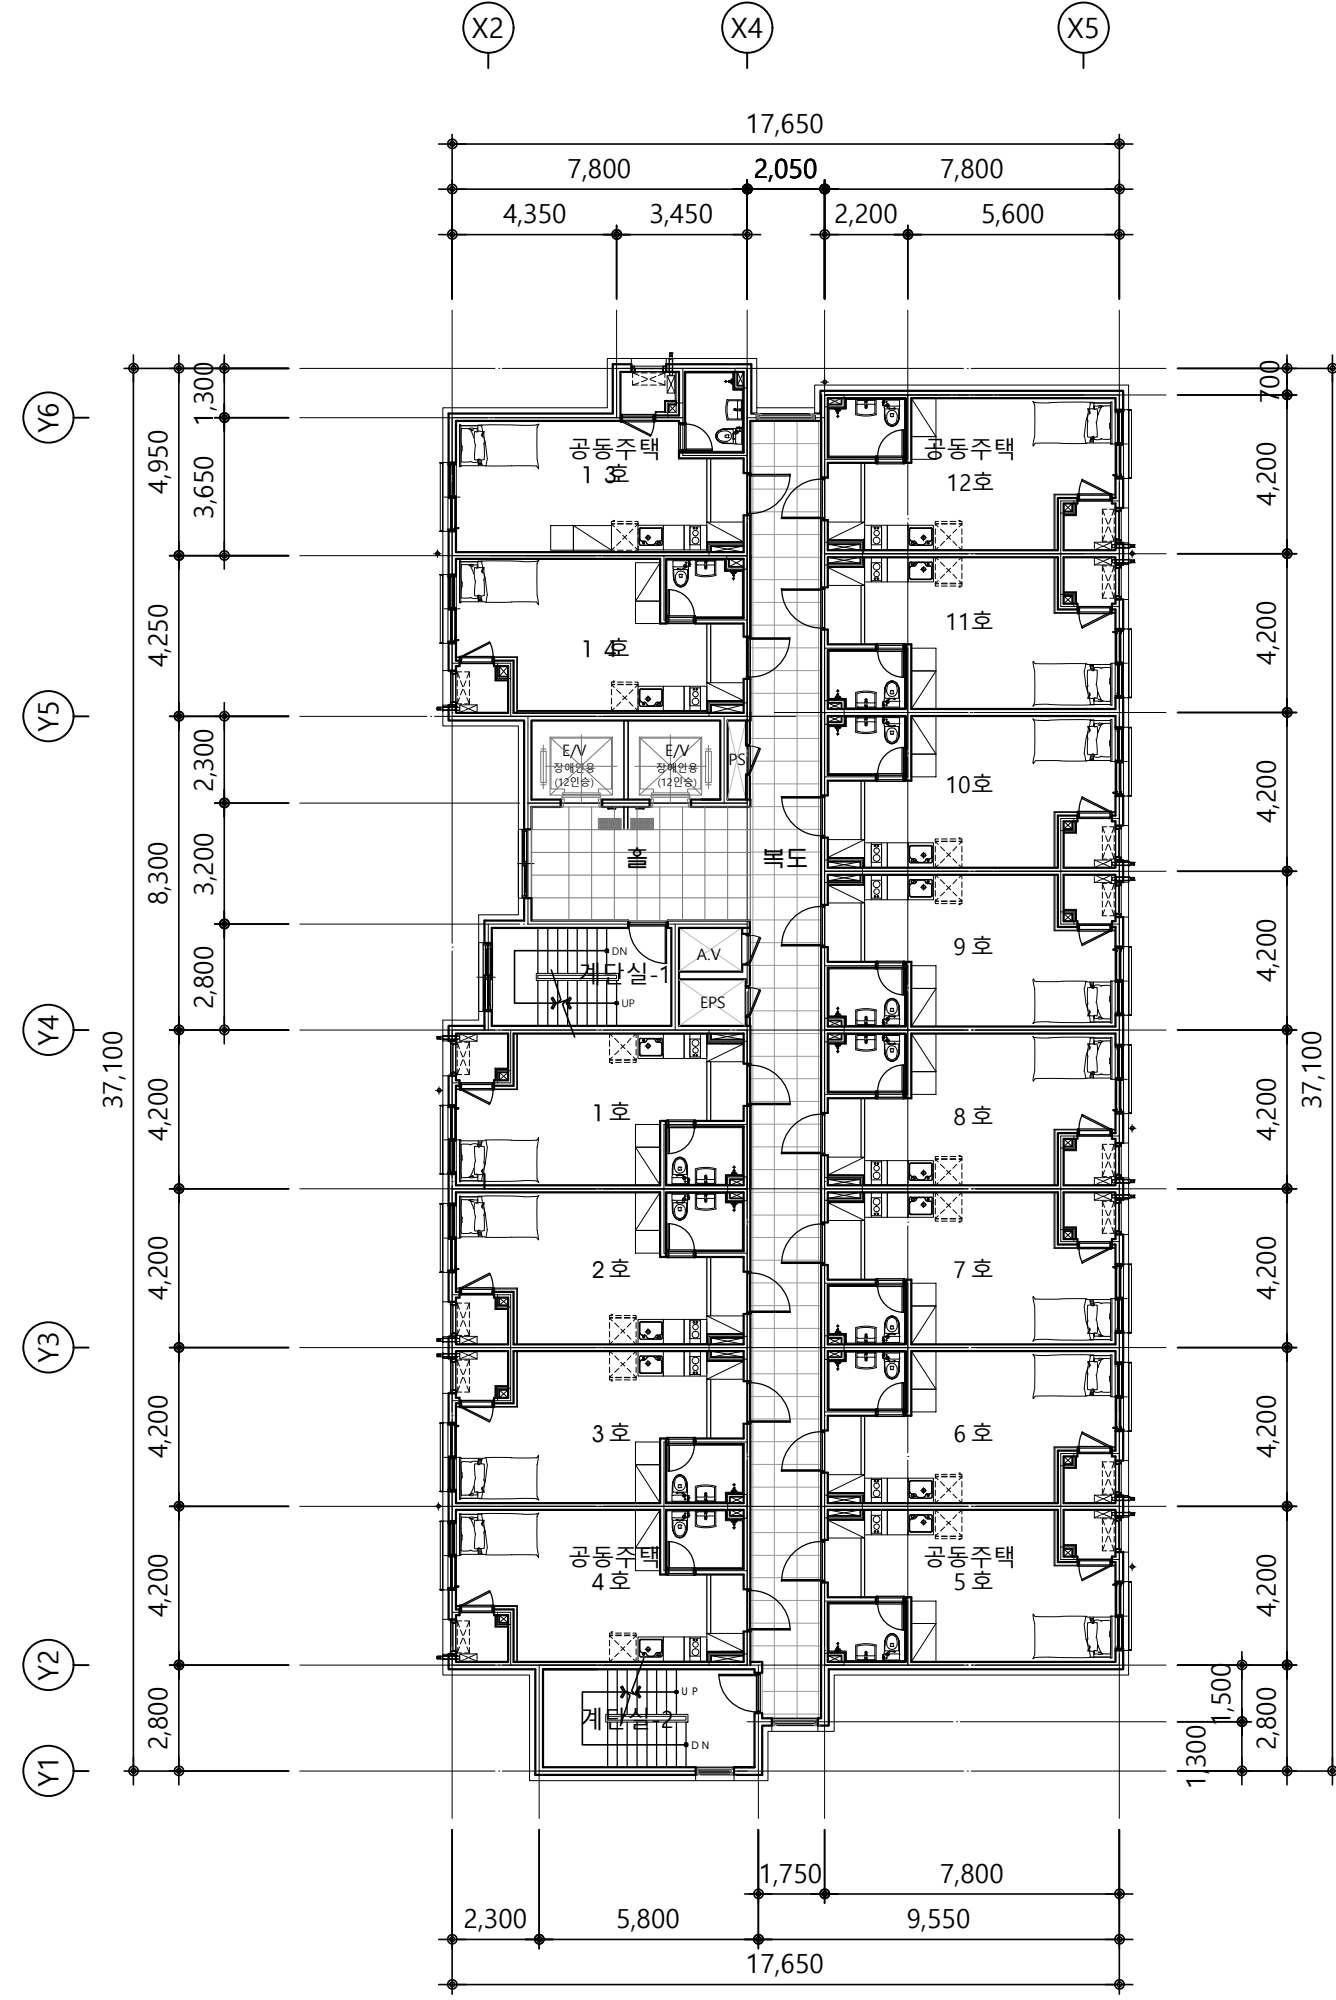

지상5~6층 평면도
축척 : 1 / 200

PROJECT TITLE
장안동 591
주거복합시설
신축공사


제이케이건축사사무소(주)
Architects & Planners
TEL : 02-533-9431 FAX : 02-532-9431



NOTE

설 계 변 경 DESCRIPTION OF REVISION					
번 호	내 용				
일 자	설 계	검 토	심 사	승 인	
	2024.06				
승인 APPROVED BY					

축척 SCALE	A1	1 / 100
	A3	1 / 200

도면명 DRAWING TITLE
지상5~6층 평면도

도면번호 DRAWING NO.
A - 305

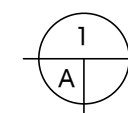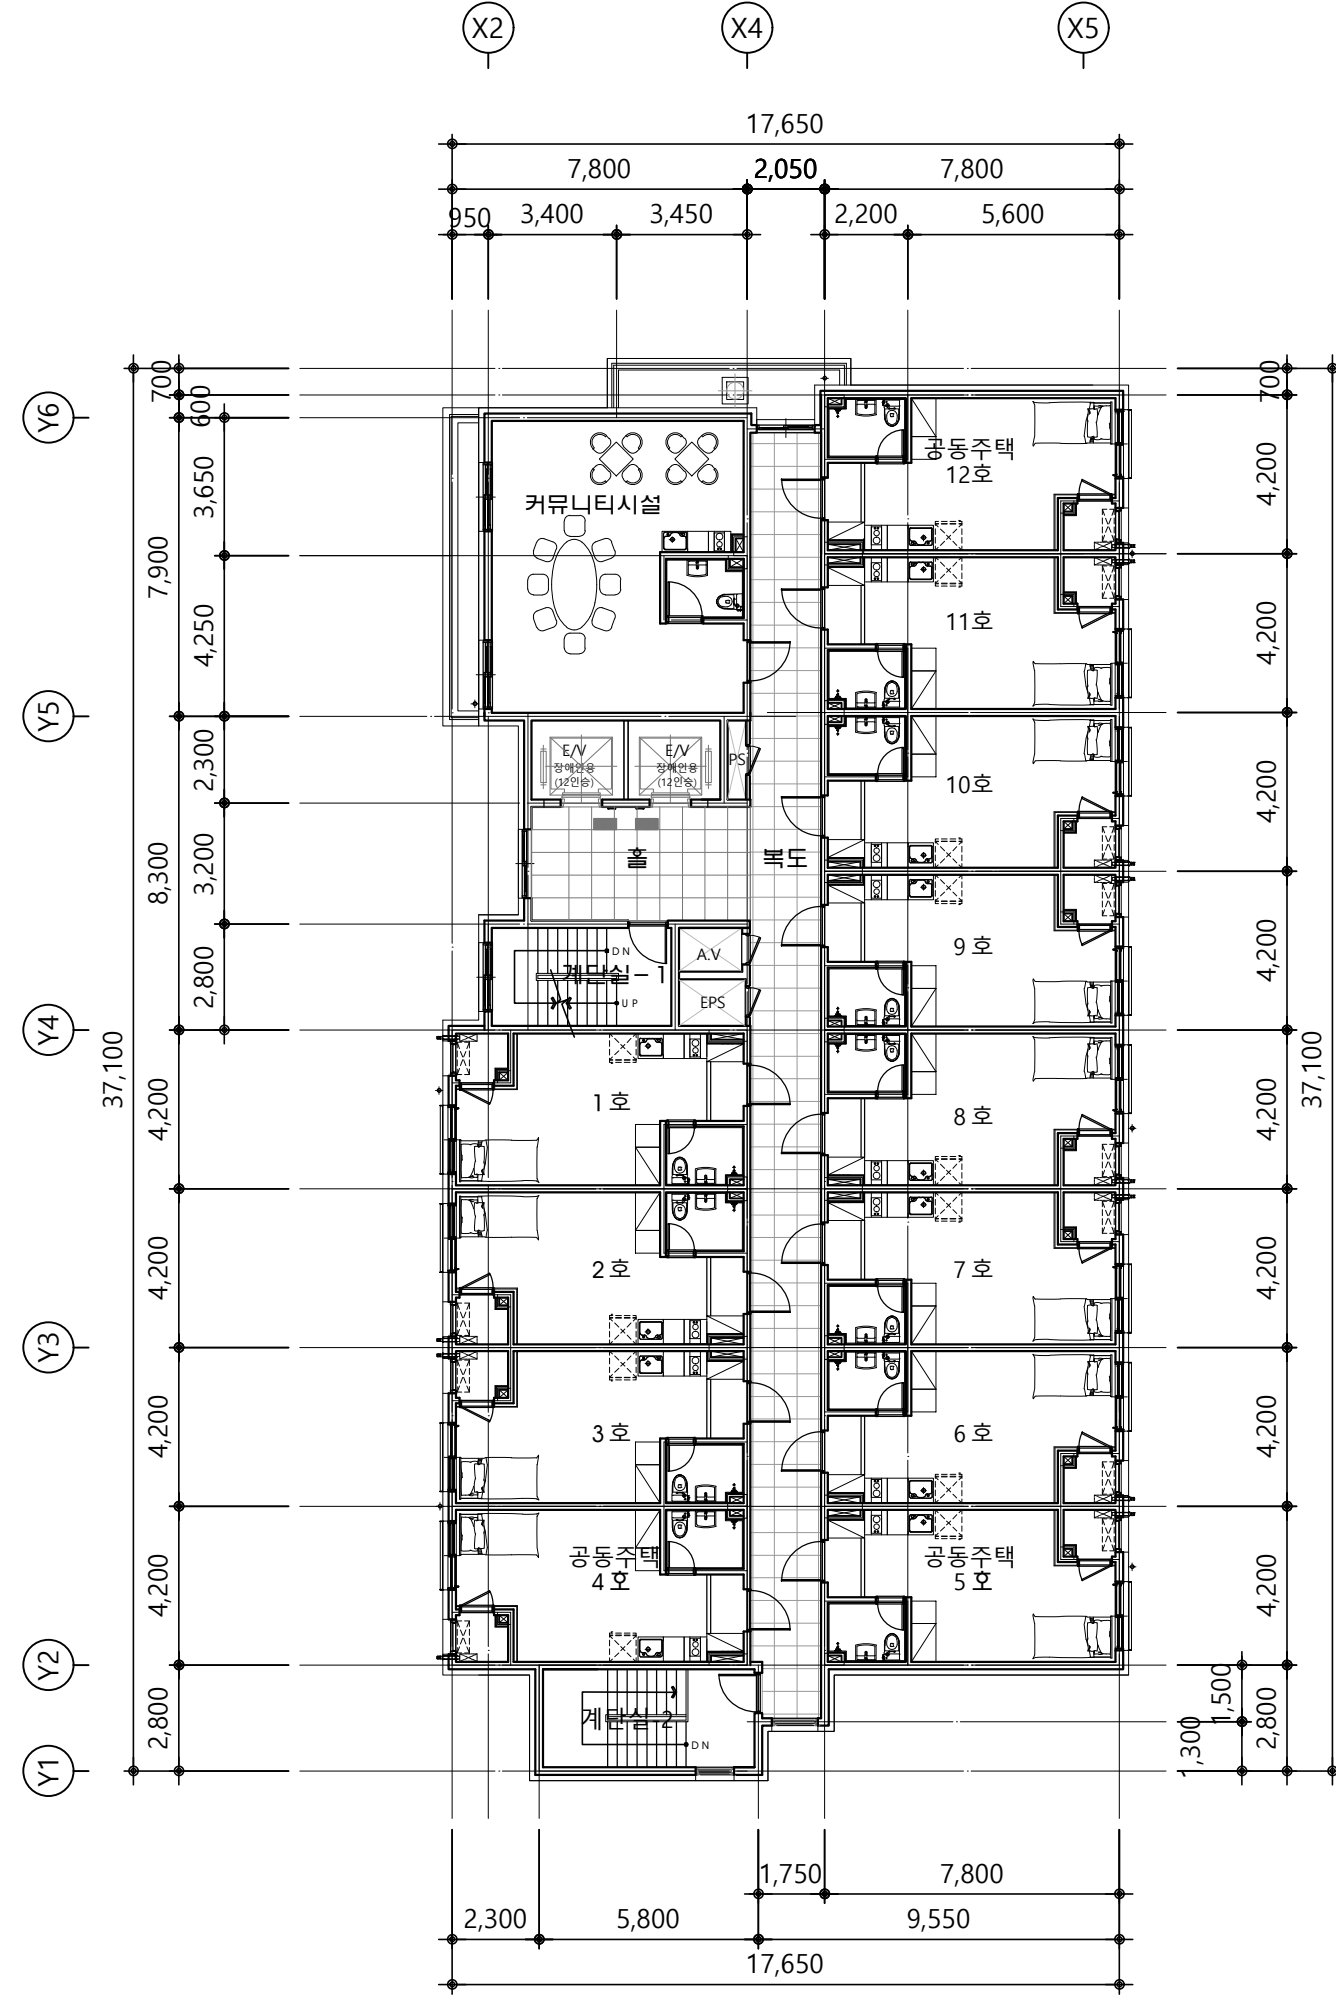

지상7층 평면도

축척 : 1 / 200

PROJECT TITLE

장안동 591
주거복합시설
신축공사

제이케이건축사사무소(주)
Architects & Planners
TEL : 02-533-9431 FAX : 02-532-9431

NOTE

설 계 변 경
DESCRIPTION OF REVISION

번 호	내 용
일 자	설 계 경 토 심 사 승 인
	2024.06
승인 APPROVED BY	


축 척 SCALE	A1	1 / 100
	A3	1 / 200

도면명 DRAWING TITLE

지상7층 평면도

도면번호 DRAWING NO.

A - 306

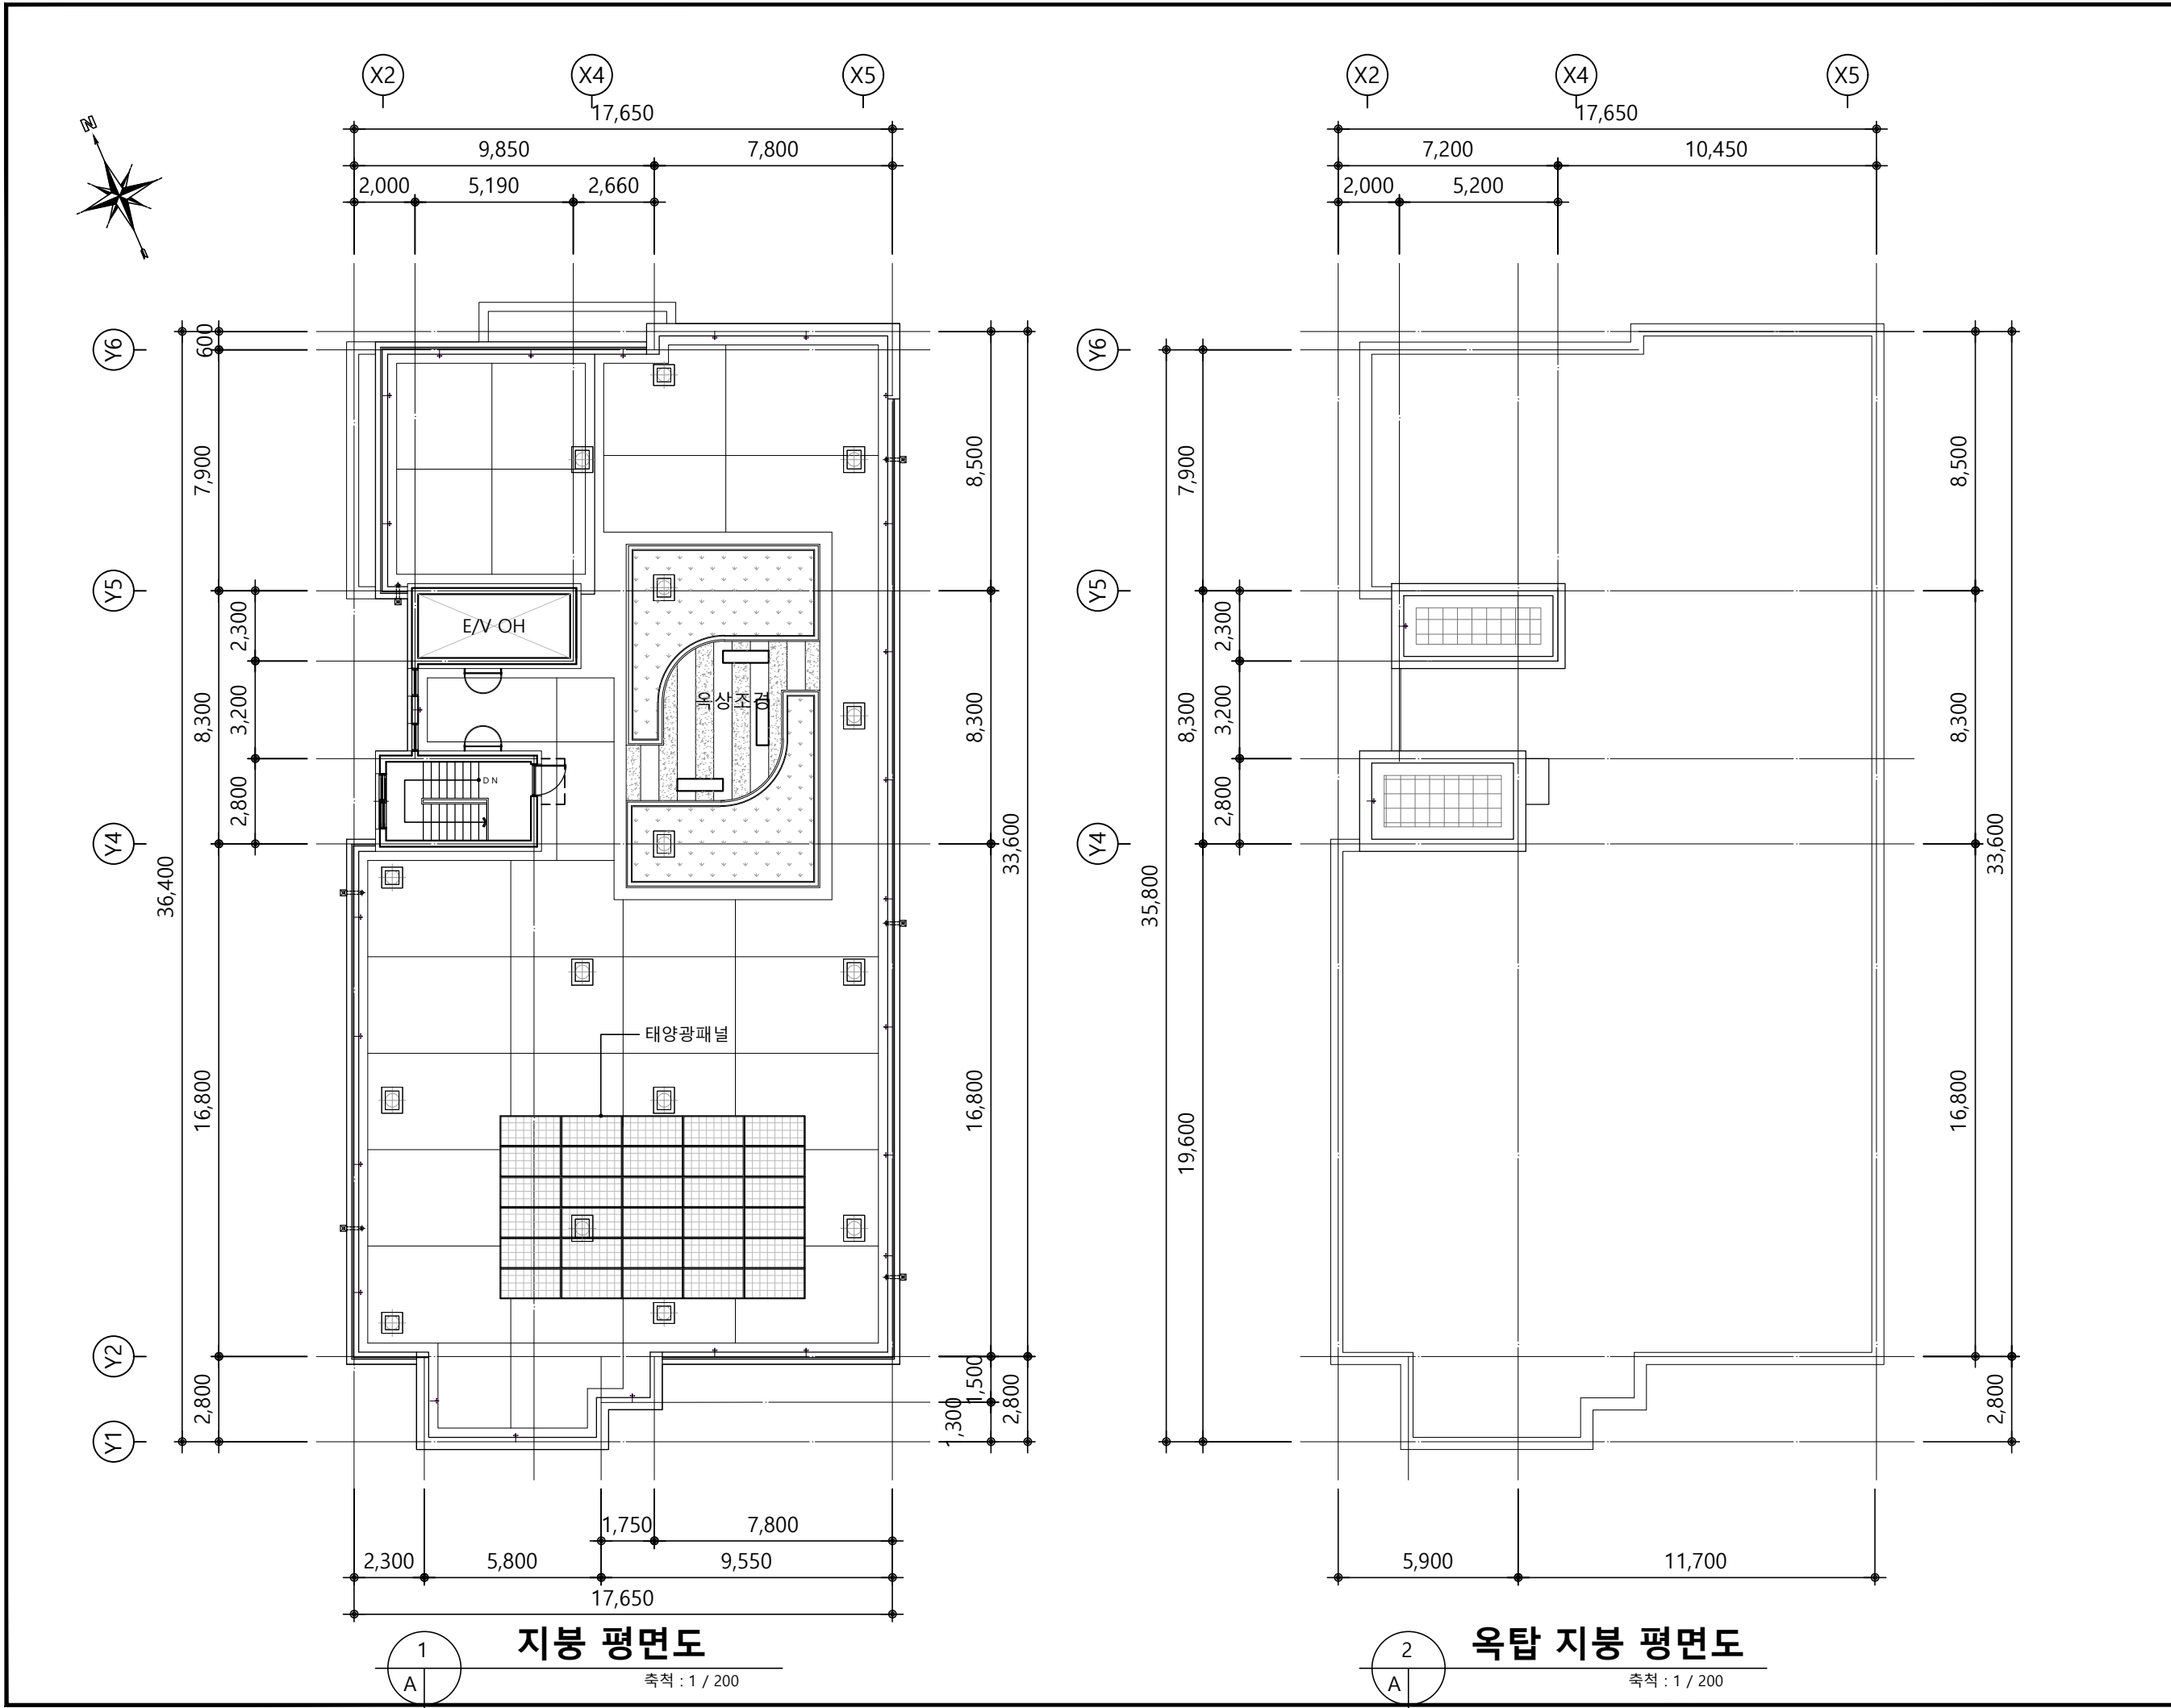


PROJECT TITLE

장안동 591
주거복합시설
신축공사

jk
제이케이건축사사무소(주)
Architects & Planners
TEL : 02-533-9431 FAX : 02-532-9431

NOTE

설 계 변 경 DESCRIPTION OF REVISION					
번 호		내 용			
일 자	설 계	검 토	심 사	승 인	
	2024. 06				
승인 APPROVED BY					
축척 SCALE	A1	1 / 100			
	A3	1 / 200			
도면명 DRAWING TITLE					
지붕,옥탑지붕 평면도					
도면번호 DRAWING NO.					
A - 307					

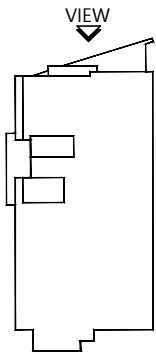

KEY PLAN

옥탑
GL+ 24,800

지붕
GL+ 22,100

지상7층
GL+ 19,100

지상6층
GL+ 16,200

지상5층
GL+ 13,300

지상4층
GL+ 10,400

지상3층
GL+ 7,500

지상2층
GL+ 4,600

지상1층
GL ± 0

22,100

2,700

3,000

2,900

2,900

2,900

2,900

2,900

2,900

4,600

X5

X4

X3

X2

X1

X0

15,750

6,850

2,050

3,300

2,500

1,050

2,200


5,000

포천석 물갈기

소방관 진입창

대리석마감

포천석마감

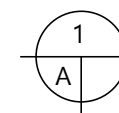

정 면 도

축척 : 1 / 150

PROJECT TITLE

장안동 591
주거복합시설
신축공사



제이케이건축사사무소(주)
Architects & Planners

TEL : 02-533-9431 FAX : 02-532-9431

NOTE

설 계 변 경

DESCRIPTION OF REVISION

번 호	내 용
일 자	설 계 경 토 심 사 승 인
2024.06	
승인 APPROVED BY	


축 척	A1	1 / 75
SCALE	A3	1 / 150

도면명 DRAWING TITLE


정 면 도

도면번호 DRAWING NO.

A - 401

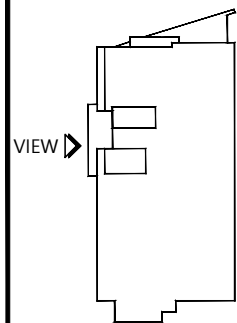

KEY PLAN

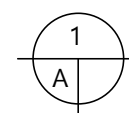

우 측 면 도

축척 : 1 / 150

PROJECT TITLE

장안동 591
주거복합시설
신축공사



제이케이건축사사무소(주)
Architects & Planners

TEL : 02-533-9431 FAX : 02-532-9431

NOTE

설 계 변 경
DESCRIPTION OF REVISION

번 호	내 용
일 자	설 계 경 토 심 사 승 인
2024.06	
승 인	APPROVED BY


축 척	A1	1 / 75
SCALE	A3	1 / 150

도면명 DRAWING TITLE

우 측 면 도


도면번호 DRAWING NO.

A - 402

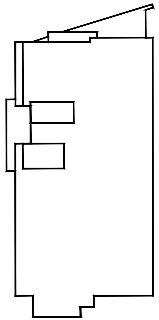

KEY PLAN

VIEW

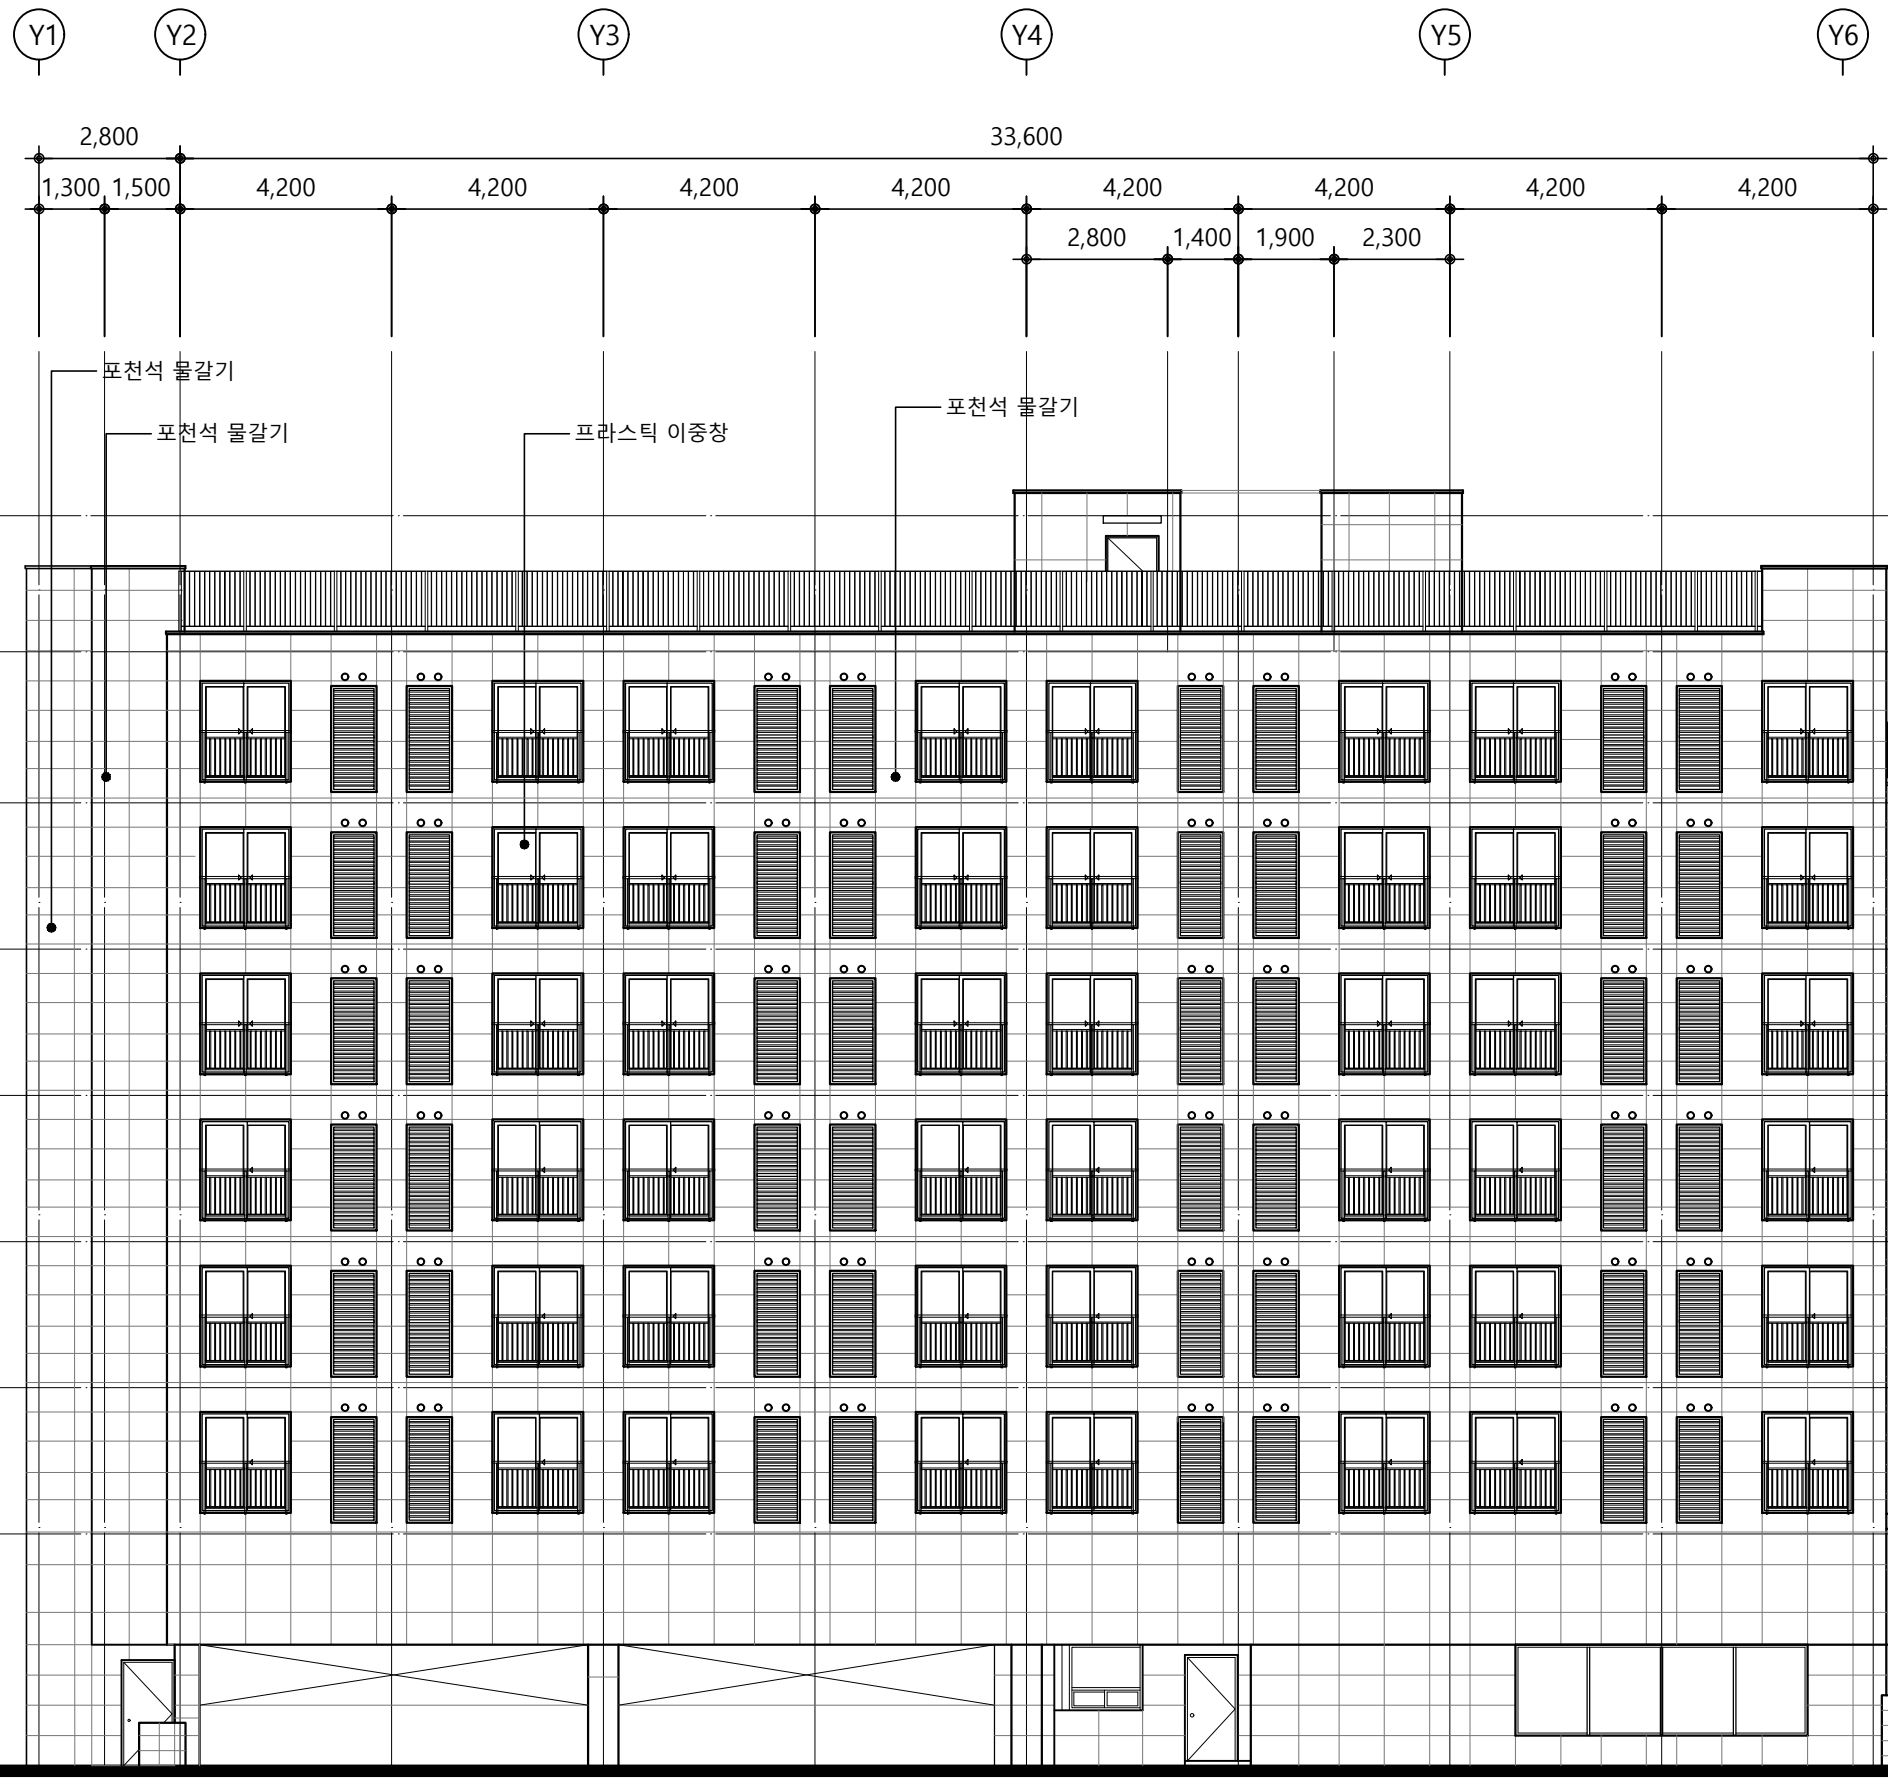

PROJECT TITLE

장안동 591
주거복합시설
신축공사



제이케이건축사사무소(주)
Architects & Planners

TEL : 02-533-9431 FAX : 02-532-9431

NOTE

설 계 변 경
DESCRIPTION OF REVISION

번 호	내 용
일 자	설 계 경 토 심 사 승 인
2024.06	
승 인	APPROVED BY


축 척	A1	1 / 75
SCALE	A3	1 / 150

도면명 DRAWING TITLE

좌 측 면 도


도면번호 DRAWING NO.

A - 403

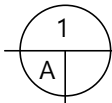

좌 측 면 도

축척 : 1 / 150

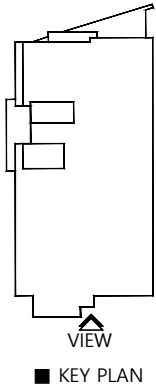

옥탑
GL+ 24,800

지붕
GL+ 22,100

지상7층
GL+ 19,100

지상6층
GL+ 16,200

지상5층
GL+ 13,300

지상4층
GL+ 10,400

지상3층
GL+ 7,500

지상2층
GL+ 4,600

지상1층
GL ± 0

22,100

2,700

3,000

2,900

2,900



2,900

2,900

2,900

2,900

4,600

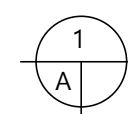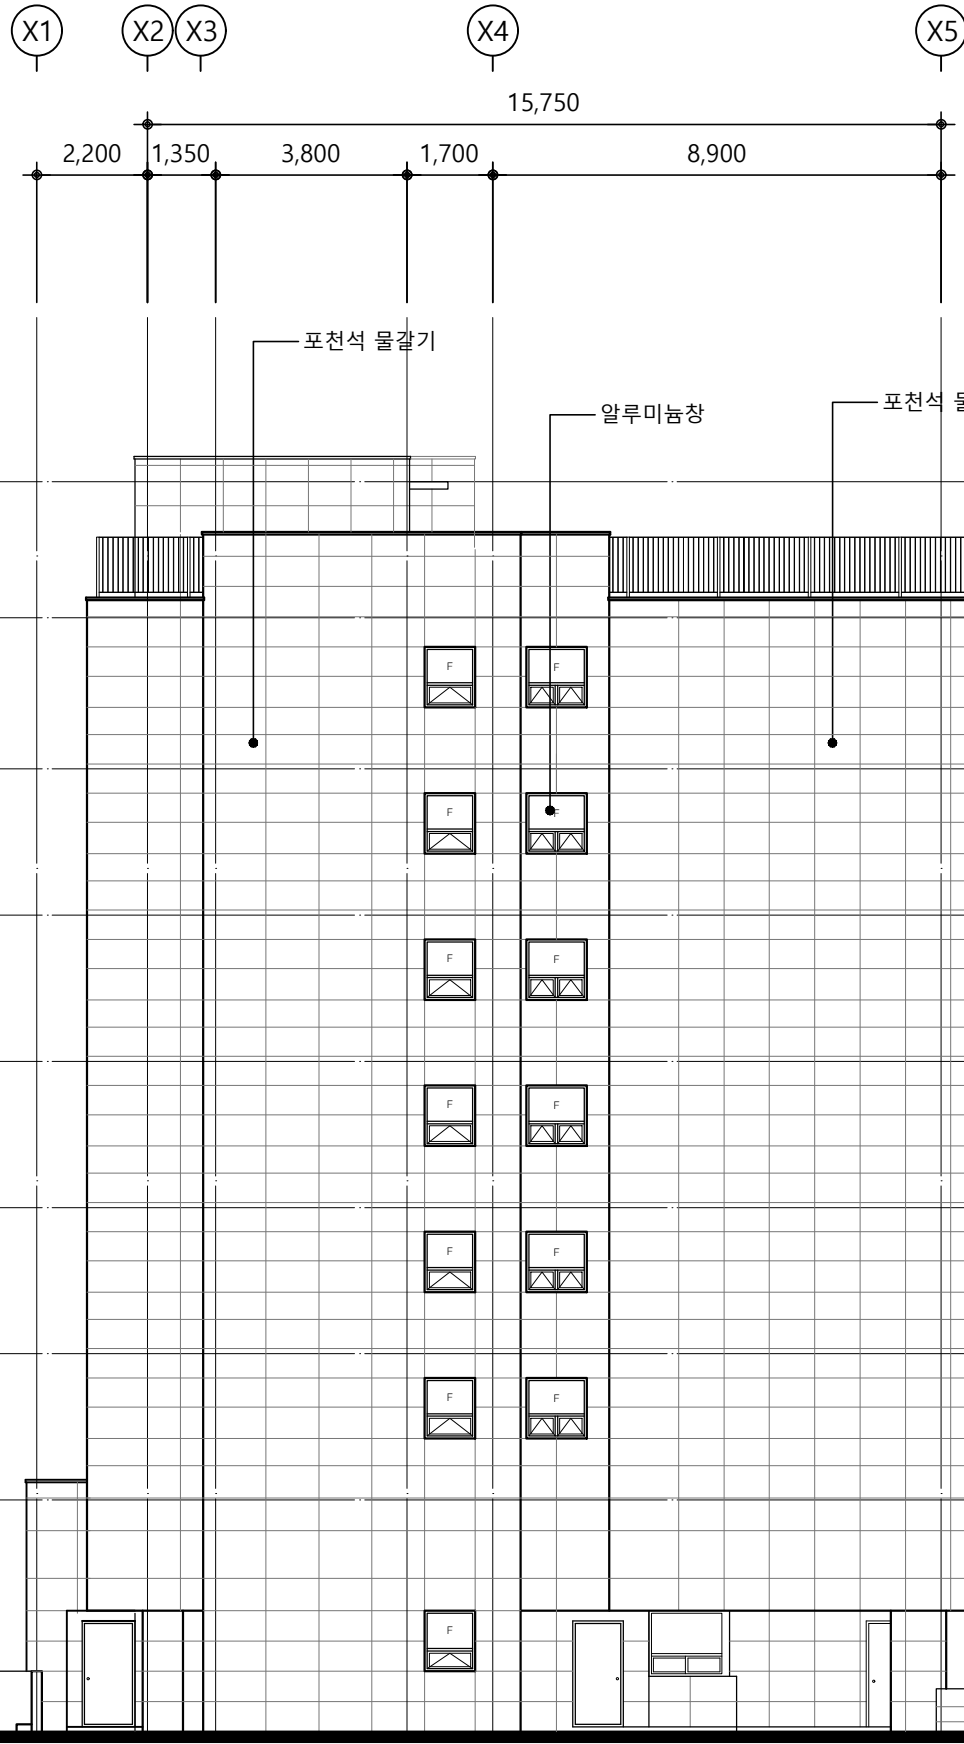

배 면 도
축척 : 1 / 150

PROJECT TITLE
장안동 591
주거복합시설
신축공사

jk
제이케이건축사사무소(주)
Architects & Planners
TEL : 02-533-9431 FAX : 02-532-9431

NOTE

설 계 변 경 DESCRIPTION OF REVISION				
번 호	내 용			
일 자	설 계	검 토	심 사	승 인
	2024.06			
승인 APPROVED BY				
축 척 SCALE	A1	1 / 75		
	A3	1 / 150		
도면명 DRAWING TITLE				
배 면 도				
도면번호 DRAWING NO.				
A - 404				