

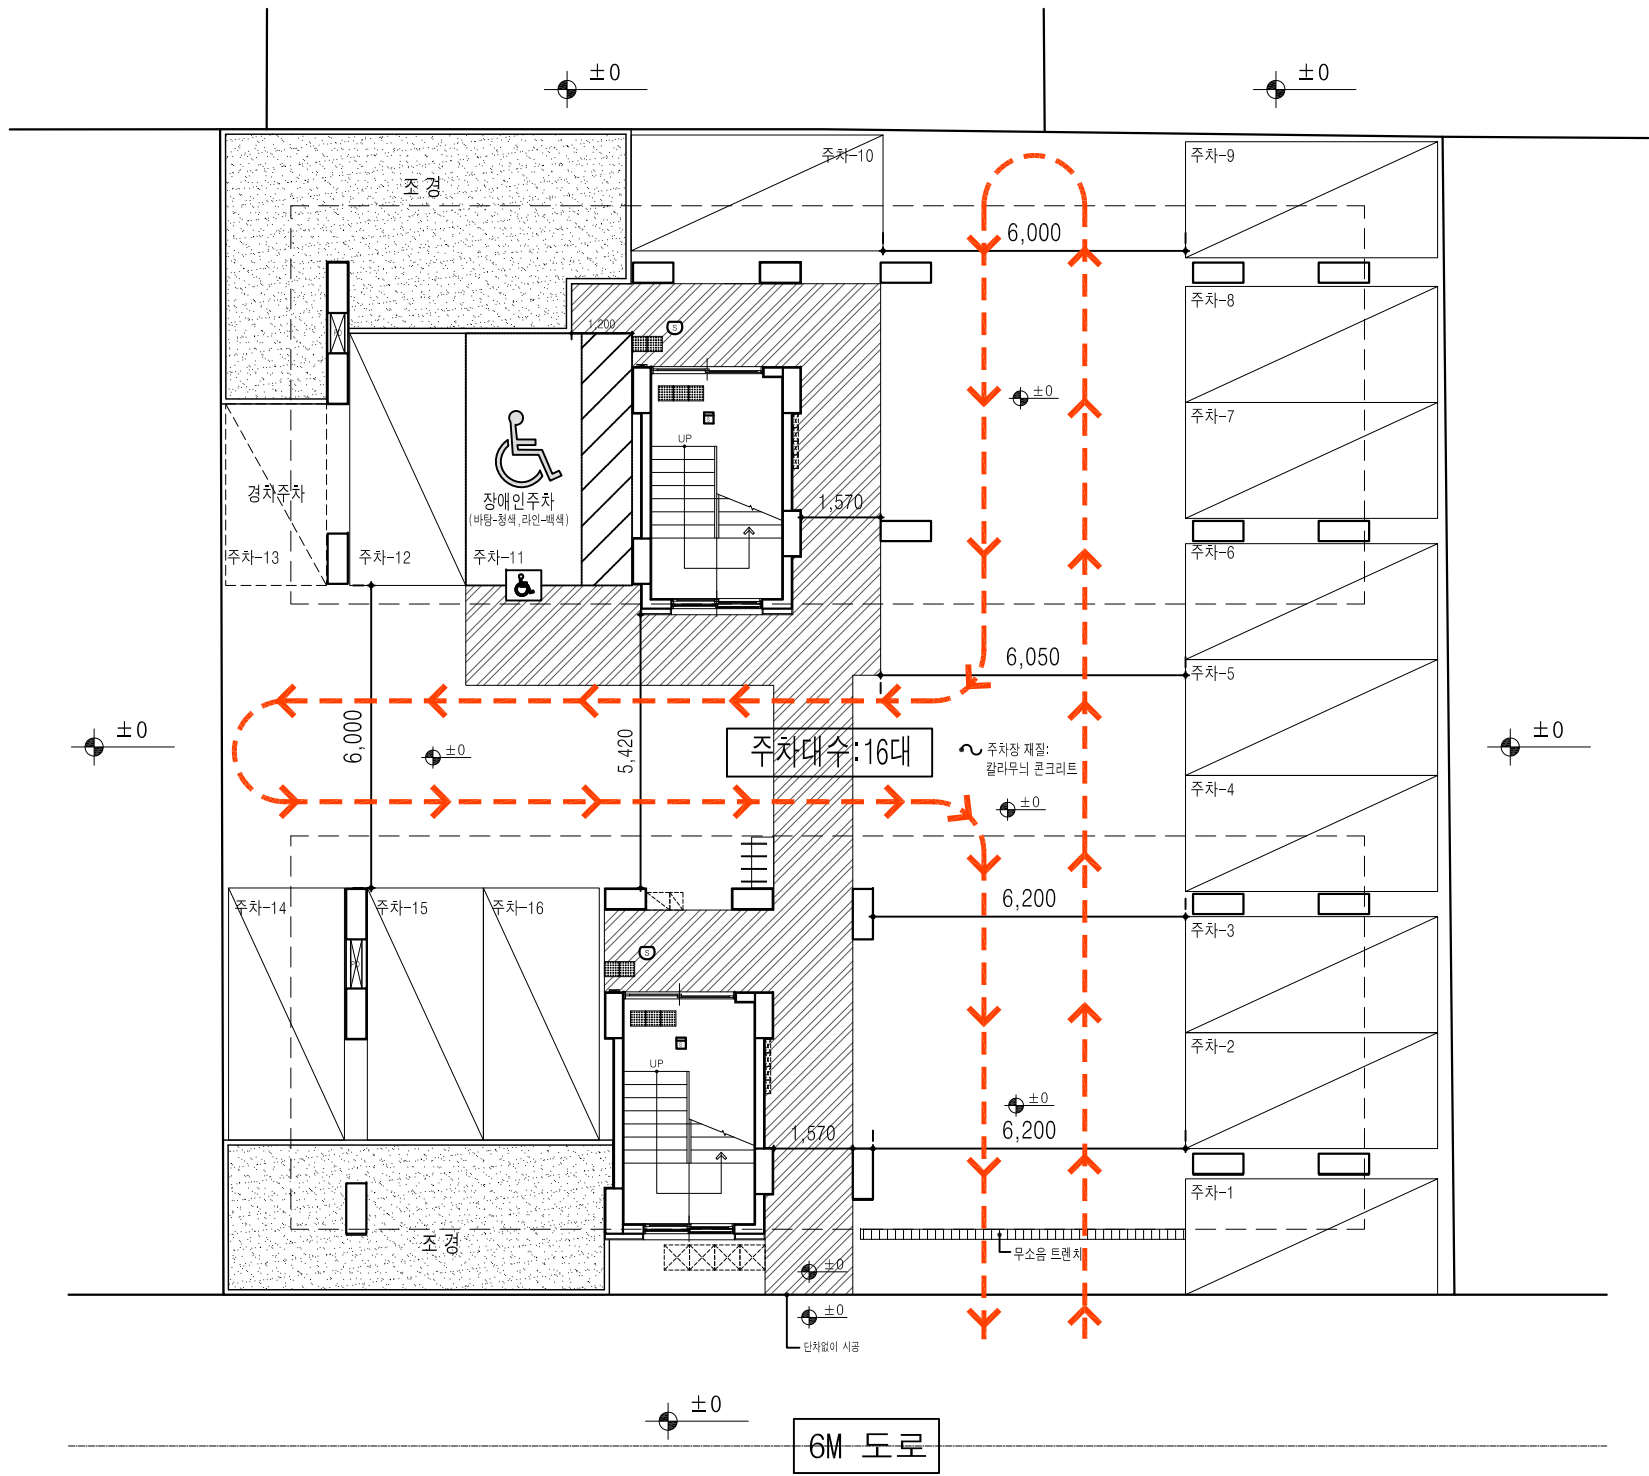



주차 계획도

|      |    |                                          |
|------|----|------------------------------------------|
| 주차대수 | 법정 | 30m2이상 60M2이하 세대당 0.8: 20세대 X 0.8 대= 16대 |
|      | 계획 | 16대 설치<br>(장애인주차:1대, 경차주차:1대, 일반주차:14대)  |

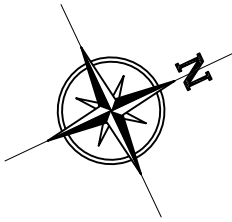

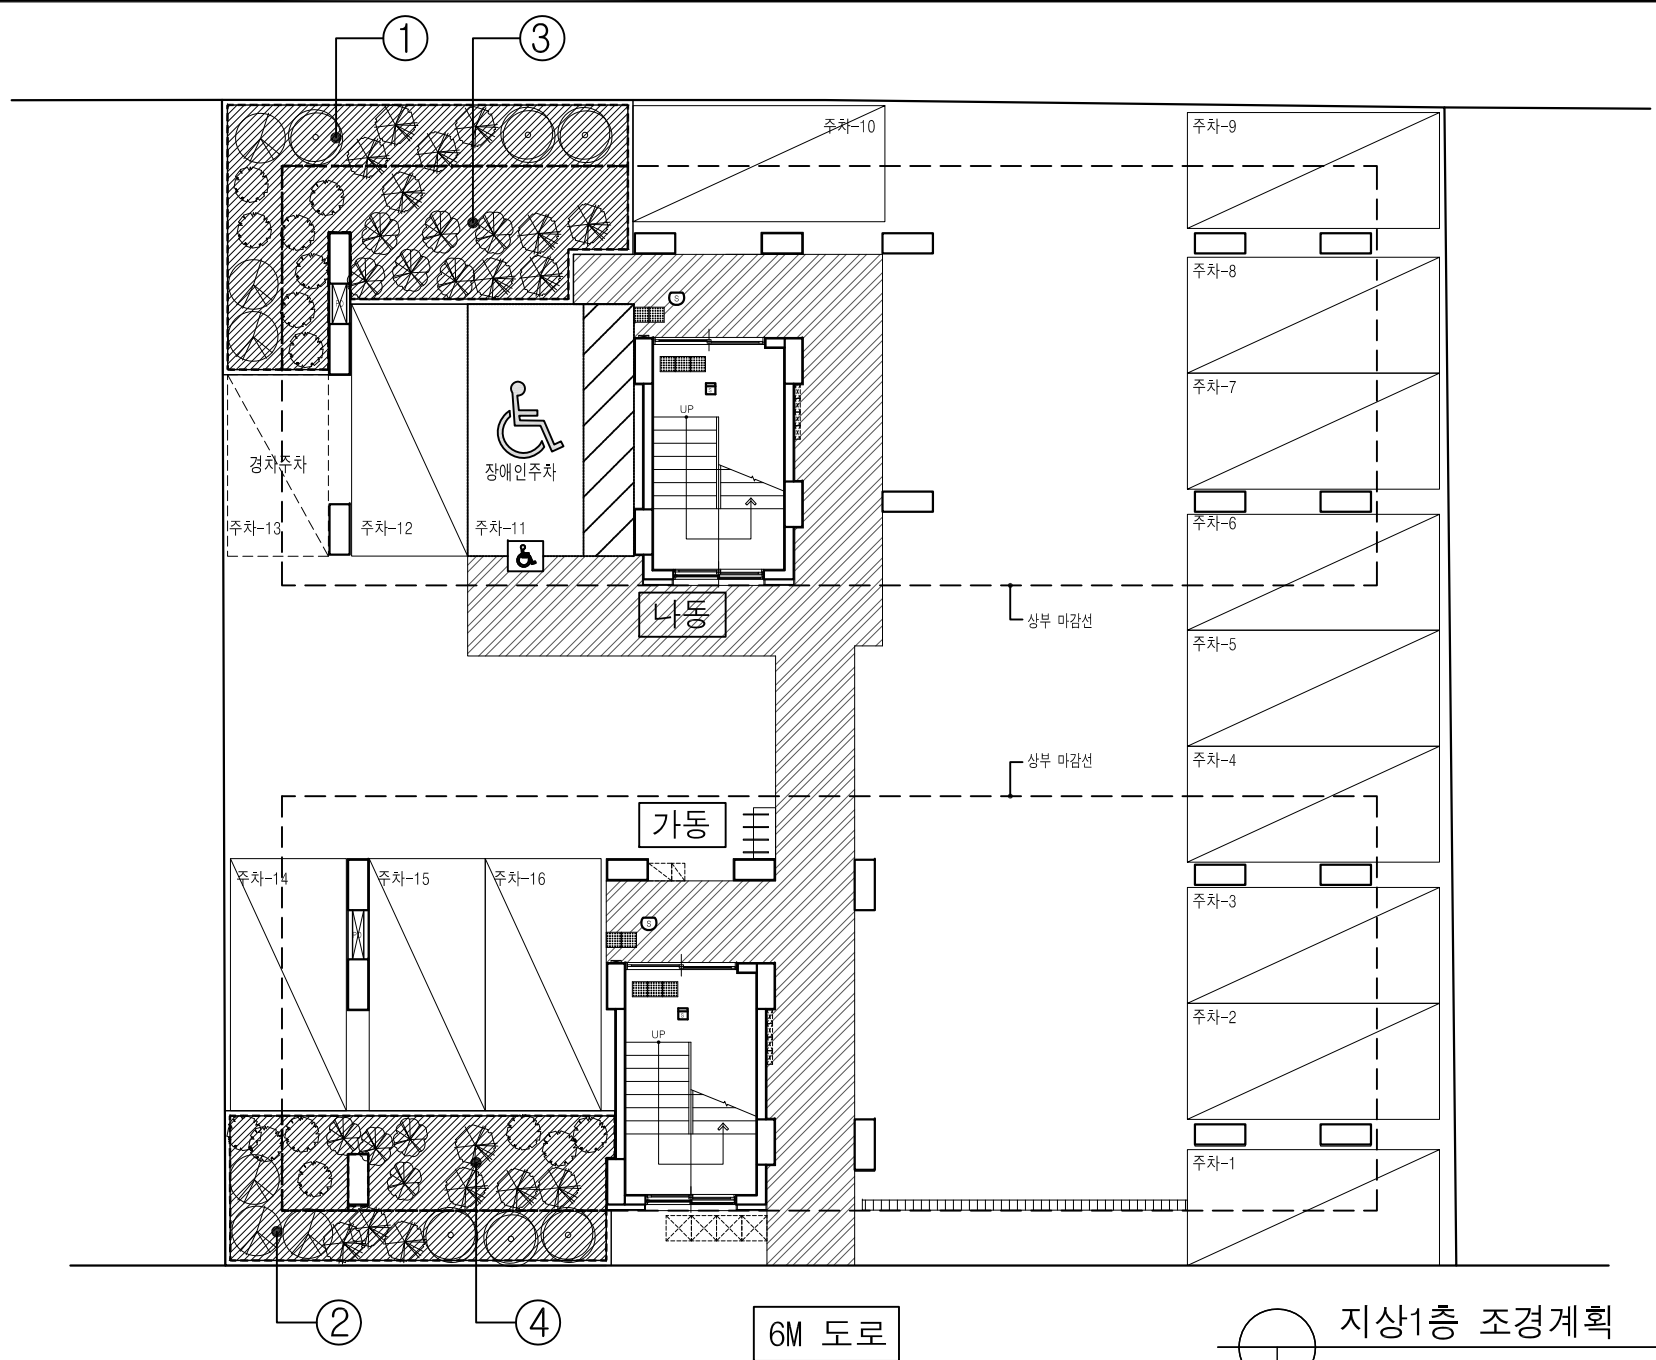

지상1층 조경계획

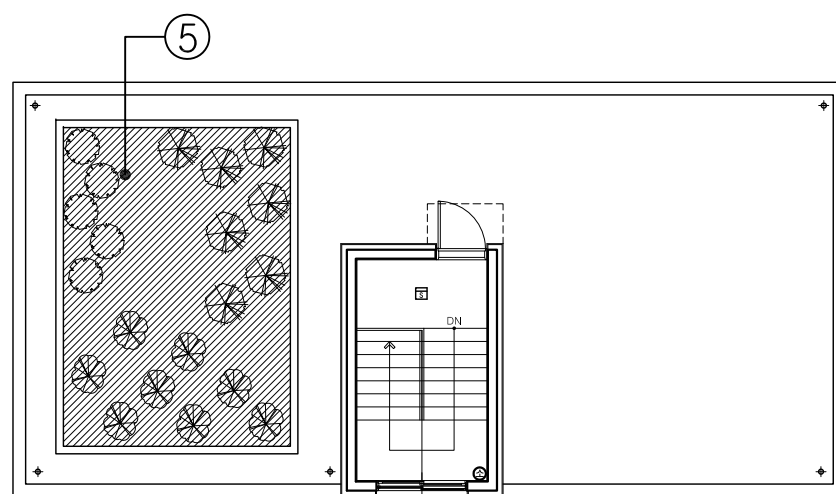


가동-옥상 조경계획

## 조경 구적표

| 산출근거                |    |        |                                  |
|---------------------|----|--------|----------------------------------|
| 지상<br>조경<br>(옥 외)   | ①  | 캐드면적 : | 13.97 m2                         |
|                     | ②  | 캐드면적 : | 9.32 m2                          |
|                     | 소계 |        | 23.29 m2                         |
| 지상<br>조경<br>(피로티하부) | ③  | 캐드면적 : | 17.65 m2                         |
|                     | ④  | 캐드면적 : | 11.82 m2                         |
|                     | 소계 |        | 29.47 / 2 = 14.74 m2             |
| 옥상<br>조경            | ⑤  | 캐드면적 : | 28.44 m2                         |
|                     |    |        |                                  |
|                     | 소계 |        | 28.44 m2 × 2/3 = 18.96 m2        |
| 합 계                 |    |        | 23.29 + 14.74 + 18.96 = 56.99 m2 |


## 조경 계획표

|                                                                                       |                       |                                                                                       |                      |
|---------------------------------------------------------------------------------------|-----------------------|---------------------------------------------------------------------------------------|----------------------|
| 법 정                                                                                   | 562.40 x 10% = 56.24㎡ |                                                                                       |                      |
| 설 계                                                                                   | 56.99㎡ ( 10.13 % )    |                                                                                       |                      |
| 식재 산출                                                                                 |                       |                                                                                       |                      |
| 법 정                                                                                   | 교 목                   | 56.24 X 0.2 = 11.25                                                                   |                      |
|                                                                                       | 관 목                   | 56.24 X 1.0 = 56.24                                                                   |                      |
| 식재구분 ( W X H )                                                                        |                       |                                                                                       |                      |
| 교 목                                                                                   | 12본                   | 관 목                                                                                   | 62본                  |
|  | 소나무(H2.5xR8xW1.0)-6본  |  | 희양목(H0.4xW0.3)-19본   |
|  | 청단풍(H3.0xR10)-6본      |  | 철쭉(H0.4xW0.3)-24본    |
|                                                                                       |                       |  | 누운향나무(H0.4xW0.4)-19본 |

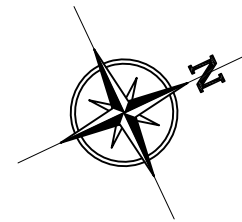

나동

가동

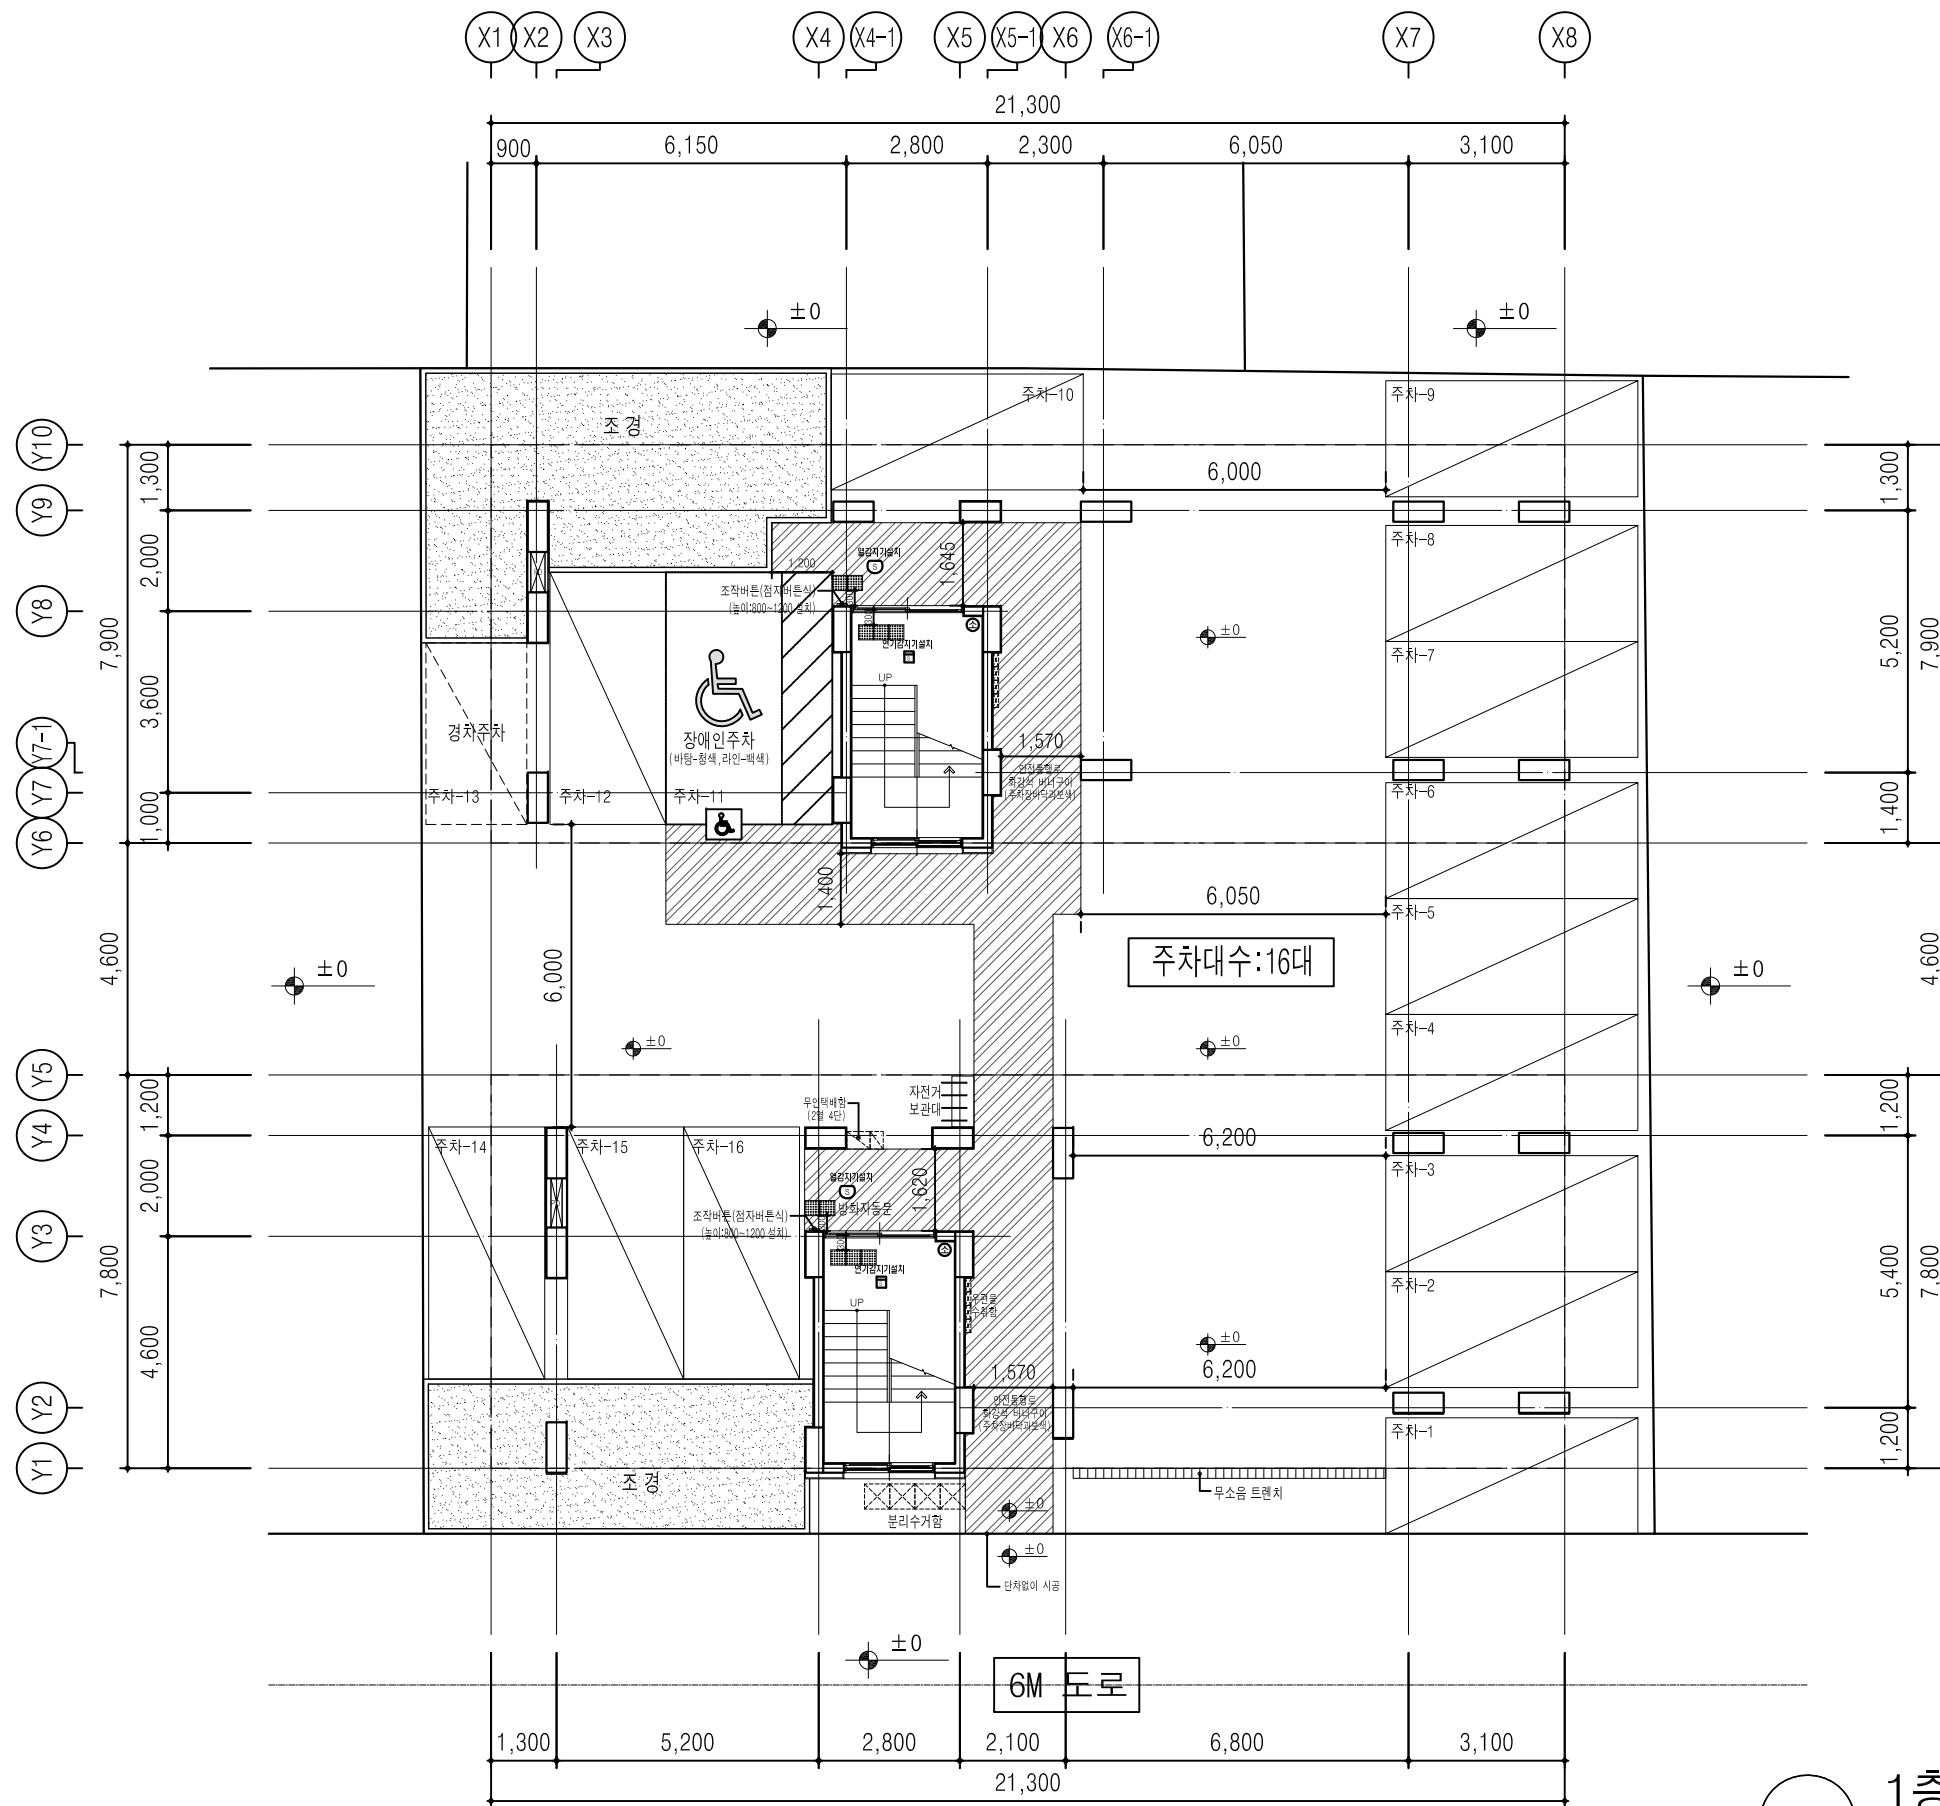


1층 평면도

SCALE : A3 : 1/150








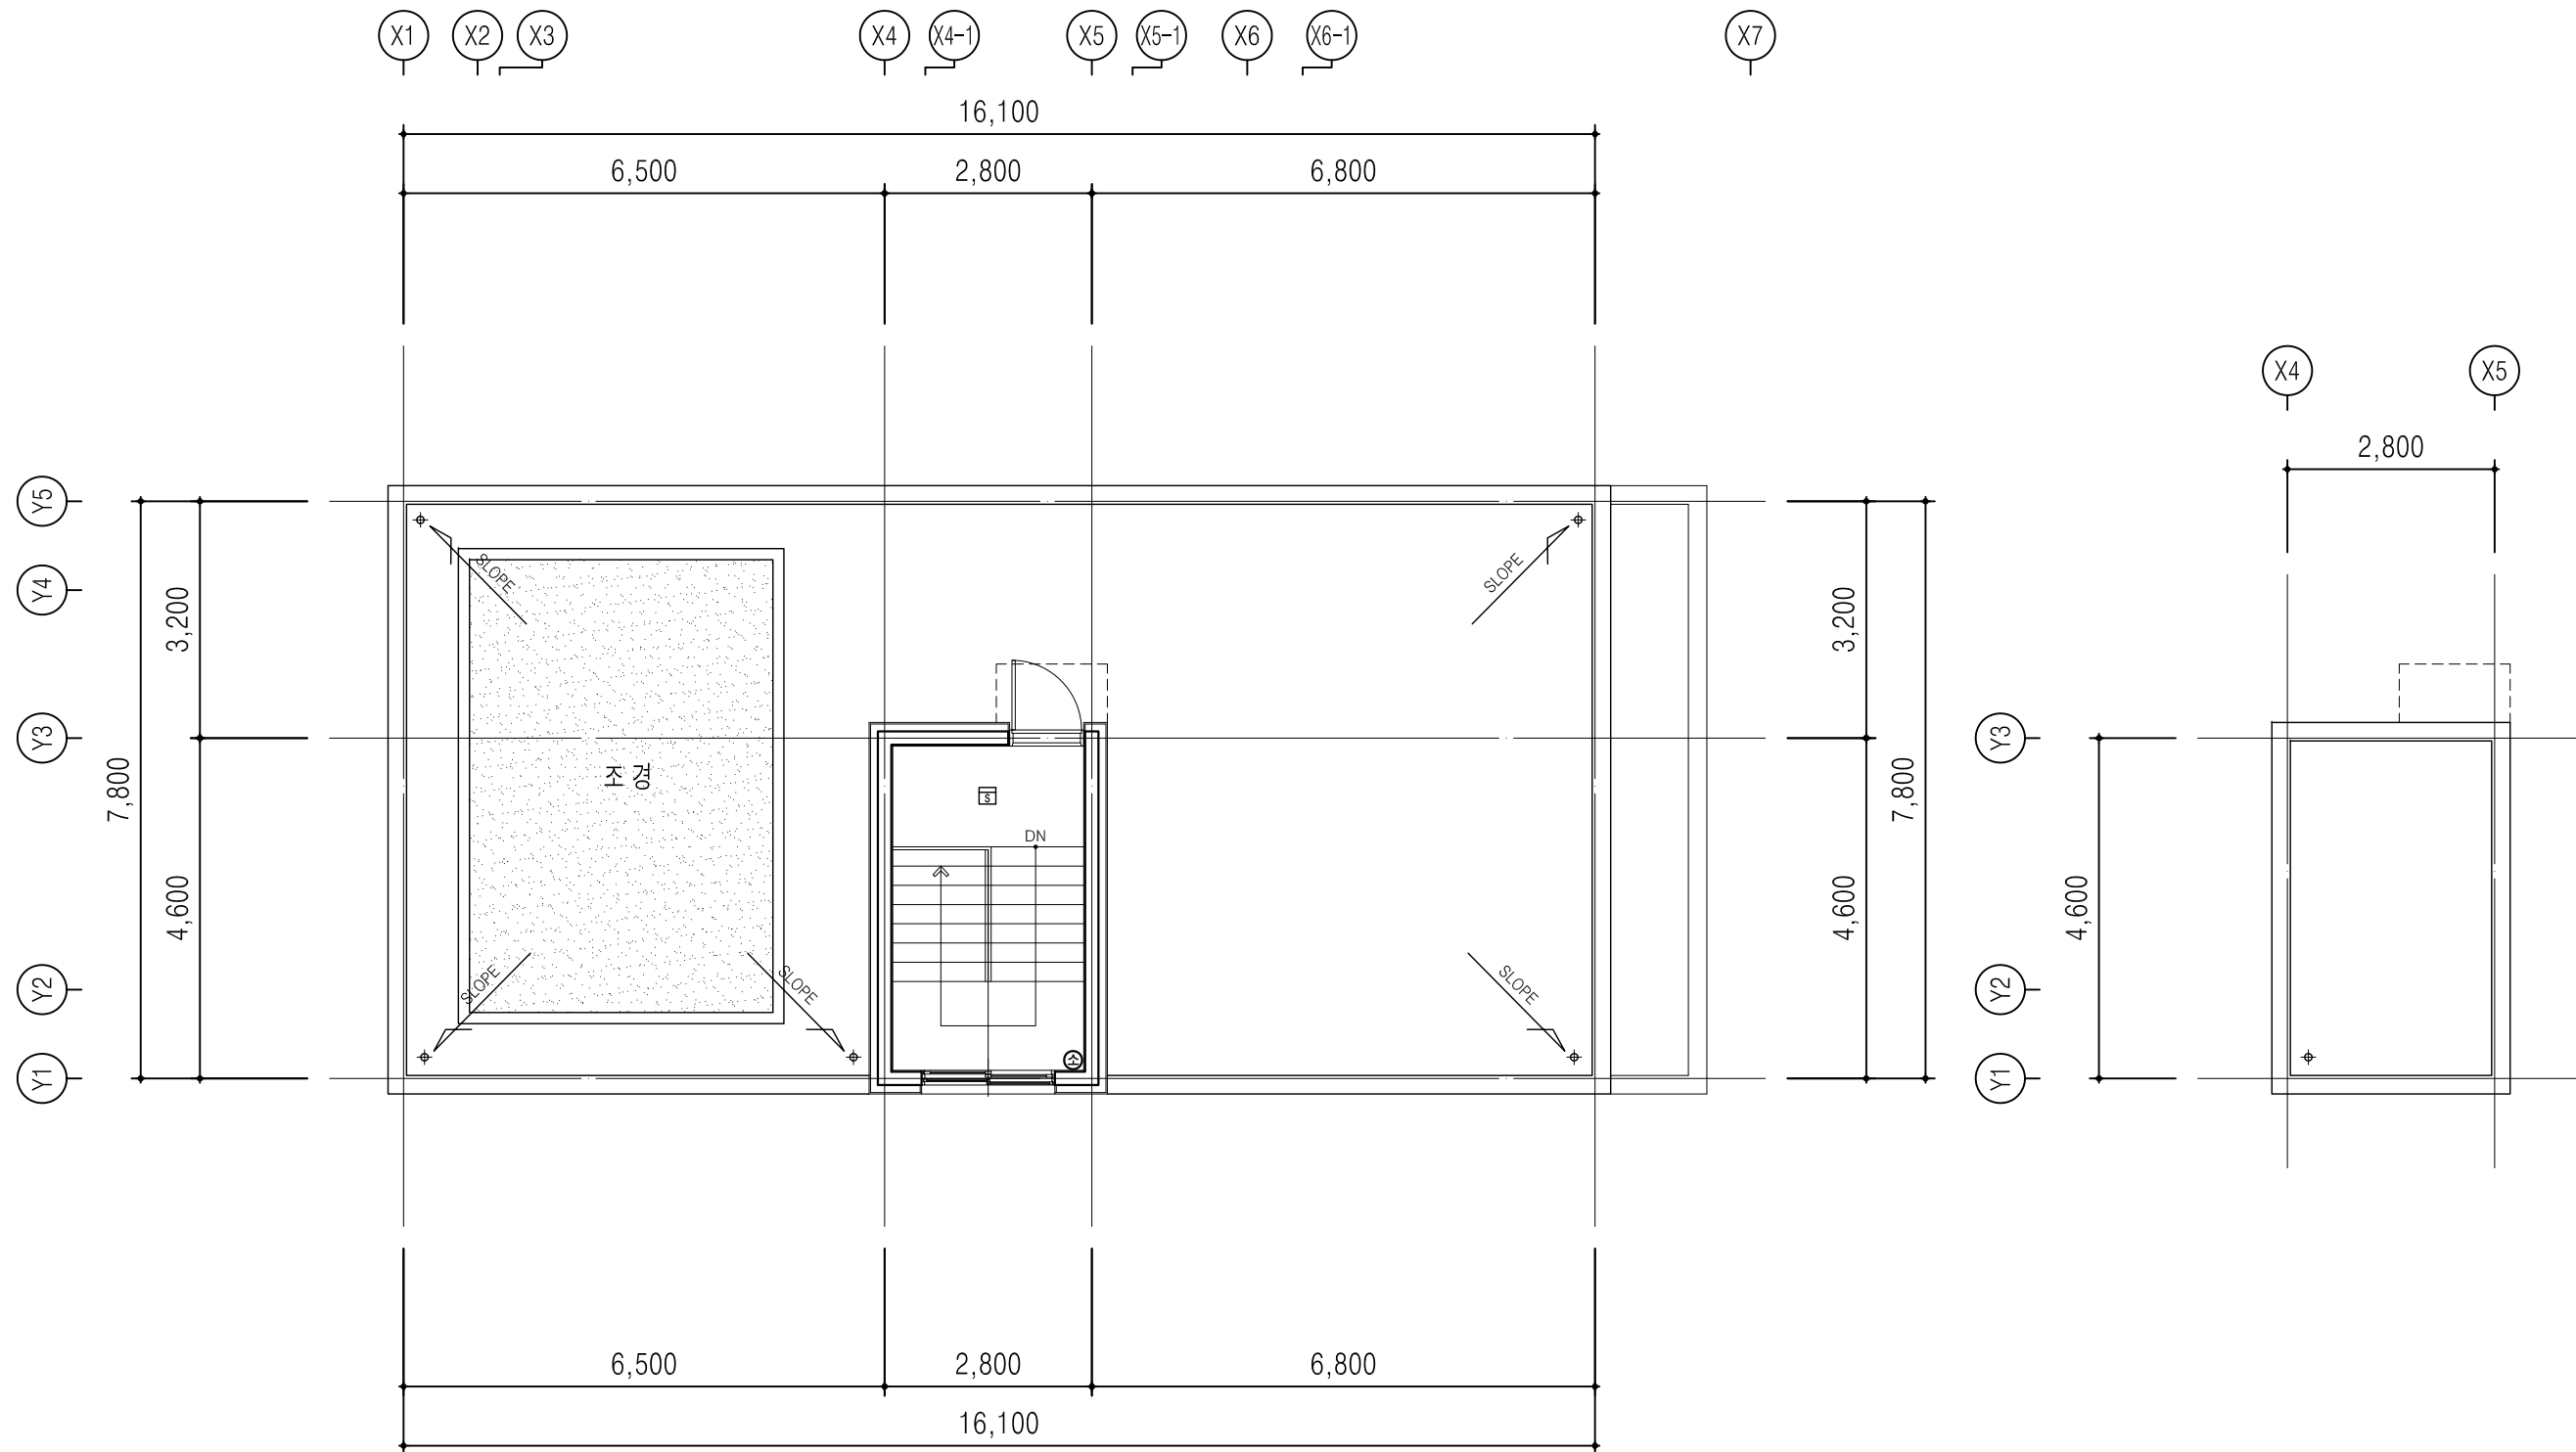







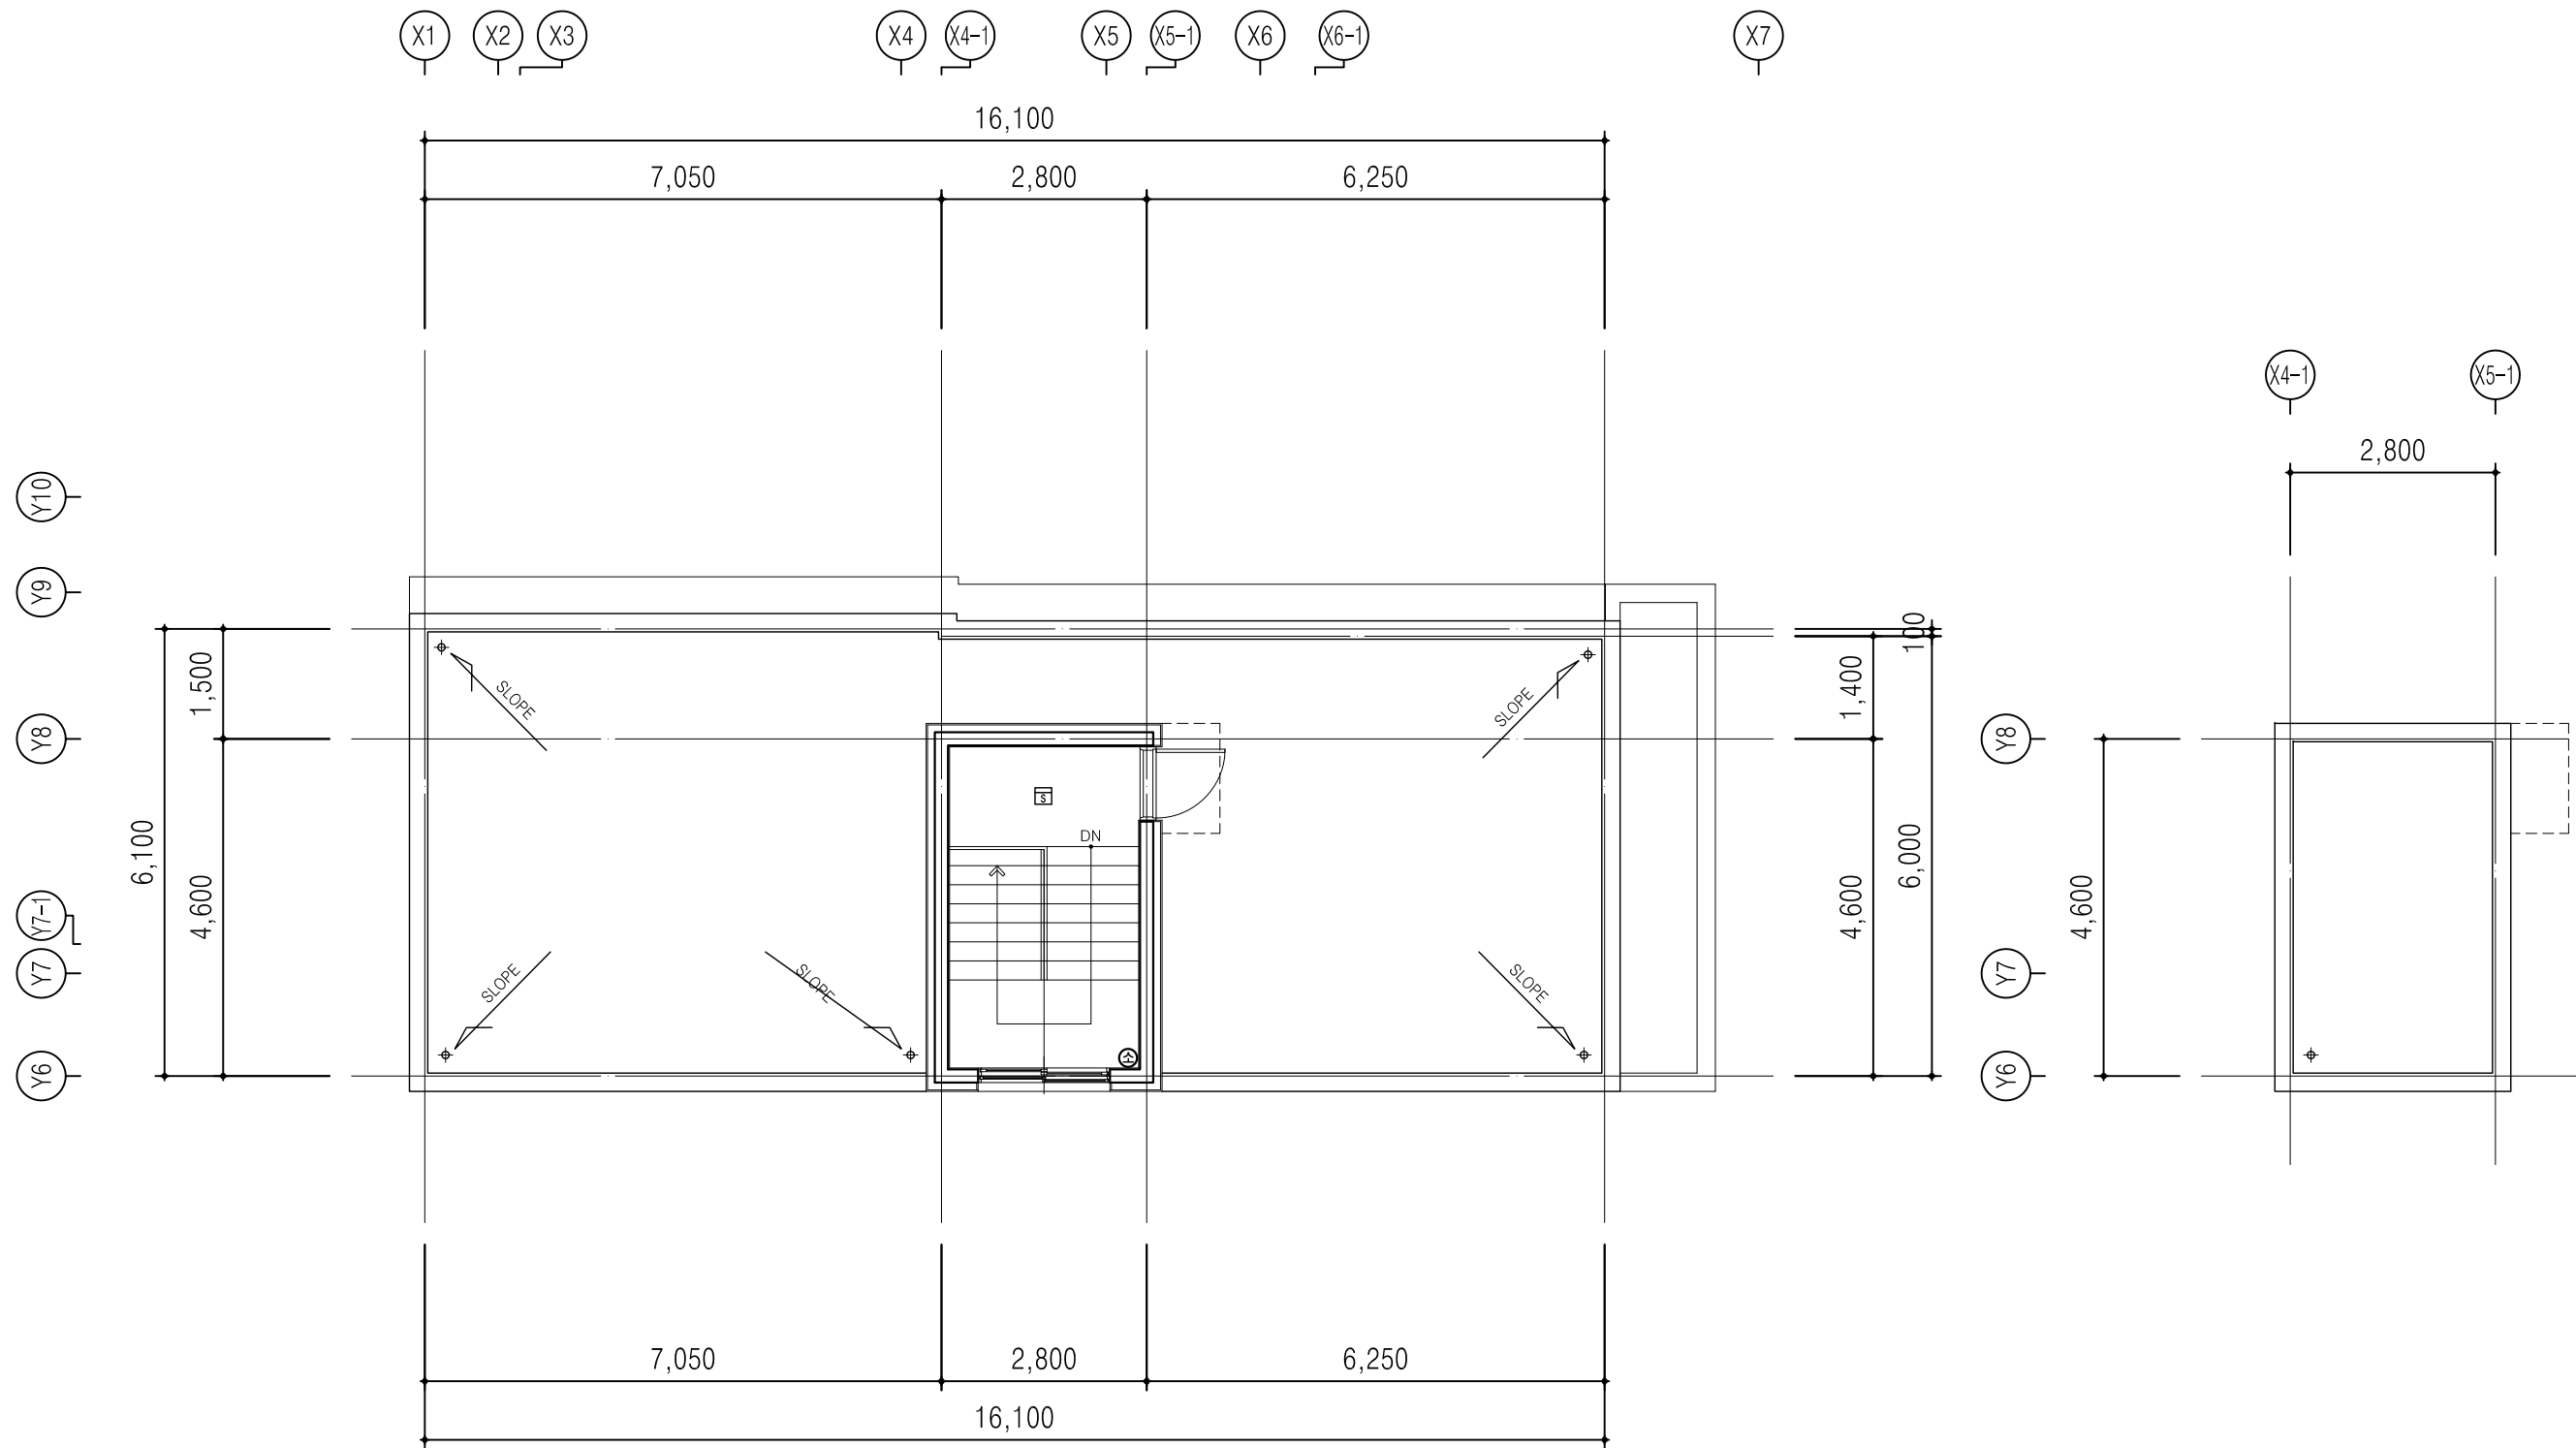

X1 X2 X3

X4 X4-1

X5 X5-1

X6 X6-1

X7

X8

Y1 Y2

Y3

Y4

Y5

화강석 마감

T22 복층유리 이중창

스텐레스 난간

화강석 마감

스텐레스 난간

차면시설

▽ 옥상지붕 바닥

▽ 5층 바닥

▽ 4층 바닥

▽ 3층 바닥

▽ 2층 바닥

▽ 1층 바닥

정면도  
SCALE : A3 : 1/120

우측면도  
SCALE : A3 : 1/120



배 면 도  
SCALE : A3 : 1/120

좌 측 면 도  
SCALE : A3 : 1/120

X1 X2 X3

X4 X4-1

X5 X5-1

X6 X6-1

X7

X8

Y6 Y7 Y7-1

Y8

Y9

Y10

화강석 마감

T22 복층유리 이중창

스텐레스 난간

화강석 마감

스텐레스 난간

차면시설

▽ 옥상지붕 바닥

▽ 5층 바닥

▽ 4층 바닥

▽ 3층 바닥

▽ 2층 바닥

▽ 1층 바닥

정면도  
SCALE : A3 : 1/120

우측면도  
SCALE : A3 : 1/120

X8

X7

X6-1

X6

X5-1

X5

X4-1

X4

X3

X2

X1

Y10

Y9

Y8

Y7-1

Y7

Y6

스텐레스 난간

T22 복층유리 이중창

차면시설

화강석 마감

스텐레스 난간

차면시설

화강석 마감

▽ 옥상지붕 바닥


▽ 5층 바닥

▽ 4층 바닥

▽ 3층 바닥


▽ 2층 바닥

▽ 1층 바닥

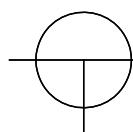

배 면 도

SCALE : A3 : 1/120

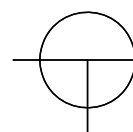

좌 측 면 도

SCALE : A3 : 1/120